


مصنع وتد الأخشاب · ملف التصميم

كوخ خشب دورين

15.00 × 10.00 م · دورين · 300 م² · مجلس رجال ومجلس نساء · 4 غرف (ماستر) · شرفتين · أرض بسور

المسقط الأفقي مع الفرش — الدور الأرضي

الأبعاد بالسنتيمتر - الجدران: قوائم 7×5 + تلبيس 2.5 من الجهتين (12 سم) | منسوب الأرضية +0.00

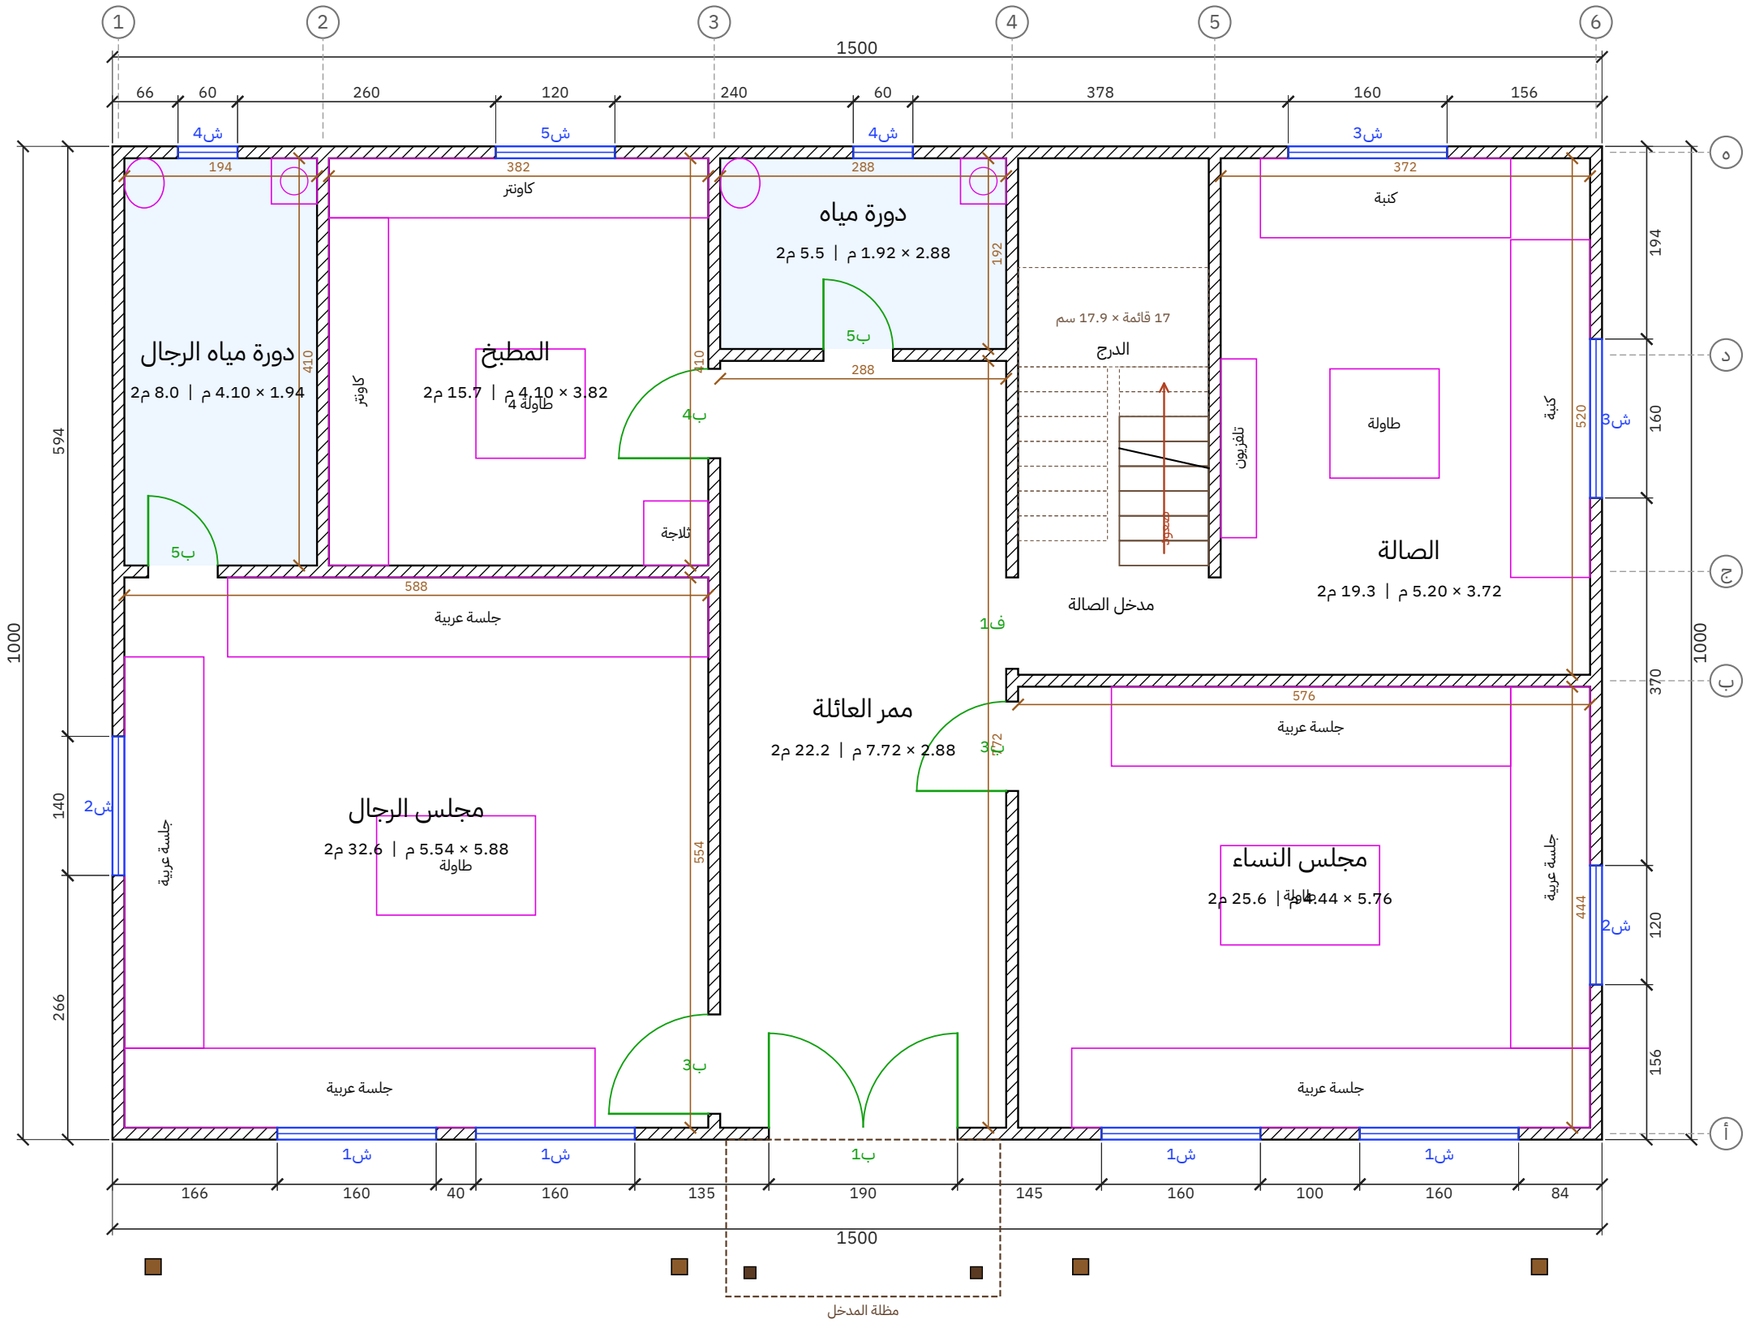


المشروع / العميل	عنوان اللوحة	المقياس	التاريخ	رقم اللوحة
كوخ خشب دورين — مجلس رجال ومجلس نساء + 4 غرف — 15.00 × 10.00 م (300 م²) **عميل — كوخ دورين**	**المسقط الأفقي — الدور الأرضي**	**1:50**	**2026-10-24**	**A-02 (2/12)**

مصنع وتد الأخشاب
Watad Wood Factory


المسقط الأفقي مع الفرش — الدور الأول

الأبعاد بالسنتيمتر - الجدران: قوائم 7×5 + تلبيس 2.5 من الجهتين (12 سم) | منسوب الأرضية +3.05

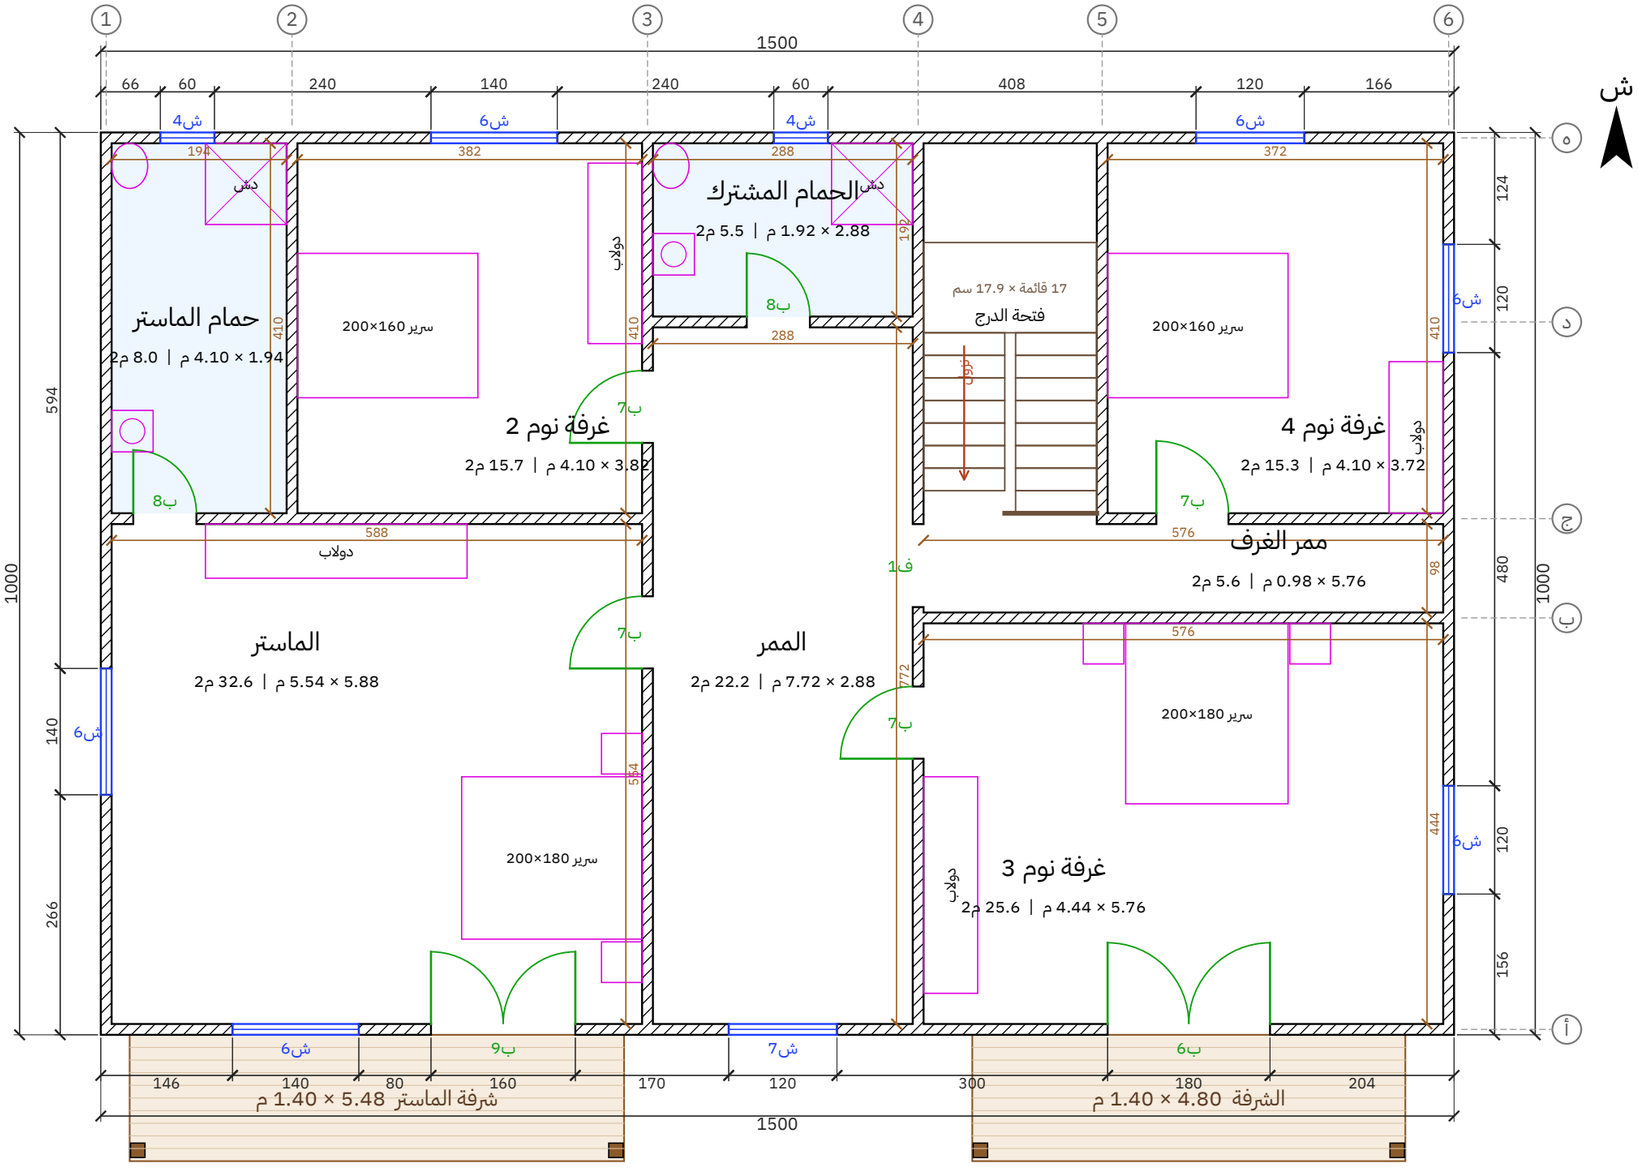


المشروع / العميل	عنوان اللوحة	المقياس	التاريخ	رقم اللوحة
كوخ خشب دورين — مجلس رجال ومجلس نساء + 4 غرف — 15.00 × 10.00 م (300 م²) عميل — كوخ دورين	المسقط الأفقي — الدور الأول	1:50	2026-10-24	A-03 (3/12)

مصنع وتد الأخشاب
Watad Wood Factory

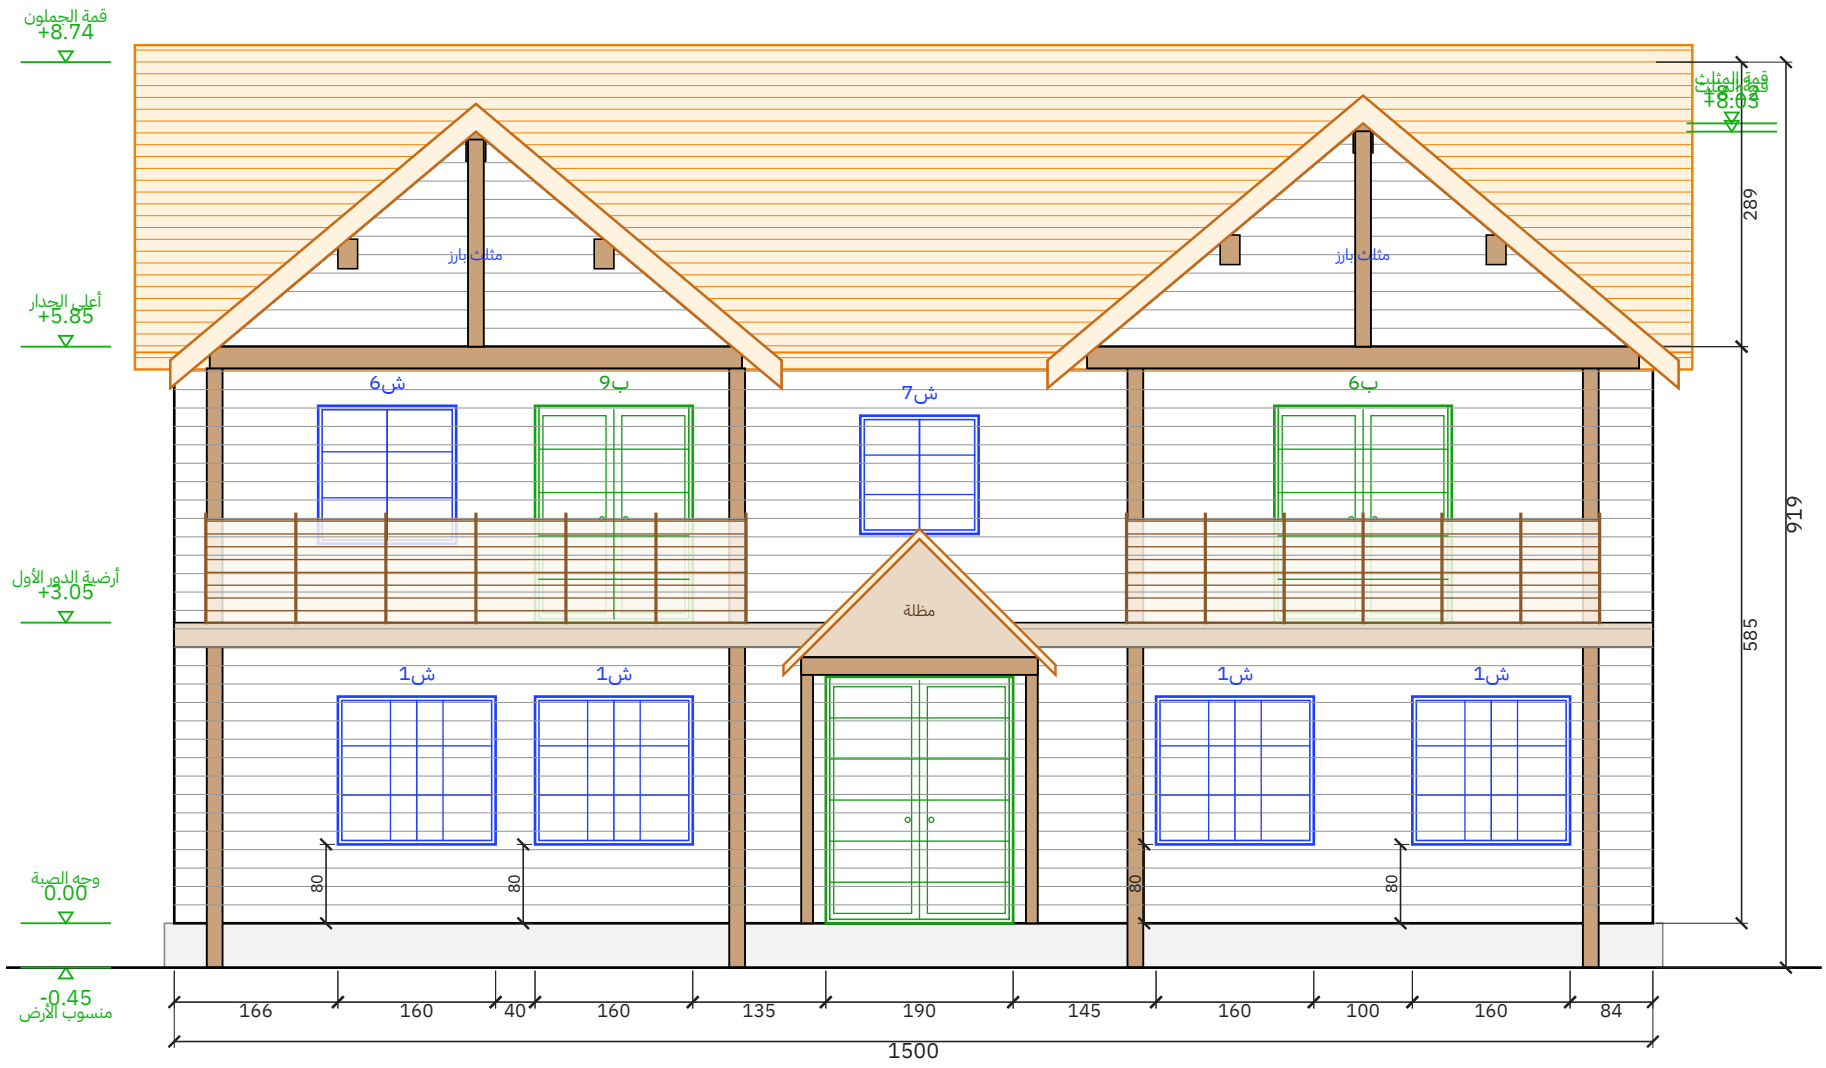

الواجهة الأمامية


مقياس 1:50 | الوحدة: سم

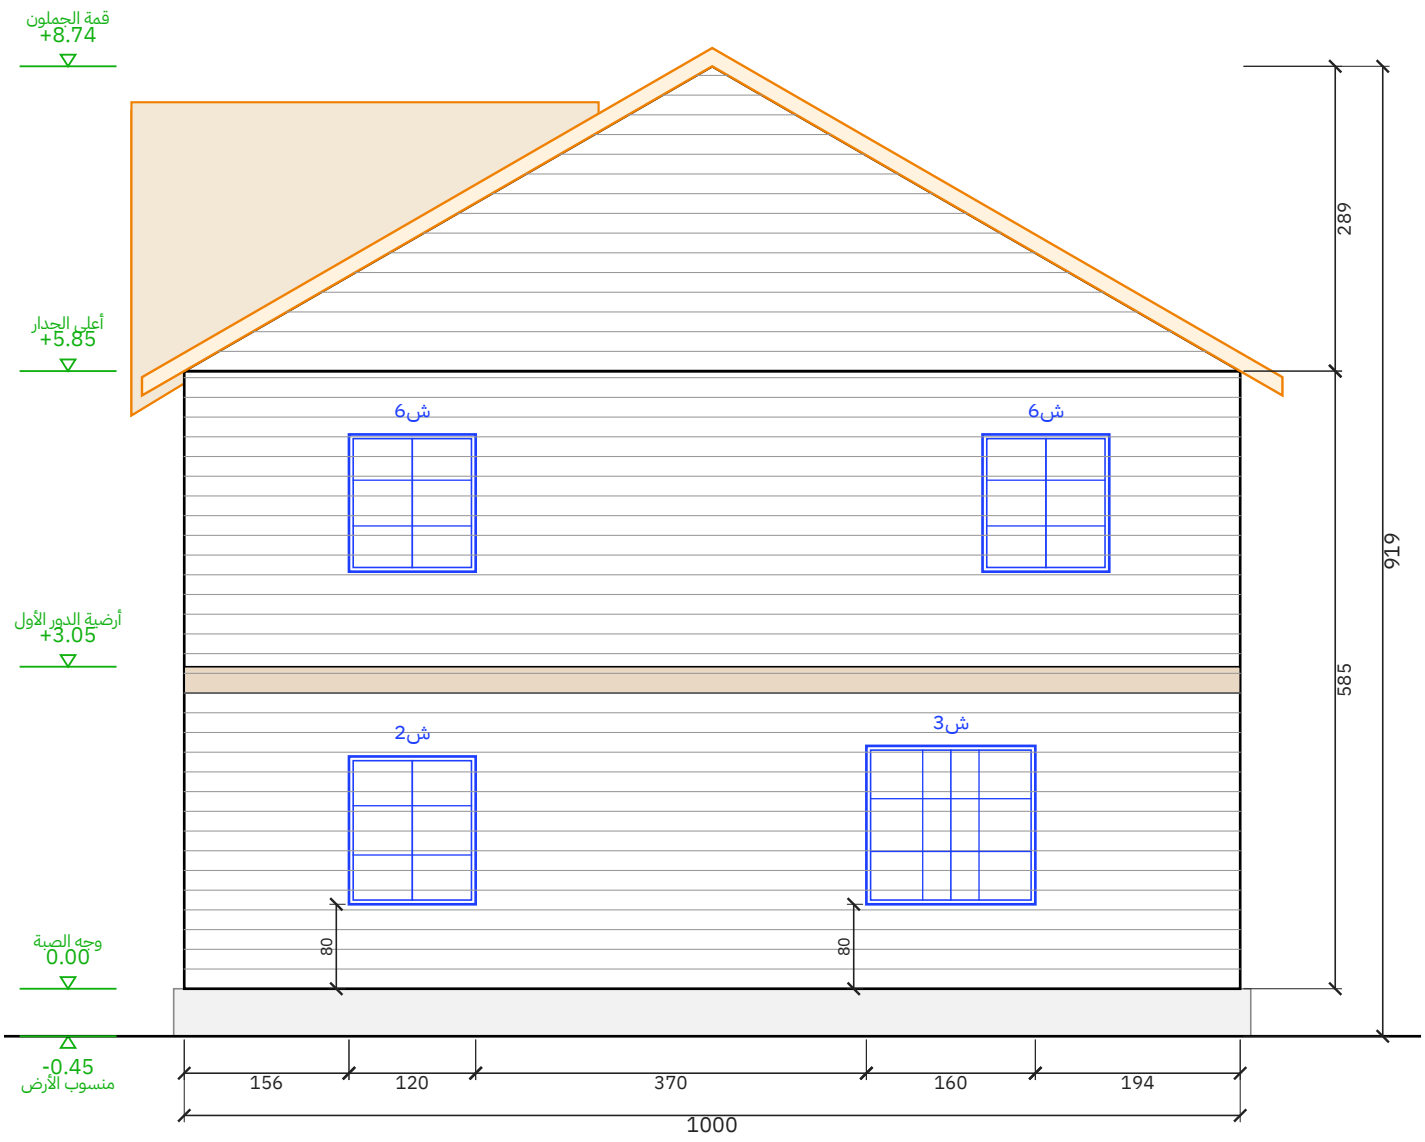

الواجهة الشرقية


مقياس 1:50 | الوحدة: سم

المشروع / العميل	عنوان اللوحة	المقياس	التاريخ	رقم اللوحة
مصنع وتد الأخشاب — Watad Wood Factory كوخ خشب دورين — مجلس رجال ومجلس نساء + 4 غرف — 10.00 × 15.00 م (300 م²) عميل — كوخ دورين	الواجهة الأمامية والواجهة الشرقية	1:50	2026-10-24	A-04 (4/12)

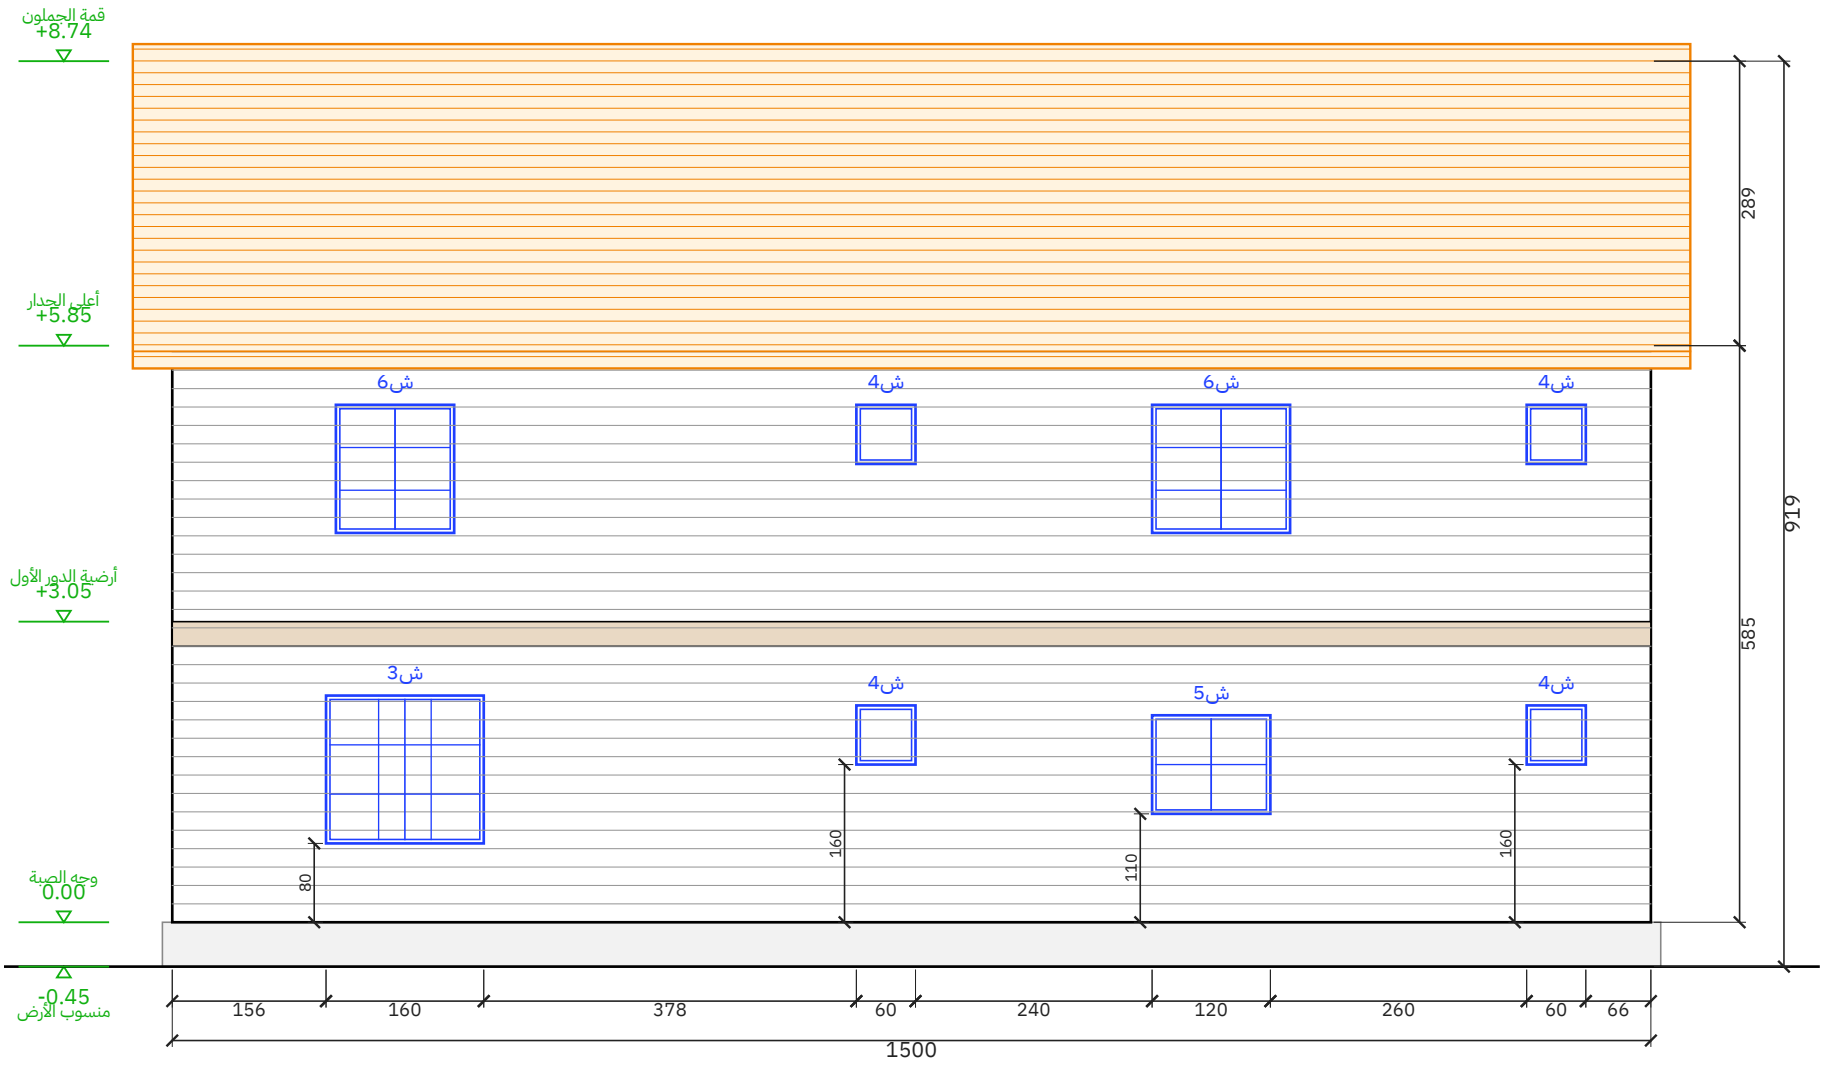

الواجهة الخلفية

مقياس 1:50 | الوحدة: سم

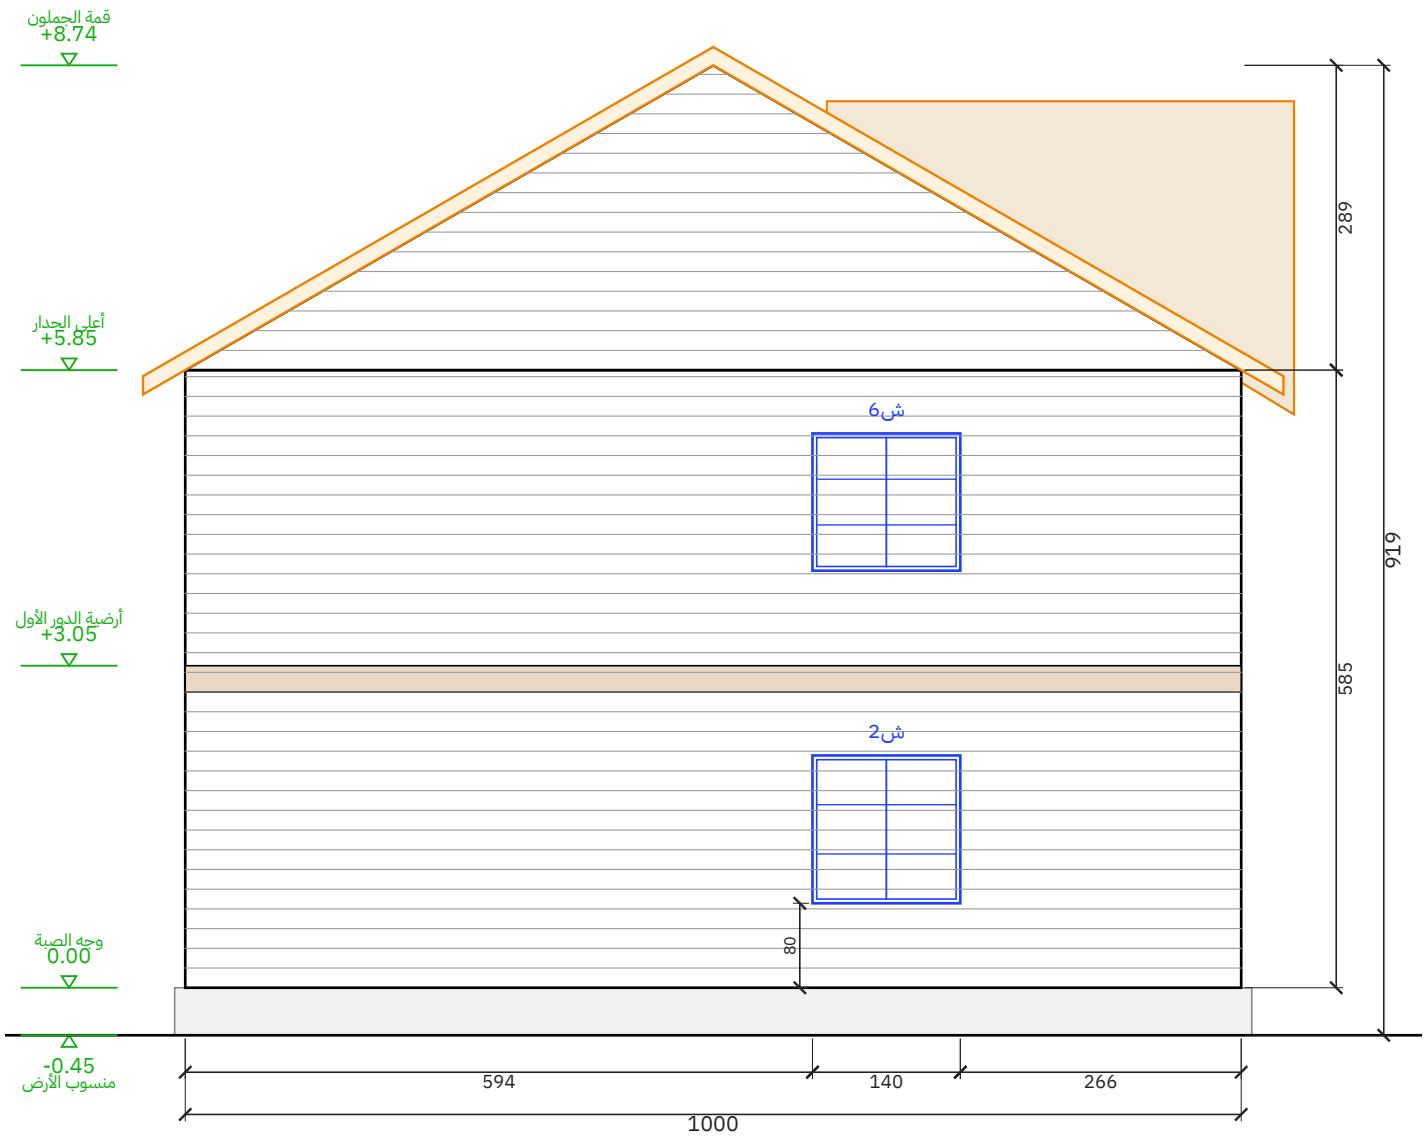

الواجهة الغربية


مقياس 1:50 | الوحدة: سم

المشروع / العميل	عنوان اللوحة	المقياس	التاريخ	رقم اللوحة
كوخ خشب دورين – مجلس رجال ومجلس نساء + 4 غرف – 10.00 × 15.00 م (300 م²) عميل – كوخ دورين	الواجهة الخلفية والواجهة الغربية	1:50	2026-10-24	A-05 (5/12)


مصنع وتد الأخشاب
Watad Wood Factory

قطاع عرضي أ-أ

مقياس 1:50 | الوحدة: سم

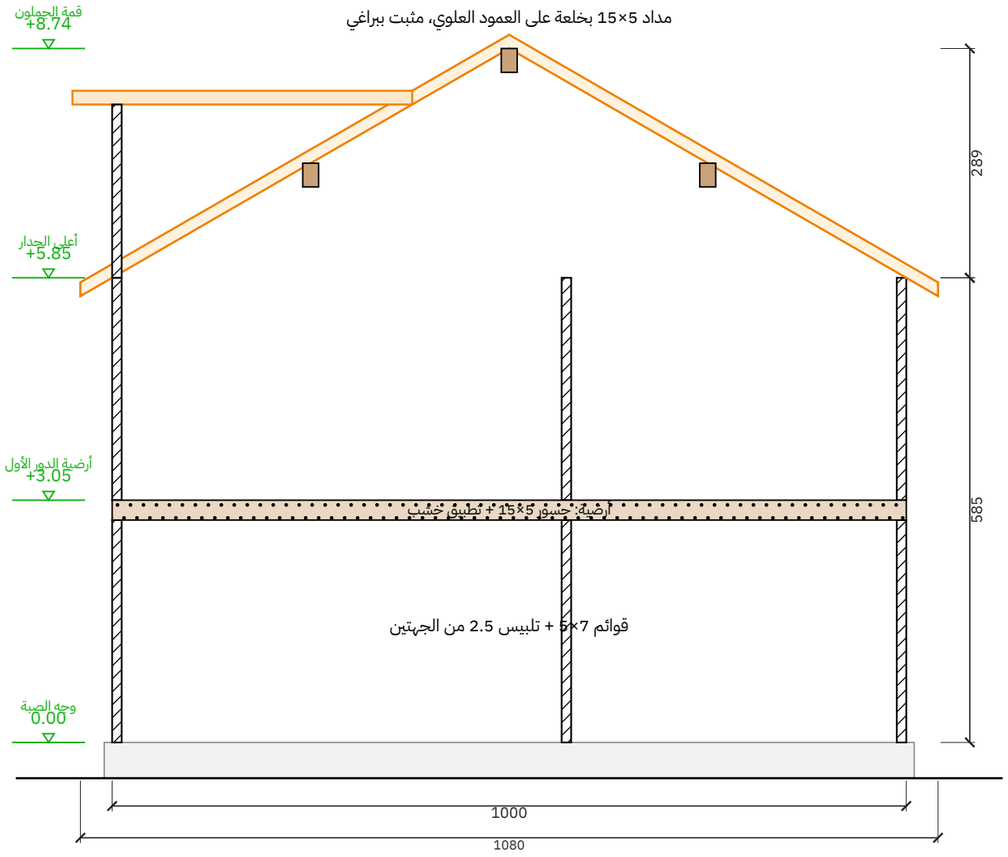


تفصيلة جلوس المداد على العلوي (1:5)

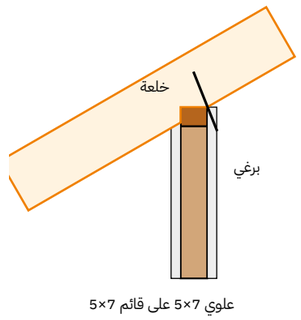

علوي 7×5 على قائم 7×5

مسقط السقف (جملون)

رفرف 40 سم من كل جهة | مقياس 1:50

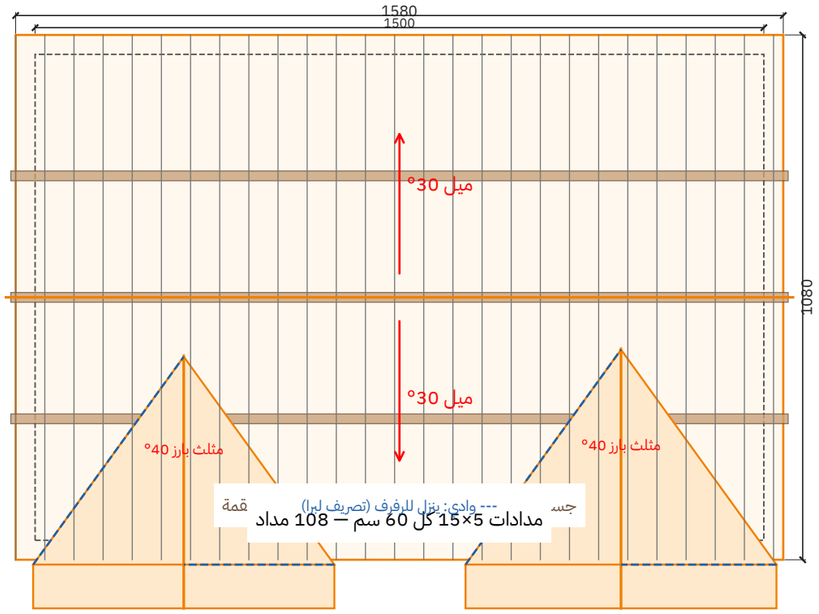

المشروع / العميل	عنوان اللوحة	المقياس	التاريخ	رقم اللوحة
كوخ خشب دورين — مجلس رجال ومجلس نساء + 4 غرف — 15.00 × 10.00 م (300 م²) **عميل — كوخ دورين**	**مسقط السقف والقطاع**	**1:50**	**2026-10-24**	**A-06 (6/12)**


مصنع وتد الأخشاب
Watad Wood Factory

لقطات المنظور الخارجي

المنظور الأمامي




منظور أمامي من اليسار

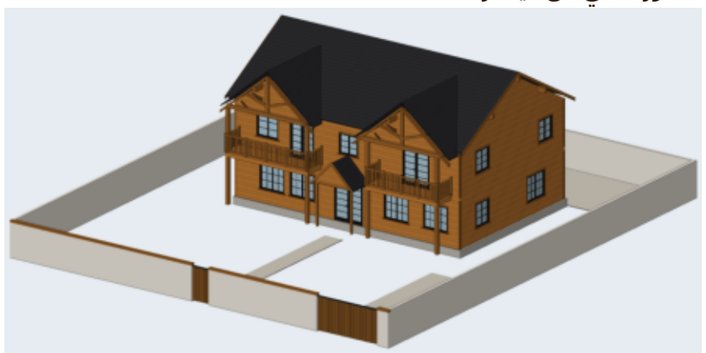


منظور أمامي من اليمين




المنظور الخلفي

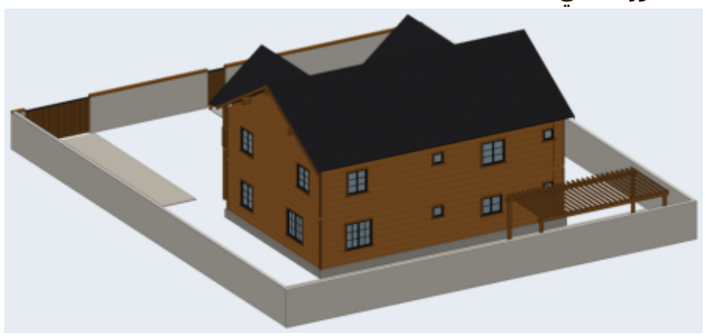

منظور خلفي من اليمين

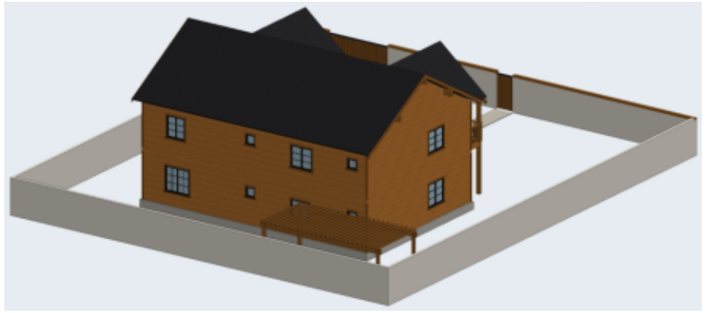

منظر علوي

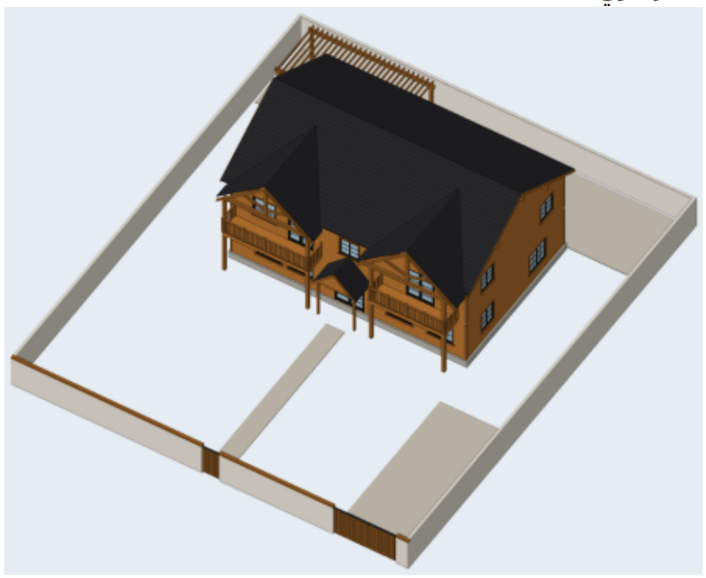

مصنع وتد الأخشاب Watad Wood Factory	المشروع / العميل كوخ خشب دورين – مجلس رجال ومجلس نساء + 4 غرف – 15.00 × 10.00 م (300 م²) عميل – كوخ دورين	عنوان اللوحة لقطات المنظور	المقياس –	التاريخ 2026-10-24	رقم اللوحة A-09 (9/12)

المقطع العلوي بالفرش — الدور الأرضي


مقطع أفقي على ارتفاع 1.90 م — توزيع الفرش ومسار الحركة



مصنع وتد الأخشاب Watad Wood Factory	المشروع / العميل كوخ خشب دورين — مجلس رجال ومجلس نساء + 4 غرف — 15.00 × 10.00 م (300 م²) عميل — كوخ دورين	عنوان اللوحة المقطع العلوي بالفرش — الدور الأرضي	المقياس —	التاريخ 2026-10-24	رقم اللوحة A-10 (10/12)

المقطع العلوي بالفرش — الدور الأول

مقطع أفقي على ارتفاع 1.90 م — توزيع الفرش ومسار الحركة

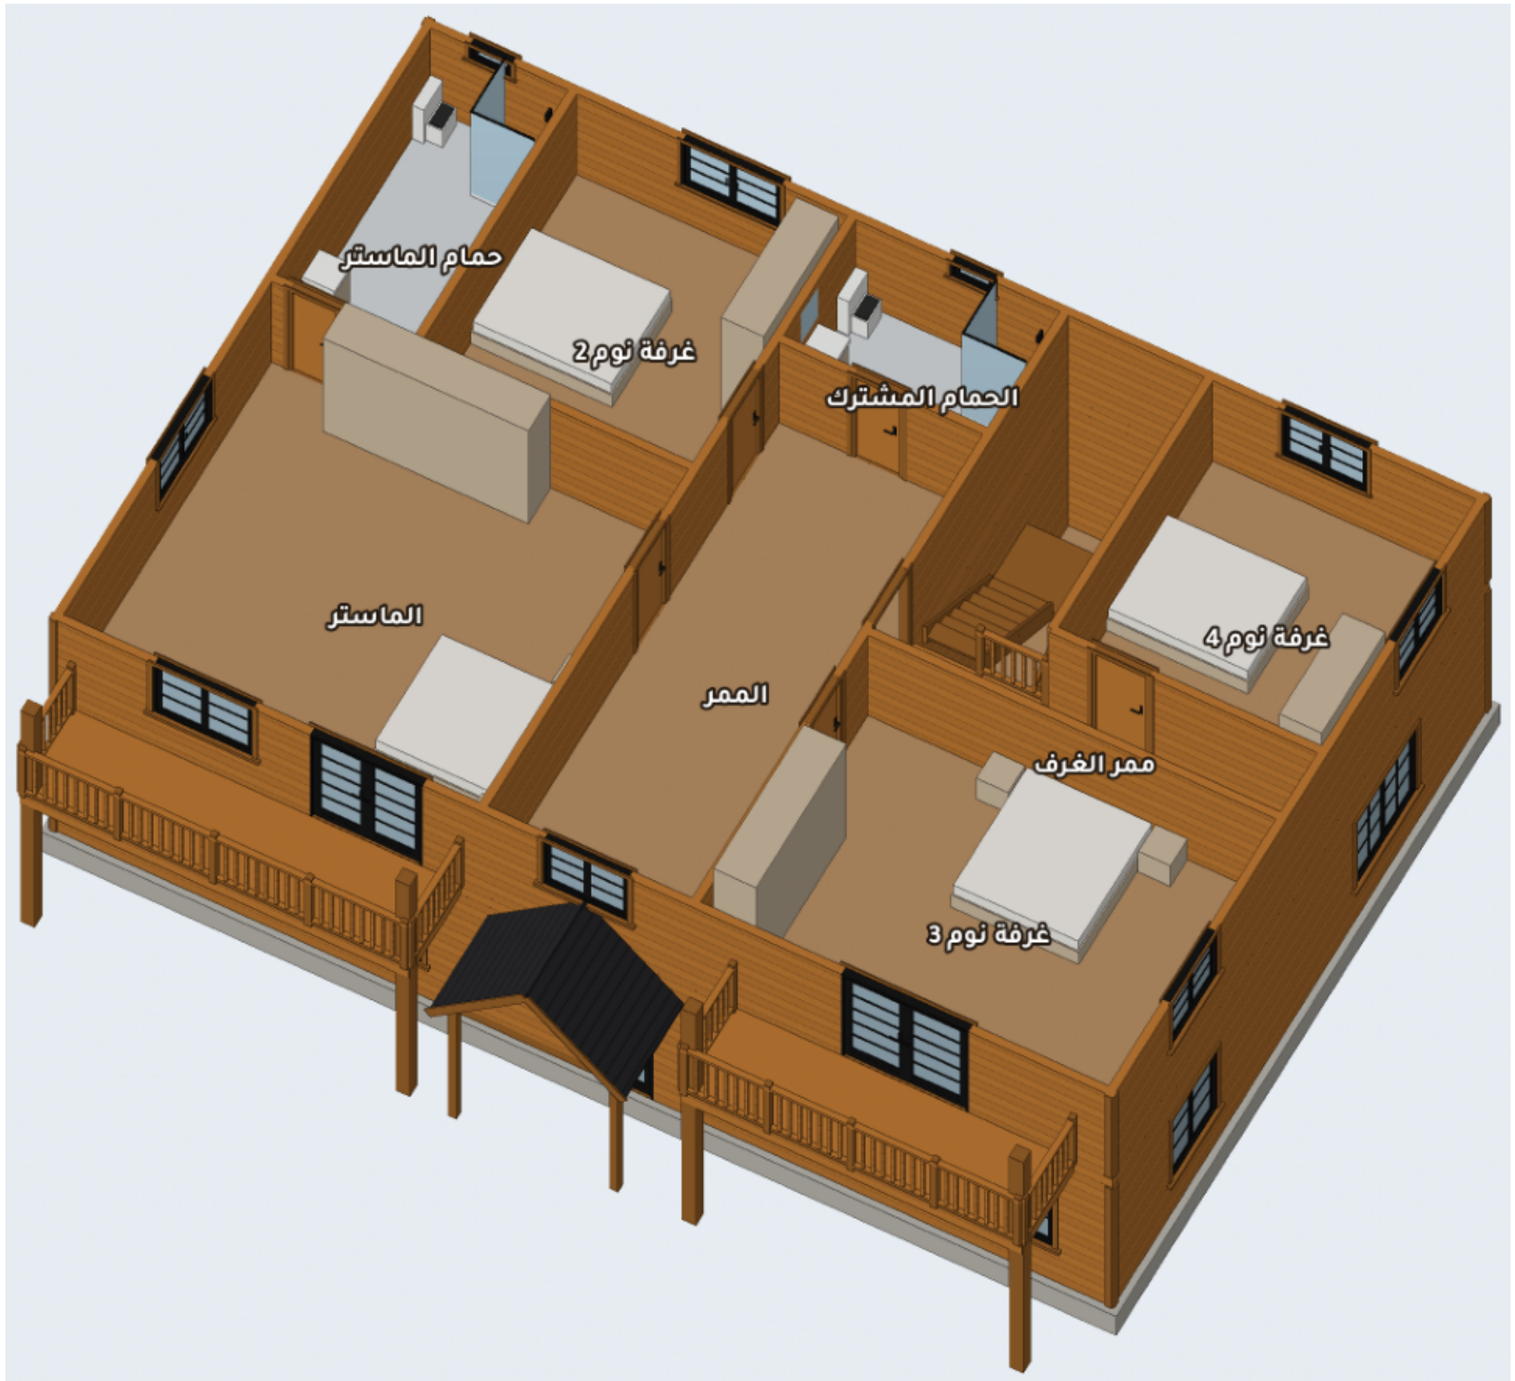

مصنع وتد الأخشاب Watad Wood Factory	المشروع / العميل كوخ خشب دورين — مجلس رجال ومجلس نساء + 4 غرف — 15.00 × 10.00 م (300 م²) عميل — كوخ دورين	عنوان اللوحة المقطع العلوي بالفرش — الدور الأول	المقياس —	التاريخ 2026-10-24	رقم اللوحة A-11 (11/12)

أمامي من اليسار – من الحديقة · الخارج – نهاراً



مصنع وتد الأخشاب

أمامي من اليمين – من الموقف · الخارج – نهاراً





مصنع وتد الأخشاب

منظر علوي – الأرض والسور · الخارج – نهاراً



مصنع وتد الأخشاب



مصنع وتد الأخشاب



مصنع وتد الأخشاب



مصنع وتد الأخشاب



مصنع وتد الأخشاب



مصنع وتد الأخشاب



مصنع وتد الأخشاب



مصنع وتد الأخشاب




مصنع وتد الأخشاب

جدول مساحات الموقع

البند	المقاس	المساحة (م²)
مساحة الأرض	24.88 × 29.00 م	721.5
مسطح الكوخ (البصمة)	15.00 × 10.00 م	150.0
جلسة خارجية	8.00 × 3.80 م	30.4
بلاط		88.1
موقف سيارة	4.68 × 10.90 م	51.0
ممر	1.20 × 12.44 م	14.9
المسطحات الخضراء (حديقة)	الباقي	387.1

الموقع العام وتنسيق الحديقة (لاندسكيب)

الأرض 25 × 29 م = 722 م² | الأبعاد بالسنتيمتر

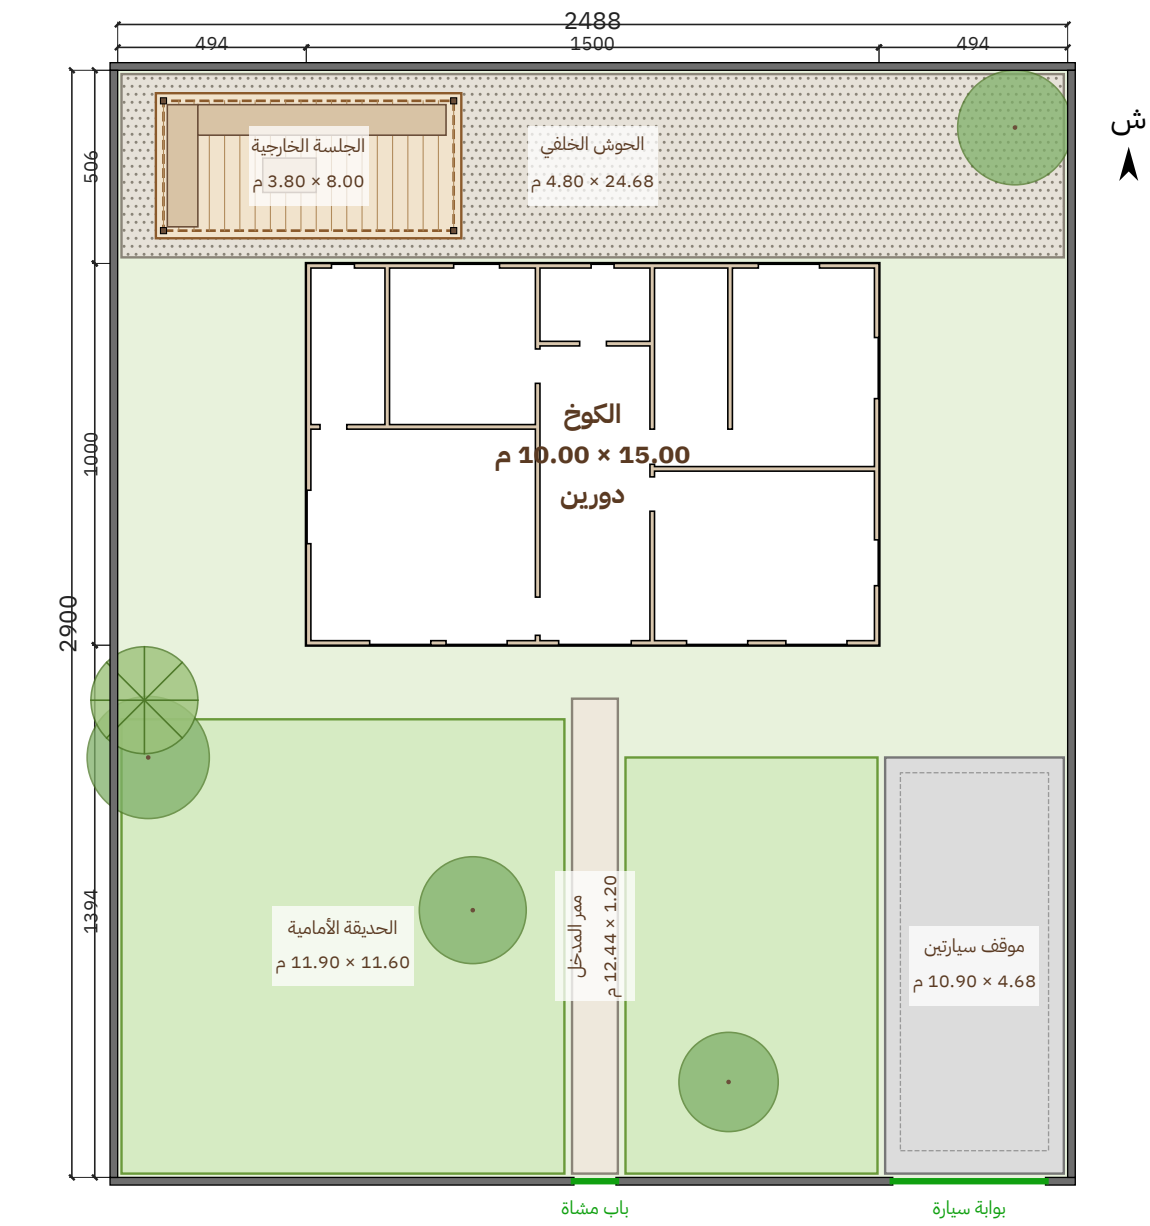

المشروع / العميل	عنوان اللوحة	المقياس	التاريخ	رقم اللوحة
كوخ خشب دورين — مجلس رجال ومجلس نساء + 4 غرف — 10.00 × 15.00 م (300 م²) عميل — كوخ دورين	الموقع العام واللاندسكيب	1:200	2026-10-24	A-01 (1/12)

مصنع وتد الأخشاب
Watad Wood Factory

جدول مقاسات الأبواب والشبابيك

مقاس الفتحة الصافي في الجدار - الوحدة: سم

الرمز	النوع	العرض (سم)	الارتفاع (سم)	ارتفاع الجلسة (سم)	العدد	الموقع
ب1	باب مزدوج	190	250	-	1	الأمامية
ب3	باب	100	220	-	1	مجلس الرجال
ب3	باب	90	210	-	1	مجلس النساء
ب4	باب	90	210	-	1	المطبخ
ب5	باب	70	210	-	2	دورة مياه الرجال - دورة مياه
ب6	باب مزدوج	180	220	-	1	الأمامية
ب7	باب	80	210	-	4	الماستر - غرفة 2 - غرفة 3 - غرفة 4
ب8	باب	70	210	-	2	حمام الماستر - الحمام المشترك
ب9	باب مزدوج	160	220	-	1	الأمامية
ف1	باب	92	220	-	2	الممر — الصالة - الممر — الدرج
ش1	شباك	160	150	80	4	الأمامية 4
ش2	شباك	120	140	80	1	الشرقية
ش2	شباك	140	140	80	1	الغربية
ش3	شباك	160	150	80	2	الشرقية - الخلفية
ش4	شباك	60	60	160	4	الخلفية 4
ش5	شباك	120	100	110	1	الخلفية
ش6	شباك	140	140	80	1	الأمامية
ش6	شباك	120	130	90	3	الشرقية 2 - الخلفية
ش6	شباك	140	130	90	2	الخلفية - الغربية
ش7	شباك	120	120	90	1	الأمامية

الإجمالي: أبواب 16 - شبابيك 20

المنظور ثلاثي الأبعاد والمواد

النمط: جوزي غامق + إطارات سوداء — رندر واقعي بخامات حقيقية



جدول المواد والألوان

الخشب / الصبغة

صبغة عسلي / سيدر

القرميد

قرميد رمادي غامق

الزجاج

زجاج شفاف

إطارات الشبابيك والأبواب

إطار ألمنيوم أسود

الكنار والزوايا

نفس الصبغة أغمق درجة


الصبة

خرسانة 45 سم


الدربزين: ألواح أفقية متقاربة (عصري)

تقسيم الشبابيك: شبكة | الباب الرئيسي: زجاج بتقسيمات (فرنسي)

أنواع الدربزين المعتمدة (من مشاريع المصنع)

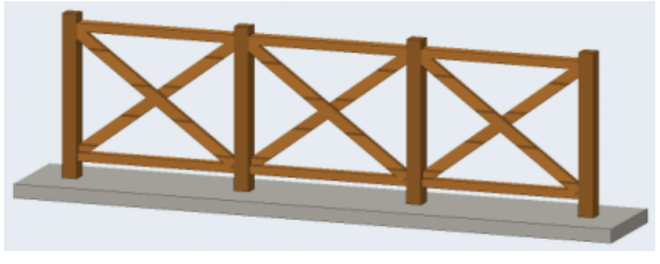

تقاطع X (صورة 5)

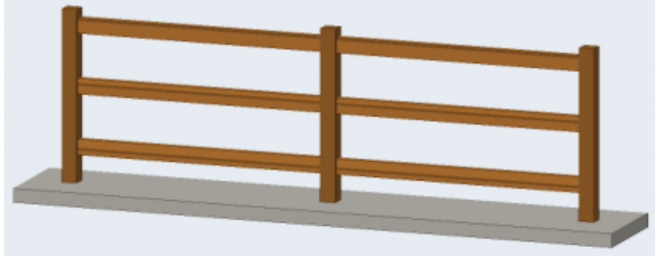

3 مرابيع أفقية (صورة 2)



قوائم رأسية متقاربة (صورة 1)

المشروع / العميل	عنوان اللوحة	المقياس	التاريخ	رقم اللوحة
كوخ خشب دورين — مجلس رجال ومجلس نساء + 4 غرف — 15.00 × 10.00 م (300 م²) **عميل — كوخ دورين**	**المنظور والمواد**	**—**	**2026-10-24**	**A-12 (12/12)**

مصنع وتد الأخشاب
Watad Wood Factory

جدول المساحات وبيانات المشروع

بيانات المشروع

البند	البيان
المشروع	كوخ خشب دورين — مجلس رجال ومجلس نساء + 4 غرف — 15.00 × 10.00 م (300 م²)
العميل	عميل — كوخ دورين
الموقع	—
الاستخدام	سكن عائلي
التاريخ	2026-10-24
نظام البناء	هيكل خشب 5×7 + تلبيس 2.5 سم من الجهتين
السقف	جملون 30° — قرميد معدني + 2 مثلث بارز

جدول المساحات

م	الفراغ	الأبعاد (م)	المساحة (م2)
1	أرضي — مجلس الرجال	5.88 × 5.54	32.58
2	أرضي — دورة مياه الرجال	1.94 × 4.10	7.95
3	أرضي — المطبخ	3.82 × 4.10	15.66
4	أرضي — ممر العائلة	2.88 × 7.72	22.23
5	أرضي — دورة مياه	2.88 × 1.92	5.53
6	أرضي — مجلس النساء	5.76 × 4.44	25.57
7	أرضي — مدخل الصالة	1.92 × 1.04	2.00
8	أرضي — الدرج	1.92 × 4.10	7.87
9	أرضي — الصالة	3.72 × 5.20	19.34
10	أول — الماستر	5.88 × 5.54	32.58
11	أول — حمام الماستر	1.94 × 4.10	7.95
12	أول — غرفة نوم 2	3.82 × 4.10	15.66
13	أول — الممر	2.88 × 7.72	22.23
14	أول — الحمام المشترك	2.88 × 1.92	5.53
15	أول — غرفة نوم 3	5.76 × 4.44	25.57
16	أول — ممر الغرف	5.76 × 0.98	5.64
17	أول — غرفة نوم 4	3.72 × 4.10	15.25
	المساحة الصافية الداخلية		269.17
	الشرفة	**4.80 × 1.40**	**6.72**
	شرفة الماستر	**5.48 × 1.40**	**7.67**
	المساحة الإجمالية المبنية	**15.00 × 10.00 × 2 دور**	**300.00**
	المساحة الكلية (المبنية + التراسات)		**314.39**