# المنظور ثلاثي الأبعاد والمواد

النمط: جوزي غامق + إطارات سوداء — رندر واقعي بخامات حقيقية



## جدول المواد والألوان

**الخشب / الصبغة**

صبغة عسلي / سيدر

**القرميد**

قرميد رمادي غامق

**الزجاج**

زجاج شفاف

**إطارات الشبابيك والأبواب**

إطار ألمنيوم أسود

**الكنار والزوايا**

نفس الصبغة أغمق درجة


**الصبة**

خرسانة 45 سم


الدربزين: ألواح أفقية متقاربة (عصري)

تقسيم الشبابيك: شبكة | الباب الرئيسي: زجاج بتقسيمات (فرنسي)

## أنواع الدربزين المعتمدة (من مشاريع المصنع)

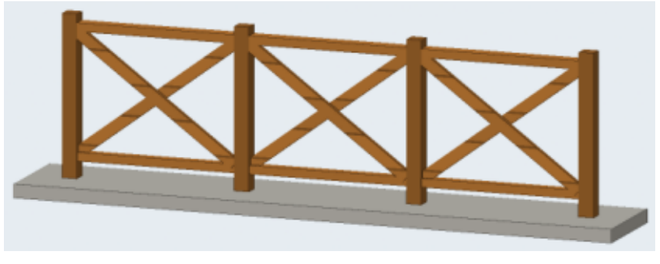

تقاطع X (صورة 5)

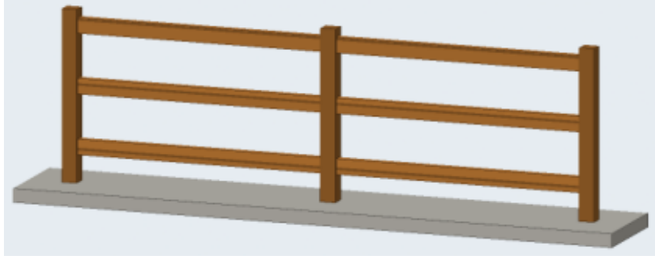

3 مرابيع أفقية (صورة 2)




قوائم رأسية متقاربة (صورة 1)

| المشروع / العميل | عنوان اللوحة | المقياس | التاريخ | رقم اللوحة |
|---|---|---|---|---|
| **كوخ خشب دورين — مجلس رجال ومجلس نساء + 4 غرف — 15.00 × 10.00 م (300 م²)**<br>**عميل — كوخ دورين** | **المنظور والمواد** | **1:50** | **2026-10-24** | **W-01 (1/23)** |

**مصنع وتد الأخشاب**
Watad Wood Factory

# المسقط الأفقي مع الفرش — الدور الأرضي

الأبعاد بالسنتيمتر - الجدران: قوائم 7×5 + تلبيس 2.5 من الجهتين (12 سم) | منسوب الأرضية +0.00

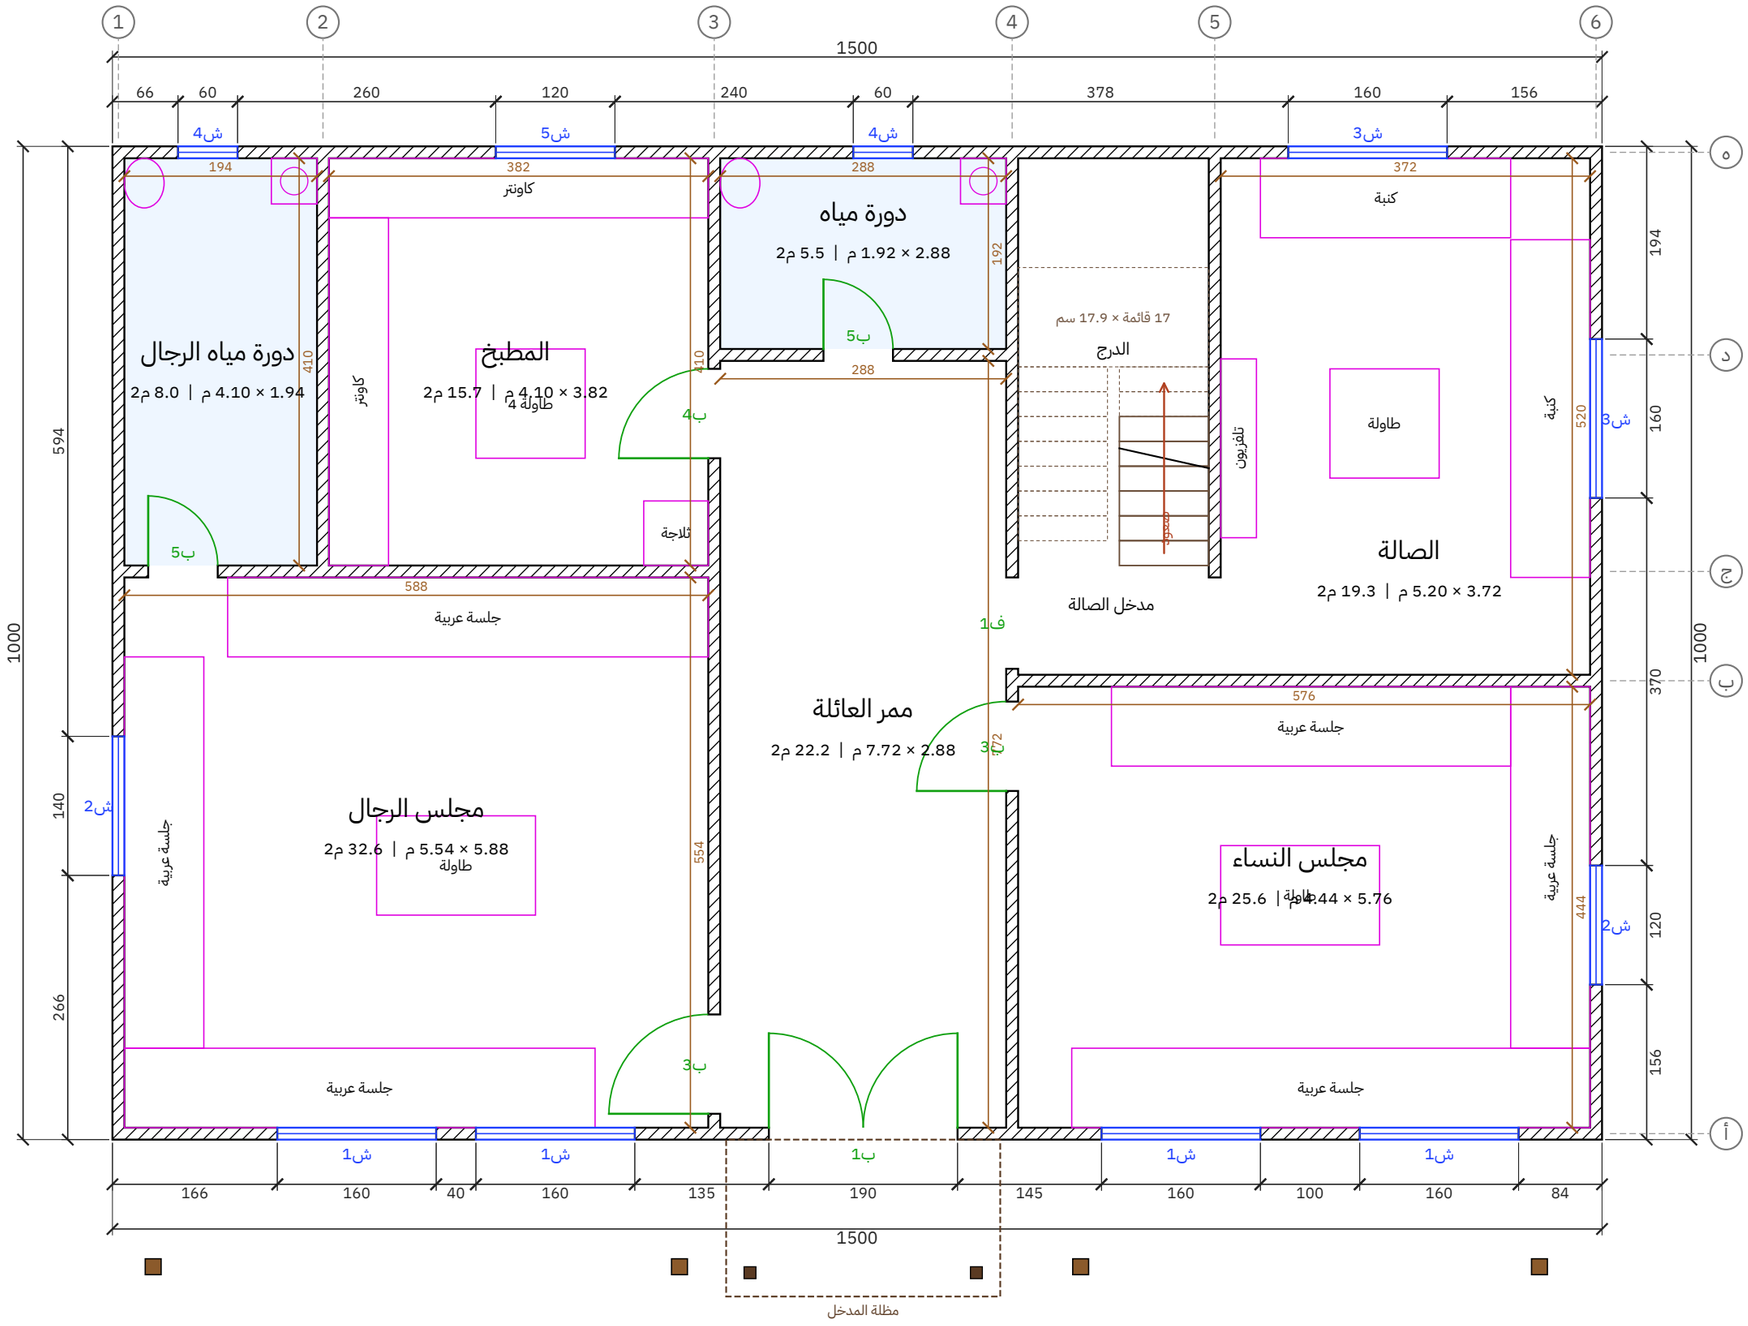



| المشروع / العميل | عنوان اللوحة | المقياس | التاريخ | رقم اللوحة |
|---|---|---|---|---|
| **كوخ خشب دورين — مجلس رجال ومجلس نساء + 4 غرف — 15.00 × 10.00 م (300 م²)**<br>**عميل — كوخ دورين** | **المسقط الأفقي — الدور الأرضي** | **1:50** | **2026-10-24** | **W-02 (2/23)** |

**مصنع وتد الأخشاب**
Watad Wood Factory


# المسقط الأفقي مع الفرش — الدور الأول

الأبعاد بالسنتيمتر - الجدران: قوائم 7×5 + تلبيس 2.5 من الجهتين (12 سم) | منسوب الأرضية +3.05

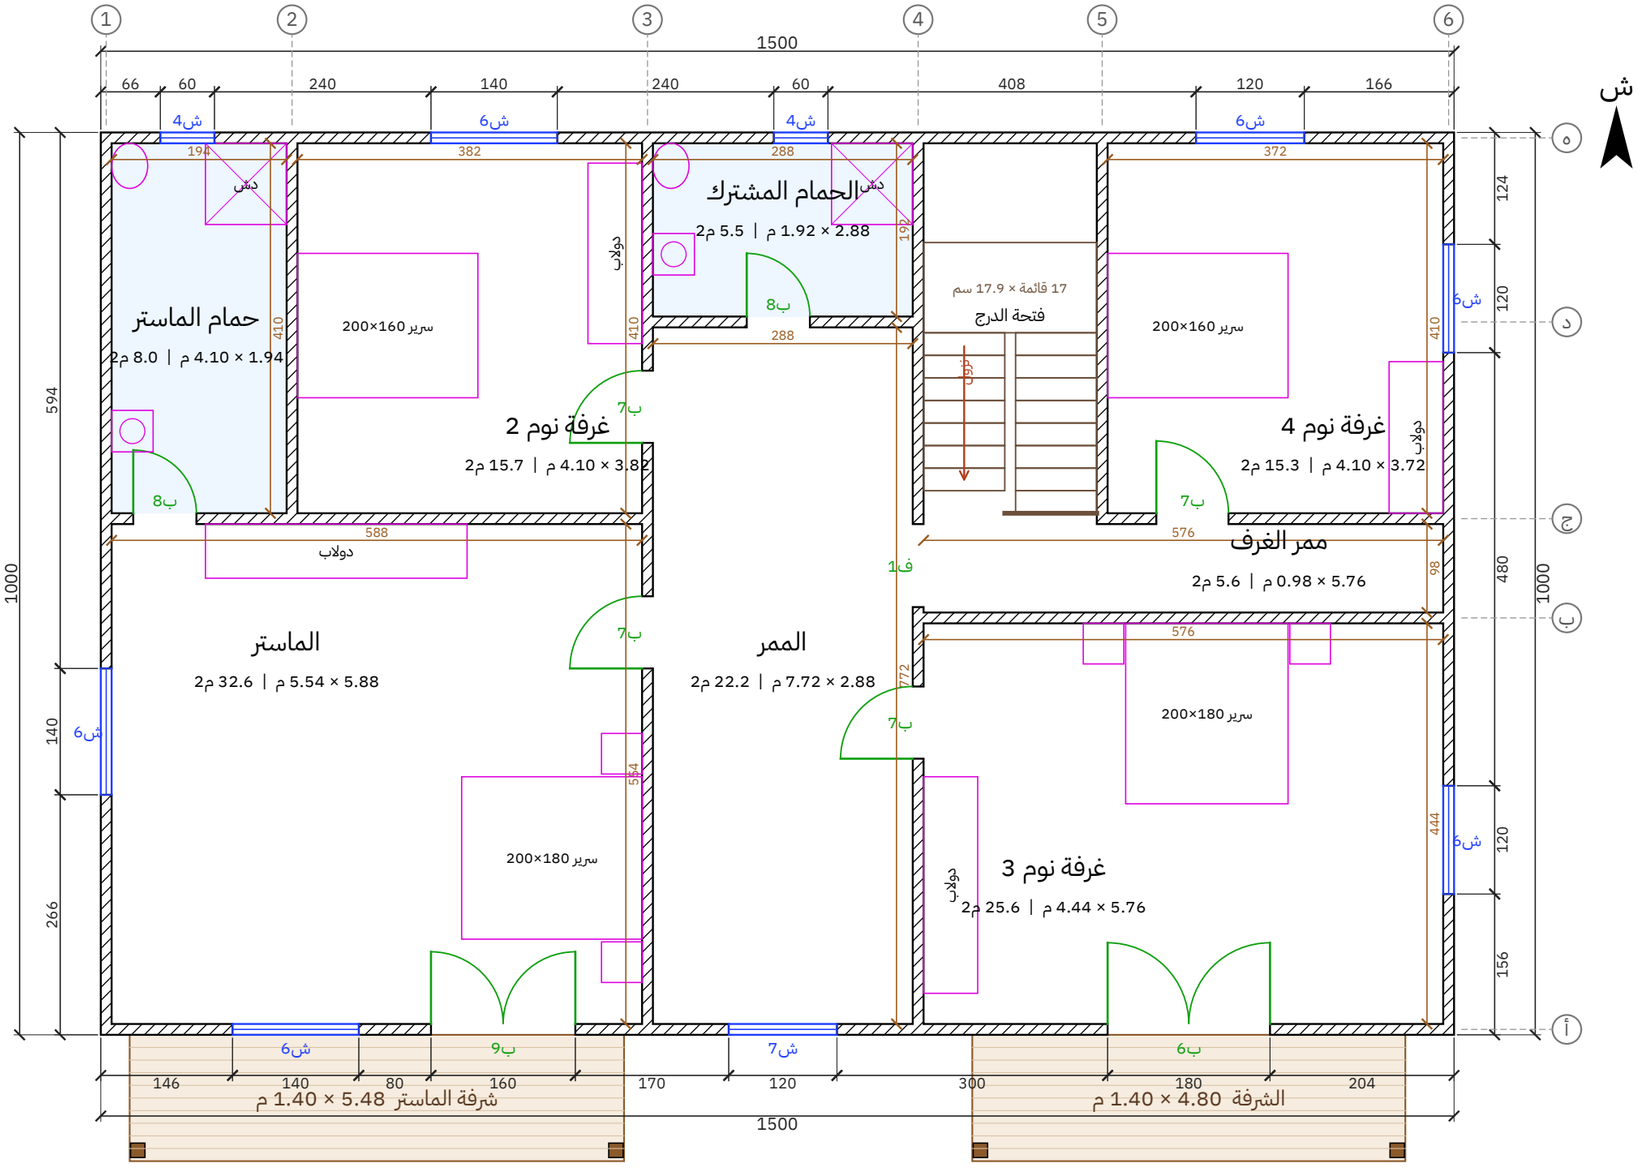



| المشروع / العميل | عنوان اللوحة | المقياس | التاريخ | رقم اللوحة |
|---|---|---|---|---|
| كوخ خشب دورين — مجلس رجال ومجلس نساء + 4 غرف — 15.00 × 10.00 م (300 م²)<br>عميل — كوخ دورين | المسقط الأفقي — الدور الأول | 1:50 | 2026-10-24 | W-03 (3/23) |

مصنع وتد الأخشاب
Watad Wood Factory

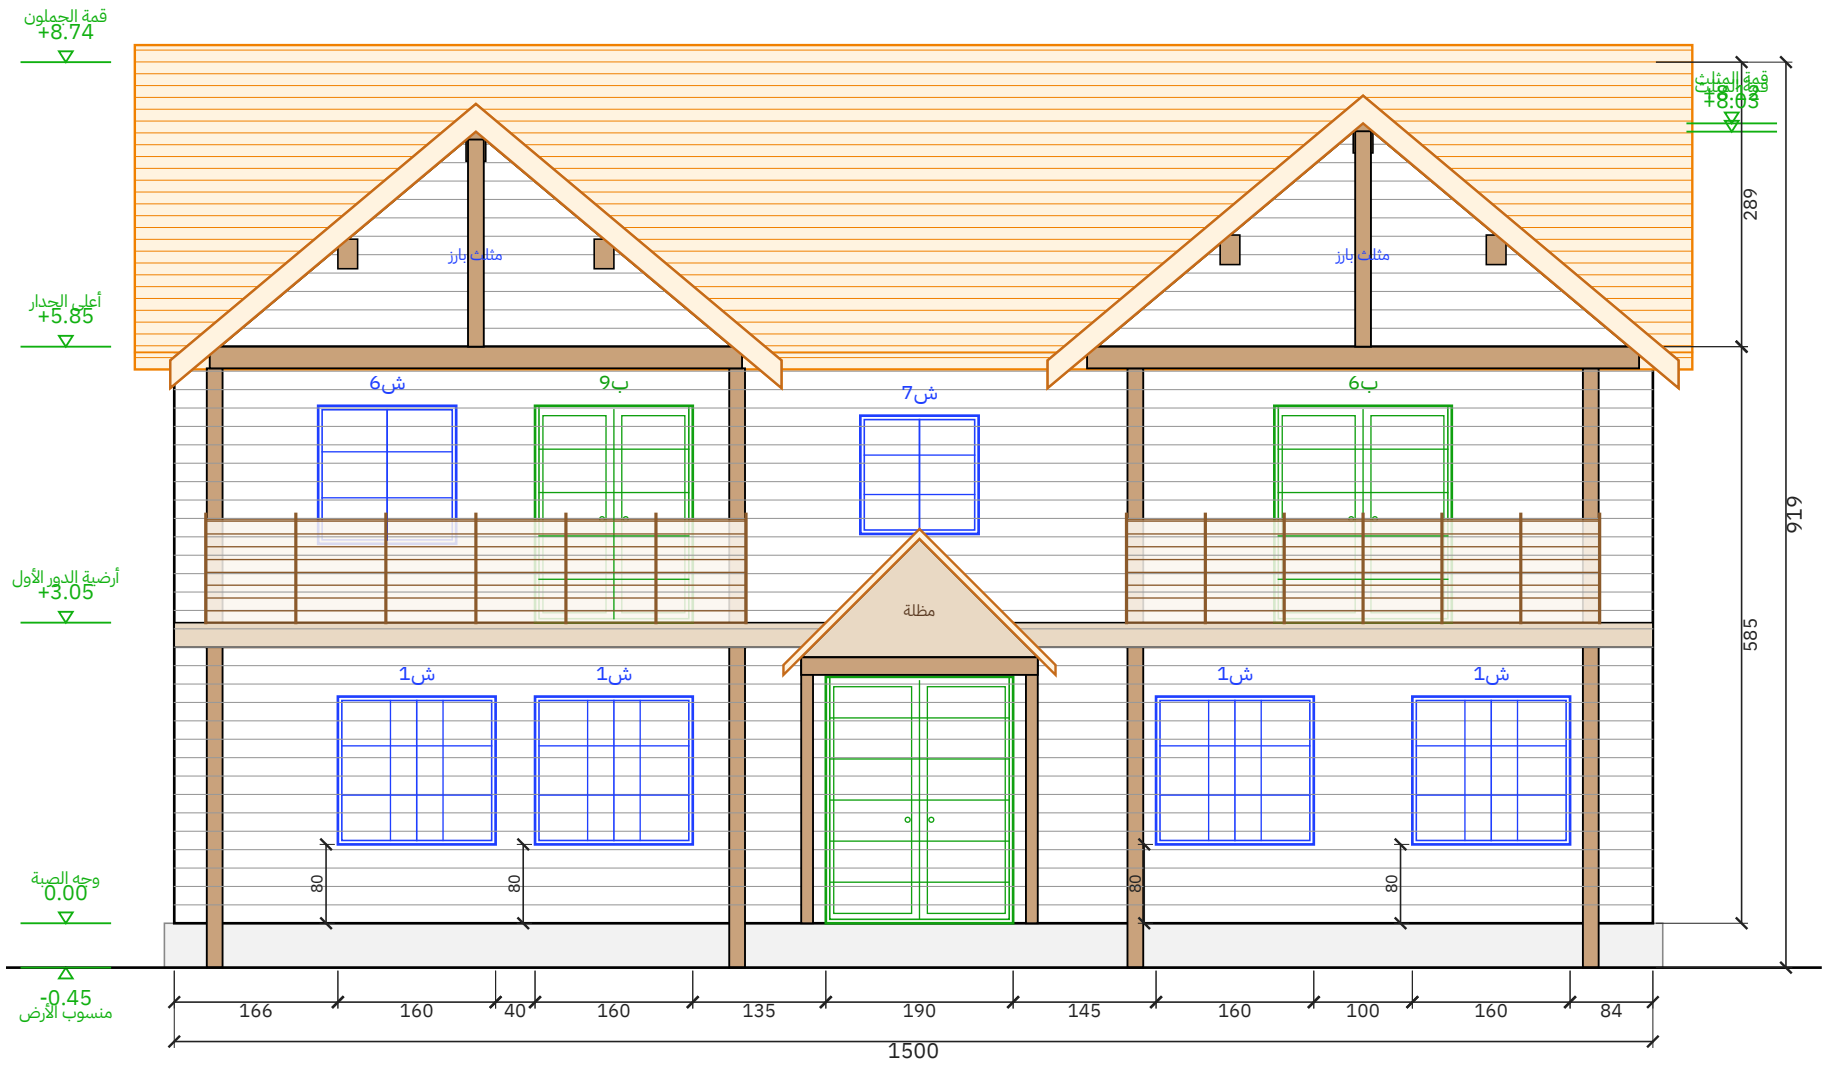


## الواجهة الأمامية

مقياس 1:50 | الوحدة: سم

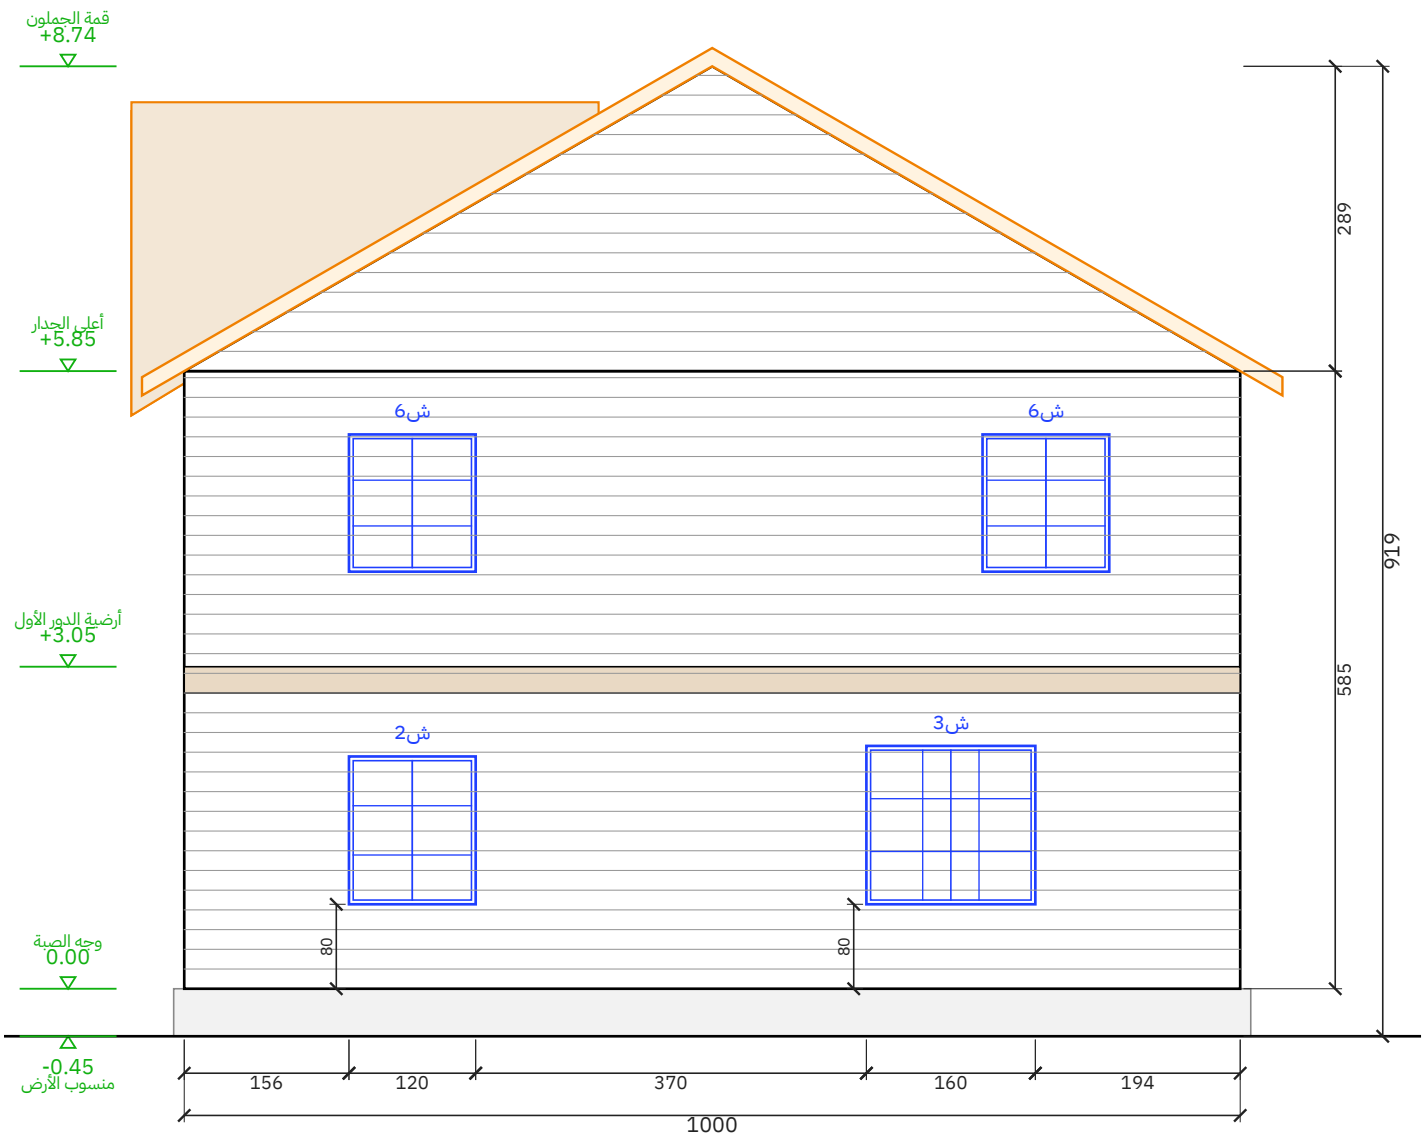



## الواجهة الشرقية

مقياس 1:50 | الوحدة: سم


| المشروع / العميل | عنوان اللوحة | المقياس | التاريخ | رقم اللوحة |
|---|---|---|---|---|
| كوخ خشب دورين – مجلس رجال ومجلس نساء + 4 غرف – 10.00 × 15.00 م (300 م²)<br>عميل – كوخ دورين | الواجهة الأمامية والواجهة الشرقية | 1:50 | 2026-10-24 | W-04 (4/23) |

مصنع وتد الأخشاب
Watad Wood Factory

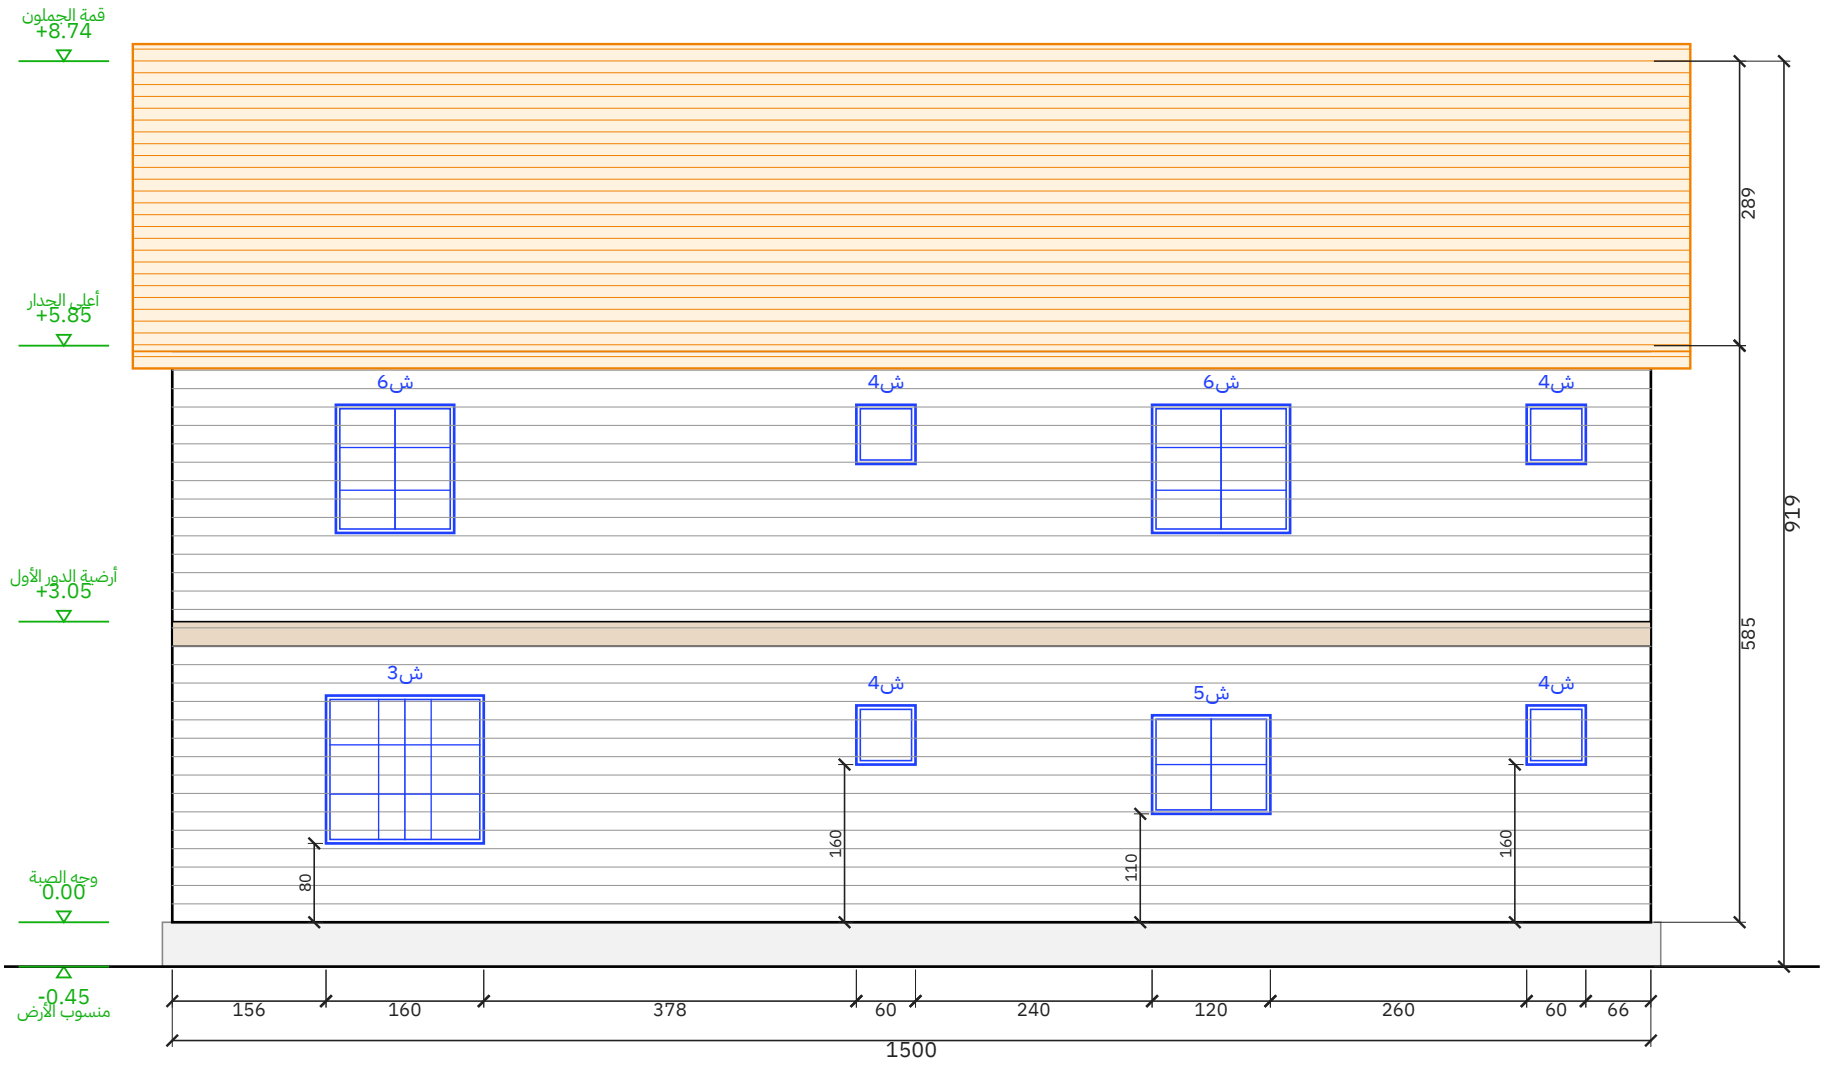


## الواجهة الخلفية

مقياس 1:50 | الوحدة: سم

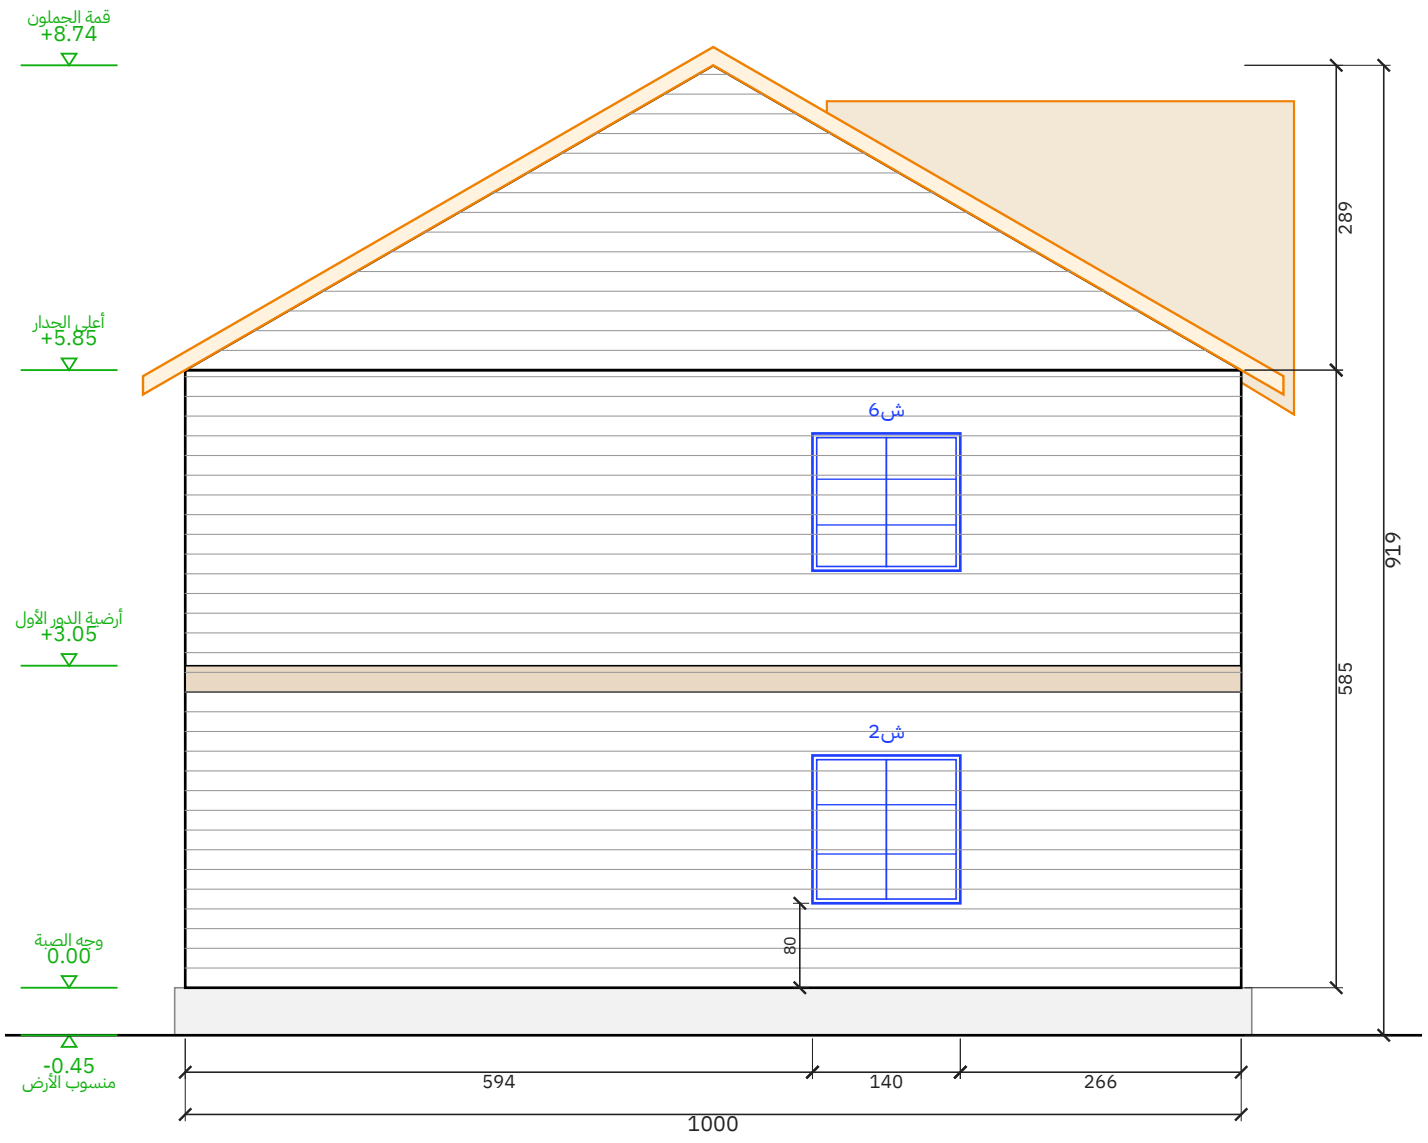


## الواجهة الغربية


مقياس 1:50 | الوحدة: سم

| المشروع / العميل | عنوان اللوحة | المقياس | التاريخ | رقم اللوحة |
|---|---|---|---|---|
| كوخ خشب دورين – مجلس رجال ومجلس نساء + 4 غرف – 10.00 × 15.00 م (300 م²)<br>عميل – كوخ دورين | الواجهة الخلفية والواجهة الغربية | 1:50 | 2026-10-24 | W-05 (5/23) |


مصنع وتد الأخشاب
Watad Wood Factory

## قطاع عرضي أ-أ

مقياس 1:50 | الوحدة: سم

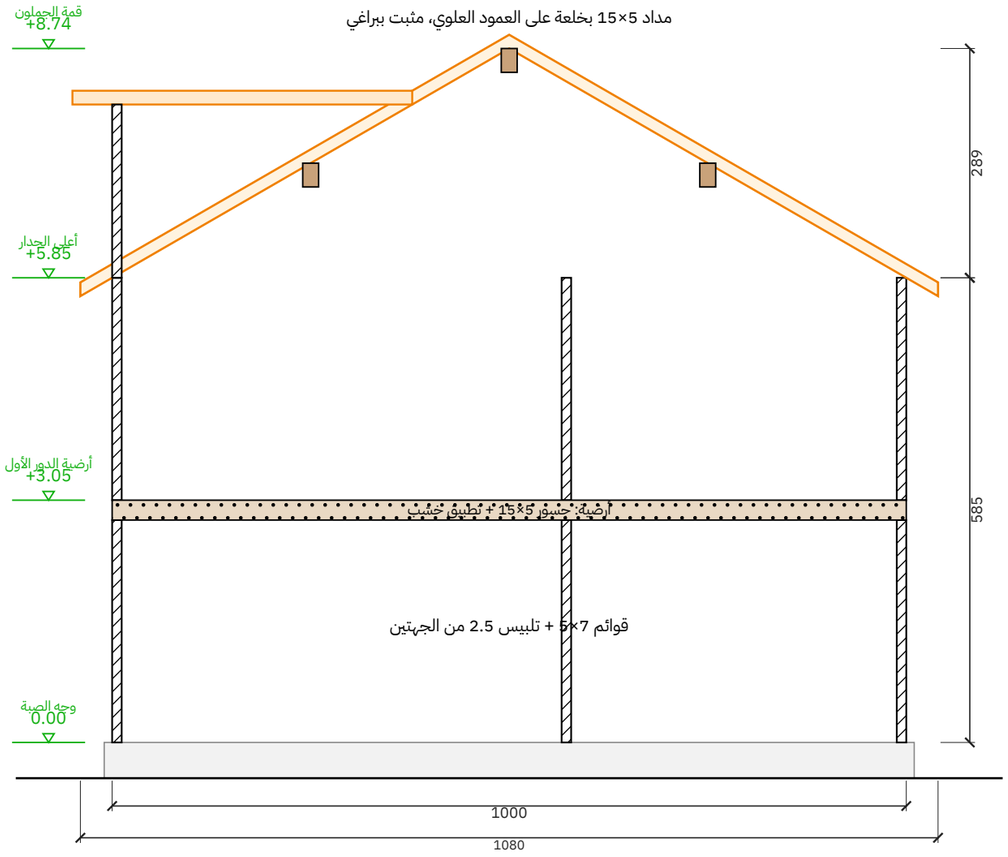



تفصيلة جلوس المداد على العلوي (1:5)

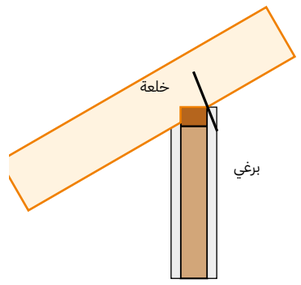


علوي 7×5 على قائم 7×5

## مسقط السقف (جملون)

رفرف 40 سم من كل جهة | مقياس 1:50

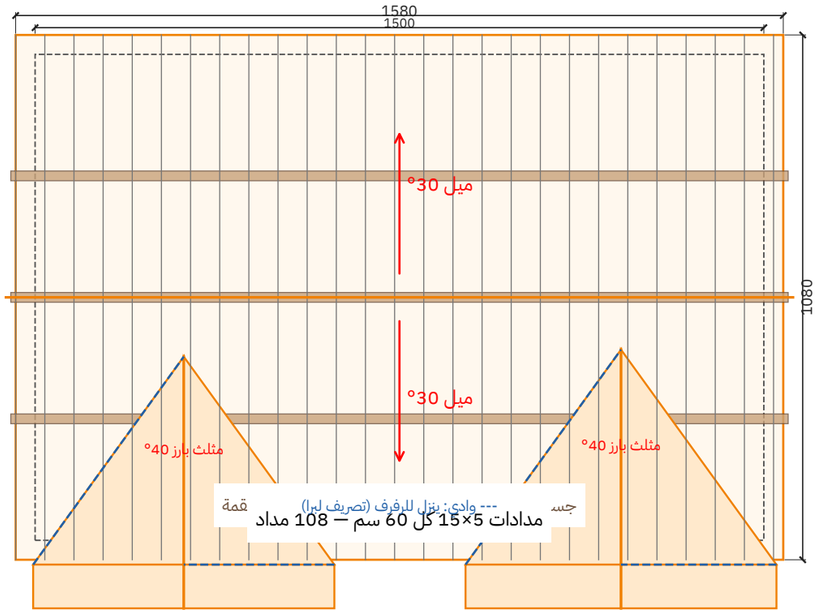


| المشروع / العميل | عنوان اللوحة | المقياس | التاريخ | رقم اللوحة |
|---|---|---|---|---|
| **كوخ خشب دورين — مجلس رجال ومجلس نساء + 4 غرف — 15.00 × 10.00 م (300 م²)**<br>**عميل — كوخ دورين** | **مسقط السقف والقطاع** | **—** | **2026-10-24** | **W-06 (6/23)** |

**مصنع وتد الأخشاب**
Watad Wood Factory

# جدول مقاسات الأبواب والشبابيك

## مقاس الفتحة الصافي في الجدار - الوحدة: سم

| الرمز | النوع | العرض (سم) | الارتفاع (سم) | ارتفاع الجلسة (سم) | العدد | الموقع |
|---|---|---|---|---|---|---|
| ب1 | باب مزدوج | 190 | 250 | - | 1 | الأمامية |
| ب3 | باب | 100 | 220 | - | 1 | مجلس الرجال |
| ب3 | باب | 90 | 210 | - | 1 | مجلس النساء |
| ب4 | باب | 90 | 210 | - | 1 | المطبخ |
| ب5 | باب | 70 | 210 | - | 2 | دورة مياه الرجال - دورة مياه |
| ب6 | باب مزدوج | 180 | 220 | - | 1 | الأمامية |
| ب7 | باب | 80 | 210 | - | 4 | الماستر - غرفة 2 - غرفة 3 - غرفة 4 |
| ب8 | باب | 70 | 210 | - | 2 | حمام الماستر - الحمام المشترك |
| ب9 | باب مزدوج | 160 | 220 | - | 1 | الأمامية |
| ف1 | باب | 92 | 220 | - | 2 | الممر — الصالة - الممر — الدرج |
| ش1 | شباك | 160 | 150 | 80 | 4 | الأمامية 4 |
| ش2 | شباك | 120 | 140 | 80 | 1 | الشرقية |
| ش2 | شباك | 140 | 140 | 80 | 1 | الغربية |
| ش3 | شباك | 160 | 150 | 80 | 2 | الشرقية - الخلفية |
| ش4 | شباك | 60 | 60 | 160 | 4 | الخلفية 4 |
| ش5 | شباك | 120 | 100 | 110 | 1 | الخلفية |
| ش6 | شباك | 140 | 140 | 80 | 1 | الأمامية |
| ش6 | شباك | 120 | 130 | 90 | 3 | الشرقية 2 - الخلفية |
| ش6 | شباك | 140 | 130 | 90 | 2 | الخلفية - الغربية |
| ش7 | شباك | 120 | 120 | 90 | 1 | الأمامية |

الإجمالي: أبواب 16 - شبابيك 20

# جدول المساحات وبيانات المشروع


## بيانات المشروع

| البند | البيان |
|---|---|
| المشروع | كوخ خشب دورين — مجلس رجال ومجلس نساء + 4 غرف — 15.00 × 10.00 م (300 م²) |
| العميل | عميل — كوخ دورين |
| الموقع | — |
| الاستخدام | سكن عائلي |
| التاريخ | 2026-10-24 |
| نظام البناء | هيكل خشب 5×7 + تلبيس 2.5 سم من الجهتين |
| السقف | جملون 30° — قرميد معدني + 2 مثلث بارز |


## جدول المساحات

| م | الفراغ | الأبعاد (م) | المساحة (م2) |
|---|---|---|---|
| 1 | أرضي — مجلس الرجال | 5.88 × 5.54 | 32.58 |
| 2 | أرضي — دورة مياه الرجال | 1.94 × 4.10 | 7.95 |
| 3 | أرضي — المطبخ | 3.82 × 4.10 | 15.66 |
| 4 | أرضي — ممر العائلة | 2.88 × 7.72 | 22.23 |
| 5 | أرضي — دورة مياه | 2.88 × 1.92 | 5.53 |
| 6 | أرضي — مجلس النساء | 5.76 × 4.44 | 25.57 |
| 7 | أرضي — مدخل الصالة | 1.92 × 1.04 | 2.00 |
| 8 | أرضي — الدرج | 1.92 × 4.10 | 7.87 |
| 9 | أرضي — الصالة | 3.72 × 5.20 | 19.34 |
| 10 | أول — الماستر | 5.88 × 5.54 | 32.58 |
| 11 | أول — حمام الماستر | 1.94 × 4.10 | 7.95 |
| 12 | أول — غرفة نوم 2 | 3.82 × 4.10 | 15.66 |
| 13 | أول — الممر | 2.88 × 7.72 | 22.23 |
| 14 | أول — الحمام المشترك | 2.88 × 1.92 | 5.53 |
| 15 | أول — غرفة نوم 3 | 5.76 × 4.44 | 25.57 |
| 16 | أول — ممر الغرف | 5.76 × 0.98 | 5.64 |
| 17 | أول — غرفة نوم 4 | 3.72 × 4.10 | 15.25 |
| | المساحة الصافية الداخلية | | 269.17 |
| | **الشرفة** | **4.80 × 1.40** | **6.72** |
| | **شرفة الماستر** | **5.48 × 1.40** | **7.67** |
| | **المساحة الإجمالية المبنية** | **15.00 × 10.00 × 2 دور** | **300.00** |
| | **المساحة الكلية (المبنية + التراسات)** | | **314.39** |

## تأطير جدار أ-جنوب — الطول 1488 سم، الارتفاع 280 سم

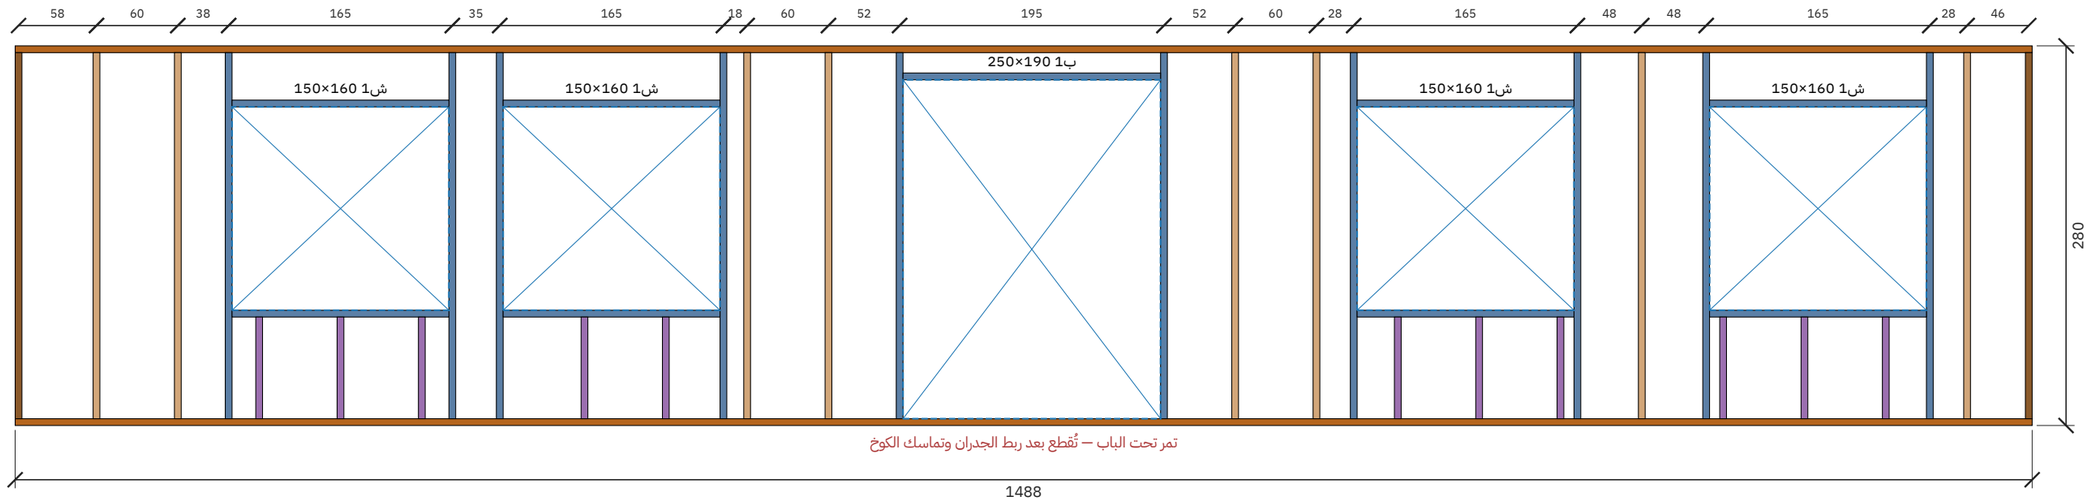


## تأطير جدار أ-شرق — الطول 988 سم، الارتفاع 280 سم

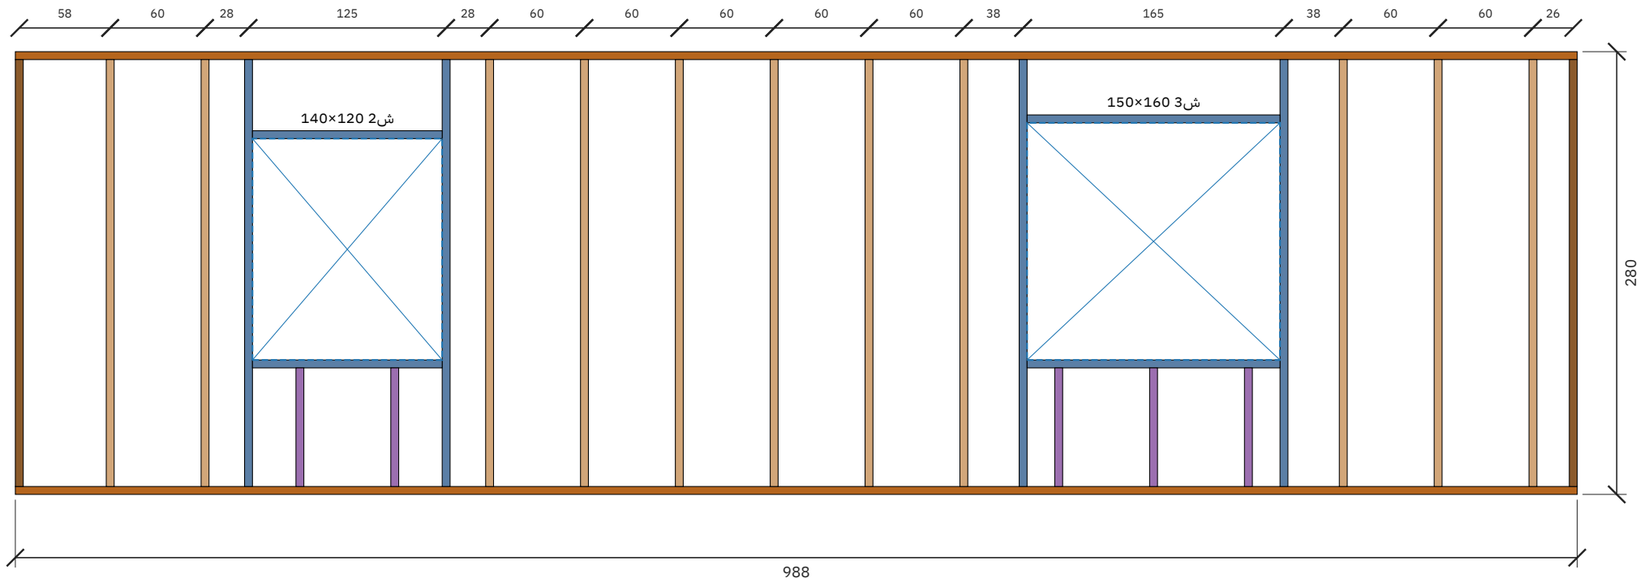



قاعدة سفلية | علوي | عمود | عمود زاوية | جنب فتحة | رأس فتحة | جلسة شباك | عمود قصير


| المشروع / العميل | عنوان اللوحة | المقياس | التاريخ | رقم اللوحة |
|---|---|---|---|---|
| **كوخ خشب دورين — مجلس رجال ومجلس نساء + 4 غرف — 15.00 × 10.00 م (300 م²)**<br>**عميل — كوخ دورين** | **لوحات التأطير (للورشة)** | **—** | **2026-10-24** | **W-09 (9/23)** |

**مصنع وتد الأخشاب**
Watad Wood Factory

## تأطير جدار أ-شمال — الطول 1488 سم، الارتفاع 280 سم

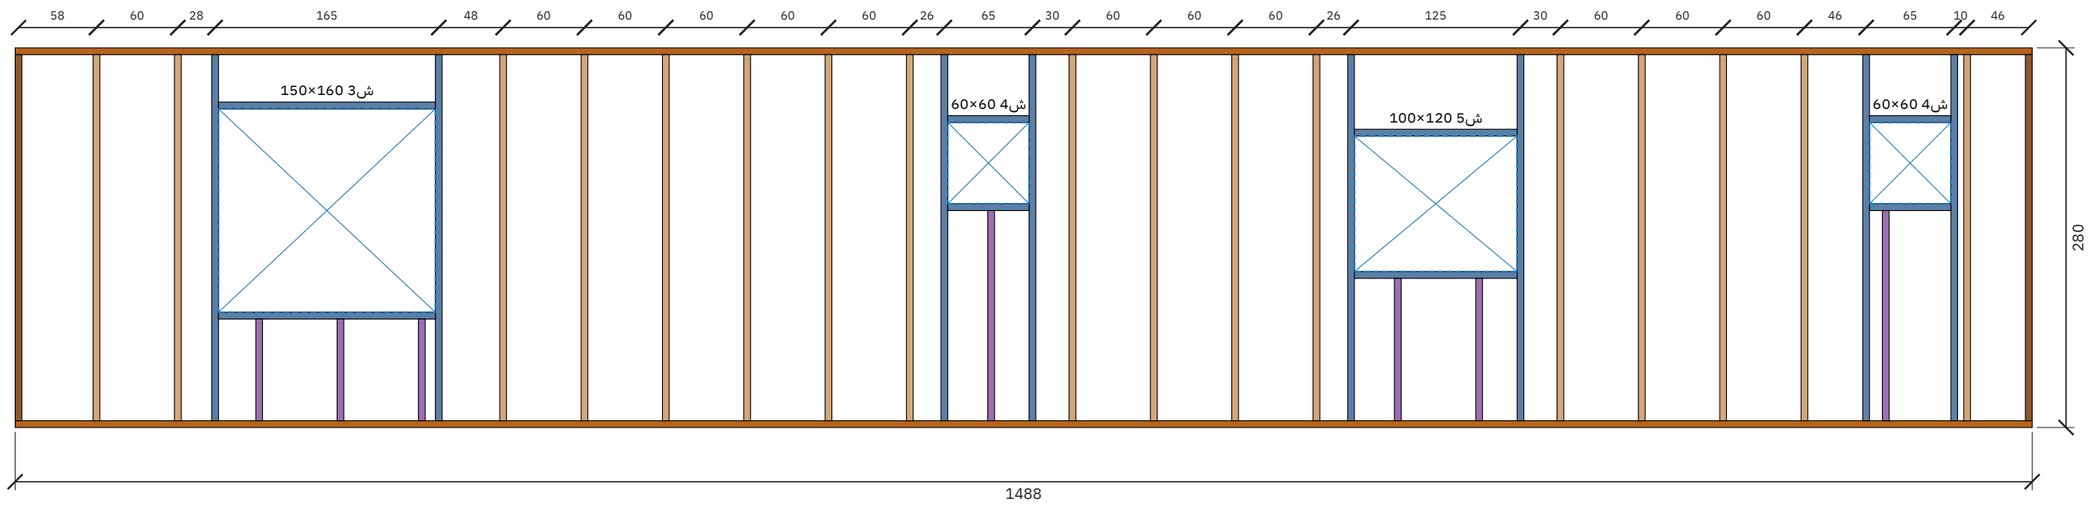



## تأطير جدار أ-غرب — الطول 988 سم، الارتفاع 280 سم

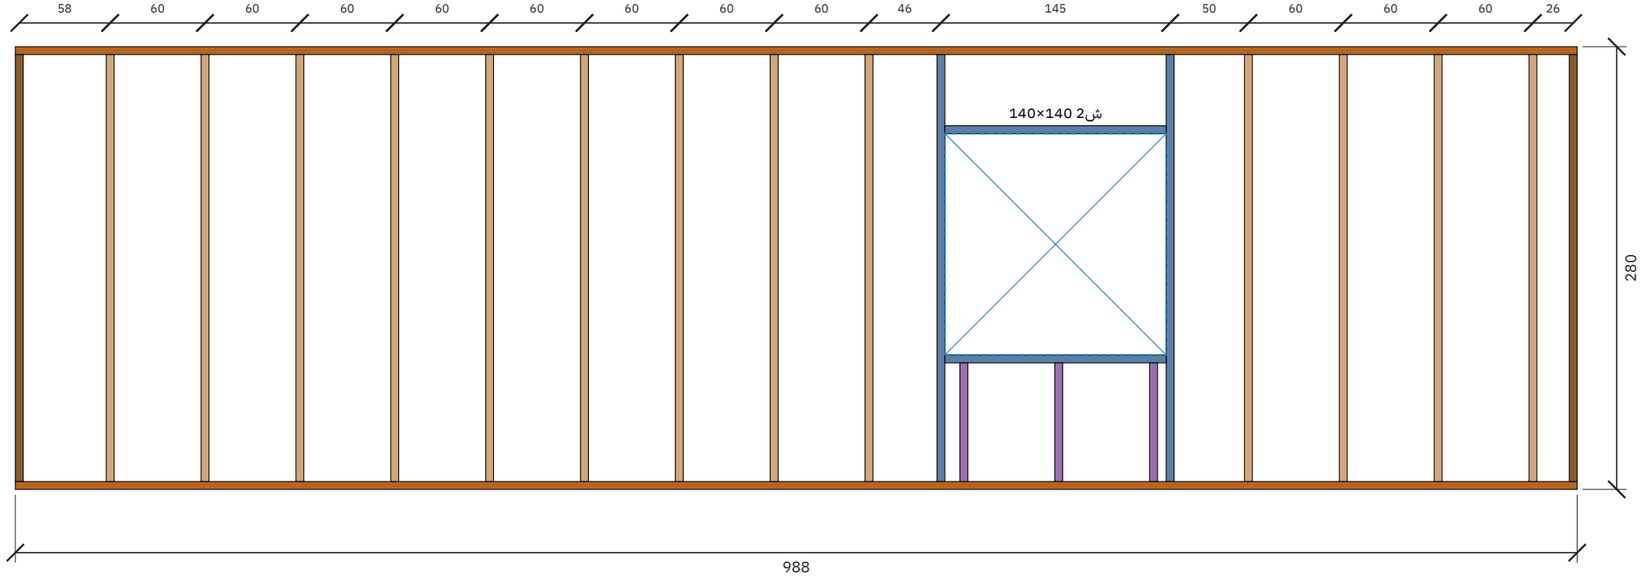



قاعدة سفلية | علوي | عمود | عمود زاوية | جنب فتحة | رأس فتحة | جلسة شباك | عمود قصير

| | | | | |
|---|---|---|---|---|
| مصنع وتد الأخشاب<br>Watad Wood Factory | المشروع / العميل<br>كوخ خشب دورين — مجلس رجال ومجلس نساء + 4 غرف — 15.00 × 10.00 م (300 م²)<br>عميل — كوخ دورين | عنوان اللوحة<br>لوحات التأطير (للورشة) | المقياس<br>— | التاريخ<br>2026-10-24 | رقم اللوحة<br>W-10 (10/23) |

## تأطير جدار أ-جدار المجلس — الطول 988 سم، الارتفاع 280 سم (داخلي)

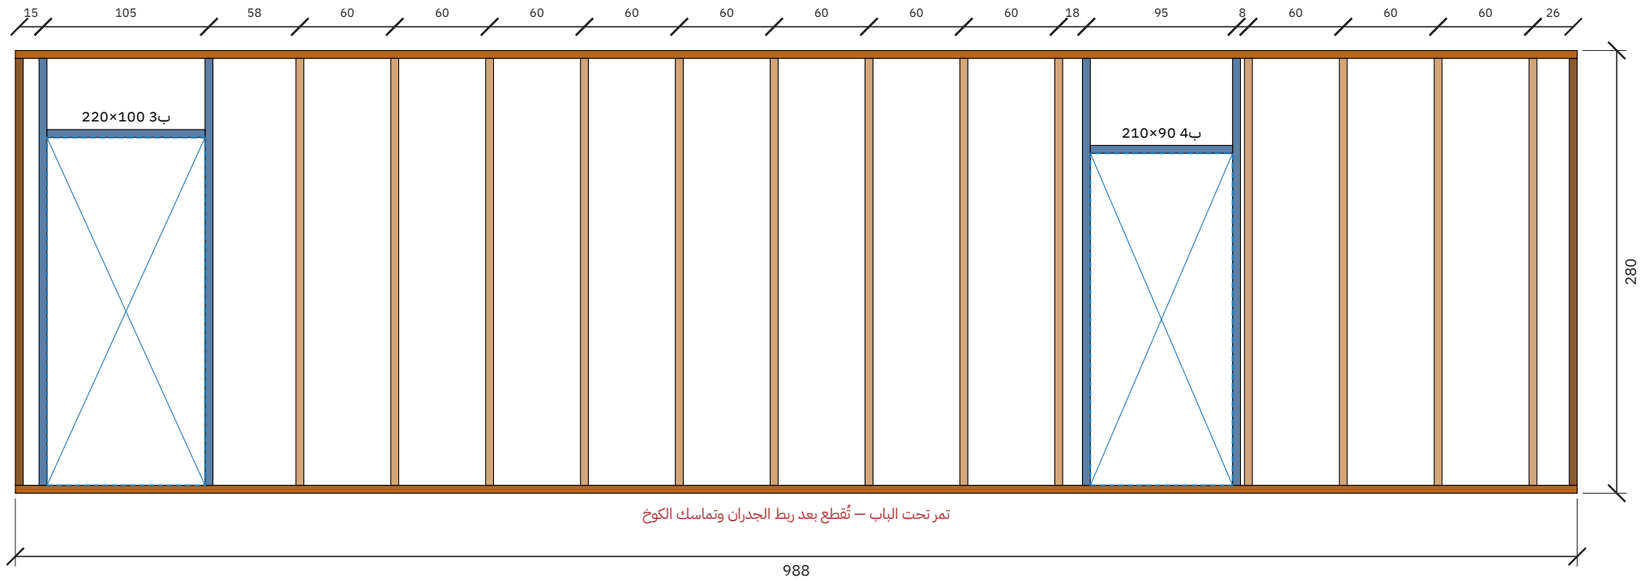



## تأطير جدار أ-خلف المجلس — الطول 600 سم، الارتفاع 280 سم (داخلي)

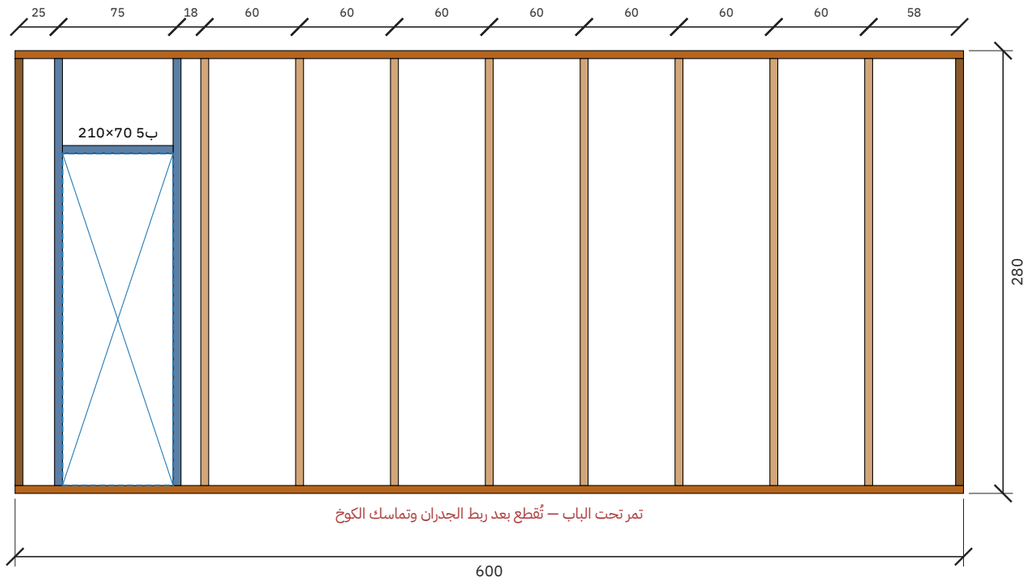



قاعدة سفلية | علوي | عمود | عمود زاوية | جنب فتحة | رأس فتحة | جلسة شباك | عمود قصير

| | | | | |
|---|---|---|---|---|
| **مصنع وتد الأخشاب**<br>Watad Wood Factory | المشروع / العميل<br>**كوخ خشب دورين — مجلس رجال ومجلس نساء + 4 غرف — 15.00 × 10.00 م (300 م²)**<br>**عميل — كوخ دورين** | عنوان اللوحة<br>**لوحات التأطير (للورشة)** | المقياس<br>**—** | التاريخ<br>**2026-10-24** | رقم اللوحة<br>**W-11 (11/23)** |

## تأطير جدار أ-جدار الدورة — الطول 422 سم، الارتفاع 280 سم (داخلي)

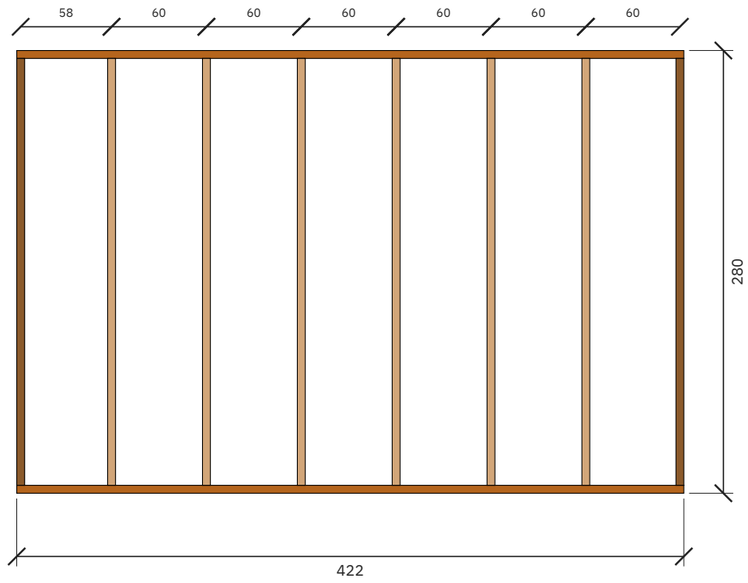


## تأطير جدار أ-دورة الممر — الطول 300 سم، الارتفاع 280 سم (داخلي)

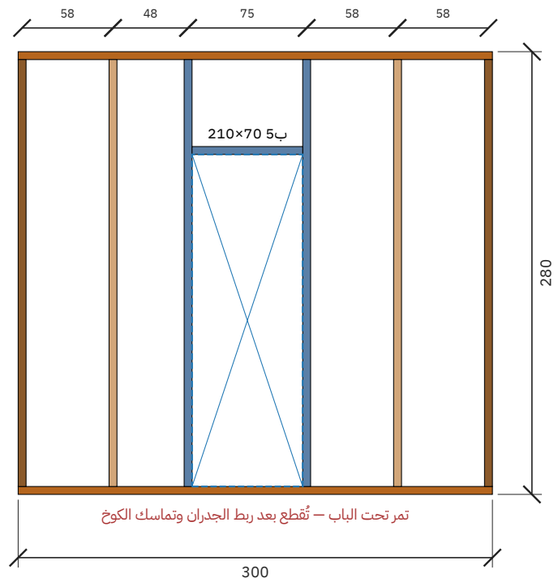



قاعدة سفلية | علوي | عمود | عمود زاوية | جنب فتحة | رأس فتحة | جلسة شباك | عمود قصير


| المشروع / العميل | عنوان اللوحة | المقياس | التاريخ | رقم اللوحة |
|---|---|---|---|---|
| **كوخ خشب دورين — مجلس رجال ومجلس نساء + 4 غرف — 15.00 × 10.00 م (300 م²)**<br>**عميل — كوخ دورين** | **لوحات التأطير (للورشة)** | **—** | **2026-10-24** | **W-12 (12/23)** |

**مصنع وتد الأخشاب**
Watad Wood Factory

## تأطير جدار أ-جدار النساء — الطول 988 سم، الارتفاع 280 سم (داخلي)

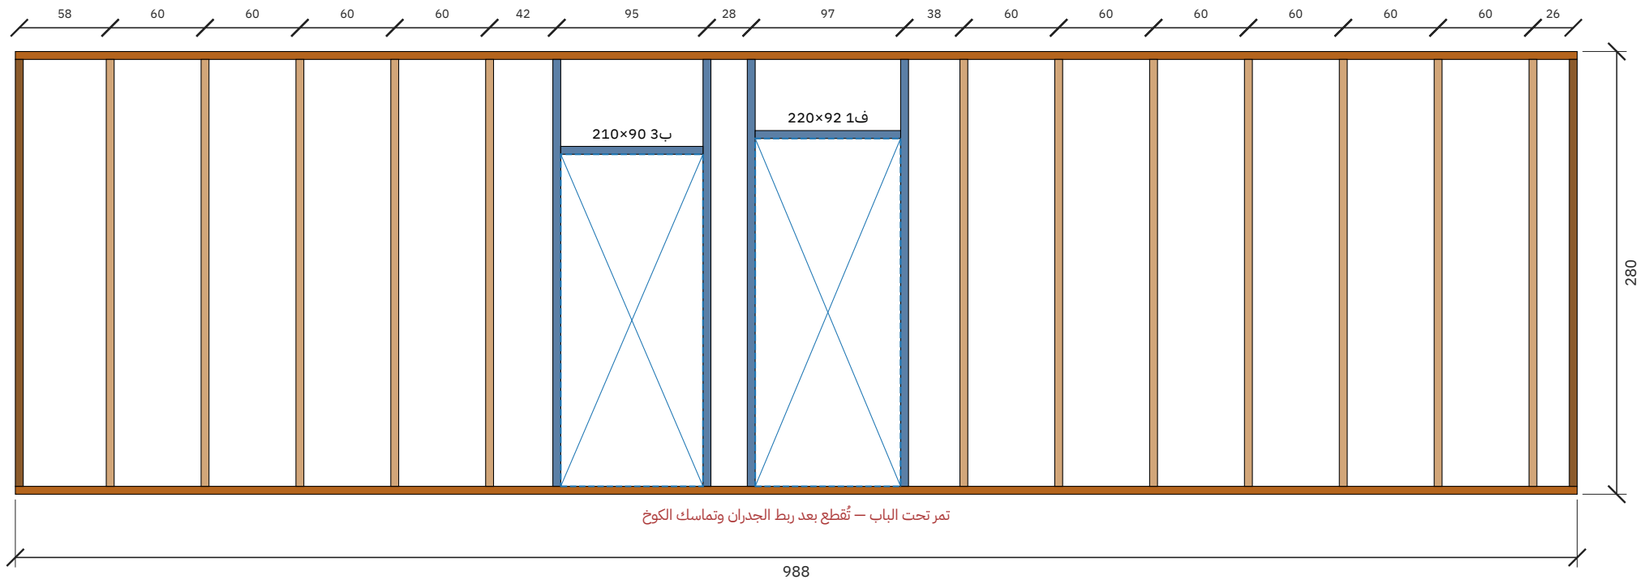


## تأطير جدار أ-خلف النساء — الطول 588 سم، الارتفاع 280 سم (داخلي)

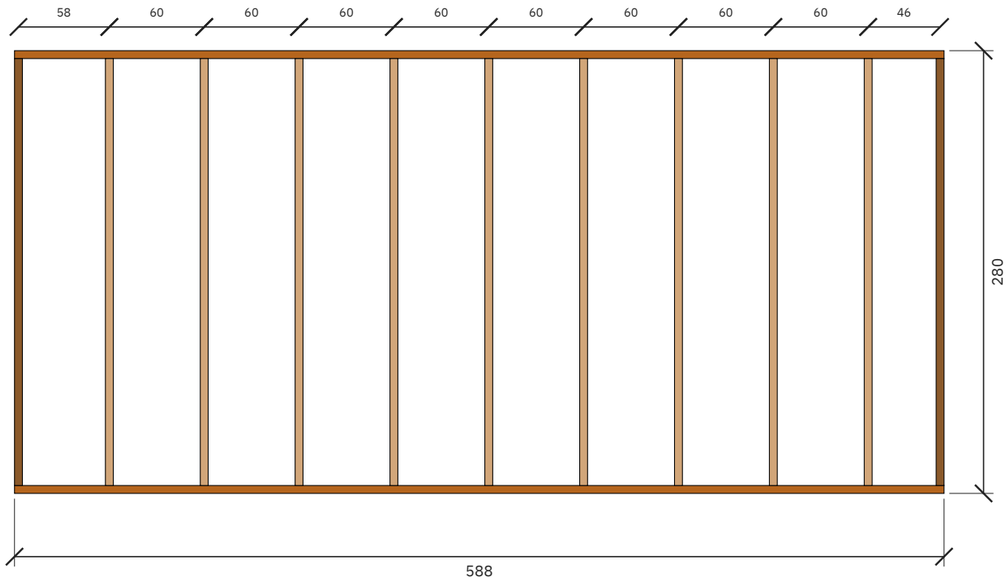



قاعدة سفلية | علوي | عمود | عمود زاوية | جنب فتحة | رأس فتحة | جلسة شباك | عمود قصير


| المشروع / العميل | عنوان اللوحة | المقياس | التاريخ | رقم اللوحة |
|---|---|---|---|---|
| كوخ خشب دورين — مجلس رجال ومجلس نساء + 4 غرف — 15.00 × 10.00 م (300 م²)<br>عميل — كوخ دورين | لوحات التأطير (للورشة) | — | 2026-10-24 | W-13 (13/23) |

مصنع وتد الأخشاب
Watad Wood Factory

## تأطير جدار أ-جدار الدرج — الطول 422 سم، الارتفاع 280 سم (داخلي)

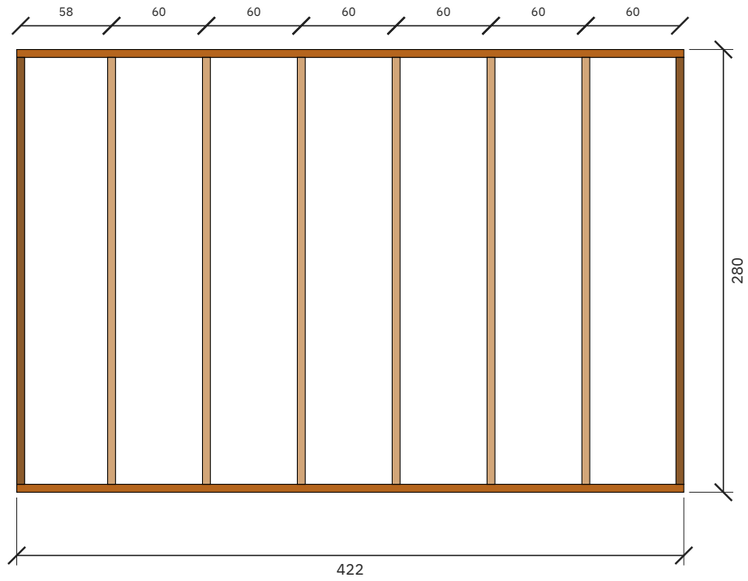


## تأطير جدار ب-جنوب — الطول 1488 سم، الارتفاع 280 سم

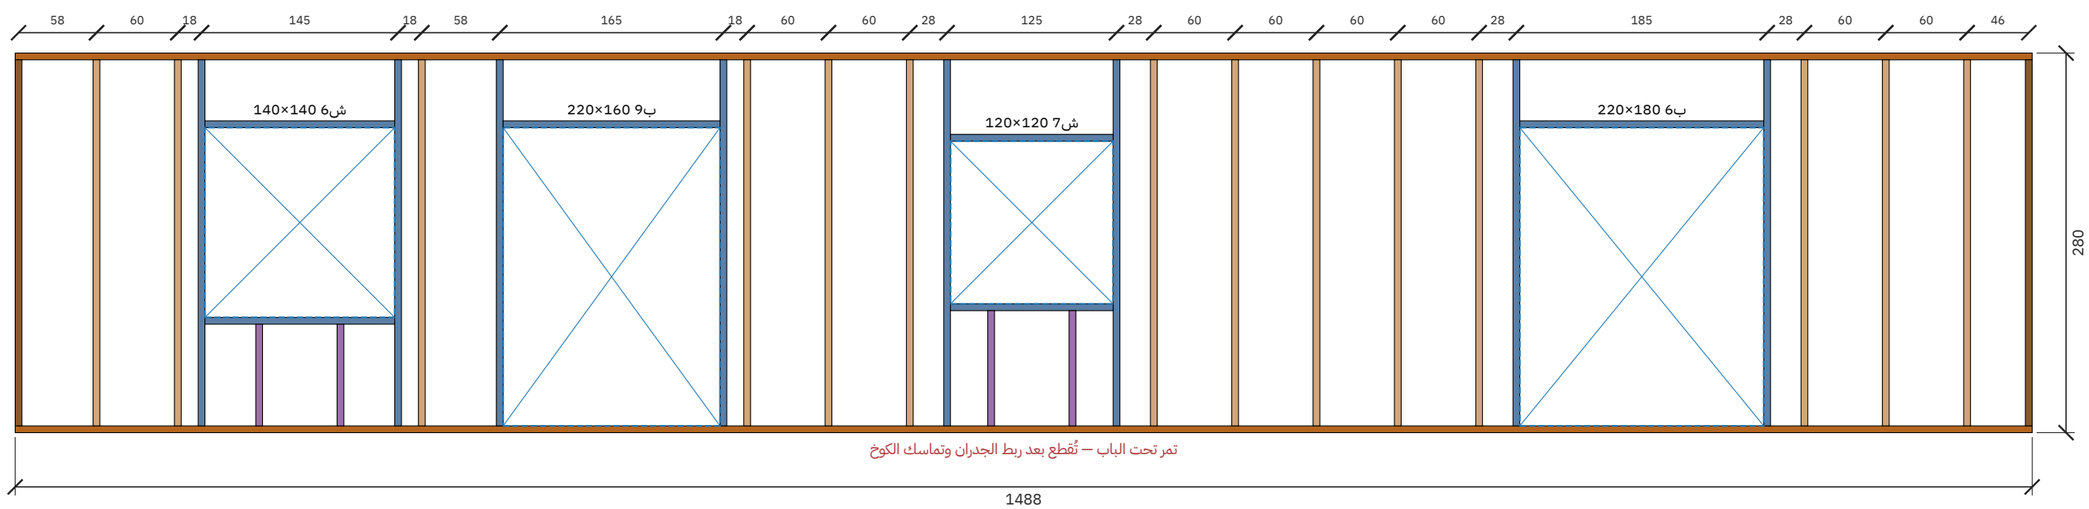



قاعدة سفلية | علوي | عمود | عمود زاوية | جنب فتحة | رأس فتحة | جلسة شباك | عمود قصير


| المشروع / العميل | عنوان اللوحة | المقياس | التاريخ | رقم اللوحة |
|---|---|---|---|---|
| **كوخ خشب دورين — مجلس رجال ومجلس نساء + 4 غرف — 15.00 × 10.00 م (300 م²)**<br>**عميل — كوخ دورين** | **لوحات التأطير (للورشة)** | **—** | **2026-10-24** | **W-14 (14/23)** |

**مصنع وتد الأخشاب**
Watad Wood Factory

## تأطير جدار ب-شرق — الطول 988 سم، الارتفاع 280 سم

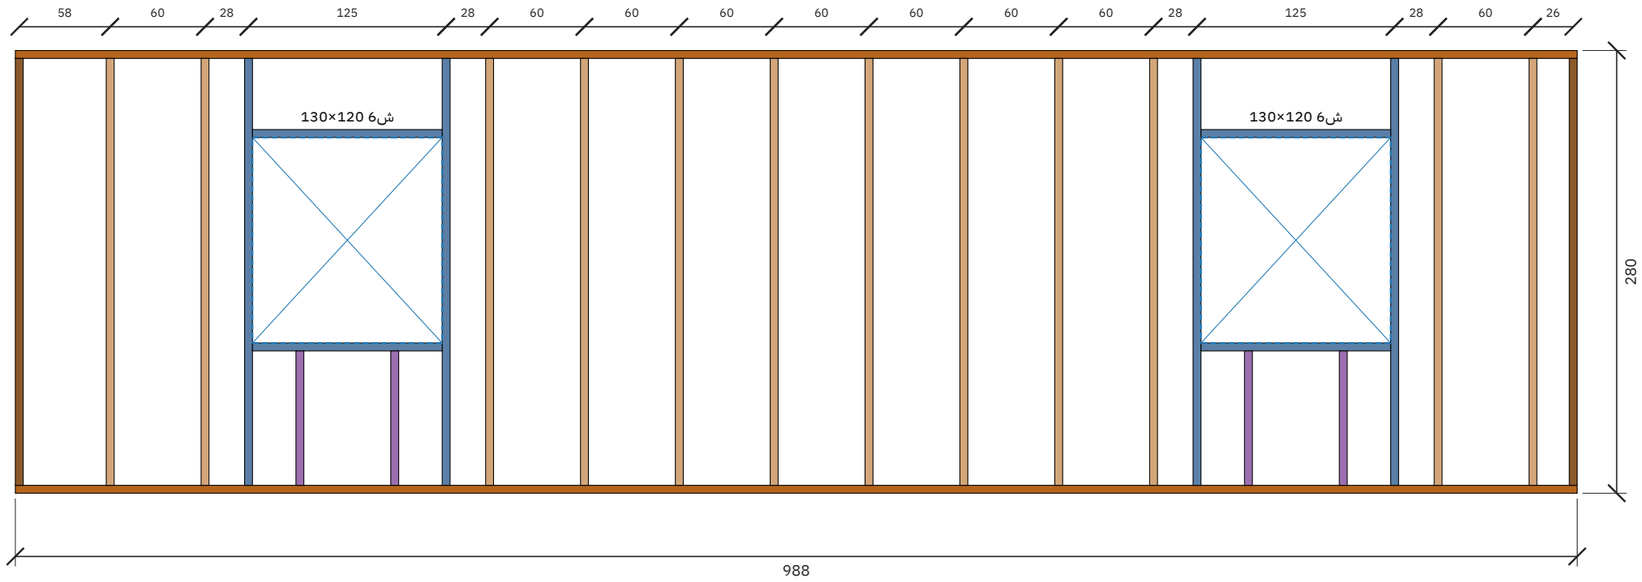


## تأطير جدار ب-شمال — الطول 1488 سم، الارتفاع 280 سم

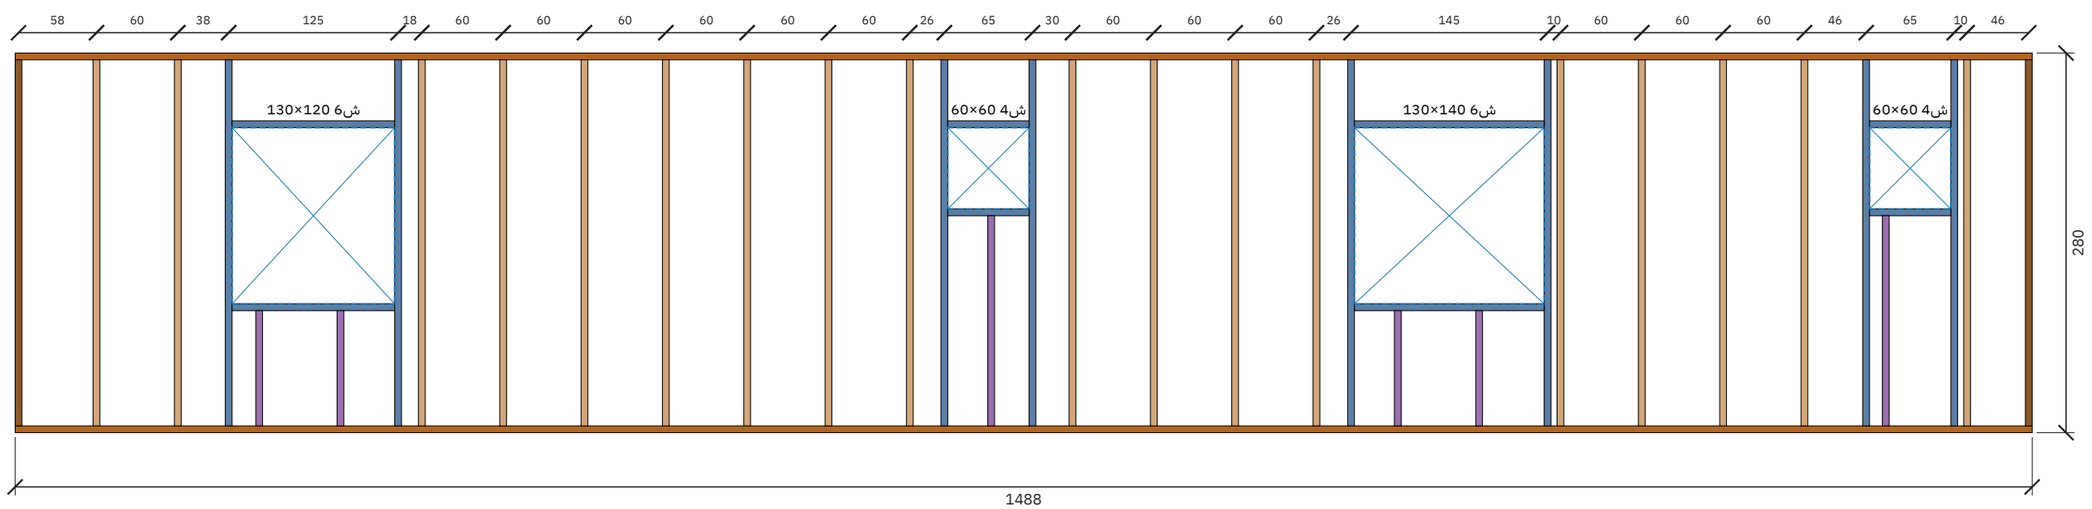



قاعدة سفلية | علوي | عمود | عمود زاوية | جنب فتحة | رأس فتحة | جلسة شباك | عمود قصير


| المشروع / العميل | عنوان اللوحة | المقياس | التاريخ | رقم اللوحة |
|---|---|---|---|---|
| **كوخ خشب دورين — مجلس رجال ومجلس نساء + 4 غرف — 15.00 × 10.00 م (300 م²)**<br>**عميل — كوخ دورين** | **لوحات التأطير (للورشة)** | **—** | **2026-10-24** | **W-15 (15/23)** |

**مصنع وتد الأخشاب**
Watad Wood Factory

## تأطير جدار ب-غرب — الطول 988 سم، الارتفاع 280 سم

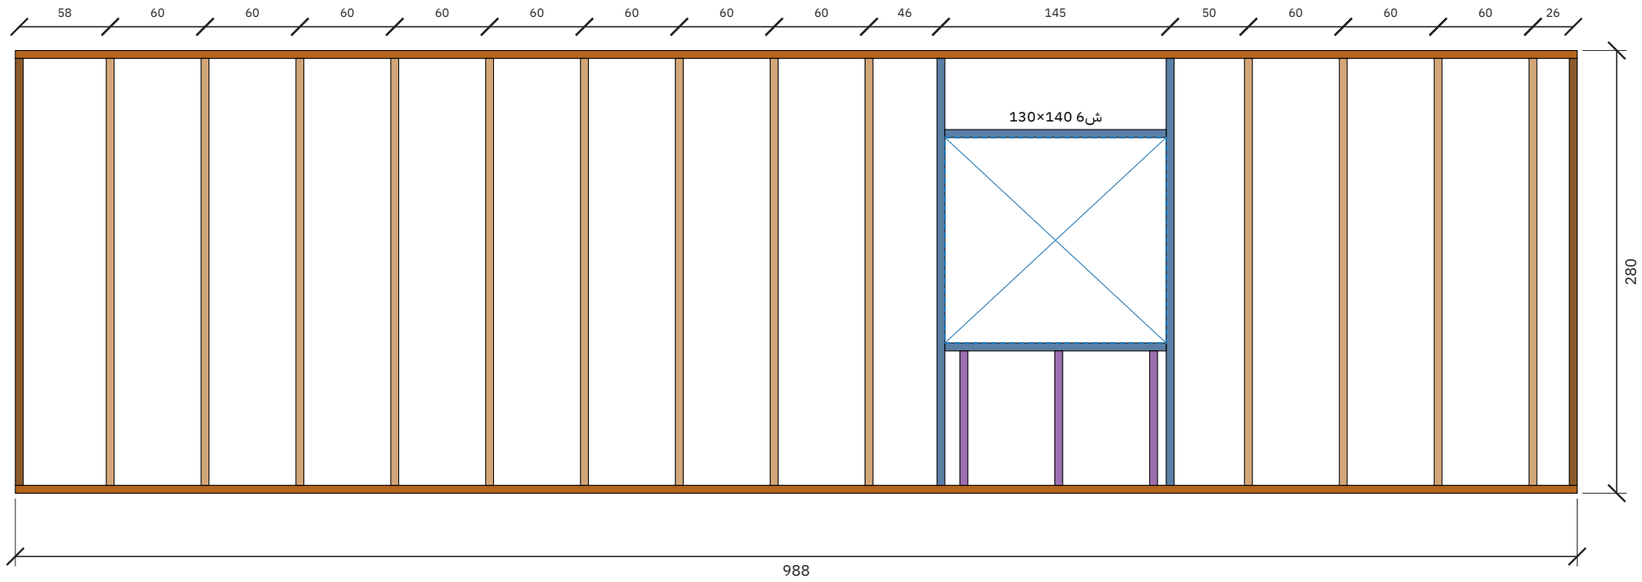



## تأطير جدار ب-جدار الماستر — الطول 988 سم، الارتفاع 280 سم (داخلي)

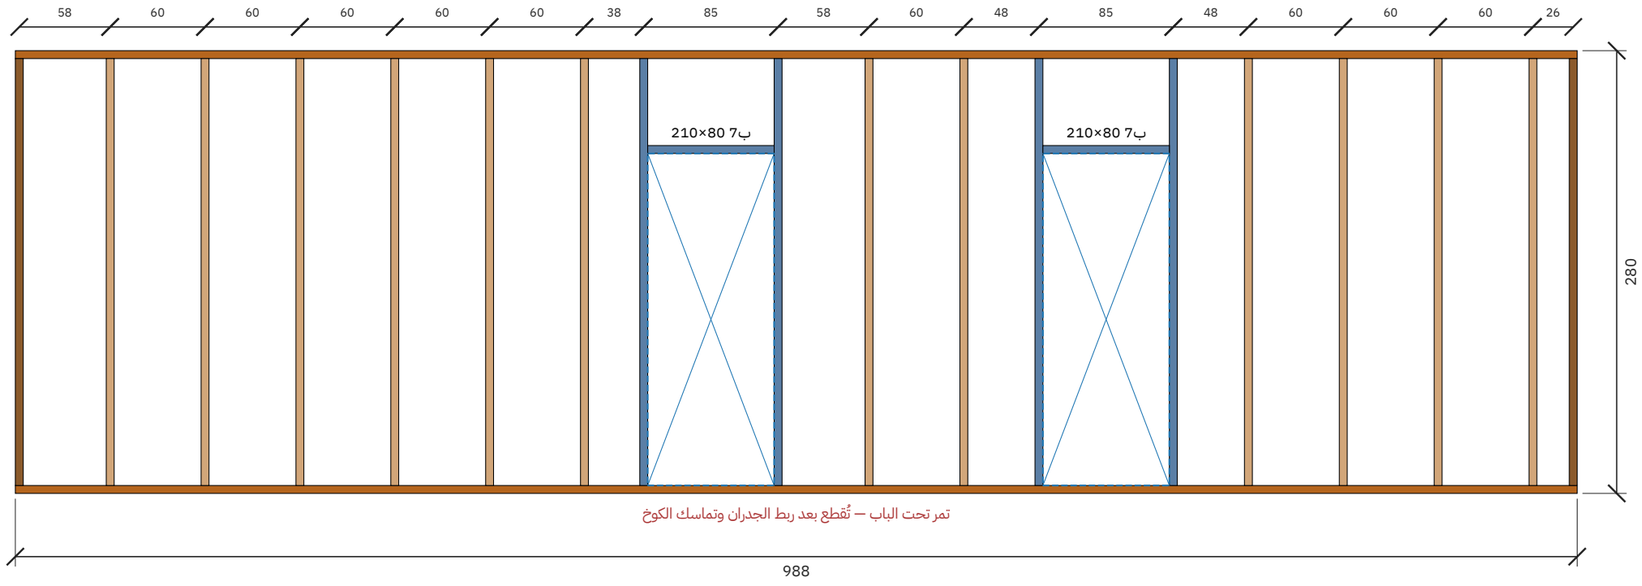



قاعدة سفلية | علوي | عمود | عمود زاوية | جنب فتحة | رأس فتحة | جلسة شباك | عمود قصير

| | | | | |
|---|---|---|---|---|
| **مصنع وتد الأخشاب**<br>Watad Wood Factory | المشروع / العميل<br>**كوخ خشب دورين — مجلس رجال ومجلس نساء + 4 غرف — 15.00 × 10.00 م (300 م²)**<br>**عميل — كوخ دورين** | عنوان اللوحة<br>**لوحات التأطير (للورشة)** | المقياس<br>**—** | التاريخ<br>**2026-10-24** | رقم اللوحة<br>**W-16 (16/23)** |

## تأطير جدار ب-خلف الماستر — الطول 600 سم، الارتفاع 280 سم (داخلي)

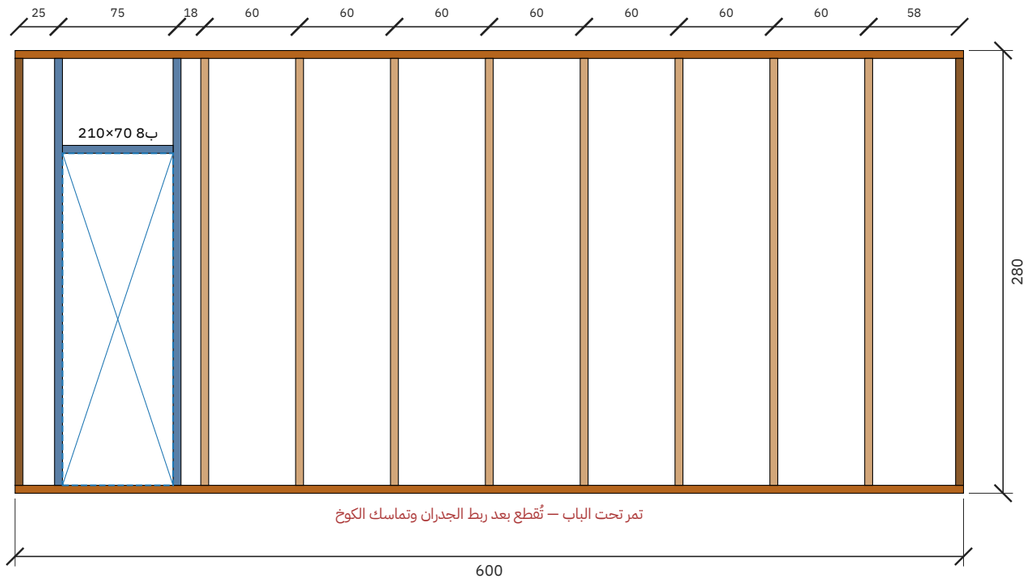


## تأطير جدار ب-جدار الحمام — الطول 422 سم، الارتفاع 280 سم (داخلي)

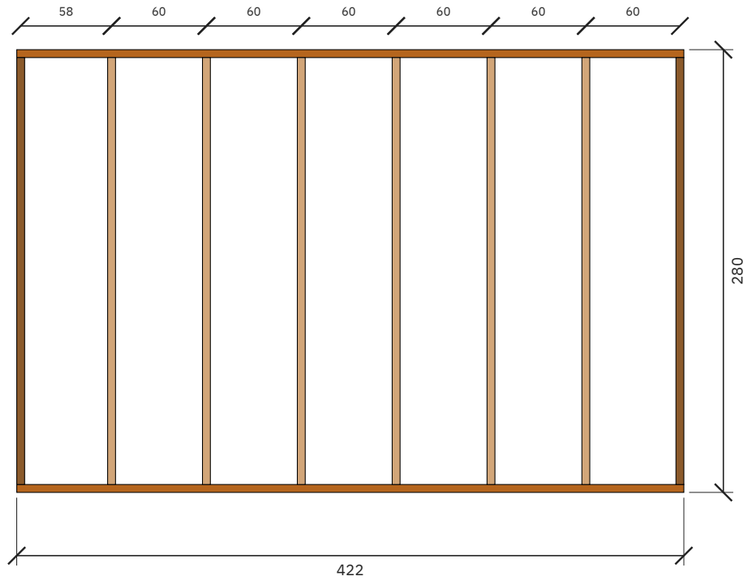



قاعدة سفلية | علوي | عمود | عمود زاوية | جنب فتحة | رأس فتحة | جلسة شباك | عمود قصير


| المشروع / العميل | عنوان اللوحة | المقياس | التاريخ | رقم اللوحة |
|---|---|---|---|---|
| **كوخ خشب دورين — مجلس رجال ومجلس نساء + 4 غرف — 15.00 × 10.00 م (300 م²)**<br>**عميل — كوخ دورين** | **لوحات التأطير (للورشة)** | **—** | **2026-10-24** | **W-17 (17/23)** |

**مصنع وتد الأخشاب**
Watad Wood Factory

## تأطير جدار ب-حمام الممر — الطول 300 سم، الارتفاع 280 سم (داخلي)

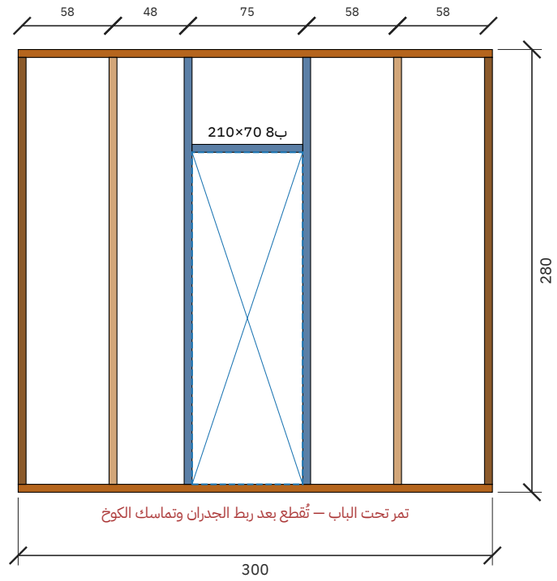



## تأطير جدار ب-جدار الغرف — الطول 988 سم، الارتفاع 280 سم (داخلي)

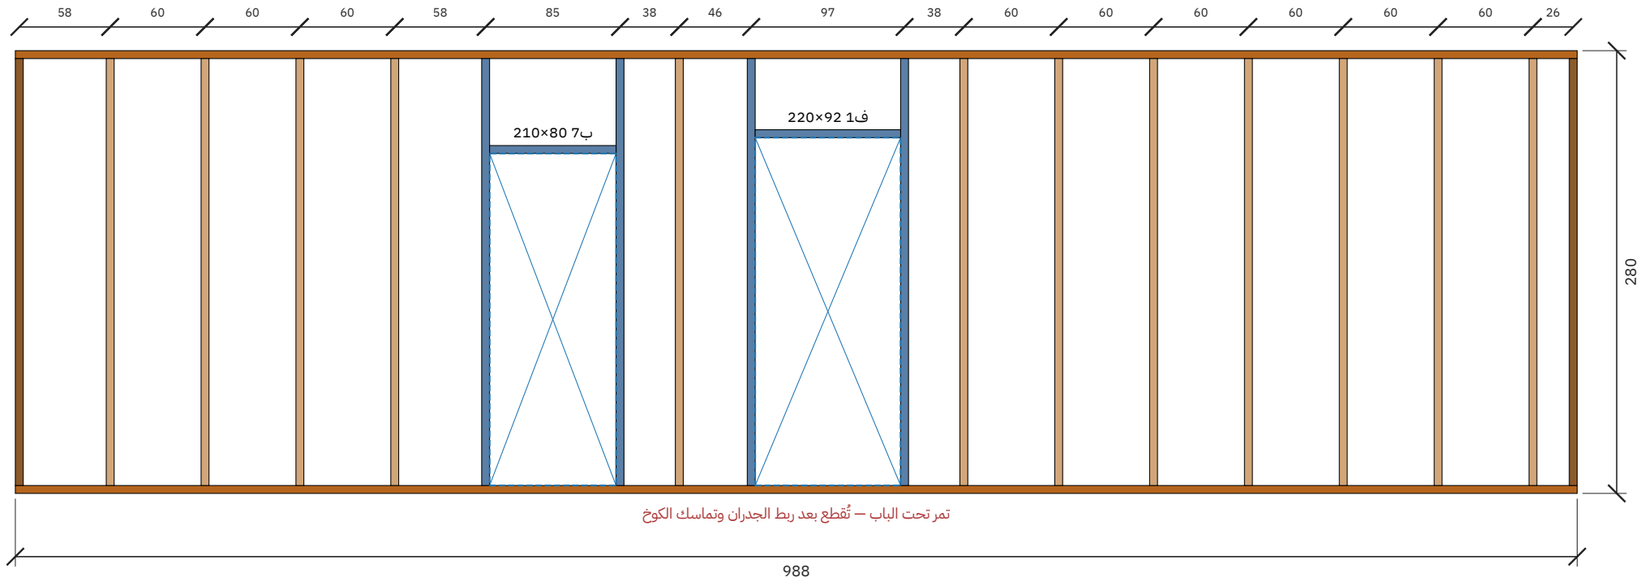



قاعدة سفلية | علوي | عمود | عمود زاوية | جنب فتحة | رأس فتحة | جلسة شباك | عمود قصير

| | | | | |
|---|---|---|---|---|
| مصنع وتد الأخشاب<br>Watad Wood Factory | المشروع / العميل<br>**كوخ خشب دورين — مجلس رجال ومجلس نساء + 4 غرف — 15.00 × 10.00 م (300 م²)**<br>**عميل — كوخ دورين** | عنوان اللوحة<br>**لوحات التأطير (للورشة)** | المقياس<br>**—** | التاريخ<br>**2026-10-24** | رقم اللوحة<br>**W-18 (18/23)** |

## تأطير جدار ب-خلف غرفة 3 — الطول 588 سم، الارتفاع 280 سم (داخلي)

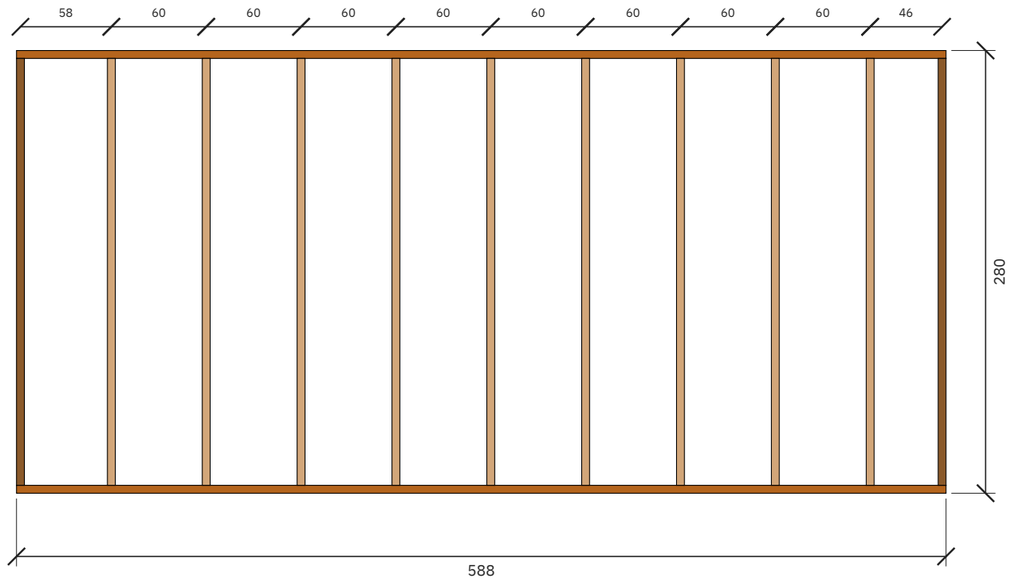



## تأطير جدار ب-غرفة 4 — الطول 384 سم، الارتفاع 280 سم (داخلي)

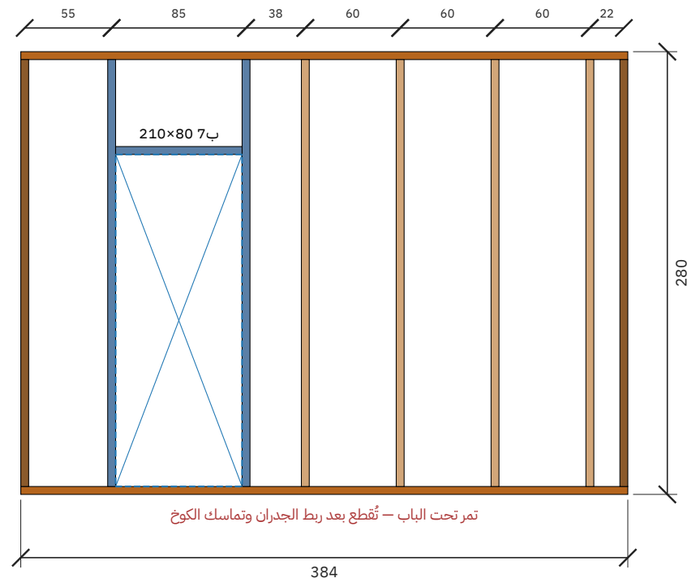


قاعدة سفلية | علوي | عمود | عمود زاوية | جنب فتحة | رأس فتحة | جلسة شباك | عمود قصير

| | | | | |
|---|---|---|---|---|
| **مصنع وتد الأخشاب**<br>Watad Wood Factory | المشروع / العميل<br>**كوخ خشب دورين — مجلس رجال ومجلس نساء + 4 غرف — 15.00 × 10.00 م (300 م²)**<br>**عميل — كوخ دورين** | عنوان اللوحة<br>**لوحات التأطير (للورشة)** | المقياس<br>**—** | التاريخ<br>**2026-10-24** | رقم اللوحة<br>**W-19 (19/23)** |

## تأطير جدار ب-جدار الدرج — الطول 422 سم، الارتفاع 280 سم (داخلي)

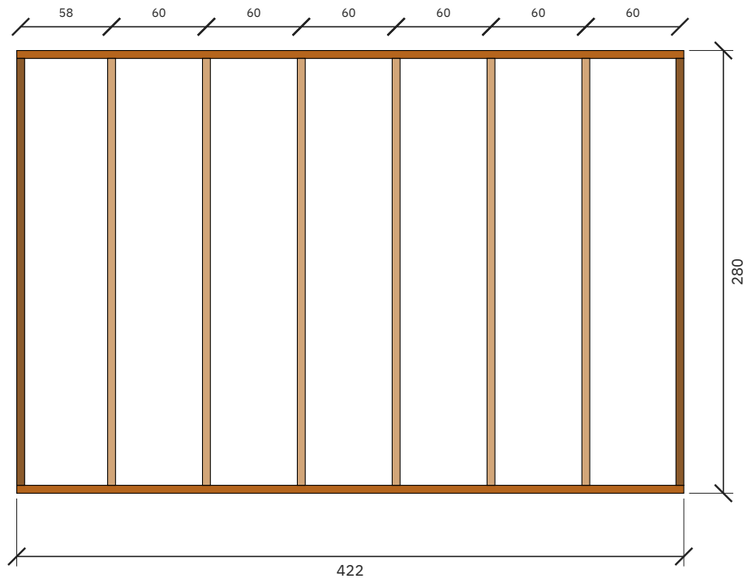


عمود قصير
جلسة شباك
رأس فتحة
جنب فتحة
عمود زاوية
عمود
علوي
قاعدة سفلية

| | | | | |
|---|---|---|---|---|
| مصنع وتد الأخشاب<br>Watad Wood Factory | المشروع / العميل<br>كوخ خشب دورين — مجلس رجال ومجلس نساء + 4 غرف — 15.00 × 10.00 م (300 م²)<br>عميل — كوخ دورين | عنوان اللوحة<br>لوحات التأطير (للورشة) | المقياس<br>— | التاريخ<br>2026-10-24 | رقم اللوحة<br>W-20 (20/23) |

## جدول الكميات وخطة تقطيع الطبليات

| البند | القيمة |
|---|---|
| الارتفاع المطلوب / المعتمد | 280 / 280 سم |
| السقف | جملون 30° — أعلى نقطة 874 سم من وجه الصبة |
| المدادات 5×15 | 108 مداد (27 خط × قطعتين موصولة فوق الجسر الحامل بتراكب 60 سم) × حتى 370 سم — من طبلية 480 |
| طبليات الطريقة الأولى (مداد + عمود) | 108 طبلية × 480 سم |
| طبليات الطريقة الثانية (3 أعمدة) | 114 طبلية × 320 سم |
| مدادات أرضية الدور العلوي 5×15 كل 60 سم | 85 مداد — 214سم×17، 216سم×17، 310سم×17، 394سم×17، 404سم×17 (طبلية 480 بالطريقة الأولى) |
| مدادات المثلث البارز (S) 40° | 16 مداد حتى 274 سم (طبلية 320) + 2 مداد وادي 589 سم — وصلة |
| | 16 مداد حتى 281 سم (طبلية 320) + 2 مداد وادي 608 سم — وصلة |
| إجمالي الطبليات 5×22.5 | 343 |
| إجمالي قطع 5×7 | 484 |
| قائمة تقطيع 5×7 | 1488سم×8 \| 988سم×16 \| 600سم×4 \| 588سم×4 \| 422سم×8 \| 384سم×2 \| 300سم×4 \| 270سم×339 \| 190سم×1 |
| | 180سم×1 \| 160سم×13 \| 155سم×4 \| 140سم×8 \| 120سم×12 \| 105سم×2 \| 100سم×1 \| 92سم×2 \| 90سم×2 |
| ألواح تلبيس 2.5 سم | 1273 لوح × 400 سم (مجموع الصفوف 4261.4 م، 46 وجه) |
| أسمنت بورد 12 مم (122×244) | 88 لوح (داخل دورات المياه) |

# جدول الكميات وخطة تقطيع الطبليات

| البند | القيمة |
|---|---|
| العزل | 642 لوح فوم صخري 80 |
| الصبة | يجهزها العميل — 20 سم، مفرغة تحت دورات المياه |

# مراجعة التصميم مقابل قواعد المصنع

| النوع | البند | التفاصيل | المقترح |
|---|---|---|---|
| ملاحظة | بحر المدادات | أطول بحر بدون جدار داخلي يحمل المداد: جهة أ: 500 سم، جهة ب: 500 سم. يحتاج رقم المصنع لأقصى بحر مسموح لتحديد المدادات اللي تُقوّى 20×5. | |
| ملاحظة | الصبة والدرج | ارتفاع الصبة 45 سم ← 3 درجة بقائمة 15.0 سم. | |
| ملاحظة | مناسيب رؤوس الفتحات | رؤوس الأبواب والشبابيك على مناسيب مختلفة: 210، 220، 230، 250 سم. | |
| تنبيه | مداد الوادي | مداد الوادي 589 سم أطول من الطبلية — يُوصل بوصلة مثبتة فوق جدار/دعامة | وصلة مزدوجة 5×15 مع براغي، ومرتكزة على جدار أو دعامة 5×7. |
| تنبيه | مداد الوادي | مداد الوادي 608 سم أطول من الطبلية — يُوصل بوصلة مثبتة فوق جدار/دعامة | وصلة مزدوجة 5×15 مع براغي، ومرتكزة على جدار أو دعامة 5×7. |
| سؤال | يحتاج تأكيد | أقصى بحر للمداد بدون جدار داخلي قبل إضافة تقوية 5×7 (مداد 20×5)؟ | |
| سؤال | يحتاج تأكيد | التغطية الصافية للوح التلبيس بعد التعشيق (مستنتجة مؤقتاً 18.67 سم من 280/15)؟ | |
| سؤال | يحتاج تأكيد | هل يوضع أعمدة قصيرة فوق رأس الشباك/الباب إلى العلوي؟ | |
| سؤال | يحتاج تأكيد | مكان الوصلة في القاعدة والعلوي إذا الجدار أطول من الطبلية؟ | |