
المسقط الأفقي مع الفرش — الدور الأرضي

الأبعاد بالسنتيمتر - الجدران: قوائم 7×5 + تلبيس 2.5 من الجهتين (12 سم) | منسوب الأرضية +0.00

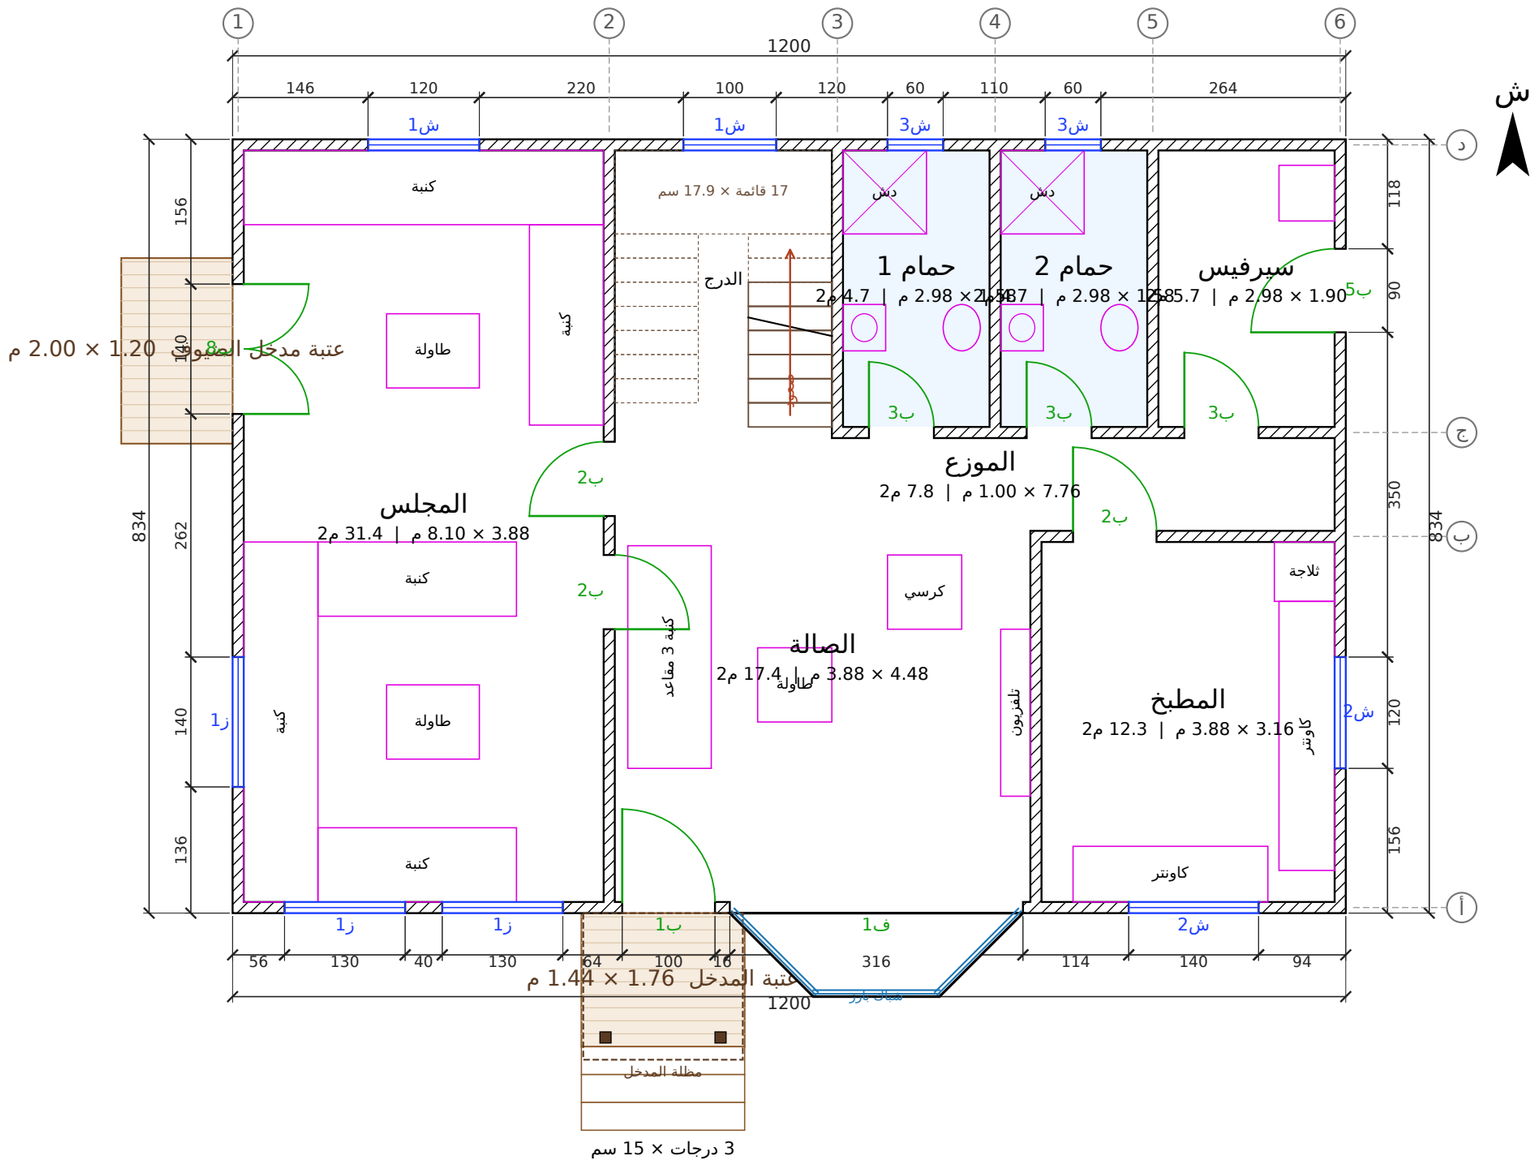


المشروع / العميل	عنوان اللوحة	المقياس	التاريخ	رقم اللوحة
كوخ دورين — 4 غرف + مجلس — 200 م² **عميل جديد**	**المسقط الأفقي — الدور الأرضي**	**1:50**	**2026-10-17**	**A-01 (1/11)**

مصنع وتد الأخشاب
Watad Wood Factory

المسقط الأفقي مع الفرش — الدور الأول

الأبعاد بالسنتيمتر - الجدران: قوائم 7×5 + تلبيس 2.5 من الجهتين (12 سم) | منسوب الأرضية +3.05

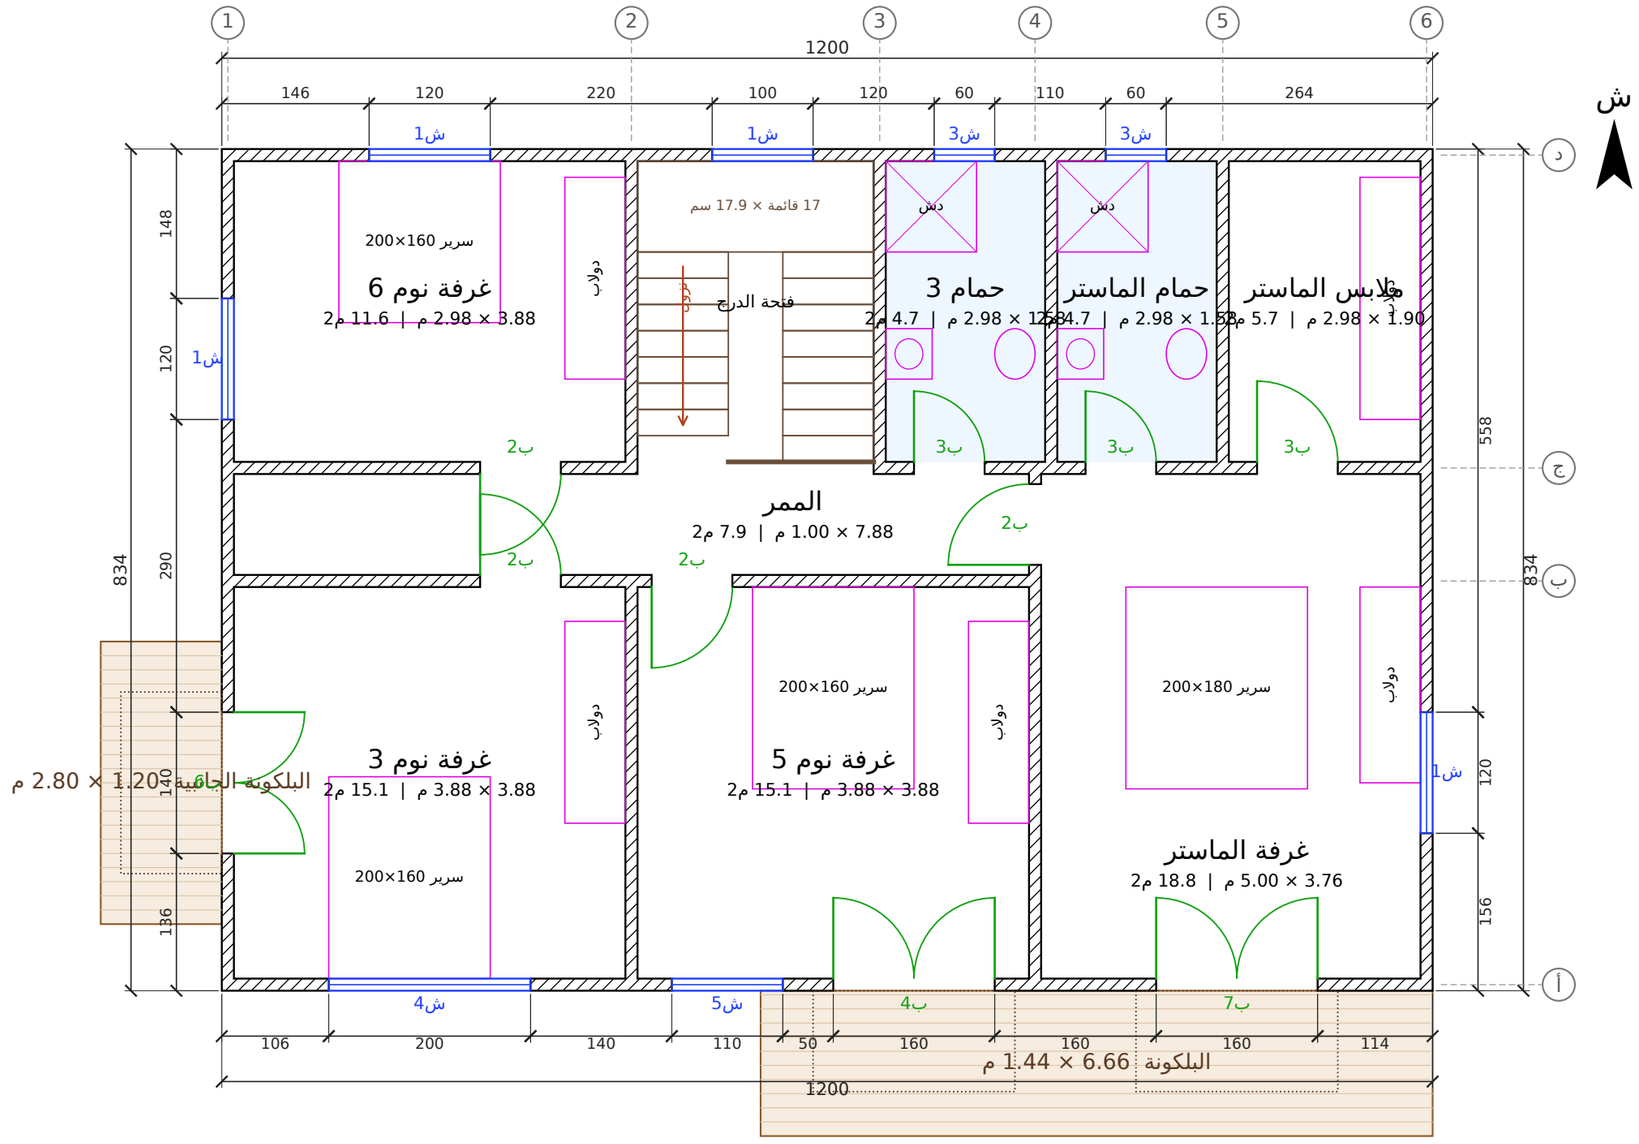


المشروع / العميل	عنوان اللوحة	المقياس	التاريخ	رقم اللوحة
كوخ دورين — 4 غرف + مجلس — 200 م² **عميل جديد**	**المسقط الأفقي — الدور الأول**	**1:50**	**2026-10-17**	**A-02 (2/11)**

مصنع وتد الأخشاب
Watad Wood Factory



الواجهة الأمامية

مقياس 1:50 | الوحدة: سم

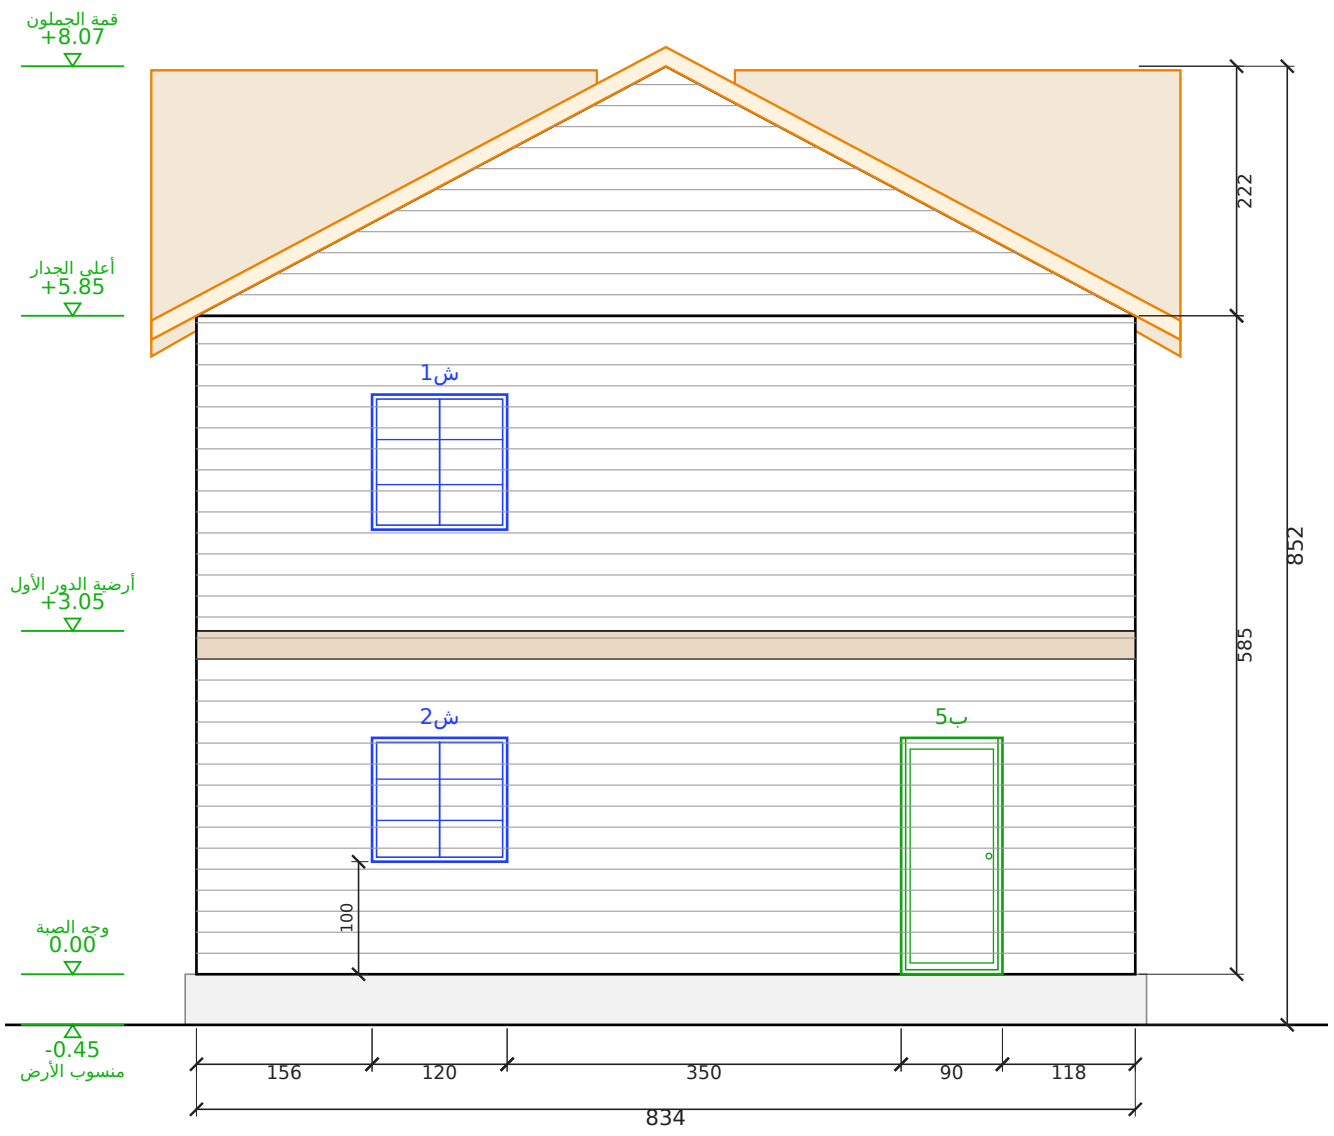


الواجهة الشرقية

مقياس 1:50 | الوحدة: سم


المشروع / العميل	عنوان اللوحة	المقياس	التاريخ	رقم اللوحة
كوخ دورين — 4 غرف + مجلس — 200 م² عميل جديد	الواجهة الأمامية والواجهة الشرقية	1:50	2026-10-17	A-03 (3/11)

مصنع وتد الأخشاب
Watad Wood Factory

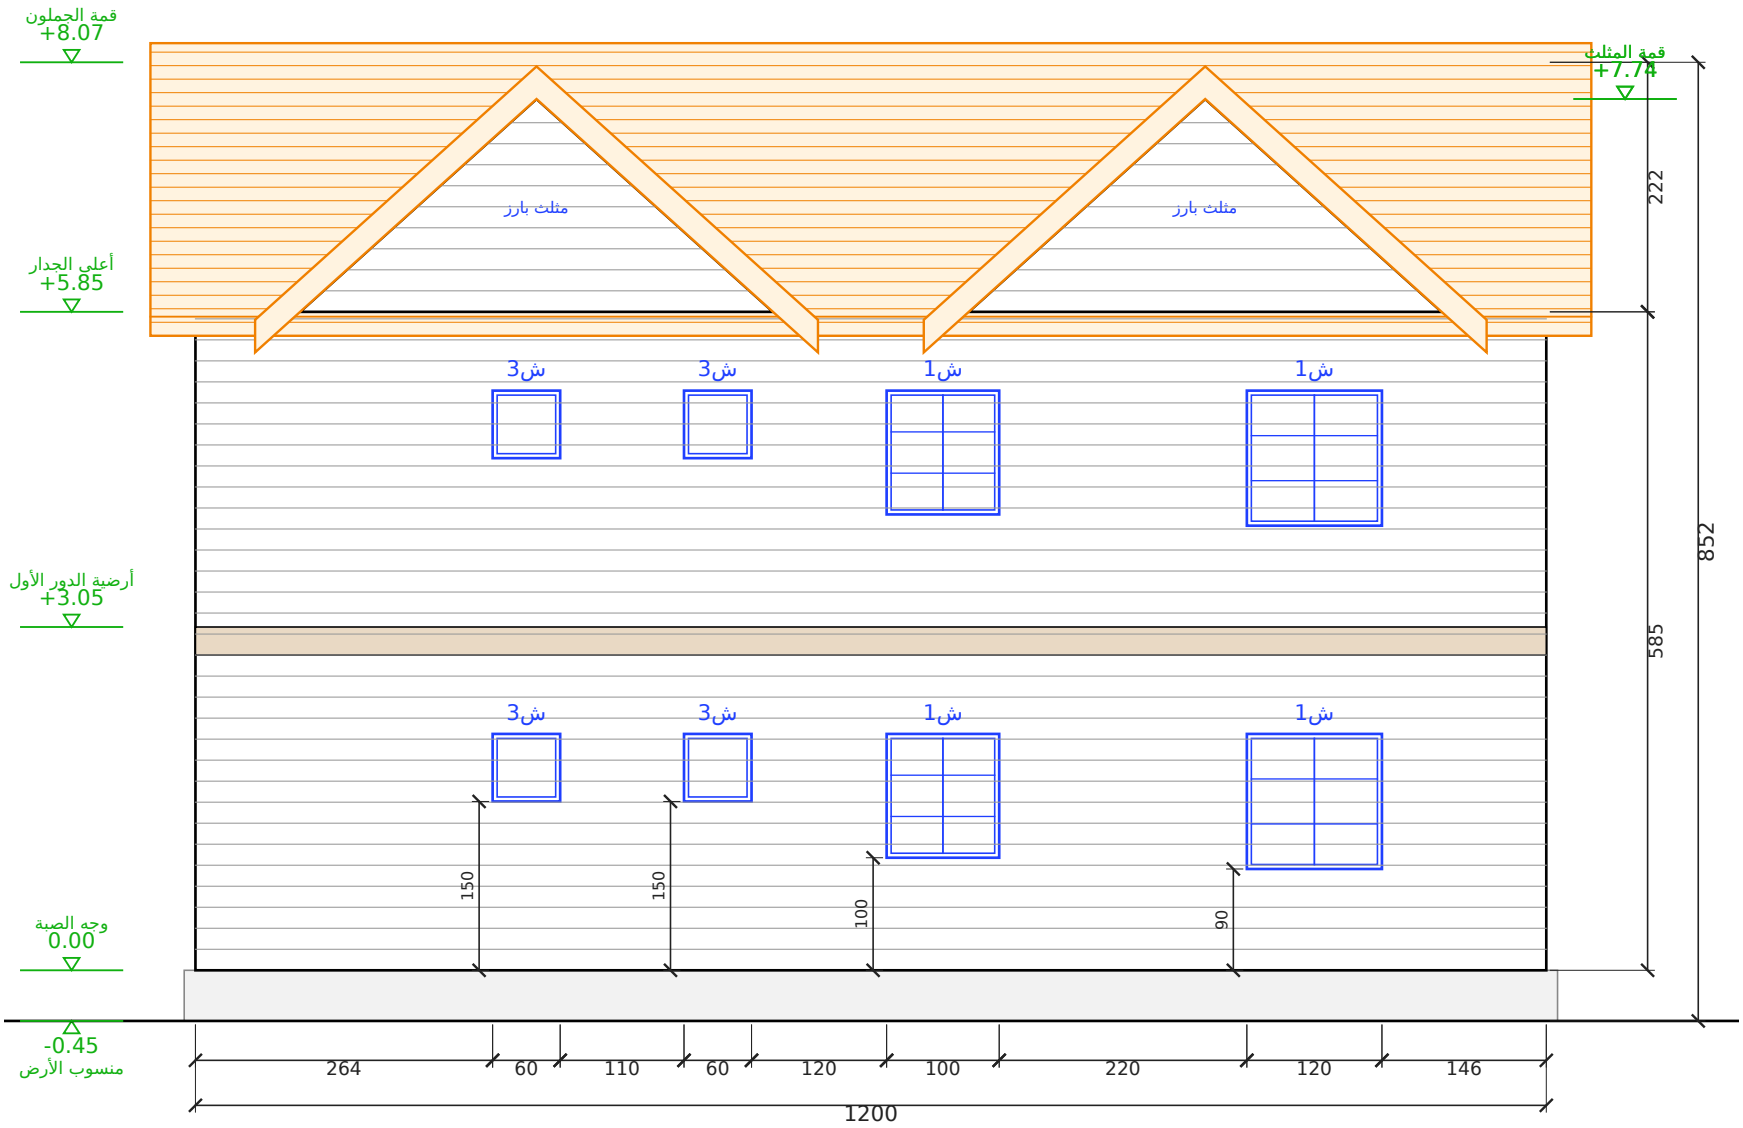

الواجهة الخلفية

مقياس 1:50 | الوحدة: سم

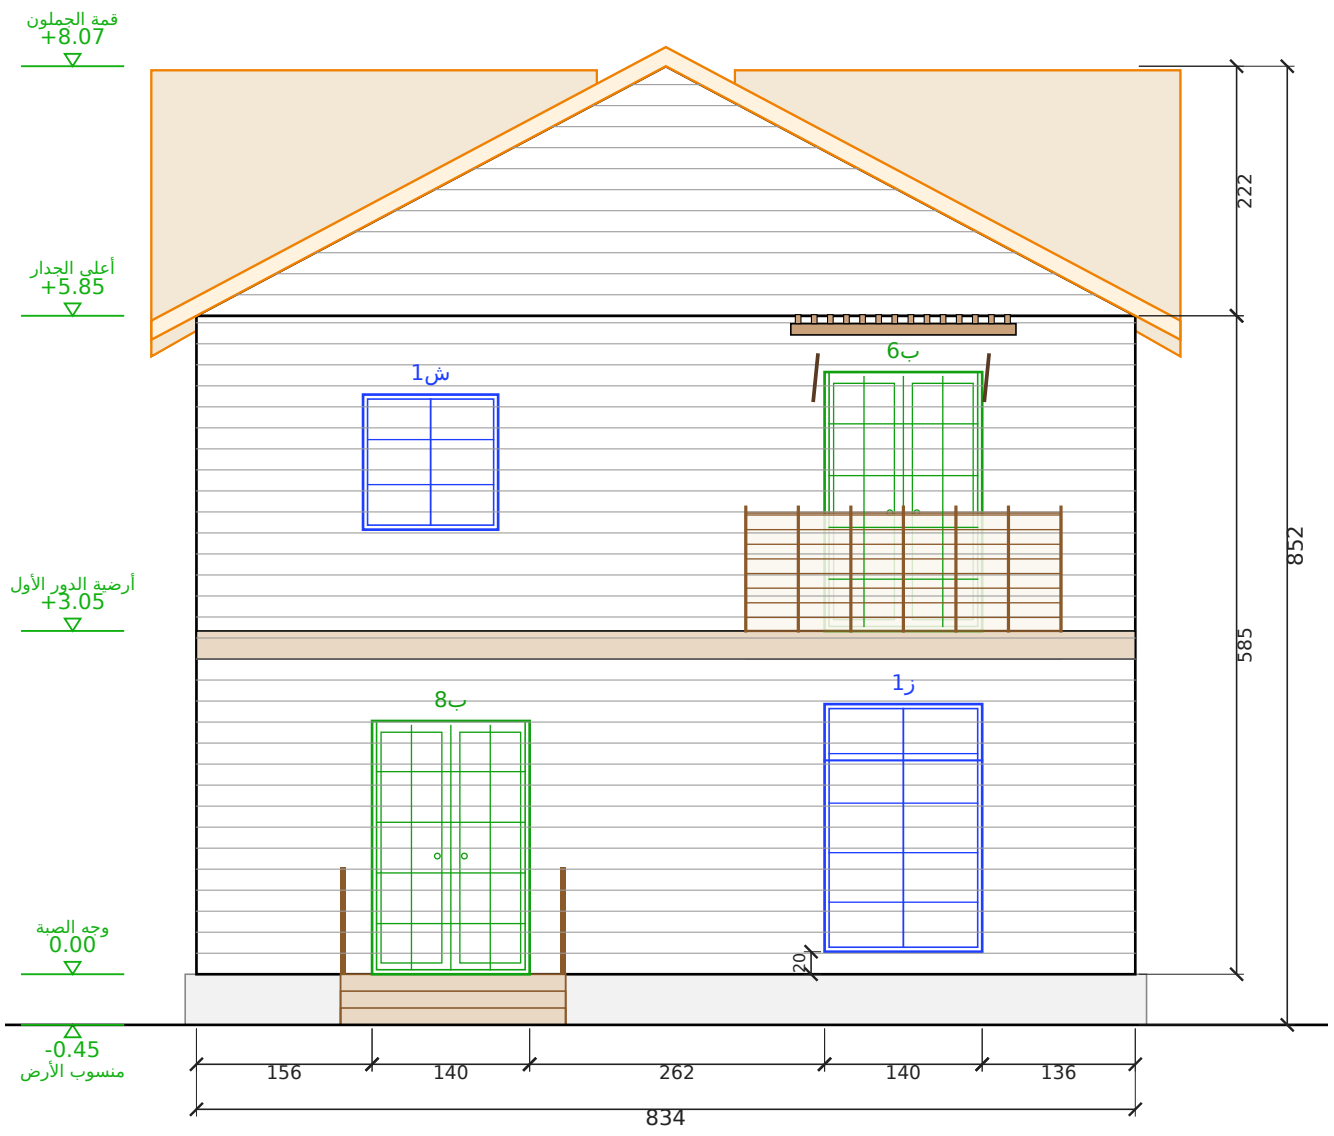


الواجهة الغربية

مقياس 1:50 | الوحدة: سم


المشروع / العميل	عنوان اللوحة	المقياس	التاريخ	رقم اللوحة
كوخ دورين — 4 غرف + مجلس — 200 م² **عميل جديد**	**الواجهة الخلفية والواجهة الغربية**	**1:50**	**2026-10-17**	**A-04 (4/11)**

مصنع وتد الأخشاب
Watad Wood Factory


مسقط السقف (جملون)
رفرف 40 سم من كل جهة | مقياس 1:50

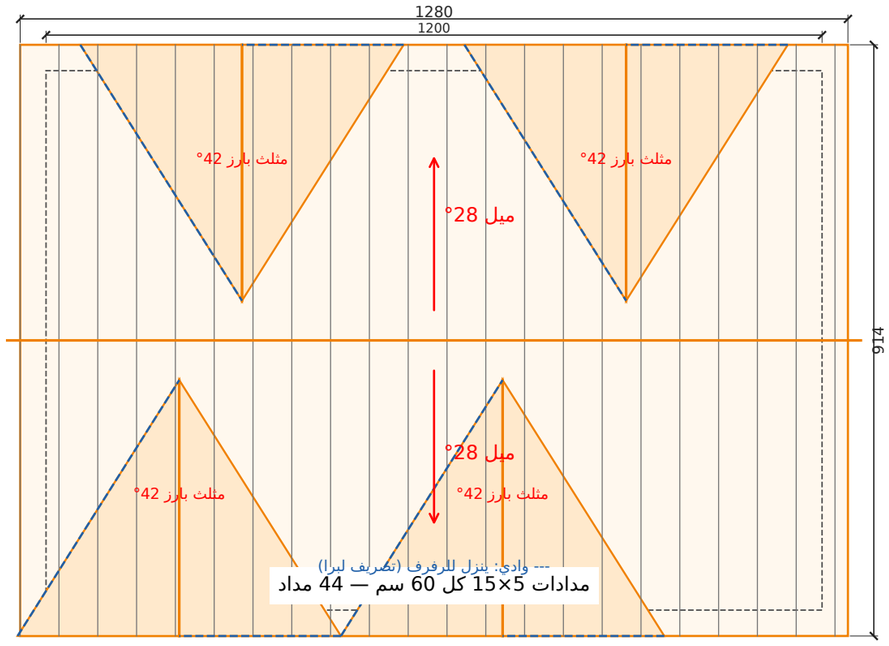

قطاع عرضي أ-أ
مقياس 1:50 | الوحدة: سم

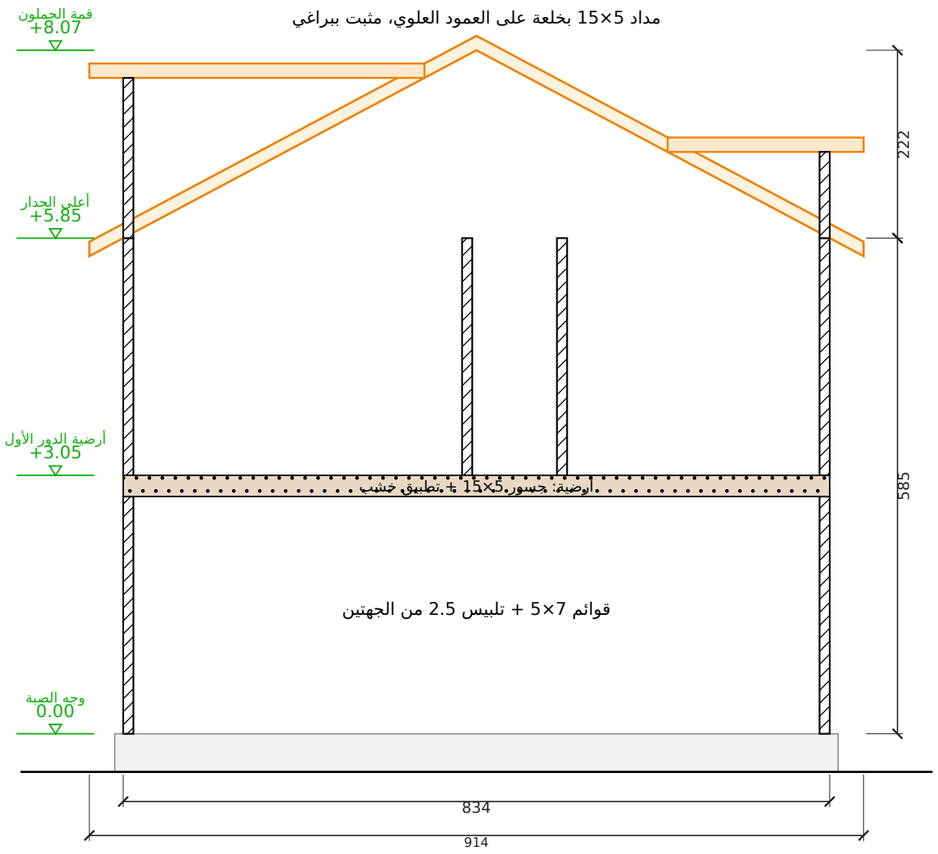

تفصيلة جلوس المداد على العلوي (1:5)

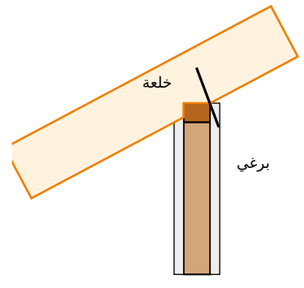

علوي 7×5 على قائم 7×5

المشروع / العميل	عنوان اللوحة	المقياس	التاريخ	رقم اللوحة
كوخ دورين — 4 غرف + مجلس — 200 م² عميل جديد	مسقط السقف والقطاع	1:50	2026-10-17	A-05 (5/11)

مصنع وتد الأخشاب
Watad Wood Factory

جدول مقاسات الأبواب والشبابيك
مقاس الفتحة الصافي في الجدار - الوحدة: سم

الرمز	النوع	العرض (سم)	الارتفاع (سم)	ارتفاع الجلسة (سم)	العدد	الموقع
ب1	باب	100	225	-	1	الأمامية
ب2	باب	80	210	-	6	المجلس - المجلس للموزع والحمام - غرفة 3 - غرفة 5 - غرفة 6 - باب جناح الماستر
ب2	باب	90	210	-	1	المطبخ
ب3	باب	70	210	-	4	حمام 1 - حمام 2 - حمام 3 - حمام الماستر
ب3	باب	80	210	-	2	السيرفيس - غرفة ملابس الماستر
ب4	باب مزدوج	160	230	-	1	الأمامية
ب5	باب	90	210	-	1	الشرقية
ب6	باب مزدوج	140	230	-	1	الغربية
ب7	باب مزدوج	160	230	-	1	الأمامية
ب8	باب مزدوج	140	225	-	1	الغربية
ف1	باب	316	250	-	1	الأمامية
ز1	شباك	130	220	20	2	الأمامية 2
ز1	شباك	140	220	20	1	الغربية
ش1	شباك	100	110	100	2	الخلفية 2
ش1	شباك	120	120	90	4	الخلفية 2 - الشرقية - الغربية
ش2	شباك	140	110	100	1	الأمامية
ش2	شباك	120	110	100	1	الشرقية
ش3	شباك	60	60	150	4	الخلفية 4
ش4	شباك	200	150	80	1	الأمامية
ش5	شباك	110	150	80	1	الأمامية

الإجمالي: أبواب 20 - شبابيك 17

جدول المساحات وبيانات المشروع والتسعير

بيانات المشروع

البند	البيان
المشروع	كوخ دورين — 4 غرف + مجلس — 200 م²
العميل	عميل جديد
الموقع	—
الاستخدام	سكن خاص
التاريخ	2026-10-17
نظام البناء	هيكل خشب 5×7 + تلبيس 2.5 سم من الجهتين
السقف	جملون 28° — قرميد معدني + 4 مثلث بارز

التسعير

عرض اليوم الوطني 96

البند	القيمة
المساحة المبنية (م2)	200.16
سعر المتر المربع — عرض اليوم الوطني 96	1,096 ريال
الإجمالي	**219,375 ريال**

ملاحظات:

- السعر للمساحة المبنية 200 م² (دورين) — الشباك البارز والبلكونات وعتبة المدخل مجاناً.
- الصبة والتمديدات الخارجية على العميل ما لم يُذكر غير ذلك.

جدول المساحات


م	الفراغ	الأبعاد (م)	المساحة (م2)
1	أرضي — المجلس	3.88 × 8.10	31.43
2	أرضي — الصالة	4.48 × 3.88	17.38
3	أرضي — المطبخ	3.16 × 3.88	12.26
4	أرضي — الموزع	7.76 × 1.00	7.76
5	أرضي — الدرج	2.34 × 2.98	6.97
6	أرضي — حمام 1	1.58 × 2.98	4.71
7	أرضي — حمام 2	1.58 × 2.98	4.71
8	أرضي — سيرفيس	1.90 × 2.98	5.66
9	أول — غرفة نوم 3	3.88 × 3.88	15.05
10	أول — غرفة نوم 5	3.88 × 3.88	15.05
11	أول — غرفة الماستر	3.76 × 5.00	18.80
12	أول — الممر	7.88 × 1.00	7.88
13	أول — غرفة نوم 6	3.88 × 2.98	11.56
14	أول — حمام 3	1.58 × 2.98	4.71
15	أول — حمام الماستر	1.58 × 2.98	4.71
16	أول — ملابس الماستر	1.90 × 2.98	5.66
	المساحة الصافية الداخلية		**174.31**
	التراس المسقوف + تراس الدور الأول (مجاناً)	**4 × 1.44 × 1.76**	**17.88**
	المساحة الإجمالية المبنية	**2 دور × 12.00 × 8.34**	**200.16**

لقطات المنظور الخارجي


المنظور الأمامي




منظور أمامي من اليسار

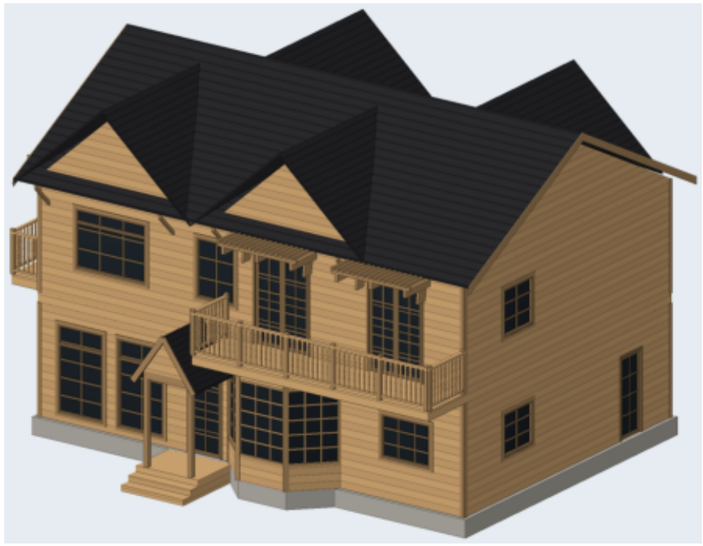

منظور أمامي من اليمين

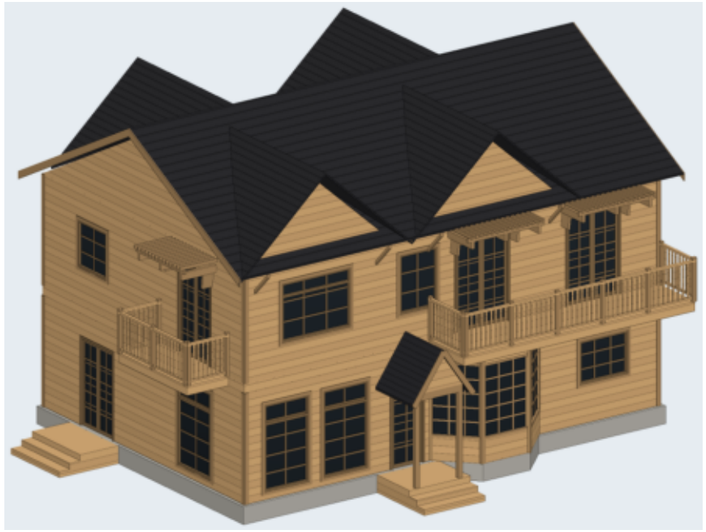


المنظور الخلفي

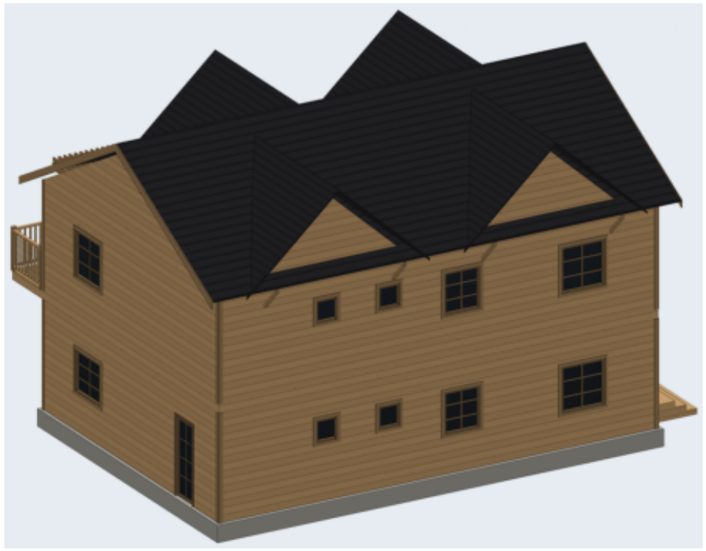

منظور خلفي من اليمين



منظر علوي

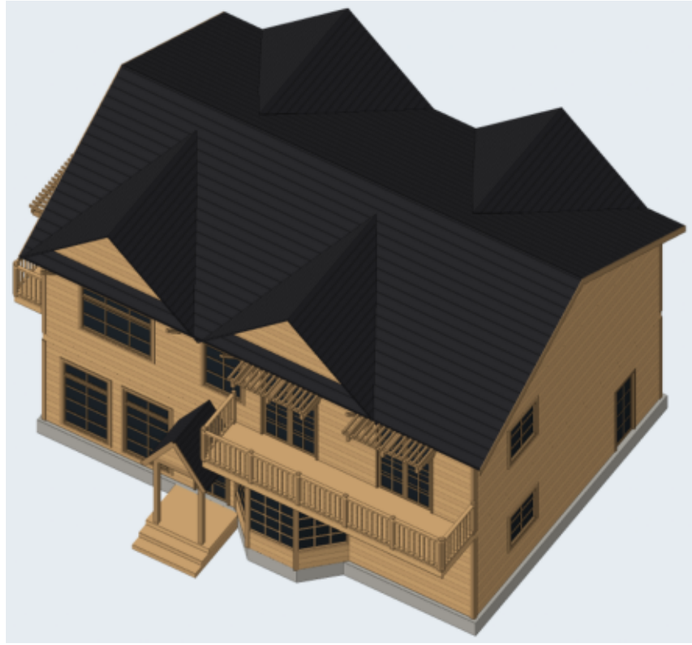


المشروع / العميل	عنوان اللوحة	المقياس	التاريخ	رقم اللوحة
كوخ دورين — 4 غرف + مجلس — 200 م² **عميل جديد**	**لقطات المنظور**	**—**	**2026-10-17**	**A-08 (8/11)**

مصنع وتد الأخشاب
Watad Wood Factory

المقطع العلوي بالفرش — الدور الأرضي

مقطع أفقي على ارتفاع 1.90 م — توزيع الفرش ومسار الحركة

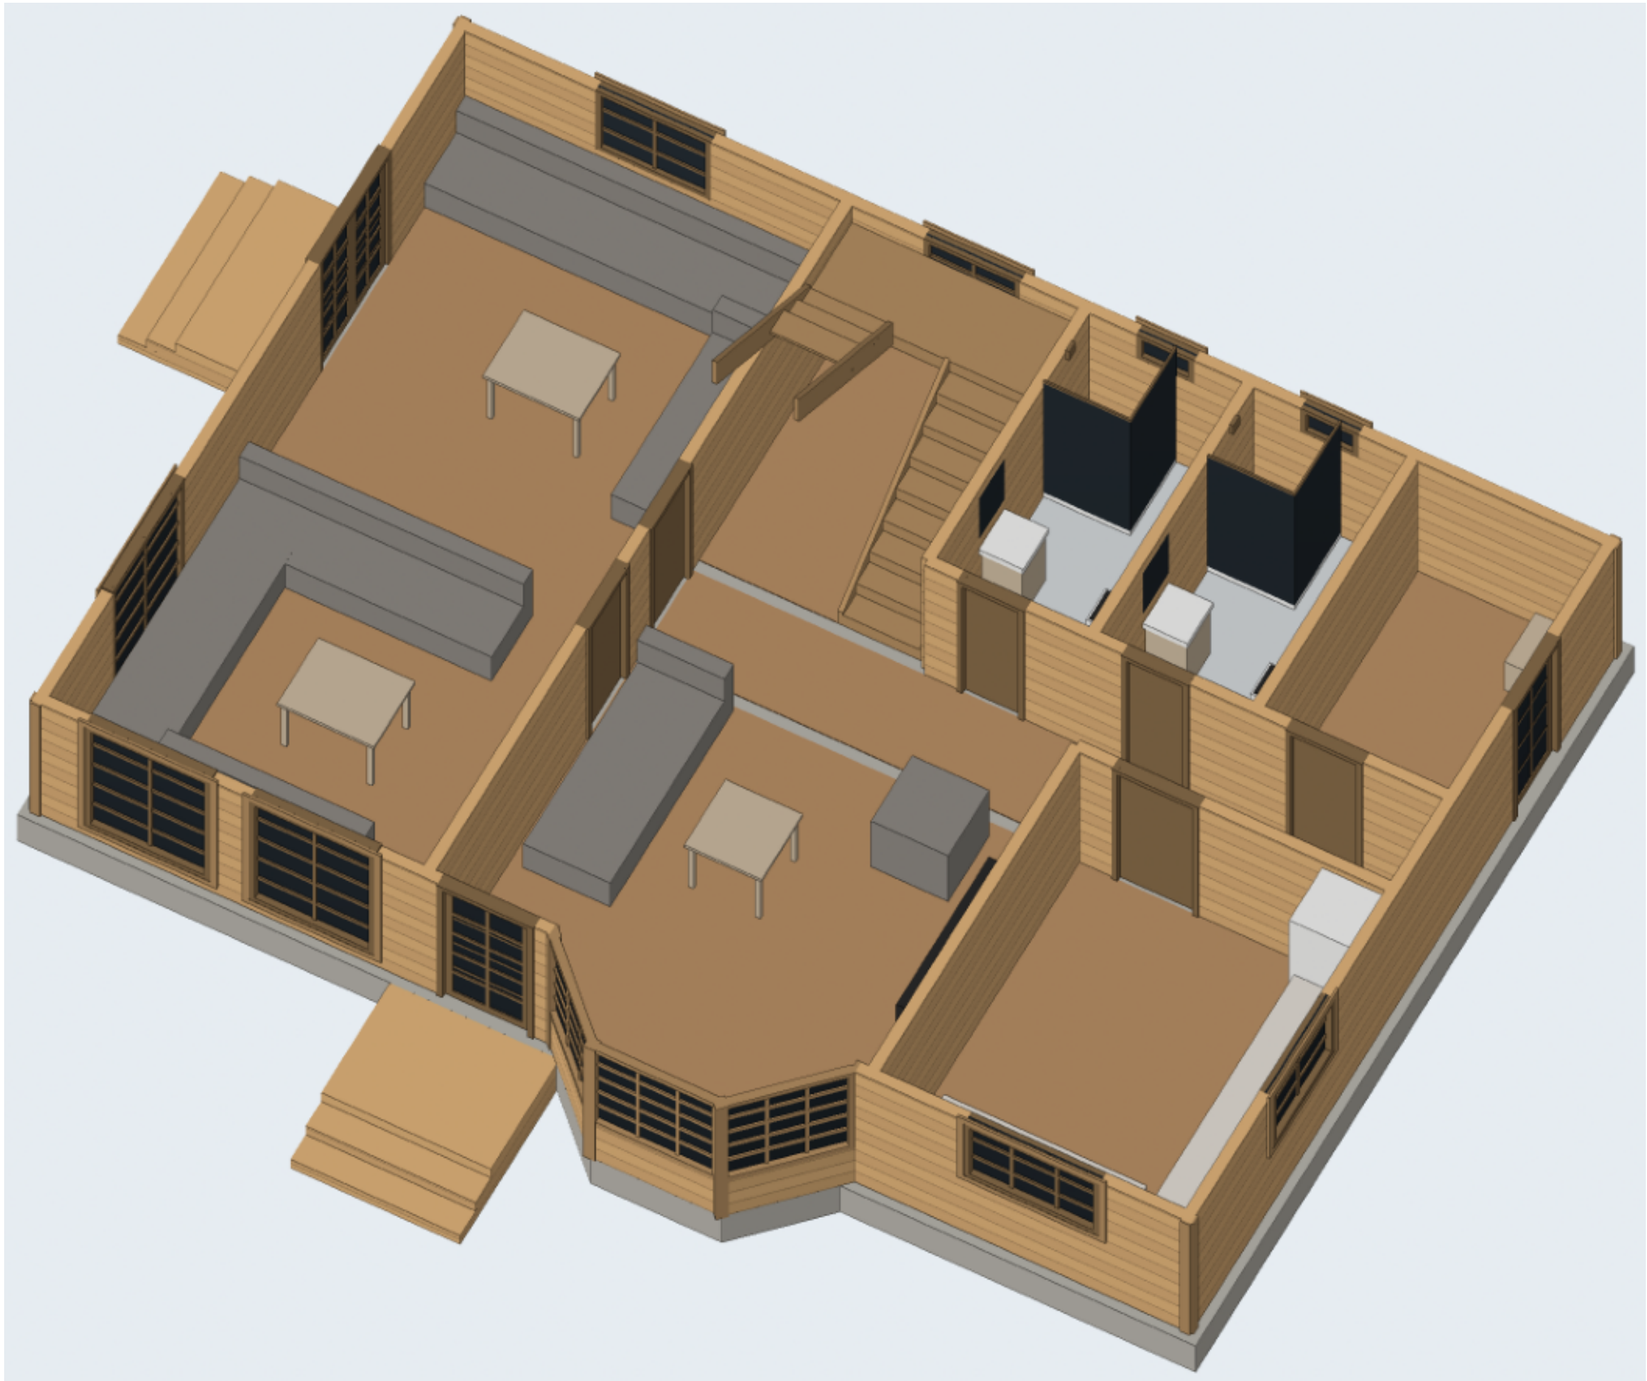


المشروع / العميل	عنوان اللوحة	المقياس	التاريخ	رقم اللوحة
كوخ دوربن — 4 غرف + مجلس — 200 م² **عميل جديد**	**المقطع العلوي بالفرش — الدور الأرضي**	**—**	**2026-10-17**	**A-09 (9/11)**

مصنع وتد الأخشاب
Watad Wood Factory

المقطع العلوي بالفرش — الدور الأول

مقطع أفقي على ارتفاع 1.90 م — توزيع الفرش ومسار الحركة

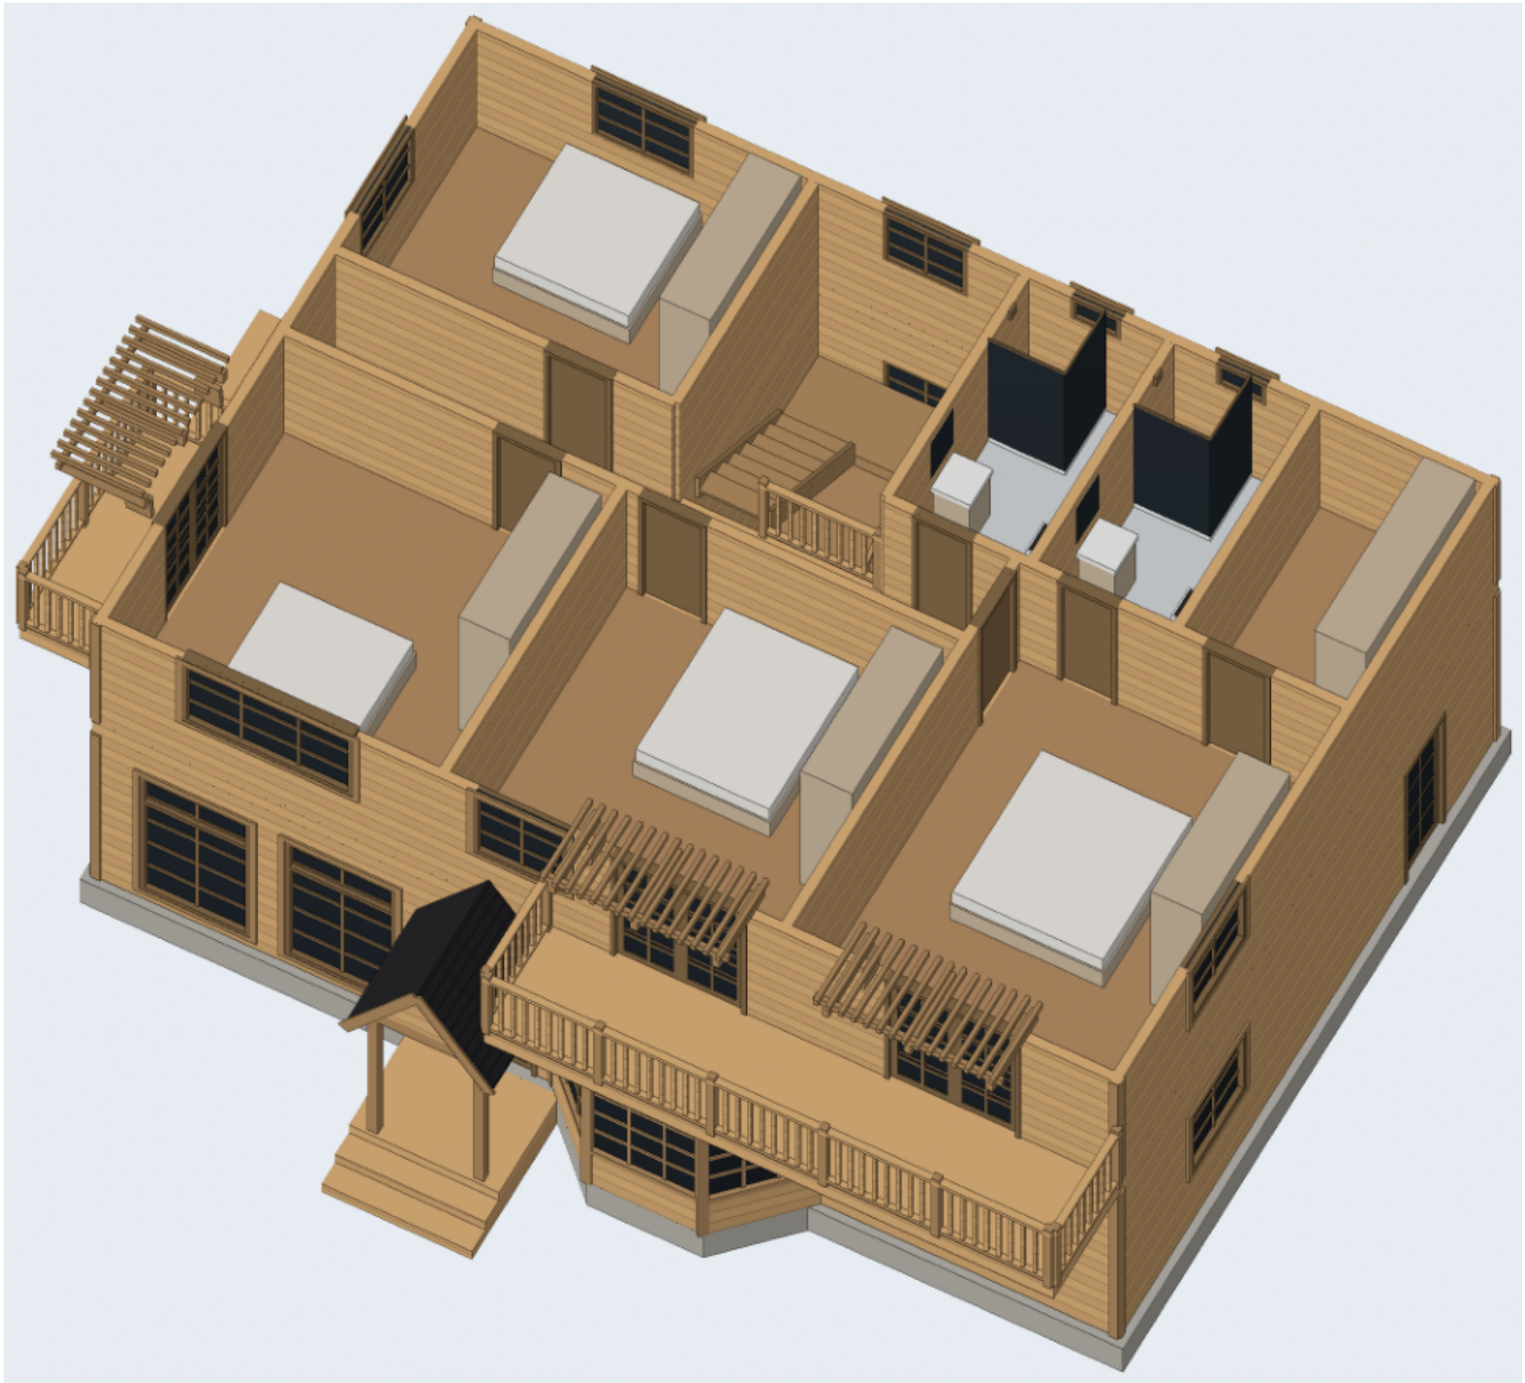


المشروع / العميل	عنوان اللوحة	المقياس	التاريخ	رقم اللوحة
كوخ دورين — 4 غرف + مجلس — 200 م² **عميل جديد**	**المقطع العلوي بالفرش — الدور الأول**	**—**	**2026-10-17**	**A-10 (10/11)**

مصنع وتد الأخشاب
Watad Wood Factory

المنظور ثلاثي الأبعاد والمواد

النمط: جوزي غامق + إطارات سوداء — رندر واقعي بخامات حقيقية

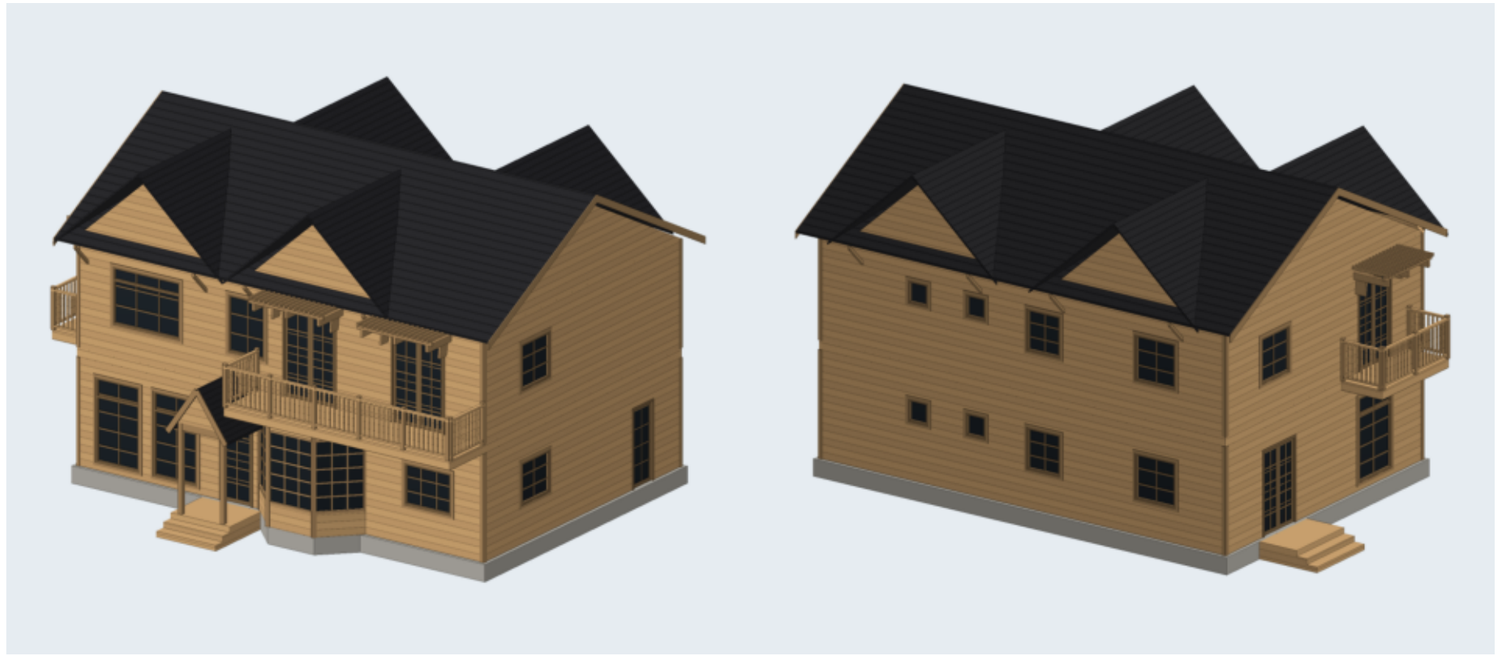

جدول المواد والألوان

الخشب / الصبغة

خشب طبيعي فاتح (بدون صبغة)

القرميد

قرميد رمادي غامق

الزجاج

زجاج عاكس غامق

إطارات الشبابيك والأبواب

إطار خشب بنفس الصبغة أغمق

الكنار والزوايا

نفس الصبغة أغمق درجة


الصبة

خرسانة 45 سم


الدربزين: ألواح أفقية متقاربة (عصري)

تقسيم الشبابيك: بدون | الباب الرئيسي: زجاج بتقسيمات (فرنسي)

أنواع الدربزين المعتمدة (من مشاريع المصنع)

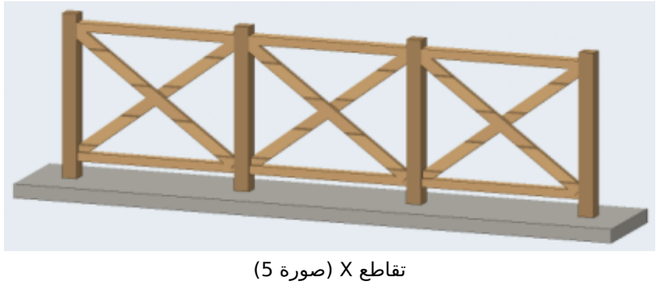

تقاطع X (صورة 5)

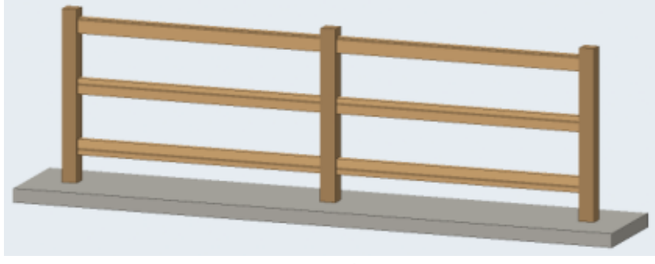

3 مرابيع أفقية (صورة 2)



قوائم رأسية متقاربة (صورة 1)

المشروع / العميل	عنوان اللوحة	المقياس	التاريخ	رقم اللوحة
كوخ دورين — 4 غرف + مجلس — 200 م² **عميل جديد**	**المنظور والمواد**	—	**2026-10-17**	**A-11 (11/11)**

مصنع وتد الأخشاب
Watad Wood Factory