المنظور ثلاثي الأبعاد والمواد

النمط: برتقالي محمر + قرميد فحمي + دربزين X — رندر واقعي بخامات حقيقية



جدول المواد والألوان

الخشب / الصبغة

صبغة عسلي / سيدر

القرميد

قرميد فحمي / أسود مزرق

الزجاج

زجاج شفاف

إطارات الشبابيك والأبواب

إطار ألمنيوم أسود

الكنار والزوايا

نفس الصبغة أغمق درجة


الصبة

خرسانة 45 سم


الدربزين: تقاطع X (صورة 5)

تقسيم الشبابيك: شبكة | الباب الرئيسي: زجاج بتقسيمات (فرنسي)

أنواع الدربزين المعتمدة (من مشاريع المصنع)

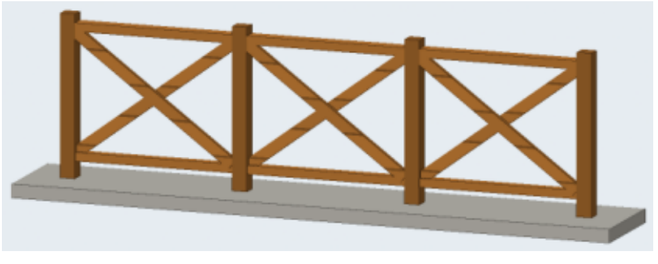

تقاطع X (صورة 5)

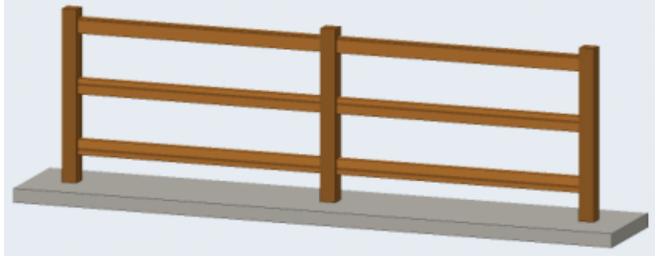

3 مرابيع أفقية (صورة 2)




قوائم رأسية متقاربة (صورة 1)

المشروع / العميل	عنوان اللوحة	المقياس	التاريخ	رقم اللوحة
مجلس وجلسة خارجية مغلقة وغرفة نوم 9.00 × 13.00 م — الحوية **عميل — الحوية**	**المنظور والمواد**	**1:50**	**2026-11-05**	**W-01 (1/15)**

مصنع وتد الأخشاب
Watad Wood Factory


المسقط الأفقي مع الفرش

الأبعاد بالسنتيمتر - الجدران: قوائم 7×5 + تلبيس 2.5 من الجهتين (12 سم)

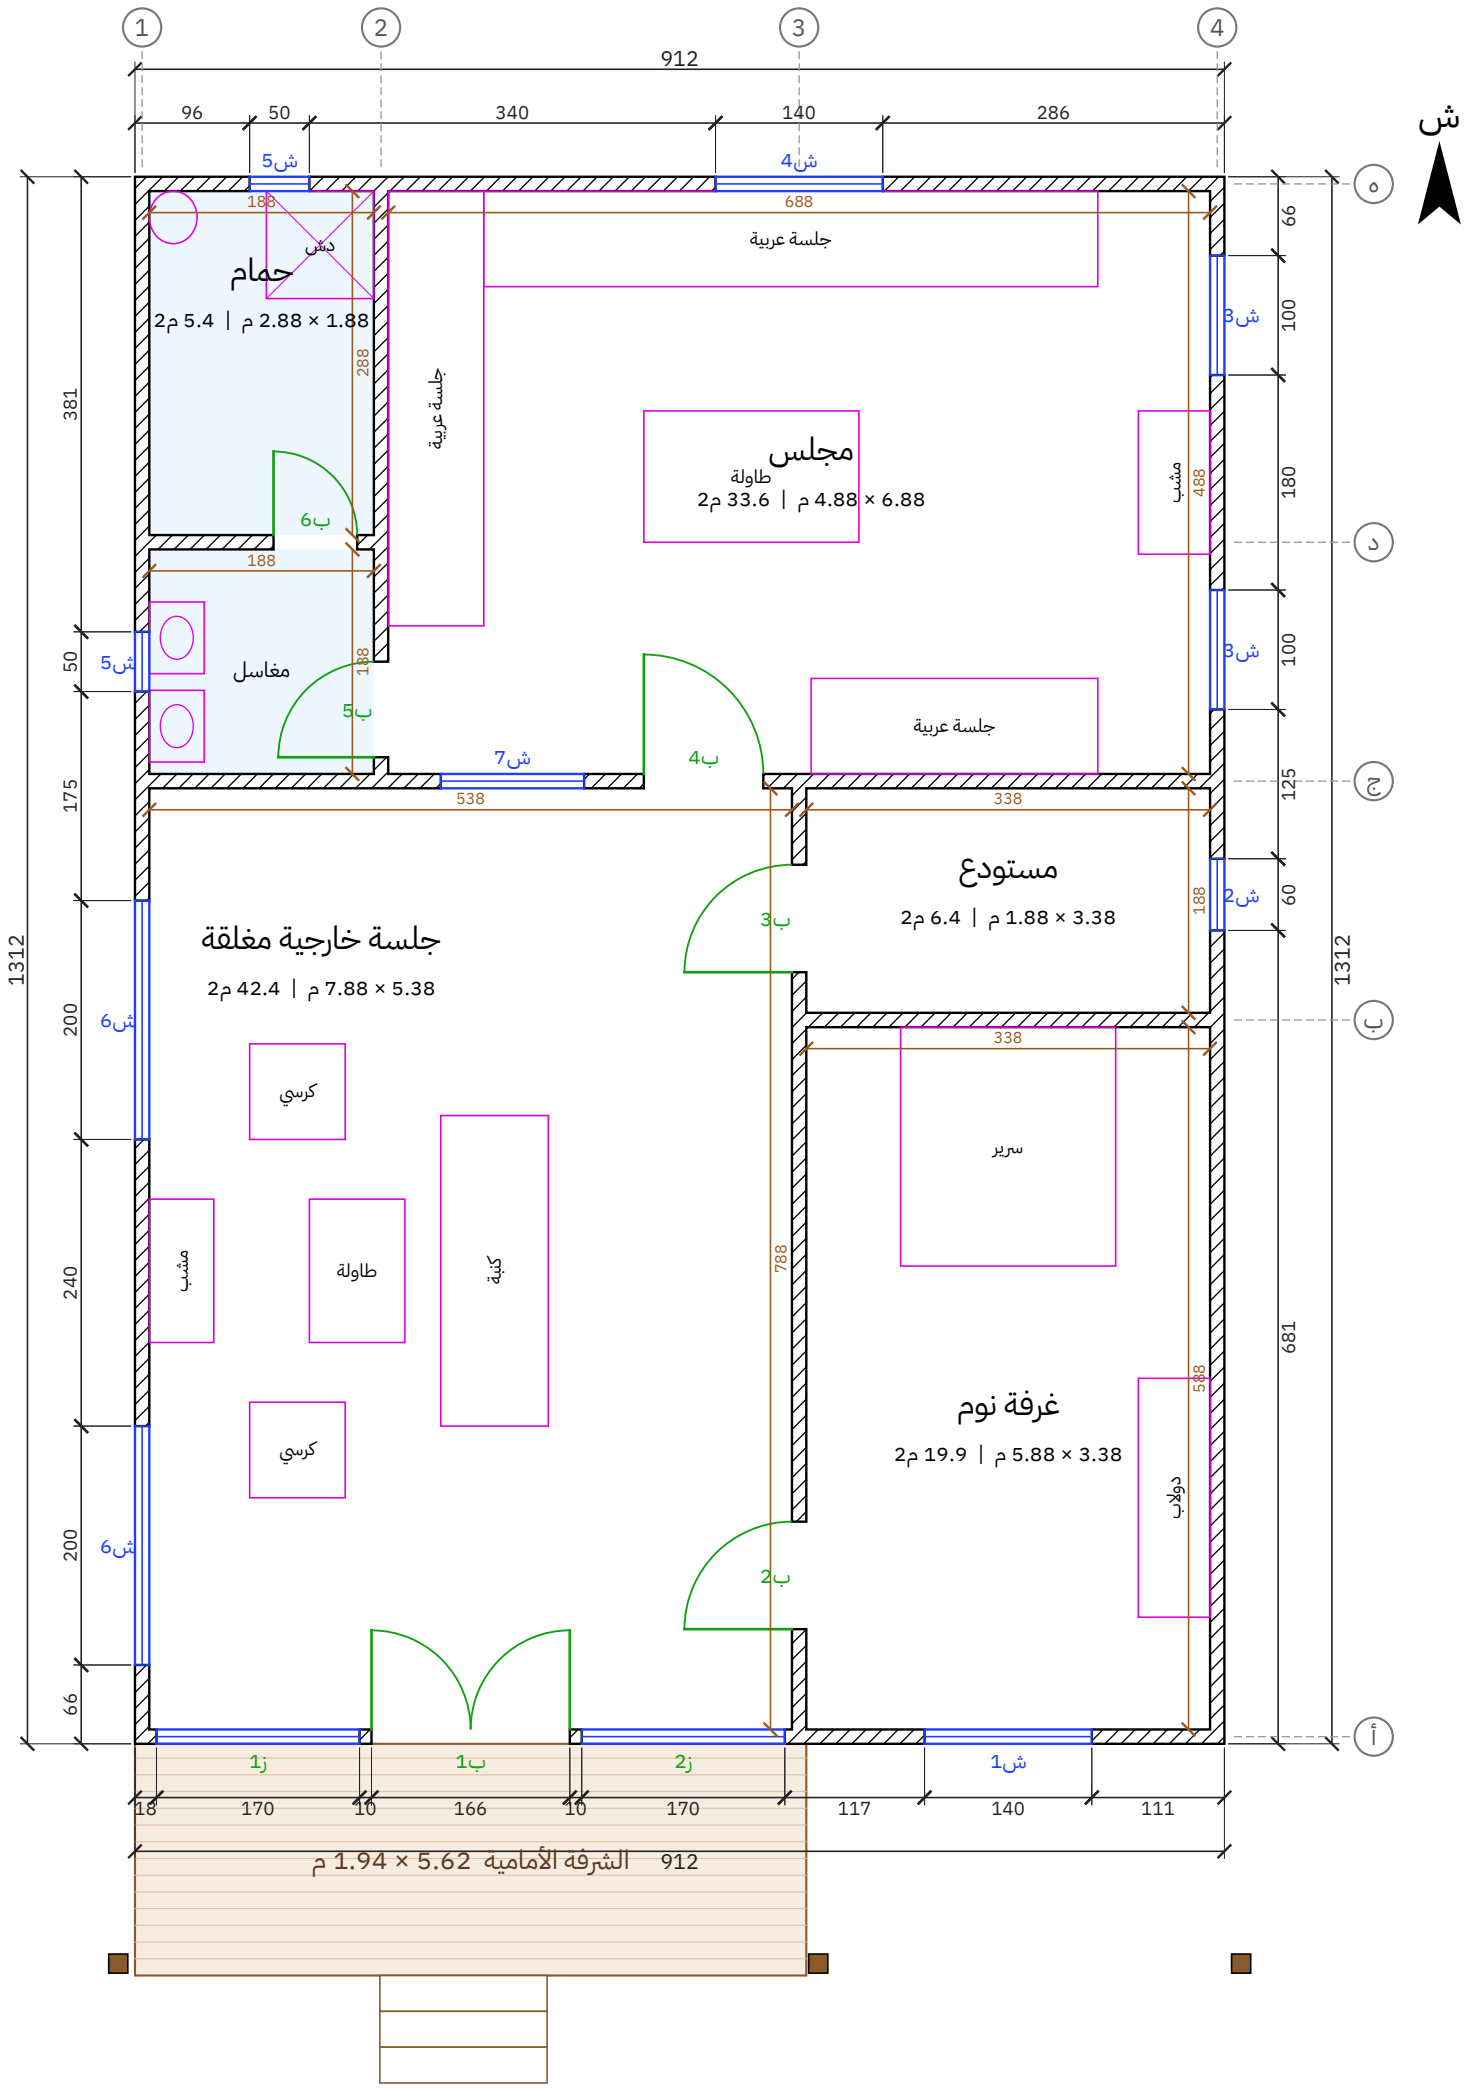


المشروع / العميل	عنوان اللوحة	المقياس	التاريخ	رقم اللوحة
مجلس وجلسة خارجية مغلقة وغرفة نوم 9.00 × 13.00 م – الحوية **عميل – الحوية**	**المسقط الأفقي**	**1:50**	**2026-11-05**	**W-02 (2/15)**

مصنع وتد الأخشاب
Watad Wood Factory

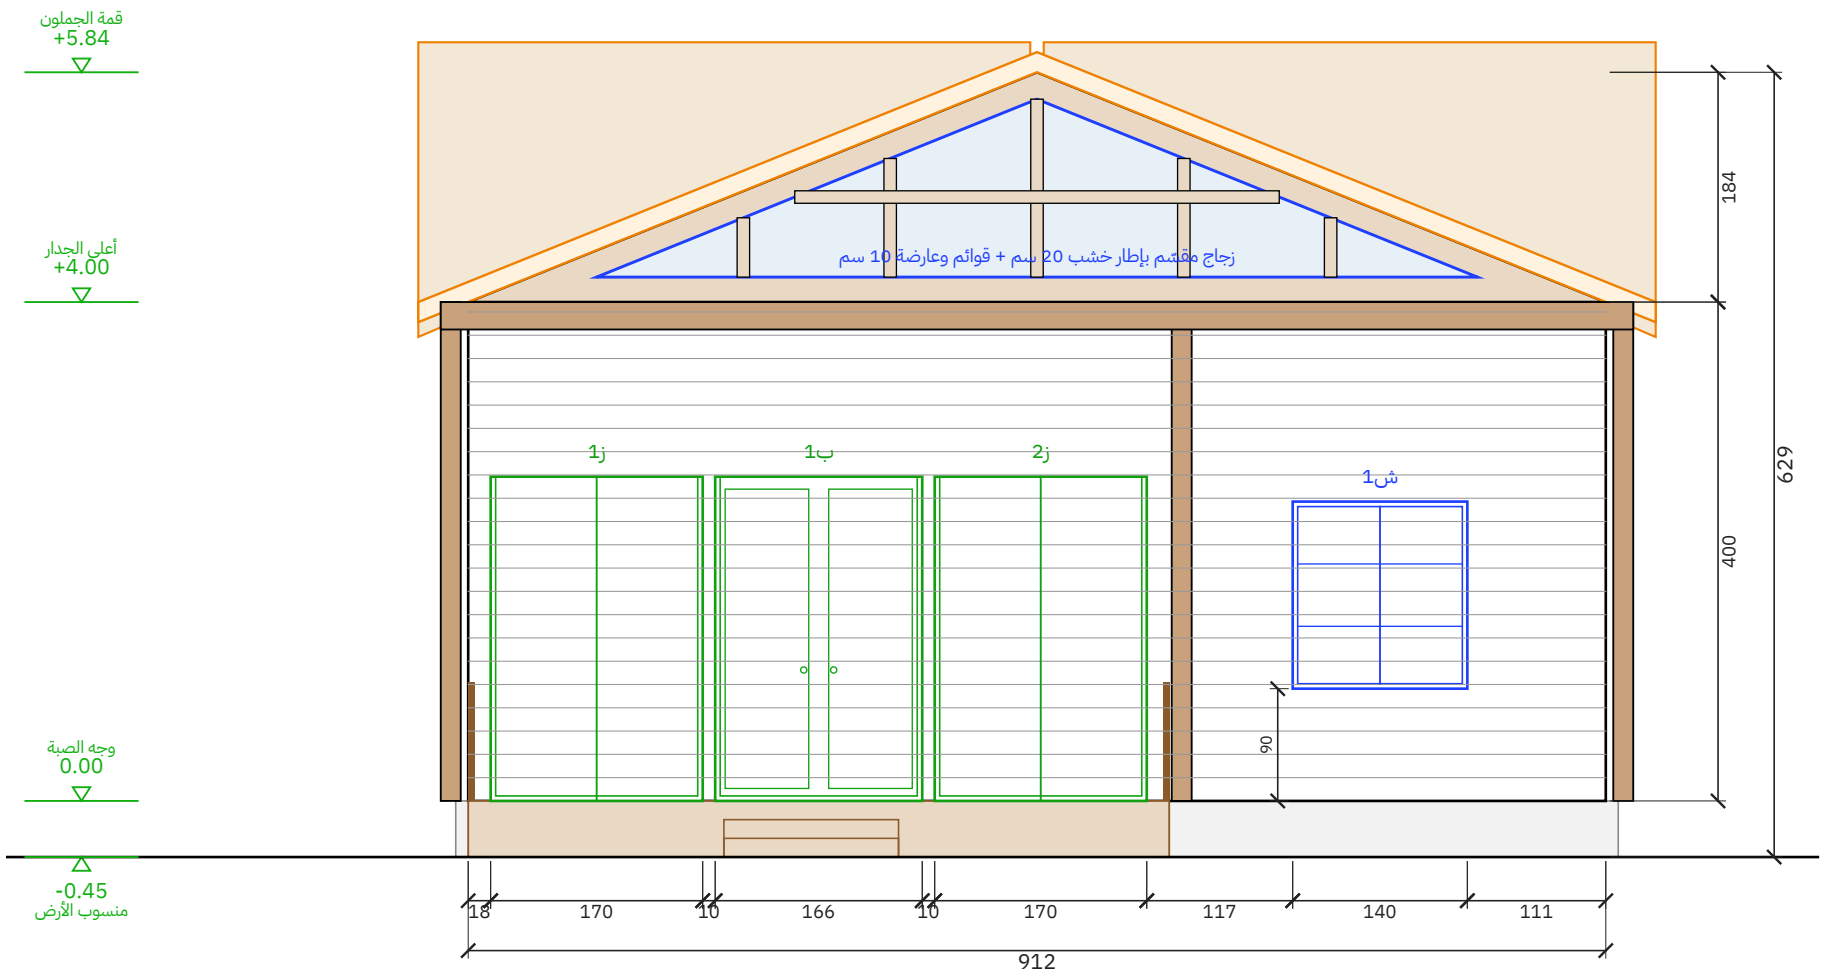

الواجهة الأمامية

مقياس 1:50 | الوحدة: سم

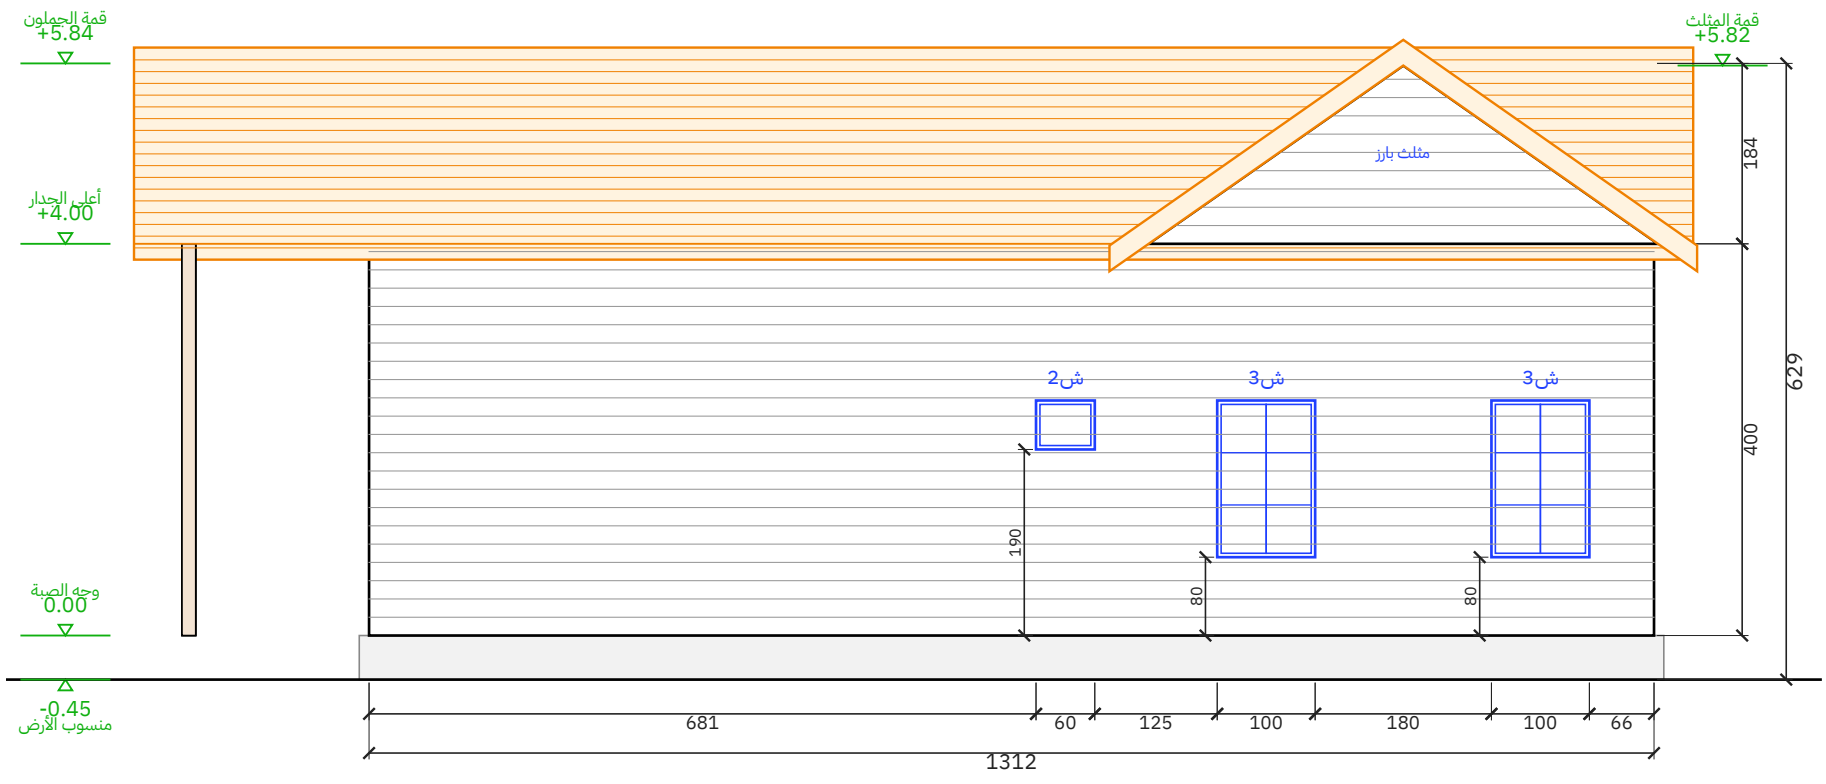


الواجهة الشرقية

مقياس 1:50 | الوحدة: سم


المشروع / العميل	عنوان اللوحة	المقياس	التاريخ	رقم اللوحة
مجلس وجلسة خارجية مغلقة وغرفة نوم 9.00 × 13.00 م – الحوية **عميل – الحوية**	**الواجهة الأمامية والواجهة الشرقية**	**1:50**	**2026-11-05**	**W-03 (3/15)**

مصنع وتد الأخشاب
Watad Wood Factory

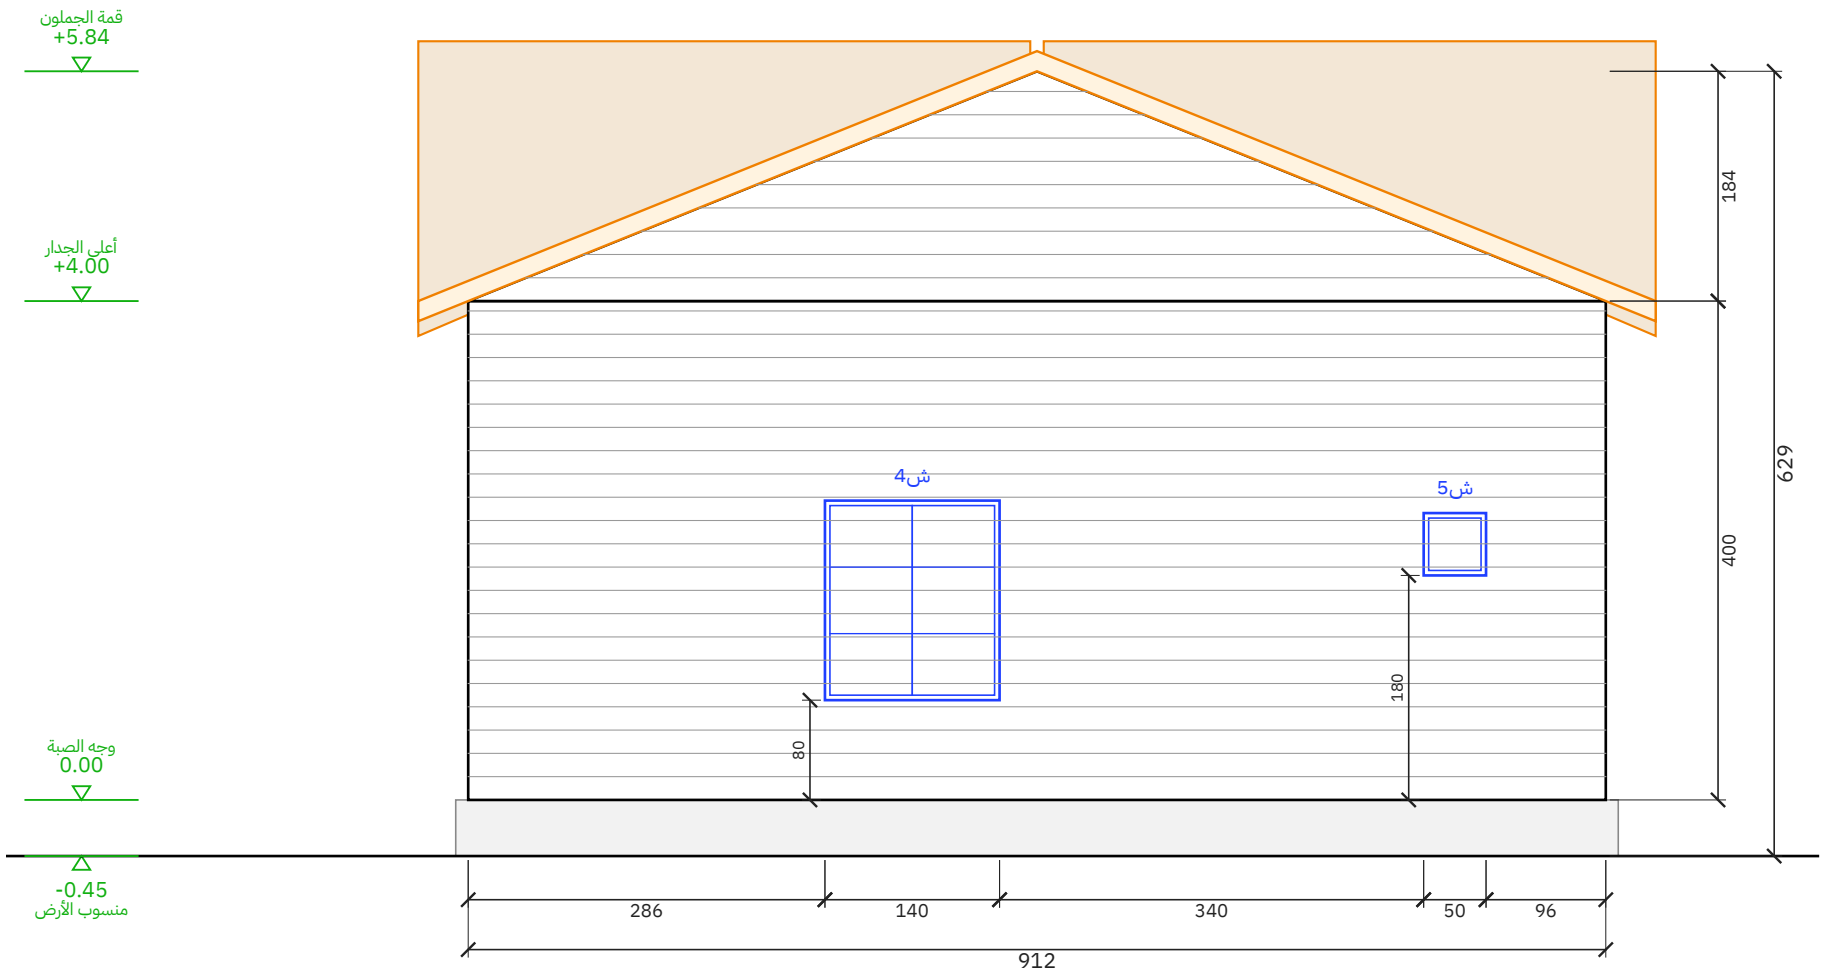

الواجهة الخلفية

مقياس 1:50 | الوحدة: سم

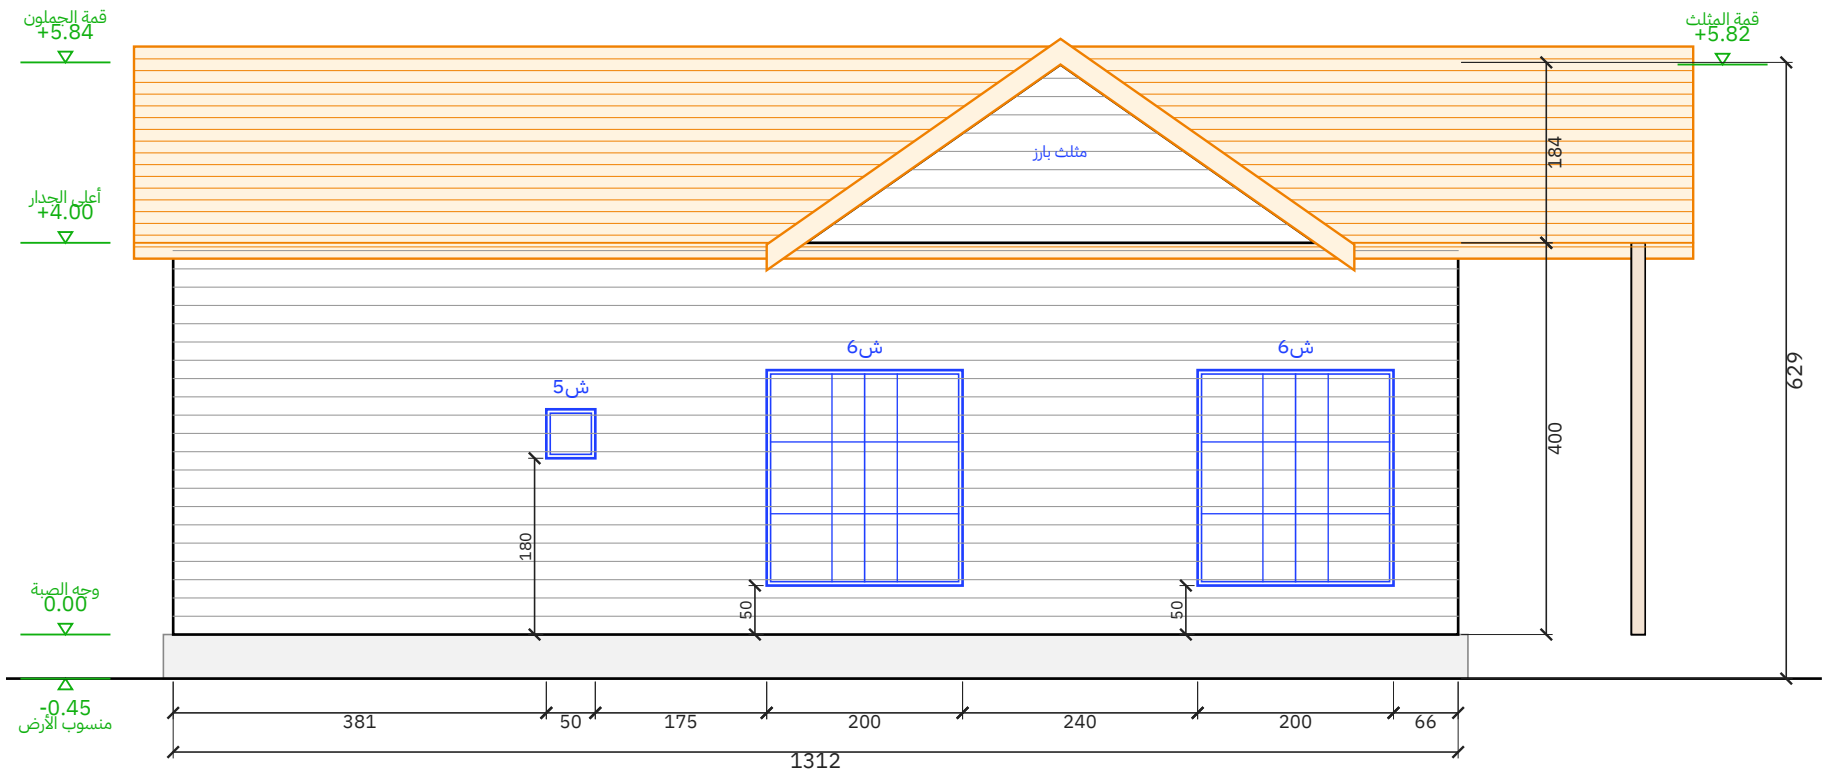


الواجهة الغربية

مقياس 1:50 | الوحدة: سم

مصنع وتد الأخشاب Watad Wood Factory	المشروع / العميل مجلس وجلسة خارجية مغلقة وغرفة نوم 9.00 × 13.00 م – الحوية عميل – الحوية	عنوان اللوحة الواجهة الخلفية والواجهة الغربية	المقياس 1:50	التاريخ 2026-11-05	رقم اللوحة W-04 (4/15)


مسقط السقف (جملون)

رفرف 40 سم من كل جهة | مقياس 1:50

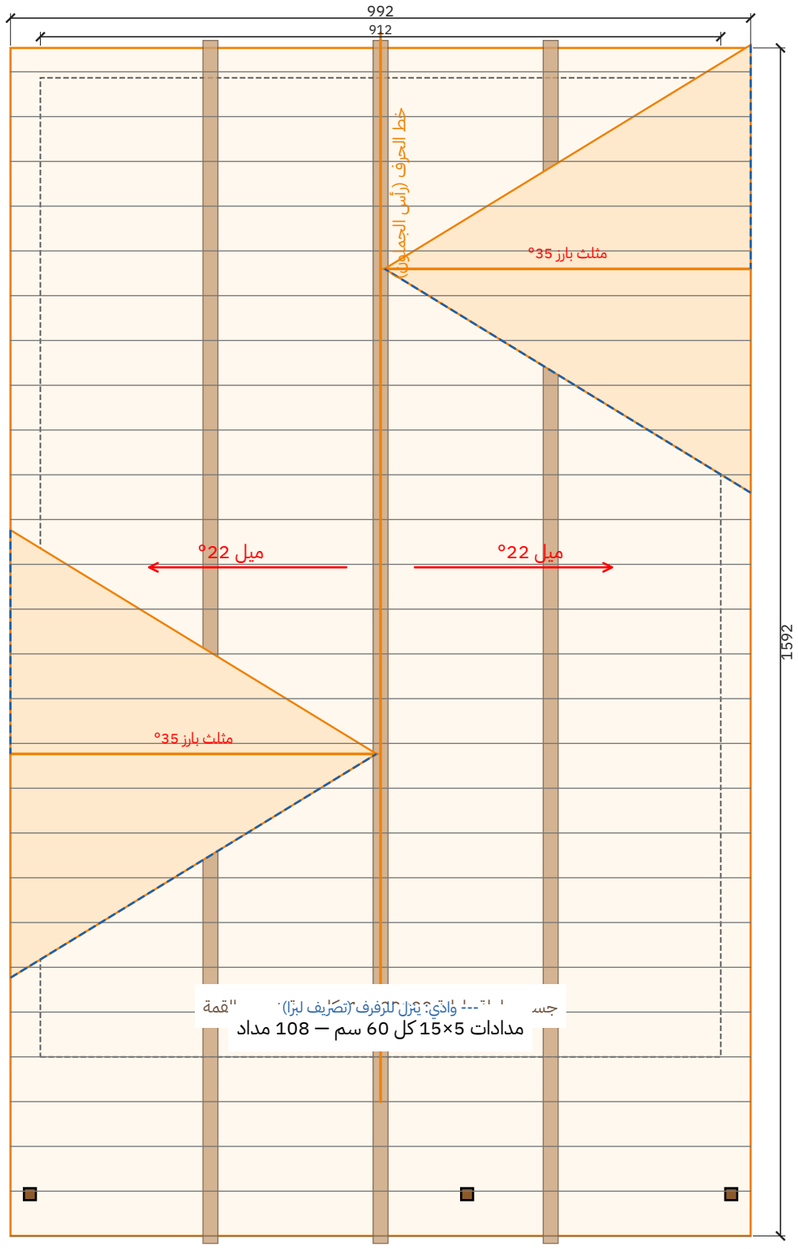


قطاع عرضي أ-أ

مقياس 1:50 | الوحدة: سم

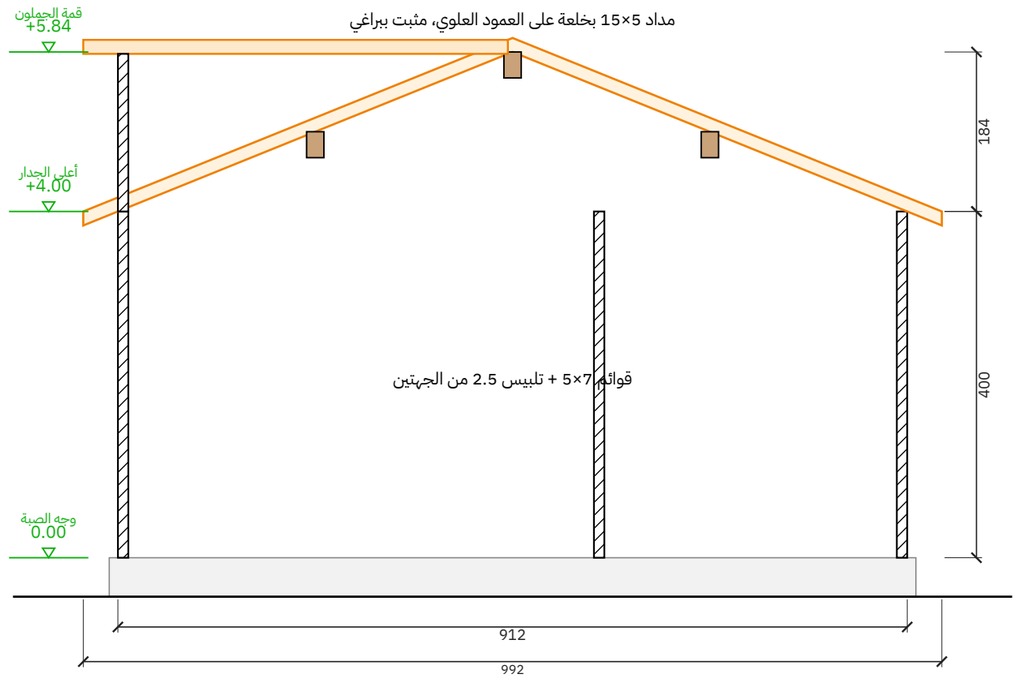

تفصيلة جلوس المداد على العلوي (1:5)

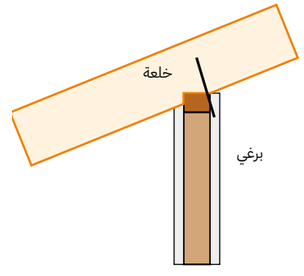

علوي 7×5 على قائم 7×5

المشروع / العميل	عنوان اللوحة	المقياس	التاريخ	رقم اللوحة
مجلس وجلسة خارجية مغلقة وغرفة نوم 9.00 × 13.00 م — الحوية **عميل — الحوية**	**مسقط السقف والقطاع**	**1:50**	**2026-11-05**	**W-05 (5/15)**

مصنع وتد الأخشاب
Watad Wood Factory

جدول مقاسات الأبواب والشبابيك

مقاس الفتحة الصافي في الجدار - الوحدة: سم

الرمز	النوع	العرض (سم)	الارتفاع (سم)	ارتفاع الجلسة (سم)	العدد	الموقع
ب1	باب مزدوج	166	260	-	1	الأمامية
ب2	باب	90	220	-	1	غرفة النوم
ب3	باب	90	220	-	1	المستودع
ب4	باب	100	230	-	1	المجلس
ب5	باب	80	210	-	1	المغاسل
ب6	باب	70	210	-	1	الحمام
ز1	باب مزدوج	170	260	-	1	الأمامية
ز2	باب مزدوج	170	260	-	1	الأمامية
ش1	شباك	140	150	90	1	الأمامية
ش2	شباك	60	50	190	1	الشرقية
ش3	شباك	100	160	80	2	الشرقية 2
ش4	شباك	140	160	80	1	الخلفية
ش5	شباك	50	50	180	2	الخلفية - الغربية
ش6	شباك	200	220	50	2	الغربية 2
ش7	شباك	120	150	90	1	المجلس على الجلسة

الإجمالي: أبواب 8 - شبابيك 10

جدول المساحات وبيانات المشروع


بيانات المشروع

البند	البيان
المشروع	مجلس وجلسة خارجية مغلقة وغرفة نوم 9.00 × 13.00 م — الحوية
العميل	عميل — الحوية
الموقع	الحوية
الاستخدام	مجلس ضيافة + جلسة مغلقة + غرفة نوم
التاريخ	2026-11-05
نظام البناء	هيكل خشب 7×5 + تلبيس 2.5 سم من الجهتين
السقف	جملون 22° — قرميد معدني + 2 مثلث بارز


جدول المساحات

م	الفراغ	الأبعاد (م)	المساحة (م2)
1	جلسة خارجية مغلقة	5.38 × 7.88	42.39
2	غرفة نوم	3.38 × 5.88	19.87
3	مستودع	3.38 × 1.88	6.35
4	مجلس	6.88 × 4.88	33.57
5	مغاسل	1.88 × 1.88	3.53
6	حمام	1.88 × 2.88	5.41
	المساحة الصافية الداخلية		**111.15**
	الشرفة الأمامية	**5.62 × 1.94**	**10.90**
	المساحة الإجمالية المبنية	**9.12 × 13.12**	**119.65**
	المساحة الكلية (المبنية + التراس)		**130.56**

تأطير جدار جنوب — الطول 900 سم، الارتفاع 400 سم

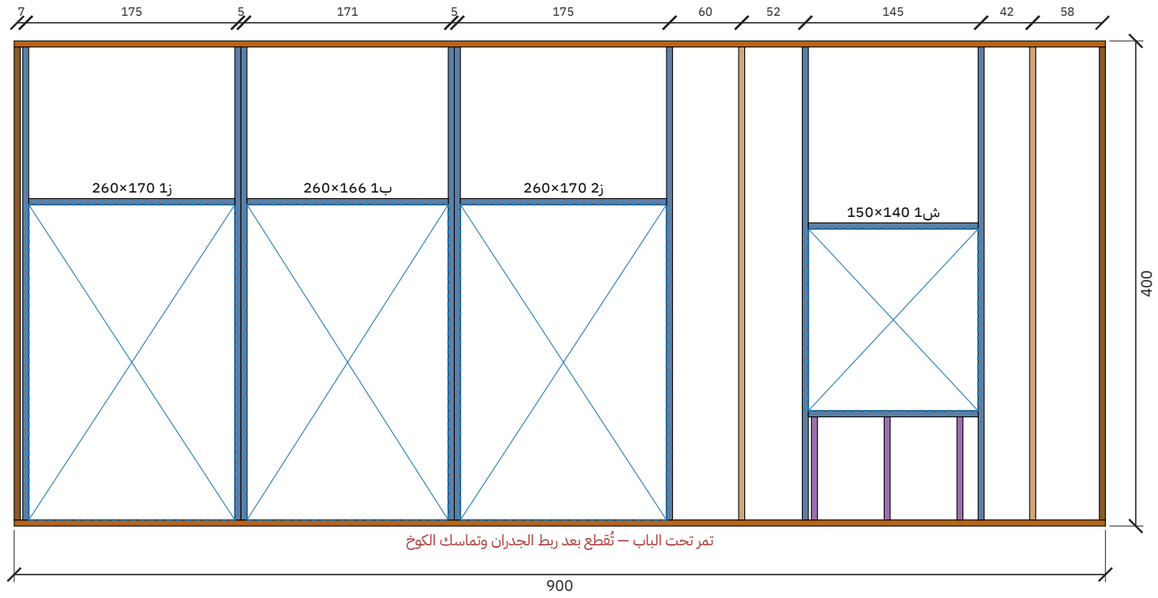

تأطير جدار شرق — الطول 1300 سم، الارتفاع 400 سم

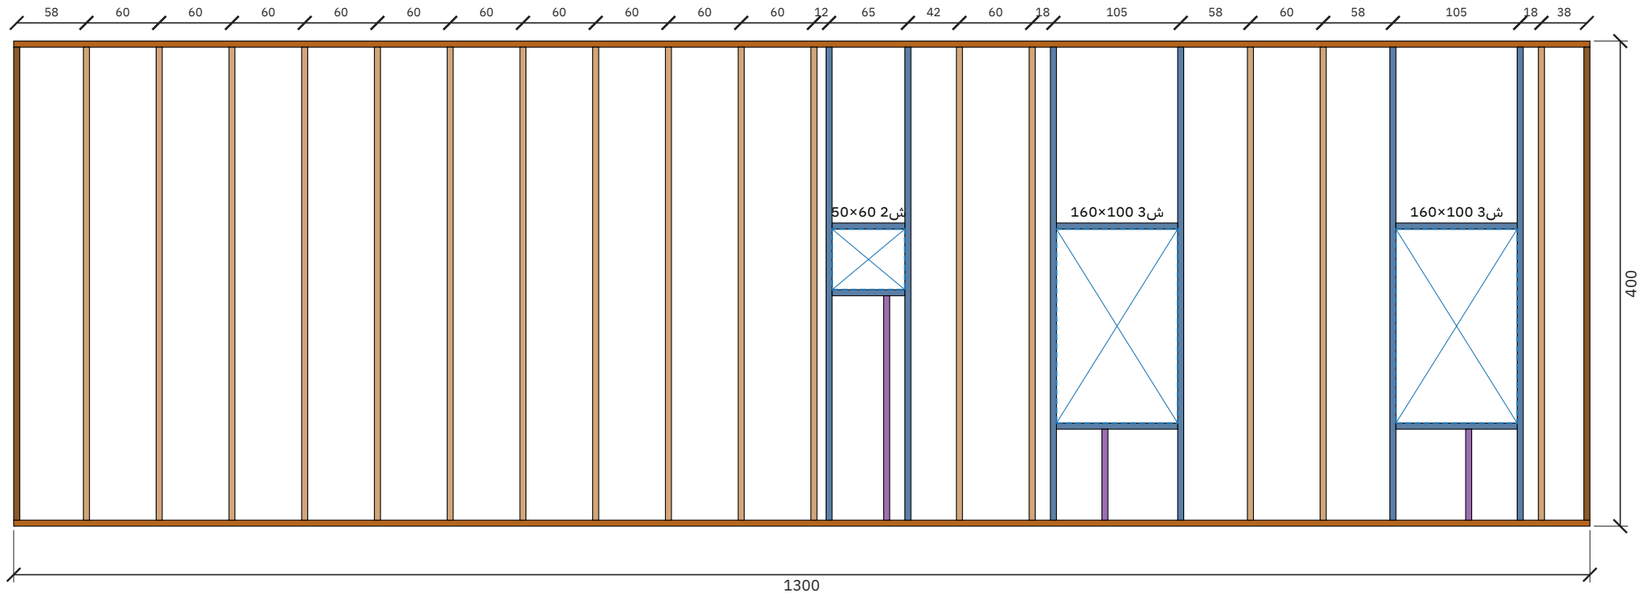


قاعدة سفلية | علوي | عمود | عمود زاوية | جنب فتحة | رأس فتحة | جلسة شباك | عمود قصير


المشروع / العميل	عنوان اللوحة	المقياس	التاريخ	رقم اللوحة
مجلس وجلسة خارجية مغلقة وغرفة نوم 9.00 × 13.00 م – الحوية **عميل – الحوية**	**لوحات التأطير (للورشة)**	**–**	**2026-11-05**	**W-08 (8/15)**

مصنع وتد الأخشاب
Watad Wood Factory

تأطير جدار شمال — الطول 900 سم، الارتفاع 400 سم

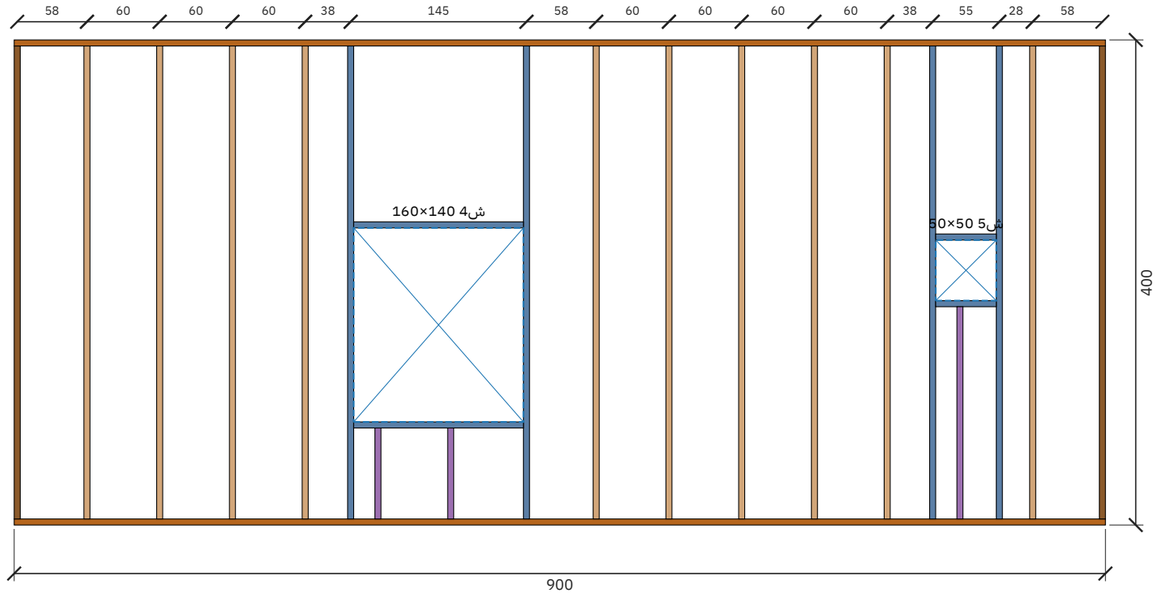

تأطير جدار غرب — الطول 1300 سم، الارتفاع 400 سم

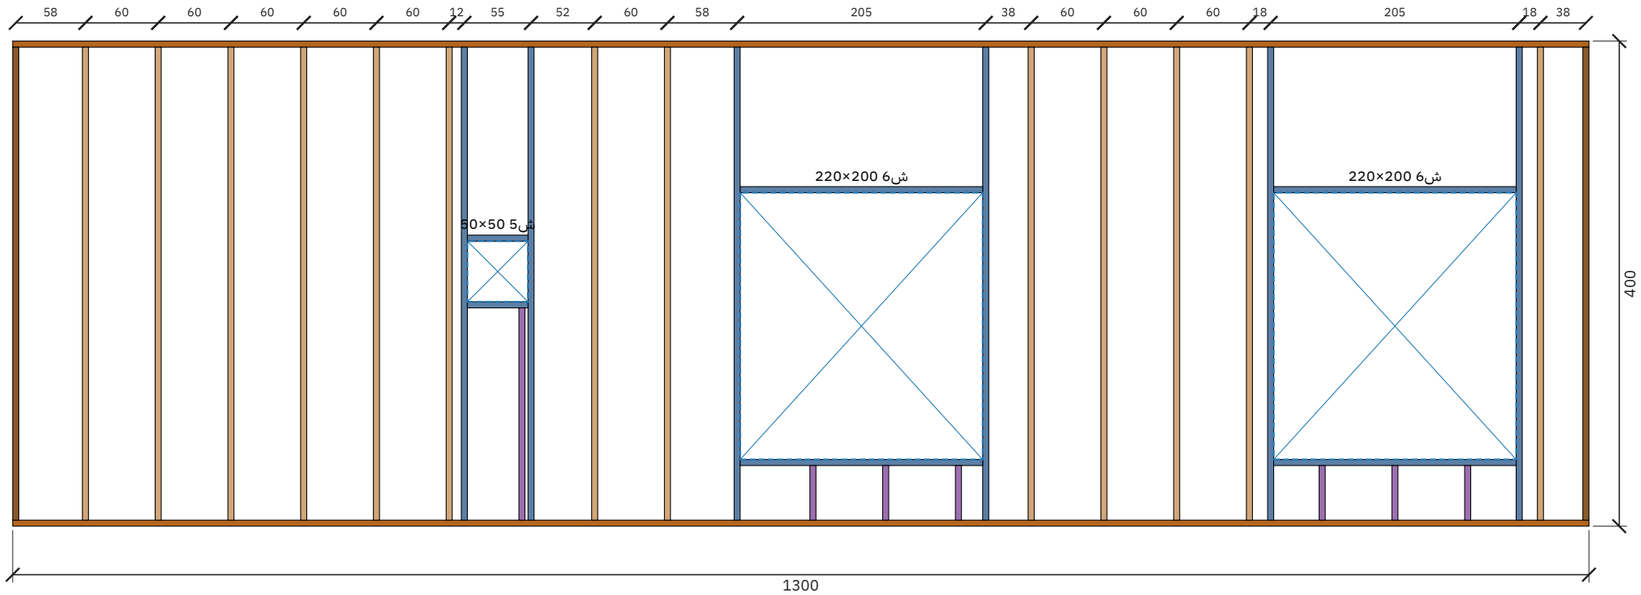


قاعدة سفلية | علوي | عمود | عمود زاوية | جنب فتحة | رأس فتحة | جلسة شباك | عمود قصير


المشروع / العميل	عنوان اللوحة	المقياس	التاريخ	رقم اللوحة
مجلس وجلسة خارجية مغلقة وغرفة نوم 9.00 × 13.00 م — الحوية **عميل — الحوية**	**لوحات التأطير (للورشة)**	—	**2026-11-05**	**W-09 (9/15)**

مصنع وتد الأخشاب
Watad Wood Factory

تأطير جدار جدار الجلسة — الغرفة والمستودع — الطول 800 سم، الارتفاع 400 سم (داخلي)

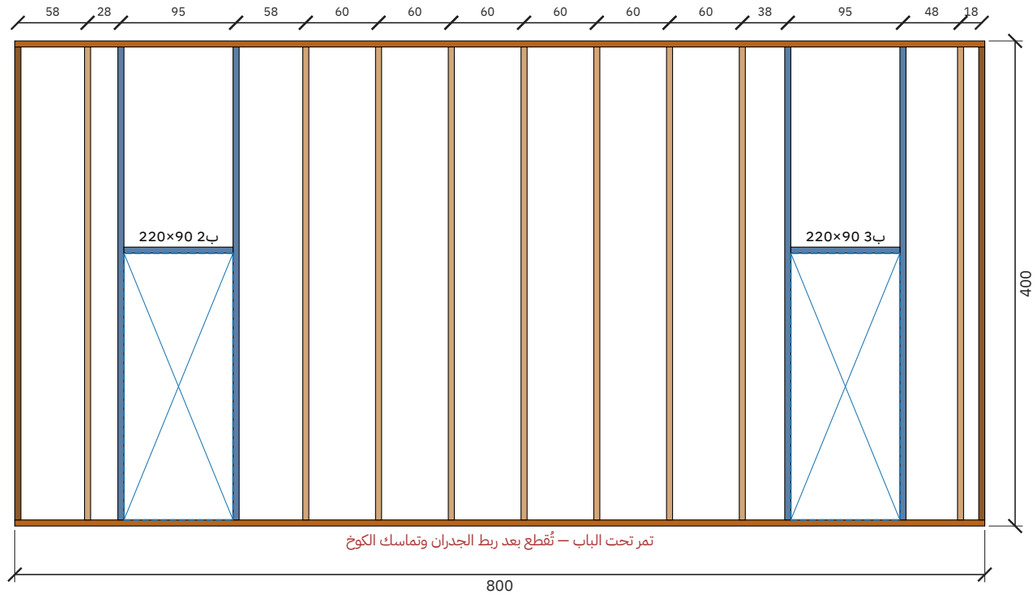


تأطير جدار جدار الغرفة — المستودع — الطول 350 سم، الارتفاع 400 سم (داخلي)

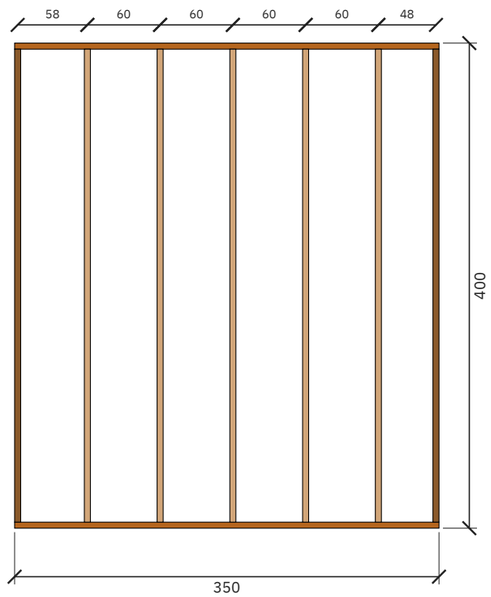


عمود قصير
جلسة شباك
رأس فتحة
جنب فتحة
عمود زاوية
عمود
علوي
قاعدة سفلية

مصنع وتد الأخشاب Watad Wood Factory	المشروع / العميل **مجلس وجلسة خارجية مغلقة وغرفة نوم 9.00 × 13.00 م — الحوية** **عميل — الحوية**	عنوان اللوحة **لوحات التأطير (للورشة)**	المقياس **—**	التاريخ **2026-11-05**	رقم اللوحة **W-10 (10/15)**

تأطير جدار جدار الجلسة — المجلس — الطول 900 سم، الارتفاع 400 سم (داخلي)

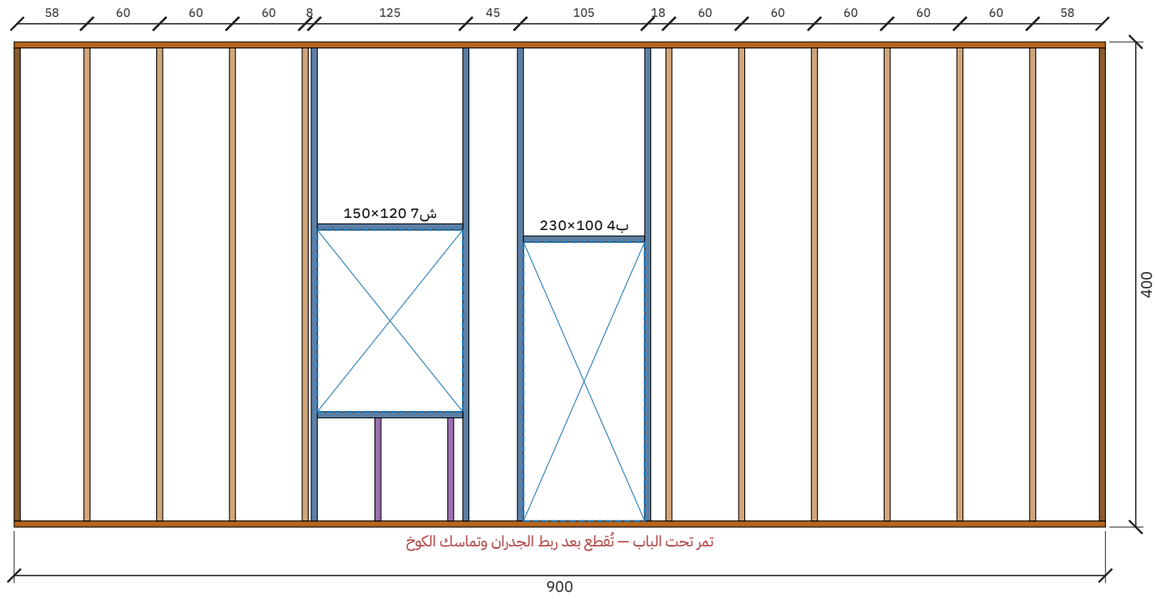


تأطير جدار جدار المجلس — المغاسل — الطول 500 سم، الارتفاع 400 سم (داخلي)

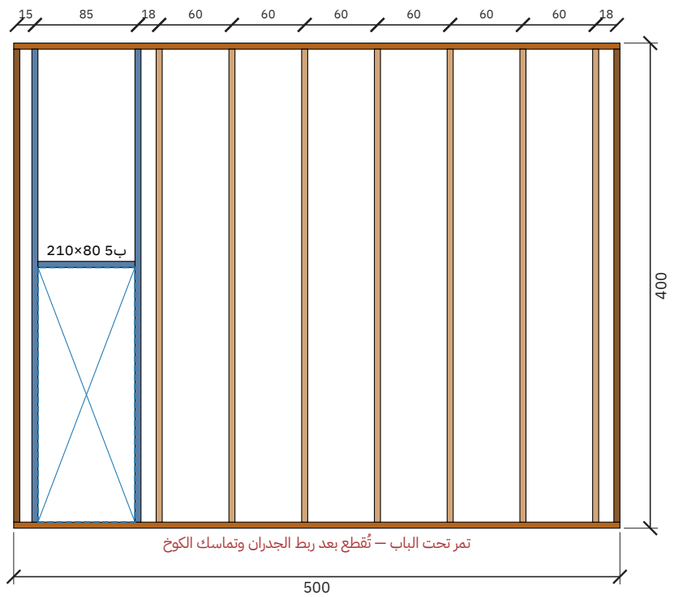

قاعدة سفلية | علوي | عمود | عمود زاوية | جنب فتحة | رأس فتحة | جلسة شباك | عمود قصير

مصنع وتد الأخشاب Watad Wood Factory	المشروع / العميل **مجلس وجلسة خارجية مغلقة وغرفة نوم 9.00 × 13.00 م — الحوية** **عميل — الحوية**	عنوان اللوحة **لوحات التأطير (للورشة)**	المقياس **—**	التاريخ **2026-11-05**	رقم اللوحة **W-11 (11/15)**

تأطير جدار جدار المغاسل — الحمام — الطول 200 سم، الارتفاع 400 سم (داخلي)

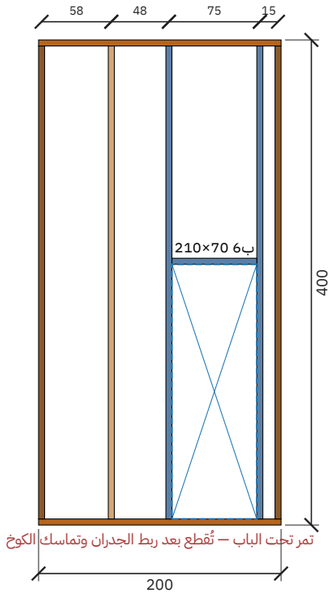

عمود قصير
جلسة شباك
رأس فتحة
جنب فتحة
عمود زاوية
عمود
علوي
قاعدة سفلية

مصنع وتد الأخشاب Watad Wood Factory	المشروع / العميل مجلس وجلسة خارجية مغلقة وغرفة نوم 9.00 × 13.00 م — الحوية عميل — الحوية	عنوان اللوحة لوحات التأطير (للورشة)	المقياس —	التاريخ 2026-11-05	رقم اللوحة W-12 (12/15)

جدول الكميات وخطة تقطيع الطبليات

البند	القيمة
الارتفاع المطلوب / المعتمد	400 / 400 سم
السقف	جملون 22° — أعلى نقطة 584 سم من وجه الصبة
المدادات 5×15	108 مداد (27 خط × قطعتين موصولة فوق الجسر الحامل بتراكب 60 سم) × حتى 321 سم — من طبلية 480
طبليات الطريقة الأولى (مداد + عمود)	108 طبلية × 480 سم
طبليات الطريقة الثانية (3 أعمدة)	6 طبلية × 320 سم
طبليات الطريقة الثانية (طويلة)	17 طبلية × 480 سم
مدادات المثلث البارز (الغربي) 35°	18 مداد حتى 366 سم (طبلية 480) + 2 مداد وادي 612 سم — وصلة
مدادات المثلث البارز (الشرقي) 35°	18 مداد حتى 366 سم (طبلية 480) + 2 مداد وادي 612 سم — وصلة
إجمالي الطبليات 5×22.5	171
إجمالي قطع 5×7	191
قائمة تقطيع 5×7	1300سم×4 | 900سم×6 | 800سم×2 | 500سم×2 | 390سم×127 | 350سم×2 | 200سم×6 | 185سم×1 | 175سم×2
	170سم×2 | 166سم×1 | 140سم×4 | 120سم×2 | 100سم×5 | 90سم×2 | 85سم×5 | 80سم×1 | 75سم×4
ألواح تلبيس 2.5 سم	684 لوح × 400 سم (مجموع الصفوف 2309.3 م، 18 وجه)
أسمنت بورد 12 مم (122×244)	36 لوح (داخل دورات المياه)

جدول الكميات وخطة تقطيع الطبليات

البند	القيمة
العزل	340 لوح فوم صخري 80
الصبة	يجهزها العميل — 20 سم، مفرغة تحت دورات المياه

مراجعة التصميم مقابل قواعد المصنع

النوع	البند	التفاصيل	المقترح
ملاحظة	بحر المدادات	أطول بحر بدون جدار داخلي يحمل المداد: جهة أ: 456 سم، جهة ب: 456 سم. يحتاج رقم المصنع لأقصى بحر مسموح لتحديد المدادات اللي تُقوّى 20×5.	
ملاحظة	الصبة والدرج	ارتفاع الصبة 45 سم ← 3 درجة بقائمة 15.0 سم.	
ملاحظة	مناسيب رؤوس الفتحات	رؤوس الأبواب والشبابيك على مناسيب مختلفة: 210، 220، 230، 240، 260، 270 سم.	
تنبيه	مداد الوادي	مداد الوادي 612 سم أطول من الطبلية — يُوصل بوصلة مثبتة فوق جدار/دعامة	وصلة مزدوجة 5×15 مع براغي، ومرتكزة على جدار أو دعامة 5×7.
سؤال	يحتاج تأكيد	أقصى بحر للمداد بدون جدار داخلي قبل إضافة تقوية 5×7 (مداد 20×5)؟	
سؤال	يحتاج تأكيد	التغطية الصافية للوح التلبيس بعد التعشيق (مستنتجة مؤقتاً 18.67 سم من 280/15)؟	
سؤال	يحتاج تأكيد	هل يوضع أعمدة قصيرة فوق رأس الشباك/الباب إلى العلوي؟	
سؤال	يحتاج تأكيد	مكان الوصلة في القاعدة والعلوي إذا الجدار أطول من الطبلية؟	