
جدول مساحات الموقع

البند	المقاس	المساحة (م²)
مساحة الأرض	19.00 × 27.00 م	513.0
مسطح الكوخ (البصمة)	9.00 × 10.00 م	90.0
تراس الكوخ	1.50 × 5.58 م	8.4
جلسة خارجية	3.20 × 7.60 م	24.3
بلاط		47.1
موقف سيارة	4.70 × 11.40 م	53.6
ممر	1.10 × 11.34 م	12.5
المسطحات الخضراء (حديقة)	الباقي	277.1

الموقع العام وتنسيق الحديقة (لاندسكيب)

الأرض 19 × 27 م = 513 م² | الأبعاد بالسنتيمتر

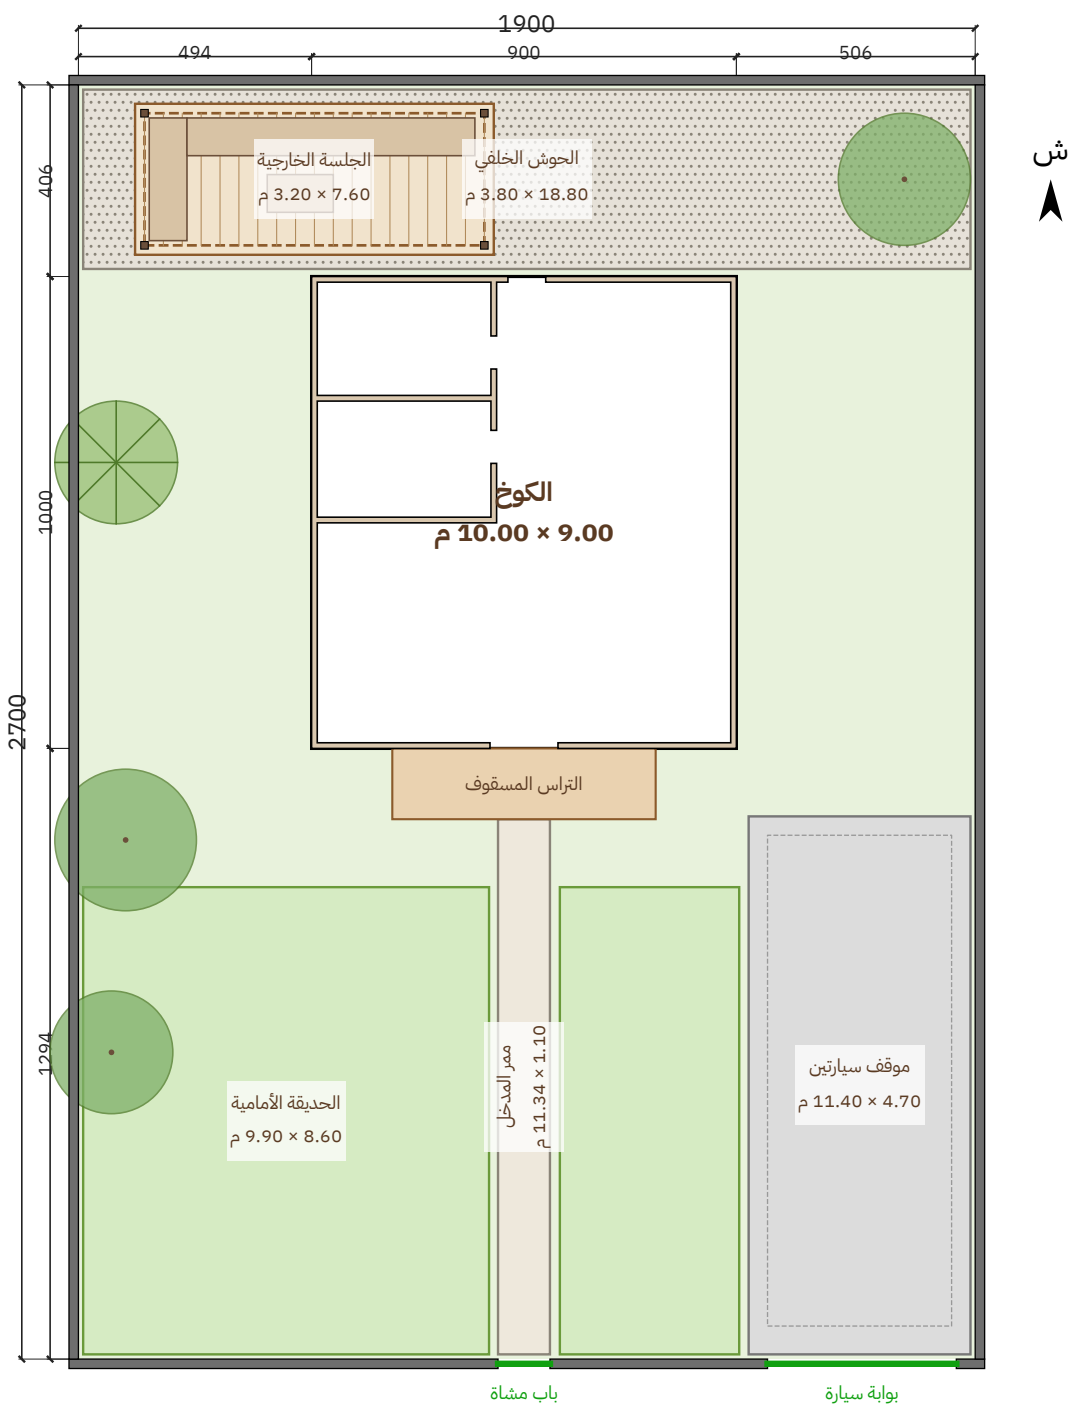


شارع عرض 16 م

المشروع / العميل	عنوان اللوحة	المقياس	التاريخ	رقم اللوحة
كوخ A-frame دورين — صالة ومطبخ أمريكي وحمامين + غرفتين وحمام — 9.00 × 10.00 م عميل — A-frame دورين	الموقع العام واللاندسكيب	1:200	2026-10-24	A-01 (1/11)

مصنع وتد الأخشاب
Watad Wood Factory

المسقط الأفقي مع الفرش


الأبعاد بالسنتيمتر - الجدران: قوائم 7×5 + تلبيس 2.5 من الجهتين (12 سم)

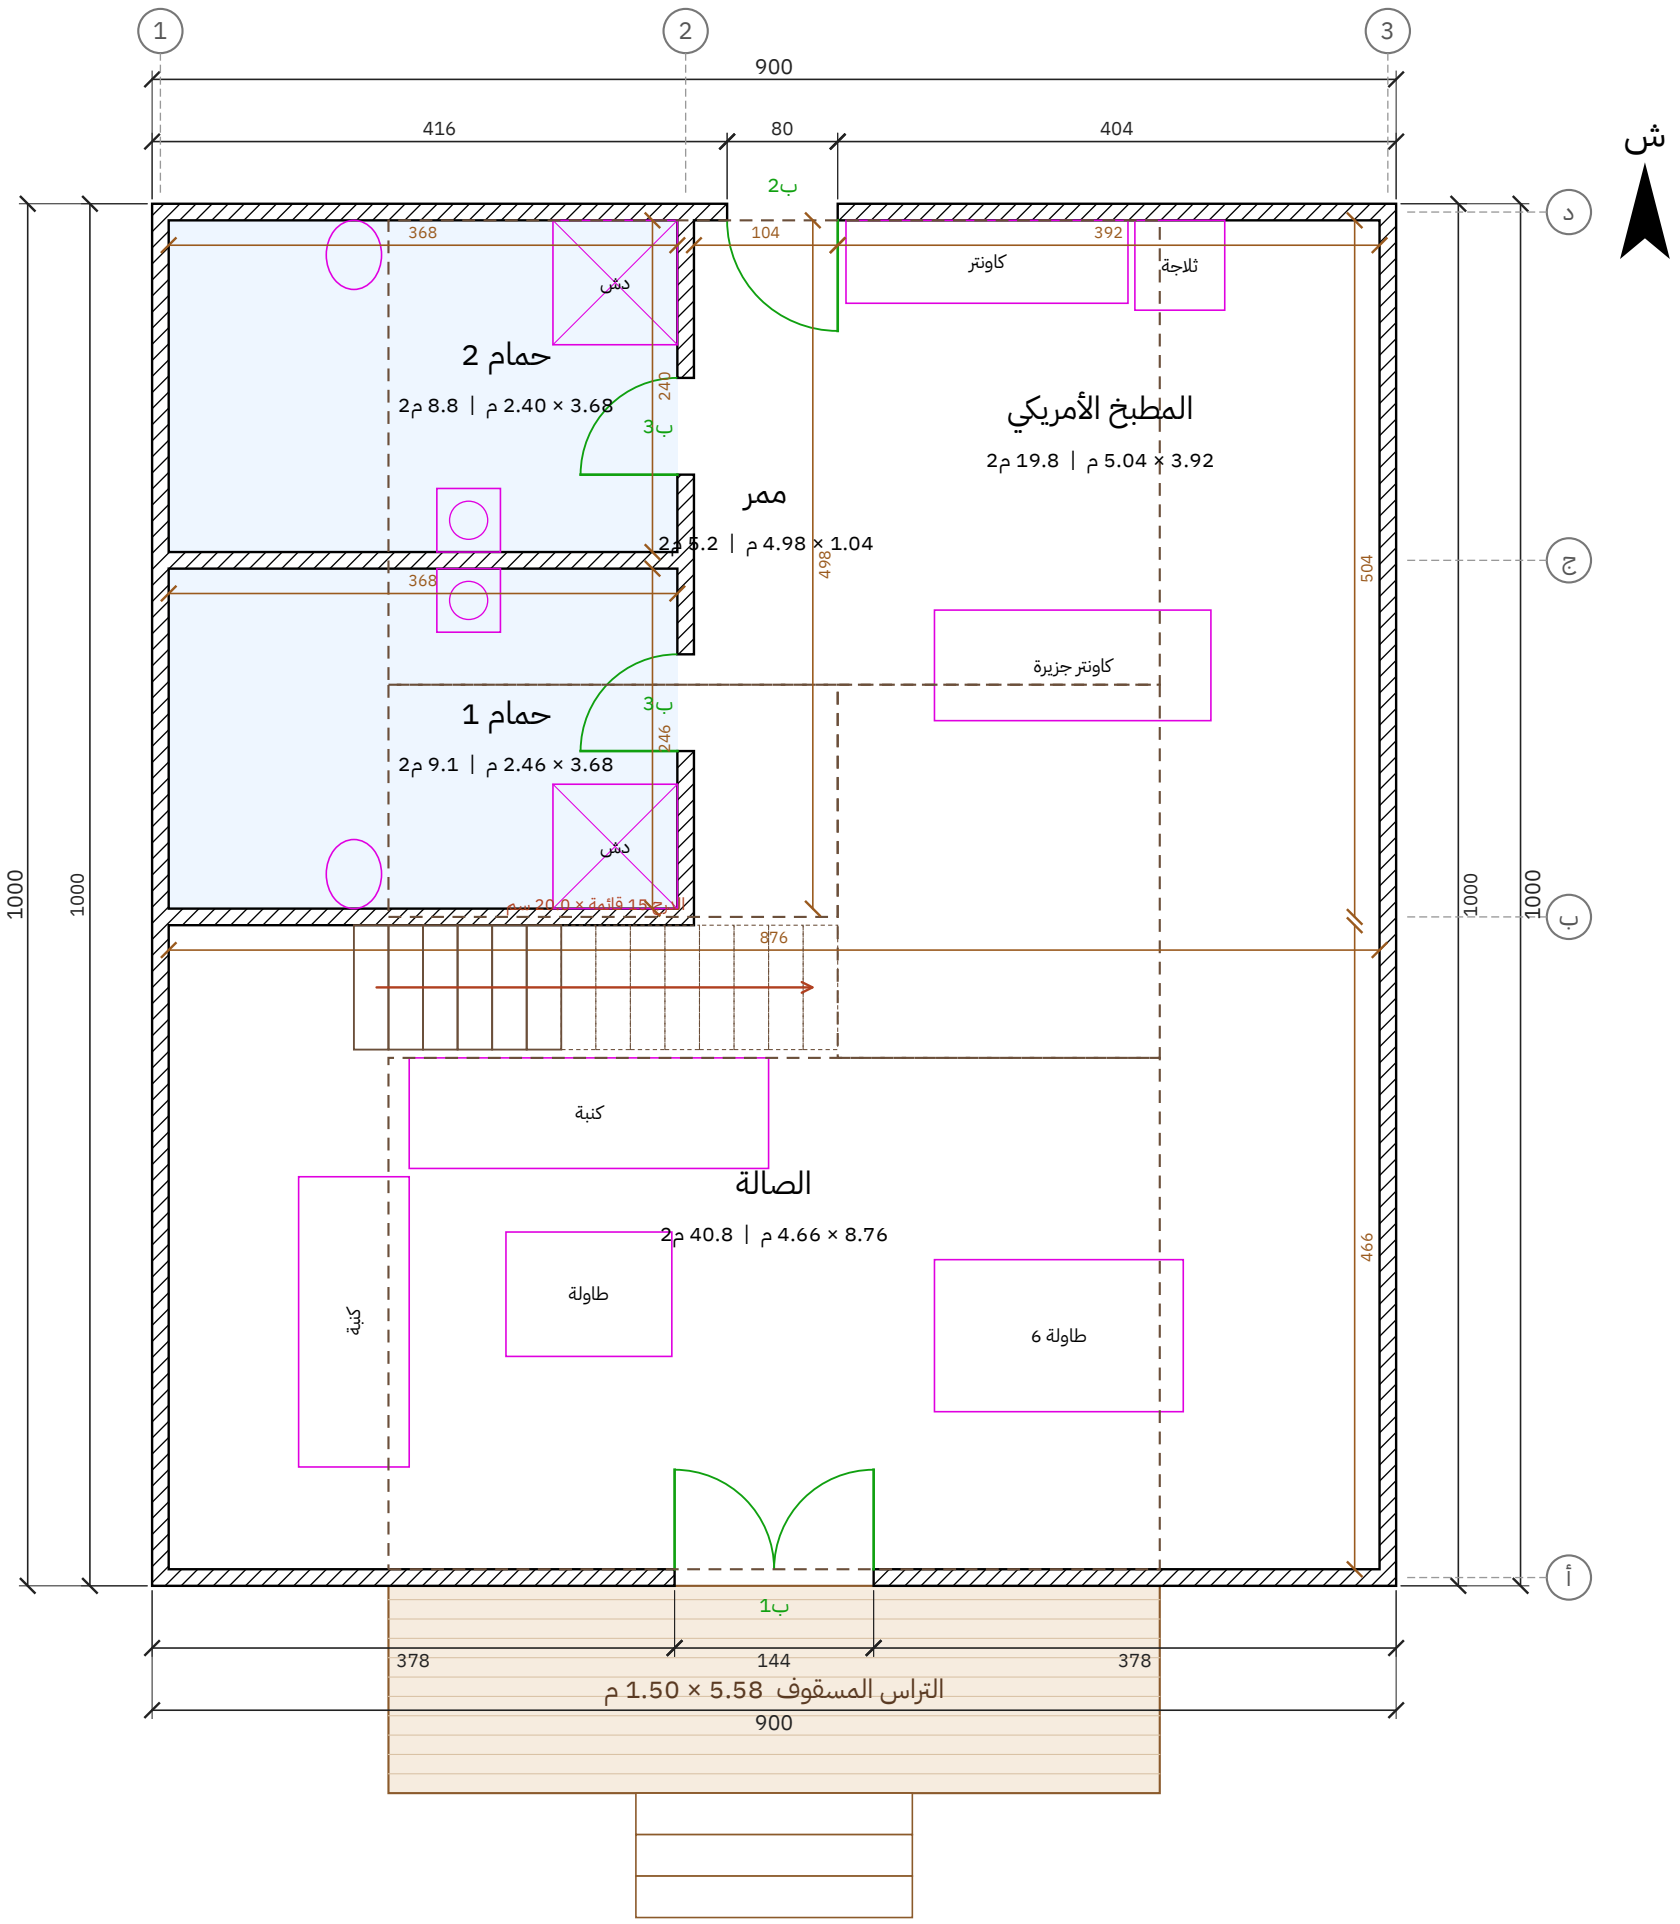

مصنع وتد الأخشاب Watad Wood Factory	المشروع / العميل كوخ A-frame دورين — صالة ومطبخ أمريكي وحمامين + غرفتين وحمام — 9.00 × 10.00 م عميل — A-frame دورين	عنوان اللوحة المسقط الأفقي	المقياس 1:50	التاريخ 2026-10-24	رقم اللوحة A-02 (2/11)


المسقط الأفقي مع الفرش — الدور الأول (داخل المثلث)

منسوب الأرضية +3.00 | الأبعاد بالسنتيمتر | الوقفة الكاملة ≥ 2.10 م بين الخطين المتقطعين

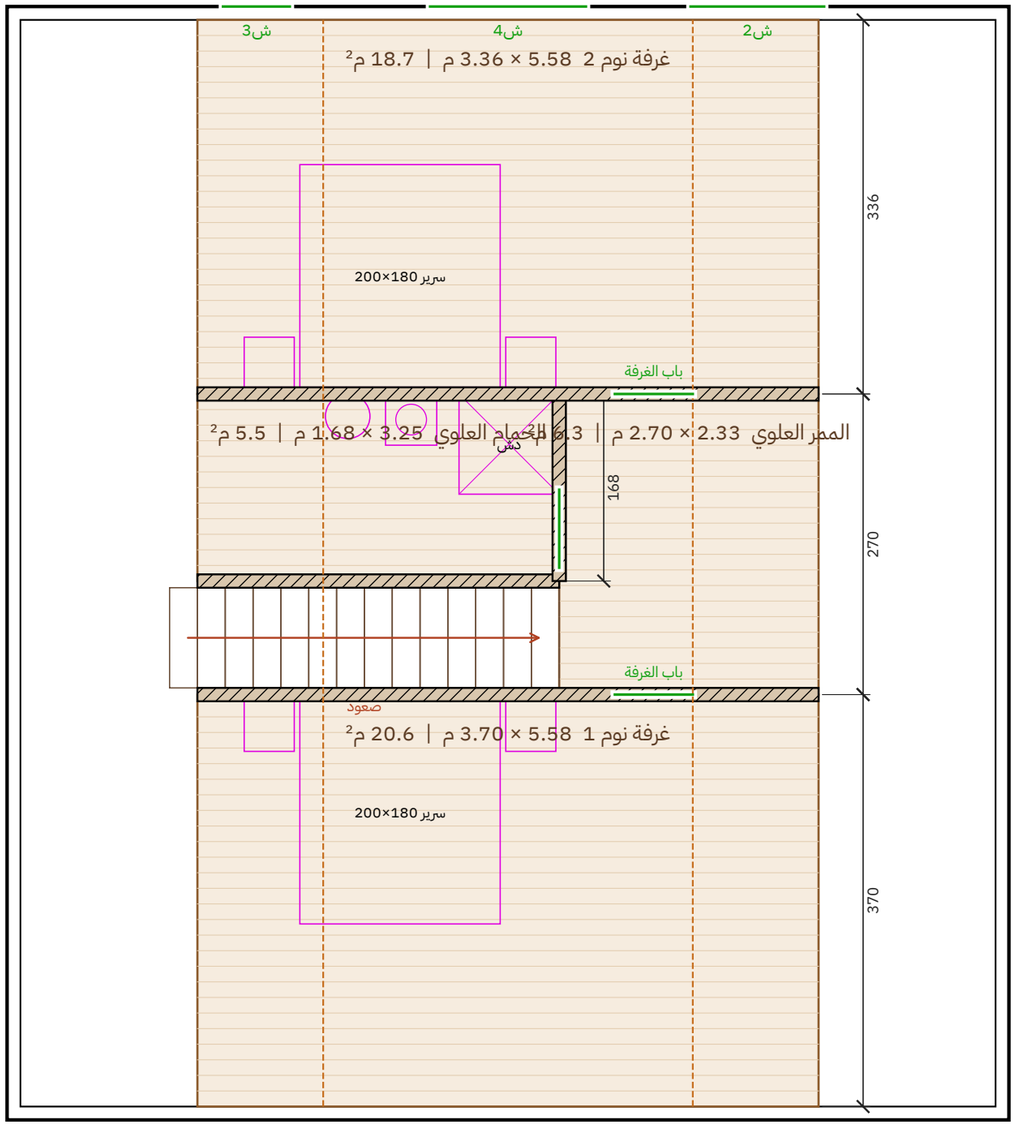

المشروع / العميل	عنوان اللوحة	المقياس	التاريخ	رقم اللوحة
كوخ A-frame دورين — صالة ومطبخ أمريكي وحمامين + غرفتين وحمام — 9.00 × 10.00 م عميل — A-frame دورين	المسقط الأفقي مع الفرش — الدور الأول (داخل المثلث)	1:50	2026-10-24	A-03 (3/11)

مصنع وتد الأخشاب
Watad Wood Factory

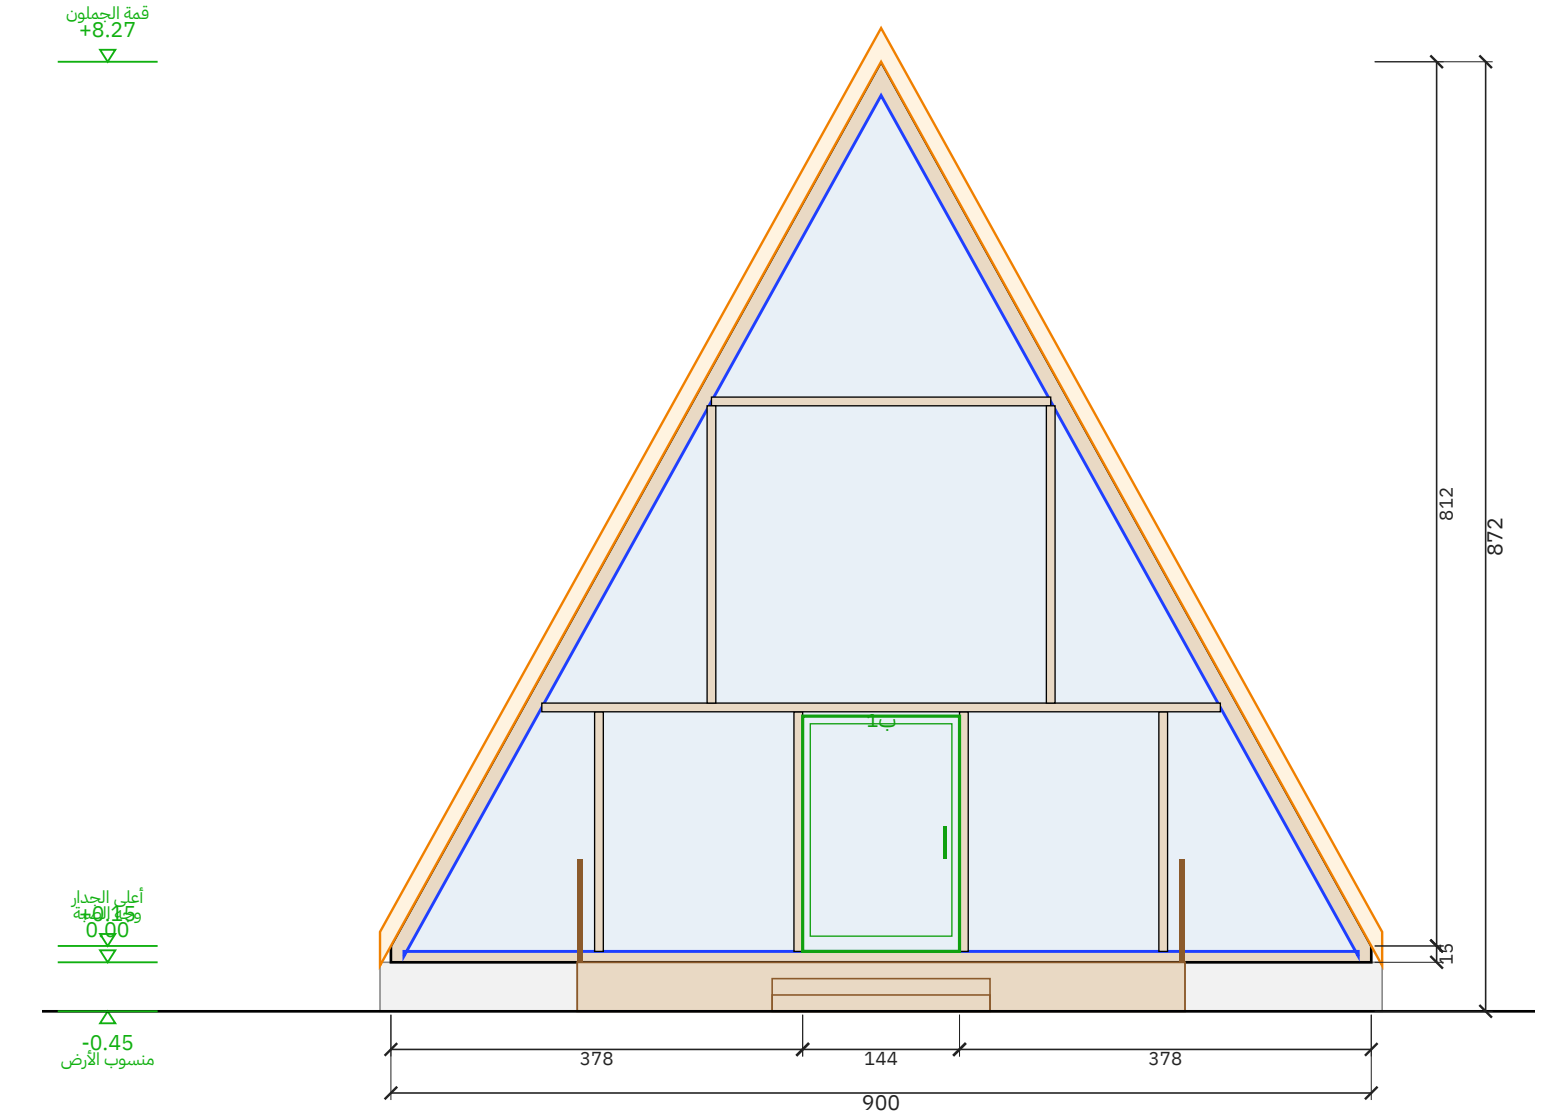

الواجهة الأمامية (مثلث زجاج كامل)

مقياس 1:50 | الوحدة: سم




الواجهة الشرقية (السقف لين الأرض)

مقياس 1:50 | الوحدة: سم


المشروع / العميل	عنوان اللوحة	المقياس	التاريخ	رقم اللوحة
نوع A-frame دورين — صالة ومطبخ أمريكي وحمامين + غرفتين وحمام — 9.00 × 10.00 م عميل — A-frame دورين	الواجهة الأمامية (مثلث زجاج كامل) والواجهة الشرقية (السقف لين الأرض)	1:50	2026-10-24	A-04 (4/11)

مصنع وتد الأخشاب
Watad Wood Factory

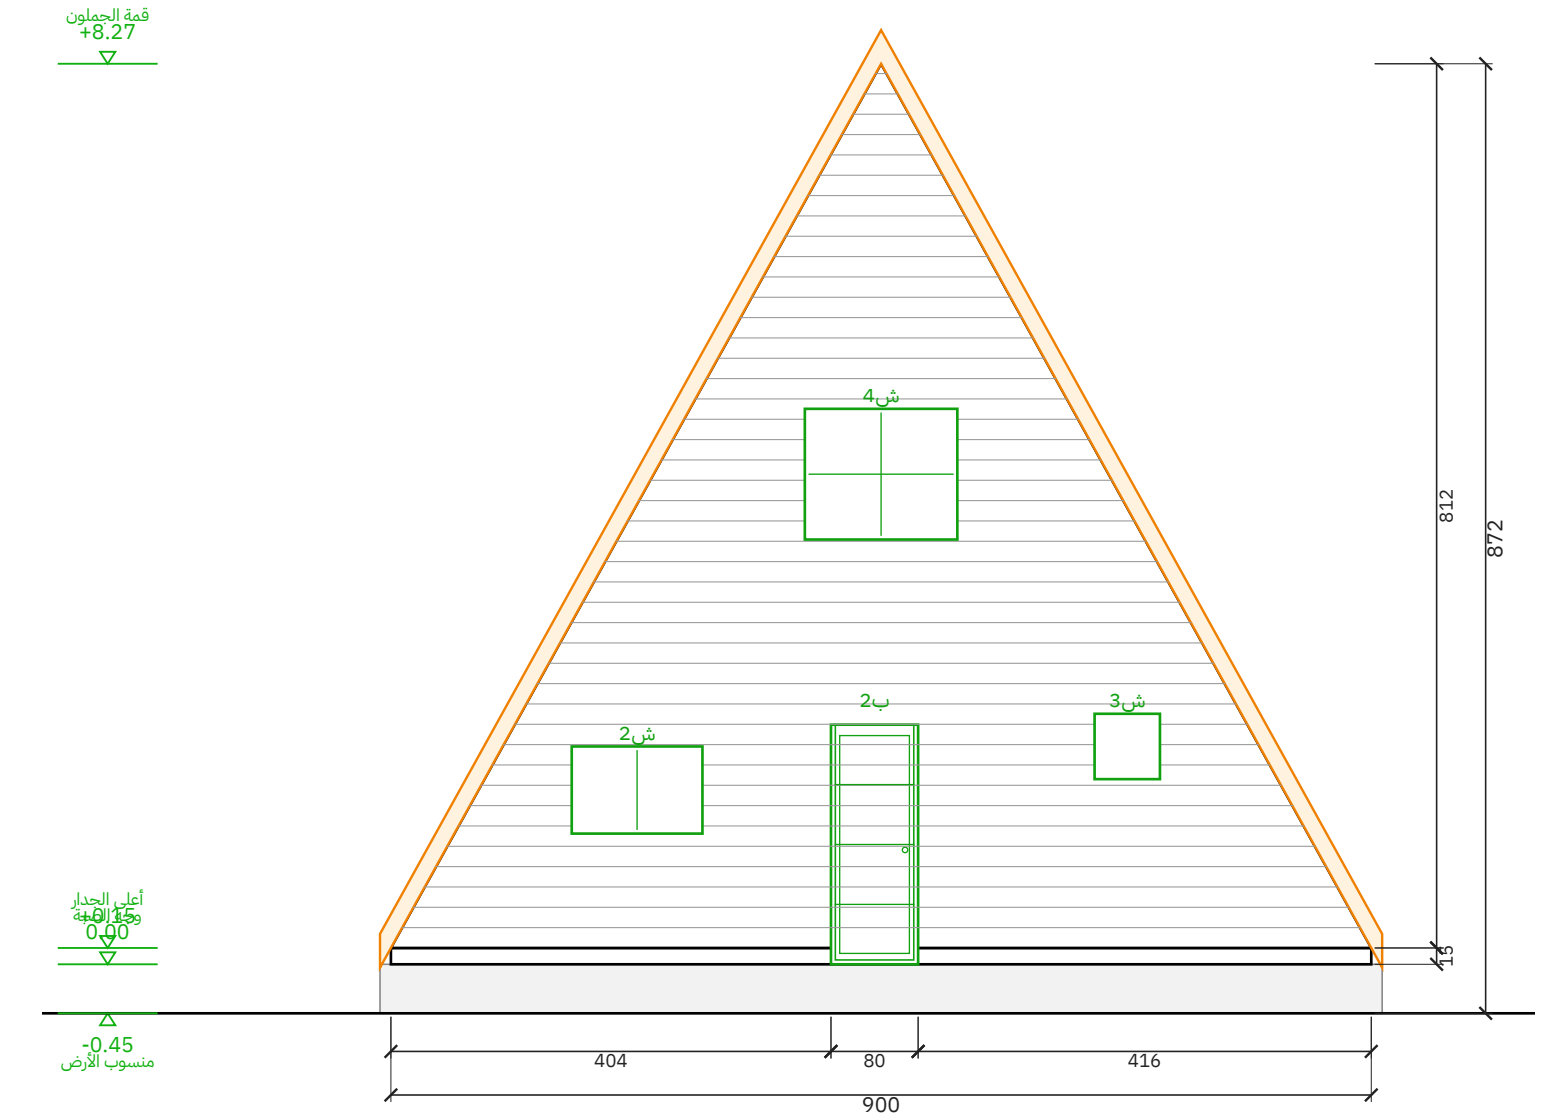

الواجهة الخلفية

مقياس 1:50 | الوحدة: سم

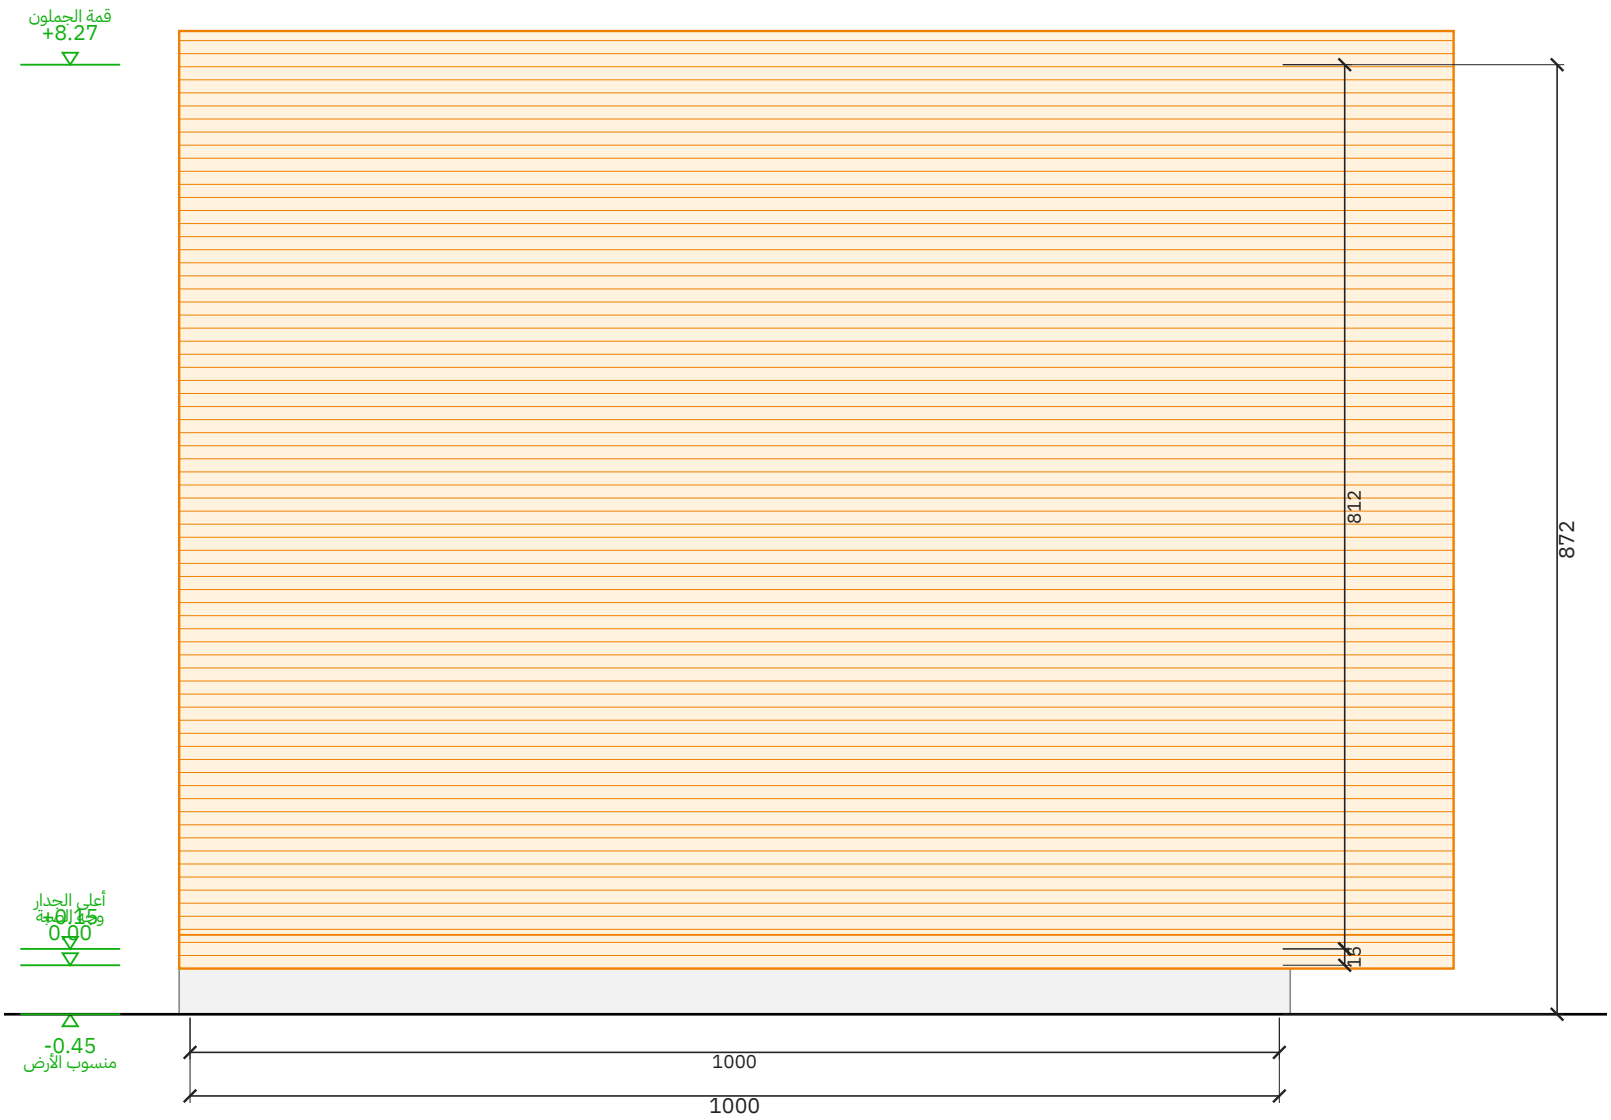

الواجهة الغربية (السقف لين الأرض)


مقياس 1:50 | الوحدة: سم

المشروع / العميل	عنوان اللوحة	المقياس	التاريخ	رقم اللوحة
نوع A-frame دورين — صالة ومطبخ أمريكي وحمامين + غرفتين وحمام — 9.00 × 10.00 م عميل — A-frame دورين	الواجهة الخلفية والواجهة الغربية (السقف لين الأرض)	1:50	2026-10-24	A-05 (5/11)

مصنع وتد الأخشاب
Watad Wood Factory


مسقط السقف (جملون)

رفرف 10 سم من كل جهة | مقياس 1:50

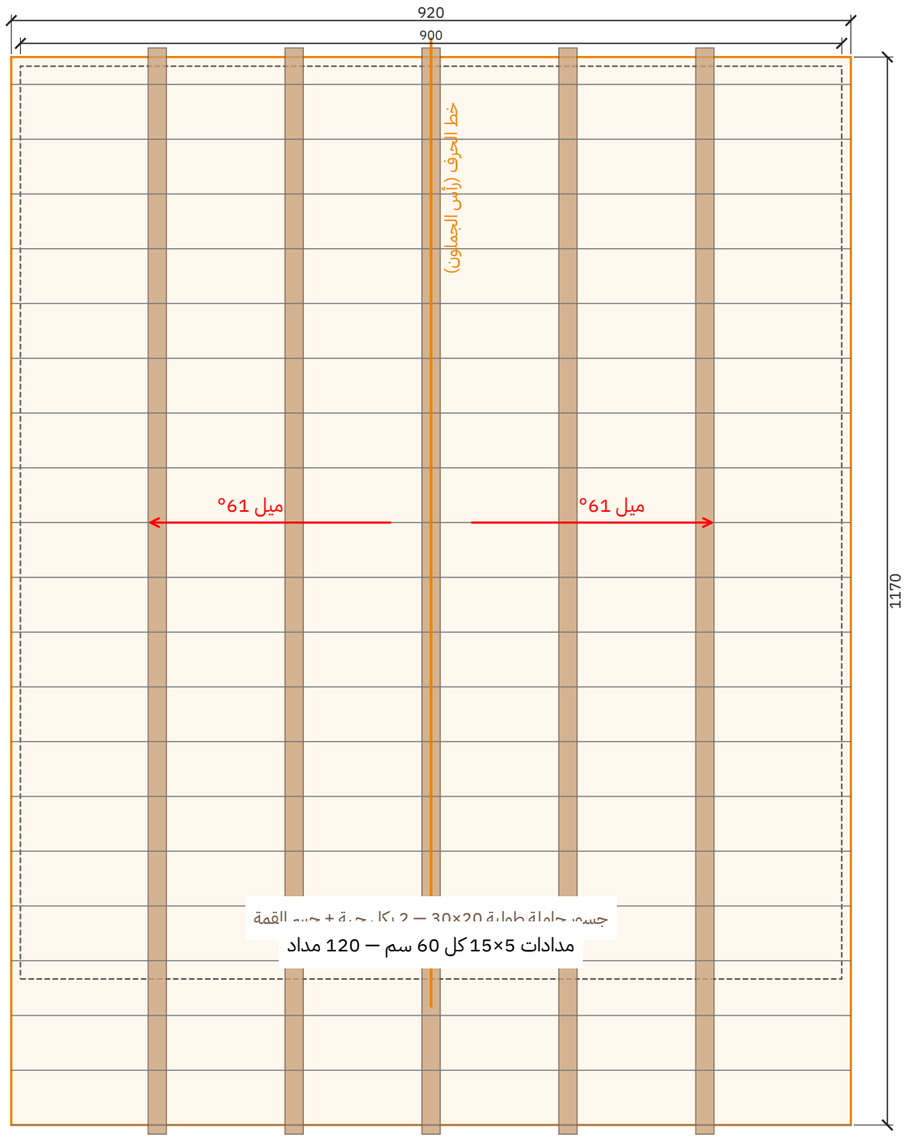


قطاع عرضي أ-أ

مقياس 1:50 | الوحدة: سم

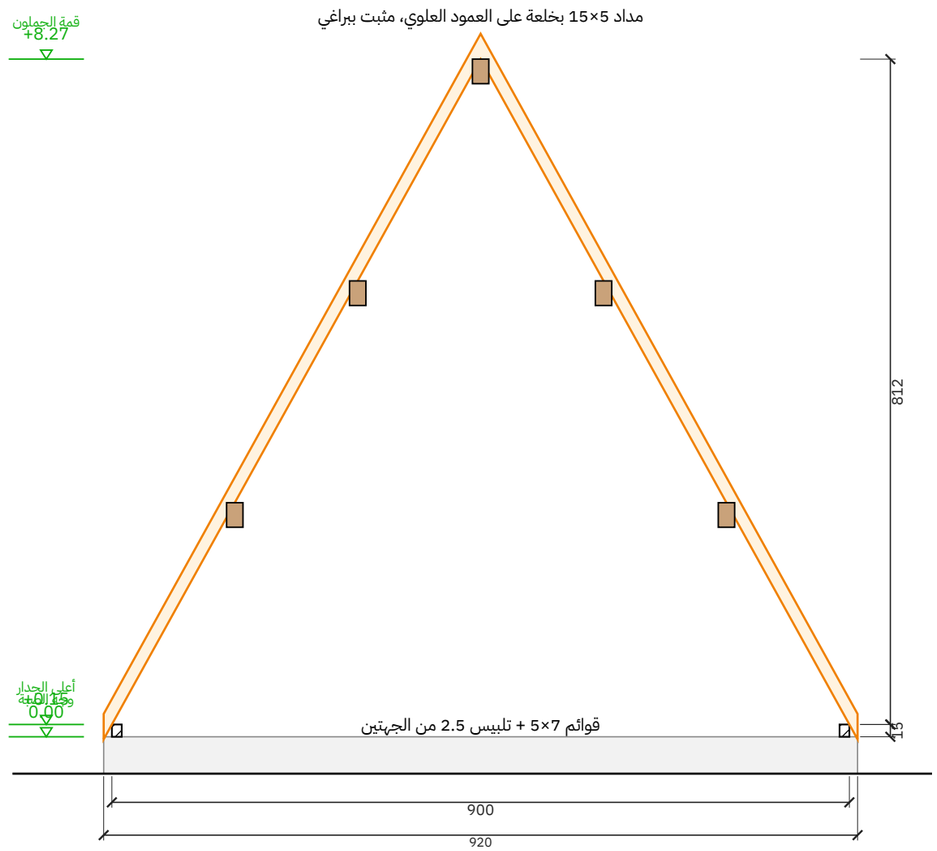

تفصيلة جلوس المداد على العلوي (1:5)

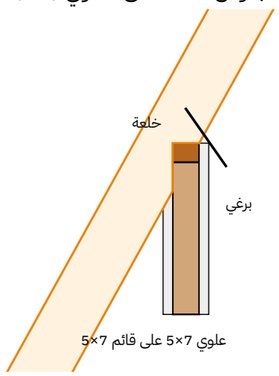

المشروع / العميل	عنوان اللوحة	المقياس	التاريخ	رقم اللوحة
كوخ A-frame دورين — صالة ومطبخ أمريكي وحمامين + غرفتين وحمام — 9.00 × 10.00 م **عميل — A-frame دورين**	**مسقط السقف والقطاع**	**1:50**	**2026-10-24**	**A-06 (6/11)**

مصنع وتد الأخشاب
Watad Wood Factory

جدول مقاسات الأبواب والشبابيك

مقاس الفتحة الصافي في الجدار - الوحدة: سم

الرمز	النوع	العرض (سم)	الارتفاع (سم)	ارتفاع الجلسة (سم)	العدد	الموقع
ب1	باب مزدوج	144	230	-	1	الأمامية (مثلث زجاج كامل)
ب2	باب	80	220	-	1	الخلفية
ب3	باب	70	210	-	2	حمام 1 - حمام 2
ش2	باب	120	80	-	1	الخلفية
ش3	باب	60	60	-	1	الخلفية
ش4	باب	140	120	-	1	الخلفية

الإجمالي: أبواب 7 - شبابيك 0

جدول المساحات وبيانات المشروع

بيانات المشروع


البند	البيان
المشروع	كوخ A-frame دورين — صالة ومطبخ أمريكي وحمامين + غرفتين وحمام — 9.00 × 10.00 م
العميل	عميل — A-frame دورين
الموقع	—
الاستخدام	سكن / استراحة
التاريخ	2026-10-24
نظام البناء	هيكل خشب 5×7 + تلبيس 2.5 سم من الجهتين
السقف	جملون 61° — قرميد معدني

جدول المساحات


م	الفراغ	الأبعاد (م)	المساحة (م2)
1	الصالة	4.66 × 8.76	40.82
2	حمام 1	2.46 × 3.68	9.05
3	حمام 2	2.40 × 3.68	8.83
4	ممر	4.98 × 1.04	5.18
5	المطبخ الأمريكي	5.04 × 3.92	19.76
	المساحة الصافية الداخلية		**83.64**
	التراس المسقوف	**1.50 × 5.58**	**8.37**
	المساحة الإجمالية المبنية	**9.00 × 10.00**	**90.00**
	المساحة الكلية (المبنية + التراس)		**98.37**

لقطات المنظور الخارجي


المنظور الأمامي

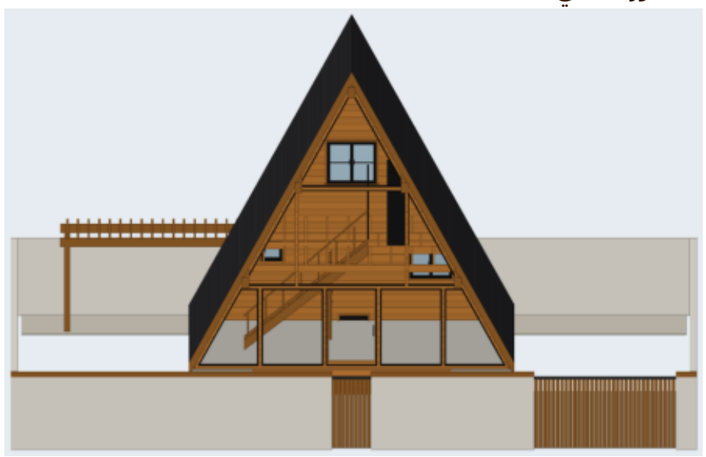


منظور أمامي من اليسار

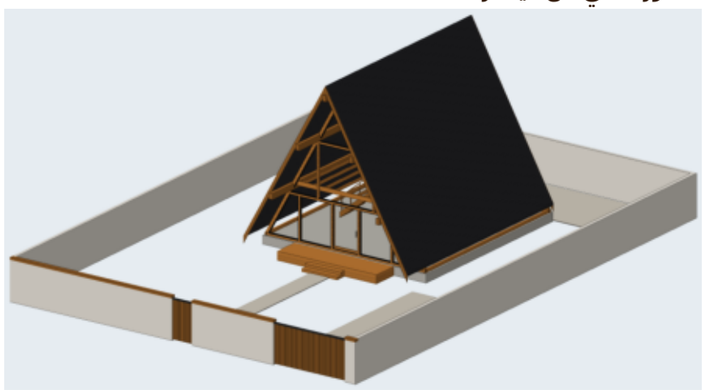


منظور أمامي من اليمين

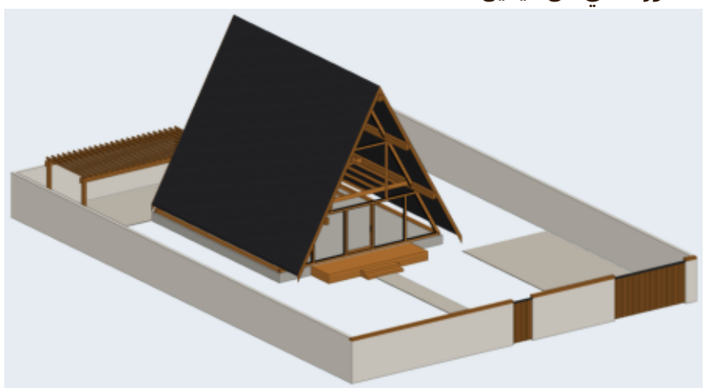


المنظور الخلفي

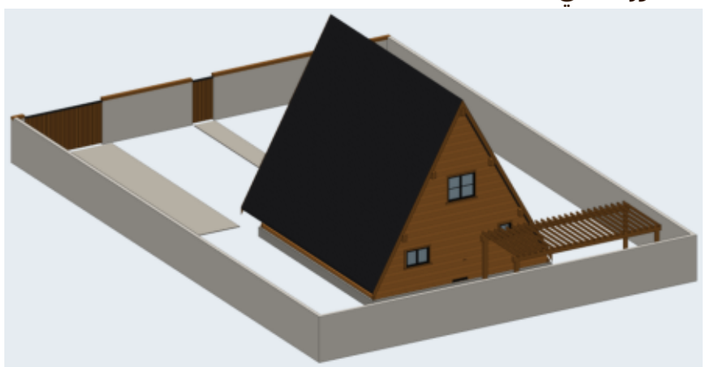

منظور خلفي من اليمين

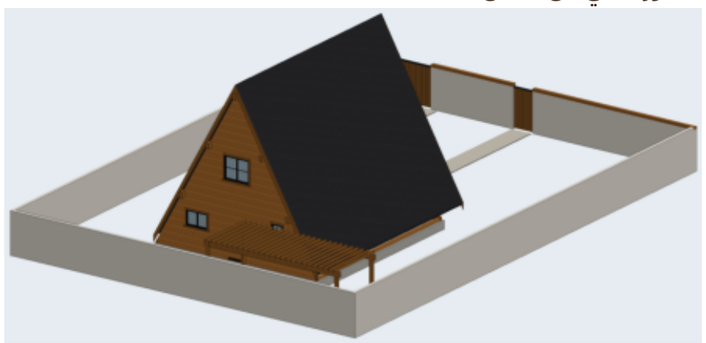

منظر علوي

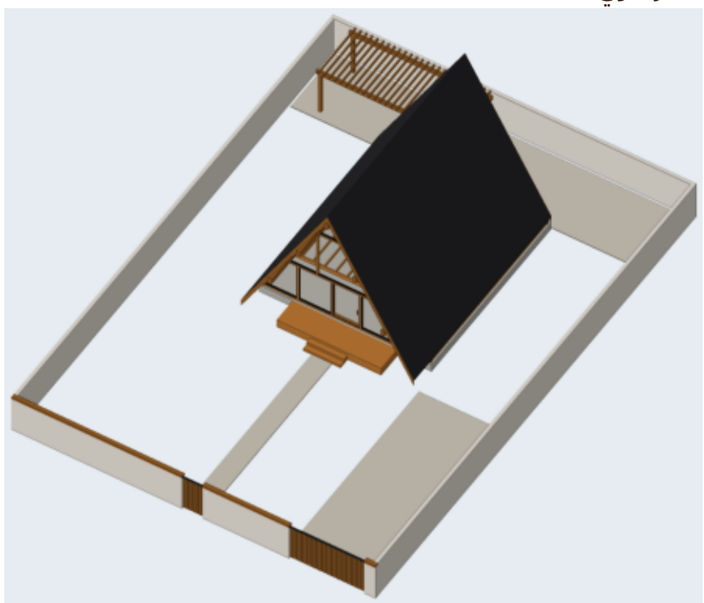


المشروع / العميل	عنوان اللوحة	المقياس	التاريخ	رقم اللوحة
كوخ A-frame دورين – صالة ومطبخ أمريكي وحمامين + غرفتين وحمام – 9.00 × 10.00 م **عميل – A-frame دورين**	**لقطات المنظور**	**–**	**2026-10-24**	**A-09 (9/11)**

مصنع وتد الأخشاب
Watad Wood Factory

المقطع العلوي بالفرش

مقطع أفقي على ارتفاع 1.90 م — توزيع الفرش ومسار الحركة

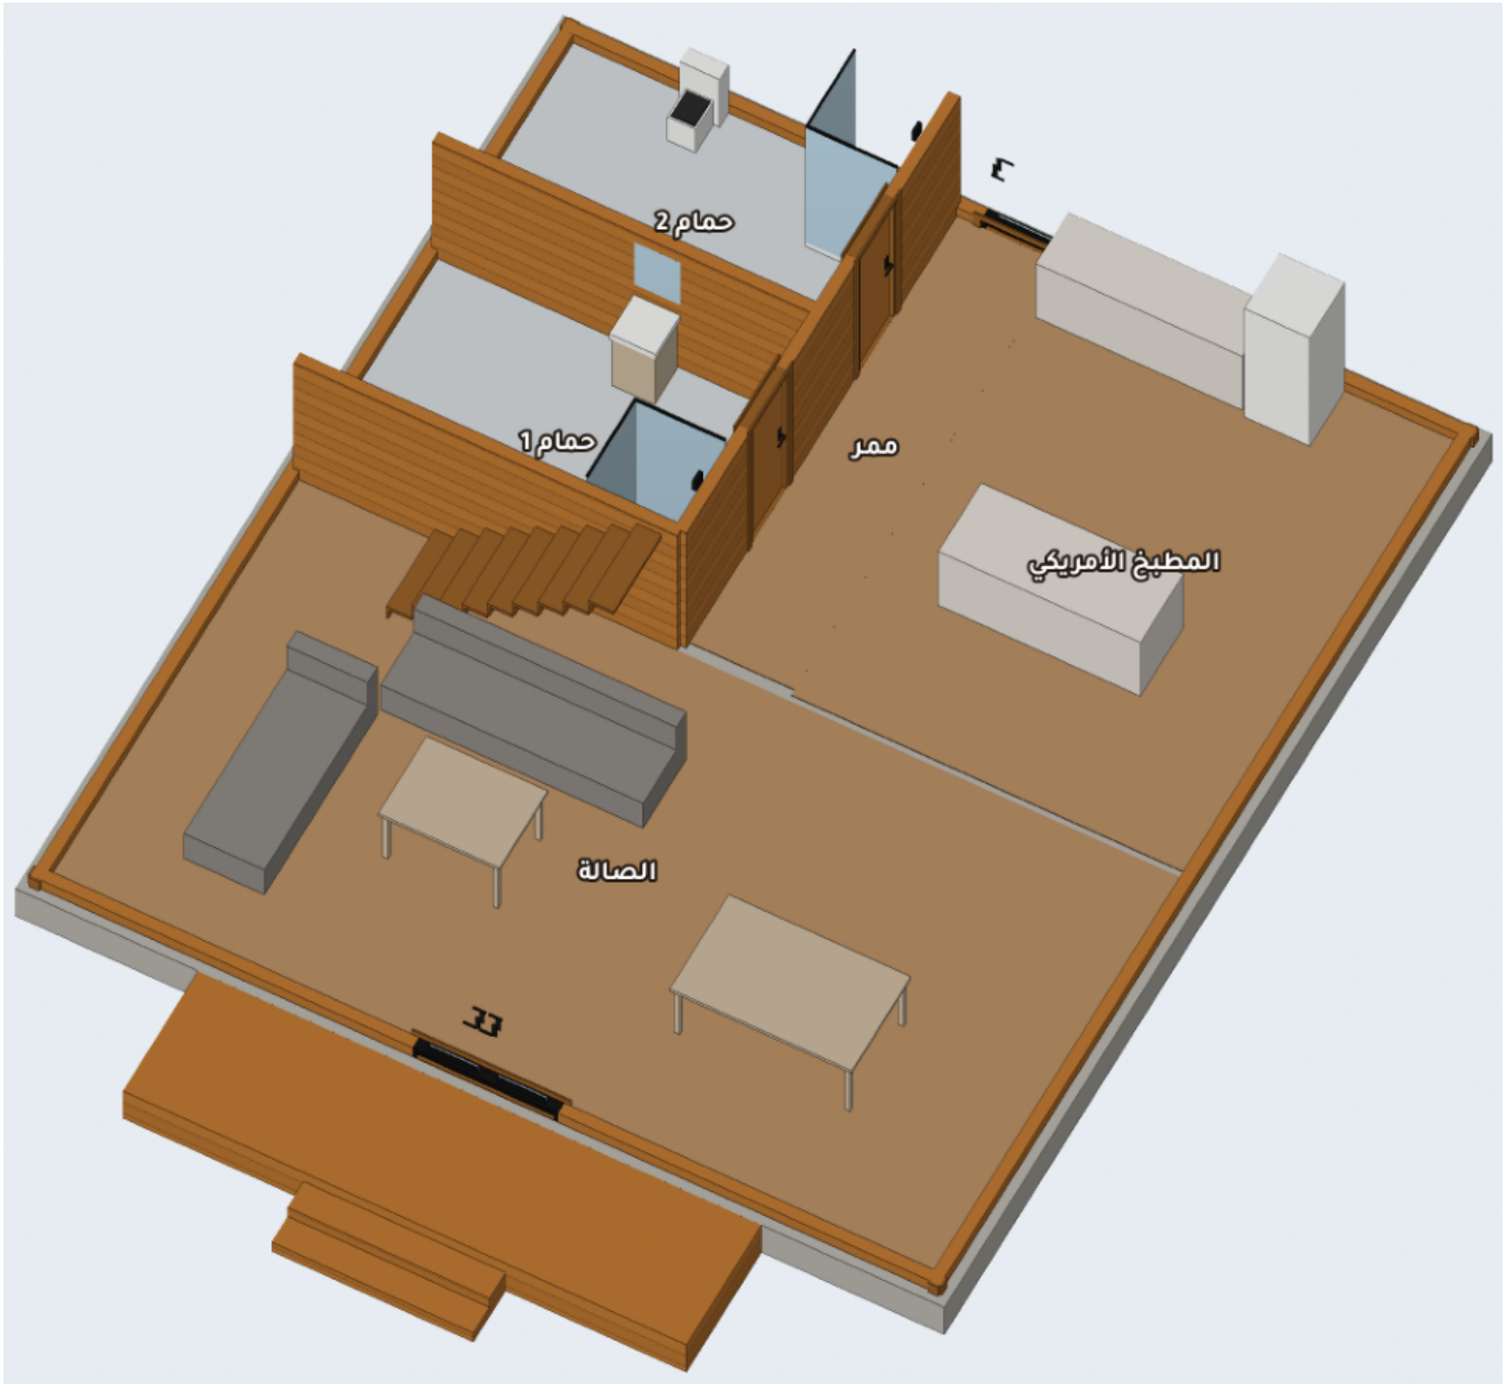


المشروع / العميل	عنوان اللوحة	المقياس	التاريخ	رقم اللوحة
كوخ A-frame دورين — صالة ومطبخ أمريكي وحمامين + غرفتين وحمام — 9.00 × 10.00 م **عميل — A-frame دورين**	**المقطع العلوي بالفرش**	**—**	**2026-10-24**	**A-10 (10/11)**

مصنع وتد الأخشاب
Watad Wood Factory

المنظور ثلاثي الأبعاد والمواد

النمط: جوزي غامق + إطارات سوداء — رندر واقعي بخامات حقيقية

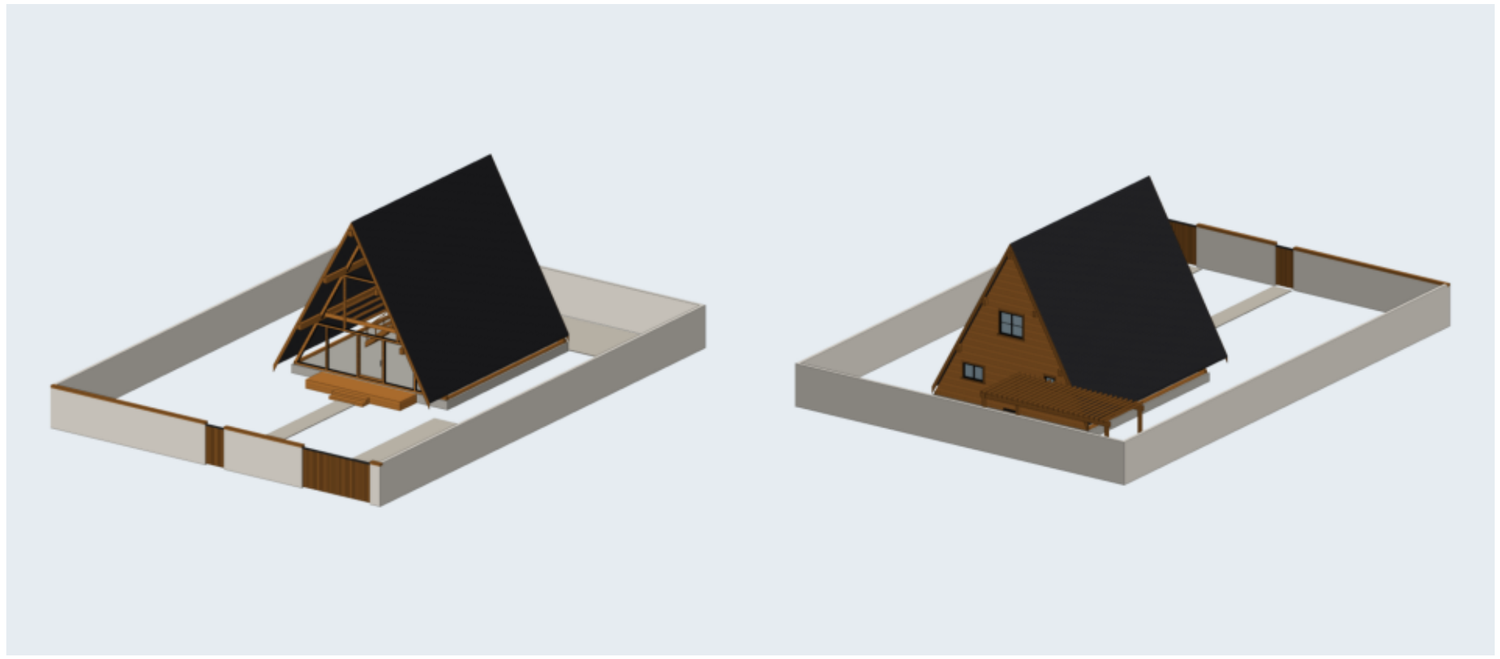

جدول المواد والألوان

الخشب / الصبغة

صبغة عسلي / سيدر

القرميد

قرميد رمادي غامق

الزجاج

زجاج شفاف

إطارات الشبابيك والأبواب

إطار ألمنيوم أسود

الكنار والزوايا

نفس الصبغة أغمق درجة


الصبة

خرسانة 45 سم


الدربزين: ألواح أفقية متقاربة (عصري)

تقسيم الشبابيك: بدون | الباب الرئيسي: زجاج بتقسيمات (فرنسي)

أنواع الدربزين المعتمدة (من مشاريع المصنع)

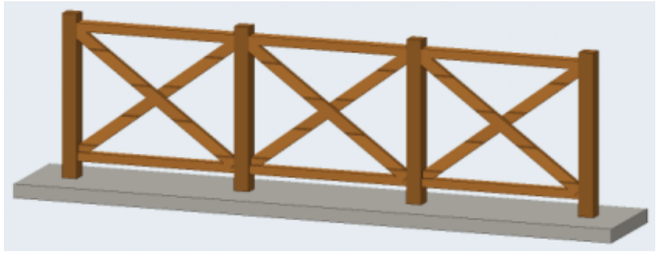

تقاطع X (صورة 5)

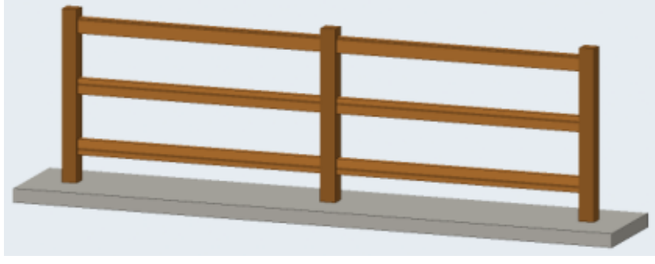

3 مرابيع أفقية (صورة 2)



قوائم رأسية متقاربة (صورة 1)

المشروع / العميل	عنوان اللوحة	المقياس	التاريخ	رقم اللوحة
كوخ A-frame دورين — صالة ومطبخ أمريكي وحمامين + غرفتين وحمام — 9.00 × 10.00 م **عميل — A-frame دورين**	**المنظور والمواد**	**—**	**2026-10-24**	**A-11 (11/11)**

مصنع وتد الأخشاب
Watad Wood Factory