
جدول مساحات الموقع

البند	المقاس	المساحة (م²)
مساحة الأرض (شبه منحرف)	25.00 × 24.27/16.23 م	499.6
مسطح الكوخ (البصمة)	13.72 × 8.24 م	113.1
تراس الكوخ	2.40 × 8.24 م	19.8
مسبح	6.60 × 3.00 م	19.8
جلسة خارجية	4.40 × 5.00 م	22.0
بلاط		15.3
موقف سيارة	5.50 × 5.50 م	30.2
ممر		12.1
أحواض زراعة	15.70 × 1.00 م	15.7
المسطحات الخضراء (حديقة)	الباقي	251.6

الموقع العام وتنسيق الحديقة (لاندسكيب)
الأرض 500 م² | الأبعاد بالسنتيمتر

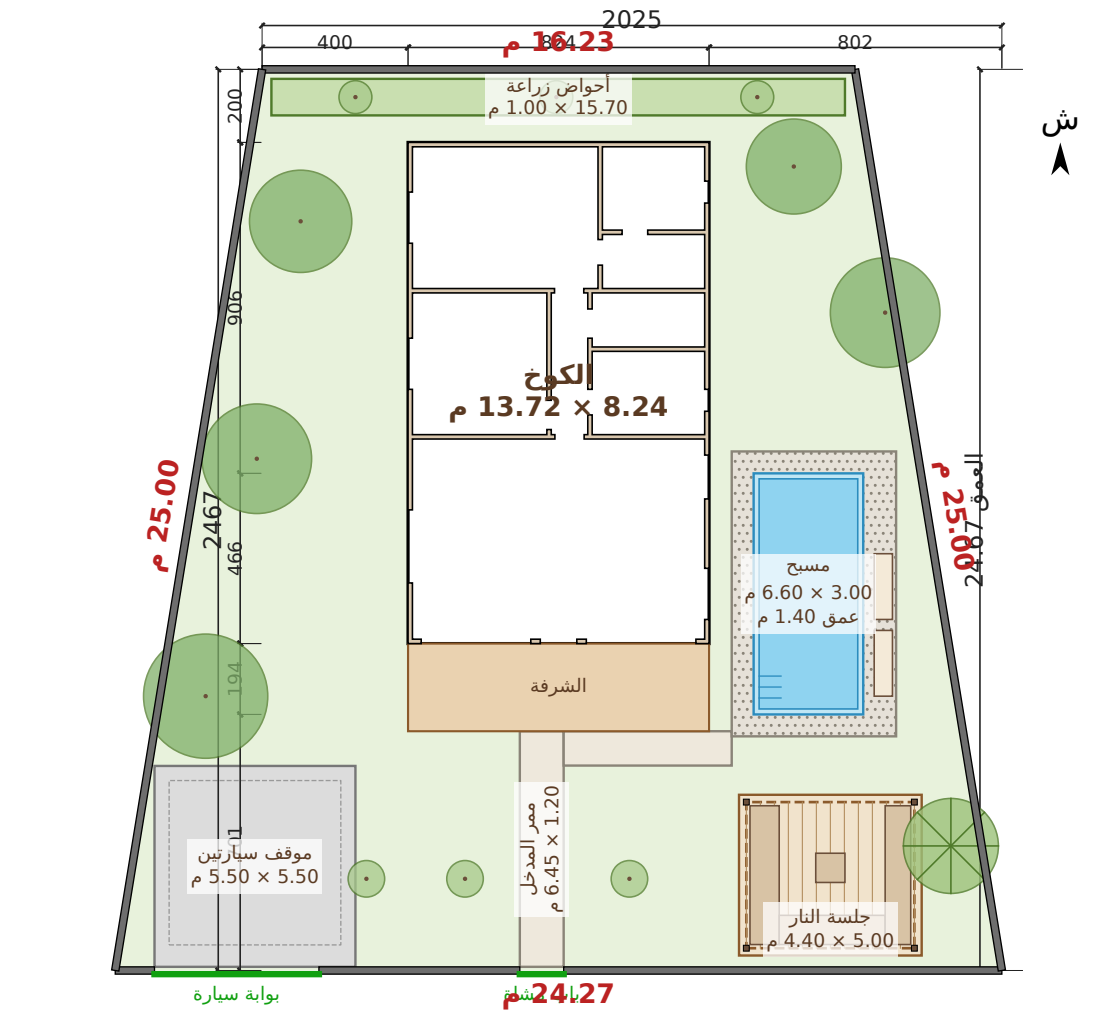


- الشاليه بآخر الأرض بعيد عن الشارع، والصالة والشرفة تطل على الحديقة والمسبح وجلسة النار.
- بوابة سيارة 4.50 م لموقف سيارتين + باب مشاة مستقل وممر مستقيم لدرج الشرفة.
- مسبح 6.60 × 3.00 م (عمق 1.40) جنب الصالة ببلاط حوله وكراسي استلقاء، يُشاف من شباك الصالة الشرقي.
- جلسة نار تحت برجولة خشب بالركن الأمامي، وأشجار ظل على السور الغربي وأحواض زراعة على السور الخلفي.
- سور بلك 2.20 م بغطاء خشب أعلى السور على أضلاع الأرض (شبه منحرف).

مصنع وتد الأخشاب Watad Wood Factory	المشروع / العميل	عنوان اللوحة	المقياس	التاريخ	رقم اللوحة
	شاليه الهدا الاستثماري — غرفتين وصالة — 113 م² = 13.72 × 8.24 عميل — الهدا (استثماري)	الموقع العام واللاندسكيب	1:200	2026-10-23	A-01 (1/10)


المسقط الأفقي مع الفرش

الأبعاد بالسنتيمتر - الجدران: قوائم 7×5 + تلبيس 2.5 من الجهتين (12 سم)

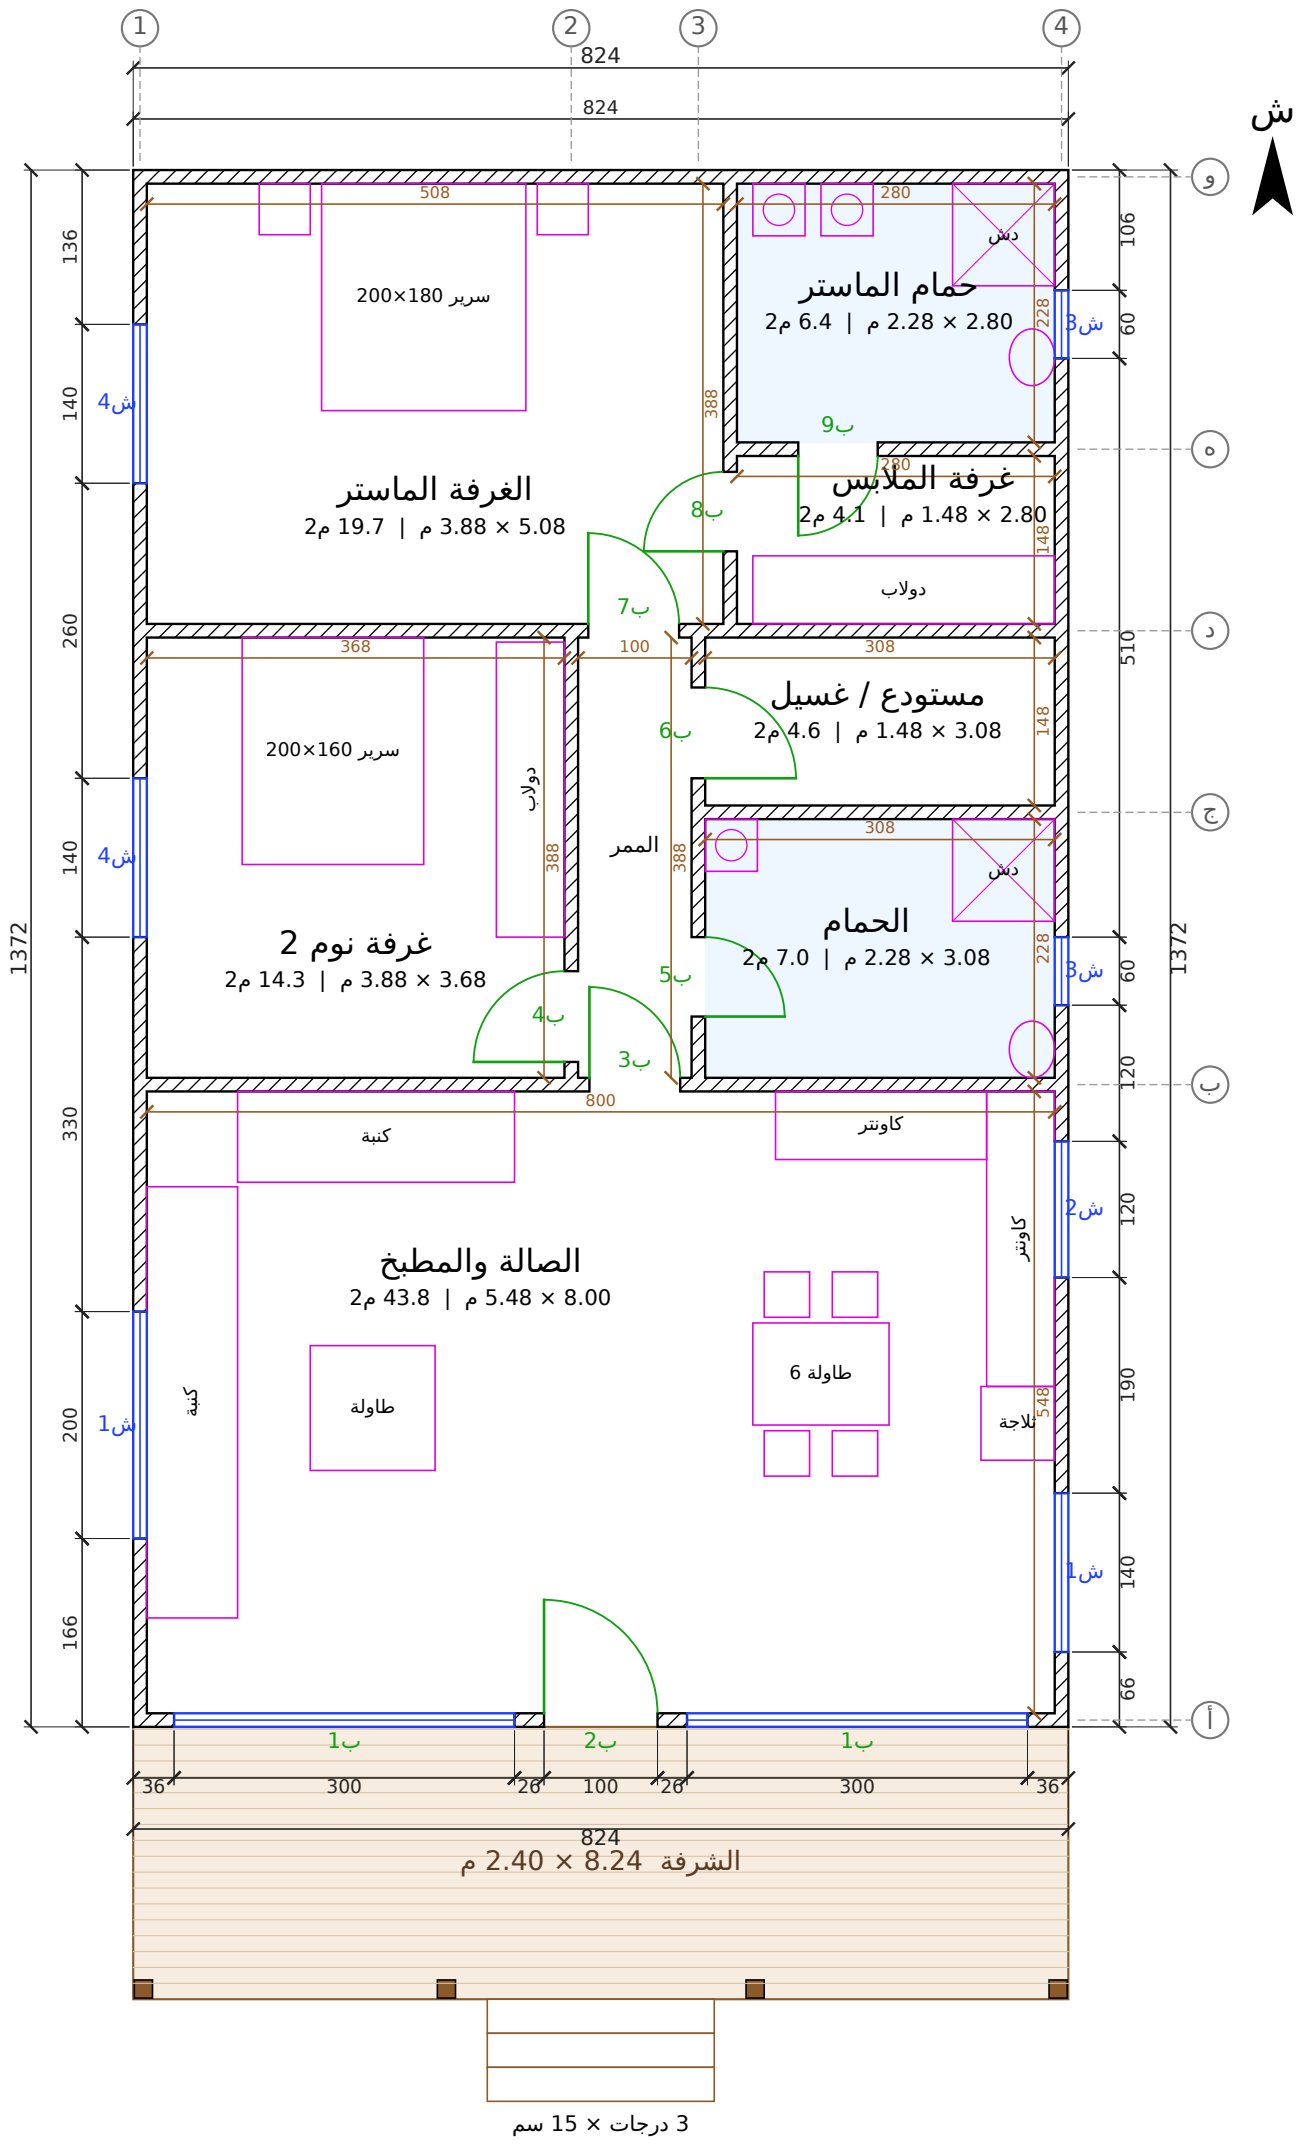


3 درجات × 15 سم

المشروع / العميل	عنوان اللوحة	المقياس	التاريخ	رقم اللوحة
مصنع وتد الأخشاب Watad Wood Factory **شاليه الهدا الاستثماري — غرفتين وصالة — 8.24 × 13.72 = 113 م²** **عميل — الهدا (استثماري)**	**المسقط الأفقي**	**1:50**	**2026-10-23**	**A-02 (2/10)**

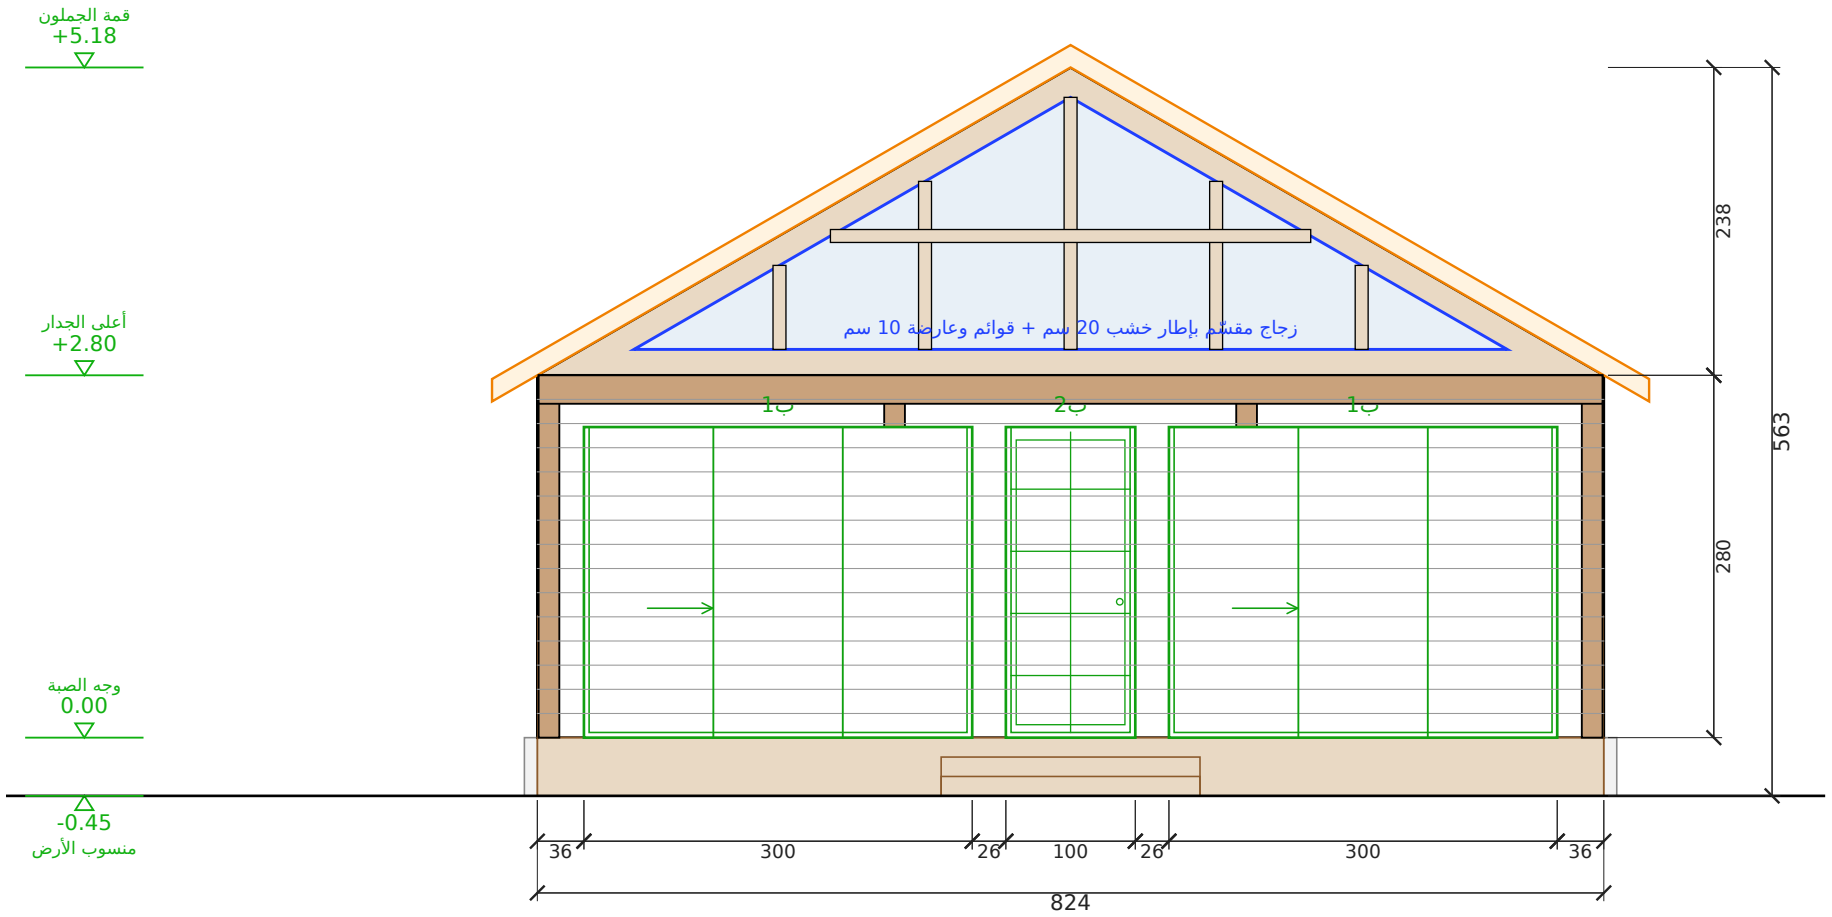

الواجهة الأمامية

مقياس 1:50 | الوحدة: سم

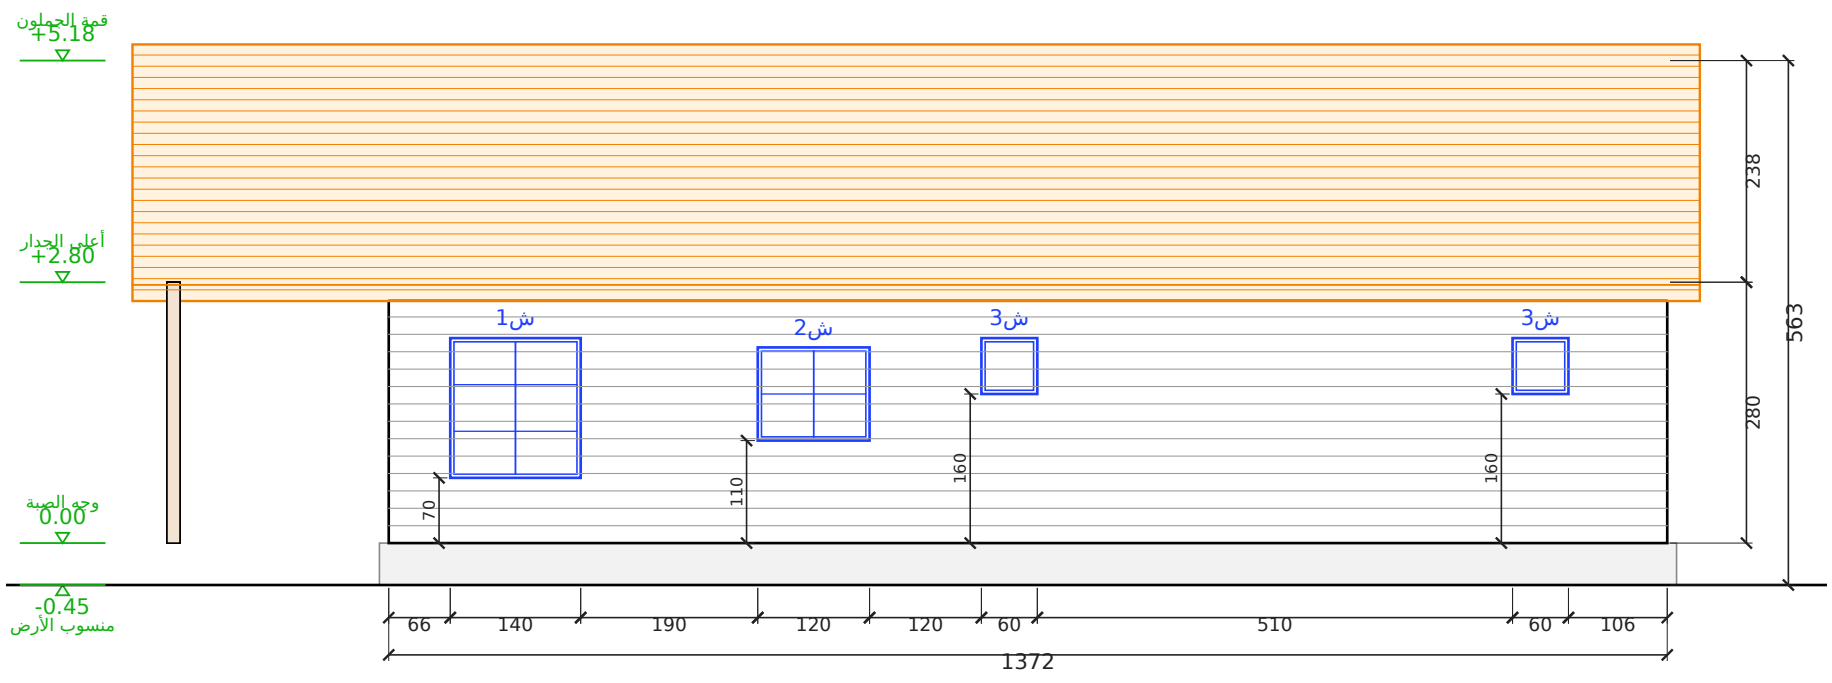


الواجهة الشرقية

مقياس 1:50 | الوحدة: سم


المشروع / العميل	عنوان اللوحة	المقياس	التاريخ	رقم اللوحة
شالية الهدا الاستثماري — غرفتين وصالة — 8.24 × 13.72 = 113 م² **عميل — الهدا (استثماري)**	**الواجهة الأمامية والواجهة الشرقية**	**1:50**	**2026-10-23**	**A-03 (3/10)**

مصنع وتد الأخشاب
Watad Wood Factory

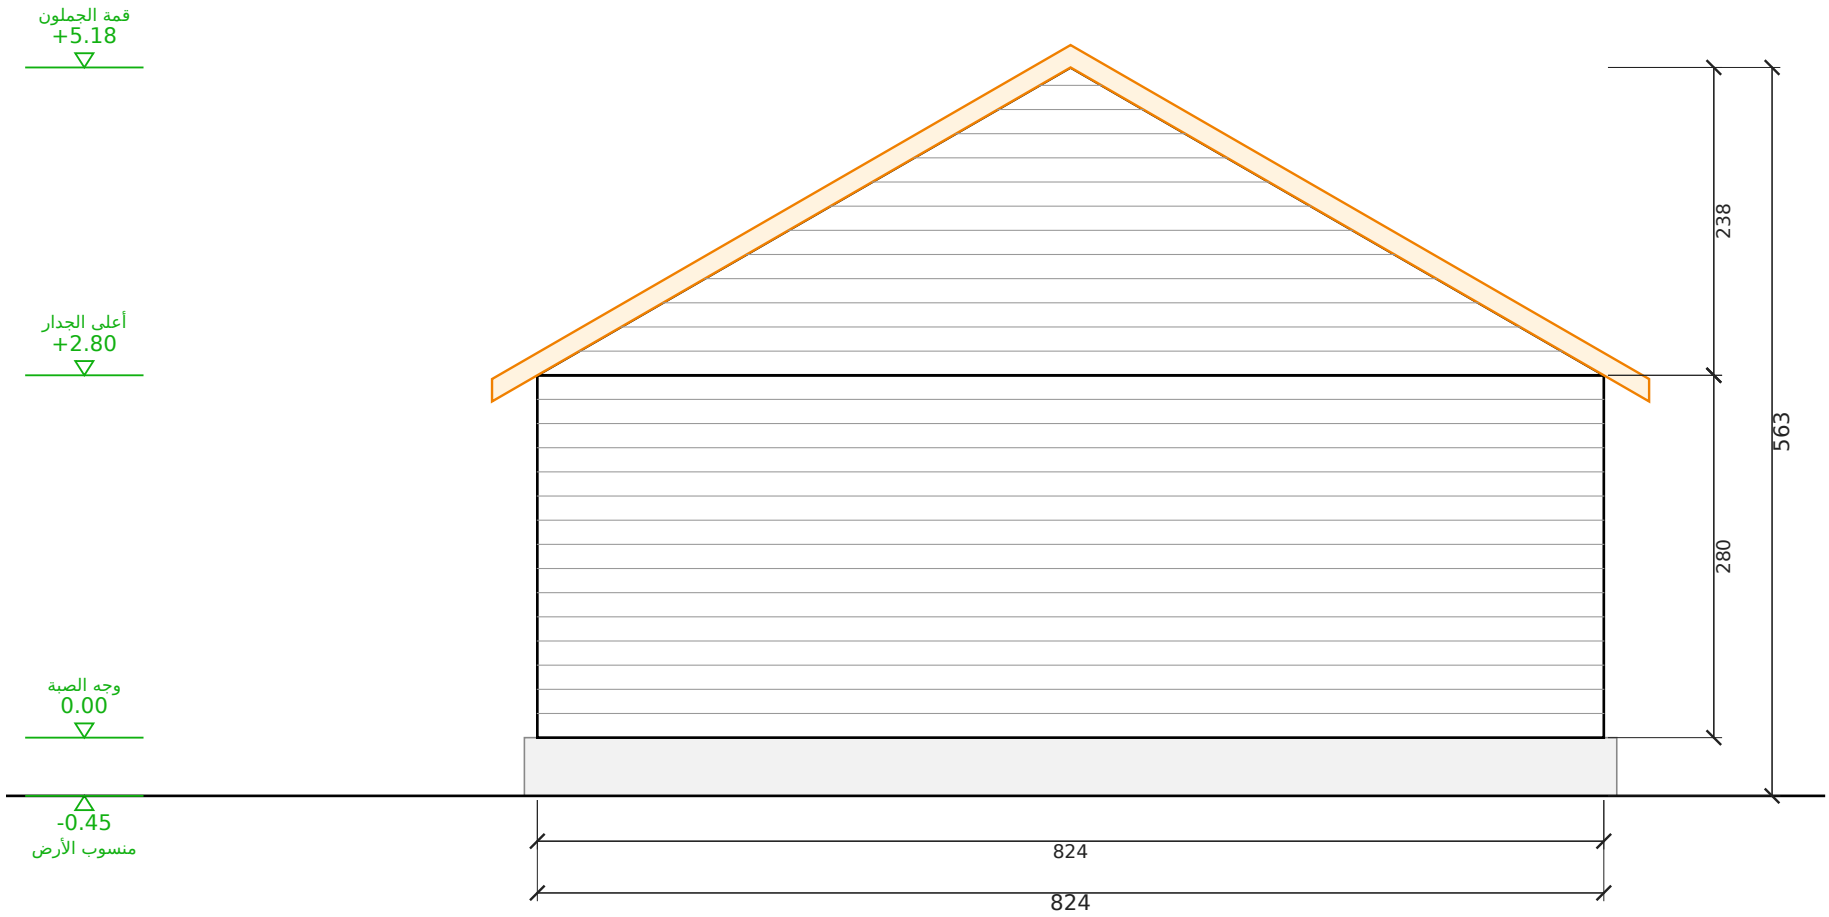

الواجهة الخلفية

مقياس 1:50 | الوحدة: سم

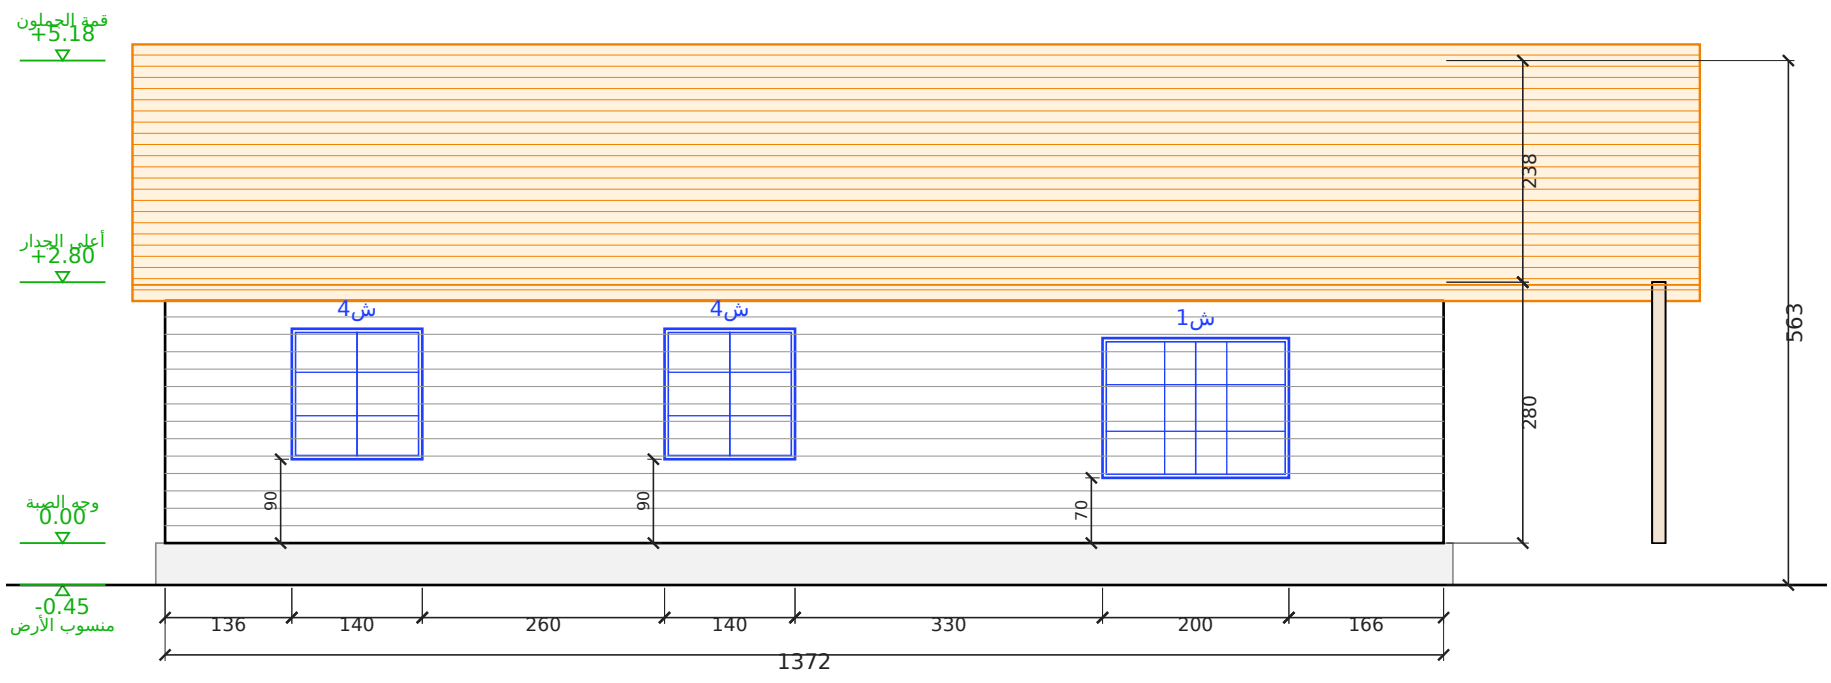


الواجهة الغربية

مقياس 1:50 | الوحدة: سم


المشروع / العميل	عنوان اللوحة	المقياس	التاريخ	رقم اللوحة
شالية الهدا الاستثماري — غرفتين وصالة — 8.24 × 13.72 = 113 م² عميل — الهدا (استثماري)	الواجهة الخلفية والواجهة الغربية	1:50	2026-10-23	A-04 (4/10)

مصنع وتد الأخشاب
Watad Wood Factory


مسقط السقف (جملون)
رفرف 35 سم من كل جهة | مقياس 1:50

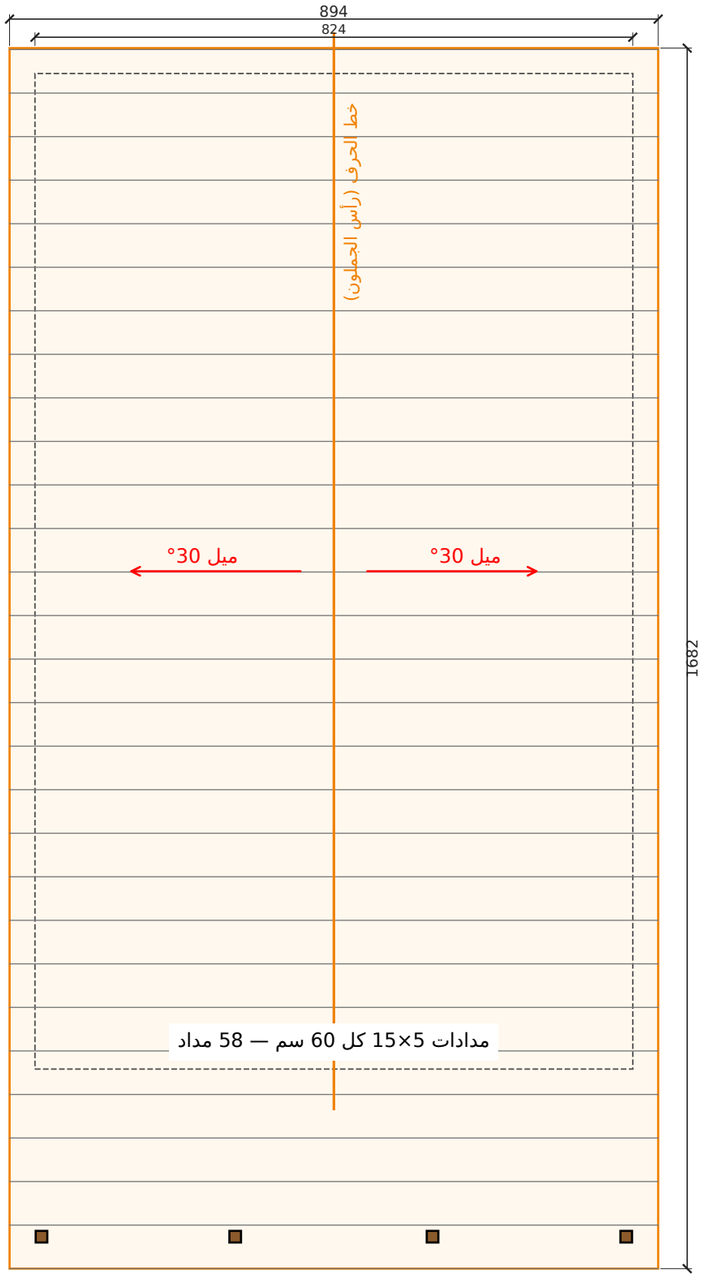

قطاع عرضي أ-أ
مقياس 1:50 | الوحدة: سم

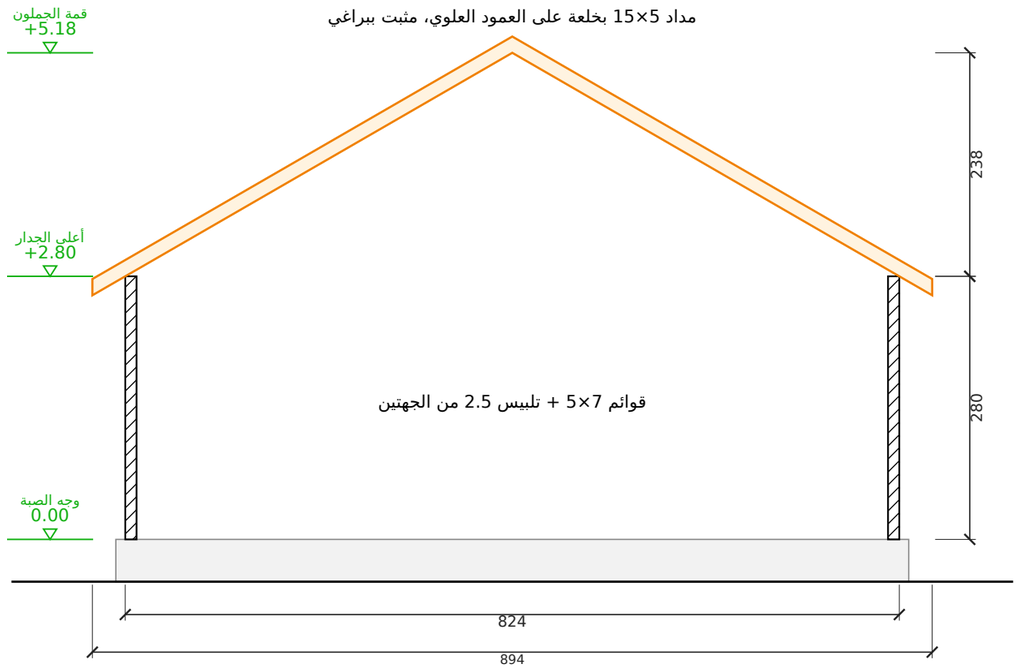

تفصيلة جلوس المداد على العلوي (1:5)

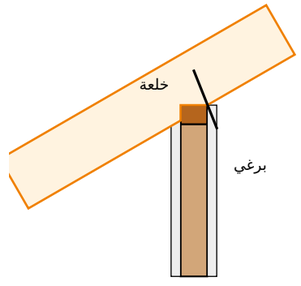

المشروع / العميل: **شاليه الهدا الاستثماري — غرفتين وصالة — 8.24 × 13.72 = 113 م²** **عميل — الهدا (استثماري)**	عنوان اللوحة: **مسقط السقف والقطاع**	المقياس: **1:50**	التاريخ: **2026-10-23**	رقم اللوحة: **A-05 (5/10)**

مصنع وتد الأخشاب
Watad Wood Factory

جدول مقاسات الأبواب والشبابيك
مقاس الفتحة الصافي في الجدار - الوحدة: سم

الرمز	النوع	العرض (سم)	الارتفاع (سم)	ارتفاع الجلسة (سم)	العدد	الموقع
ب1	باب	300	240	-	2	الأمامية 2
ب2	باب	100	240	-	1	الأمامية
ب3	باب	80	210	-	1	باب الممر
ب4	باب	80	210	-	1	غرفة نوم 2
ب5	باب	70	210	-	1	الحمام
ب6	باب	80	210	-	1	مستودع / غسيل
ب7	باب	80	210	-	1	الماستر
ب8	باب	70	210	-	1	غرفة الملابس
ب9	باب	70	210	-	1	حمام الماستر
ش1	شباك	140	150	70	1	الشرقية
ش1	شباك	200	150	70	1	الغربية
ش2	شباك	120	100	110	1	الشرقية
ش3	شباك	60	60	160	2	الشرقية 2
ش4	شباك	140	140	90	2	الغربية 2

الإجمالي: أبواب 10 - شبابيك 7

جدول المساحات وبيانات المشروع والتسعير

بيانات المشروع

البند	البيان
المشروع	شاليه الهدا الاستثماري — غرفتين وصالة — 8.24 × 13.72 = 113 م²
العميل	عميل — الهدا (استثماري)
الموقع	الهدا — الطائف
الاستخدام	شاليه استثماري (تأجير)
التاريخ	2026-10-23
نظام البناء	هيكل خشب 5×7 + تلبيس 2.5 سم من الجهتين
السقف	جملون 30° — قرميد معدني

جدول المساحات

م	الفراغ	الأبعاد (م)	المساحة (م2)
1	الصالة والمطبخ	8.00 × 5.48	43.84
2	غرفة نوم 2	3.68 × 3.88	14.28
3	الممر	1.00 × 3.88	3.88
4	الحمام	3.08 × 2.28	7.02
5	مستودع / غسيل	3.08 × 1.48	4.56
6	الغرفة الماستر	5.08 × 3.88	19.71
7	غرفة الملابس	2.80 × 1.48	4.14
8	حمام الماستر	2.80 × 2.28	6.38
	المساحة الصافية الداخلية		**103.82**
	الشرفة	**8.24 × 2.40**	**19.78**
	المساحة الإجمالية المبنية	**8.24 × 13.72**	**113.05**
	المساحة الكلية (المبنية + التراس)		**132.83**

التسعير المفصّل

البند	المبلغ (ريال)
الكوخ المبني 113.05 م² × 1,096	123,903
الشرفة الأمامية المسقوفة (أرضية + امتداد السقف + 4 أعمدة + دربزين) — 19.78 م² × 1,096	21,679
الإجمالي (ريال)	**145,582**

ملاحظات:


- السعر للشاليه والشرفة حسب المخطط المعتمد — التراس يُسعّر بنفس سعر متر الكوخ.
- أعمال الموقع (السور والبوابات والمسبح والبلاط والزراعة) عن طريق المقاول وتُسعّر منفصلة.
- الصبة والتمديدات الخارجية على العميل ما لم يُذكر غير ذلك.

لقطات المنظور الخارجي


المنظور الأمامي




منظور أمامي من اليسار

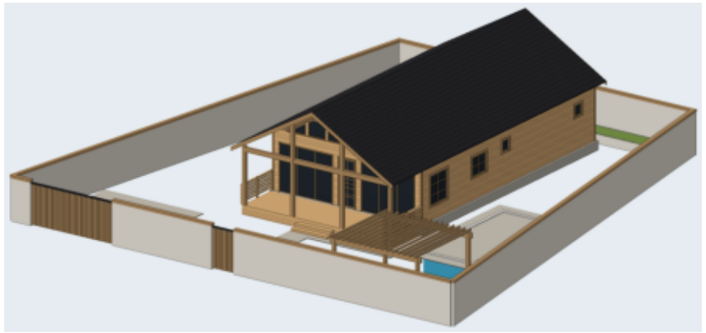


منظور أمامي من اليمين

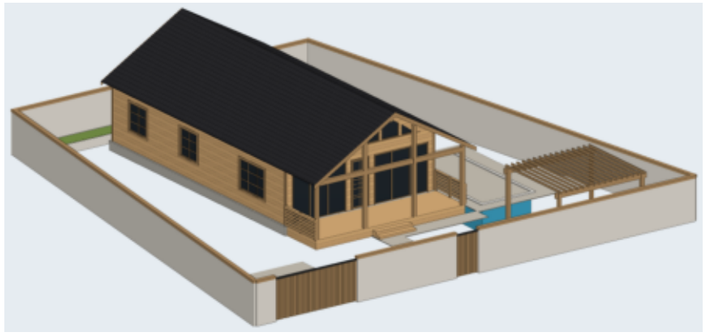


المنظور الخلفي

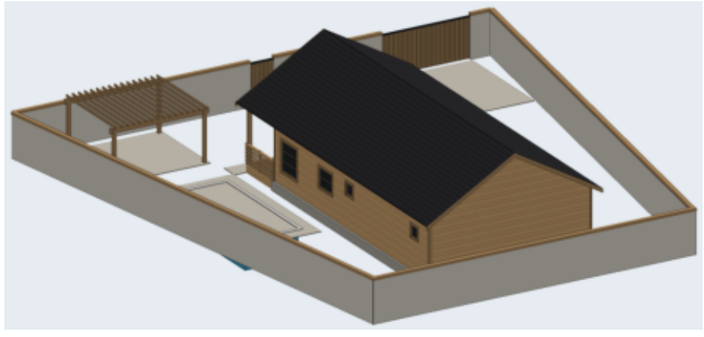

منظور خلفي من اليمين

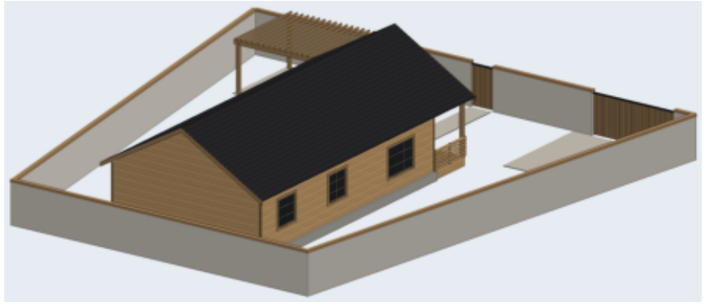

منظر علوي

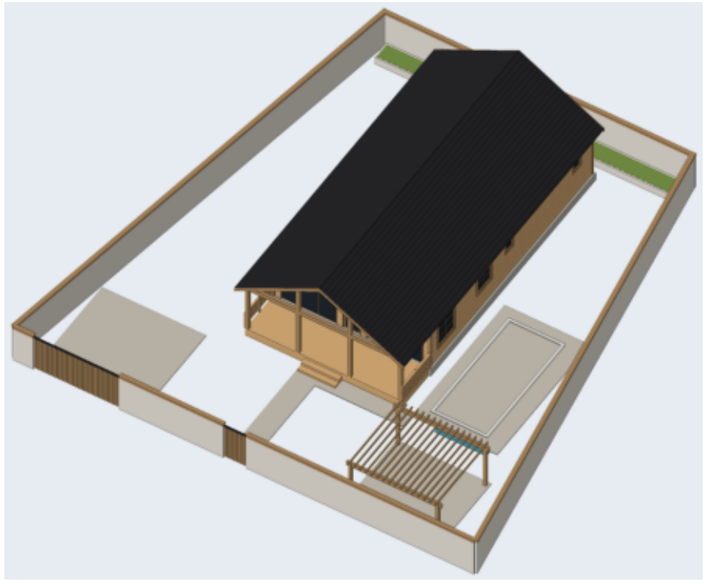


المشروع / العميل	عنوان اللوحة	المقياس	التاريخ	رقم اللوحة
شاليه الهدا الاستثماري — غرفتين وصالة — 8.24 × 13.72 = 113 م² **عميل — الهدا (استثماري)**	**لقطات المنظور**	**—**	**2026-10-23**	**A-08 (8/10)**

مصنع وتد الأخشاب
Watad Wood Factory

المقطع العلوي بالفرش

مقطع أفقي على ارتفاع 1.90 م — توزيع الفرش ومسار الحركة

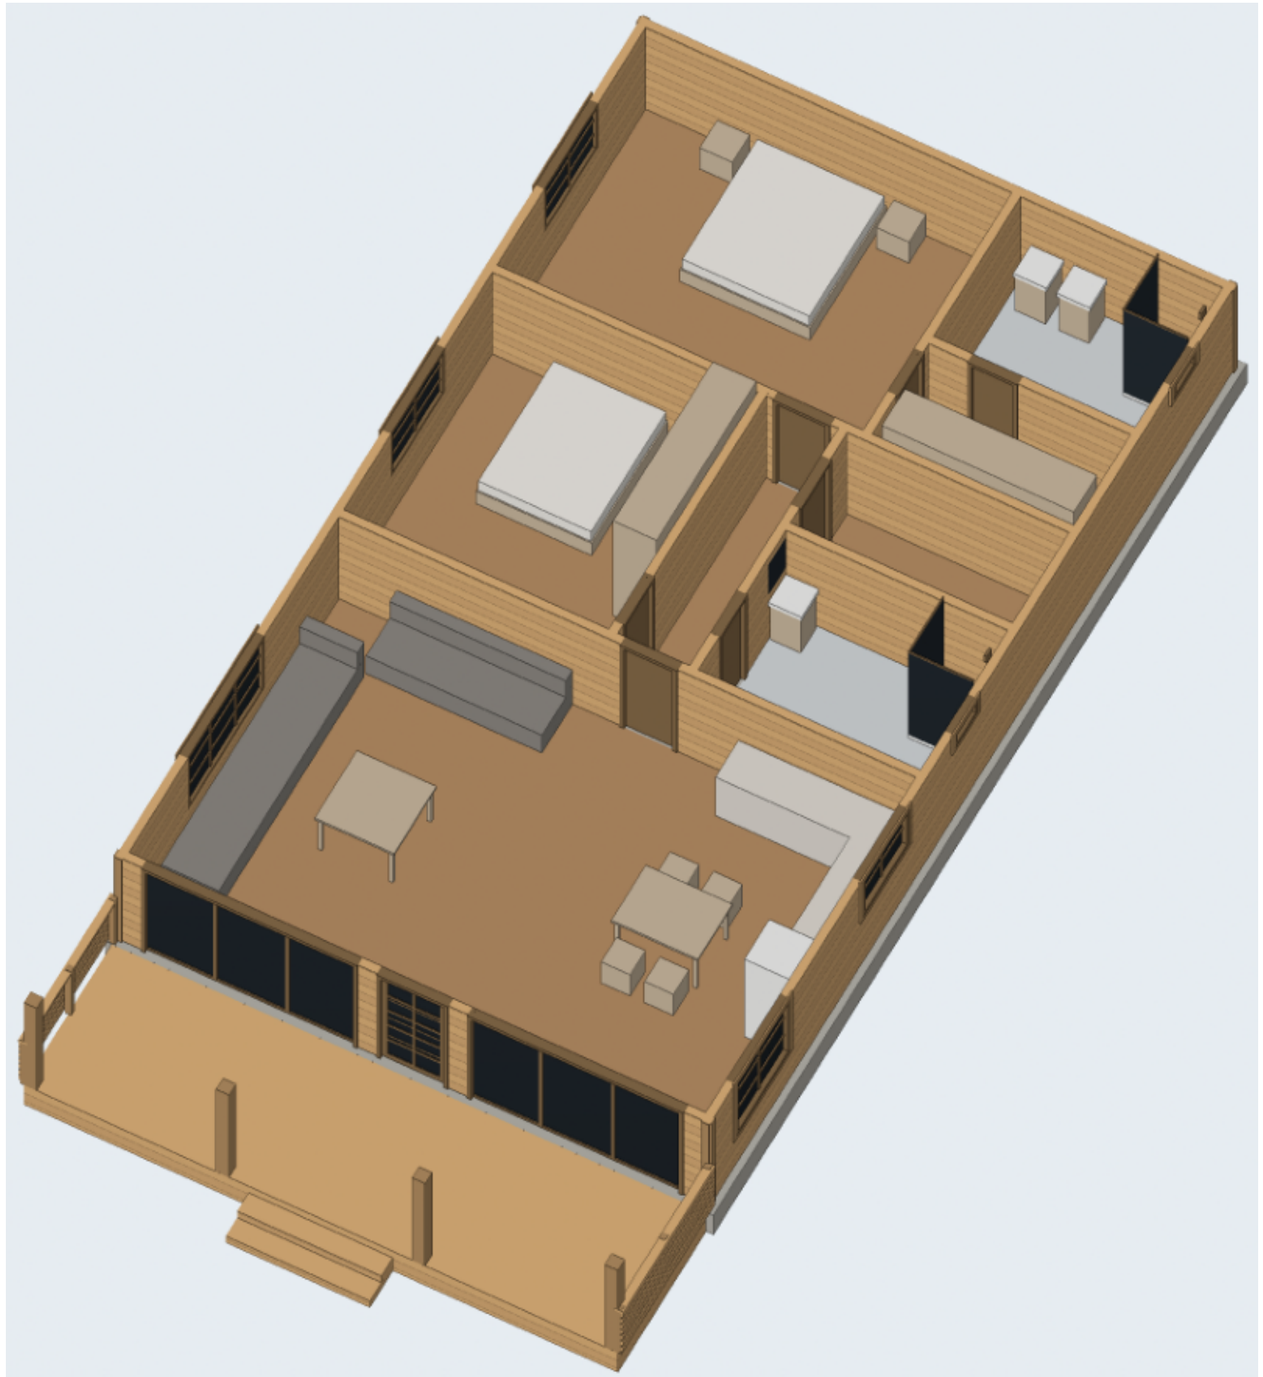


المشروع / العميل	عنوان اللوحة	المقياس	التاريخ	رقم اللوحة
شاليه الهدا الاستثماري — غرفتين وصالة — 8.24 × 13.72 = 113 م² **عميل — الهدا (استثماري)**	**المقطع العلوي بالفرش**	**—**	**2026-10-23**	**A-09 (9/10)**

مصنع وتد الأخشاب
Watad Wood Factory

المنظور ثلاثي الأبعاد والمواد

النمط: جوزي غامق + إطارات سوداء — رندر واقعي بخامات حقيقية

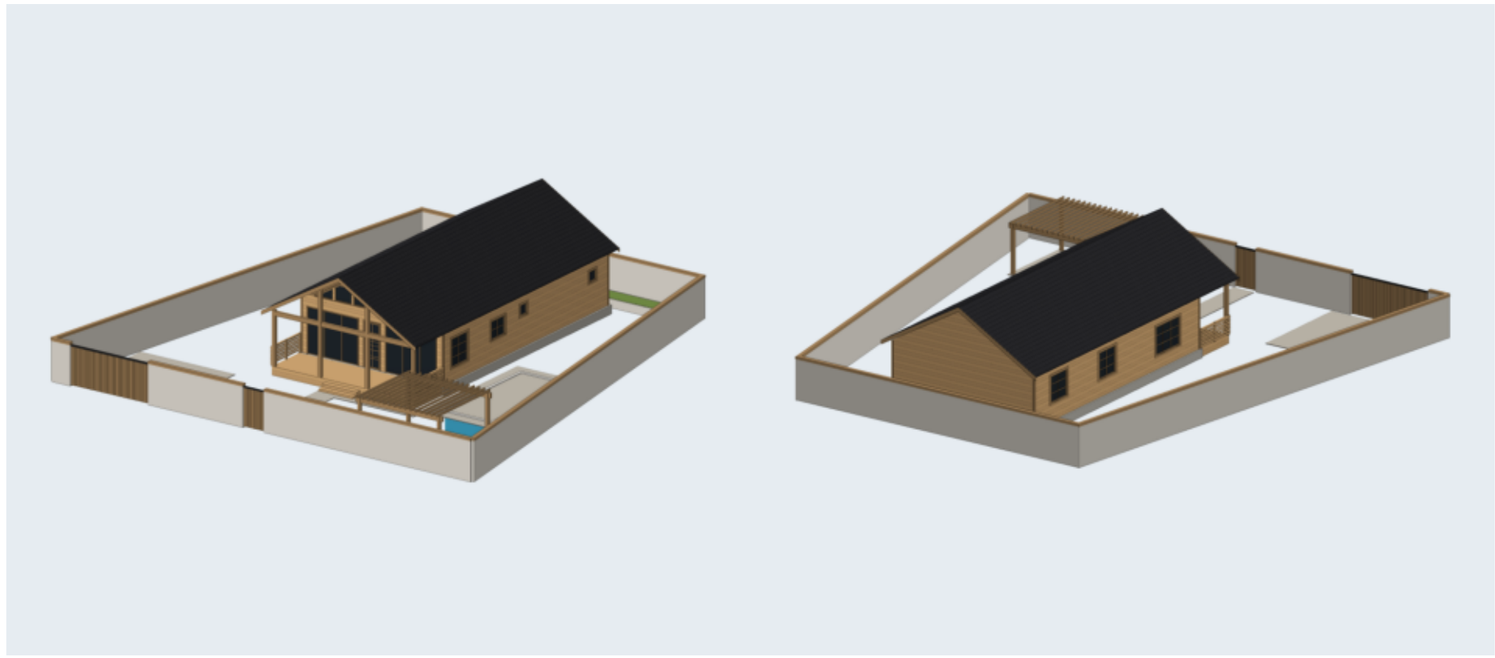

جدول المواد والألوان

الخشب / الصبغة

خشب طبيعي فاتح (بدون صبغة)

القرميد

قرميد رمادي غامق

الزجاج

زجاج عاكس غامق

إطارات الشبابيك والأبواب

إطار خشب بنفس الصبغة أغمق

الكنار والزوايا

نفس الصبغة أغمق درجة


الصبة

خرسانة 45 سم


الدربزين: ألواح أفقية متقاربة (عصري)

تقسيم الشبابيك: بدون | الباب الرئيسي: سحاب زجاج

أنواع الدربزين المعتمدة (من مشاريع المصنع)

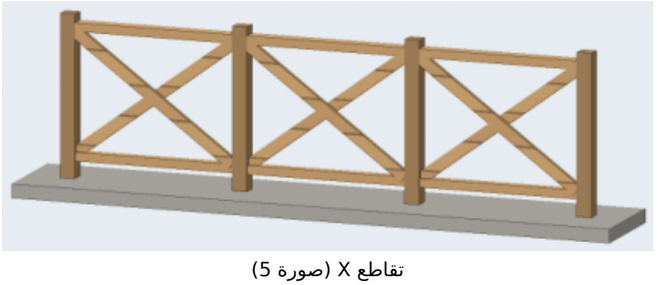

تقاطع X (صورة 5)

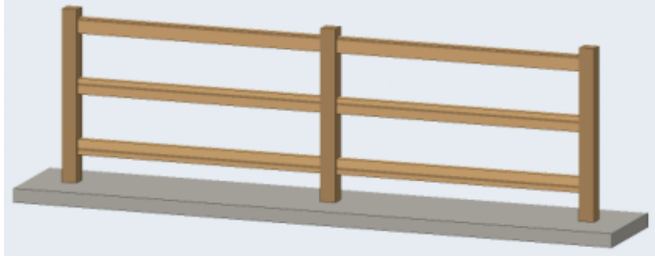

3 مرابيع أفقية (صورة 2)



قوائم رأسية متقاربة (صورة 1)

المشروع / العميل	عنوان اللوحة	المقياس	التاريخ	رقم اللوحة
شاليه الهدا الاستثماري — غرفتين وصالة — 8.24 × 13.72 = 113 م² **عميل — الهدا (استثماري)**	**المنظور والمواد**	**—**	**2026-10-23**	**A-10 (10/10)**

مصنع وتد الأخشاب
Watad Wood Factory