


مصنع وتد الأخشاب · ملف التصميم

مجلس خشب منفصل 4.00 × 6.00 م بواجهة زجاج

مجلس 4.00 × 6.00 م • مدخل مسقوف 2.00 × 2.00 م • صالة مدخل ومغسلة • دورة مياه • الواجهة كلها زجاج بإطار أسود


المسقط الأفقي مع الفرش

الأبعاد بالسنتيمتر - الجدران: قوائم 7×5 + تلبيس 2.5 من الجهتين (12 سم)

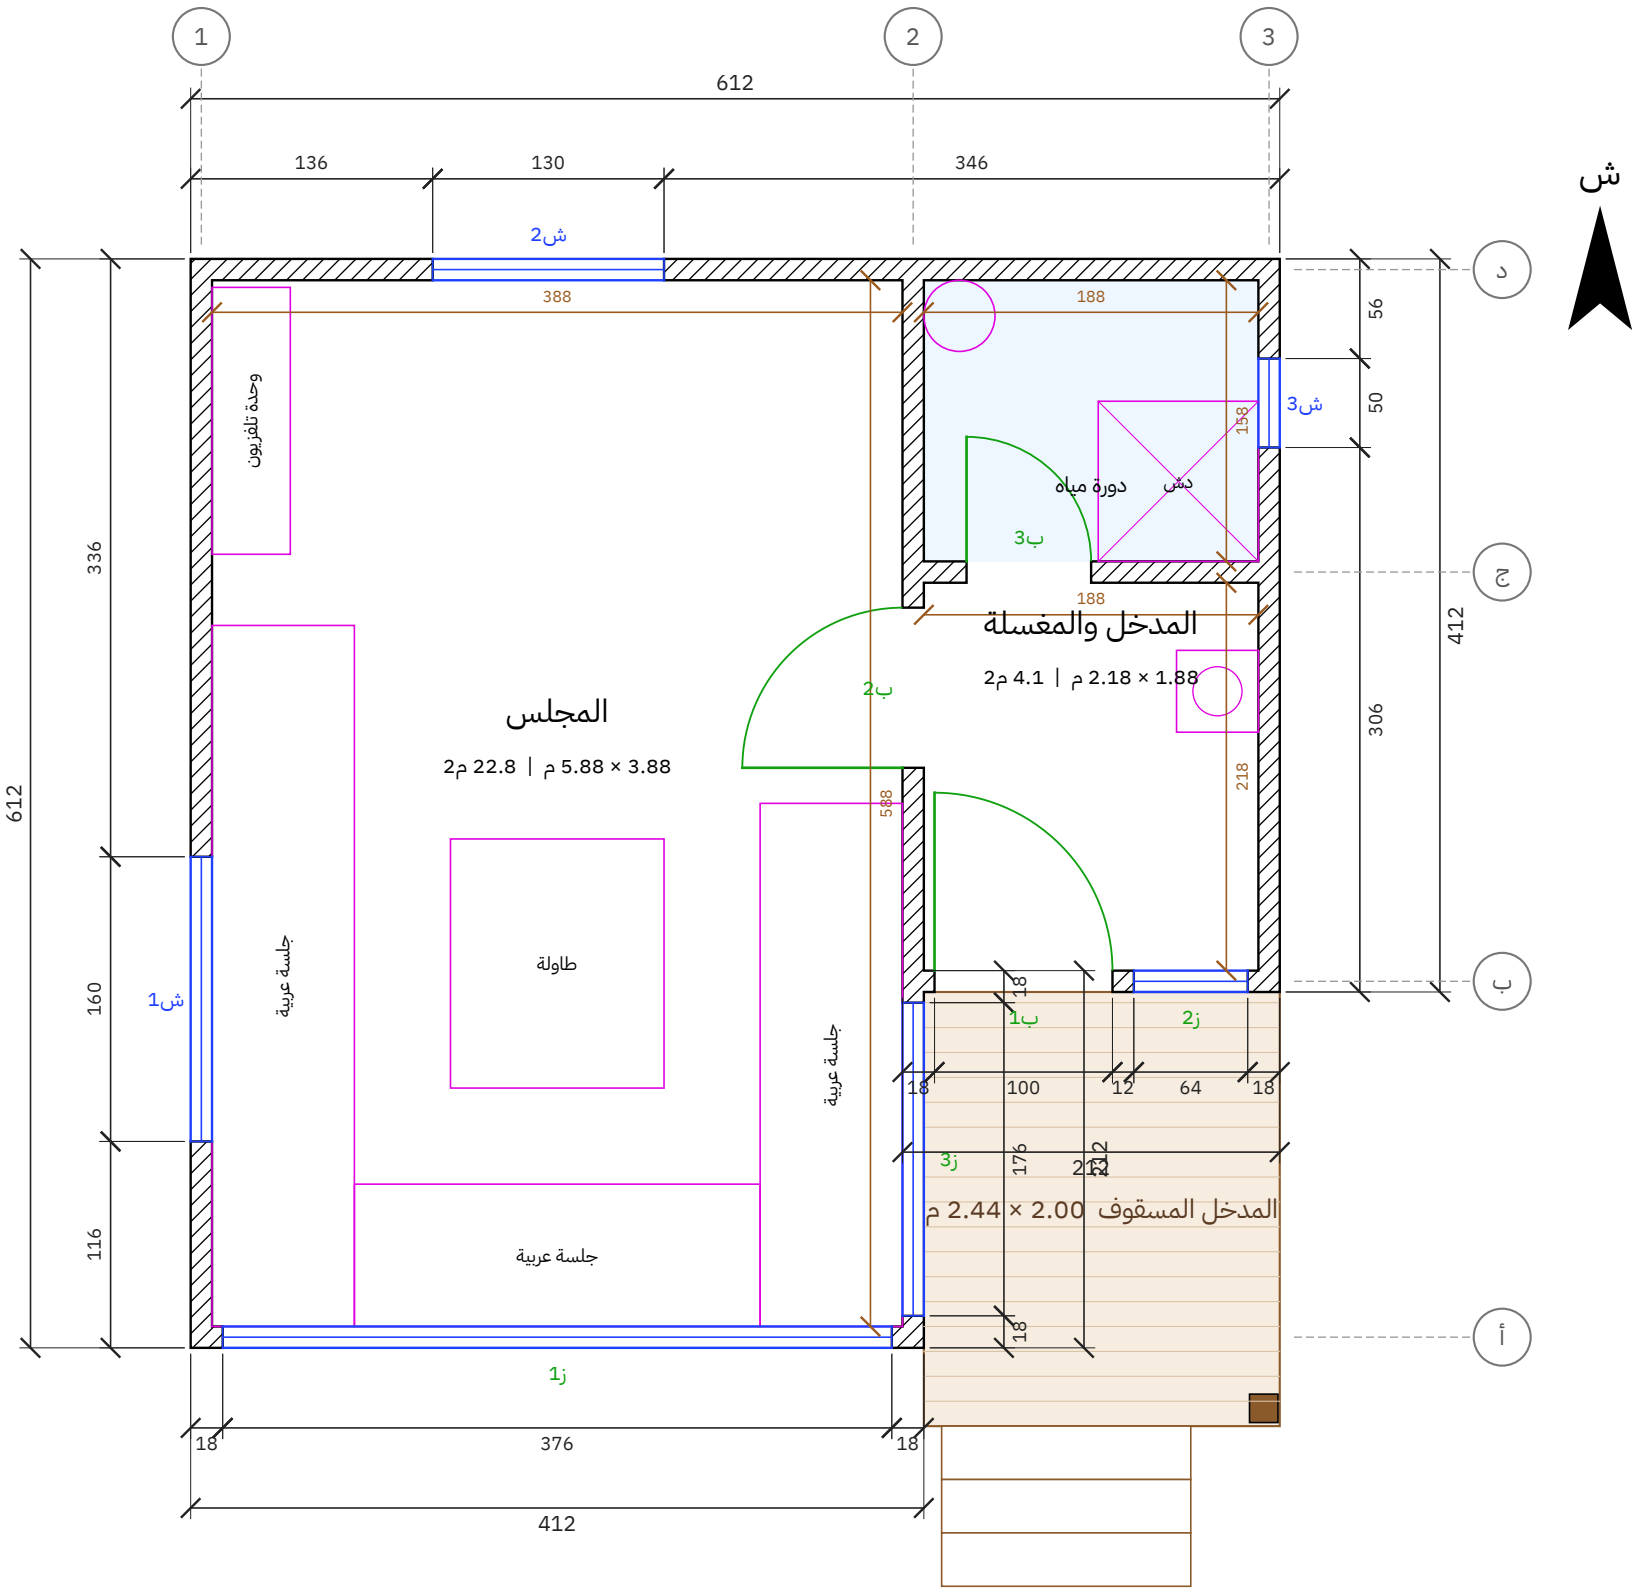


3 درجات × 15 سم

مصنع وتد الأخشاب Watad Wood Factory	المشروع / العميل مجلس خشب منفصل 4.00 × 6.00 م بواجهة زجاج ومدخل ودورة مياه عميل – مجلس منفصل	عنوان اللوحة المسقط الأفقي	المقياس 1:50	التاريخ 2026-11-03	رقم اللوحة A-02 (2/11)

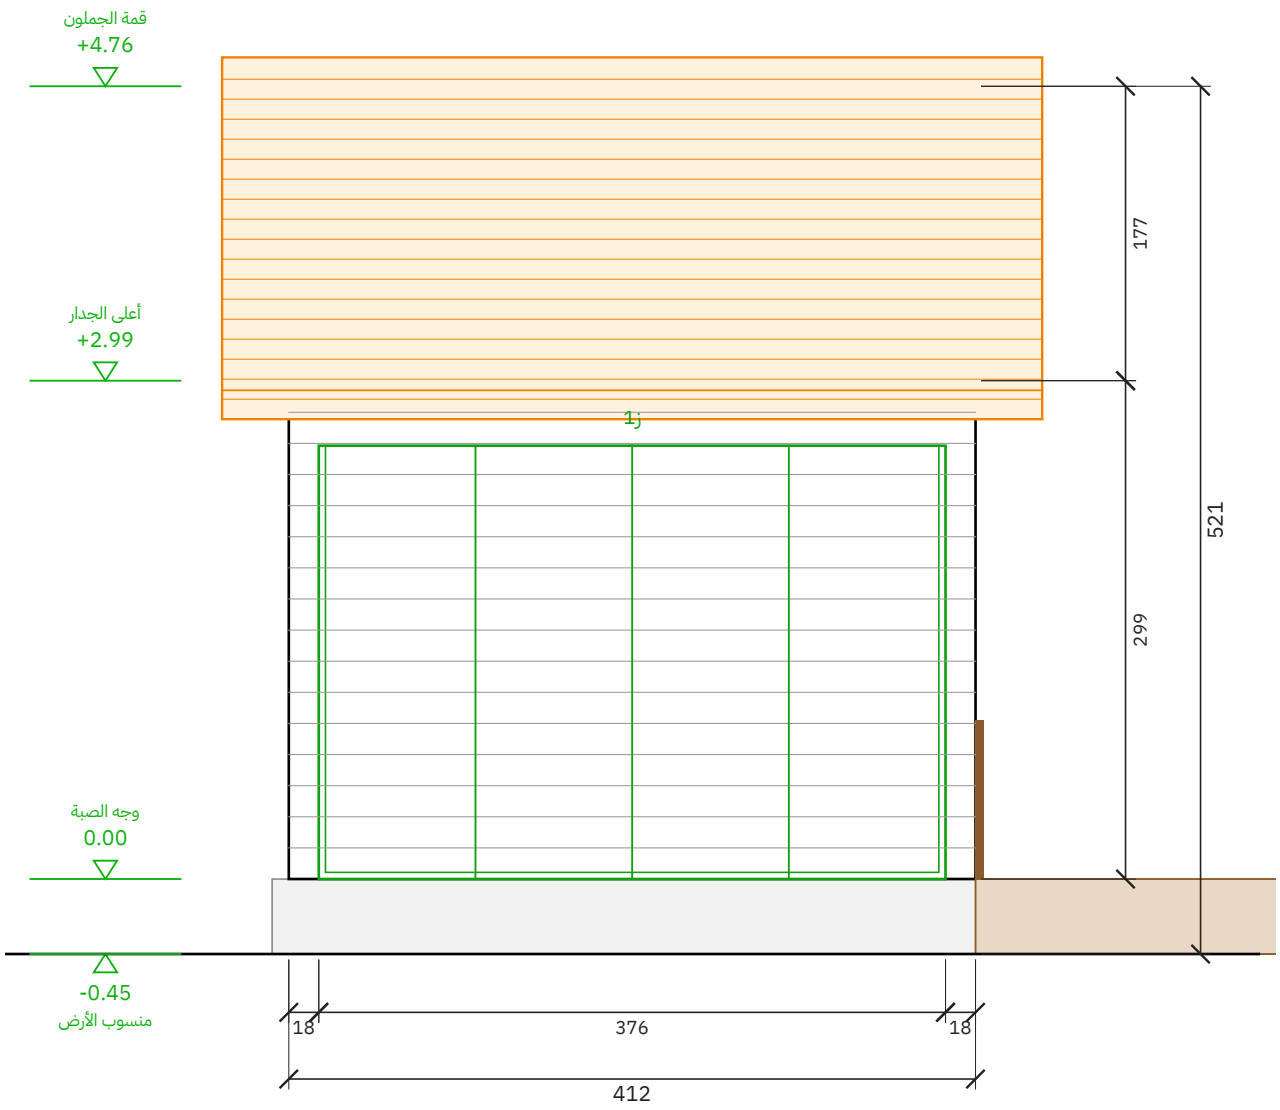

الواجهة الأمامية


مقياس 1:50 | الوحدة: سم

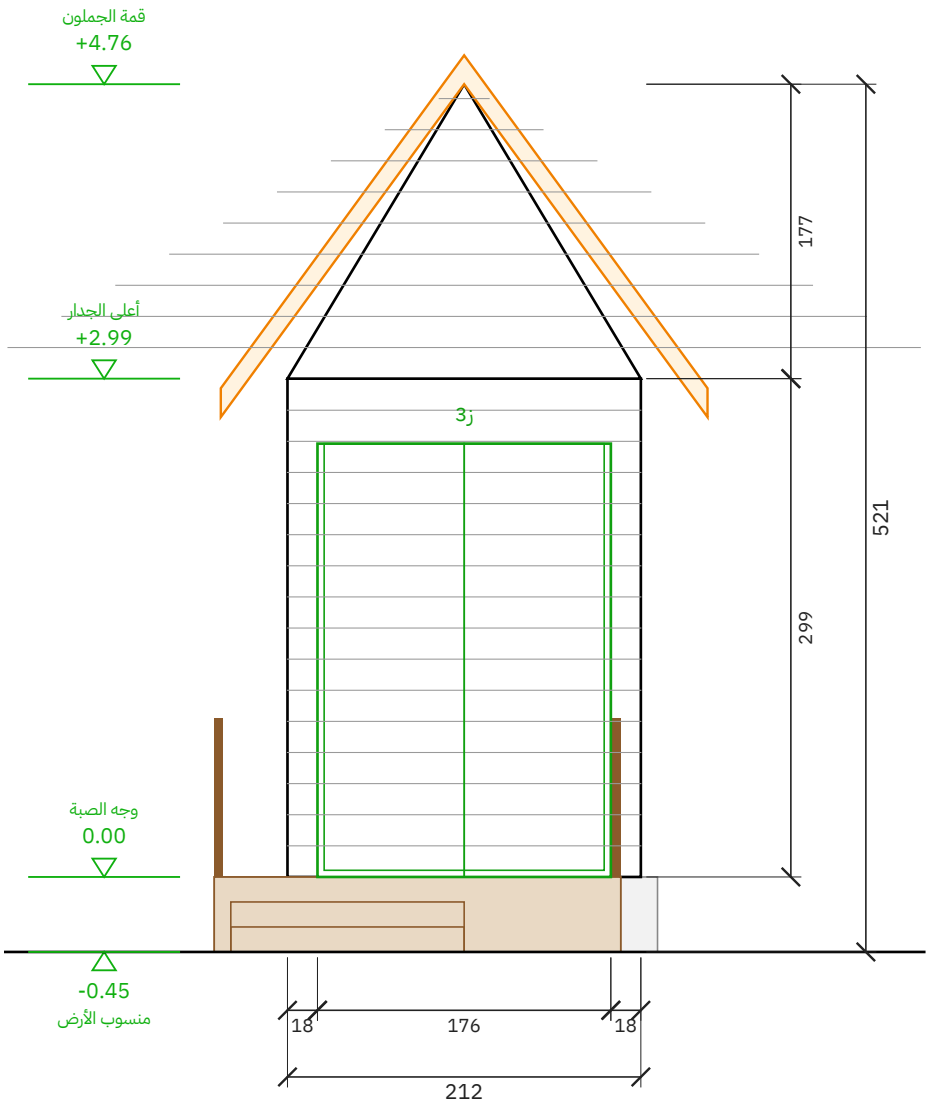

الواجهة الأمامية – المدخل


مقياس 1:50 | الوحدة: سم

المشروع / العميل	عنوان اللوحة	المقياس	التاريخ	رقم اللوحة
مصنع وتد الأخشاب Watad Wood Factory مجلس خشب منفصل 4.00 × 6.00 م بواجهة زجاج ومدخل ودورة مياه عميل – مجلس منفصل	الواجهة الأمامية والواجهة الأمامية – المدخل	1:50	2026-11-03	A-03 (3/11)

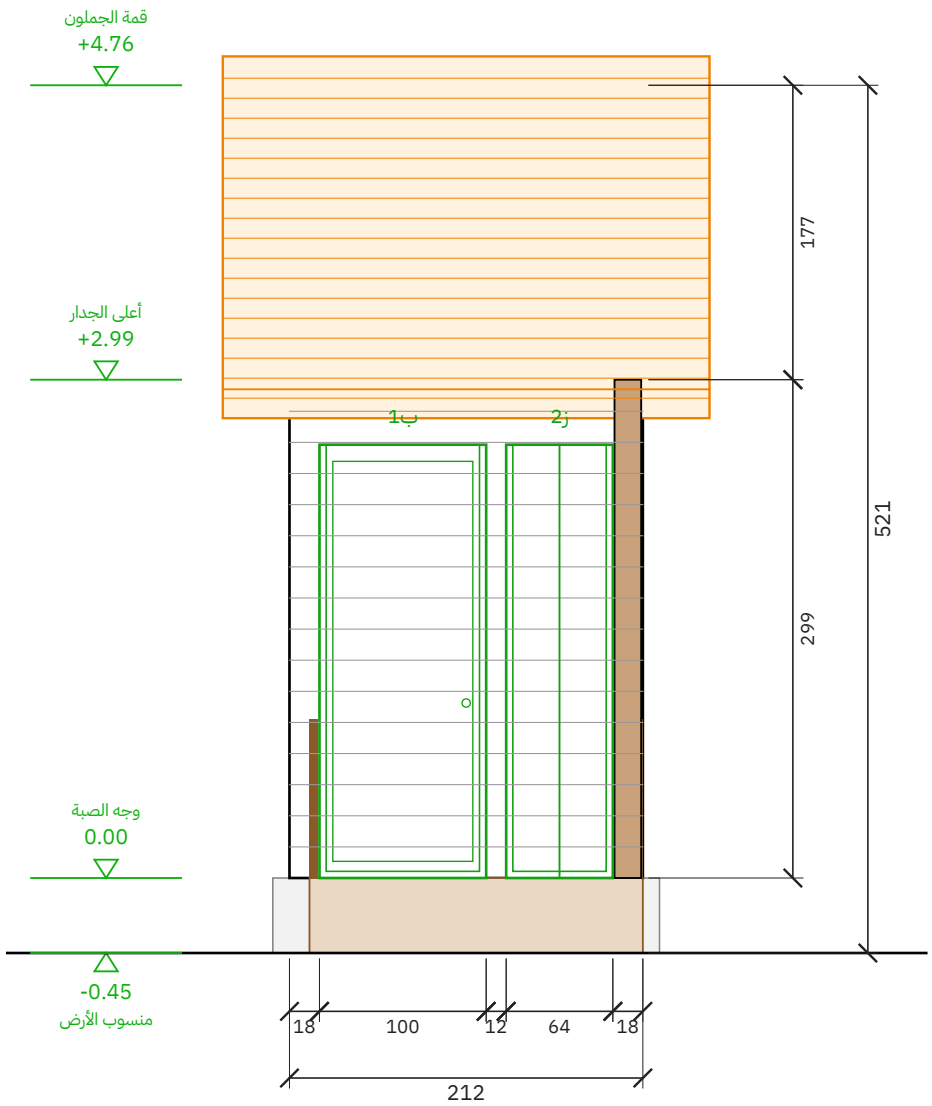

الواجهة الأمامية – المدخل

مقياس 1:50 | الوحدة: سم

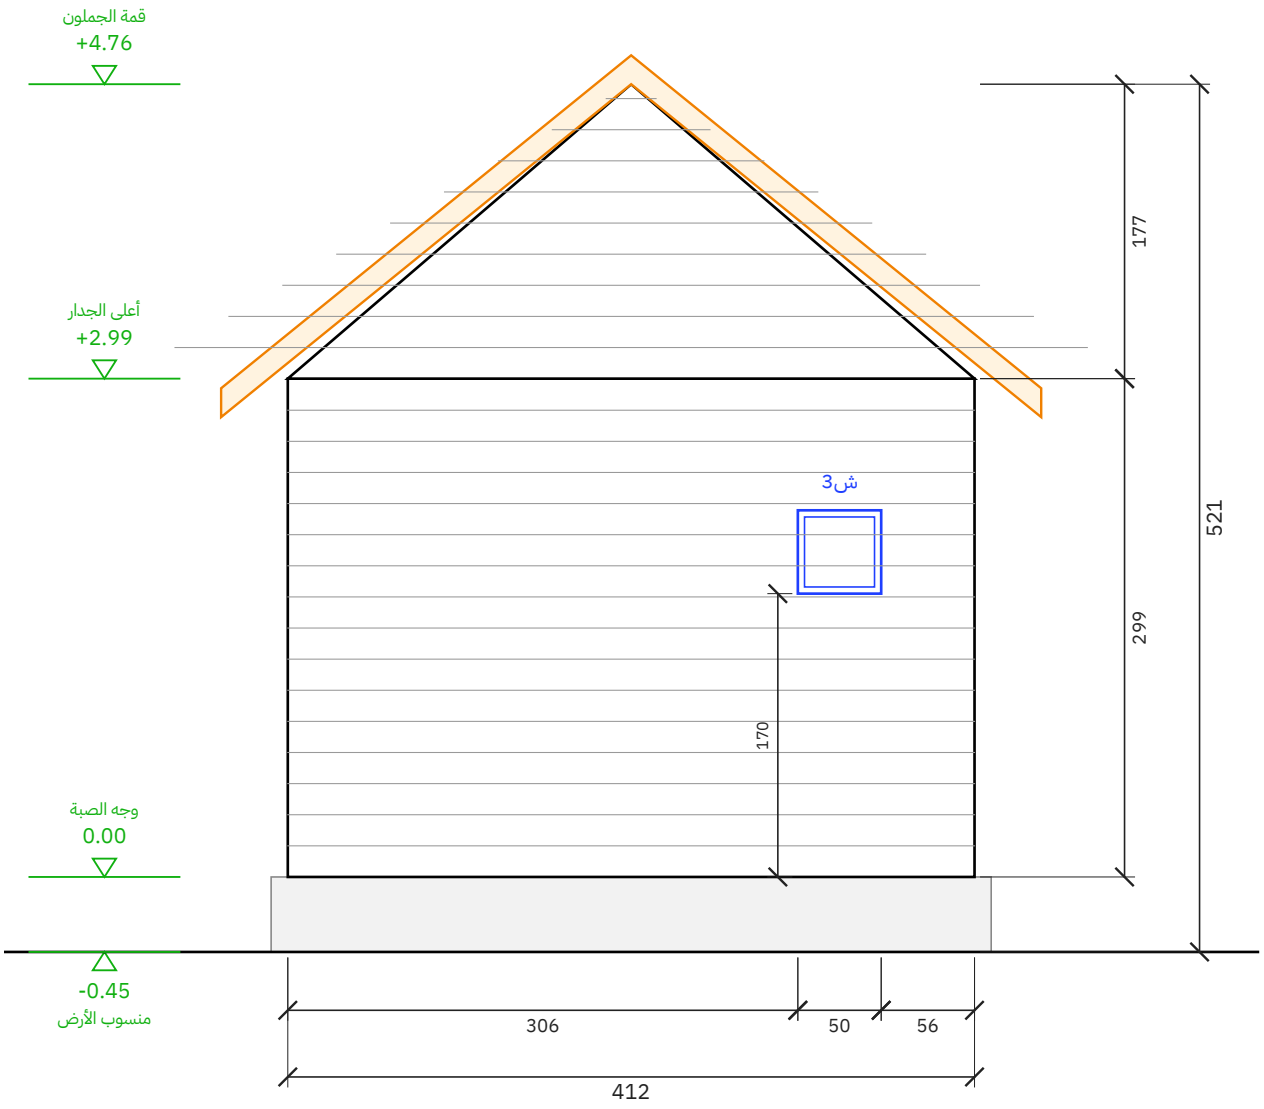


الواجهة الشرقية

مقياس 1:50 | الوحدة: سم


المشروع / العميل	عنوان اللوحة	المقياس	التاريخ	رقم اللوحة
مجلس خشب منفصل 4.00 × 6.00 م بواجهة زجاج ومدخل ودورة مياه عميل – مجلس منفصل	الواجهة الأمامية – المدخل والواجهة الشرقية	1:50	2026-11-03	A-04 (4/11)

مصنع وتد الأخشاب
Watad Wood Factory

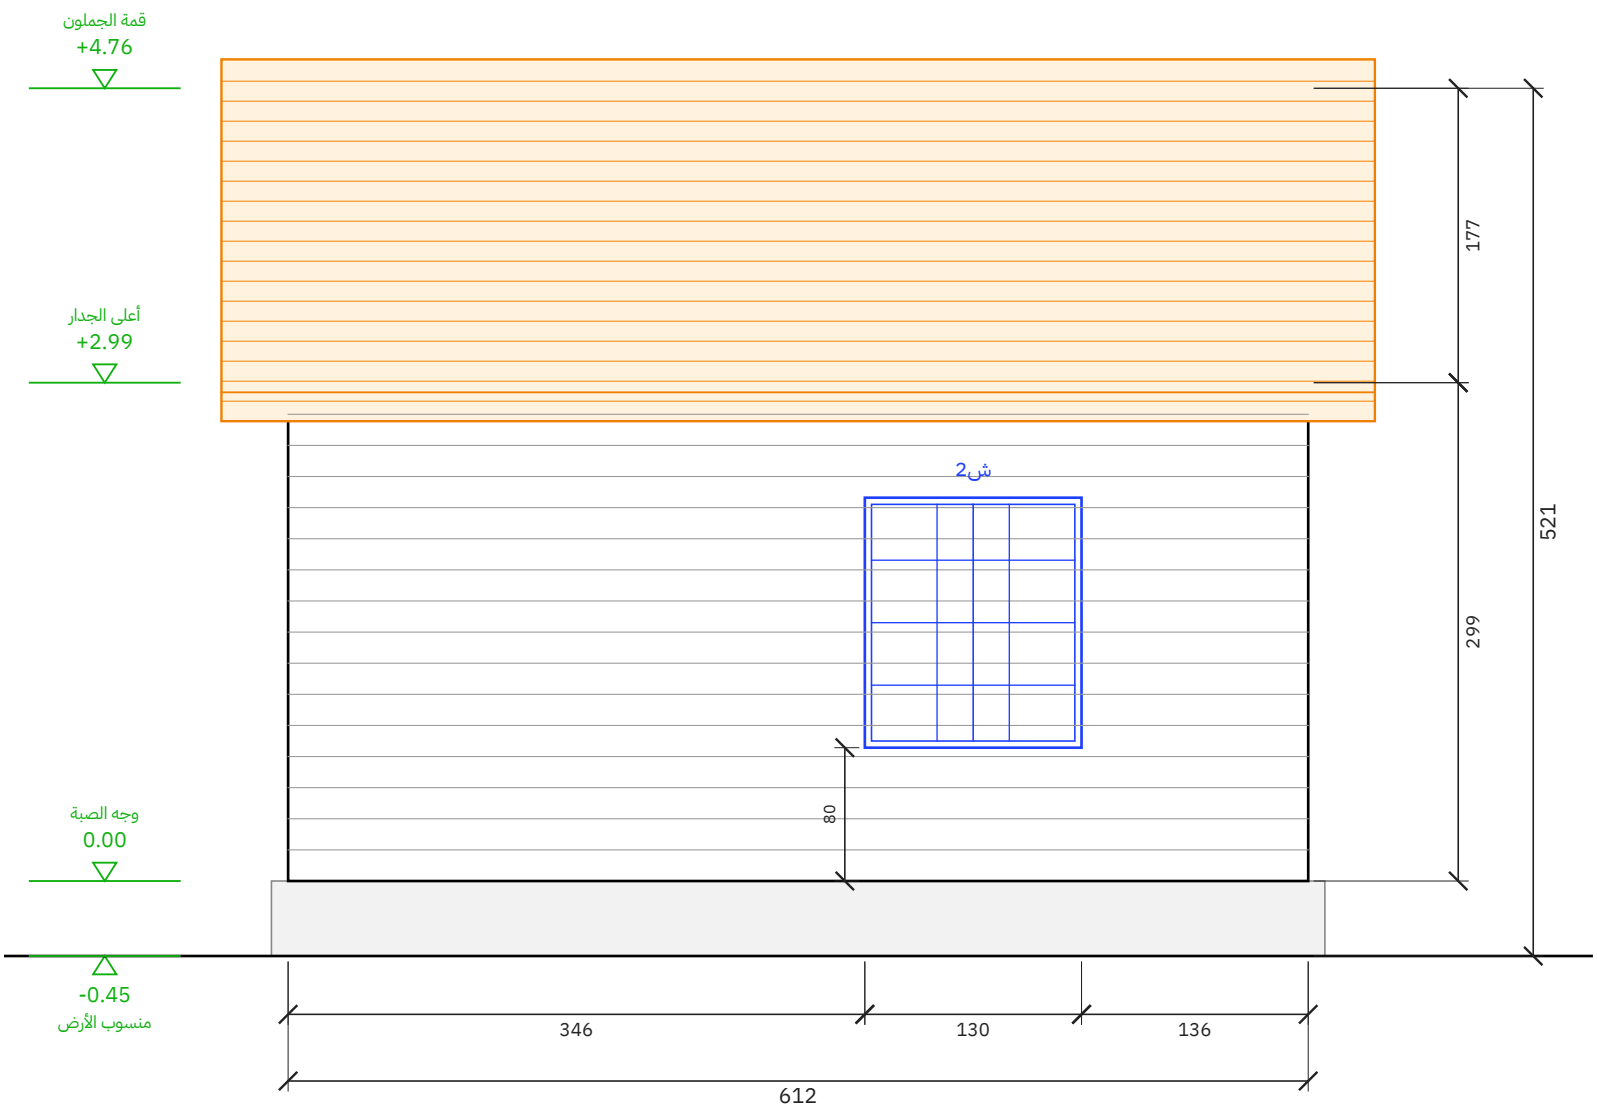

الواجهة الخلفية

مقياس 1:50 | الوحدة: سم

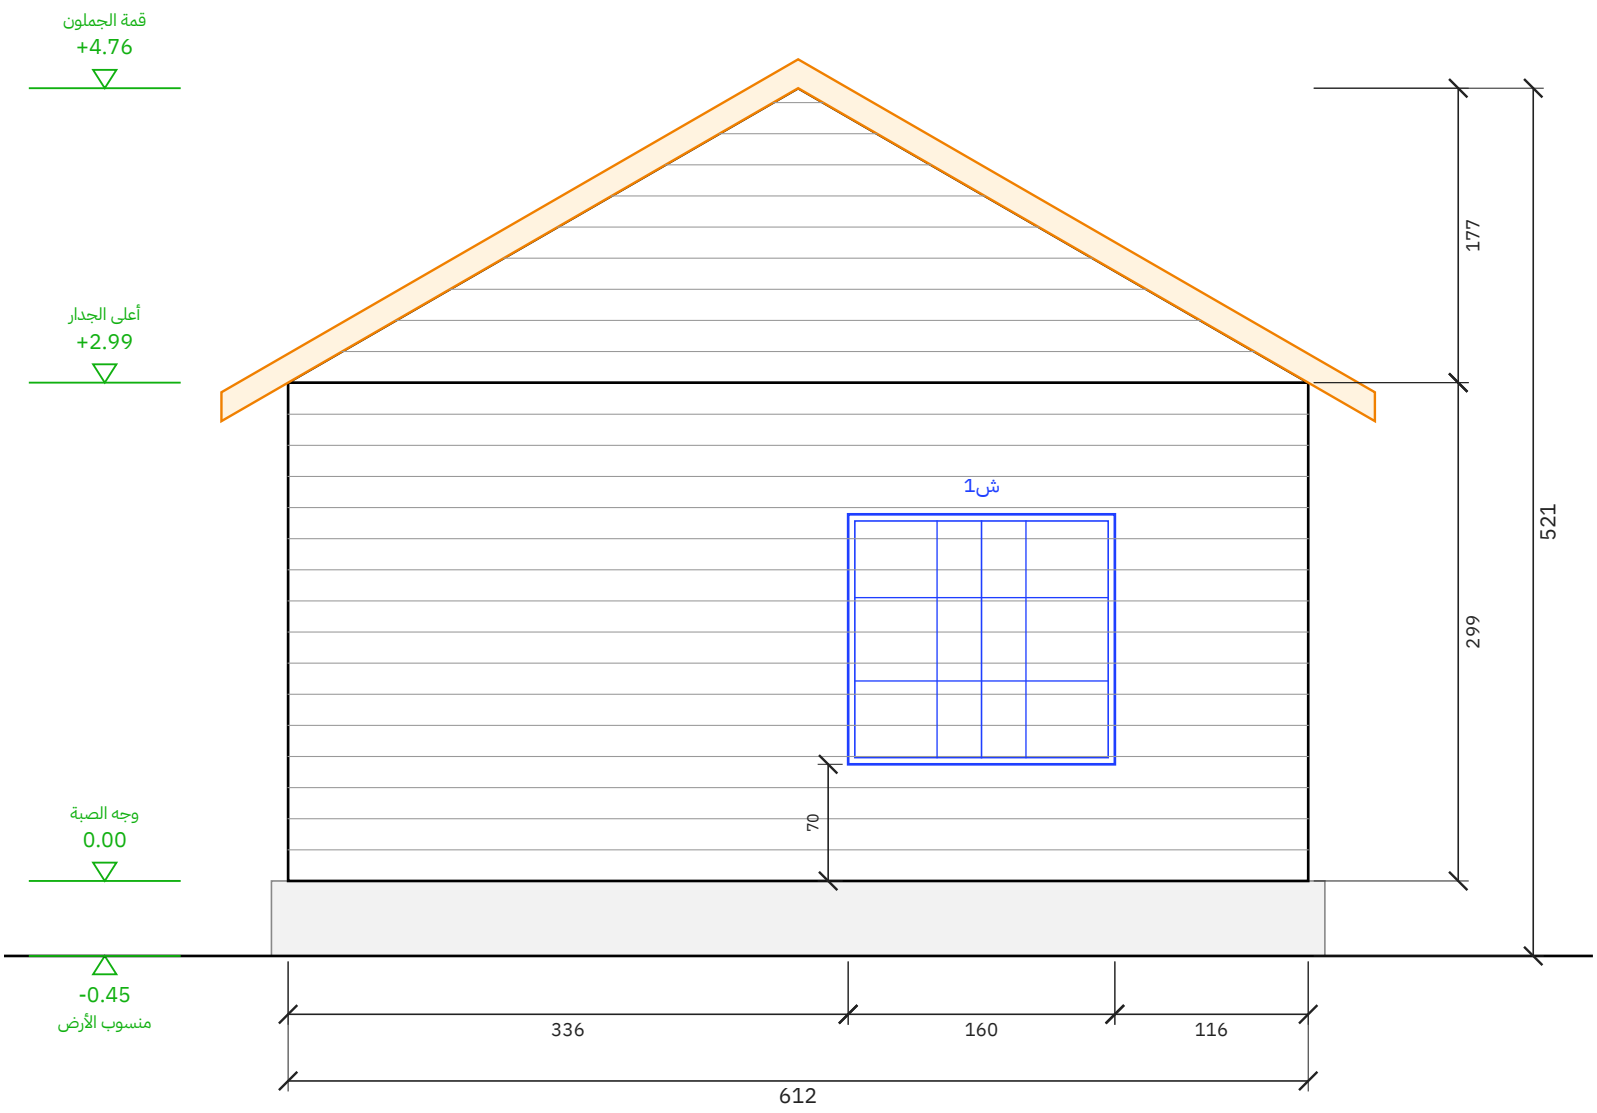

الواجهة الغربية


مقياس 1:50 | الوحدة: سم

المشروع / العميل	عنوان اللوحة	المقياس	التاريخ	رقم اللوحة
مجلس خشب منفصل 4.00 × 6.00 م بواجهة زجاج ومدخل ودورة مياه عميل – مجلس منفصل	الواجهة الخلفية والواجهة الغربية	1:50	2026-11-03	A-05 (5/11)

مصنع وتد الأخشاب
Watad Wood Factory


مسقط السقف (جملون)

رفرف 40 سم من كل جهة | مقياس 1:50

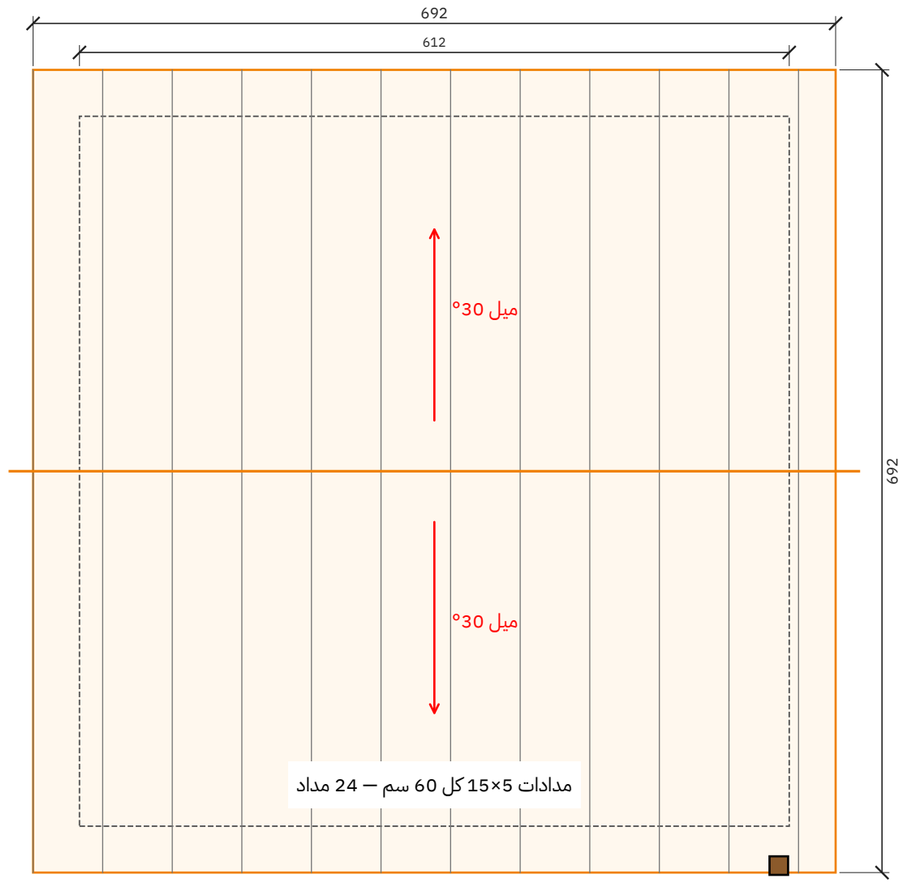


قطاع عرضي أ-أ

مقياس 1:50 | الوحدة: سم

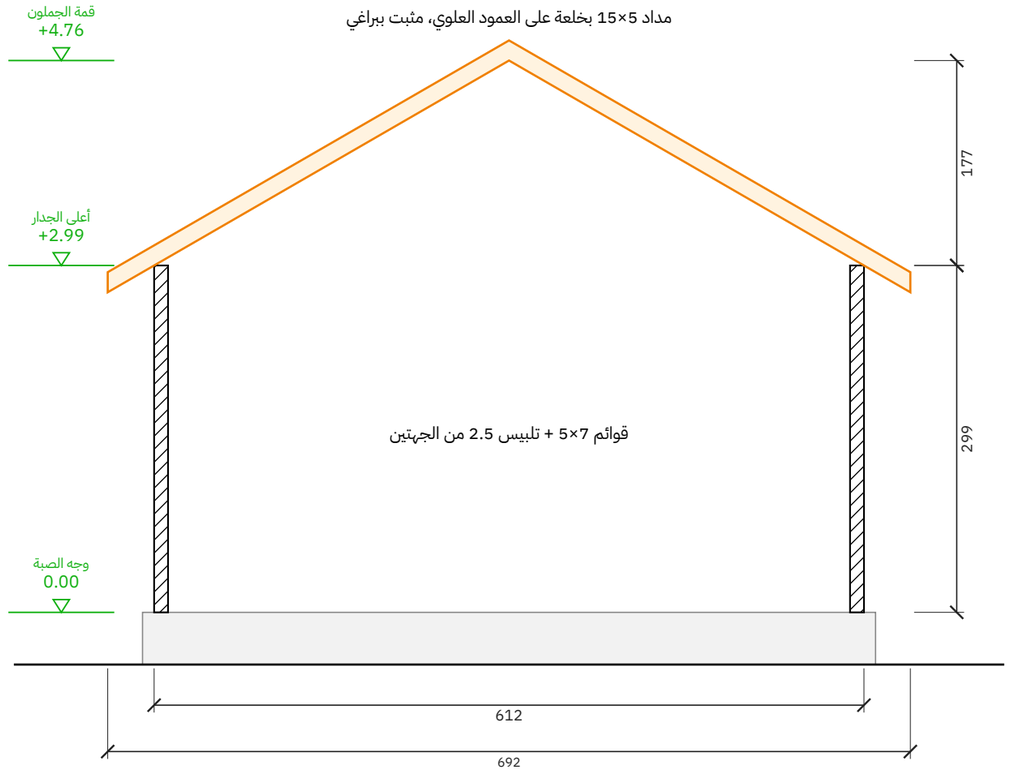

تفصيلة جلوس المداد على العلوي (1:5)

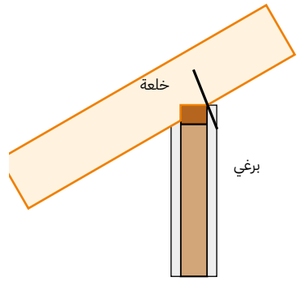


مصنع وتد الأخشاب Watad Wood Factory	المشروع / العميل مجلس خشب منفصل 4.00 × 6.00 م بواجهة زجاج ومدخل ودورة مياه عميل — مجلس منفصل	عنوان اللوحة مسقط السقف والقطاع	المقياس 1:50	التاريخ 2026-11-03	رقم اللوحة A-06 (6/11)

لقطات المنظور الخارجي


المنظور الأمامي




منظور أمامي من اليسار

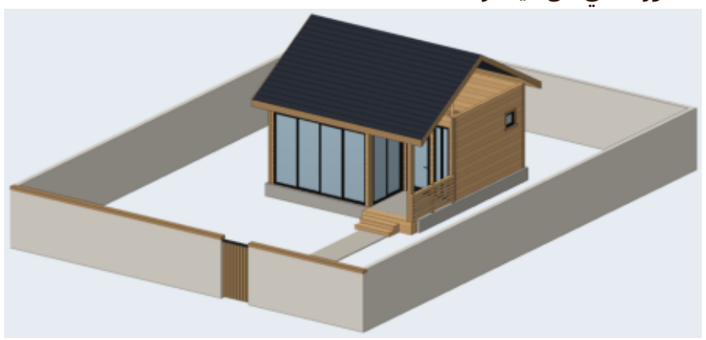

منظور أمامي من اليمين

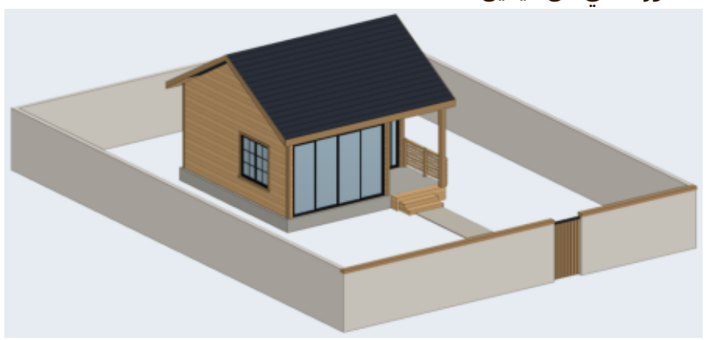


المنظور الخلفي

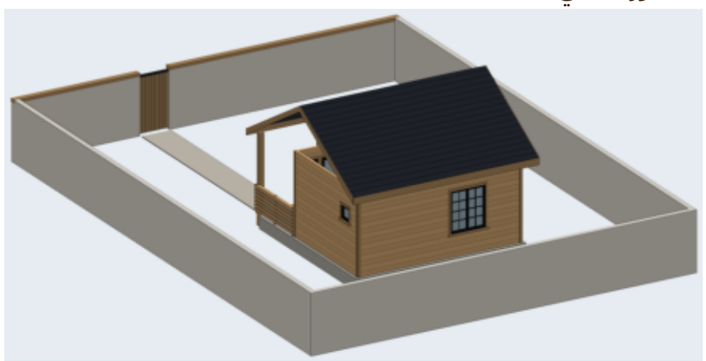

منظور خلفي من اليمين



منظر علوي

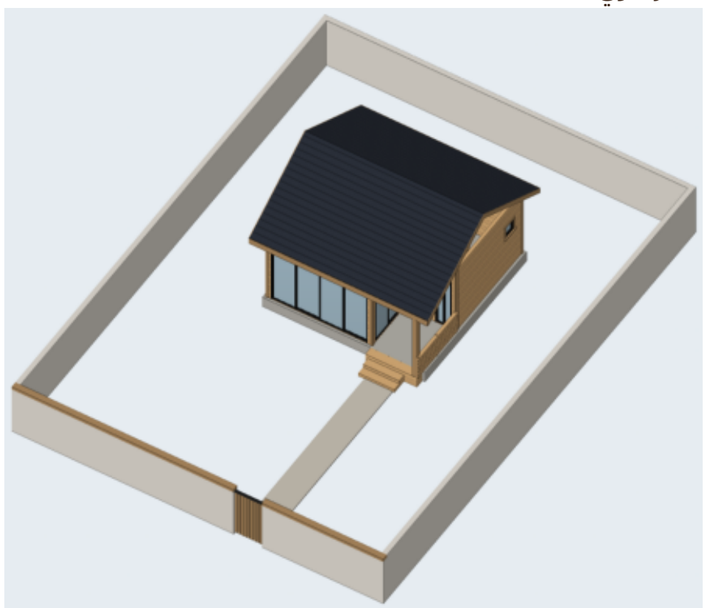

المشروع / العميل	عنوان اللوحة	المقياس	التاريخ	رقم اللوحة
مجلس خشب منفصل 4.00 × 6.00 م بواجهة زجاج ومدخل ودورة مياه **عميل – مجلس منفصل**	**لقطات المنظور**	–	**2026-11-03**	**A-09 (9/11)**

مصنع وتد الأخشاب
Watad Wood Factory

المقطع العلوي بالفرش

مقطع أفقي على ارتفاع 1.90 م — توزيع الفرش ومسار الحركة



المشروع / العميل	عنوان اللوحة	المقياس	التاريخ	رقم اللوحة
مجلس خشب منفصل 4.00 × 6.00 م بواجهة زجاج ومدخل ودورة مياه عميل — مجلس منفصل	المقطع العلوي بالفرش	—	2026-11-03	A-10 (10/11)

مصنع وتد الأخشاب
Watad Wood Factory



مصنع وتد الأخشاب

أمامي – المدخل · الخارج – نهاراً



مصنع وتد الأخشاب



مصنع وتد الأخشاب

منظر علوي – الأرض والسور · الخارج – نهاراً



مصنع وتد الأخشاب



مصنع وتد الأخشاب



مصنع وتد الأخشاب



مصنع وتد الأخشاب



مصنع وتد الأخشاب




مصنع وتد الأخشاب

جدول مساحات الموقع

البند	المقاس	المساحة (م²)
مساحة الأرض	14.00 × 19.00 م	266.0
مسطح الكوخ (البصمة)	6.12 × 6.12 م	37.5
تراس الكوخ	2.00 × 2.44 م	4.9
ممر	1.10 × 8.40 م	9.2
المسطحات الخضراء (حديقة)	الباقي	214.4

الموقع العام وتنسيق الحديقة (لاندسكيب)

الأرض 14 × 19 م = 266 م² | الأبعاد بالسنتيمتر

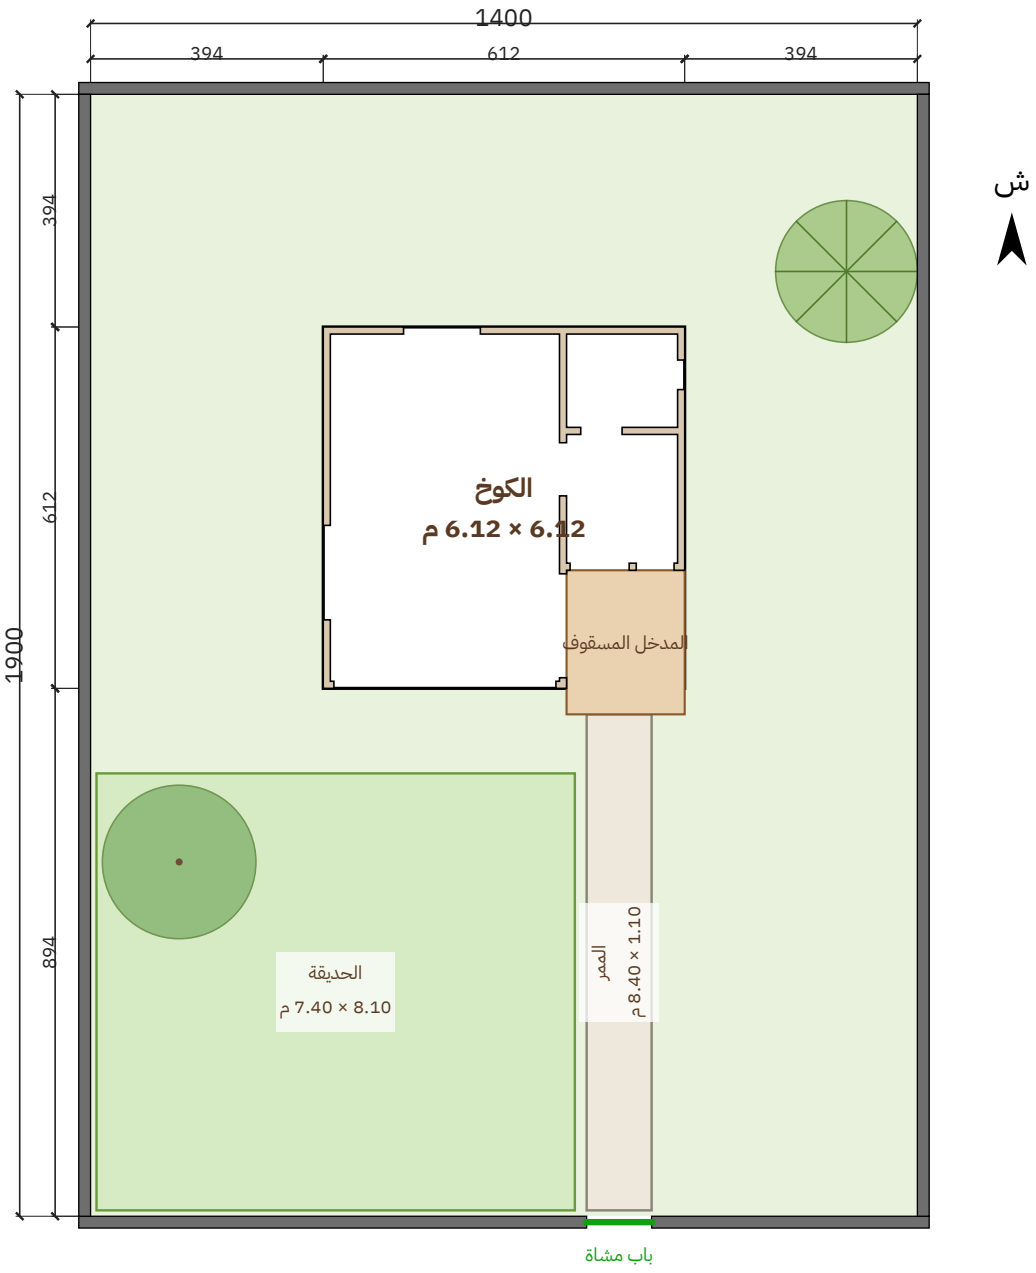

شارع عرض 14 م

المشروع / العميل	عنوان اللوحة	المقياس	التاريخ	رقم اللوحة
مجلس خشب منفصل 4.00 × 6.00 م بواجهة زجاج ومدخل ودورة مياه عميل – مجلس منفصل	الموقع العام واللاندسكيب	1:200	2026-11-03	A-01 (1/11)

مصنع وتد الأخشاب
Watad Wood Factory

جدول مقاسات الأبواب والشبابيك


مقاس الفتحة الصافي في الجدار - الوحدة: سم

الرمز	النوع	العرض (سم)	الارتفاع (سم)	ارتفاع الجلسة (سم)	العدد	الموقع
ب1	باب	100	260	-	1	الأمامية — المدخل
ب2	باب	90	220	-	1	المدخل — المجلس
ب3	باب	70	210	-	1	دورة المياه
ز1	باب	376	260	-	1	الأمامية
ز2	باب	64	260	-	1	الأمامية — المدخل
ز3	باب مزدوج	176	260	-	1	الأمامية — المدخل
ش1	شباك	160	150	70	1	الغربية
ش2	شباك	130	150	80	1	الخلفية
ش3	شباك	50	50	170	1	الشرقية

الإجمالي: أبواب 6 - شبابيك 3

المنظور ثلاثي الأبعاد والمواد

النمط: خشب طبيعي + قرميد فحمي — رندر واقعي بخامات حقيقية

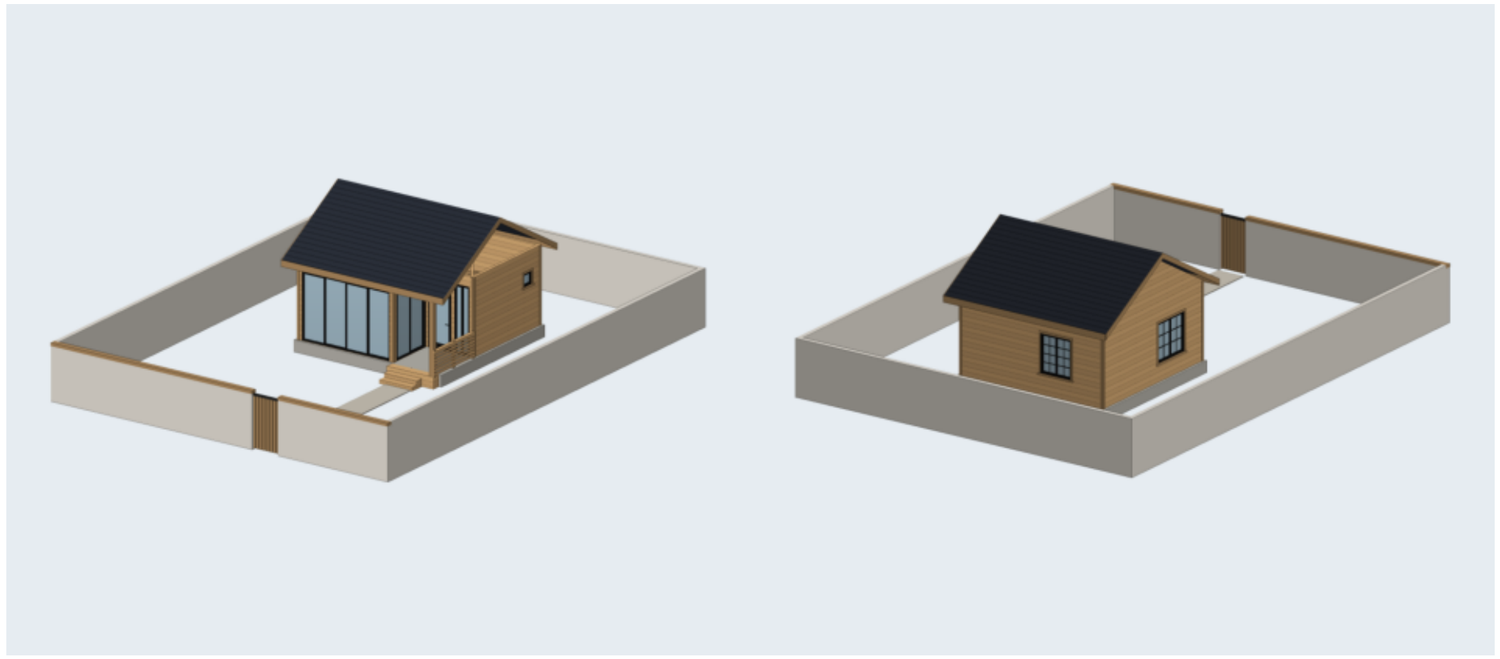

جدول المواد والألوان

الخشب / الصبغة

خشب طبيعي فاتح (بدون صبغة)

القرميد

قرميد فحمي / أسود مزرق

الزجاج

زجاج شفاف

إطارات الشبابيك والأبواب

إطار ألمنيوم أسود

الكنار والزوايا

نفس الصبغة أغمق درجة


الصبة

خرسانة 45 سم


الدربزين: ألواح أفقية متقاربة (عصري)

تقسيم الشبابيك: شبكة | الباب الرئيسي: زجاج بتقسيمات (فرنسي)

أنواع الدربزين المعتمدة (من مشاريع المصنع)

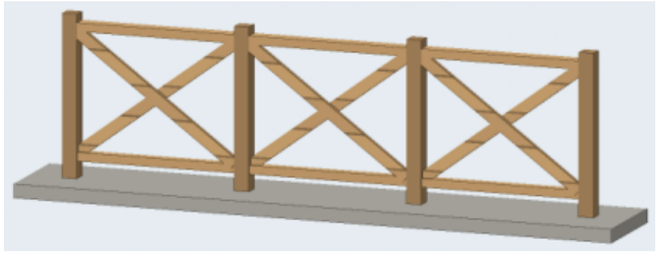

تقاطع X (صورة 5)

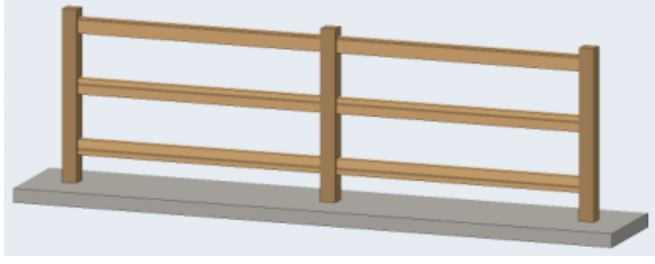

3 مرابيع أفقية (صورة 2)



قوائم رأسية متقاربة (صورة 1)

المشروع / العميل	عنوان اللوحة	المقياس	التاريخ	رقم اللوحة
مجلس خشب منفصل 4.00 × 6.00 م بواجهة زجاج ومدخل ودورة مياه **عميل – مجلس منفصل**	**المنظور والمواد**	–	**2026-11-03**	**A-11 (11/11)**

مصنع وتد الأخشاب
Watad Wood Factory

جدول المساحات وبيانات المشروع

بيانات المشروع

البند	البيان
المشروع	مجلس خشب منفصل 4.00 × 6.00 م بواجهة زجاج ومدخل ودورة مياه
العميل	عميل — مجلس منفصل
الموقع	—
الاستخدام	مجلس ضيافة
التاريخ	2026-11-03
نظام البناء	هيكل خشب 5×7 + تلبيس 2.5 سم من الجهتين
السقف	جملون 30° — قرميد معدني

جدول المساحات

م	الفراغ	الأبعاد (م)	المساحة (م2)
1	المجلس	3.88 × 5.88	22.81
2	المدخل والمغسلة	1.88 × 2.18	4.10
3	دورة مياه	1.88 × 1.58	2.97
	المساحة الصافية الداخلية		**29.88**
	المدخل المسقوف	**2.00 × 2.44**	**4.88**
	المساحة الإجمالية المبنية	**6.12 × 6.12**	**37.45**
	المساحة الكلية (المبنية + التراس)		**42.33**