

المسقط الأفقي مع الفرش

الأبعاد بالسنتيمتر - الجدران: قوائم 7×5 + تلبيس 2.5 من الجهتين (12 سم)

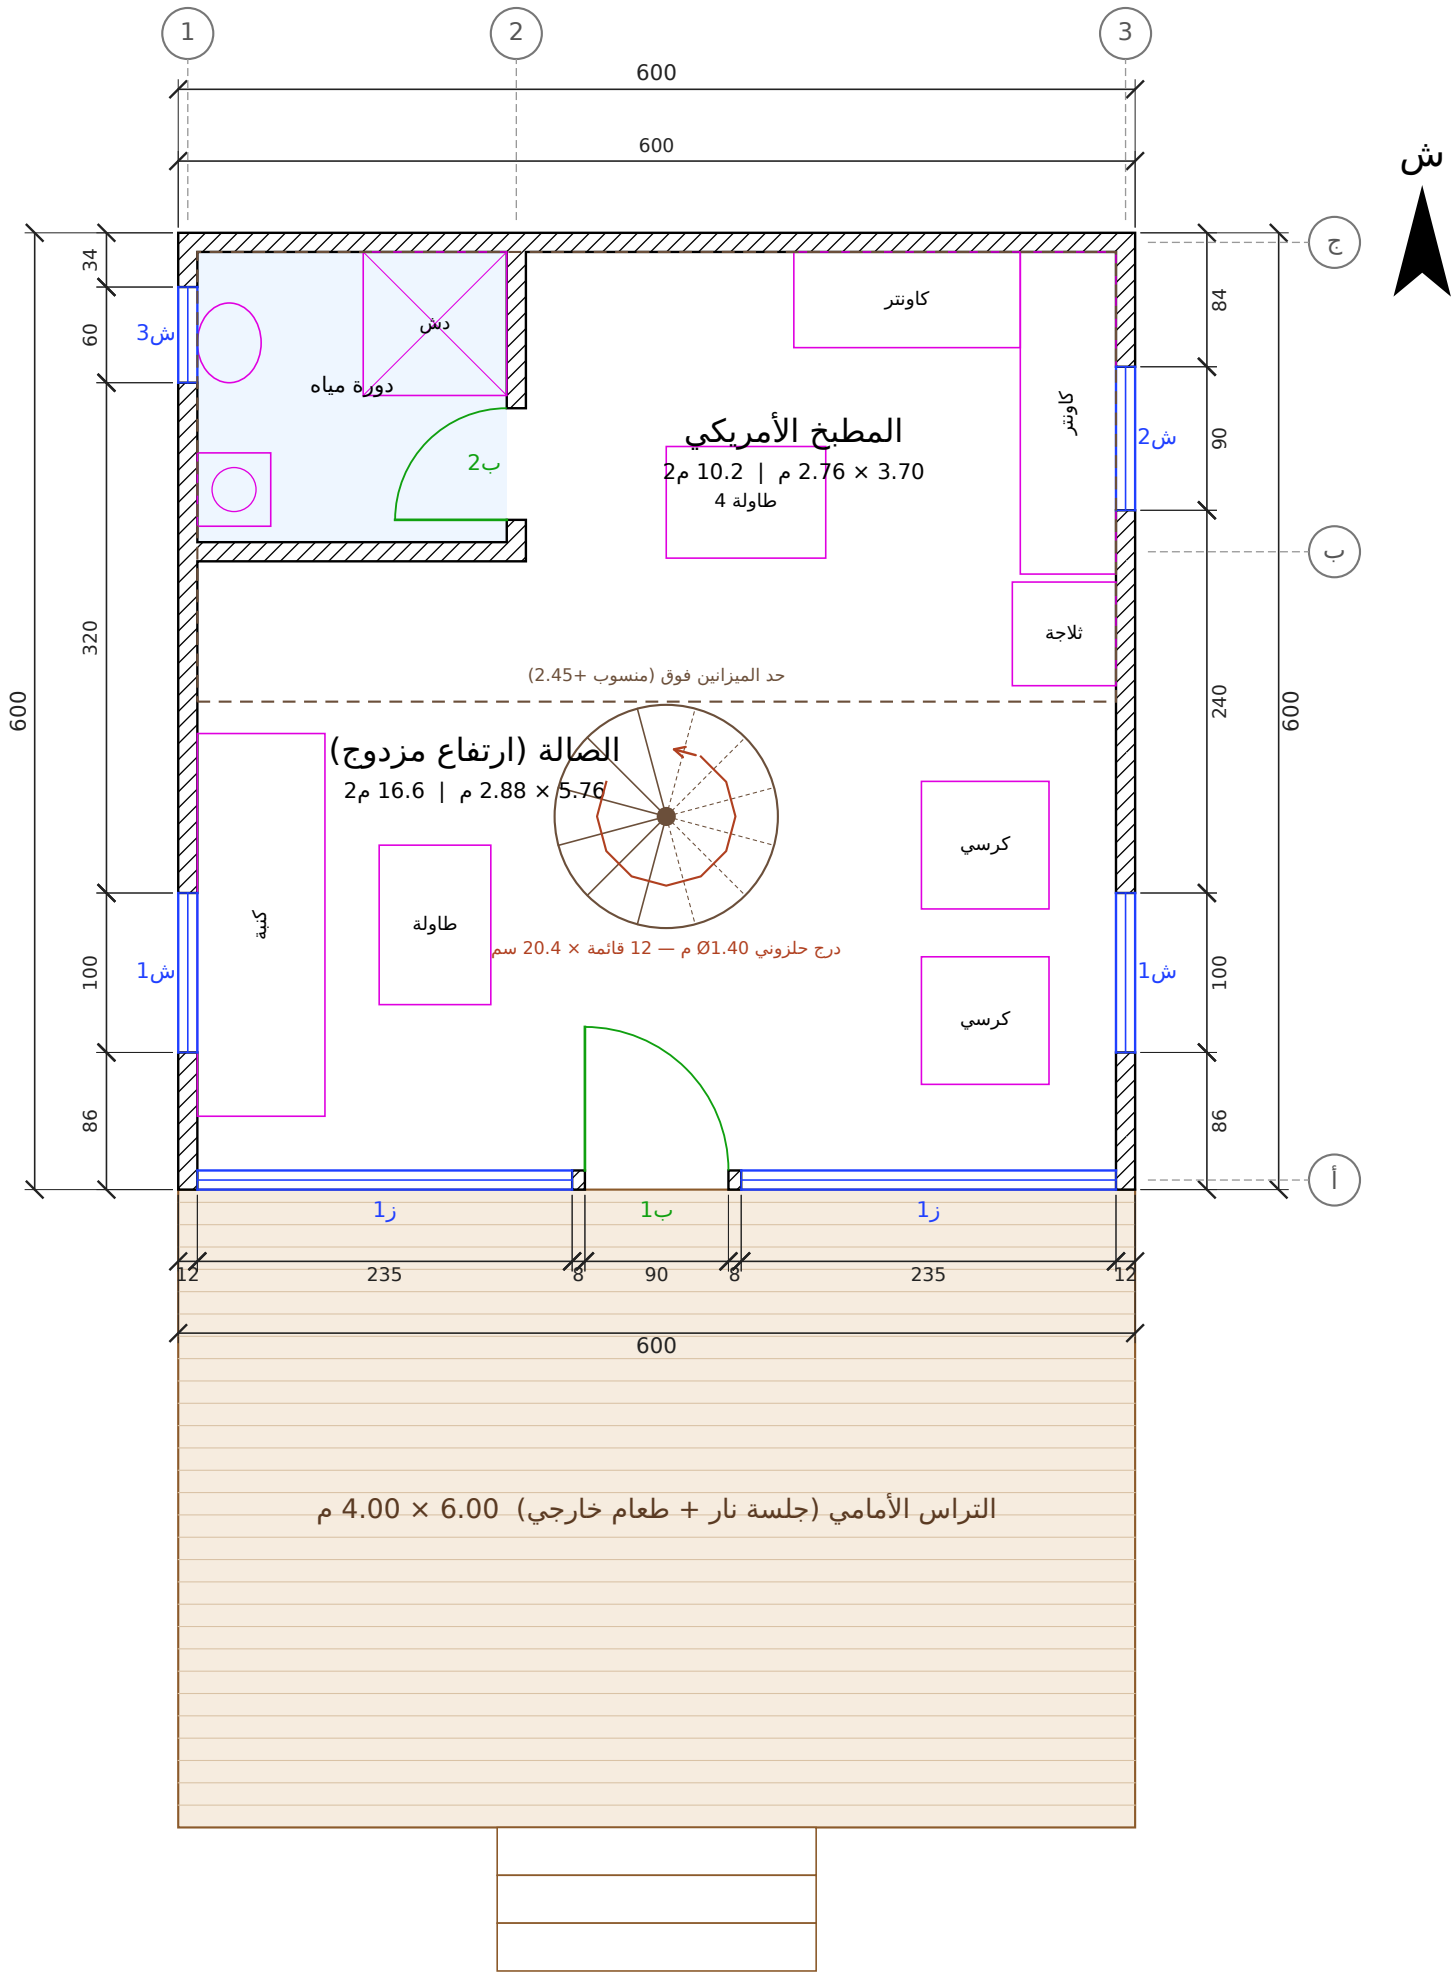


مصنع وتد الأخشاب Watad Wood Factory	المشروع / العميل كوخ A-frame بواجهة زجاج كاملة + ميزانين — 6 × 6 = 36 م² عميل — A-frame 6×6	عنوان اللوحة المسقط الأفقي	المقياس 1:50	التاريخ 2026-10-20	رقم اللوحة A-01 (1/10)

مسقط الميزانين (نص الدور) — غرفة النوم
منسوب أرضية الميزانين +2.45 | الأبعاد بالسنتيمتر

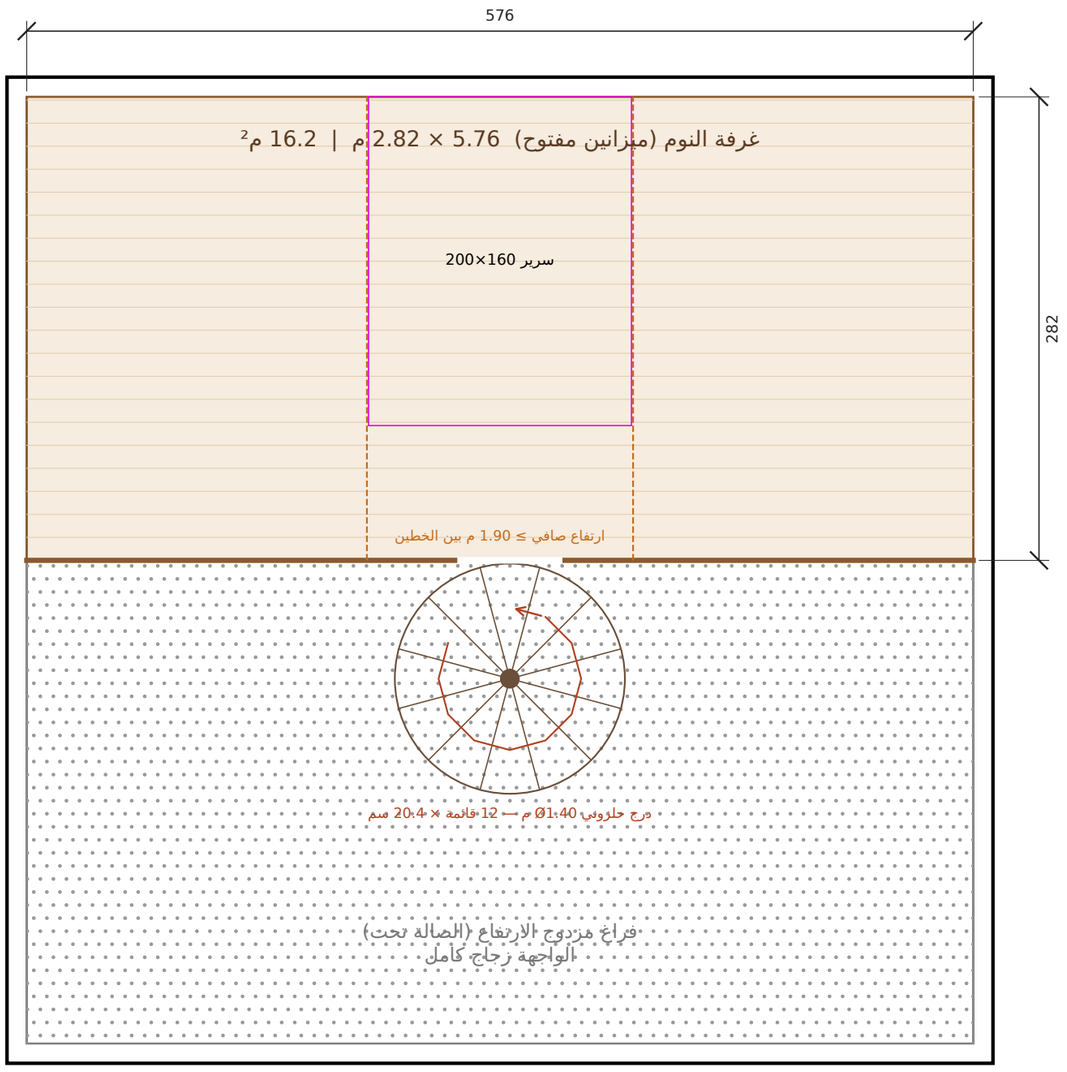


المشروع / العميل	عنوان اللوحة	المقياس	التاريخ	رقم اللوحة
كوخ A-frame بواجهة زجاج كاملة + ميزانين — 6 × 6 = 36 م² **عميل — A-frame 6×6**	**مسقط الميزانين**	**1:50**	**2026-10-20**	**A-02 (2/10)**

مصنع وتد الأخشاب
Watad Wood Factory

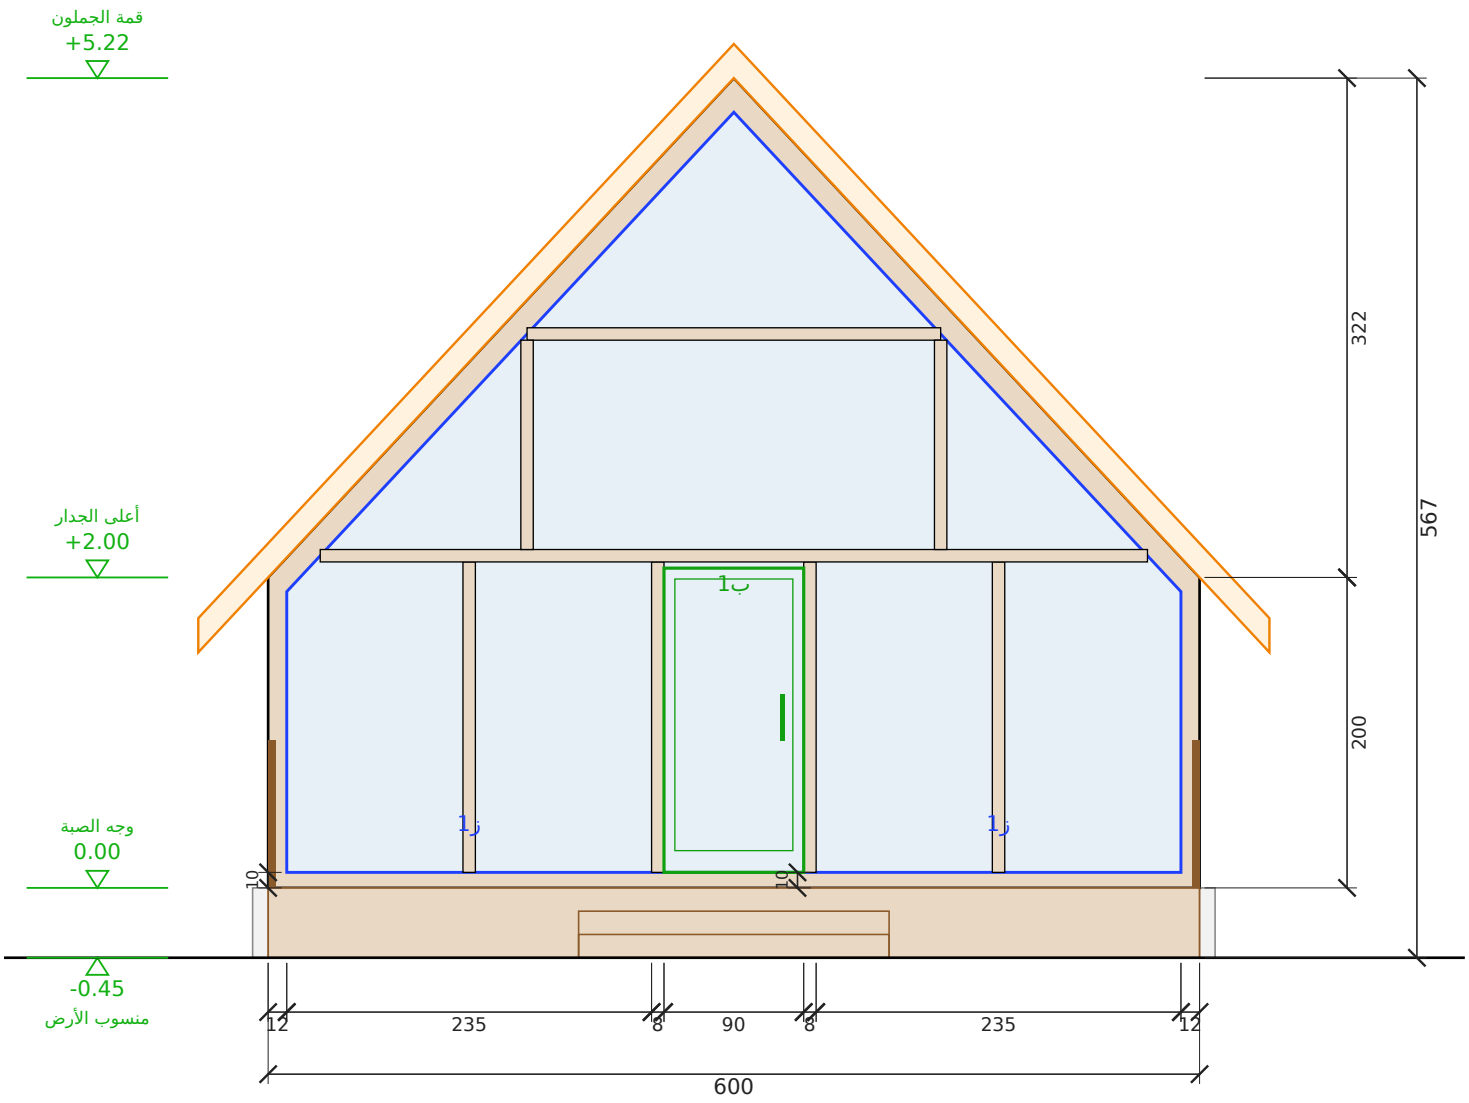

الواجهة الأمامية (زجاج كامل)


مقياس 1:50 | الوحدة: سم

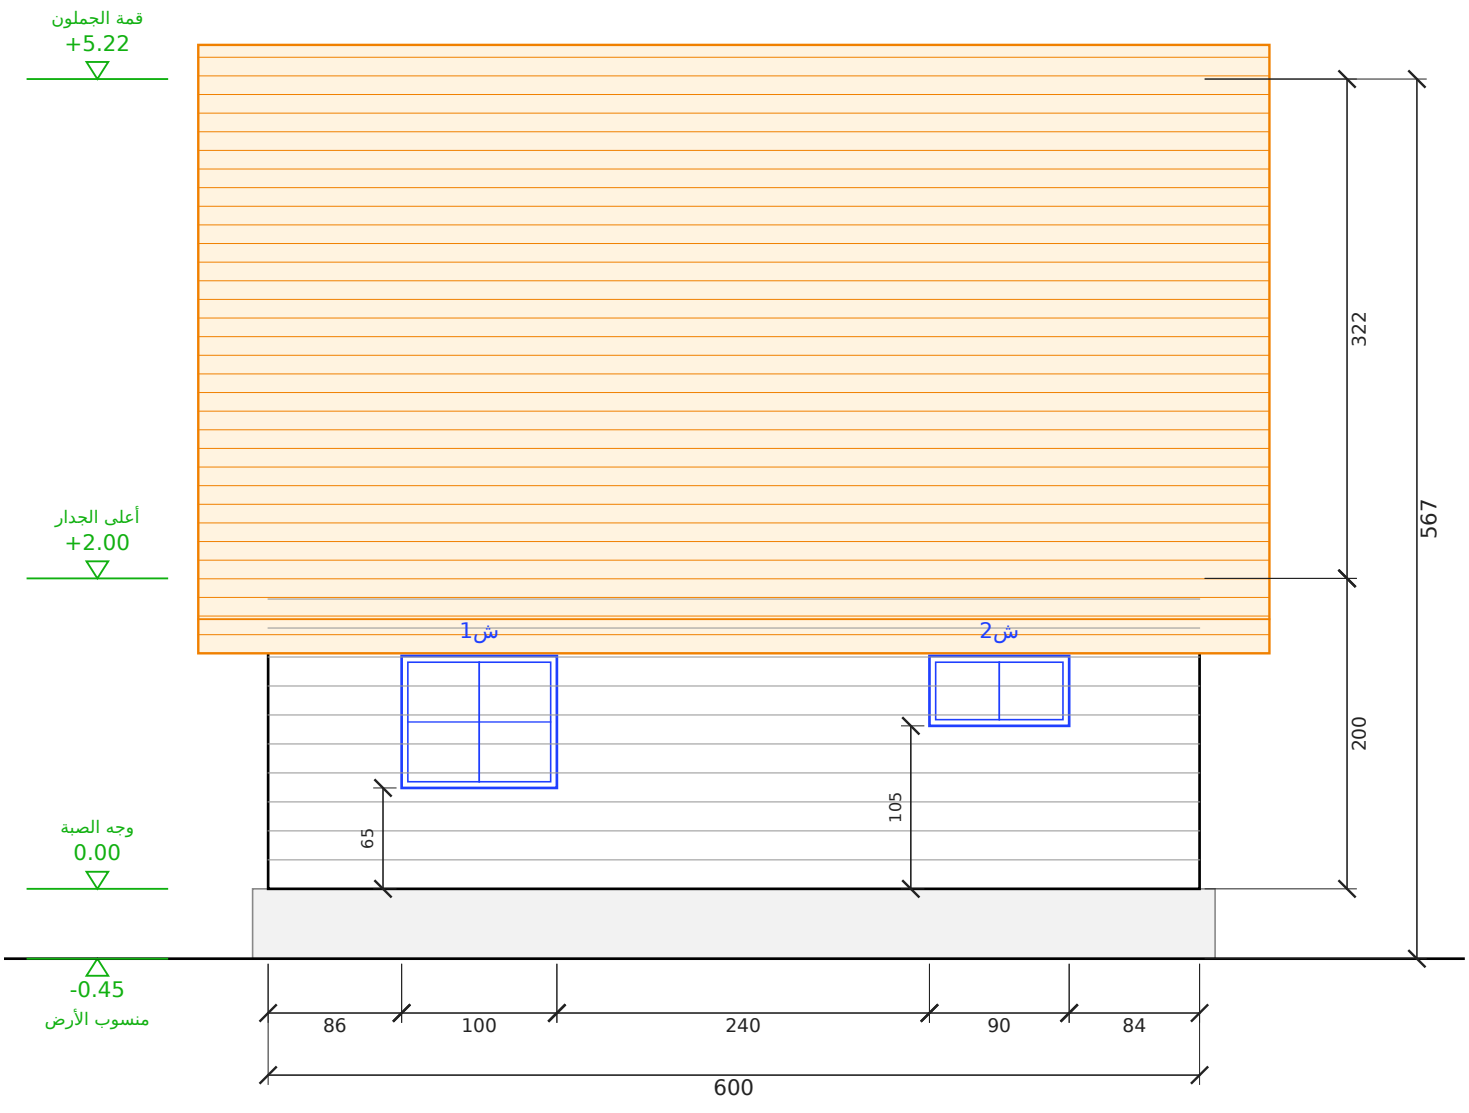

الواجهة الشرقية


مقياس 1:50 | الوحدة: سم

المشروع / العميل	عنوان اللوحة	المقياس	التاريخ	رقم اللوحة
مصنع وتد الأخشاب Watad Wood Factory كوخ A-frame بواجهة زجاج كاملة + ميزانين — 6 × 6 = 36 م² عميل — A-frame 6×6	الواجهة الأمامية (زجاج كامل) والواجهة الشرقية	1:50	2026-10-20	A-03 (3/10)

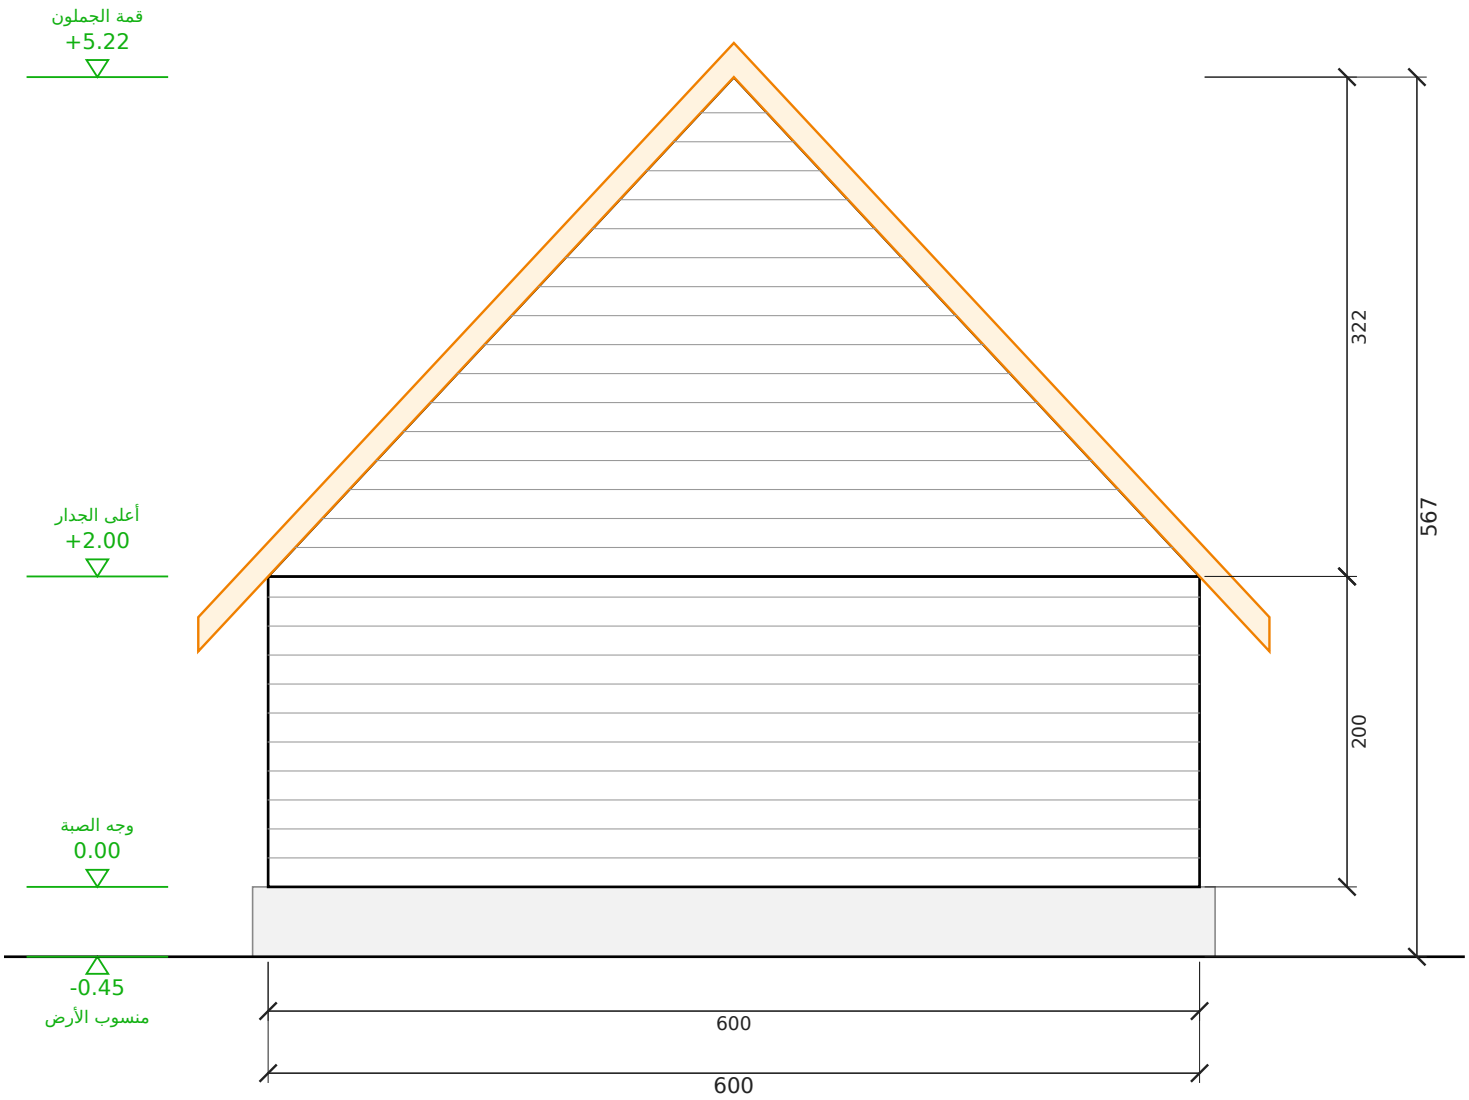

الواجهة الخلفية

مقياس 1:50 | الوحدة: سم

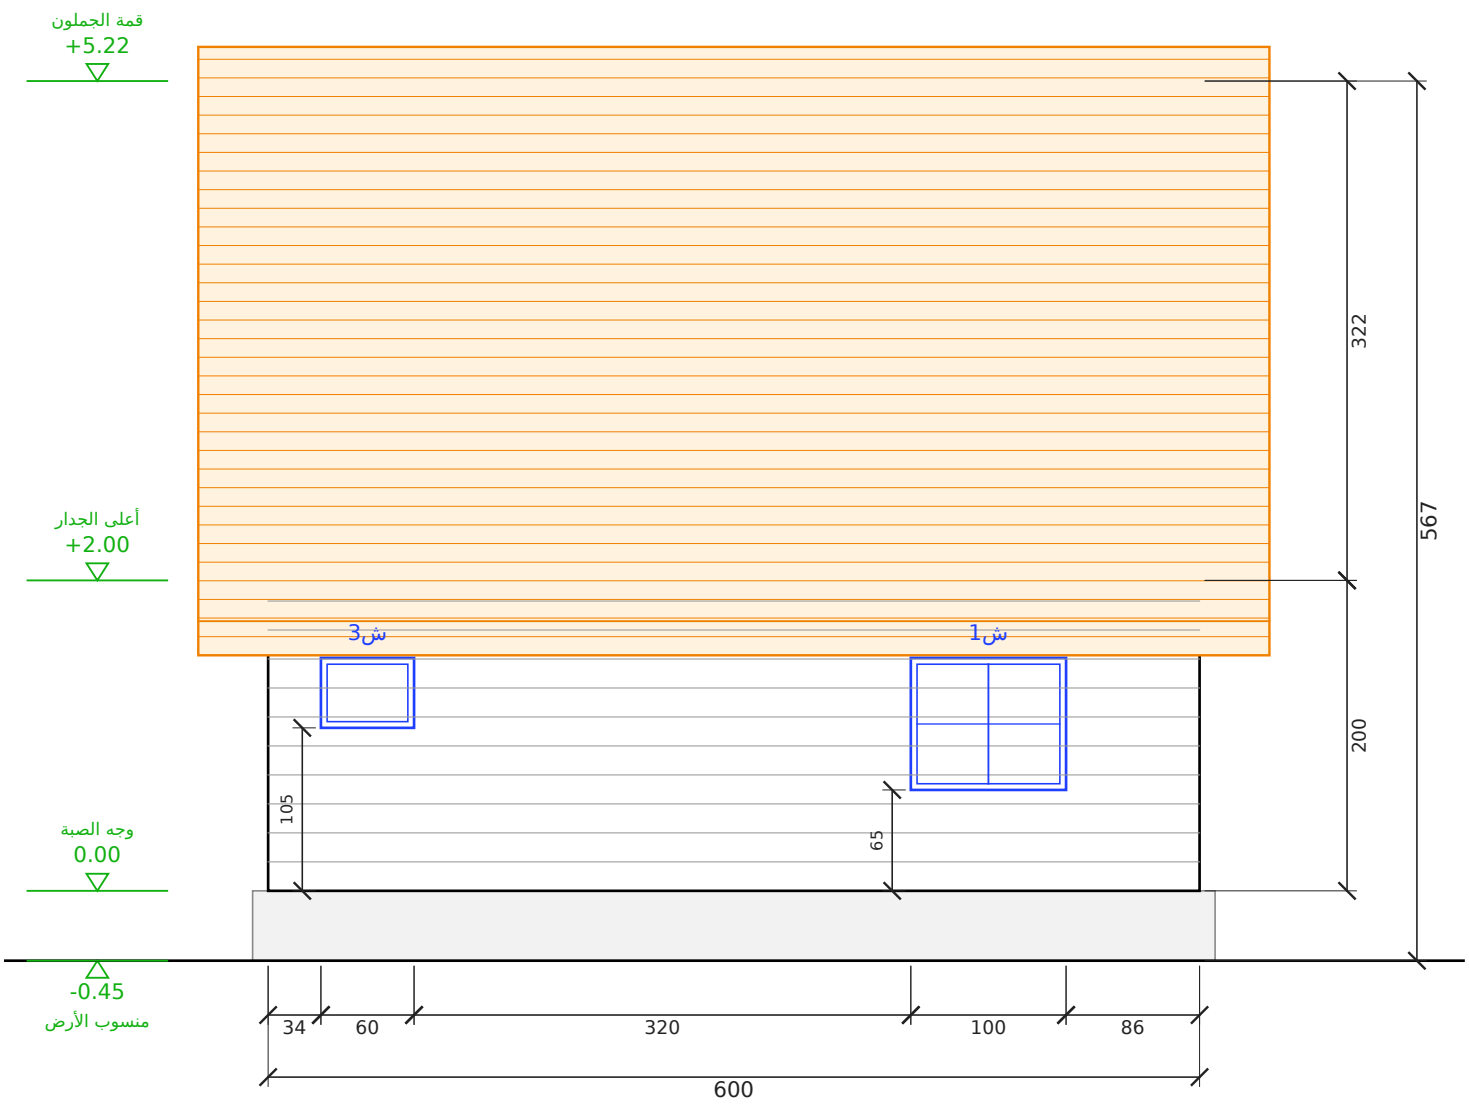


الواجهة الغربية


مقياس 1:50 | الوحدة: سم

المشروع / العميل	عنوان اللوحة	المقياس	التاريخ	رقم اللوحة
مصنع وتد الأخشاب Watad Wood Factory **كوخ A-frame بواجهة زجاج كاملة + ميزانين — 6 × 6 = 36 م²** **عميل — A-frame 6×6**	**الواجهة الخلفية والواجهة الغربية**	**1:50**	**2026-10-20**	**A-04 (4/10)**


مسقط السقف (جملون)
رفرف 45 سم من كل جهة | مقياس 1:50

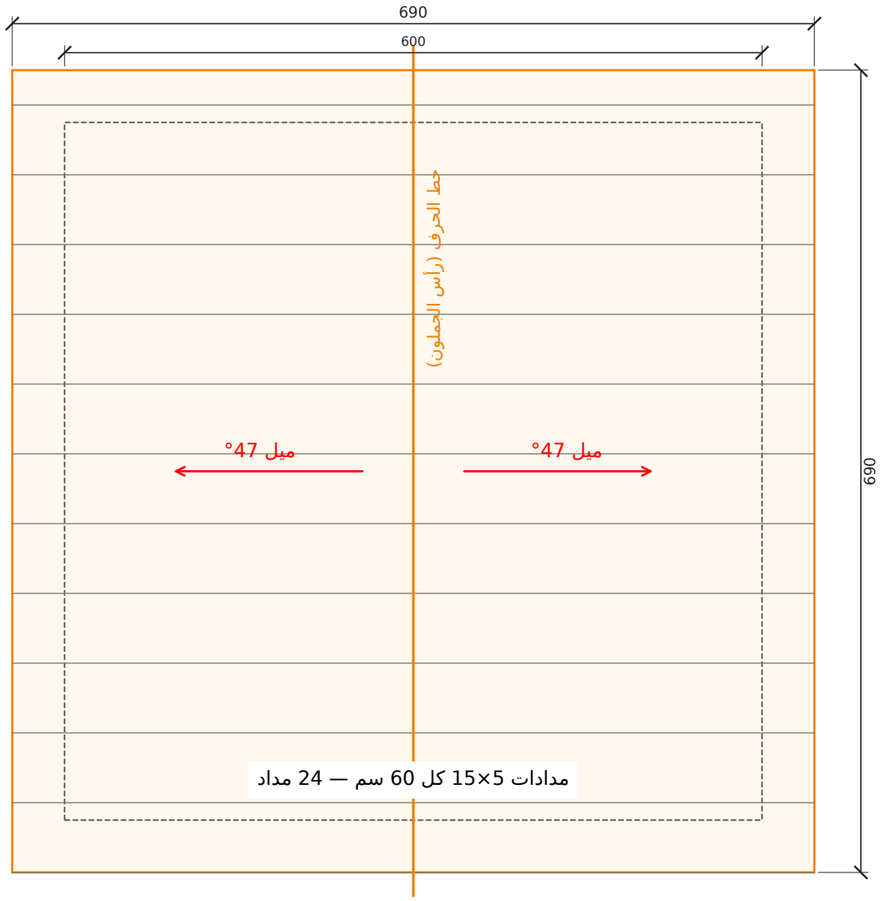

قطاع عرضي أ-أ
مقياس 1:50 | الوحدة: سم

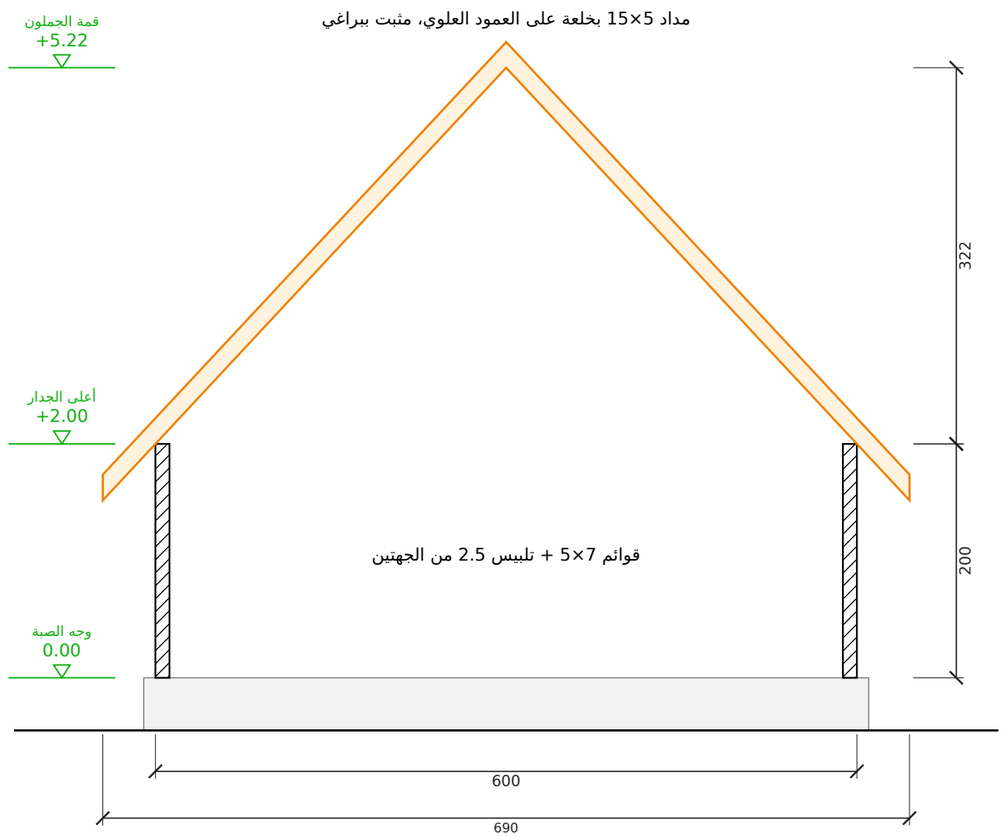

تفصيلة جلوس المداد على العلوي (1:5)

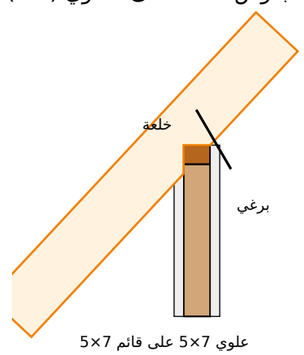

مصنع وتد الأخشاب Watad Wood Factory	المشروع / العميل **كوخ A-frame بواجهة زجاج كاملة + ميزانين — 6 × 6 = 36 م²** **عميل — A-frame 6×6**	عنوان اللوحة **مسقط السقف والقطاع**	المقياس **1:50**	التاريخ **2026-10-20**	رقم اللوحة **A-05 (5/10)**

جدول مقاسات الأبواب والشبابيك
مقاس الفتحة الصافي في الجدار - الوحدة: سم

الرمز	النوع	العرض (سم)	الارتفاع (سم)	ارتفاع الجلسة (سم)	العدد	الموقع
ب1	باب	90	210	-	1	الأمامية (زجاج كامل)
ب2	باب	70	205	-	1	دورة المياه
ز1	شباك	235	200	10	2	الأمامية (زجاج كامل) 2
ش1	شباك	100	85	65	2	الشرقية - الغربية
ش2	شباك	90	45	105	1	الشرقية
ش3	شباك	60	45	105	1	الغربية

الإجمالي: أبواب 2 - شبابيك 6

جدول المساحات وبيانات المشروع

بيانات المشروع

البند	البيان
المشروع	كوخ A-frame بواجهة زجاج كاملة + ميزانين — 6 × 6 = 36 م²
العميل	عميل — A-frame 6×6
الموقع	—
الاستخدام	استراحة / سكن
التاريخ	2026-10-20
نظام البناء	هيكل خشب 5×7 + تلبيس 2.5 سم من الجهتين
السقف	جملون 47° — قرميد معدني

جدول المساحات


م	الفراغ	الأبعاد (م)	المساحة (م2)
1	الصالة (ارتفاع مزدوج)	5.76 × 2.88	16.59
2	المطبخ الأمريكي	3.70 × 2.76	10.21
3	دورة مياه	1.94 × 1.82	3.53
	المساحة الصافية الداخلية		**30.33**
	التراس المسقوف	**6.00 × 4.00**	**24.00**
	المساحة الإجمالية المبنية	**6.00 × 6.00**	**36.00**

لقطات المنظور الخارجي

المنظور الأمامي




منظور أمامي من اليسار

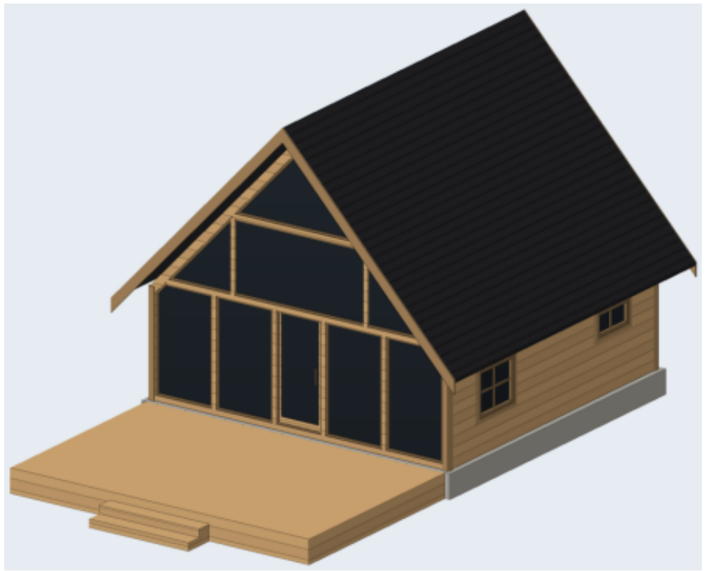

منظور أمامي من اليمين




المنظور الخلفي

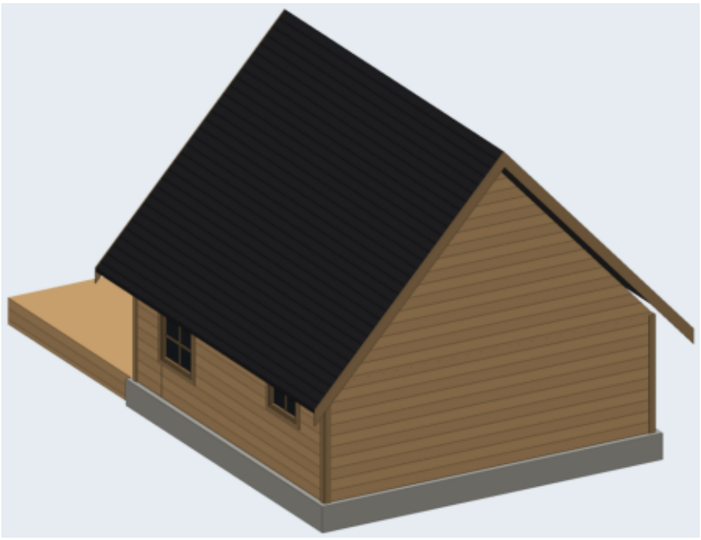

منظور خلفي من اليمين



منظر علوي

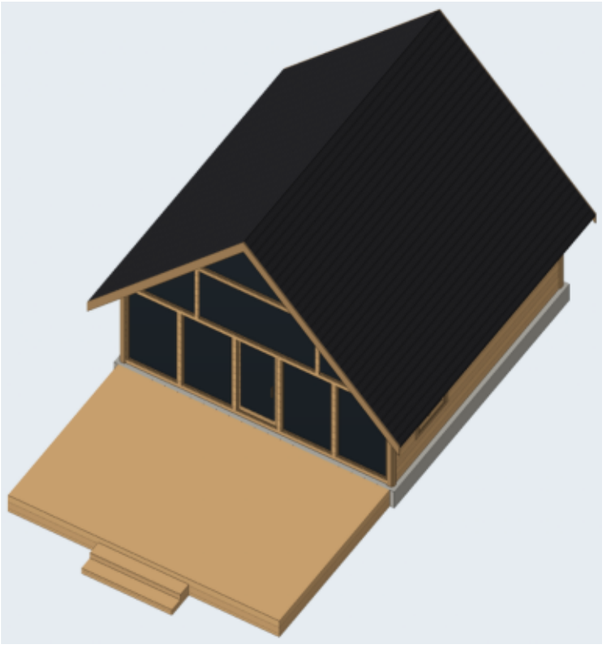


المشروع / العميل	عنوان اللوحة	المقياس	التاريخ	رقم اللوحة
كوخ A-frame بواجهة زجاج كاملة + ميزانين — 6 × 6 = 36 م² **عميل — A-frame 6×6**	**لقطات المنظور**	**—**	**2026-10-20**	**A-08 (8/10)**

مصنع وتد الأخشاب
Watad Wood Factory

المقطع العلوي بالفرش

مقطع أفقي على ارتفاع 1.90 م — توزيع الفرش ومسار الحركة

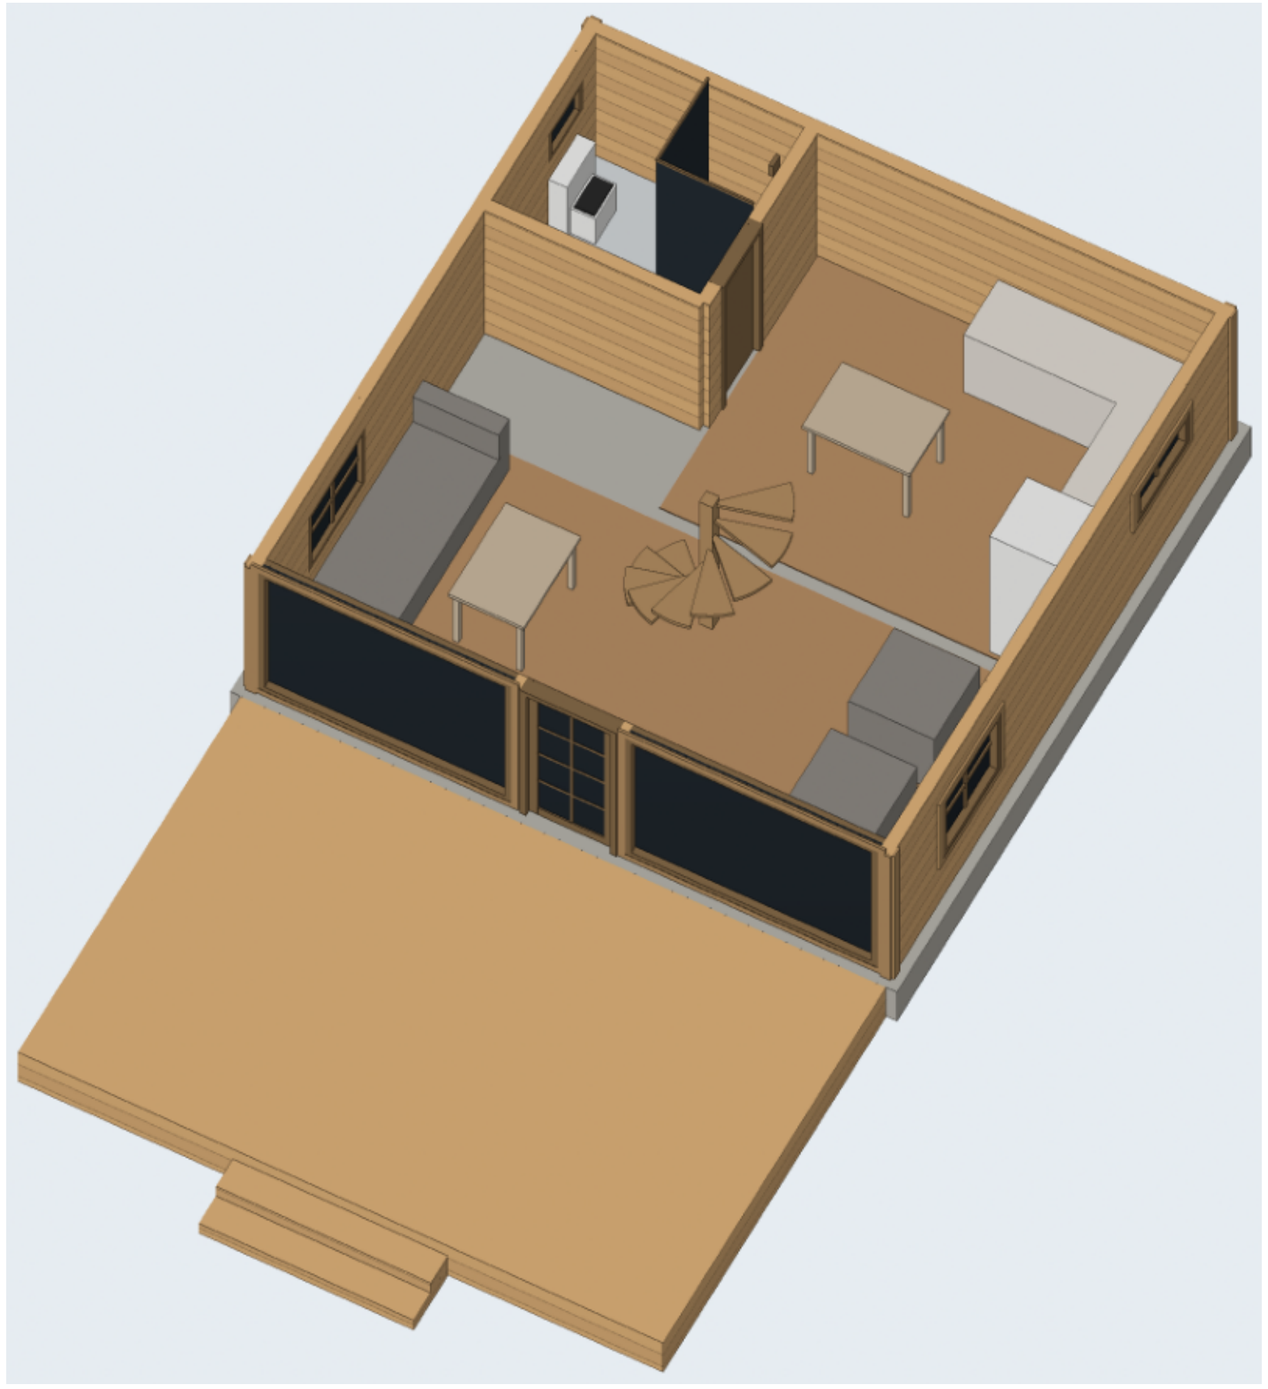

المشروع / العميل	عنوان اللوحة	المقياس	التاريخ	رقم اللوحة
كوخ A-frame بواجهة زجاج كاملة + ميزانين — 6 × 6 = 36 م² عميل — A-frame 6×6	المقطع العلوي بالفرش	—	2026-10-20	A-09 (9/10)

مصنع وتد الأخشاب
Watad Wood Factory

المنظور ثلاثي الأبعاد والمواد

النمط: جوزي غامق + إطارات سوداء — رندر واقعي بخامات حقيقية



جدول المواد والألوان

الخشب / الصبغة

خشب طبيعي فاتح (بدون صبغة)

القرميد

قرميد رمادي غامق

الزجاج

زجاج عاكس غامق

إطارات الشبابيك والأبواب

إطار خشب بنفس الصبغة أغمق

الكنار والزوايا

نفس الصبغة أغمق درجة


الصبة

خرسانة 45 سم


الدربزين: ألواح أفقية متقاربة (عصري)

تقسيم الشبابيك: بدون | الباب الرئيسي: زجاج بتقسيمات (فرنسي)

أنواع الدربزين المعتمدة (من مشاريع المصنع)

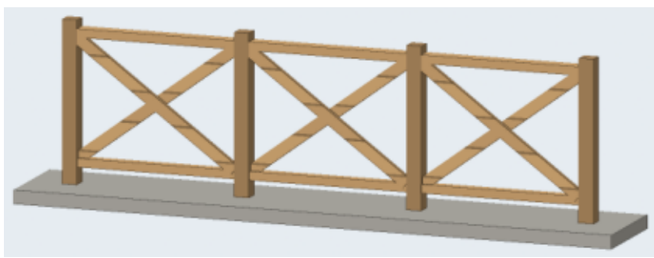

تقاطع X (صورة 5)

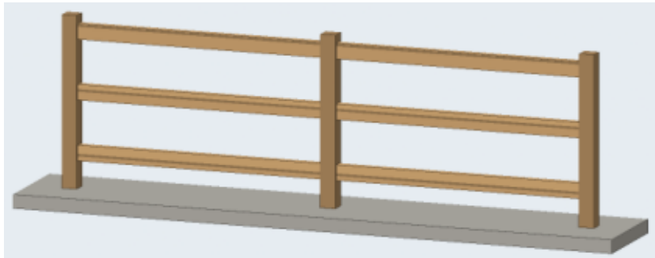

3 مرابيع أفقية (صورة 2)



قوائم رأسية متقاربة (صورة 1)

المشروع / العميل	عنوان اللوحة	المقياس	التاريخ	رقم اللوحة
مصنع وتد الأخشاب Watad Wood Factory **كوخ A-frame بواجهة زجاج كاملة + ميزانين — 6 × 6 = 36 م²** **عميل — A-frame 6×6**	**المنظور والمواد**	**—**	**2026-10-20**	**A-10 (10/10)**