
المسقط الأفقي مع الفرش


الأبعاد بالسنتيمتر - الجدران: قوائم 7×5 + تلبيس 2.5 من الجهتين (12 سم)

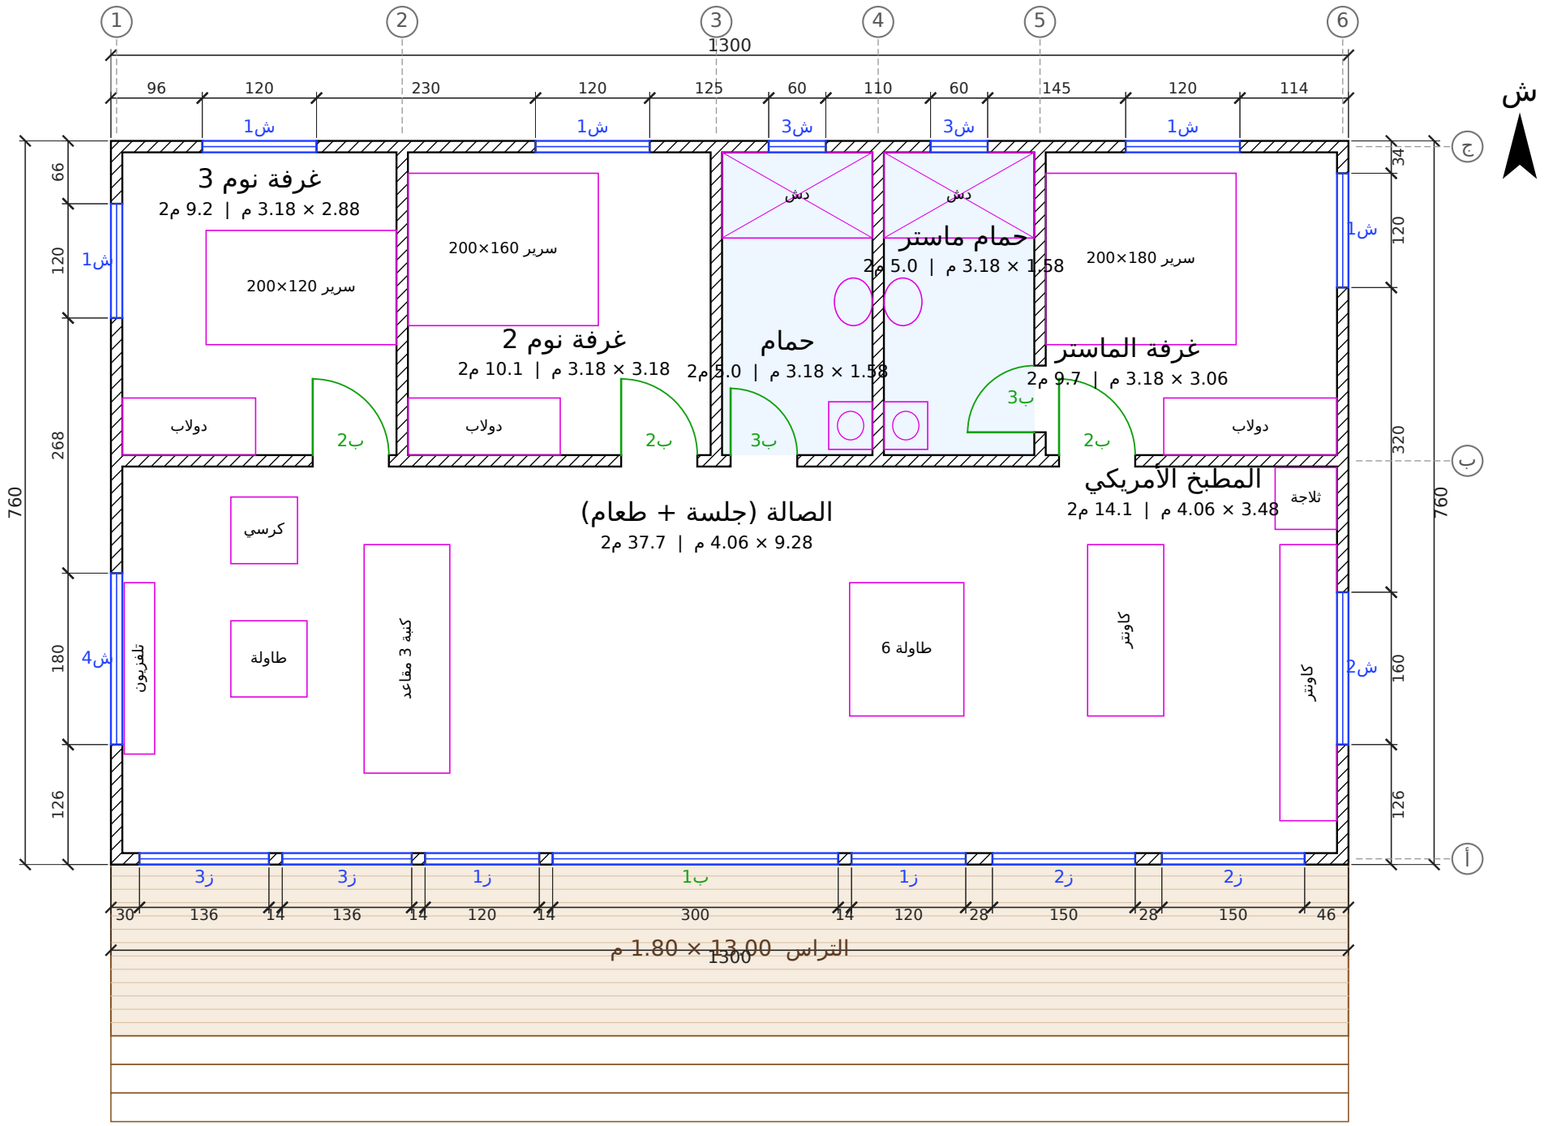

3 درجات × 15 سم


المشروع / العميل	عنوان اللوحة	المقياس	التاريخ	رقم اللوحة
كوخ 3 غرف بواجهة زجاج — 98.8 م² **عميل — تصميم رقم 5**	**المسقط الأفقي**	**1:50**	**2026-10-18**	**A-01 (1/9)**

مصنع وتد الأخشاب
Watad Wood Factory

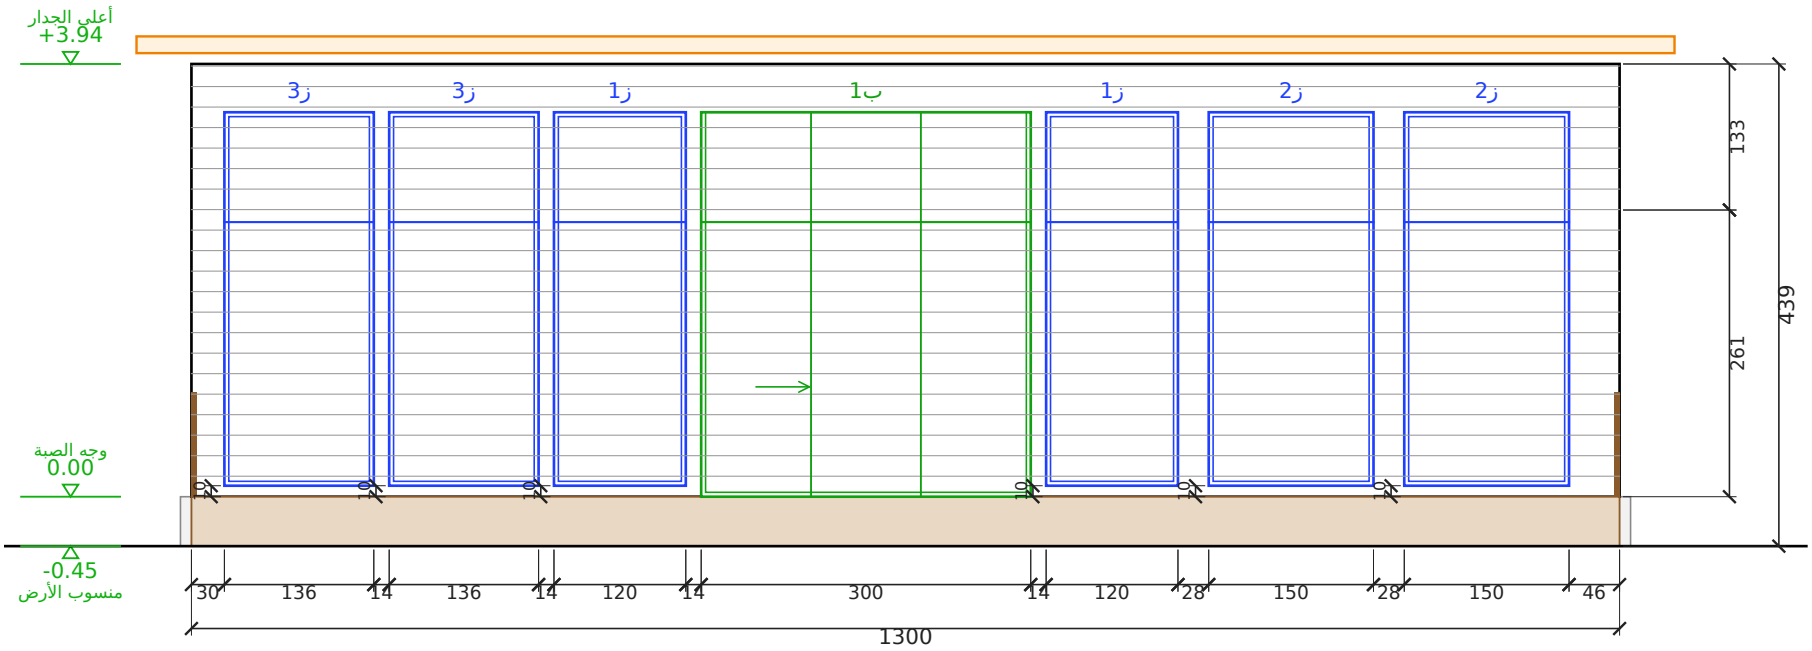

الواجهة الأمامية

مقياس 1:90 | الوحدة: سم

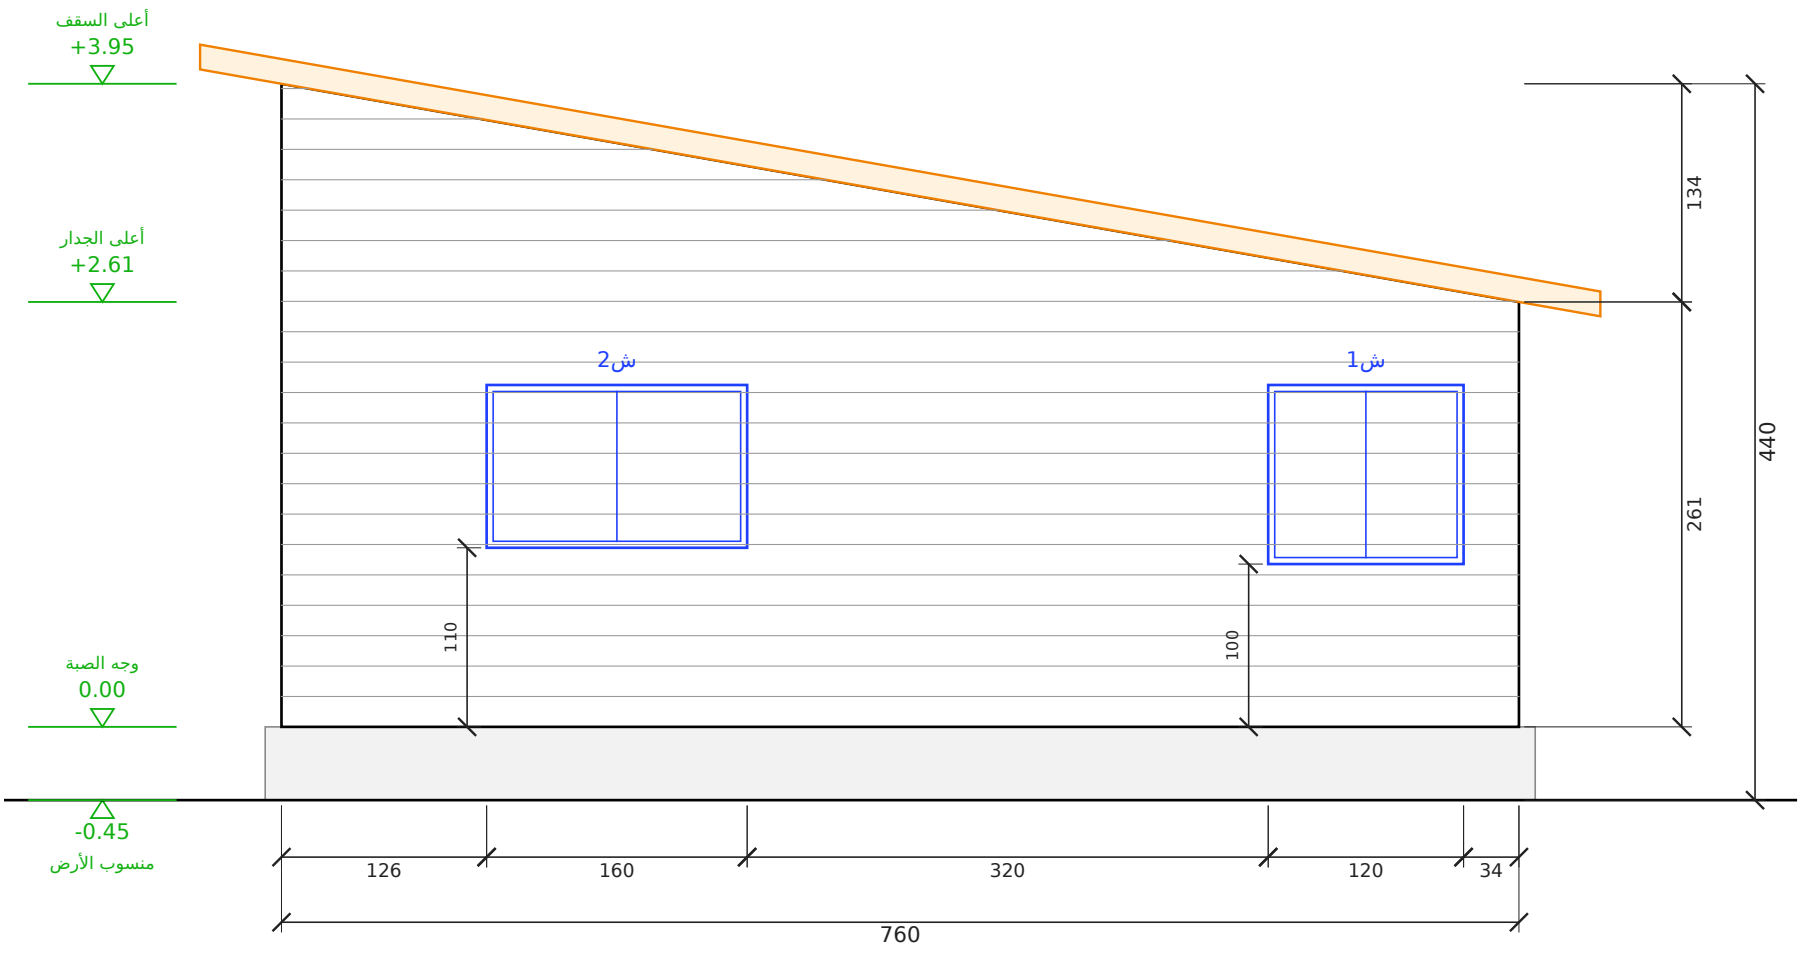


الواجهة الشرقية

مقياس 1:50 | الوحدة: سم


المشروع / العميل	عنوان اللوحة	المقياس	التاريخ	رقم اللوحة
كوخ 3 غرف بواجهة زجاج — 98.8 م² **عميل — تصميم رقم 5**	**الواجهة الأمامية والواجهة الشرقية**	**1:50**	**2026-10-18**	**A-02 (2/9)**

مصنع وتد الأخشاب
Watad Wood Factory

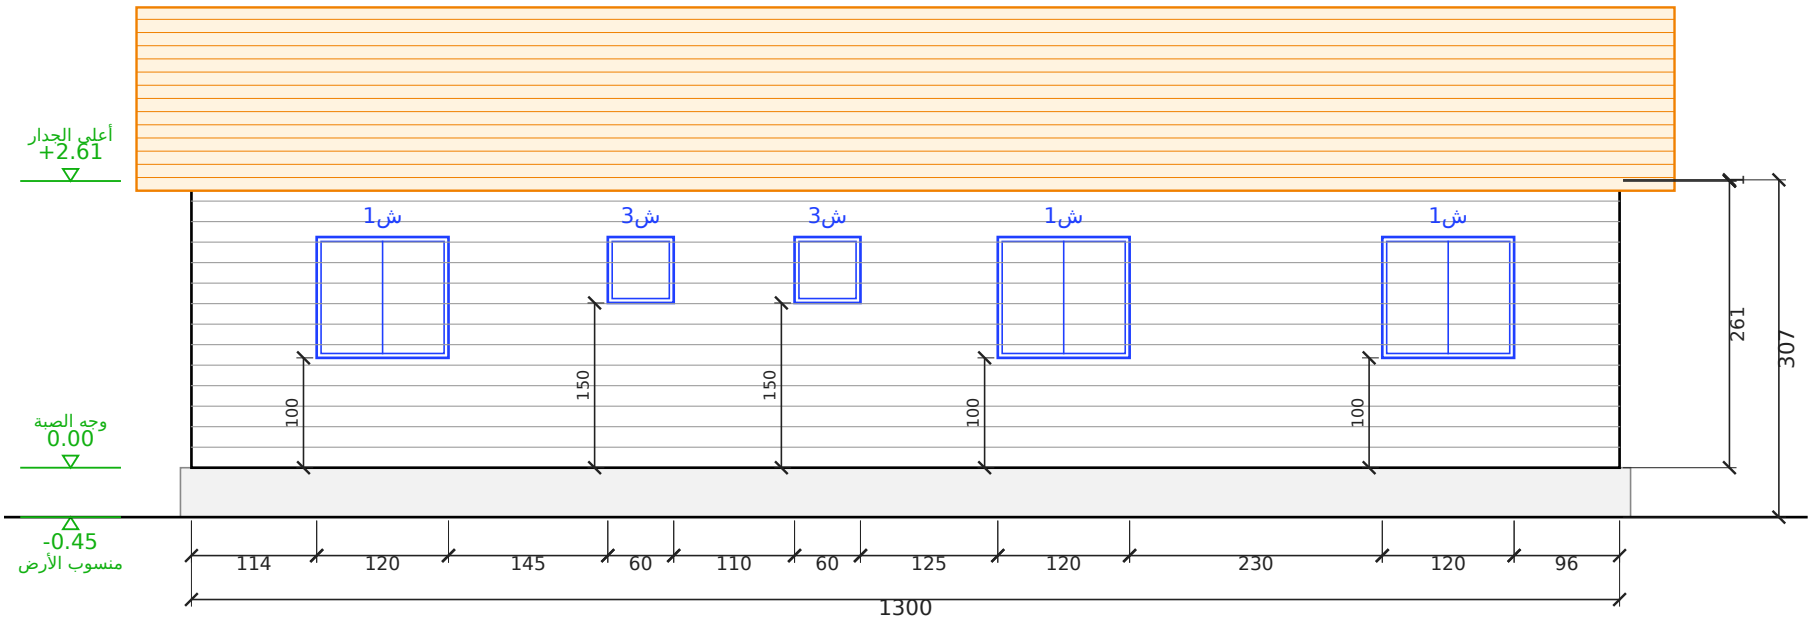

الواجهة الخلفية

مقياس 1:50 | الوحدة: سم

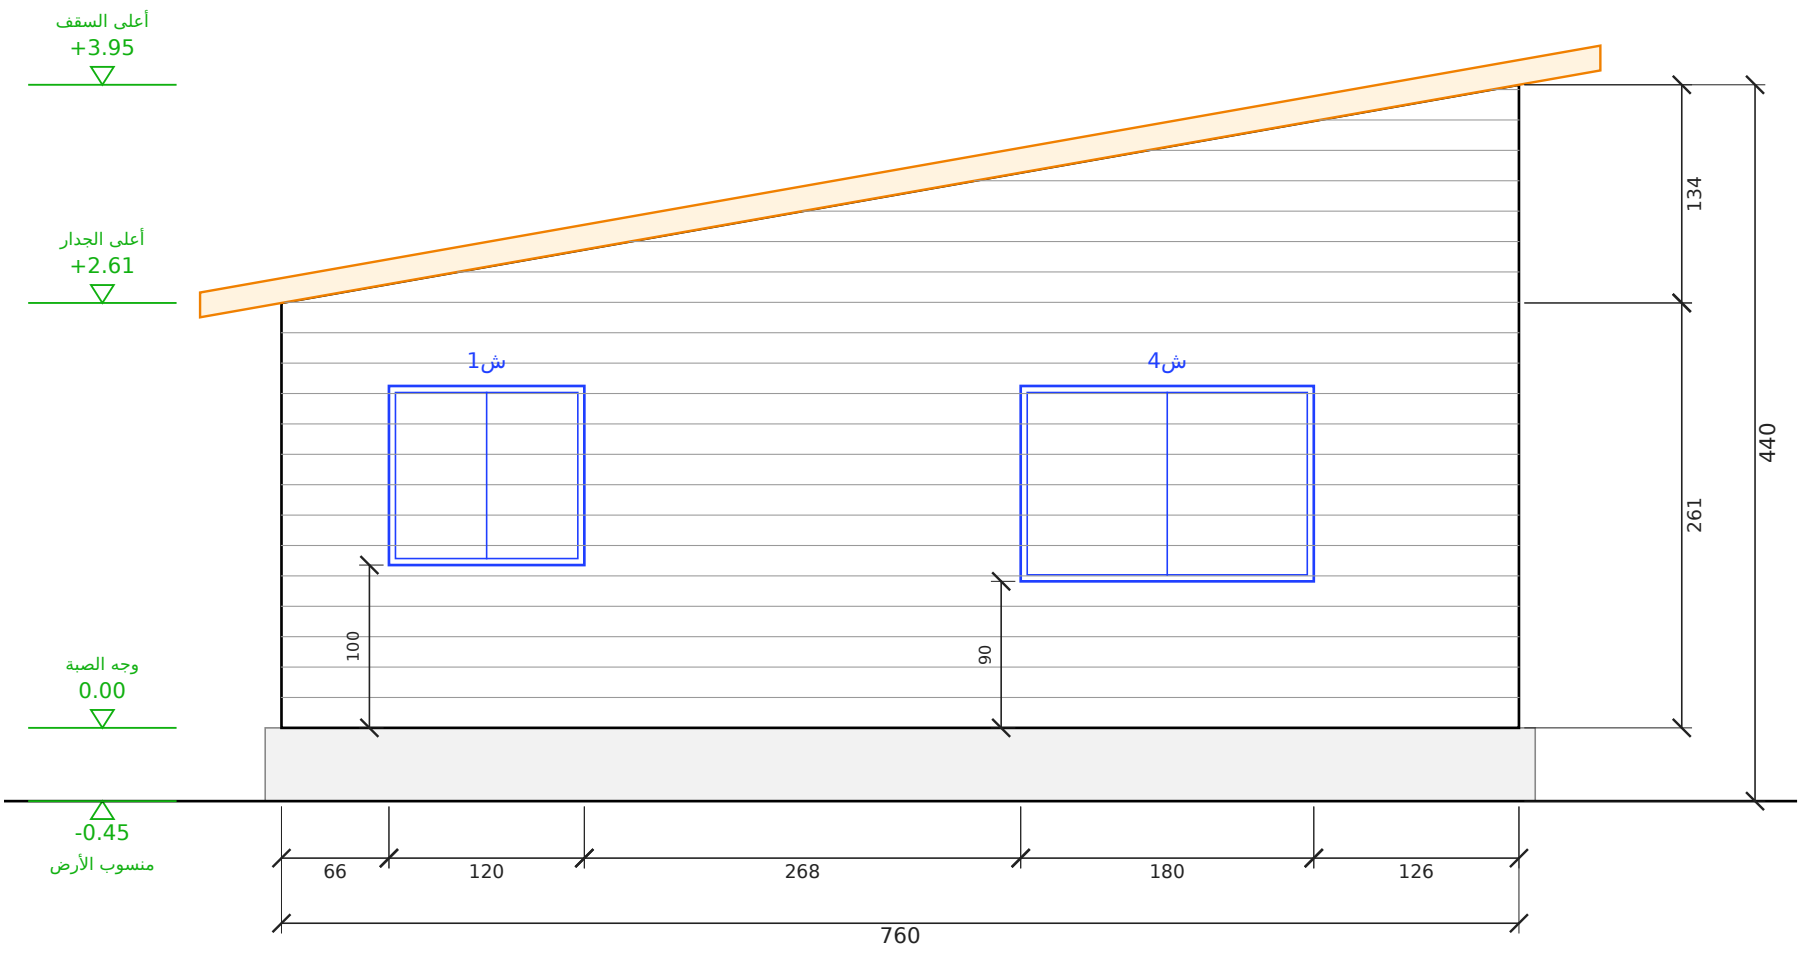


الواجهة الغربية

مقياس 1:50 | الوحدة: سم


المشروع / العميل	عنوان اللوحة	المقياس	التاريخ	رقم اللوحة
كوخ 3 غرف بواجهة زجاج — 98.8 م² **عميل — تصميم رقم 5**	**الواجهة الخلفية والواجهة الغربية**	**1:50**	**2026-10-18**	**A-03 (3/9)**

مصنع وتد الأخشاب
Watad Wood Factory


مسقط السقف (مائل باتجاه واحد)
رفرف 50 سم من كل جهة | مقياس 1:50

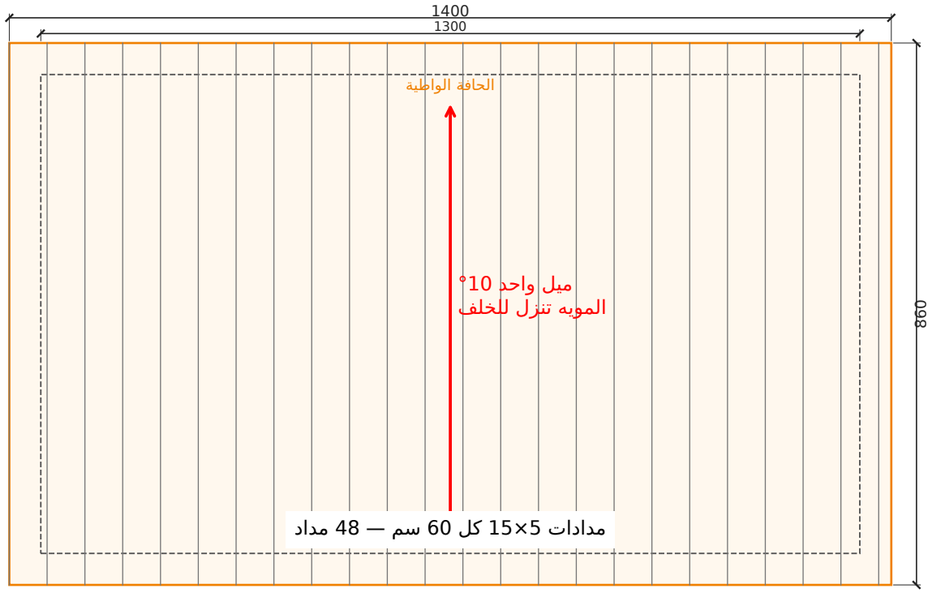

قطاع عرضي أ-أ
مقياس 1:50 | الوحدة: سم

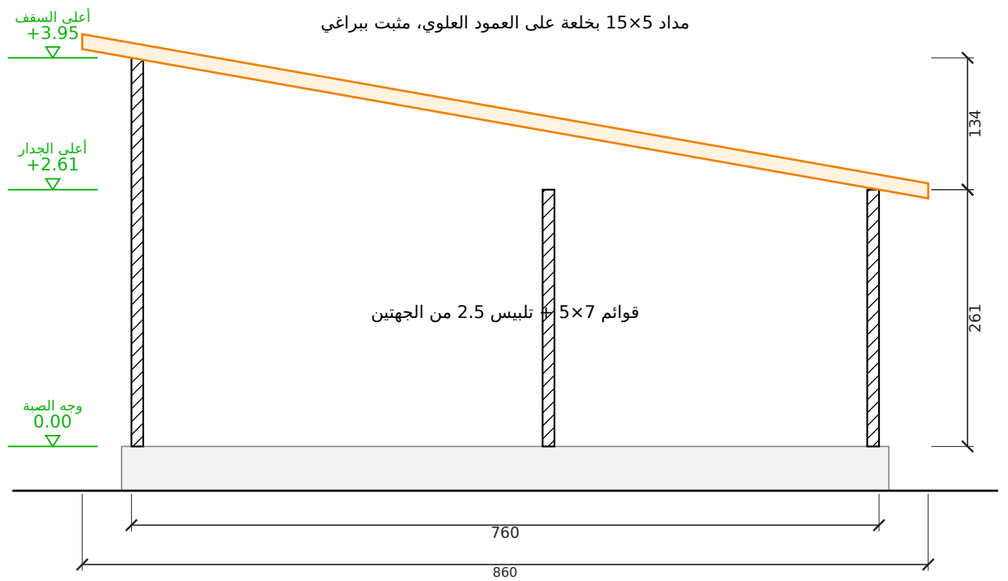

تفصيلة جلوس المداد على العلوي (1:5)

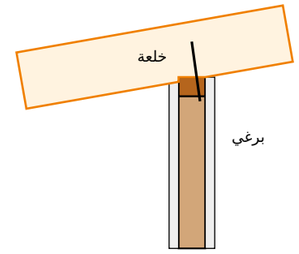

علوي 7×5 على قائم 7×5

المشروع / العميل	عنوان اللوحة	المقياس	التاريخ	رقم اللوحة
كوخ 3 غرف بواجهة زجاج — 98.8 م² **عميل — تصميم رقم 5**	**مسقط السقف والقطاع**	**1:50**	**2026-10-18**	**A-04 (4/9)**

مصنع وتد الأخشاب
Watad Wood Factory

جدول مقاسات الأبواب والشبابيك
مقاس الفتحة الصافي في الجدار - الوحدة: سم

الرمز	النوع	العرض (سم)	الارتفاع (سم)	ارتفاع الجلسة (سم)	العدد	الموقع
ب1	باب	300	350	-	1	الأمامية
ب2	باب	80	210	-	3	غرفة نوم 3 - غرفة نوم 2 - الماستر
ب3	باب	70	210	-	2	الحمام المشترك - حمام الماستر
ز1	شباك	120	340	10	2	الأمامية 2
ز2	شباك	150	340	10	2	الأمامية 2
ز3	شباك	136	340	10	2	الأمامية 2
ش1	شباك	120	110	100	5	الشرقية - الخلفية 3 - الغربية
ش2	شباك	160	100	110	1	الشرقية
ش3	شباك	60	60	150	2	الخلفية 2
ش4	شباك	180	120	90	1	الغربية

الإجمالي: أبواب 6 - شبابيك 15

جدول المساحات وبيانات المشروع

بيانات المشروع


البند	البيان
المشروع	كوخ 3 غرف بواجهة زجاج — 98.8 م²
العميل	عميل — تصميم رقم 5
الموقع	—
الاستخدام	سكن
التاريخ	2026-10-18
نظام البناء	هيكل خشب 5×7 + تلبيس 2.5 سم من الجهتين
السقف	مائل باتجاه واحد 10° — قرميد معدني

جدول المساحات


م	الفراغ	الأبعاد (م)	المساحة (م2)
1	الصالة (جلسة + طعام)	9.28 × 4.06	37.68
2	المطبخ الأمريكي	3.48 × 4.06	14.13
3	غرفة نوم 3	2.88 × 3.18	9.16
4	غرفة نوم 2	3.18 × 3.18	10.11
5	حمام	1.58 × 3.18	5.02
6	حمام ماستر	1.58 × 3.18	5.02
7	غرفة الماستر	3.06 × 3.18	9.73
	المساحة الصافية الداخلية		**90.86**
	التراس المسقوف	**13.00 × 1.80**	**23.40**
	المساحة الإجمالية المبنية	**13.00 × 7.60**	**98.80**

لقطات المنظور الخارجي


المنظور الأمامي

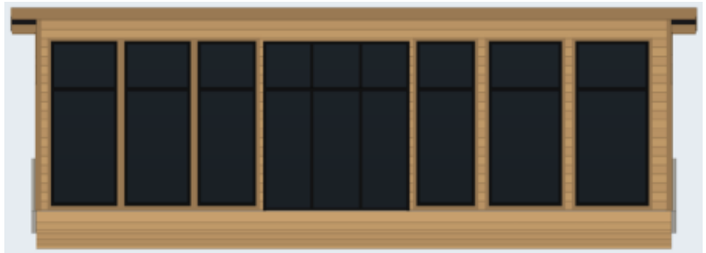

منظور أمامي من اليسار

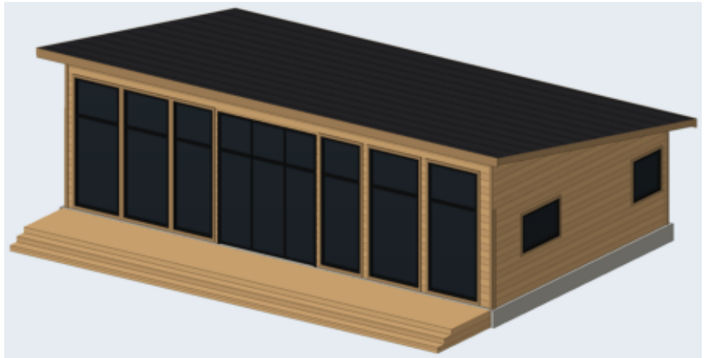


منظور أمامي من اليمين

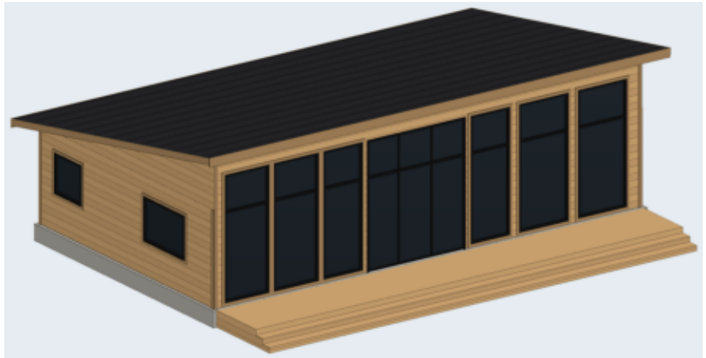

المنظور الخلفي



منظور خلفي من اليمين

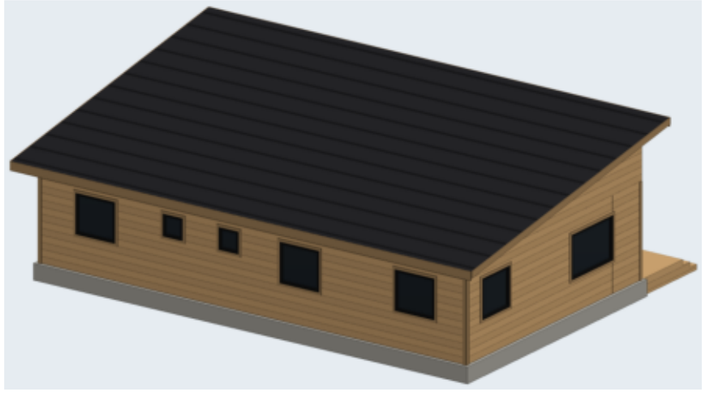


منظر علوي



مصنع وتد الأخشاب Watad Wood Factory	المشروع / العميل **كوخ 3 غرف بواجهة زجاج — 98.8 م²** **عميل — تصميم رقم 5**	عنوان اللوحة **لقطات المنظور**	المقياس **—**	التاريخ **2026-10-18**	رقم اللوحة **A-07 (7/9)**

المقطع العلوي بالفرش

مقطع أفقي على ارتفاع 1.90 م — توزيع الفرش ومسار الحركة

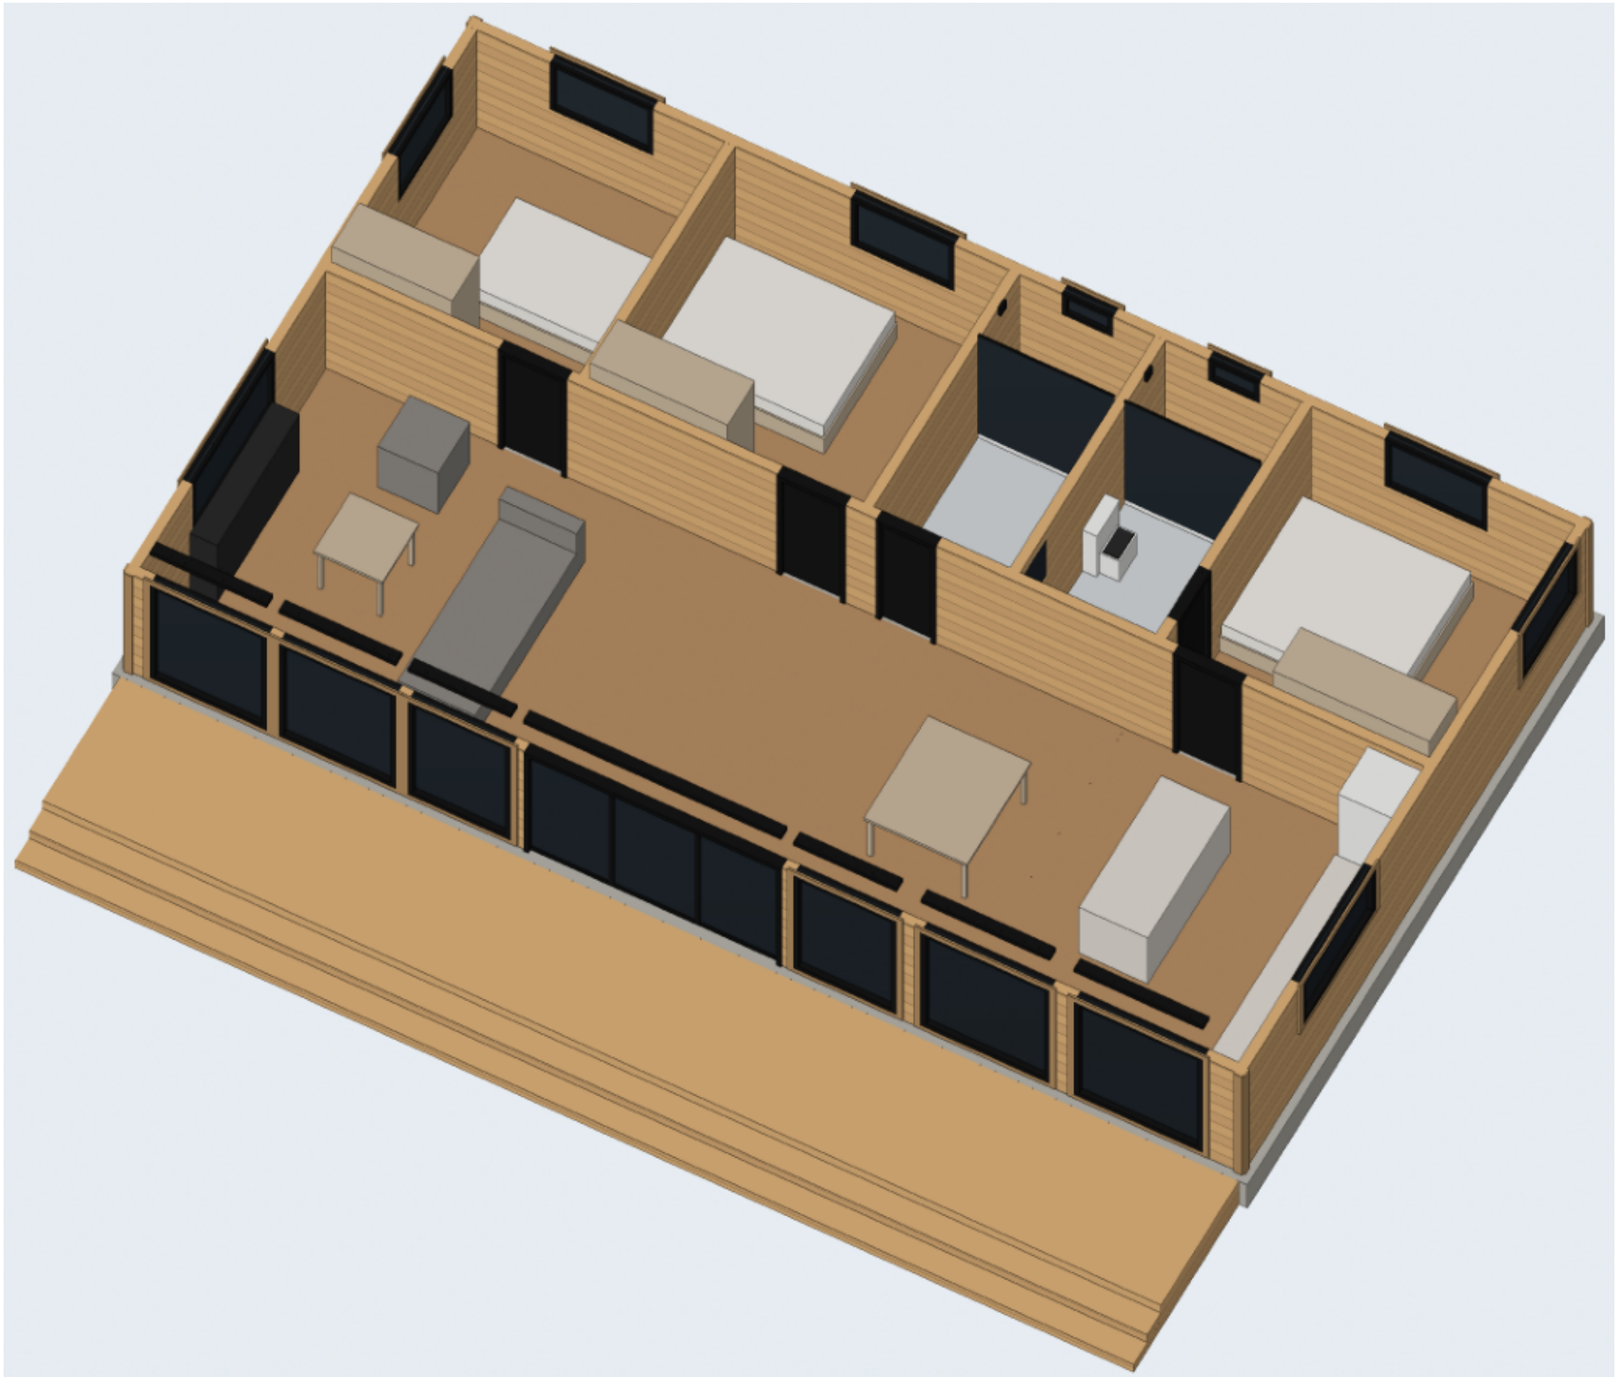


المشروع / العميل	عنوان اللوحة	المقياس	التاريخ	رقم اللوحة
كوخ 3 غرف بواجهة زجاج — 98.8 م² **عميل — تصميم رقم 5**	**المقطع العلوي بالفرش**	**—**	**2026-10-18**	**A-08 (8/9)**

مصنع وتد الأخشاب
Watad Wood Factory

المنظور ثلاثي الأبعاد والمواد

النمط: جوزي غامق + إطارات سوداء — رندر واقعي بخامات حقيقية

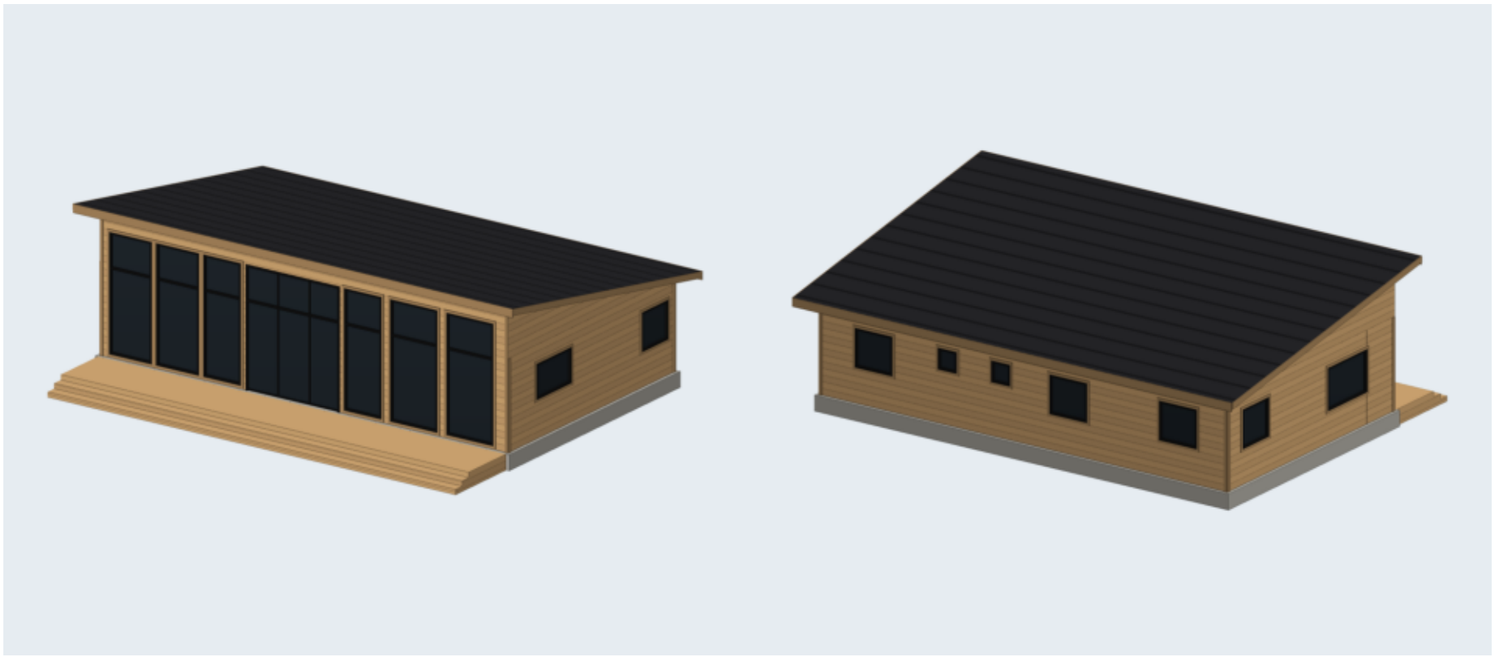

جدول المواد والألوان

الخشب / الصبغة

خشب طبيعي فاتح (بدون صبغة)

القرميد

قرميد رمادي غامق

الزجاج

زجاج عاكس غامق

إطارات الشبابيك والأبواب

إطار ألمنيوم أسود

الكنار والزوايا

نفس الصبغة أغمق درجة


الصبة

خرسانة 45 سم


الدربزين: ألواح أفقية متقاربة (عصري)

تقسيم الشبابيك: بدون | الباب الرئيسي: سحاب زجاج

أنواع الدربزين المعتمدة (من مشاريع المصنع)

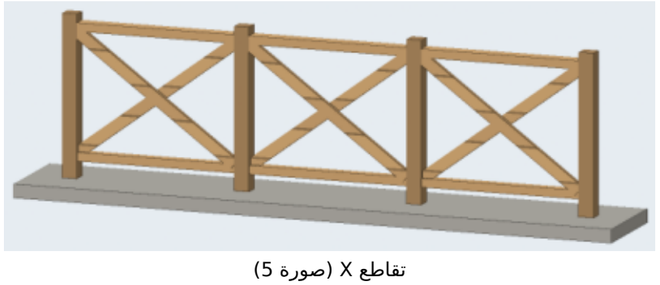

تقاطع X (صورة 5)

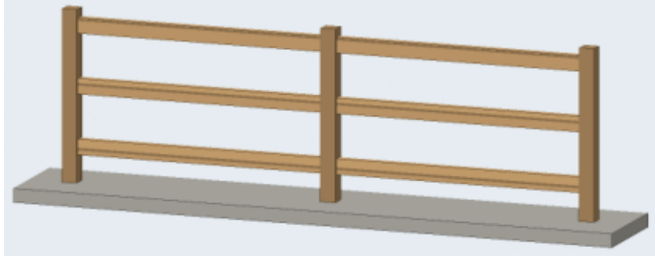

3 مرابيع أفقية (صورة 2)



قوائم رأسية متقاربة (صورة 1)

المشروع / العميل	عنوان اللوحة	المقياس	التاريخ	رقم اللوحة
مصنع وتد الأخشاب Watad Wood Factory **كوخ 3 غرف بواجهة زجاج — 98.8 م²** **عميل — تصميم رقم 5**	**المنظور والمواد**	**—**	**2026-10-18**	**A-09 (9/9)**