
جدول مساحات الموقع

البند	المقاس	المساحة (م²)
مساحة الأرض (شبه منحرف)	25.00 × 24.27/16.23 م	499.6
مسطح الأكواخ (2)	2 × 12.62 × 7.00 م	176.7
تراس الكوخ	2 × 2.40 × 7.00 م	33.6
مسبح	2 × 4.80 × 2.30 م	22.1
بلاط		18.7
موقف سيارة	2 × 5.50 × 3.00 م	33.0
ممر	2 × 7.55 × 1.00 م	15.1
أحواض زراعة	2 × 6.60 × 1.00 م	13.2
المسطحات الخضراء (حديقة)	الباقي	187.2

الموقع العام وتنسيق الحديقة (لاندسكيب)
الأرض 500 م² | الأبعاد بالسنتيمتر

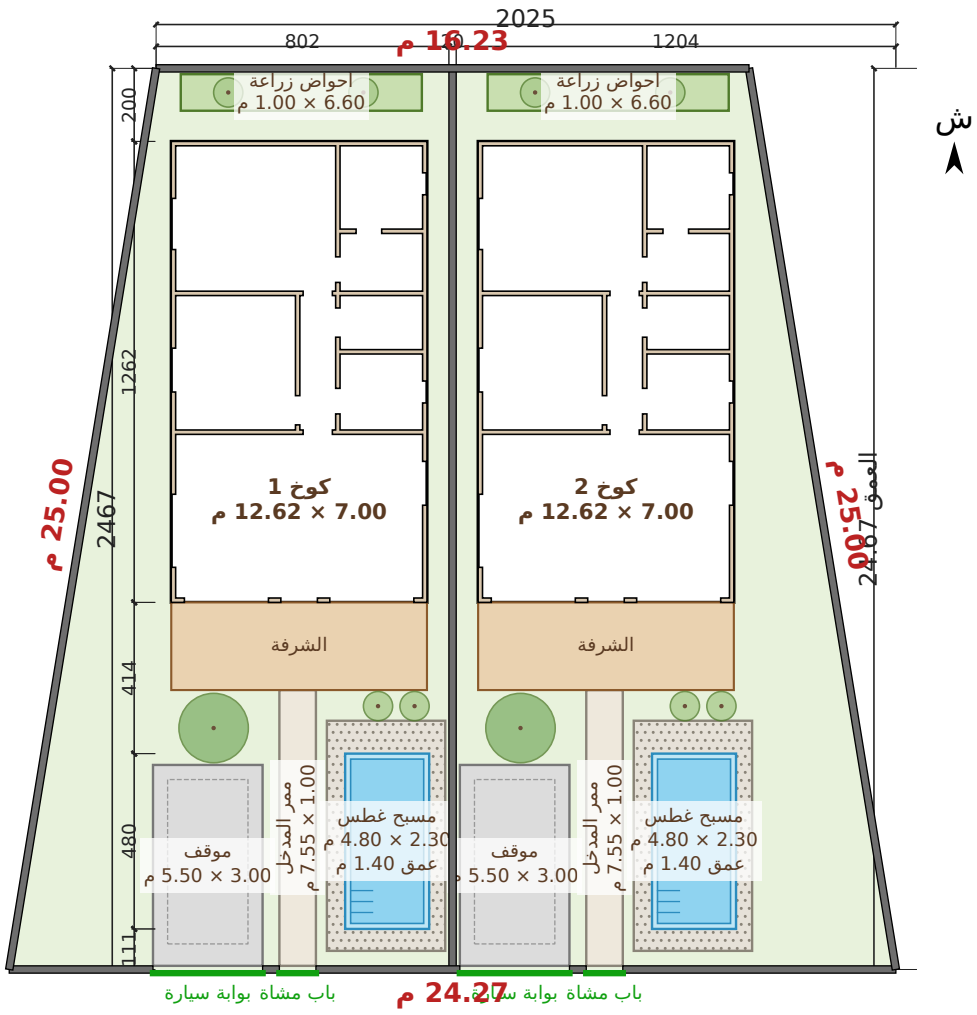


- الأرض مقسومة بسور بالنص لوحدتين مستقلتين (≈ 250 م² لكل وحدة) — تأجير مستقل وخصوصية كاملة.
- كل وحدة: بوابة سيارة 3.00 م لموقف + باب مشاة بممر مستقيم لدرج الشرفة، ومسبح غطس 2.30 × 4.80 م ببلاط حوله.
- الشاليه بآخر الأرض بعيد عن الشارع، والصالة والشرفة تطل على الحديقة والمسبح.
- سور بلك 2.20 م بغطاء خشب على أضلاع الأرض (شبه منحرف) + السور الفاصل بين الوحدتين.
- ممرات جانبية حول كل شاليه (≈ 0.60 م عند الركن الخلفي وتوسع للأمام) للصيانة، وأحواض زراعة على السور الخلفي.

مصنع وتد الأخشاب Watad Wood Factory	المشروع / العميل	عنوان اللوحة	المقياس	التاريخ	رقم اللوحة
	شاليهين الهدا الاستثماري — غرفتين وصالة لكل شاليه — 2 × 12.62 × 7.00 = 88.3 م² عميل — الهدا (استثماري)	الموقع العام واللاندسكيب	1:200	2026-10-23	A-01 (1/10)


المسقط الأفقي مع الفرش

الأبعاد بالسنتيمتر - الجدران: قوائم 7×5 + تلبيس 2.5 من الجهتين (12 سم)

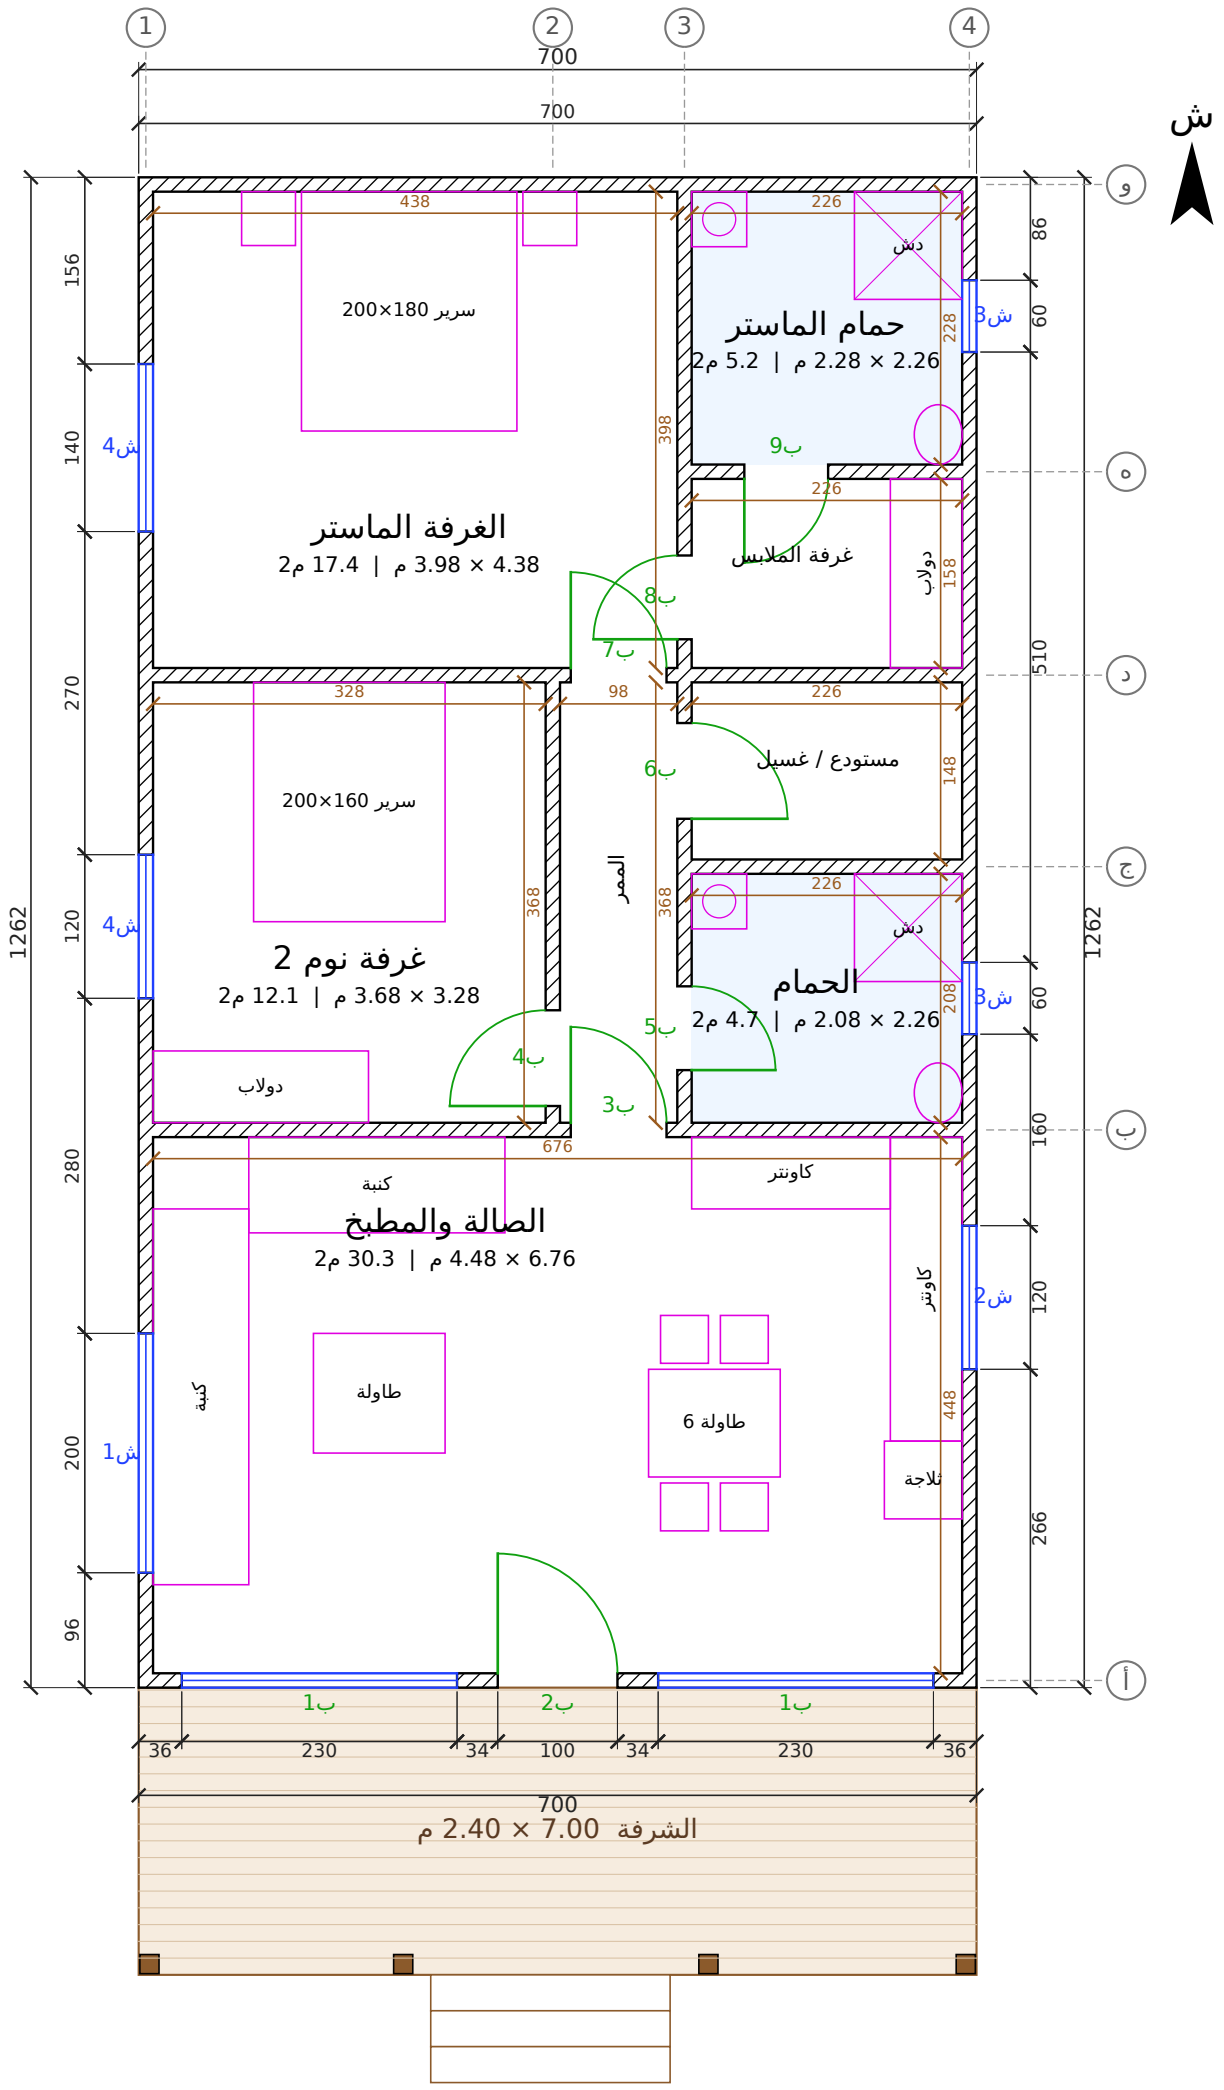


المشروع / العميل	عنوان اللوحة	المقياس	التاريخ	رقم اللوحة
شاليهين الهدا الاستثماري — غرفتين وصالة لكل شاليه — 7.00 × 12.62 = 88.3 م² × 2 عميل — الهدا (استثماري)	المسقط الأفقي	1:50	2026-10-23	A-02 (2/10)

مصنع وتد الأخشاب
Watad Wood Factory

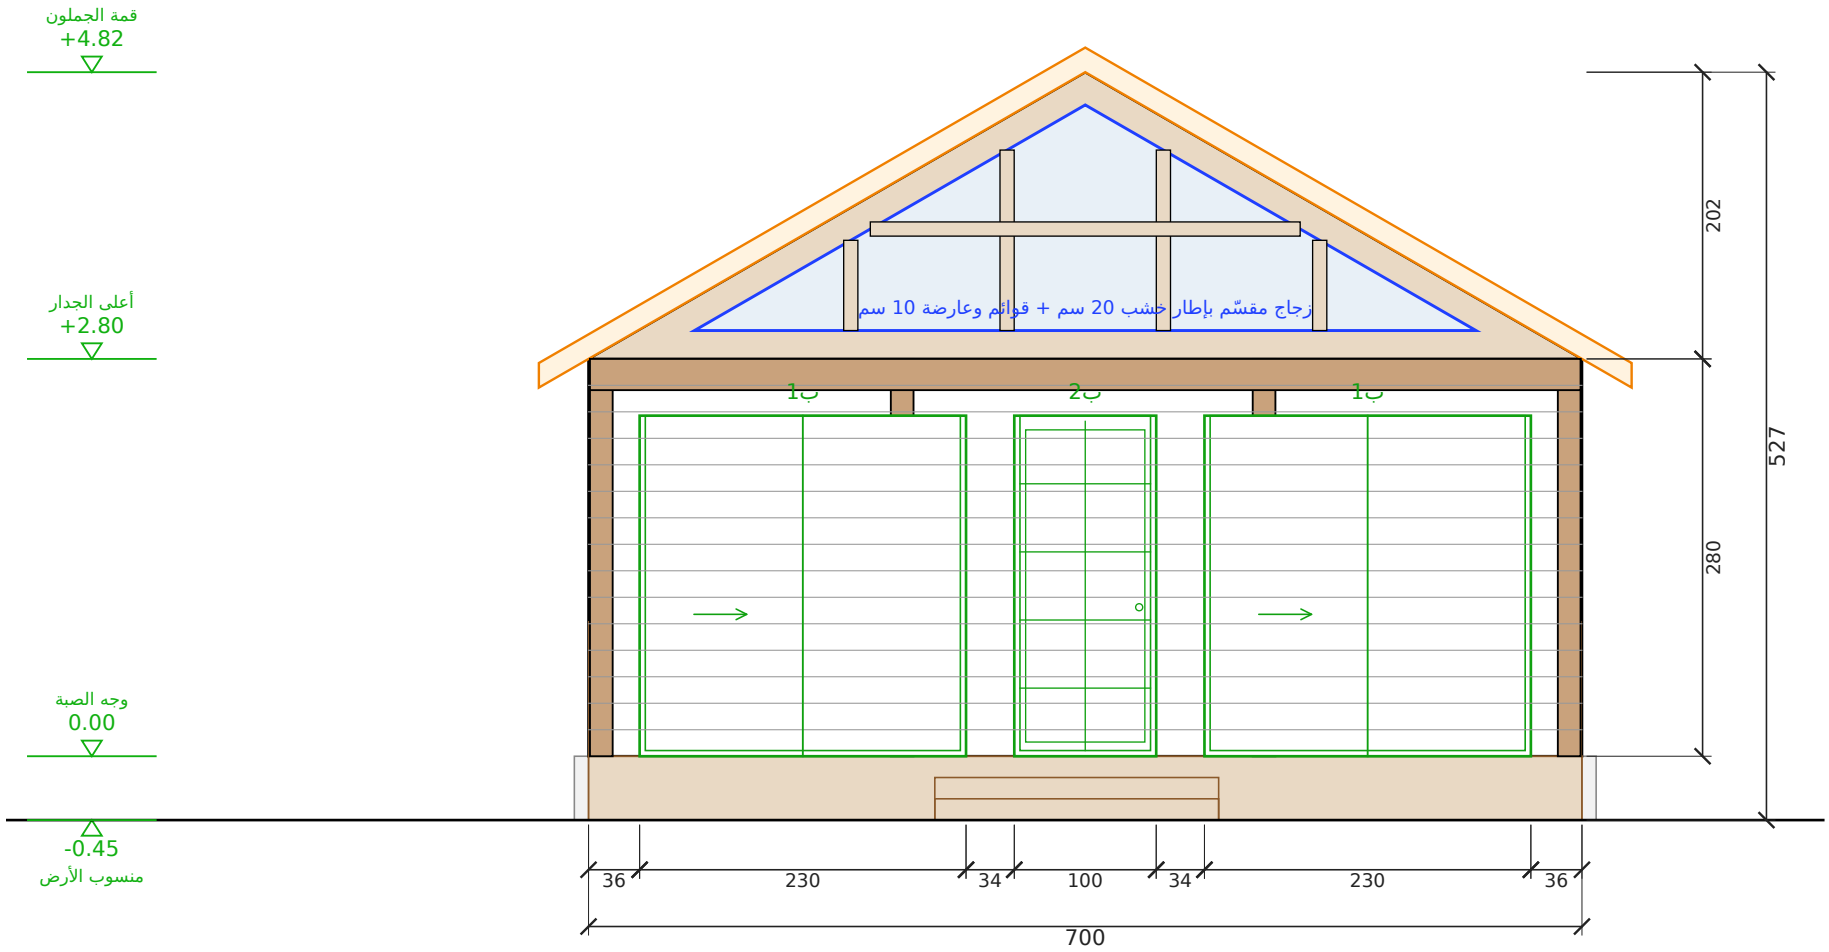

الواجهة الأمامية

مقياس 1:50 | الوحدة: سم

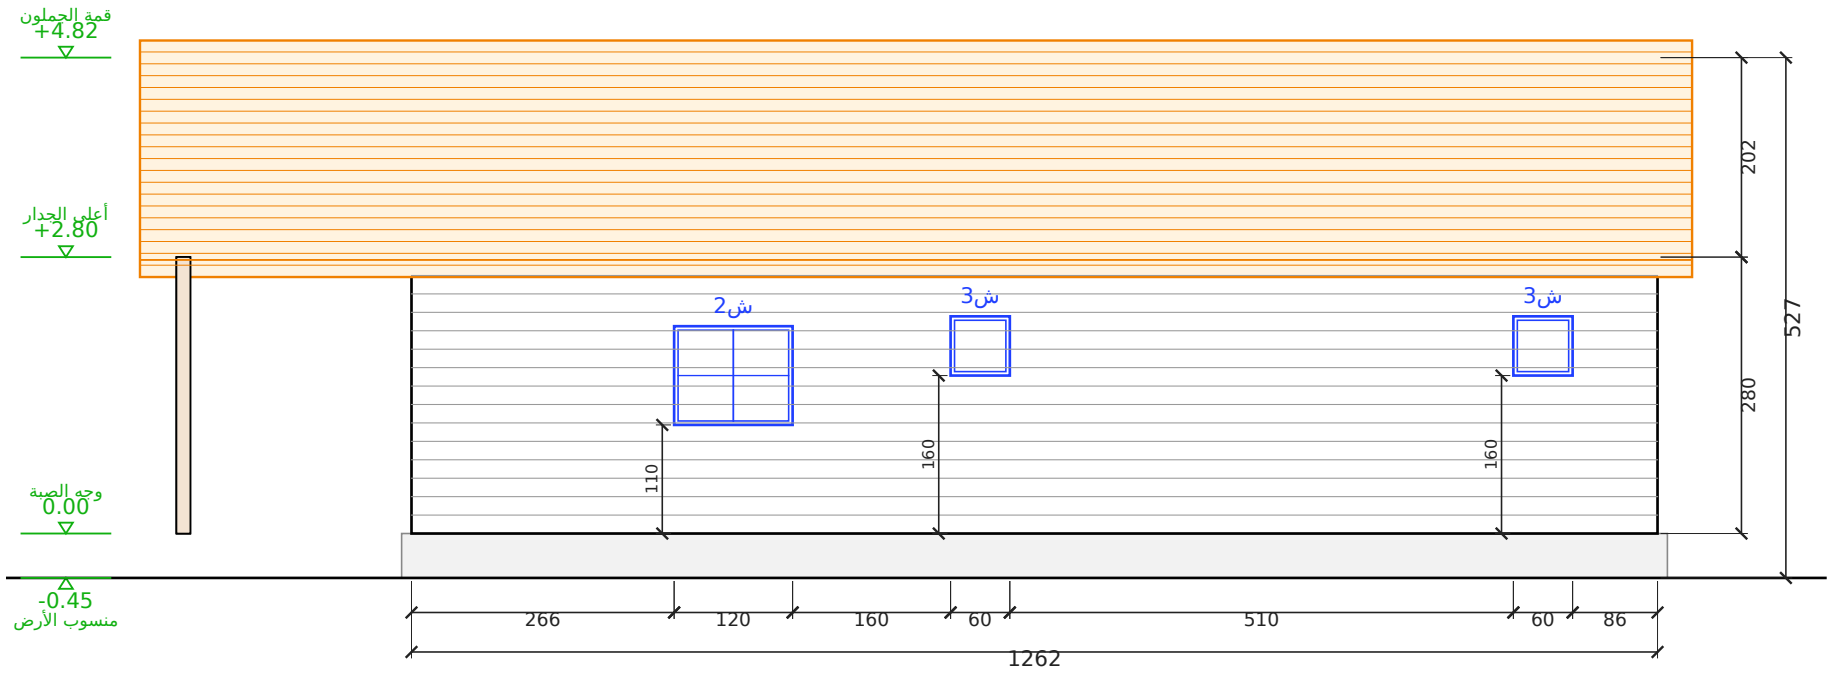


الواجهة الشرقية

مقياس 1:50 | الوحدة: سم


المشروع / العميل	عنوان اللوحة	المقياس	التاريخ	رقم اللوحة
شاليهين الهدا الاستثماري — غرفتين وصالة لكل شاليه — 7.00 × 12.62 × 2 = 88.3 م² عميل — الهدا (استثماري)	الواجهة الأمامية والواجهة الشرقية	1:50	2026-10-23	A-03 (3/10)

مصنع وتد الأخشاب
Watad Wood Factory

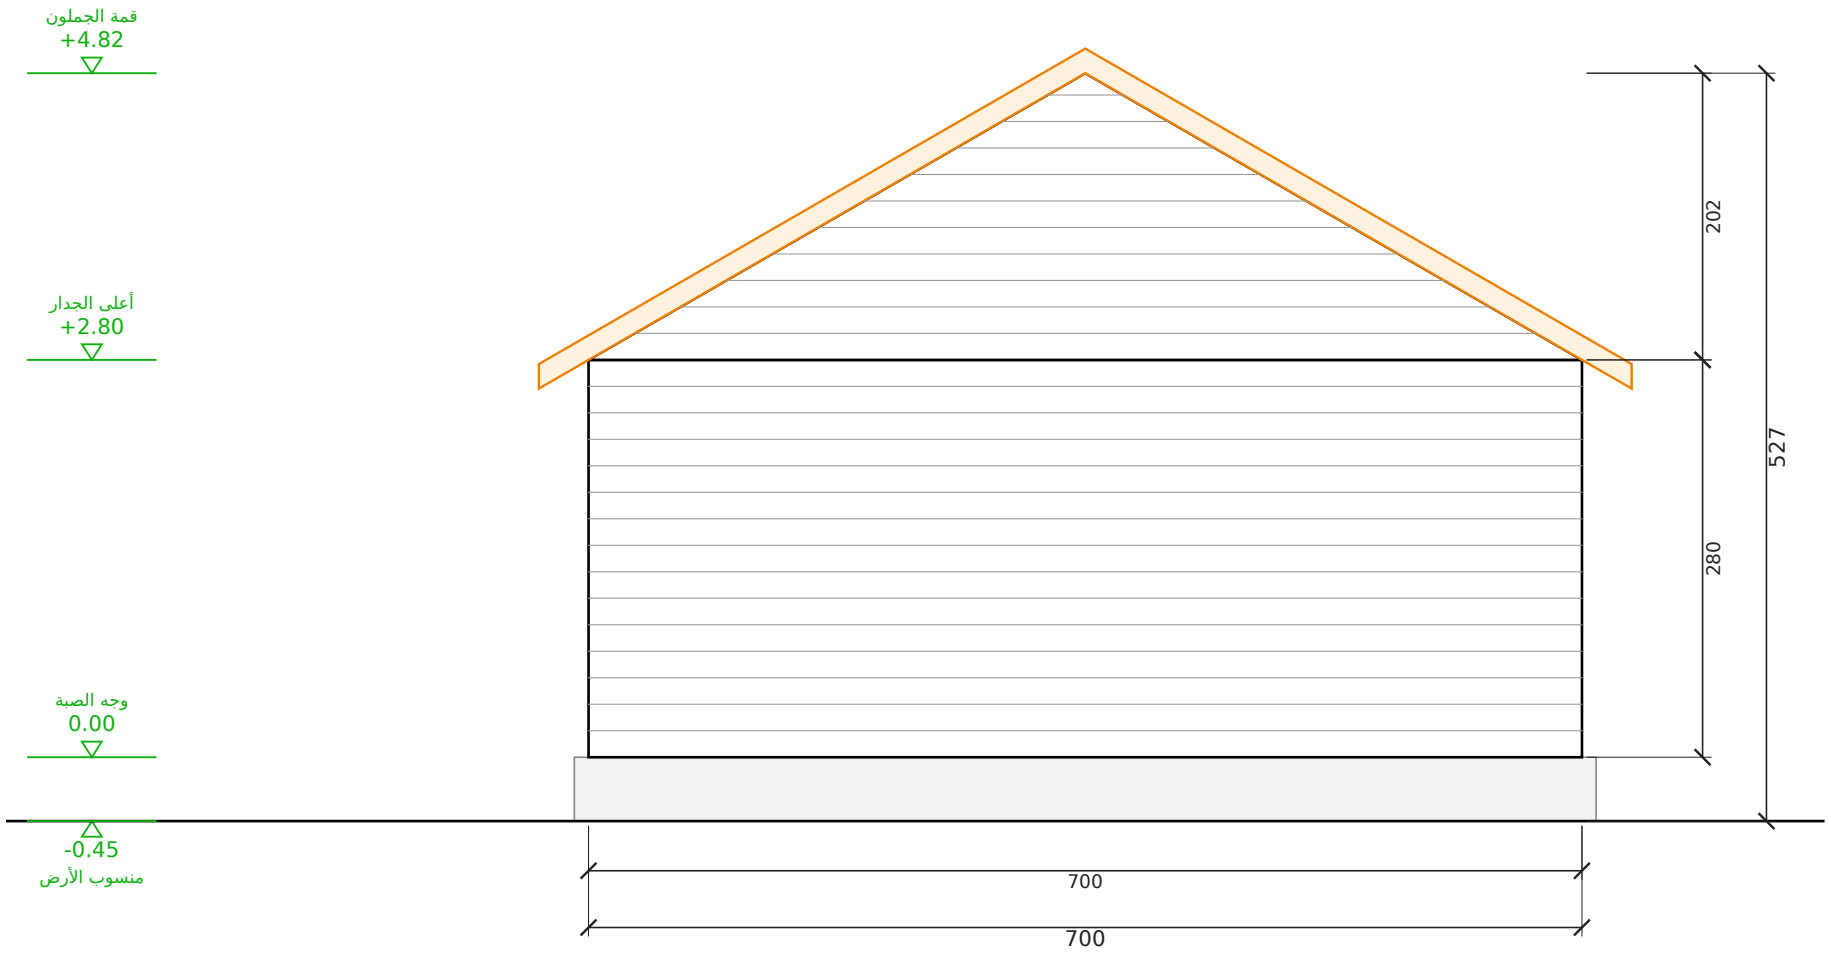

الواجهة الخلفية

مقياس 1:50 | الوحدة: سم

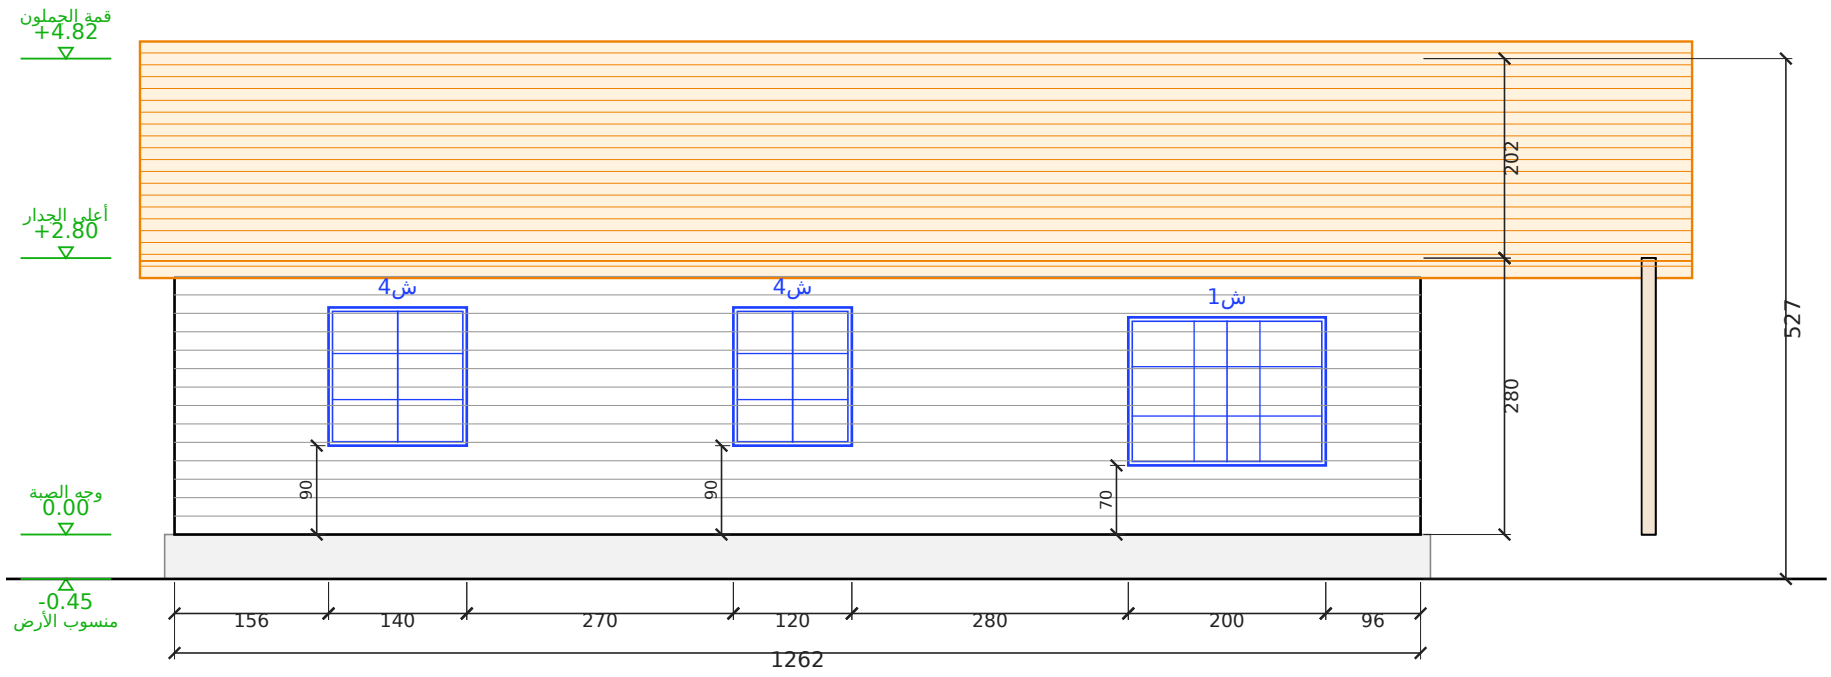


الواجهة الغربية

مقياس 1:50 | الوحدة: سم


المشروع / العميل	عنوان اللوحة	المقياس	التاريخ	رقم اللوحة
شاليهين الهدا الاستثماري — غرفتين وصالة لكل شاليه — 7.00 × 12.62 = 88.3 م² × 2 عميل — الهدا (استثماري)	الواجهة الخلفية والواجهة الغربية	1:50	2026-10-23	A-04 (4/10)

مصنع وتد الأخشاب
Watad Wood Factory


مسقط السقف (جملون)
رفرف 35 سم من كل جهة | مقياس 1:50

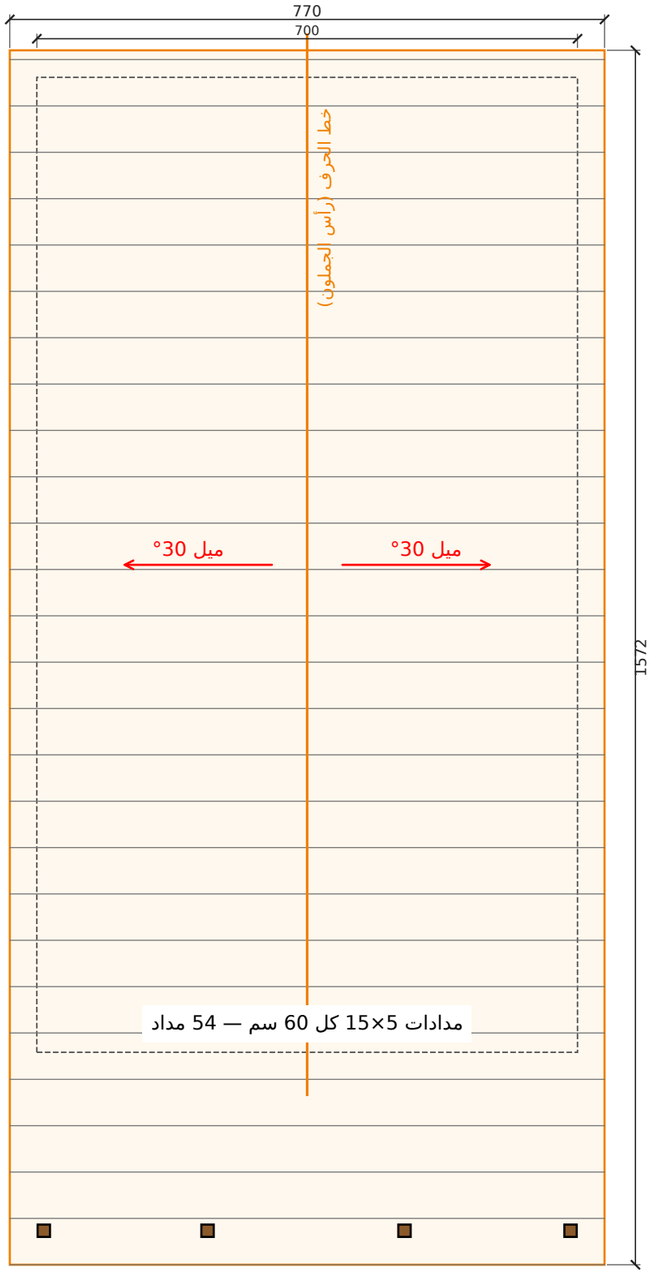

قطاع عرضي أ-أ
مقياس 1:50 | الوحدة: سم

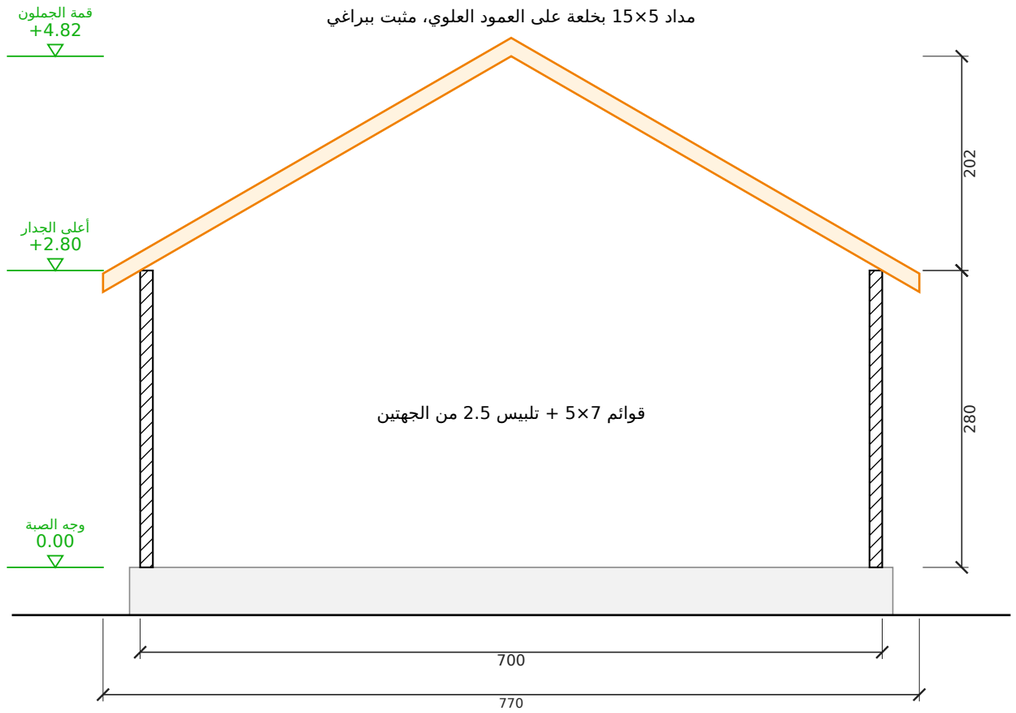

تفصيلة جلوس المداد على العلوي (1:5)

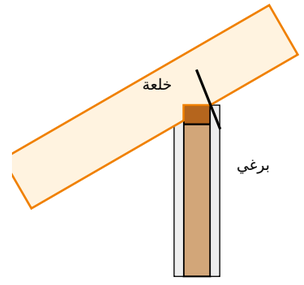

المشروع / العميل	عنوان اللوحة	المقياس	التاريخ	رقم اللوحة
شاليهين الهدا الاستثماري — غرفتين وصالة لكل شاليه — 7.00 × 12.62 = 88.3 م² × 2 **عميل — الهدا (استثماري)**	**مسقط السقف والقطاع**	**1:50**	**2026-10-23**	**A-05 (5/10)**

مصنع وتد الأخشاب
Watad Wood Factory

جدول مقاسات الأبواب والشبابيك
مقاس الفتحة الصافي في الجدار - الوحدة: سم

الرمز	النوع	العرض (سم)	الارتفاع (سم)	ارتفاع الجلسة (سم)	العدد	الموقع
ب1	باب مزدوج	230	240	-	2	الأمامية 2
ب2	باب	100	240	-	1	الأمامية
ب3	باب	80	210	-	1	باب الممر
ب4	باب	80	210	-	1	غرفة نوم 2
ب5	باب	70	210	-	1	الحمام
ب6	باب	80	210	-	1	مستودع / غسيل
ب7	باب	80	210	-	1	الماستر
ب8	باب	70	210	-	1	غرفة الملابس
ب9	باب	70	210	-	1	حمام الماستر
ش1	شباك	200	150	70	1	الغربية
ش2	شباك	120	100	110	1	الشرقية
ش3	شباك	60	60	160	2	الشرقية 2
ش4	شباك	140	140	90	1	الغربية
ش4	شباك	120	140	90	1	الغربية

الإجمالي: أبواب 10 - شبابيك 6

جدول المساحات وبيانات المشروع والتسعير

بيانات المشروع

البند	البيان
المشروع	شاليهين الهدا الاستثماري — غرفتين وصالة لكل شاليه — 7.00 × 12.62 = 88.3 م² × 2
العميل	عميل — الهدا (استثماري)
الموقع	الهدا — الطائف
الاستخدام	شاليهين استثماري (تأجير)
التاريخ	2026-10-23
نظام البناء	هيكل خشب 5×7 + تلبيس 2.5 سم من الجهتين
السقف	جملون 30° — قرميد معدني

جدول المساحات

م	الفراغ	الأبعاد (م)	المساحة (م2)
1	الصالة والمطبخ	6.76 × 4.48	30.28
2	غرفة نوم 2	3.28 × 3.68	12.07
3	الممر	0.98 × 3.68	3.61
4	الحمام	2.26 × 2.08	4.70
5	مستودع / غسيل	2.26 × 1.48	3.34
6	الغرفة الماستر	4.38 × 3.98	17.43
7	غرفة الملابس	2.26 × 1.58	3.57
8	حمام الماستر	2.26 × 2.28	5.15
	المساحة الصافية الداخلية		**80.16**
	الشرفة	**7.00 × 2.40**	**16.80**
	المساحة الإجمالية المبنية	**7.00 × 12.62**	**88.34**
	المساحة الكلية (المبنية + التراس)		**105.14**

التسعير المفصّل

البند	المبلغ (ريال)
الكوخ المبني 88.34 م² × 1,096	96,821
شرفة الشاليه الأول المسقوفة (أرضية + امتداد السقف + 4 أعمدة + دربزين) — 16.80 م² × 1,096	18,413
الشاليه الثاني (مطابق — 88.34 م² + شرفة 16.8 م²) — 105.14 م² × 1,096	115,233
الإجمالي (ريال)	**230,467**

ملاحظات:


- السعر للشاليهين والشرفتين حسب المخطط المعتمد — التراس يُسعّر بنفس سعر متر الكوخ.
- أعمال الموقع (السور والبوابات والمسابح والبلاط والزراعة) عن طريق المقاول وتُسعّر منفصلة.
- الصبة والتمديدات الخارجية على العميل ما لم يُذكر غير ذلك.

لقطات المنظور الخارجي


المنظور الأمامي




منظور أمامي من اليسار

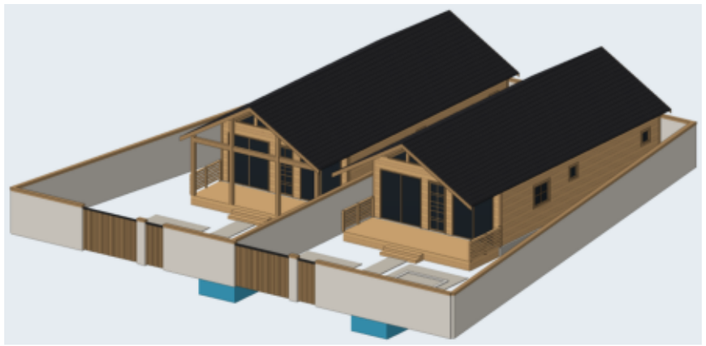


منظور أمامي من اليمين

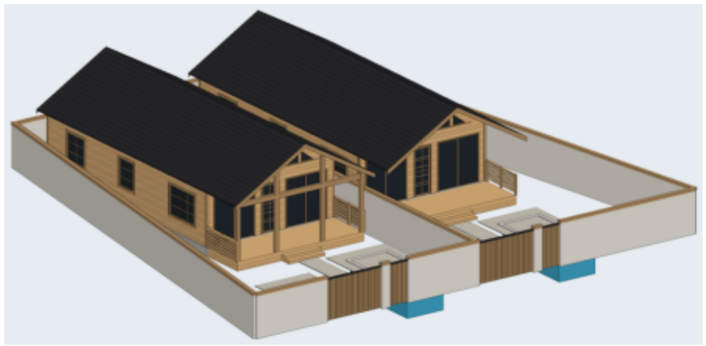


المنظور الخلفي

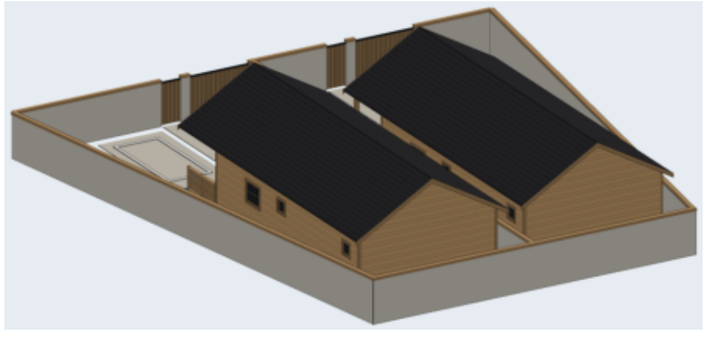

منظور خلفي من اليمين

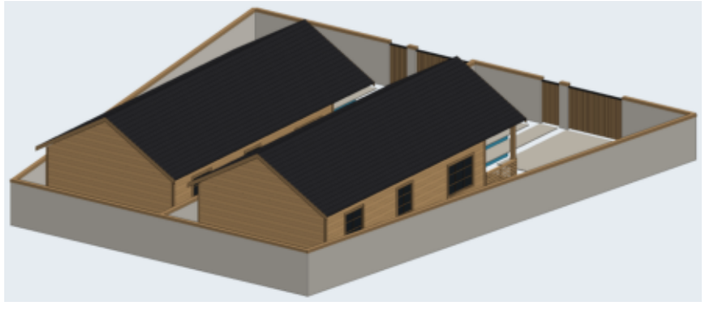


منظر علوي

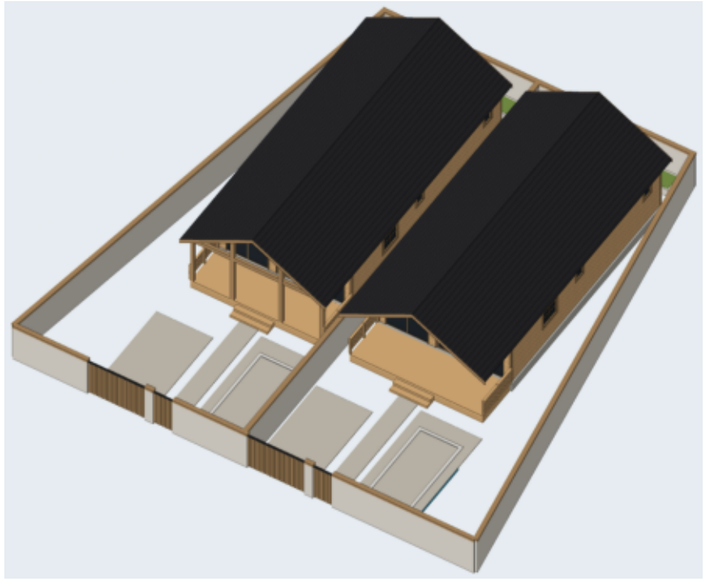

مصنع وتد الأخشاب Watad Wood Factory	المشروع / العميل **شاليهين الهدا الاستثماري — غرفتين وصالة لكل شاليه — 7.00 × 12.62 = 88.3 م² × 2** **عميل — الهدا (استثماري)**	عنوان اللوحة **لقطات المنظور**	المقياس **—**	التاريخ **2026-10-23**	رقم اللوحة **A-08 (8/10)**

المقطع العلوي بالفرش


مقطع أفقي على ارتفاع 1.90 م — توزيع الفرش ومسار الحركة

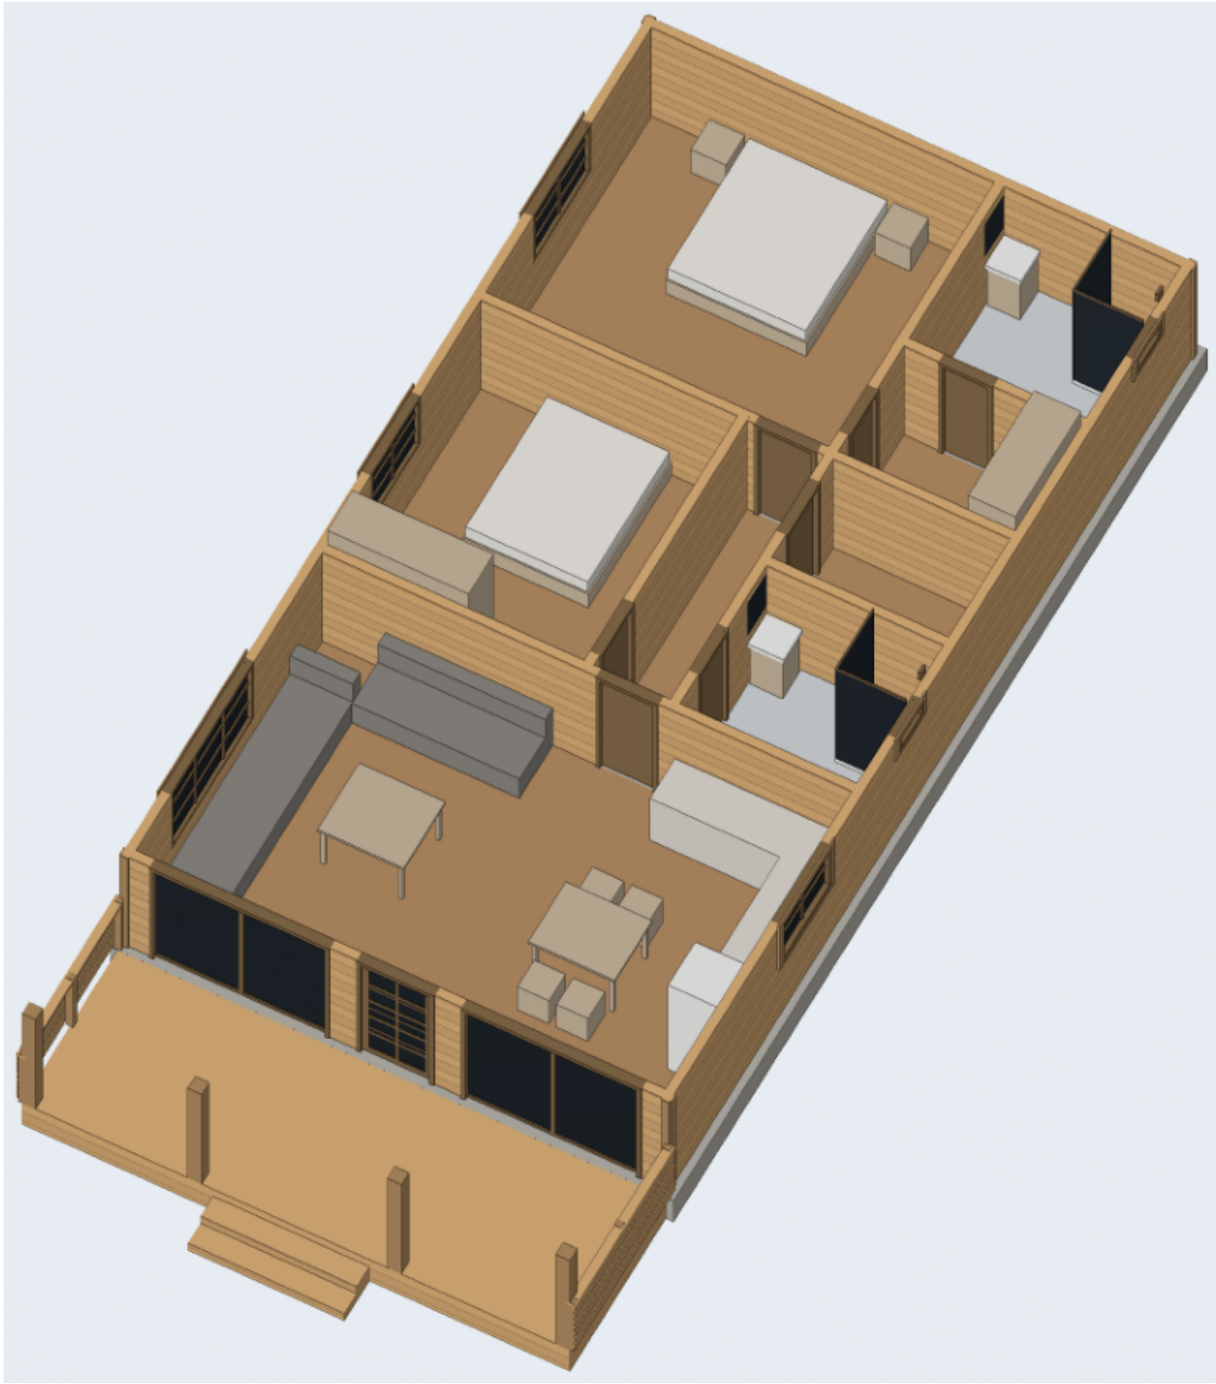

مصنع وتد الأخشاب Watad Wood Factory	المشروع / العميل	عنوان اللوحة	المقياس	التاريخ	رقم اللوحة
	شاليهين الهدا الاستثماري — غرفتين وصالة لكل شاليه — 7.00 × 12.62 = 88.3 م² × 2 عميل — الهدا (استثماري)	المقطع العلوي بالفرش	—	2026-10-23	A-09 (9/10)

المنظور ثلاثي الأبعاد والمواد

النمط: جوزي غامق + إطارات سوداء — رندر واقعي بخامات حقيقية

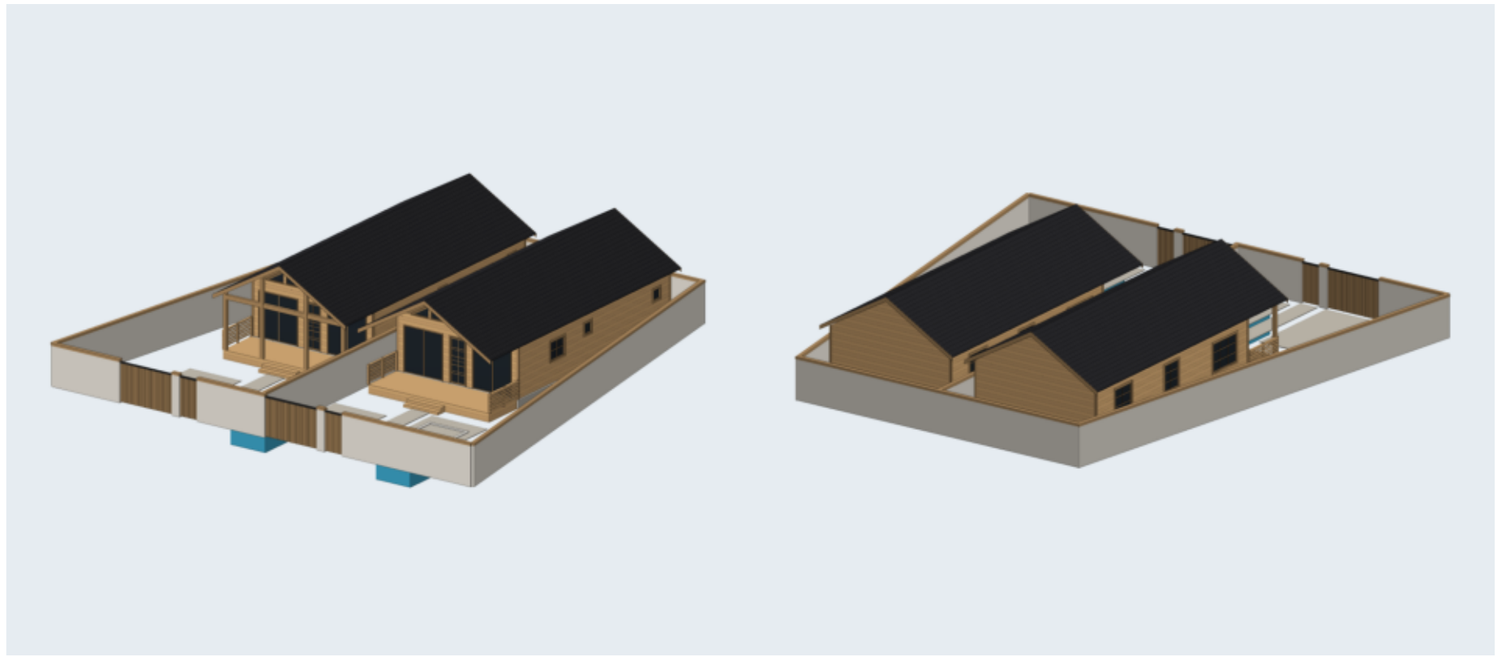

جدول المواد والألوان

الخشب / الصبغة

خشب طبيعي فاتح (بدون صبغة)

القرميد

قرميد رمادي غامق

الزجاج

زجاج عاكس غامق

إطارات الشبابيك والأبواب

إطار خشب بنفس الصبغة أغمق

الكنار والزوايا

نفس الصبغة أغمق درجة


الصبة

خرسانة 45 سم


الدربزين: ألواح أفقية متقاربة (عصري)

تقسيم الشبابيك: بدون | الباب الرئيسي: سحاب زجاج

أنواع الدربزين المعتمدة (من مشاريع المصنع)

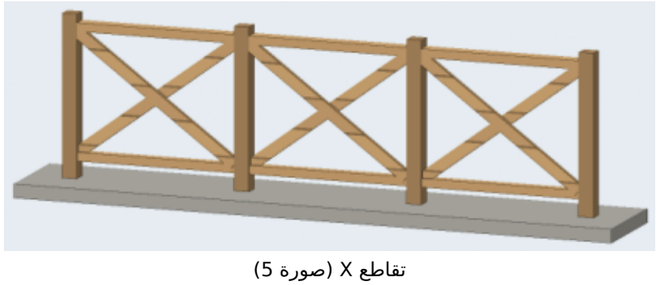

تقاطع X (صورة 5)

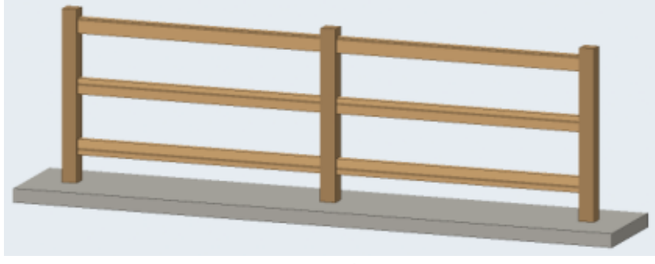

3 مرابيع أفقية (صورة 2)



قوائم رأسية متقاربة (صورة 1)

المشروع / العميل	عنوان اللوحة	المقياس	التاريخ	رقم اللوحة
مصنع وتد الأخشاب Watad Wood Factory **شاليهين الهدا الاستثماري — غرفتين وصالة لكل شاليه — 7.00 × 12.62 = 88.3 م² × 2** **عميل — الهدا (استثماري)**	**المنظور والمواد**	**—**	**2026-10-23**	**A-10 (10/10)**