


المنظور ثلاثي الأبعاد والمواد

النمط: جوزي غامق + إطارات سوداء — رندر واقعي بخامات حقيقية

جدول المواد والألوان

 

الخشب / الصبغة

خشب طبيعي فاتح (بدون صبغة)



القرميد

قرميد رمادي غامق



الزجاج

زجاج عاكس غامق



إطارات الشبابيك والأبواب

إطار ألومنيوم أسود



الكنار والزوايا

نفس الصبغة أعمق درجة



الصبة

خرسانة 45 سم


الدريزين: ألواح أفقية متقاربة (عصري)

تقسيم الشبابيك: بدون | الباب الرئيسي: سحب زجاج


أنواع الدريزين المعتمدة (من مشاريع المصنع)



قوائم رأسية متقاربة (صورة 1)

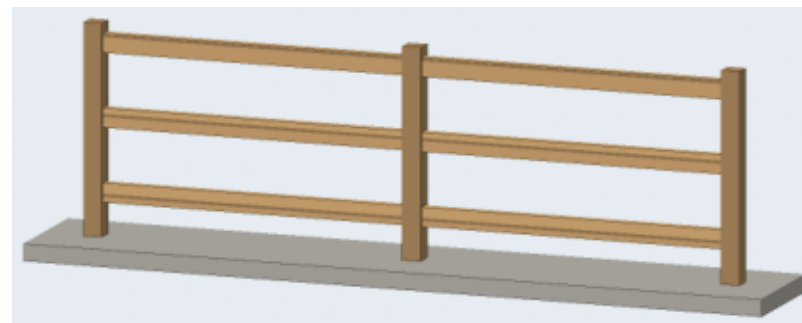

3 مربيع أفقية (صورة 2)

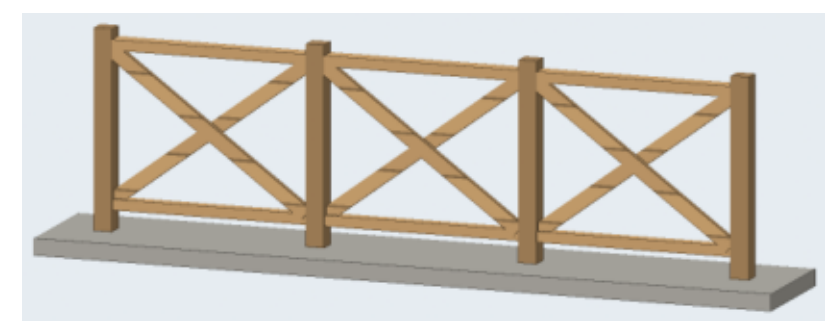

تقاطع X (صورة 5)

رقم اللوحة

W-01 (1/11)

التاريخ

2026-10-06

المقياس

1:50

عنوان اللوحة

المنظور والمواد

المشروع / العميل

مجلس 5x4 بواجهة زجاج
عميل — مجلس

مصنع وتد الأخشاب

Watad Wood Factory



Architectural floor plan of a room with a central seating area, a table, and a kitchen. The plan includes dimensions, labels for furniture, and a north arrow.

Room Dimensions: 500 (width) x 400 (depth).

Central Area: The central area is labeled "المجلس" (The Council) with dimensions 3.76 x 4.76 م (3.76 x 4.76 m) and 2 م 17.9 (2 m 17.9). It contains a "طاولة" (Table) and a "كبة" (Cushion).

Kitchen Area: The kitchen area is labeled "المطبخ" (The Kitchen) with dimensions 1.80 x 5.00 م (1.80 x 5.00 m). It contains a "كبة" (Cushion) and a "ش 1" (Sh 1) label.

Dimensions and Layout:

- Overall width: 500
- Overall depth: 400
- Top wall: 500
- Bottom wall: 500
- Left wall: 400
- Right wall: 400
- Top wall segments: 154, 100, 146
- Bottom wall segments: 20, 96, 14, 240, 14, 96, 20
- Central area dimensions: 3.76 x 4.76 م
- Kitchen area dimensions: 1.80 x 5.00 م


Labels and Furniture:

- المجلس (The Council)
- المطبخ (The Kitchen)
- كبة (Cushion)
- طاولة (Table)
- ش 1 (Sh 1)
- ر 1 (R 1)
- ب 1 (B 1)

North Arrow: A black arrow pointing upwards, labeled "ش" (Sh) for North.


Scale: 3 درجات 15 سم (3 degrees 15 cm)

المشروع / العمل	عنوان اللوحة	المقياس	التاريخ	رقم اللوحة
مصنع وتد الأخشاب Watad Wood Factory	مجلس 5×4 بواجهة زجاج عميل – مجلس	المسقط الأفقي	2026-10-06	W-02 (2/11)

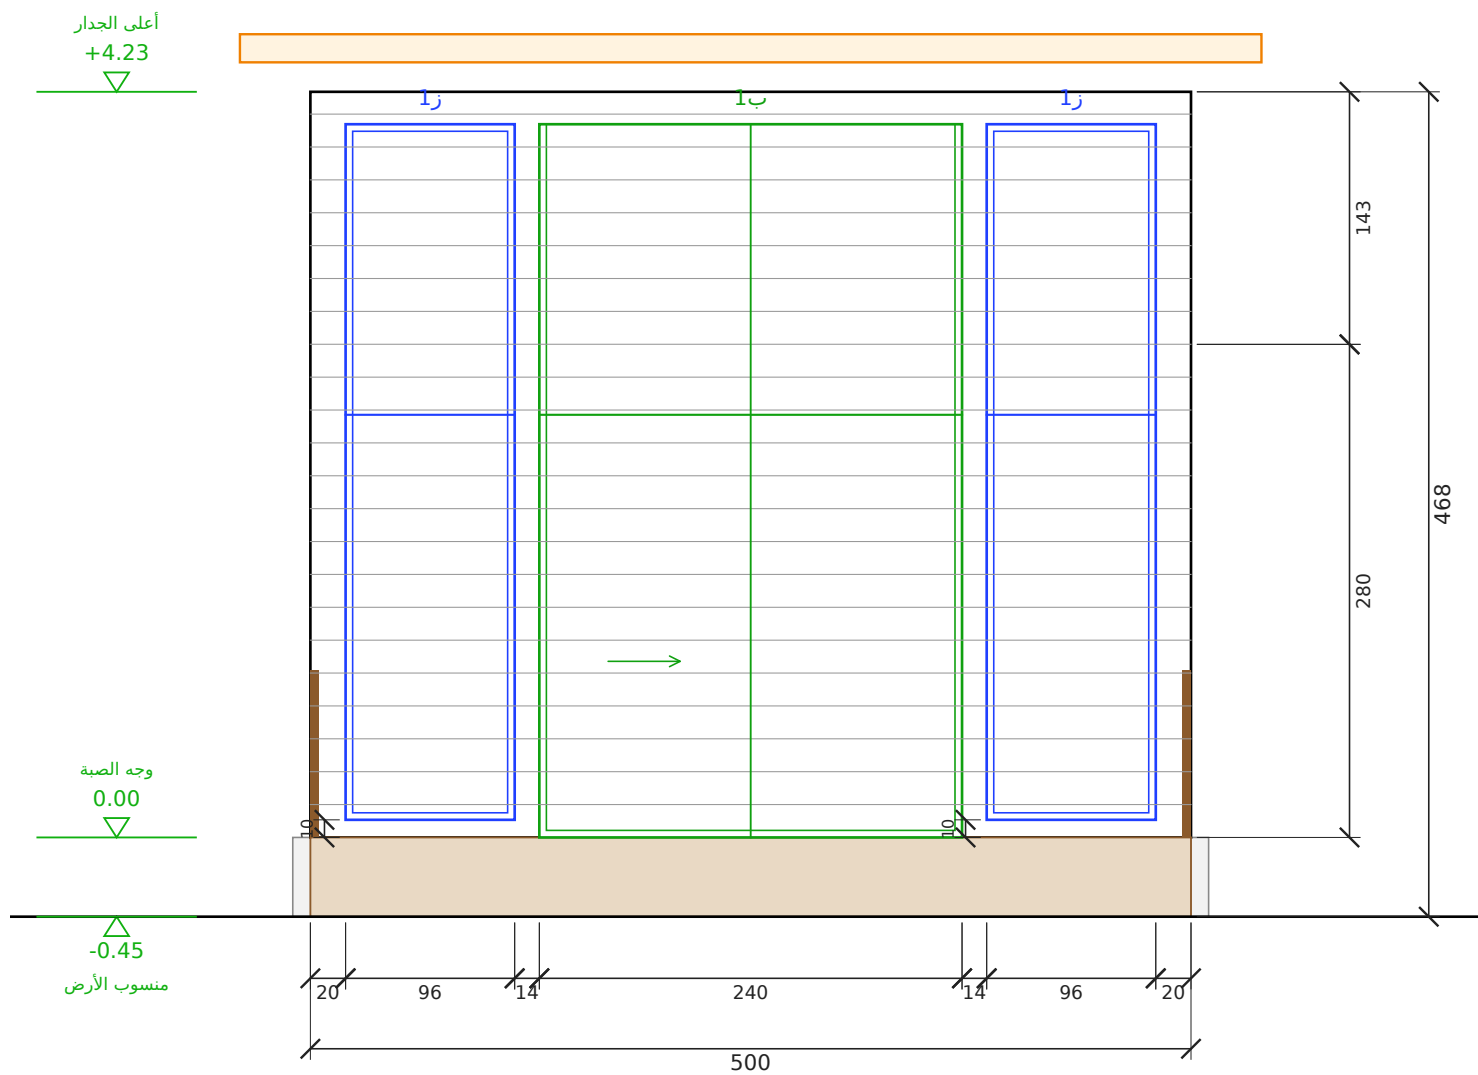

الواجهة الأمامية (زجاج)


مقياس 1:50 | الوحدة: سم

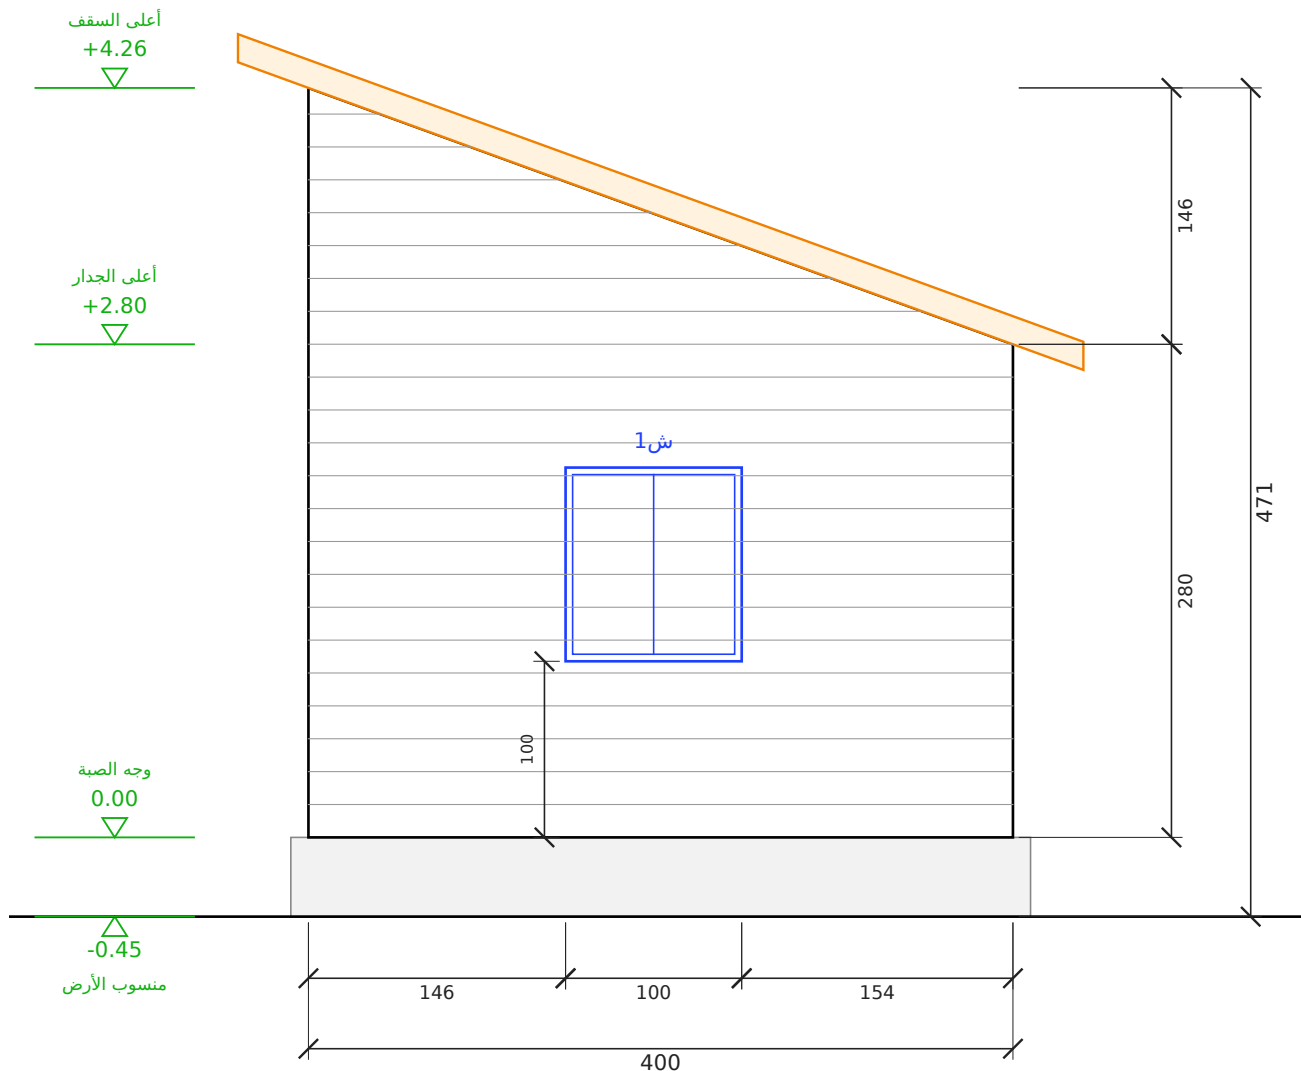

الواجهة الشرقية


مقياس 1:50 | الوحدة: سم

رقم اللوحة	التاريخ	المقياس	عنوان اللوحة	المشروع / العميل	مصنع وتد الأخشاب Watad Wood Factory
W-03 (3/11)	2026-10-06	1:50	الواجهة الأمامية (زجاج) والواجهة الشرقية	مجلس 5x4 بواجهة زجاج عميل - مجلس	

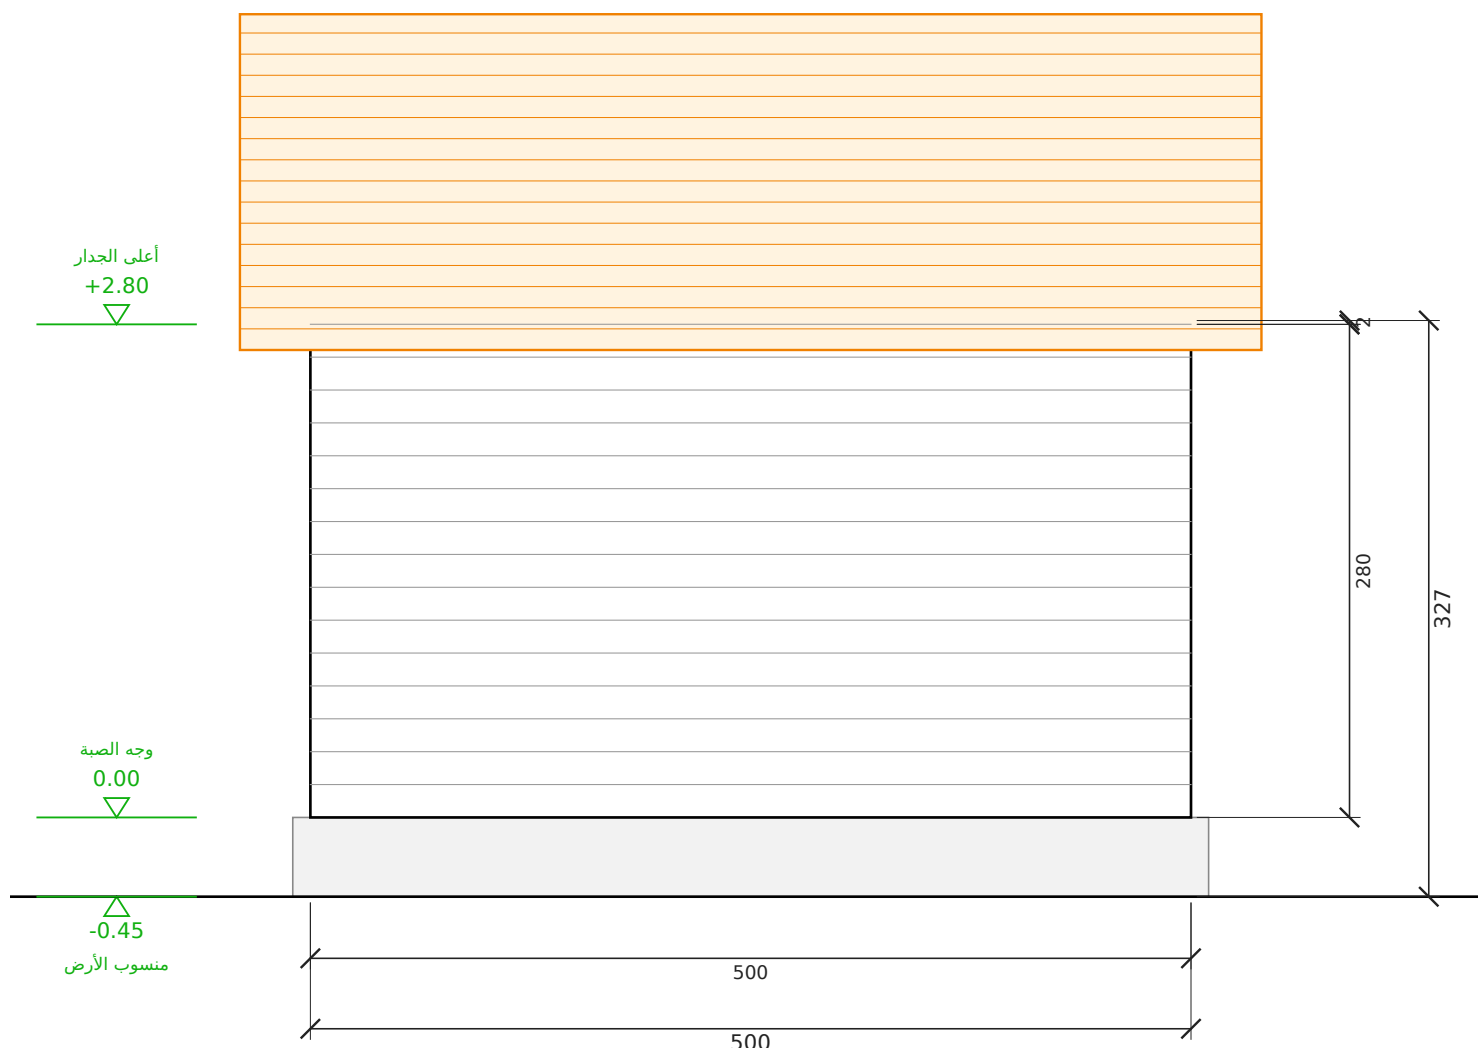

الواجهة الخلفية

مقياس 1:50 | الوحدة: سم

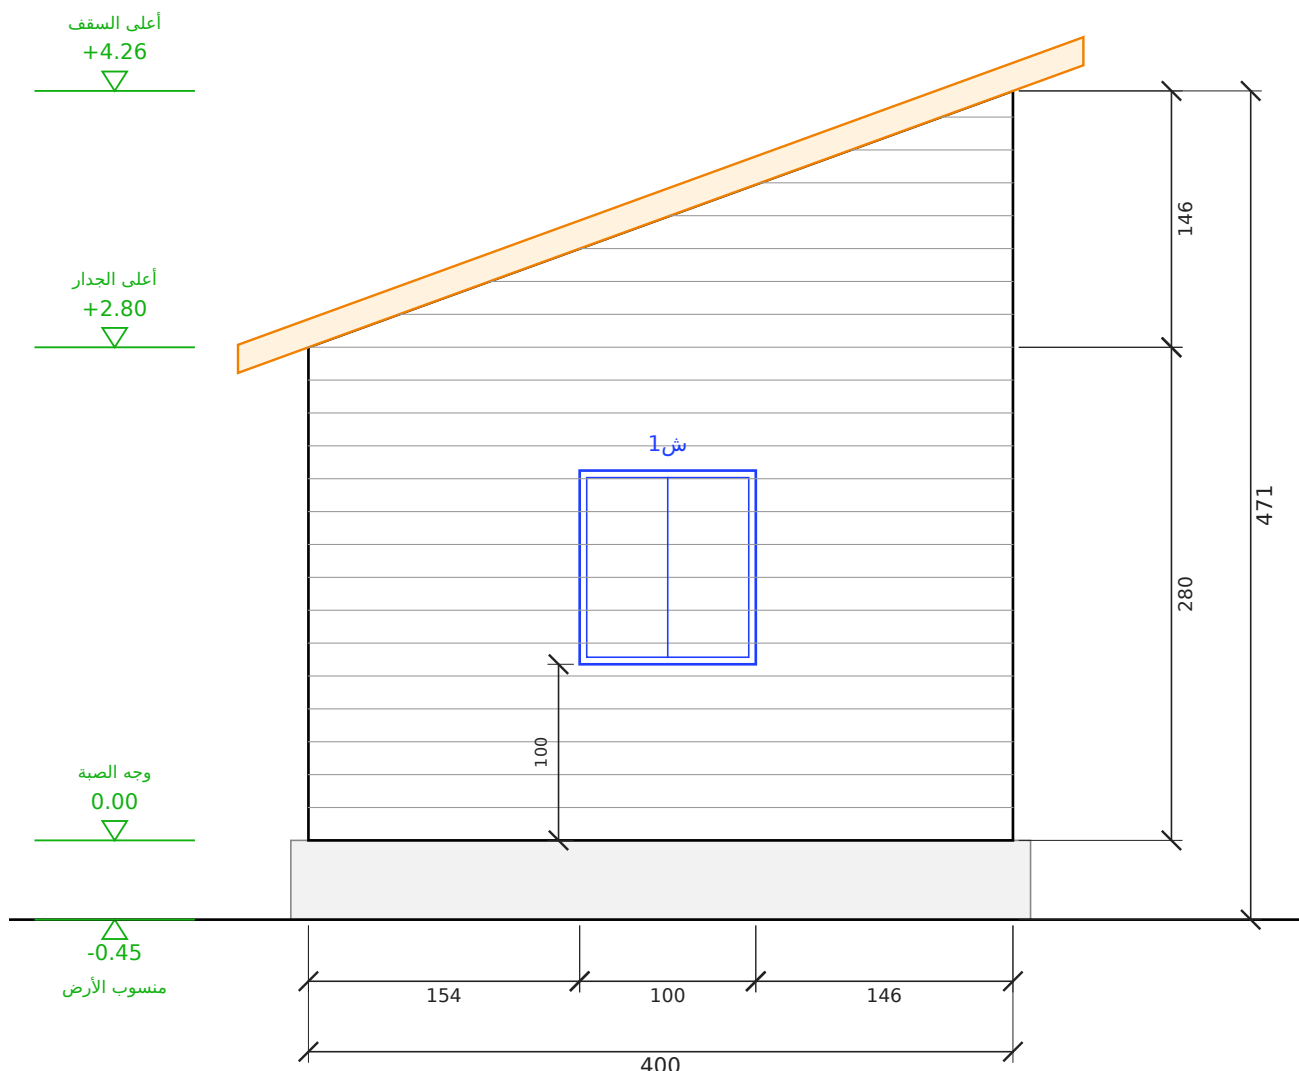


الواجهة الغربية



مقياس 1:50 | الوحدة: سم

رقم اللوحة	التاريخ	المقياس	عنوان اللوحة	المشروع / العميل	مصنع وتد الأخشاب Watad Wood Factory
W-04 (4/11)	2026-10-06	1:50	الواجهة الخلفية والواجهة الغربية	مجلس 5x4 بواجهة زجاج عميل - مجلس	

مسقط السقف (مائل باتجاه واحد)
ررف 40 سم من كل جهة | مقياس 1:50

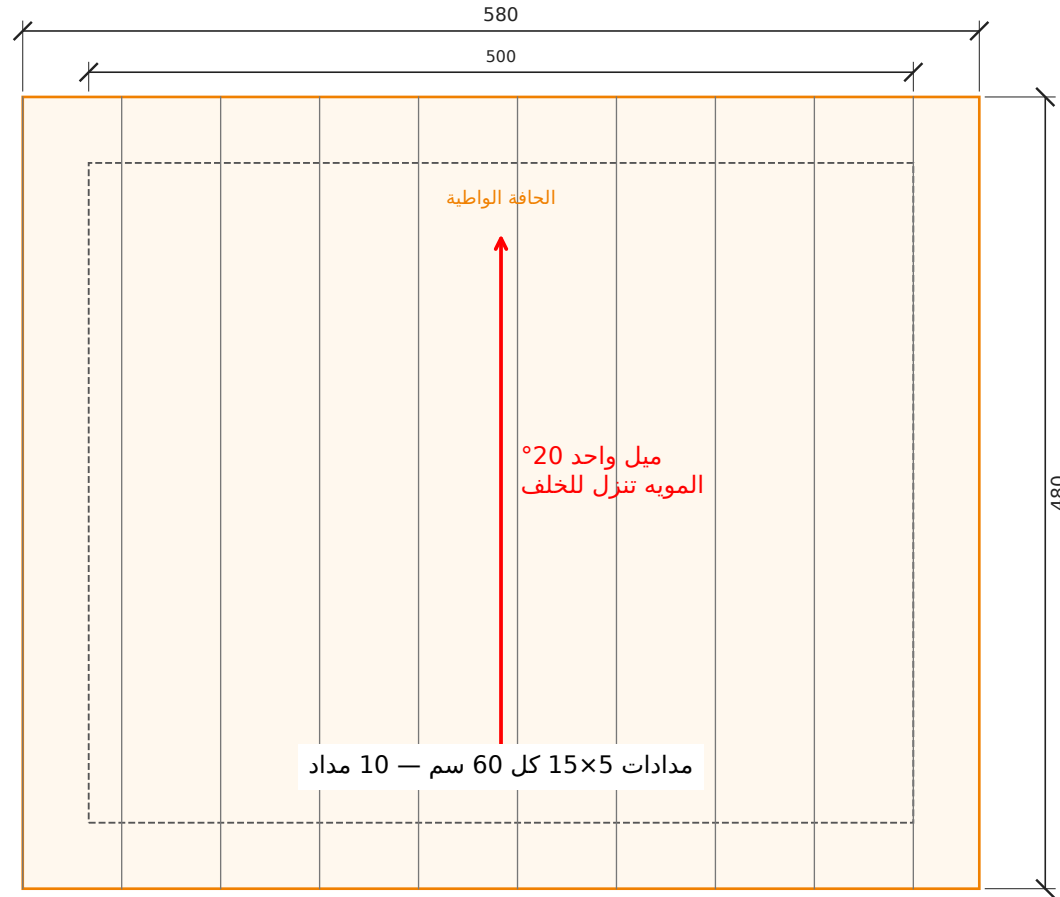

قطاع عرضي أ-أ
مقياس 1:50 | الوحدة: سم

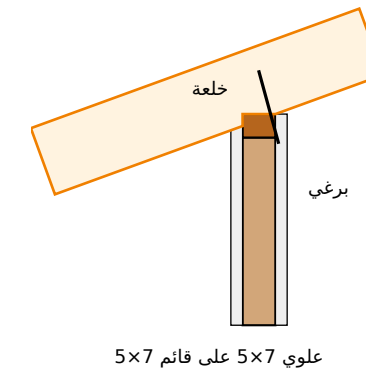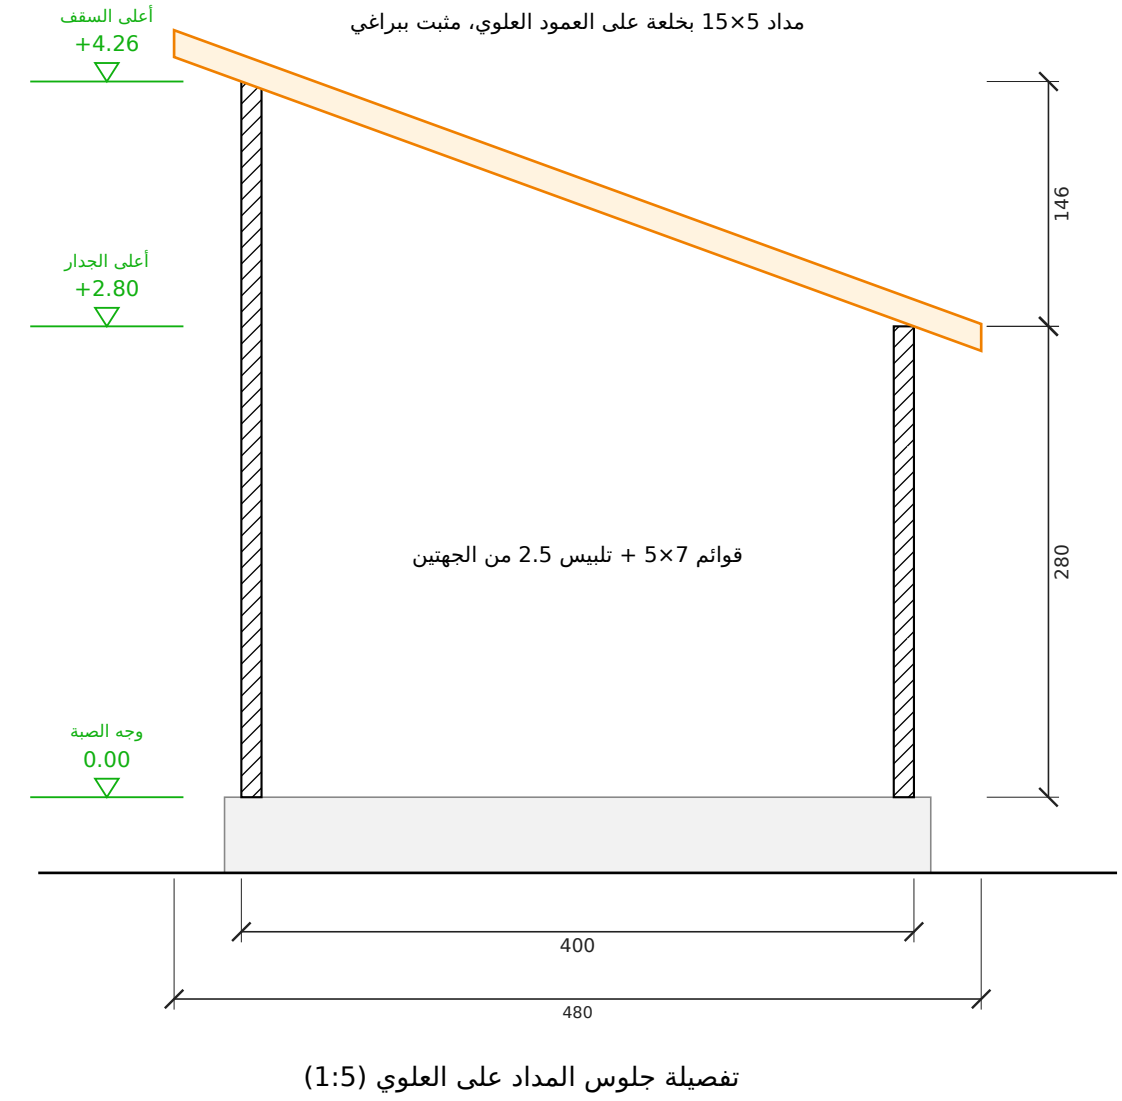

رقم اللوحة

W-05 (5/11)

التاريخ

2026-10-06

المقياس

1:50

عنوان اللوحة

مسقط السقف والقطاع

المشروع / العميل

مجلس 5×4 بواجهة زجاج
عميل — مجلس

مصنع وتد الأخشاب
Watad Wood Factory



جدول مقاسات الأبواب والشبابيك
مقاس الفتحة الصافي في الجدار - الوحدة: سم

الرمز	النوع	العرض (سم)	الارتفاع (سم)	ارتفاع الجلسة (سم)	العدد	الموقع
ب1	باب	240	405	-	1	الأمامية (زجاج)
ر1	شباك	96	395	10	2	الأمامية (زجاج) 2
ش1	شباك	100	110	100	2	الشرقية - الغربية

الإجمالي: أبواب 1 - شبابيك 4

جدول المساحات وبيانات المشروع والتسعير

جدول المساحات

م	الفراغ	الأبعاد (م)	المساحة (م2)
1	المجلس	4.76 × 3.76	17.90
	المساحة الصافية الداخلية		17.90
	التراس المسقوف (مجاناً)	5.00 × 1.80	9.00
	المساحة الإجمالية المبنية	5.00 × 4.00	20.00

بيانات المشروع

البند	البيان
المشروع	مجلس 5×4 بواجهة زجاج
العميل	عميل — مجلس
الموقع	—
الاستخدام	مجلس
التاريخ	2026-10-06
نظام البناء	هيكل خشب 5×7 + تليس 2.5 سم من الجهتين
السقف	مائل باتجاه واحد 20° — قرميد معدني


التسعير

البند	القيمة
المساحة المبنية (م2)	20.00
سعر المتر المربع	1,096 ريال
الإجمالي	21,920 ريال


ملاحظات:

- السعر للمساحة المبنية حسب المخطط المعتمد.
- الصبة والتמידات الخارجية على العميل ما لم يُذكر غير ذلك.

تأطير جدار جنوب — الطول 488 سم، الارتفاع 426 سم

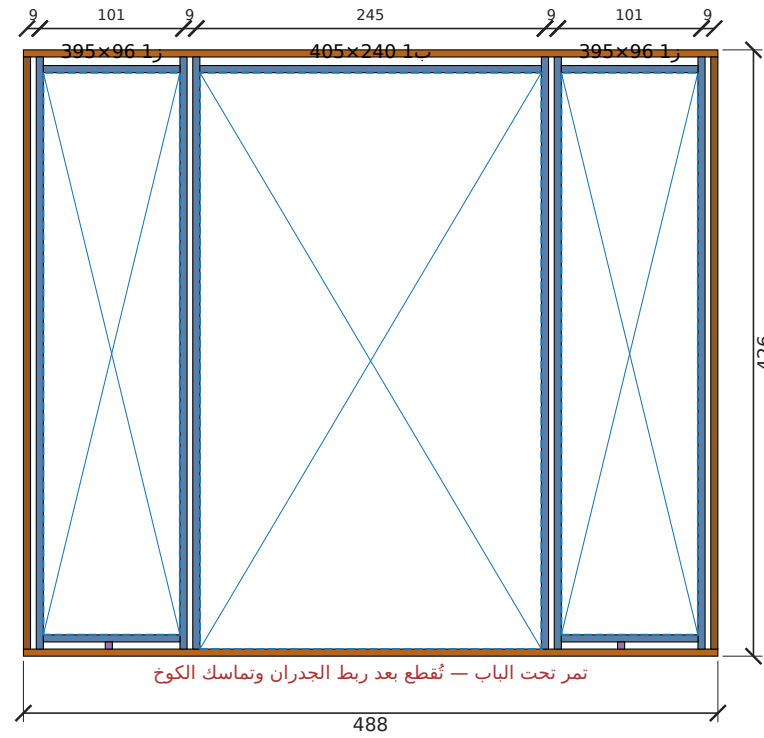

تأطير جدار شرق — الطول 388 سم، الارتفاع 280 سم

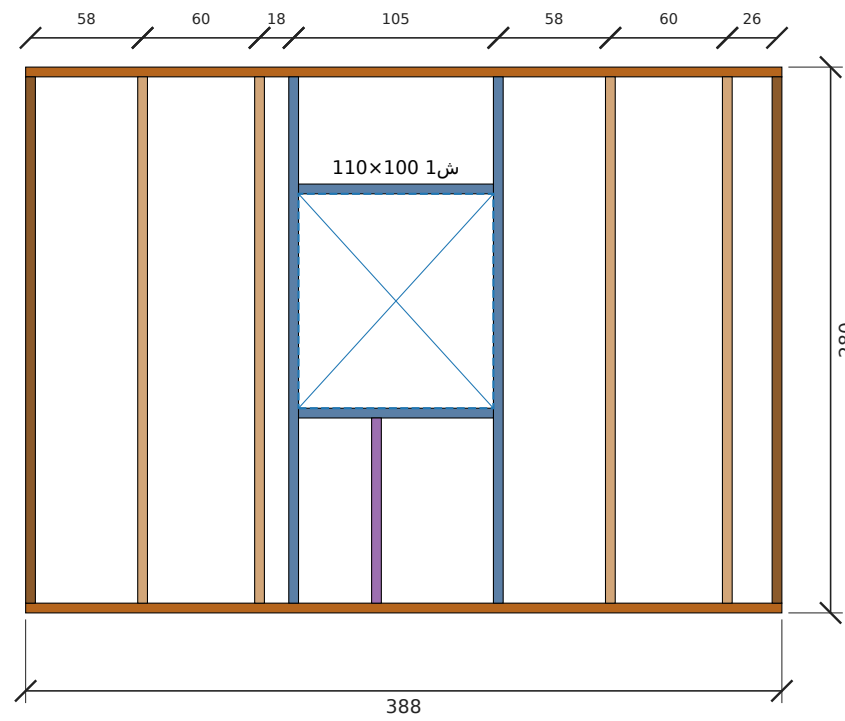

قاعدة سفلية علوي عمود عمود زاوية جنب فتحة رأس فتحة جلسة شباك عمود قصير

رقم اللوحة

W-08 (8/11)

التاريخ

2026-10-06

المقياس

—

عنوان اللوحة

لوحات التأطير (للورشة)


المشروع / العميل

مجلس 5×4 بواجهة زجاج
عميل — مجلس


مصنع وتد الأخشاب
Watad Wood Factory



تأطير جدار شمال — الطول 488 سم، الارتفاع 280 سم

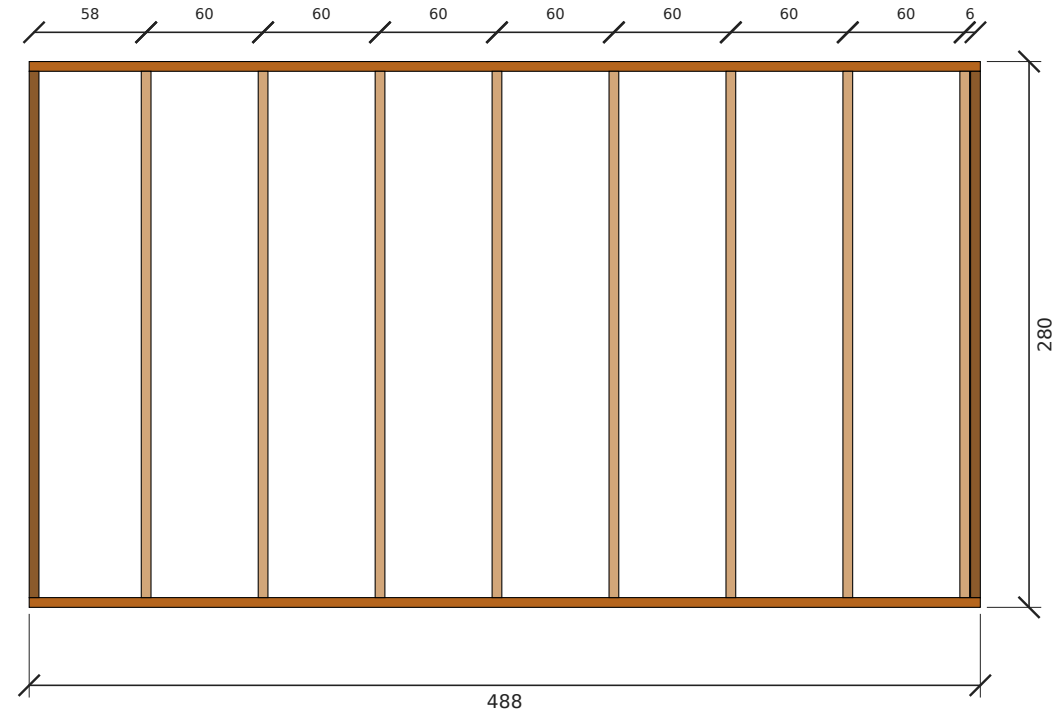

تأطير جدار غرب — الطول 388 سم، الارتفاع 280 سم

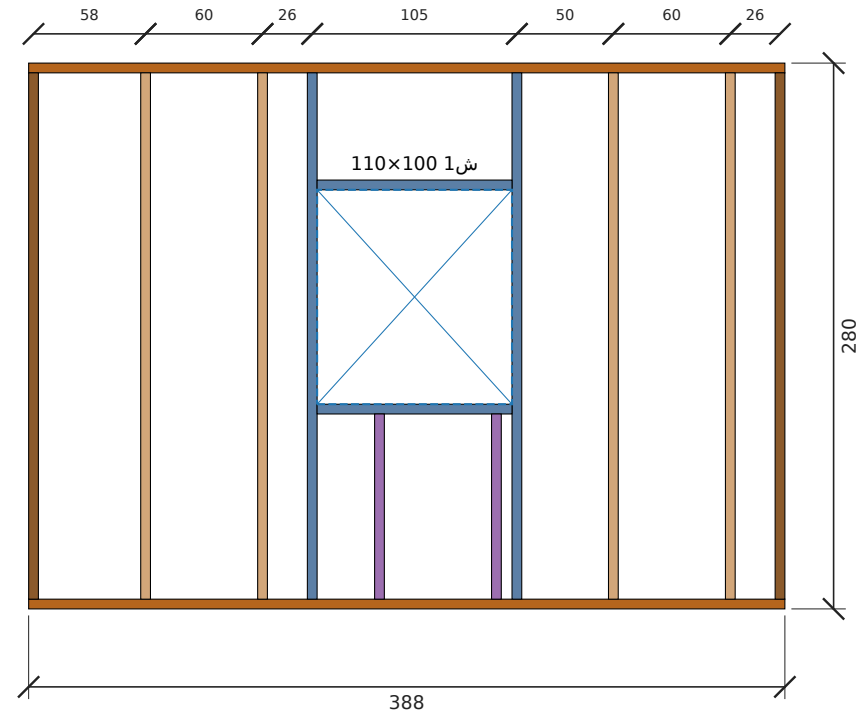

قاعدة سفلية علوي عمود عمود زاوية جنب فتحة رأس فتحة جلسة شباك عمود قصير

رقم اللوحة

W-09 (9/11)

التاريخ

2026-10-06

المقياس

—

عنوان اللوحة

لوحات التأطير (للورشة)

المشروع / العميل

مجلس 5x4 بواجهة زجاج
عميل — مجلس

مصنع وتد الأخشاب
Watad Wood Factory



جدول الكميات وخطة تقطيع الطبلیات

البند	القيمة
الارتفاع المطلوب / المعتمد	280 / 280 سم
السقف	جملون 20° — قمة 426 سم من وجه الصبة
المدادات 15×5	10 مداد (10 لكل جهة) × 511 سم — من طبلية 520
طبلیات الطريقة الأولى (مداد + عمود)	10 طبلية × 520 سم
طبلیات الطريقة الثانية (3 أعمدة)	10 طبلية × 320 سم
طبلیات الطريقة الثانية (طويلة)	2 طبلية × 520 سم
إجمالي الطبلیات 22.5×5	22
إجمالي قطع 5×7	56
قائمة تقطيع 5×7	488سم×4 416سم×8 388سم×4 270سم×26 240سم×1 100سم×4 96سم×4 95سم×3 5سم×2
ألواح تلبیس 2.5 سم	99 لوح × 400 سم (مجموع الصفوف 385.6 م، 8 وجه)
أسمنت بورد 12 مم (244×122)	0 لوح (داخل دورات المياه)
العزل	بدون (غير مطلوب)
الصبة	یجهزها العميل — 20 سم، مفرغة تحت دورات المياه

مراجعة التصميم مقابل قواعد المصنع

النوع	البند	التفاصيل	المقترح
ملاحظة	بحر المدادات	أطول بحر بدون جدار داخلي يحمل المداد: جهة أ: 400 سم. يحتاج رقم المصنع لأقصى بحر مسموح لتحديد المدادات اللي تُقوّى 5×20.	
ملاحظة	الصبة والدرج	ارتفاع الصبة 45 سم ← 3 درجة بقائمة 15.0 سم.	
ملاحظة	مناسيب رؤوس الفتحات	رؤوس الأبواب والشبابيك على مناسيب مختلفة: 210، 405 سم.	
سؤال	يحتاج تأكيد	أقصى بحر للمداد بدون جدار داخلي قبل إضافة تقوية 5×7 (مداد 5×20)؟	
سؤال	يحتاج تأكيد	التغطية الصافية للوح التلبيس بعد التعشيق (مستنتجة مؤقتاً 18.67 سم من 280/15)؟	
سؤال	يحتاج تأكيد	هل يوضع أعمدة قصيرة فوق رأس الشباك/الباب إلى العلوي؟	
سؤال	يحتاج تأكيد	مكان الوصلة في القاعدة والعلوي إذا الجدار أطول من الطيلية؟	