

Architectural floor plan of a room with a central seating area, a table, and a kitchen. The plan includes dimensions, labels for furniture, and a north arrow.

Room Dimensions: 500 (width) x 400 (depth).

Central Area: The central area is labeled "المجلس" (The Council) with dimensions 3.76 x 4.76 م (3.76 x 4.76 m) and 2 م 17.9 (2 m 17.9). It contains a "طاولة" (Table) and a "كبة" (Cushion).

Kitchen Area: The kitchen area is labeled "المطبخ" (The Kitchen) with dimensions 1.80 x 5.00 م (1.80 x 5.00 m). It contains a "كبة" (Cushion) and a "ش 1" (Sh 1) label.

Dimensions and Layout:


- Overall width: 500
- Overall depth: 400
- Top wall: 500
- Left wall: 400
- Right wall: 400
- Bottom wall: 500
- Top wall offset: 154
- Left wall offset: 100
- Right wall offset: 100
- Bottom wall offset: 146
- Top wall offset: 154
- Left wall offset: 100
- Right wall offset: 100
- Bottom wall offset: 146
- Top wall offset: 154
- Left wall offset: 100
- Right wall offset: 100
- Bottom wall offset: 146

Labels and Furniture:

- المجلس (The Council)
- المطبخ (The Kitchen)
- كبة (Cushion)
- ش 1 (Sh 1)
- طاولة (Table)
- التراس (The Terrace)
- 3 درجات 15 سم (3 steps 15 cm)


North Arrow: A black arrow pointing upwards, labeled "ش" (North).

المشروع / العمل	عنوان اللوحة	المقياس	التاريخ	رقم اللوحة
مصنع وتد الأخشاب Watad Wood Factory	مجلس 5×4 بواجهة زجاج عميل — مجلس	المسقط الأفقي	2026-10-06	A-01 (1/9)

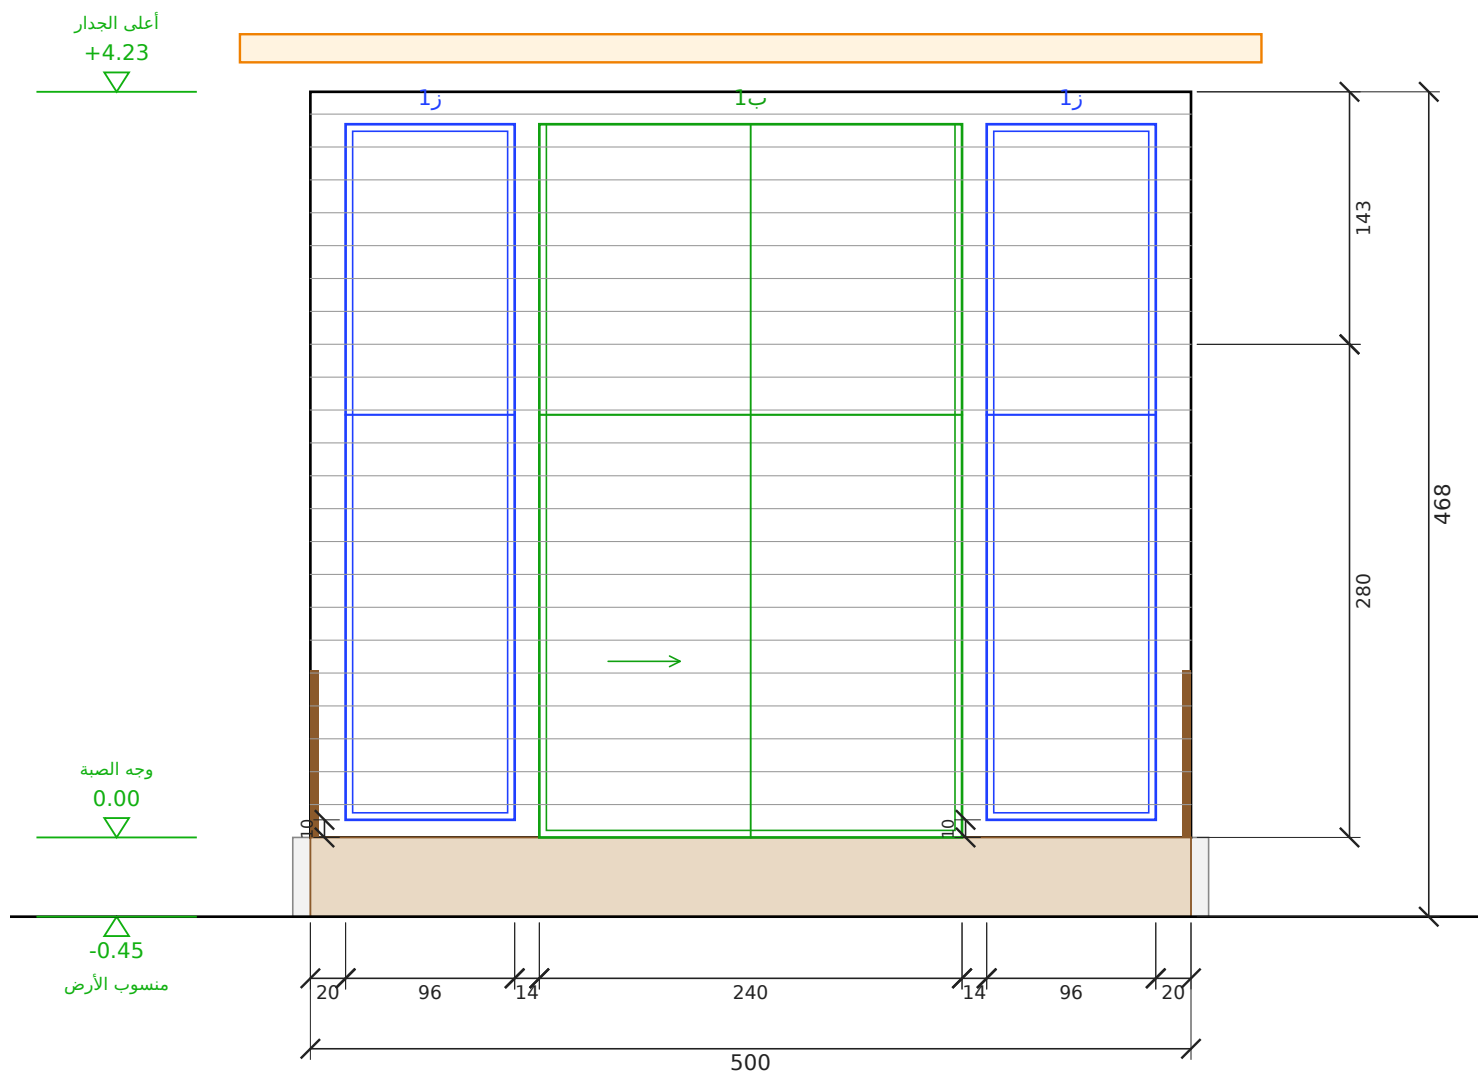

الواجهة الأمامية (زجاج)


مقياس 1:50 | الوحدة: سم

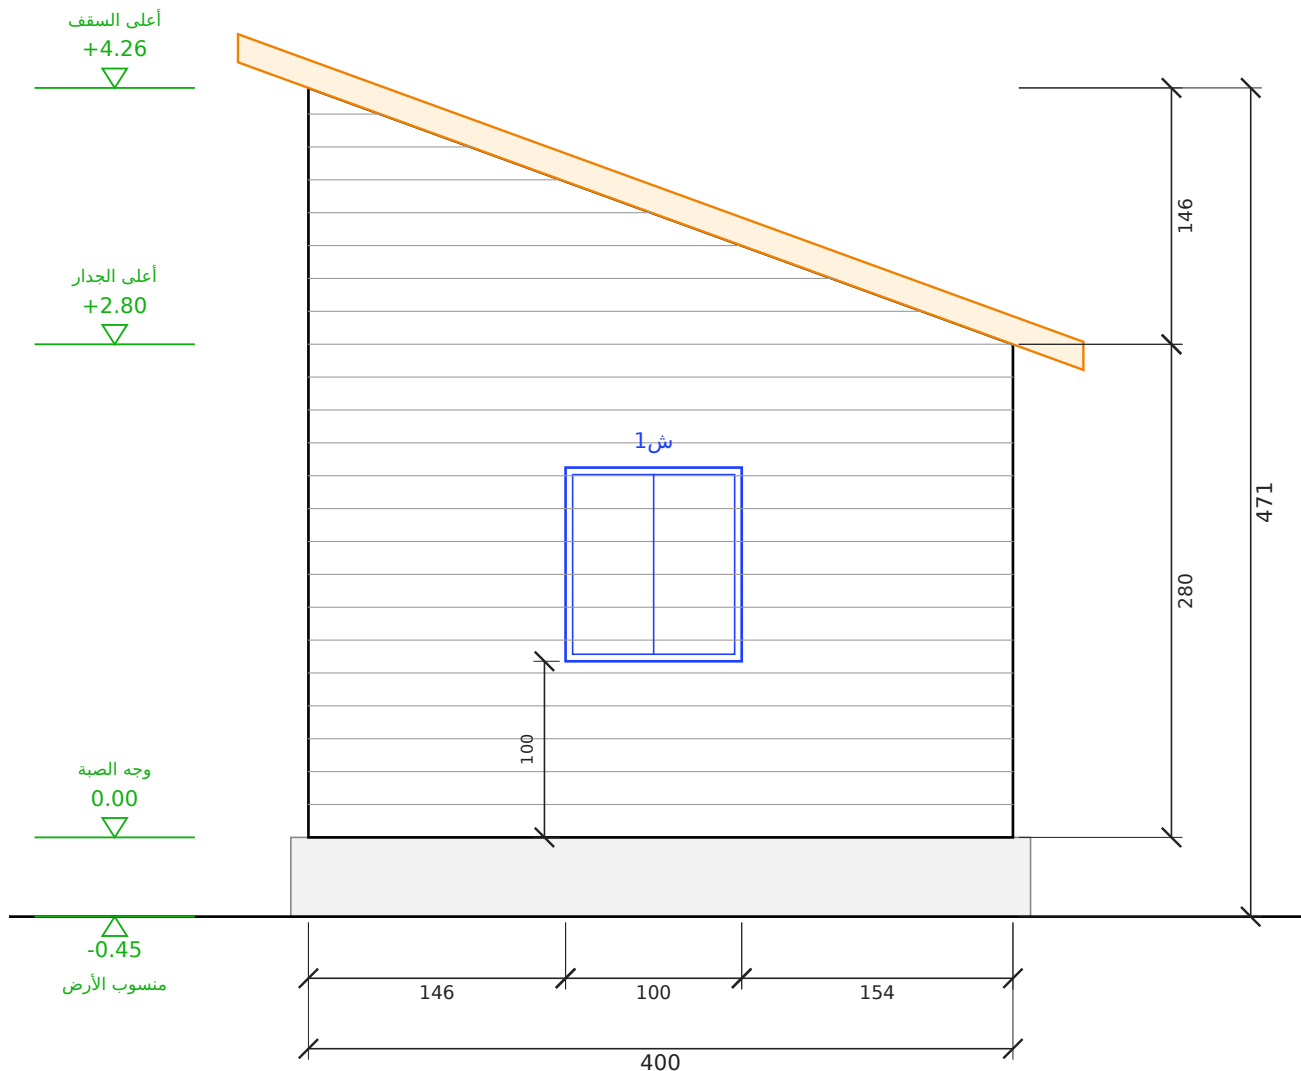

الواجهة الشرقية


مقياس 1:50 | الوحدة: سم

رقم اللوحة	التاريخ	المقياس	عنوان اللوحة	المشروع / العميل	مصنع وتد الأخشاب Watad Wood Factory
A-02 (2/9)	2026-10-06	1:50	الواجهة الأمامية (زجاج) والواجهة الشرقية	مجلس 5x4 بواجهة زجاج عميل - مجلس	

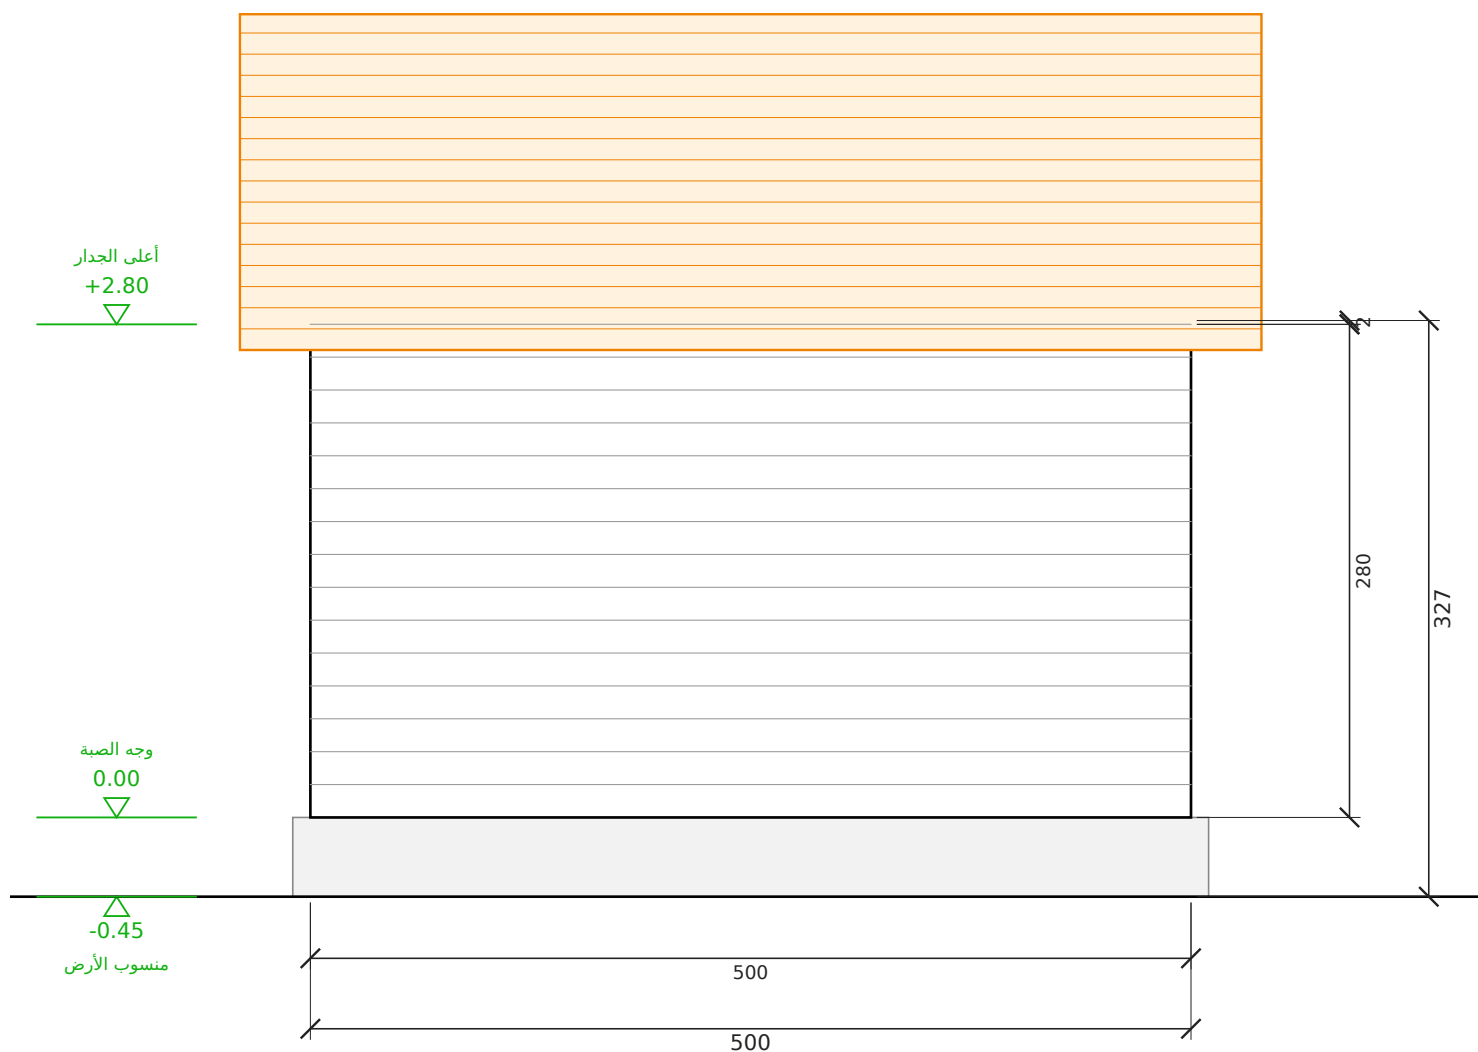

الواجهة الخلفية

مقياس 1:50 | الوحدة: سم

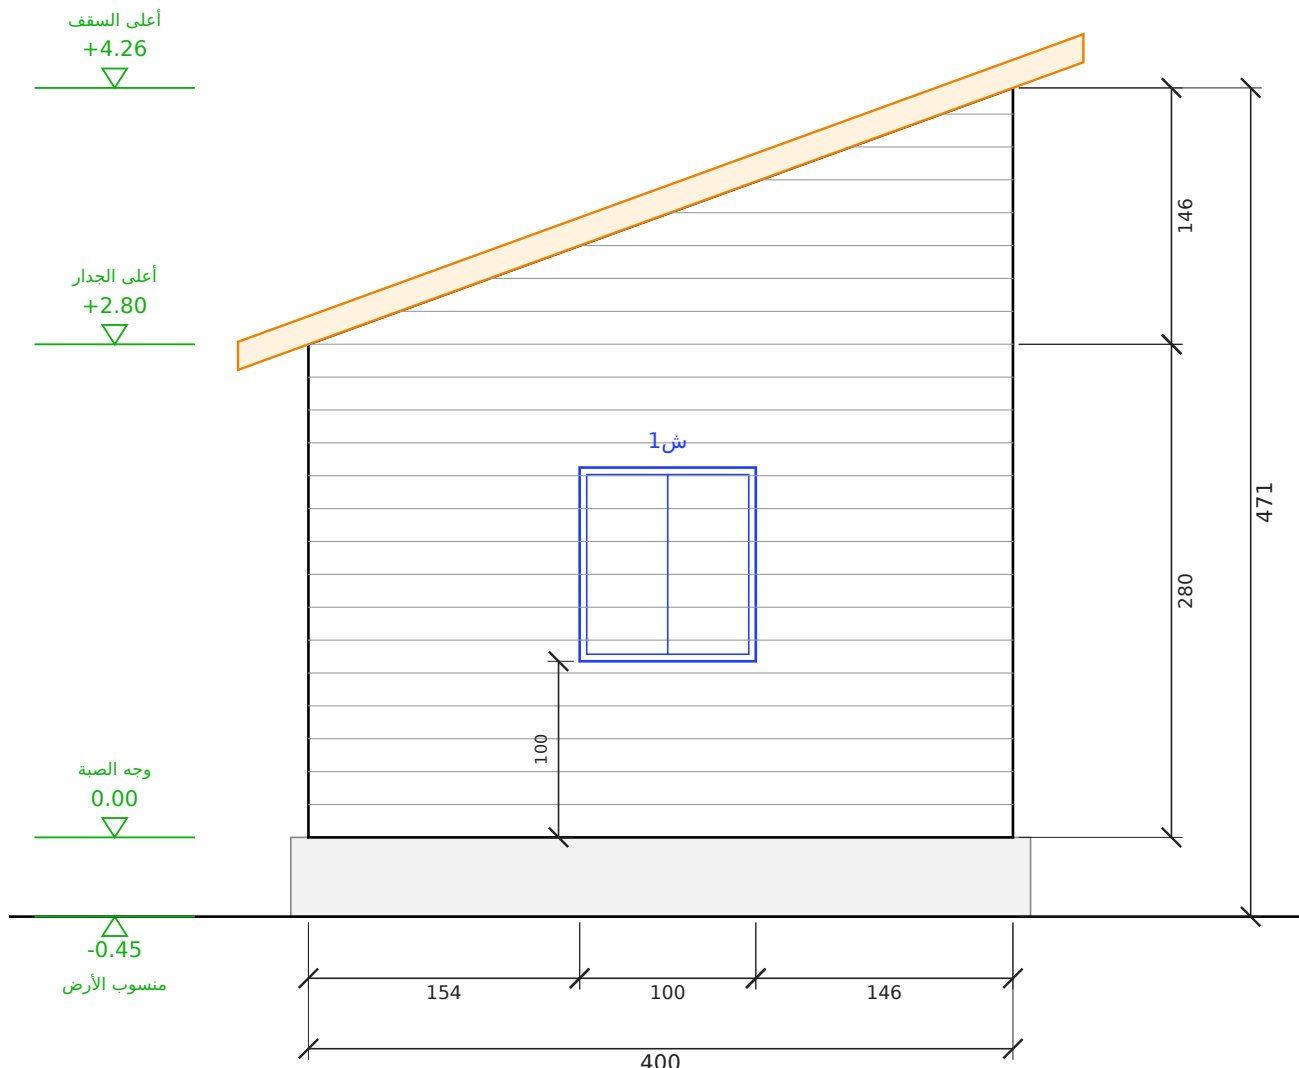


الواجهة الغربية



مقياس 1:50 | الوحدة: سم

رقم اللوحة	التاريخ	المقياس	عنوان اللوحة	المشروع / العميل	مصنع وتد الأخشاب Watad Wood Factory
A-03 (3/9)	2026-10-06	1:50	الواجهة الخلفية والواجهة الغربية	مجلس 5x4 بواجهة زجاج عميل - مجلس	

مسقط السقف (مائل باتجاه واحد)
رفر 40 سم من كل جهة | مقياس 1:50

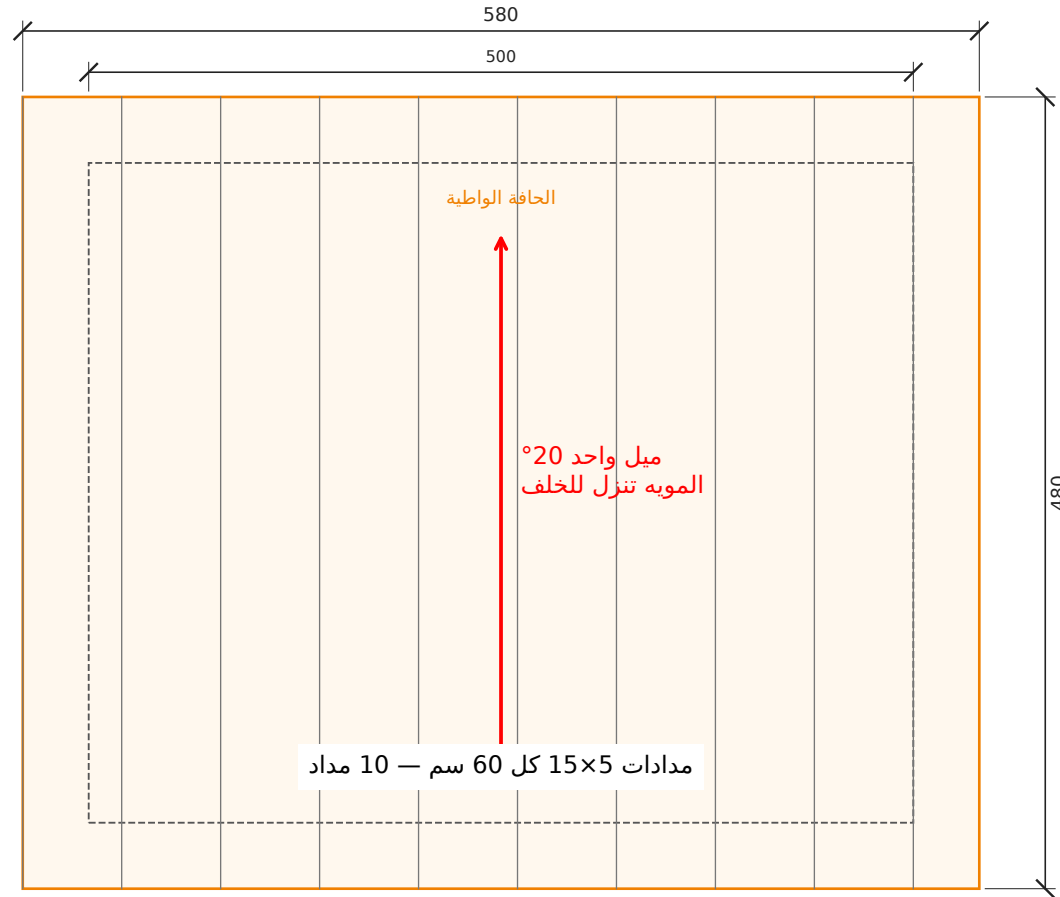

قطاع عرضي أ-أ
مقياس 1:50 | الوحدة: سم

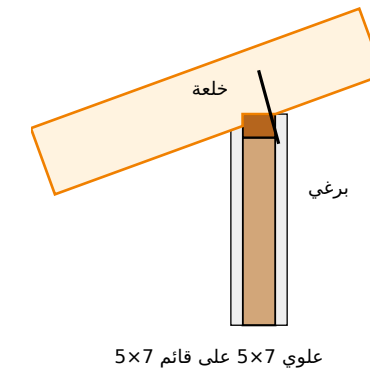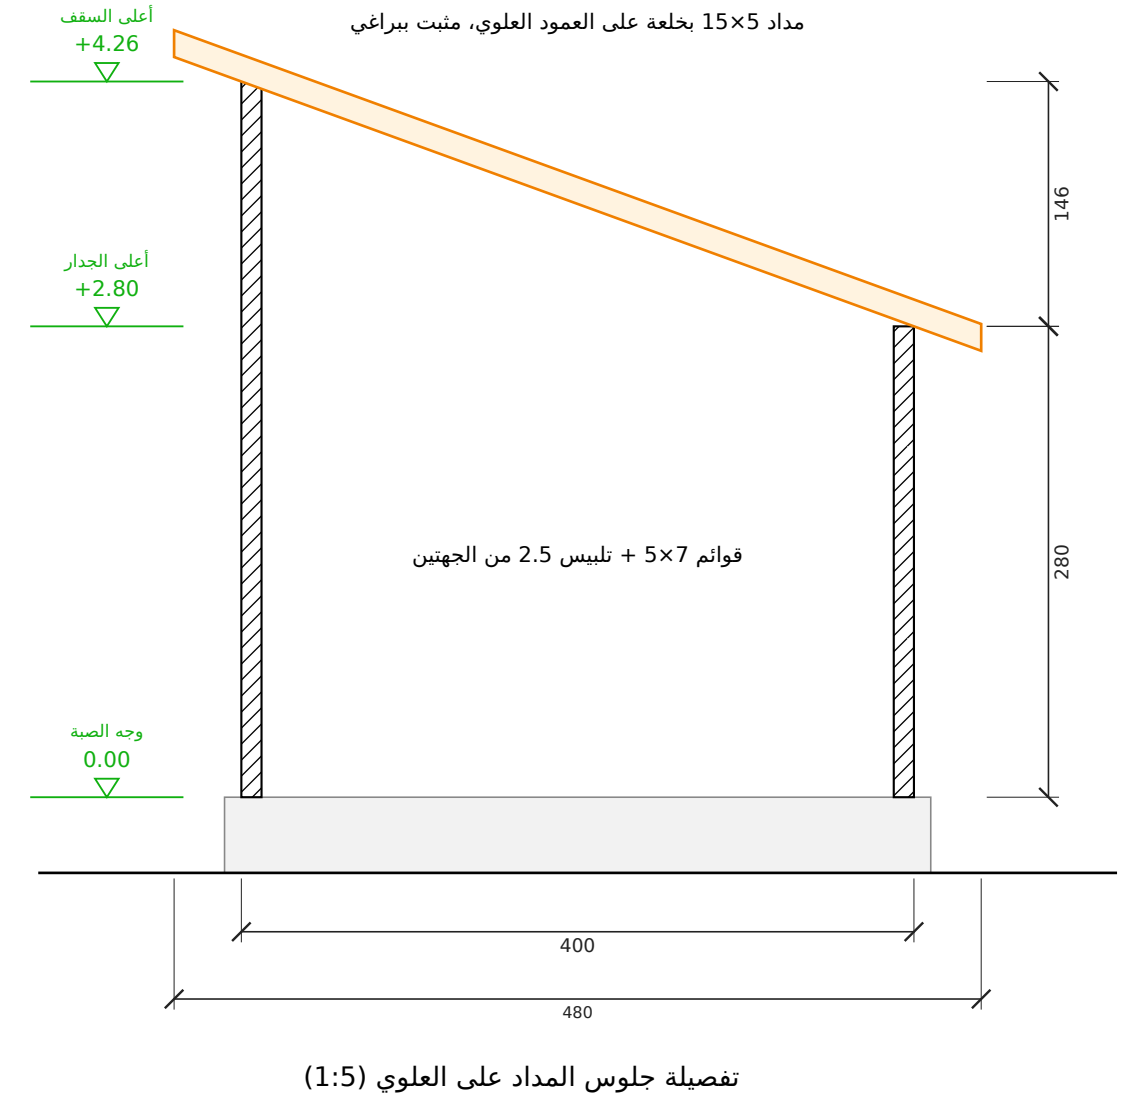

رقم اللوحة

A-04 (4/9)

التاريخ

2026-10-06

المقياس

1:50

عنوان اللوحة

مسقط السقف والقطاع

المشروع / العميل

مجلس 5×4 بواجهة زجاج
عميل — مجلس

مصنع وتد الأخشاب
Watad Wood Factory



جدول مقاسات الأبواب والشبابيك
مقاس الفتحة الصافي في الجدار - الوحدة: سم

الرمز	النوع	العرض (سم)	الارتفاع (سم)	ارتفاع الجلسة (سم)	العدد	الموقع
ب1	باب	240	405	-	1	الأمامية (زجاج)
ر1	شباك	96	395	10	2	الأمامية (زجاج) 2
ش1	شباك	100	110	100	2	الشرقية - الغربية

الإجمالي: أبواب 1 - شبابيك 4

جدول المساحات وبيانات المشروع والتسعير

جدول المساحات

م	الفراغ	الأبعاد (م)	المساحة (م2)
1	المجلس	4.76 × 3.76	17.90
	المساحة الصافية الداخلية		17.90
	التراس المسقوف (مجاناً)	5.00 × 1.80	9.00
	المساحة الإجمالية المبنية	5.00 × 4.00	20.00

بيانات المشروع

البند	البيان
المشروع	مجلس 5×4 بواجهة زجاج
العميل	عميل — مجلس
الموقع	—
الاستخدام	مجلس
التاريخ	2026-10-06
نظام البناء	هيكل خشب 5×7 + تليس 2.5 سم من الجهتين
السقف	مائل باتجاه واحد 20° — قرميد معدني

التسعير

البند	القيمة
المساحة المبنية (م2)	20.00
سعر المتر المربع	1,096 ريال
الإجمالي	21,920 ريال

ملاحظات:

- السعر للمساحة المبنية حسب المخطط المعتمد.
- الصبة والتמידات الخارجية على العميل ما لم يُذكر غير ذلك.

لقطات المنظور الخارجي

المنظور الأمامي



منظور أمامي من اليسار



منظور أمامي من اليمين



المنظور الخلفي



منظور خلفي من اليمين



منظر علوي



رقم اللوحة

A-07 (7/9)

التاريخ

2026-10-06

المقياس

—

عنوان اللوحة

لقطات المنظور

المشروع / العميل

مجلس 5x4 بواجهة زجاج
عميل — مجلس

مصنع وتد الأخشاب
Watad Wood Factory



المقطع العلوي بالفرش

مقطع أفقي على ارتفاع 1.90 م — توزيع الفرش ومسار الحركة



رقم اللوحة

A-08 (8/9)

التاريخ

2026-10-06

المقياس

—

عنوان اللوحة

المقطع العلوي بالفرش

المشروع / العميل

مجلس 5x4 بواجهة زجاج
عميل — مجلس


مصنع وتد الأخشاب
Watad Wood Factory



المنظور ثلاثي الأبعاد والمواد

النمط: جوزي غامق + إطارات سوداء — رندر واقعي بخامات حقيقية

جدول المواد والألوان

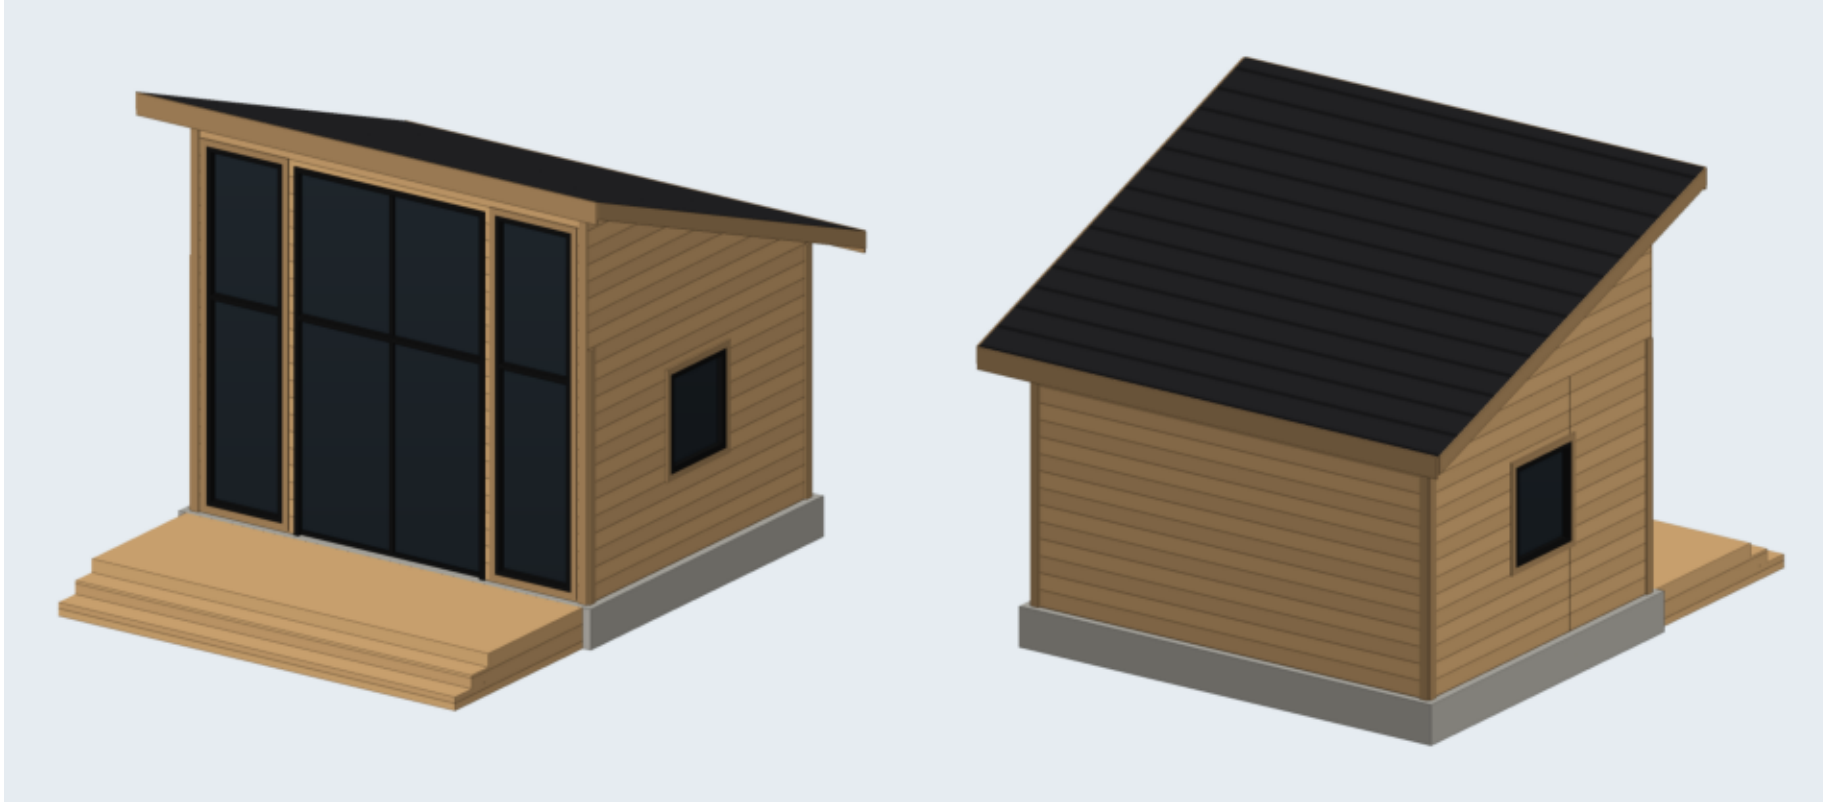

الخشب / الصبغة
خشب طبيعي فاتح (بدون صبغة)



القرميد
قرميد رمادي غامق




الزجاج
زجاج عاكس غامق



إطارات الشبابيك والأبواب
إطار ألومنيوم أسود



الكنار والزوايا
نفس الصبغة أعمق درجة

 

الصبة
خرسانة 45 سم


الدريزين: ألواح أفقية متقاربة (عصري)

تقسيم الشبابيك: بدون | الباب الرئيسي: سحب زجاج


أنواع الدريزين المعتمدة (من مشاريع المصنع)



قوائم رأسية متقاربة (صورة 1)

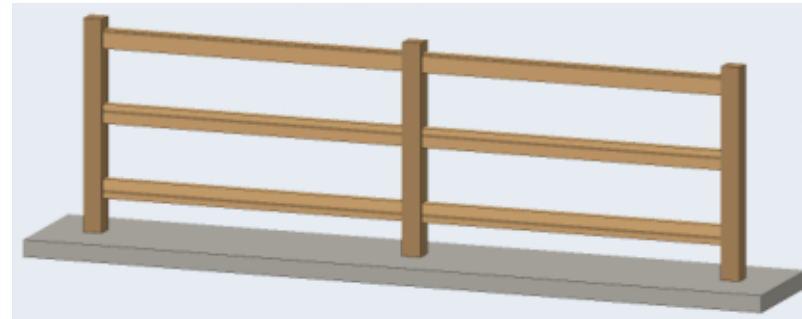

3 مربيع أفقية (صورة 2)

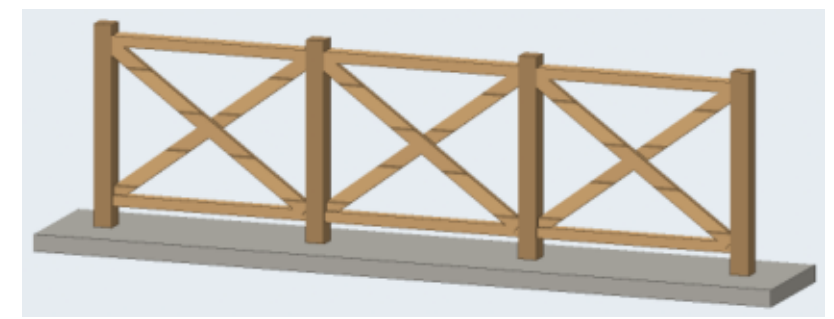

تقاطع X (صورة 5)

رقم اللوحة

A-09 (9/9)

التاريخ

2026-10-06

المقياس

—

عنوان اللوحة

المنظور والمواد

المشروع / العميل

مجلس 5x4 بواجهة زجاج
عميل — مجلس

مصنع وتد الأخشاب
Watad Wood Factory

