
المنظور ثلاثي الأبعاد والمواد

النمط: جوزي غامق + إطارات سوداء — رندر واقعي بخامات حقيقية

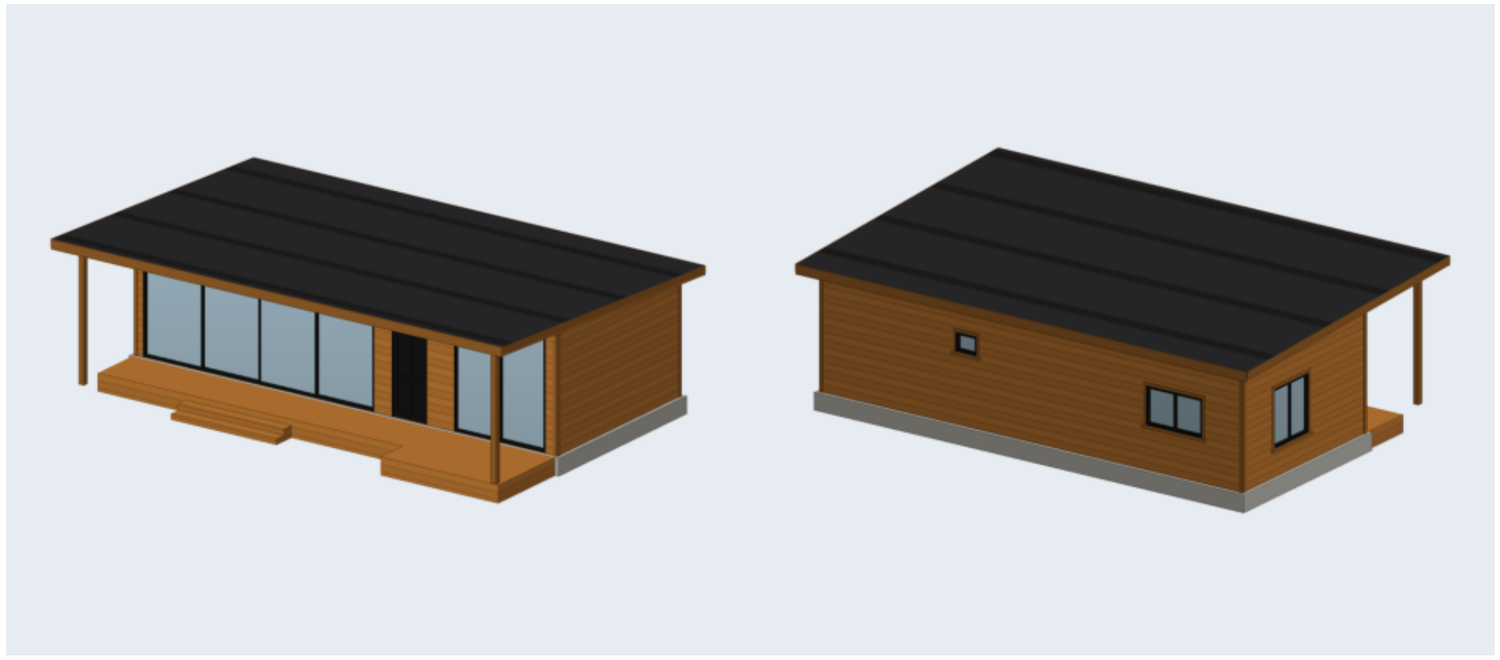

جدول المواد والألوان

الخشب / الصبغة

صبغة عسلي / سيدر

السقف (صاج معدني)

صاج رمادي غامق

الزجاج

زجاج شفاف

إطارات الشبابيك والأبواب

إطار ألمنيوم أسود

الكنار والزوايا

نفس الصبغة أغمق درجة


الصبة

خرسانة 45 سم


الدربزين: ألواح أفقية متقاربة (عصري)

تقسيم الشبابيك: بدون | الباب الرئيسي: سحاب زجاج

أنواع الدربزين المعتمدة (من مشاريع المصنع)

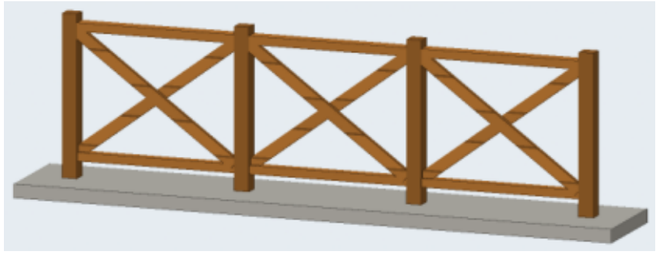

تقاطع X (صورة 5)

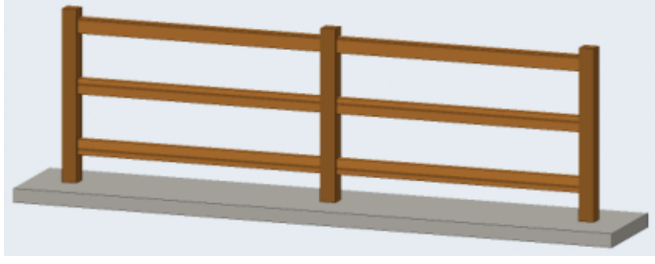

3 مرابيع أفقية (صورة 2)




قوائم رأسية متقاربة (صورة 1)

المشروع / العميل	عنوان اللوحة	المقياس	التاريخ	رقم اللوحة
مصنع وتد الأخشاب Watad Wood Factory — **شاليه 12.00 × 5.00 م — صالة ومطبخ مفتوح + غرفة نوم + حمام — واجهة زجاج وتراس** **عميل — شاليه 12 × 5**	**المنظور والمواد**	**1:50**	**2026-11-10**	**W-01 (1/13)**


المسقط الأفقي مع الفرش

الأبعاد بالسنتيمتر - الجدران: قوائم 7×5 + تلبيس 2.5 من الجهتين (12 سم)

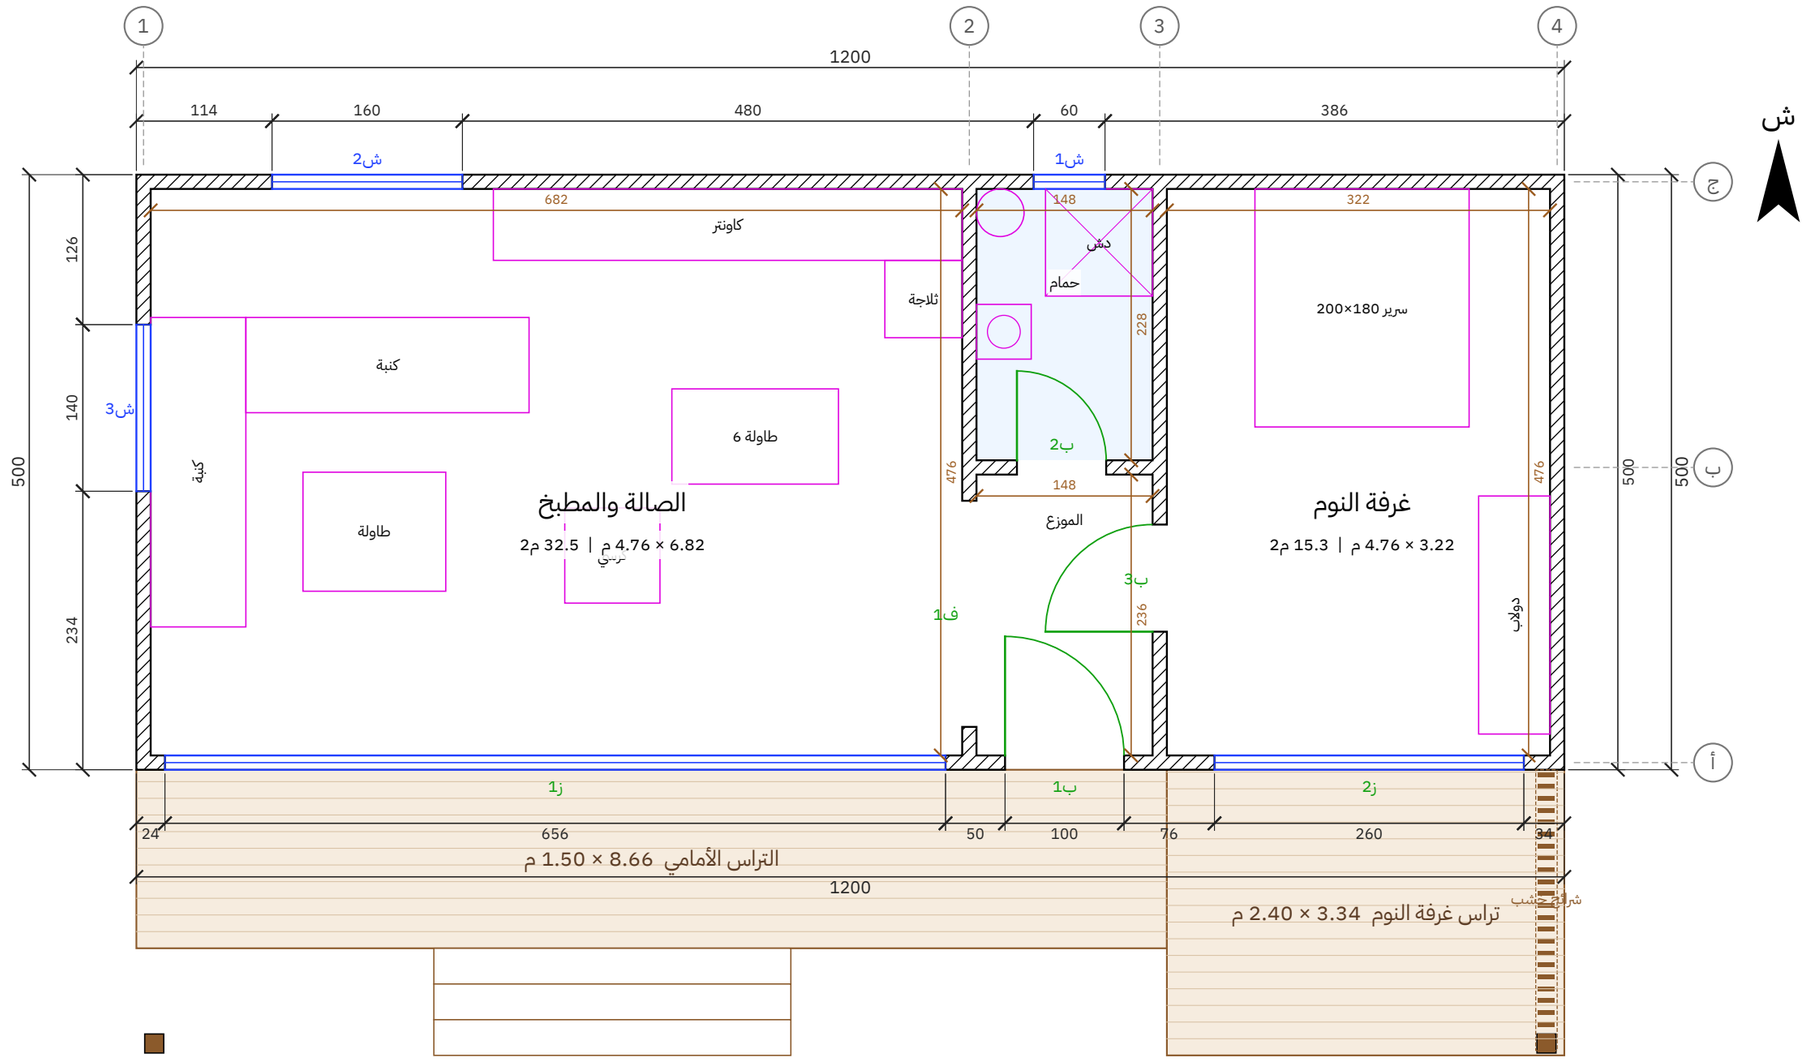


المشروع / العميل	عنوان اللوحة	المقياس	التاريخ	رقم اللوحة
شاليه 12.00 × 5.00 م – صالة ومطبخ مفتوح + غرفة نوم + حمام – واجهة زجاج وتراس **عميل – شاليه 12 × 5**	**المسقط الأفقي**	**1:50**	**2026-11-10**	**W-02 (2/13)**

مصنع وتد الأخشاب
Watad Wood Factory

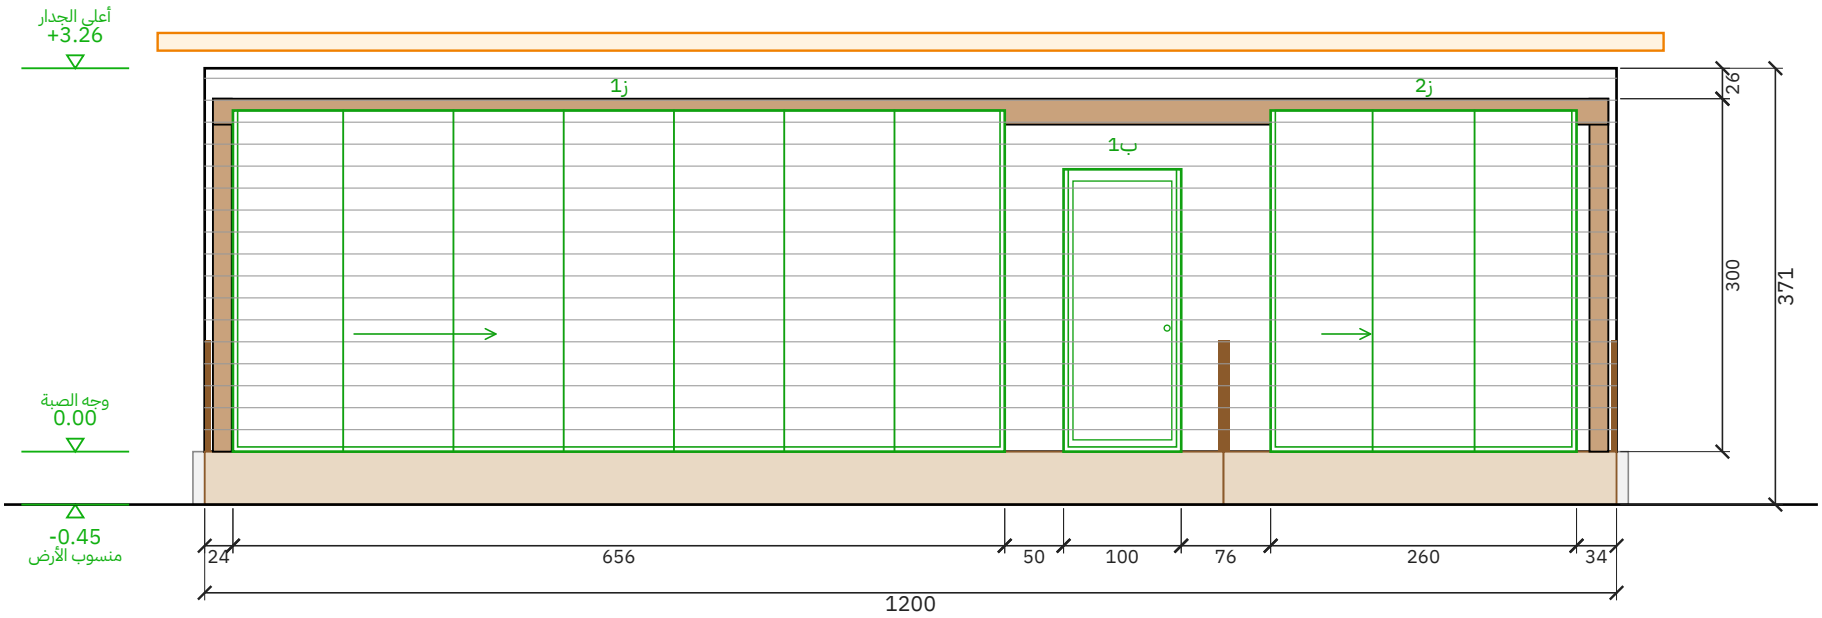

الواجهة الأمامية (زجاج على التراس)

مقياس 1:50 | الوحدة: سم

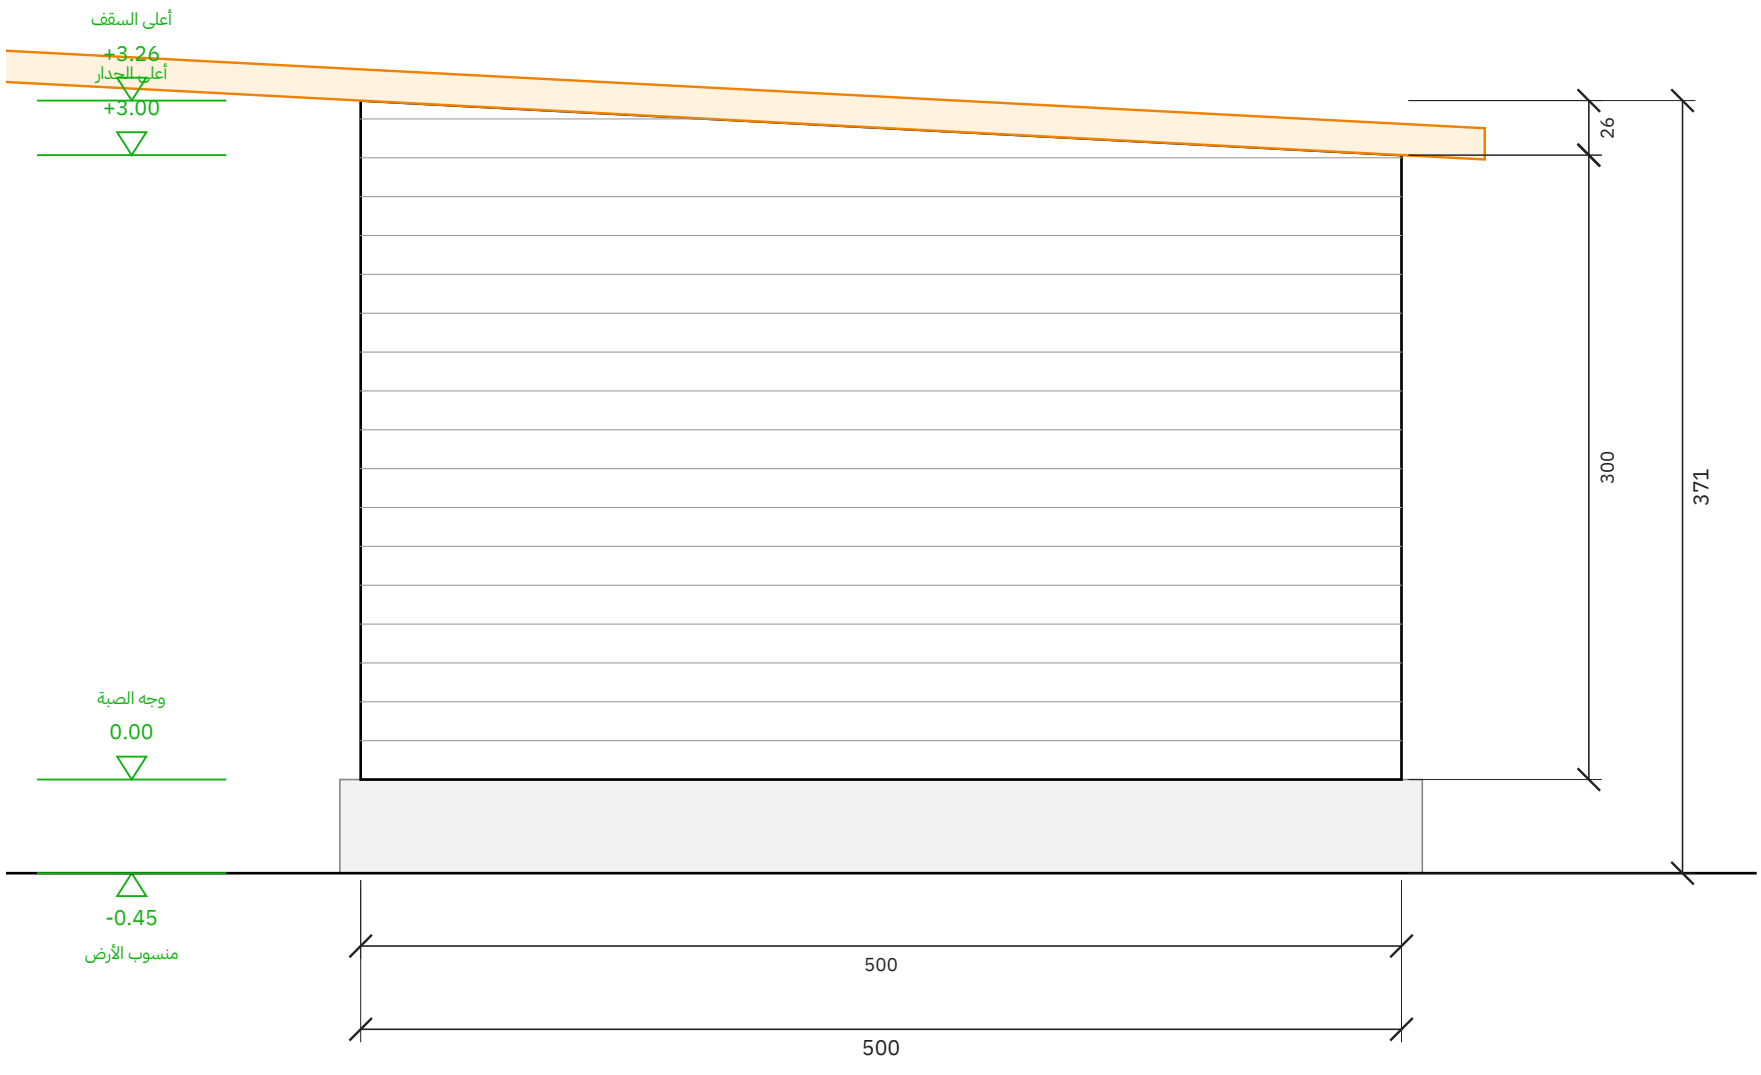


الواجهة الشرقية

مقياس 1:50 | الوحدة: سم


المشروع / العميل	عنوان اللوحة	المقياس	التاريخ	رقم اللوحة
شاليه 12.00 × 5.00 م — صالة ومطبخ مفتوح + غرفة نوم + حمام — واجهة زجاج وتراس عميل — شاليه 12 × 5	الواجهة الأمامية (زجاج على التراس) والواجهة الشرقية	1:50	2026-11-10	W-03 (3/13)

مصنع وتد الأخشاب
Watad Wood Factory

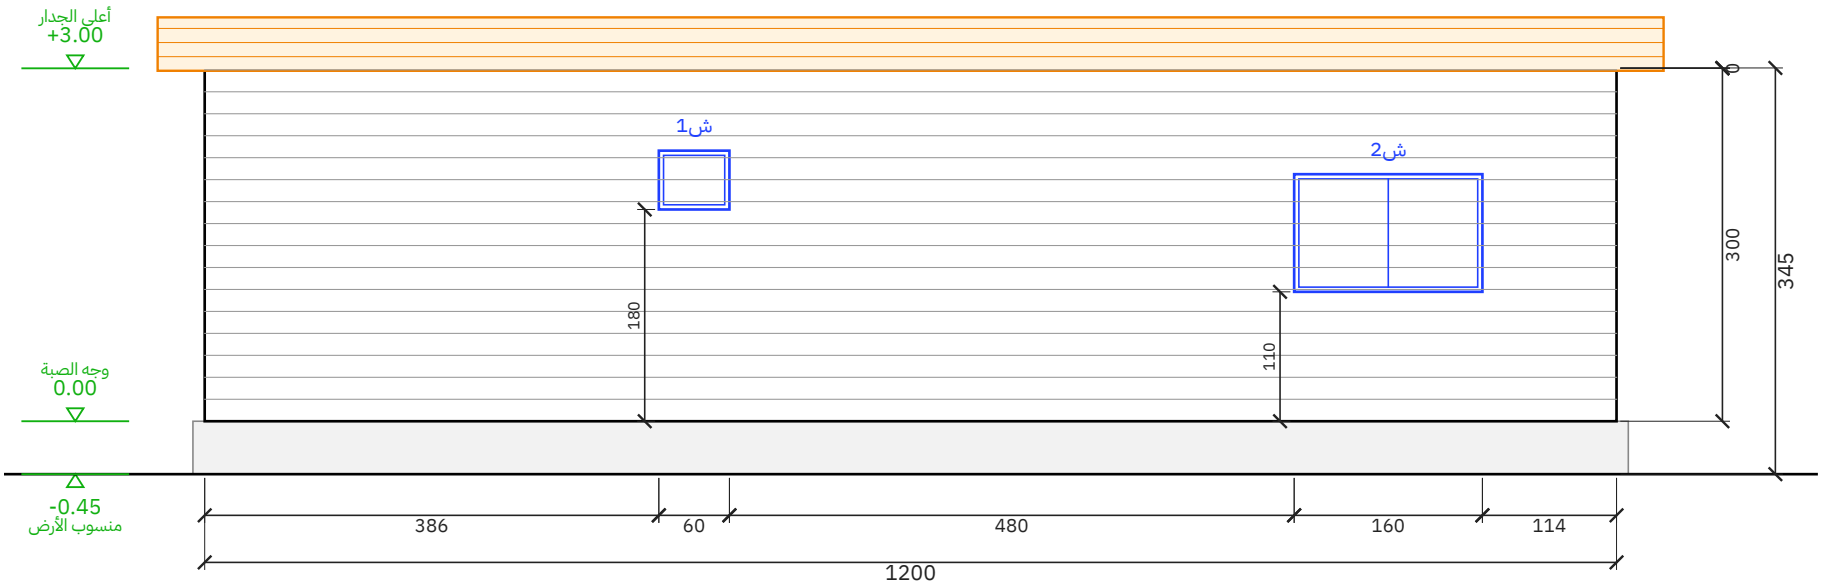

الواجهة الخلفية

مقياس 1:50 | الوحدة: سم

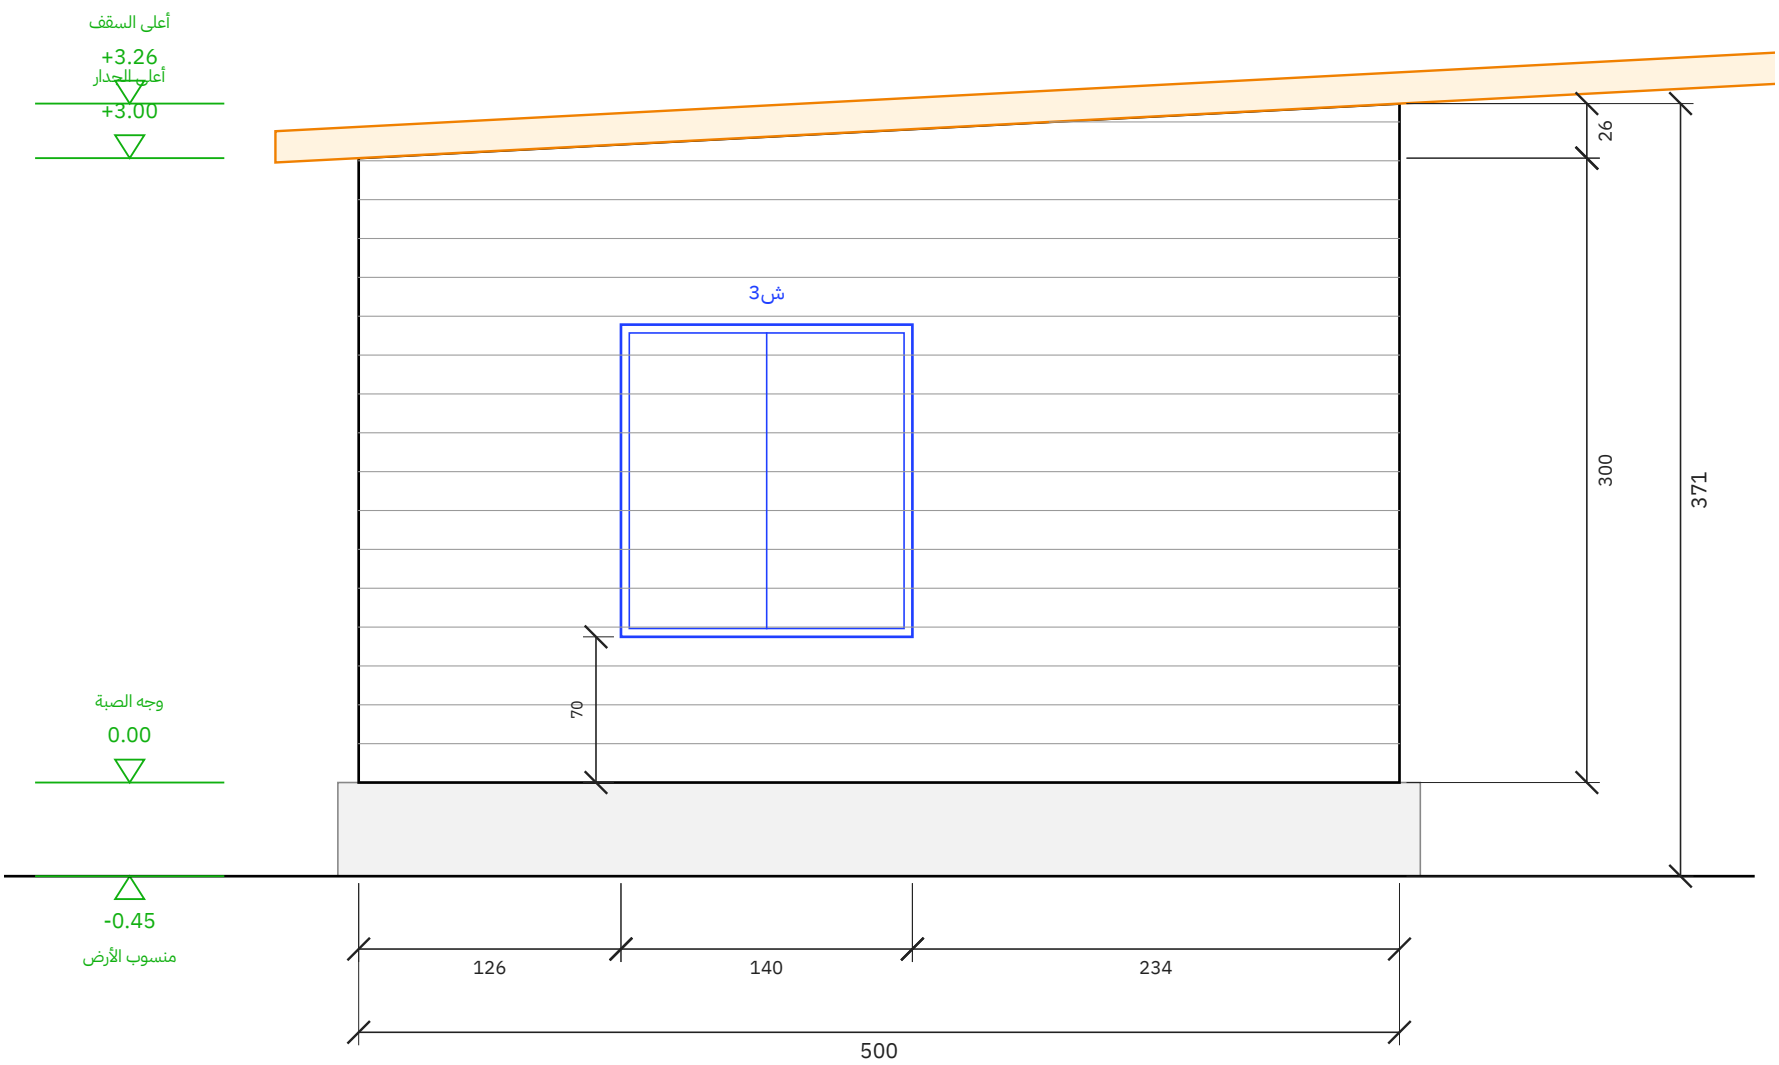

الواجهة الغربية


مقياس 1:50 | الوحدة: سم

المشروع / العميل	عنوان اللوحة	المقياس	التاريخ	رقم اللوحة
شاليه 12.00 × 5.00 م — صالة ومطبخ مفتوح + غرفة نوم + حمام — واجهة زجاج وتراس عميل — شاليه 12 × 5	الواجهة الخلفية والواجهة الغربية	1:50	2026-11-10	W-04 (4/13)

مصنع وتد الأخشاب
Watad Wood Factory


مسقط السقف (مائل باتجاه واحد)

رفرف 40 سم من كل جهة | مقياس 1:50

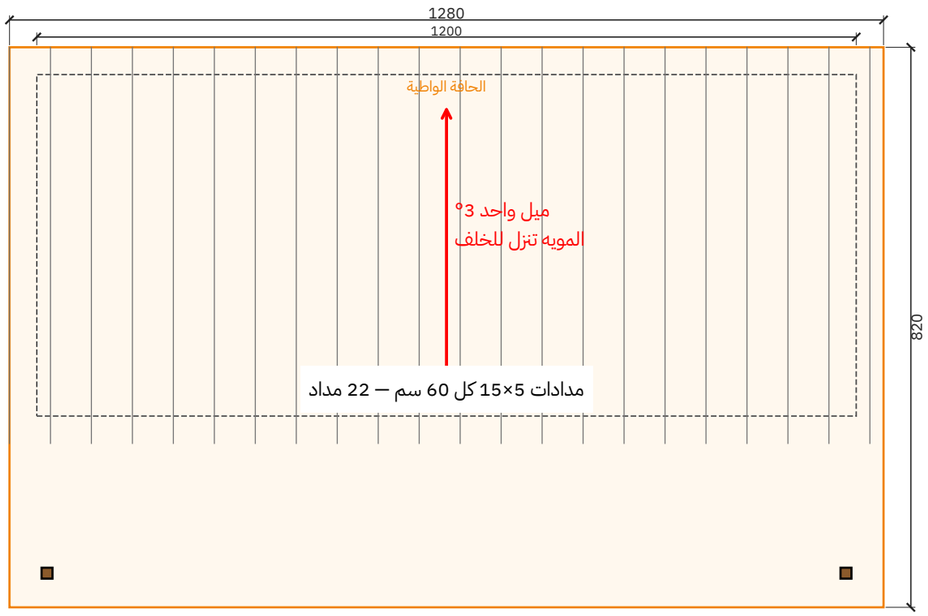


قطاع عرضي أ-أ

مقياس 1:50 | الوحدة: سم

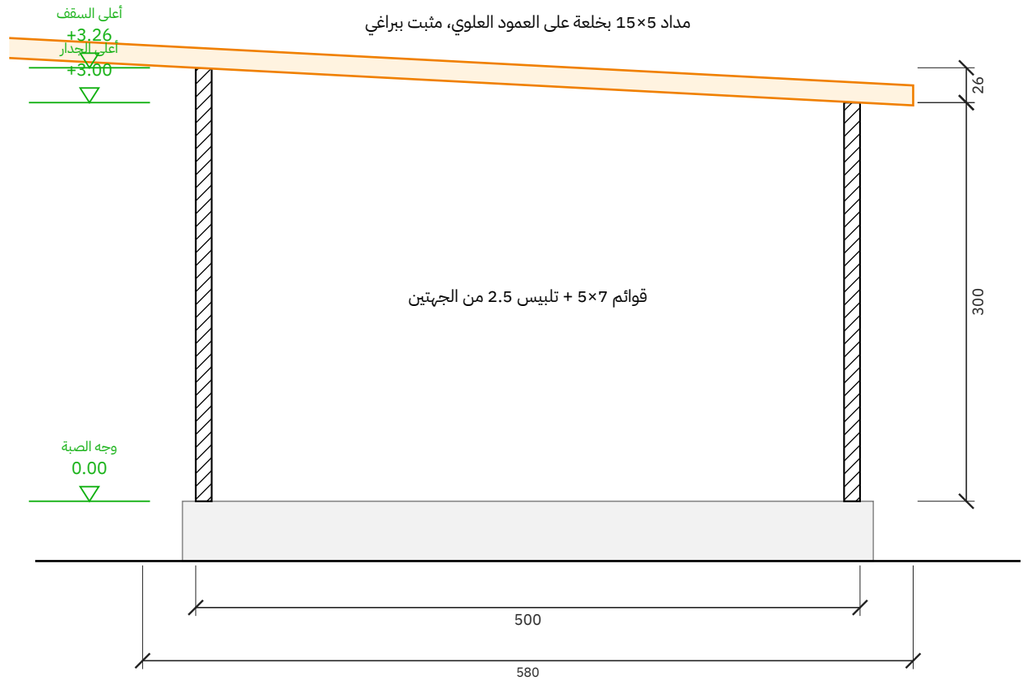

تفصيلة جلوس المداد على العلوي (1:5)

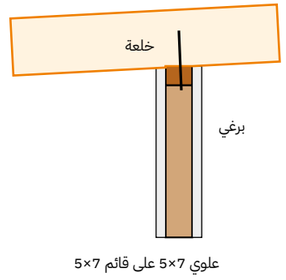

المشروع / العميل **شاليه 12.00 × 5.00 م — صالة ومطبخ مفتوح + غرفة نوم + حمام — واجهة زجاج وتراس** **عميل — شاليه 12 × 5**	عنوان اللوحة **مسقط السقف والقطاع**	المقياس **1:50**	التاريخ **2026-11-10**	رقم اللوحة **W-05 (5/13)**

مصنع وتد الأخشاب
Watad Wood Factory

جدول مقاسات الأبواب والشبابيك

مقاس الفتحة الصافي في الجدار - الوحدة: سم

الرمز	النوع	العرض (سم)	الارتفاع (سم)	ارتفاع الجلسة (سم)	العدد	الموقع
ب1	باب	100	240	-	1	الأمامية (زجاج على التراس)
ب2	باب	75	210	-	1	الحمام
ب3	باب	90	220	-	1	غرفة النوم
ز1	باب	656	290	-	1	الأمامية (زجاج على التراس)
ز2	باب مزدوج	260	290	-	1	الأمامية (زجاج على التراس)
ف1	باب	190	240	-	1	فتحة الموزع على الصالة
ش1	شباك	60	50	180	1	الخلفية
ش2	شباك	160	100	110	1	الخلفية
ش3	شباك	140	150	70	1	الغربية

الإجمالي: أبواب 6 - شبابيك 3

جدول المساحات وبيانات المشروع


بيانات المشروع

البند	البيان
المشروع	شاليه 12.00 × 5.00 م — صالة ومطبخ مفتوح + غرفة نوم + حمام — واجهة زجاج وتراس
العميل	عميل — شاليه 12 × 5
الموقع	—
الاستخدام	شاليه
التاريخ	2026-11-10
نظام البناء	هيكل خشب 5×7 + تلبيس 2.5 سم من الجهتين
السقف	مائل باتجاه واحد 3° — صاج معدني + عزل مائي


جدول المساحات

م	الفراغ	الأبعاد (م)	المساحة (م2)
1	الصالة والمطبخ	6.82 × 4.76	32.46
2	الموزع	1.48 × 2.36	3.49
3	حمام	1.48 × 2.28	3.37
4	غرفة النوم	3.22 × 4.76	15.33
	المساحة الصافية الداخلية		54.66
	التراس الأمامي	**8.66 × 1.50**	**12.99**
	تراس غرفة النوم	**3.34 × 2.40**	**8.02**
	المساحة الإجمالية المبنية	**12.00 × 5.00**	**60.00**
	المساحة الكلية (المبنية + التراسات)		**81.01**

تأطير جدار جنوب — الطول 1188 سم، الارتفاع 326 سم

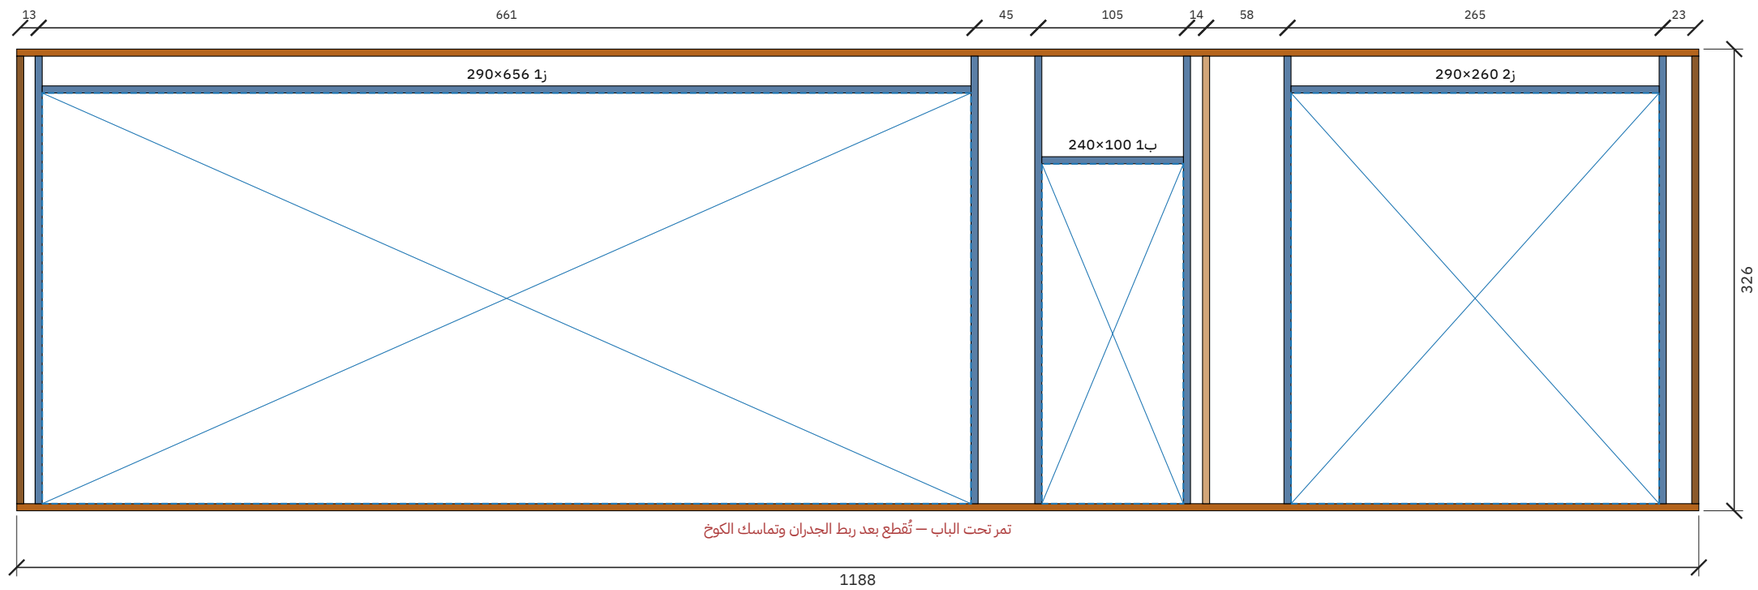

تأطير جدار شرق — الطول 488 سم، الارتفاع 300 سم

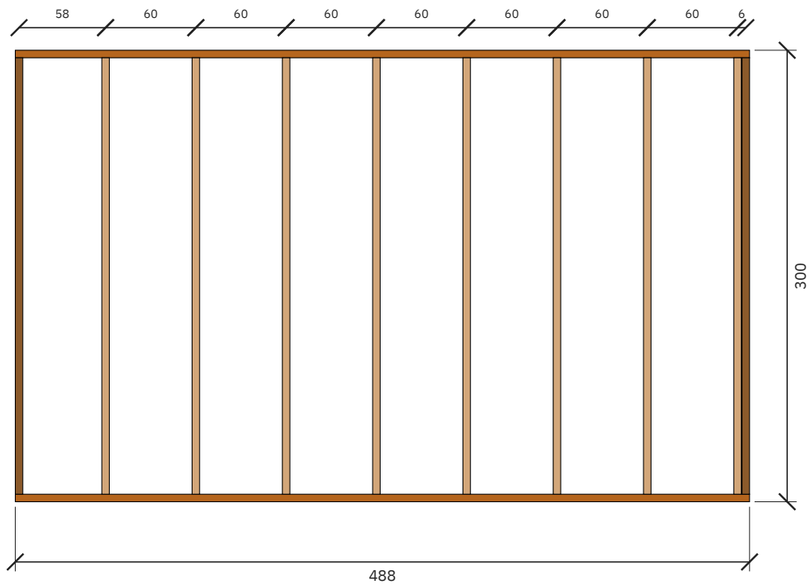


عمود قصير | جلسة شباك | رأس فتحة | جنب فتحة | عمود زاوية | عمود | علوي | قاعدة سفلية


المشروع / العميل	عنوان اللوحة	المقياس	التاريخ	رقم اللوحة
شاليه 12.00 × 5.00 م — صالة ومطبخ مفتوح + غرفة نوم + حمام — واجهة زجاج وتراس **عميل — شاليه 12 × 5**	**لوحات التأطير (للورشة)**	**—**	**2026-11-10**	**W-08 (8/13)**

مصنع وتد الأخشاب
Watad Wood Factory

تأطير جدار شمال — الطول 1188 سم، الارتفاع 300 سم

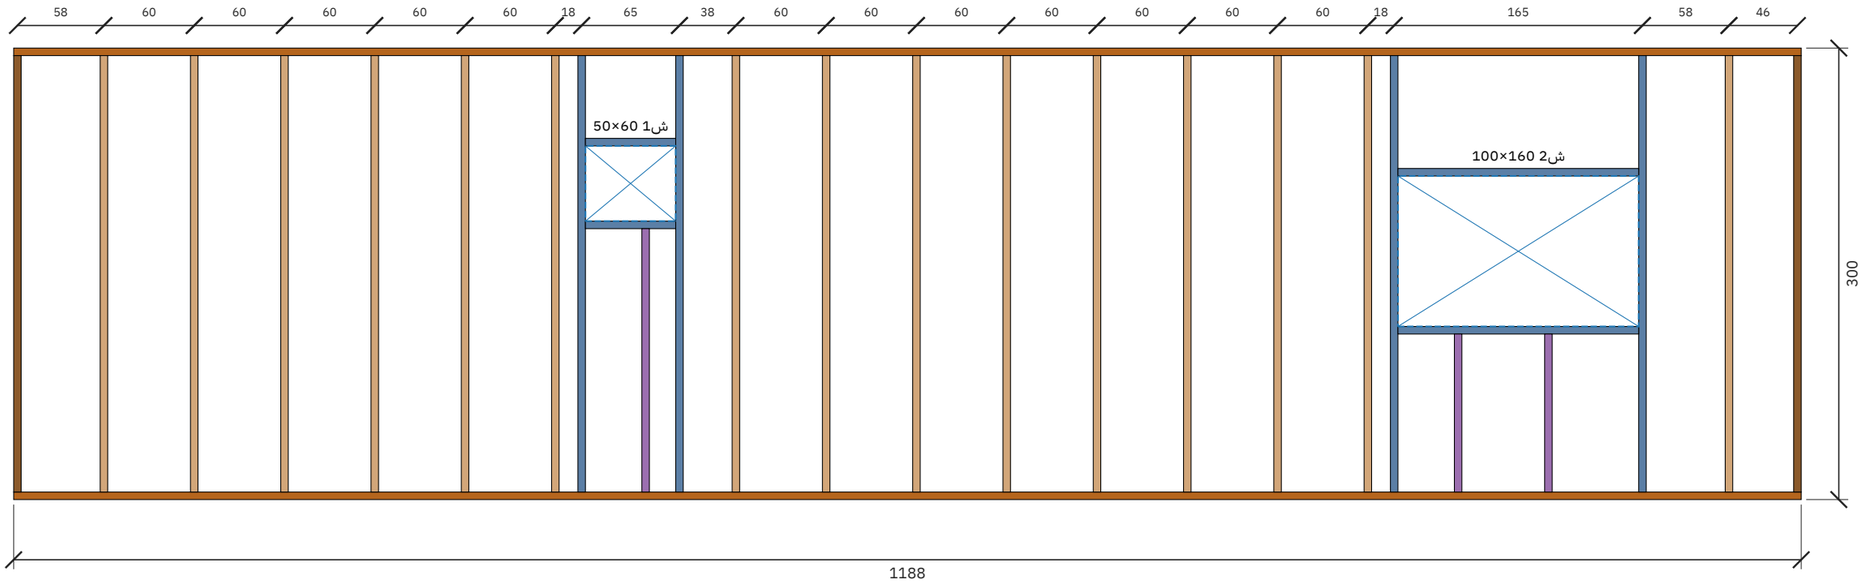


تأطير جدار غرب — الطول 488 سم، الارتفاع 300 سم

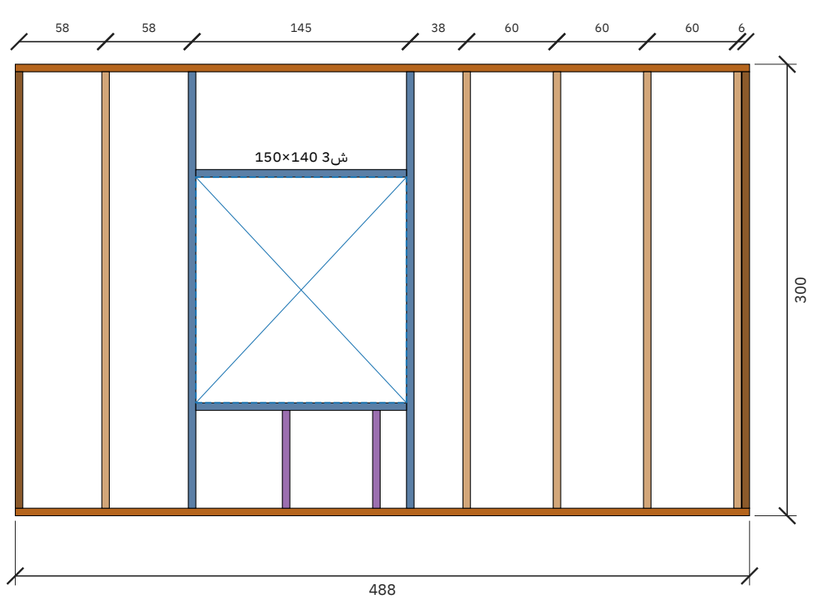


قاعدة سفلية | علوي | عمود | عمود زاوية | جنب فتحة | رأس فتحة | جلسة شباك | عمود قصير

مصنع وتد الأخشاب Watad Wood Factory	المشروع / العميل **شاليه 12.00 × 5.00 م — صالة ومطبخ مفتوح + غرفة نوم + حمام — واجهة زجاج وتراس** **عميل — شاليه 12 × 5**	عنوان اللوحة **لوحات التأطير (للورشة)**	المقياس **—**	التاريخ **2026-11-10**	رقم اللوحة **W-09 (9/13)**

تأطير جدار جدار الصالة – الموزع والحمام – الطول 488 سم، الارتفاع 300 سم (داخلي)

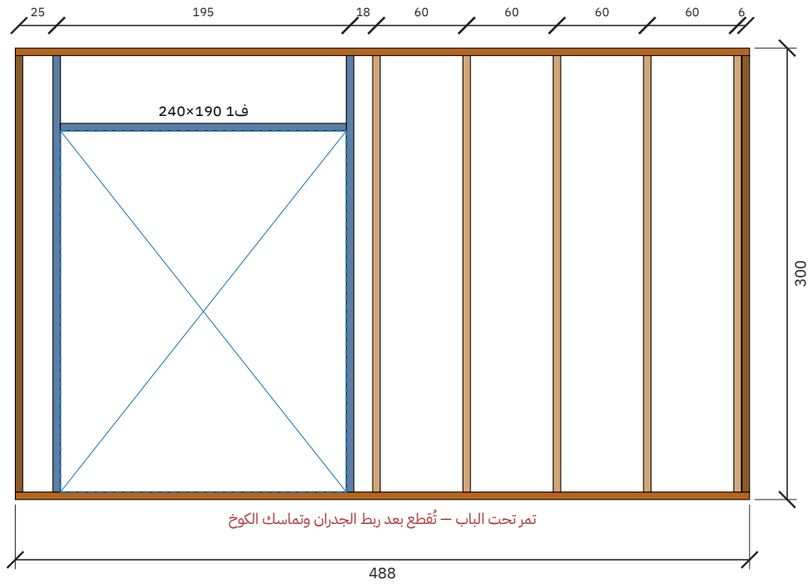


تأطير جدار جدار الموزع – الحمام – الطول 160 سم، الارتفاع 300 سم (داخلي)

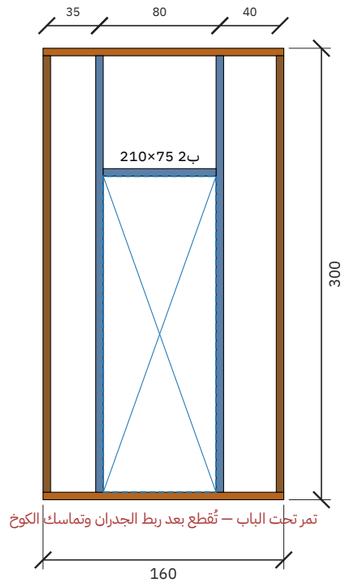

عمود قصير | جلسة شباك | رأس فتحة | جنب فتحة | عمود زاوية | عمود | علوي | قاعدة سفلية

مصنع وتد الأخشاب Watad Wood Factory	المشروع / العميل **شاليه 12.00 × 5.00 م – صالة ومطبخ مفتوح + غرفة نوم + حمام – واجهة زجاج وتراس** **عميل – شاليه 12 × 5**	عنوان اللوحة **لوحات التأطير (للورشة)**	المقياس **–**	التاريخ **2026-11-10**	رقم اللوحة **W-10 (10/13)**

تأطير جدار جدار غرفة النوم — الطول 488 سم، الارتفاع 300 سم (داخلي)

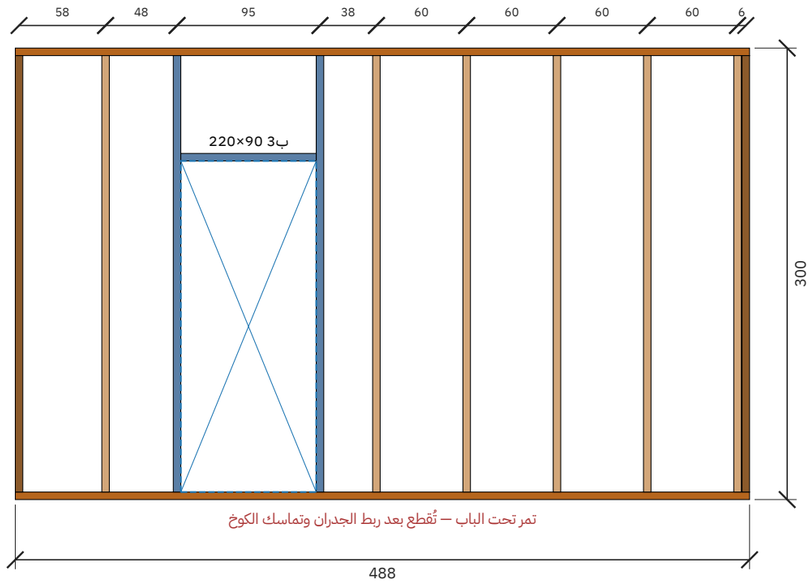

عمود قصير
جلسة شباك
رأس فتحة
جنب فتحة
عمود زاوية
عمود
علوي
قاعدة سفلية

مصنع وتد الأخشاب Watad Wood Factory	المشروع / العميل **شاليه 12.00 × 5.00 م — صالة ومطبخ مفتوح + غرفة نوم + حمام — واجهة زجاج وتراس** **عميل — شاليه 12 × 5**	عنوان اللوحة **لوحات التأطير (للورشة)**	المقياس **—**	التاريخ **2026-11-10**	رقم اللوحة **W-11 (11/13)**

جدول الكميات وخطة تقطيع الطبليات

البند	القيمة
الارتفاع المطلوب / المعتمد	300 / 300 سم
السقف	مائل باتجاه واحد 3° — أعلى نقطة 326 سم من وجه الصبة
المدادات 5×15	22 مداد (22 لكل جهة) × حتى 821 سم — من طبلية None
طبليات الطريقة الأولى (مداد + عمود)	22 طبلية × 520 سم
طبليات الطريقة الثانية (3 أعمدة)	26 طبلية × 320 سم
إجمالي الطبليات 5×22.5	48
إجمالي قطع 5×7	103
قائمة تقطيع 5×7	1188سم×4 | 656سم×1 | 488سم×8 | 316سم×9 | 290سم×63 | 260سم×1 | 190سم×1 | 175سم×1 | 160سم×4
	140سم×2 | 105سم×2 | 100سم×1 | 90سم×1 | 75سم×1 | 65سم×2 | 60سم×2
ألواح تلبيس 2.5 سم	284 لوح × 400 سم (مجموع الصفوف 968.3 م، 14 وجه)
أسمنت بورد 12 مم (122×244)	16 لوح (داخل دورات المياه)
العزل	135 لوح فوم صخري 80
الصبة	يجهزها العميل — 20 سم، مفرغة تحت دورات المياه

مراجعة التصميم مقابل قواعد المصنع

النوع	البند	التفاصيل	المقترح
ملاحظة	بحر المدادات	أطول بحر بدون جدار داخلي يحمل المداد: جهة أ: 500 سم. يحتاج رقم المصنع لأقصى بحر مسموح لتحديد المدادات اللي تُقوّى 20×5.	
ملاحظة	الصبة والدرج	ارتفاع الصبة 45 سم ← 3 درجة بقائمة 15.0 سم.	
ملاحظة	مناسيب رؤوس الفتحات	رؤوس الأبواب والشبابيك على مناسيب مختلفة: 210، 220، 230، 240، 290 سم.	
خطأ	طول المداد	طول المداد 821 سم أطول من كل الأطوال المتوفرة — يحتاج قرار (للمائل: roof.splice على جدار داخلي حامل)	
تنبيه	ميل سقف خفيف (بموافقة المصنع)	ميل 3° أقل من 20° — يصرّف باتجاه واحد بس يحتاج تغطية صاج معدني (مو قرميد) وعزل مائي تحت الصاج ووصلات مختومة.	صاج معدني بطول واحد من الحافة العالية للواطية بدون وصلات عرضية.
سؤال	يحتاج تأكيد	أقصى بحر للمداد بدون جدار داخلي قبل إضافة تقوية 5×7 (مداد 20×5)؟	
سؤال	يحتاج تأكيد	التغطية الصافية للوح التلبيس بعد التعشيق (مستنتجة مؤقتاً 18.67 سم من 280/15)؟	
سؤال	يحتاج تأكيد	هل يوضع أعمدة قصيرة فوق رأس الشباك/الباب إلى العلوي؟	
سؤال	يحتاج تأكيد	مكان الوصلة في القاعدة والعلوي إذا الجدار أطول من الطبلية؟	