

# المسقط الأفقي مع الفرش

الأبعاد بالسنتيمتر - الجدران: قوائم 5×7 + تلبيس 2.5 من الجهتين (12 سم)

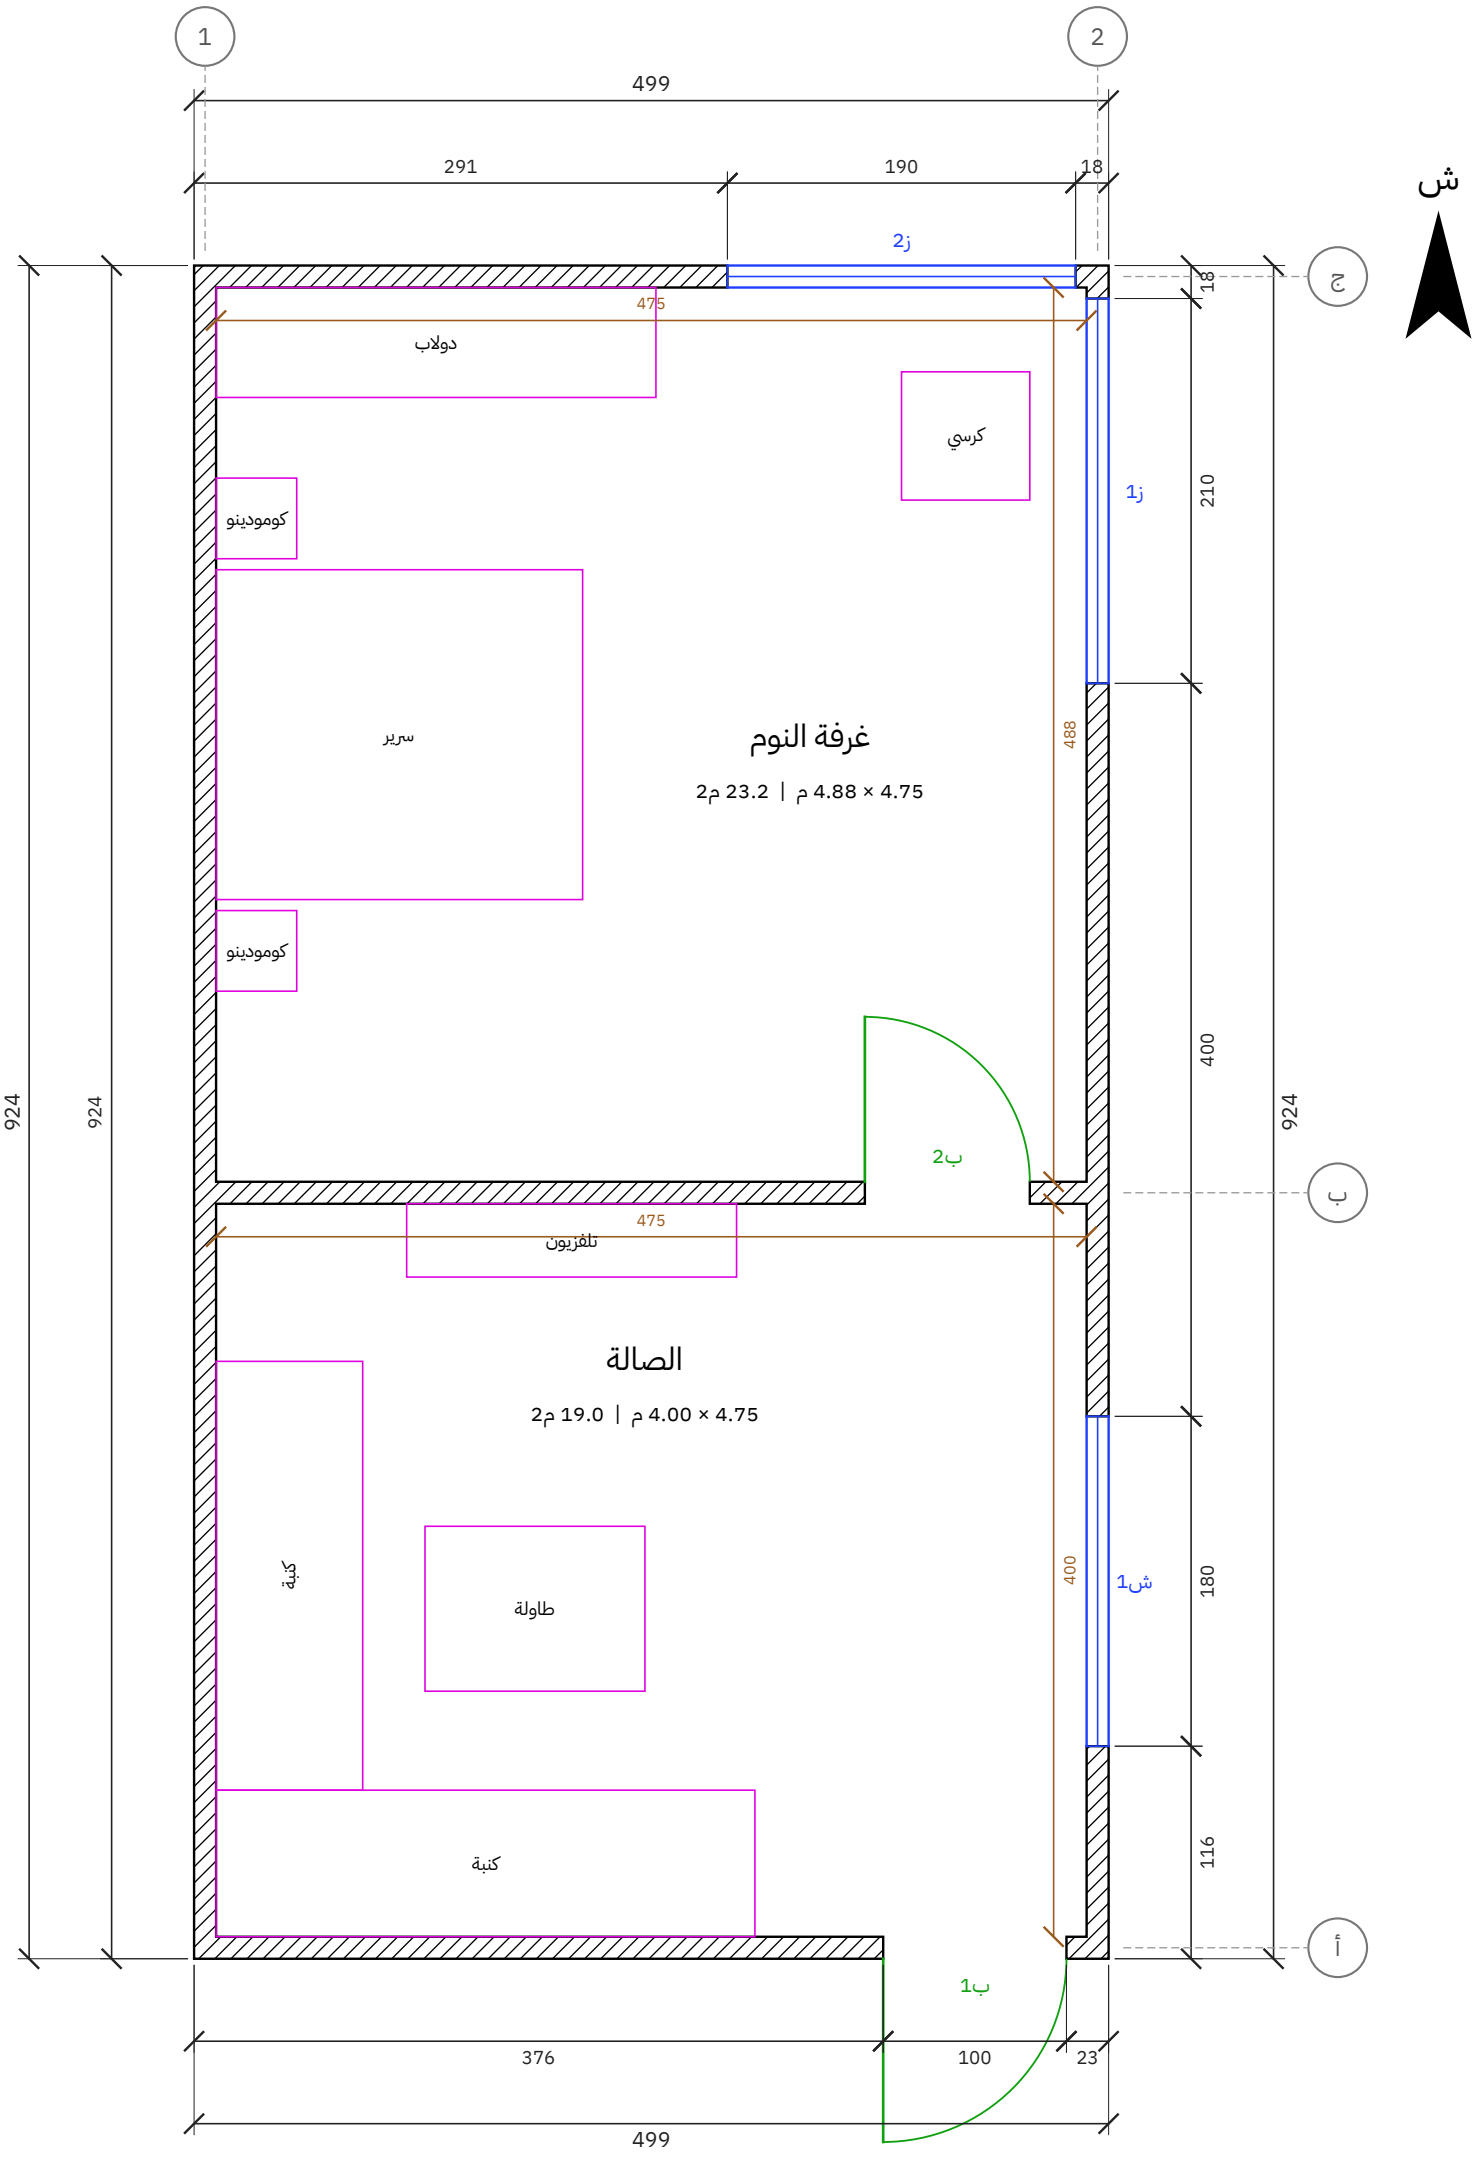



| المشروع / العميل | عنوان اللوحة | المقياس | التاريخ | رقم اللوحة |
|---|---|---|---|---|
| ملحق سطح – غرفة نوم + صالة – 4.75 × 9.00 م<br>عميل – ملحق سطح | المسقط الأفقي | 1:50 | 2026-10-30 | A-01 (1/9) |

مصنع وتد الأخشاب
Watad Wood Factory

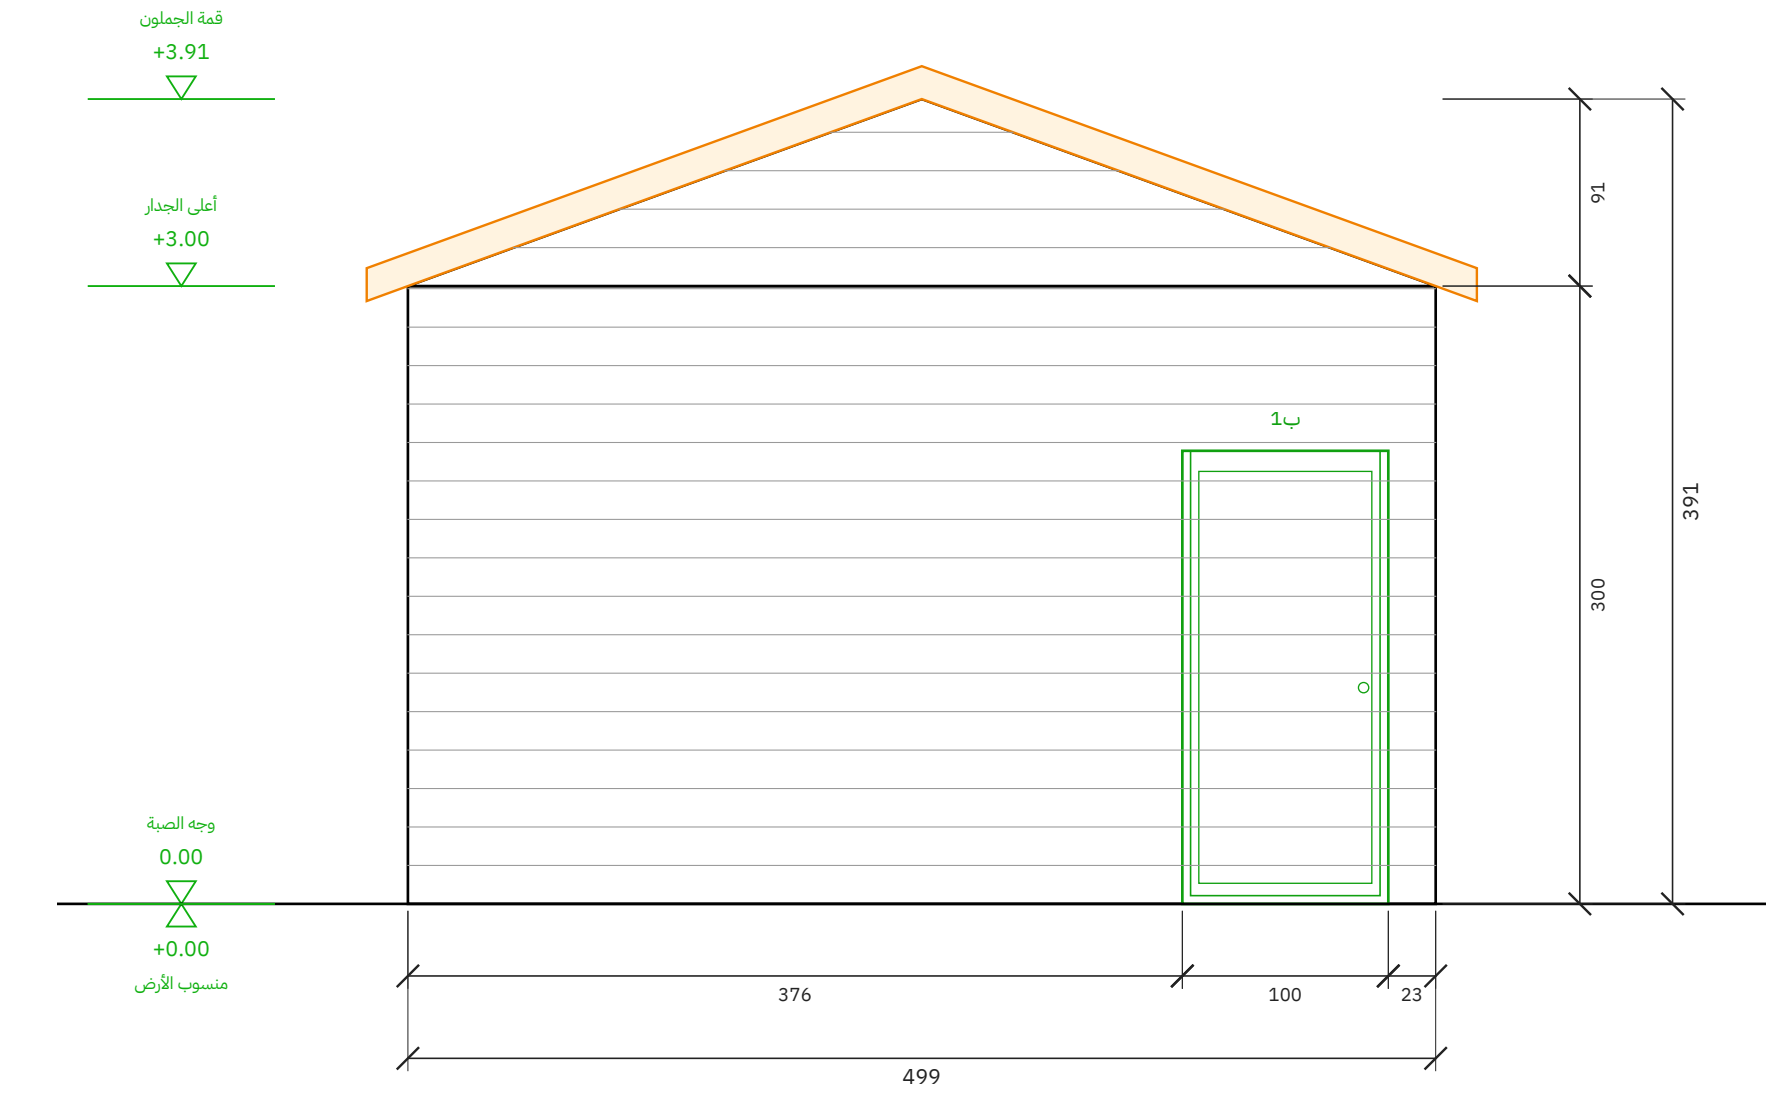


## جدار المدخل (جهة السطح)

مقياس 1:50 | الوحدة: سم

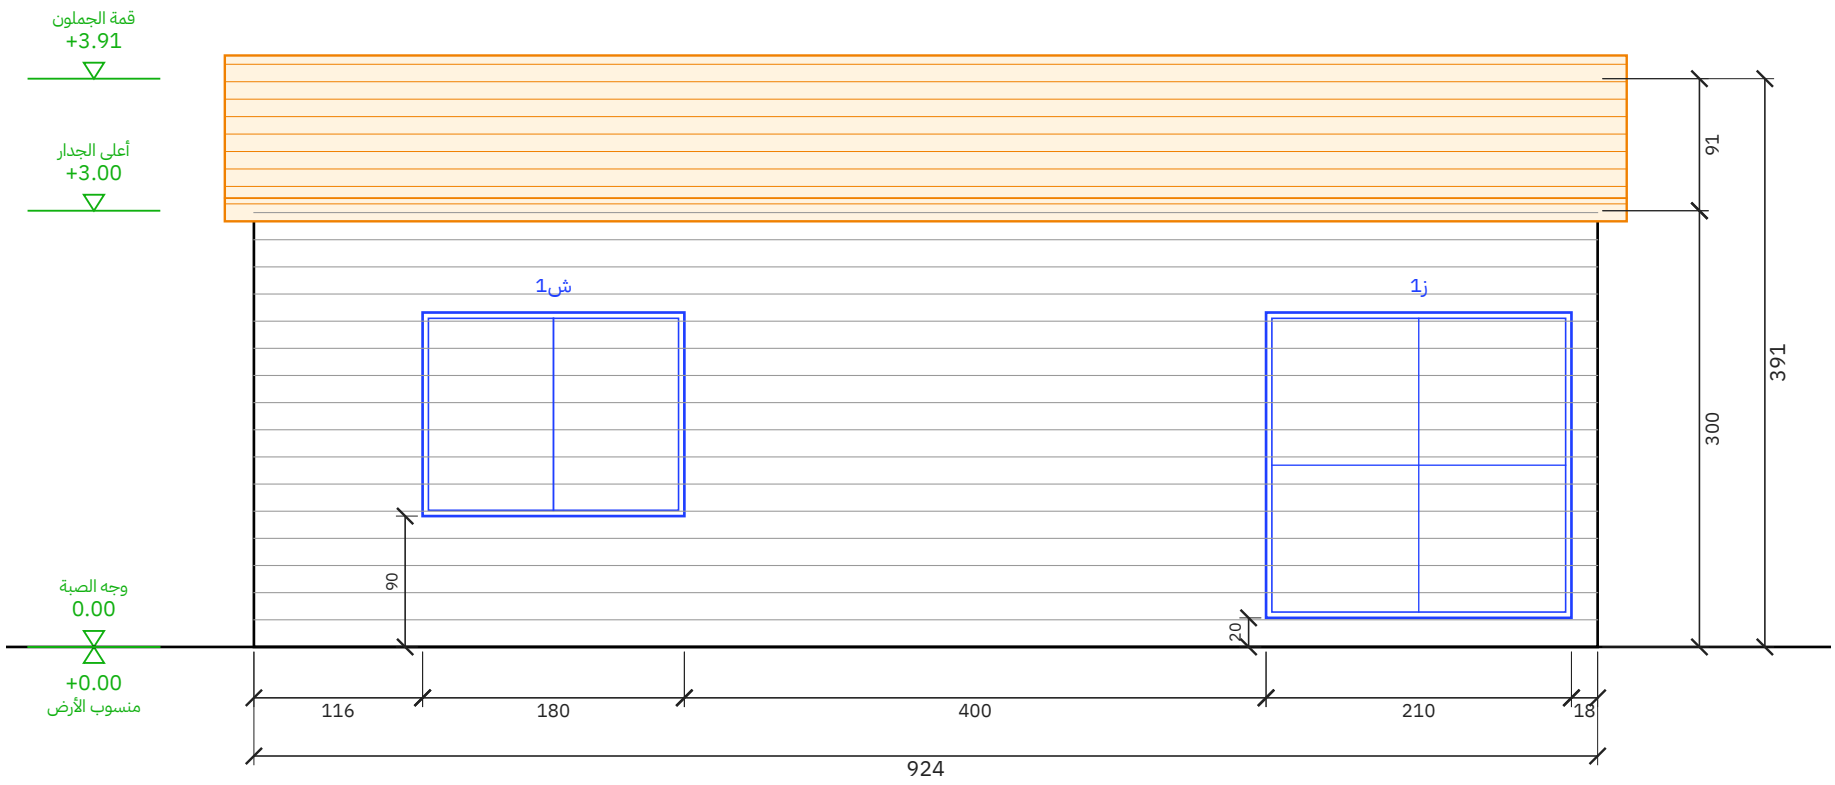



## الجدار الأيمن (القائم + الرفع)

مقياس 1:50 | الوحدة: سم


| المشروع / العميل | عنوان اللوحة | المقياس | التاريخ | رقم اللوحة |
|---|---|---|---|---|
| ملحق سطح – غرفة نوم + صالة – 4.75 × 9.00 م<br>عميل – ملحق سطح | جدار المدخل (جهة السطح) والجدار الأيمن (القائم + الرفع) | 1:50 | 2026-10-30 | A-02 (2/9) |

مصنع وتد الأخشاب
Watad Wood Factory

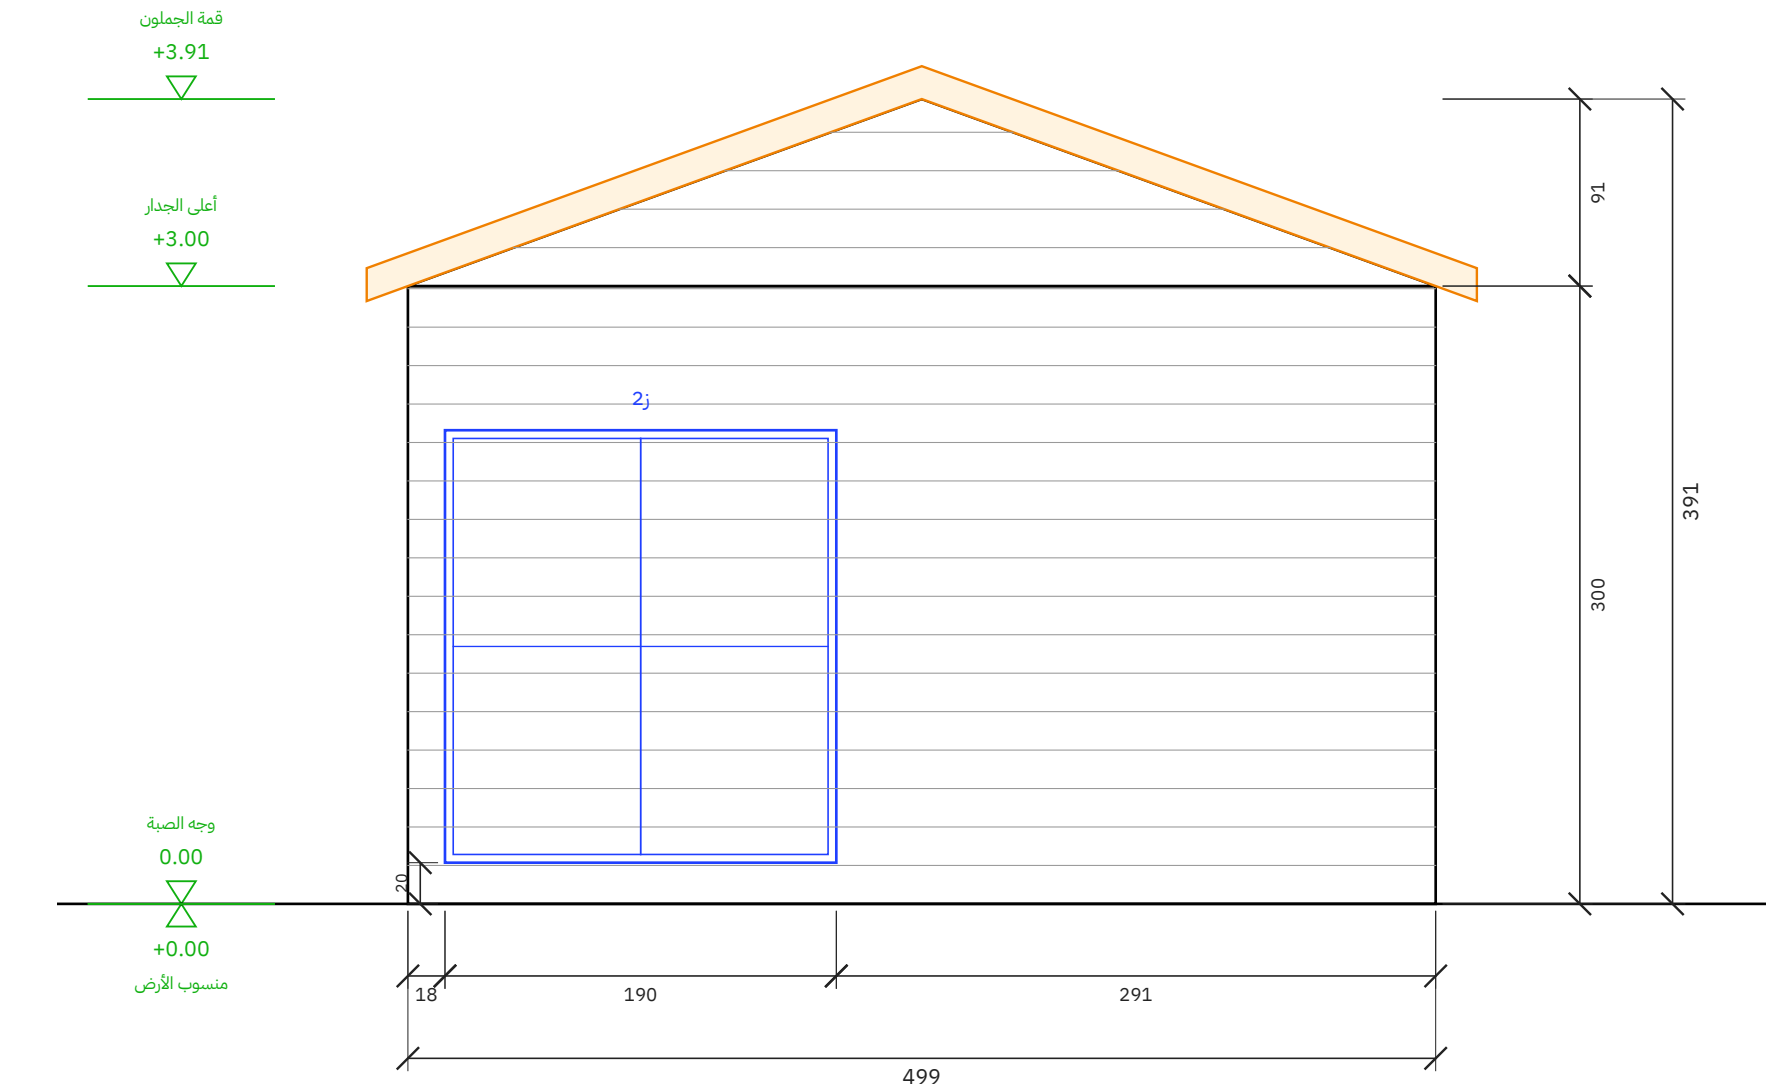


## الجدار الخلفي (غرفة النوم)

مقياس 1:50 | الوحدة: سم

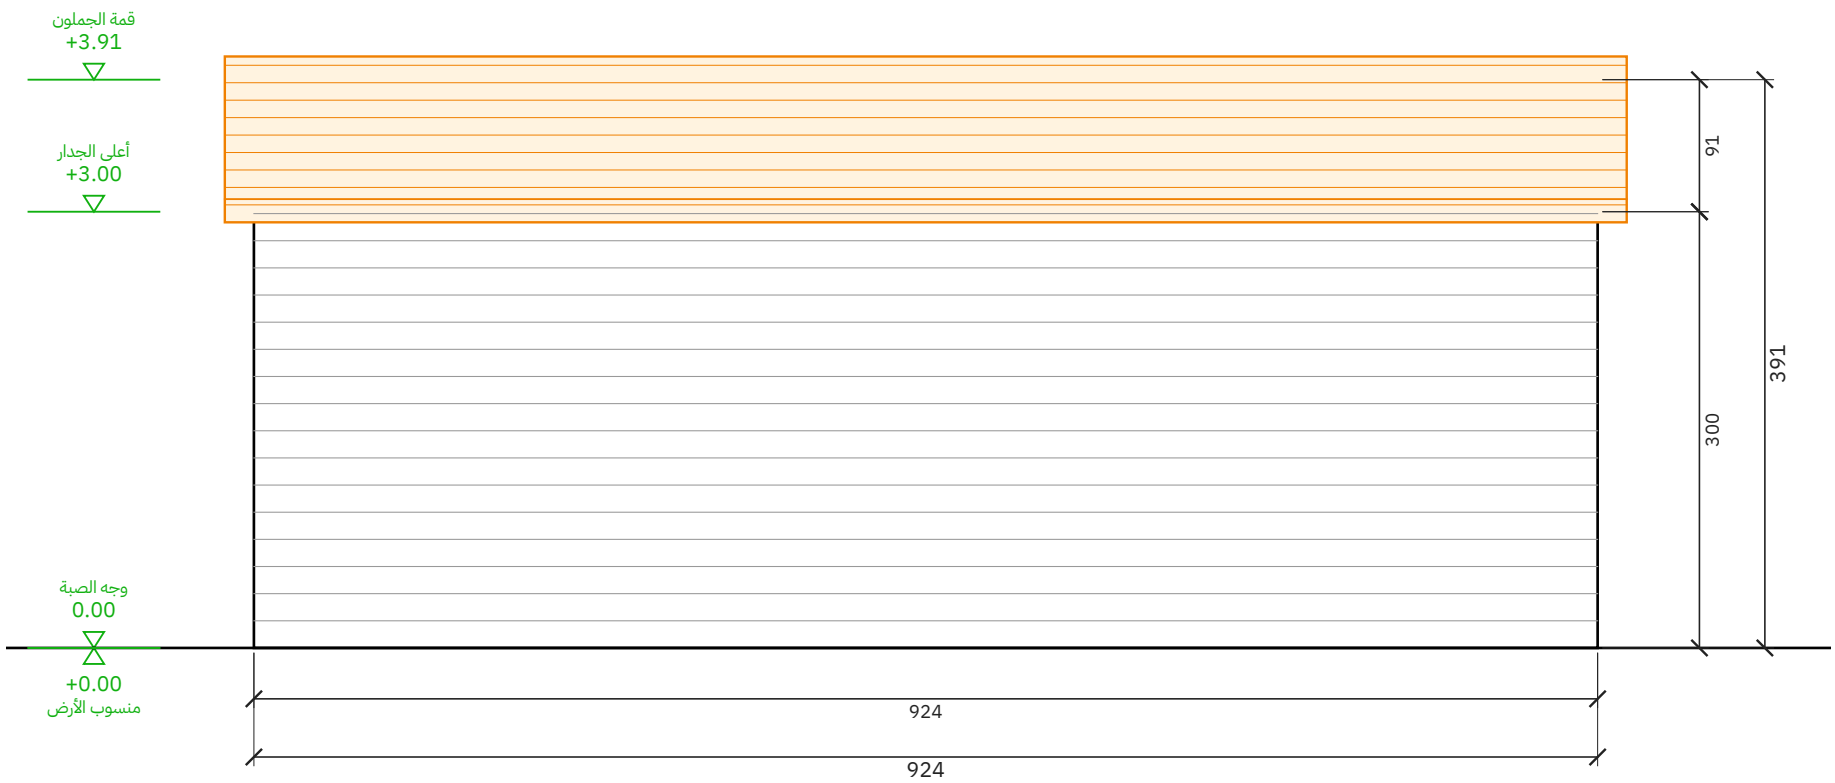


## الجدار الأيسر (القائم + الرفع)


مقياس 1:50 | الوحدة: سم

| المشروع / العميل | عنوان اللوحة | المقياس | التاريخ | رقم اللوحة |
|---|---|---|---|---|
| ملحق سطح – غرفة نوم + صالة – 4.75 × 9.00 م<br>عميل – ملحق سطح | الجدار الخلفي (غرفة النوم) والجدار الأيسر (القائم + الرفع) | 1:50 | 2026-10-30 | A-03 (3/9) |

مصنع وتد الأخشاب
Watad Wood Factory


## مسقط السقف (جملون)

رفرف 20 سم من كل جهة | مقياس 1:50

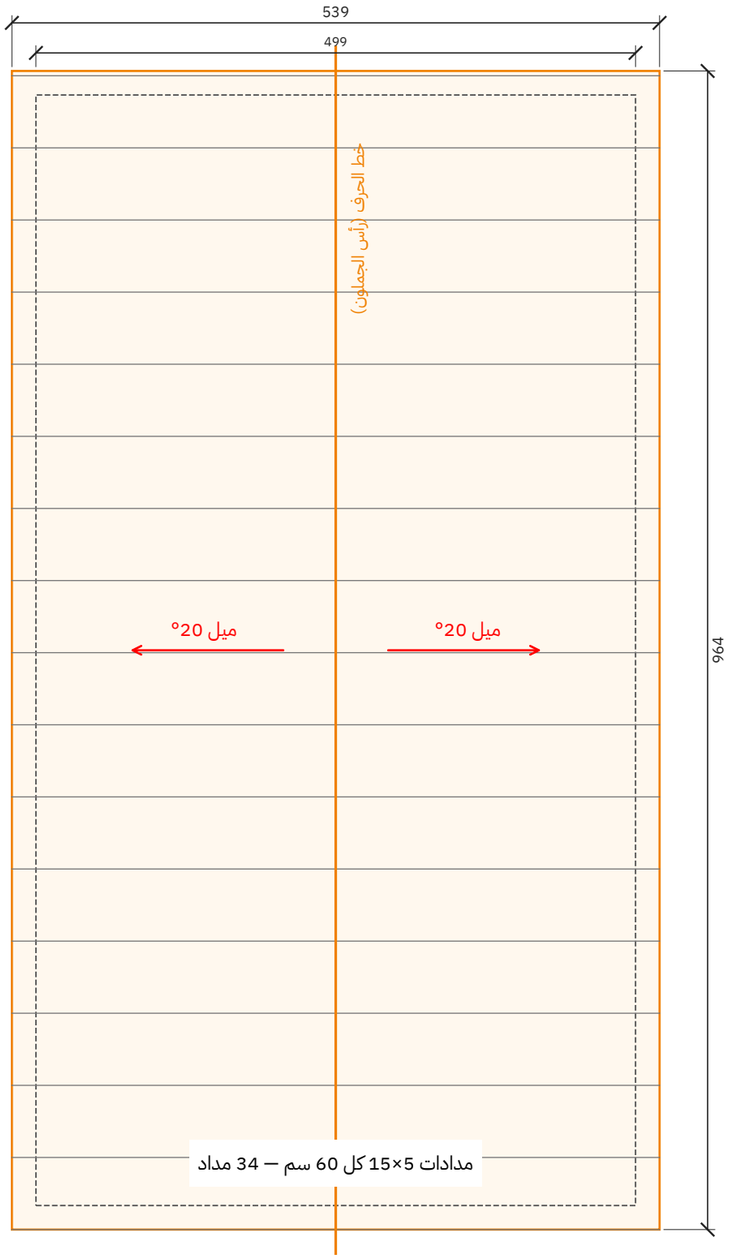



## قطاع عرضي أ-أ

مقياس 1:50 | الوحدة: سم

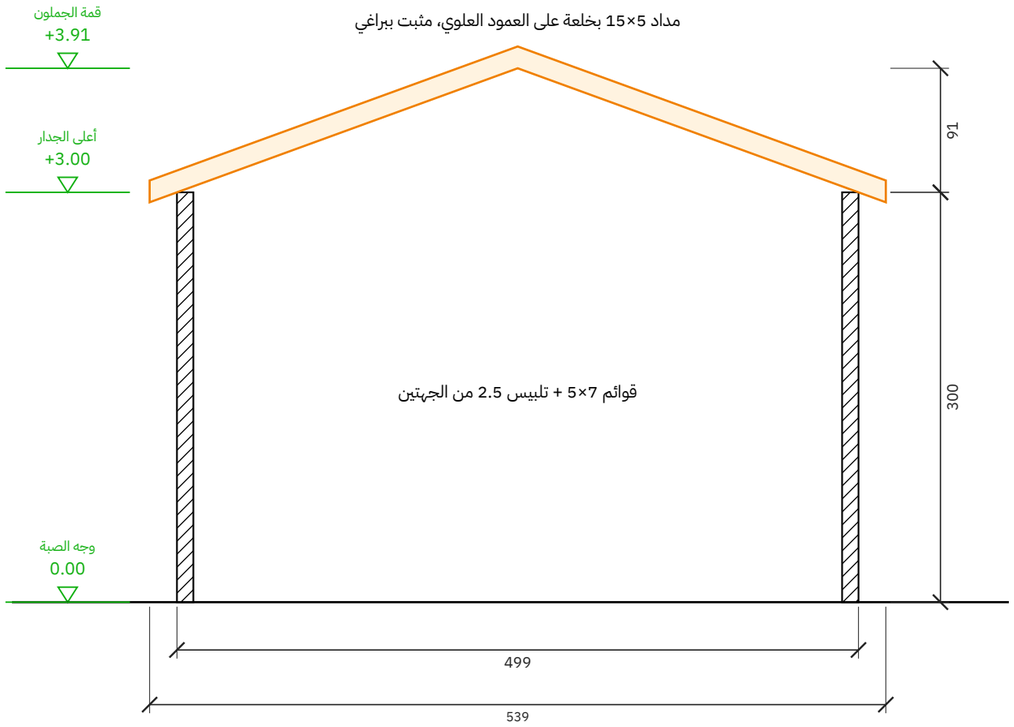


تفصيلة جلوس المداد على العلوي (1:5)

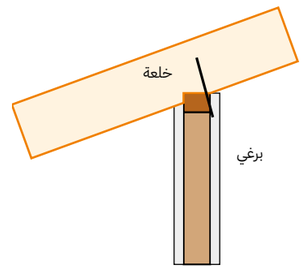


| | | | | | |
|---|---|---|---|---|---|
| مصنع وتد الأخشاب<br>Watad Wood Factory | المشروع / العميل<br>ملحق سطح — غرفة نوم + صالة — 4.75 × 9.00 م<br>عميل — ملحق سطح | عنوان اللوحة<br>مسقط السقف والقطاع | المقياس<br>1:50 | التاريخ<br>2026-10-30 | رقم اللوحة<br>A-04 (4/9) |

## جدول مقاسات الأبواب والشبابيك

مقاس الفتحة الصافي في الجدار - الوحدة: سم

| الرمز | النوع | العرض (سم) | الارتفاع (سم) | ارتفاع الجلسة (سم) | العدد | الموقع |
|---|---|---|---|---|---|---|
| ب1 | باب | 100 | 220 | - | 1 | جدار المدخل (جهة السطح) |
| ب2 | باب | 90 | 210 | - | 1 | غرفة النوم |
| ز1 | شباك | 210 | 210 | 20 | 1 | الجدار الأيمن (القائم + الرفع) |
| ز2 | شباك | 190 | 210 | 20 | 1 | الجدار الخلفي (غرفة النوم) |
| ش1 | شباك | 180 | 140 | 90 | 1 | الجدار الأيمن (القائم + الرفع) |

الإجمالي: أبواب 2 - شبابيك 3

# جدول المساحات وبيانات المشروع

## بيانات المشروع

| البند | البيان |
|---|---|
| المشروع | ملحق سطح — غرفة نوم + صالة — 4.75 × 9.00 م |
| العميل | عميل — ملحق سطح |
| الموقع | — |
| الاستخدام | ملحق سكني على السطح |
| التاريخ | 2026-10-30 |
| نظام البناء | هيكل خشب 5×7 + تلبيس 2.5 سم من الجهتين |
| السقف | جملون 20° — قرميد معدني |

## جدول المساحات


| م | الفراغ | الأبعاد (م) | المساحة (م2) |
|---|---|---|---|
| 1 | الصالة | 4.75 × 4.00 | 19.00 |
| 2 | غرفة النوم | 4.75 × 4.88 | 23.18 |
| | **المساحة الصافية الداخلية** | | **42.18** |
| | **المساحة الإجمالية المبنية** | **4.99 × 9.24** | **46.11** |

# لقطات المنظور الخارجي


المنظور الأمامي



منظور أمامي من اليسار

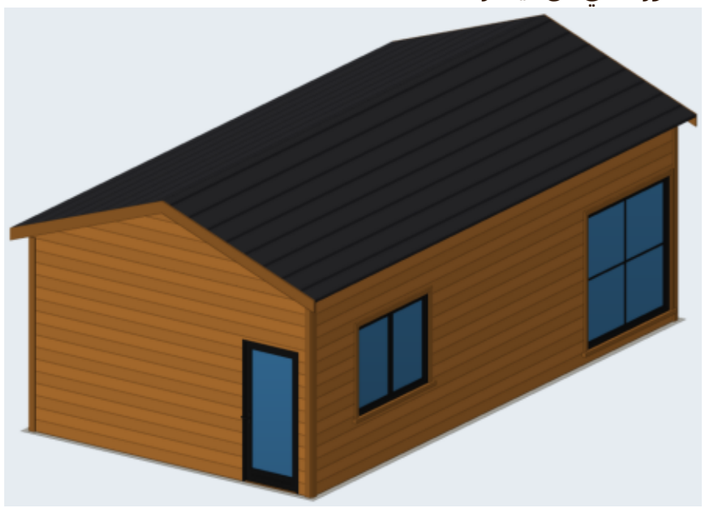


منظور أمامي من اليمين

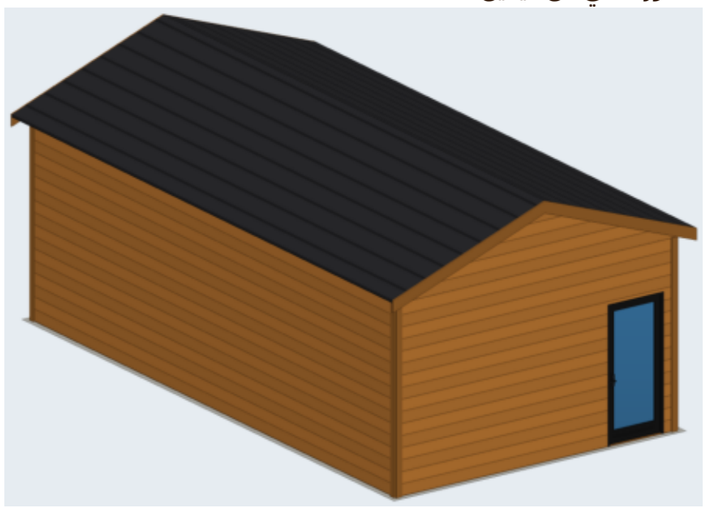

المنظور الخلفي



منظور خلفي من اليمين

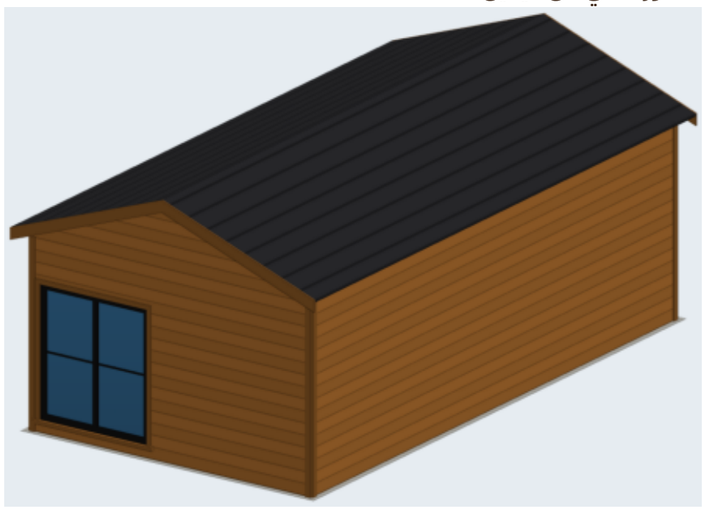

منظر علوي




| | | | | |
|---|---|---|---|---|
| المشروع / العميل<br>ملحق سطح – غرفة نوم + صالة – 4.75 × 9.00 م<br>عميل – ملحق سطح | عنوان اللوحة<br>لقطات المنظور | المقياس<br>– | التاريخ<br>2026-10-30 | رقم اللوحة<br>A-07 (7/9) |

مصنع وتد الأخشاب
Watad Wood Factory

# المقطع العلوي بالفرش

مقطع أفقي على ارتفاع 1.90 م — توزيع الفرش ومسار الحركة

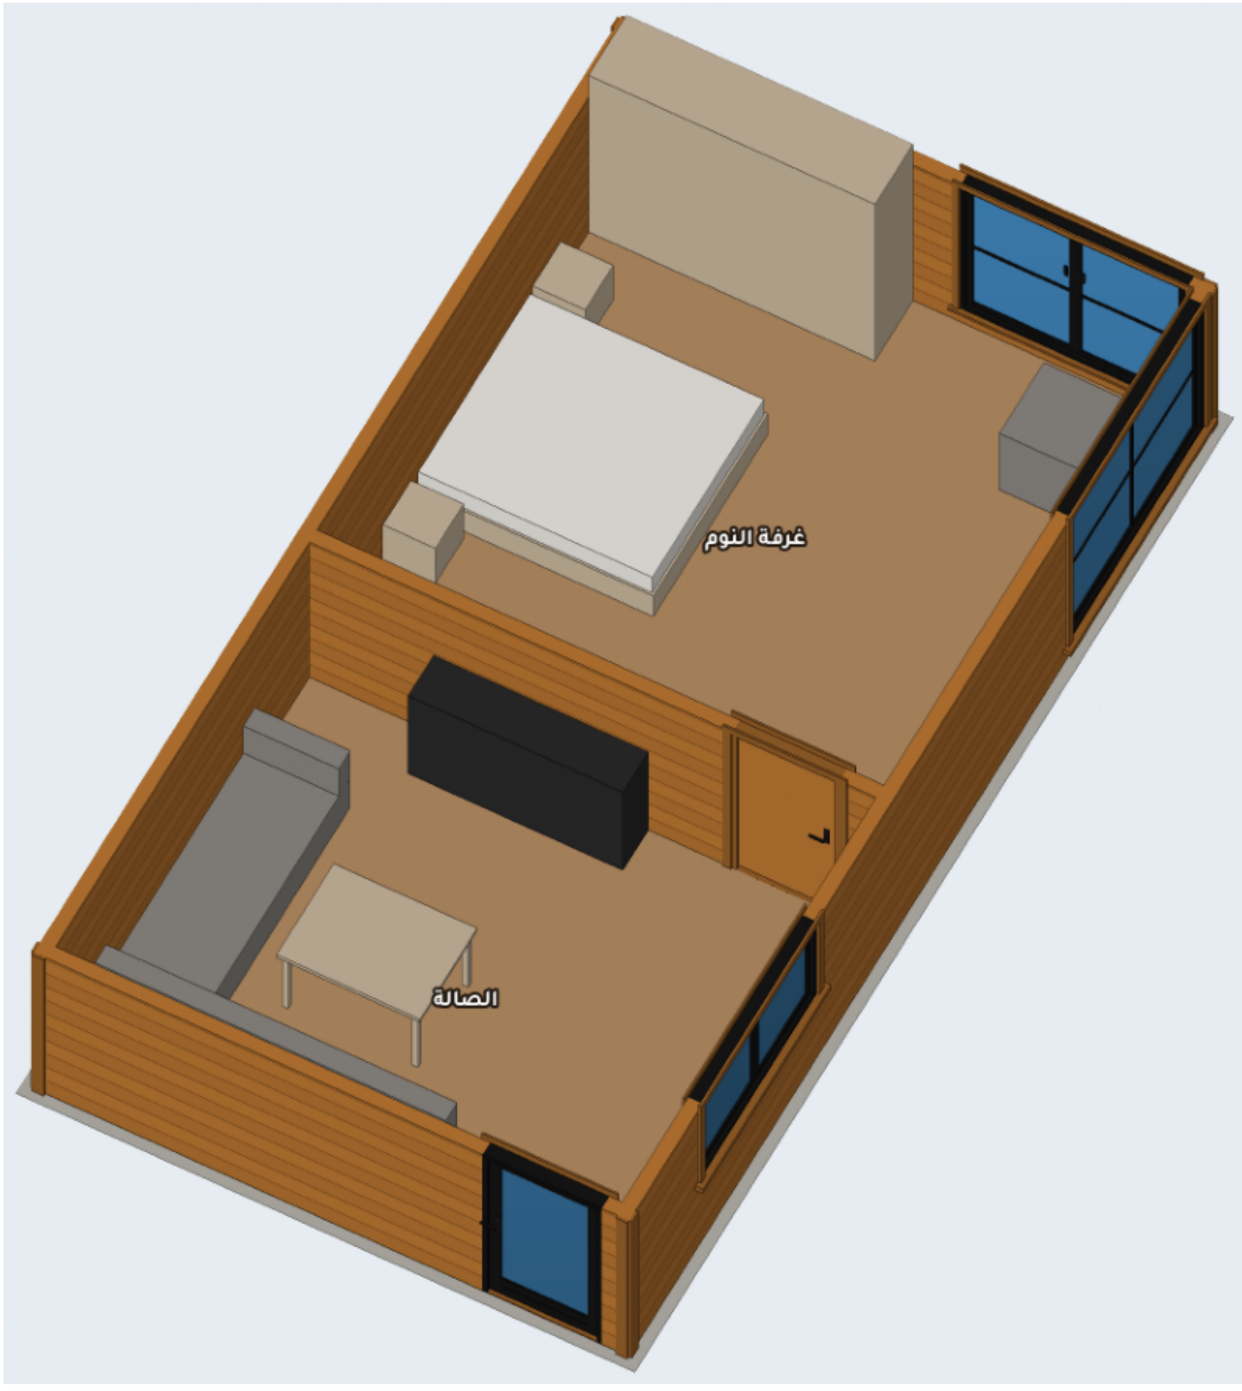


| المشروع / العميل | عنوان اللوحة | المقياس | التاريخ | رقم اللوحة |
|---|---|---|---|---|
| مصنع وتد الأخشاب — Watad Wood Factory<br>ملحق سطح — غرفة نوم + صالة — 4.75 × 9.00 م<br>عميل — ملحق سطح | المقطع العلوي بالفرش | — | 2026-10-30 | A-08 (8/9) |

# المنظور ثلاثي الأبعاد والمواد

النمط: جوزي غامق + إطارات سوداء — رندر واقعي بخامات حقيقية



## جدول المواد والألوان

**الخشب / الصبغة**

صبغة عسلي / سيدر

**القرميد**

قرميد رمادي غامق

**الزجاج**

زجاج أزرق (بلو) عاكس

**إطارات الشبابيك والأبواب**

إطار ألمنيوم أسود

**الكنار والزوايا**

نفس الصبغة أغمق درجة


**الصبة**

خرسانة 0 سم


الدربزين: ألواح أفقية متقاربة (عصري)

تقسيم الشبابيك: شبكة | الباب الرئيسي: زجاج بتقسيمات (فرنسي)

## أنواع الدربزين المعتمدة (من مشاريع المصنع)

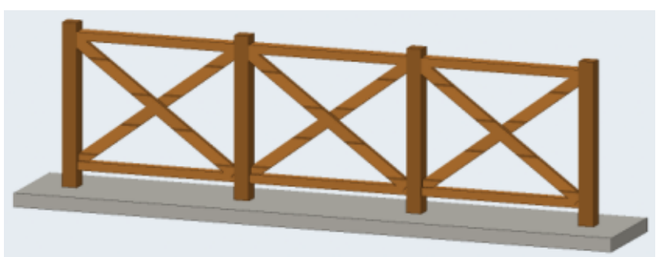

تقاطع X (صورة 5)

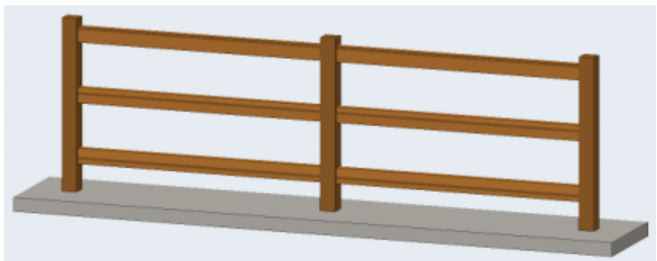

3 مرابيع أفقية (صورة 2)



قوائم رأسية متقاربة (صورة 1)

| المشروع / العميل | عنوان اللوحة | المقياس | التاريخ | رقم اللوحة |
|---|---|---|---|---|
| **مصنع وتد الأخشاب** Watad Wood Factory<br>**ملحق سطح — غرفة نوم + صالة — 4.75 × 9.00 م**<br>**عميل — ملحق سطح** | **المنظور والمواد** | — | **2026-10-30** | **A-09 (9/9)** |