


مصنع وتد الأخشاب · ملف التصميم

جلسة شتوية – بلكونة

36 م² · مظلة خشب · جلسة عربية L · مشب نار حجري · فوانيس


المسقط الأفقي مع الفرش

الأبعاد بالسنتيمتر - الجدران: قوائم 7×5 + تلبيس 2.5 من الجهتين (12 سم)

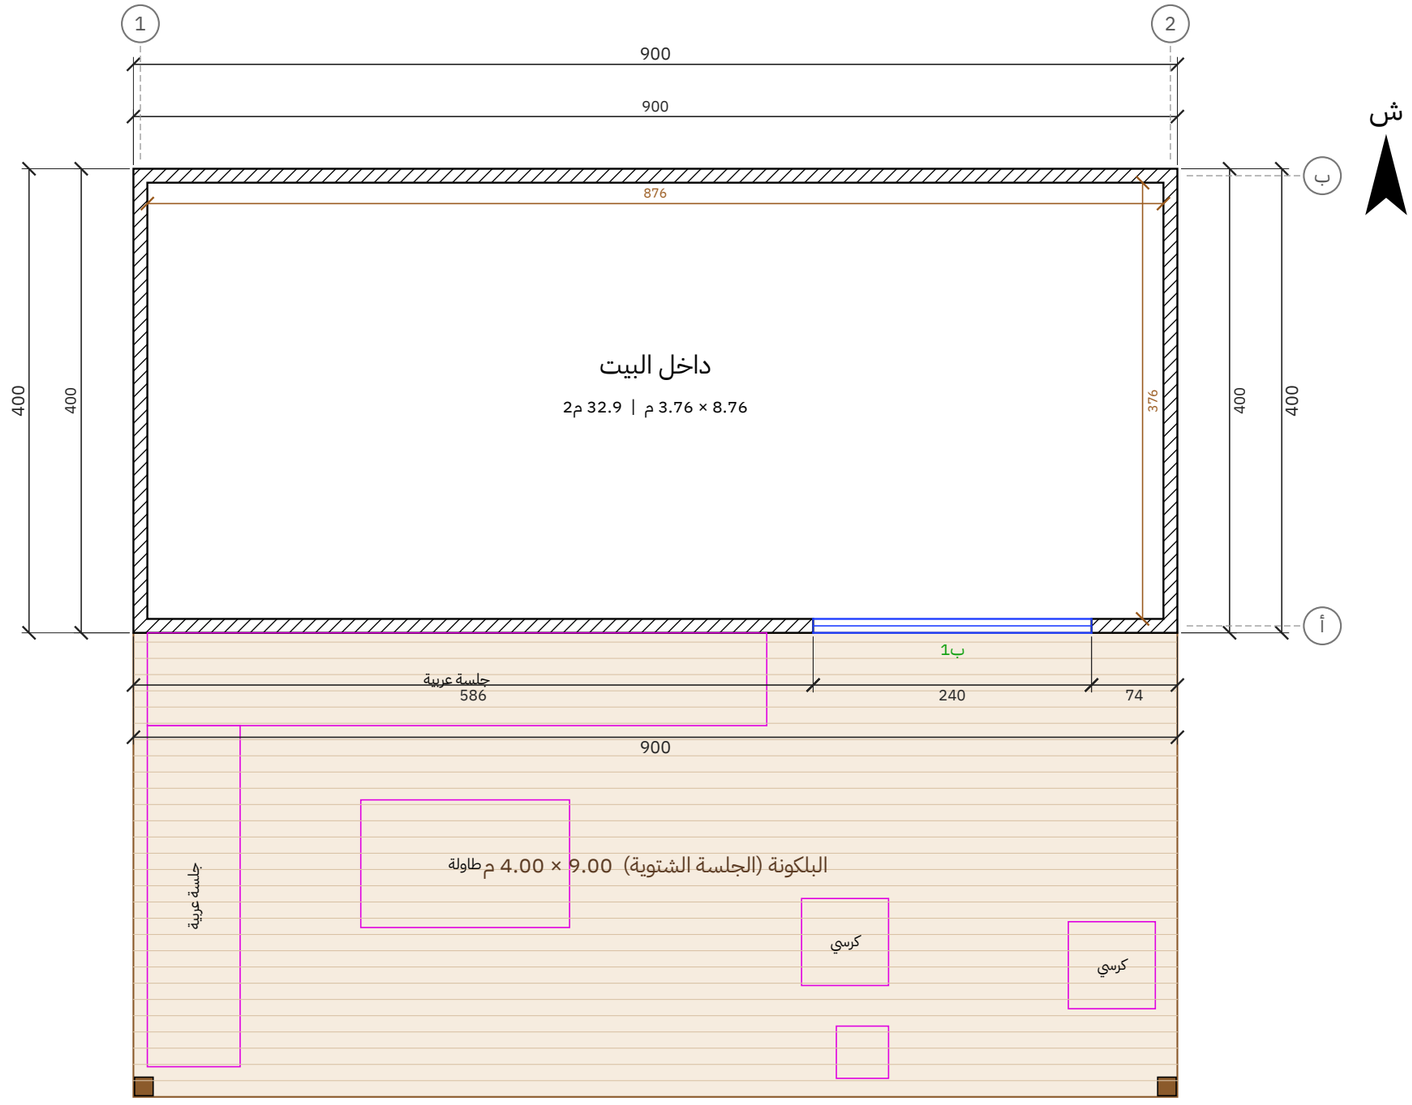


المشروع / العميل	عنوان اللوحة	المقياس	التاريخ	رقم اللوحة
جلسة شتوية – بلكونة 9.00 × 4.00 م (36 م²) **مشروع – جلسة شتوية**	**المسقط الأفقي**	**1:50**	**2026-10-25**	**A-01 (1/9)**

مصنع وتد الأخشاب
Watad Wood Factory

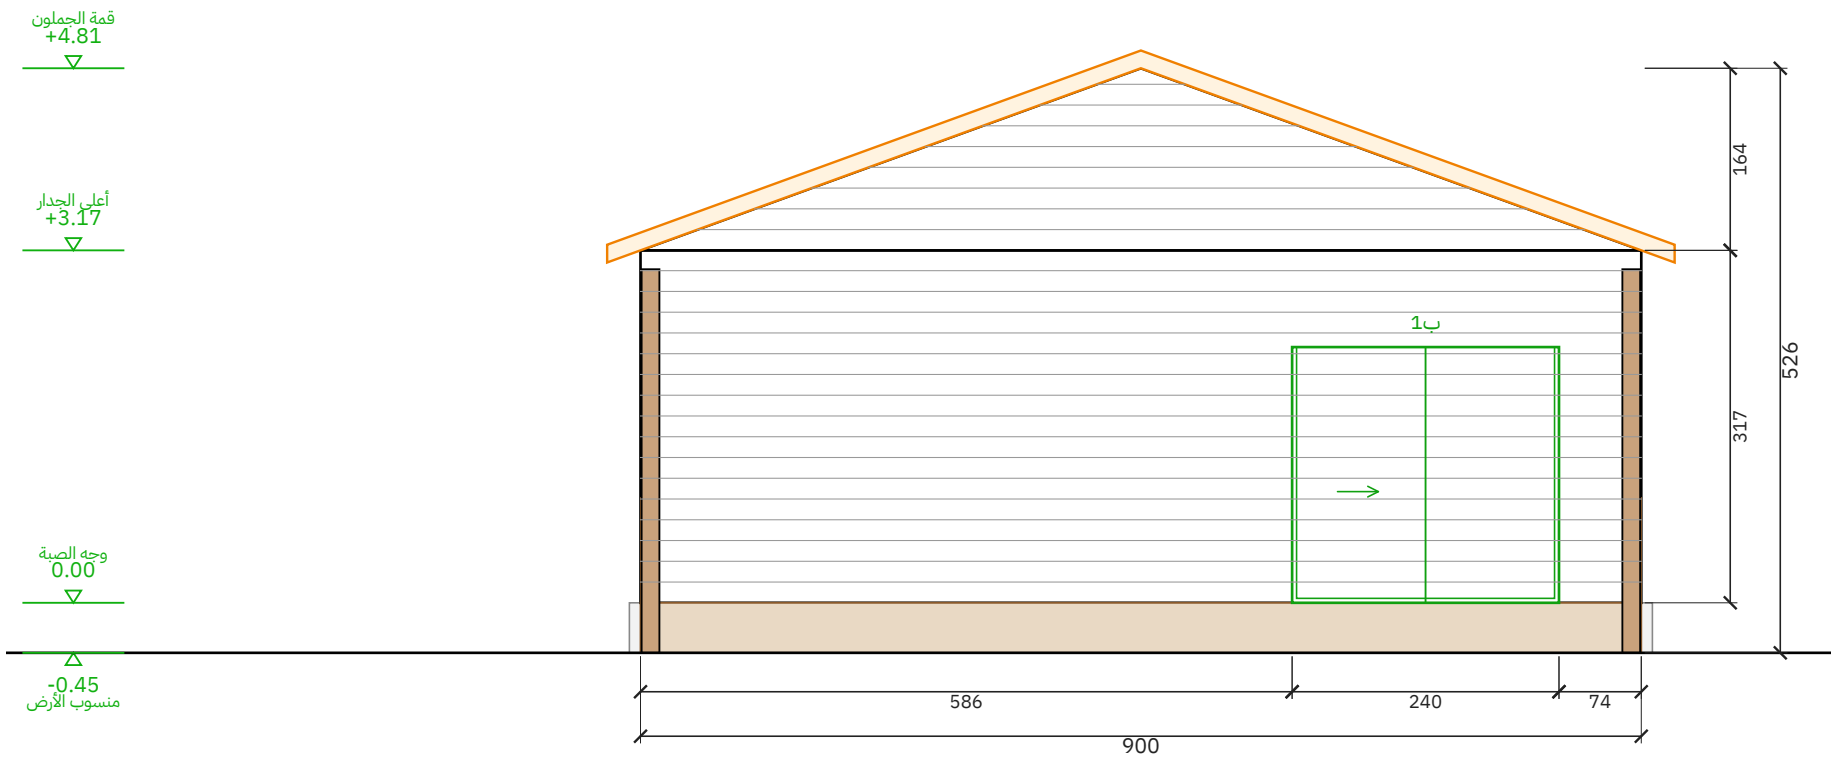

جدار البيت على البلكونة

مقياس 1:50 | الوحدة: سم

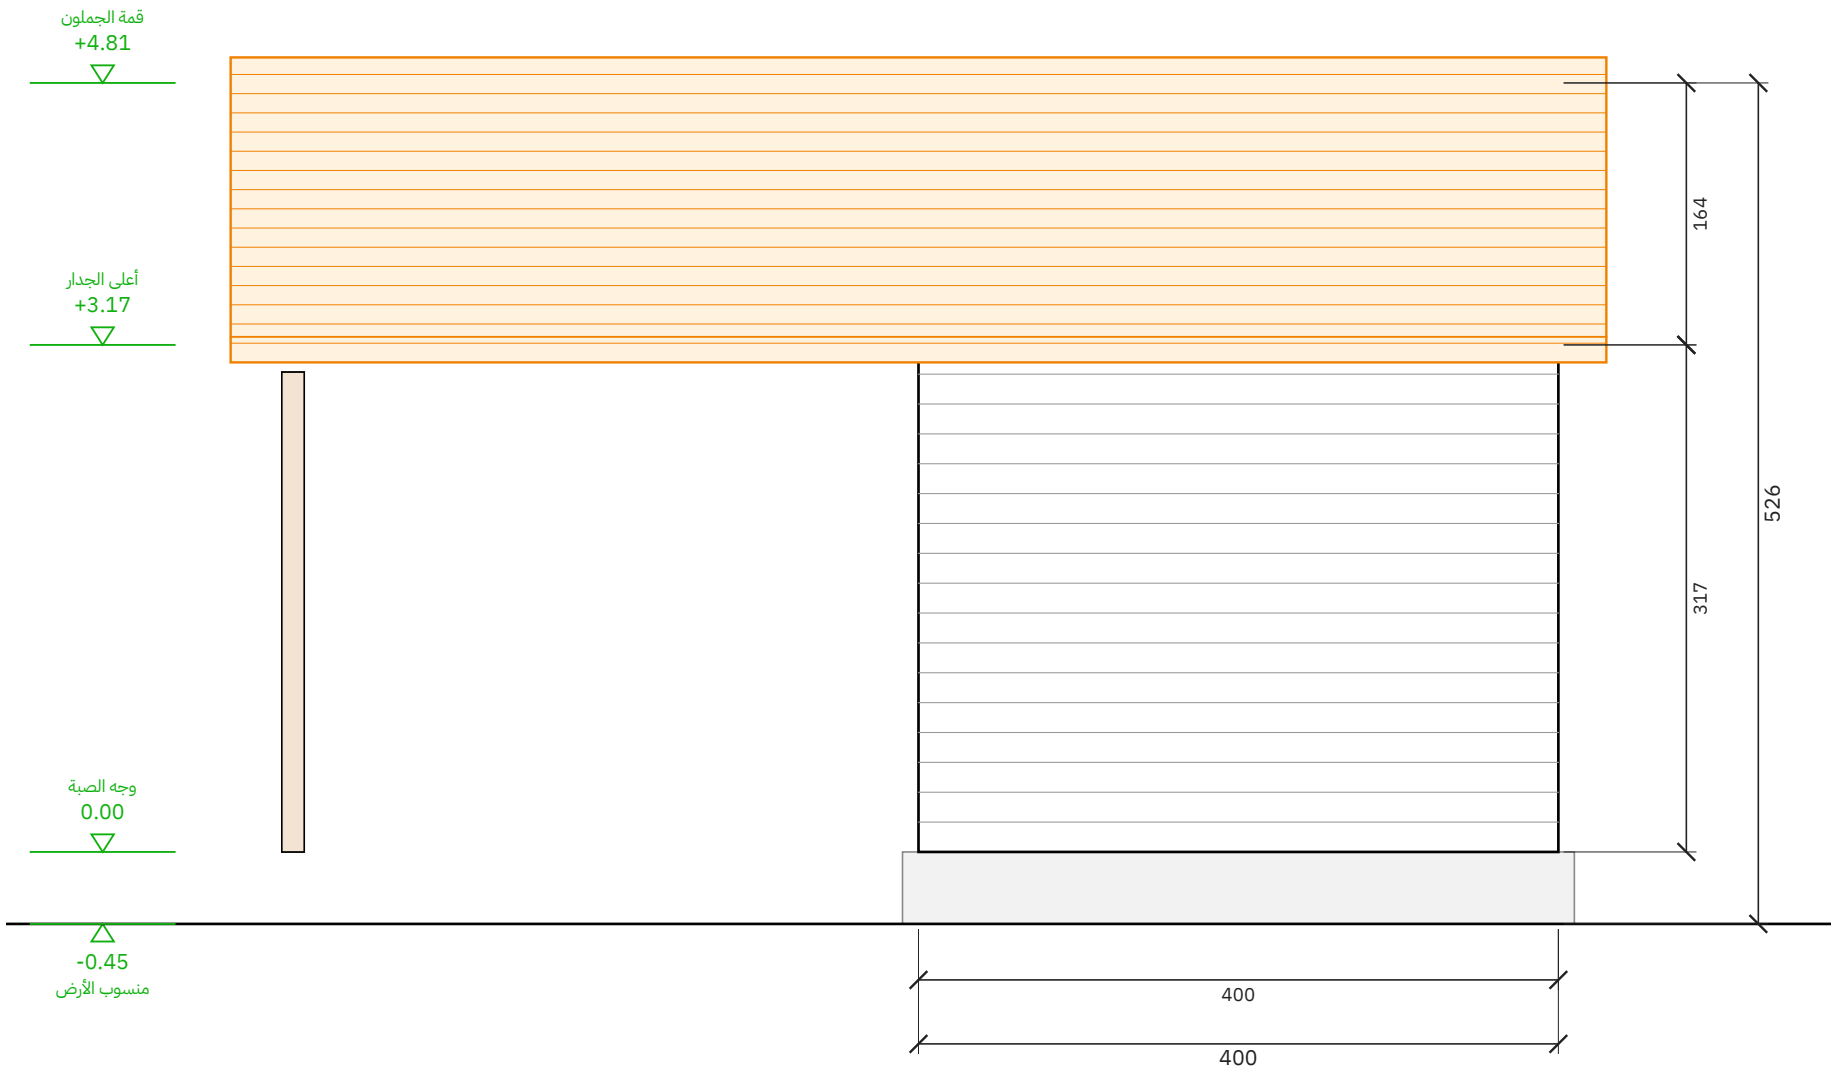


شرق

مقياس 1:50 | الوحدة: سم


المشروع / العميل	عنوان اللوحة	المقياس	التاريخ	رقم اللوحة
جلسة شتوية – بلكونة 9.00 × 4.00 م (36 م²) مشروع – جلسة شتوية	جدار البيت على البلكونة وشرق	1:50	2026-10-25	A-02 (2/9)

مصنع وتد الأخشاب
Watad Wood Factory

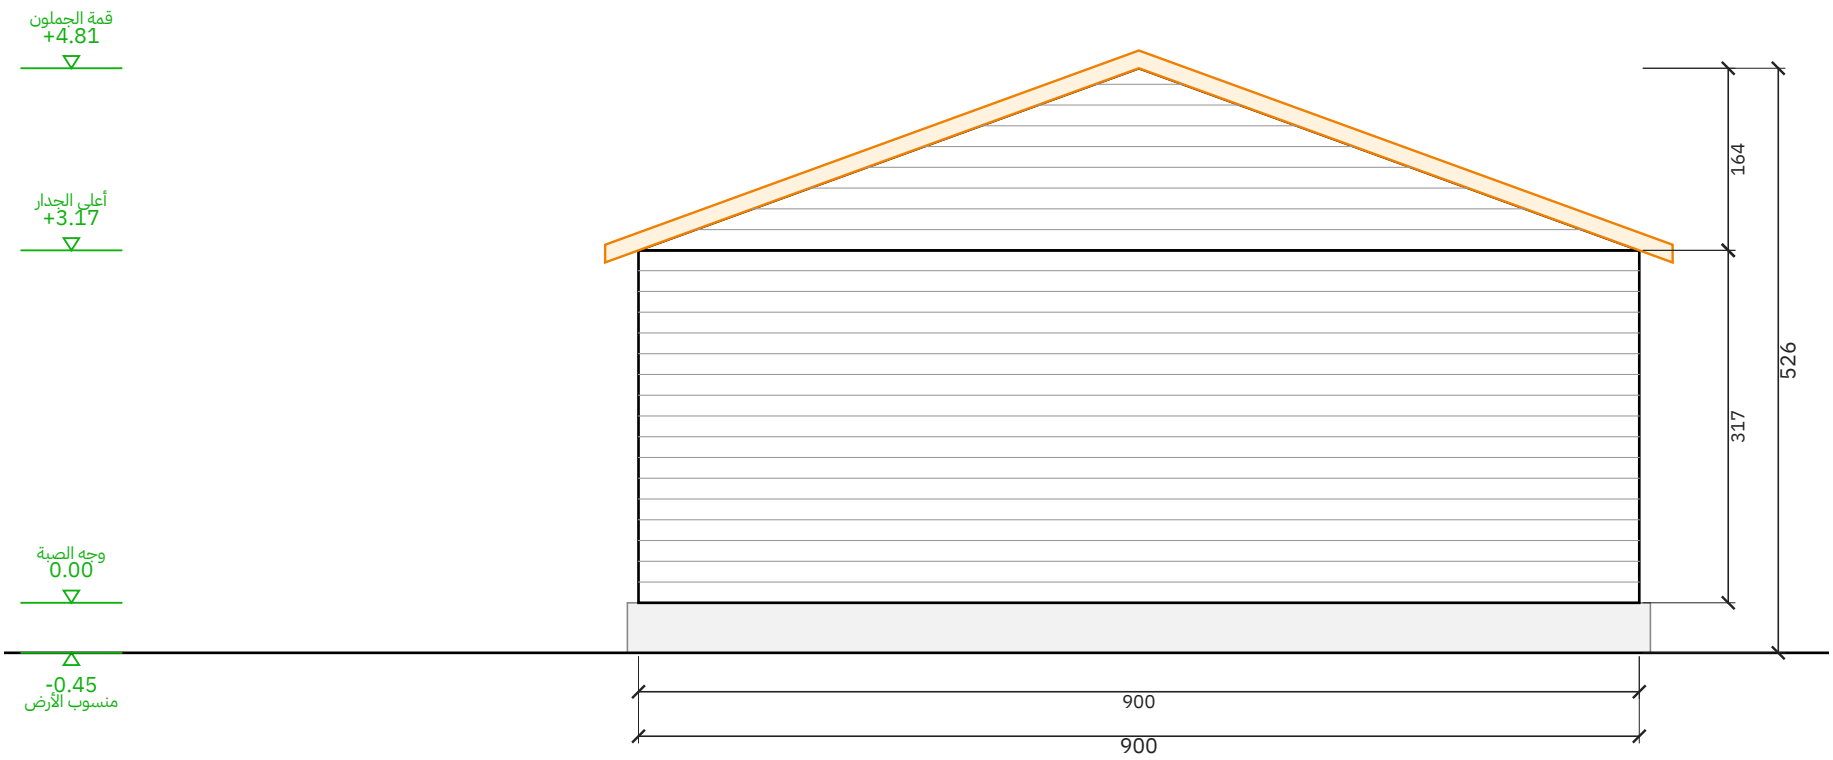

شمال

مقياس 1:50 | الوحدة: سم

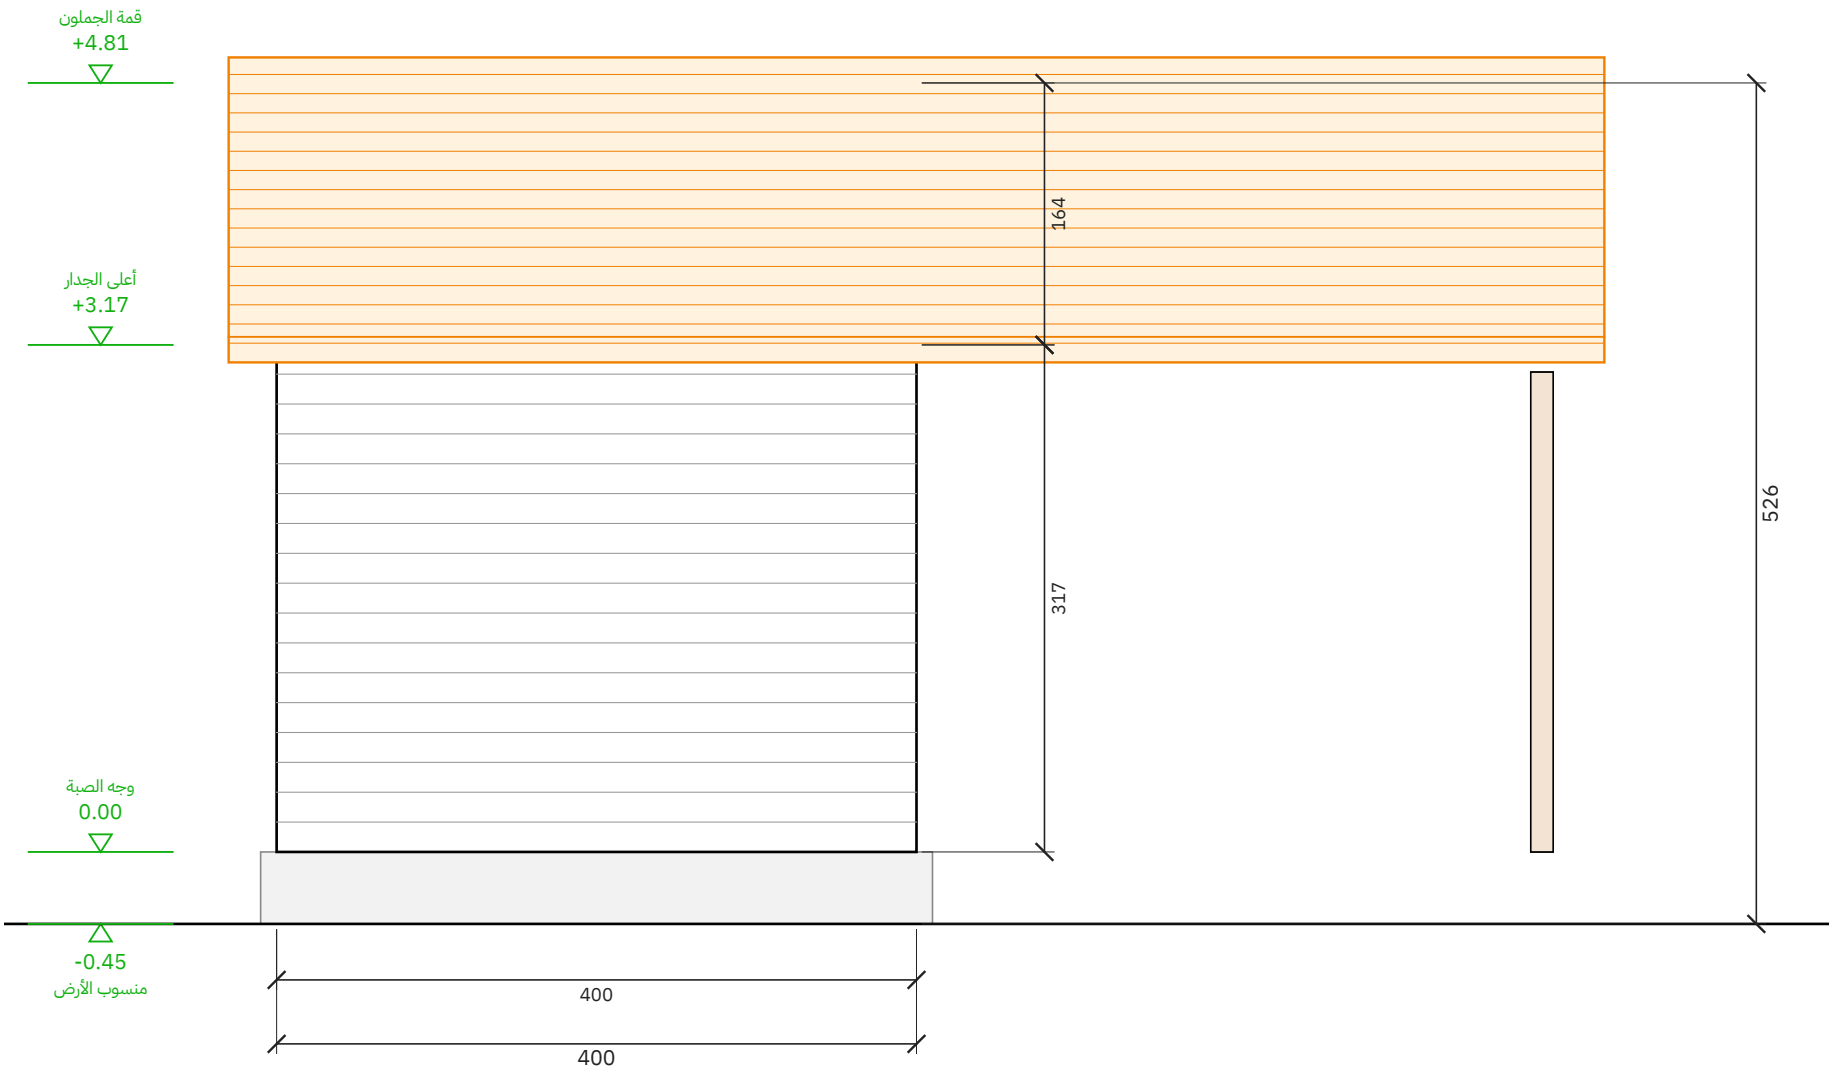

غرب


مقياس 1:50 | الوحدة: سم

المشروع / العميل	عنوان اللوحة	المقياس	التاريخ	رقم اللوحة
جلسة شتوية – بلكونة 9.00 × 4.00 م (36 م²) **مشروع – جلسة شتوية**	**شمال وغرب**	**1:50**	**2026-10-25**	**A-03 (3/9)**

مصنع وتد الأخشاب
Watad Wood Factory


مسقط السقف (جملون)

رفرف 30 سم من كل جهة | مقياس 1:50

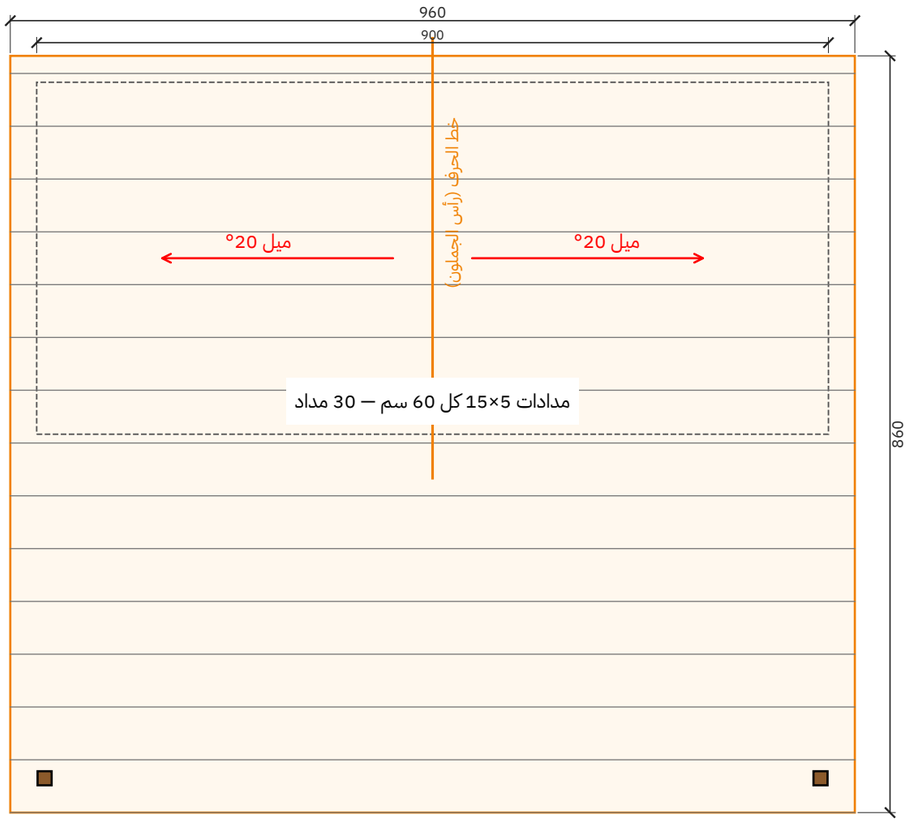


قطاع عرضي أ-أ

مقياس 1:50 | الوحدة: سم

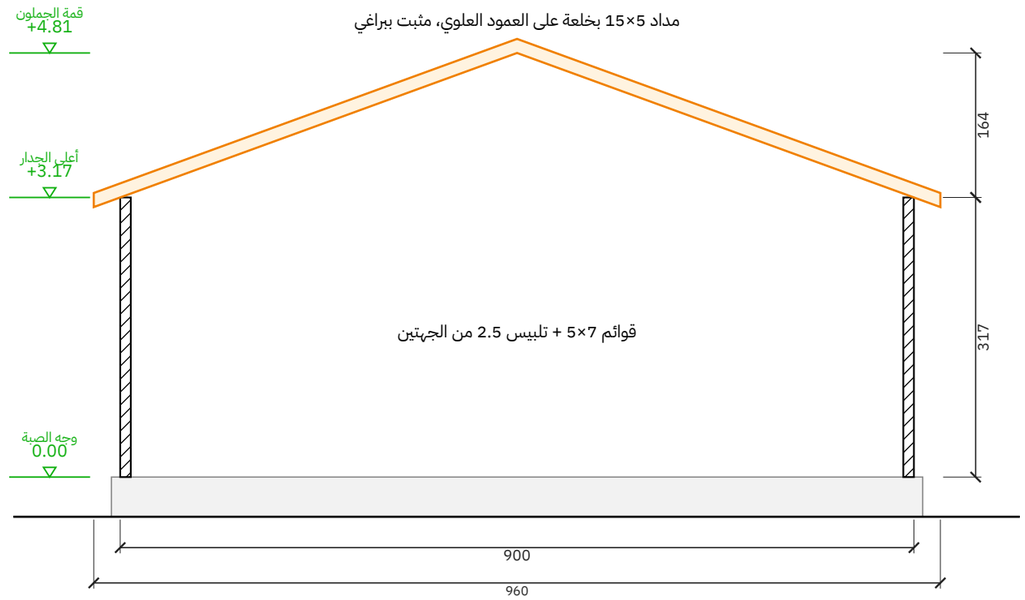

تفصيلة جلوس المداد على العلوي (1:5)

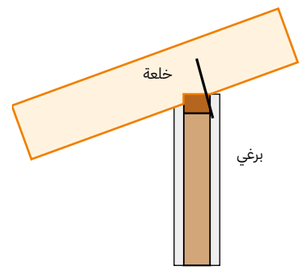


المشروع / العميل	عنوان اللوحة	المقياس	التاريخ	رقم اللوحة
جلسة شتوية – بلكونة 9.00 × 4.00 م (36 م²) مشروع – جلسة شتوية	مسقط السقف والقطاع	1:50	2026-10-25	A-04 (4/9)


مصنع وتد الأخشاب
Watad Wood Factory

لقطات المنظور الخارجي

المنظور الأمامي

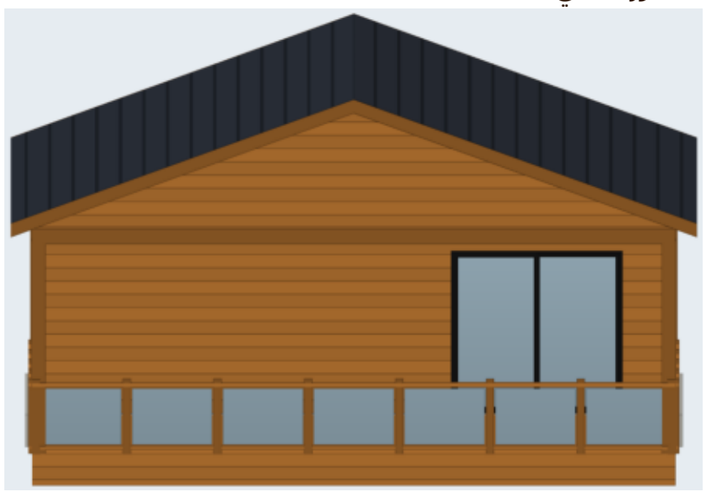


منظور أمامي من اليسار

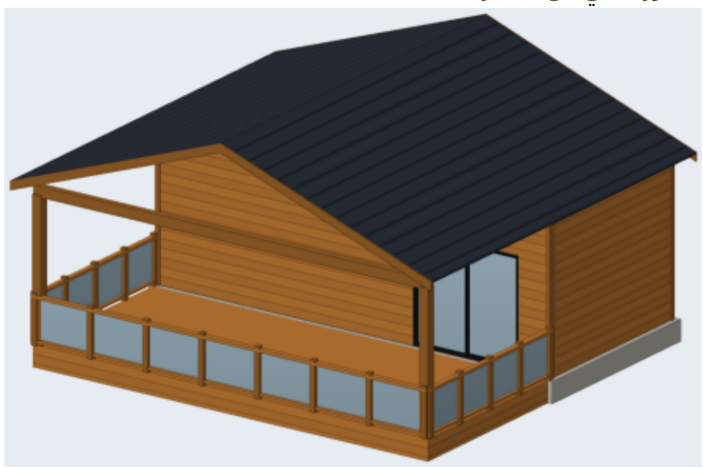


منظور أمامي من اليمين




المنظور الخلفي

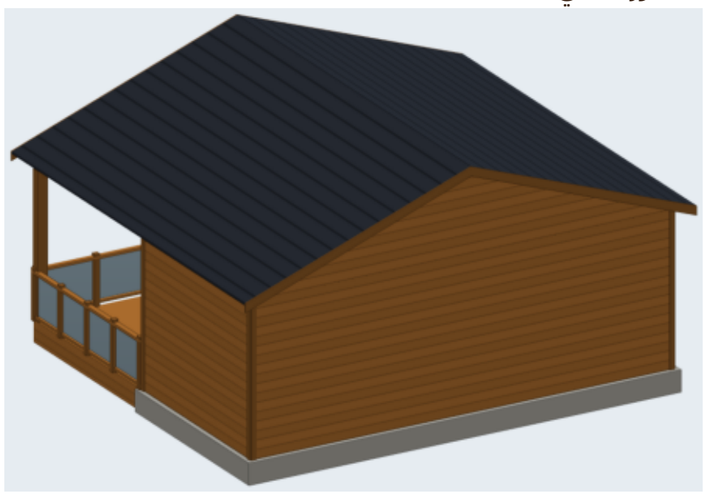

منظور خلفي من اليمين

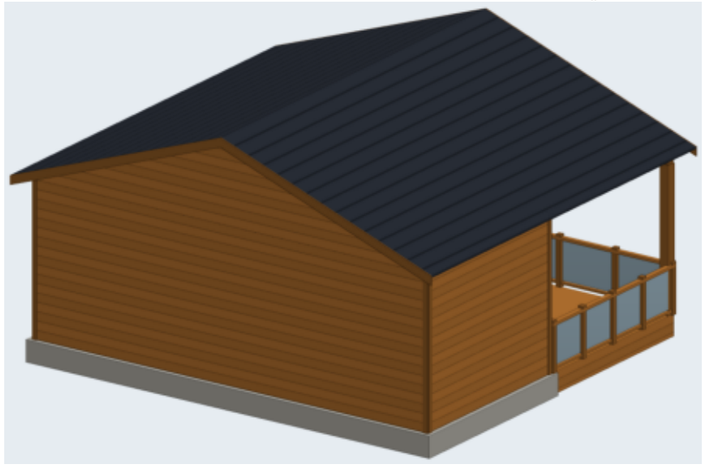

منظر علوي

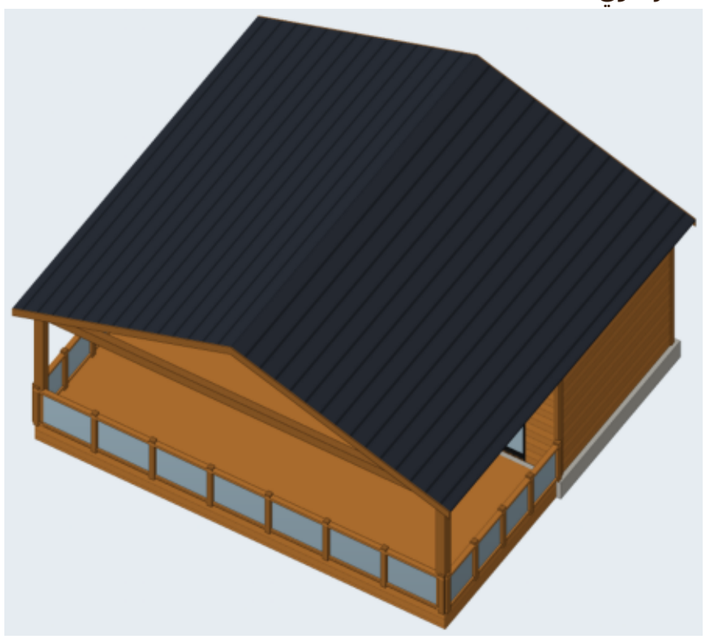


المشروع / العميل جلسة شتوية – بلكونة 9.00 × 4.00 م (36 م²) مشروع – جلسة شتوية	عنوان اللوحة لقطات المنظور	المقياس –	التاريخ 2026-10-25	رقم اللوحة A-07 (7/9)

مصنع وتد الأخشاب
Watad Wood Factory

المقطع العلوي بالفرش

مقطع أفقي على ارتفاع 1.90 م — توزيع الفرش ومسار الحركة

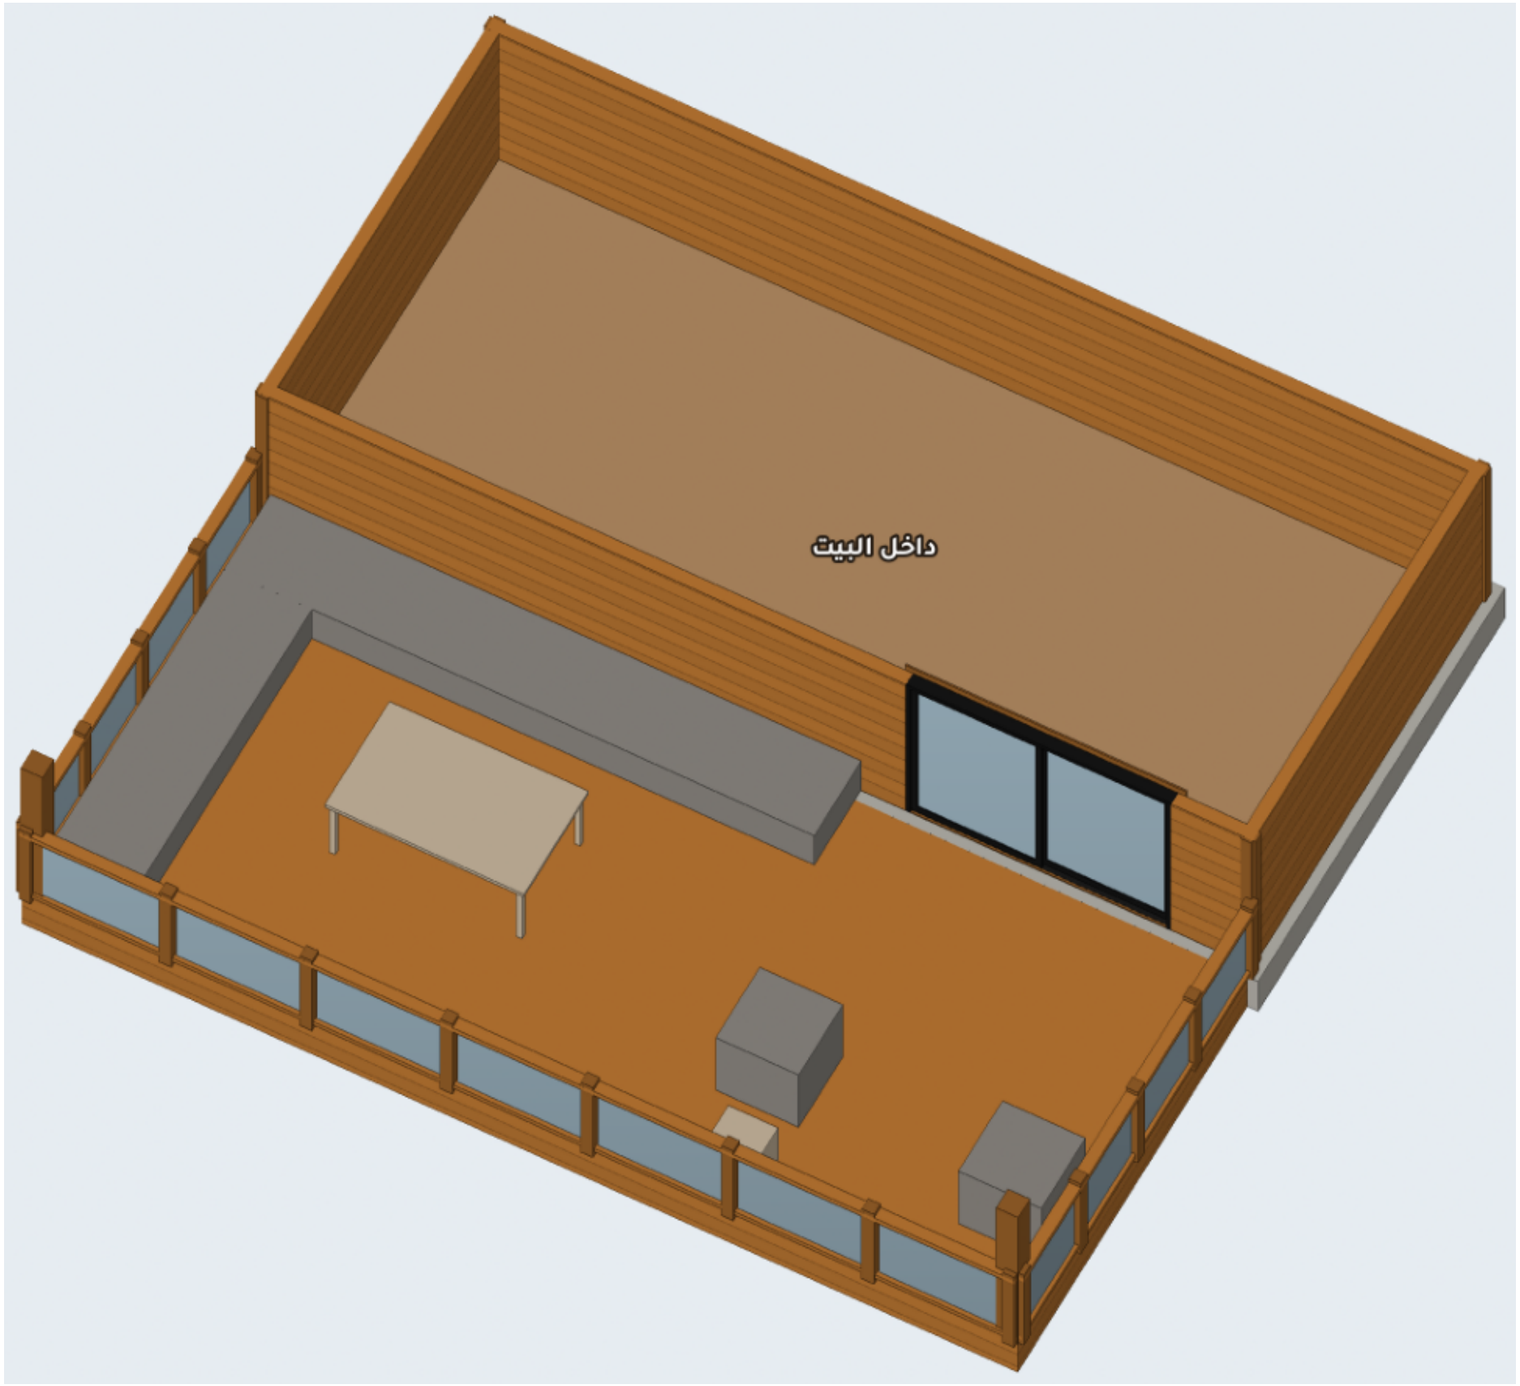

المشروع / العميل	عنوان اللوحة	المقياس	التاريخ	رقم اللوحة
جلسة شتوية — بلكونة 9.00 × 4.00 م (36 م²) **مشروع — جلسة شتوية**	**المقطع العلوي بالفرش**	—	**2026-10-25**	**A-08 (8/9)**

مصنع وتد الأخشاب
Watad Wood Factory



مصنع وتد الأخشاب



مصنع وتد الأخشاب



مصنع وتد الأخشاب



مصنع وتد الأخشاب



مصنع وتد الأخشاب



مصنع وتد الأخشاب

جدول مقاسات الأبواب والشبابيك


مقاس الفتحة الصافي في الجدار - الوحدة: سم

الرمز	النوع	العرض (سم)	الارتفاع (سم)	ارتفاع الجلسة (سم)	العدد	الموقع
ب1	باب مزدوج	240	230	-	1	جدار البيت على البلكونة

الإجمالي: أبواب 1 - شبابيك 0

المنظور ثلاثي الأبعاد والمواد

النمط: برتقالي محمر + قرميد فحمي + دربزين X — رندر واقعي بخامات حقيقية

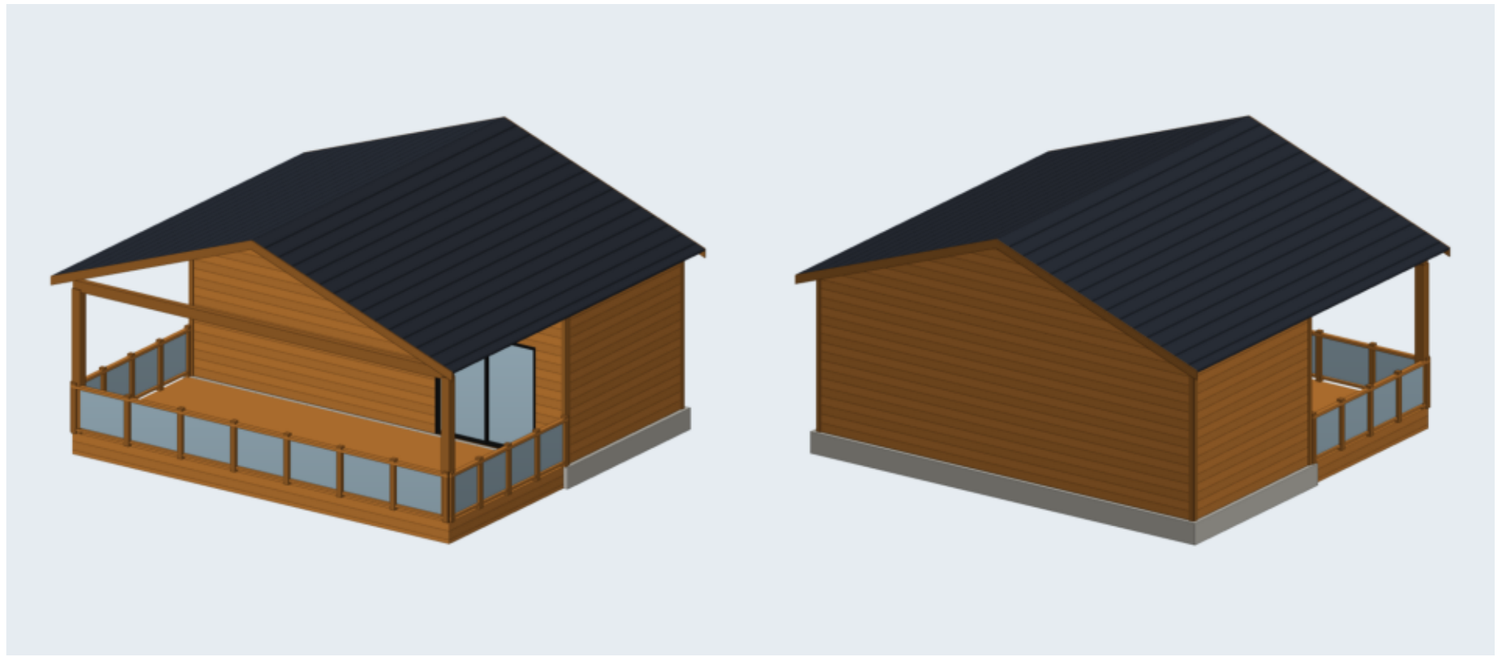

جدول المواد والألوان

الخشب / الصبغة

صبغة عسلي / سيدر

القرميد

قرميد فحمي / أسود مزرق

الزجاج

زجاج شفاف

إطارات الشبابيك والأبواب

إطار ألمنيوم أسود

الكنار والزوايا

نفس الصبغة أغمق درجة


الصبة

خرسانة 45 سم


الدربزين: ألواح أفقية متقاربة (عصري)

تقسيم الشبابيك: بدون | الباب الرئيسي: سحاب زجاج

أنواع الدربزين المعتمدة (من مشاريع المصنع)

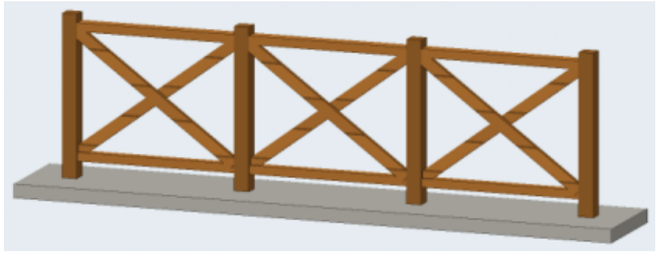

تقاطع X (صورة 5)

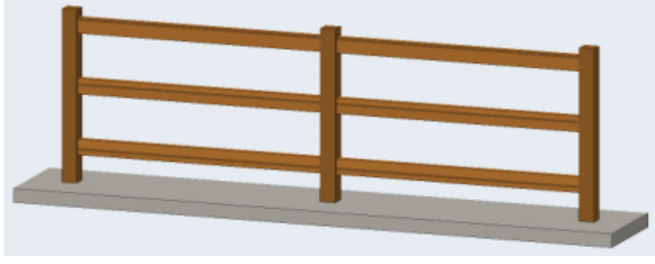

3 مرابيع أفقية (صورة 2)



قوائم رأسية متقاربة (صورة 1)

المشروع / العميل	عنوان اللوحة	المقياس	التاريخ	رقم اللوحة
مصنع وتد الأخشاب Watad Wood Factory **جلسة شتوية – بلكونة 9.00 × 4.00 م (36 م²)** **مشروع – جلسة شتوية**	**المنظور والمواد**	**–**	**2026-10-25**	**A-09 (9/9)**

جدول المساحات وبيانات المشروع

بيانات المشروع

البند	البيان
المشروع	جلسة شتوية — بلكونة 9.00 × 4.00 م (36 م²)
العميل	مشروع — جلسة شتوية
الموقع	—
الاستخدام	جلسة خارجية شتوية
التاريخ	2026-10-25
نظام البناء	هيكل خشب 5×7 + تلبيس 2.5 سم من الجهتين
السقف	جملون 20° — قرميد معدني

جدول المساحات

م	الفراغ	الأبعاد (م)	المساحة (م2)
1	داخل البيت	8.76 × 3.76	32.94
	المساحة الصافية الداخلية		**32.94**
	البلكونة (الجلسة الشتوية)	**9.00 × 4.00**	**36.00**
	المساحة الإجمالية المبنية	**9.00 × 4.00**	**36.00**
	المساحة الكلية (المبنية + التراس)		**72.00**