

المسقط الأفقي مع الفرش

الأبعاد بالسنتيمتر - الجدران: قوائم 7×5 + تلبيس 2.5 من الجهتين (12 سم)

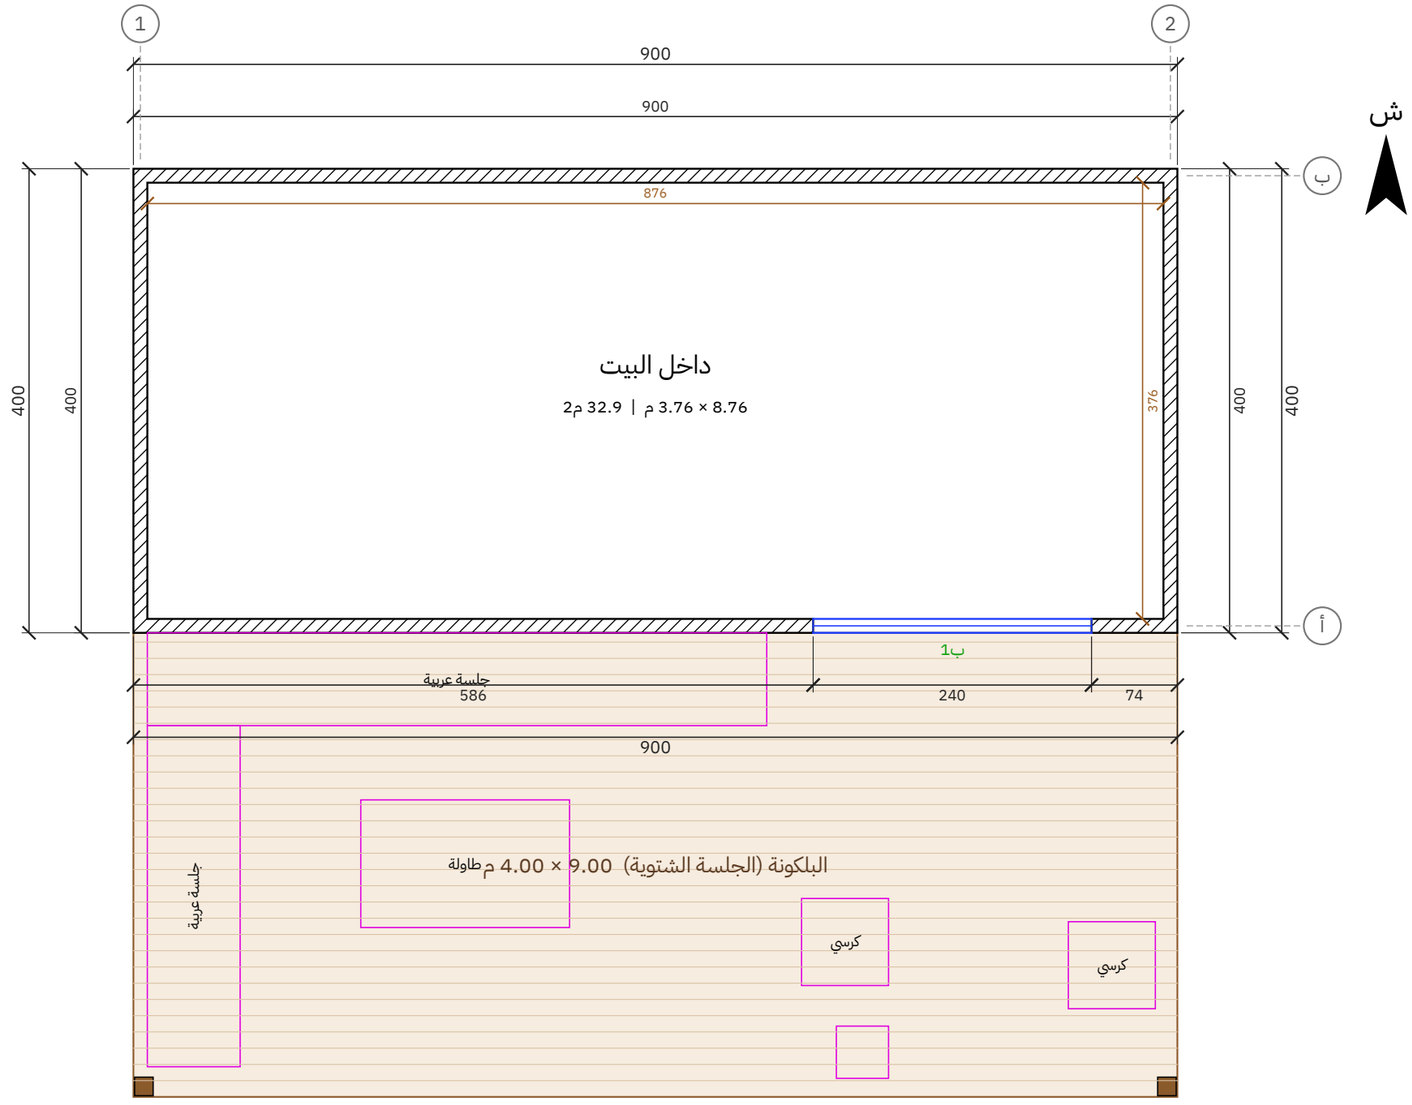


المشروع / العميل	عنوان اللوحة	المقياس	التاريخ	رقم اللوحة
جلسة شتوية – بلكونة 9.00 × 4.00 م (36 م²) **مشروع – جلسة شتوية**	**المسقط الأفقي**	**1:50**	**2026-10-25**	**A-01 (1/9)**

مصنع وتد الأخشاب
Watad Wood Factory

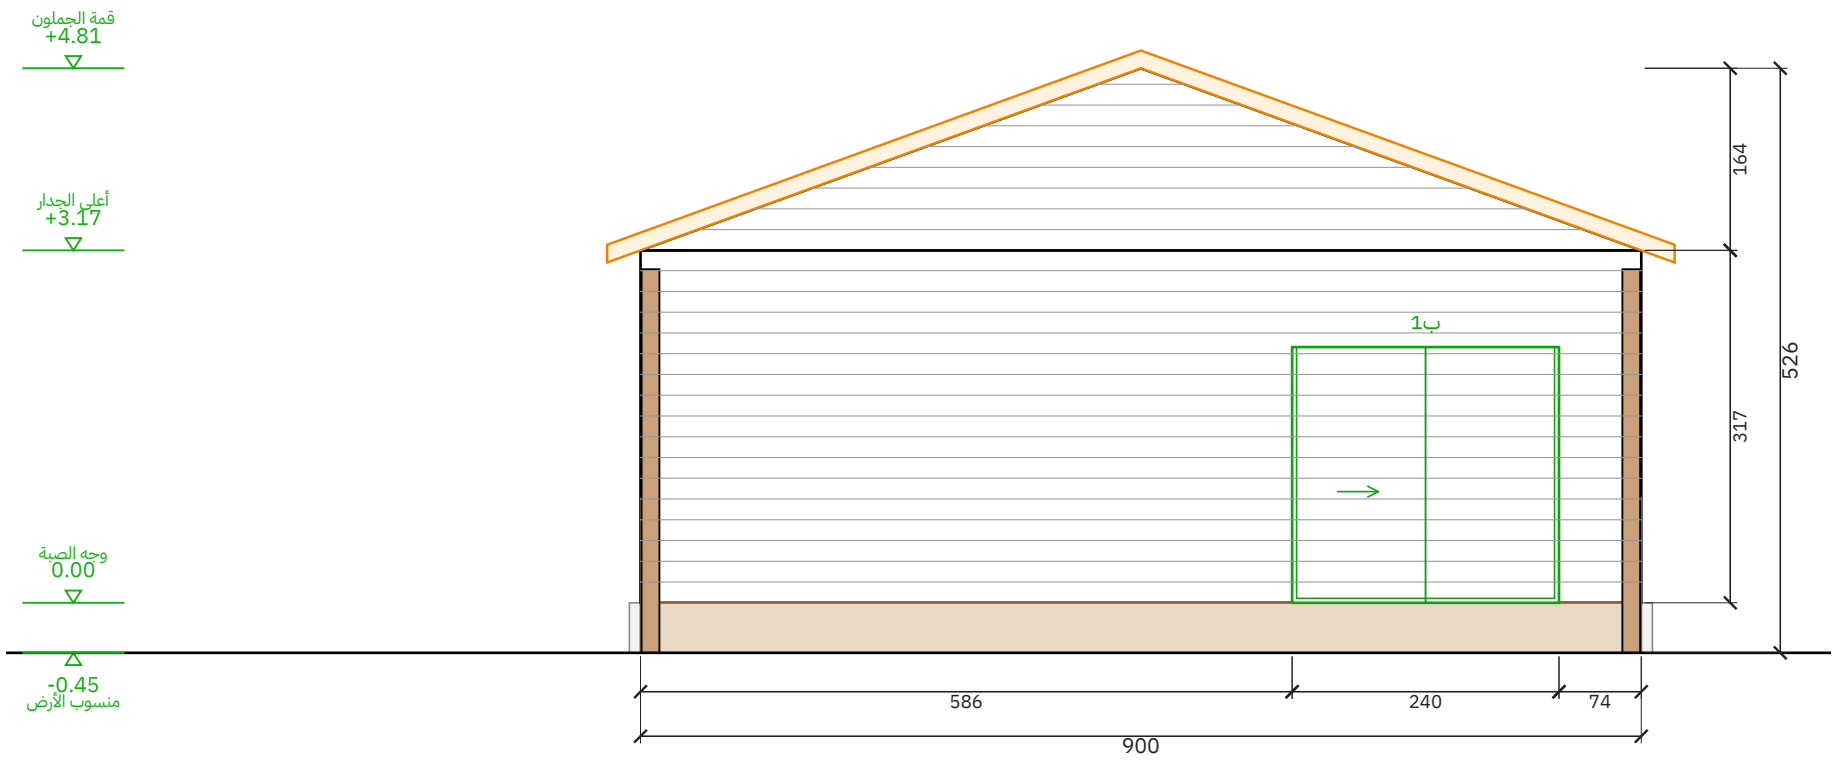

جدار البيت على البلكونة

مقياس 1:50 | الوحدة: سم

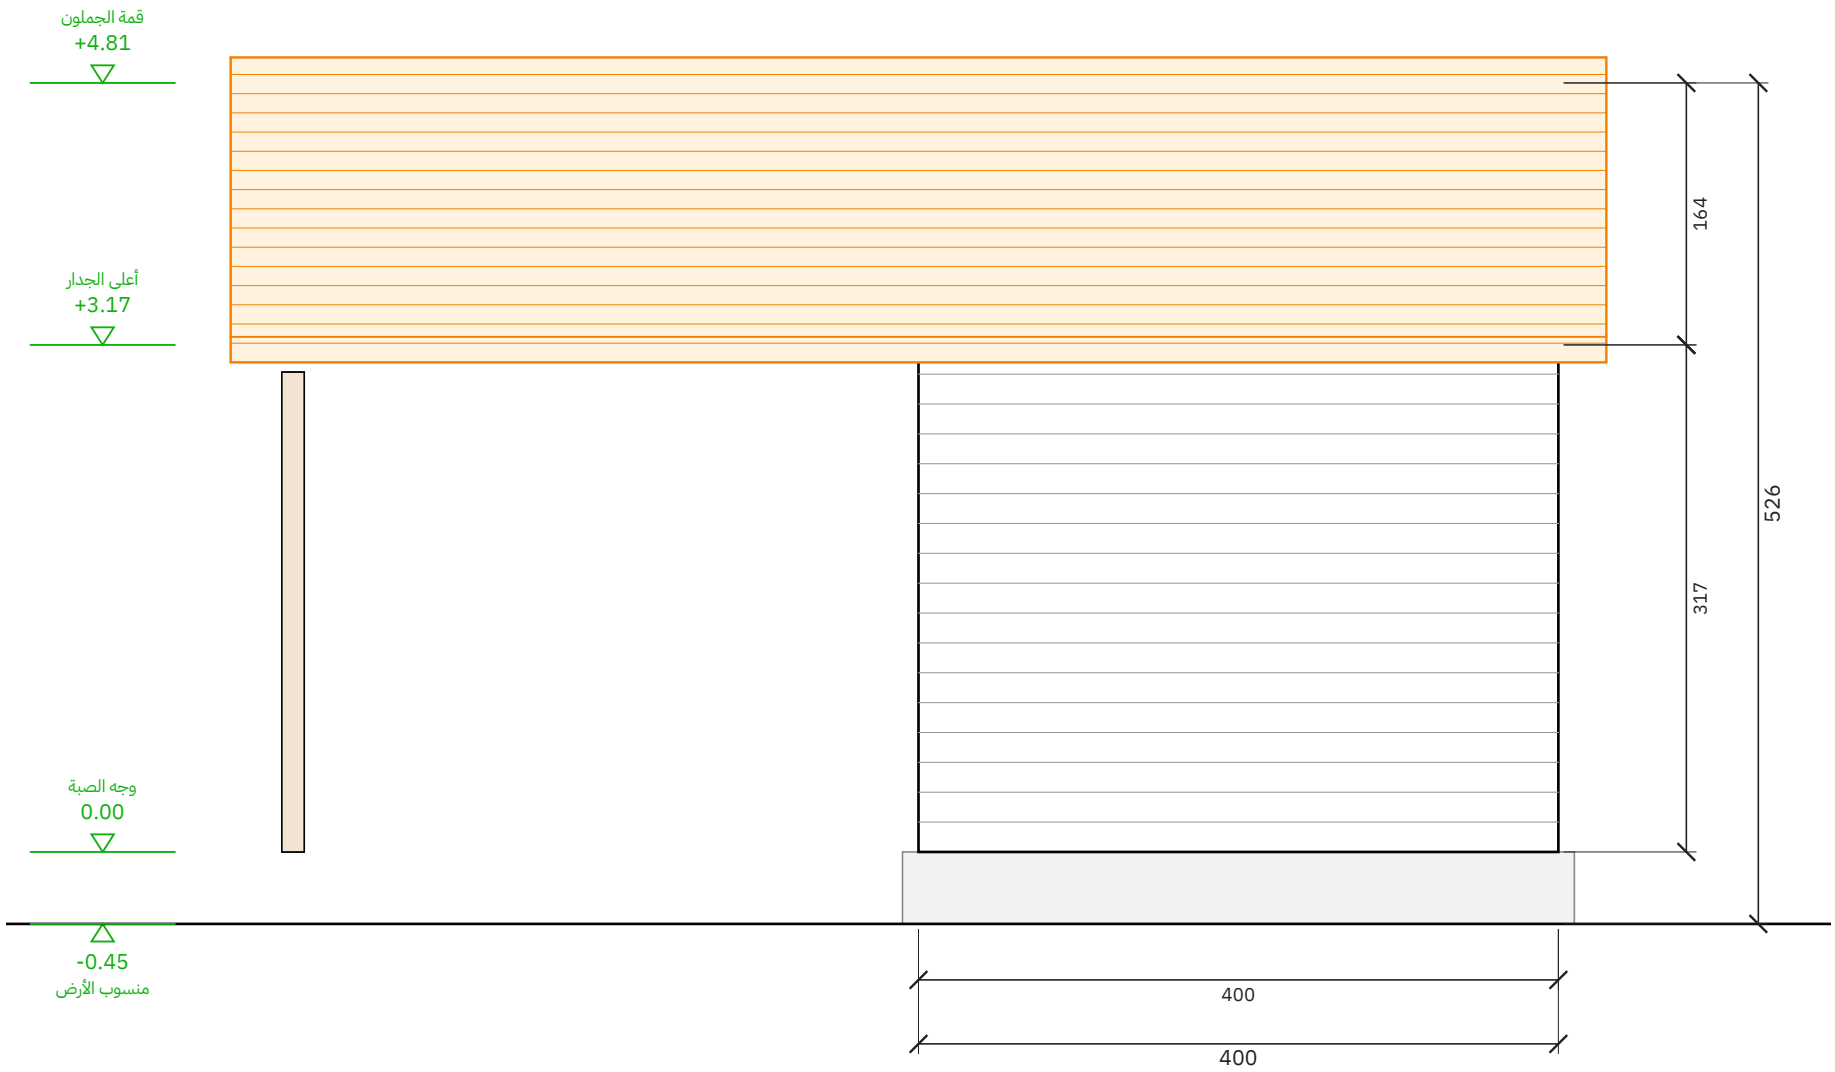


شرق

مقياس 1:50 | الوحدة: سم


المشروع / العميل	عنوان اللوحة	المقياس	التاريخ	رقم اللوحة
جلسة شتوية – بلكونة 9.00 × 4.00 م (36 م²) **مشروع – جلسة شتوية**	**جدار البيت على البلكونة وشرق**	**1:50**	**2026-10-25**	**A-02 (2/9)**

مصنع وتد الأخشاب
Watad Wood Factory

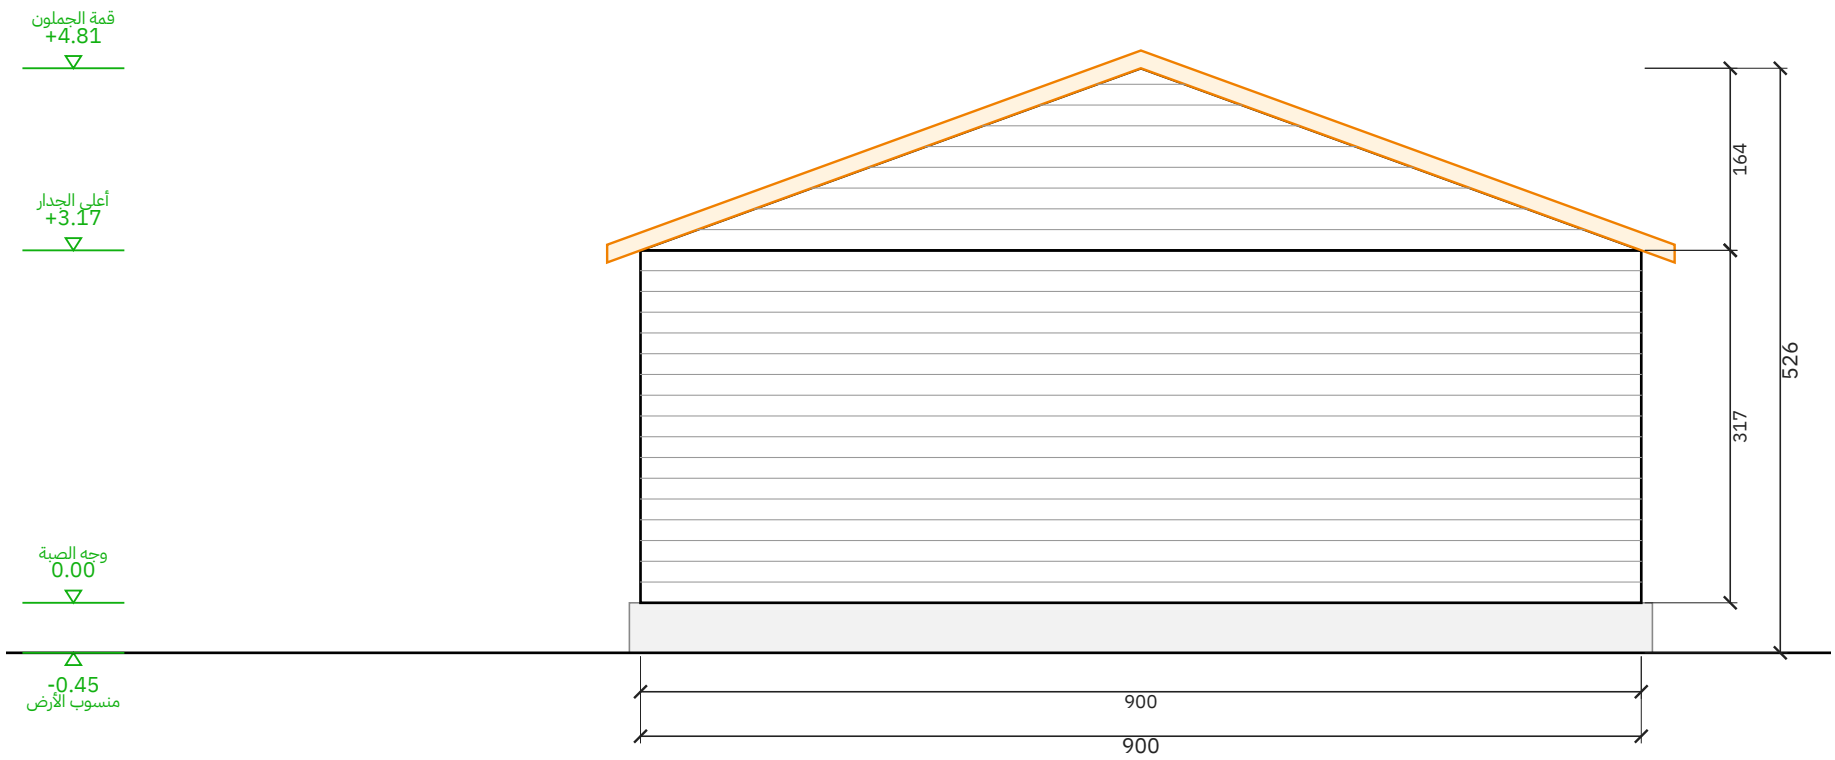

شمال

مقياس 1:50 | الوحدة: سم

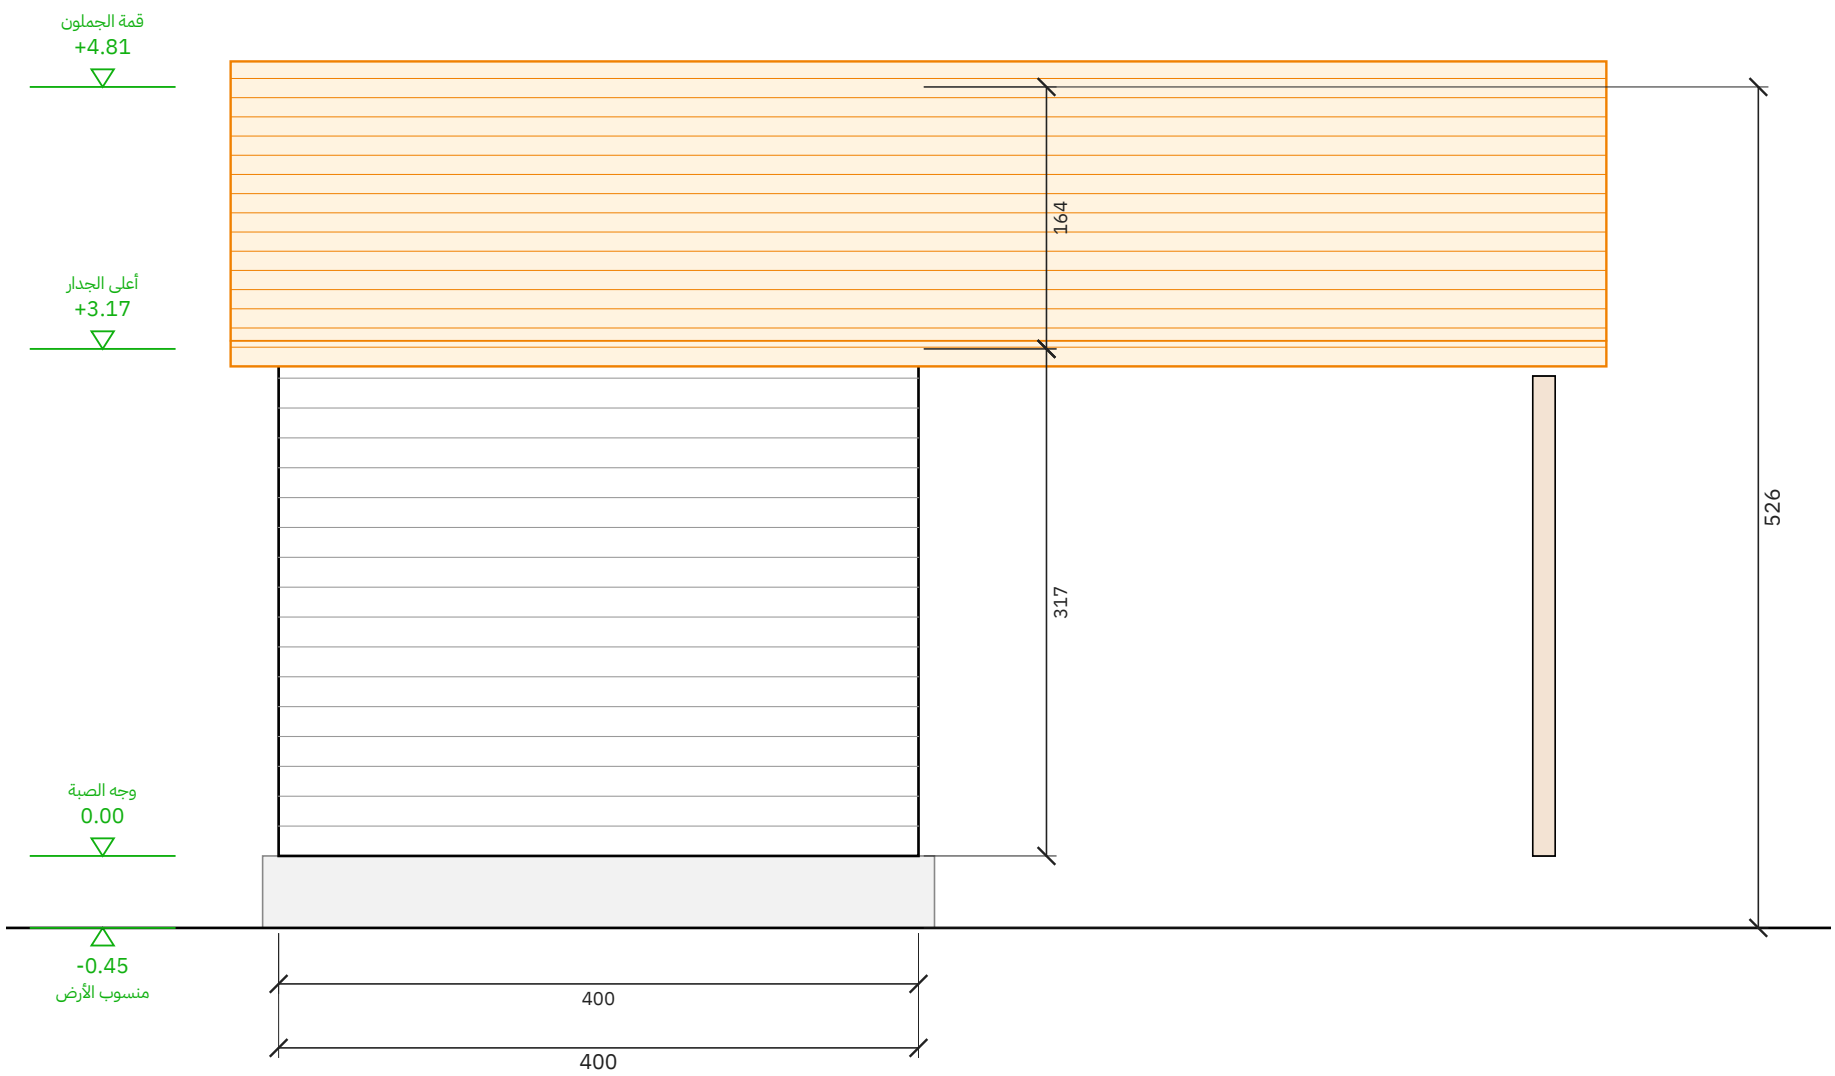

غرب


مقياس 1:50 | الوحدة: سم

المشروع / العميل	عنوان اللوحة	المقياس	التاريخ	رقم اللوحة
جلسة شتوية – بلكونة 9.00 × 4.00 م (36 م²) **مشروع – جلسة شتوية**	**شمال وغرب**	**1:50**	**2026-10-25**	**A-03 (3/9)**

مصنع وتد الأخشاب
Watad Wood Factory


مسقط السقف (جملون)

رفرف 30 سم من كل جهة | مقياس 1:50

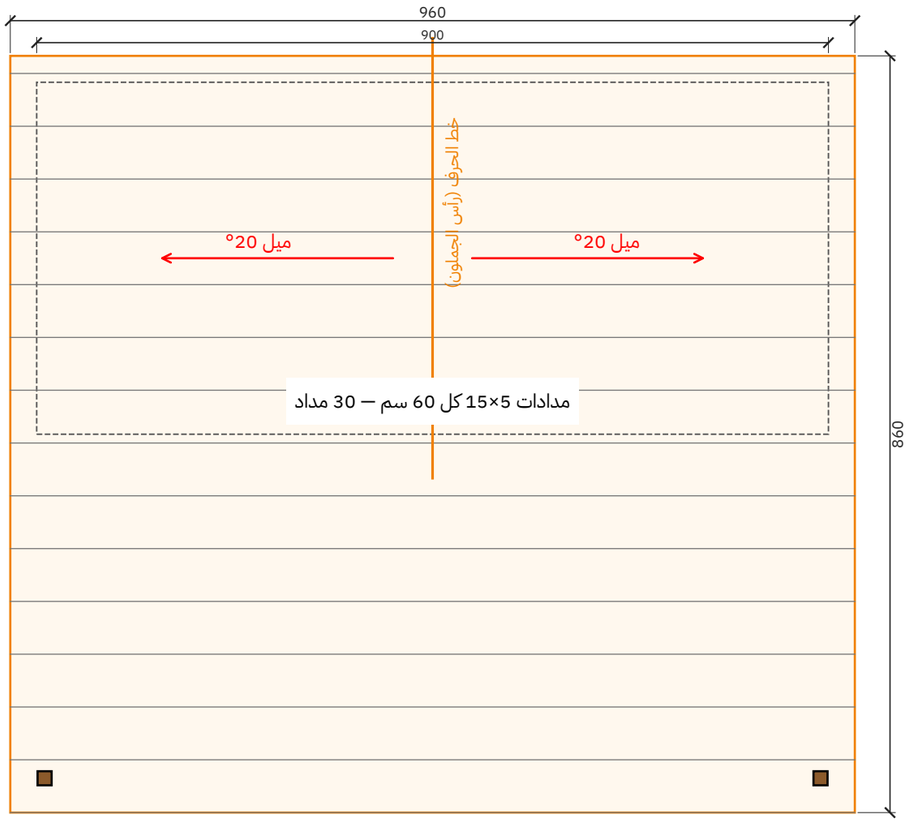


قطاع عرضي أ-أ

مقياس 1:50 | الوحدة: سم

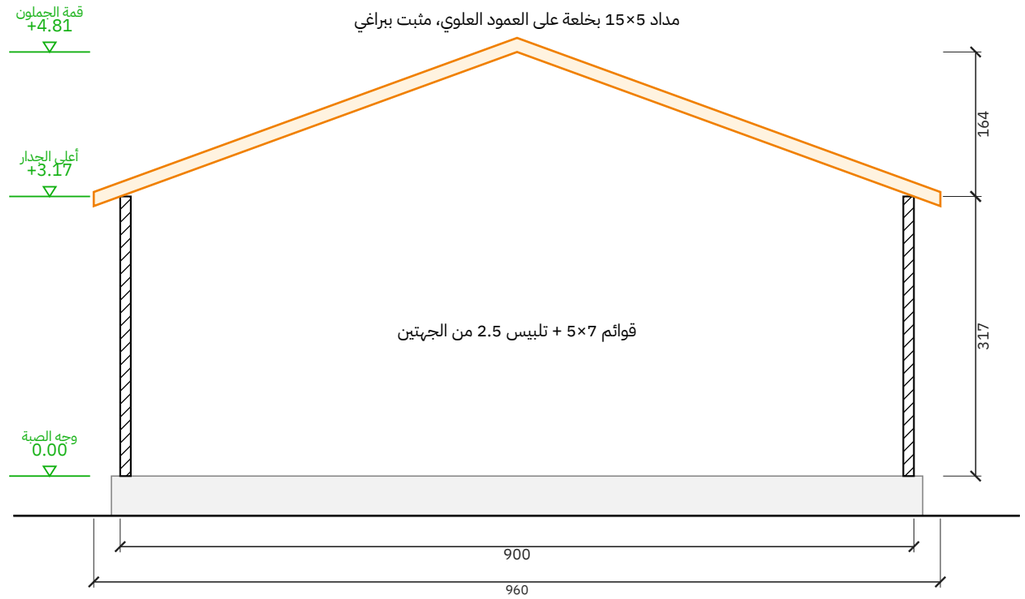

تفصيلة جلوس المداد على العلوي (1:5)

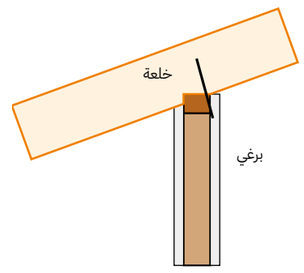

المشروع / العميل: جلسة شتوية – بلكونة 9.00 × 4.00 م (36 م²) — مشروع – جلسة شتوية	عنوان اللوحة: مسقط السقف والقطاع	المقياس: 1:50	التاريخ: 2026-10-25	رقم اللوحة: A-04 (4/9)

مصنع وتد الأخشاب
Watad Wood Factory

جدول مقاسات الأبواب والشبابيك

مقاس الفتحة الصافي في الجدار - الوحدة: سم

الرمز	النوع	العرض (سم)	الارتفاع (سم)	ارتفاع الجلسة (سم)	العدد	الموقع
ب1	باب مزدوج	240	230	-	1	جدار البيت على البلكونة

الإجمالي: أبواب 1 - شبابيك 0

جدول المساحات وبيانات المشروع

بيانات المشروع


البند	البيان
المشروع	جلسة شتوية — بلكونة 9.00 × 4.00 م (36 م²)
العميل	مشروع — جلسة شتوية
الموقع	—
الاستخدام	جلسة خارجية شتوية
التاريخ	2026-10-25
نظام البناء	هيكل خشب 5×7 + تلبيس 2.5 سم من الجهتين
السقف	جملون 20° — قرميد معدني

جدول المساحات


م	الفراغ	الأبعاد (م)	المساحة (م2)
1	داخل البيت	8.76 × 3.76	32.94
	المساحة الصافية الداخلية		**32.94**
	البلكونة (الجلسة الشتوية)	**9.00 × 4.00**	**36.00**
	المساحة الإجمالية المبنية	**9.00 × 4.00**	**36.00**
	المساحة الكلية (المبنية + التراس)		**72.00**

لقطات المنظور الخارجي

المنظور الأمامي

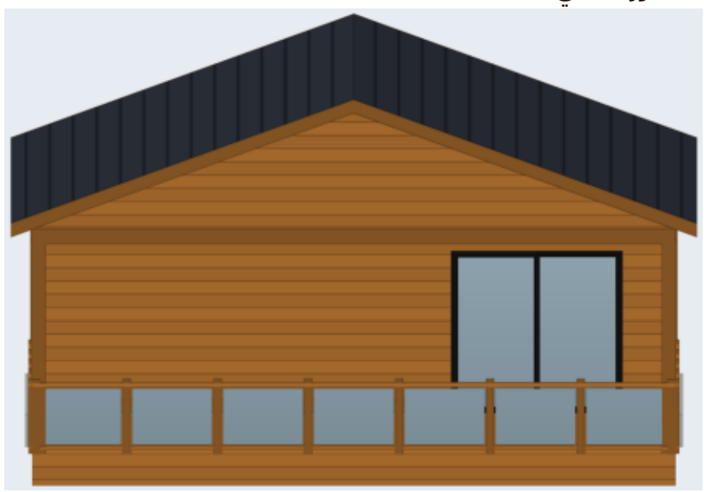


منظور أمامي من اليسار

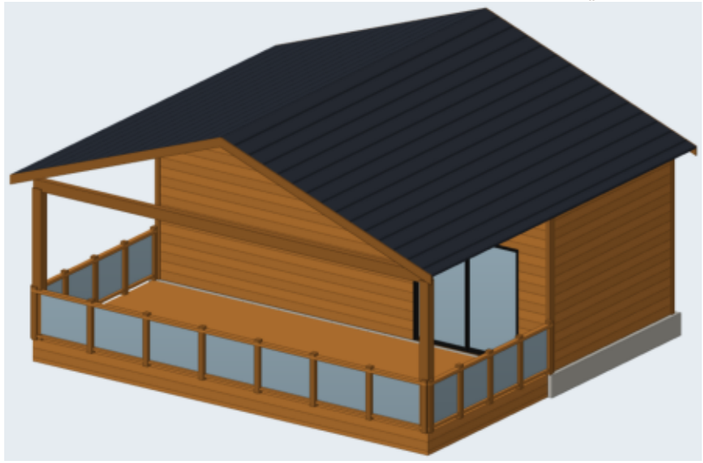


منظور أمامي من اليمين




المنظور الخلفي

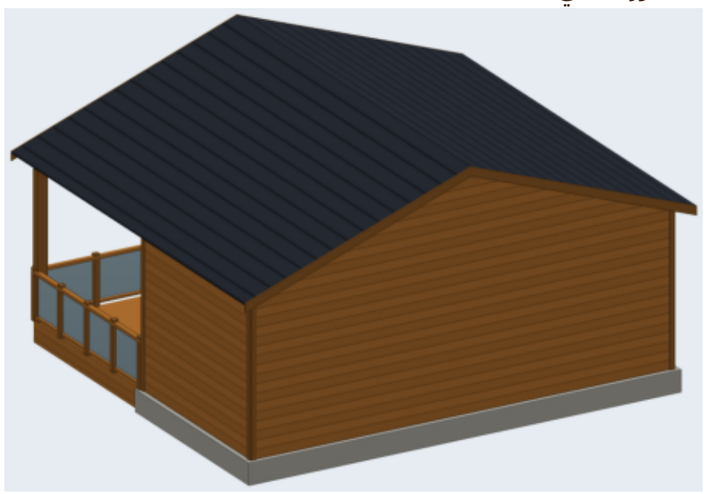

منظور خلفي من اليمين

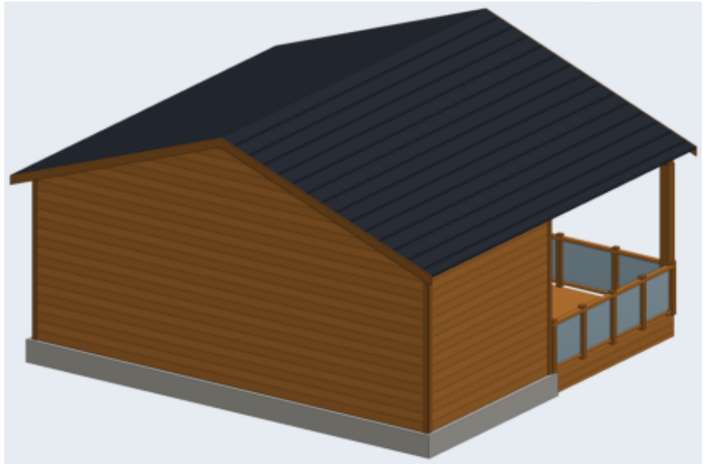


منظر علوي

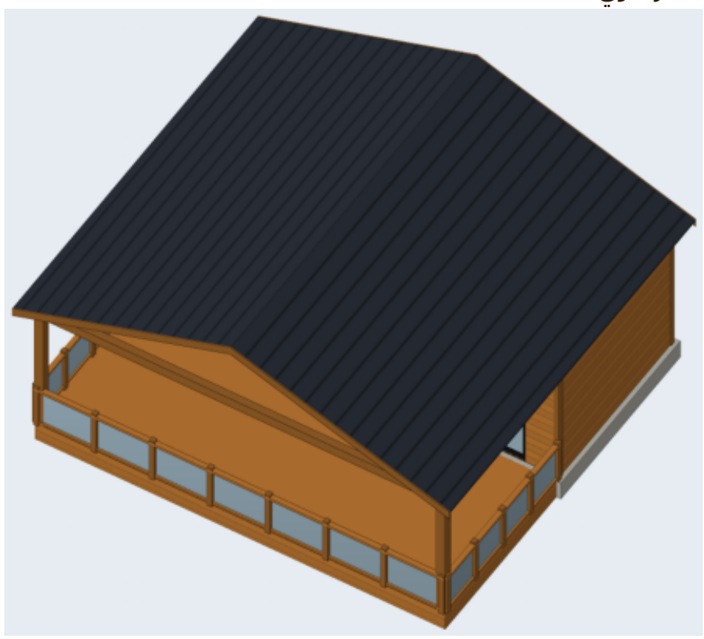

مصنع وتد الأخشاب Watad Wood Factory	المشروع / العميل جلسة شتوية – بلكونة 9.00 × 4.00 م (36 م²) مشروع – جلسة شتوية	عنوان اللوحة لقطات المنظور	المقياس –	التاريخ 2026-10-25	رقم اللوحة A-07 (7/9)

المقطع العلوي بالفرش


مقطع أفقي على ارتفاع 1.90 م — توزيع الفرش ومسار الحركة

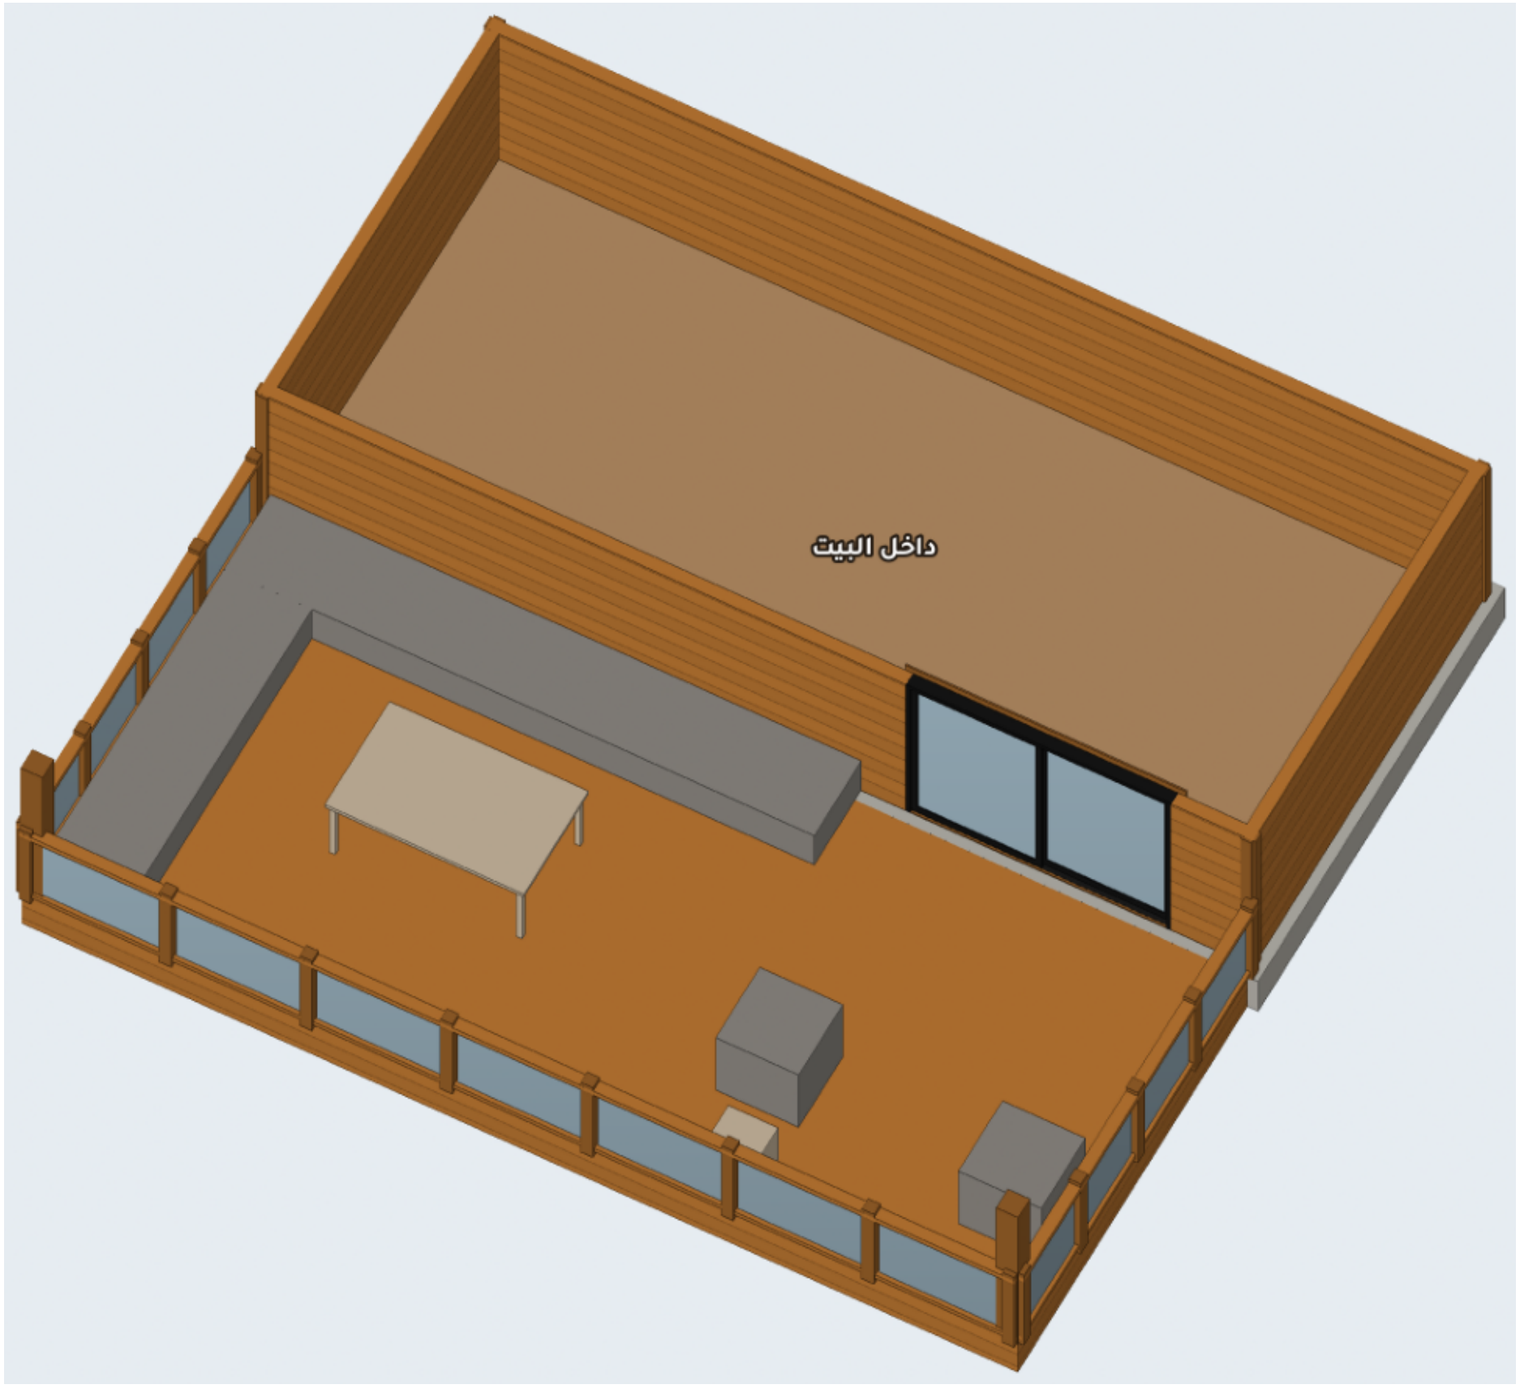

المشروع / العميل	عنوان اللوحة	المقياس	التاريخ	رقم اللوحة
مصنع وتد الأخشاب Watad Wood Factory جلسة شتوية – بلكونة 9.00 × 4.00 م (36 م²) مشروع – جلسة شتوية	المقطع العلوي بالفرش	–	2026-10-25	A-08 (8/9)

المنظور ثلاثي الأبعاد والمواد

النمط: برتقالي محمر + قرميد فحمي + دربزين X — رندر واقعي بخامات حقيقية

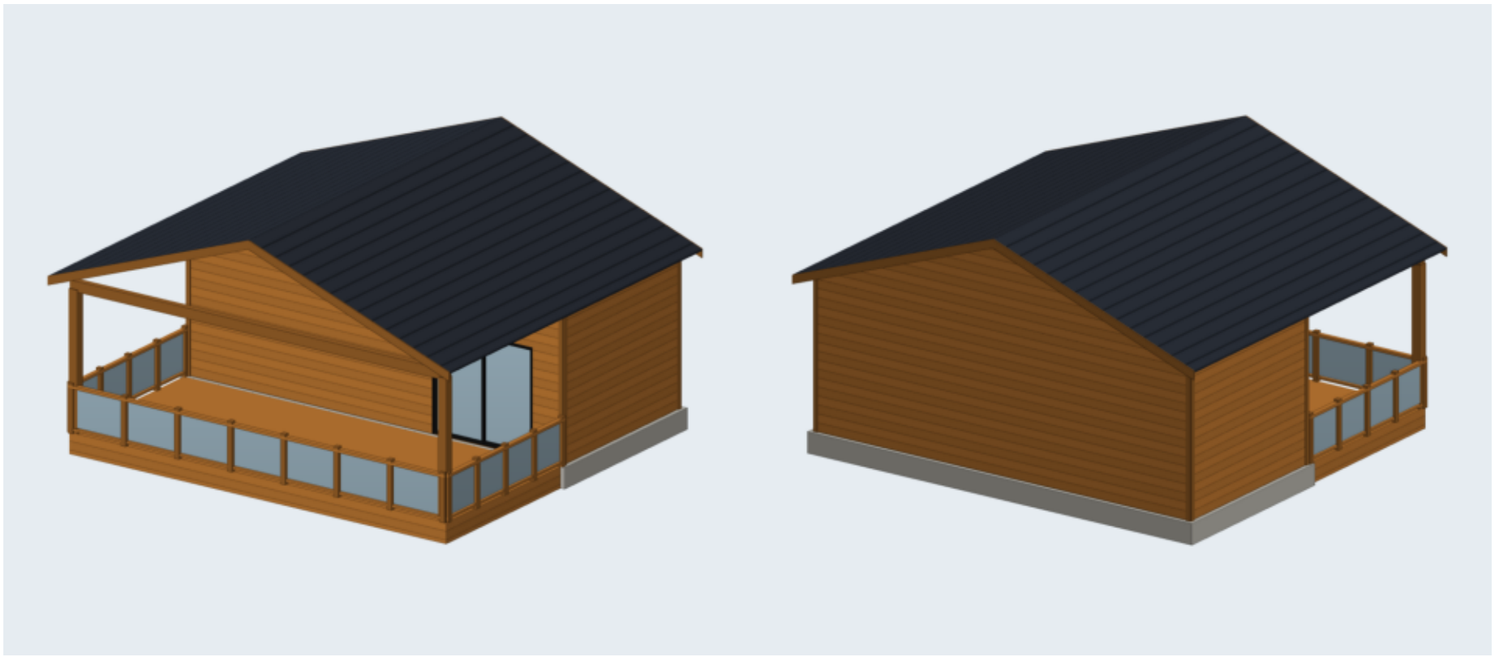

جدول المواد والألوان

الخشب / الصبغة

صبغة عسلي / سيدر

القرميد

قرميد فحمي / أسود مزرق

الزجاج

زجاج شفاف

إطارات الشبابيك والأبواب

إطار ألمنيوم أسود

الكنار والزوايا

نفس الصبغة أغمق درجة


الصبة

خرسانة 45 سم


الدربزين: ألواح أفقية متقاربة (عصري)

تقسيم الشبابيك: بدون | الباب الرئيسي: سحاب زجاج

أنواع الدربزين المعتمدة (من مشاريع المصنع)

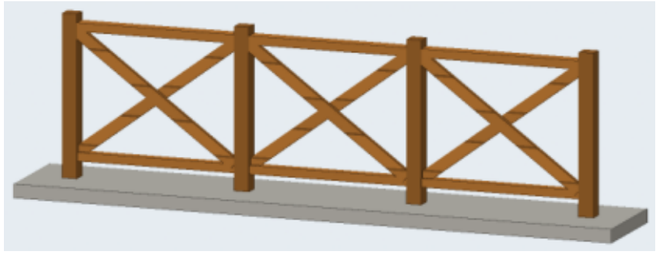

تقاطع X (صورة 5)

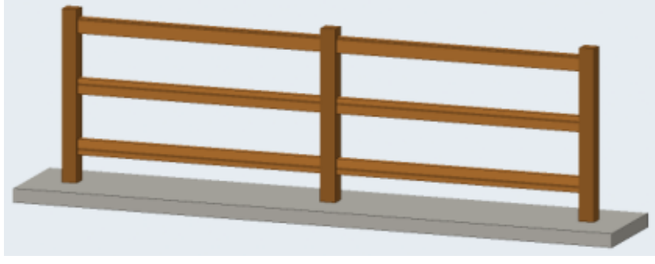

3 مرابيع أفقية (صورة 2)



قوائم رأسية متقاربة (صورة 1)

المشروع / العميل	عنوان اللوحة	المقياس	التاريخ	رقم اللوحة
مصنع وتد الأخشاب Watad Wood Factory **جلسة شتوية – بلكونة 9.00 × 4.00 م (36 م²)** **مشروع – جلسة شتوية**	**المنظور والمواد**	–	**2026-10-25**	**A-09 (9/9)**