المنظور ثلاثي الأبعاد والمواد

النمط: جوزي غامق + إطارات سوداء — رندر واقعي بخامات حقيقية



جدول المواد والألوان

الخشب / الصبغة

صبغة عسلي / سيدر

القرميد

قرميد رمادي غامق

الزجاج

زجاج شفاف

إطارات الشبابيك والأبواب

إطار ألمنيوم أسود

الكنار والزوايا

نفس الصبغة أغمق درجة


الصبة

خرسانة 45 سم


الدربزين: ألواح أفقية متقاربة (عصري)

تقسيم الشبابيك: بدون | الباب الرئيسي: سحاب زجاج

أنواع الدربزين المعتمدة (من مشاريع المصنع)

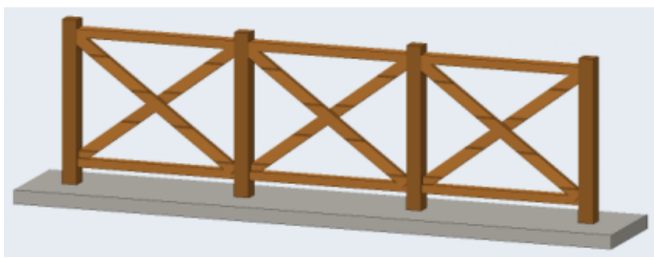

تقاطع X (صورة 5)

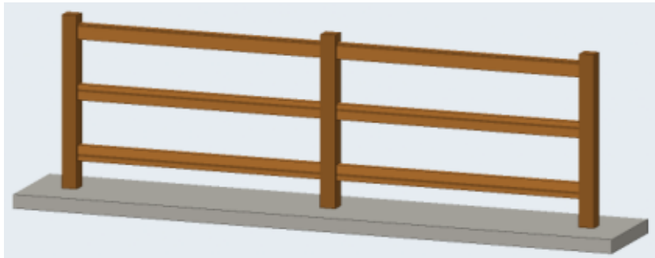

3 مرابيع أفقية (صورة 2)




قوائم رأسية متقاربة (صورة 1)

مصنع وتد الأخشاب Watad Wood Factory	المشروع / العميل **كوخ مزرعة حايل الاستثماري — دورين — صالة + غرفة نوم + تراس — 6.00 × 7.00 م (× 3 أكواخ)** **عميل — حايل (مزرعة استثمارية)**	عنوان اللوحة **المنظور والمواد**	المقياس **1:50**	التاريخ **2026-10-23**	رقم اللوحة **W-01 (1/16)**

المسقط الأفقي مع الفرش — الدور الأرضي


الأبعاد بالسنتيمتر - الجدران: قوائم 7×5 + تلبيس 2.5 من الجهتين (12 سم) | منسوب الأرضية +0.00

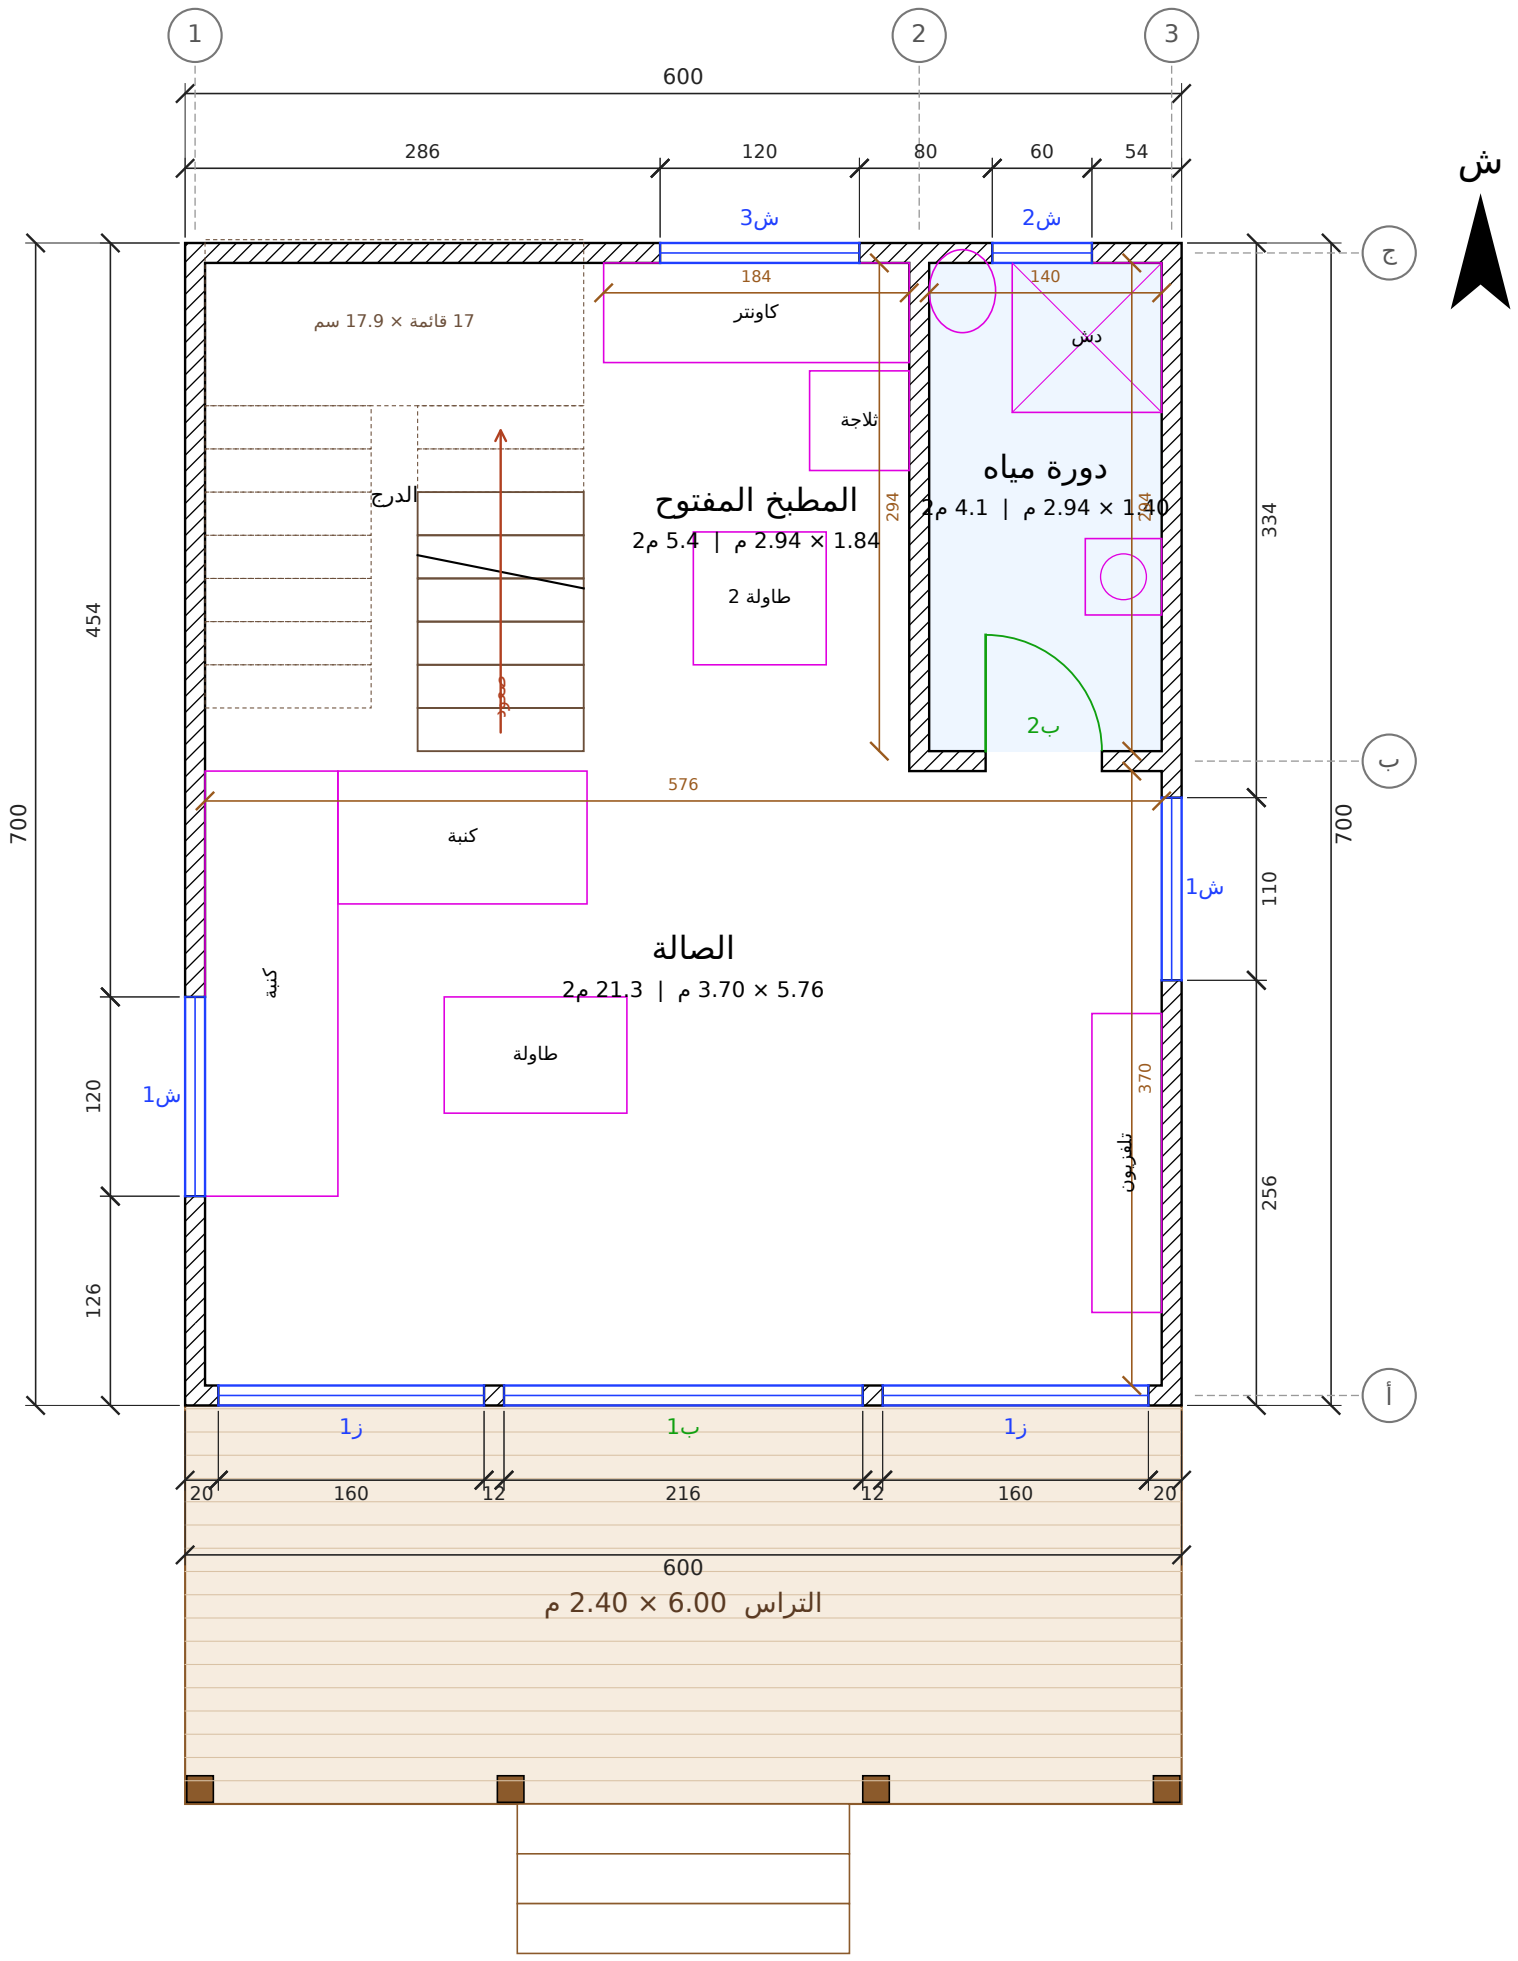


مصنع وتد الأخشاب Watad Wood Factory	المشروع / العميل كوخ مزرعة حايل الاستثماري — دورين — صالة + غرفة نوم + تراس — 6.00 × 7.00 م (× 3 أكواخ) عميل — حايل (مزرعة استثمارية)	عنوان اللوحة المسقط الأفقي — الدور الأرضي	المقياس 1:50	التاريخ 2026-10-23	رقم اللوحة W-02 (2/16)

المسقط الأفقي مع الفرش — الدور الأول

الأبعاد بالسنتيمتر - الجدران: قوائم 7×5 + تلبيس 2.5 من الجهتين (12 سم) | منسوب الأرضية +3.05

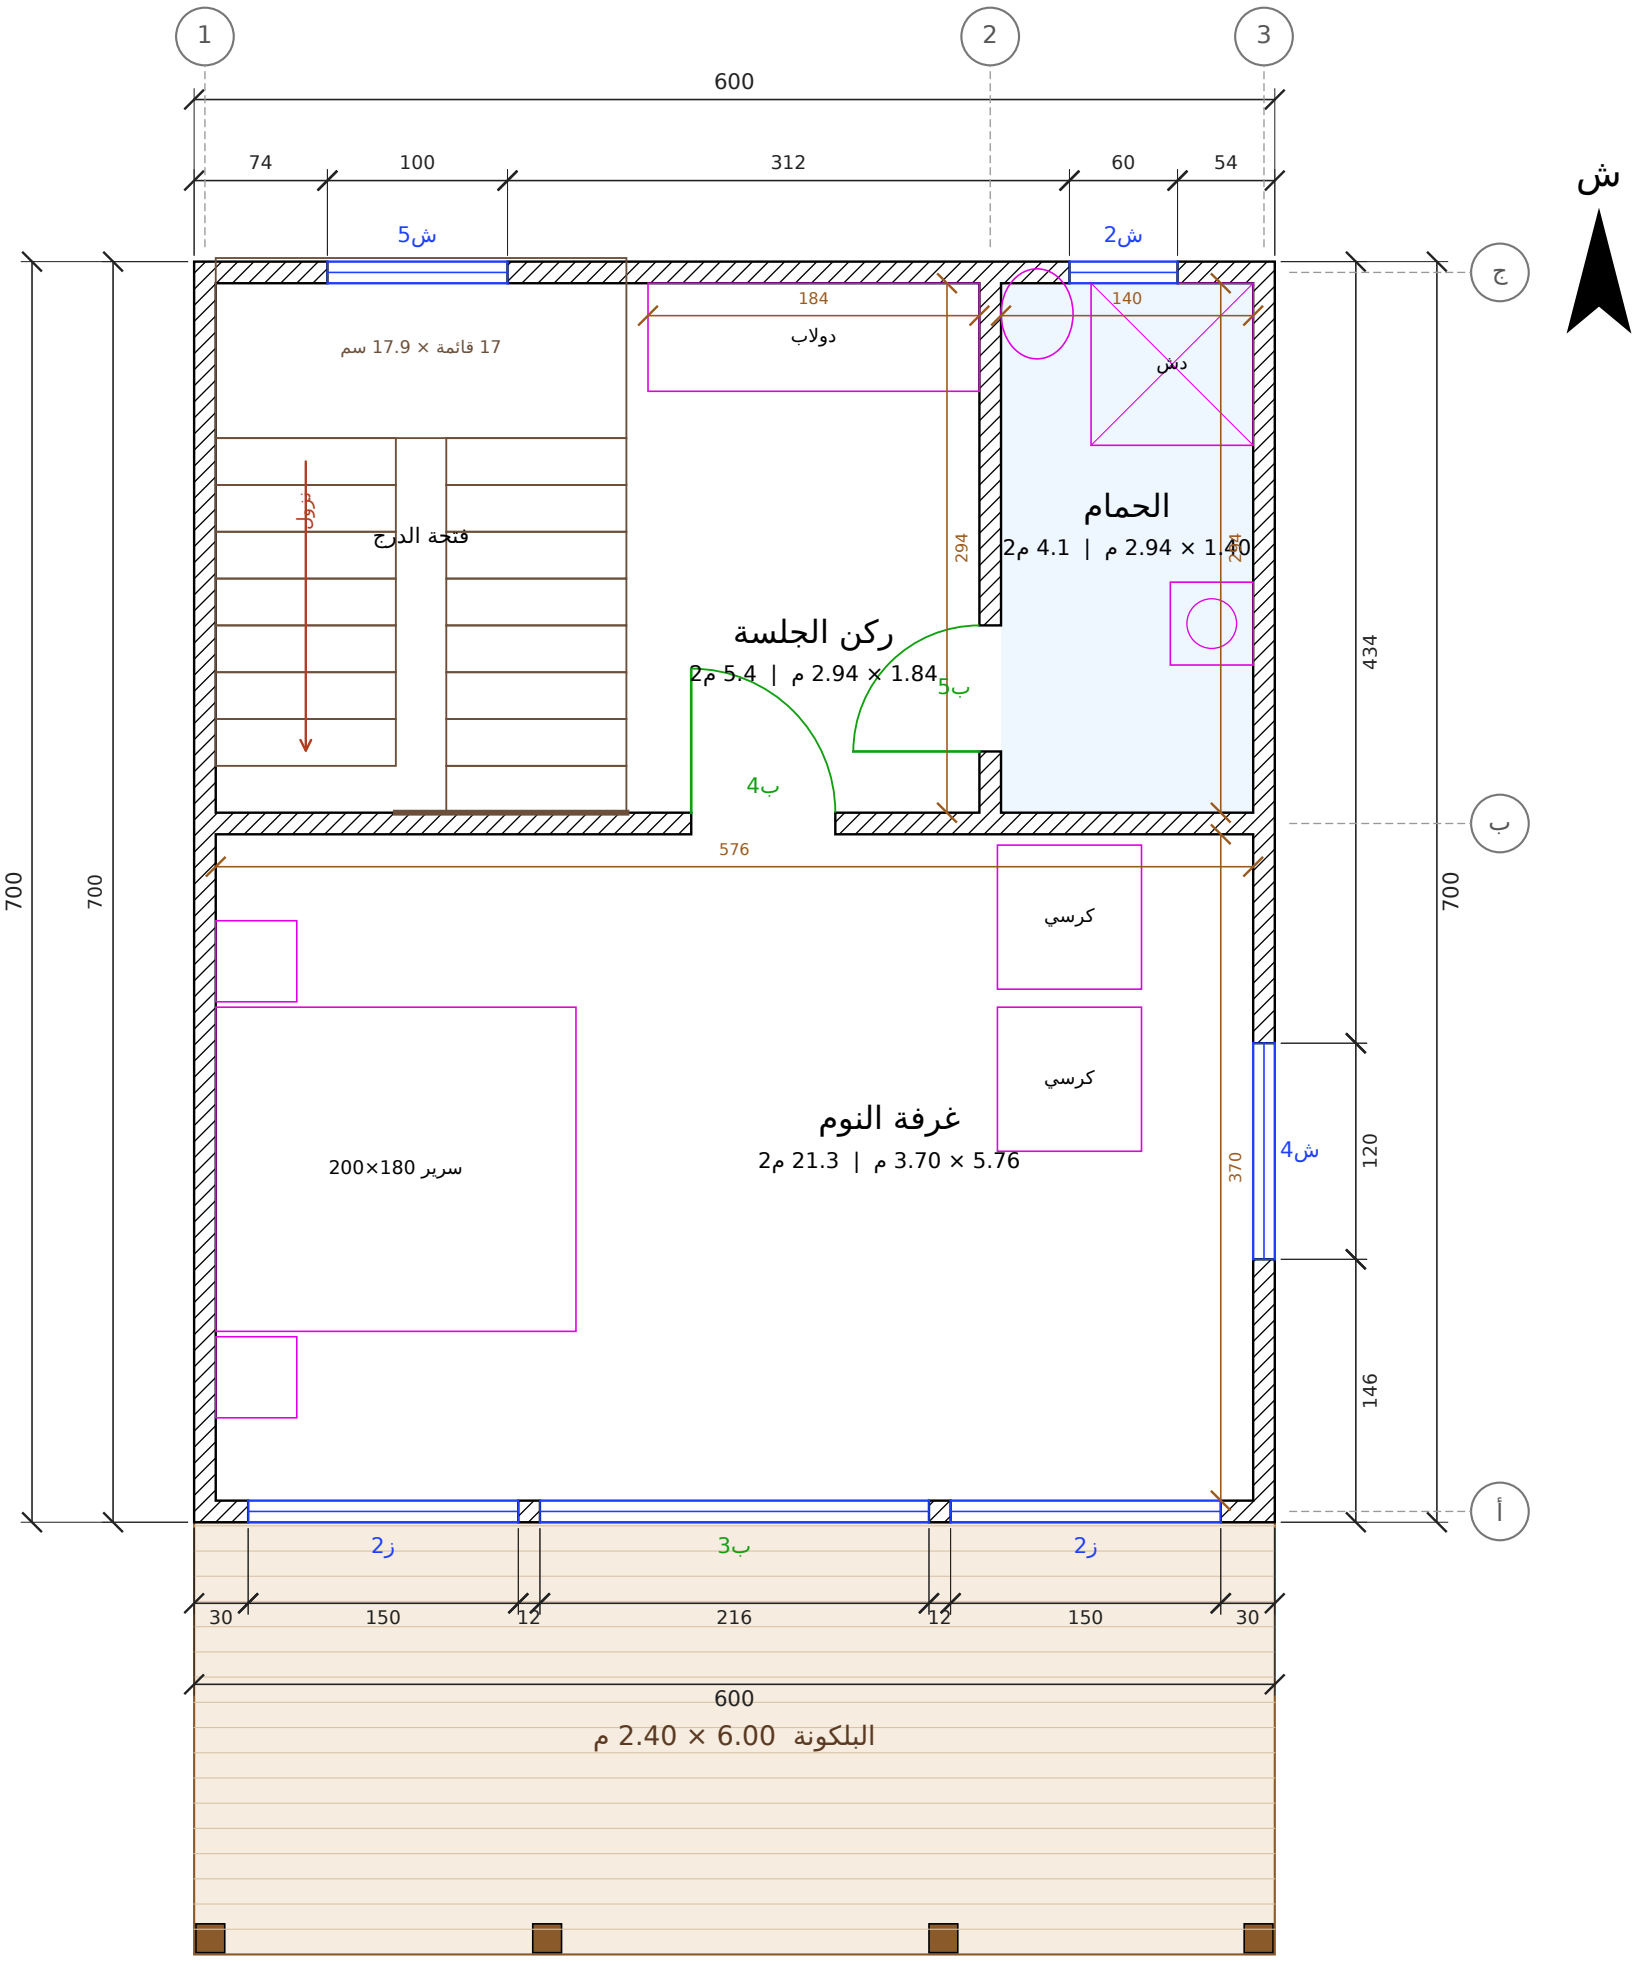


المشروع / العميل	عنوان اللوحة	المقياس	التاريخ	رقم اللوحة
مصنع وتد الأخشاب — كوخ مزرعة حايل الاستثماري — دورين — صالة + غرفة نوم + تراس — 6.00 × 7.00 م (3×2 أكواخ) عميل — حايل (مزرعة استثمارية) Watad Wood Factory	**المسقط الأفقي — الدور الأول**	**1:50**	**2026-10-23**	**W-03 (3/16)**

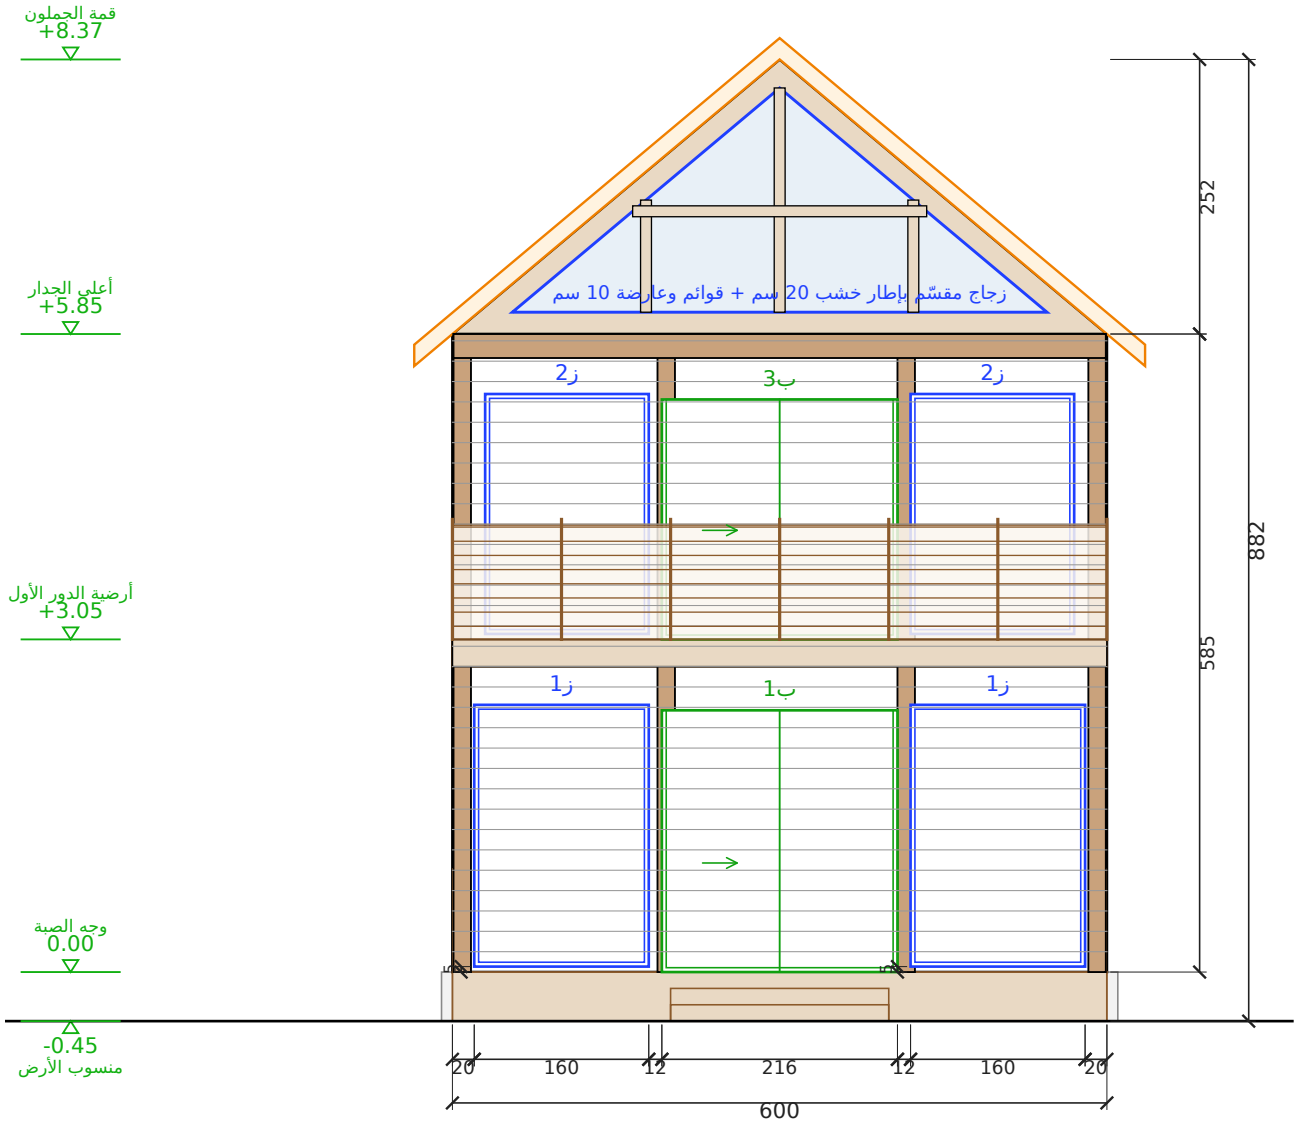

الواجهة الأمامية (زجاج على التراس)

مقياس 1:50 | الوحدة: سم

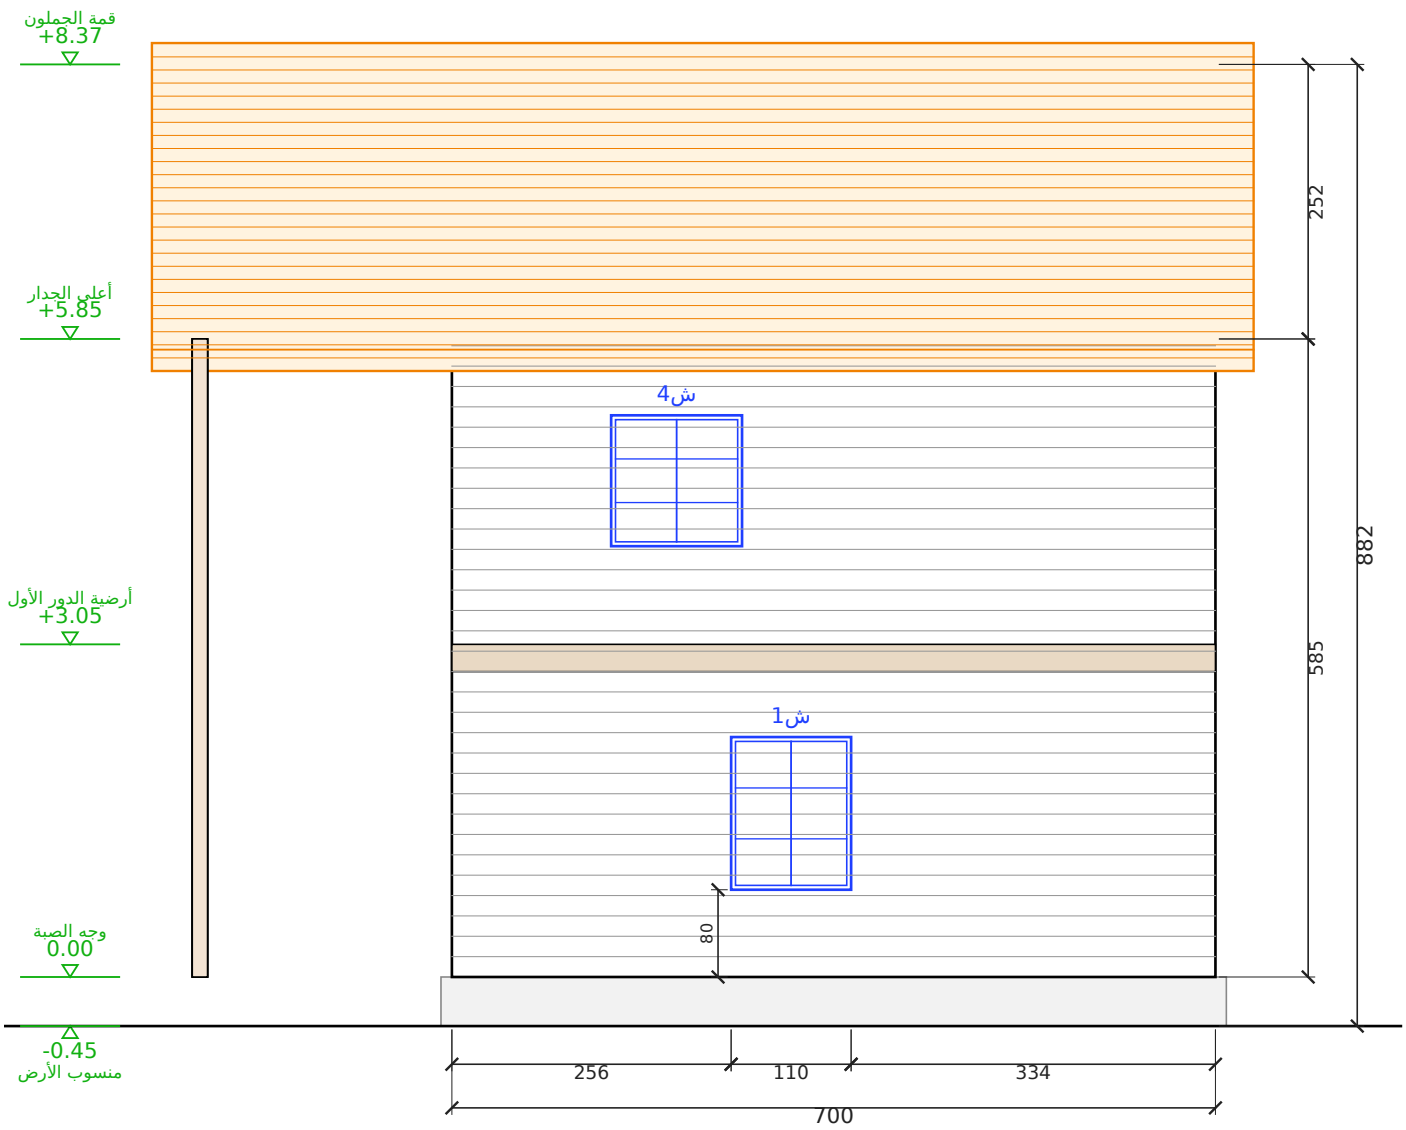


الواجهة الشرقية

مقياس 1:50 | الوحدة: سم


المشروع / العميل	عنوان اللوحة	المقياس	التاريخ	رقم اللوحة
مصنع وتد الأخشاب — كوخ مزرعة حايل الاستثماري — دورين — صالة + غرفة نوم + تراس — 6.00 × 7.00 م (× 3 أكواخ) عميل — حايل (مزرعة استثمارية)	**الواجهة الأمامية (زجاج على التراس) والواجهة الشرقية**	1:50	**2026-10-23**	**W-04 (4/16)**

Watad Wood Factory

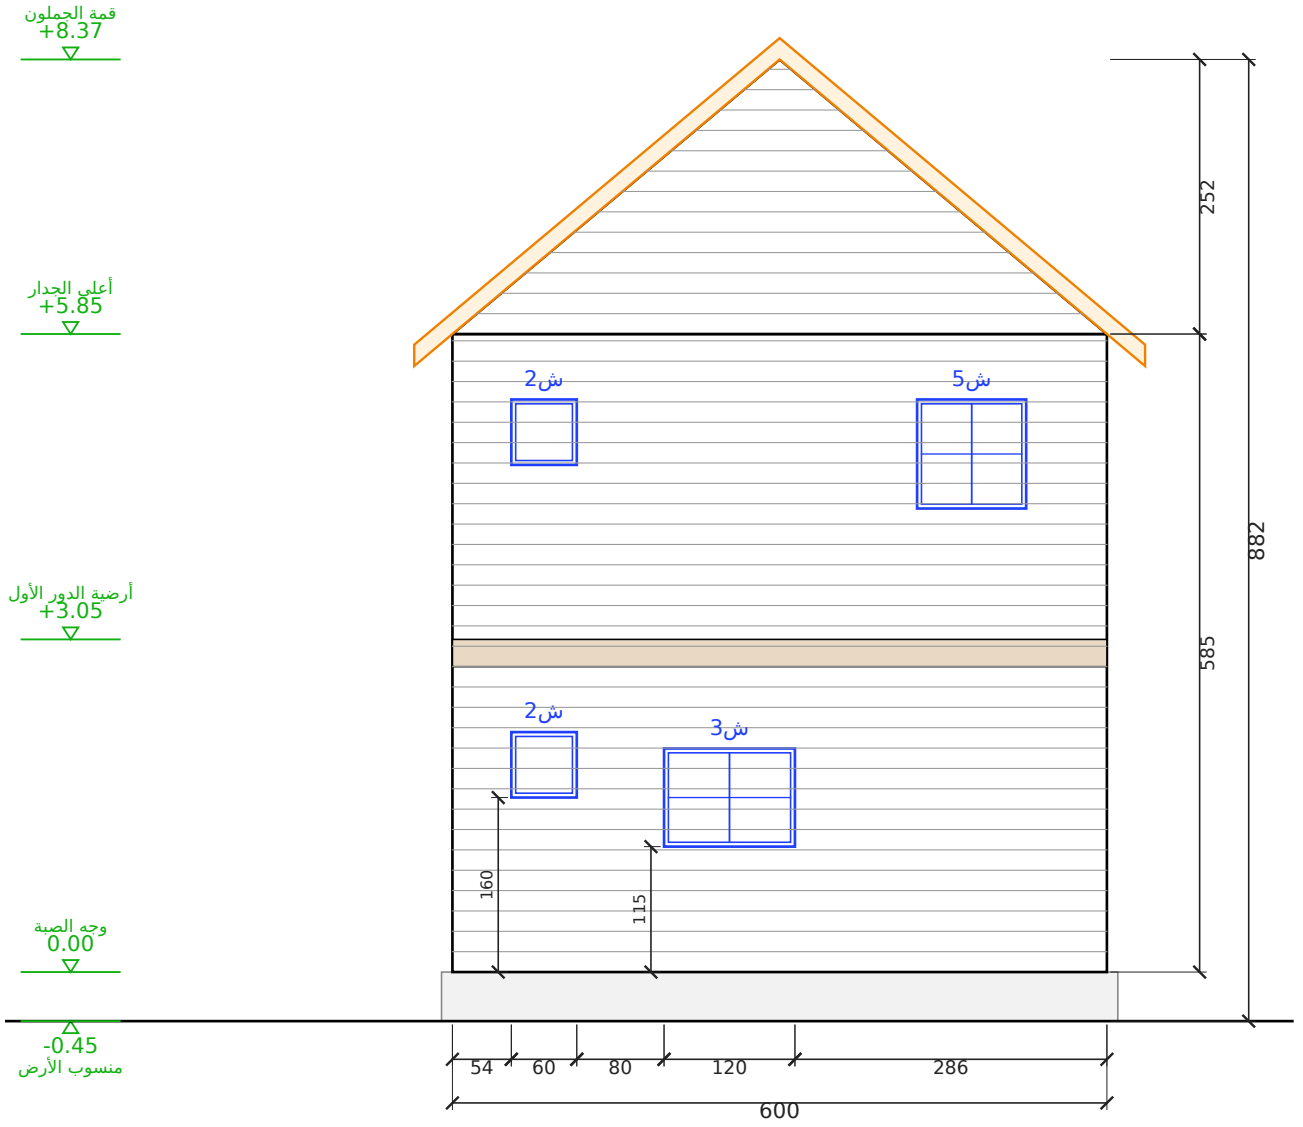

الواجهة الخلفية

مقياس 1:50 | الوحدة: سم

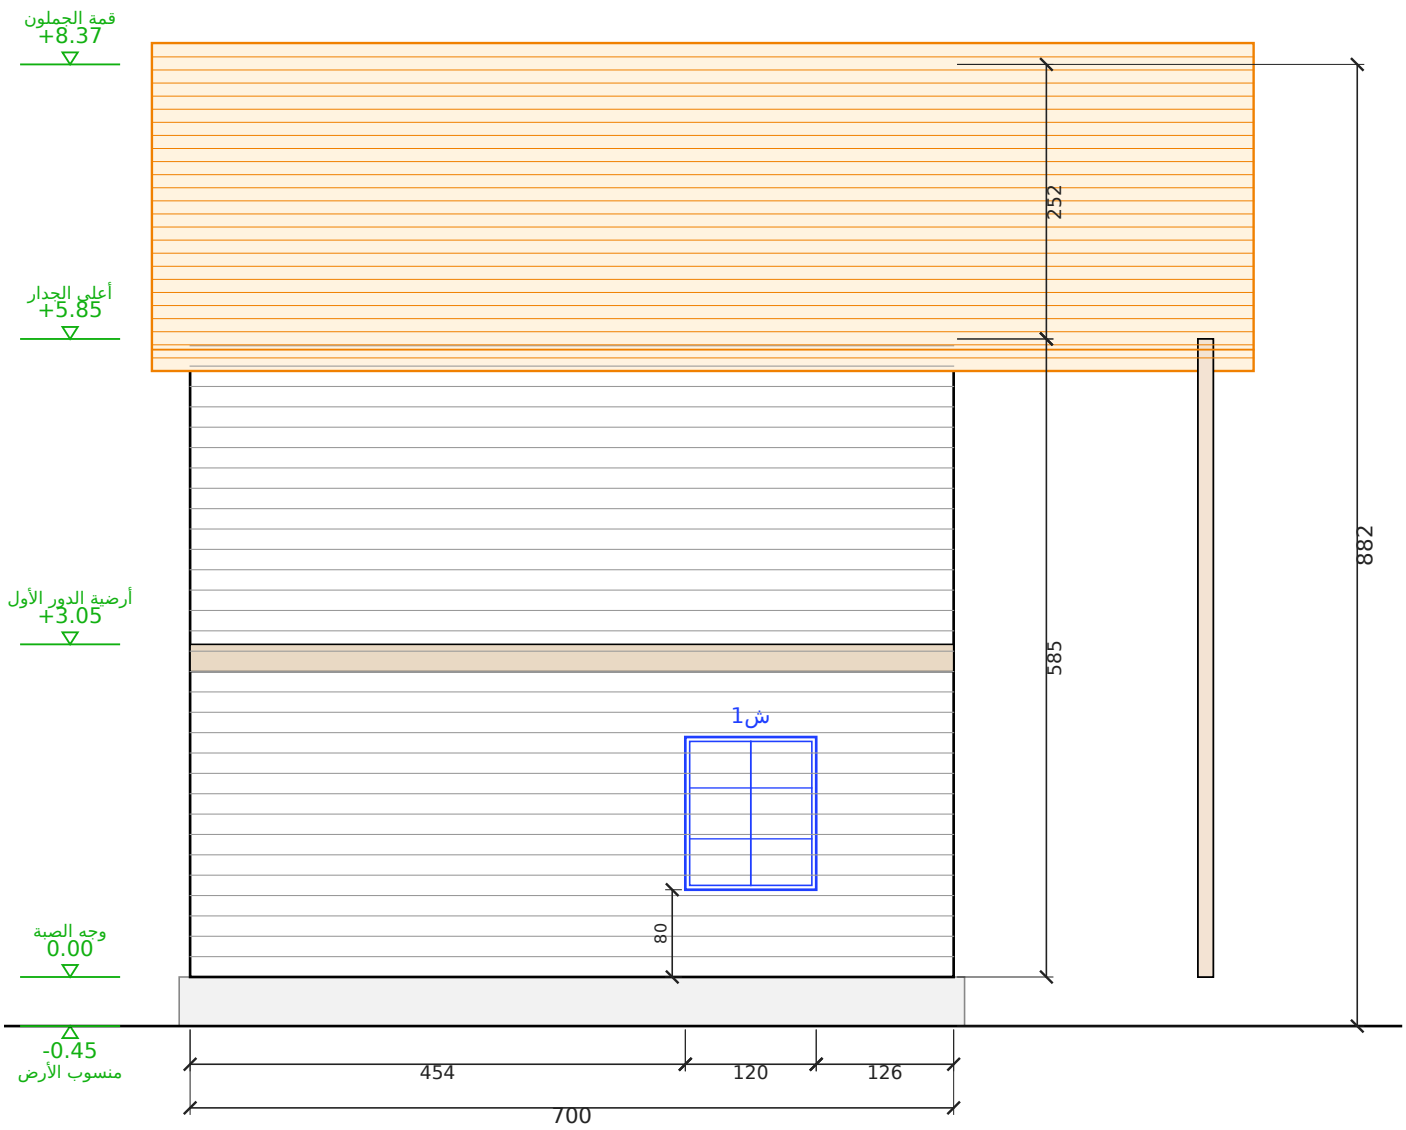


الواجهة الغربية

مقياس 1:50 | الوحدة: سم


المشروع / العميل	عنوان اللوحة	المقياس	التاريخ	رقم اللوحة
كوخ مزرعة حايل الاستثماري — دورين — صالة + غرفة نوم + تراس — 6.00 × 7.00 م (× 3 أكواخ) **عميل — حايل (مزرعة استثمارية)**	**الواجهة الخلفية والواجهة الغربية**	**1:50**	**2026-10-23**	**W-05 (5/16)**

مصنع وتد الأخشاب
Watad Wood Factory


مسقط السقف (جملون)
رفرف 35 سم من كل جهة | مقياس 1:50

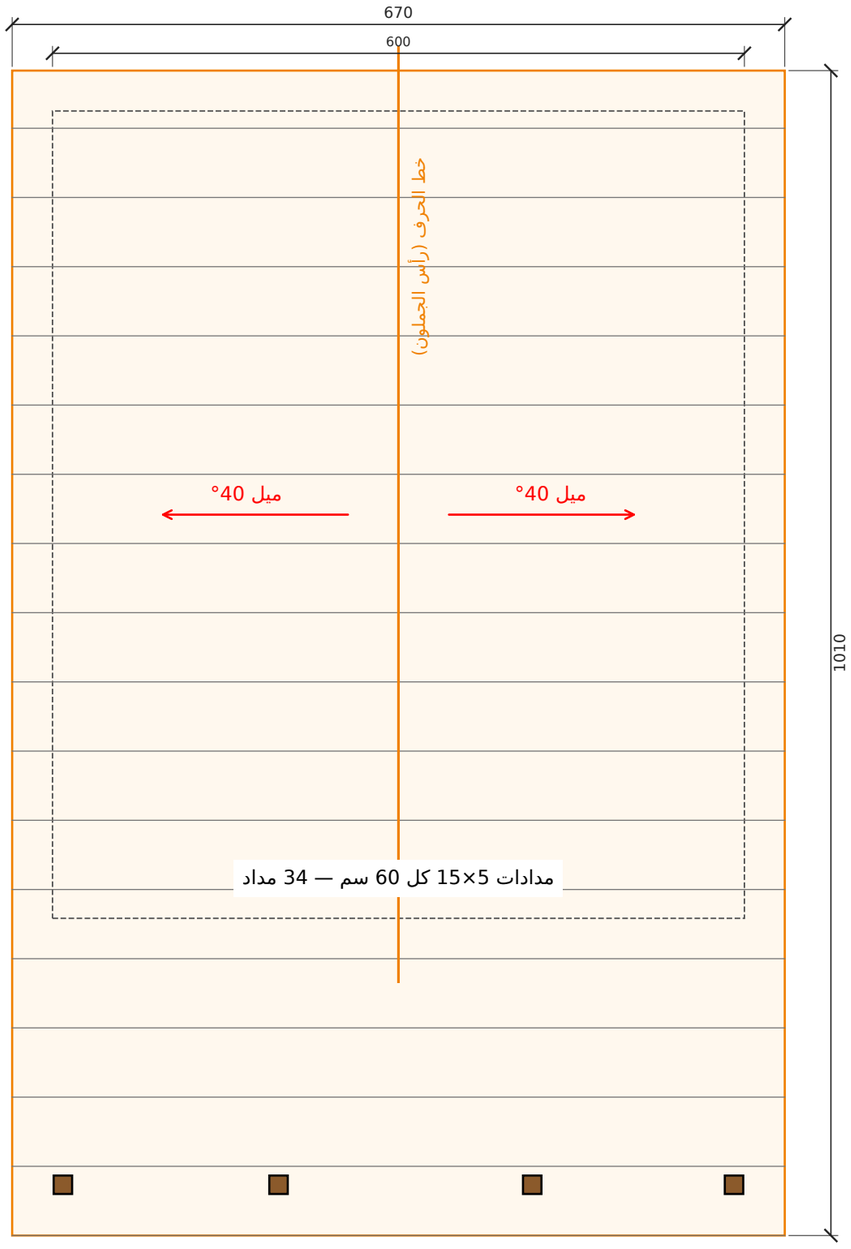

قطاع عرضي أ-أ
مقياس 1:50 | الوحدة: سم

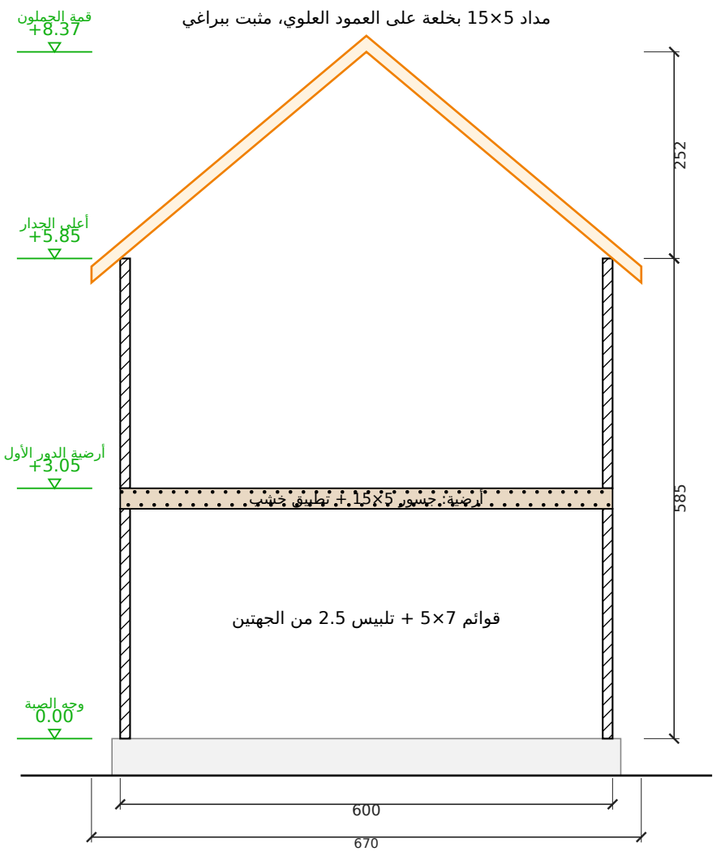

تفصيلة جلوس المداد على العلوي (1:5)

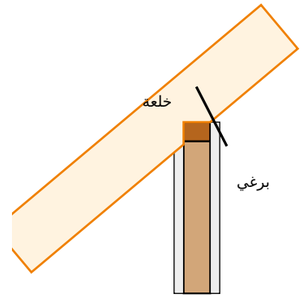

علوي 7×5 على قائم 7×5

المشروع / العميل	عنوان اللوحة	المقياس	التاريخ	رقم اللوحة
كوخ مزرعة حايل الاستثماري — دورين — صالة + غرفة نوم + تراس — 6.00 × 7.00 م (× 3 أكواخ) **عميل — حايل (مزرعة استثمارية)**	**مسقط السقف والقطاع**	**—**	**2026-10-23**	**W-06 (6/16)**

مصنع وتد الأخشاب
Watad Wood Factory

جدول مقاسات الأبواب والشبابيك
مقاس الفتحة الصافي في الجدار - الوحدة: سم

الرمز	النوع	العرض (سم)	الارتفاع (سم)	ارتفاع الجلسة (سم)	العدد	الموقع
ب1	باب مزدوج	216	240	-	1	الأمامية (زجاج على التراس)
ب2	باب	70	210	-	1	دورة المياه
ب3	باب مزدوج	216	220	-	1	الأمامية (على البلكونة)
ب4	باب	80	210	-	1	غرفة النوم
ب5	باب	70	210	-	1	الحمام
ز1	شباك	160	240	5	2	الأمامية (زجاج على التراس) 2
ز2	شباك	150	220	5	2	الأمامية (على البلكونة) 2
ش1	شباك	110	140	80	1	الشرقية
ش1	شباك	120	140	80	1	الغربية
ش2	شباك	60	60	160	2	الخلفية 2
ش3	شباك	120	90	115	1	الخلفية
ش4	شباك	120	120	90	1	الشرقية
ش5	شباك	100	100	120	1	الخلفية

الإجمالي: أبواب 5 - شبابيك 11

جدول المساحات وبيانات المشروع والتسعير

بيانات المشروع

البند	البيان
المشروع	كوخ مزرعة حايل الاستثماري — دورين — صالة + غرفة نوم + تراس — 6.00 × 7.00 م (× 3 أكواخ)
العميل	عميل — حايل (مزرعة استثمارية)
الموقع	حايل — مزرعة
الاستخدام	3 أكواخ استثمارية (تأجير) — نفس التصميم
التاريخ	2026-10-23
نظام البناء	هيكل خشب 5×7 + تلبيس 2.5 سم من الجهتين
السقف	جملون 40° — قرميد معدني

جدول المساحات

م	الفراغ	الأبعاد (م)	المساحة (م2)
1	أرضي — الصالة	5.76 × 3.70	21.31
2	أرضي — المطبخ المفتوح	1.84 × 2.94	5.41
3	أرضي — الدرج	2.28 × 2.94	6.70
4	أرضي — دورة مياه	1.40 × 2.94	4.12
5	أول — غرفة النوم	5.76 × 3.70	21.31
6	أول — ركن الجلسة	1.84 × 2.94	5.41
7	أول — الحمام	1.40 × 2.94	4.12
	المساحة الصافية الداخلية		68.38
	التراس	**6.00 × 2.40**	**14.40**
	البلكونة	**6.00 × 2.40**	**14.40**
	المساحة الإجمالية المبنية	**6.00 × 7.00 × 2 دور**	**84.00**
	المساحة الكلية (المبنية + التراس والبلكونة)		**112.80**


التسعير المفصّل

البند	المبلغ (ريال)
الكوخ المبني 84.00 م² × 1,096	92,064
تراس الأرضي + بلكونة الأول (6.00 × 2.40 × 2) — 28.80 م² × 1,096	31,565
الإجمالي (ريال)	**123,629**


ملاحظات:

- السعر لكوخ واحد (الدورين والتراس والبلكونة) — الأكواخ الثلاثة نفس التصميم والسعر.
- الصبة والتمديدات الخارجية على العميل ما لم يُذكر غير ذلك.

تأطير جدار أ-جنوب — الطول 588 سم، الارتفاع 280 سم

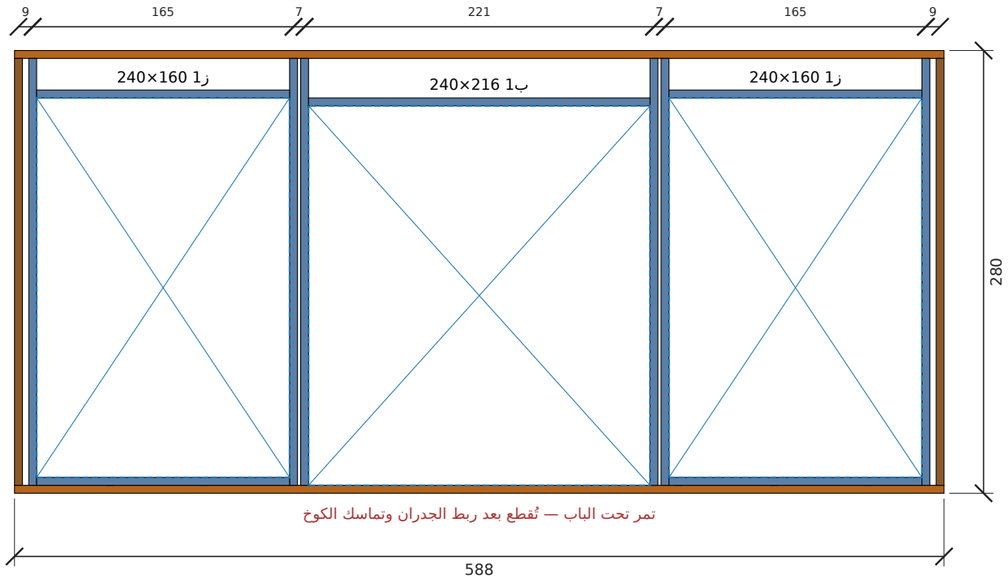


تأطير جدار أ-شرق — الطول 688 سم، الارتفاع 280 سم

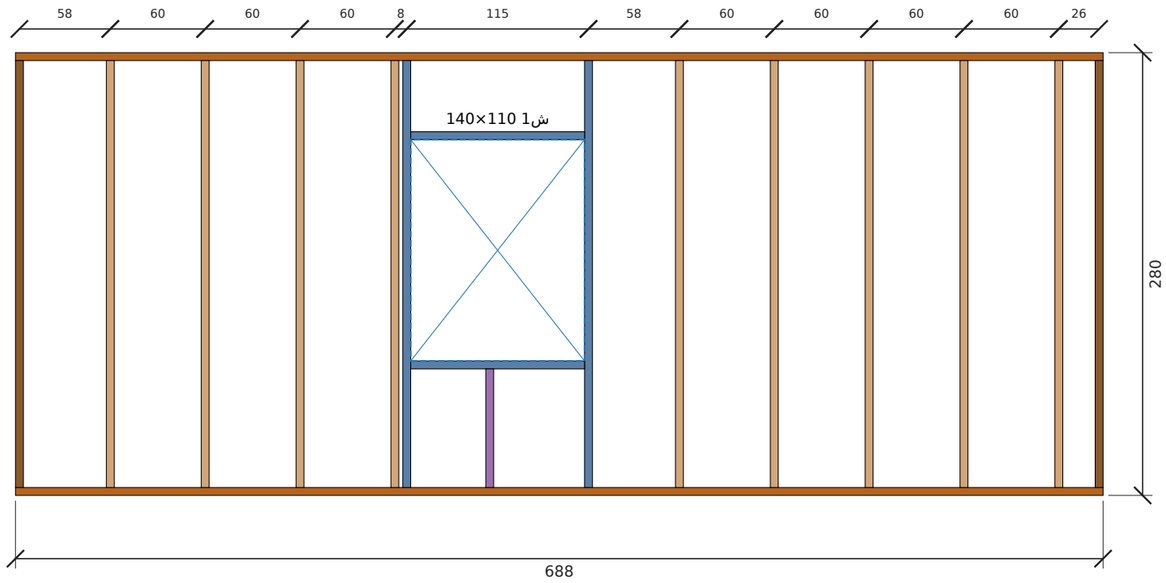


عمود قصير | جلسة شباك | رأس فتحة | جنب فتحة | عمود زاوية | عمود | علوي | قاعدة سفلية

مصنع وتد الأخشاب Watad Wood Factory	المشروع / العميل **كوخ مزرعة حايل الاستثماري — دورين — صالة + غرفة نوم + تراس — 6.00 × 7.00 م** **عميل — حايل (مزرعة استثمارية)**	عنوان اللوحة **لوحات التأطير (للورشة) (× 3 أكواخ)**	المقياس **—**	التاريخ **2026-10-23**	رقم اللوحة **W-09 (9/16)**

تأطير جدار أ-شمال — الطول 588 سم، الارتفاع 280 سم

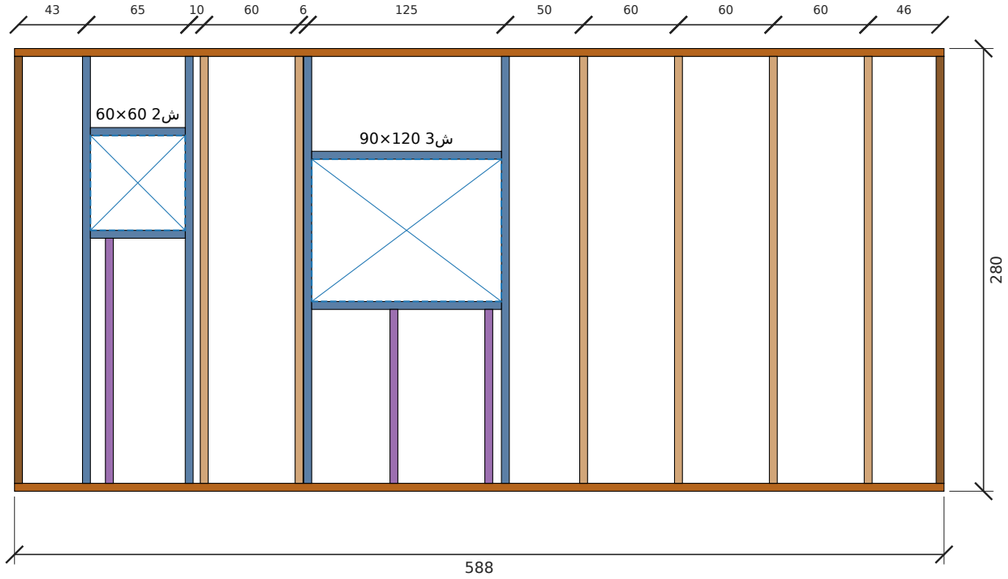


تأطير جدار أ-غرب — الطول 688 سم، الارتفاع 280 سم

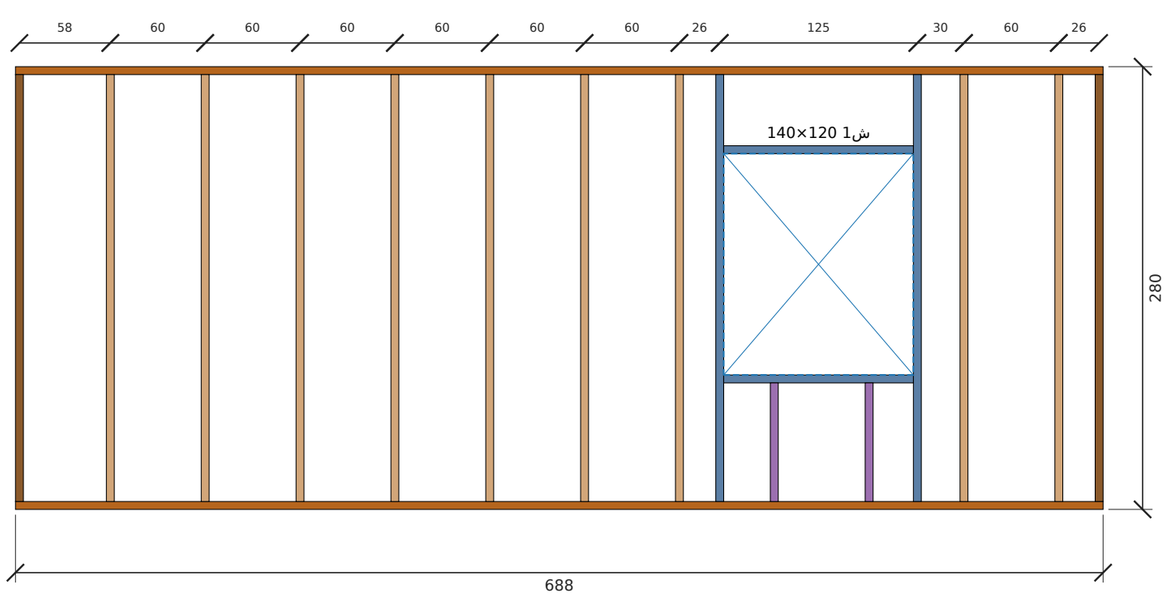


قاعدة سفلية | علوي | عمود | عمود زاوية | جنب فتحة | رأس فتحة | جلسة شباك | عمود قصير

مصنع وتد الأخشاب Watad Wood Factory	المشروع / العميل كوخ مزرعة حايل الاستثماري — دورين — صالة + غرفة نوم + تراس — 6.00 × 7.00 م عميل — حايل (مزرعة استثمارية)	عنوان اللوحة لوحات التأطير (للورشة) (× 3 أكواخ)	المقياس —	التاريخ 2026-10-23	رقم اللوحة W-10 (10/16)

تأطير جدار أ-جدار الدورة — الطول 152 سم، الارتفاع 280 سم (داخلي)

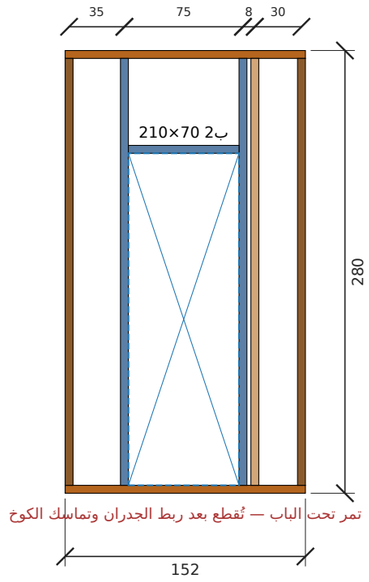


تأطير جدار أ-جدار الدورة الجانبي — الطول 306 سم، الارتفاع 280 سم (داخلي)

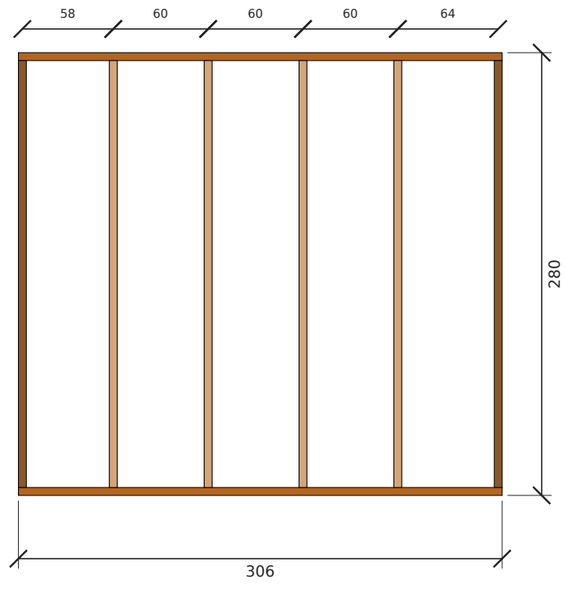


قاعدة سفلية | علوي | عمود | عمود زاوية | جنب فتحة | رأس فتحة | جلسة شباك | عمود قصير

مصنع وتد الأخشاب Watad Wood Factory	المشروع / العميل كوخ مزرعة حايل الاستثماري — دورين — صالة + غرفة نوم + تراس — 6.00 × 7.00 م عميل — حايل (مزرعة استثمارية)	عنوان اللوحة لوحات التأطير (للورشة) (× 3 أكواخ)	المقياس —	التاريخ 2026-10-23	رقم اللوحة W-11 (11/16)

تأطير جدار ب-جنوب — الطول 588 سم، الارتفاع 280 سم

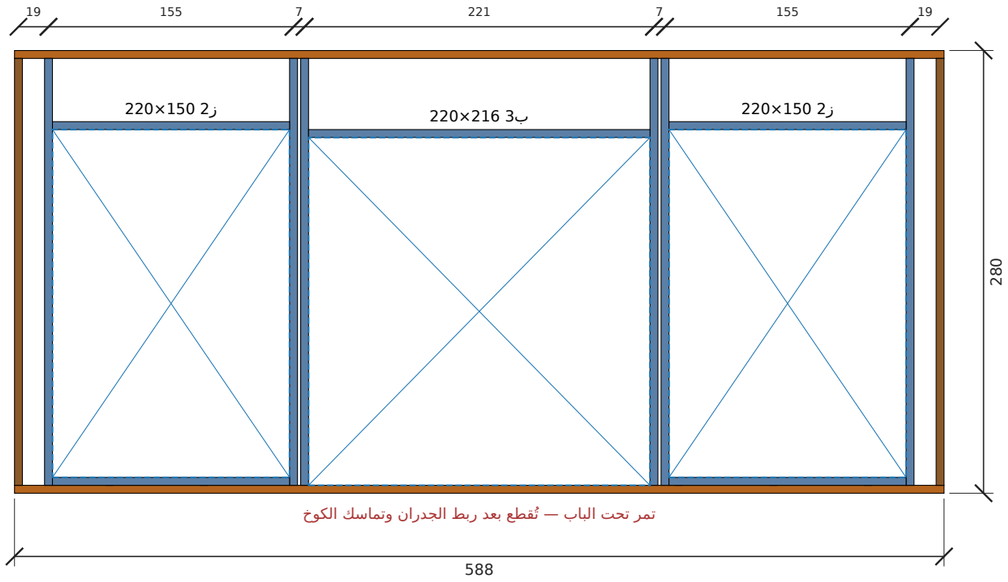


تأطير جدار ب-شرق — الطول 688 سم، الارتفاع 280 سم

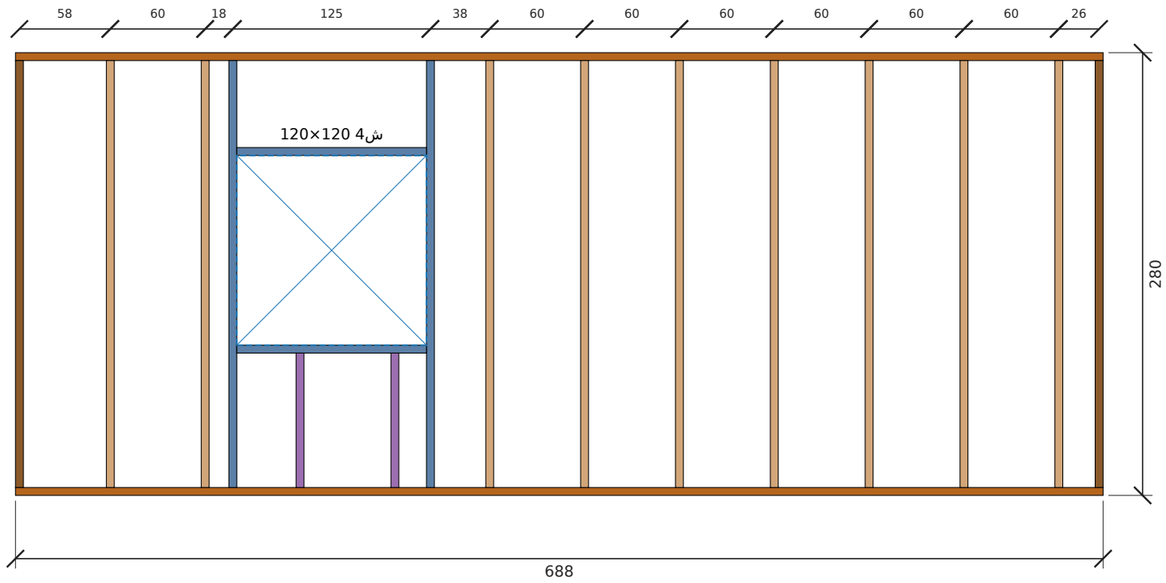


عمود قصير — جلسة شباك — رأس فتحة — جنب فتحة — عمود زاوية — عمود — علوي — قاعدة سفلية

مصنع وتد الأخشاب Watad Wood Factory	المشروع / العميل **كوخ مزرعة حايل الاستثماري — دورين — صالة + غرفة نوم + تراس — 6.00 × 7.00 م** **عميل — حايل (مزرعة استثمارية)**	عنوان اللوحة **لوحات التأطير (للورشة) (× 3 أكواخ)**	المقياس **—**	التاريخ **2026-10-23**	رقم اللوحة **W-12 (12/16)**

تأطير جدار ب-شمال — الطول 588 سم، الارتفاع 280 سم

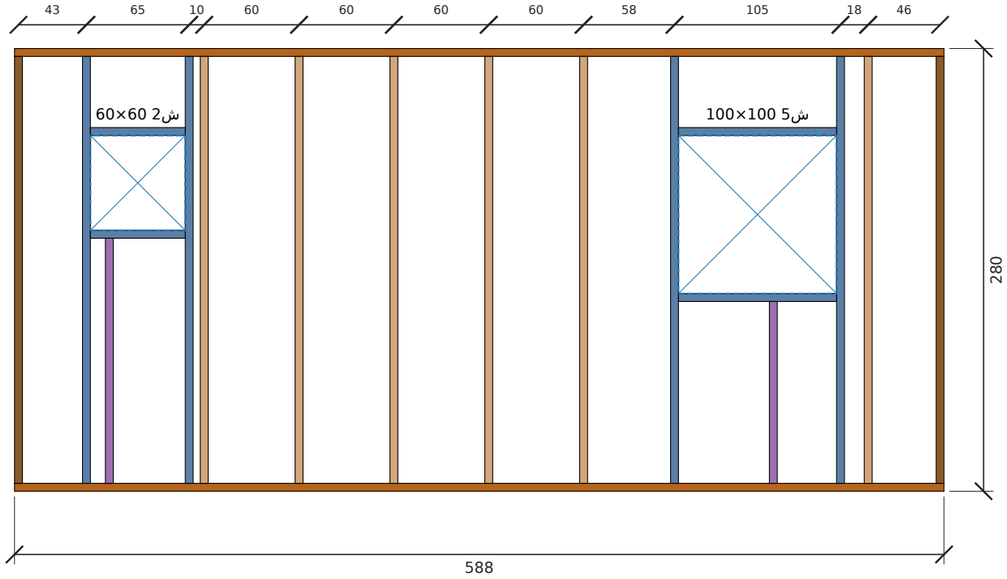


تأطير جدار ب-غرب — الطول 688 سم، الارتفاع 280 سم

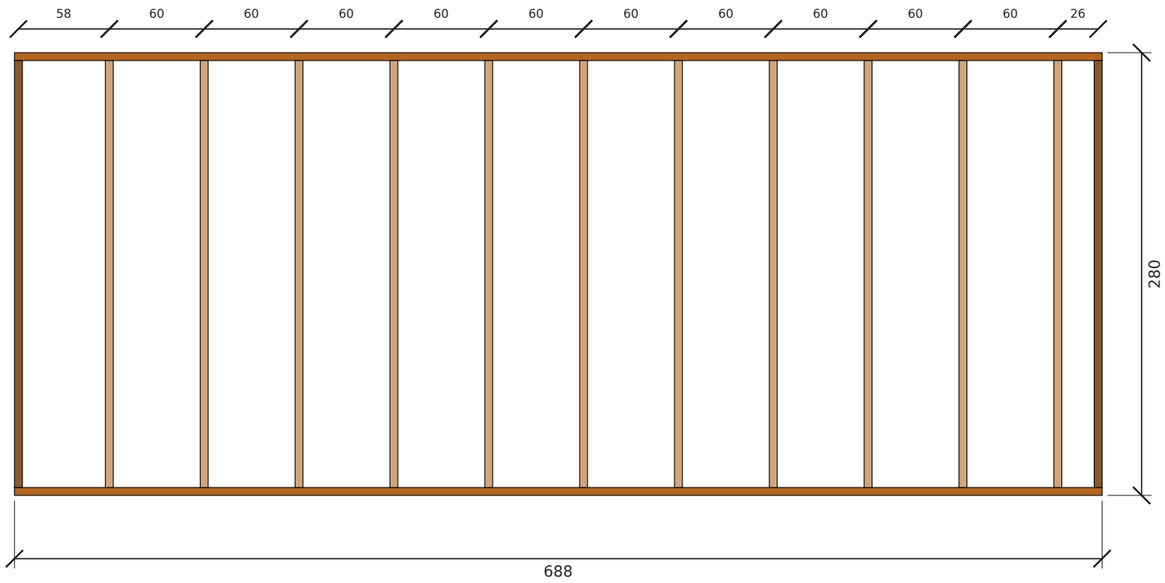


قاعدة سفلية | علوي | عمود | عمود زاوية | جنب فتحة | رأس فتحة | جلسة شباك | عمود قصير

مصنع وتد الأخشاب Watad Wood Factory	المشروع / العميل كوخ مزرعة حايل الاستثماري — دورين — صالة + غرفة نوم + تراس — 6.00 × 7.00 م عميل — حايل (مزرعة استثمارية)	عنوان اللوحة لوحات التأطير (للورشة) (× 3 أكواخ)	المقياس —	التاريخ 2026-10-23	رقم اللوحة W-13 (13/16)

تأطير جدار ب-جدار الغرفة — الطول 588 سم، الارتفاع 280 سم (داخلي)

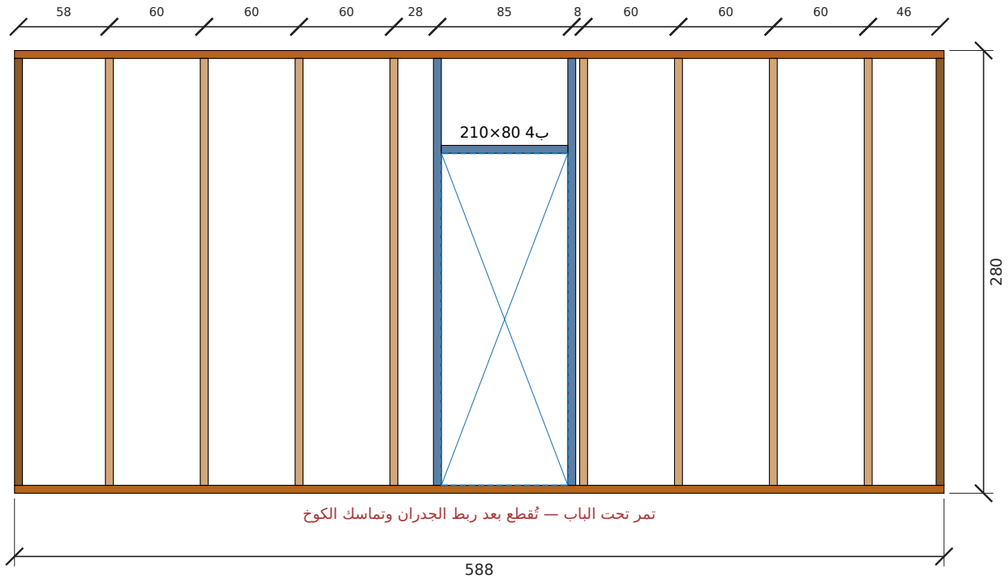

تأطير جدار ب-جدار الحمام — الطول 306 سم، الارتفاع 280 سم (داخلي)

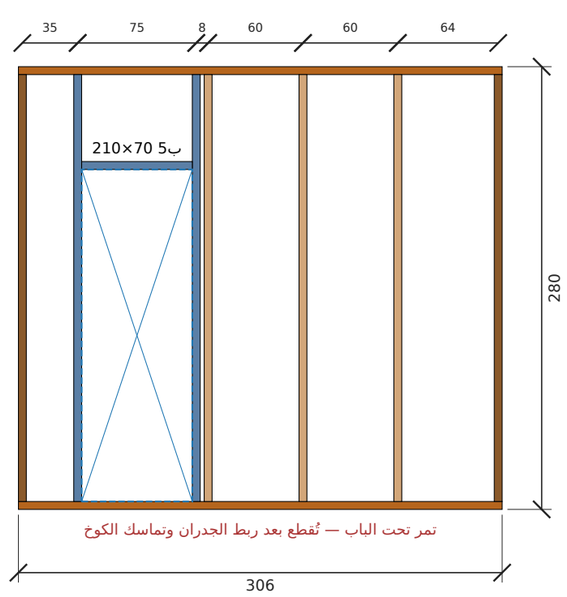

قاعدة سفلية | علوي | عمود | عمود زاوية | جنب فتحة | رأس فتحة | جلسة شباك | عمود قصير

مصنع وتد الأخشاب Watad Wood Factory	المشروع / العميل **كوخ مزرعة حايل الاستثماري — دورين — صالة + غرفة نوم + تراس — 6.00 × 7.00 م (× 3 أكواخ)** **عميل — حايل (مزرعة استثمارية)**	عنوان اللوحة **لوحات التأطير (للورشة)**	المقياس **—**	التاريخ **2026-10-23**	رقم اللوحة **W-14 (14/16)**

جدول الكميات وخطة تقطيع الطبليات

البند	القيمة
الارتفاع المطلوب / المعتمد	280 / 280 سم
السقف	جملون 40° — أعلى نقطة 837 سم من وجه الصبة
المدادات 5×15	34 مداد (17 لكل جهة) × حتى 437 سم — من طبلية 480
طبليات الطريقة الأولى (مداد + عمود)	34 طبلية × 480 سم
طبليات الطريقة الثانية (3 أعمدة)	44 طبلية × 320 سم
مدادات أرضية الدور العلوي 5×15 كل 60 سم	24 مداد — 162سم×12، 446سم×12 (طبلية 480 بالطريقة الأولى)
إجمالي الطبليات 5×22.5	102
إجمالي قطع 5×7	193
قائمة تقطيع 5×7	688سم×8 | 588سم×10 | 306سم×4 | 270سم×122 | 216سم×2 | 160سم×4 | 155سم×2 | 152سم×2 | 150سم×4
	120سم×6 | 115سم×1 | 110سم×4 | 100سم×2 | 85سم×2 | 80سم×1 | 75سم×3 | 70سم×2 | 60سم×4
ألواح تلبيس 2.5 سم	383 لوح × 400 سم (مجموع الصفوف 1263.6 م، 24 وجه)
أسمنت بورد 12 مم (122×244)	40 لوح (داخل دورات المياه)
العزل	201 لوح فوم صخري 80
الصبة	يجهزها العميل — 20 سم، مفرغة تحت دورات المياه

مراجعة التصميم مقابل قواعد المصنع

النوع	البند	التفاصيل	المقترح
ملاحظة	بحر المدادات	أطول بحر بدون جدار داخلي يحمل المداد: جهة أ: 300 سم، جهة ب: 300 سم. يحتاج رقم المصنع لأقصى بحر مسموح لتحديد المدادات اللي تُقوّى 20×5.	
ملاحظة	الصبة والدرج	ارتفاع الصبة 45 سم ← 3 درجة بقائمة 15.0 سم.	
ملاحظة	مناسيب رؤوس الفتحات	رؤوس الأبواب والشبابيك على مناسيب مختلفة: 205، 210، 220، 225، 240، 245 سم.	
سؤال	يحتاج تأكيد	أقصى بحر للمداد بدون جدار داخلي قبل إضافة تقوية 5×7 (مداد 20×5)؟	
سؤال	يحتاج تأكيد	التغطية الصافية للوح التلبيس بعد التعشيق (مستنتجة مؤقتاً 18.67 سم من 280/15)؟	
سؤال	يحتاج تأكيد	هل يوضع أعمدة قصيرة فوق رأس الشباك/الباب إلى العلوي؟	
سؤال	يحتاج تأكيد	مكان الوصلة في القاعدة والعلوي إذا الجدار أطول من الطبلية؟	