
المسقط الأفقي مع الفرش — الدور الأرضي


الأبعاد بالسنتيمتر - الجدران: قوائم 7×5 + تلبيس 2.5 من الجهتين (12 سم) | منسوب الأرضية +0.00

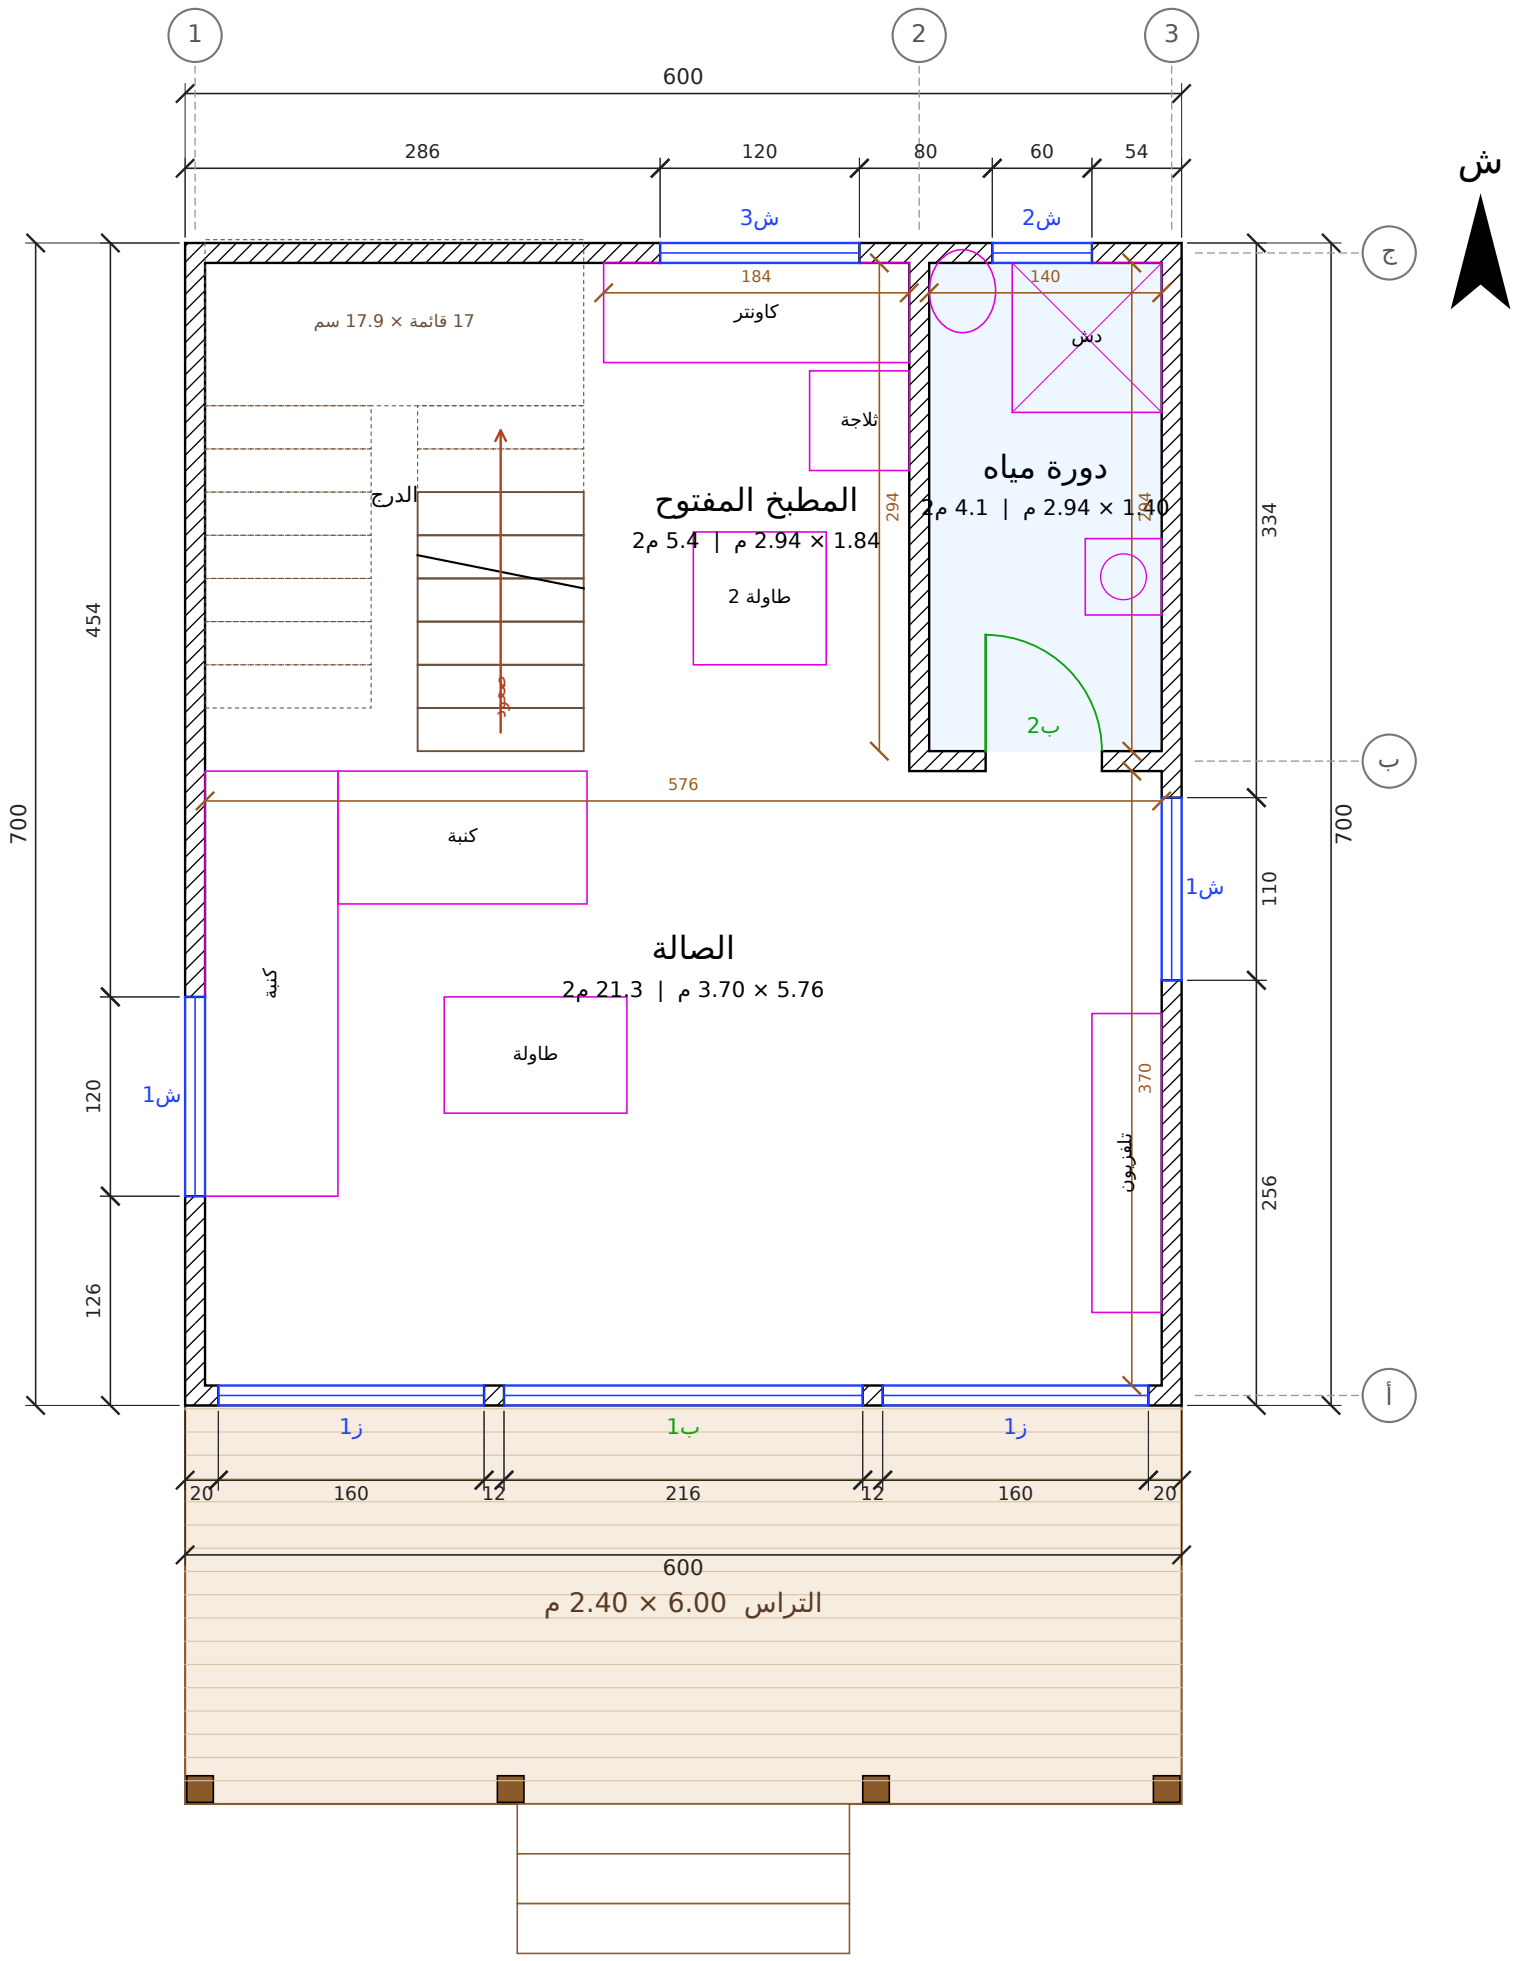


	المشروع / العميل	عنوان اللوحة	المقياس	التاريخ	رقم اللوحة
مصنع وتد الأخشاب Watad Wood Factory	كوخ مزرعة حايل الاستثماري — دورين — صالة + غرفة نوم + تراس — 6.00 × 7.00 م (× 3 أكواخ) عميل — حايل (مزرعة استثمارية)	المسقط الأفقي — الدور الأرضي	1:50	2026-10-23	A-01 (1/11)

المسقط الأفقي مع الفرش — الدور الأول

الأبعاد بالسنتيمتر - الجدران: قوائم 7×5 + تلبيس 2.5 من الجهتين (12 سم) | منسوب الأرضية +3.05

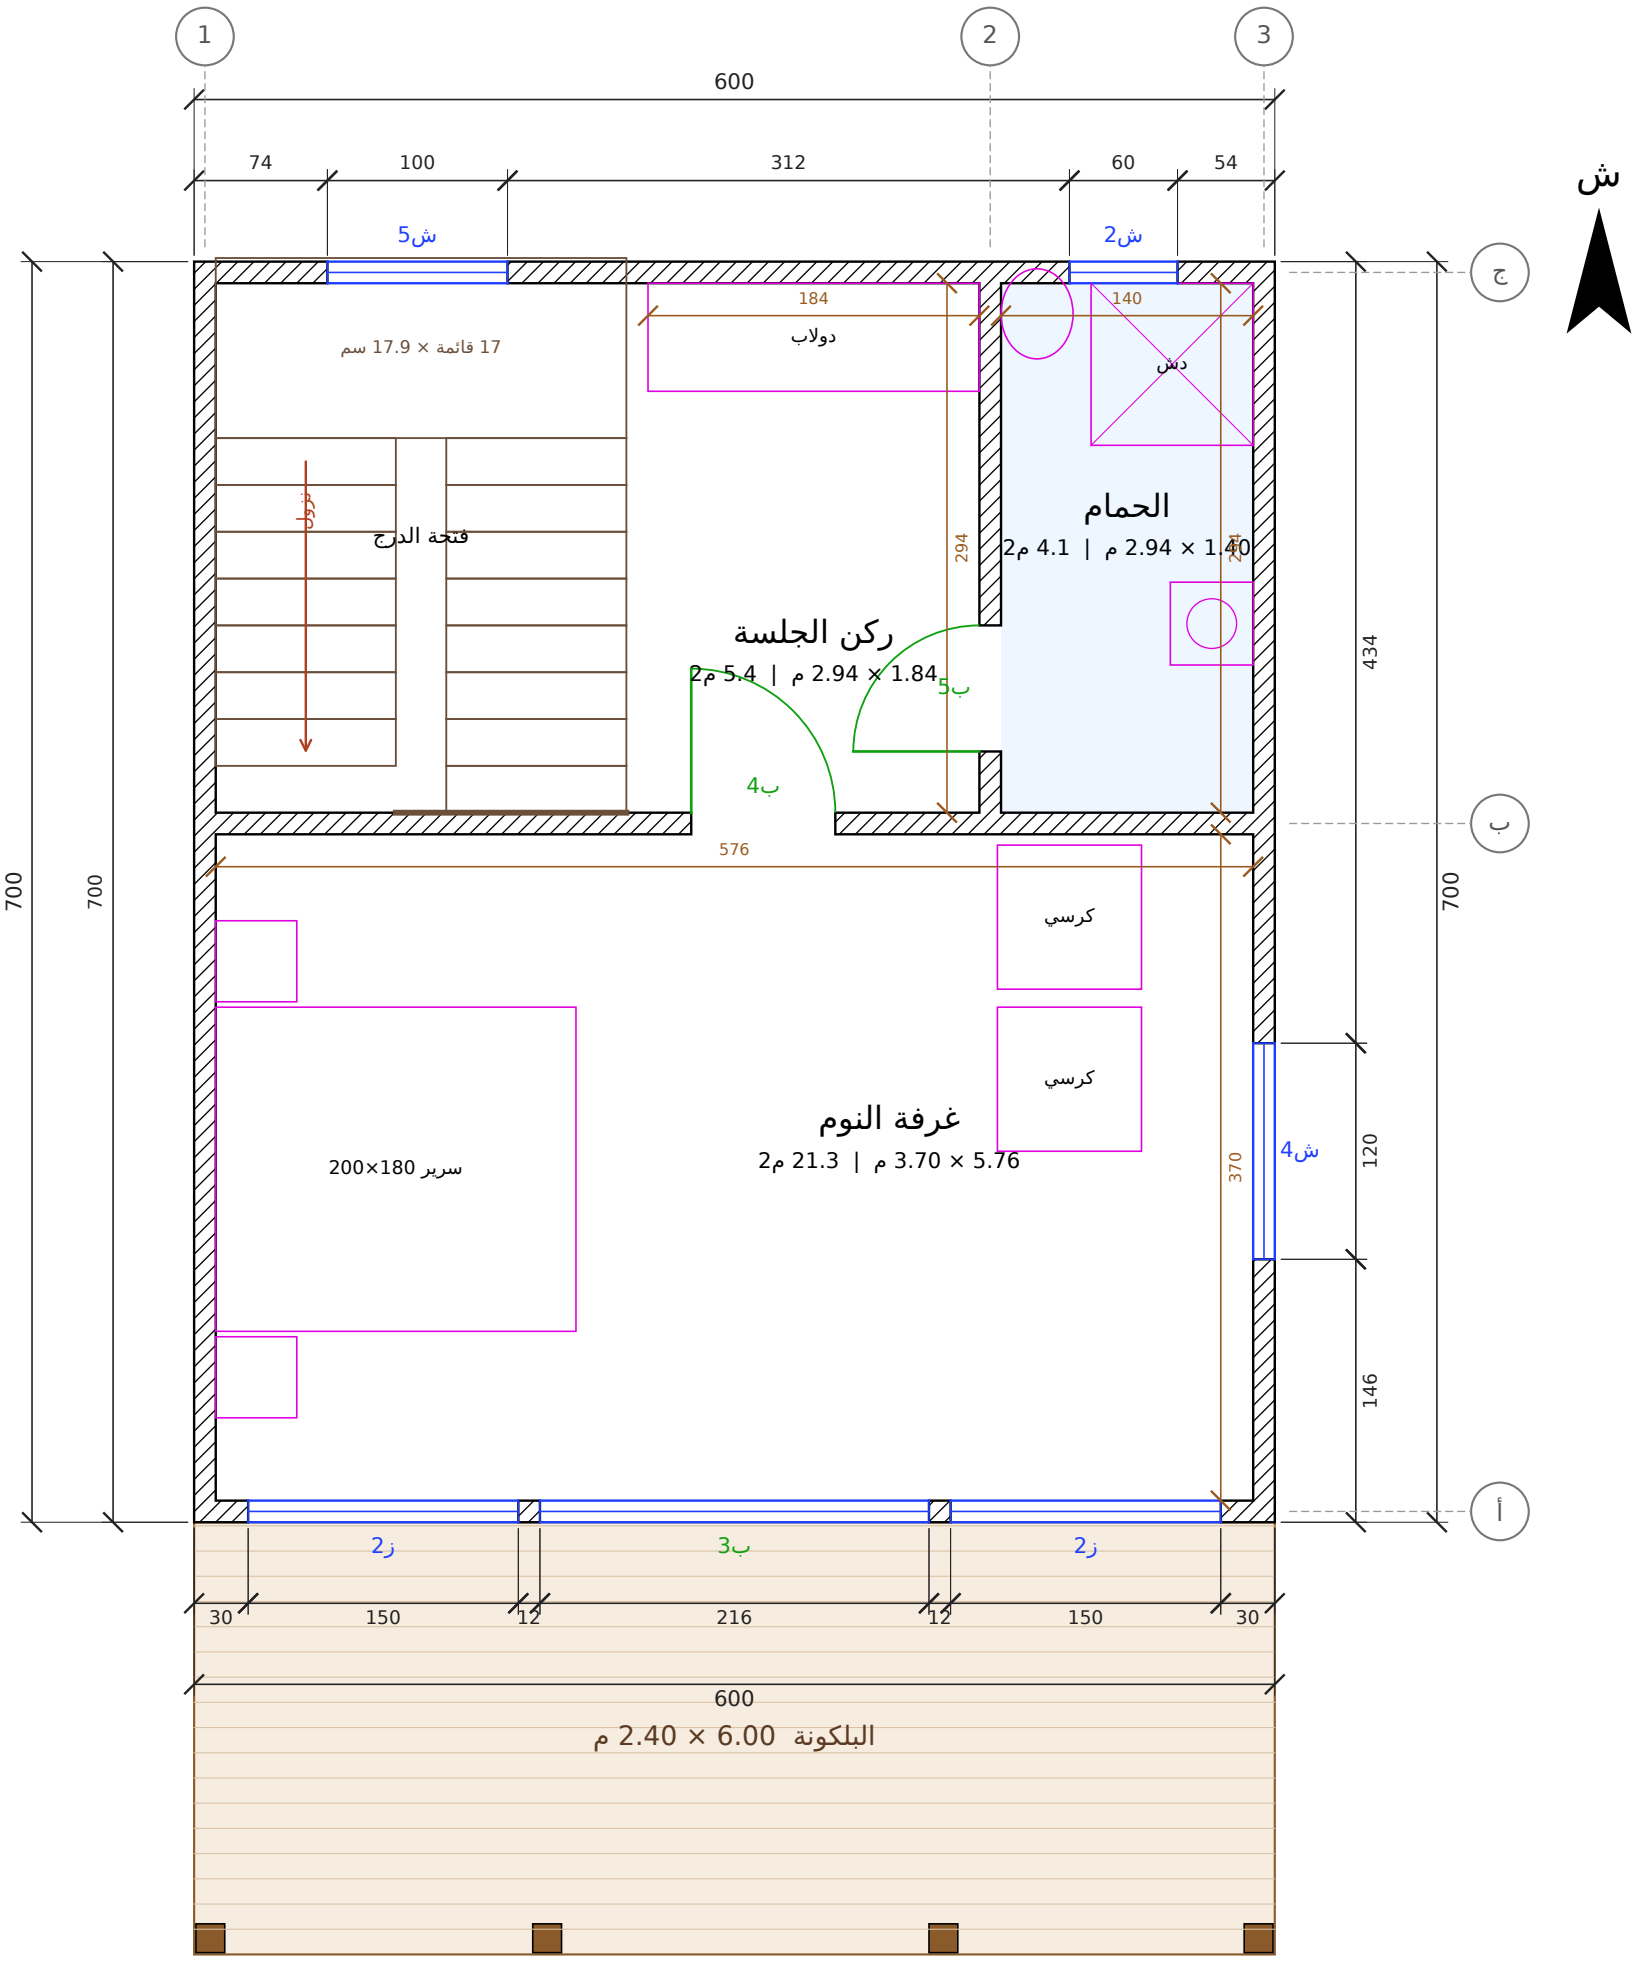


المشروع / العميل	عنوان اللوحة	المقياس	التاريخ	رقم اللوحة
مصنع وتد الأخشاب — كوخ مزرعة حايل الاستثماري — دورين — صالة + غرفة نوم + تراس — 6.00 × 7.00 م (3×2 أكواخ) عميل — حايل (مزرعة استثمارية) Watad Wood Factory	**المسقط الأفقي — الدور الأول**	**1:50**	**2026-10-23**	**A-02 (2/11)**

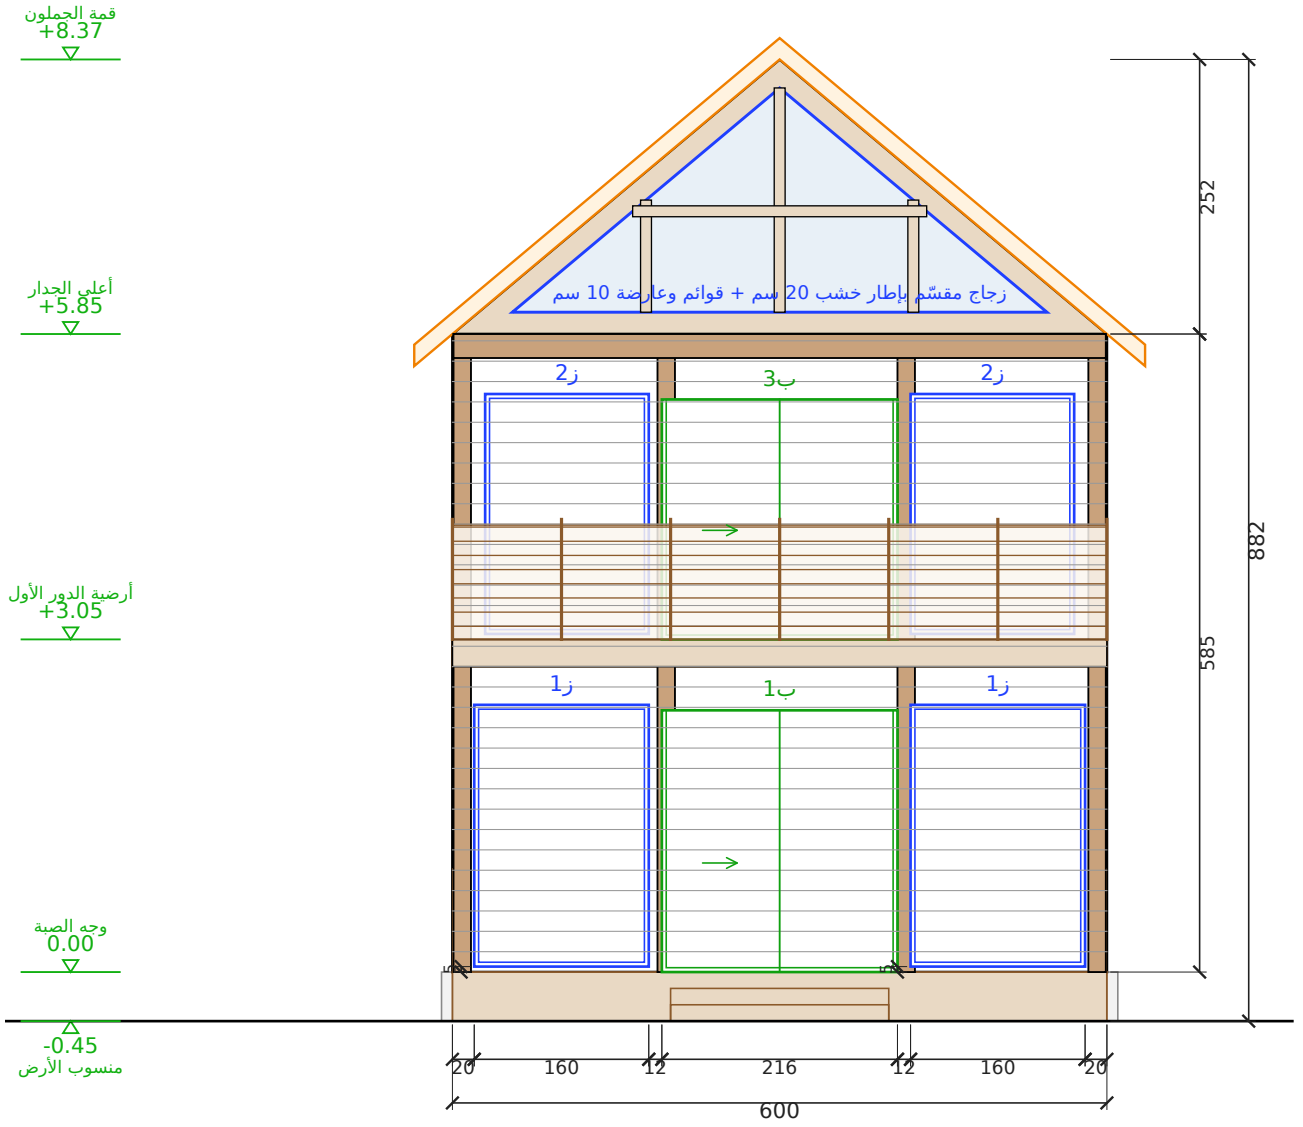

الواجهة الأمامية (زجاج على التراس)

مقياس 1:50 | الوحدة: سم

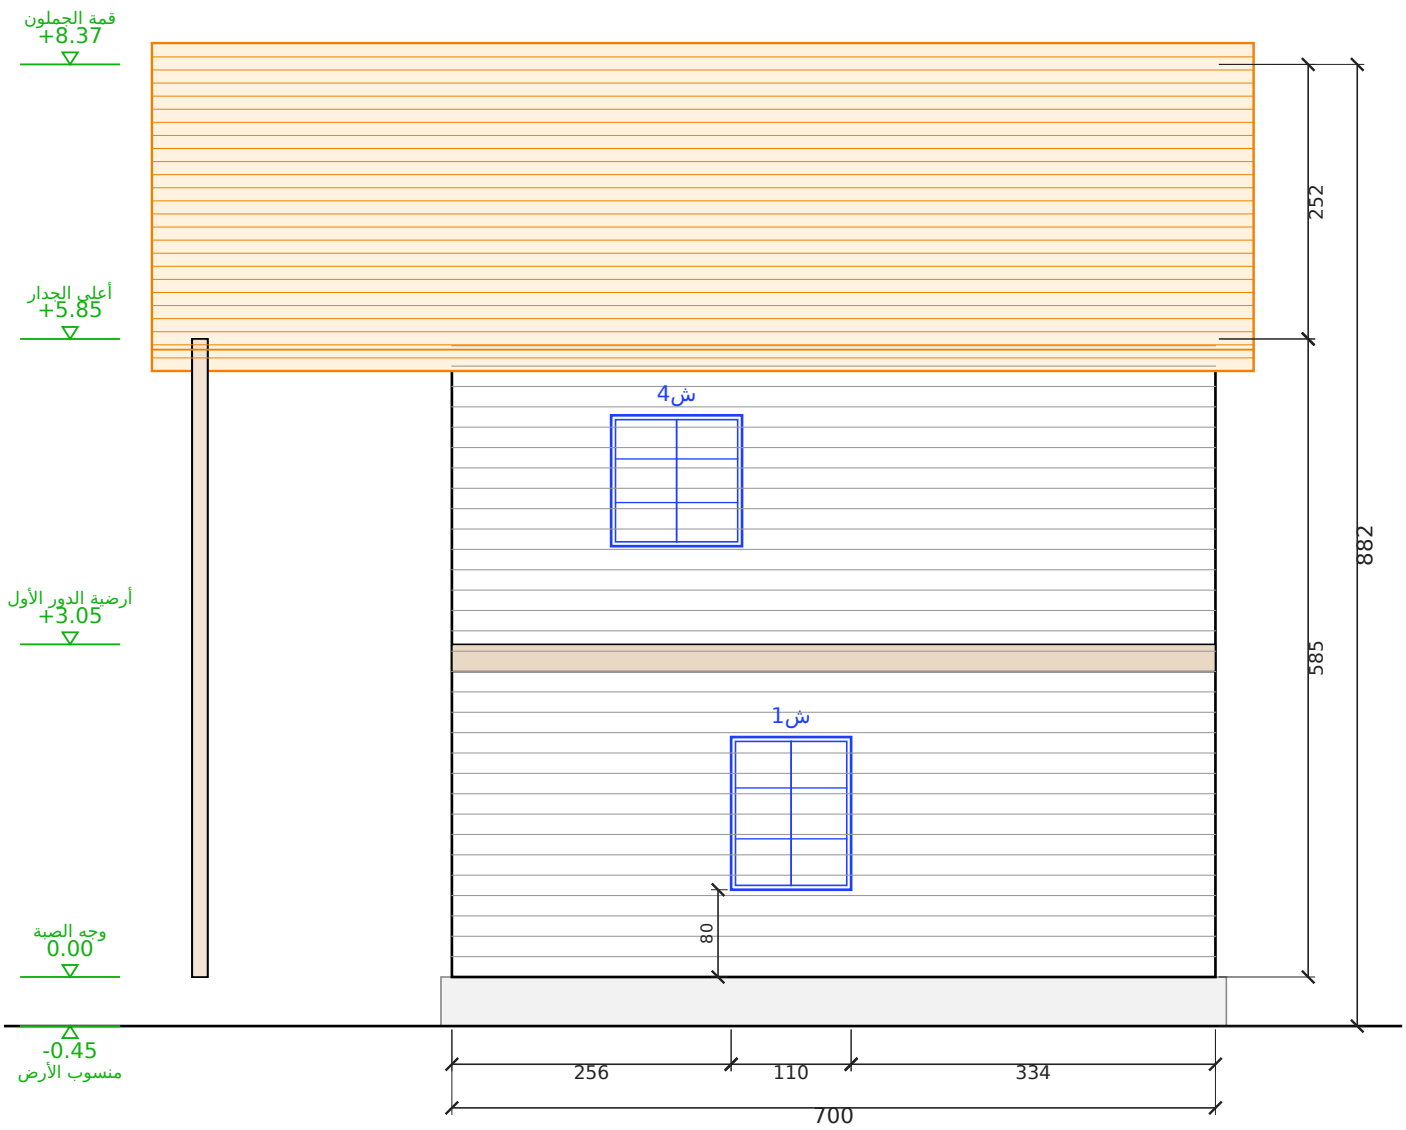


الواجهة الشرقية

مقياس 1:50 | الوحدة: سم


المشروع / العميل	عنوان اللوحة	المقياس	التاريخ	رقم اللوحة
كوخ مزرعة حايل الاستثماري — دورين — صالة + غرفة نوم + تراس — 6.00 × 7.00 م (× 3 أكواخ) عميل — حايل (مزرعة استثمارية)	**الواجهة الأمامية (زجاج على التراس) والواجهة الشرقية**	1:50	2026-10-23	A-03 (3/11)

مصنع وتد الأخشاب
Watad Wood Factory

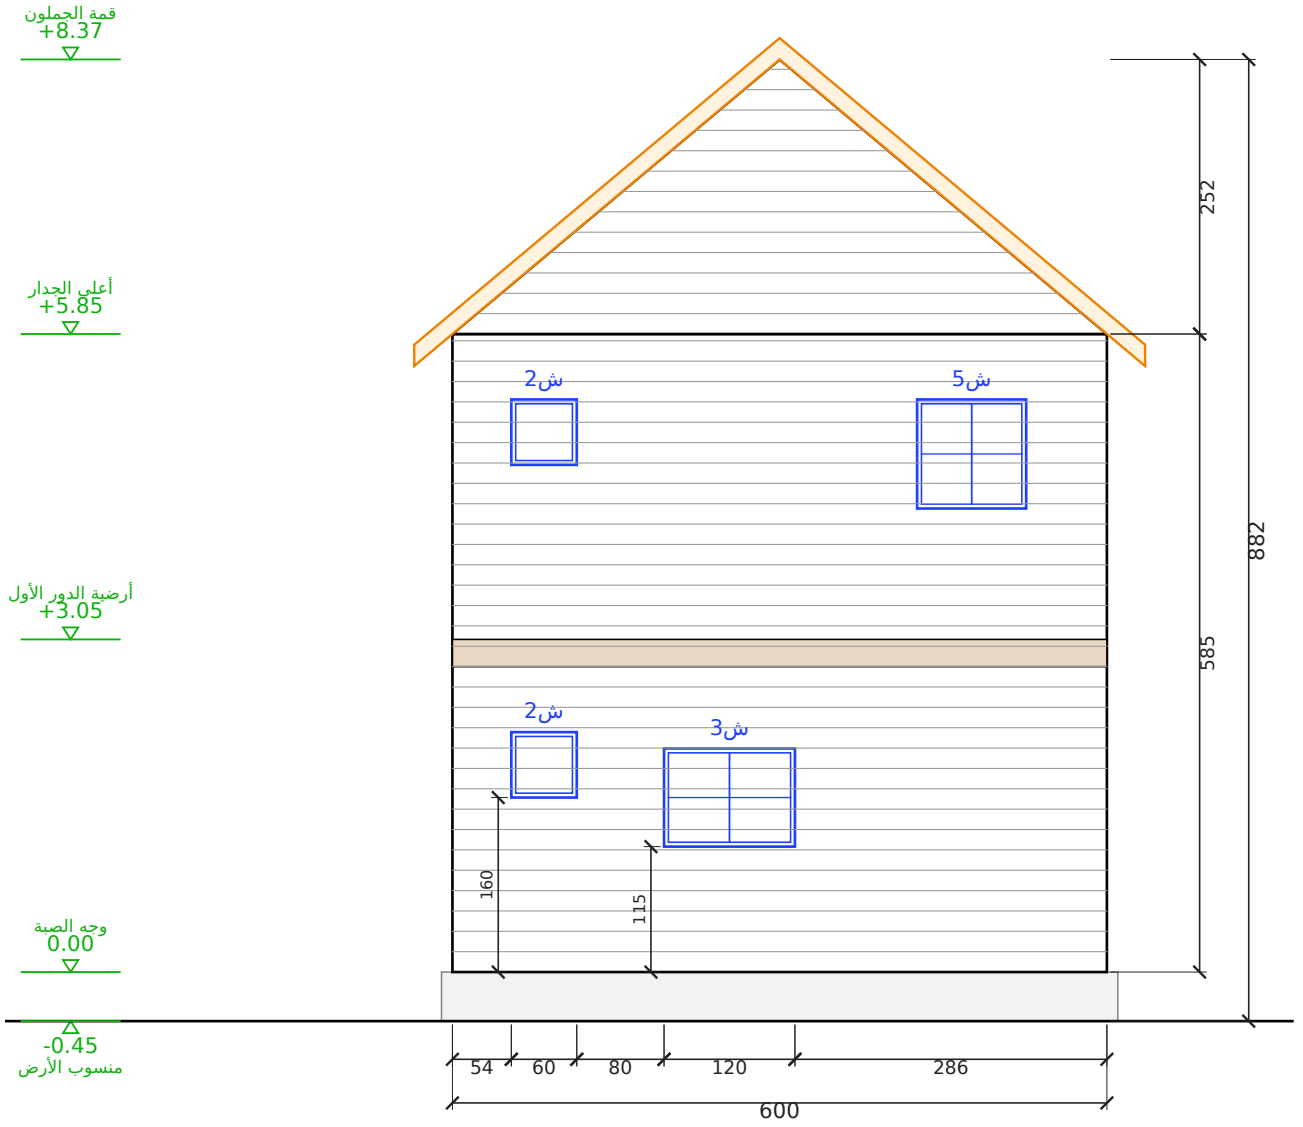

الواجهة الخلفية

مقياس 1:50 | الوحدة: سم

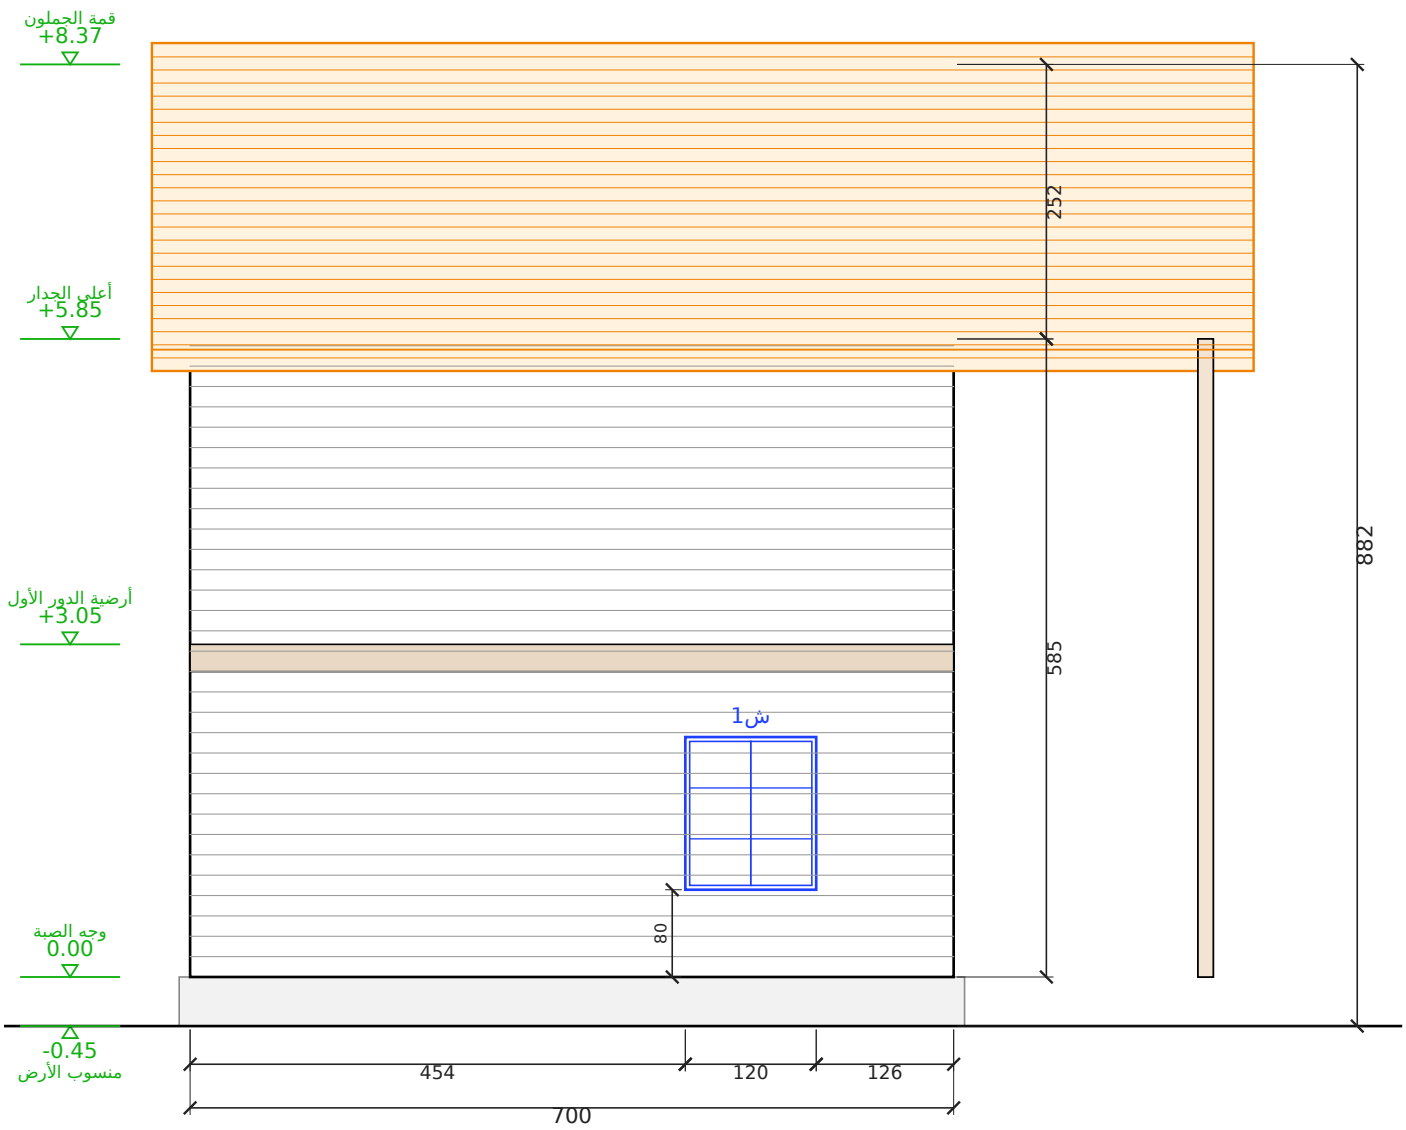


الواجهة الغربية


مقياس 1:50 | الوحدة: سم

المشروع / العميل	عنوان اللوحة	المقياس	التاريخ	رقم اللوحة
مصنع وتد الأخشاب Watad Wood Factory كوخ مزرعة حايل الاستثماري — دورين — صالة + غرفة نوم + تراس — 6.00 × 7.00 م (× 3 أكواخ) عميل — حايل (مزرعة استثمارية)	**الواجهة الخلفية والواجهة الغربية**	**1:50**	**2026-10-23**	**A-04 (4/11)**


مسقط السقف (جملون)
رفرف 35 سم من كل جهة | مقياس 1:50

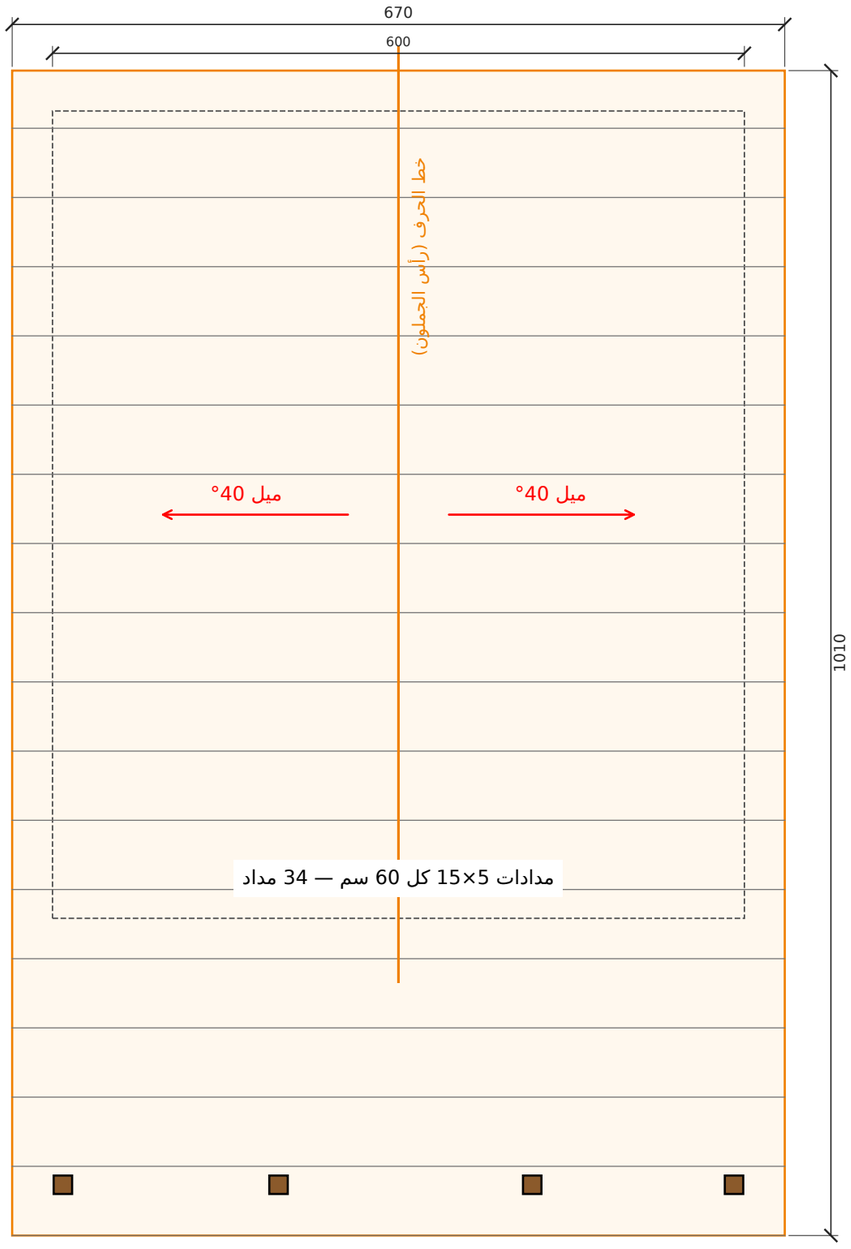

قطاع عرضي أ-أ
مقياس 1:50 | الوحدة: سم

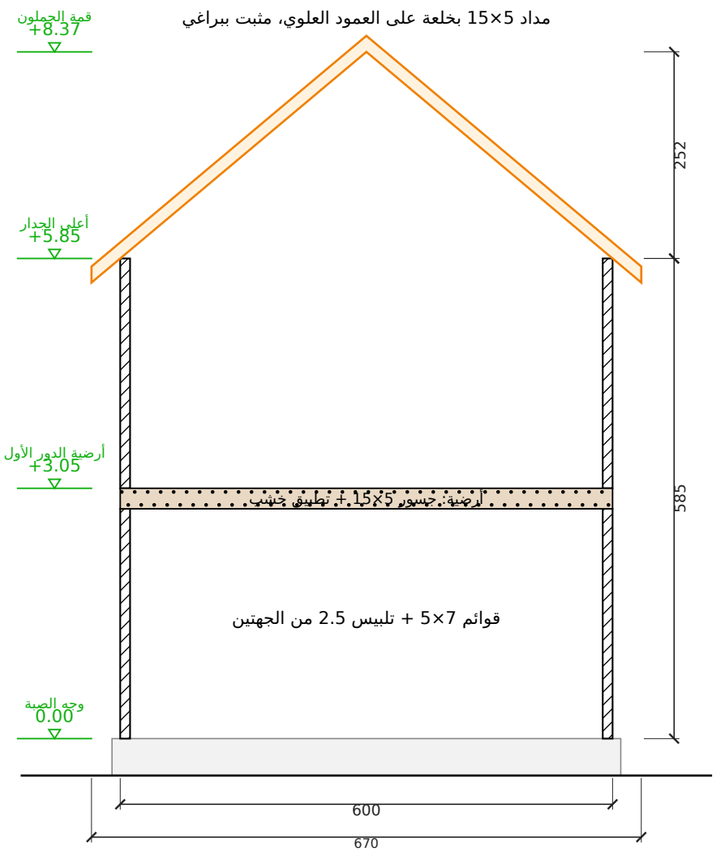

تفصيلة جلوس المداد على العلوي (1:5)

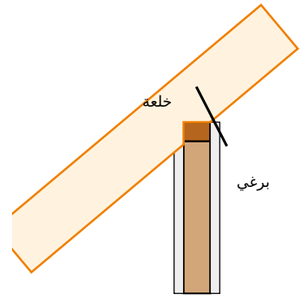

علوي 7×5 على قائم 7×5

مصنع وتد الأخشاب Watad Wood Factory	المشروع / العميل كوخ مزرعة حايل الاستثماري — دورين — صالة + غرفة نوم + تراس — 6.00 × 7.00 م (× 3 أكواخ) عميل — حايل (مزرعة استثمارية)	عنوان اللوحة مسقط السقف والقطاع	المقياس 1:50	التاريخ 2026-10-23	رقم اللوحة A-05 (5/11)

جدول مقاسات الأبواب والشبابيك
مقاس الفتحة الصافي في الجدار - الوحدة: سم

الرمز	النوع	العرض (سم)	الارتفاع (سم)	ارتفاع الجلسة (سم)	العدد	الموقع
ب1	باب مزدوج	216	240	-	1	الأمامية (زجاج على التراس)
ب2	باب	70	210	-	1	دورة المياه
ب3	باب مزدوج	216	220	-	1	الأمامية (على البلكونة)
ب4	باب	80	210	-	1	غرفة النوم
ب5	باب	70	210	-	1	الحمام
ز1	شباك	160	240	5	2	الأمامية (زجاج على التراس) 2
ز2	شباك	150	220	5	2	الأمامية (على البلكونة) 2
ش1	شباك	110	140	80	1	الشرقية
ش1	شباك	120	140	80	1	الغربية
ش2	شباك	60	60	160	2	الخلفية 2
ش3	شباك	120	90	115	1	الخلفية
ش4	شباك	120	120	90	1	الشرقية
ش5	شباك	100	100	120	1	الخلفية

الإجمالي: أبواب 5 - شبابيك 11

جدول المساحات وبيانات المشروع والتسعير

بيانات المشروع

البند	البيان
المشروع	كوخ مزرعة حايل الاستثماري — دورين — صالة + غرفة نوم + تراس — 6.00 × 7.00 م (× 3 أكواخ)
العميل	عميل — حايل (مزرعة استثمارية)
الموقع	حايل — مزرعة
الاستخدام	3 أكواخ استثمارية (تأجير) — نفس التصميم
التاريخ	2026-10-23
نظام البناء	هيكل خشب 5×7 + تلبيس 2.5 سم من الجهتين
السقف	جملون 40° — قرميد معدني

جدول المساحات

م	الفراغ	الأبعاد (م)	المساحة (م2)
1	أرضي — الصالة	5.76 × 3.70	21.31
2	أرضي — المطبخ المفتوح	1.84 × 2.94	5.41
3	أرضي — الدرج	2.28 × 2.94	6.70
4	أرضي — دورة مياه	1.40 × 2.94	4.12
5	أول — غرفة النوم	5.76 × 3.70	21.31
6	أول — ركن الجلسة	1.84 × 2.94	5.41
7	أول — الحمام	1.40 × 2.94	4.12
	المساحة الصافية الداخلية		68.38
	التراس	**6.00 × 2.40**	**14.40**
	البلكونة	**6.00 × 2.40**	**14.40**
	المساحة الإجمالية المبنية	**6.00 × 7.00 × 2 دور**	**84.00**
	المساحة الكلية (المبنية + التراس والبلكونة)		**112.80**

التسعير المفصّل

البند	المبلغ (ريال)
الكوخ المبني 84.00 م² × 1,096	92,064
تراس الأرضي + بلكونة الأول (6.00 × 2.40 × 2) — 28.80 م² × 1,096	31,565
الإجمالي (ريال)	**123,629**

ملاحظات:

- السعر لكوخ واحد (الدورين والتراس والبلكونة) — الأكواخ الثلاثة نفس التصميم والسعر.
- الصبة والتمديدات الخارجية على العميل ما لم يُذكر غير ذلك.

لقطات المنظور الخارجي

المنظور الأمامي



منظور أمامي من اليسار



منظور أمامي من اليمين




المنظور الخلفي



منظور خلفي من اليمين



منظر علوي

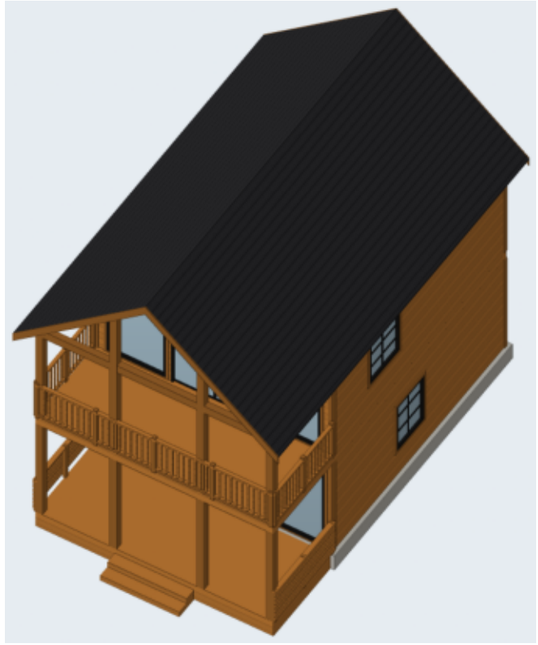

مصنع وتد الأخشاب Watad Wood Factory	المشروع / العميل كوخ مزرعة حايل الاستثماري — دورين — صالة + غرفة نوم + تراس — 6.00 × 7.00 م (× 3 أكواخ) عميل — حايل (مزرعة استثمارية)	عنوان اللوحة لقطات المنظور	المقياس —	التاريخ 2026-10-23	رقم اللوحة A-08 (8/11)

المقطع العلوي بالفرش — الدور الأرضي


مقطع أفقي على ارتفاع 1.90 م — توزيع الفرش ومسار الحركة



مصنع وتد الأخشاب Watad Wood Factory	المشروع / العميل **كوخ مزرعة حايل الاستثماري — دورين — صالة + غرفة نوم + تراس — 6.00 × 7.00 م (× 3 أكواخ)** **عميل — حايل (مزرعة استثمارية)**	عنوان اللوحة **المقطع العلوي بالفرش — الدور الأرضي**	المقياس **—**	التاريخ **2026-10-23**	رقم اللوحة **A-09 (9/11)**

المقطع العلوي بالفرش — الدور الأول

مقطع أفقي على ارتفاع 1.90 م — توزيع الفرش ومسار الحركة

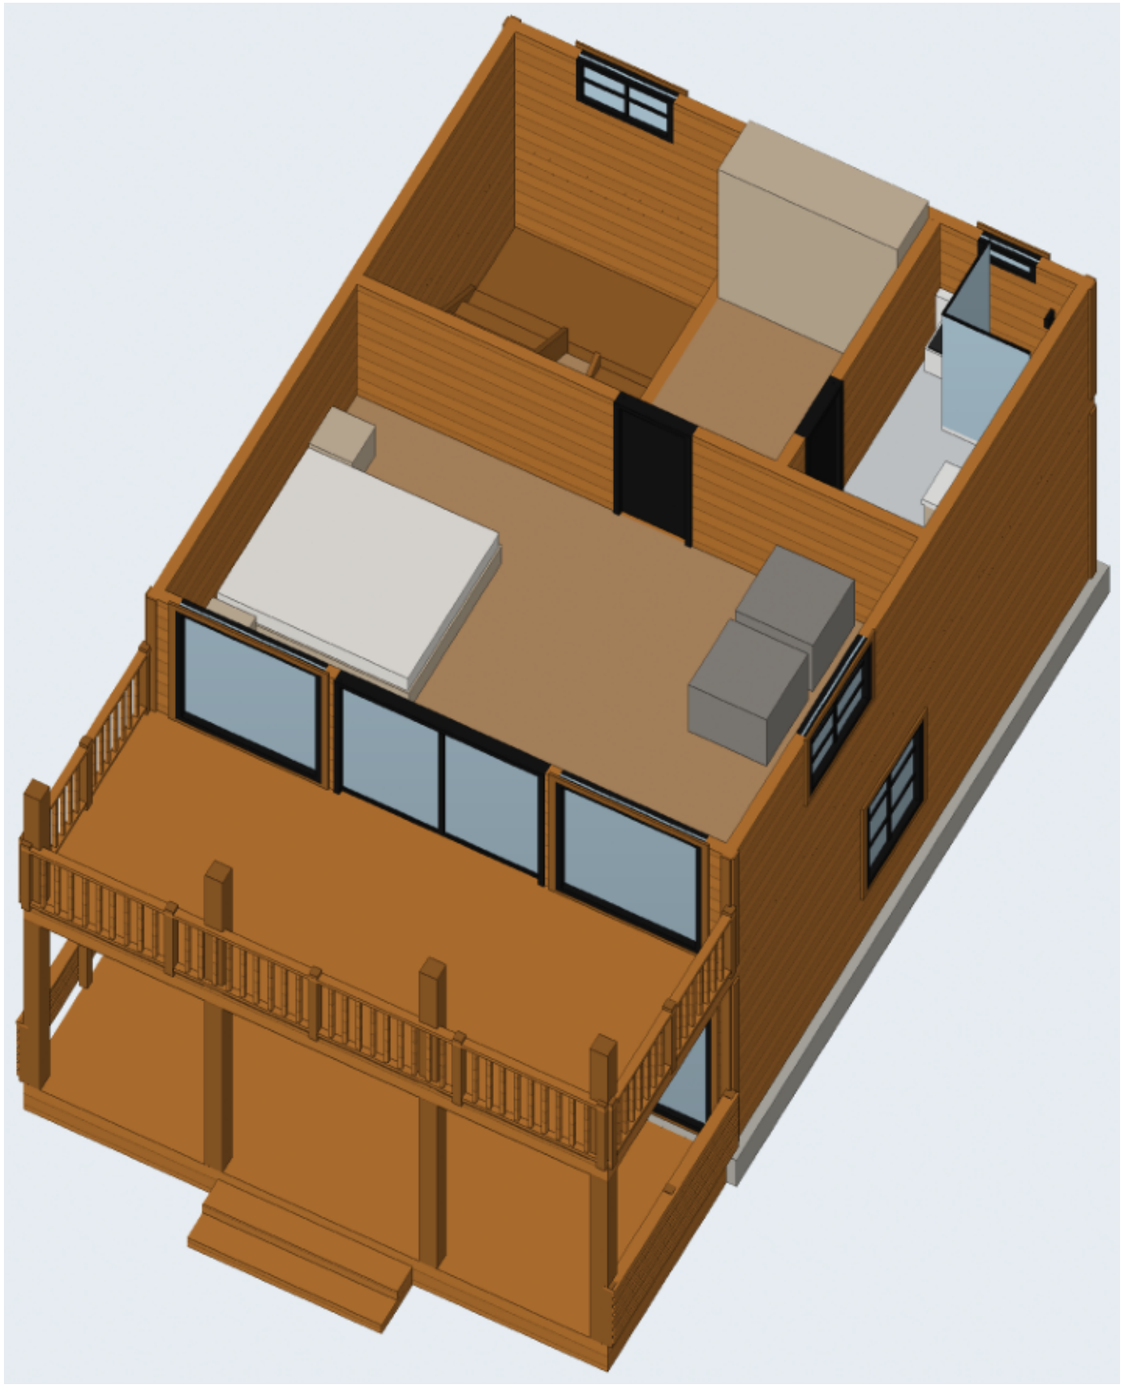

مصنع وتد الأخشاب Watad Wood Factory	المشروع / العميل كوخ مزرعة حايل الاستثماري — دورين — صالة + غرفة نوم + تراس — 6.00 × 7.00 م (× 3 أكواخ) عميل — حايل (مزرعة استثمارية)	عنوان اللوحة المقطع العلوي بالفرش — الدور الأول	المقياس —	التاريخ 2026-10-23	رقم اللوحة A-10 (10/11)

المنظور ثلاثي الأبعاد والمواد

النمط: جوزي غامق + إطارات سوداء — رندر واقعي بخامات حقيقية



جدول المواد والألوان

الخشب / الصبغة

صبغة عسلي / سيدر

القرميد

قرميد رمادي غامق

الزجاج

زجاج شفاف

إطارات الشبابيك والأبواب

إطار ألمنيوم أسود

الكنار والزوايا

نفس الصبغة أغمق درجة


الصبة

خرسانة 45 سم


الدربزين: ألواح أفقية متقاربة (عصري)

تقسيم الشبابيك: بدون | الباب الرئيسي: سحاب زجاج

أنواع الدربزين المعتمدة (من مشاريع المصنع)

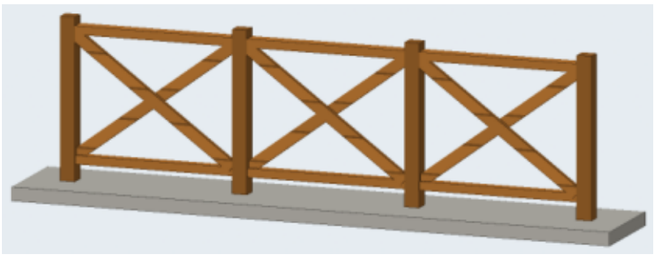

تقاطع X (صورة 5)

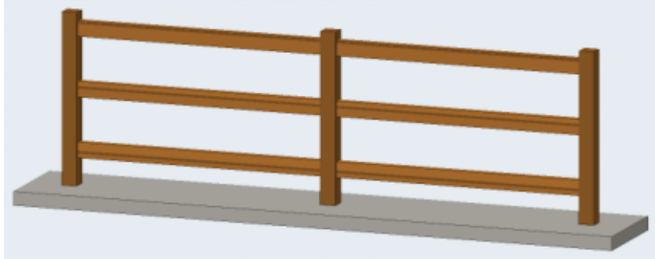

3 مرابيع أفقية (صورة 2)



قوائم رأسية متقارية (صورة 1)

مصنع وتد الأخشاب Watad Wood Factory	المشروع / العميل **كوخ مزرعة حايل الاستثماري — دورين — صالة + غرفة نوم + تراس — 6.00 × 7.00 م (× 3 أكواخ)** **عميل — حايل (مزرعة استثمارية)**	عنوان اللوحة **المنظور والمواد**	المقياس **—**	التاريخ **2026-10-23**	رقم اللوحة **A-11 (11/11)**