
المنظور ثلاثي الأبعاد والمواد

النمط: جوزي غامق + إطارات سوداء — رندر واقعي بخامات حقيقية

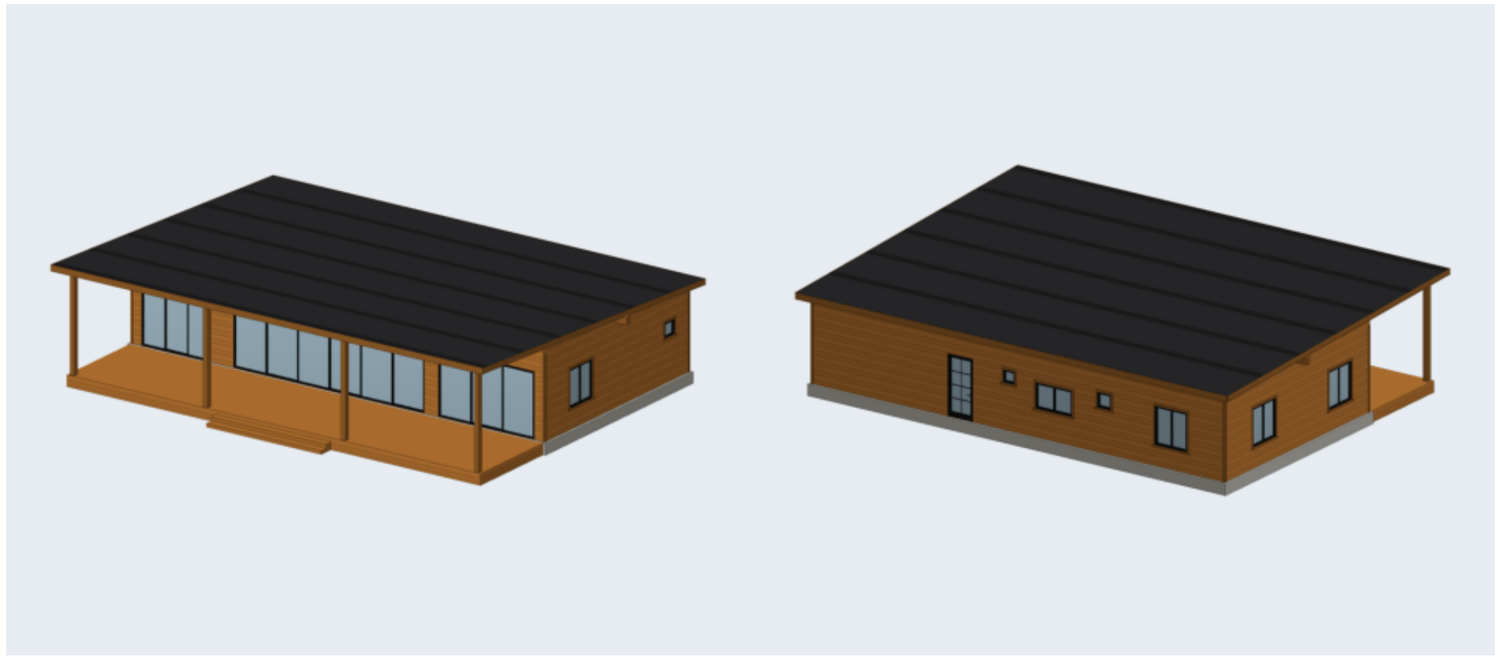

جدول المواد والألوان

الخشب / الصبغة
صبغة عسلي / سيدر

السقف (صاج معدني)
صاج رمادي غامق

الزجاج
زجاج شفاف

إطارات الشبابيك والأبواب
إطار ألمنيوم أسود


الكنار والزوايا
نفس الصبغة أغمق درجة

الصبة
خرسانة 45 سم


الدربزين: ألواح أفقية متقاربة (عصري)

تقسيم الشبابيك: بدون | الباب الرئيسي: سحاب زجاج

أنواع الدربزين المعتمدة (من مشاريع المصنع)

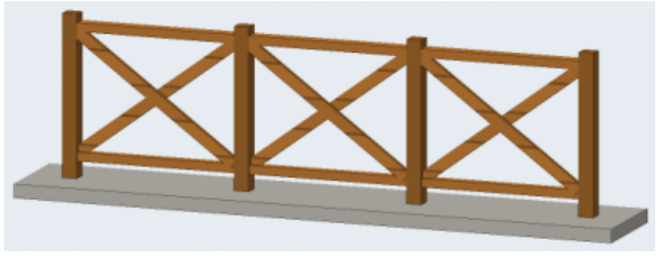

تقاطع X (صورة 5)

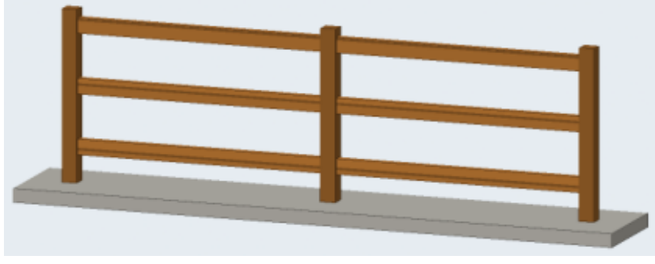

3 مرابيع أفقية (صورة 2)




قوائم رأسية متقاربة (صورة 1)

المشروع / العميل	عنوان اللوحة	المقياس	التاريخ	رقم اللوحة
فيلا دور واحد 18.00 × 9.00 م — 3 غرف نوم + صالة وطعام + تراس 4.00 × 18.00 **عميل — فيلا 18 × 9**	**المنظور والمواد**	**1:50**	**2026-11-10**	**W-01 (1/16)**

مصنع وتد الأخشاب
Watad Wood Factory


المسقط الأفقي مع الفرش

الأبعاد بالسنتيمتر - الجدران: قوائم 7×5 + تلبيس 2.5 من الجهتين (12 سم)

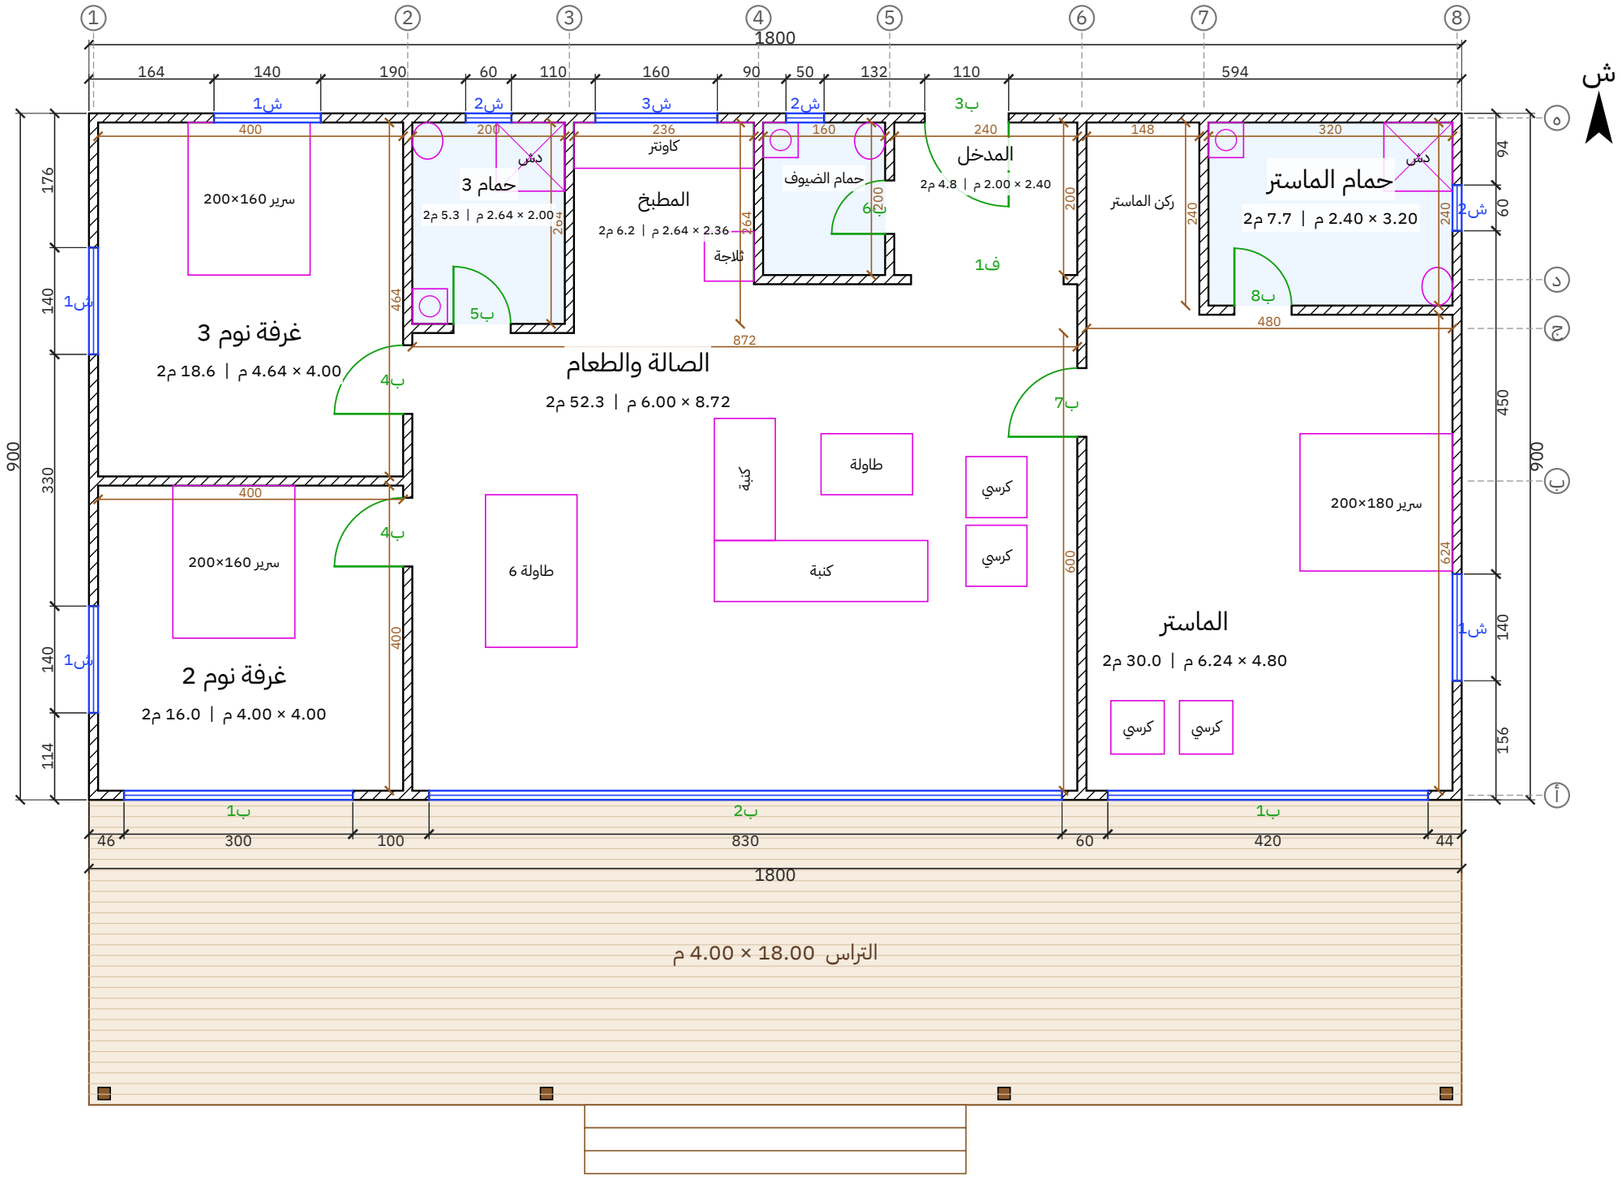


المشروع / العميل **فيلا دور واحد 18.00 × 9.00 م — 3 غرف نوم + صالة وطعام + تراس 4.00 × 18.00** **عميل — فيلا 18 × 9**	عنوان اللوحة **المسقط الأفقي**	المقياس **1:50**	التاريخ **2026-11-10**	رقم اللوحة **W-02 (2/16)**

مصنع وتد الأخشاب
Watad Wood Factory

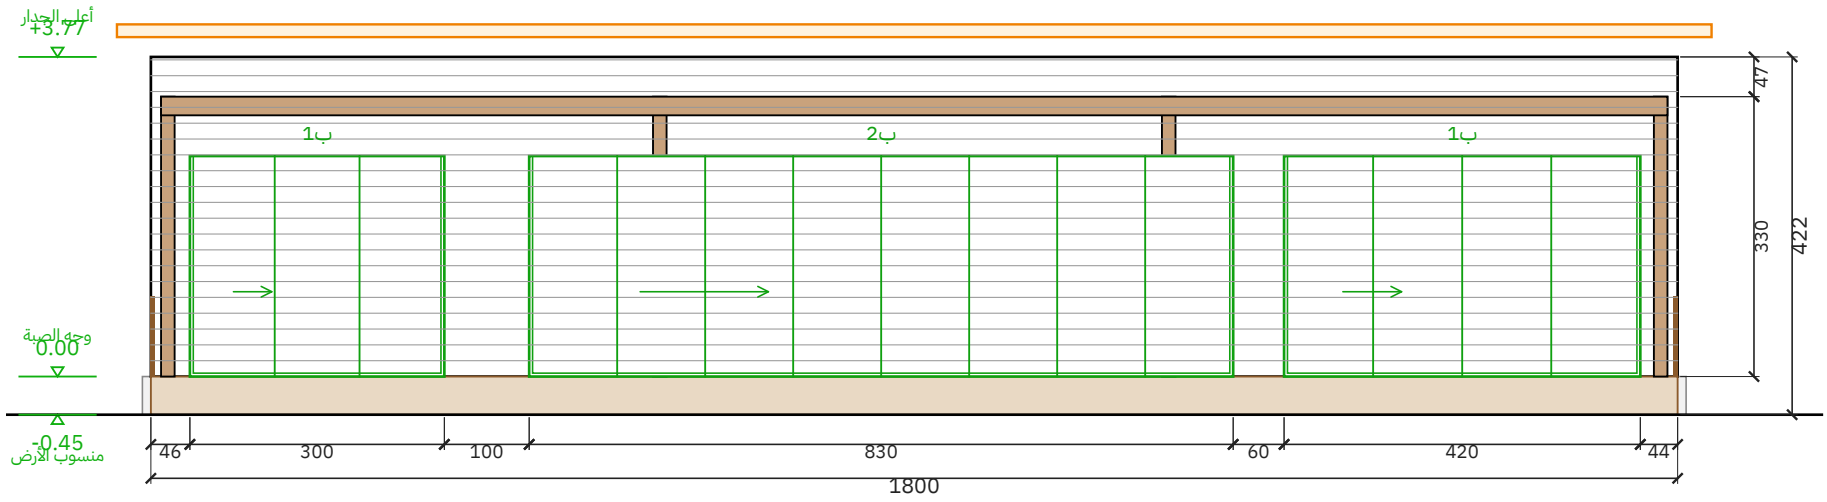

الواجهة الأمامية (على التراس)

مقياس 1:50 | الوحدة: سم

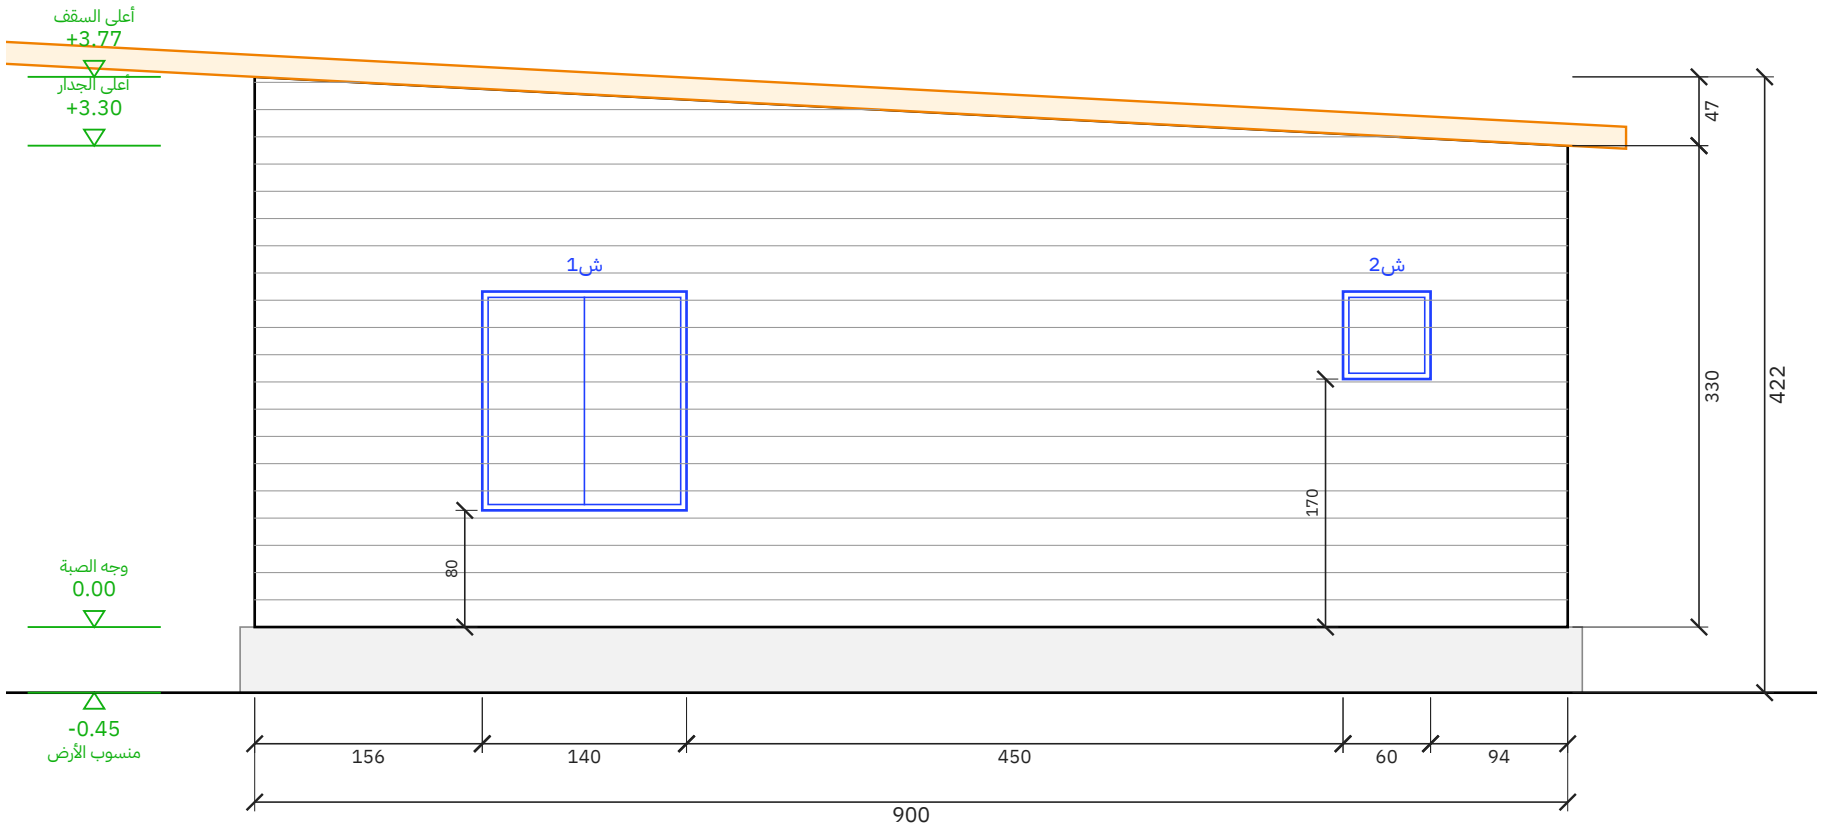


الواجهة الشرقية

مقياس 1:50 | الوحدة: سم


المشروع / العميل	عنوان اللوحة	المقياس	التاريخ	رقم اللوحة
فيلا دور واحد 18.00 × 9.00 م — 3 غرف نوم + صالة وطعام + تراس 18.00 × 4.00 عميل — فيلا 18 × 9	الواجهة الأمامية (على التراس) والواجهة الشرقية	1:50	2026-11-10	W-03 (3/16)

مصنع وتد الأخشاب
Watad Wood Factory

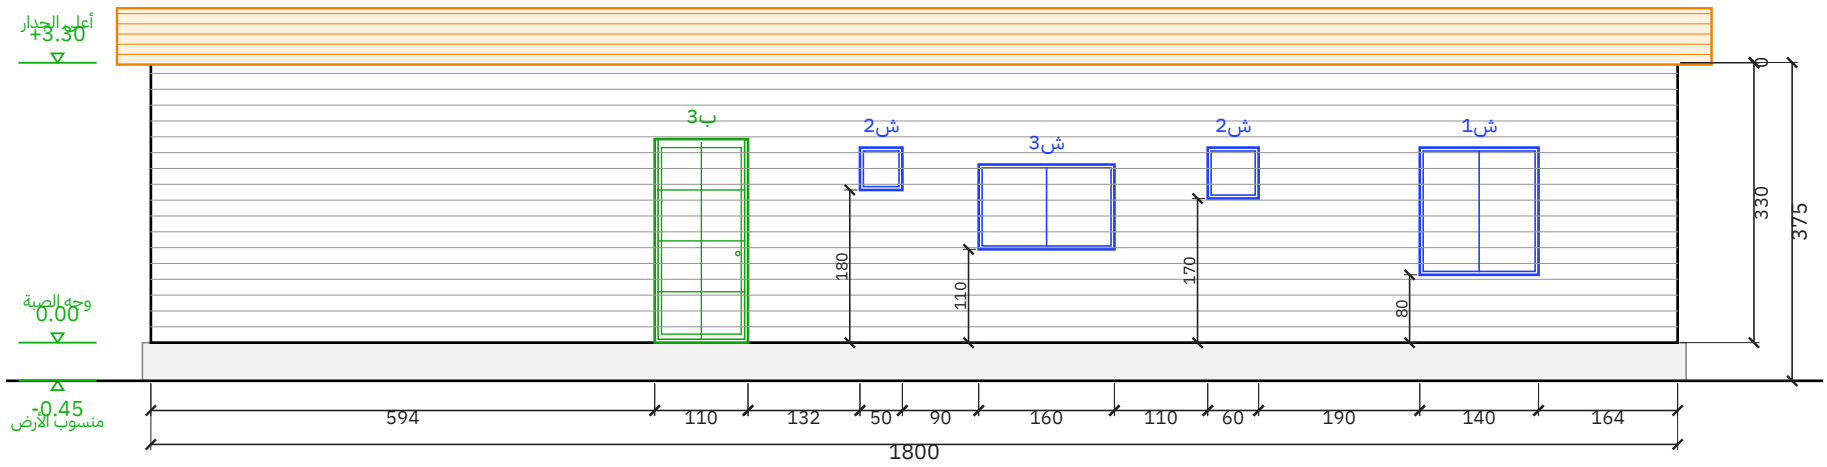

الواجهة الخلفية (المدخل)

مقياس 1:50 | الوحدة: سم

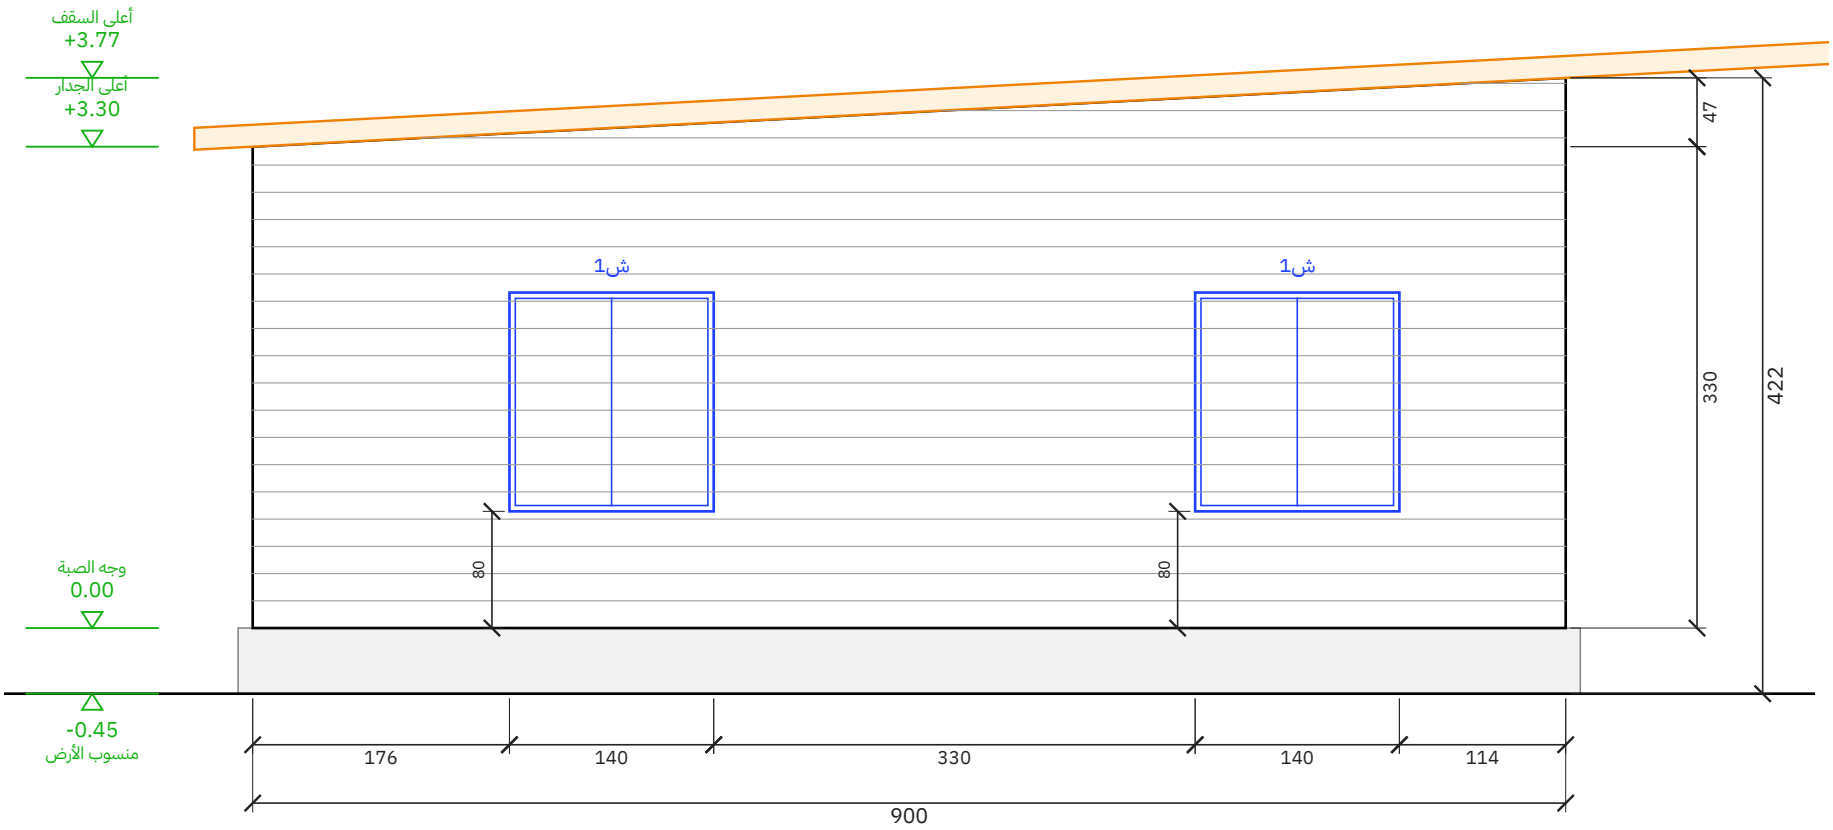

الواجهة الغربية


مقياس 1:50 | الوحدة: سم

المشروع / العميل	عنوان اللوحة	المقياس	التاريخ	رقم اللوحة
فيلا دور واحد 18.00 × 9.00 م — 3 غرف نوم + صالة وطعام + تراس 4.00 × 18.00 عميل — فيلا 18 × 9	الواجهة الخلفية (المدخل) والواجهة الغربية	1:50	2026-11-10	W-04 (4/16)

مصنع وتد الأخشاب
Watad Wood Factory


مسقط السقف (مائل باتجاه واحد)

رفرف 40 سم من كل جهة | مقياس 1:50

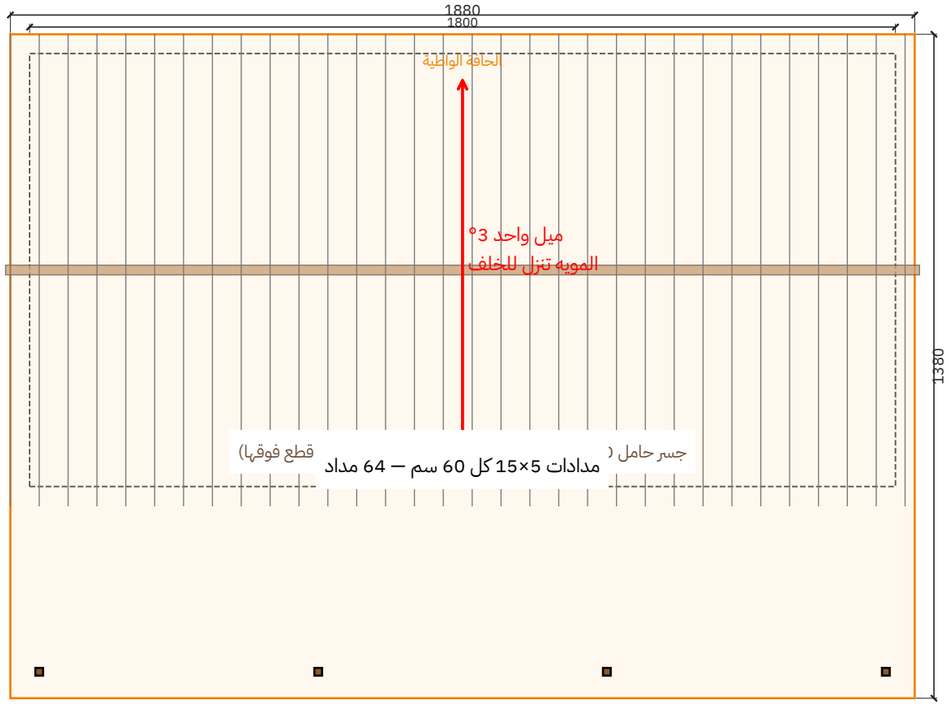


قطاع عرضي أ-أ

مقياس 1:50 | الوحدة: سم

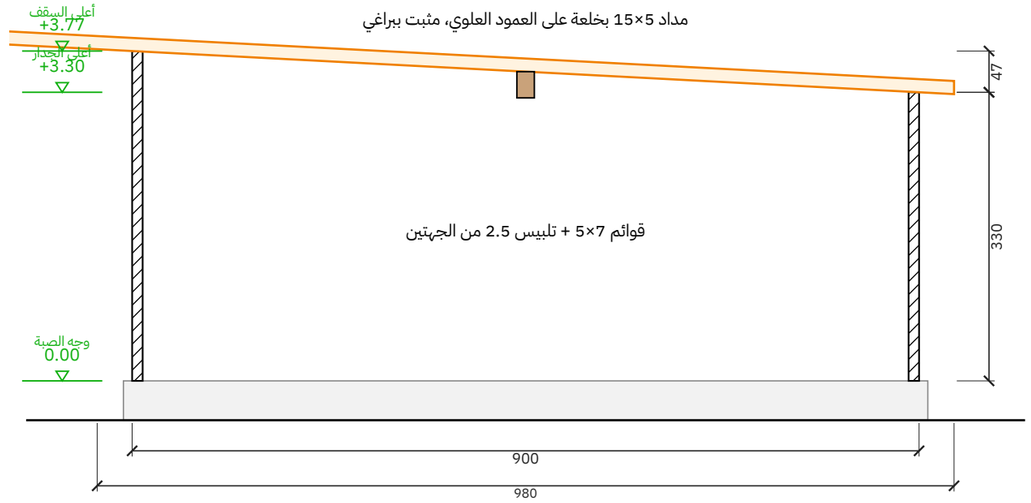

تفصيلة جلوس المداد على العلوي (1:5)

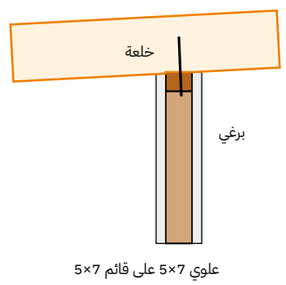

علوي 7×5 على قائم 7×5

المشروع / العميل	عنوان اللوحة	المقياس	التاريخ	رقم اللوحة
فيلا دور واحد 18.00 × 9.00 م — 3 غرف نوم + صالة وطعام + تراس 4.00 × 18.00 **عميل — فيلا 18 × 9**	**مسقط السقف والقطاع**	**1:50**	**2026-11-10**	**W-05 (5/16)**

مصنع وتد الأخشاب
Watad Wood Factory

جدول مقاسات الأبواب والشبابيك

مقاس الفتحة الصافي في الجدار - الوحدة: سم

الرمز	النوع	العرض (سم)	الارتفاع (سم)	ارتفاع الجلسة (سم)	العدد	الموقع
ب1	باب	300	260	-	1	الأمامية (على التراس)
ب1	باب	420	260	-	1	الأمامية (على التراس)
ب2	باب	830	260	-	1	الأمامية (على التراس)
ب3	باب	110	240	-	1	الخلفية (المدخل)
ب4	باب	90	220	-	2	غرفة نوم 2 - غرفة نوم 3
ب5	باب	75	210	-	1	حمام 3
ب6	باب	70	210	-	1	دورة مياه الضيوف
ب7	باب	90	220	-	1	الماستر
ب8	باب	75	210	-	1	حمام الماستر
ف1	باب	200	240	-	1	فتحة المدخل على الصالة
ش1	شباك	140	150	80	4	الشرقية - الخلفية (المدخل) - الغربية 2
ش2	شباك	60	60	170	2	الشرقية - الخلفية (المدخل)
ش2	شباك	50	50	180	1	الخلفية (المدخل)
ش3	شباك	160	100	110	1	الخلفية (المدخل)

الإجمالي: أبواب 11 - شبابيك 8

جدول المساحات وبيانات المشروع


بيانات المشروع

البند	البيان
المشروع	فيلا دور واحد 18.00 × 9.00 م — 3 غرف نوم + صالة وطعام + تراس 18.00 × 4.00
العميل	عميل — فيلا 18 × 9
الموقع	—
الاستخدام	سكني
التاريخ	2026-11-10
نظام البناء	هيكل خشب 5×7 + تلبيس 2.5 سم من الجهتين
السقف	مائل باتجاه واحد 3° — صاج معدني + عزل مائي


جدول المساحات

م	الفراغ	الأبعاد (م)	المساحة (م2)
1	غرفة نوم 2	4.00 × 4.00	16.00
2	غرفة نوم 3	4.00 × 4.64	18.56
3	حمام 3	2.00 × 2.64	5.28
4	الصالة والطعام	8.72 × 6.00	52.32
5	المطبخ	2.36 × 2.64	6.23
6	حمام الضيوف	1.60 × 2.00	3.20
7	المدخل	2.40 × 2.00	4.80
8	الماستر	4.80 × 6.24	29.95
9	ركن الماستر	1.48 × 2.40	3.55
10	حمام الماستر	3.20 × 2.40	7.68
	المساحة الصافية الداخلية		**147.57**
	التراس المسقوف	**18.00 × 4.00**	**72.00**
	المساحة الإجمالية المبنية	**18.00 × 9.00**	**162.00**
	المساحة الكلية (المبنية + التراس)		**234.00**

تأطير جدار جنوب — الطول 1788 سم، الارتفاع 377 سم

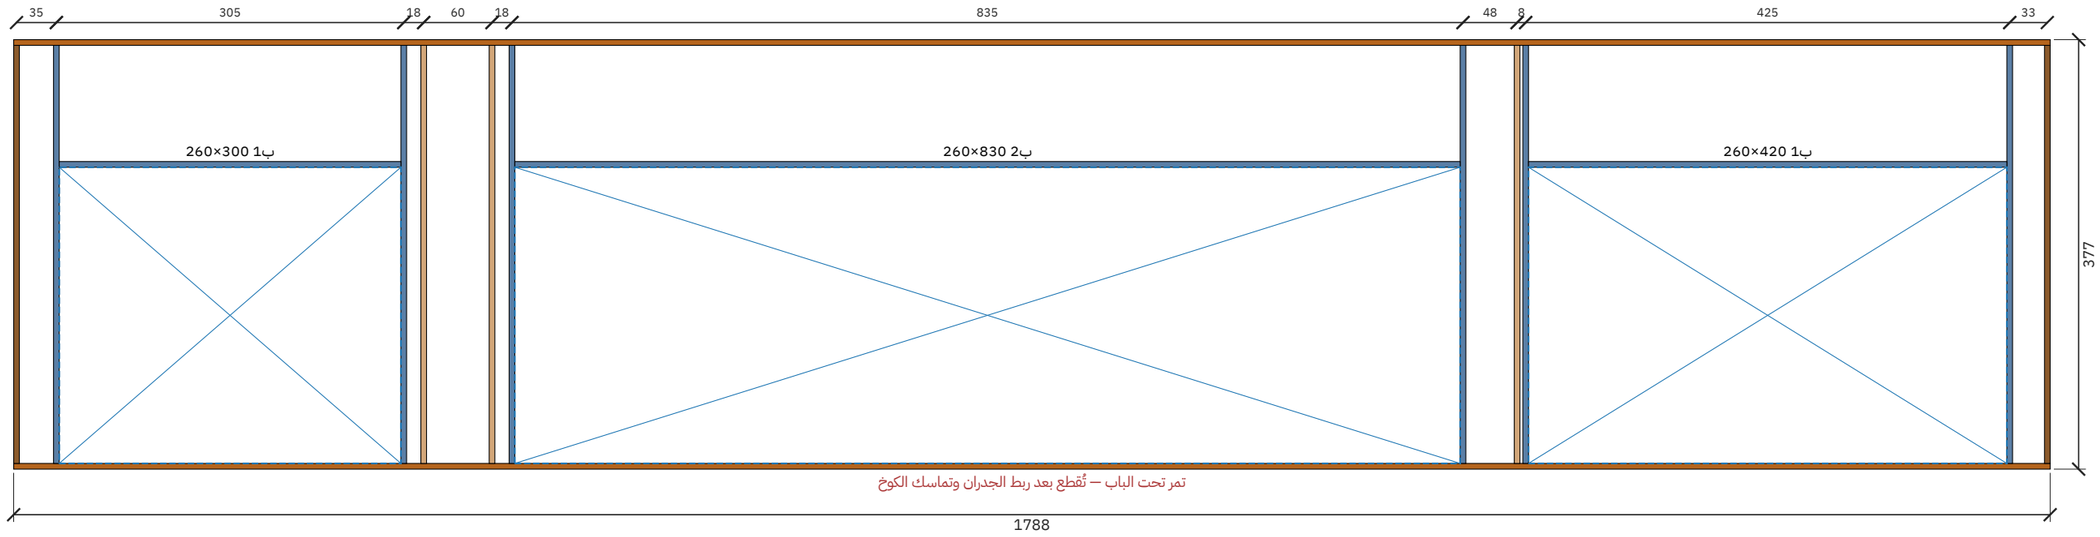

تأطير جدار شرق — الطول 888 سم، الارتفاع 330 سم

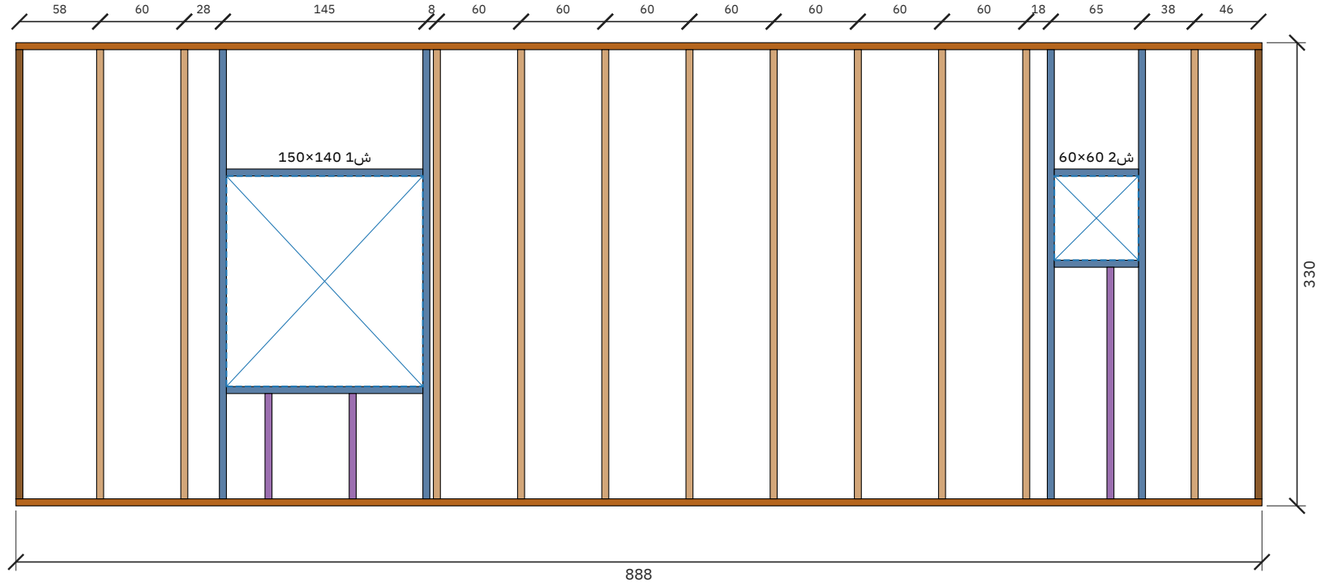


قاعدة سفلية | علوي | عمود | عمود زاوية | جنب فتحة | رأس فتحة | جلسة شباك | عمود قصير


المشروع / العميل	عنوان اللوحة	المقياس	التاريخ	رقم اللوحة
فيلا دور واحد 18.00 × 9.00 م — 3 غرف نوم + صالة وطعام + تراس 18.00 × 4.00 **عميل — فيلا 18 × 9**	**لوحات التأطير (للورشة)**	—	**2026-11-10**	**W-08 (8/16)**

مصنع وتد الأخشاب
Watad Wood Factory

تأطير جدار شمال — الطول 1788 سم، الارتفاع 330 سم

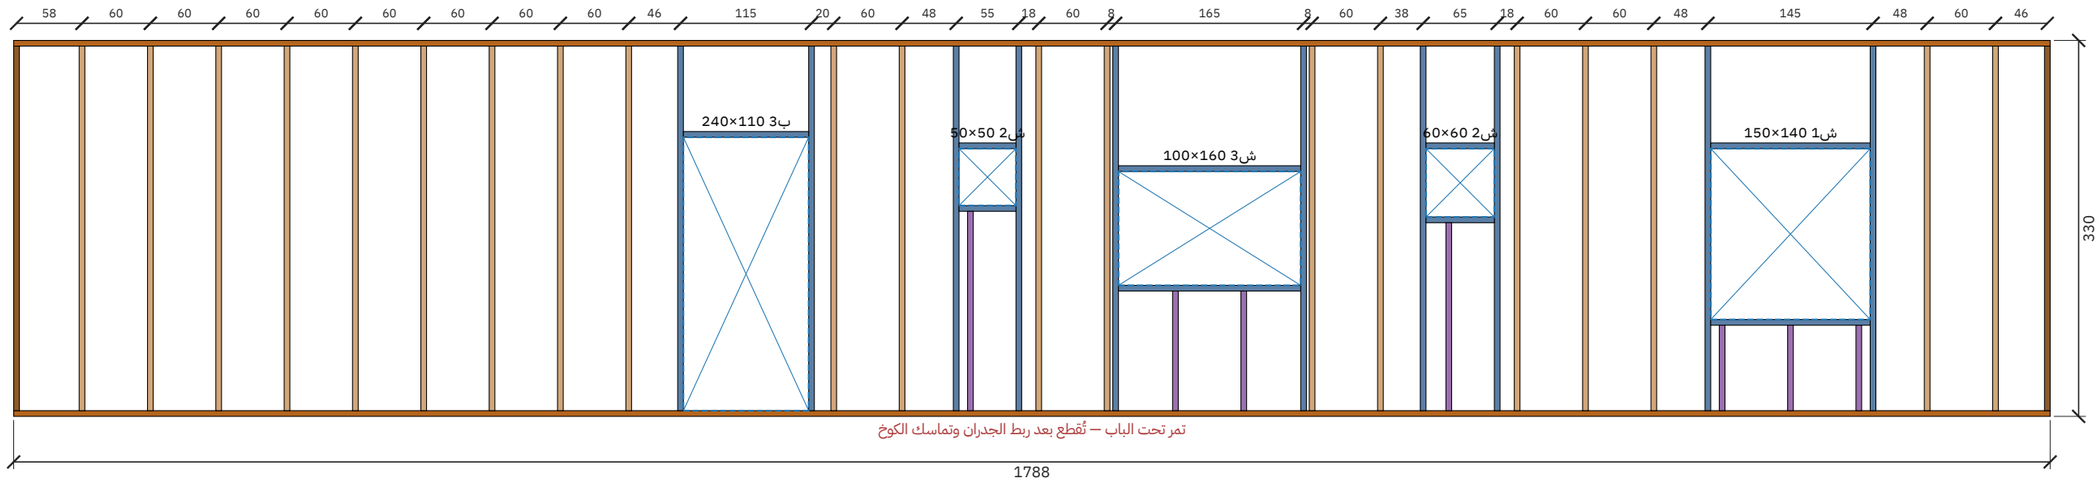

تأطير جدار غرب — الطول 888 سم، الارتفاع 330 سم

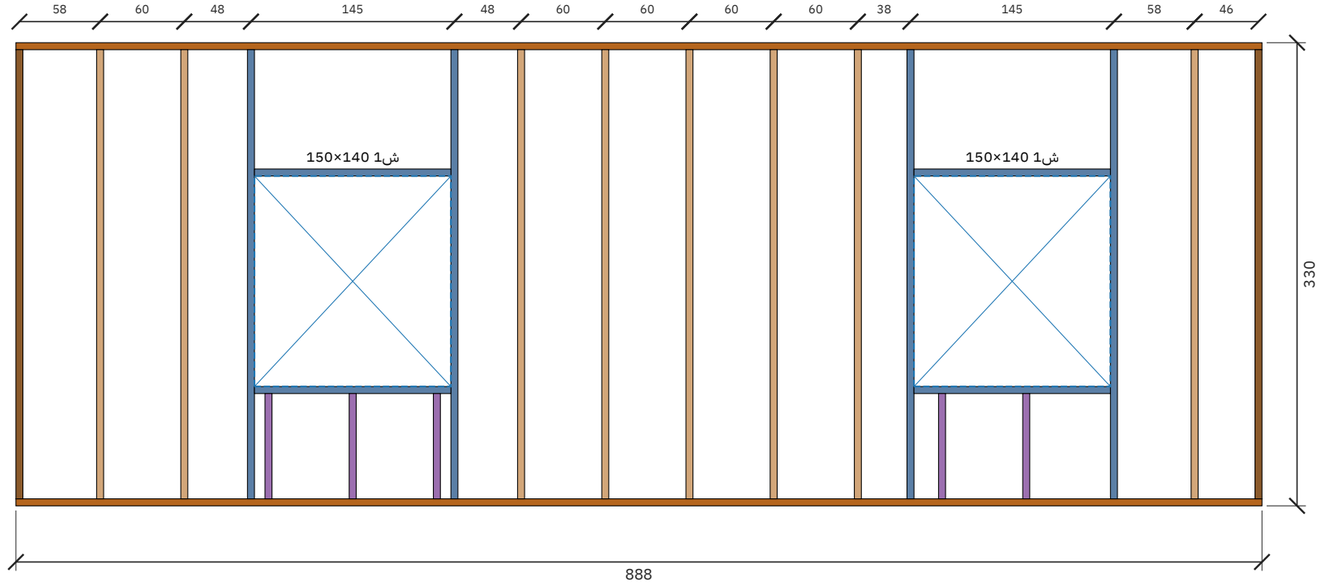


قاعدة سفلية | علوي | عمود | عمود زاوية | جنب فتحة | رأس فتحة | جلسة شباك | عمود قصير


المشروع / العميل	عنوان اللوحة	المقياس	التاريخ	رقم اللوحة
فيلا دور واحد 18.00 × 9.00 م — 3 غرف نوم + صالة وطعام + تراس 4.00 × 18.00 **عميل — فيلا 18 × 9**	**لوحات التأطير (للورشة)**	—	**2026-11-10**	**W-09 (9/16)**

مصنع وتد الأخشاب
Watad Wood Factory

تأطير جدار جدار الغرف — الصالة — الطول 888 سم، الارتفاع 330 سم (داخلي)

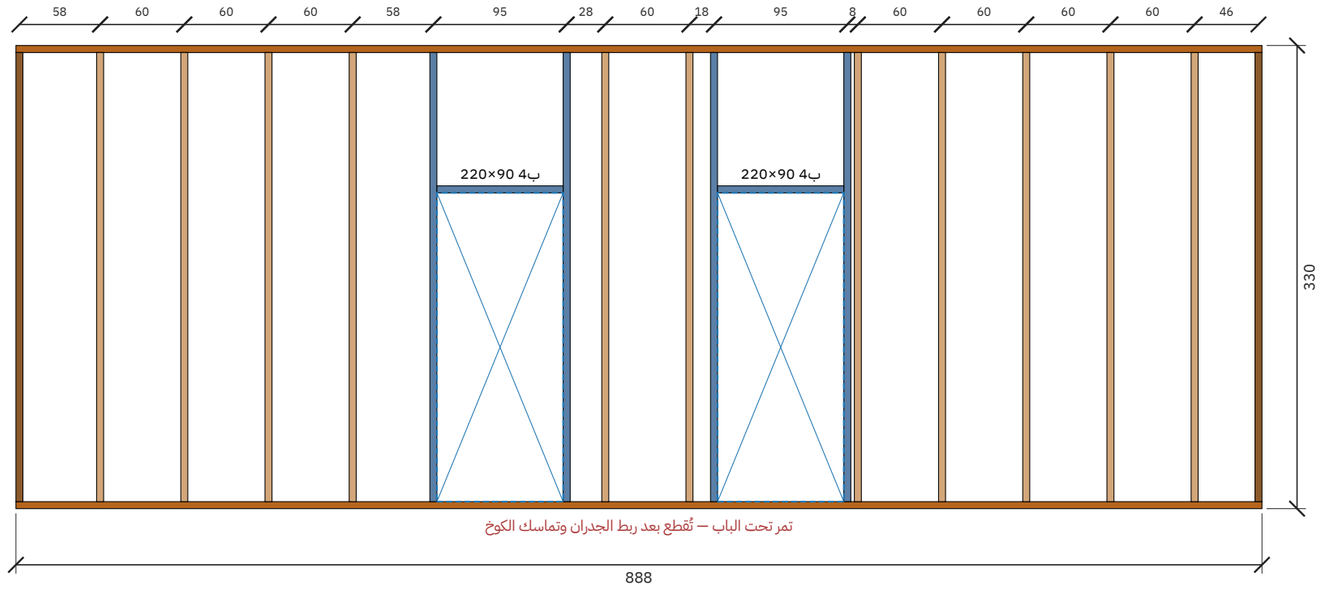

تأطير جدار جدار بين الغرفتين — الطول 412 سم، الارتفاع 330 سم (داخلي)

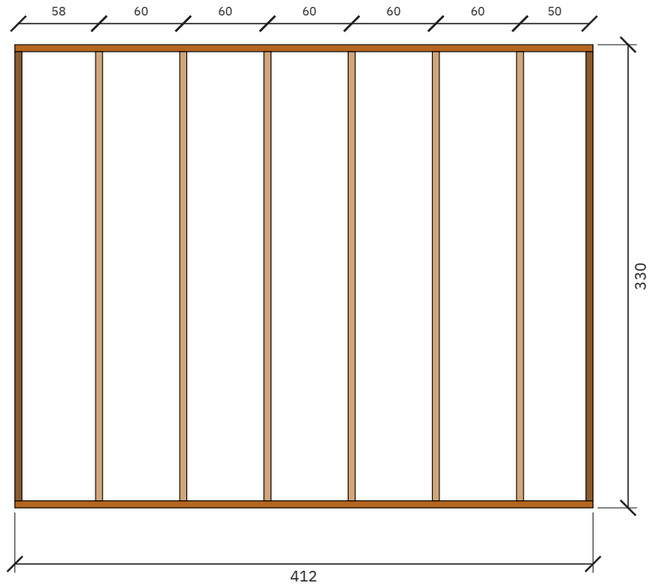


قاعدة سفلية | علوي | عمود | عمود زاوية | جنب فتحة | رأس فتحة | جلسة شباك | عمود قصير


المشروع / العميل	عنوان اللوحة	المقياس	التاريخ	رقم اللوحة
فيلا دور واحد 18.00 × 9.00 م — 3 غرف نوم + صالة وطعام + تراس 18.00 × 4.00 **عميل — فيلا 18 × 9**	**لوحات التأطير (للورشة)**	—	**2026-11-10**	**W-10 (10/16)**

مصنع وتد الأخشاب
Watad Wood Factory

تأطير جدار جدار حمام 3 — الطول 212 سم، الارتفاع 330 سم (داخلي)

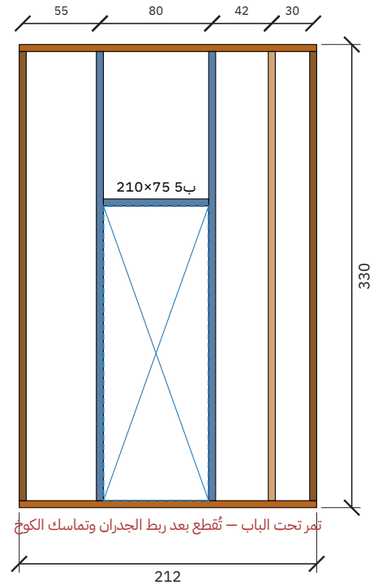


تأطير جدار جدار حمام 3 — المطبخ — الطول 276 سم، الارتفاع 330 سم (داخلي)

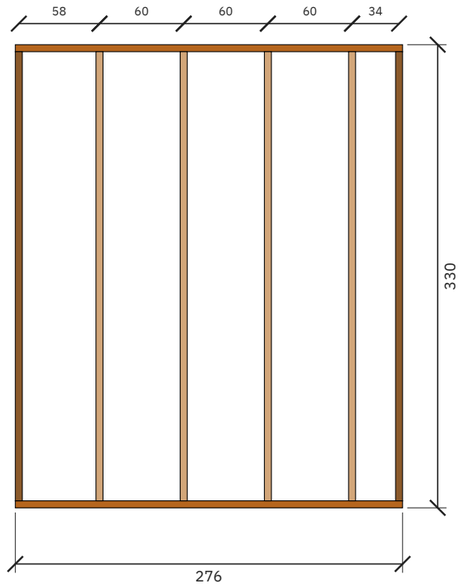


قاعدة سفلية | علوي | عمود | عمود زاوية | جنب فتحة | رأس فتحة | جلسة شباك | عمود قصير

مصنع وتد الأخشاب Watad Wood Factory	المشروع / العميل **فيلا دور واحد 18.00 × 9.00 م — 3 غرف نوم + صالة وطعام + تراس 4.00 × 18.00** **عميل — فيلا 18 × 9**	عنوان اللوحة **لوحات التأطير (للورشة)**	المقياس **—**	التاريخ **2026-11-10**	رقم اللوحة **W-11 (11/16)**

تأطير جدار جدار المطبخ — الضيوف — الطول 212 سم، الارتفاع 330 سم (داخلي)

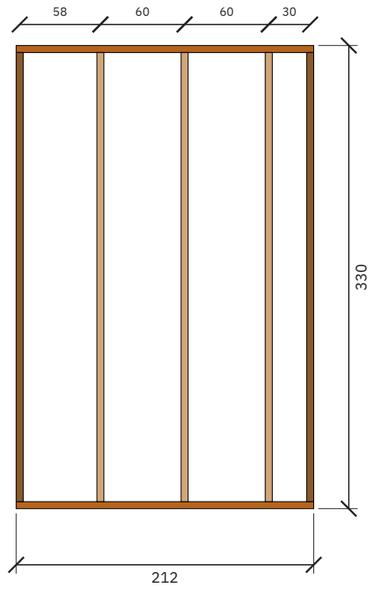


تأطير جدار جدار دورة مياه الضيوف — المدخل — الطول 212 سم، الارتفاع 330 سم (داخلي)

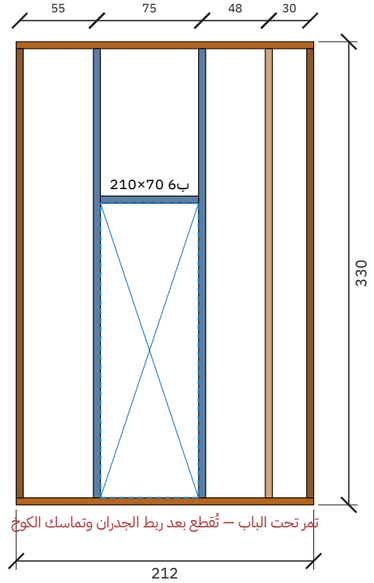


قاعدة سفلية | علوي | عمود | عمود زاوية | جنب فتحة | رأس فتحة | جلسة شباك | عمود قصير

مصنع وتد الأخشاب Watad Wood Factory	المشروع / العميل فيلا دور واحد 18.00 × 9.00 م — 3 غرف نوم + صالة وطعام + تراس 18.00 × 4.00 عميل — فيلا 18 × 9	عنوان اللوحة لوحات التأطير (للورشة)	المقياس —	التاريخ 2026-11-10	رقم اللوحة W-12 (12/16)

تأطير جدار جدار المدخل — الصالة — الطول 424 سم، الارتفاع 330 سم (داخلي)

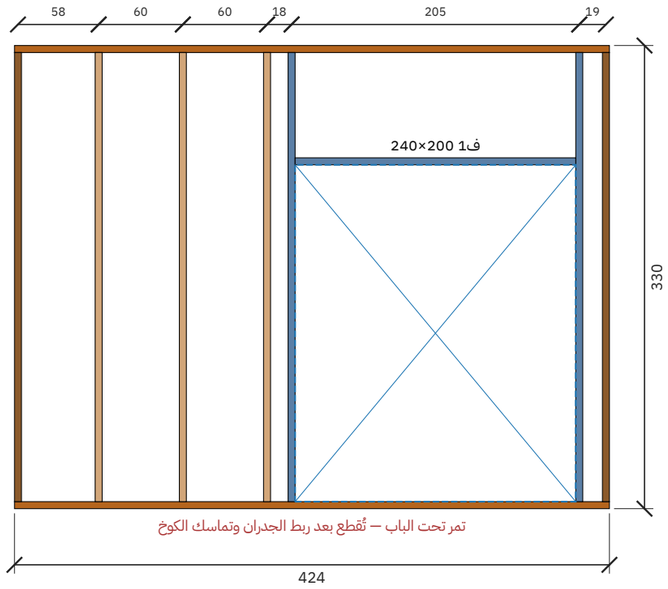


تأطير جدار جدار الماستر — الصالة — الطول 888 سم، الارتفاع 330 سم (داخلي)

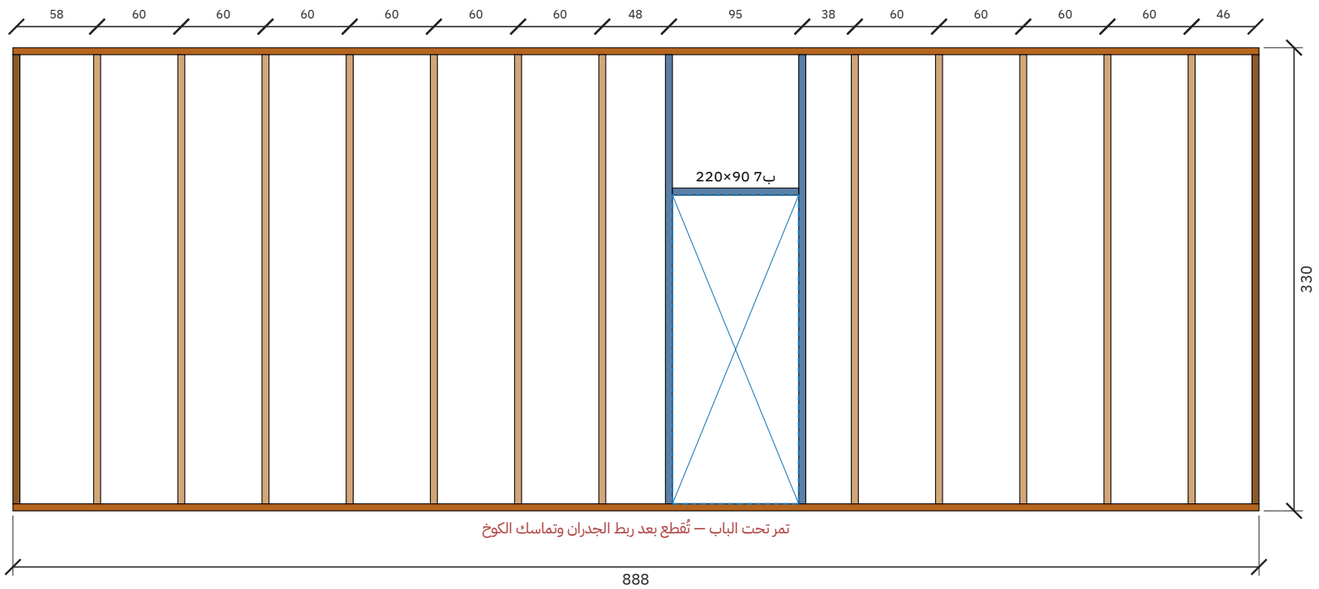


قاعدة سفلية | علوي | عمود | عمود زاوية | جنب فتحة | رأس فتحة | جلسة شباك | عمود قصير

مصنع وتد الأخشاب Watad Wood Factory	المشروع / العميل **فيلا دور واحد 18.00 × 9.00 م — 3 غرف نوم + صالة وطعام + تراس 18.00 × 4.00** **عميل — فيلا 18 × 9**	عنوان اللوحة **لوحات التأطير (للورشة)**	المقياس **—**	التاريخ **2026-11-10**	رقم اللوحة **W-13 (13/16)**

تأطير جدار جدار حمام الماستر — الطول 332 سم، الارتفاع 330 سم (داخلي)

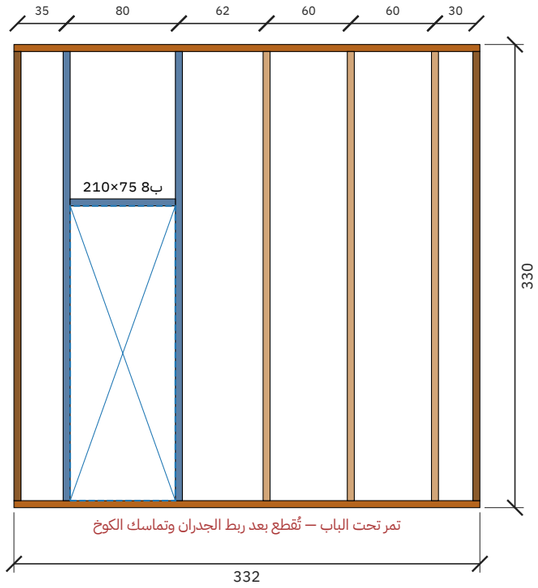

تأطير جدار جدار الحمام — المخزن — الطول 252 سم، الارتفاع 330 سم (داخلي)

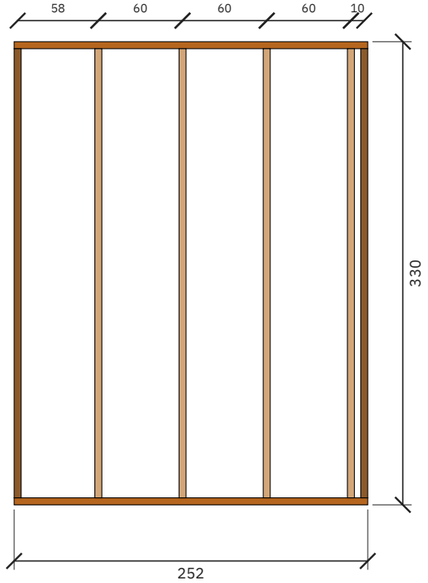

قاعدة سفلية | علوي | عمود | عمود زاوية | جنب فتحة | رأس فتحة | جلسة شباك | عمود قصير

المشروع / العميل	عنوان اللوحة	المقياس	التاريخ	رقم اللوحة
فيلا دور واحد 18.00 × 9.00 م — 3 غرف نوم + صالة وطعام + تراس 18.00 × 4.00 **عميل — فيلا 18 × 9**	**لوحات التأطير (للورشة)**	—	**2026-11-10**	**W-14 (14/16)**

مصنع وتد الأخشاب
Watad Wood Factory

جدول الكميات وخطة تقطيع الطبليات

البند	القيمة
الارتفاع المطلوب / المعتمد	330 / 330 سم
السقف	مائل باتجاه واحد 3° — أعلى نقطة 377 سم من وجه الصبة
المدادات 5×15	64 مداد (32 خط × قطعتين موصولة فوق الجسر الحامل بتراكب 60 سم) × حتى 521 سم — من طبلية None
طبليات الطريقة الأولى (مداد + عمود)	64 طبلية × 520 سم
طبليات الطريقة الثانية (3 أعمدة)	49 طبلية × 320 سم
إجمالي الطبليات 5×22.5	113
إجمالي قطع 5×7	226
قائمة تقطيع 5×7	1788سم×4 | 888سم×8 | 830سم×1 | 424سم×2 | 420سم×1 | 412سم×2 | 367سم×11 | 332سم×2 | 320سم×145
	300سم×1 | 276سم×2 | 252سم×2 | 212سم×6 | 200سم×1 | 175سم×1 | 165سم×2 | 160سم×2 | 140سم×8
ألواح تلبيس 2.5 سم	677 لوح × 400 سم (مجموع الصفوف 2239.4 م، 28 وجه)
أسمنت بورد 12 مم (122×244)	56 لوح (داخل دورات المياه)
العزل	350 لوح فوم صخري 80
الصبة	يجهزها العميل — 20 سم، مفرغة تحت دورات المياه

مراجعة التصميم مقابل قواعد المصنع

النوع	البند	التفاصيل	المقترح
ملاحظة	بحر المدادات	أطول بحر بدون جدار داخلي يحمل المداد: جهة أ: 900 سم. يحتاج رقم المصنع لأقصى بحر مسموح لتحديد المدادات اللي تُقوّى 20×5.	
ملاحظة	الصبة والدرج	ارتفاع الصبة 45 سم ← 3 درجة بقائمة 15.0 سم.	
ملاحظة	مناسيب رؤوس الفتحات	رؤوس الأبواب والشبابيك على مناسيب مختلفة: 210، 220، 230، 240، 260 سم.	
خطأ	طول المداد	طول المداد 521 سم أطول من كل الأطوال المتوفرة — يحتاج قرار (للمائل: roof.splice على جدار داخلي حامل)	
تنبيه	ميل سقف خفيف (بموافقة المصنع)	ميل 3° أقل من 20° — يصرّف باتجاه واحد بس يحتاج تغطية صاج معدني (مو قرميد) وعزل مائي تحت الصاج ووصلات مختومة.	صاج معدني بطول واحد من الحافة العالية للواطية بدون وصلات عرضية.
سؤال	يحتاج تأكيد	أقصى بحر للمداد بدون جدار داخلي قبل إضافة تقوية 7×5 (مداد 20×5)؟	
سؤال	يحتاج تأكيد	التغطية الصافية للوح التلبيس بعد التعشيق (مستنتجة مؤقتاً 18.67 سم من 280/15)؟	
سؤال	يحتاج تأكيد	هل يوضع أعمدة قصيرة فوق رأس الشباك/الباب إلى العلوي؟	
سؤال	يحتاج تأكيد	مكان الوصلة في القاعدة والعلوي إذا الجدار أطول من الطبلية؟	