

# المسقط الأفقي مع الفرش

الأبعاد بالسنتيمتر - الجدران: قوائم 7×5 + تلبيس 2.5 من الجهتين (12 سم)

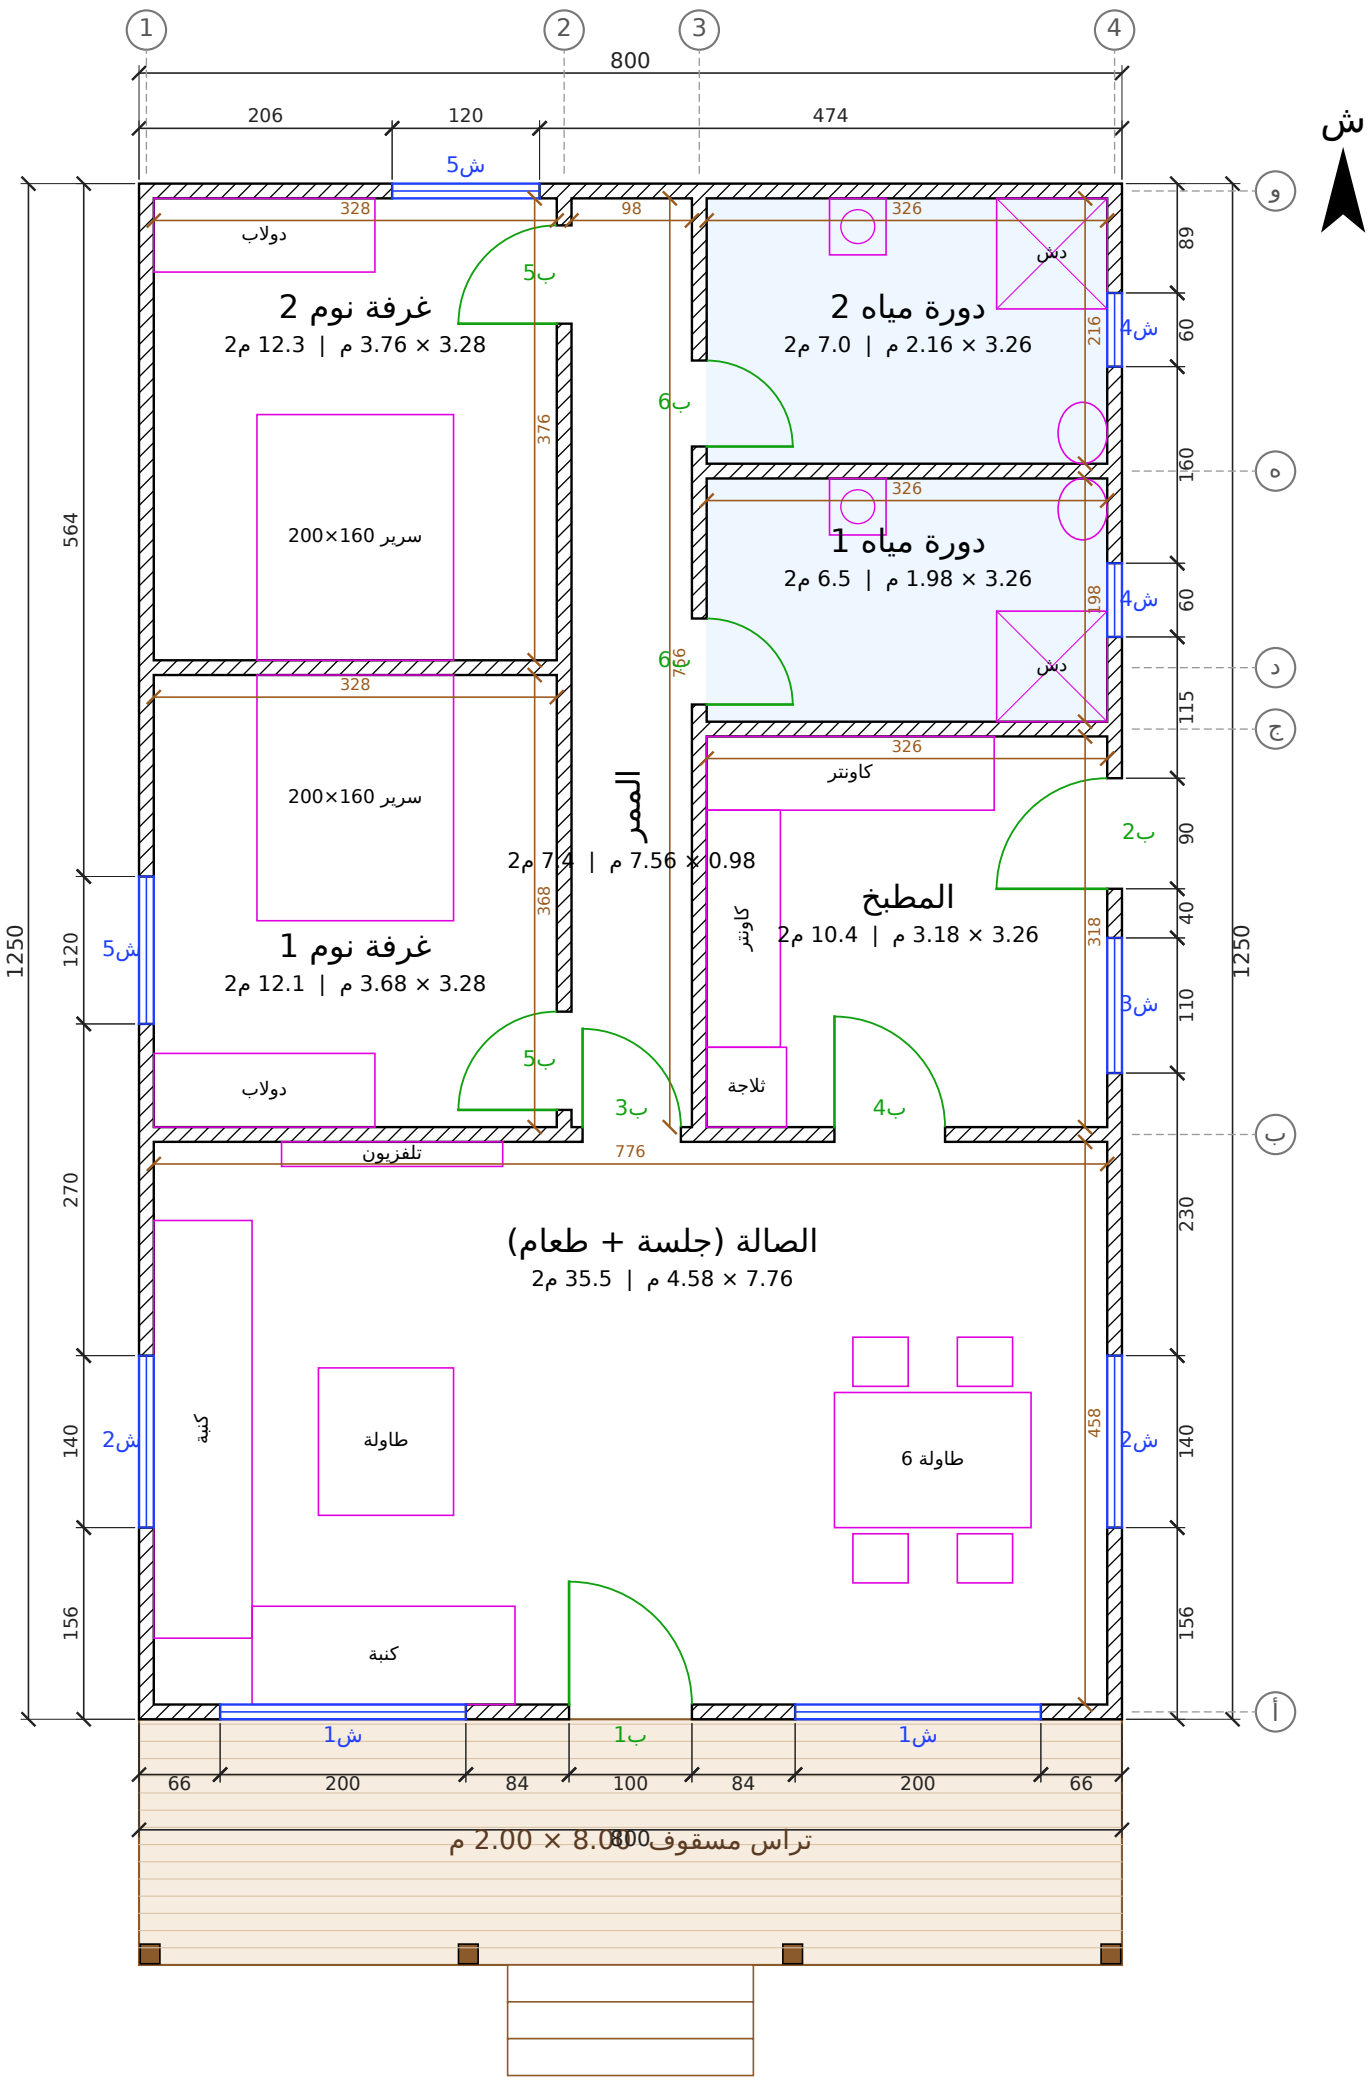



| المشروع / العميل | عنوان اللوحة | المقياس | التاريخ | رقم اللوحة |
|---|---|---|---|---|
| **مصنع وتد الأخشاب** Watad Wood Factory<br>**استراحة — غرفتين + صالة كبيرة — 8.00 × 12.50 = 100 م²**<br>**عميل — استراحة مكة** | **المسقط الأفقي** | **1:50** | **2026-10-21** | **A-01 (1/9)** |

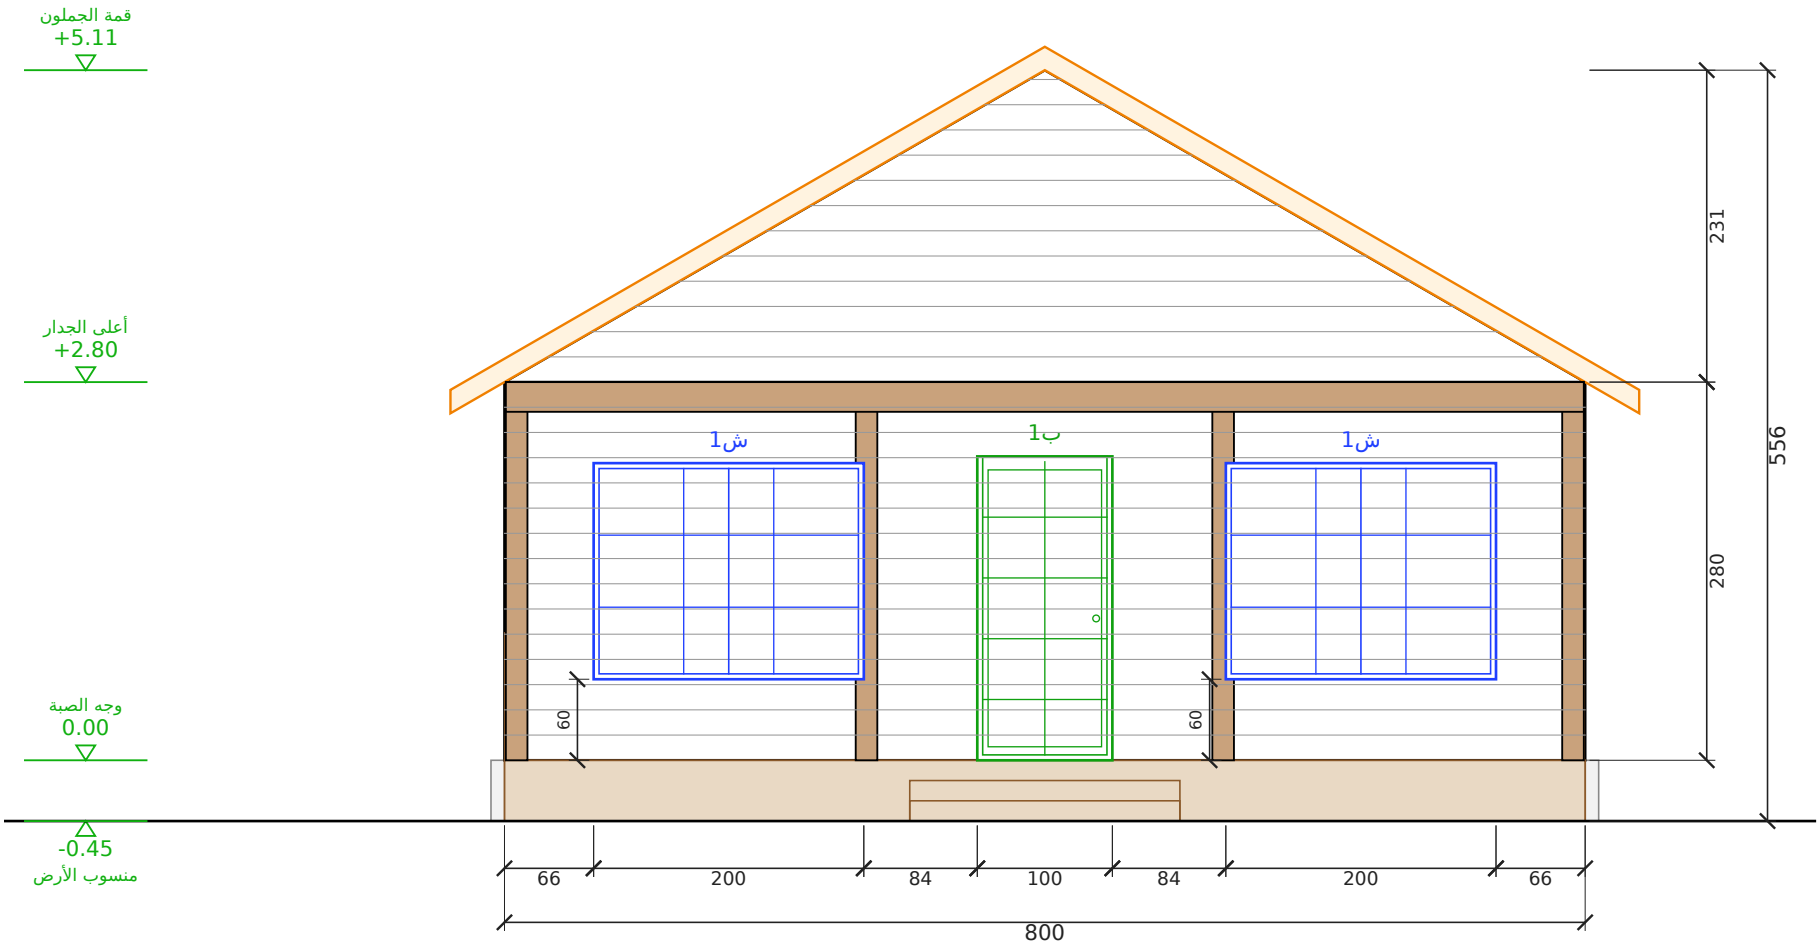


## الواجهة الأمامية

مقياس 1:50 | الوحدة: سم

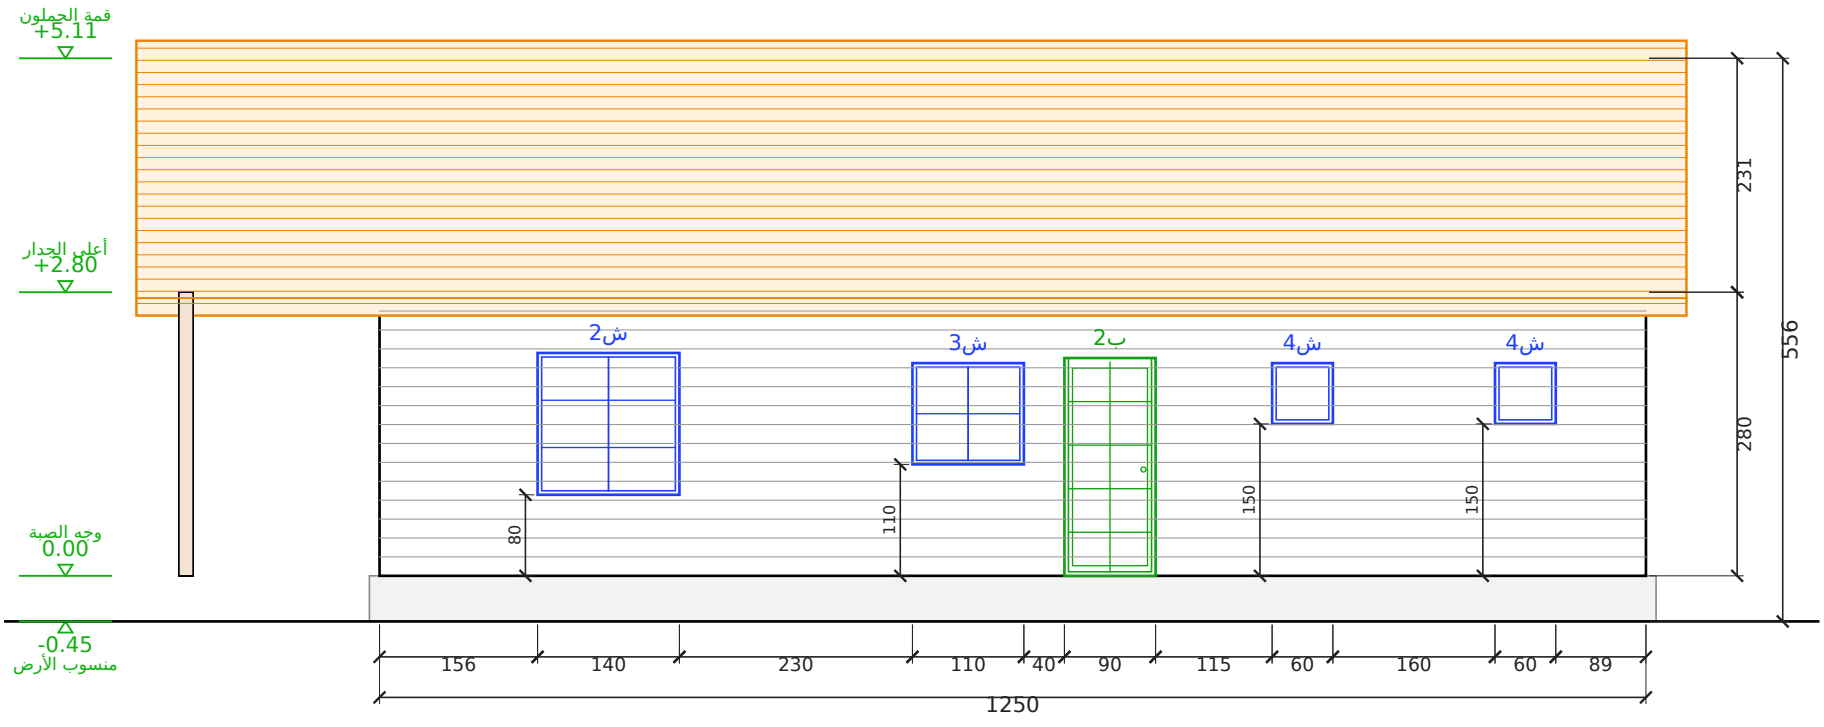



## الواجهة الشرقية

مقياس 1:50 | الوحدة: سم


| المشروع / العميل | عنوان اللوحة | المقياس | التاريخ | رقم اللوحة |
|---|---|---|---|---|
| استراحة — غرفتين + صالة كبيرة — 8.00 × 12.50 = 100 م²<br>عميل — استراحة مكة | الواجهة الأمامية والواجهة الشرقية | 1:50 | 2026-10-21 | A-02 (2/9) |

مصنع وتد الأخشاب
Watad Wood Factory

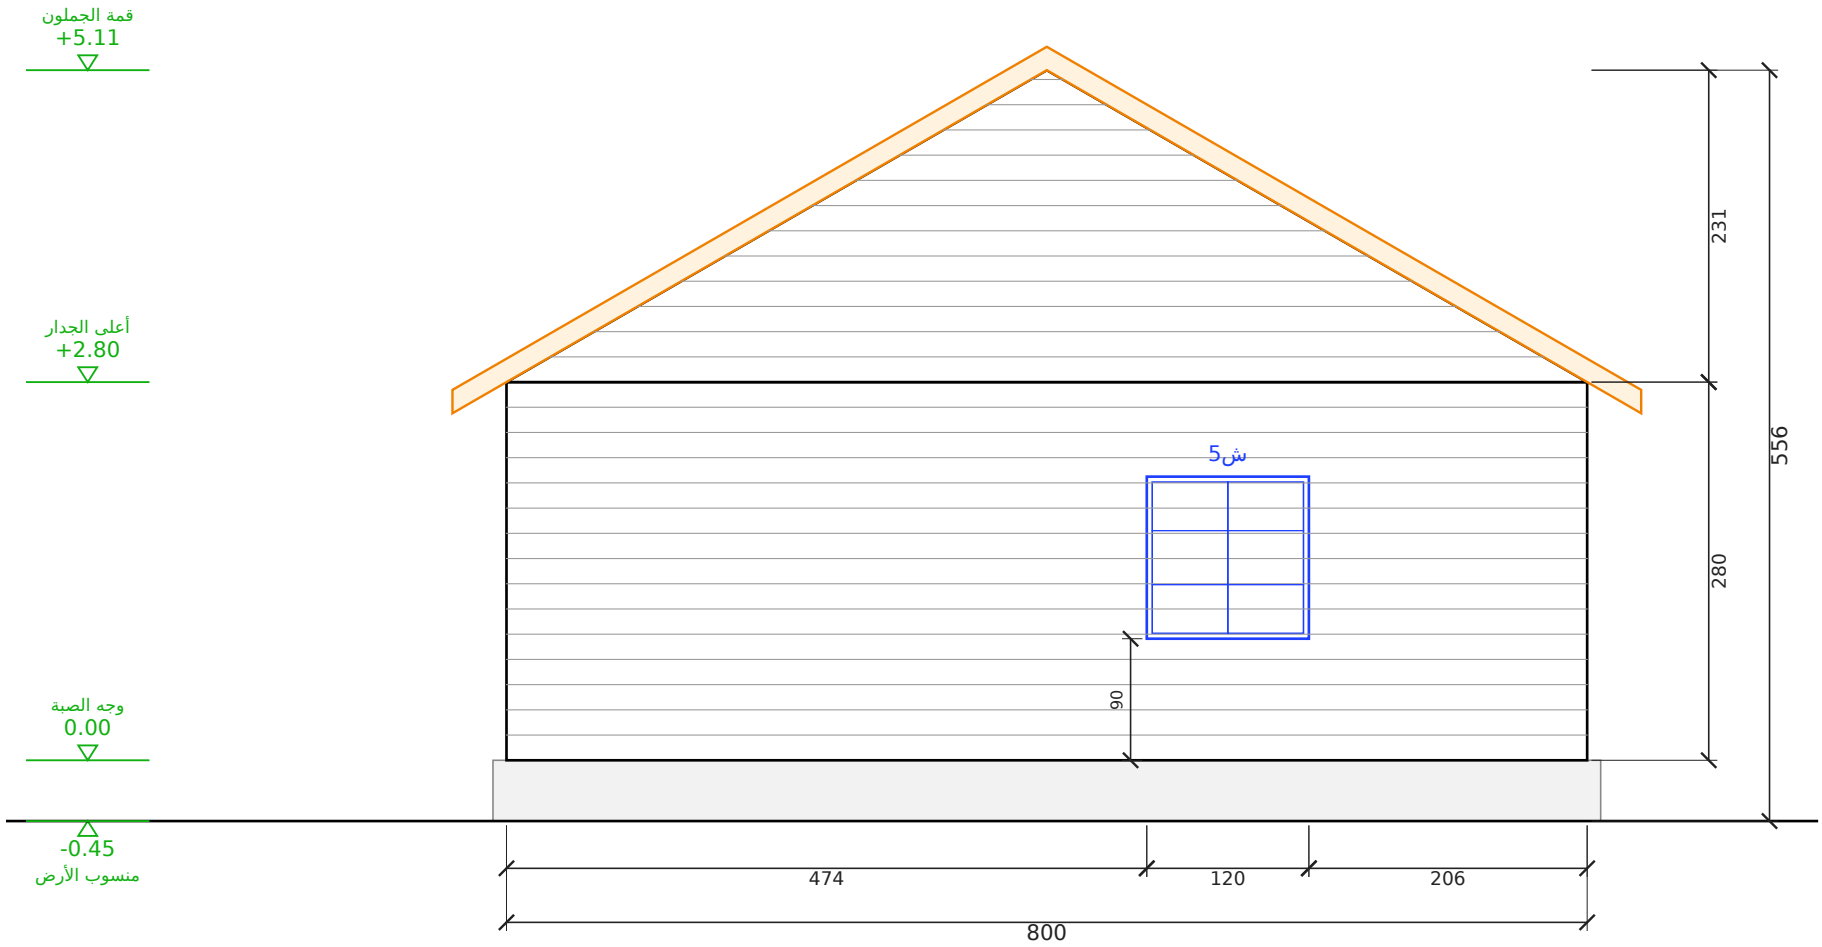


## الواجهة الخلفية

مقياس 1:50 | الوحدة: سم

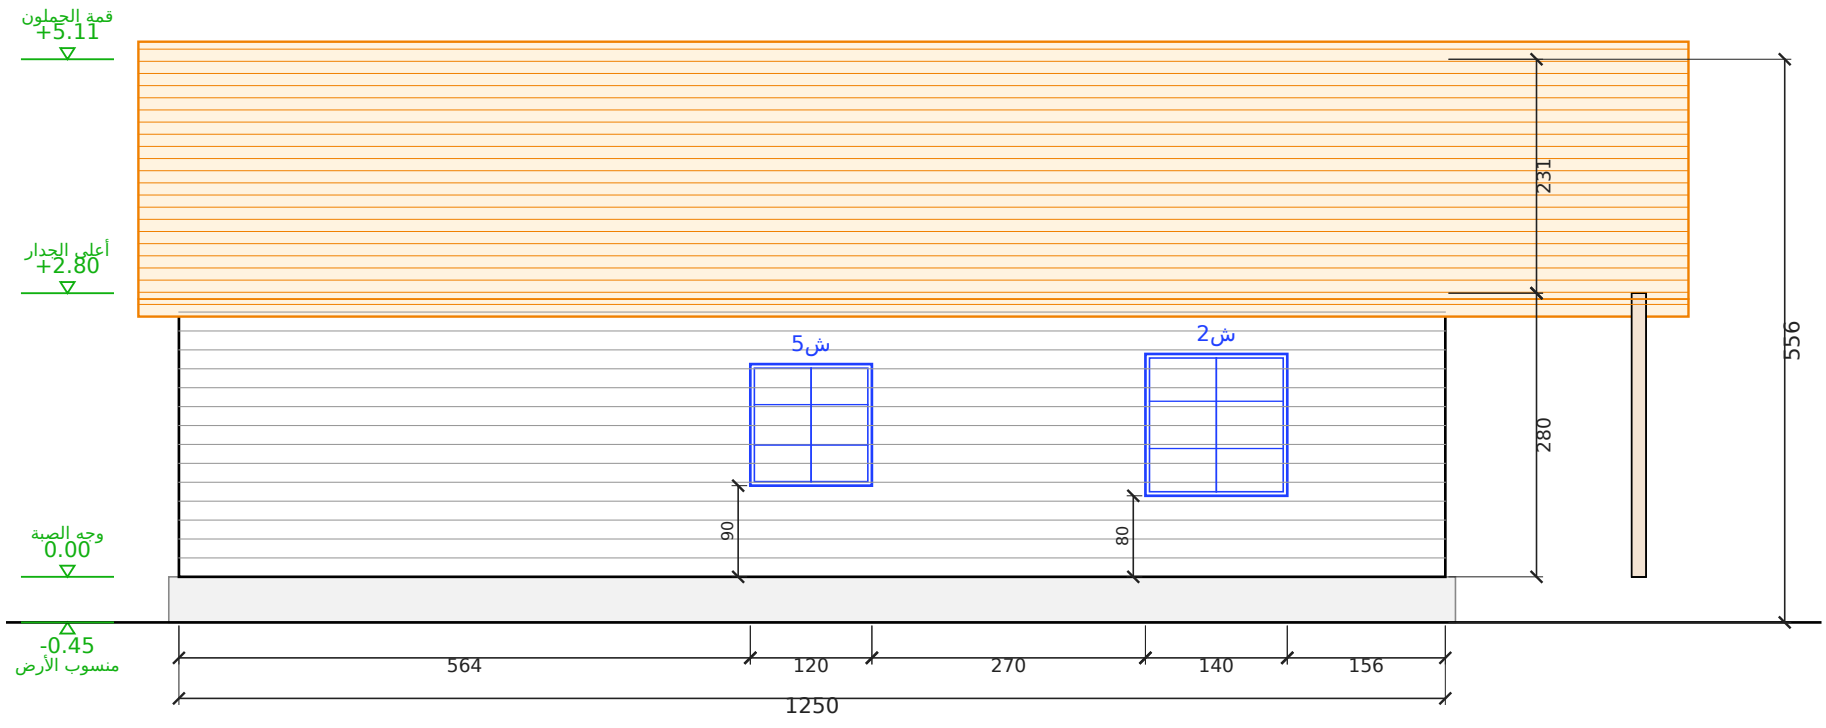



## الواجهة الغربية

مقياس 1:50 | الوحدة: سم


| المشروع / العميل | عنوان اللوحة | المقياس | التاريخ | رقم اللوحة |
|---|---|---|---|---|
| استراحة — غرفتين + صالة كبيرة — 8.00 × 12.50 = 100 م² عميل — استراحة مكة | الواجهة الخلفية والواجهة الغربية | 1:50 | 2026-10-21 | A-03 (3/9) |

مصنع وتد الأخشاب
Watad Wood Factory


## مسقط السقف (جملون)
رفرف 40 سم من كل جهة | مقياس 1:50

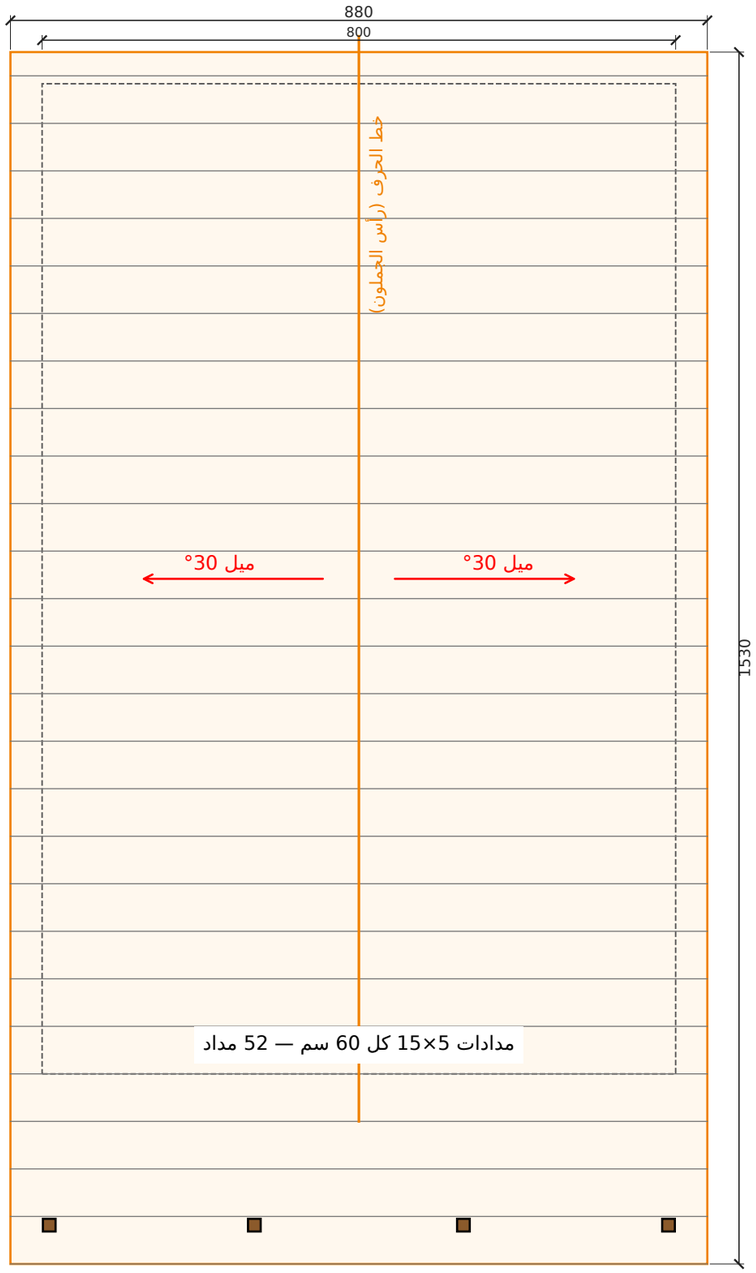


## قطاع عرضي أ-أ
مقياس 1:50 | الوحدة: سم

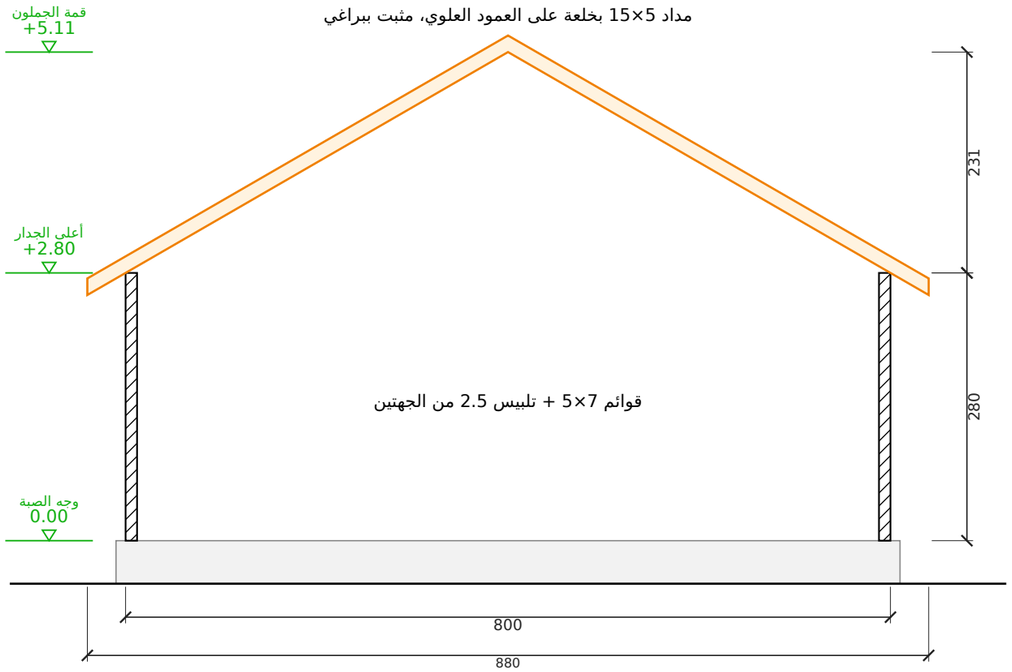


### تفصيلة جلوس المداد على العلوي (1:5)

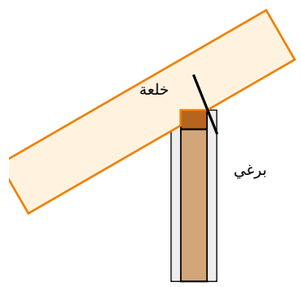


| | | | | |
|---|---|---|---|---|
| **مصنع وتد الأخشاب**<br>Watad Wood Factory | المشروع / العميل<br>**استراحة — غرفتين + صالة كبيرة — 8.00 × 12.50 = 100 م²**<br>**عميل — استراحة مكة** | عنوان اللوحة<br>**مسقط السقف والقطاع** | المقياس<br>**1:50** | التاريخ<br>**2026-10-21** | رقم اللوحة<br>**A-04 (4/9)** |

## جدول مقاسات الأبواب والشبابيك
## مقاس الفتحة الصافي في الجدار - الوحدة: سم

| الرمز | النوع | العرض (سم) | الارتفاع (سم) | ارتفاع الجلسة (سم) | العدد | الموقع |
|---|---|---|---|---|---|---|
| ب1 | باب | 100 | 225 | - | 1 | الأمامية |
| ب2 | باب | 90 | 215 | - | 1 | الشرقية |
| ب3 | باب | 80 | 210 | - | 1 | باب الممر العائلي |
| ب4 | باب | 90 | 210 | - | 1 | المطبخ |
| ب5 | باب | 80 | 210 | - | 2 | غرفة نوم 1 - غرفة نوم 2 |
| ب6 | باب | 70 | 210 | - | 2 | دورة مياه 1 - دورة مياه 2 |
| ش1 | شباك | 200 | 160 | 60 | 2 | الأمامية 2 |
| ش2 | شباك | 140 | 140 | 80 | 2 | الشرقية - الغربية |
| ش3 | شباك | 110 | 100 | 110 | 1 | الشرقية |
| ش4 | شباك | 60 | 60 | 150 | 2 | الشرقية 2 |
| ش5 | شباك | 120 | 120 | 90 | 2 | الخلفية - الغربية |

الإجمالي: أبواب 8 - شبابيك 9

# جدول المساحات وبيانات المشروع

## بيانات المشروع

| البند | البيان |
|---|---|
| المشروع | استراحة — غرفتين + صالة كبيرة — 8.00 × 12.50 = 100 م² |
| العميل | عميل — استراحة مكة |
| الموقع | مكة |
| الاستخدام | استراحة |
| التاريخ | 2026-10-21 |
| نظام البناء | هيكل خشب 5×7 + تلبيس 2.5 سم من الجهتين |
| السقف | جملون 30° — قرميد معدني |

## جدول المساحات


| م | الفراغ | الأبعاد (م) | المساحة (م2) |
|---|---|---|---|
| 1 | الصالة (جلسة + طعام) | 7.76 × 4.58 | 35.54 |
| 2 | غرفة نوم 1 | 3.28 × 3.68 | 12.07 |
| 3 | غرفة نوم 2 | 3.28 × 3.76 | 12.33 |
| 4 | الممر | 0.98 × 7.56 | 7.41 |
| 5 | المطبخ | 3.26 × 3.18 | 10.37 |
| 6 | دورة مياه 1 | 3.26 × 1.98 | 6.45 |
| 7 | دورة مياه 2 | 3.26 × 2.16 | 7.04 |
| | **المساحة الصافية الداخلية** | | **91.22** |
| | **التراس المسقوف** | **8.00 × 2.00** | **16.00** |
| | **المساحة الإجمالية المبنية** | **8.00 × 12.50** | **100.00** |

# لقطات المنظور الخارجي


المنظور الأمامي




منظور أمامي من اليسار

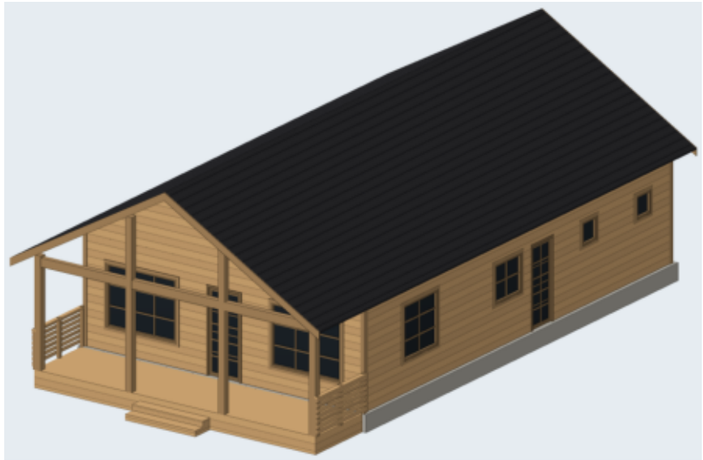


منظور أمامي من اليمين

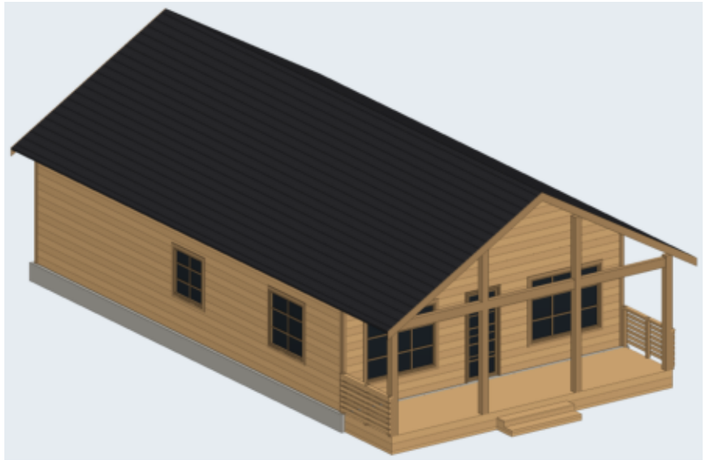


منظر علوي

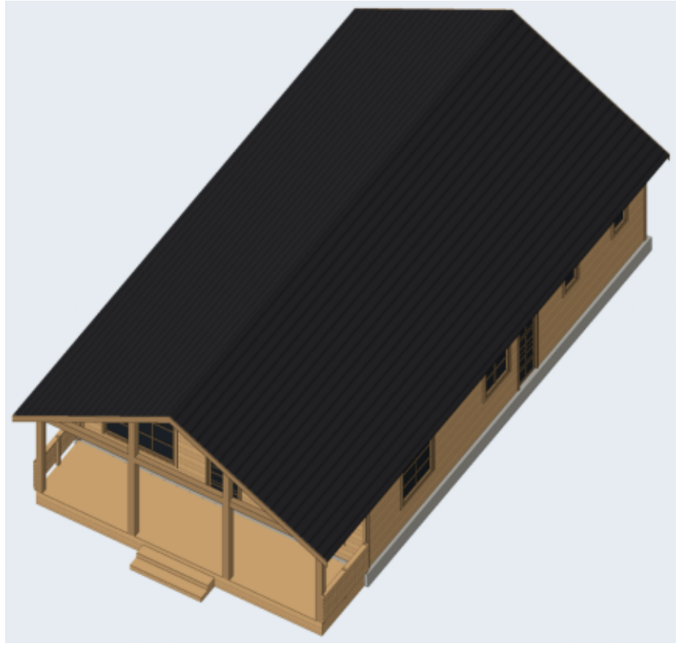

المنظور الخلفي

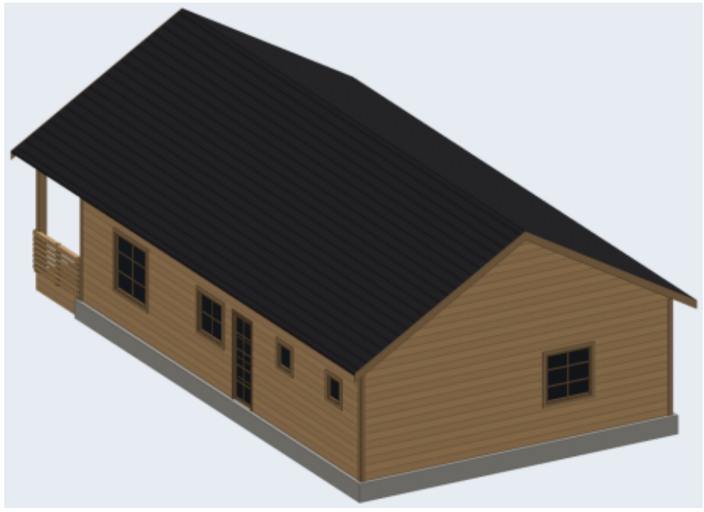

منظور خلفي من اليمين

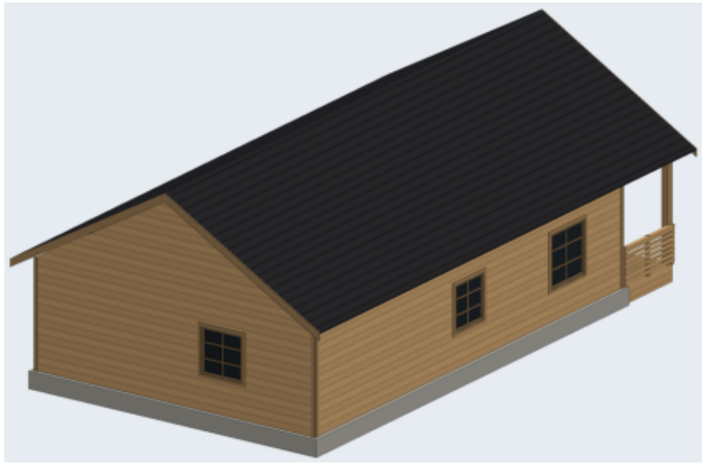


| المشروع / العميل | عنوان اللوحة | المقياس | التاريخ | رقم اللوحة |
|---|---|---|---|---|
| **استراحة — غرفتين + صالة كبيرة — 8.00 × 12.50 = 100 م²**<br>**عميل — استراحة مكة** | **لقطات المنظور** | **—** | **2026-10-21** | **A-07 (7/9)** |

**مصنع وتد الأخشاب**
Watad Wood Factory

# المقطع العلوي بالفرش

مقطع أفقي على ارتفاع 1.90 م — توزيع الفرش ومسار الحركة

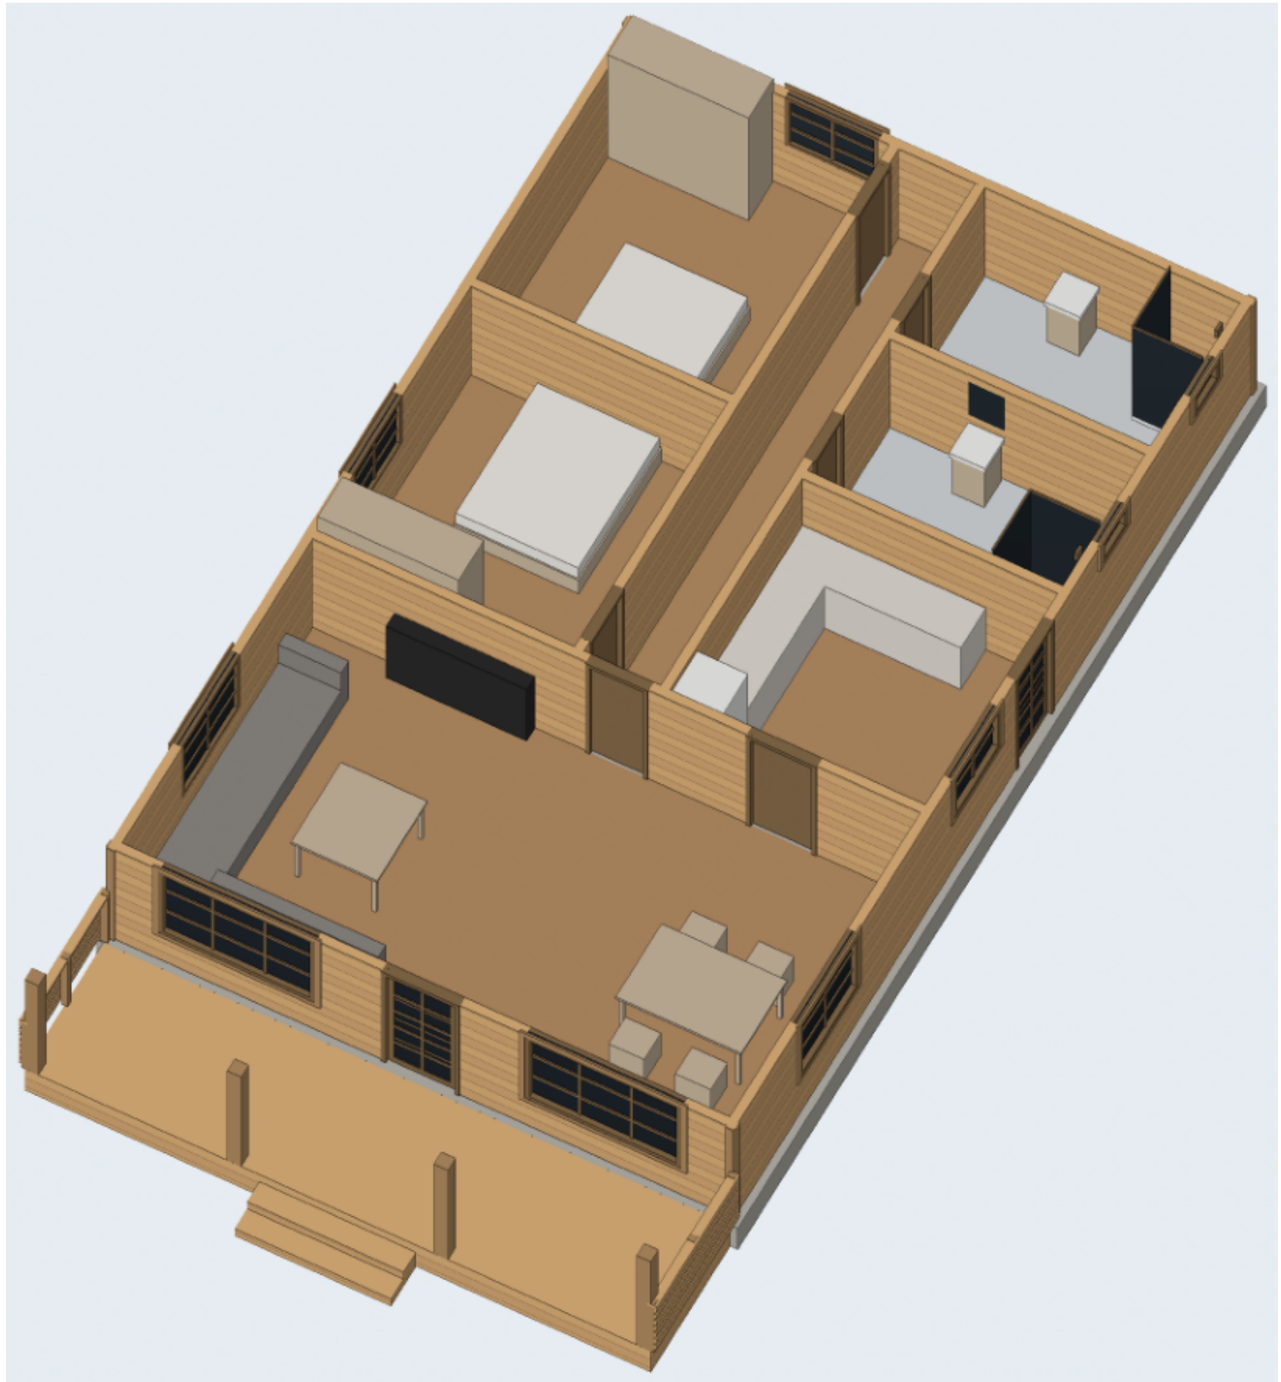

| المشروع / العميل | عنوان اللوحة | المقياس | التاريخ | رقم اللوحة |
|---|---|---|---|---|
| **استراحة — غرفتين + صالة كبيرة — 8.00 × 12.50 = 100 م²**<br>**عميل — استراحة مكة** | **المقطع العلوي بالفرش** | **—** | **2026-10-21** | **A-08 (8/9)** |

**مصنع وتد الأخشاب**
Watad Wood Factory

# المنظور ثلاثي الأبعاد والمواد

النمط: جوزي غامق + إطارات سوداء — رندر واقعي بخامات حقيقية



## جدول المواد والألوان

**الخشب / الصبغة**

خشب طبيعي فاتح (بدون صبغة)

**القرميد**

قرميد رمادي غامق

**الزجاج**

زجاج عاكس غامق

**إطارات الشبابيك والأبواب**

إطار خشب بنفس الصبغة أغمق

**الكنار والزوايا**

نفس الصبغة أغمق درجة


**الصبة**

خرسانة 45 سم


الدربزين: ألواح أفقية متقاربة (عصري)

تقسيم الشبابيك: بدون | الباب الرئيسي: زجاج بتقسيمات (فرنسي)

## أنواع الدربزين المعتمدة (من مشاريع المصنع)

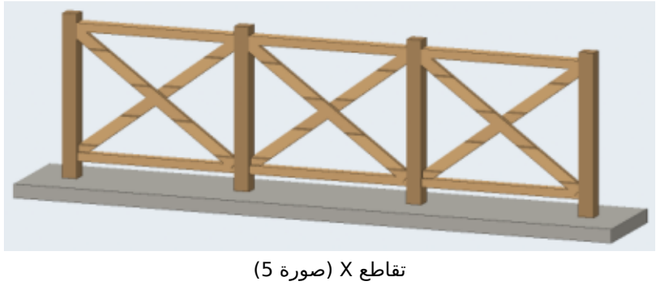

تقاطع X (صورة 5)

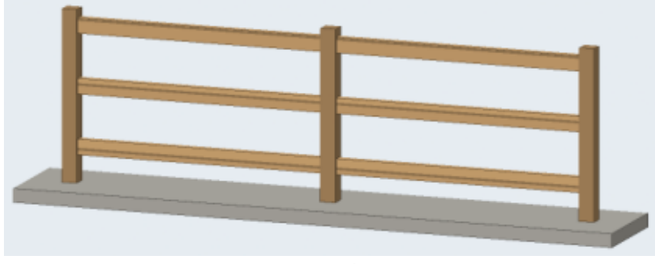

3 مرابيع أفقية (صورة 2)



قوائم رأسية متقاربة (صورة 1)

| المشروع / العميل | عنوان اللوحة | المقياس | التاريخ | رقم اللوحة |
|---|---|---|---|---|
| **مصنع وتد الأخشاب** Watad Wood Factory<br>**استراحة — غرفتين + صالة كبيرة — 8.00 × 12.50 = 100 م²**<br>**عميل — استراحة مكة** | **المنظور والمواد** | **—** | **2026-10-21** | **A-09 (9/9)** |