

المنظور ثلاثي الأبعاد والمواد

النمط: برتقالي محمر + قرميد فحمي + دريزين X — معاينة تقريبية، الإخراج النهائي من 3ds Max

جدول المواد والألوان



الخشب / الصبغة

صبغة برتقالي محمر



القرميد

قرميد فحمي / أسود مزرقي



الزجاج

زجاج عاكس غامق




إطارات الشبابيك والأبواب

إطار خشب بنفس الصبغة أغمق



الكنار والزوايا

نفس الصبغة أغمق درجة

 

الصبغة

خرسانة 20 سم


الدريزين: تقاطع X (صورة 5)

تقسيم الشبابيك: شبكة | الباب الرئيسي: خشب مصمت


أنواع الدريزين المعتمدة (من مشاريع المصنع)



قوائم رأسية متقاربة (صورة 1)

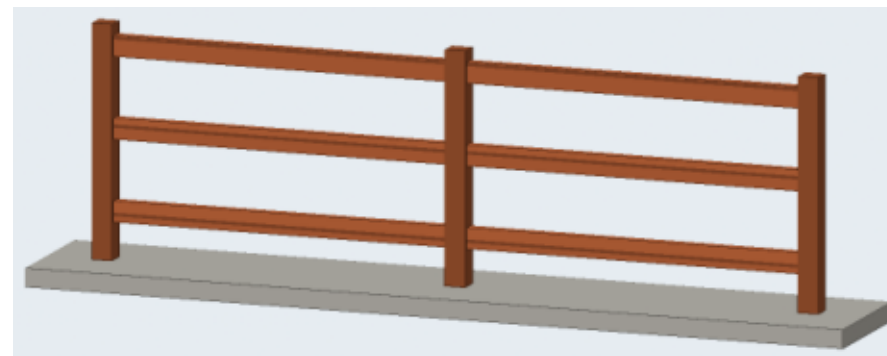



3 مربيع أفقية (صورة 2)

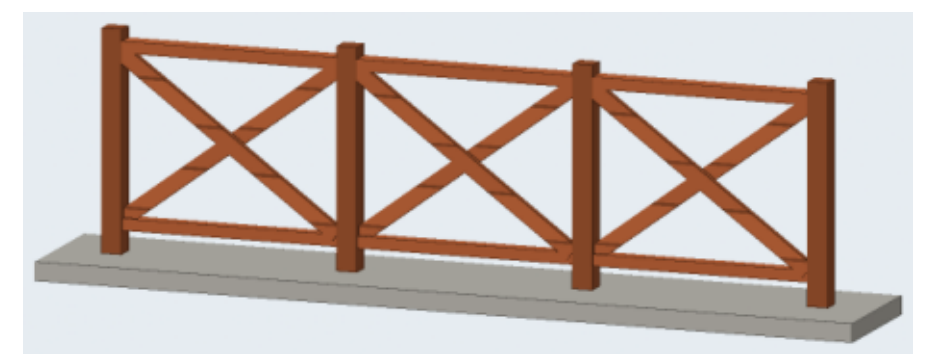

تقاطع X (صورة 5)


المسقط الأفقي مع الفرش
الأبعاد بالسنتيمتر - الجدران: قوائم 5×7 + تليس 2.5 من الجهتين (12 سم)

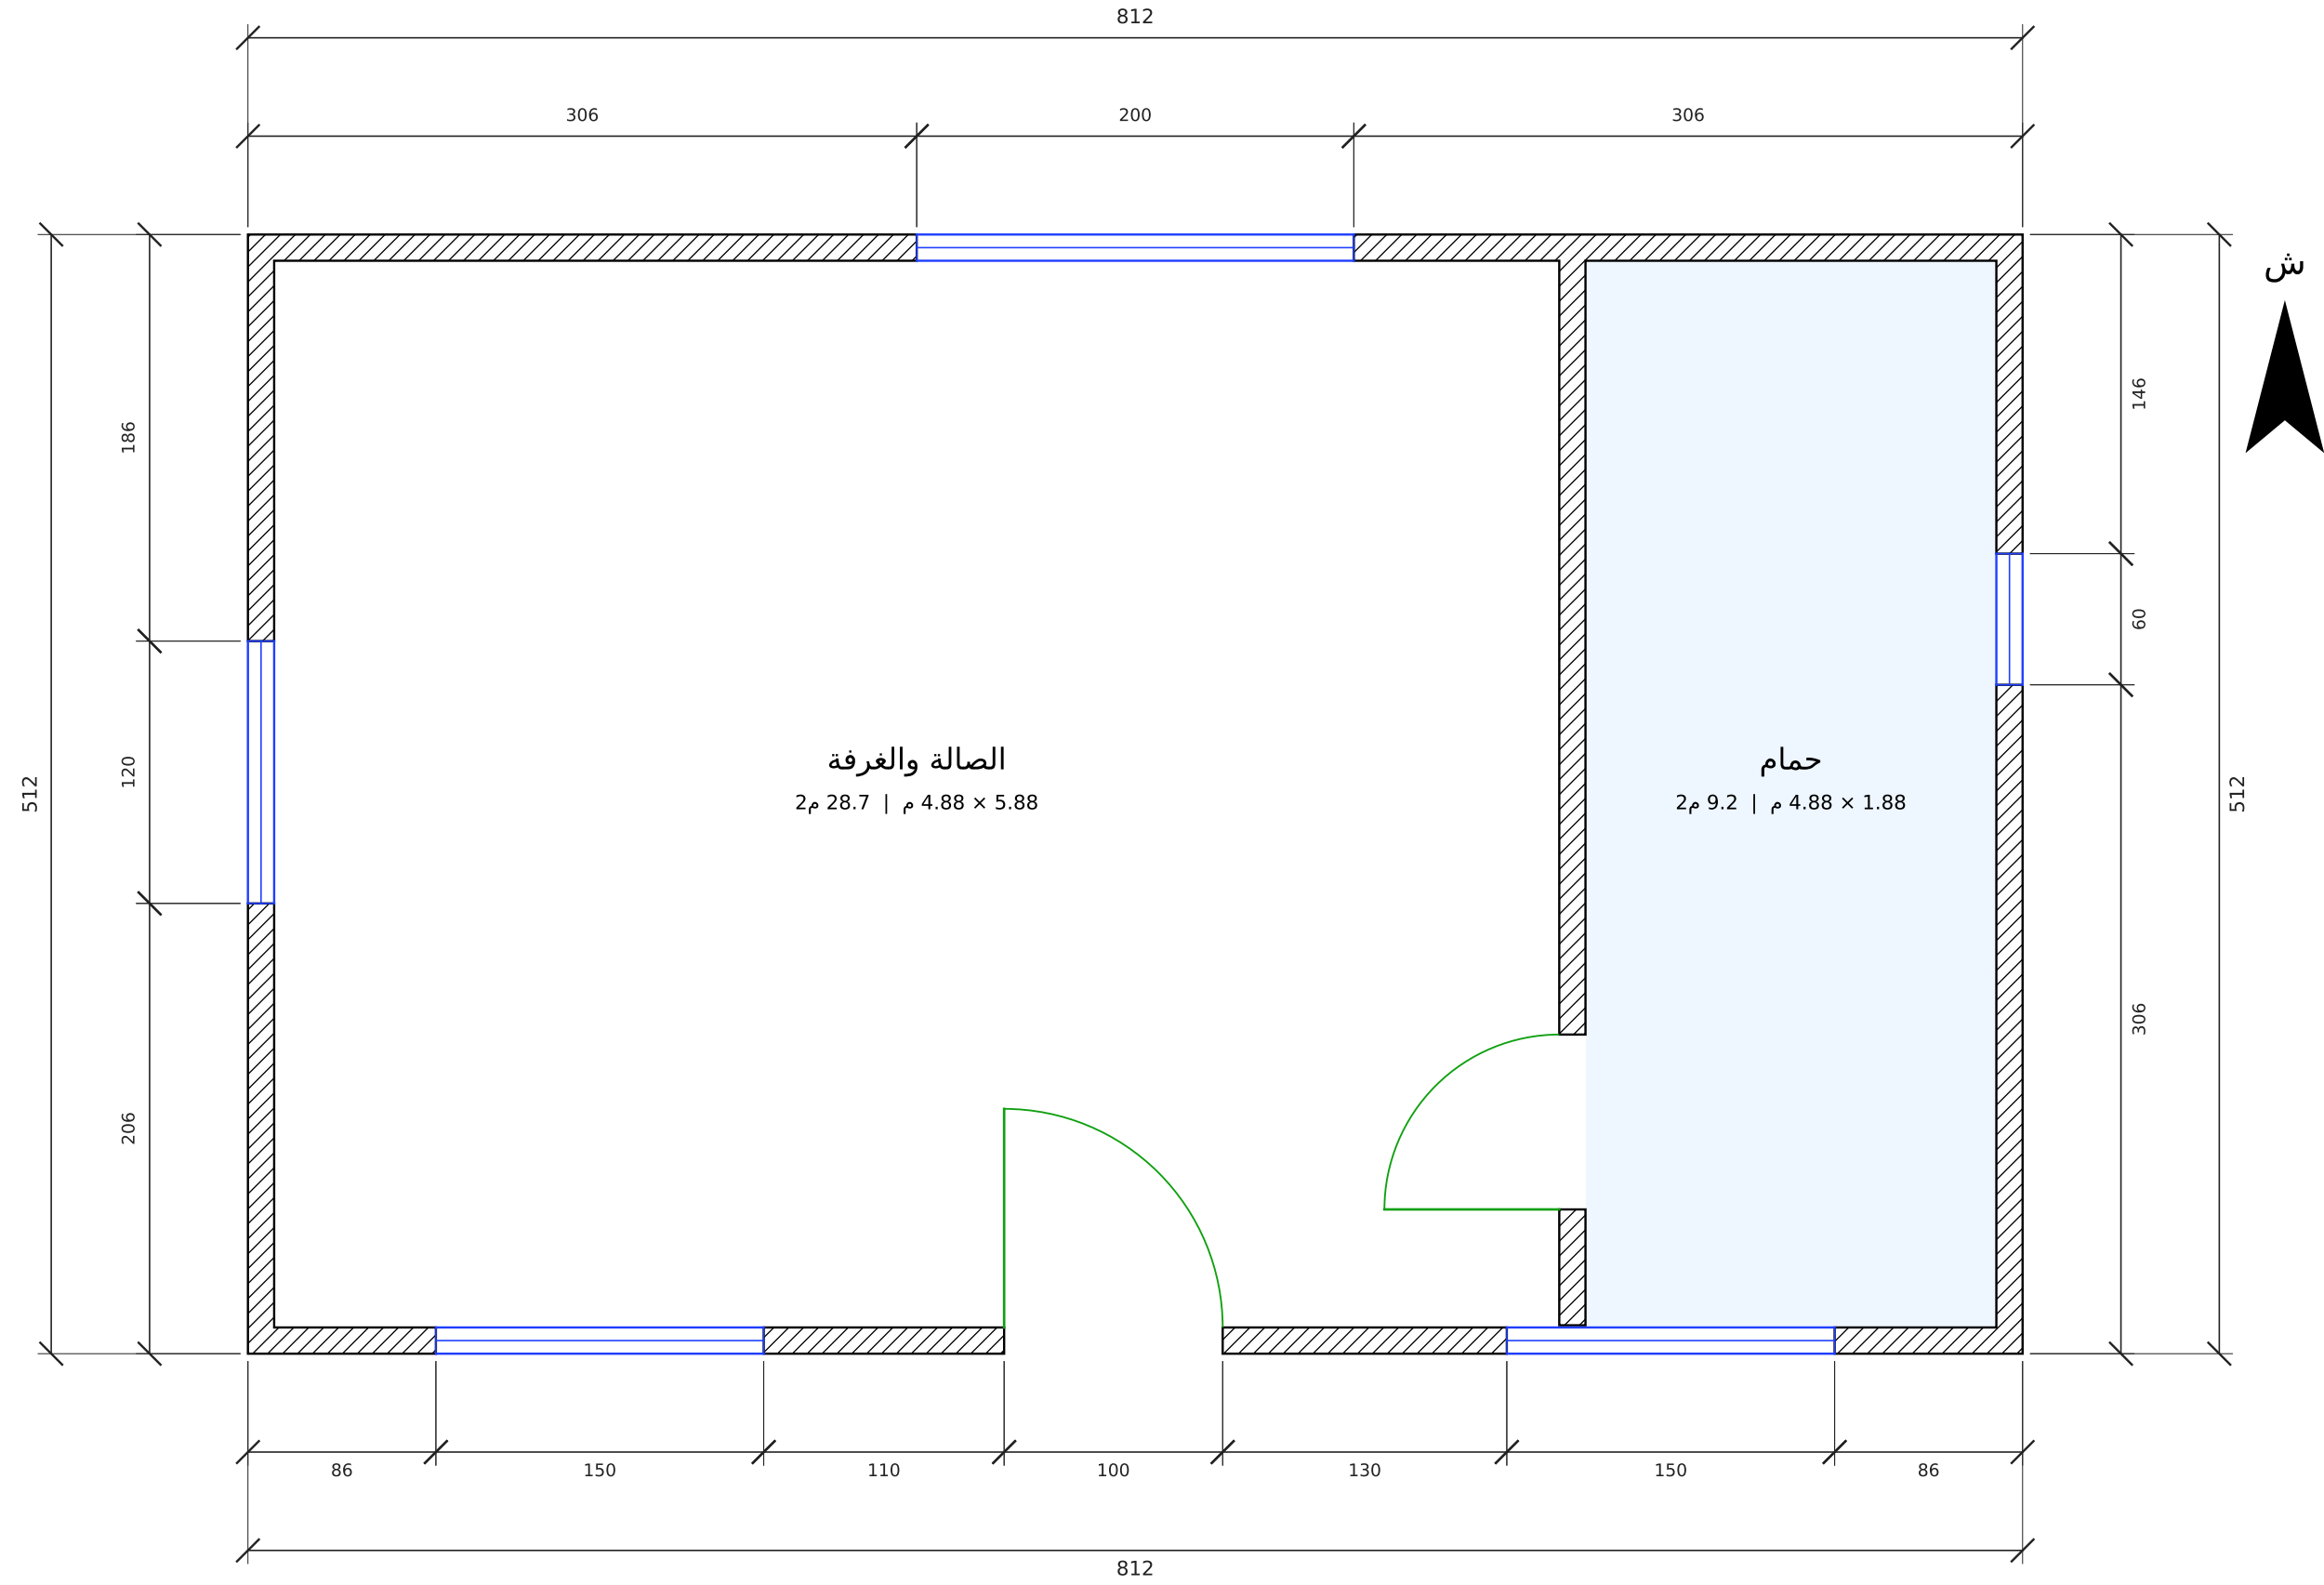

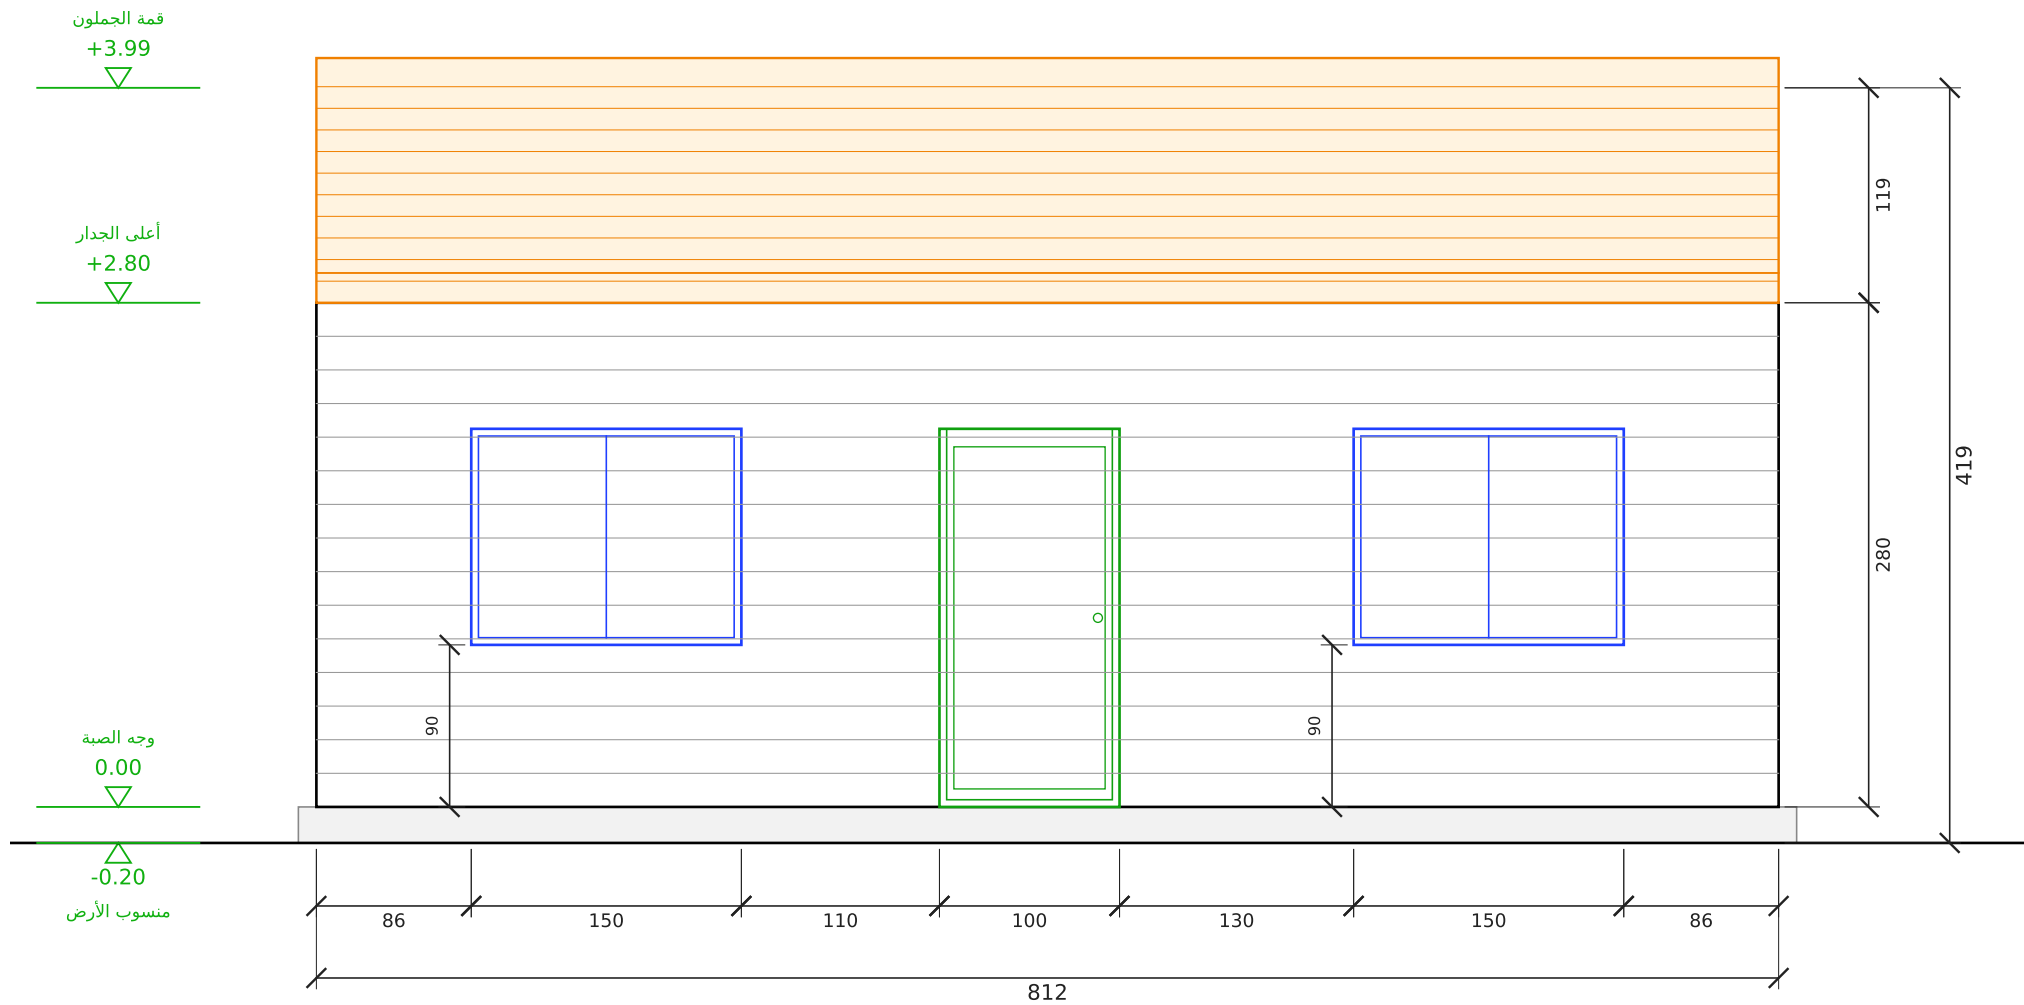


جنوب-W1

مقياس 1:50 | الوحدة: سم

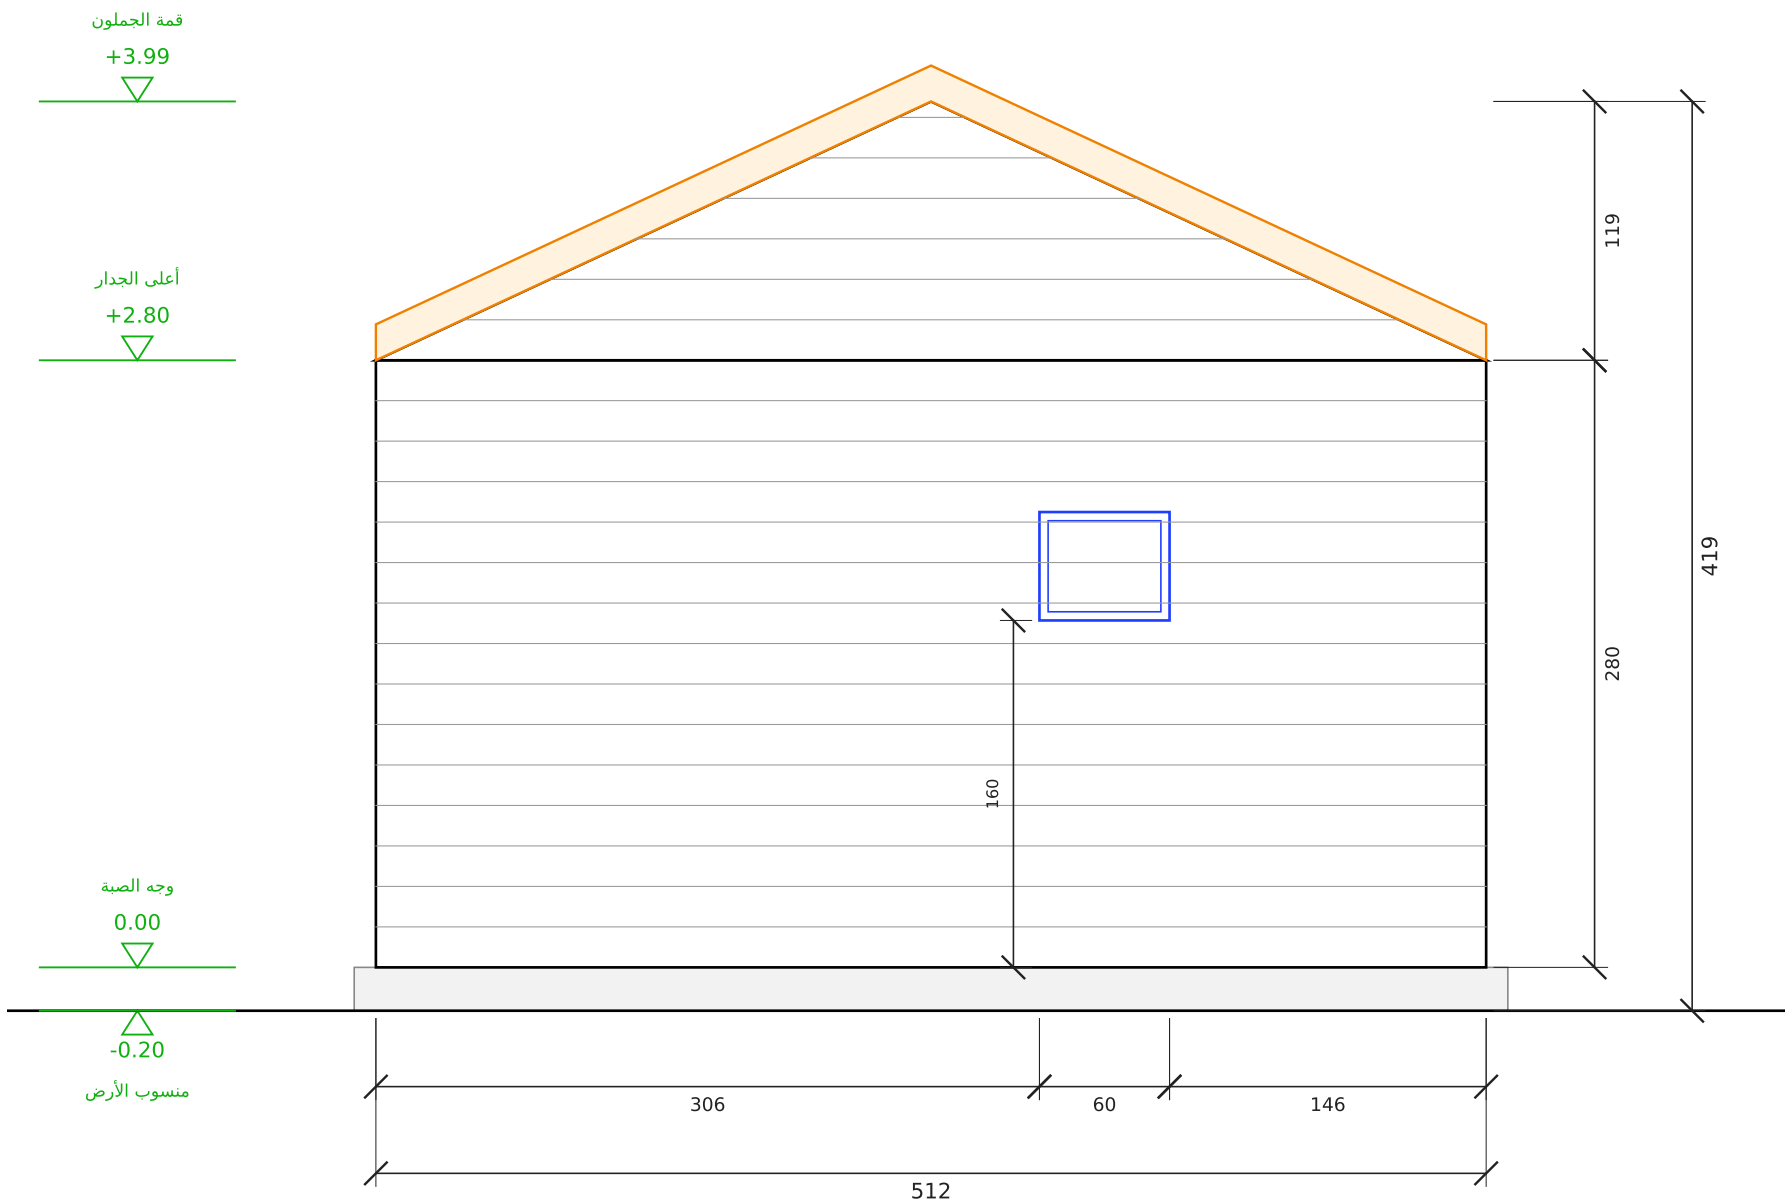


شرق-W2

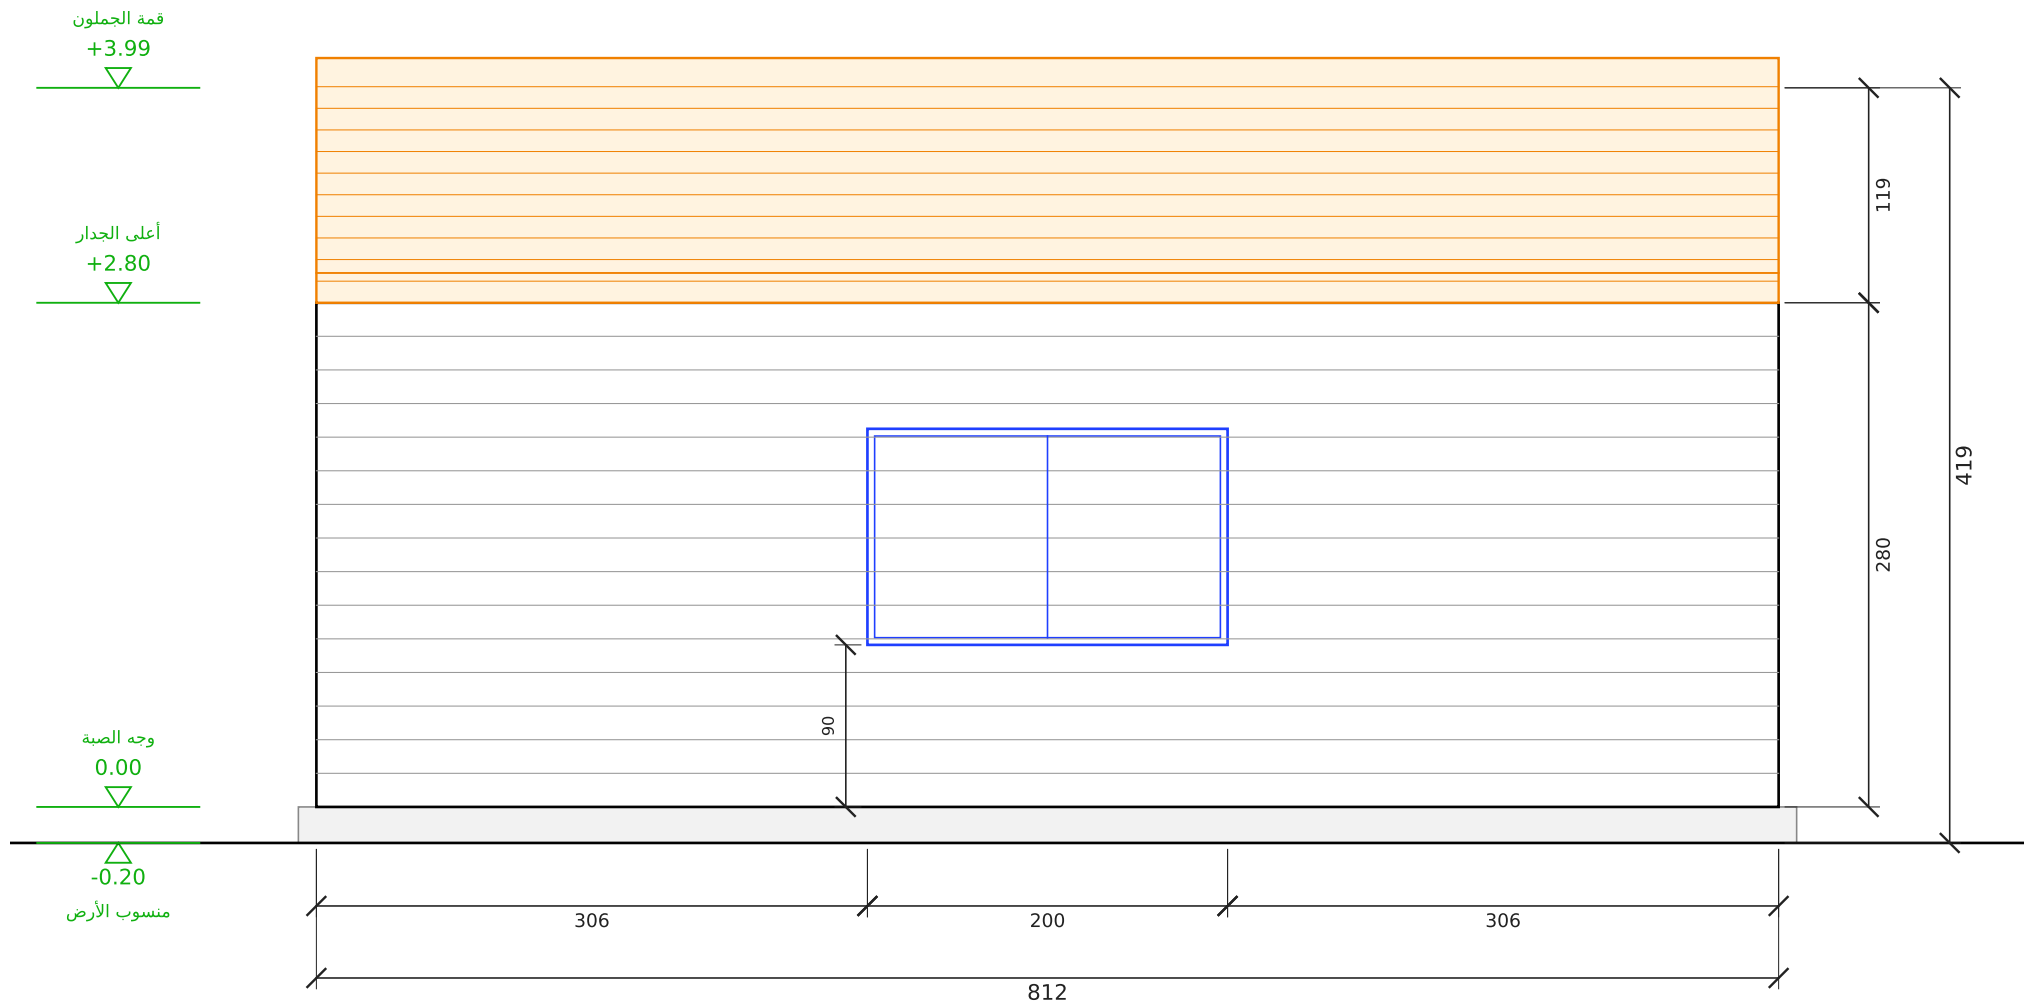


شمال-W3

مقياس 1:50 | الوحدة: سم

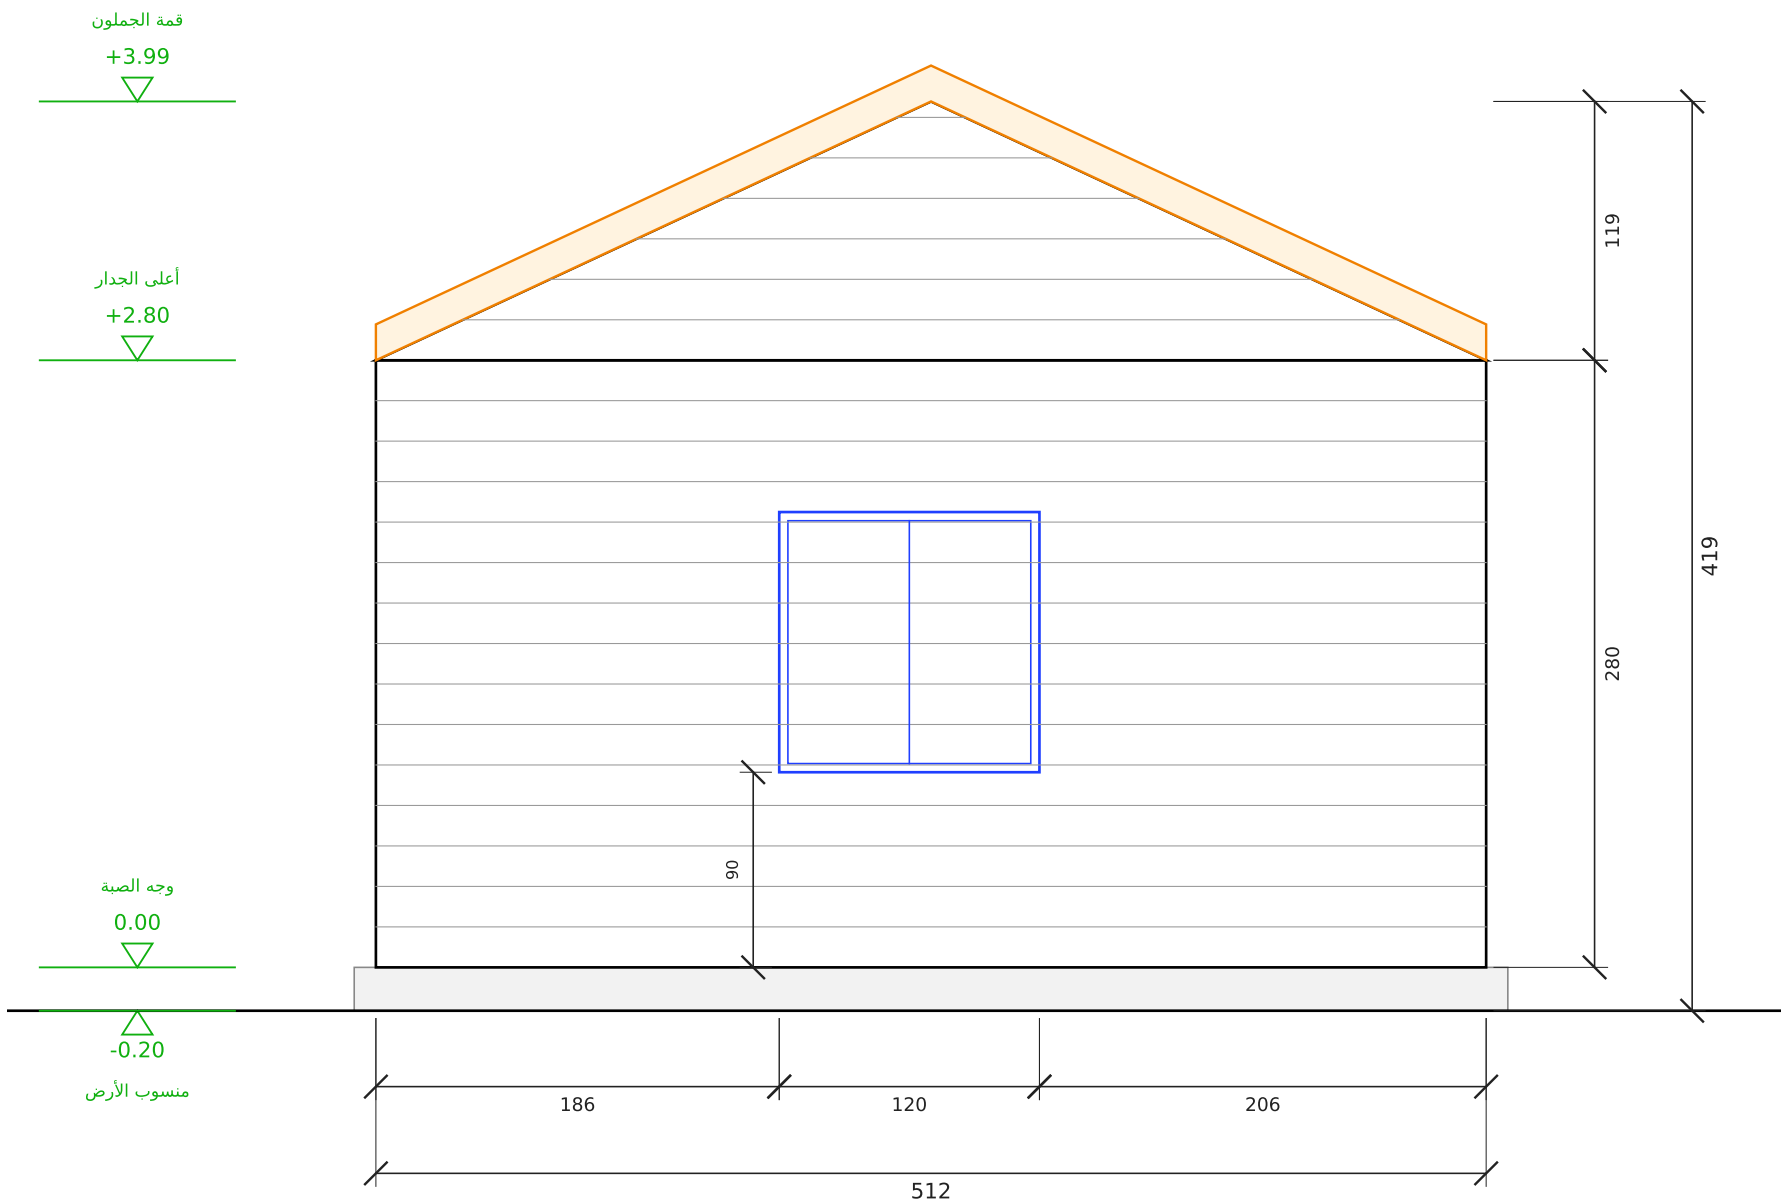


غرب-W4


مسقط السقف (جملون)
رفرف 0 سم من كل جهة | مقياس 1:50

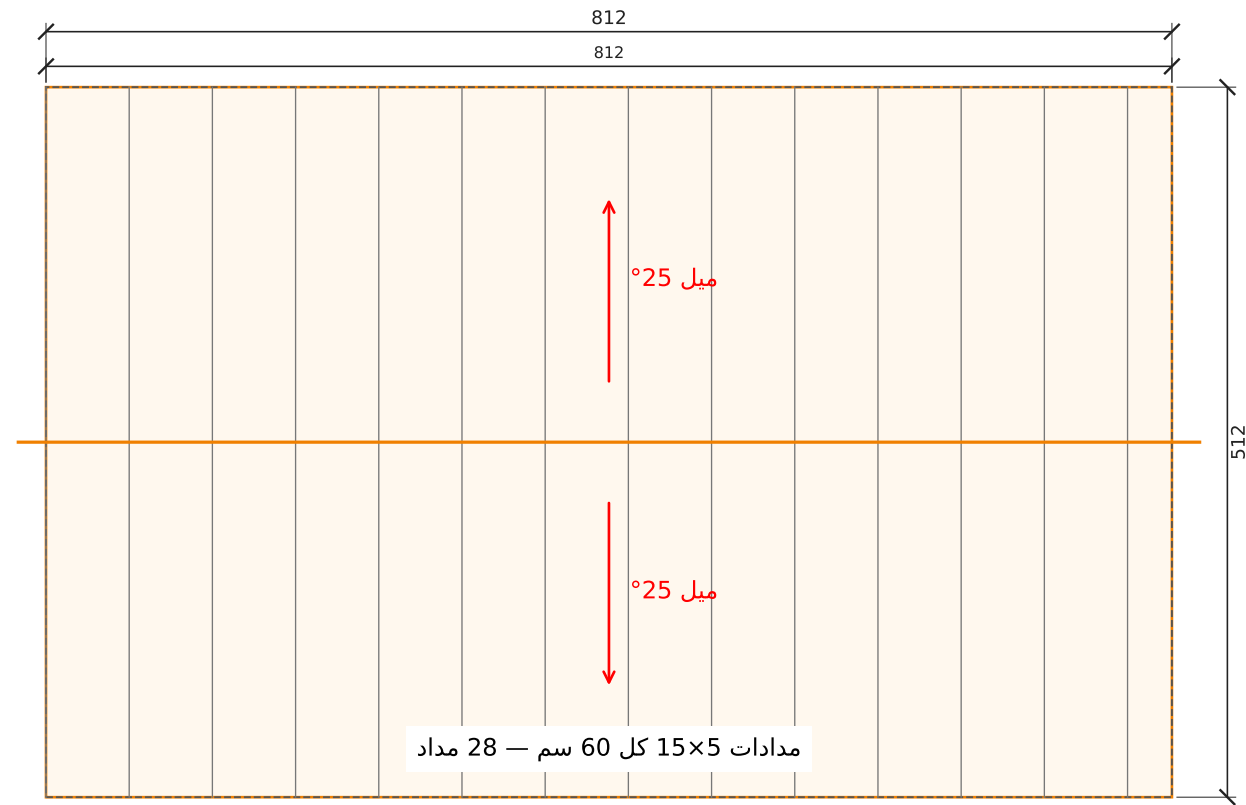

قطاع عرضي أ-أ
مقياس 1:50 | الوحدة: سم

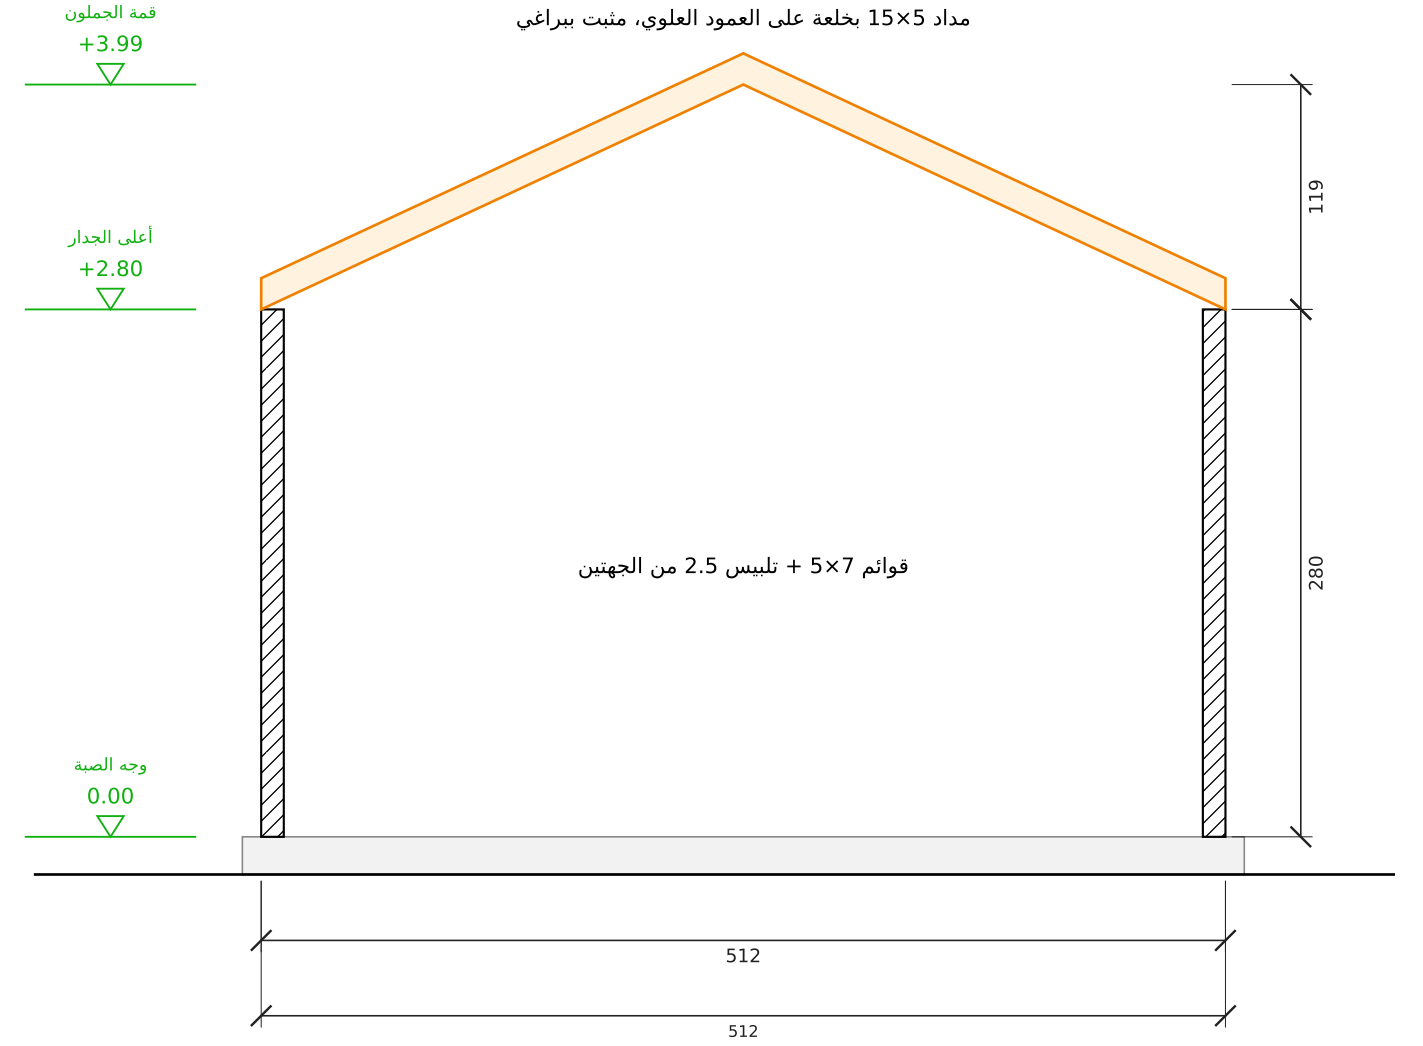

تفصيلة جلوس المدا على العلوي (1:5)

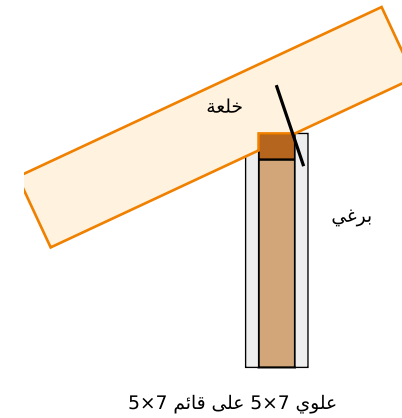

جدول مقاسات الأبواب والشبابيك
مقاس الفتحة الصافي في الجدار - الوحدة: سم

الرمز	النوع	العرض (سم)	الارتفاع (سم)	ارتفاع الجلسة (سم)	العدد	الموقع
	باب	100	210	-	1	جنوب-W1
	باب	80	210	-	1	باب حمام
	شباك	150	120	90	2	جنوب W1-2
	شباك	60	50	160	1	شرق-W2
	شباك	200	120	90	1	شمال-W3
	شباك	120	120	90	1	غرب-W4

الإجمالي: أبواب 2 - شبابيك 5


مصنع وتد الأخشاب
Watad Wood Factory

البند	القيمة
المشروع	sample-cabin
العميل	مثال تجريبي
الموقع	
الاستخدام	
المدير	
التاريخ	
المقياس	1:50
الوحدة	سم


جدول المساحات

م	الفراغ	الأبعاد الداخلية (م)	المساحة (م2)
1	الصالة والغرفة	5.88 × 4.88	28.69
2	حمام	1.88 × 4.88	9.17
	المساحة الصافية الداخلية		37.87
	المساحة الإجمالية الخارجية	8.12 × 5.12	41.57

تأطير جدار W1-جنوب — الطول 800 سم، الارتفاع 280 سم

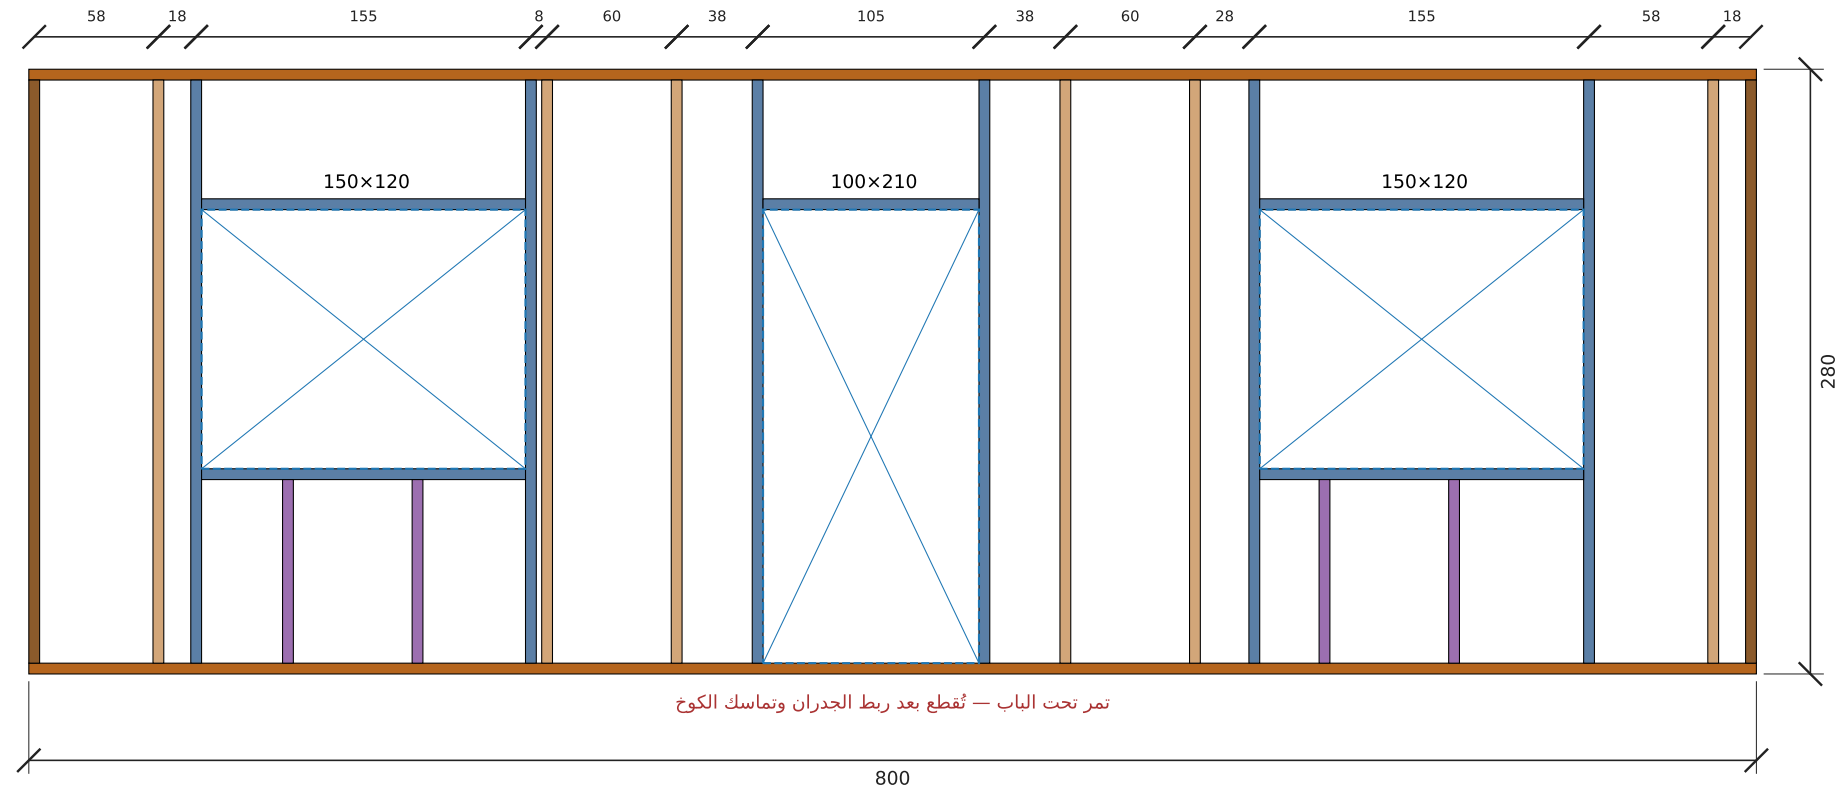


تأطير جدار W2-شرق — الطول 500 سم، الارتفاع 280 سم

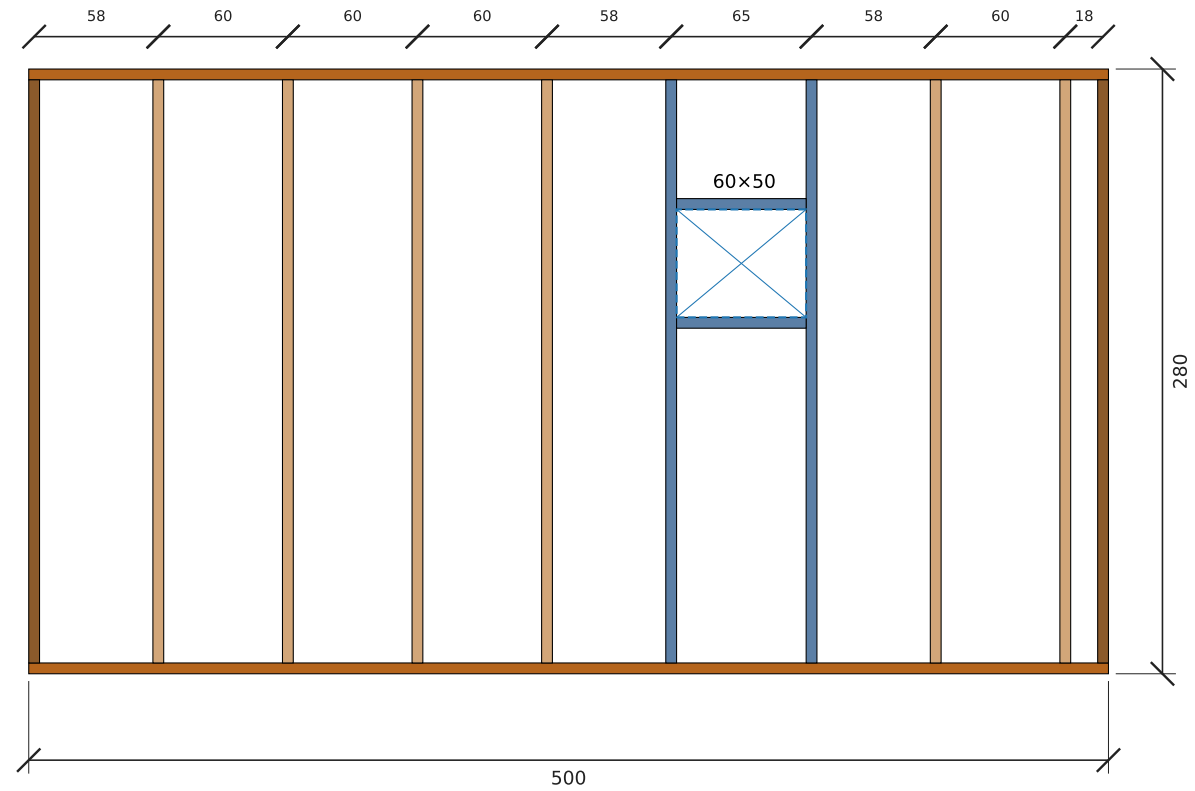


عمود قصير جلسة شباك رأس فتحة جنب فتحة عمود زاوية عمود عمود علوي قاعدة سفلية

تأطير جدار W3-شمال — الطول 800 سم، الارتفاع 280 سم

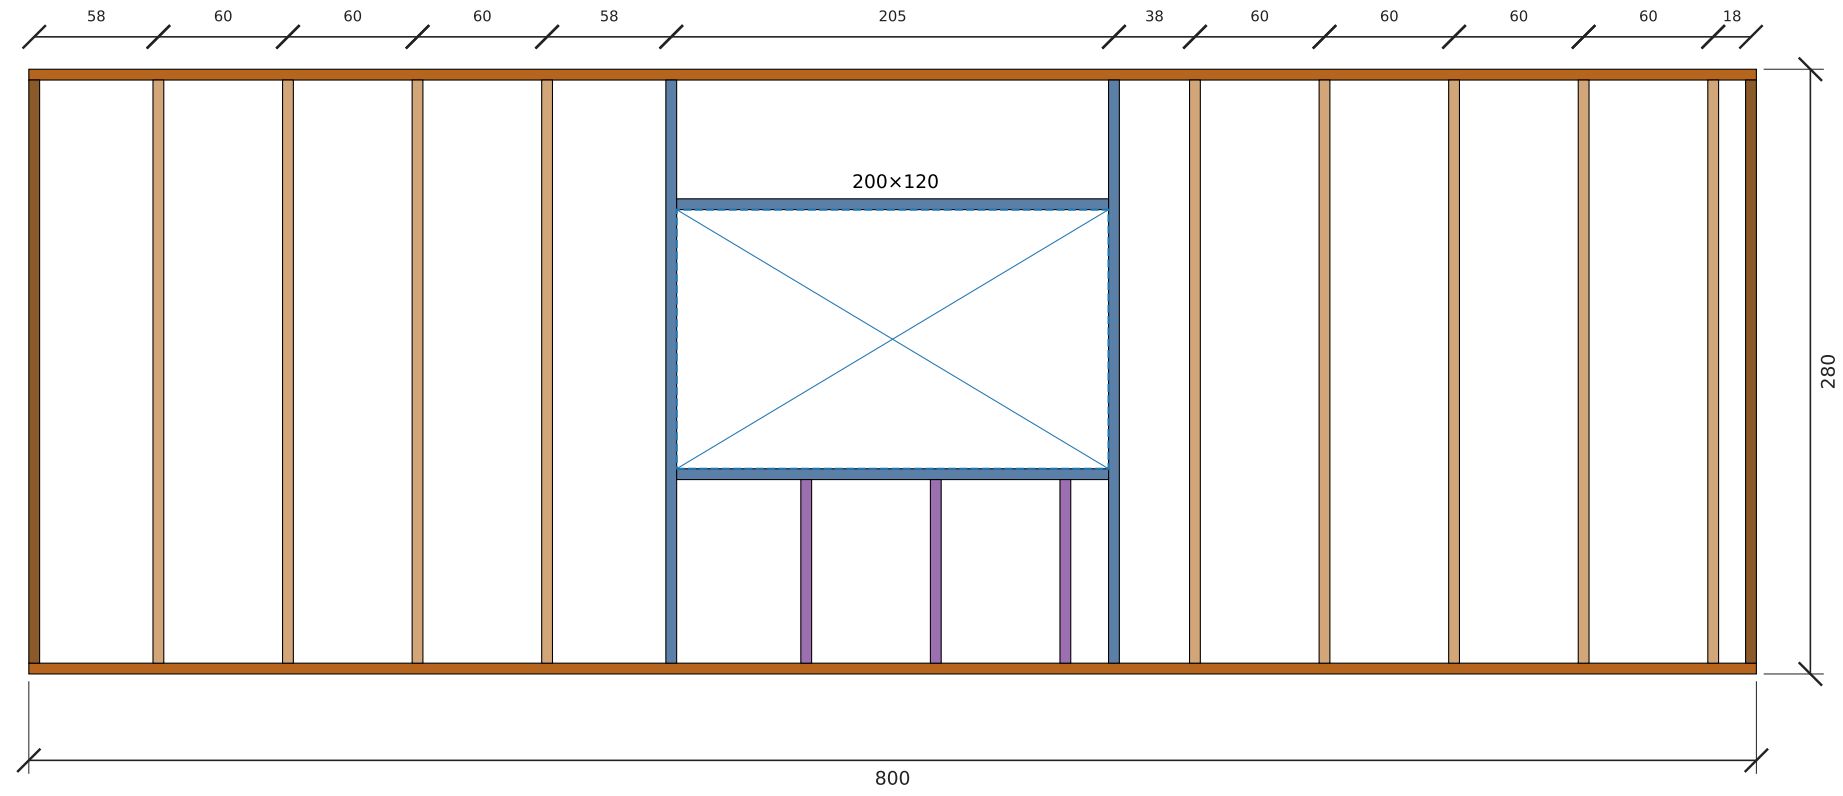


تأطير جدار W4-غرب — الطول 500 سم، الارتفاع 280 سم

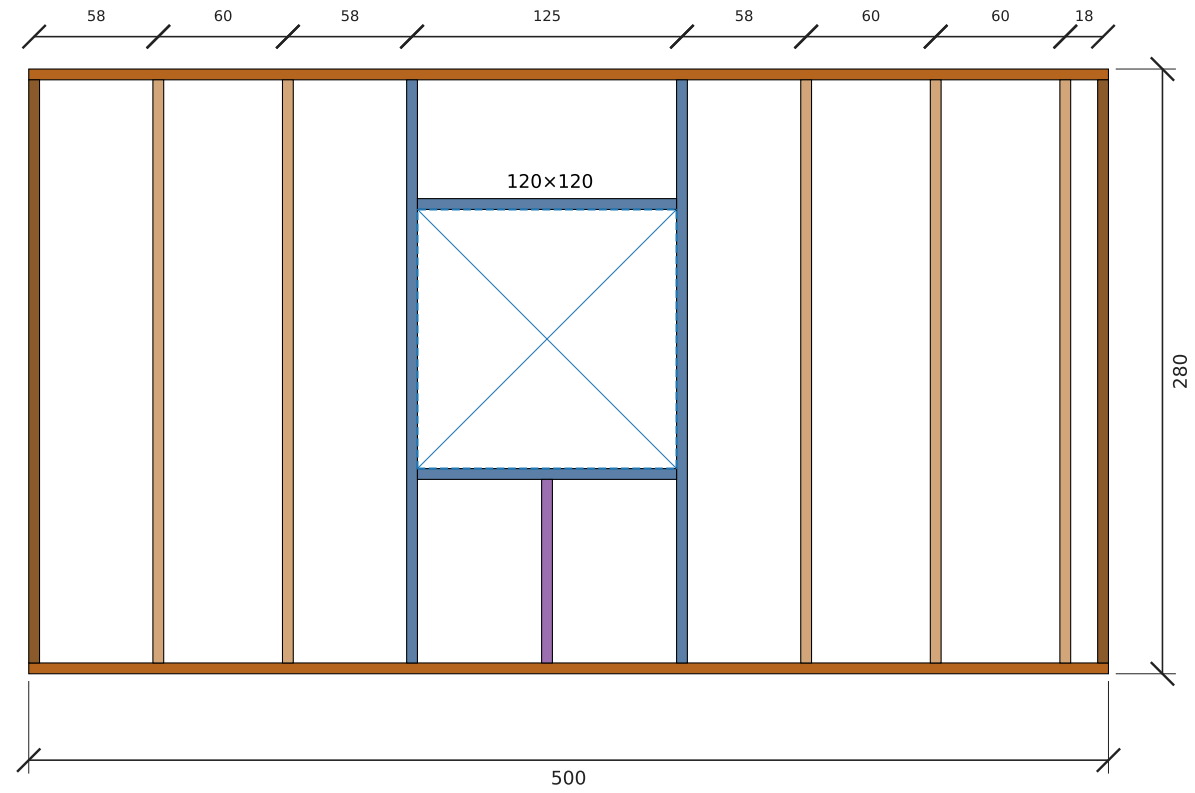

قاعدة سفلية علوي عمود عمود زاوية جنب فتحة رأس فتحة جلسة شباك عمود قصير

تأطير جدار W5-داخلي — الطول 500 سم، الارتفاع 280 سم (داخلي)

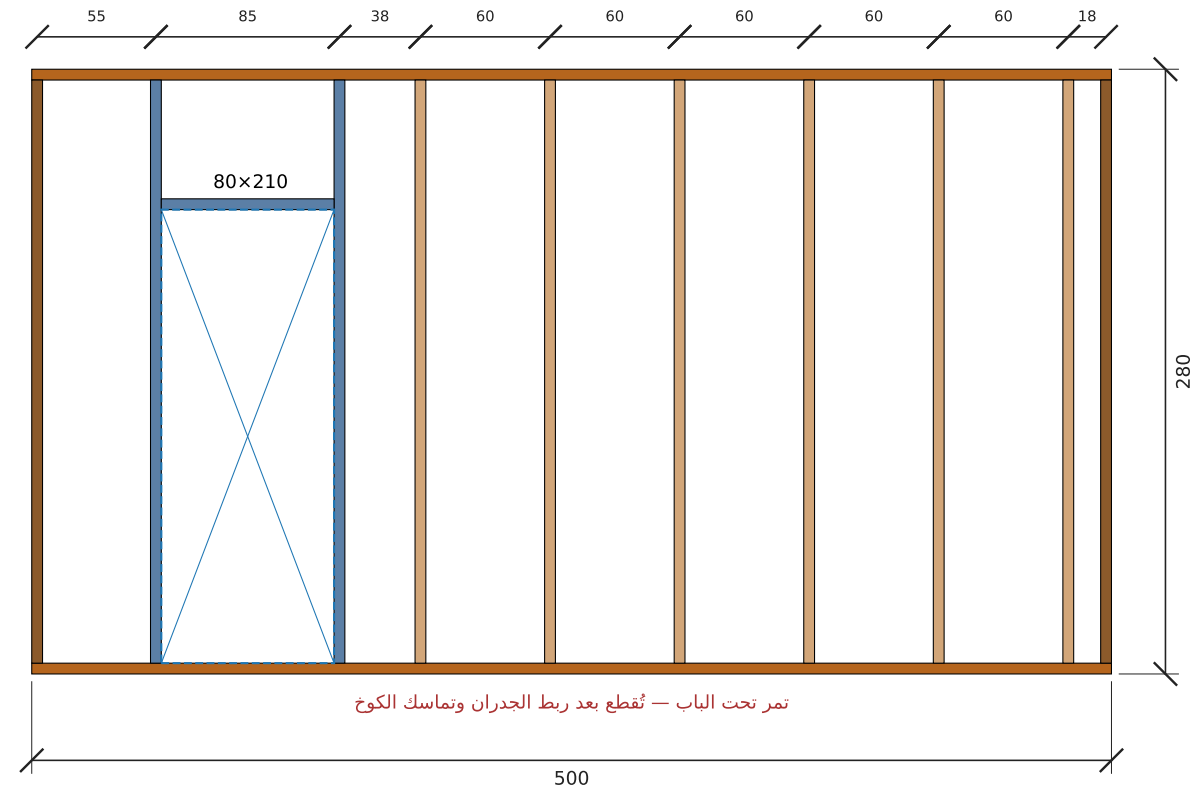

عمود قصير عمود زاوية عمود جلسة شباك رأس فتحة جنب فتحة علوي قاعدة سفلية

جدول الكميات وخطة تقطيع الطبلیات

البند	القيمة
الارتفاع المطلوب / المعتمد	280 / 280 سم
السقف	جملون 25° — قمة 399 سم من وجه الصبة
المدادات 15×5	28 مداد (14 لكل جهة) × 282 سم — من طبلية 320
طبلیات الطريقة الأولى (مداد + عمود)	28 طبلية × 320 سم
طبلیات الطريقة الثانية (3 أعمدة)	20 طبلية × 320 سم
إجمالي الطبلیات 22.5×5	48
إجمالي قطع 5×7	86
قائمة تقطيع 5×7	800سم×4 500سم×6 270سم×56 200سم×2 150سم×4 120سم×2 100سم×1 85سم×8 80سم×1
	60سم×2
ألواح تلبیس 2.5 سم	173 لوح × 400 سم (مجموع الصفوف 612.4 م، 10 وجه)
أسمنت بورد 12 مم (244×122)	24 لوح (داخل دورات المياه)
العزل	بدون (غير مطلوب)
الصبة	یجهزها العميل — 20 سم، مفرغة تحت دورات المياه

مراجعة التصميم مقابل قواعد المصنع

النوع	البند	التفاصيل	المقترح
خطأ	ش2 في W1-جنوب	الفتحة تقع على التقاء الجدار W5-داخلي (عند 600 سم) — الباب يصطدم بالجدار ولا يوجد مكان لجنب الإطار 5×7.	تُبعد حافة الفتحة 11 سم على الأقل عن محور الجدار الملتقي، أو يُعاد توزيع الجدران الداخلية.
ملاحظة	بحر المدادات	أطول بحر بدون جدار داخلي يحمل المداد: جهة أ: 256 سم، جهة ب: 256 سم. يحتاج رقم المصنع لأقصى بحر مسموح لتحديد المدادات اللي تُقوّى 5×20.	
سؤال	يحتاج تأكيد	أقصى بحر للمداد بدون جدار داخلي قبل إضافة تقوية 5×7 (مداد 5×20)؟	
سؤال	يحتاج تأكيد	التغطية الصافية للوح التليس بعد التعشيق (مستنتجة مؤقتاً 18.67 سم من 280/15)؟	
سؤال	يحتاج تأكيد	هل يوضع أعمدة قصيرة فوق رأس الشباك/الباب إلى العلوي؟	
سؤال	يحتاج تأكيد	مكان الوصلة في القاعدة والعلوي إذا الجدار أطول من الطيلية؟	