
الموقع العام وتنسيق الحديقة (لاندسكيب)

الأرض 10 × 30 م = 300 م² | الأبعاد بالسنتيمتر

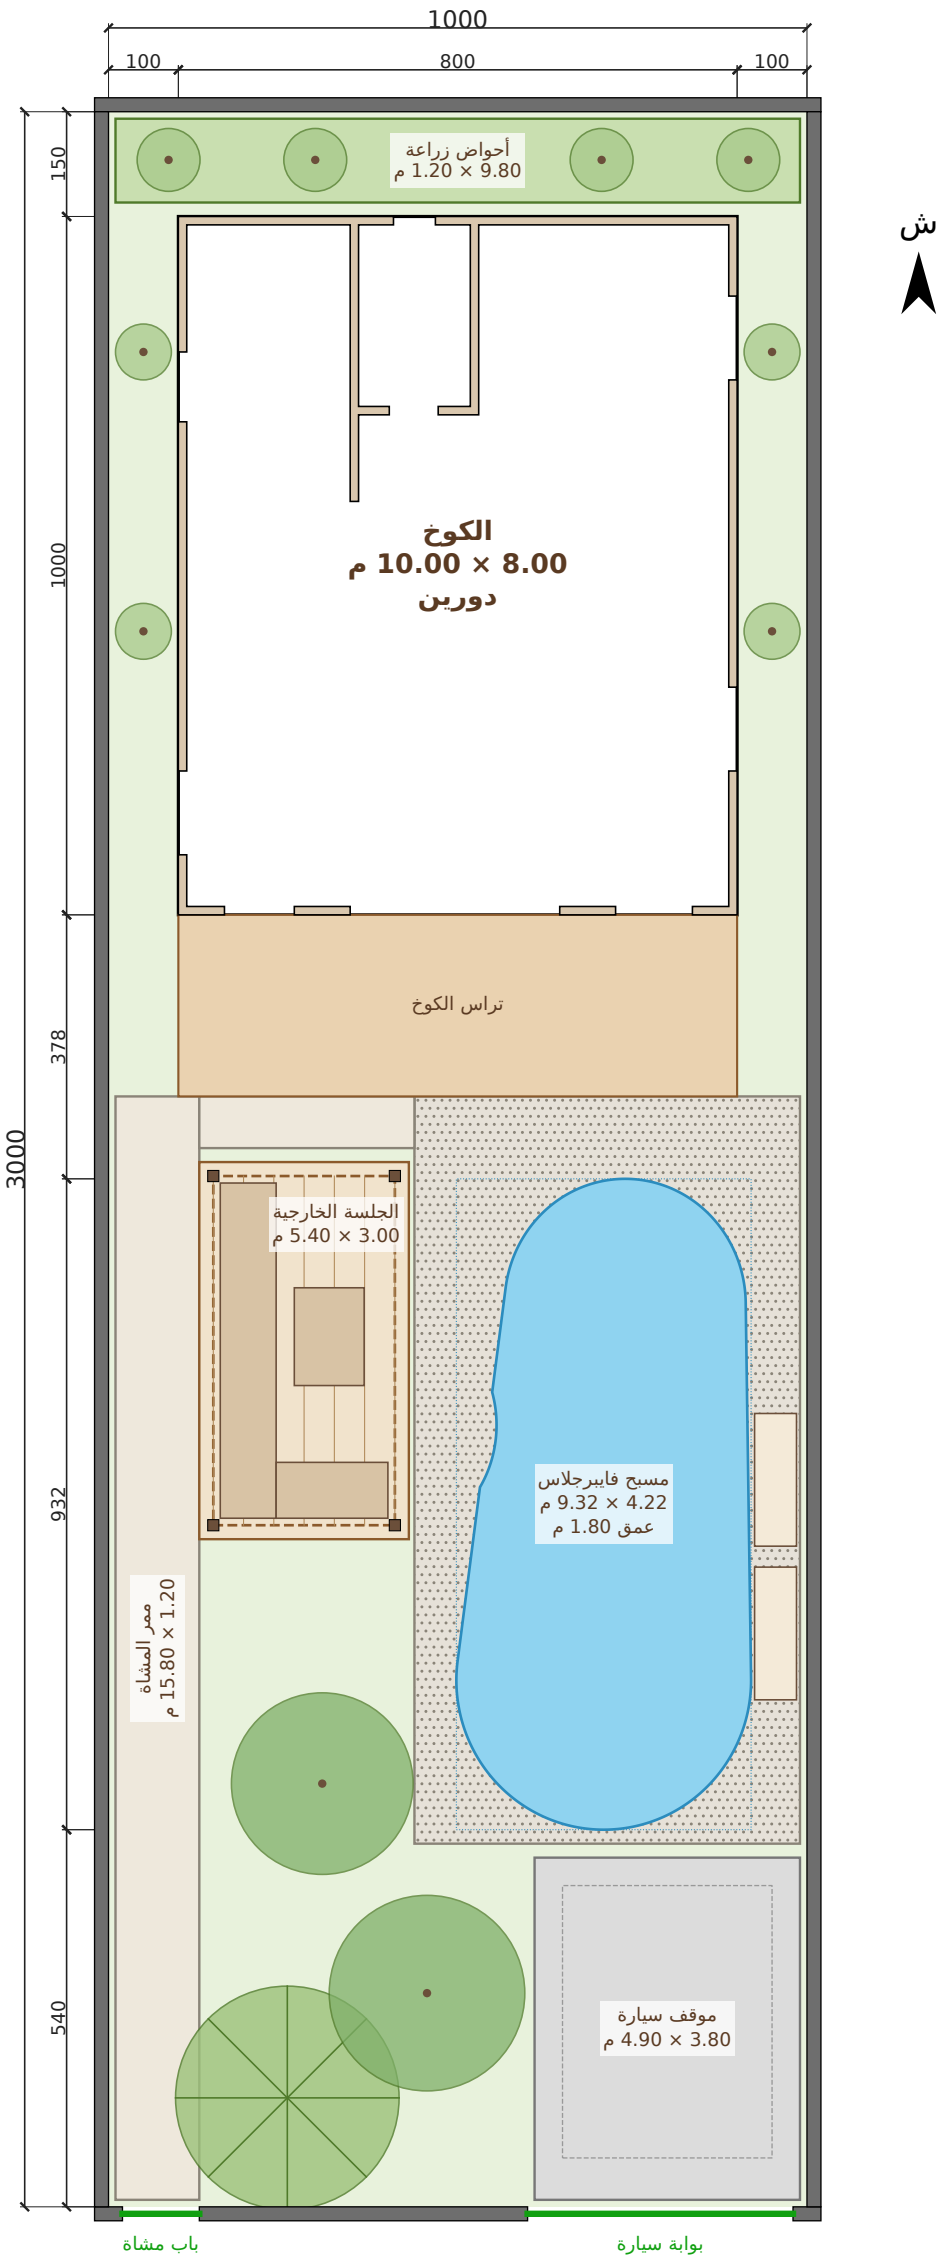

شارع عرض 16 م

جدول مساحات الموقع

البند	المقاس	المساحة (م²)
مساحة الأرض	10.00 × 30.00 م	300.0
مسطح الكوخ (البصمة)	8.00 × 10.00 م	80.0
تراس الكوخ	8.00 × 2.60 م	20.8
مسبح	4.22 × 9.32 م	39.3
جلسة خارجية	3.00 × 5.40 م	16.2
بلاط		19.7
موقف سيارة	3.80 × 4.90 م	18.6
ممر		21.2
أحواض زراعة	9.80 × 1.20 م	11.8
المسطحات الخضراء (حديقة)	الباقي	72.3

• الكوخ في آخر الأرض بعيد عن الشارع (خصوصية)، والصالة والبلكونة يطلّون على المسبح والحديقة.

• بوابة سيارة 3.80 م + باب مشاة مستقل، سور بلك 2.50 م بغطاء خشب أعلى السور.

• ممر المشاة من الباب للتراس بمحاذاة السور الغربي، والموقف عند البوابة بدون ما يقطع الحديقة.

• مسبح فايبرجلاس جاهز بشكل حر 9.32 × 4.22 م بعمق 1.20–1.80 م، حوله بلاط وإطار رخام، وكراسي استلقاء على الجهة الشرقية.

• جلسة خارجية تحت برجولة خشب بين المسبح والسور، وظل أشجار من جهة الشارع.

• بلكونة 8.00 × 2.40 م على الدور الأول وتراس 8.00 × 2.60 م بالأرضي، أعمدة خشب من الأرض للسقف، والسقف ممتد يغطي البلكونة.


المساحة الكلية: 80 + 80 + 20.8 + 19.2 = 200 م².

المشروع / العميل	عنوان اللوحة	المقياس	التاريخ	رقم اللوحة
كوخ دورين + تنسيق حديقة ومسبح — جدة **عميل جديد — جدة**	**الموقع العام واللاندسكيب**	**1:200**	**2026-10-18**	**A-01 (1/12)**

مصنع وتد الأخشاب
Watad Wood Factory

المسقط الأفقي مع الفرش — الدور الأرضي


الأبعاد بالسنتيمتر - الجدران: قوائم 7×5 + تلبيس 2.5 من الجهتين (12 سم) | منسوب الأرضية +0.00

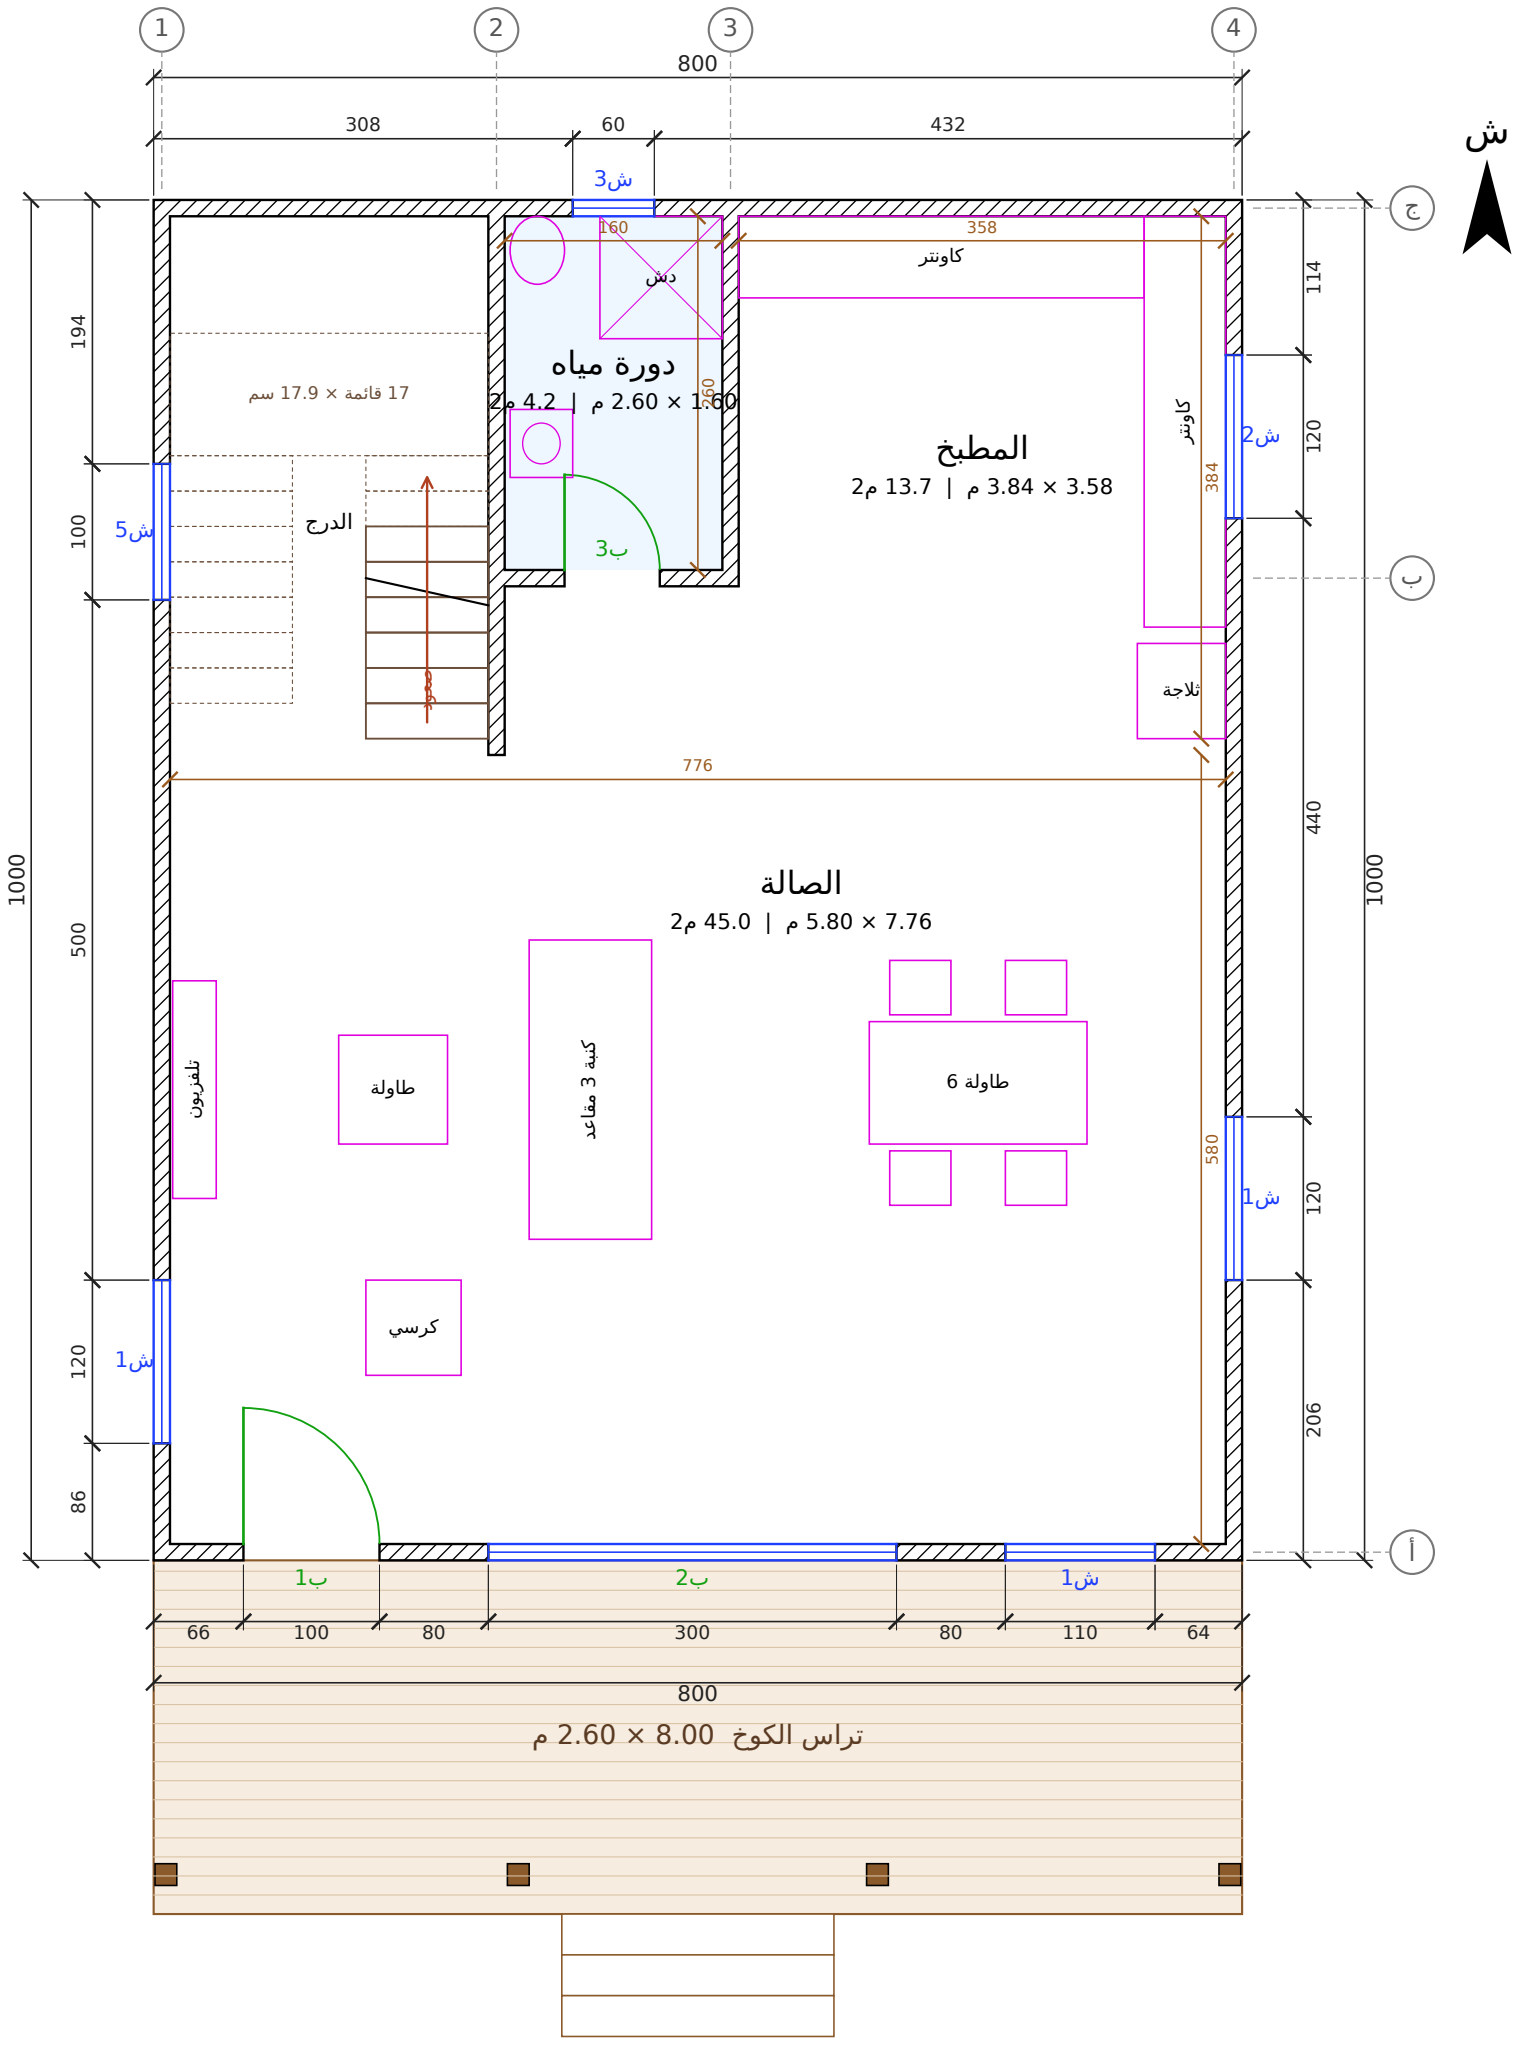


المشروع / العميل	عنوان اللوحة	المقياس	التاريخ	رقم اللوحة
مصنع وتد الأخشاب Watad Wood Factory **كوخ دورين + تنسيق حديقة ومسبح — جدة** **عميل جديد — جدة**	**المسقط الأفقي — الدور الأرضي**	**1:50**	**2026-10-18**	**A-02 (2/12)**

المسقط الأفقي مع الفرش — الدور الأول

الأبعاد بالسنتيمتر - الجدران: قوائم 7×5 + تلبيس 2.5 من الجهتين (12 سم) | منسوب الأرضية +3.05

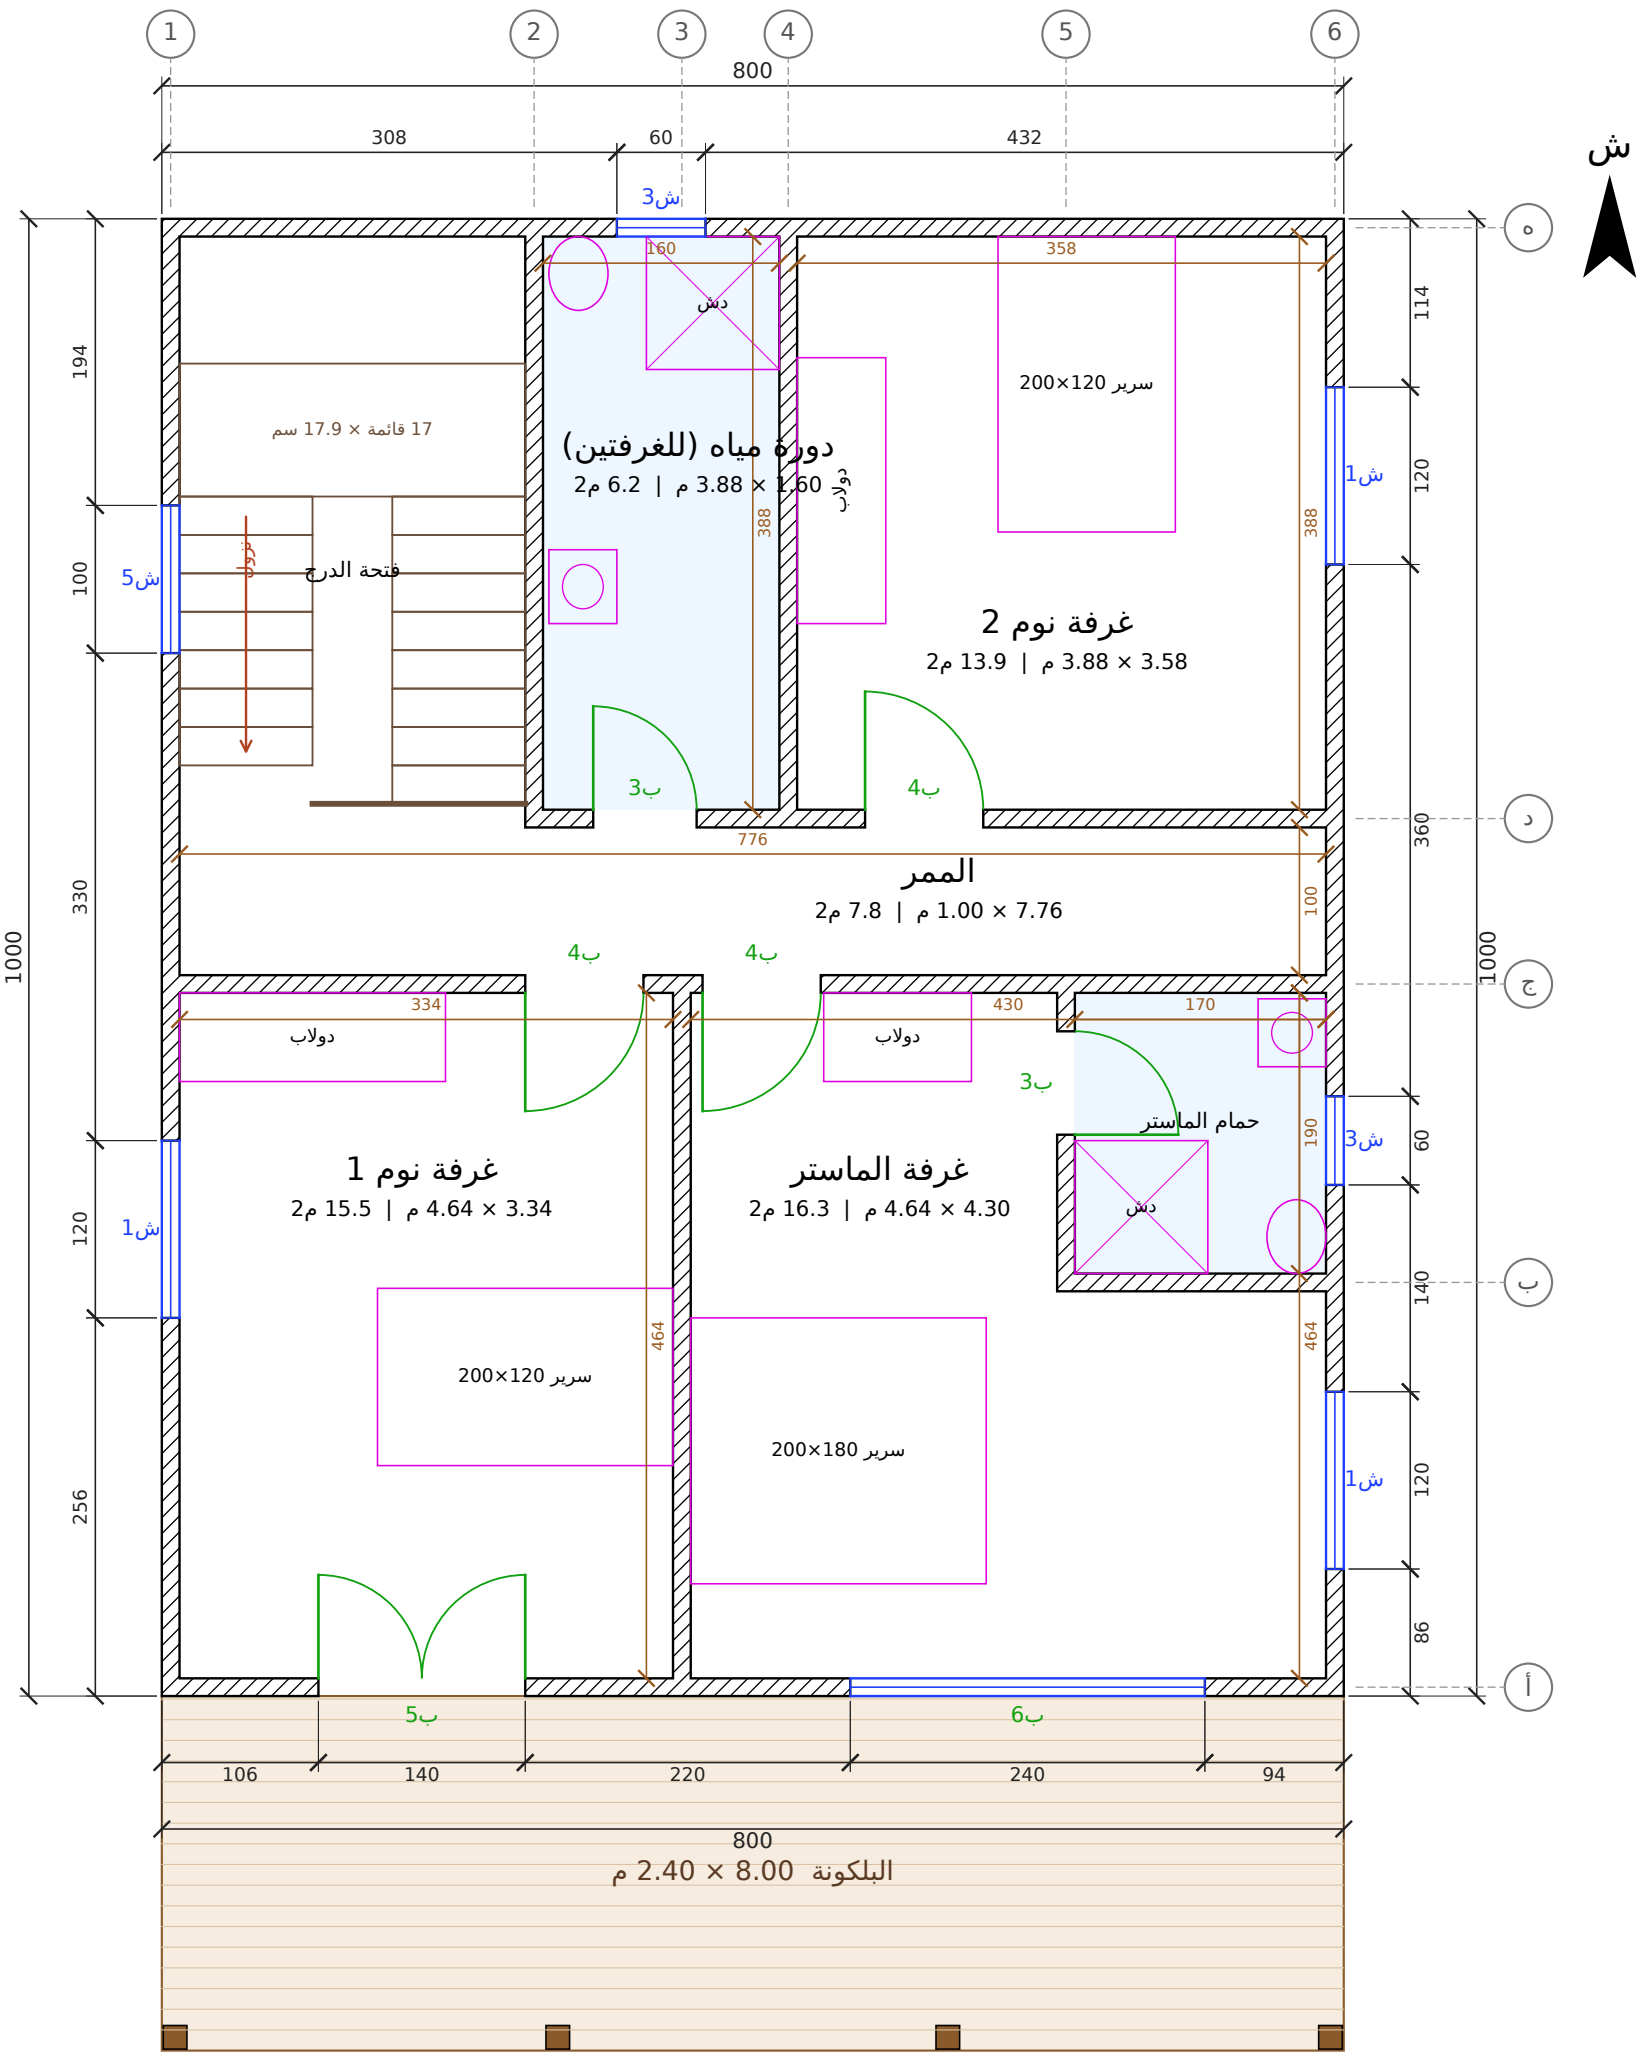


المشروع / العميل	عنوان اللوحة	المقياس	التاريخ	رقم اللوحة
مصنع وتد الأخشاب Watad Wood Factory **كوخ دورين + تنسيق حديقة ومسبح — جدة** **عميل جديد — جدة**	**المسقط الأفقي — الدور الأول**	**1:50**	**2026-10-18**	**A-03 (3/12)**

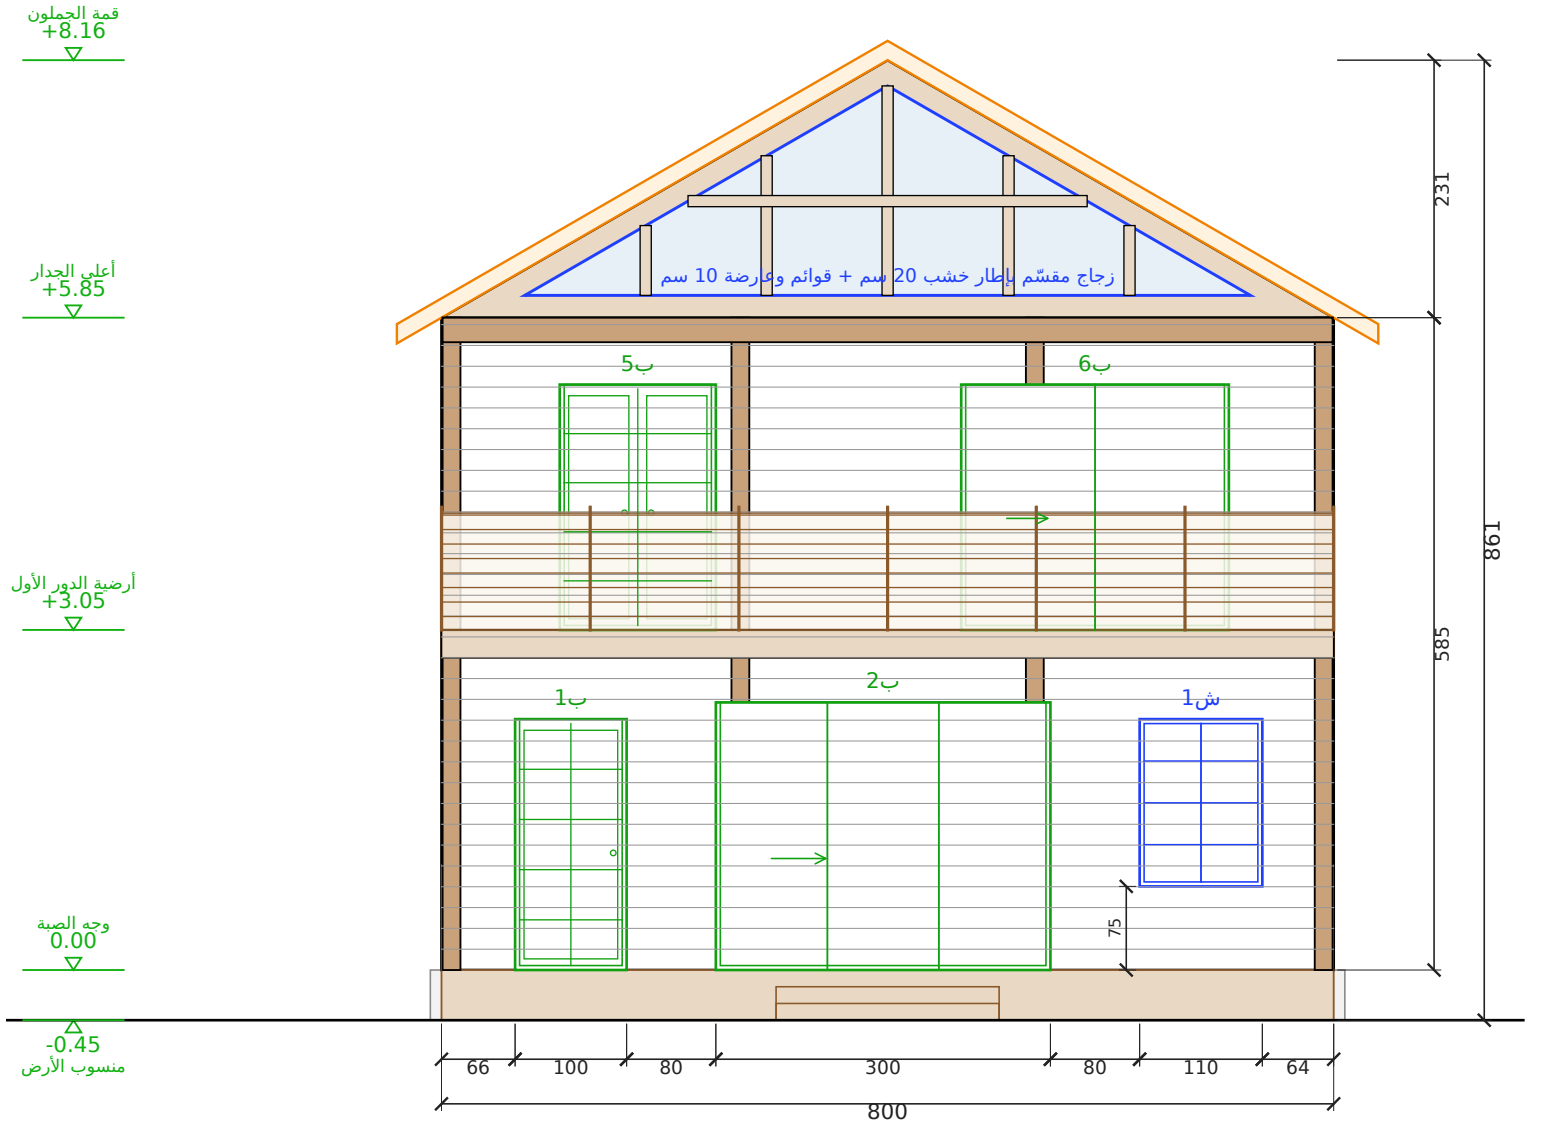

الواجهة الأمامية (على الحديقة)

مقياس 1:50 | الوحدة: سم

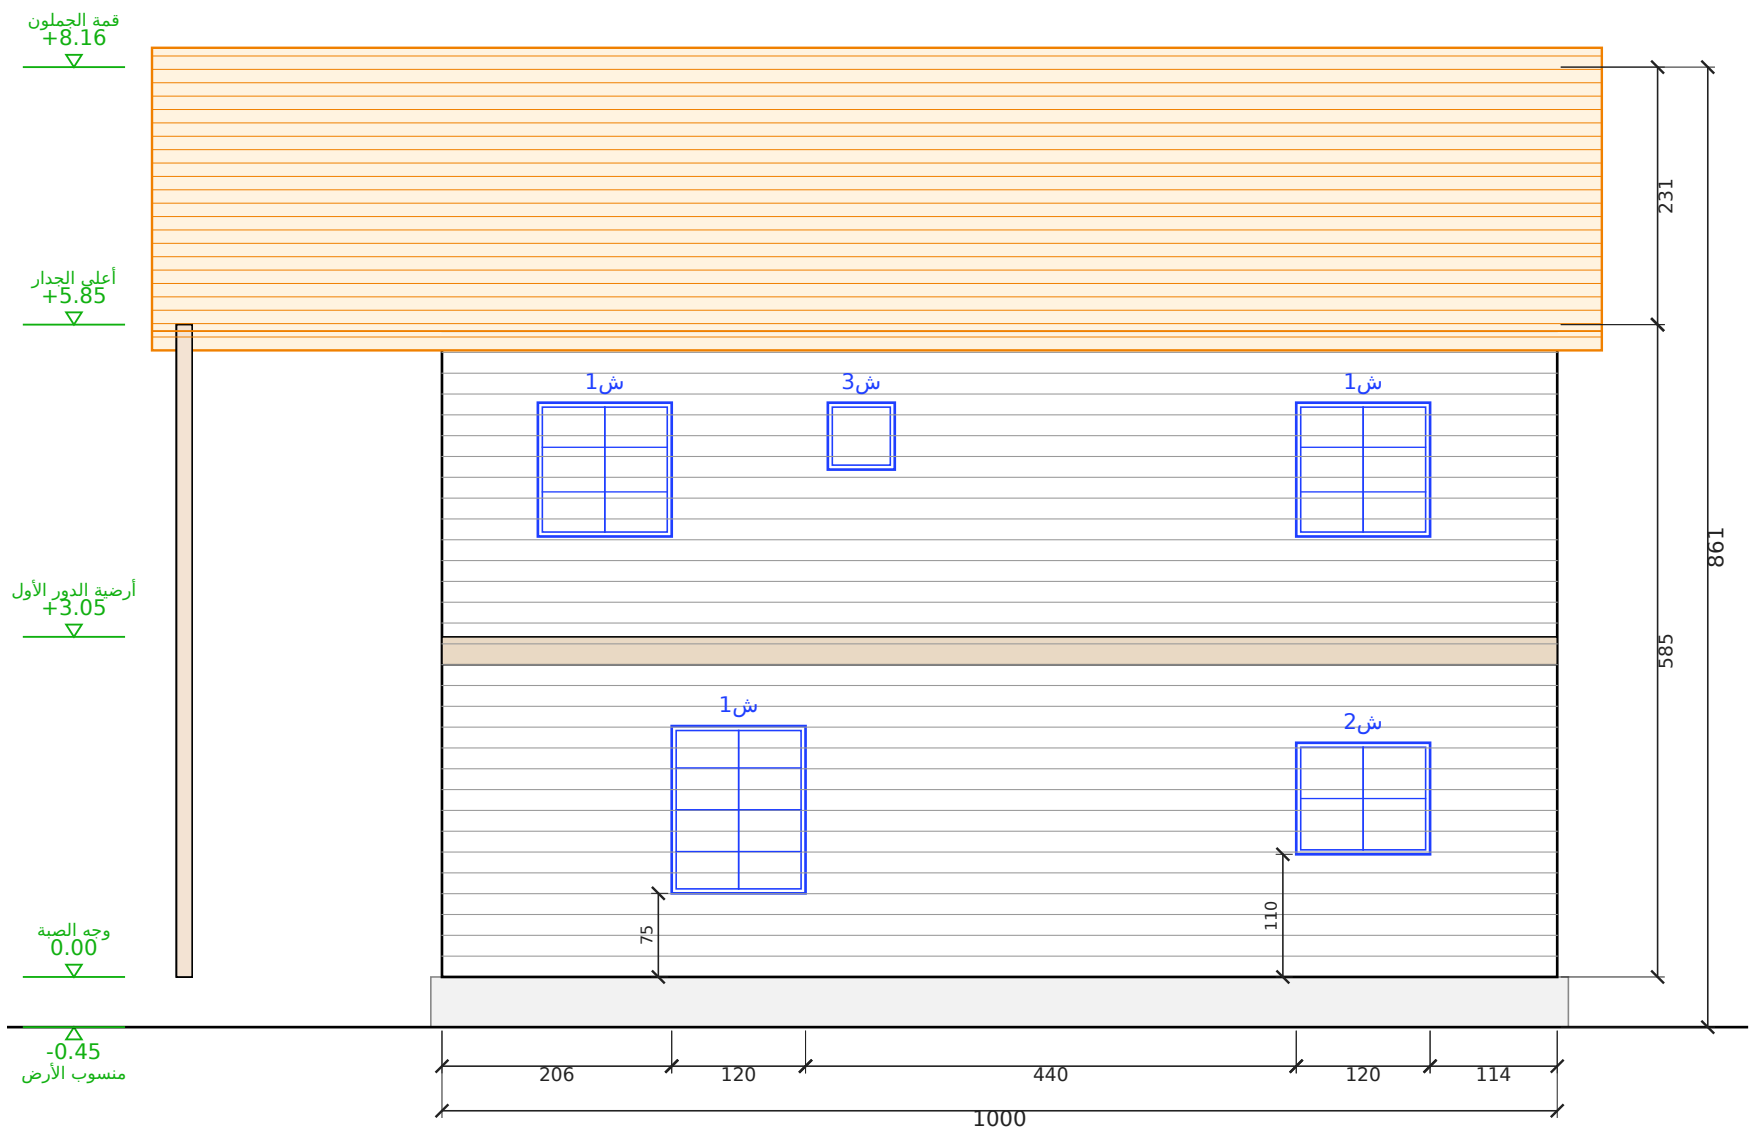


الواجهة الشرقية

مقياس 1:50 | الوحدة: سم


المشروع / العميل	عنوان اللوحة	المقياس	التاريخ	رقم اللوحة
كوخ دورين + تنسيق حديقة ومسبح — جدة عميل جديد — جدة	الواجهة الأمامية (على الحديقة) والواجهة الشرقية	1:50	2026-10-18	A-04 (4/12)

مصنع وتد الأخشاب
Watad Wood Factory

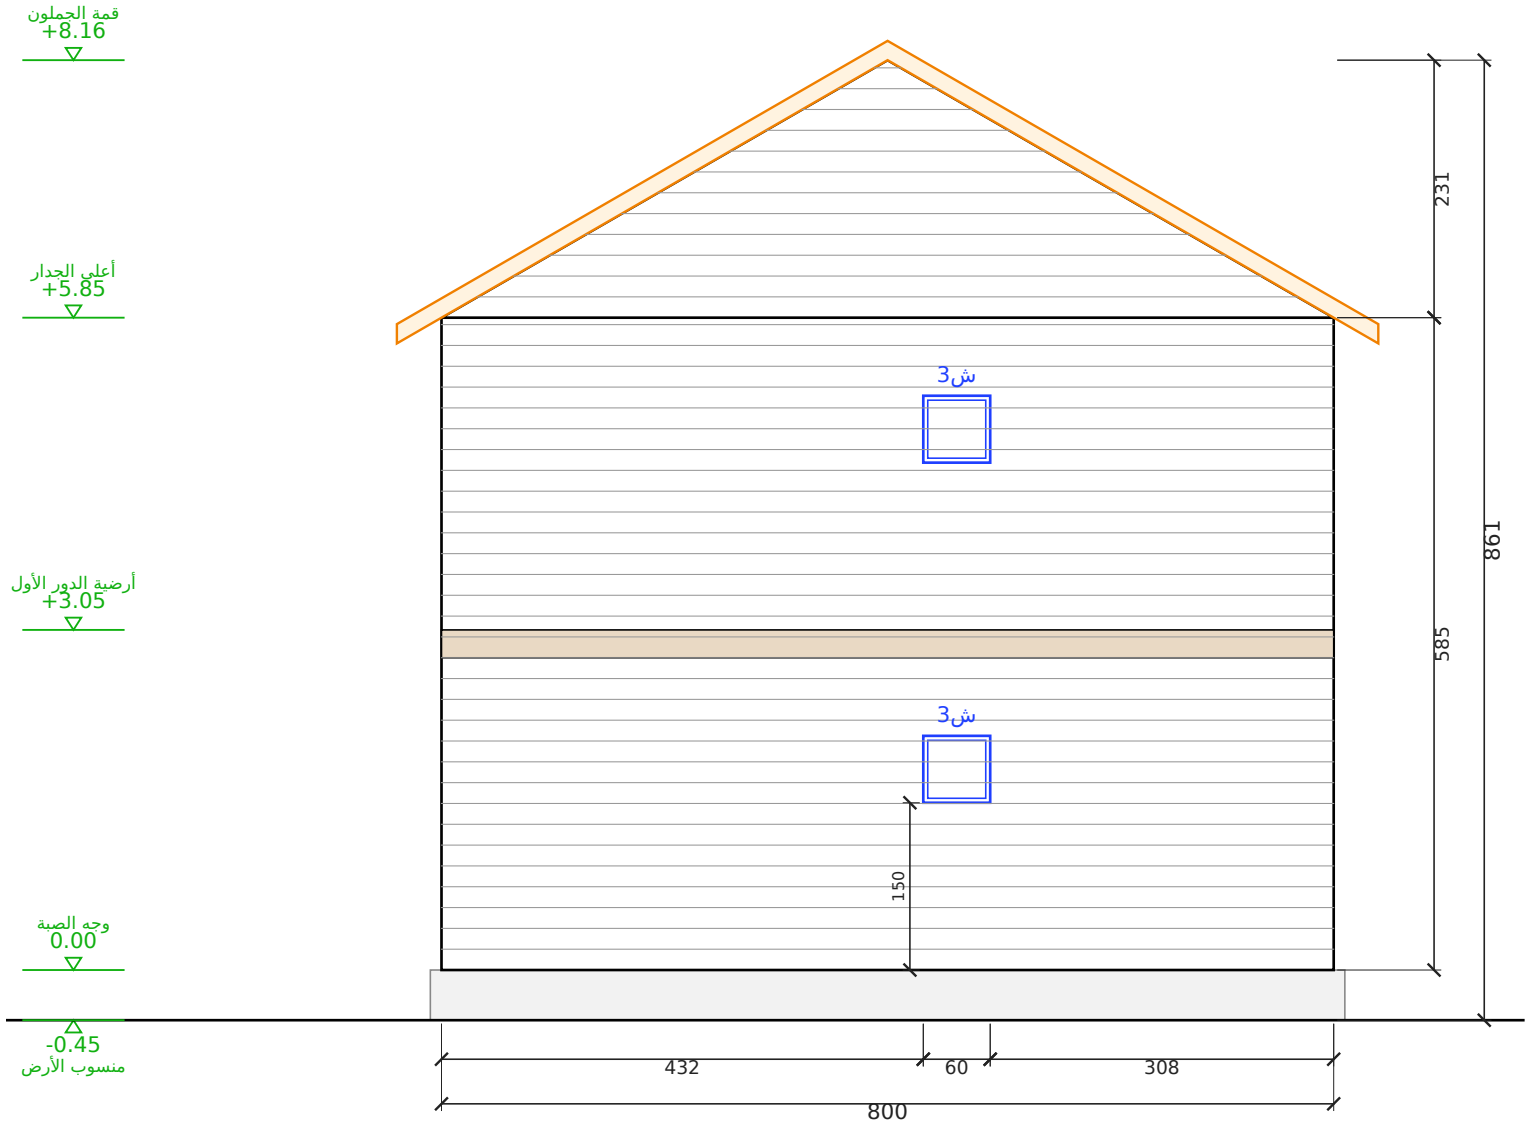

الواجهة الخلفية

مقياس 1:50 | الوحدة: سم

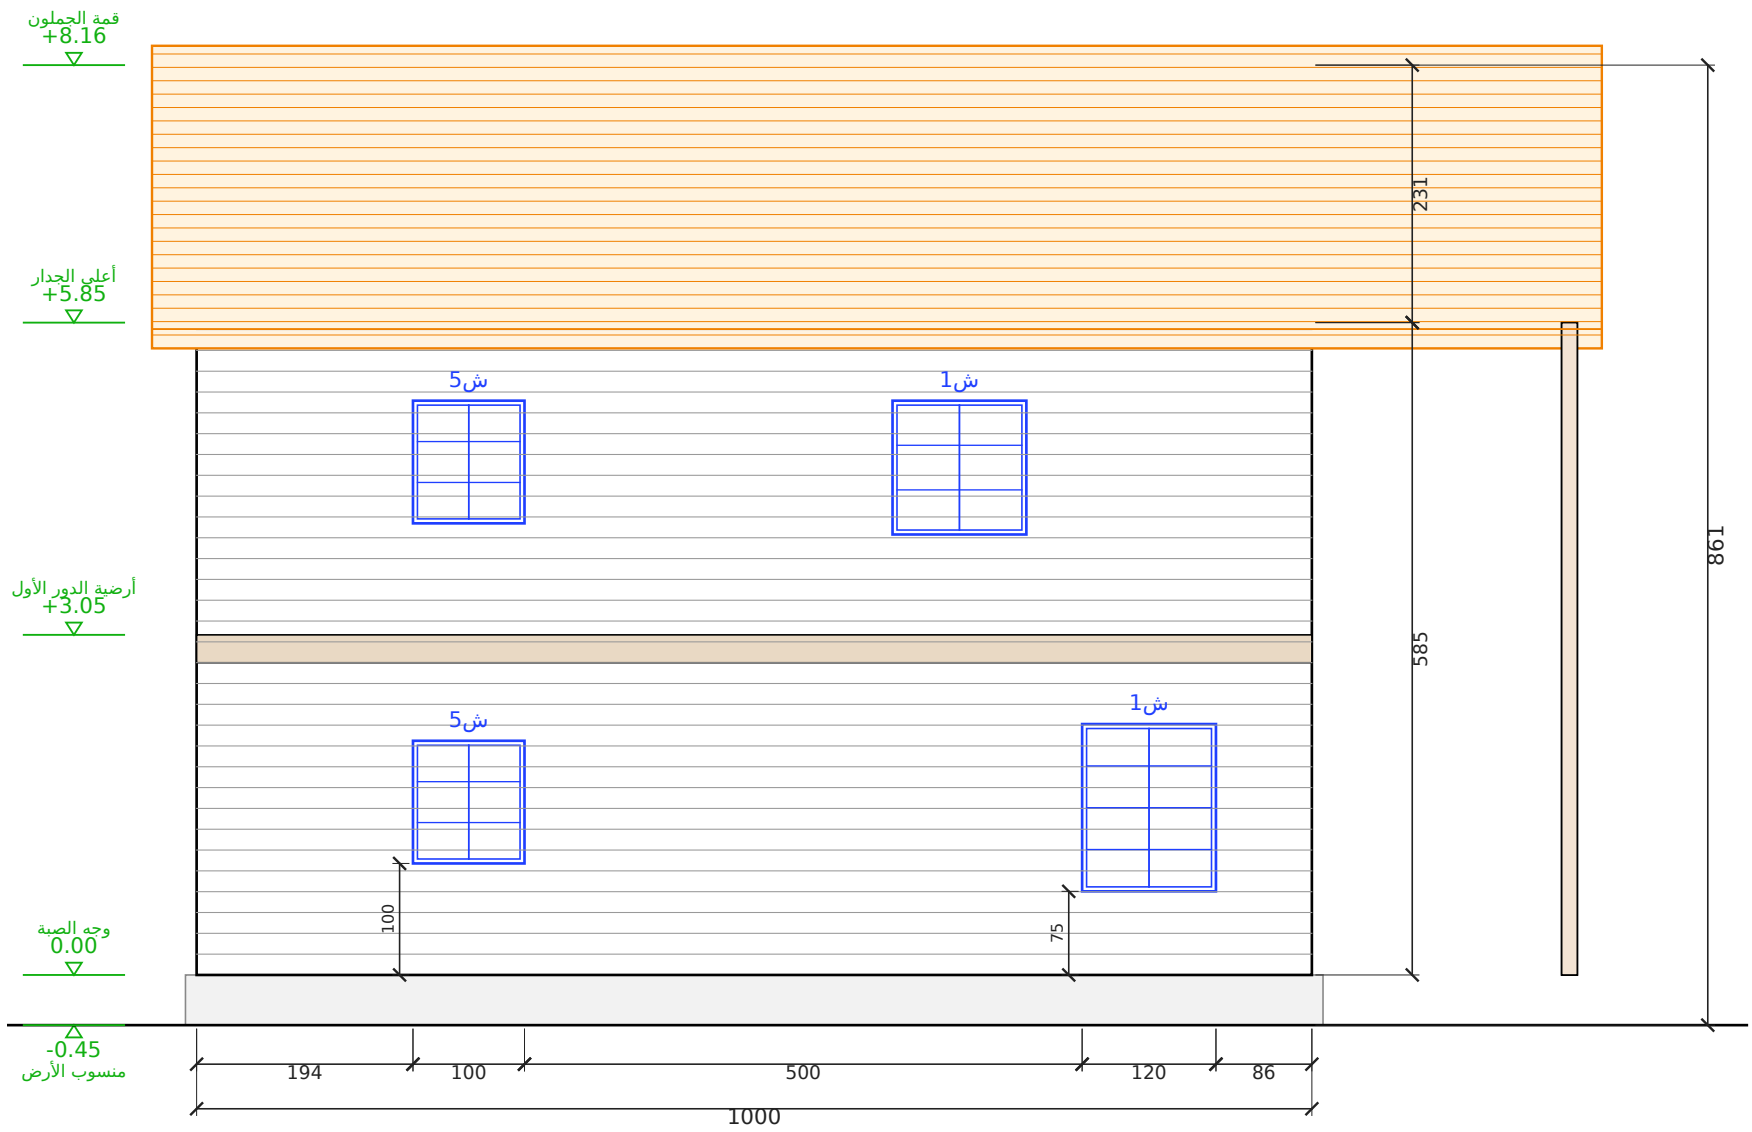


الواجهة الغربية

مقياس 1:50 | الوحدة: سم


المشروع / العميل	عنوان اللوحة	المقياس	التاريخ	رقم اللوحة
كوخ دورين + تنسيق حديقة ومسبح — جدة **عميل جديد — جدة**	**الواجهة الخلفية والواجهة الغربية**	**1:50**	**2026-10-18**	**A-05 (5/12)**

مصنع وتد الأخشاب
Watad Wood Factory


مسقط السقف (جملون)
رفرف 40 سم من كل جهة | مقياس 1:50

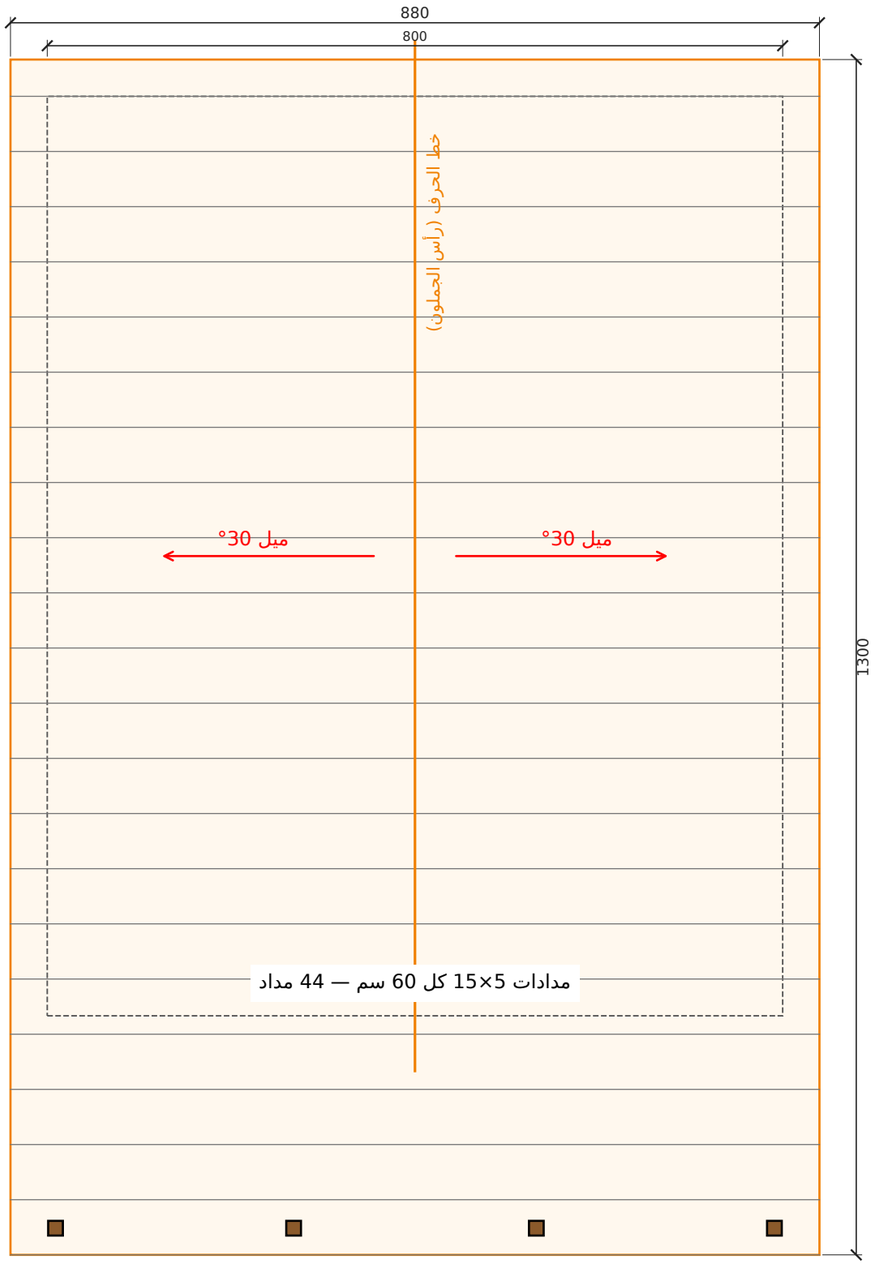

قطاع عرضي أ-أ
مقياس 1:50 | الوحدة: سم

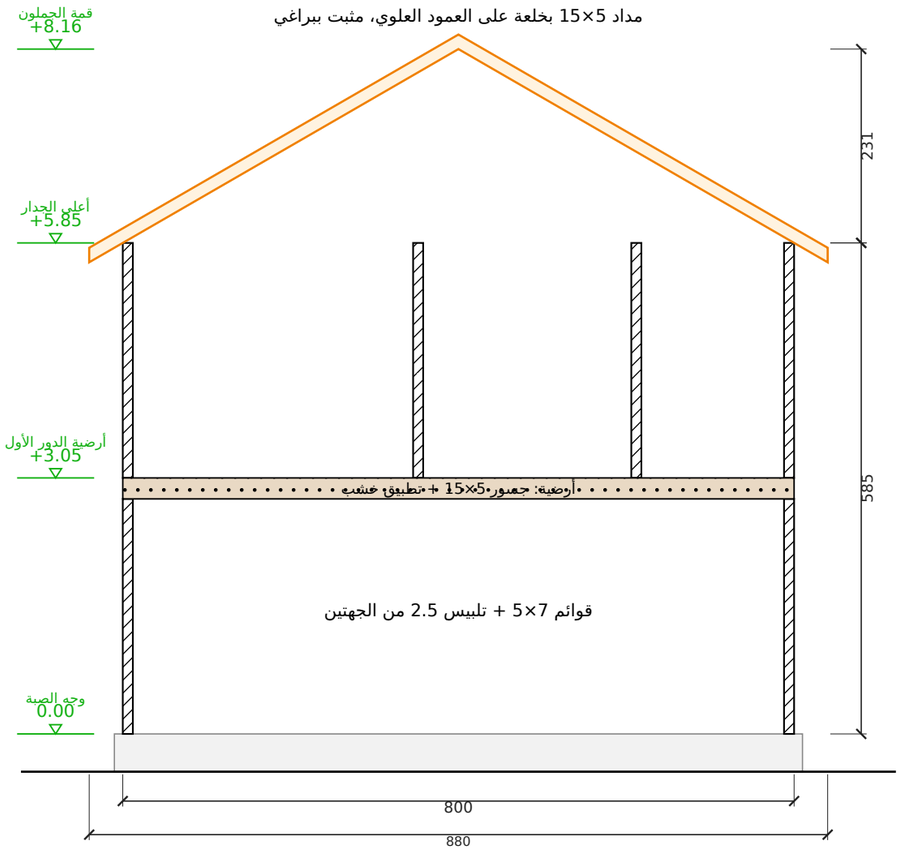

تفصيلة جلوس المداد على العلوي (1:5)

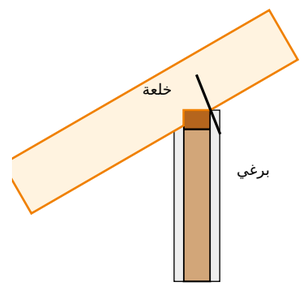

علوي 7×5 على قائم 7×5

المشروع / العميل	عنوان اللوحة	المقياس	التاريخ	رقم اللوحة
كوخ دورين + تنسيق حديقة ومسبح — جدة **عميل جديد — جدة**	**مسقط السقف والقطاع**	**1:50**	**2026-10-18**	**A-06 (6/12)**

مصنع وتد الأخشاب
Watad Wood Factory

جدول مقاسات الأبواب والشبابيك
مقاس الفتحة الصافي في الجدار - الوحدة: سم

الرمز	النوع	العرض (سم)	الارتفاع (سم)	ارتفاع الجلسة (سم)	العدد	الموقع
ب1	باب	100	225	-	1	الأمامية (على الحديقة)
ب2	باب	300	240	-	1	الأمامية (على الحديقة)
ب3	باب	70	210	-	3	دورة المياه 2 - حمام الماستر
ب4	باب	80	210	-	3	غرفة 1 - الماستر - غرفة 2
ب5	باب مزدوج	140	220	-	1	الأمامية (على الحديقة)
ب6	باب مزدوج	240	220	-	1	الأمامية (على الحديقة)
ش1	شباك	110	150	75	1	الأمامية (على الحديقة)
ش1	شباك	120	150	75	2	الشرقية - الغربية
ش1	شباك	120	120	90	3	الشرقية 2 - الغربية
ش2	شباك	120	100	110	1	الشرقية
ش3	شباك	60	60	150	3	الخلفية 2 - الشرقية
ش5	شباك	100	110	100	2	الغربية 2

الإجمالي: أبواب 10 - شبابيك 12

جدول المساحات وبيانات المشروع والتسعير

بيانات المشروع

البند	البيان
المشروع	كوخ دورين + تنسيق حديقة ومسبح — جدة
العميل	عميل جديد — جدة
الموقع	جدة
الاستخدام	سكن خاص / استجمام
التاريخ	2026-10-18
نظام البناء	هيكل خشب 5×7 + تلبيس 2.5 سم من الجهتين
السقف	جملون 30° — قرميد معدني

التسعير

البند	القيمة
المساحة الكلية — الكوخ + التراس والبلكونة (م2)	200.00
سعر المتر المربع	1,096 ريال
الإجمالي	**219,200 ريال**

ملاحظات:

- السعر على المساحة الكلية 200 م²: الدورين 160 + التراس 20.8 + البلكونة 19.2 (شامل الأعمدة).
- أعمال الموقع (السور، المسبح، الحديقة، البيارة، الخزان، التمديدات الخارجية) تقديرية بأسعار السوق وتُنفّذ مع مقاول الموقع.

جدول المساحات


م	الفراغ	الأبعاد (م)	المساحة (م2)
1	أرضي — الصالة	7.76 × 5.80	45.01
2	أرضي — الدرج	2.34 × 3.00	7.02
3	أرضي — دورة مياه	1.60 × 2.60	4.16
4	أرضي — المطبخ	3.58 × 3.84	13.75
5	أول — غرفة نوم 1	3.34 × 4.64	15.50
6	أول — غرفة الماستر	4.30 × 4.64	16.28
7	أول — حمام الماستر	1.70 × 1.90	3.23
8	أول — الممر	7.76 × 1.00	7.76
9	أول — دورة مياه (للغرفتين)	1.60 × 3.88	6.21
10	أول — غرفة نوم 2	3.58 × 3.88	13.89
	المساحة الصافية الداخلية		132.80
	تراس الكوخ	**8.00 × 2.60**	**20.80**
	البلكونة	**8.00 × 2.40**	**19.20**
	المساحة الإجمالية المبنية	**8.00 × 10.00 × 2 دور**	**160.00**
	المساحة الكلية (المبنية + التراس والبلكونة)		**200.00**

لقطات المنظور الخارجي


المنظور الأمامي




منظور أمامي من اليسار

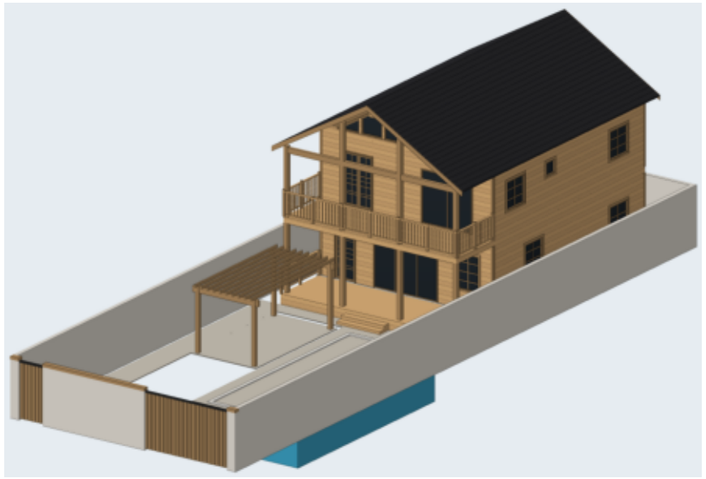


منظور أمامي من اليمين

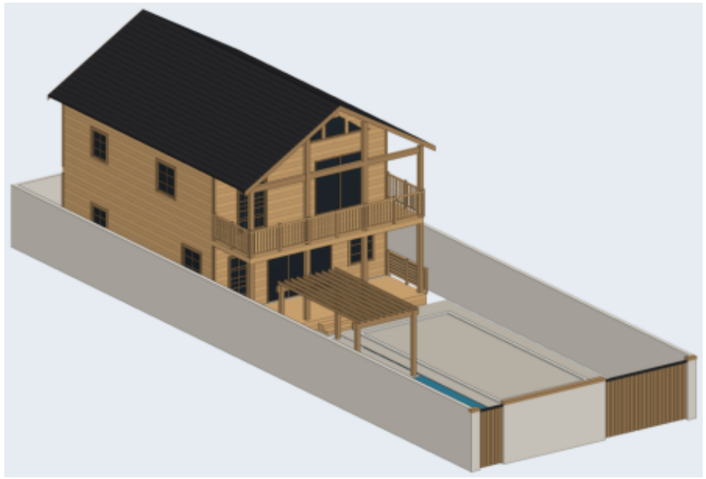


المنظور الخلفي

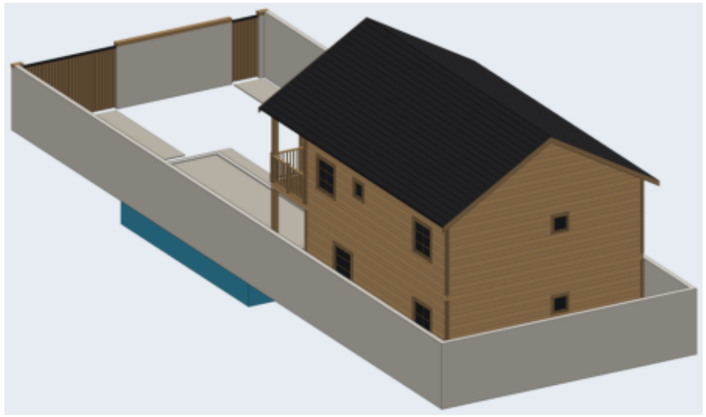

منظور خلفي من اليمين

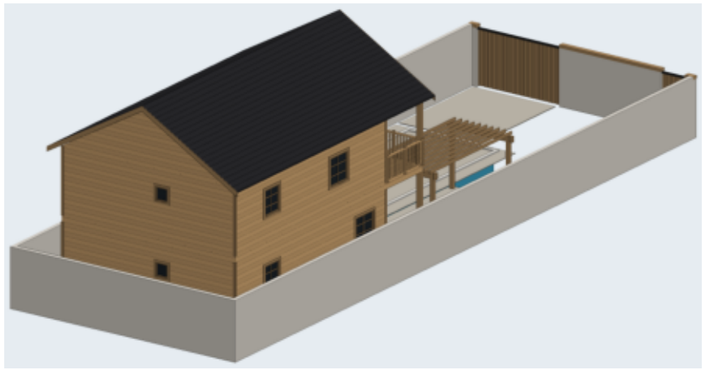

منظر علوي

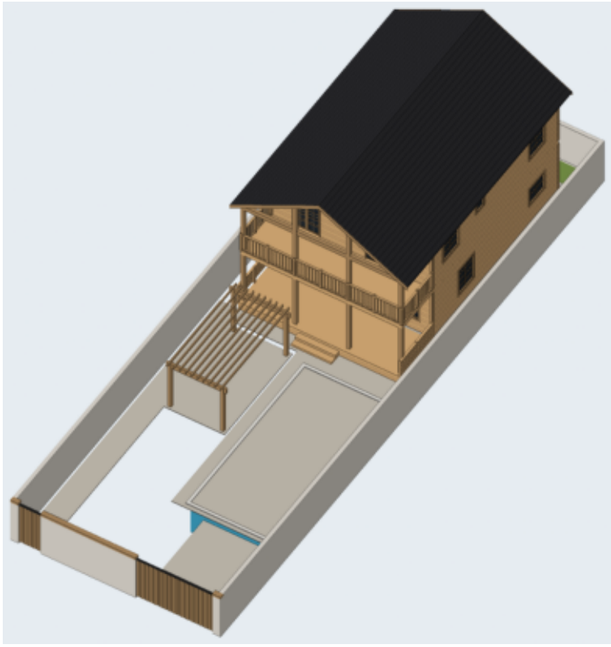


المشروع / العميل	عنوان اللوحة	المقياس	التاريخ	رقم اللوحة
كوخ دورين + تنسيق حديقة ومسبح — جدة **عميل جديد — جدة**	**لقطات المنظور**	**—**	**2026-10-18**	**A-09 (9/12)**

مصنع وتد الأخشاب
Watad Wood Factory

المقطع العلوي بالفرش — الدور الأرضي

مقطع أفقي على ارتفاع 1.90 م — توزيع الفرش ومسار الحركة

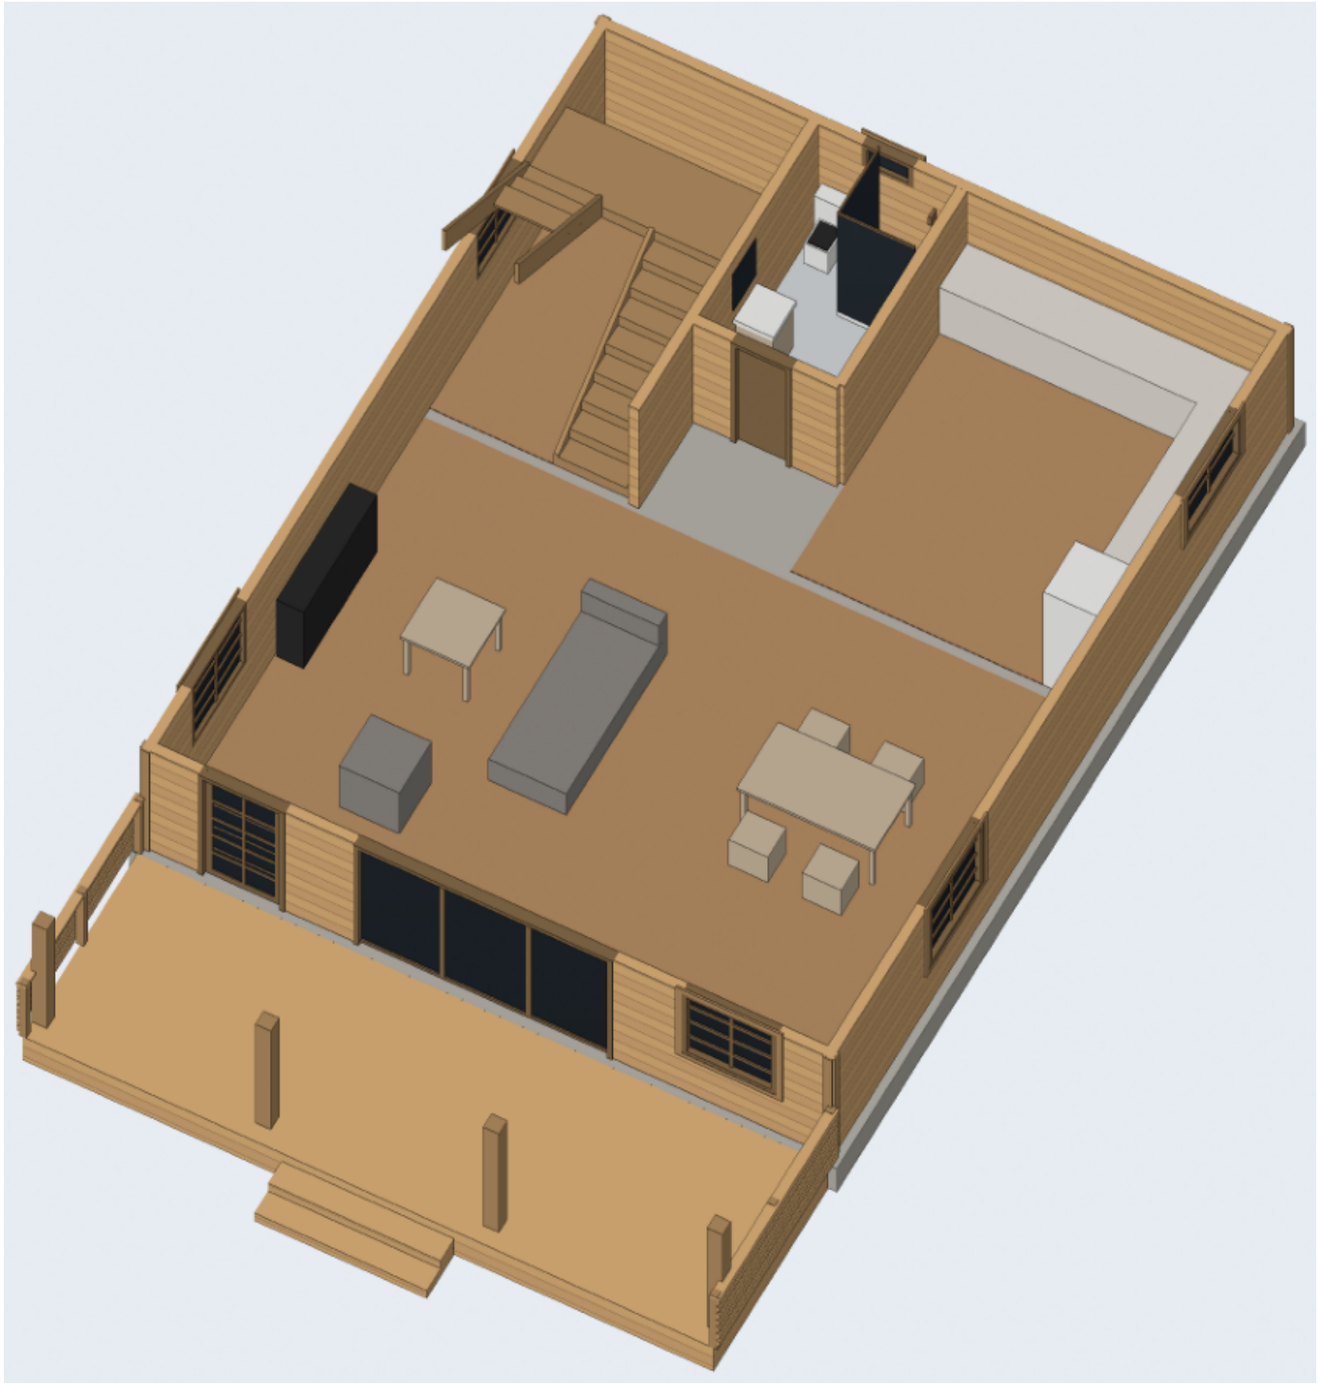


المشروع / العميل	عنوان اللوحة	المقياس	التاريخ	رقم اللوحة
كوخ دورين + تنسيق حديقة ومسبح — جدة **عميل جديد — جدة**	**المقطع العلوي بالفرش — الدور الأرضي**	**—**	**2026-10-18**	**A-10 (10/12)**

مصنع وتد الأخشاب
Watad Wood Factory

المقطع العلوي بالفرش — الدور الأول

مقطع أفقي على ارتفاع 1.90 م — توزيع الفرش ومسار الحركة

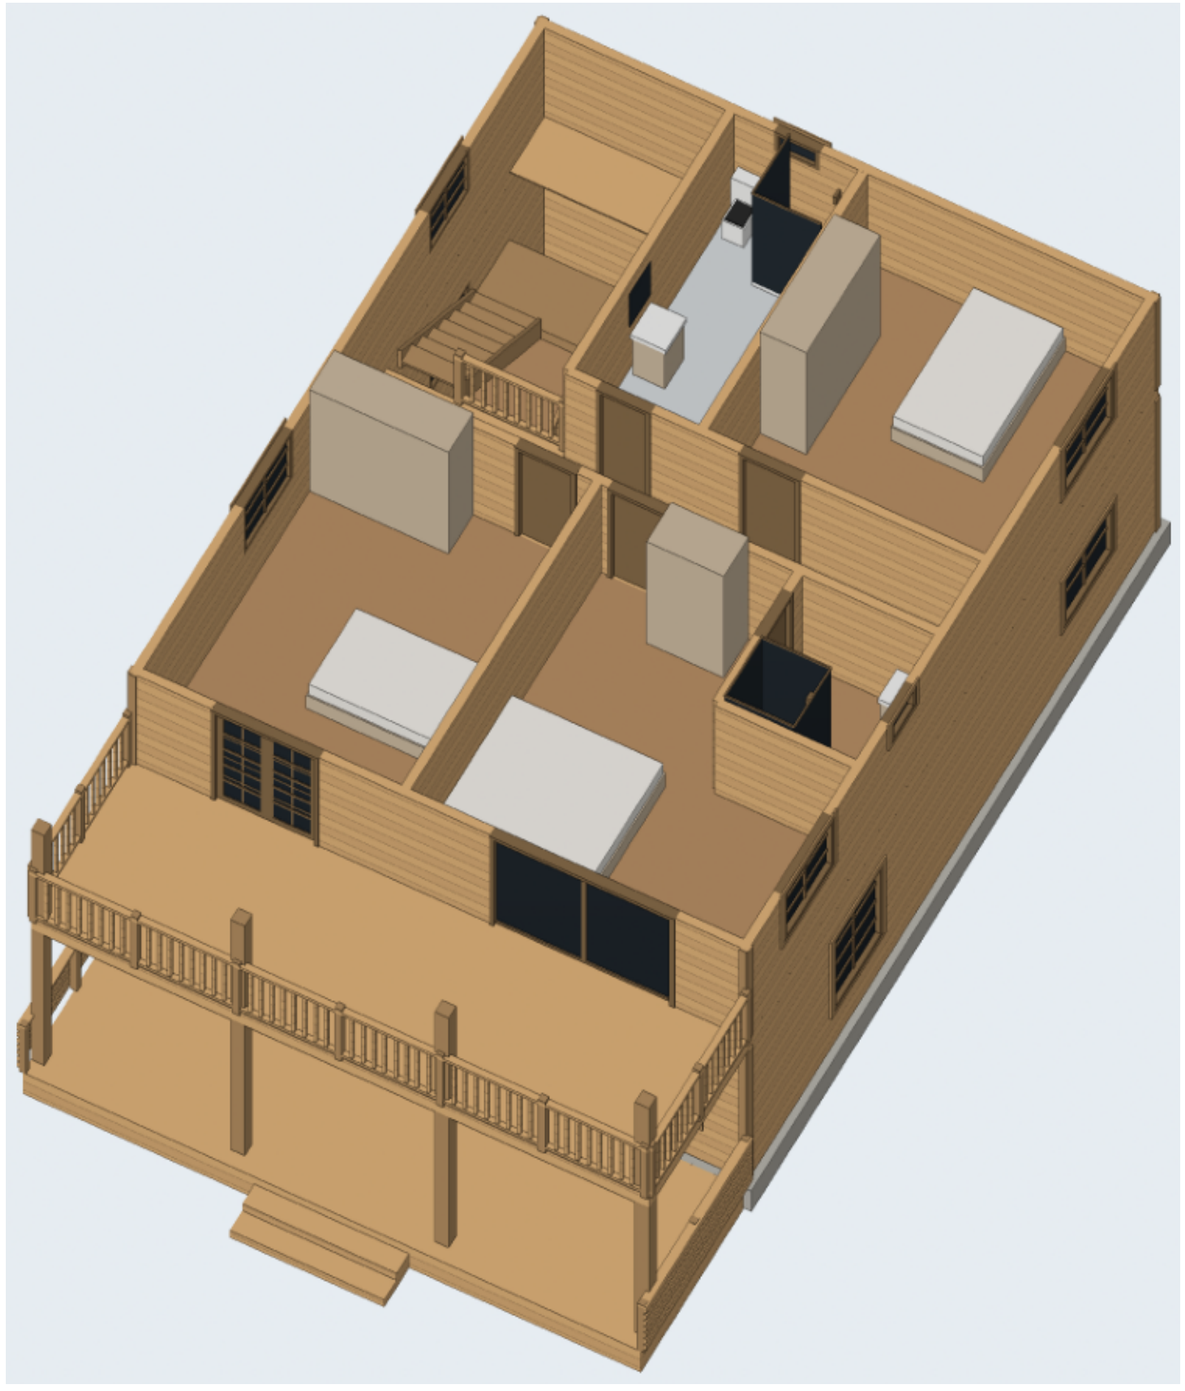


المشروع / العميل	عنوان اللوحة	المقياس	التاريخ	رقم اللوحة
كوخ دورين + تنسيق حديقة ومسبح — جدة **عميل جديد — جدة**	**المقطع العلوي بالفرش — الدور الأول**	**—**	**2026-10-18**	**A-11 (11/12)**

مصنع وتد الأخشاب
Watad Wood Factory

المنظور ثلاثي الأبعاد والمواد

النمط: جوزي غامق + إطارات سوداء — رندر واقعي بخامات حقيقية

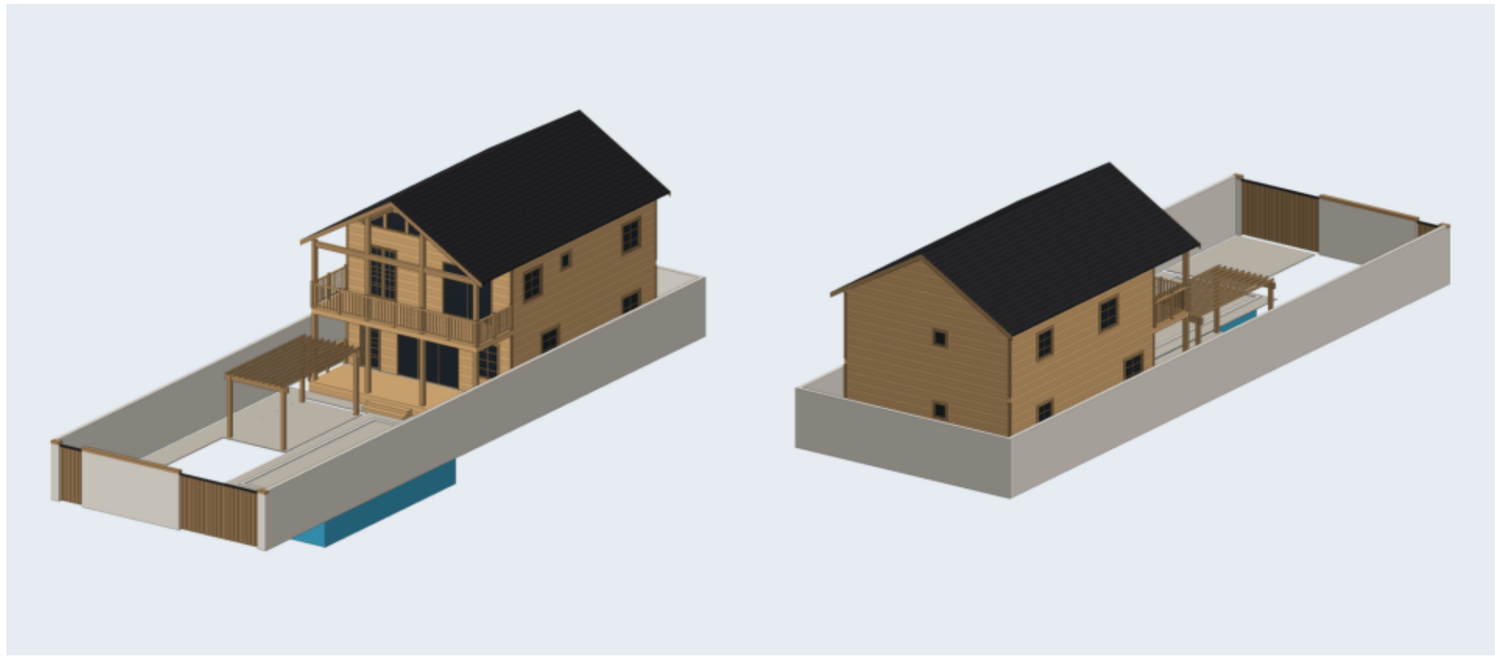

جدول المواد والألوان

الخشب / الصبغة

خشب طبيعي فاتح (بدون صبغة)

القرميد

قرميد رمادي غامق

الزجاج

زجاج عاكس غامق

إطارات الشبابيك والأبواب

إطار خشب بنفس الصبغة أغمق

الكنار والزوايا

نفس الصبغة أغمق درجة


الصبة

خرسانة 45 سم


الدربزين: ألواح أفقية متقاربة (عصري)

تقسيم الشبابيك: بدون | الباب الرئيسي: زجاج بتقسيمات (فرنسي)

أنواع الدربزين المعتمدة (من مشاريع المصنع)

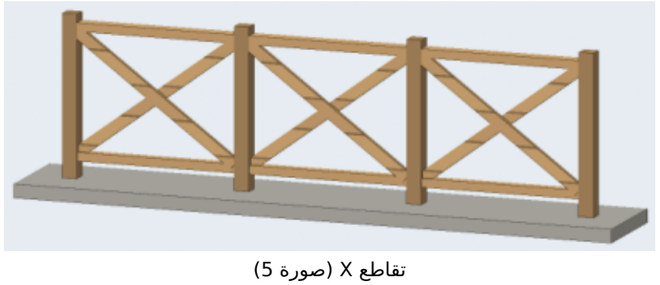

تقاطع X (صورة 5)

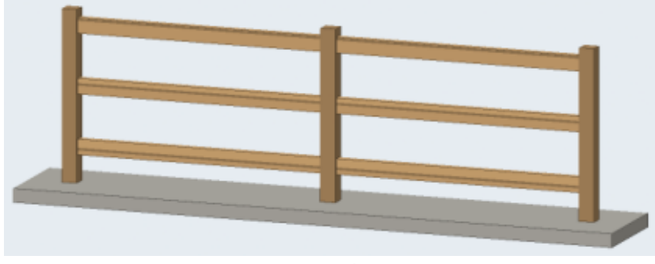

3 مرابيع أفقية (صورة 2)



قوائم رأسية متقاربة (صورة 1)

المشروع / العميل	عنوان اللوحة	المقياس	التاريخ	رقم اللوحة
كوخ دورين + تنسيق حديقة ومسبح — جدة **عميل جديد — جدة**	**المنظور والمواد**	**—**	**2026-10-18**	**A-12 (12/12)**

مصنع وتد الأخشاب
Watad Wood Factory