
المسقط الأفقي مع الفرش — الدور الأرضي

الأبعاد بالسنتيمتر - الجدران: قوائم 7×5 + تلبيس 2.5 من الجهتين (12 سم) | منسوب الأرضية +0.00

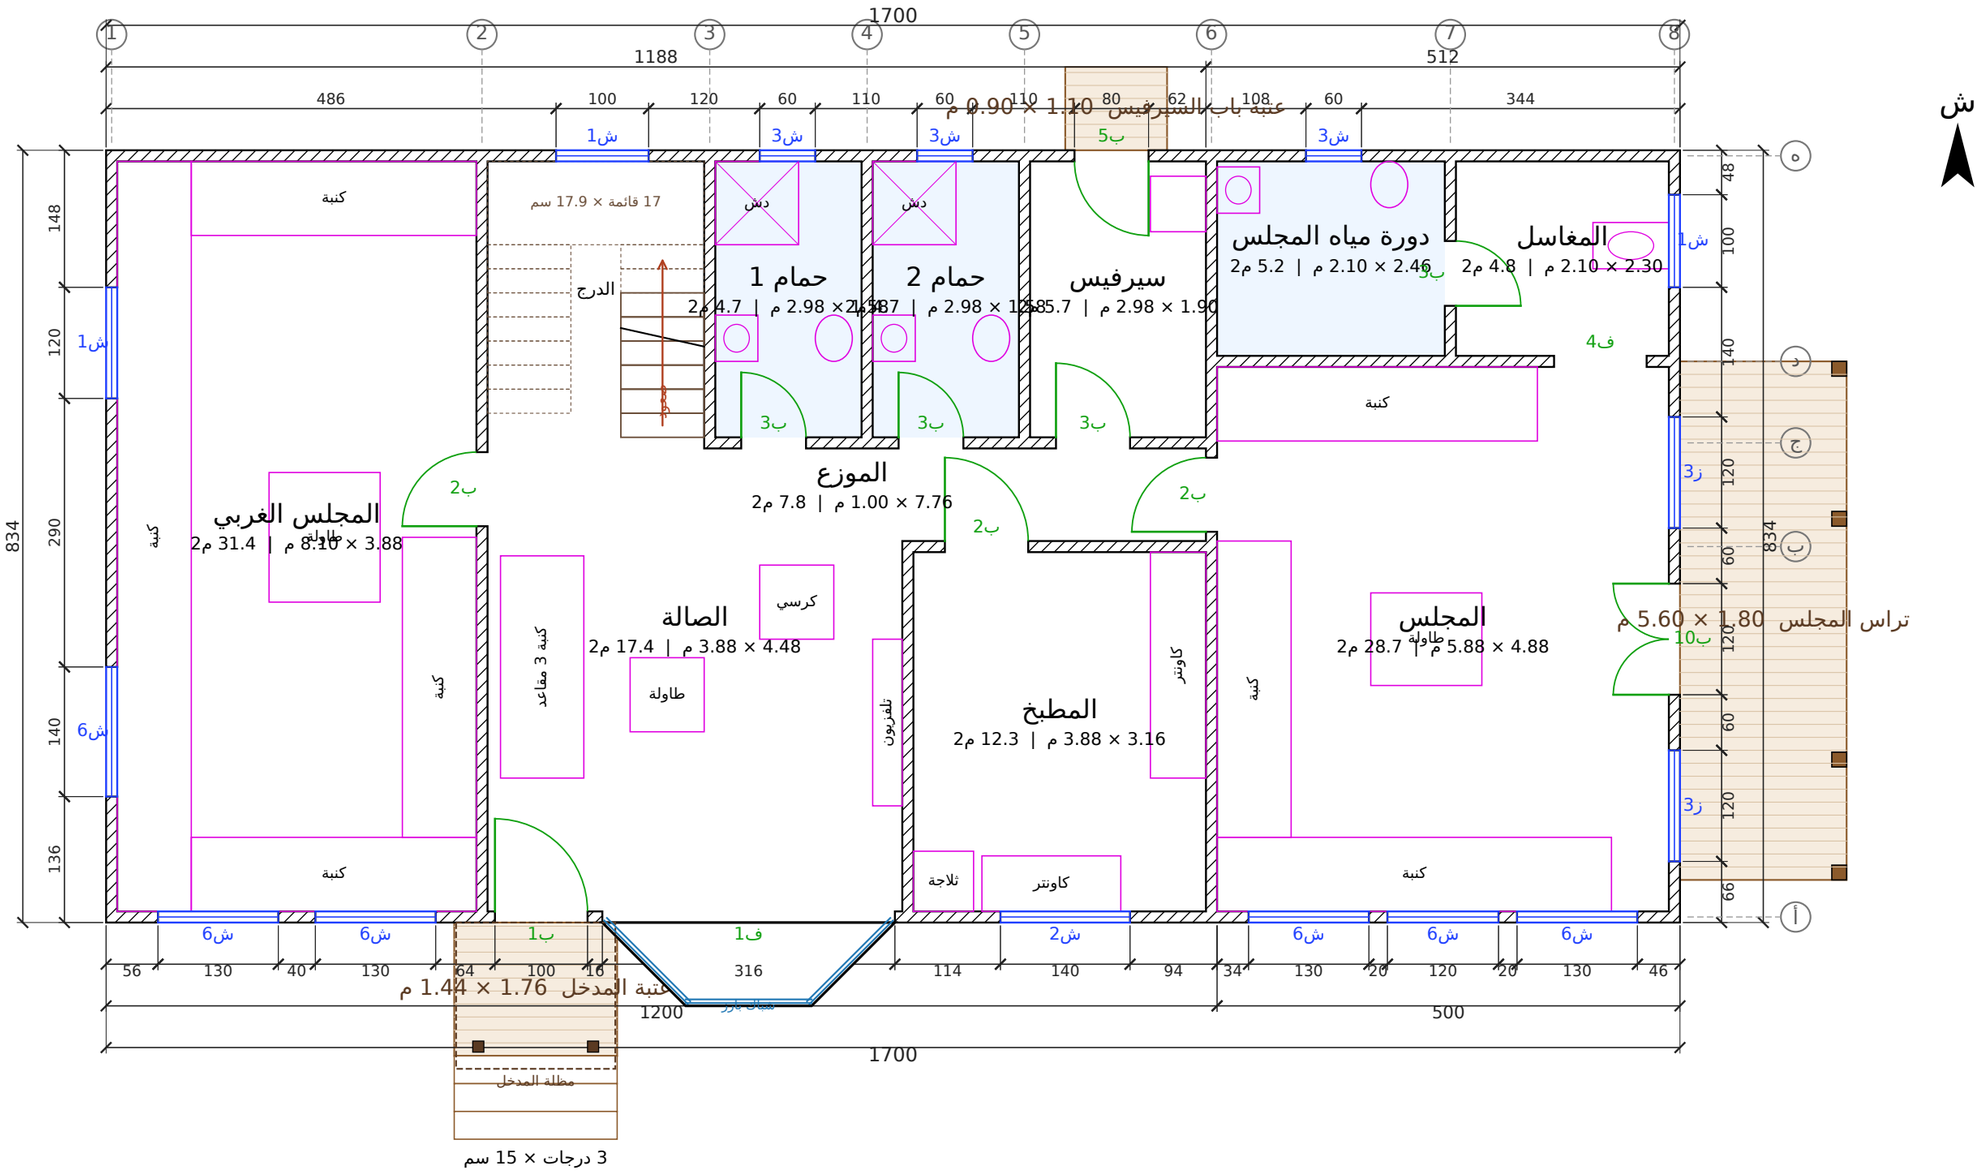


المشروع / العميل	عنوان اللوحة	المقياس	التاريخ	رقم اللوحة
كوخ دورين + ملحق مجلس — 5 غرف **عميل جديد**	**المسقط الأفقي — الدور الأرضي**	**1:50**	**2026-10-17**	**A-01 (1/14)**

مصنع وتد الأخشاب
Watad Wood Factory

المسقط الأفقي مع الفرش — الدور الأول

الأبعاد بالسنتيمتر - الجدران: قوائم 5×7 + تلبيس 2.5 من الجهتين (12 سم) | منسوب الأرضية +3.05

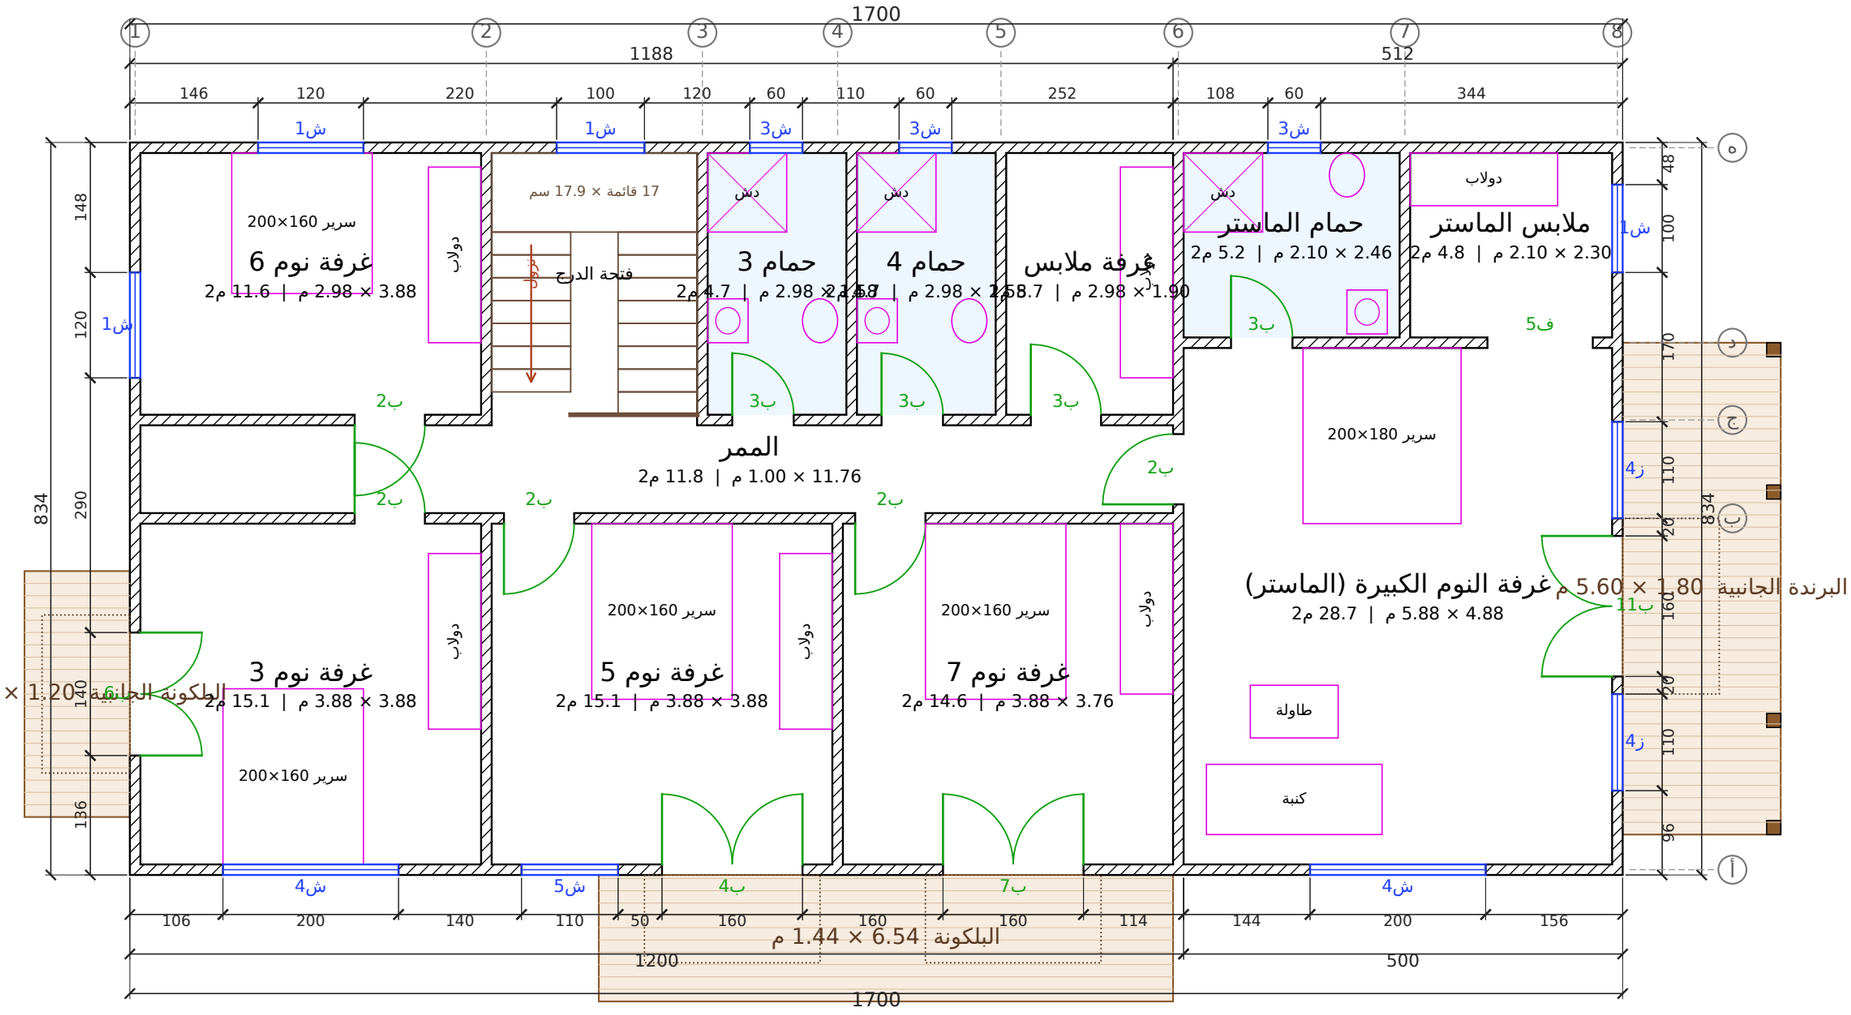


المشروع / العميل	عنوان اللوحة	المقياس	التاريخ	رقم اللوحة
كوخ دورين + ملحق مجلس — 5 غرف عميل جديد	المسقط الأفقي — الدور الأول	1:50	2026-10-17	A-02 (2/14)

مصنع وتد الأخشاب
Watad Wood Factory



الواجهة الأمامية

مقياس 1:50 | الوحدة: سم

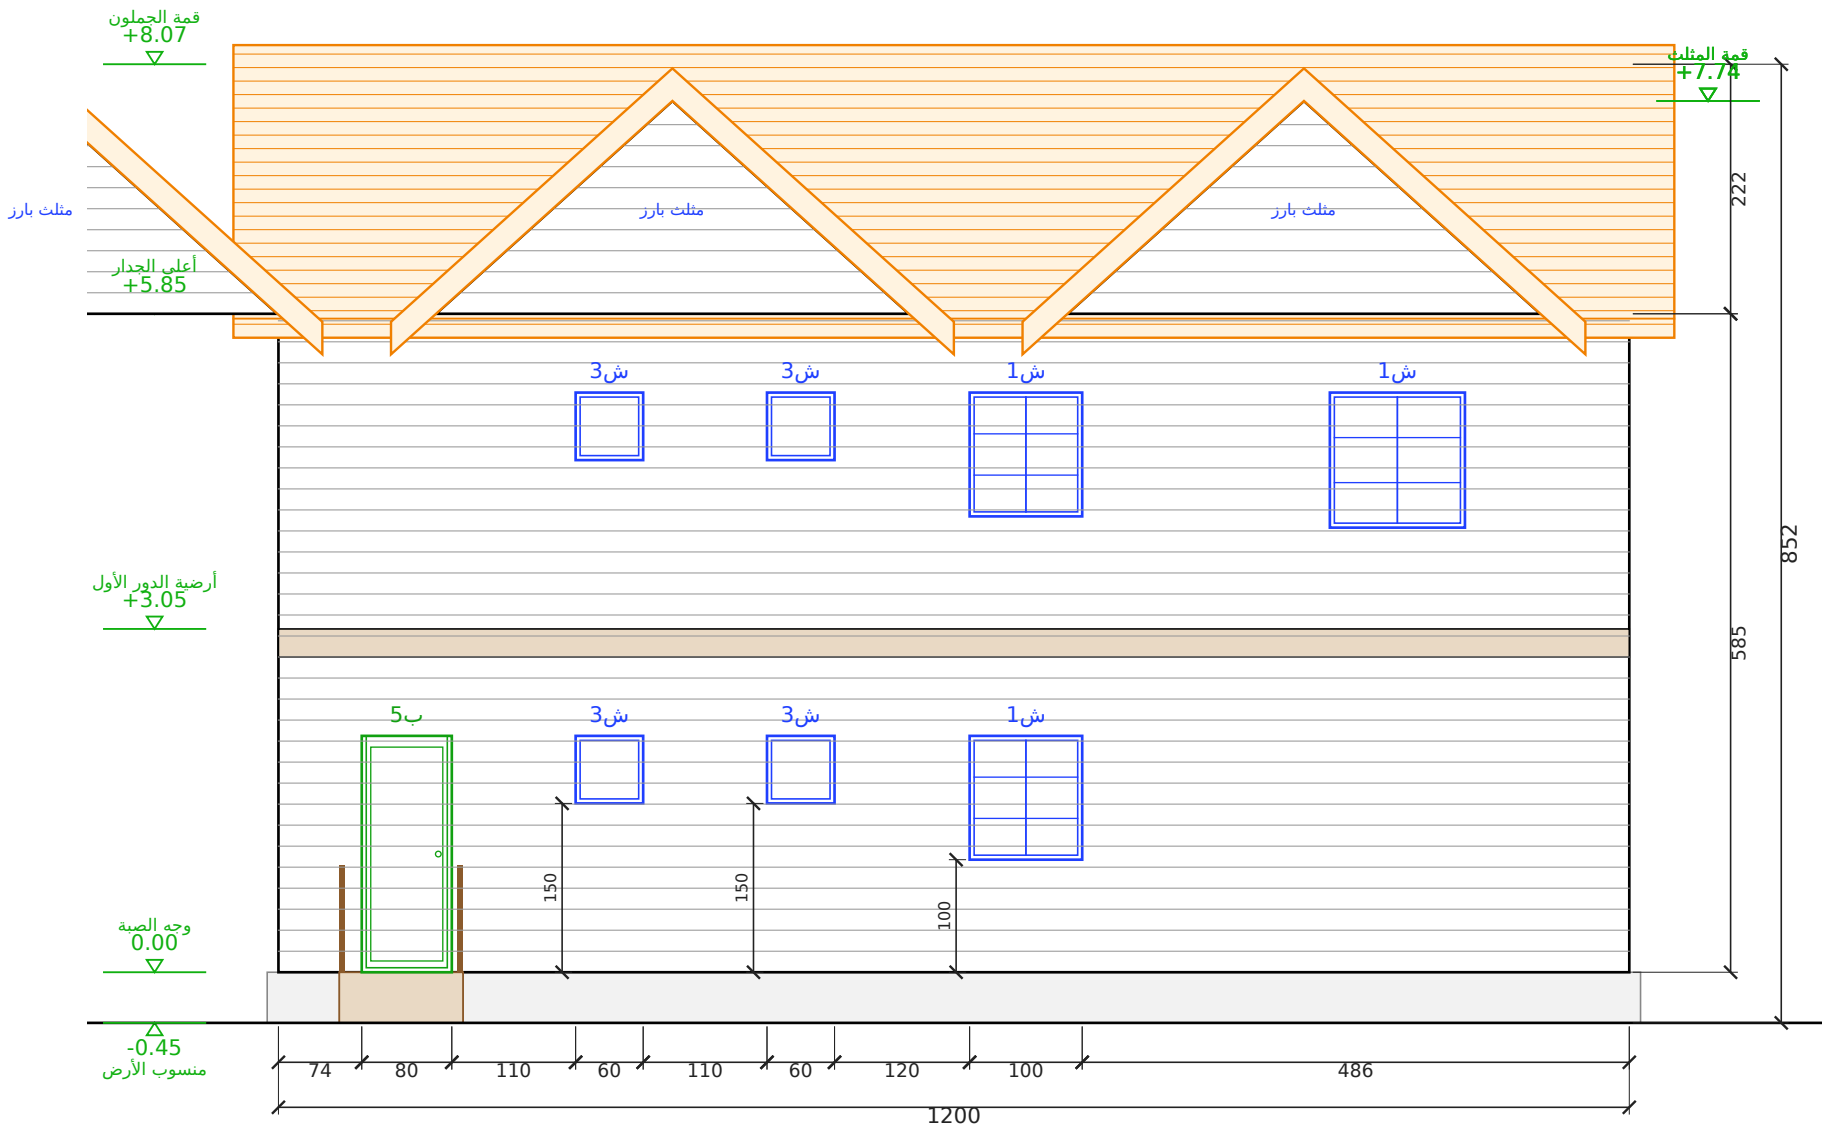


الواجهة الخلفية

مقياس 1:50 | الوحدة: سم


المشروع / العميل	عنوان اللوحة	المقياس	التاريخ	رقم اللوحة
كوخ دورين + ملحق مجلس — 5 غرف **عميل جديد**	**الواجهة الأمامية والواجهة الخلفية**	**1:50**	**2026-10-17**	**A-03 (3/14)**

مصنع وتد الأخشاب
Watad Wood Factory

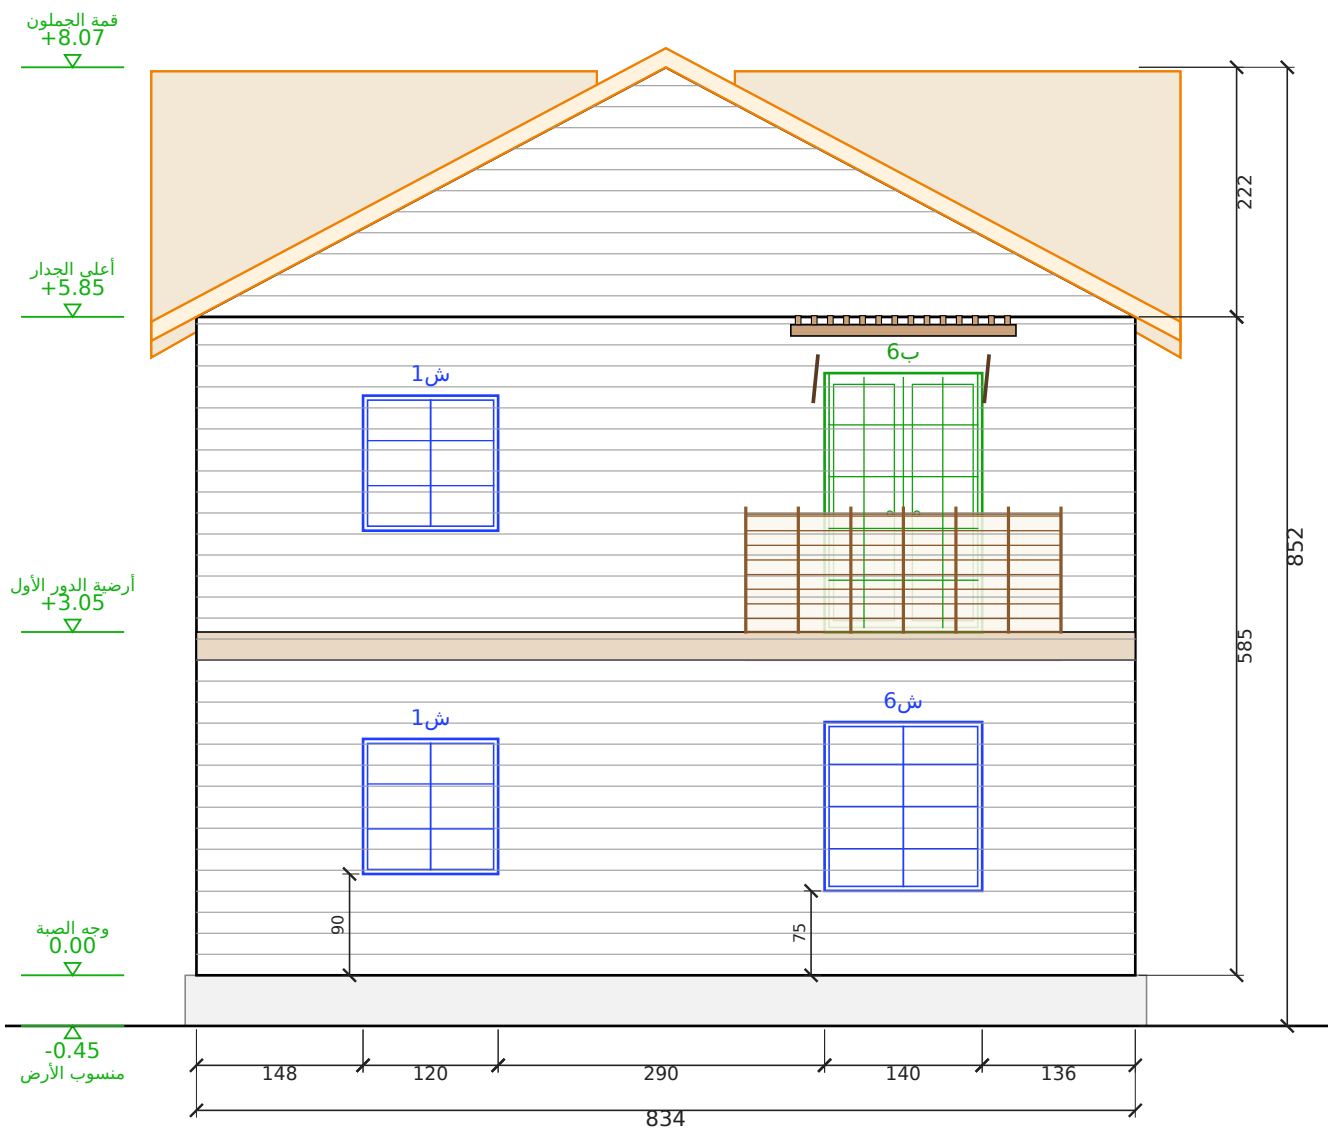

الواجهة الغربية

مقياس 1:50 | الوحدة: سم

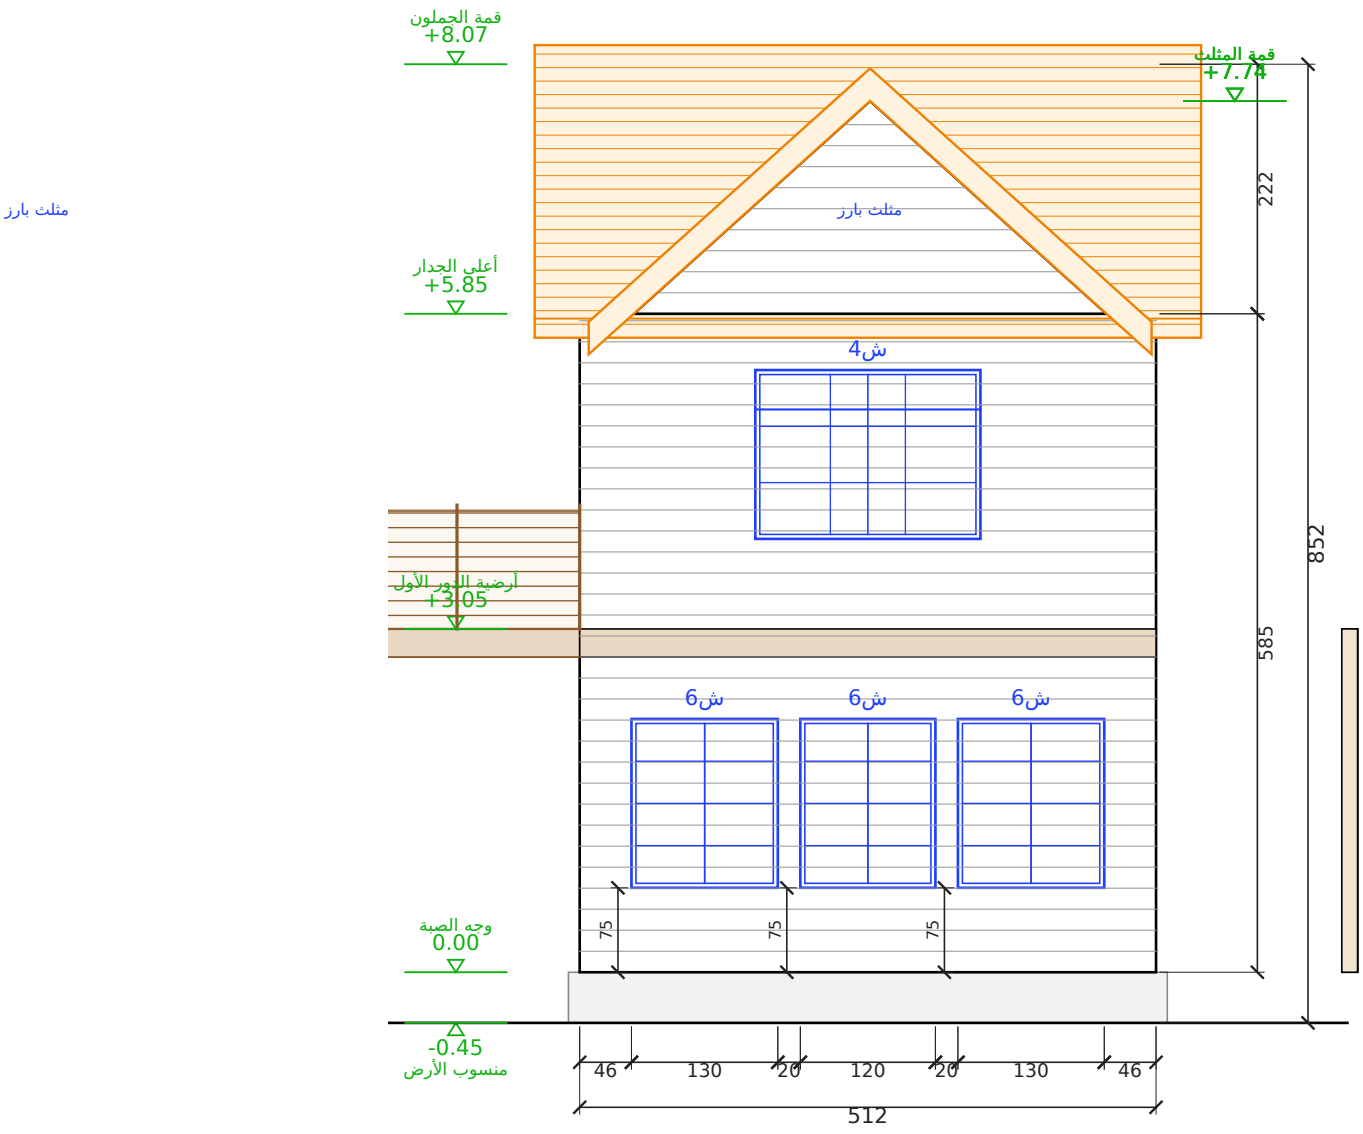


الواجهة الأمامية

مقياس 1:50 | الوحدة: سم


المشروع / العميل	عنوان اللوحة	المقياس	التاريخ	رقم اللوحة
كوخ دورين + ملحق مجلس — 5 غرف **عميل جديد**	**الواجهة الغربية والواجهة الأمامية**	**1:50**	**2026-10-17**	**A-04 (4/14)**

مصنع وتد الأخشاب
Watad Wood Factory

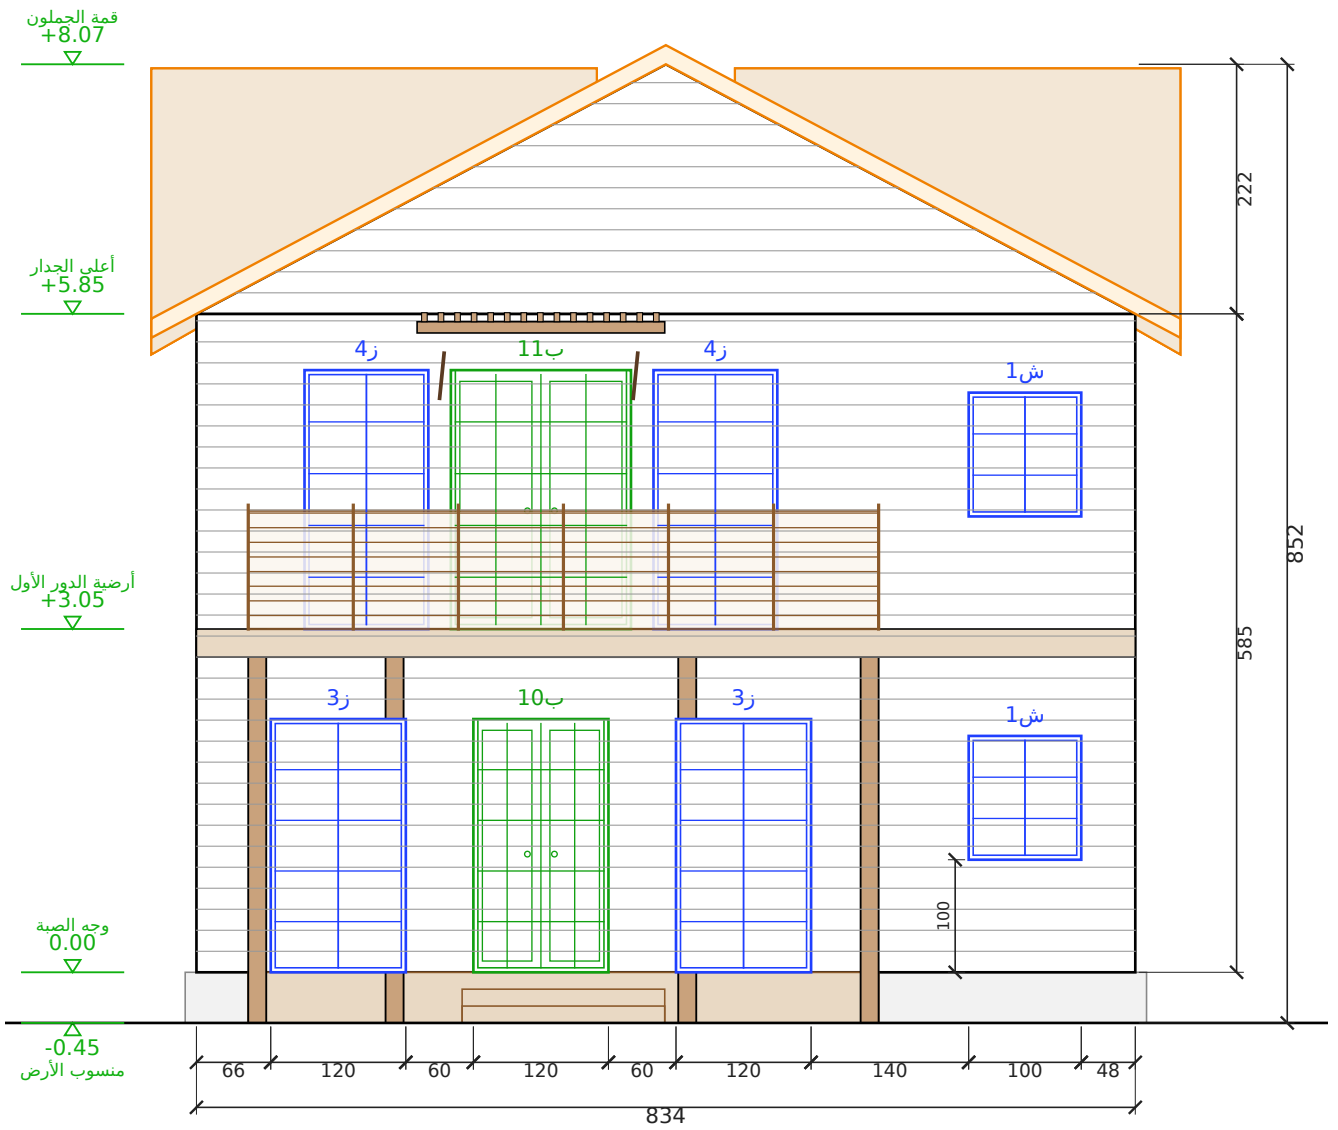

الواجهة الشرقية

مقياس 1:50 | الوحدة: سم

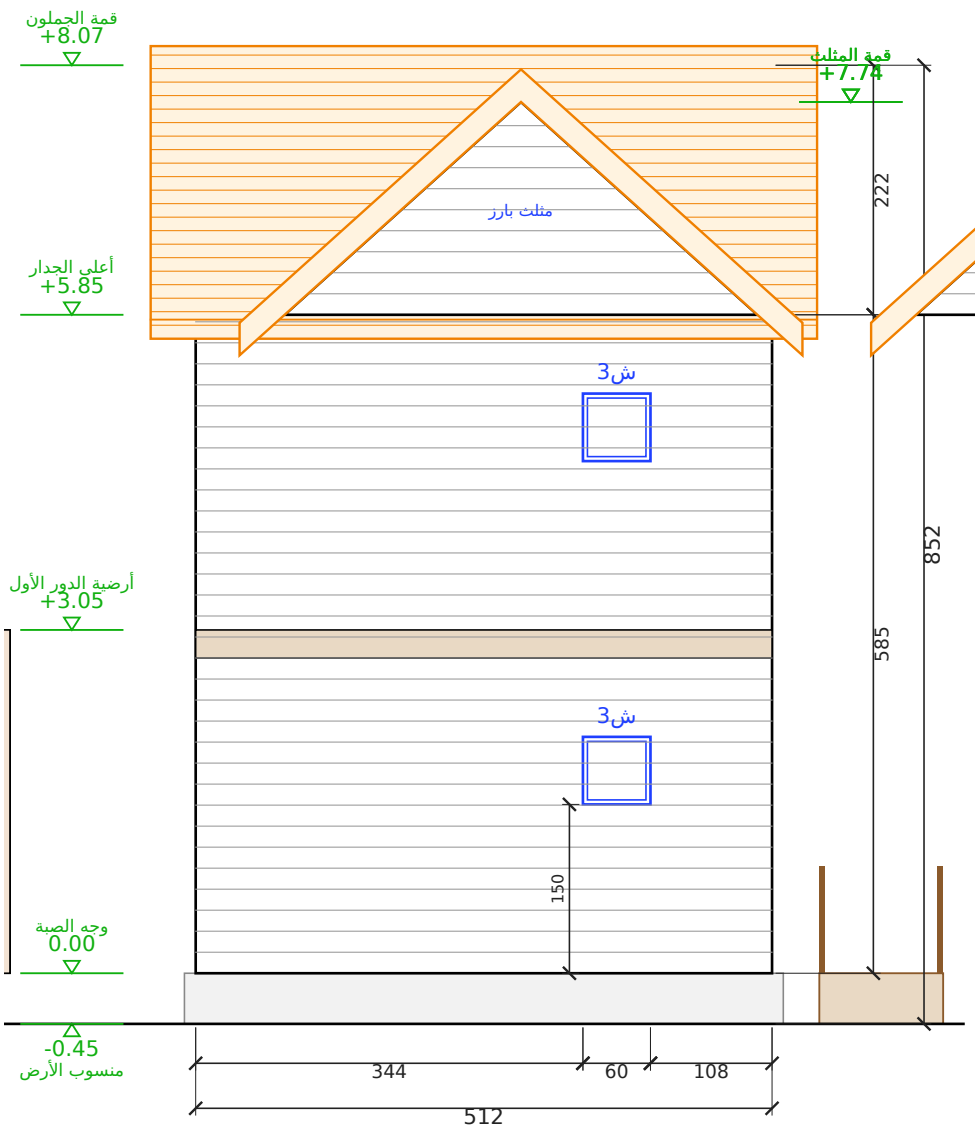


الواجهة الخلفية

مقياس 1:50 | الوحدة: سم


المشروع / العميل	عنوان اللوحة	المقياس	التاريخ	رقم اللوحة
كوخ دورين + ملحق مجلس — 5 غرف **عميل جديد**	**الواجهة الشرقية والواجهة الخلفية**	**1:50**	**2026-10-17**	**A-05 (5/14)**

مصنع وتد الأخشاب
Watad Wood Factory


مسقط السقف (جملون)
رفرف 40 سم من كل جهة | مقياس 1:50

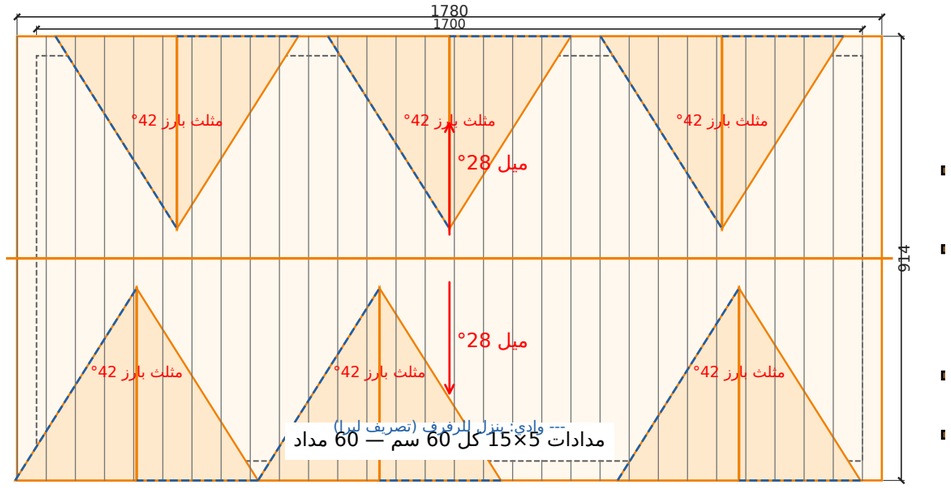

قطاع عرضي أ-أ
مقياس 1:50 | الوحدة: سم

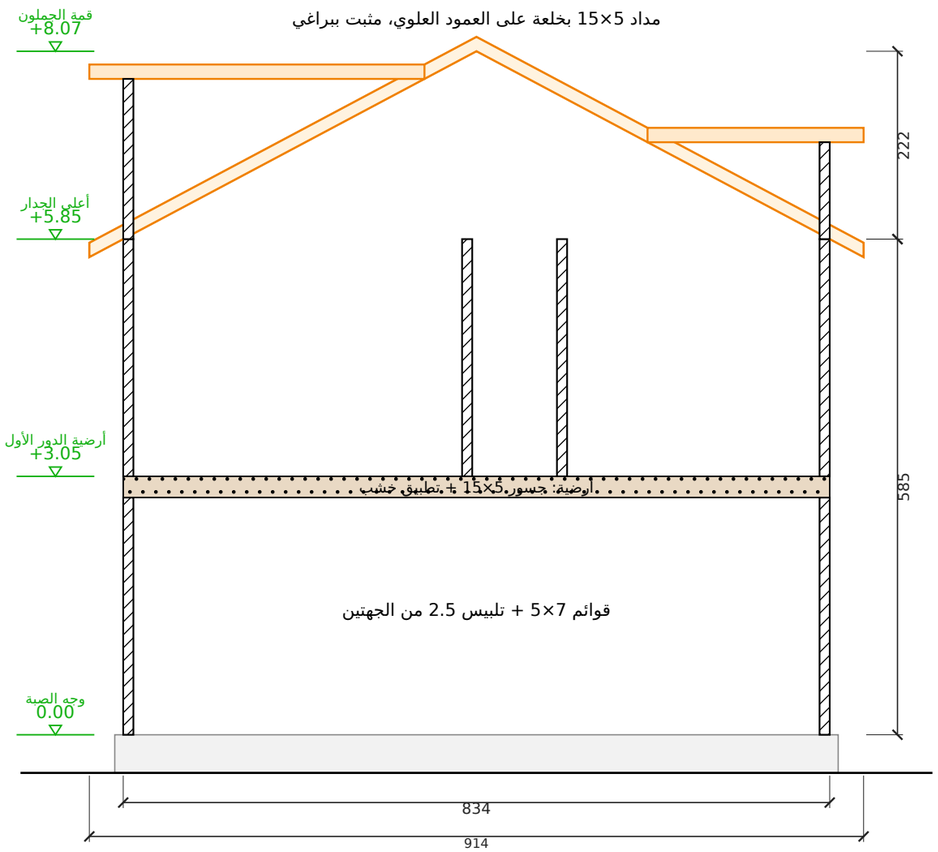

تفصيلة جلوس المداد على العلوي (1:5)

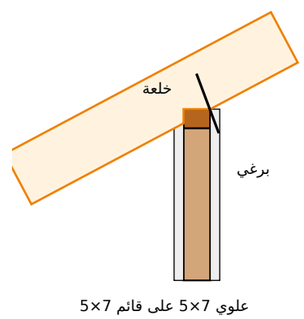

المشروع / العميل	عنوان اللوحة	المقياس	التاريخ	رقم اللوحة
كوخ دورين + ملحق مجلس — 5 غرف **عميل جديد**	**مسقط السقف والقطاع**	**1:50**	**2026-10-17**	**A-06 (6/14)**

مصنع وتد الأخشاب
Watad Wood Factory

جدول مقاسات الأبواب والشبابيك

مقاس الفتحة الصافي في الجدار - الوحدة: سم

الرمز	النوع	العرض (سم)	الارتفاع (سم)	ارتفاع الجلسة (سم)	العدد	الموقع
ب1	باب	100	225	-	1	الأمامية
ب10	باب مزدوج	120	225	-	1	الشرقية
ب11	باب مزدوج	160	230	-	1	الشرقية
ب2	باب	80	210	-	7	باب المجلس من الموزع (ملاحظة العميل) - المجلس الغربي - غرفة النوم الكبيرة - غرفة 3 - غرفة 5 - غرفة 7 - غرفة 6
ب2	باب	90	210	-	1	المطبخ
ب3	باب	70	210	-	6	حمام 1 - حمام 2 - دورة مياه المجلس - حمام 3 - حمام 4 - حمام الماستر
ب3	باب	80	210	-	2	السيرفيس - غرفة ملابس/مخزن
ب4	باب مزدوج	160	230	-	1	الأمامية
ب5	باب	80	210	-	1	الخلفية
ب6	باب مزدوج	140	230	-	1	الغربية
ب7	باب مزدوج	160	230	-	1	الأمامية
ف1	باب	316	250	-	1	الأمامية
ف4	باب	100	240	-	1	فتحة المغاسل
ف5	باب	120	240	-	1	فتحة غرفة الملابس
ز3	شباك	120	225	0	2	الشرقية 2
ز4	شباك	110	230	0	2	الشرقية 2
ش1	شباك	100	110	100	4	الخلفية 2 - الشرقية 2
ش1	شباك	120	120	90	3	الغربية 2 - الخلفية
ش2	شباك	140	110	100	1	الأمامية
ش3	شباك	60	60	150	6	الخلفية 6
ش4	شباك	200	150	80	2	الأمامية 2
ش5	شباك	110	150	80	1	الأمامية
ش6	شباك	130	150	75	4	الأمامية 4
ش6	شباك	140	150	75	1	الغربية
ش6	شباك	120	150	75	1	الأمامية

الإجمالي: أبواب 26 - شبابيك 27

جدول المساحات وبيانات المشروع والتسعير

بيانات المشروع

البند	البيان
المشروع	كوخ دورين + ملحق مجلس — 5 غرف
العميل	عميل جديد
الموقع	—
الاستخدام	سكن خاص
التاريخ	2026-10-17
نظام البناء	هيكل خشب 5×7 + تلبيس 2.5 سم من الجهتين
السقف	جملون 28° — قرميد معدني + 6 مثلث بارز

التسعير

عرض اليوم الوطني 96

البند	القيمة
المساحة المبنية (م2)	283.56
سعر المتر المربع — عرض اليوم الوطني 96	1,096 ريال
الإجمالي	**310,782 ريال**

ملاحظات:

- السعر للمساحة المبنية (دورين + الملحق) — الشباك البارز والبلكونات والبرندة والعتبات مجاناً.
- الصبة والتمديدات الخارجية على العميل ما لم يُذكر غير ذلك.

جدول المساحات

م	الفراغ	الأبعاد (م)	المساحة (م2)
1	أرضي — المجلس الغربي	3.88 × 8.10	31.43
2	أرضي — المجلس	4.88 × 5.88	28.69
3	أرضي — دورة مياه المجلس	2.46 × 2.10	5.17
4	أرضي — المغاسل	2.30 × 2.10	4.83
5	أرضي — الصالة	4.48 × 3.88	17.38
6	أرضي — المطبخ	3.16 × 3.88	12.26
7	أرضي — الموزع	7.76 × 1.00	7.76
8	أرضي — الدرج	2.34 × 2.98	6.97
9	أرضي — حمام 1	1.58 × 2.98	4.71
10	أرضي — حمام 2	1.58 × 2.98	4.71
11	أرضي — سيرفيس	1.90 × 2.98	5.66
12	أول — غرفة نوم 3	3.88 × 3.88	15.05
13	أول — غرفة نوم 5	3.88 × 3.88	15.05
14	أول — غرفة نوم 7	3.76 × 3.88	14.59
15	أول — غرفة النوم الكبيرة (الماستر)	4.88 × 5.88	28.69
16	أول — حمام الماستر	2.46 × 2.10	5.17
17	أول — ملابس الماستر	2.30 × 2.10	4.83
18	أول — الممر	11.76 × 1.00	11.76
19	أول — غرفة نوم 6	3.88 × 2.98	11.56
20	أول — حمام 3	1.58 × 2.98	4.71
21	أول — حمام 4	1.58 × 2.98	4.71
22	أول — غرفة ملابس	1.90 × 2.98	5.66
	المساحة الصافية الداخلية		**251.36**
	التراس المسقوف + تراس الدور الأول (مجاناً)	**1.76 × 1.44 × 6**	**36.46**
	المساحة الإجمالية المبنية	**17.00 × 8.34 × 2 دور**	**283.56**

الصور الواقعية — الخارج

أمامي من اليسار



أمامي من اليمين



الواجهة الأمامية



خلفي من اليسار



رندر واقعي بخامات حقيقية وإضاءة طبيعية — الألوان النهائية حسب عينات المورد

مصنع وتد الأخشاب Watad Wood Factory	المشروع / العميل كوخ دوربن + ملحق مجلس — 5 غرف عميل جديد	عنوان اللوحة الصور الواقعية — الخارج	المقياس —	التاريخ 2026-10-17	رقم اللوحة A-09 (9/14)

الصور الواقعية — وقت الغروب

أمامي من اليسار — وقت الغروب



أمامي من اليمين — وقت الغروب



المشروع / العميل	عنوان اللوحة	المقياس	التاريخ	رقم اللوحة
كوخ دورين + ملحق مجلس — 5 غرف **عميل جديد**	**الصور الواقعية — الغروب**	**—**	**2026-10-17**	**A-10 (10/14)**

مصنع وتد الأخشاب
Watad Wood Factory

الصور الواقعية — الداخل

المجلس



غرفة النوم الكبيرة (الماستر)



غرفة النوم الكبيرة (الماستر) — منظر 2



الصالة



غرفة نوم الضيوف



غرفة الطعام




الأثاث للتوضيح فقط — مواقع القطع ومقاساتها حسب المسقط

مصنع وتد الأخشاب Watad Wood Factory	المشروع / العميل **كوخ دورين + ملحق مجلس — 5 غرف** **عميل جديد**	عنوان اللوحة **الصور الواقعية — الداخل**	المقياس **—**	التاريخ **2026-10-17**	رقم اللوحة **A-11 (11/14)**

المقطع العلوي بالفرش — الدور الأرضي

مقطع أفقي على ارتفاع 1.90 م — توزيع الفرش ومسار الحركة

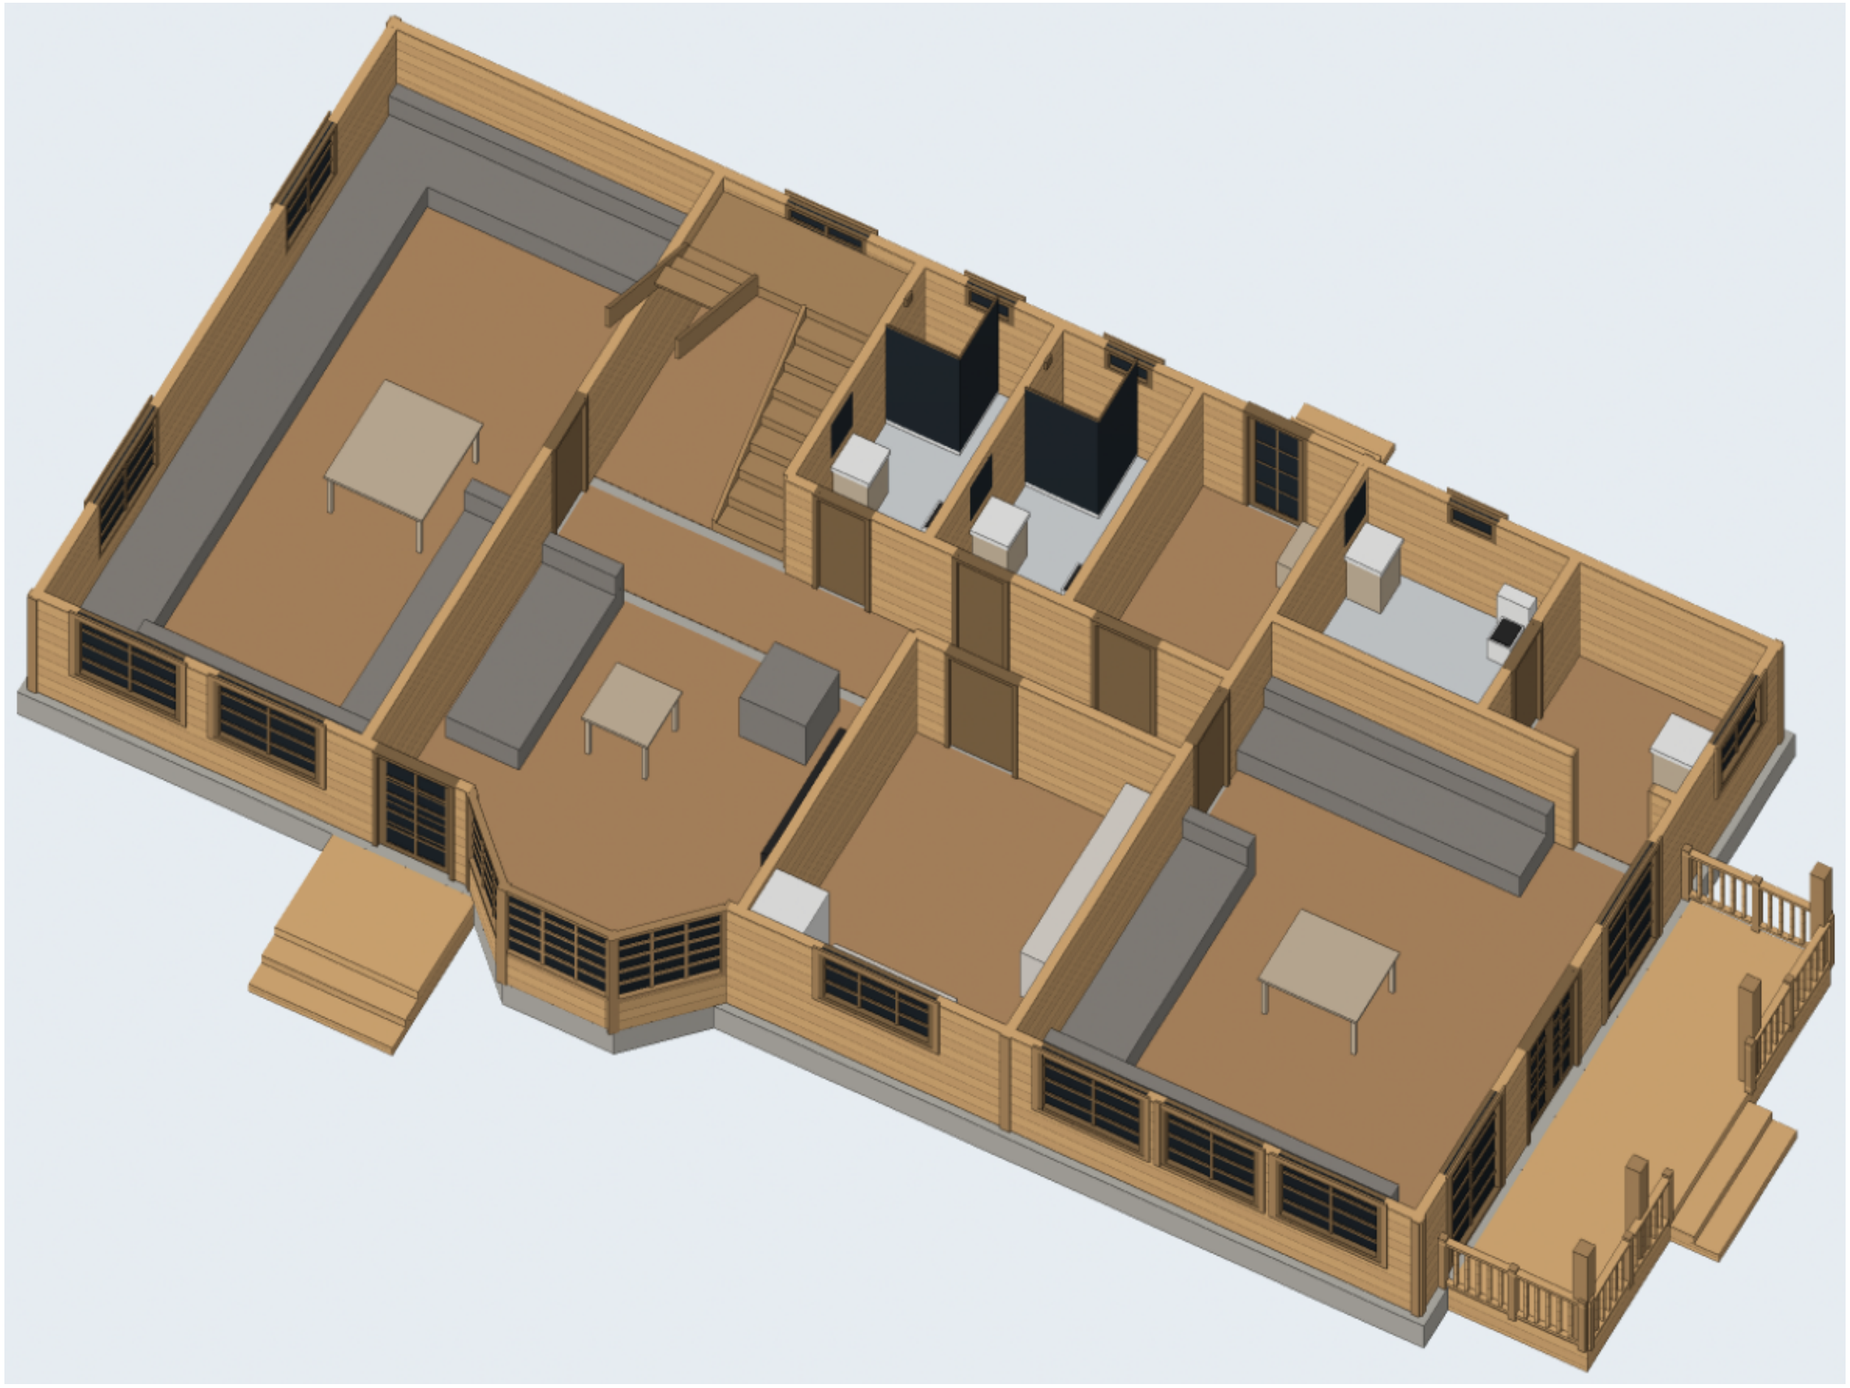


المشروع / العميل	عنوان اللوحة	المقياس	التاريخ	رقم اللوحة
كوخ دورين + ملحق مجلس — 5 غرف **عميل جديد**	**المقطع العلوي بالفرش — الدور الأرضي**	**—**	**2026-10-17**	**A-12 (12/14)**

مصنع وتد الأخشاب
Watad Wood Factory

المقطع العلوي بالفرش — الدور الأول

مقطع أفقي على ارتفاع 1.90 م — توزيع الفرش ومسار الحركة

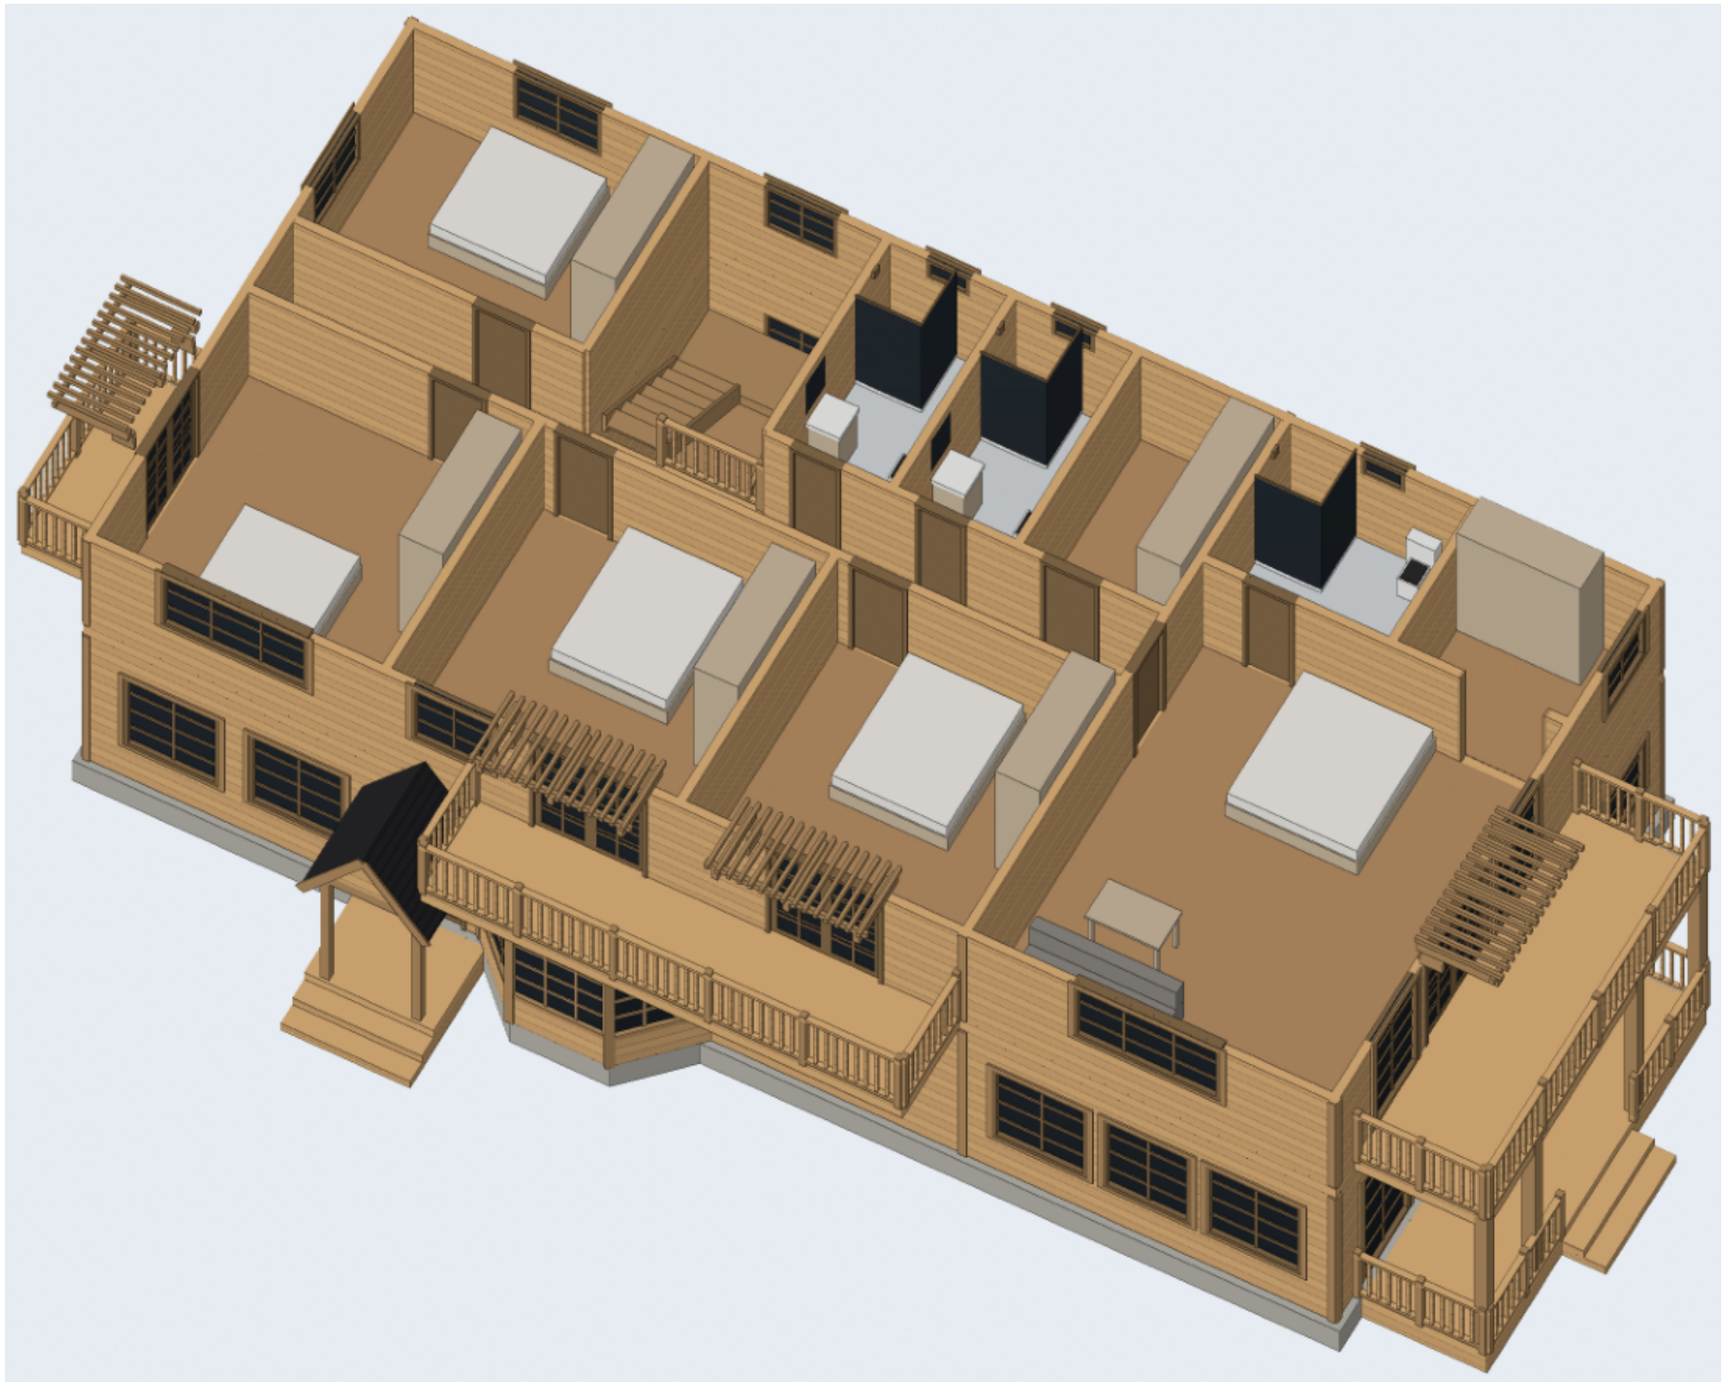

المشروع / العميل	عنوان اللوحة	المقياس	التاريخ	رقم اللوحة
كوخ دورين + ملحق مجلس — 5 غرف **عميل جديد**	**المقطع العلوي بالفرش — الدور الأول**	**—**	**2026-10-17**	**A-13 (13/14)**

مصنع وتد الأخشاب
Watad Wood Factory

المنظور ثلاثي الأبعاد والمواد

النمط: جوزي غامق + إطارات سوداء — رندر واقعي بخامات حقيقية





جدول المواد والألوان

الخشب / الصبغة

خشب طبيعي فاتح (بدون صبغة)

القرميد

قرميد رمادي غامق

الزجاج

زجاج عاكس غامق

إطارات الشبابيك والأبواب

إطار خشب بنفس الصبغة أغمق

الكنار والزوايا

نفس الصبغة أغمق درجة


الصبة

خرسانة 45 سم


الدربزين: ألواح أفقية متقاربة (عصري)

تقسيم الشبابيك: بدون | الباب الرئيسي: زجاج بتقسيمات (فرنسي)

أنواع الدربزين المعتمدة (من مشاريع المصنع)

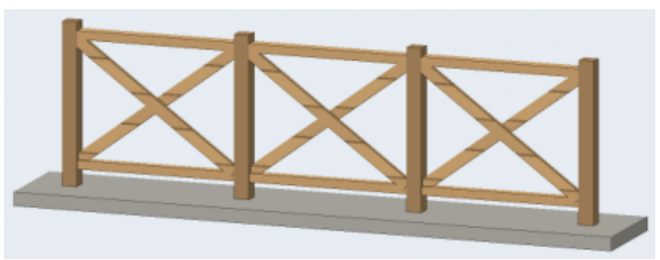

تقاطع X (صورة 5)

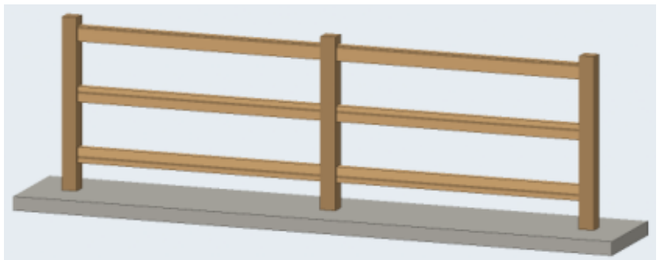

3 مرابيع أفقية (صورة 2)



قوائم رأسية متقاربة (صورة 1)

المشروع / العميل	عنوان اللوحة	المقياس	التاريخ	رقم اللوحة
كوخ دورين + ملحق مجلس — 5 غرف **عميل جديد**	**المنظور والمواد**	**—**	**2026-10-17**	**A-14 (14/14)**

مصنع وتد الأخشاب
Watad Wood Factory