
المنظور ثلاثي الأبعاد والمواد

النمط: جوزي غامق + إطارات سوداء — رندر واقعي بخامات حقيقية

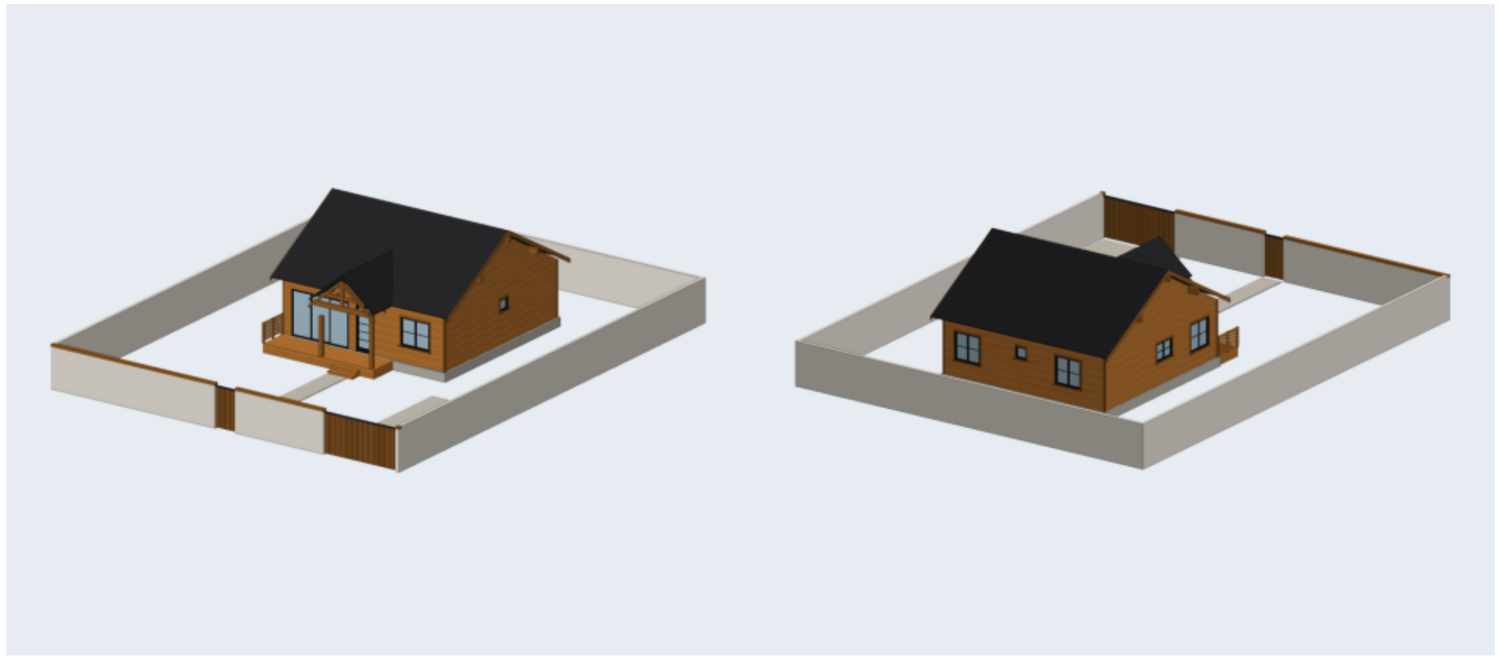

جدول المواد والألوان

الخشب / الصبغة

صبغة عسلي / سيدر

القرميد

قرميد رمادي غامق

الزجاج

زجاج شفاف

إطارات الشبابيك والأبواب

إطار ألمنيوم أسود

الكنار والزوايا

نفس الصبغة أغمق درجة


الصبة

خرسانة 45 سم


الدربزين: ألواح أفقية متقاربة (عصري)

تقسيم الشبابيك: شبكة | الباب الرئيسي: سحاب زجاج

أنواع الدربزين المعتمدة (من مشاريع المصنع)

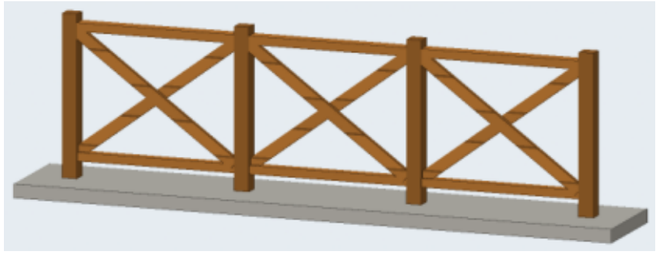

تقاطع X (صورة 5)

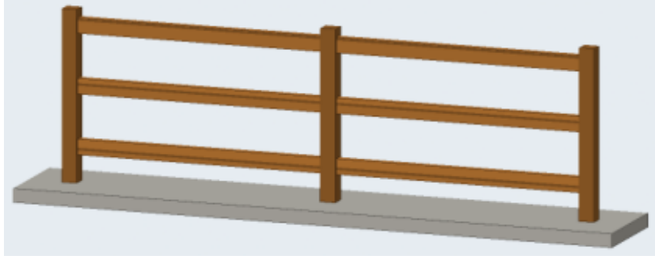

3 مرابيع أفقية (صورة 2)




قوائم رأسية متقاربة (صورة 1)

المشروع / العميل **كوخ خشب 9.00 × 9.00 م — ثلاث غرف وصالة واسعة ومطبخ سيرفس** **عميل — كوخ 9×9**	عنوان اللوحة **المنظور والمواد**	المقياس **1:50**	التاريخ **2026-11-03**	رقم اللوحة **W-01 (1/14)**

مصنع وتد الأخشاب
Watad Wood Factory


المسقط الأفقي مع الفرش

الأبعاد بالسنتيمتر - الجدران: قوائم 7×5 + تلبيس 2.5 من الجهتين (12 سم)

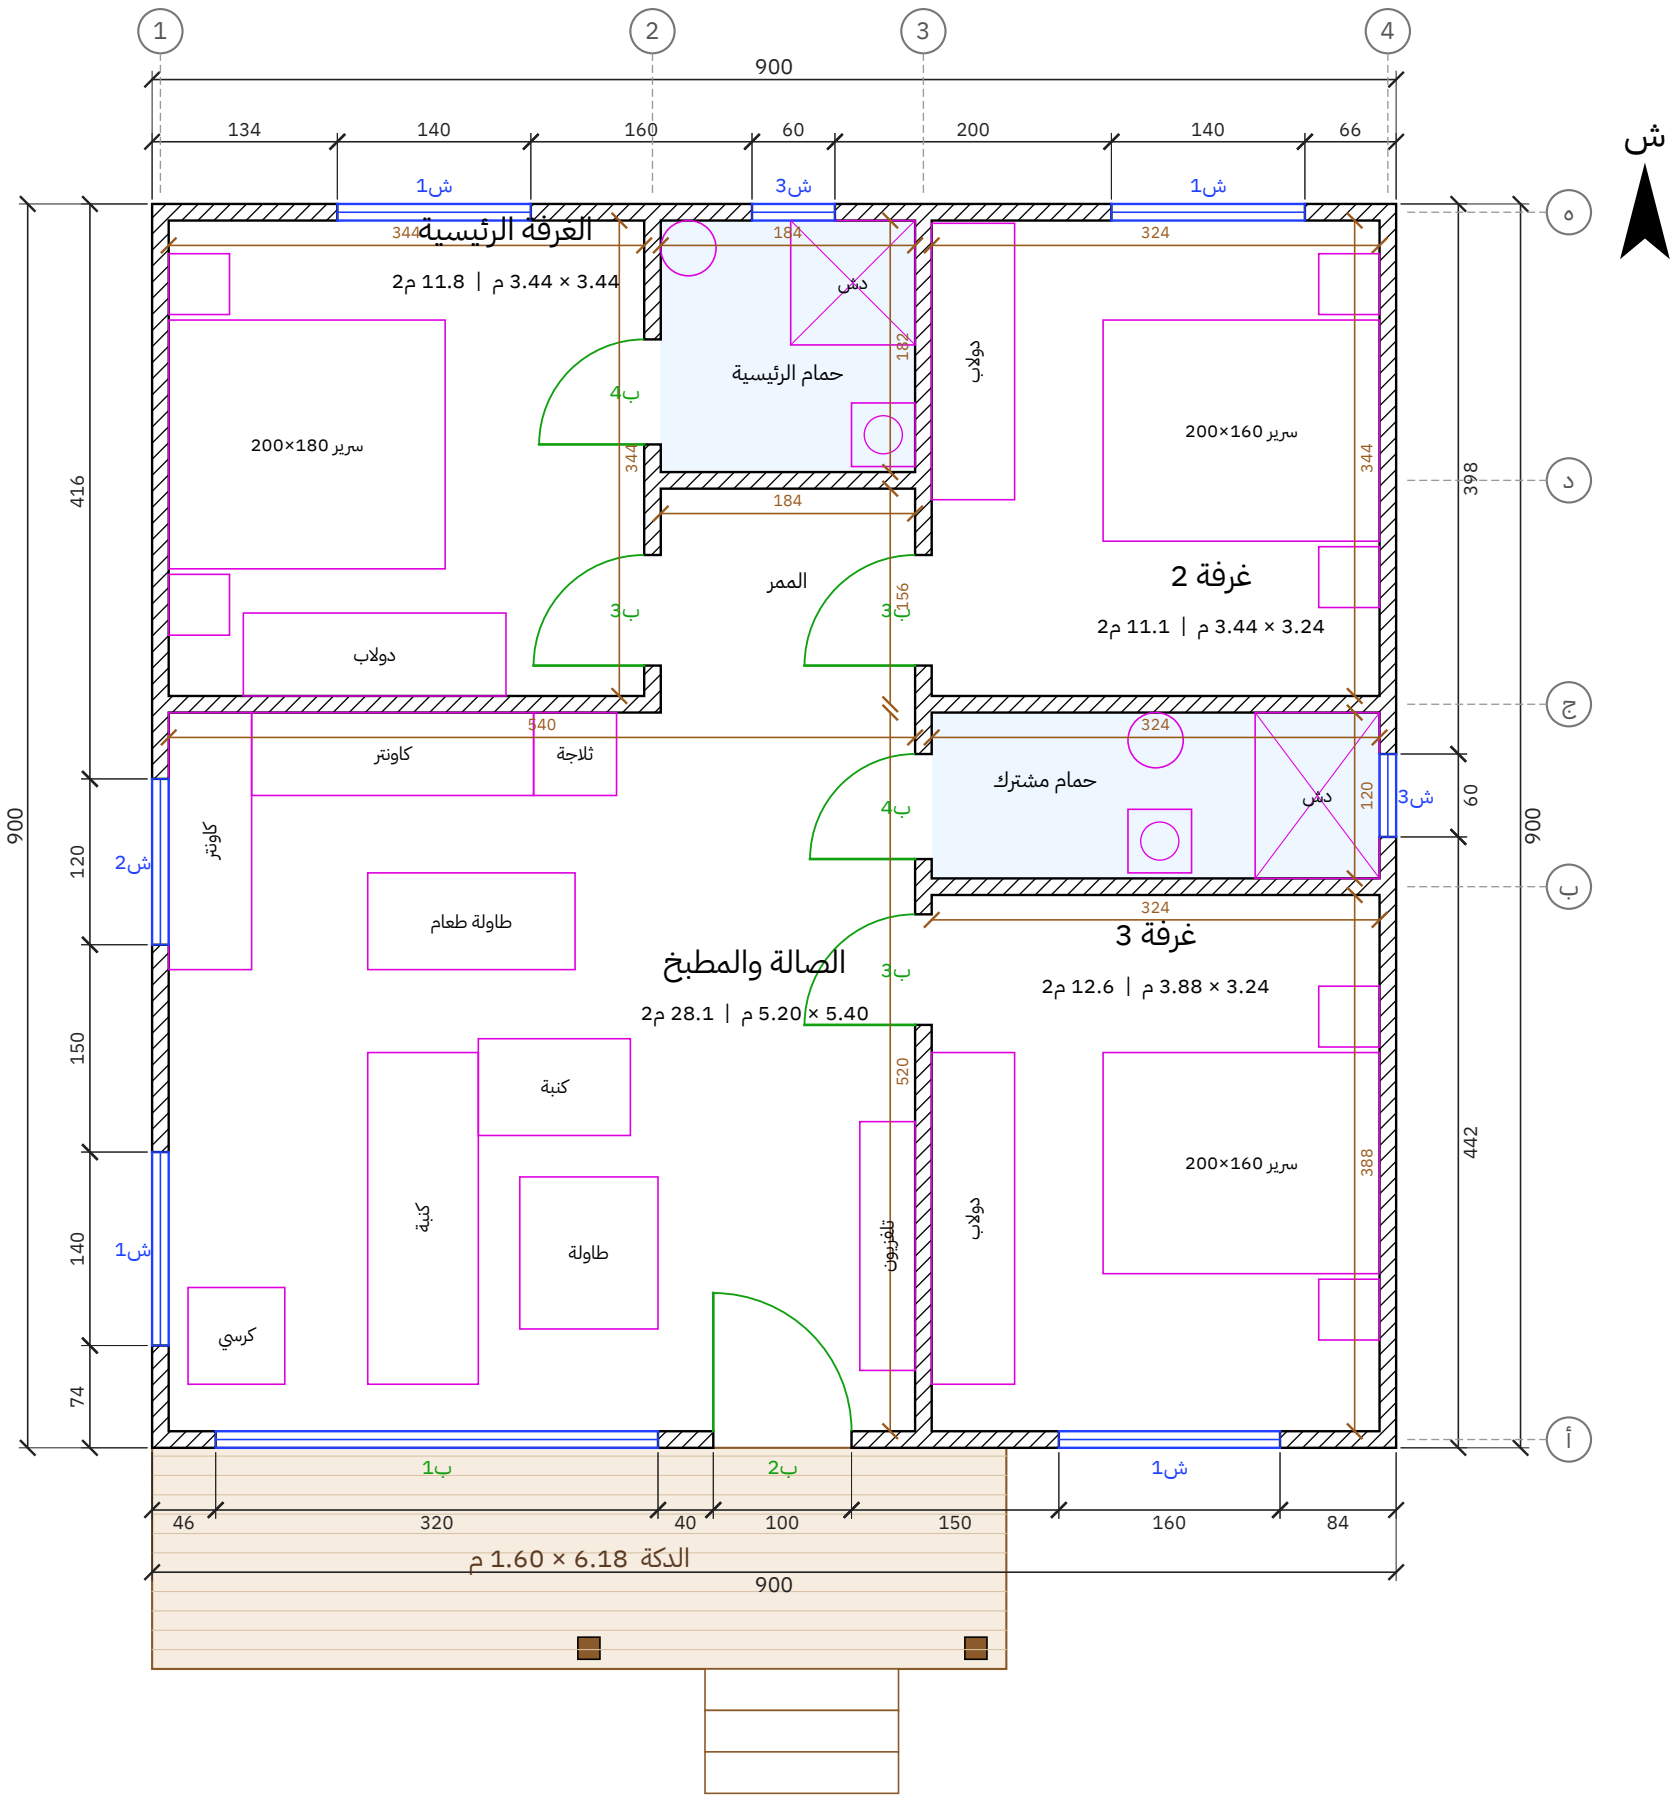


3 درجات × 15 سم

مصنع وتد الأخشاب Watad Wood Factory	المشروع / العميل كوخ خشب 9.00 × 9.00 م – ثلاث غرف وصالة واسعة ومطبخ سيرفس عميل – كوخ 9×9	عنوان اللوحة المسقط الأفقي	المقياس 1:50	التاريخ 2026-11-03	رقم اللوحة W-02 (2/14)

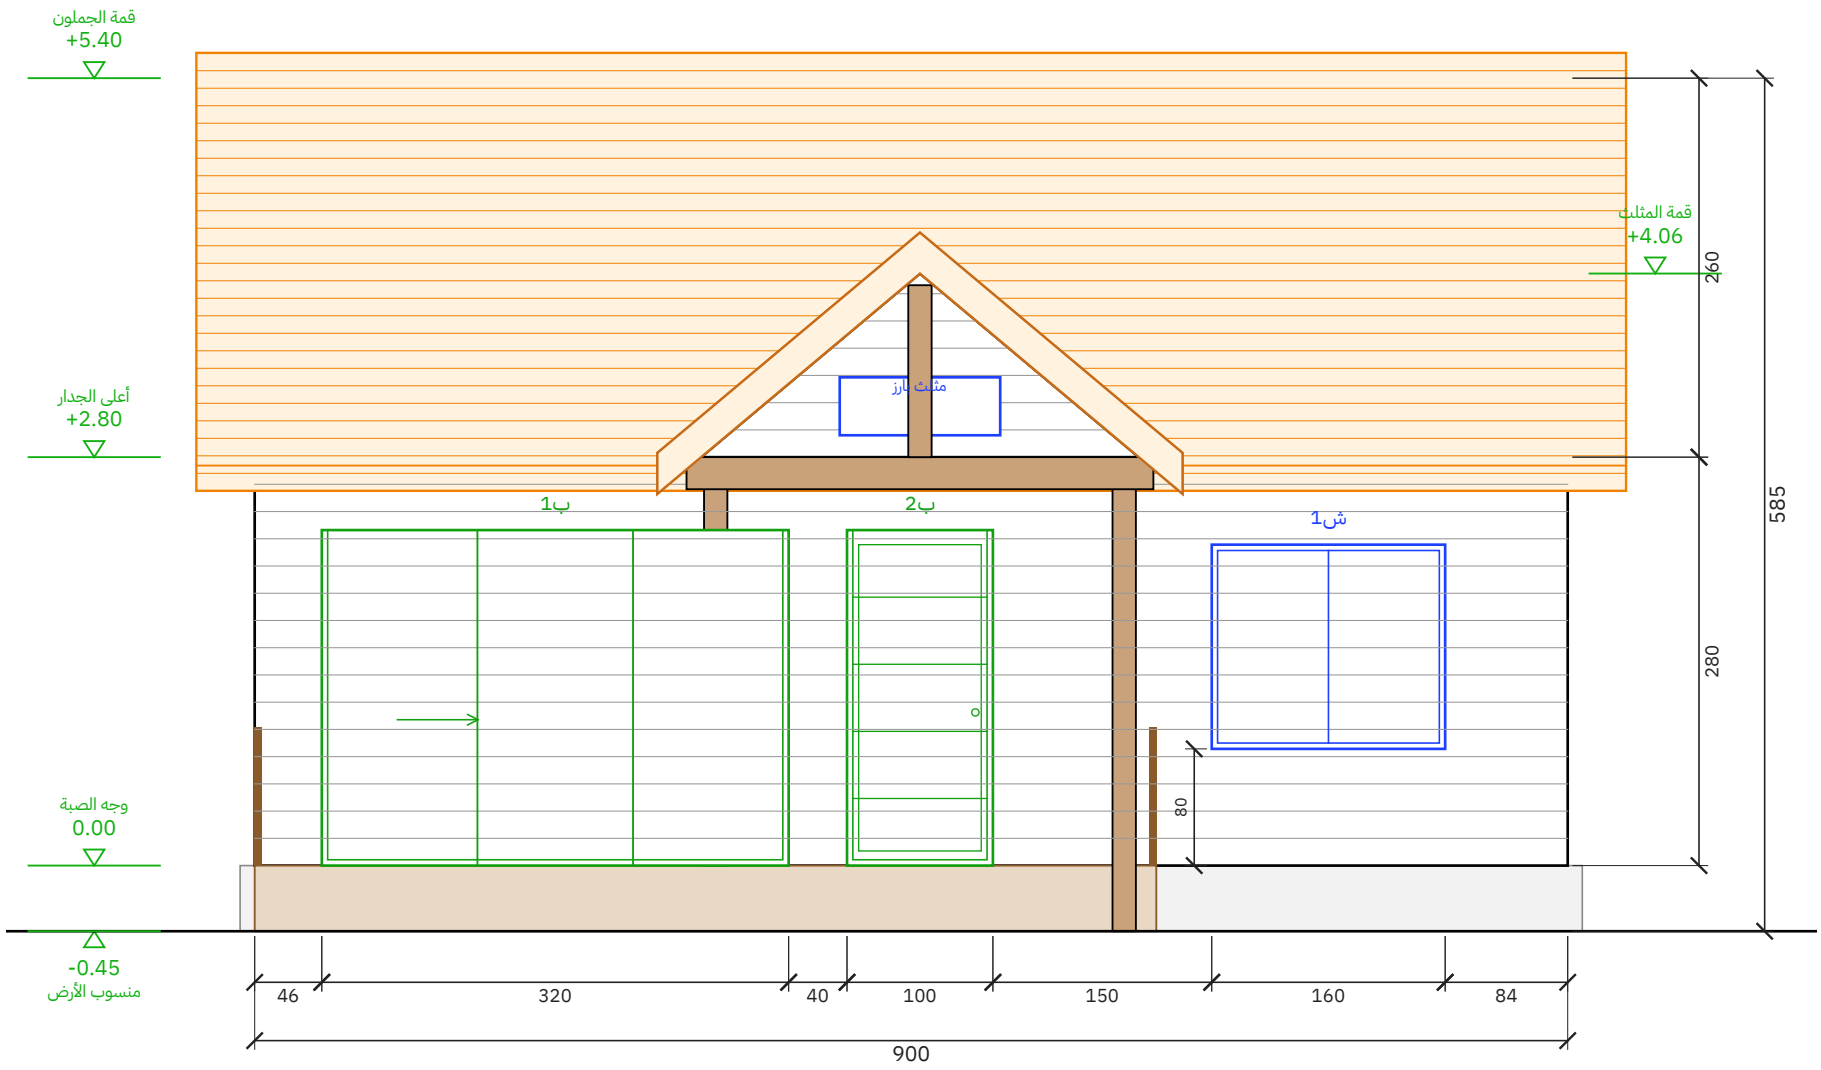

الواجهة الأمامية

مقياس 1:50 | الوحدة: سم

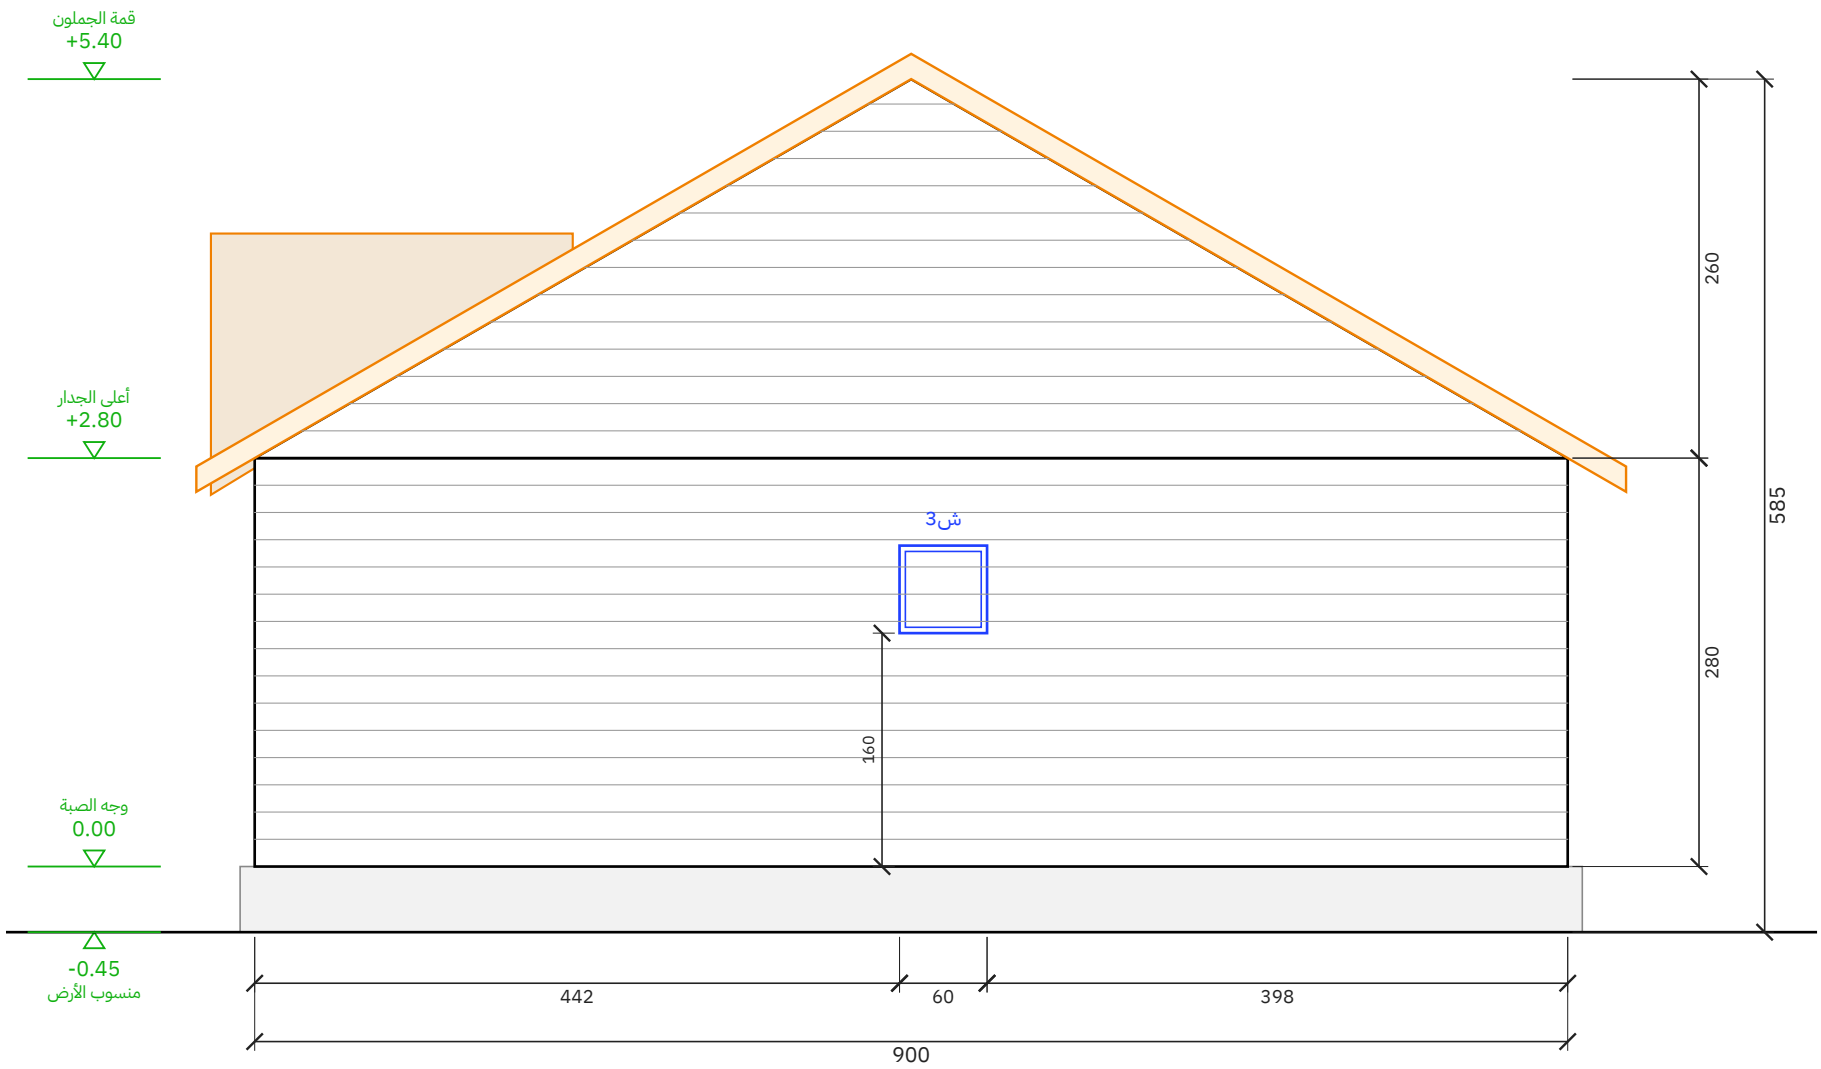


الواجهة الشرقية

مقياس 1:50 | الوحدة: سم


المشروع / العميل	عنوان اللوحة	المقياس	التاريخ	رقم اللوحة
كوخ خشب 9.00 × 9.00 م – ثلاث غرف وصالة واسعة ومطبخ سيرفس عميل – كوخ 9×9	الواجهة الأمامية والواجهة الشرقية	1:50	2026-11-03	W-03 (3/14)

مصنع وتد الأخشاب
Watad Wood Factory

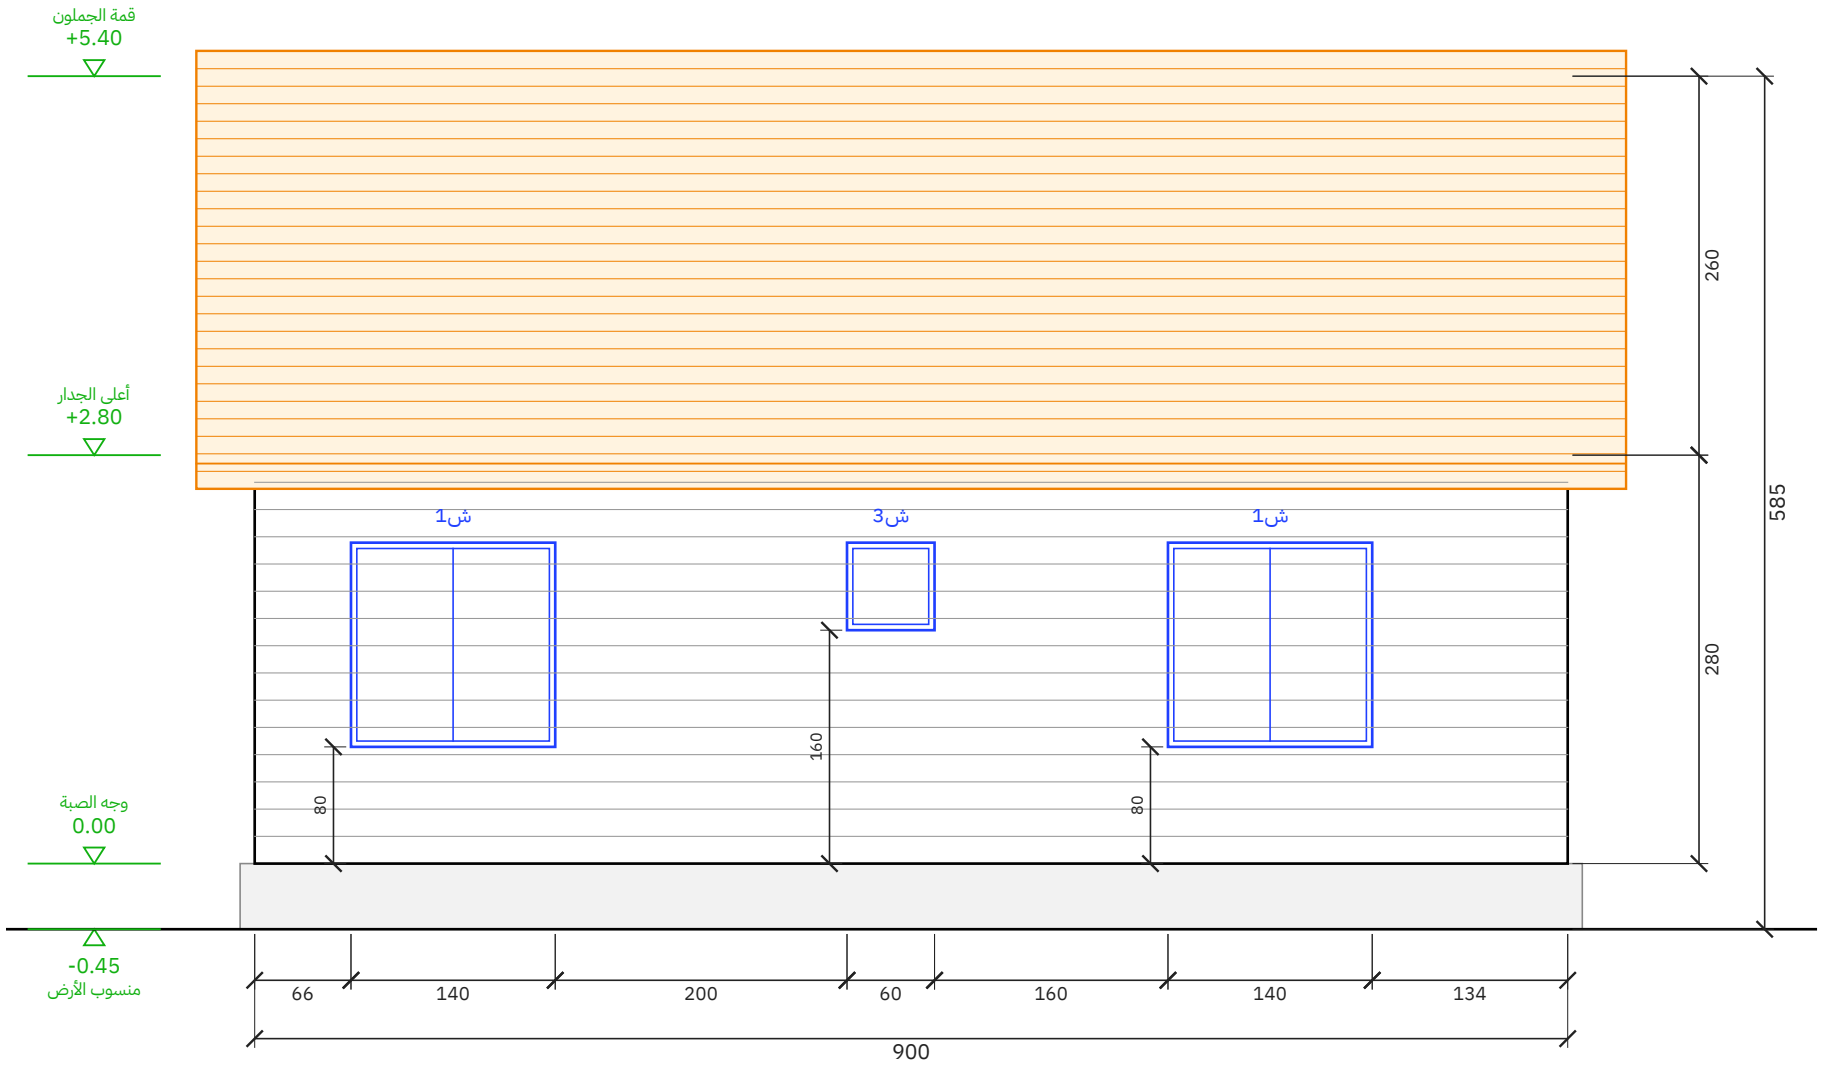

الواجهة الخلفية

مقياس 1:50 | الوحدة: سم

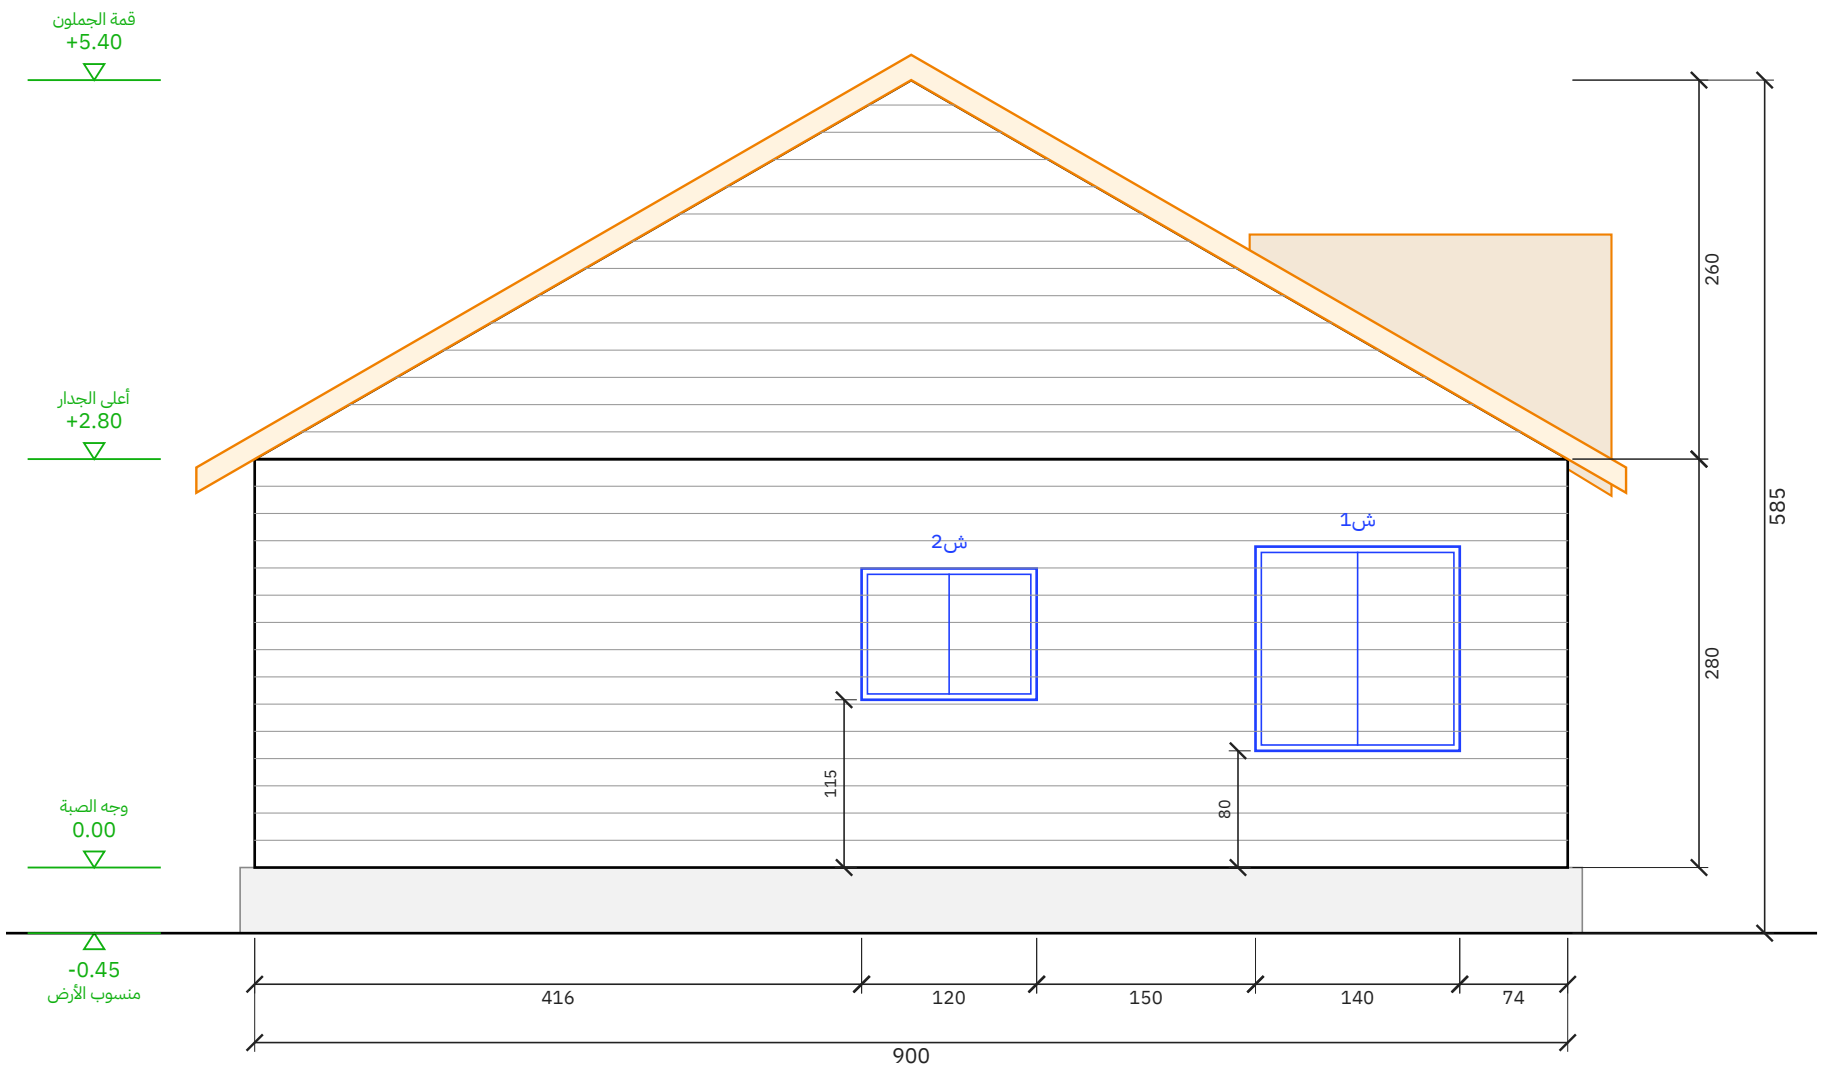

الواجهة الغربية


مقياس 1:50 | الوحدة: سم

المشروع / العميل	عنوان اللوحة	المقياس	التاريخ	رقم اللوحة
كوخ خشب 9.00 × 9.00 م – ثلاث غرف وصالة واسعة ومطبخ سيرفس عميل – كوخ 9×9	الواجهة الخلفية والواجهة الغربية	1:50	2026-11-03	W-04 (4/14)

مصنع وتد الأخشاب
Watad Wood Factory


مسقط السقف (جملون)

رفرف 40 سم من كل جهة | مقياس 1:50

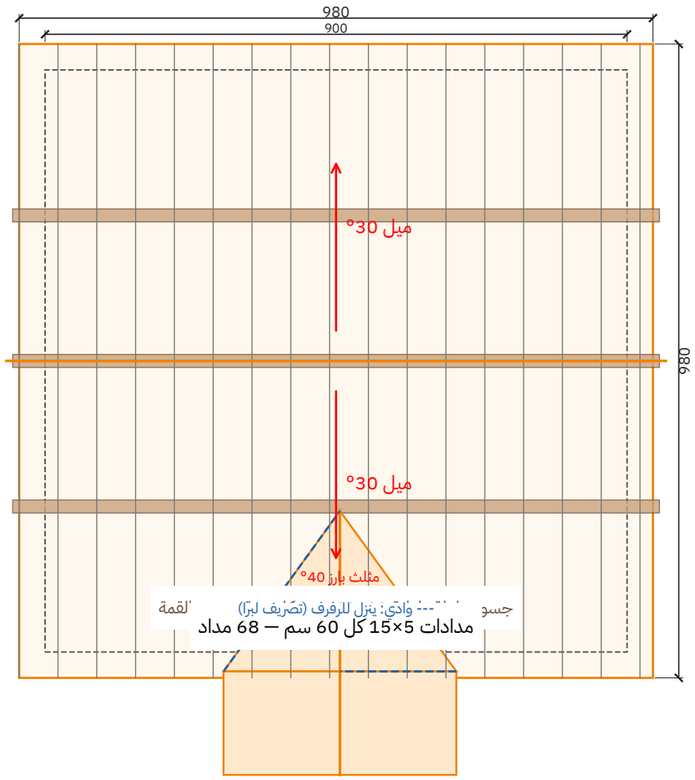


قطاع عرضي أ-أ

مقياس 1:50 | الوحدة: سم

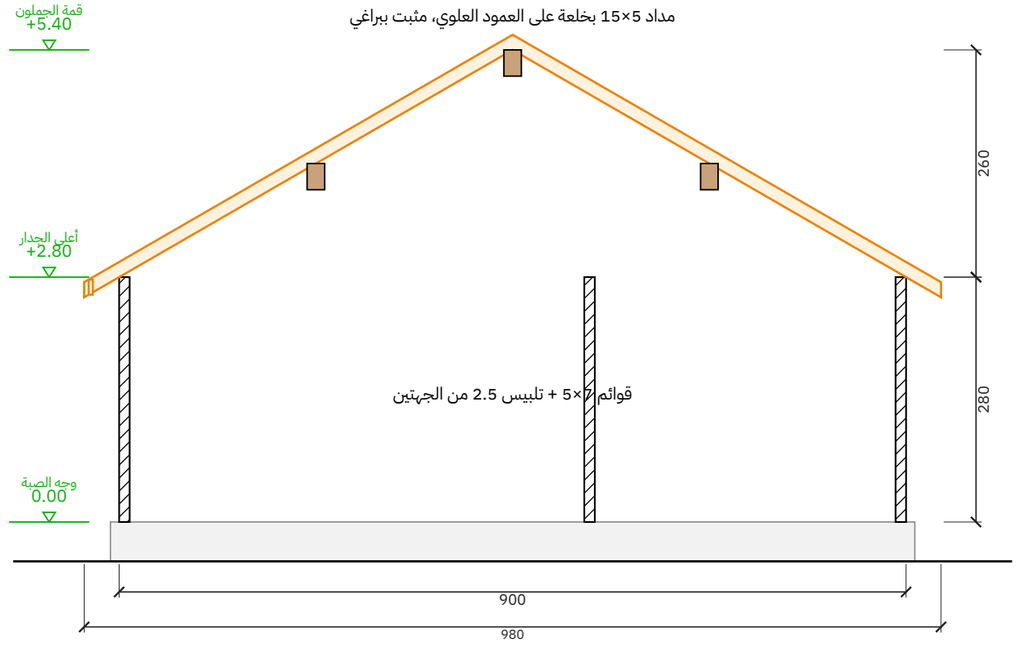

تفصيلة جلوس المداد على العلوي (1:5)

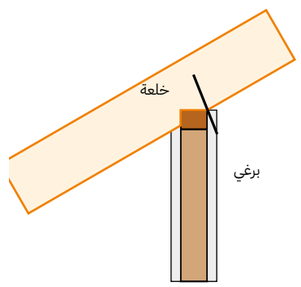

علوي 7×5 على قائم 7×5

المشروع / العميل	عنوان اللوحة	المقياس	التاريخ	رقم اللوحة
كوخ خشب 9.00 × 9.00 م — ثلاث غرف وصالة واسعة ومطبخ سيرفس **عميل — كوخ 9×9**	**مسقط السقف والقطاع**	**1:50**	**2026-11-03**	**W-05 (5/14)**

مصنع وتد الأخشاب
Watad Wood Factory

جدول مقاسات الأبواب والشبابيك

مقاس الفتحة الصافي في الجدار - الوحدة: سم

الرمز	النوع	العرض (سم)	الارتفاع (سم)	ارتفاع الجلسة (سم)	العدد	الموقع
ب1	باب	320	230	-	1	الأمامية
ب2	باب	100	230	-	1	الأمامية
ب3	باب	80	210	-	3	غرفة 3 - غرفة 2 - الغرفة الرئيسية
ب4	باب	76	210	-	2	الحمام المشترك - حمام الرئيسية
ش1	شباك	160	140	80	1	الأمامية
ش1	شباك	140	140	80	3	الخلفية 2 - الغربية
ش2	شباك	120	90	115	1	الغربية
ش3	شباك	60	60	160	2	الشرقية - الخلفية

الإجمالي: أبواب 7 - شبابيك 7

جدول المساحات وبيانات المشروع


بيانات المشروع

البند	البيان
المشروع	كوخ خشب 9.00 × 9.00 م — ثلاث غرف وصالة واسعة ومطبخ سيرفس
العميل	عميل — كوخ 9×9
الموقع	—
الاستخدام	سكن — ثلاث غرف
التاريخ	2026-11-03
نظام البناء	هيكل خشب 5×7 + تلبيس 2.5 سم من الجهتين
السقف	جملون 30° — قرميد معدني + 1 مثلث بارز


جدول المساحات

م	الفراغ	الأبعاد (م)	المساحة (م2)
1	الصالة والمطبخ	5.40 × 5.20	28.08
2	غرفة 3	3.24 × 3.88	12.57
3	حمام مشترك	3.24 × 1.20	3.89
4	غرفة 2	3.24 × 3.44	11.15
5	الغرفة الرئيسية	3.44 × 3.44	11.83
6	الممر	1.84 × 1.56	2.87
7	حمام الرئيسية	1.84 × 1.82	3.35
	المساحة الصافية الداخلية		**73.74**
	الدكة	**6.18 × 1.60**	**9.89**
	المساحة الإجمالية المبنية	**9.00 × 9.00**	**81.00**
	المساحة الكلية (المبنية + التراس)		**90.89**

تأطير جدار جنوب — الطول 888 سم، الارتفاع 280 سم

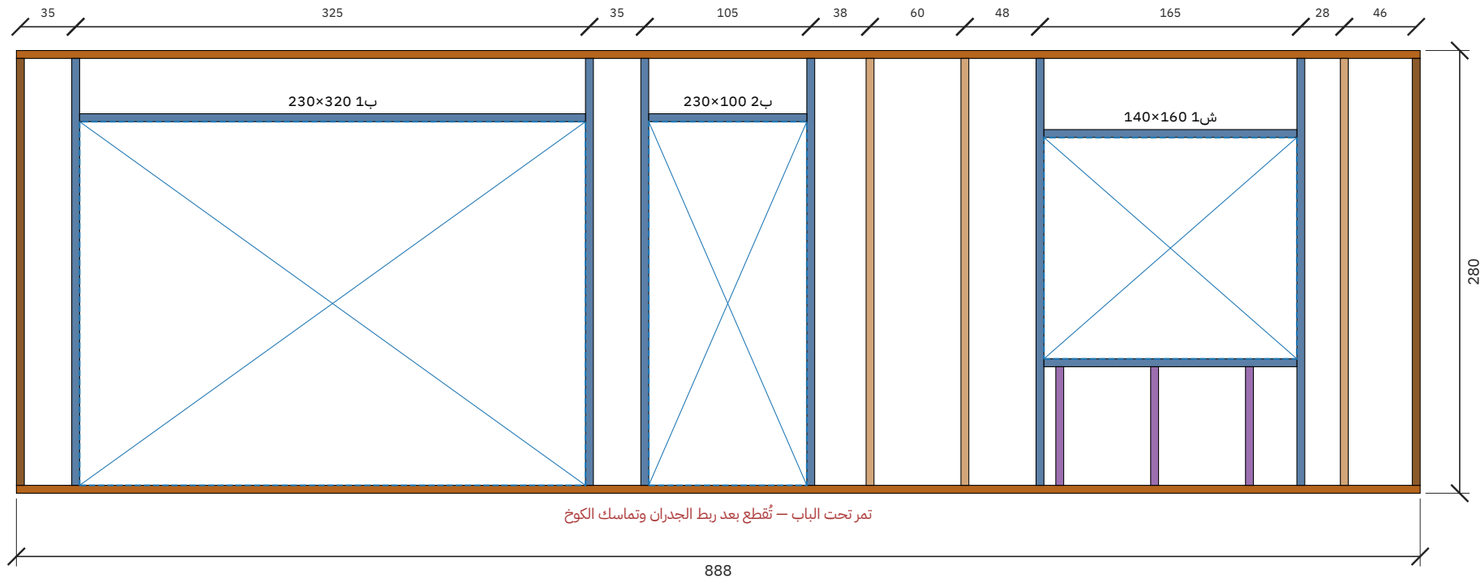

تأطير جدار شرق — الطول 888 سم، الارتفاع 280 سم

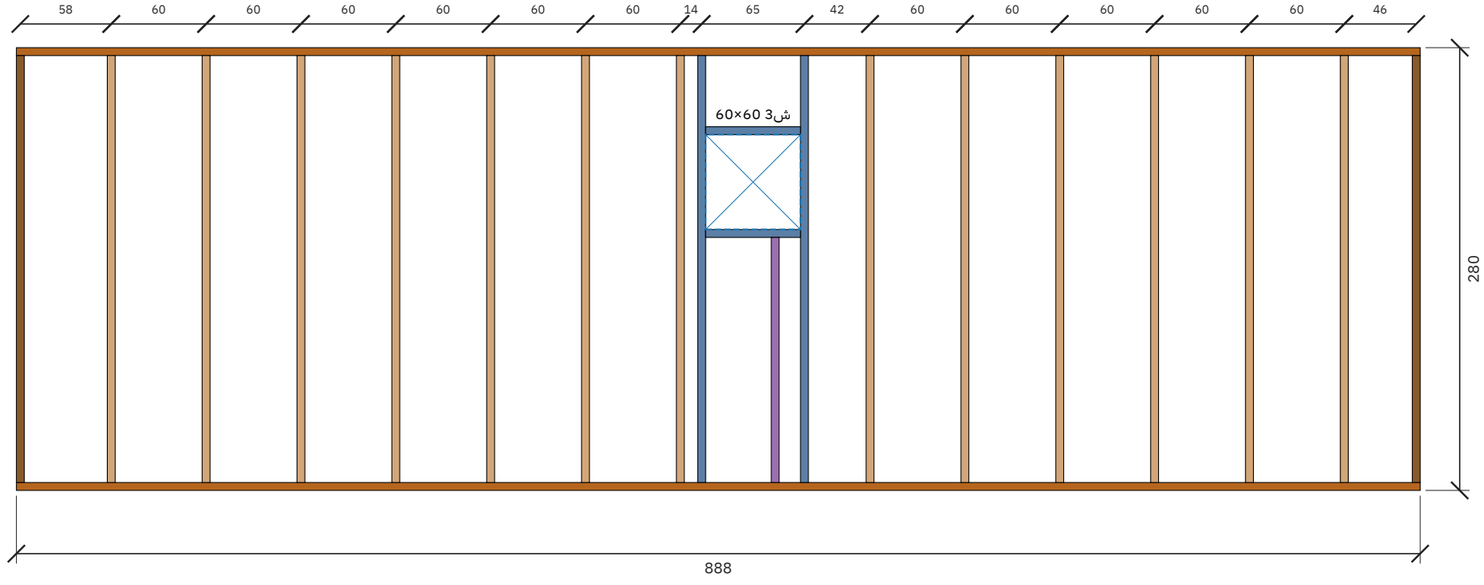


قاعدة سفلية — علوي — عمود — عمود زاوية — جنب فتحة — رأس فتحة — جلسة شباك — عمود قصير


المشروع / العميل	عنوان اللوحة	المقياس	التاريخ	رقم اللوحة
كوخ خشب 9.00 × 9.00 م — ثلاث غرف وصالة واسعة ومطبخ سيرفس **عميل — كوخ 9×9**	**لوحات التأطير (للورشة)**	**—**	**2026-11-03**	**W-08 (8/14)**

مصنع وتد الأخشاب
Watad Wood Factory

تأطير جدار شمال — الطول 888 سم، الارتفاع 280 سم

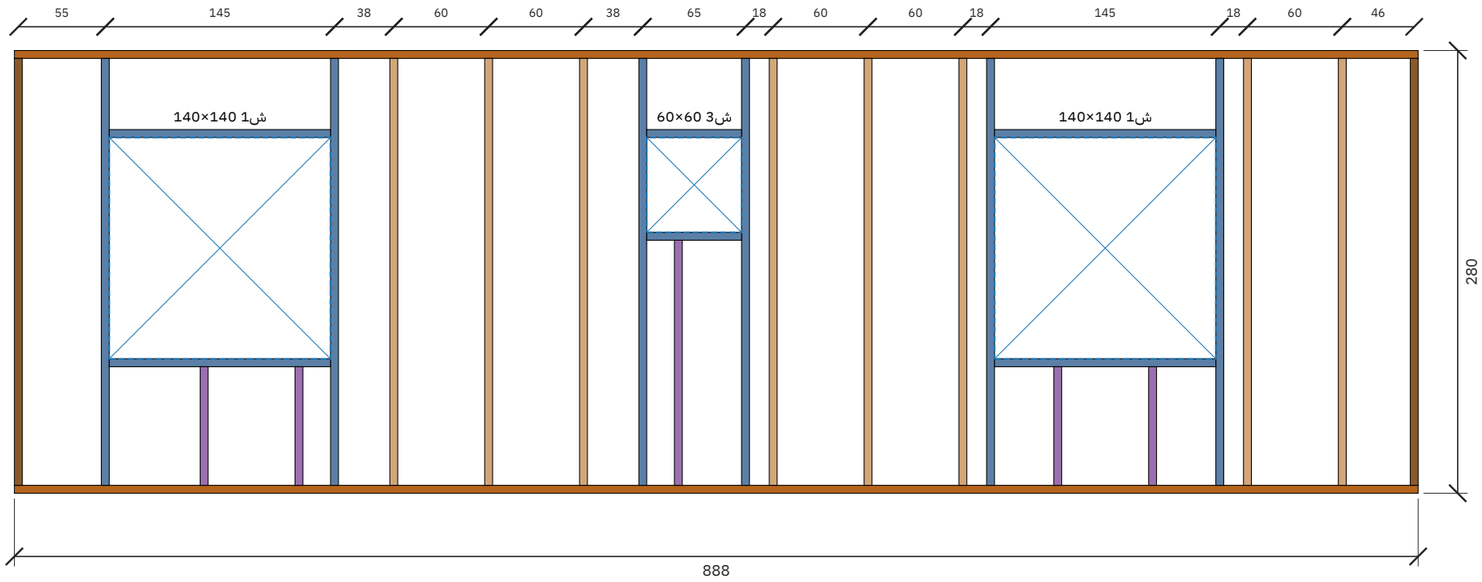

تأطير جدار غرب — الطول 888 سم، الارتفاع 280 سم

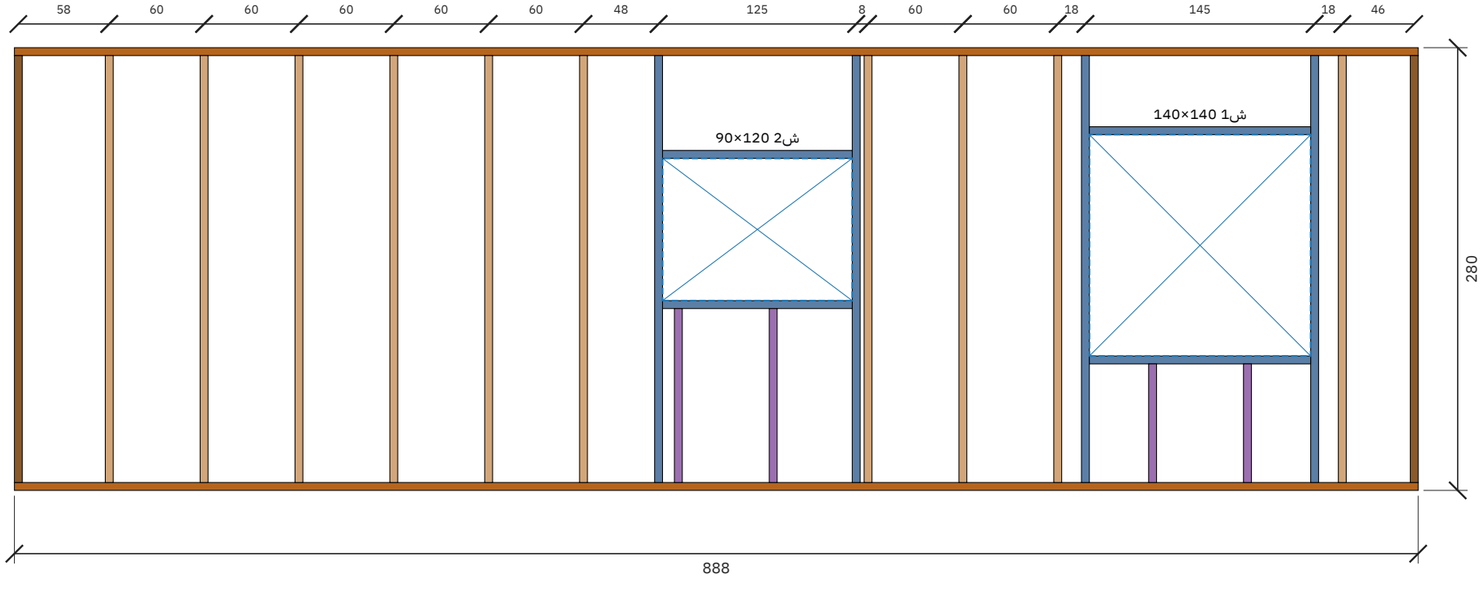


قاعدة سفلية | علوي | عمود | عمود زاوية | جنب فتحة | رأس فتحة | جلسة شباك | عمود قصير


المشروع / العميل	عنوان اللوحة	المقياس	التاريخ	رقم اللوحة
كوخ خشب 9.00 × 9.00 م — ثلاث غرف وصالة واسعة ومطبخ سيرفس **عميل — كوخ 9×9**	**لوحات التأطير (للورشة)**	**—**	**2026-11-03**	**W-09 (9/14)**

مصنع وتد الأخشاب
Watad Wood Factory

تأطير جدار جدار الغرف الشرقي — الطول 888 سم، الارتفاع 280 سم (داخلي)

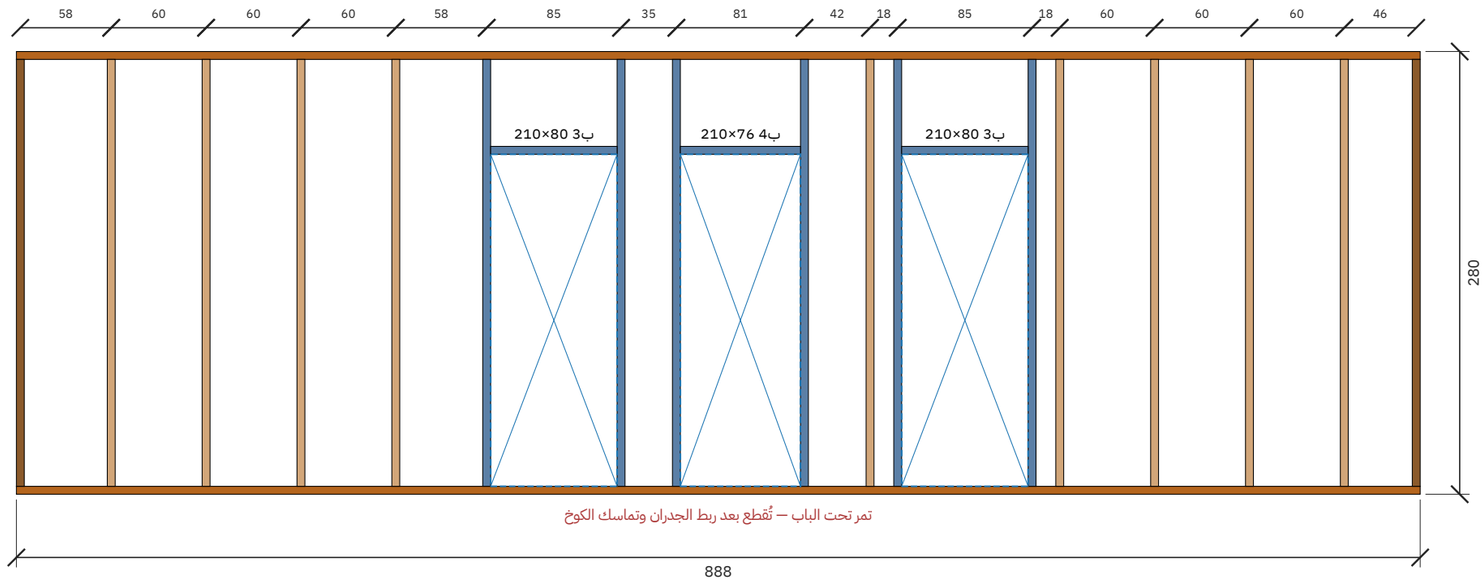

تأطير جدار جدار غرفة 3 — الطول 336 سم، الارتفاع 280 سم (داخلي)

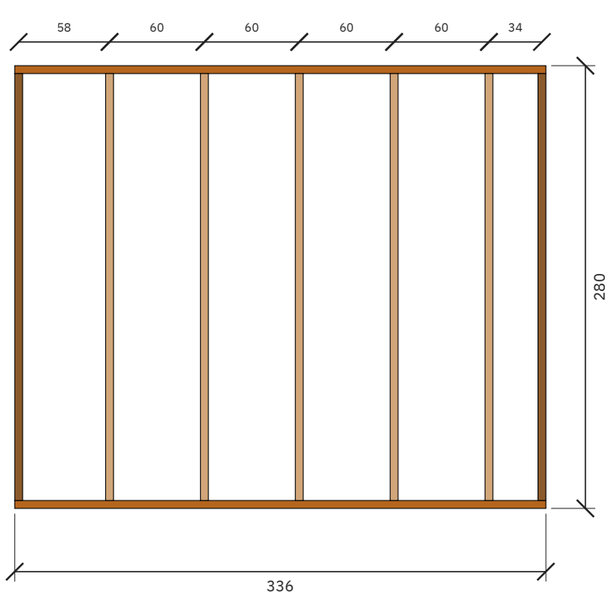


قاعدة سفلية | علوي | عمود | عمود زاوية | جنب فتحة | رأس فتحة | جلسة شباك | عمود قصير


المشروع / العميل	عنوان اللوحة	المقياس	التاريخ	رقم اللوحة
كوخ خشب 9.00 × 9.00 م — ثلاث غرف وصالة واسعة ومطبخ سيرفس **عميل — كوخ 9×9**	**لوحات التأطير (للورشة)**	**—**	**2026-11-03**	**W-10 (10/14)**

مصنع وتد الأخشاب
Watad Wood Factory

تأطير جدار جدار غرفة 2 — الطول 336 سم، الارتفاع 280 سم (داخلي)

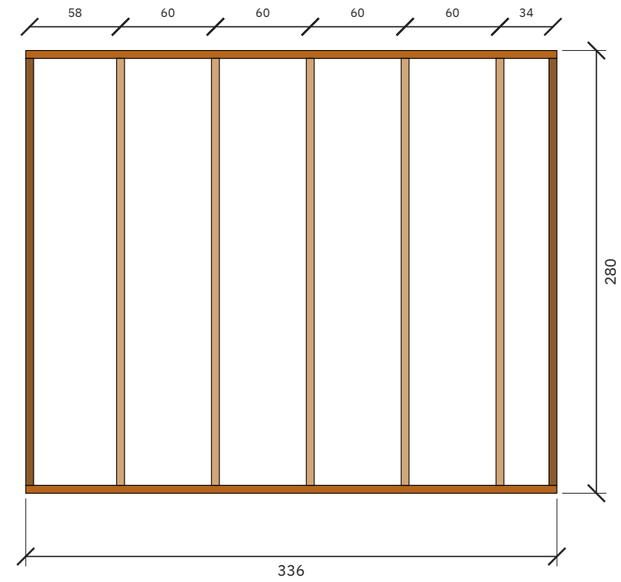


تأطير جدار جدار الرئيسية/المطبخ — الطول 356 سم، الارتفاع 280 سم (داخلي)

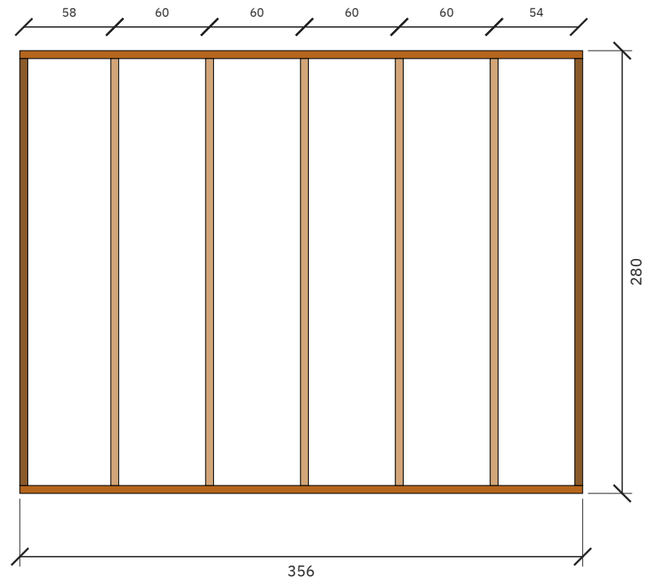


قاعدة سفلية | علوي | عمود | عمود زاوية | جنب فتحة | رأس فتحة | جلسة شباك | عمود قصير

مصنع وتد الأخشاب Watad Wood Factory	المشروع / العميل كوخ خشب 9.00 × 9.00 م — ثلاث غرف وصالة واسعة ومطبخ سيرفس عميل — كوخ 9×9	عنوان اللوحة لوحات التأطير (للورشة)	المقياس —	التاريخ 2026-11-03	رقم اللوحة W-11 (11/14)

تأطير جدار جدار الرئيسية الشرقي — الطول 356 سم، الارتفاع 280 سم (داخلي)

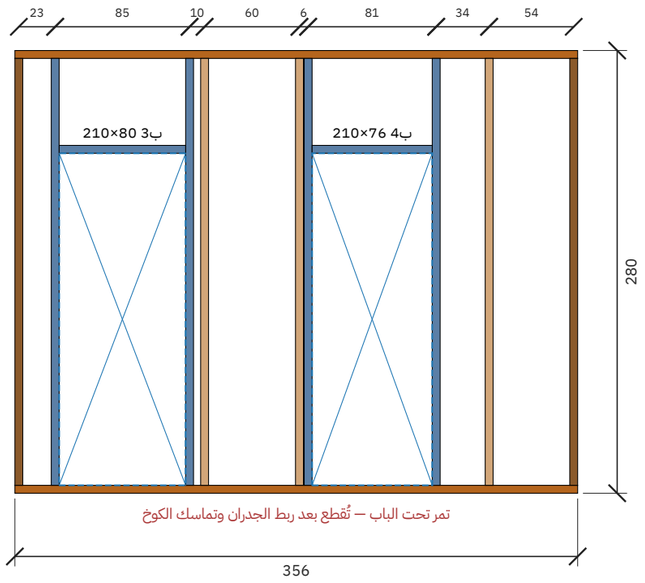

تأطير جدار جدار حمام الرئيسية — الطول 196 سم، الارتفاع 280 سم (داخلي)

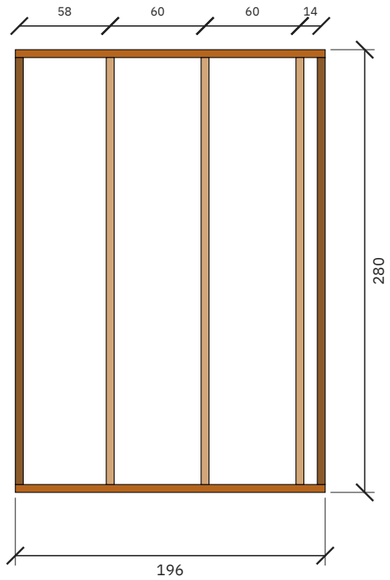

عمود قصير | جلسة شباك | رأس فتحة | جنب فتحة | عمود زاوية | عمود | علوي | قاعدة سفلية

المشروع / العميل	عنوان اللوحة	المقياس	التاريخ	رقم اللوحة
كوخ خشب 9.00 × 9.00 م — ثلاث غرف وصالة واسعة ومطبخ سيرفس **عميل — كوخ 9×9**	**لوحات التأطير (للورشة)**	**—**	**2026-11-03**	**W-12 (12/14)**

مصنع وتد الأخشاب
Watad Wood Factory

جدول الكميات وخطة تقطيع الطبليات

البند	القيمة
الارتفاع المطلوب / المعتمد	280 / 280 سم
السقف	جملون 30° — أعلى نقطة 540 سم من وجه الصبة
المدادات 5×15	68 مداد (17 خط × قطعتين موصولة فوق الجسر الحامل بتراكب 60 سم) × حتى 341 سم — من طبلية 480
طبليات الطريقة الأولى (مداد + عمود)	68 طبلية × 480 سم
طبليات الطريقة الثانية (3 أعمدة)	25 طبلية × 320 سم
مدادات المثلث البارز (S) 40°	10 مداد حتى 235 سم (طبلية 320) + 2 مداد وادي 342 سم
إجمالي الطبليات 5×22.5	105
إجمالي قطع 5×7	166
قائمة تقطيع 5×7	888سم×10 | 356سم×4 | 336سم×4 | 320سم×1 | 270سم×112 | 196سم×2 | 160سم×2 | 155سم×2 | 140سم×6
	120سم×2 | 110سم×2 | 100سم×1 | 80سم×3 | 76سم×2 | 75سم×9 | 60سم×4
ألواح تلبيس 2.5 سم	337 لوح × 400 سم (مجموع الصفوف 1253.2 م، 20 وجه)
أسمنت بورد 12 مم (122×244)	32 لوح (داخل دورات المياه)
العزل	196 لوح فوم صخري 80
الصبة	يجهزها العميل — 20 سم، مفرغة تحت دورات المياه

مراجعة التصميم مقابل قواعد المصنع

النوع	البند	التفاصيل	المقترح
ملاحظة	بحر المدادات	أطول بحر بدون جدار داخلي يحمل المداد: جهة أ: 450 سم، جهة ب: 362 سم. يحتاج رقم المصنع لأقصى بحر مسموح لتحديد المدادات اللي تُقوّى 20×5.	
ملاحظة	الصبة والدرج	ارتفاع الصبة 45 سم ← 3 درجة بقائمة 15.0 سم.	
ملاحظة	مناسيب رؤوس الفتحات	رؤوس الأبواب والشبابيك على مناسيب مختلفة: 205، 210، 220، 230 سم.	
سؤال	يحتاج تأكيد	أقصى بحر للمداد بدون جدار داخلي قبل إضافة تقوية 5×7 (مداد 20×5)؟	
سؤال	يحتاج تأكيد	التغطية الصافية للوح التلبيس بعد التعشيق (مستنتجة مؤقتاً 18.67 سم من 280/15)؟	
سؤال	يحتاج تأكيد	هل يوضع أعمدة قصيرة فوق رأس الشباك/الباب إلى العلوي؟	
سؤال	يحتاج تأكيد	مكان الوصلة في القاعدة والعلوي إذا الجدار أطول من الطبلية؟	