


مصنع وتد الأخشاب · ملف التصميم

كوخ خشب 9.00 × 9.00 م – ثلاث غرف

81 م² · صالة واسعة ومطبخ سيرفس · غرفة رئيسية بحمامها + غرفتين + حمام مشترك · دكة أمامية


المسقط الأفقي مع الفرش

الأبعاد بالسنتيمتر - الجدران: قوائم 7×5 + تلبيس 2.5 من الجهتين (12 سم)

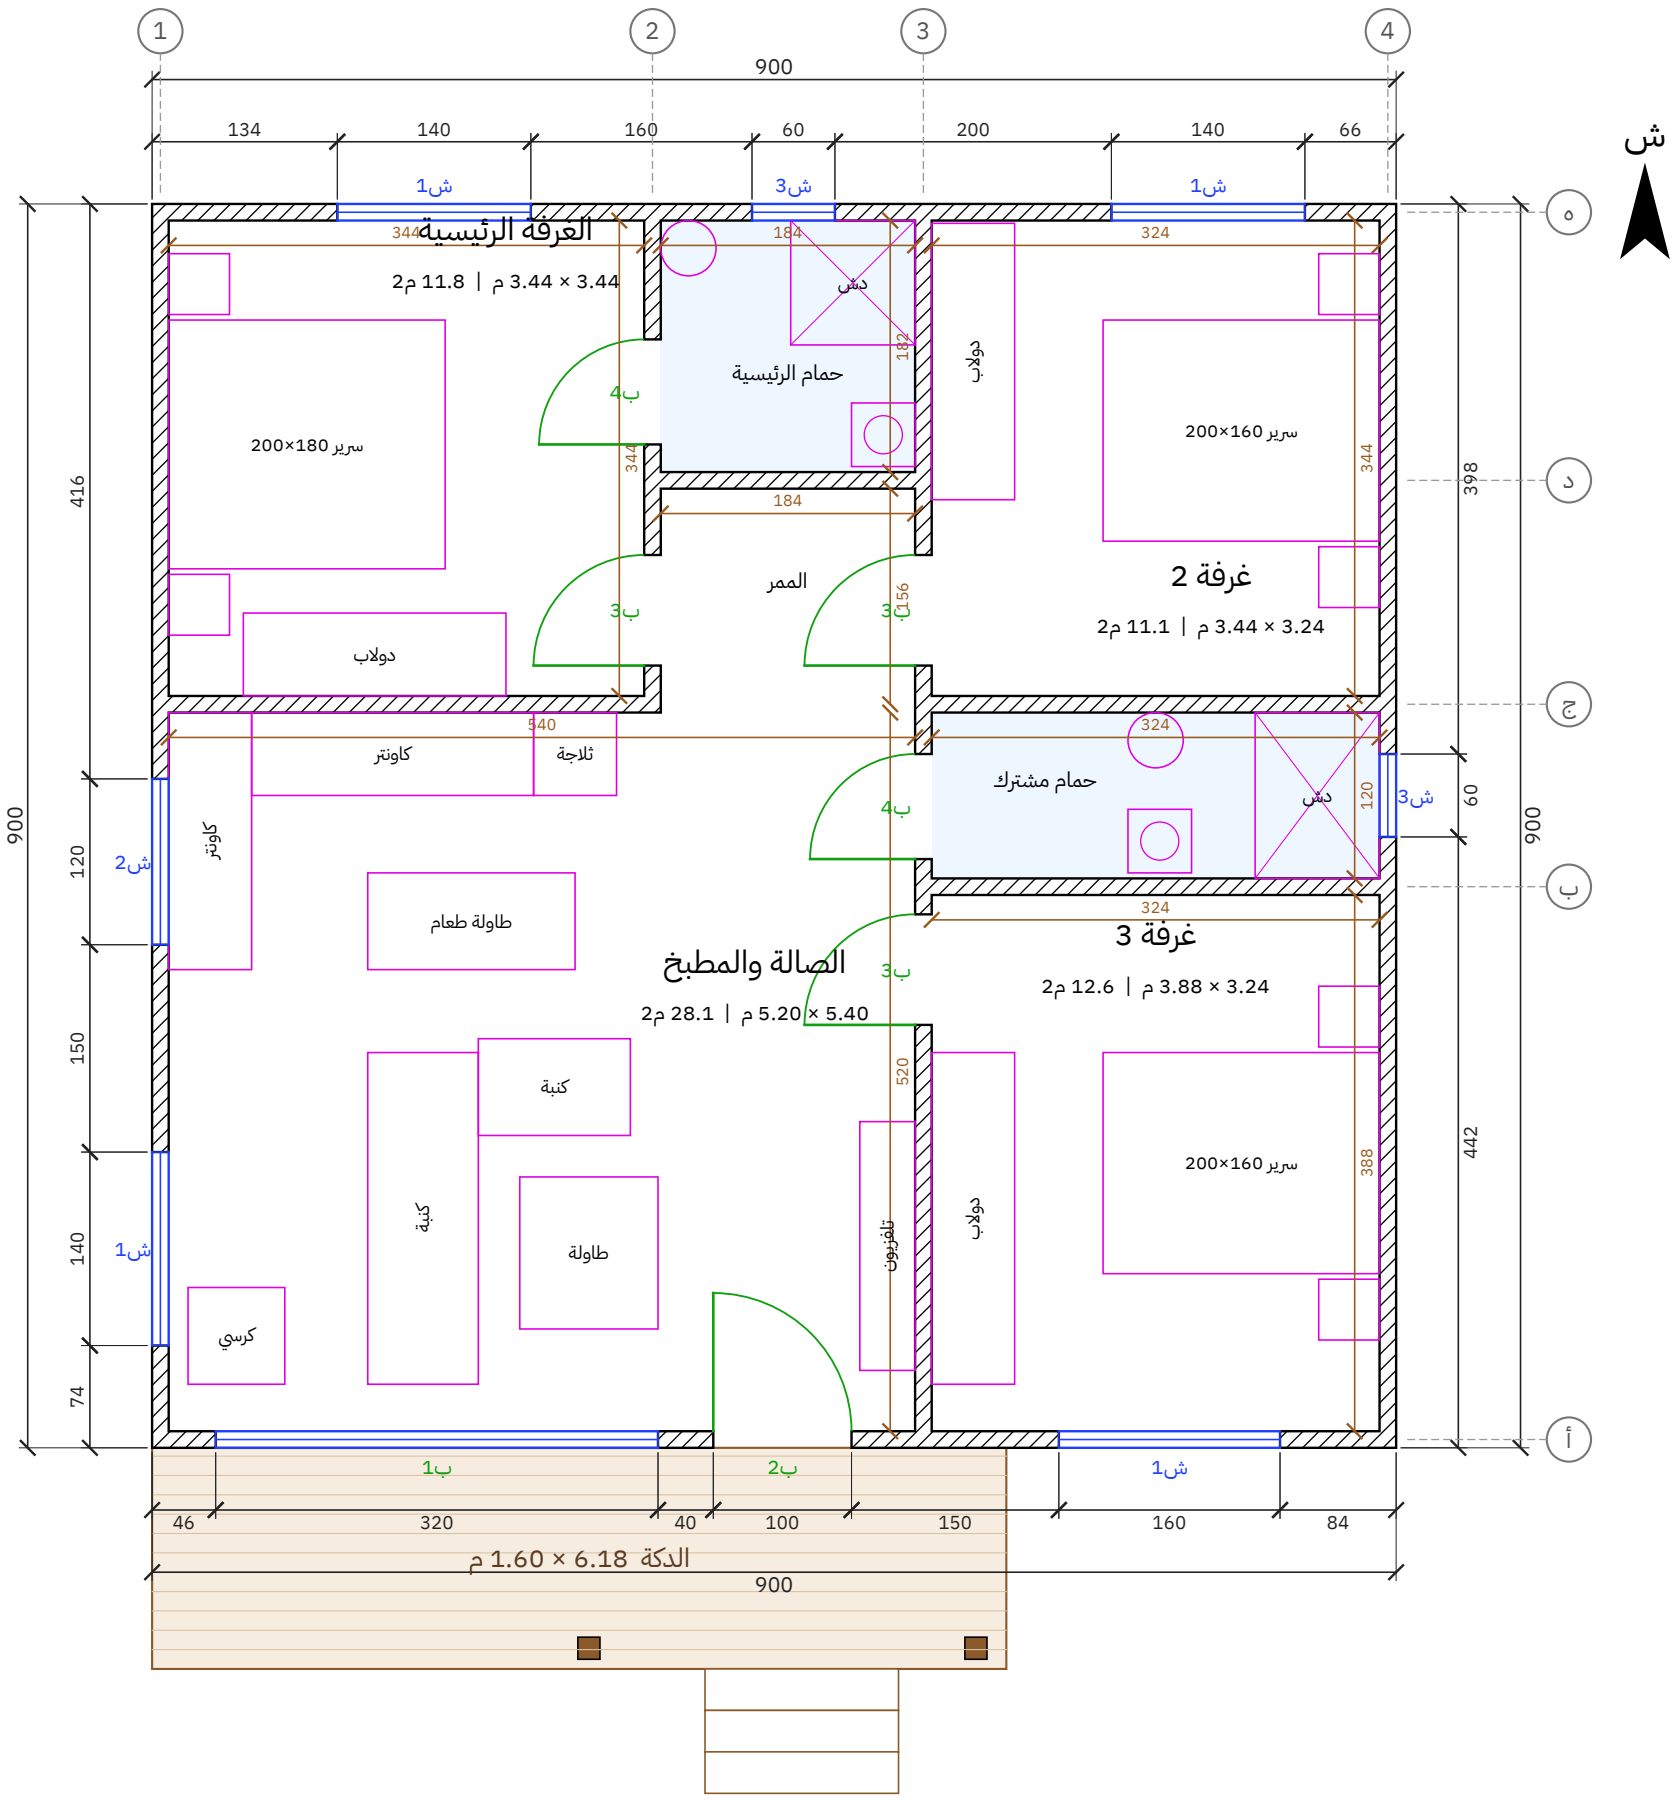


3 درجات × 15 سم

مصنع وتد الأخشاب Watad Wood Factory	المشروع / العميل كوخ خشب 9.00 × 9.00 م – ثلاث غرف وصالة واسعة ومطبخ سيرفس عميل – كوخ 9×9	عنوان اللوحة المسقط الأفقي	المقياس 1:50	التاريخ 2026-11-03	رقم اللوحة A-02 (2/10)

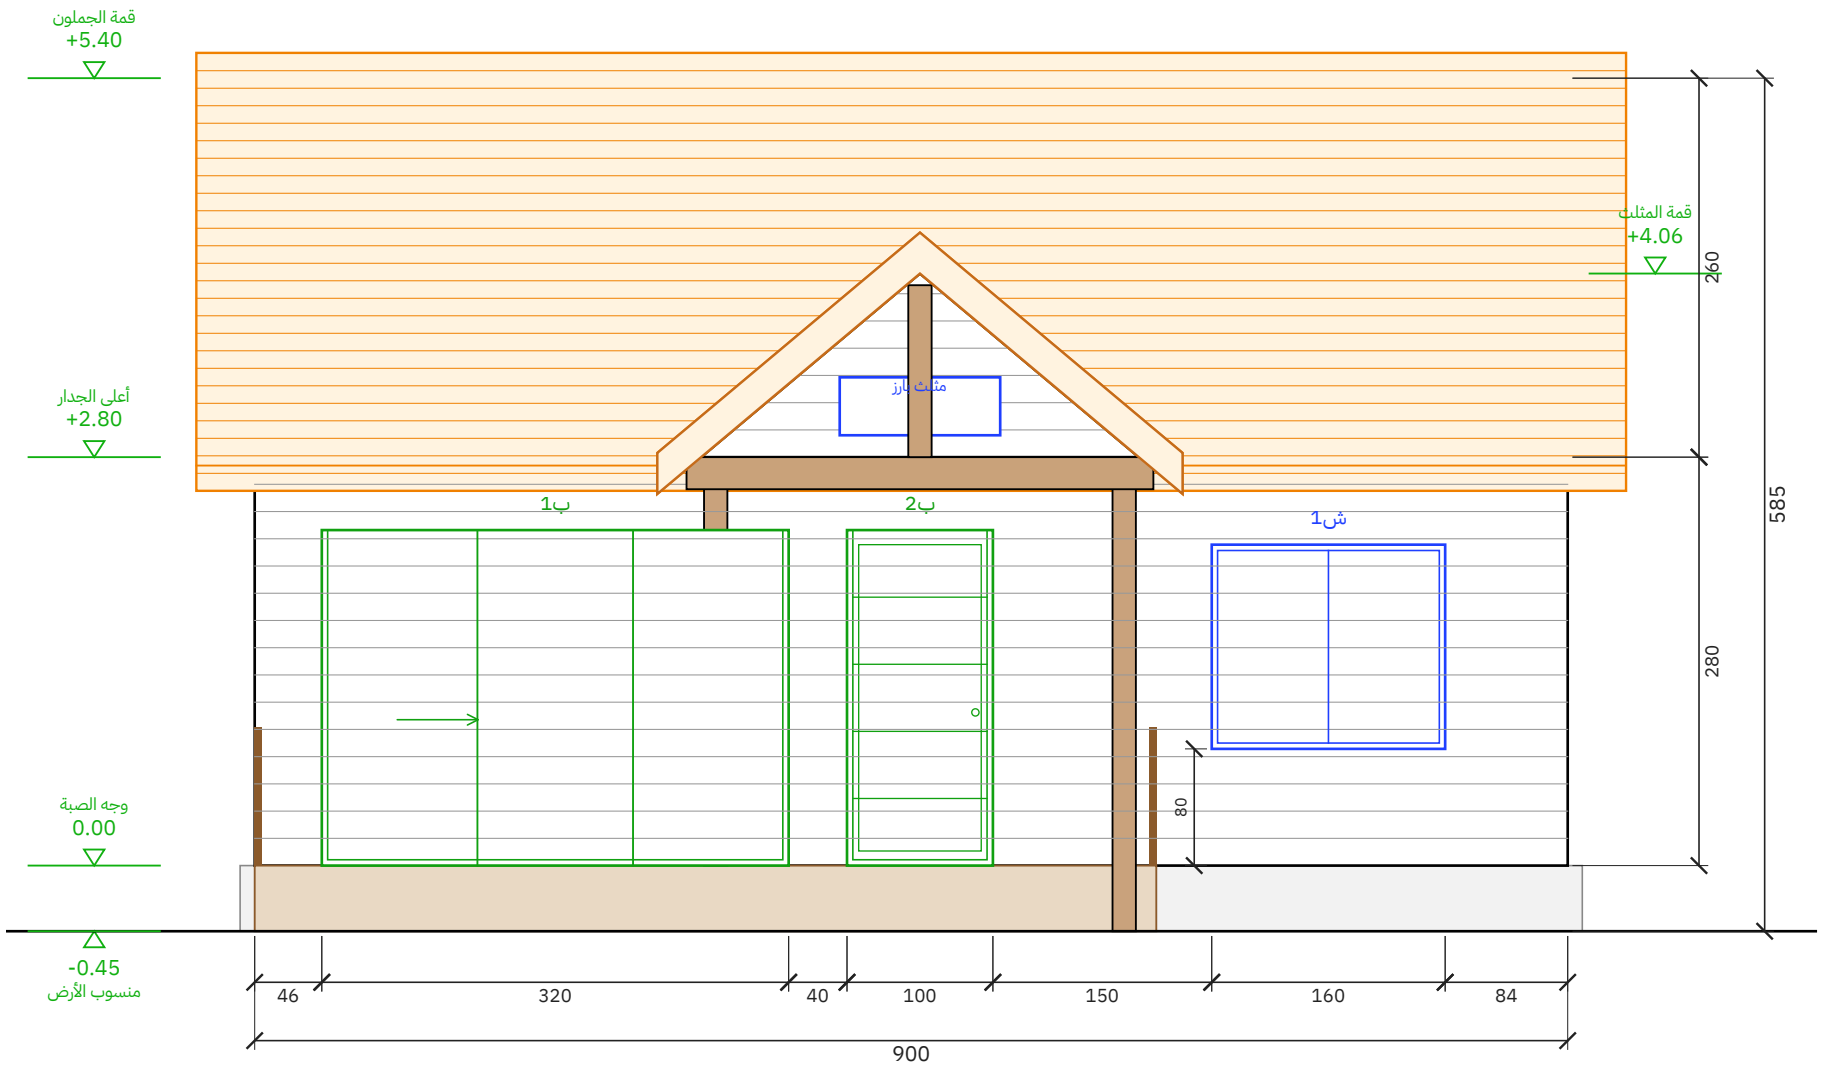

الواجهة الأمامية

مقياس 1:50 | الوحدة: سم

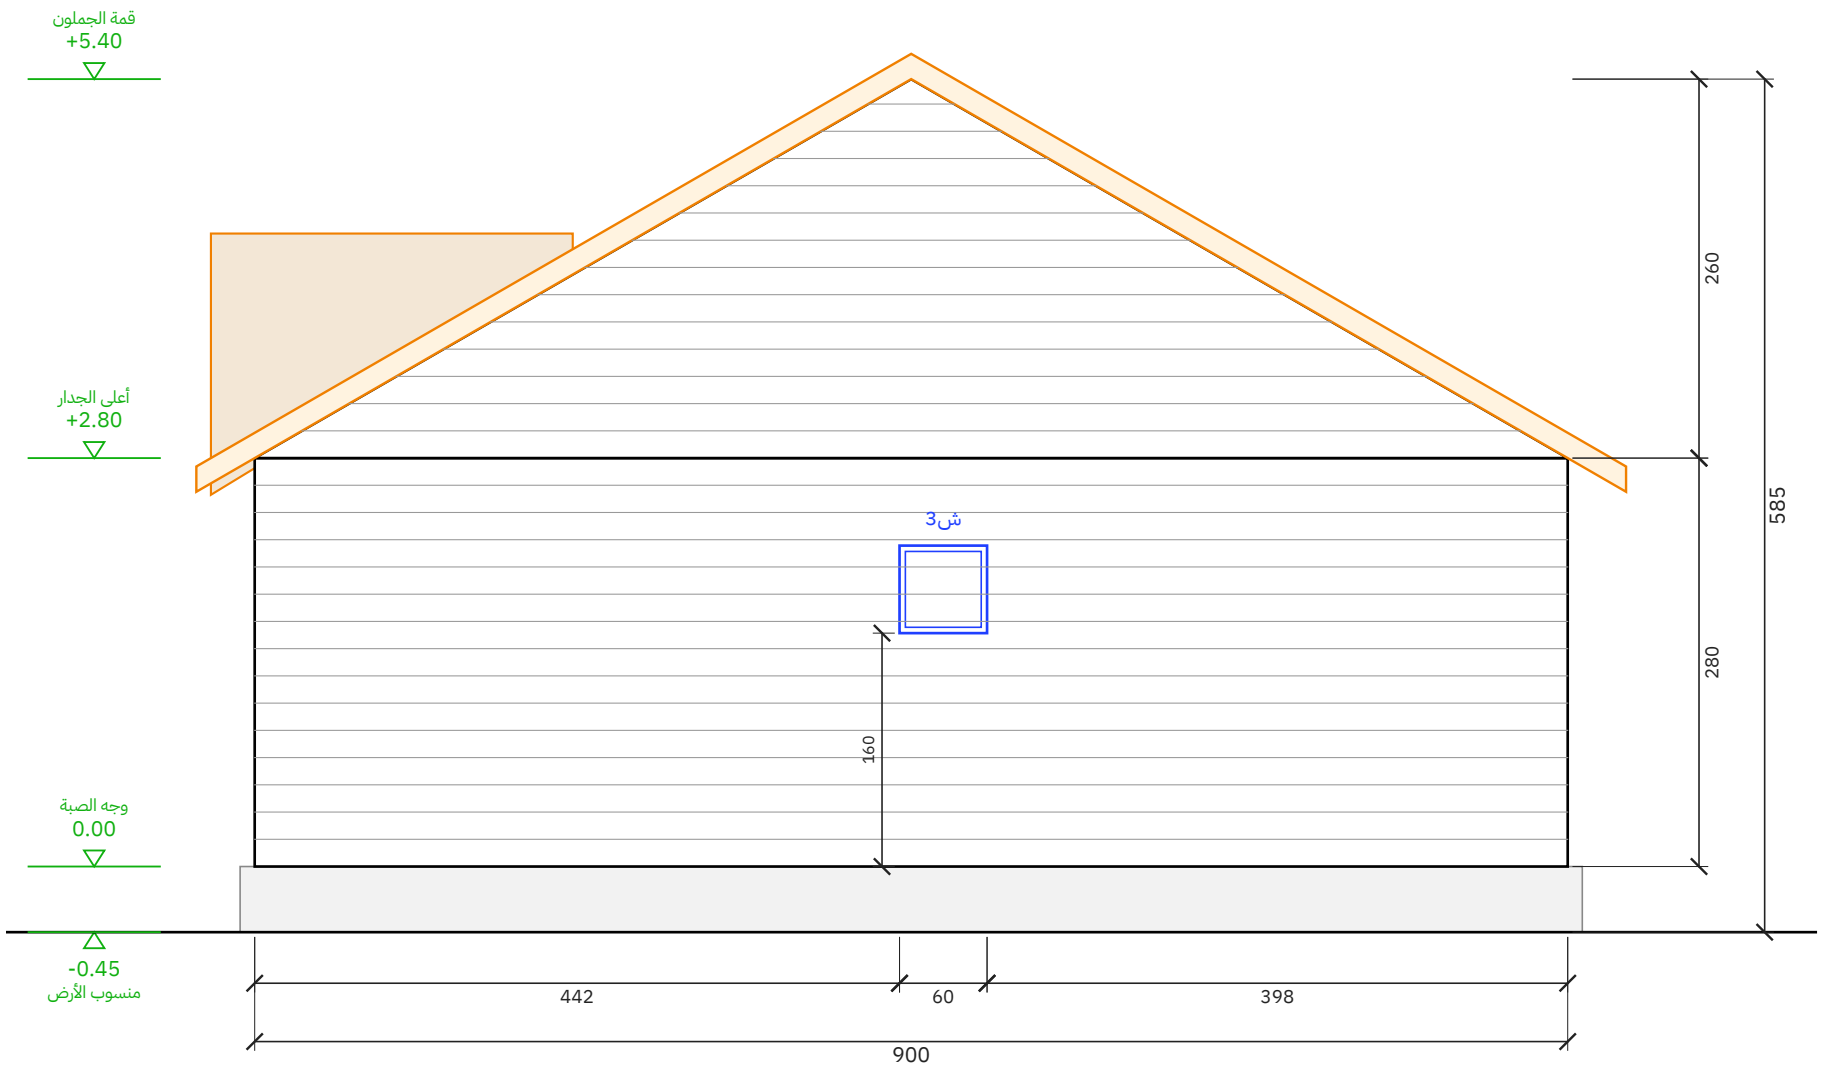


الواجهة الشرقية

مقياس 1:50 | الوحدة: سم


المشروع / العميل	عنوان اللوحة	المقياس	التاريخ	رقم اللوحة
كوخ خشب 9.00 × 9.00 م – ثلاث غرف وصالة واسعة ومطبخ سيرفس عميل – كوخ 9×9	الواجهة الأمامية والواجهة الشرقية	1:50	2026-11-03	A-03 (3/10)

مصنع وتد الأخشاب
Watad Wood Factory

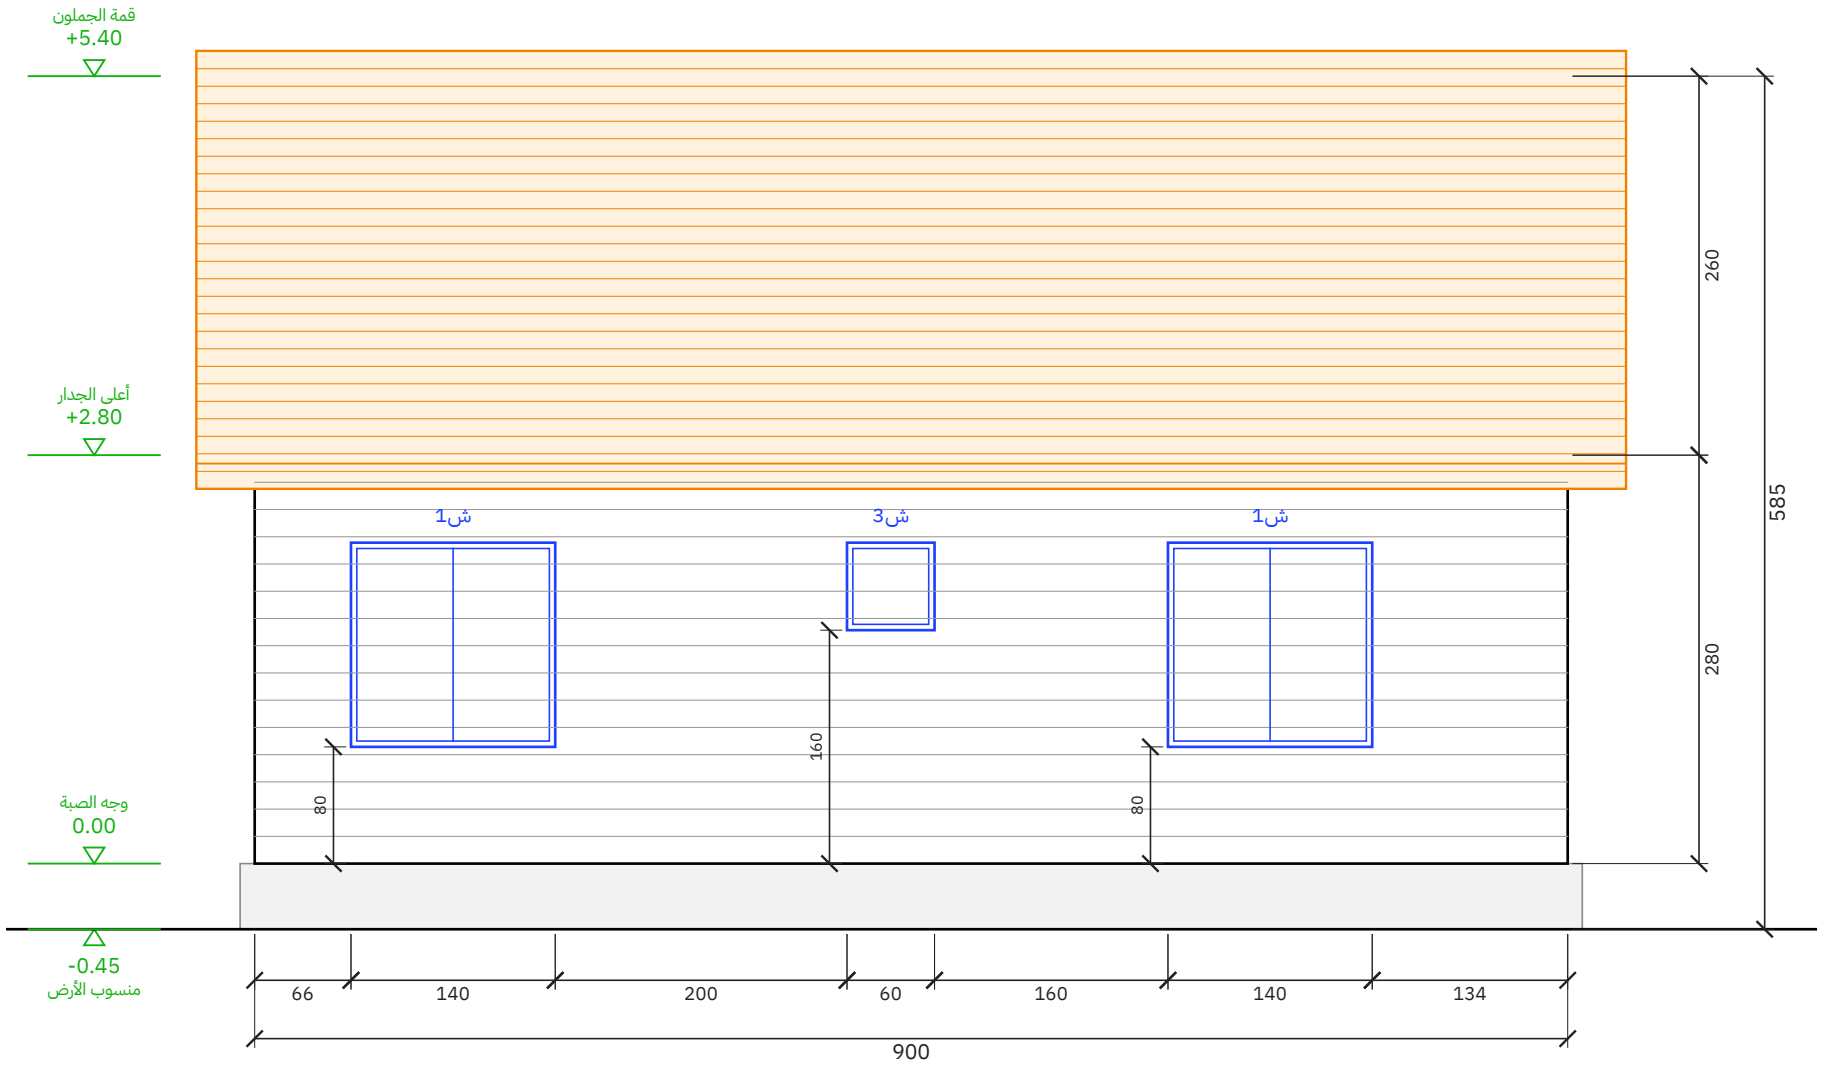

الواجهة الخلفية

مقياس 1:50 | الوحدة: سم

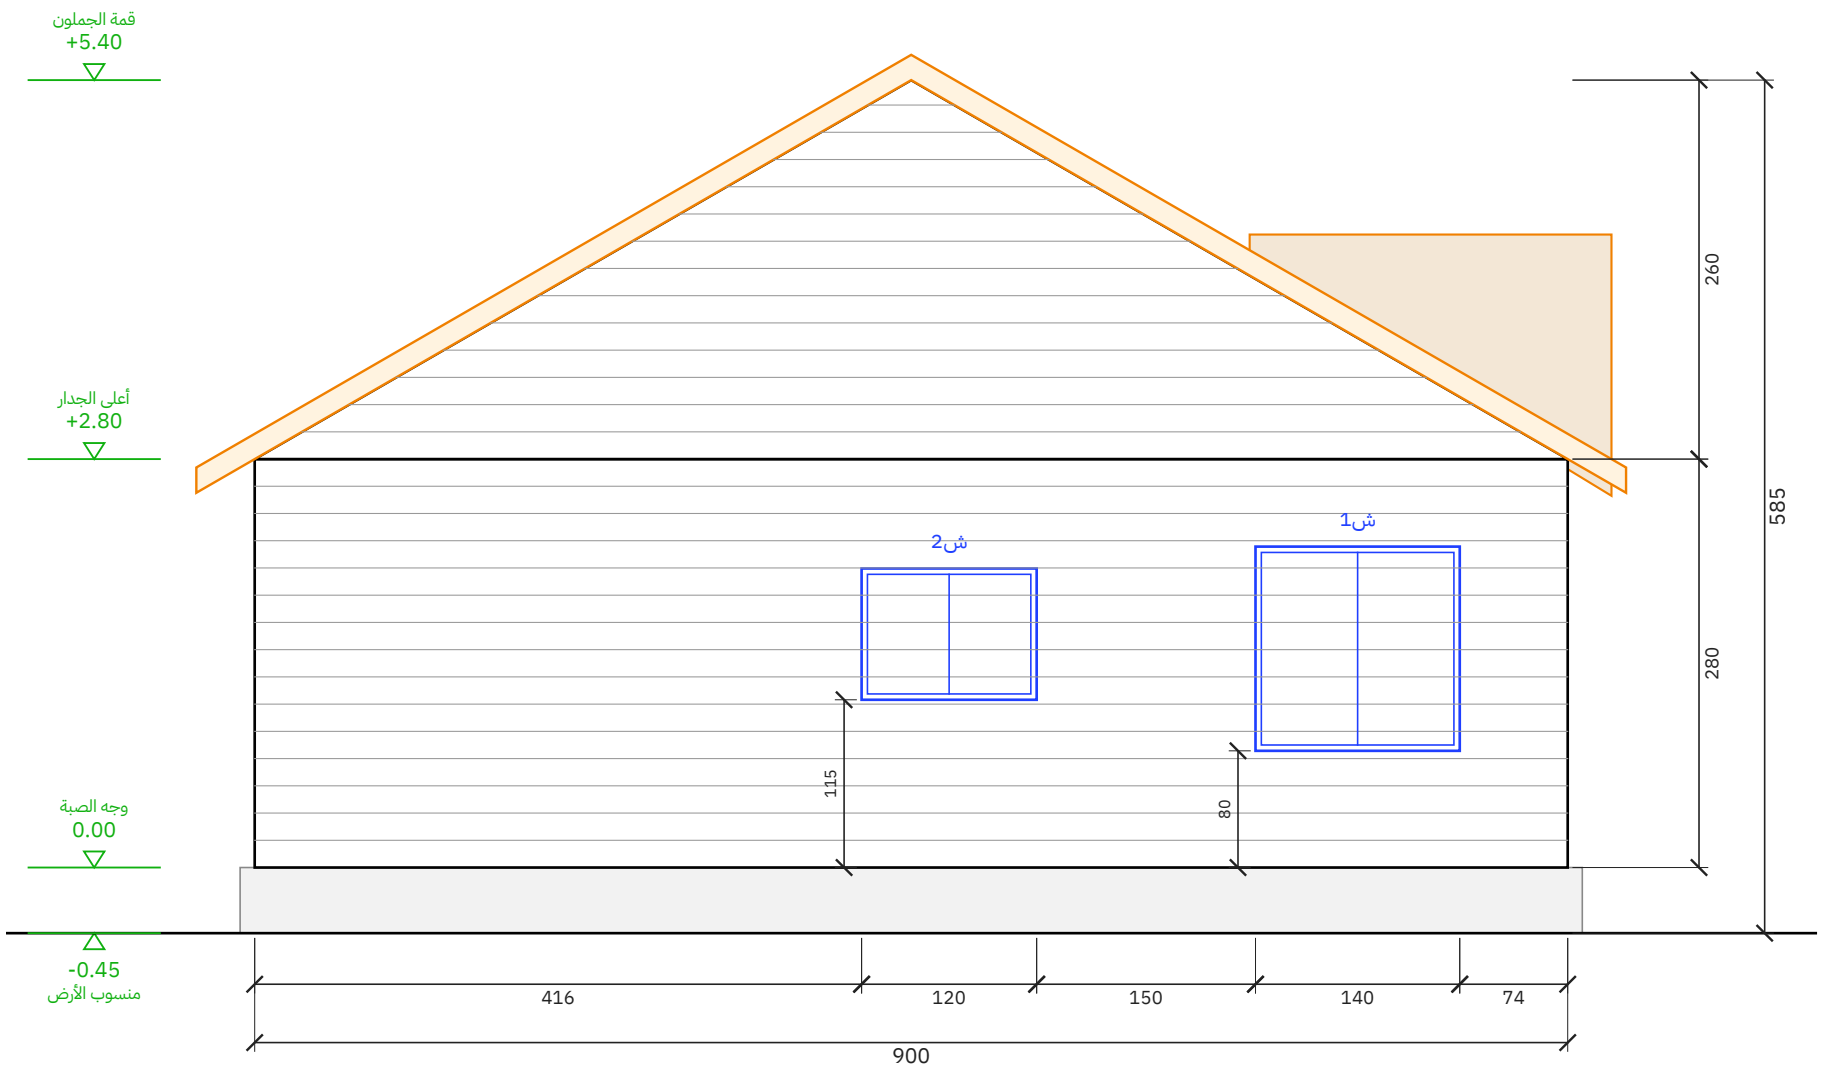

الواجهة الغربية


مقياس 1:50 | الوحدة: سم

المشروع / العميل	عنوان اللوحة	المقياس	التاريخ	رقم اللوحة
كوخ خشب 9.00 × 9.00 م – ثلاث غرف وصالة واسعة ومطبخ سيرفس عميل – كوخ 9×9	الواجهة الخلفية والواجهة الغربية	1:50	2026-11-03	A-04 (4/10)

مصنع وتد الأخشاب
Watad Wood Factory


مسقط السقف (جملون)

رفرف 40 سم من كل جهة | مقياس 1:50

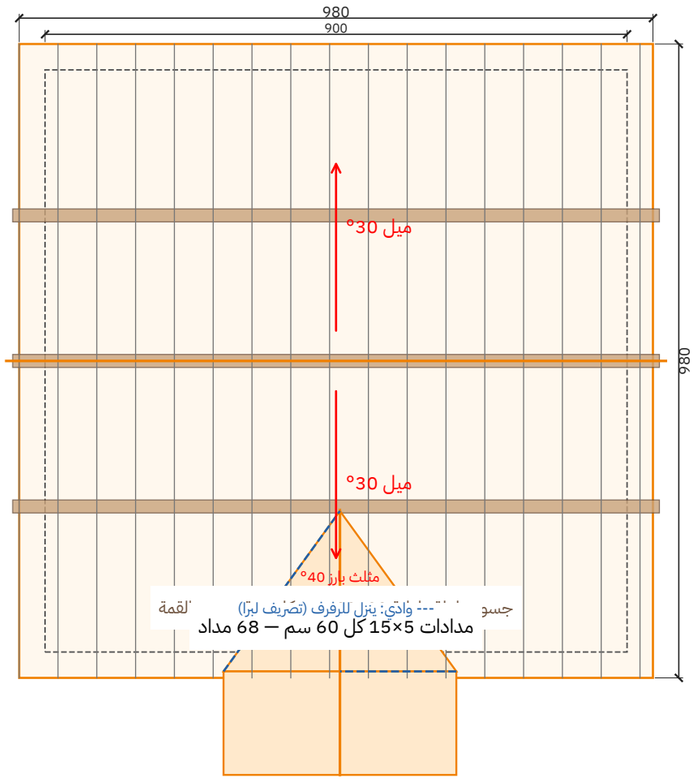


قطاع عرضي أ-أ

مقياس 1:50 | الوحدة: سم

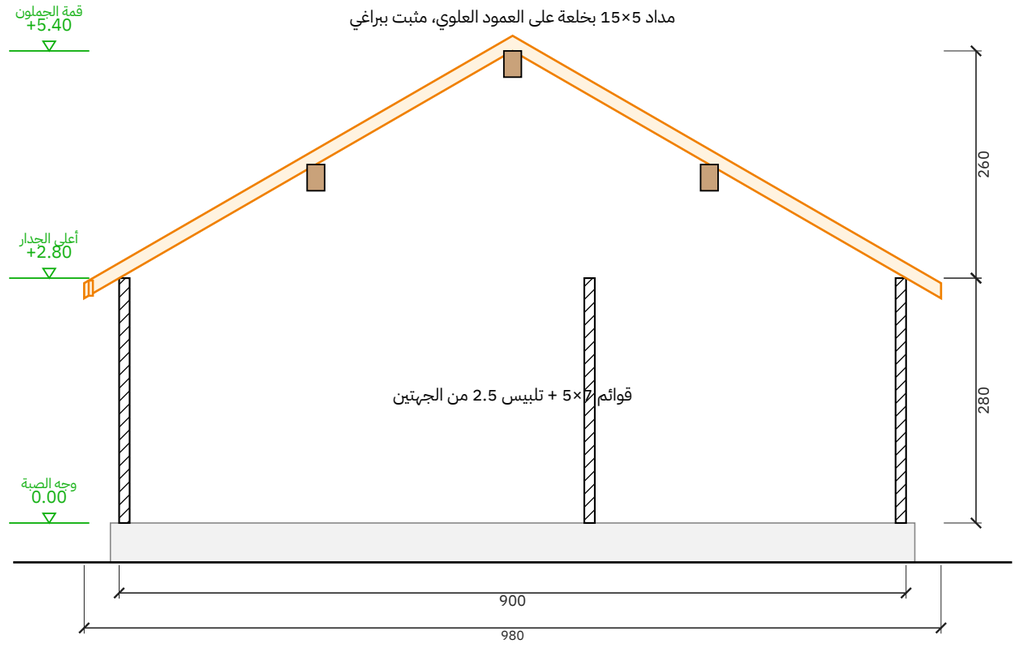

تفصيلة جلوس المداد على العلوي (1:5)

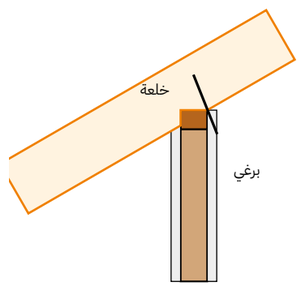

علوي 7×5 على قائم 7×5

المشروع / العميل **كوخ خشب 9.00 × 9.00 م — ثلاث غرف وصالة واسعة ومطبخ سيرفس** **عميل — كوخ 9×9**	عنوان اللوحة **مسقط السقف والقطاع**	المقياس **1:50**	التاريخ **2026-11-03**	رقم اللوحة **A-05 (5/10)**	**مصنع وتد الأخشاب** Watad Wood Factory

لقطات المنظور الخارجي

المنظور الأمامي




منظور أمامي من اليسار



منظور أمامي من اليمين




المنظور الخلفي

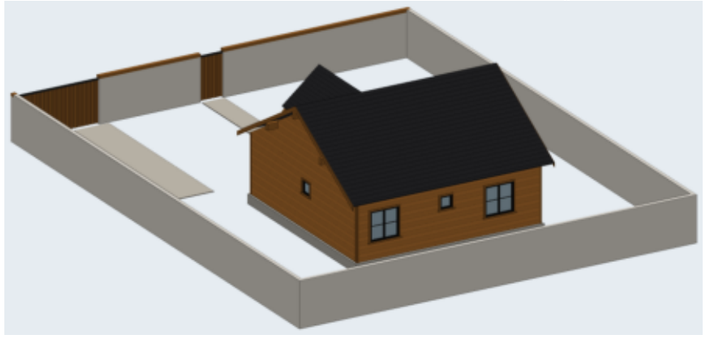

منظور خلفي من اليمين



منظر علوي

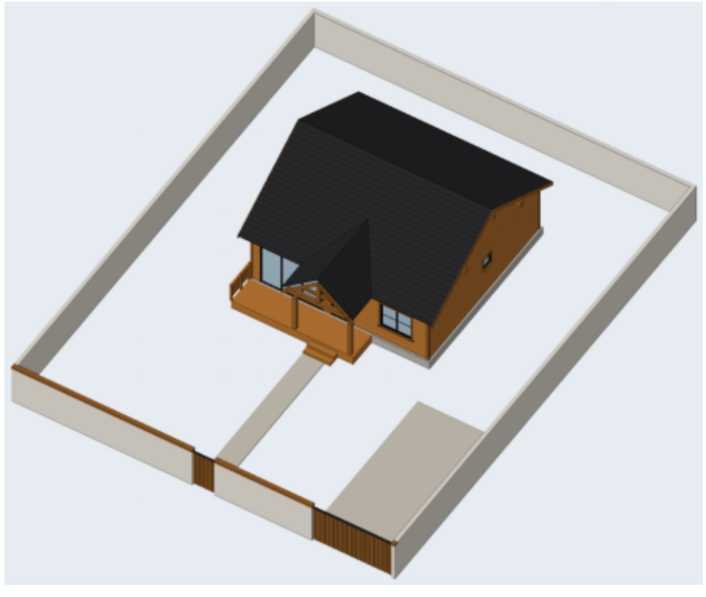


المشروع / العميل	عنوان اللوحة	المقياس	التاريخ	رقم اللوحة
كوخ خشب 9.00 × 9.00 م – ثلاث غرف وصالة واسعة ومطبخ سيرفس **عميل – كوخ 9×9**	**لقطات المنظور**	**–**	**2026-11-03**	**A-08 (8/10)**

مصنع وتد الأخشاب
Watad Wood Factory

المقطع العلوي بالفرش

مقطع أفقي على ارتفاع 1.90 م — توزيع الفرش ومسار الحركة

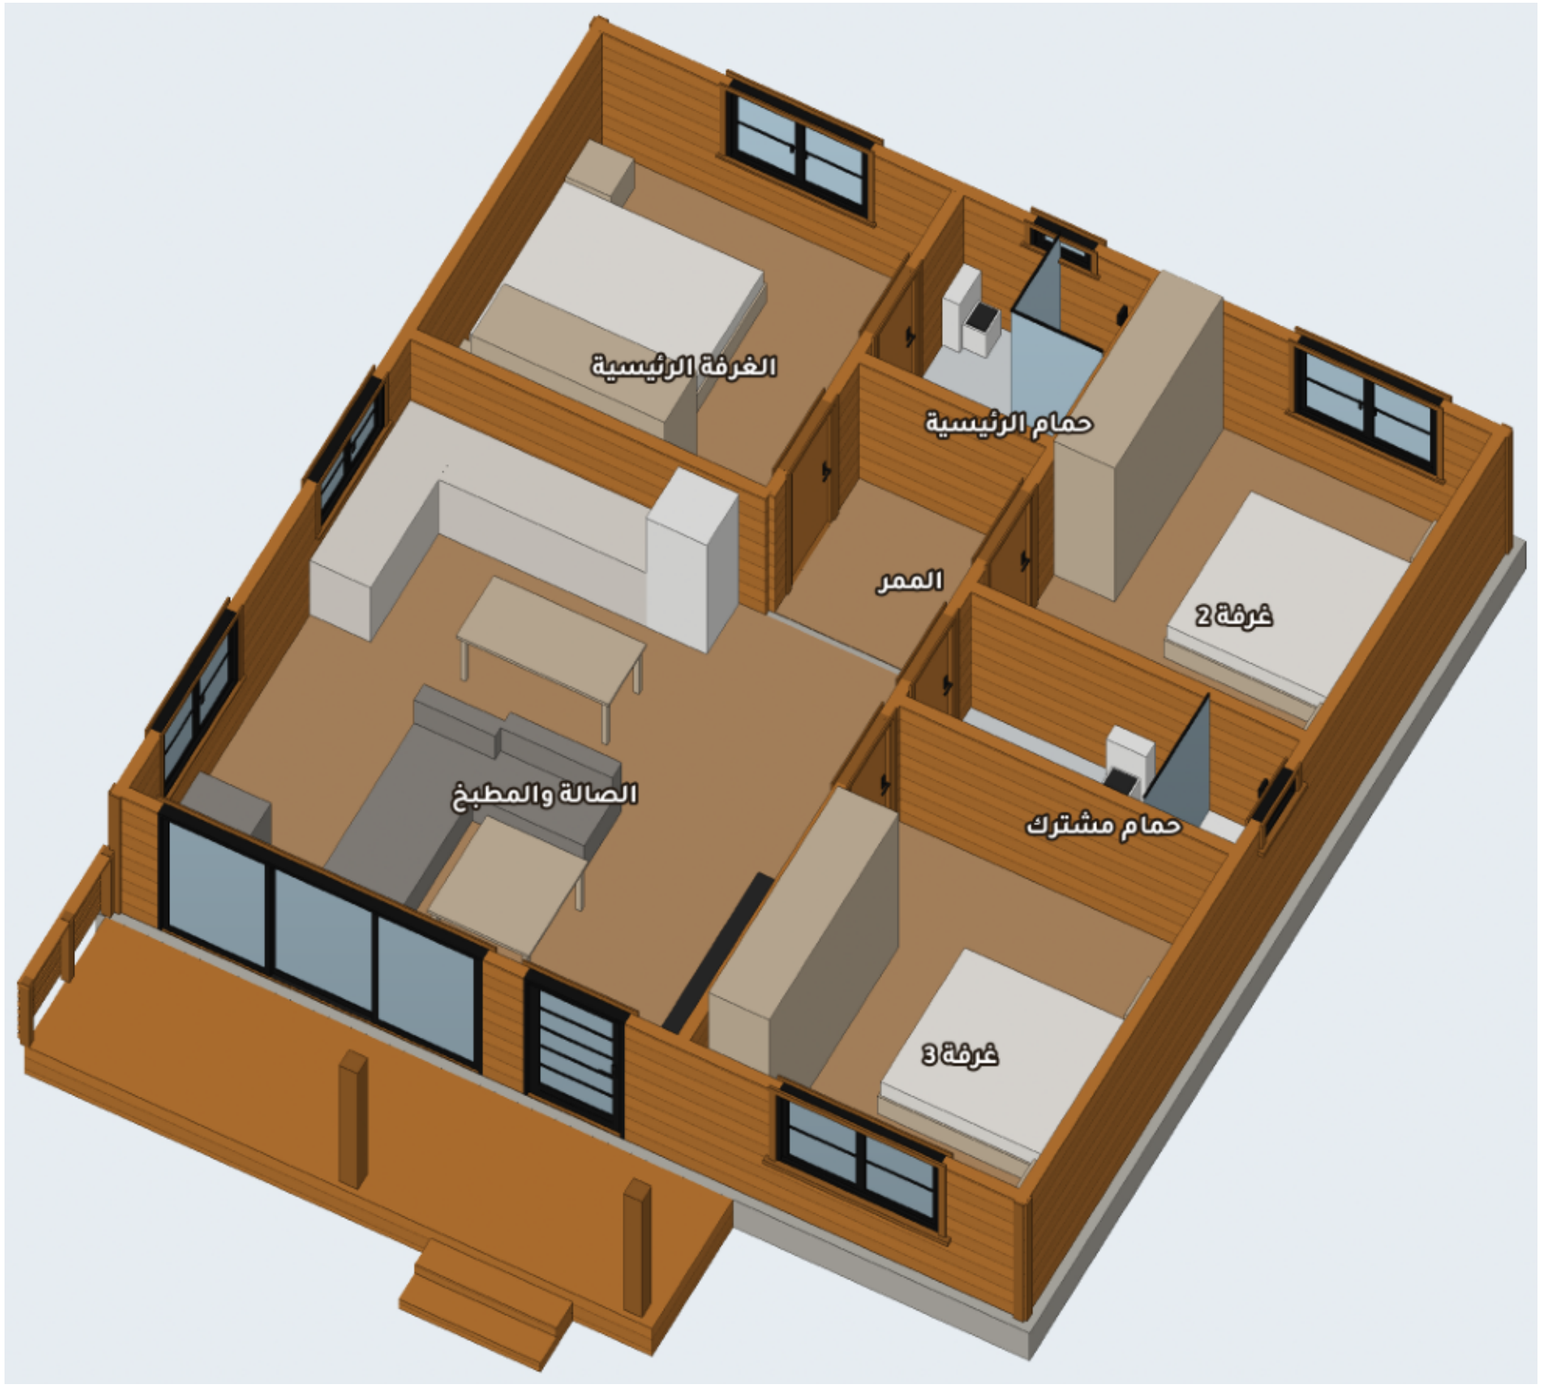

المشروع / العميل	عنوان اللوحة	المقياس	التاريخ	رقم اللوحة
كوخ خشب 9.00 × 9.00 م — ثلاث غرف وصالة واسعة ومطبخ سيرفس عميل — كوخ 9×9	المقطع العلوي بالفرش	—	2026-11-03	A-09 (9/10)

مصنع وتد الأخشاب
Watad Wood Factory



مصنع وتد الأخشاب

أمامي من الموقف · الخارج – نهاراً



مصنع وتد الأخشاب



مصنع وتد الأخشاب

منظر علوي – الأرض والسور · الخارج – نهاراً





مصنع وتد الأخشاب



مصنع وتد الأخشاب



مصنع وتد الأخشاب

الصالة – جدار التلفزيون · الداخل



مصنع وتد الأخشاب




مصنع وتد الأخشاب

جدول مساحات الموقع

البند	المقاس	المساحة (م²)
مساحة الأرض	19.00 × 24.00 م	456.0
مسطح الكوخ (البصمة)	9.00 × 9.00 م	81.0
تراس الكوخ	1.60 × 6.18 م	9.9
موقف سيارة	4.30 × 8.90 م	38.3
ممر	1.10 × 9.24 م	10.2
المسطحات الخضراء (حديقة)	الباقي	316.7

الموقع العام وتنسيق الحديقة (لاندسكيب)

الأرض 19 × 24 م = 456 م² | الأبعاد بالسنتيمتر

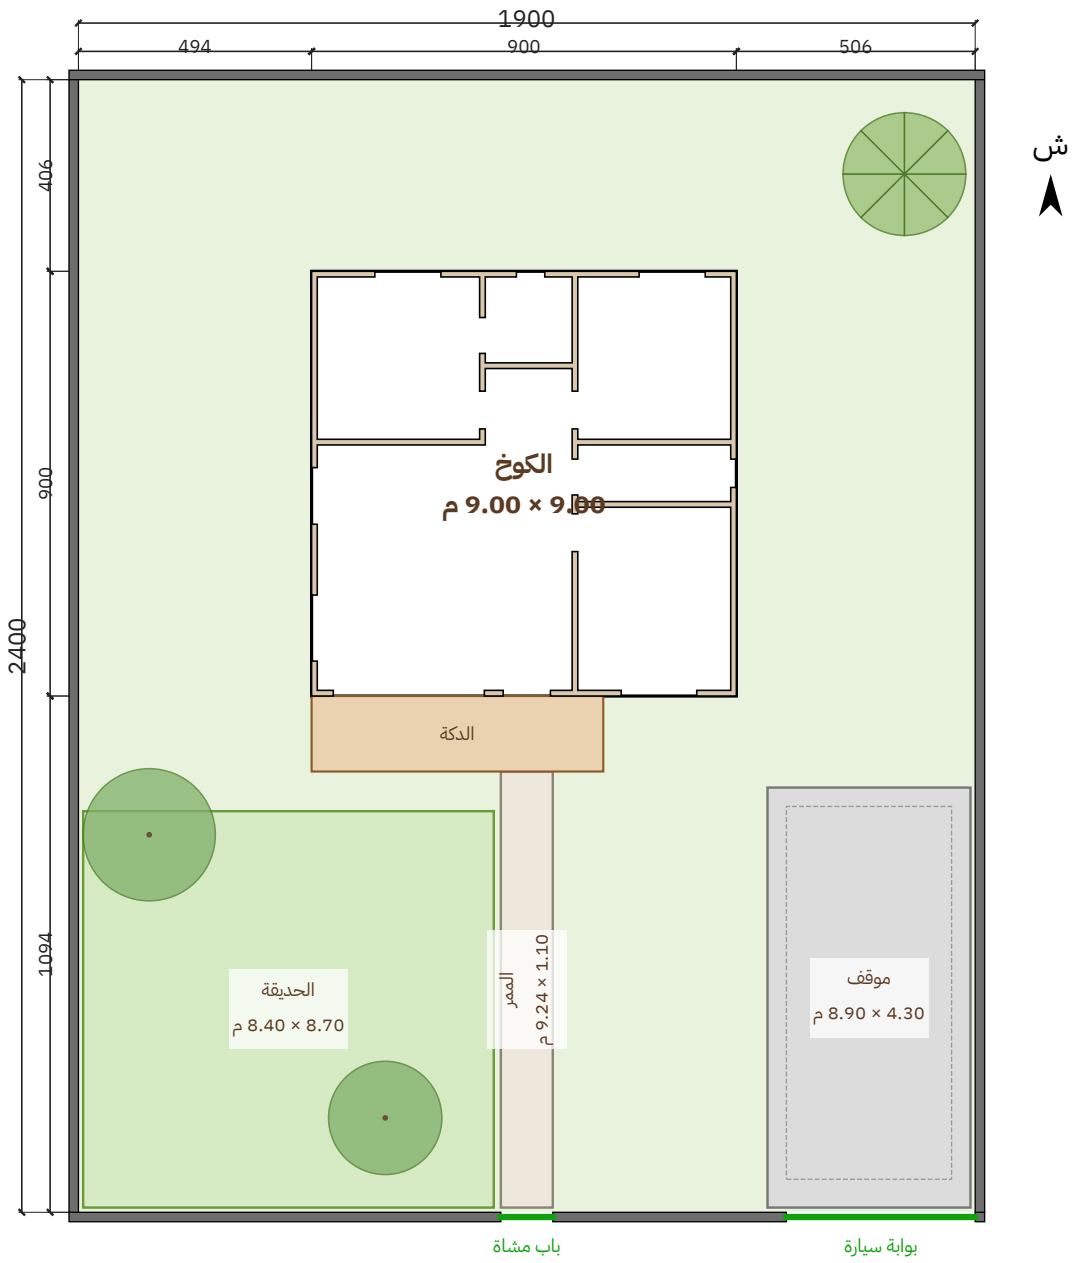

المشروع / العميل	عنوان اللوحة	المقياس	التاريخ	رقم اللوحة
كوخ خشب 9.00 × 9.00 م – ثلاث غرف وصالة واسعة ومطبخ سيرفس **عميل – كوخ 9×9**	**الموقع العام واللاندسكيب**	**1:200**	**2026-11-03**	**A-01 (1/10)**

مصنع وتد الأخشاب
Watad Wood Factory

جدول مقاسات الأبواب والشبابيك


مقاس الفتحة الصافي في الجدار - الوحدة: سم

الرمز	النوع	العرض (سم)	الارتفاع (سم)	ارتفاع الجلسة (سم)	العدد	الموقع
ب1	باب	320	230	-	1	الأمامية
ب2	باب	100	230	-	1	الأمامية
ب3	باب	80	210	-	3	غرفة 3 - غرفة 2 - الغرفة الرئيسية
ب4	باب	76	210	-	2	الحمام المشترك - حمام الرئيسية
ش1	شباك	160	140	80	1	الأمامية
ش1	شباك	140	140	80	3	الخلفية 2 - الغربية
ش2	شباك	120	90	115	1	الغربية
ش3	شباك	60	60	160	2	الشرقية - الخلفية

الإجمالي: أبواب 7 - شبابيك 7

المنظور ثلاثي الأبعاد والمواد

النمط: جوزي غامق + إطارات سوداء — رندر واقعي بخامات حقيقية

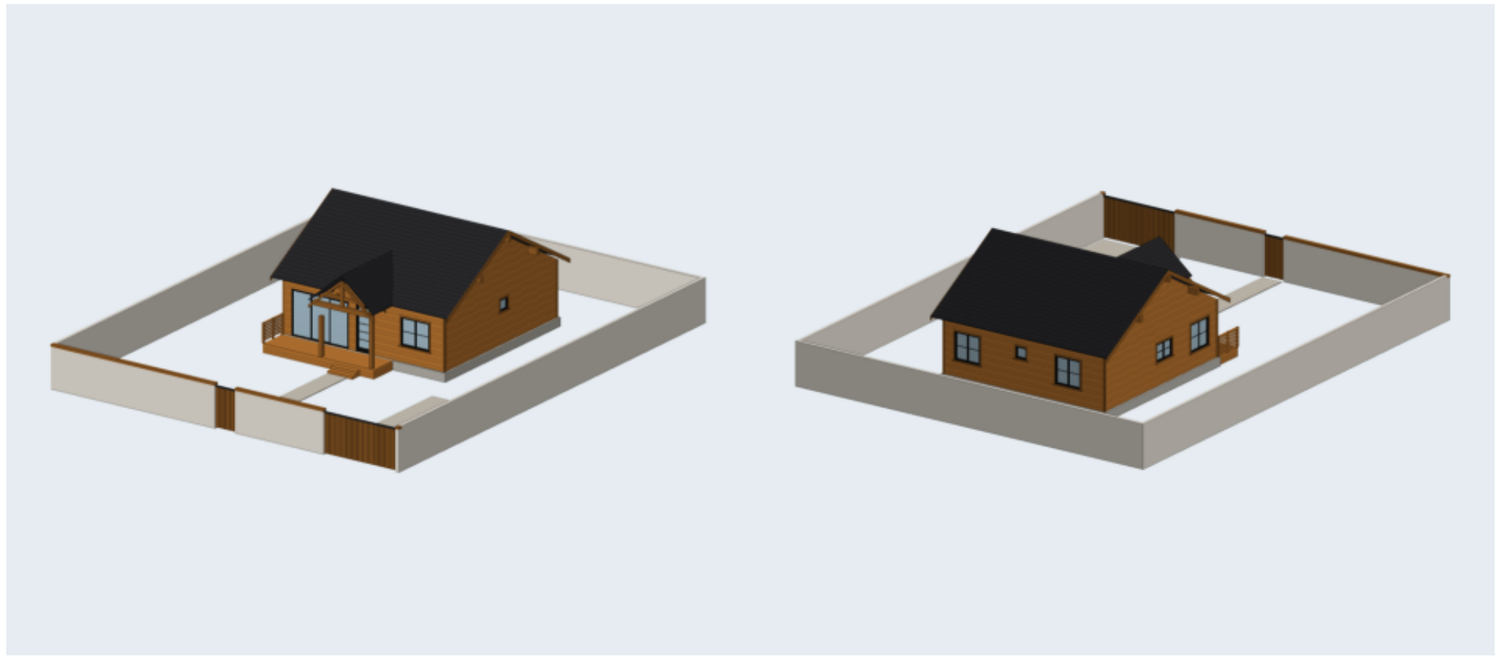

جدول المواد والألوان

الخشب / الصبغة

صبغة عسلي / سيدر

القرميد

قرميد رمادي غامق

الزجاج

زجاج شفاف

إطارات الشبابيك والأبواب

إطار ألمنيوم أسود

الكنار والزوايا

نفس الصبغة أغمق درجة


الصبة

خرسانة 45 سم


الدربزين: ألواح أفقية متقاربة (عصري)

تقسيم الشبابيك: شبكة | الباب الرئيسي: سحاب زجاج

أنواع الدربزين المعتمدة (من مشاريع المصنع)

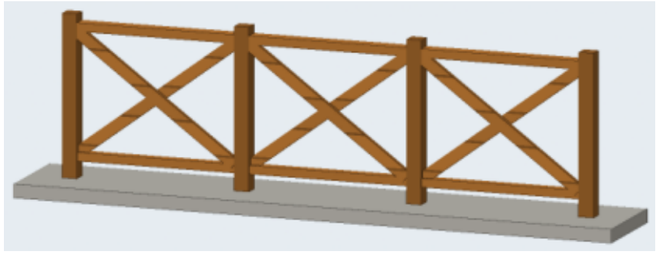

تقاطع X (صورة 5)

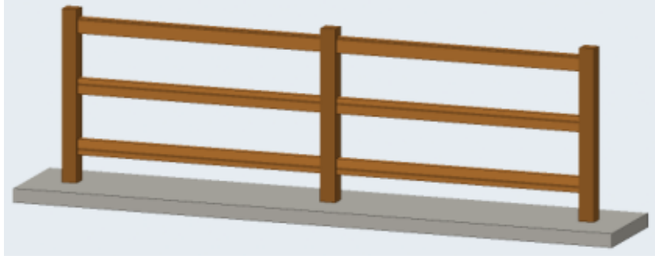

3 مرابيع أفقية (صورة 2)



قوائم رأسية متقاربة (صورة 1)

مصنع وتد الأخشاب Watad Wood Factory	المشروع / العميل كوخ خشب 9.00 × 9.00 م — ثلاث غرف وصالة واسعة ومطبخ سيرفس عميل — كوخ 9×9	عنوان اللوحة المنظور والمواد	المقياس —	التاريخ 2026-11-03	رقم اللوحة A-10 (10/10)

جدول المساحات وبيانات المشروع

بيانات المشروع

البند	البيان
المشروع	كوخ خشب 9.00 × 9.00 م — ثلاث غرف وصالة واسعة ومطبخ سيرفس
العميل	عميل — كوخ 9×9
الموقع	—
الاستخدام	سكن — ثلاث غرف
التاريخ	2026-11-03
نظام البناء	هيكل خشب 5×7 + تلبيس 2.5 سم من الجهتين
السقف	جملون 30° — قرميد معدني + 1 مثلث بارز

جدول المساحات

م	الفراغ	الأبعاد (م)	المساحة (م2)
1	الصالة والمطبخ	5.40 × 5.20	28.08
2	غرفة 3	3.24 × 3.88	12.57
3	حمام مشترك	3.24 × 1.20	3.89
4	غرفة 2	3.24 × 3.44	11.15
5	الغرفة الرئيسية	3.44 × 3.44	11.83
6	الممر	1.84 × 1.56	2.87
7	حمام الرئيسية	1.84 × 1.82	3.35
	المساحة الصافية الداخلية		**73.74**
	الدكة	**6.18 × 1.60**	**9.89**
	المساحة الإجمالية المبنية	**9.00 × 9.00**	**81.00**
	المساحة الكلية (المبنية + التراس)		**90.89**