
مصنع وتد الأخشاب · ملف التصميم

مجلس خشب منفصل 4.00 × 6.00 م


المبنى 6.00 × 6.00 م = 36 م² · جلسة U · مدخل بمغسلة ودورة مياه · جلسة أمامية مسقوفة

المسقط الأفقي مع الفرش

الأبعاد بالسنتيمتر - الجدران: قوائم 7×5 + تلبيس 2.5 من الجهتين (12 سم)

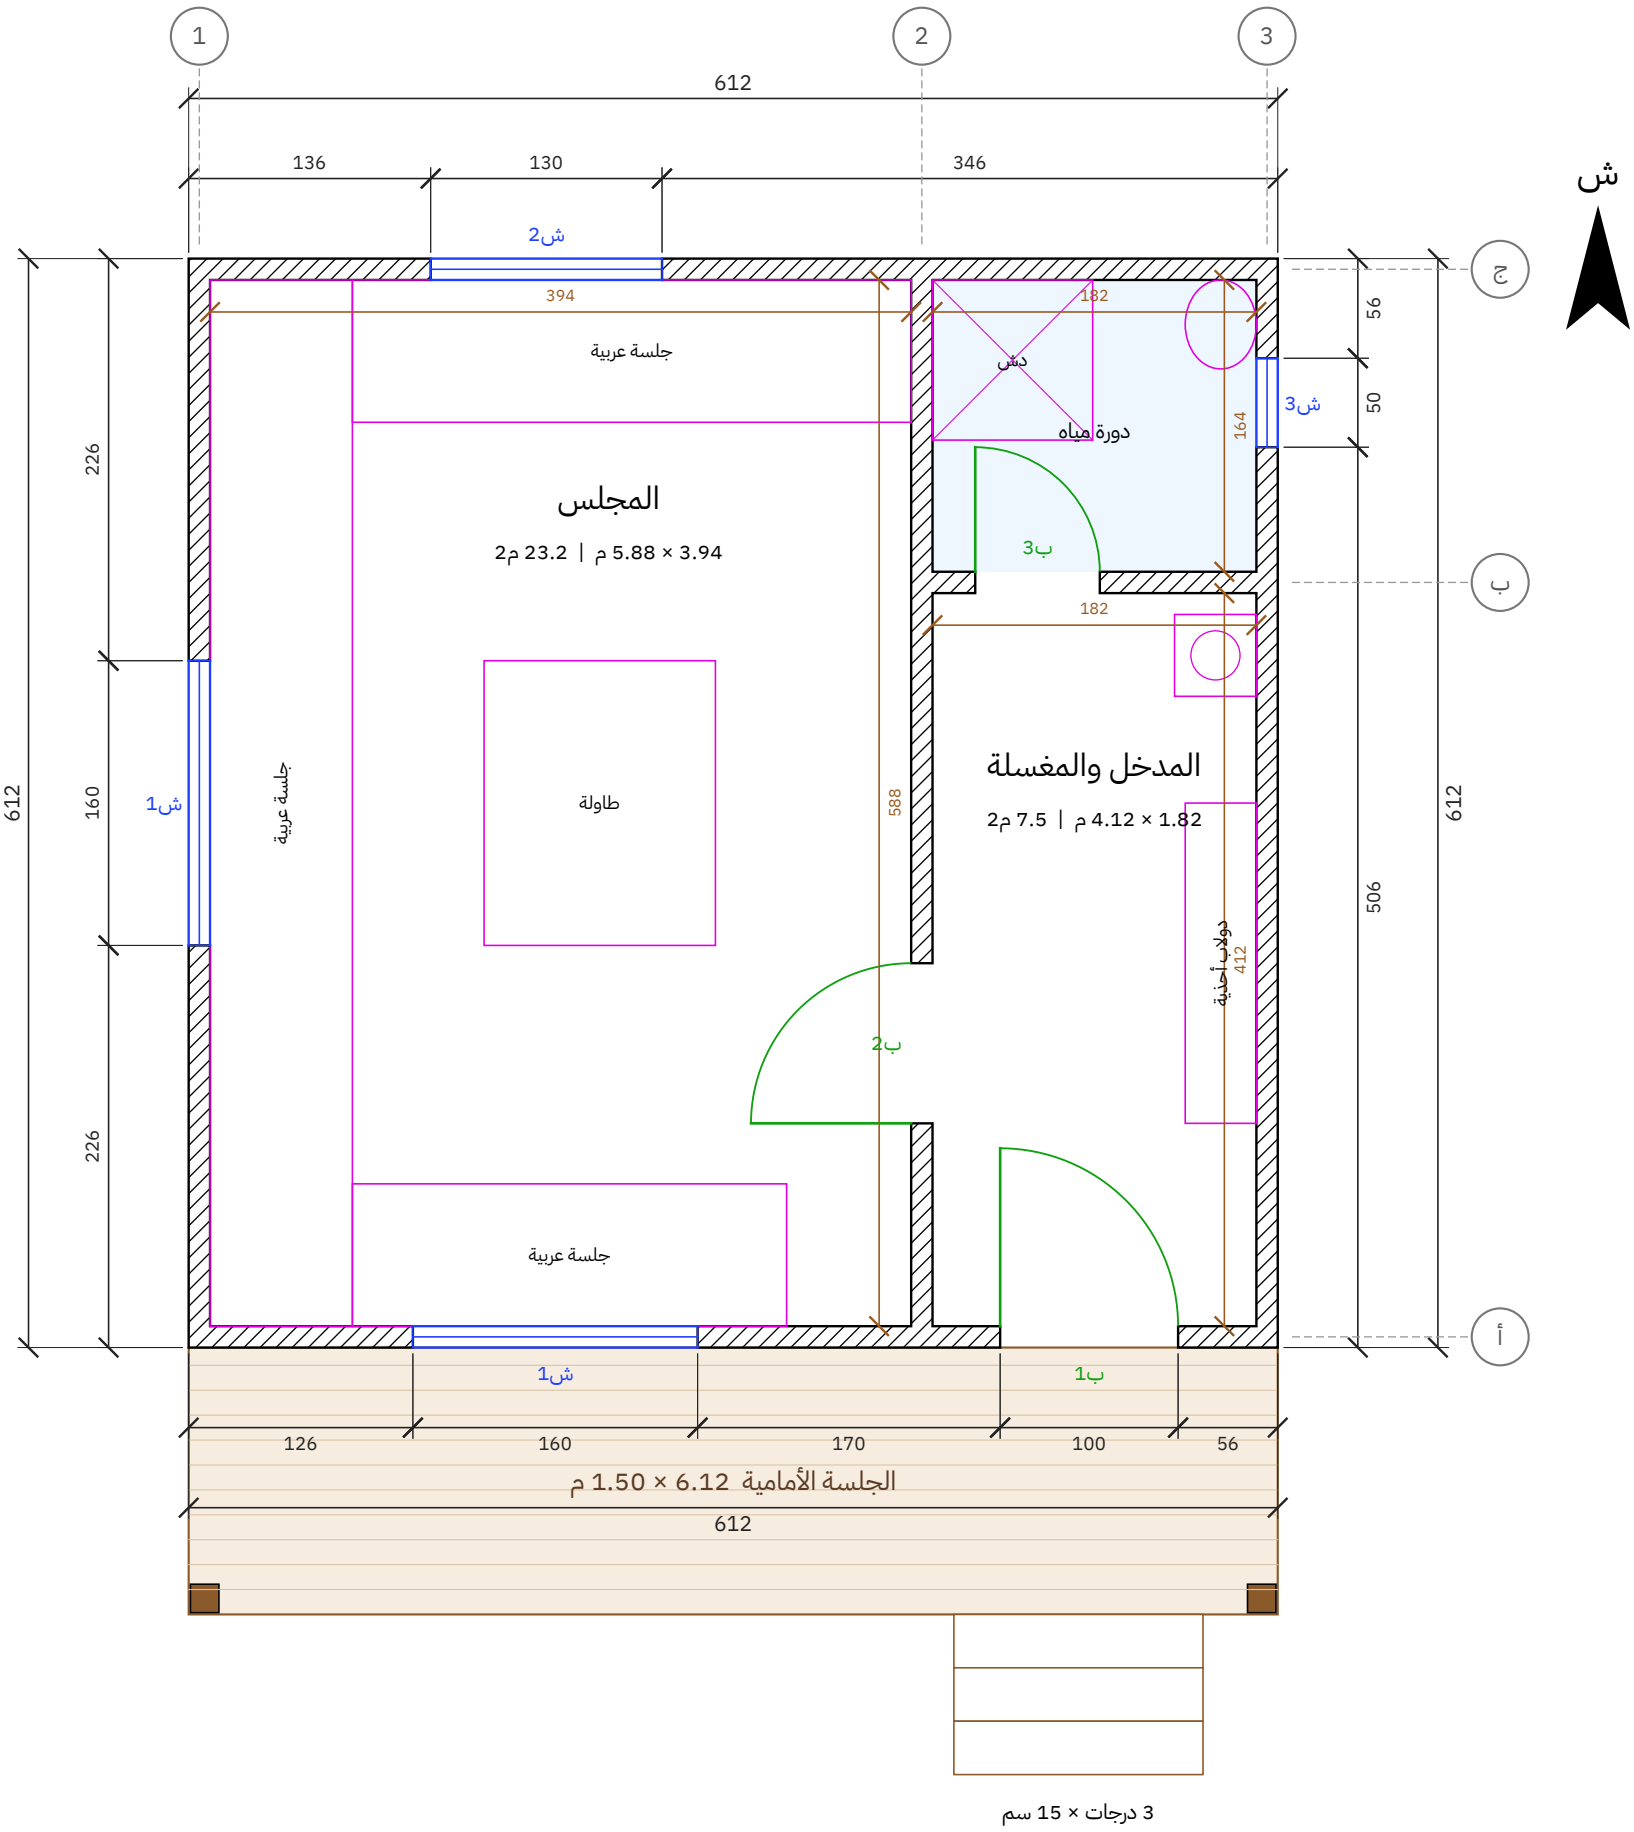


المشروع / العميل	عنوان اللوحة	المقياس	التاريخ	رقم اللوحة
مصنع وتد الأخشاب — Watad Wood Factory مجلس خشب منفصل 4.00 × 6.00 م بمدخل ودورة مياه — المبنى 6.00 × 6.00 م عميل — مجلس منفصل	المسقط الأفقي	1:50	2026-11-03	A-02 (2/10)

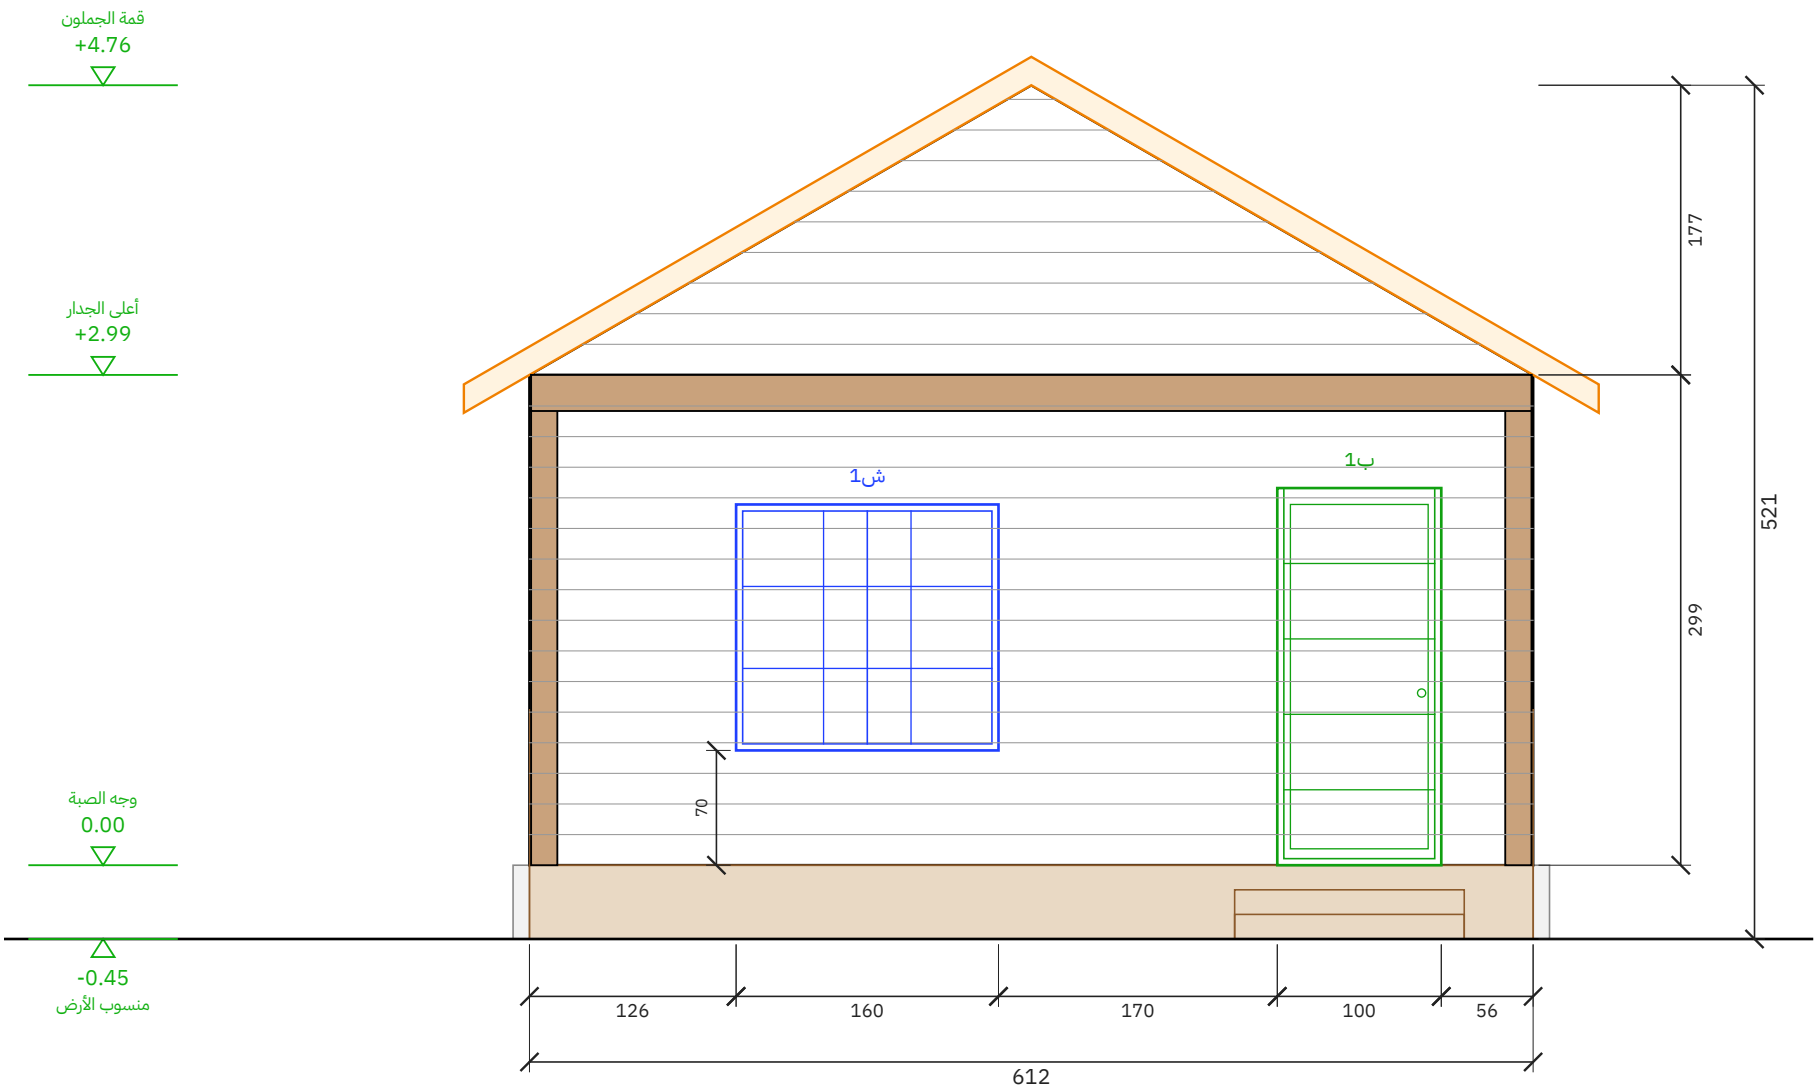

الواجهة الأمامية

مقياس 1:50 | الوحدة: سم

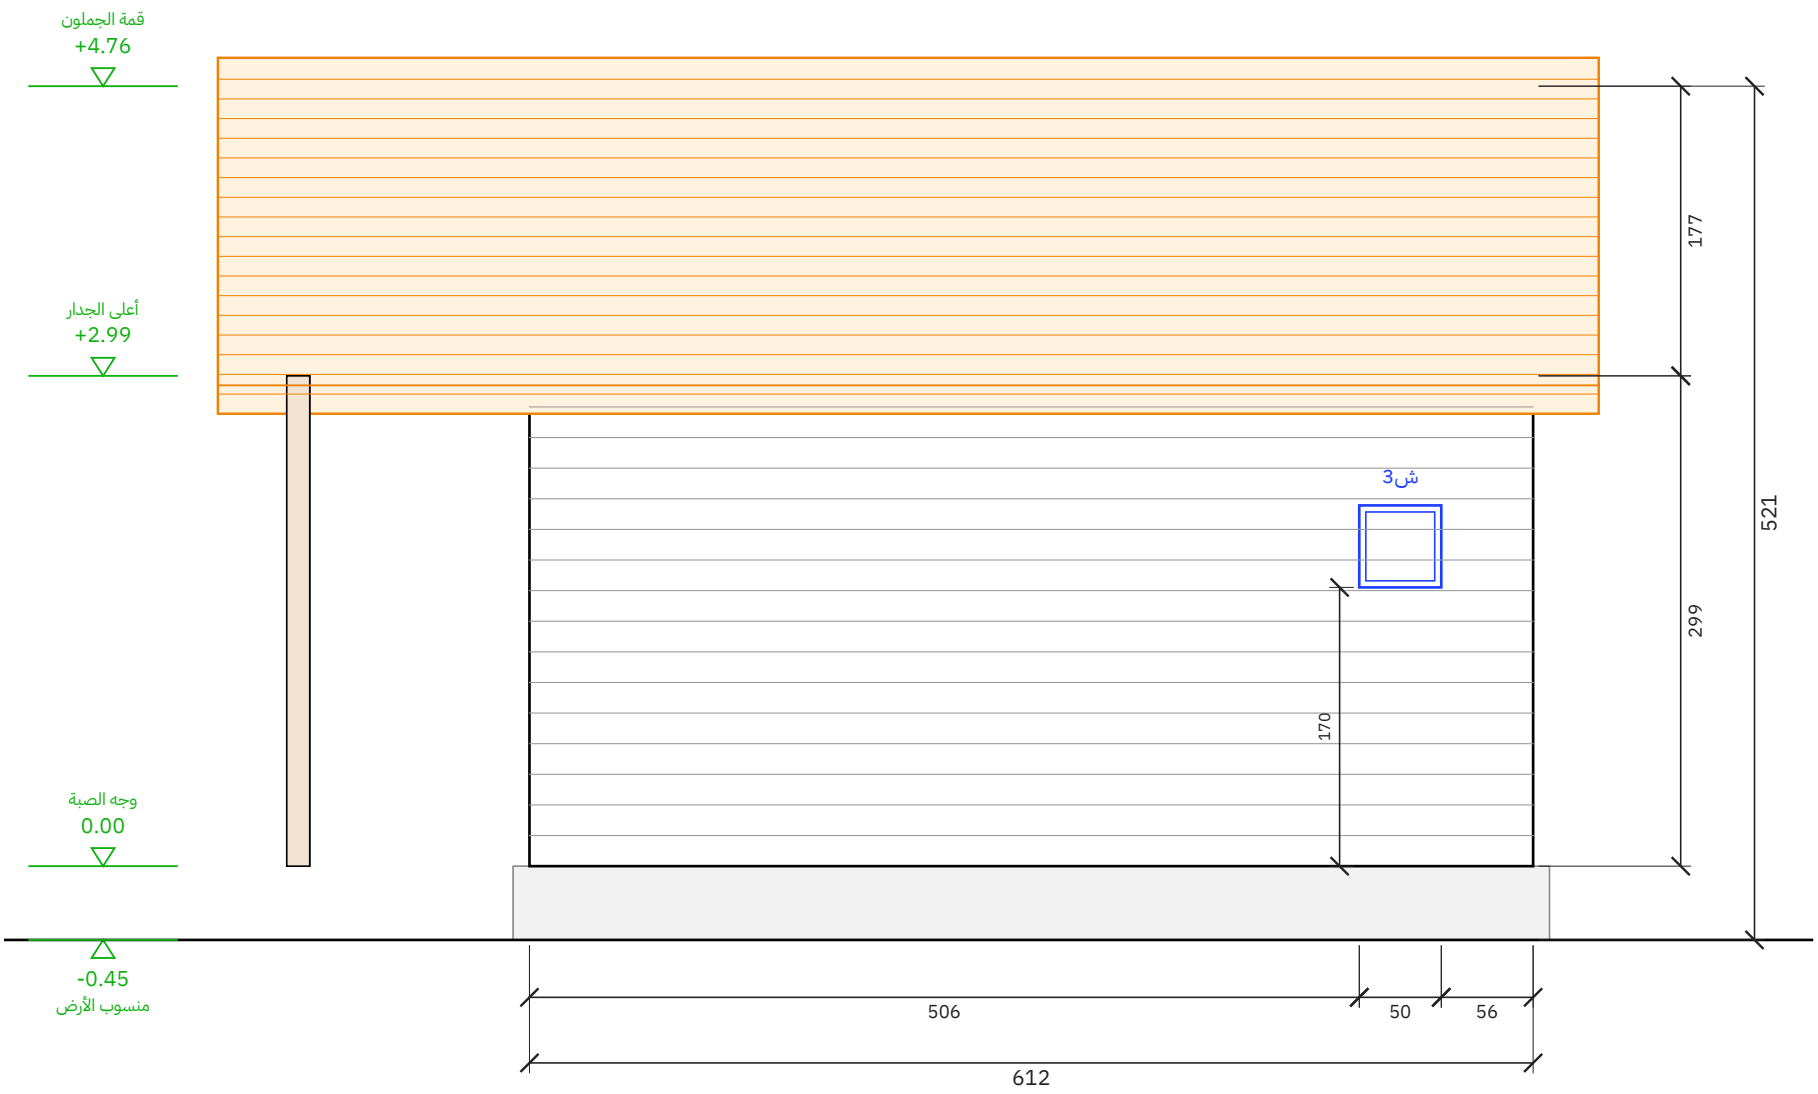


الواجهة الشرقية

مقياس 1:50 | الوحدة: سم


المشروع / العميل	عنوان اللوحة	المقياس	التاريخ	رقم اللوحة
مجلس خشب منفصل 4.00 × 6.00 م بمدخل ودورة مياه — المبنى 6.00 × 6.00 م عميل — مجلس منفصل	الواجهة الأمامية والواجهة الشرقية	1:50	2026-11-03	A-03 (3/10)

مصنع وتد الأخشاب
Watad Wood Factory

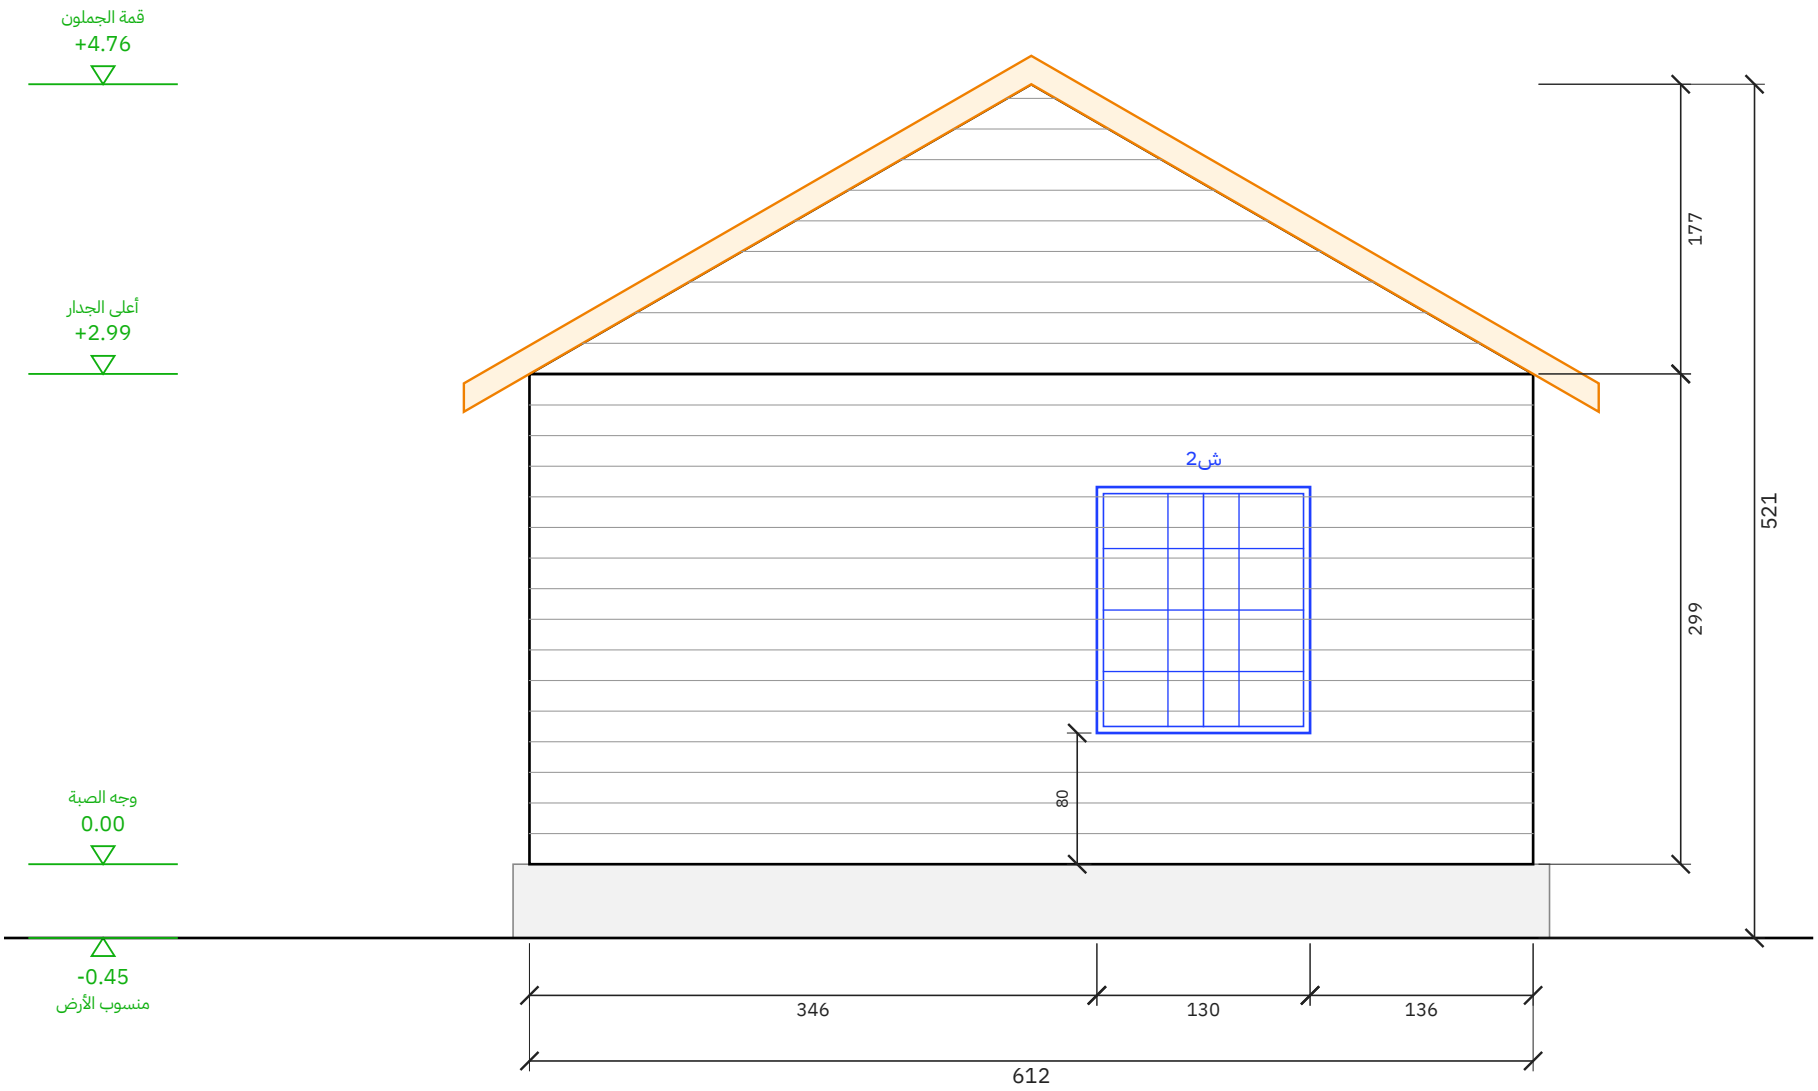

الواجهة الخلفية

مقياس 1:50 | الوحدة: سم

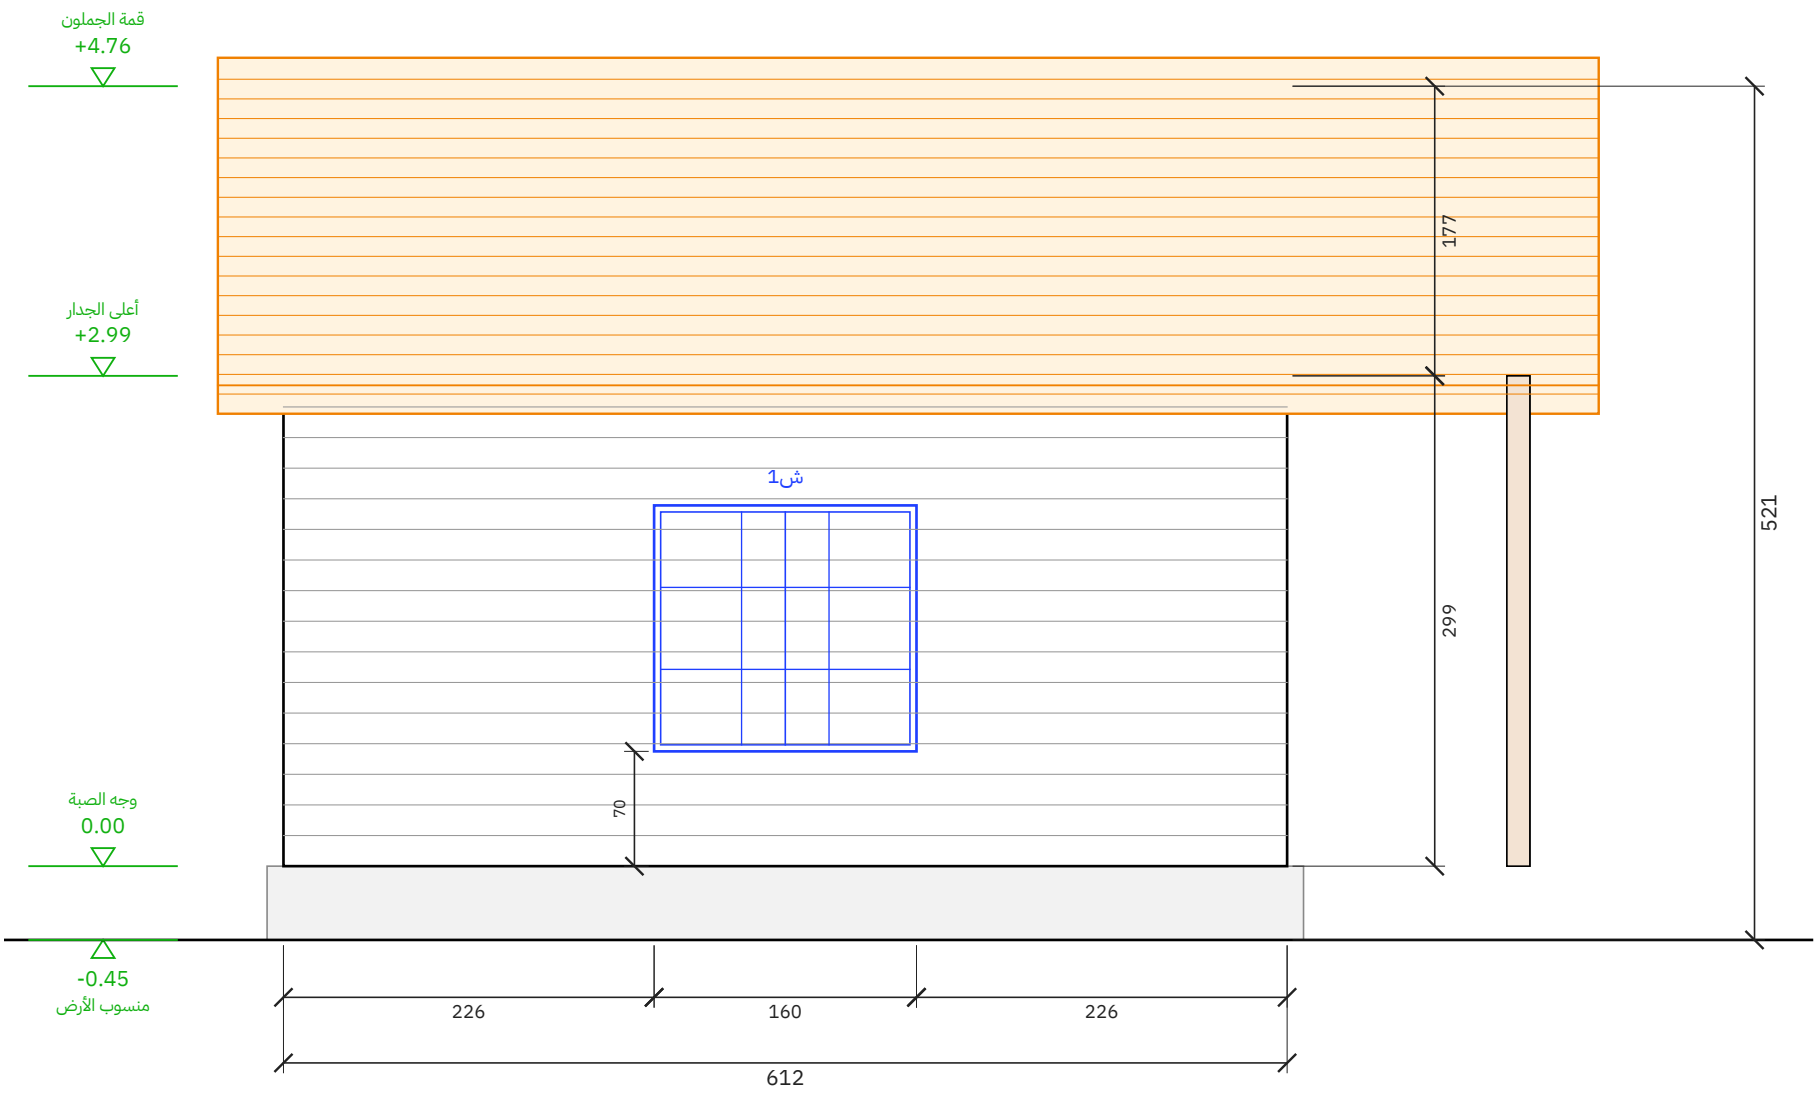

الواجهة الغربية


مقياس 1:50 | الوحدة: سم

المشروع / العميل	عنوان اللوحة	المقياس	التاريخ	رقم اللوحة
مجلس خشب منفصل 4.00 × 6.00 م بمدخل ودورة مياه — المبنى 6.00 × 6.00 م عميل — مجلس منفصل	الواجهة الخلفية والواجهة الغربية	1:50	2026-11-03	A-04 (4/10)

مصنع وتد الأخشاب
Watad Wood Factory


مسقط السقف (جملون)

رفرف 40 سم من كل جهة | مقياس 1:50

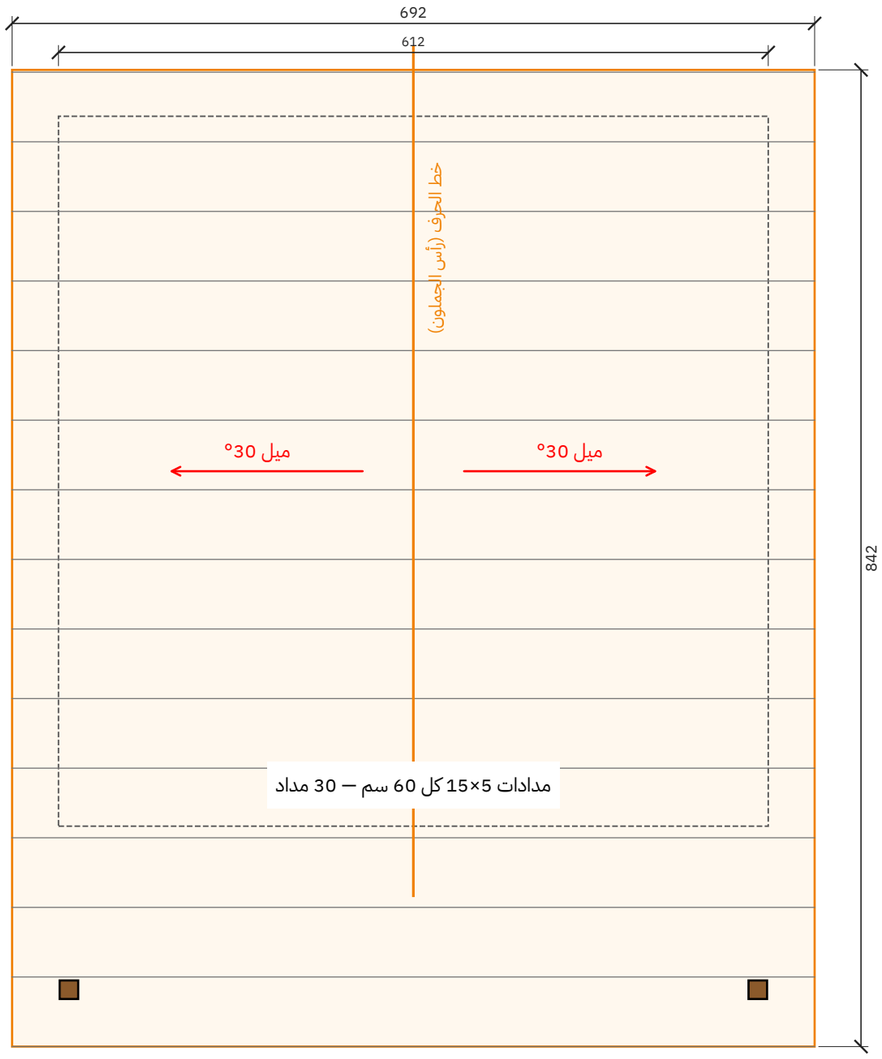


قطاع عرضي أ-أ

مقياس 1:50 | الوحدة: سم

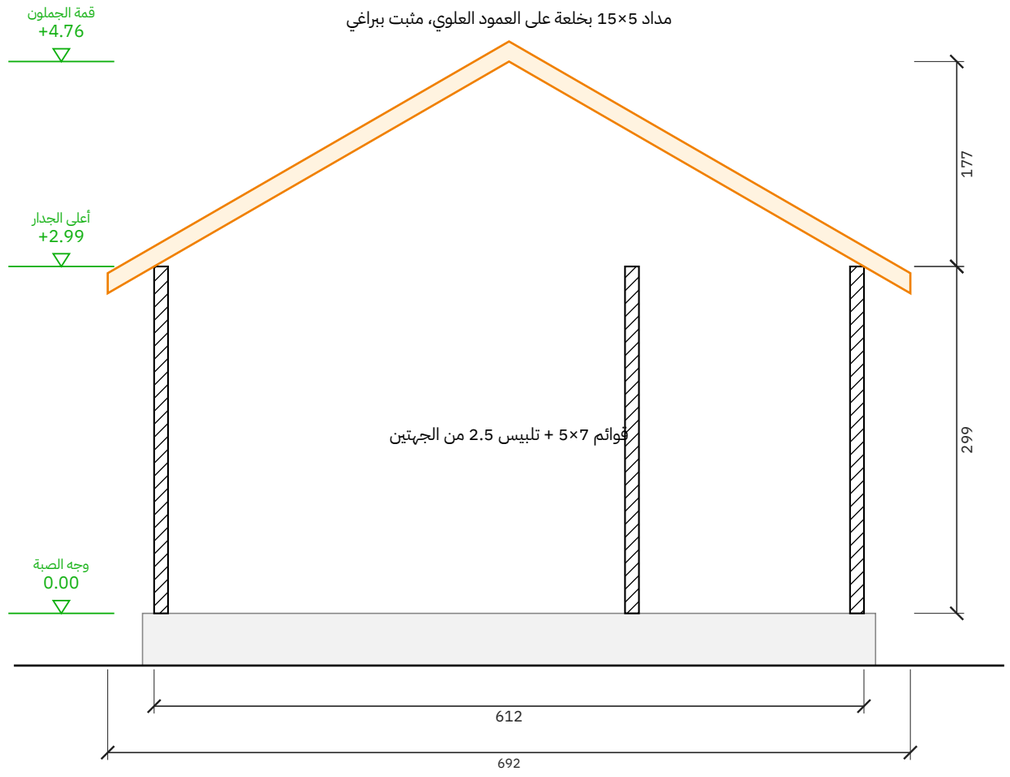

تفصيلة جلوس المداد على العلوي (1:5)

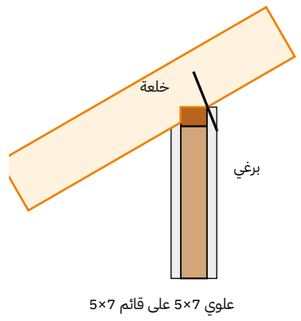


مصنع وتد الأخشاب Watad Wood Factory	المشروع / العميل مجلس خشب منفصل 4.00 × 6.00 م بمدخل ودورة مياه — المبنى 6.00 × 6.00 م عميل — مجلس منفصل	عنوان اللوحة مسقط السقف والقطاع	المقياس 1:50	التاريخ 2026-11-03	رقم اللوحة A-05 (5/10)

لقطات المنظور الخارجي


المنظور الأمامي




منظور أمامي من اليسار

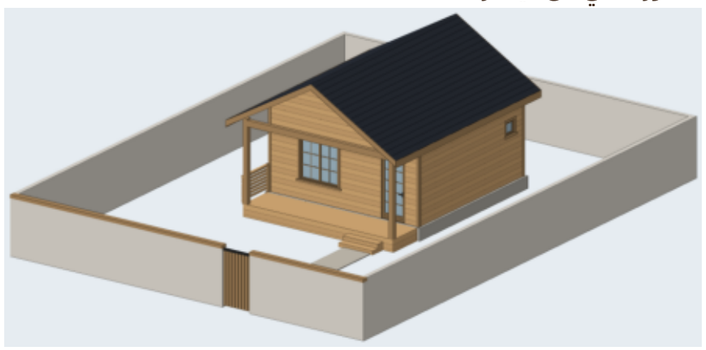


منظور أمامي من اليمين

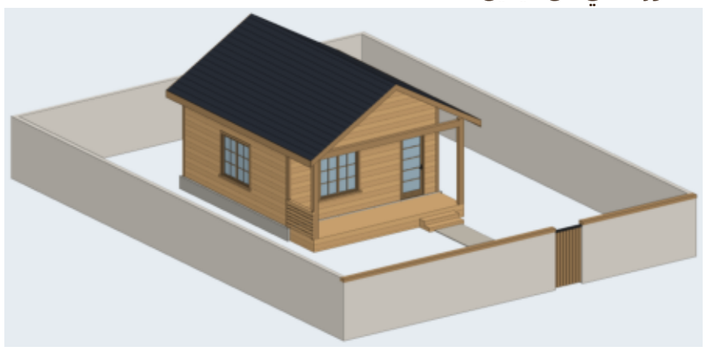


المنظور الخلفي

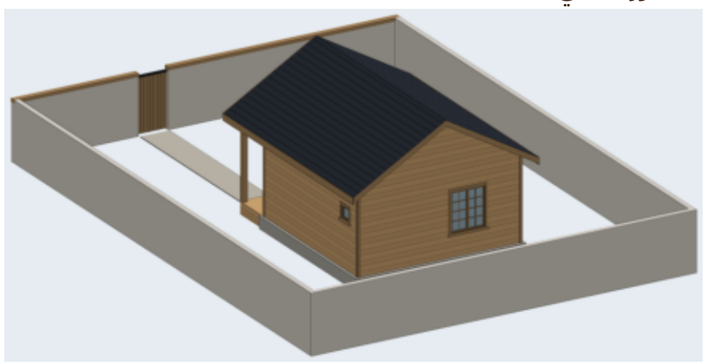

منظور خلفي من اليمين

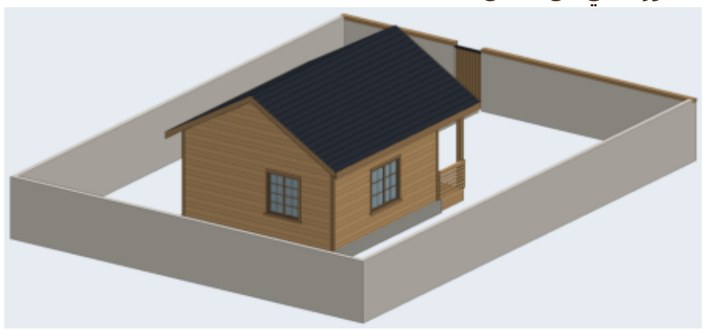

منظر علوي

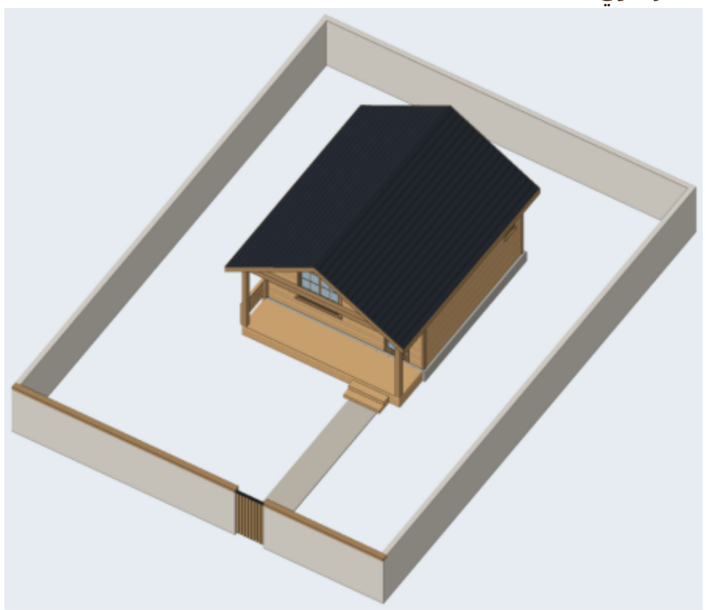


المشروع / العميل	عنوان اللوحة	المقياس	التاريخ	رقم اللوحة
مجلس خشب منفصل 4.00 × 6.00 م بمدخل ودورة مياه — المبنى 6.00 × 6.00 م **عميل — مجلس منفصل**	**لقطات المنظور**	—	**2026-11-03**	**A-08 (8/10)**

مصنع وتد الأخشاب
Watad Wood Factory

المقطع العلوي بالفرش

مقطع أفقي على ارتفاع 1.90 م — توزيع الفرش ومسار الحركة

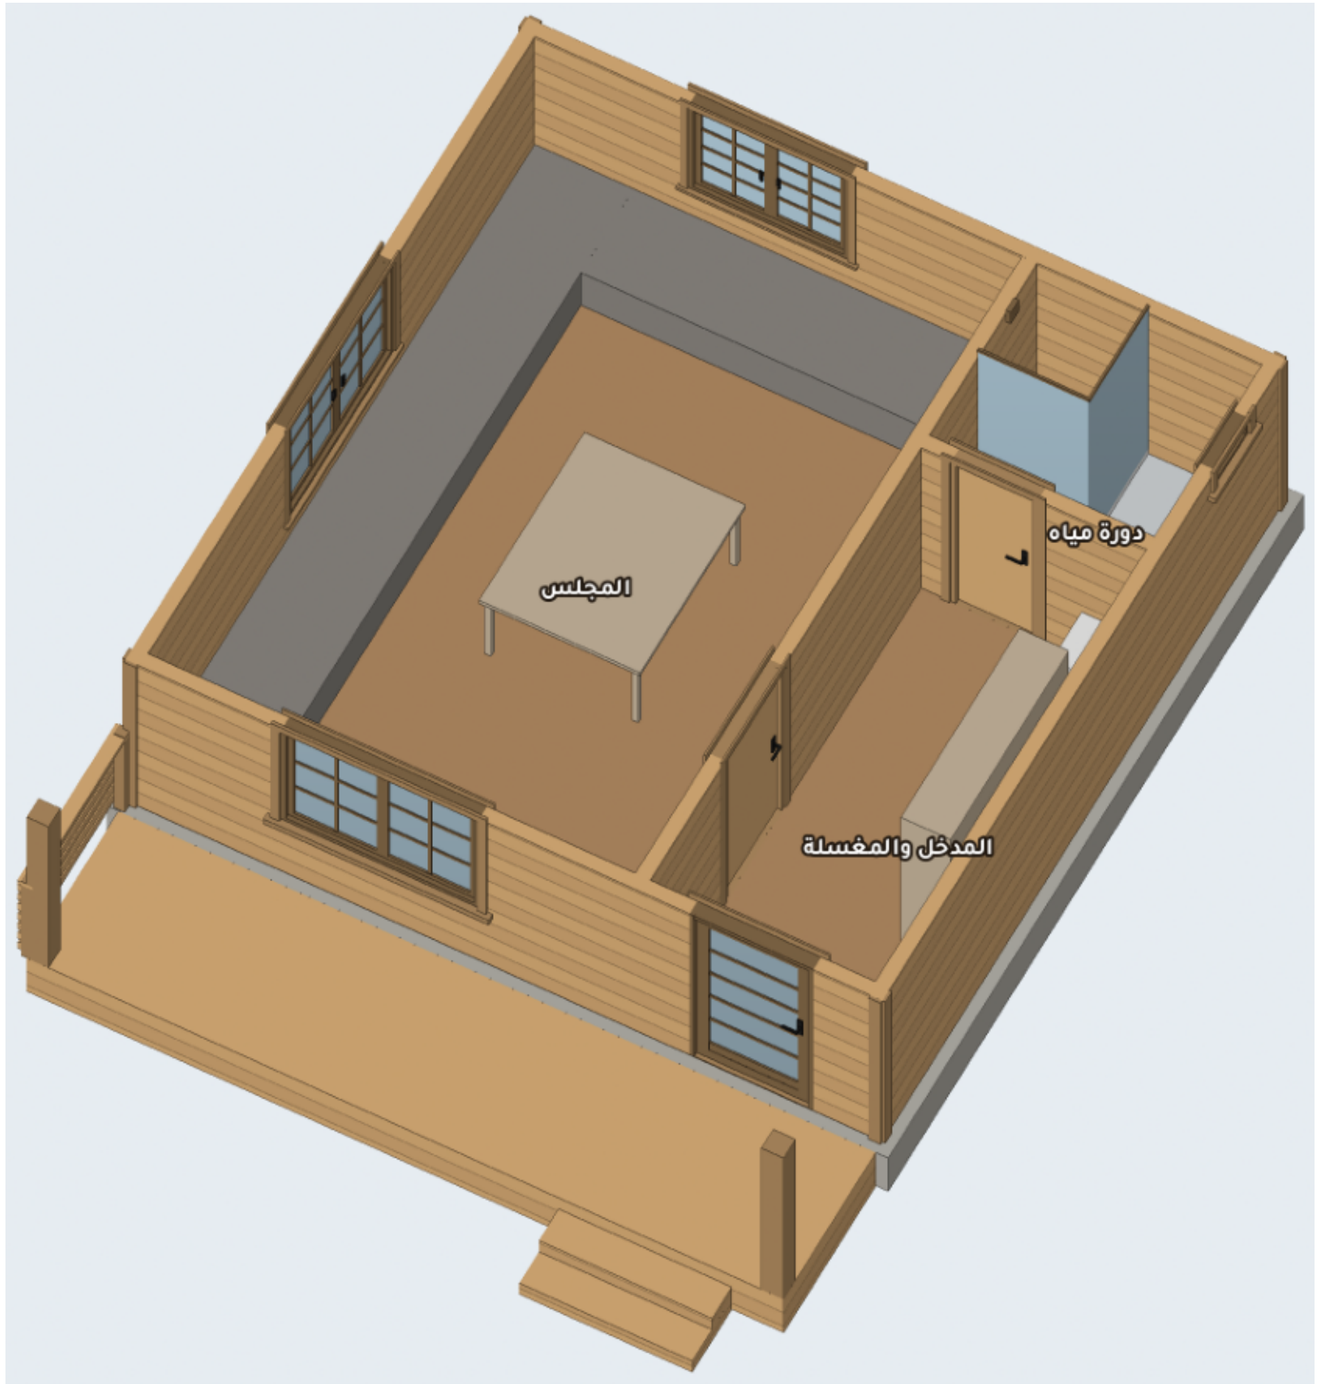

مصنع وتد الأخشاب Watad Wood Factory	المشروع / العميل مجلس خشب منفصل 4.00 × 6.00 م بمدخل ودورة مياه — المبنى 6.00 × 6.00 م عميل — مجلس منفصل	عنوان اللوحة المقطع العلوي بالفرش	المقياس —	التاريخ 2026-11-03	رقم اللوحة A-09 (9/10)



مصنع وتد الأخشاب

أمامي – المدخل · الخارج – نهاراً



مصنع وتد الأخشاب



مصنع وتد الأخشاب

منظر علوي – الأرض والسور · الخارج – نهاراً



مصنع وتد الأخشاب



مصنع وتد الأخشاب




مصنع وتد الأخشاب

جدول مساحات الموقع

البند	المقاس	المساحة (م²)
مساحة الأرض	14.00 × 19.00 م	266.0
مسطح الكوخ (البصمة)	6.12 × 6.12 م	37.5
تراس الكوخ	6.12 × 1.50 م	9.2
ممر	1.10 × 7.34 م	8.1
المسطحات الخضراء (حديقة)	الباقي	211.3

الموقع العام وتنسيق الحديقة (لاندسكيب)

الأرض 14 × 19 م = 266 م² | الأبعاد بالسنتيمتر

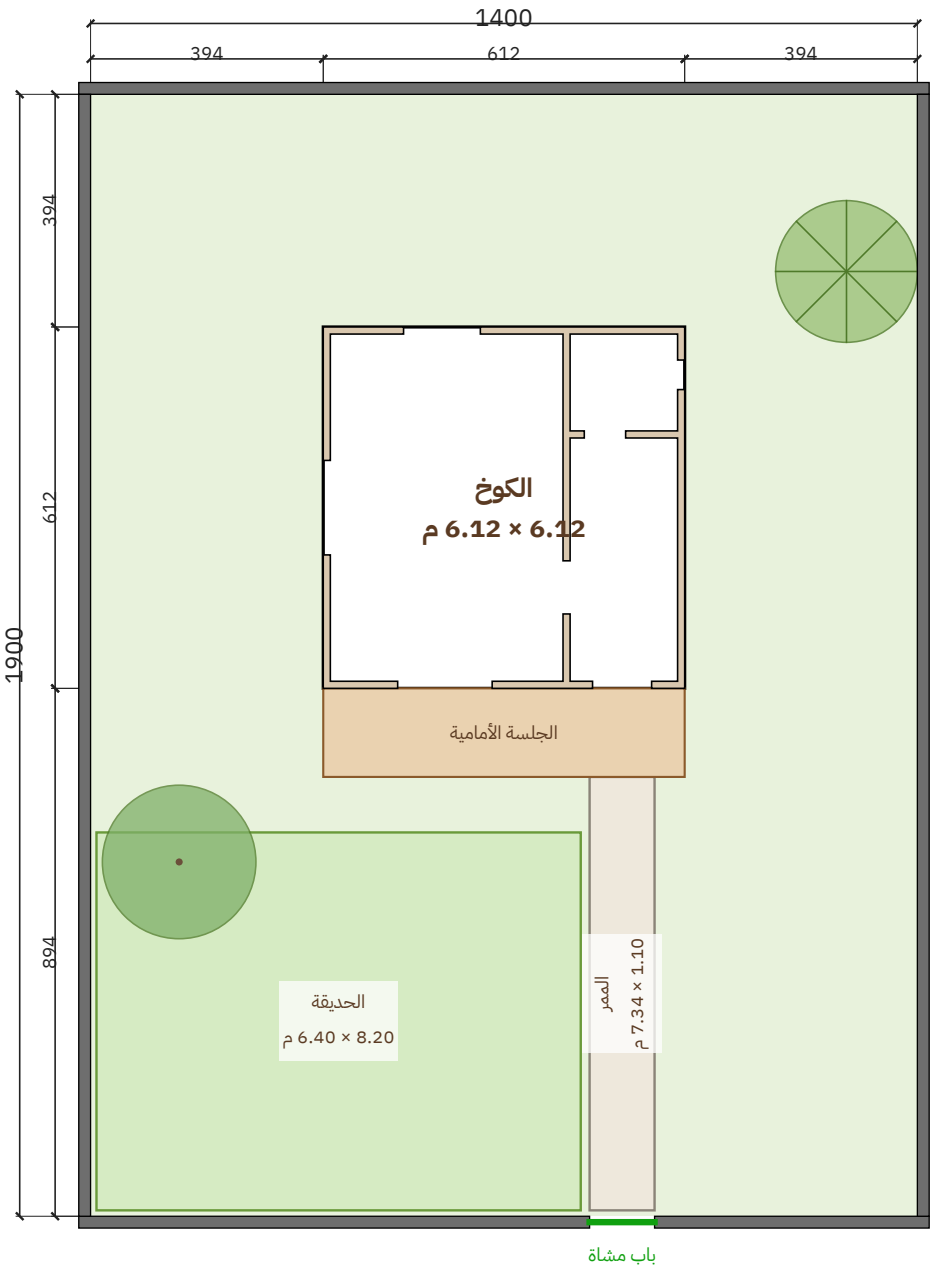

المشروع / العميل	عنوان اللوحة	المقياس	التاريخ	رقم اللوحة
مجلس خشب منفصل 4.00 × 6.00 م بمدخل ودورة مياه — المبنى 6.00 × 6.00 م عميل — مجلس منفصل	الموقع العام واللاندسكيب	1:200	2026-11-03	A-01 (1/10)

مصنع وتد الأخشاب
Watad Wood Factory

جدول مقاسات الأبواب والشبابيك


مقاس الفتحة الصافي في الجدار - الوحدة: سم

الرمز	النوع	العرض (سم)	الارتفاع (سم)	ارتفاع الجلسة (سم)	العدد	الموقع
ب1	باب	100	230	-	1	الأمامية
ب2	باب	90	220	-	1	المدخل — المجلس
ب3	باب	70	210	-	1	دورة المياه
ش1	شباك	160	150	70	2	الأمامية - الغربية
ش2	شباك	130	150	80	1	الخلفية
ش3	شباك	50	50	170	1	الشرقية

الإجمالي: أبواب 3 - شبابيك 4

المنظور ثلاثي الأبعاد والمواد

النمط: خشب طبيعي + قرميد فحمي — رندر واقعي بخامات حقيقية

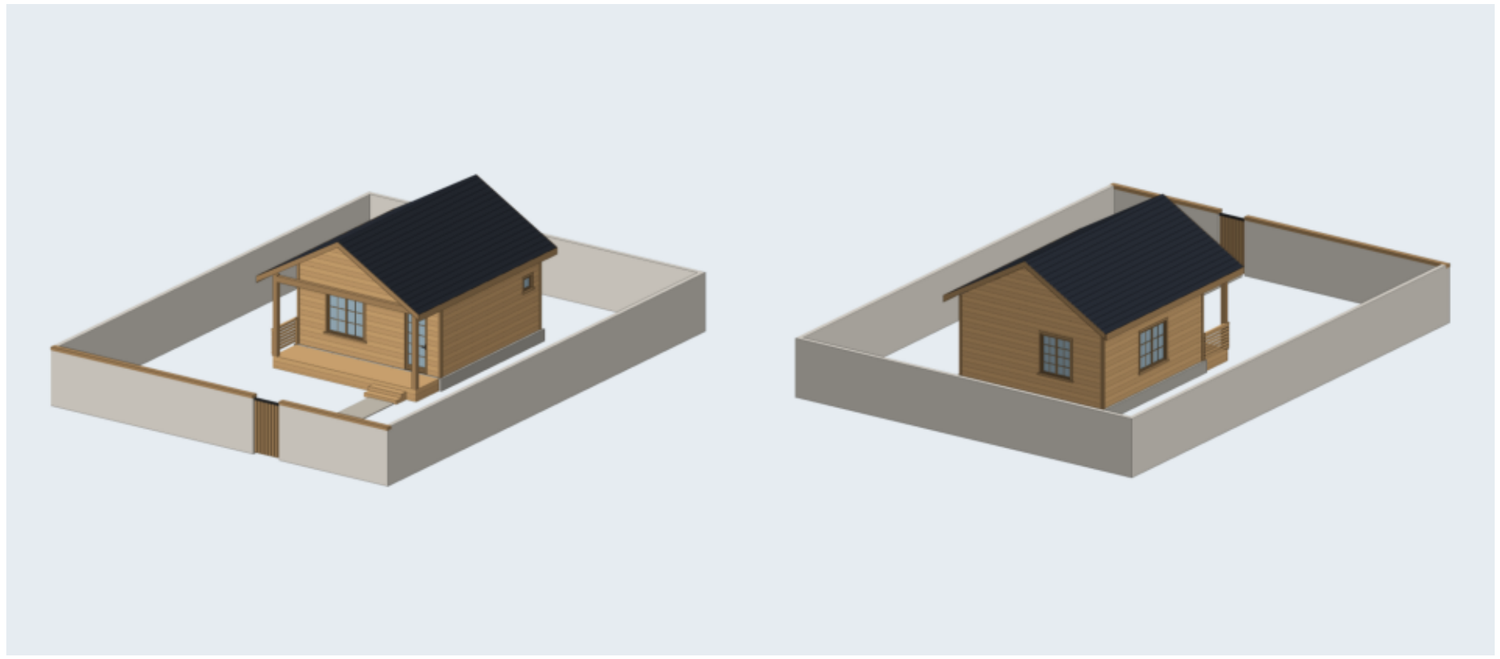

جدول المواد والألوان

الخشب / الصبغة

خشب طبيعي فاتح (بدون صبغة)

القرميد

قرميد فحمي / أسود مزرق

الزجاج

زجاج شفاف

إطارات الشبابيك والأبواب

إطار خشب بنفس الصبغة أغمق

الكنار والزوايا

نفس الصبغة أغمق درجة


الصبة

خرسانة 45 سم


الدربزين: ألواح أفقية متقاربة (عصري)

تقسيم الشبابيك: شبكة | الباب الرئيسي: زجاج بتقسيمات (فرنسي)

أنواع الدربزين المعتمدة (من مشاريع المصنع)

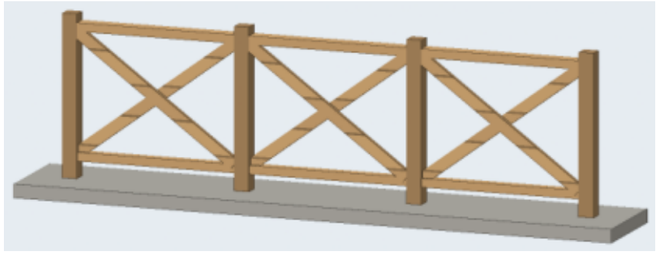

تقاطع X (صورة 5)

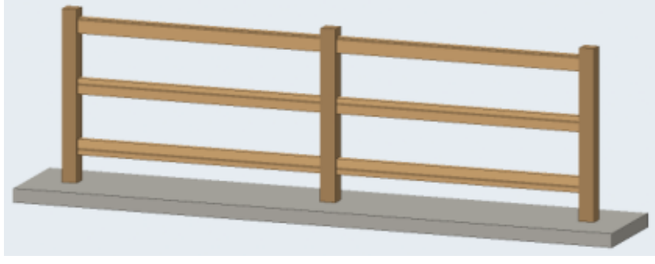

3 مرابيع أفقية (صورة 2)



قوائم رأسية متقاربة (صورة 1)

المشروع / العميل	عنوان اللوحة	المقياس	التاريخ	رقم اللوحة
مجلس خشب منفصل 4.00 × 6.00 م بمدخل ودورة مياه — المبنى 6.00 × 6.00 م **عميل — مجلس منفصل**	**المنظور والمواد**	—	**2026-11-03**	**A-10 (10/10)**

مصنع وتد الأخشاب
Watad Wood Factory

جدول المساحات وبيانات المشروع

بيانات المشروع

البند	البيان
المشروع	مجلس خشب منفصل 4.00 × 6.00 م بمدخل ودورة مياه — المبنى 6.00 × 6.00 م
العميل	عميل — مجلس منفصل
الموقع	—
الاستخدام	مجلس ضيافة
التاريخ	2026-11-03
نظام البناء	هيكل خشب 5×7 + تلبيس 2.5 سم من الجهتين
السقف	جملون 30° — قرميد معدني

جدول المساحات

م	الفراغ	الأبعاد (م)	المساحة (م2)
1	المجلس	3.94 × 5.88	23.17
2	المدخل والمغسلة	1.82 × 4.12	7.50
3	دورة مياه	1.82 × 1.64	2.98
	المساحة الصافية الداخلية		**33.65**
	الجلسة الأمامية	**6.12 × 1.50**	**9.18**
	المساحة الإجمالية المبنية	**6.12 × 6.12**	**37.45**
	المساحة الكلية (المبنية + التراس)		**46.63**