



المسقط الأفقي ومسقط السقف  
مقياس 1:50 | الوحدة: سم

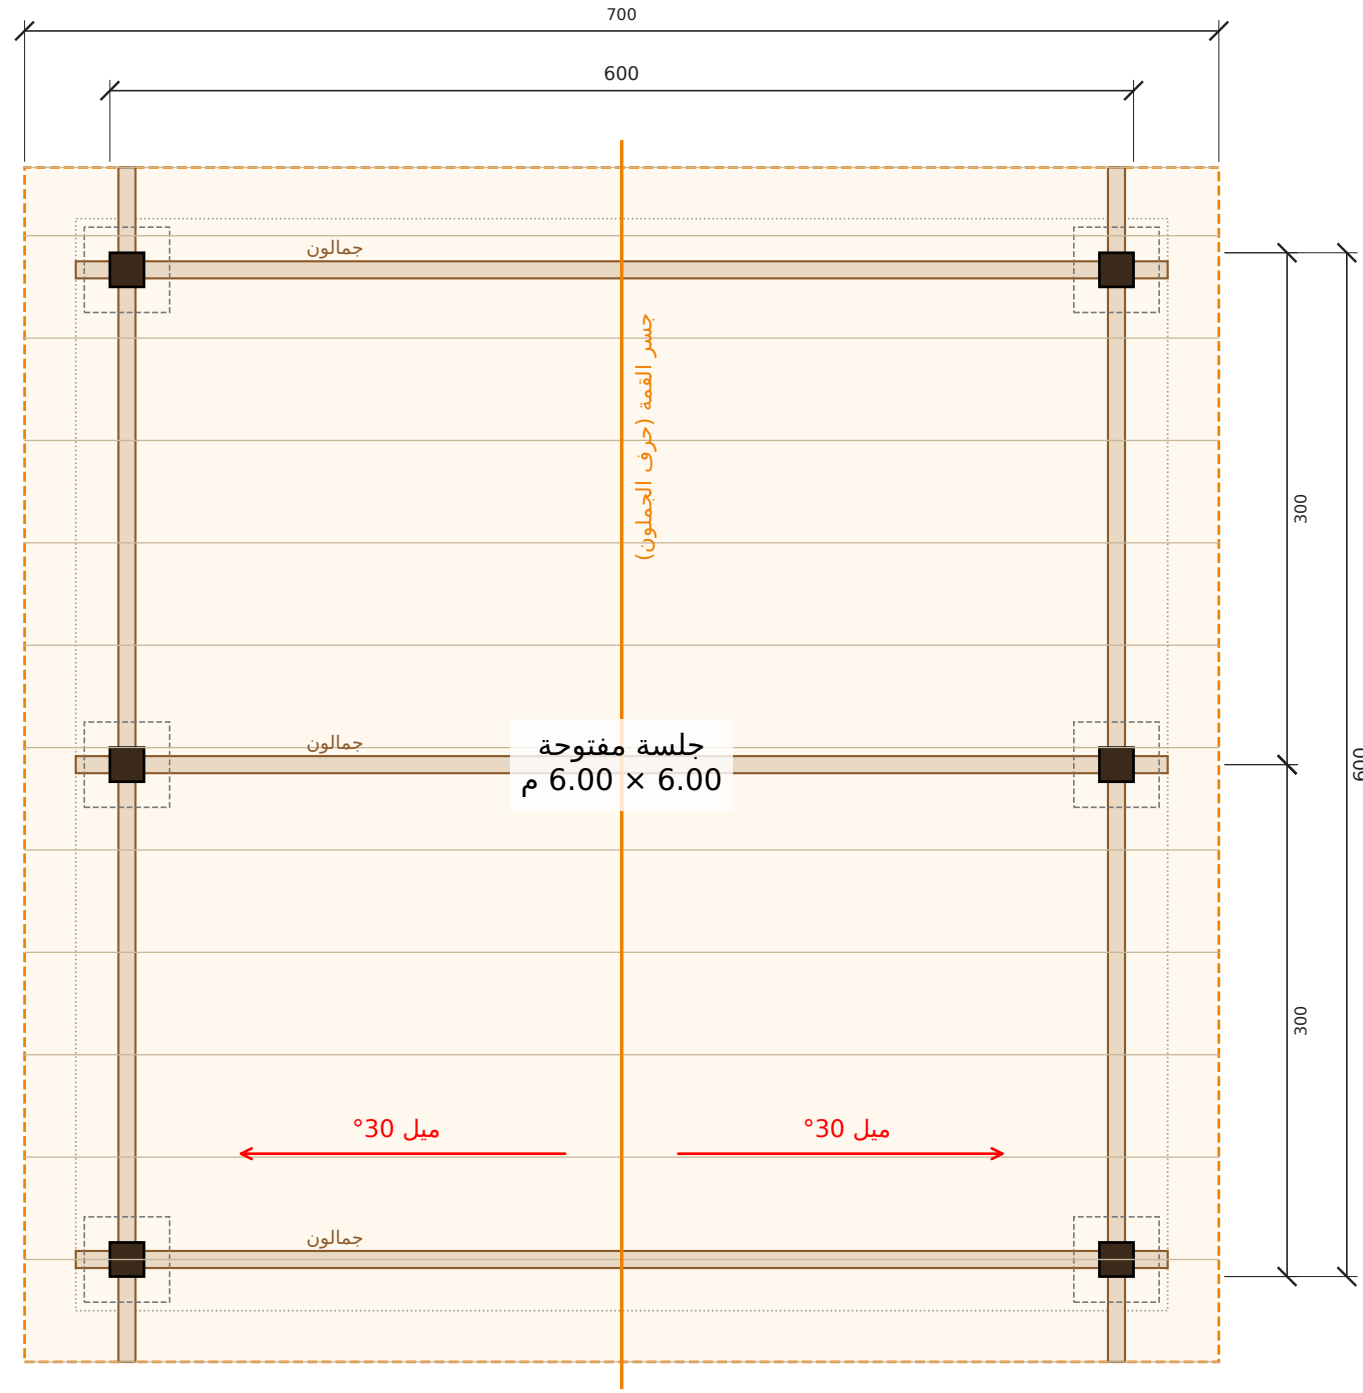

الواجهة الأمامية (الجملون)

■ عمود 20×20 على قاعدة حديد ومسمار تثبيت في قاعدة خرسانة 50×50 (المتقطع) ■ الرفرف المتقطع = حدود السقف

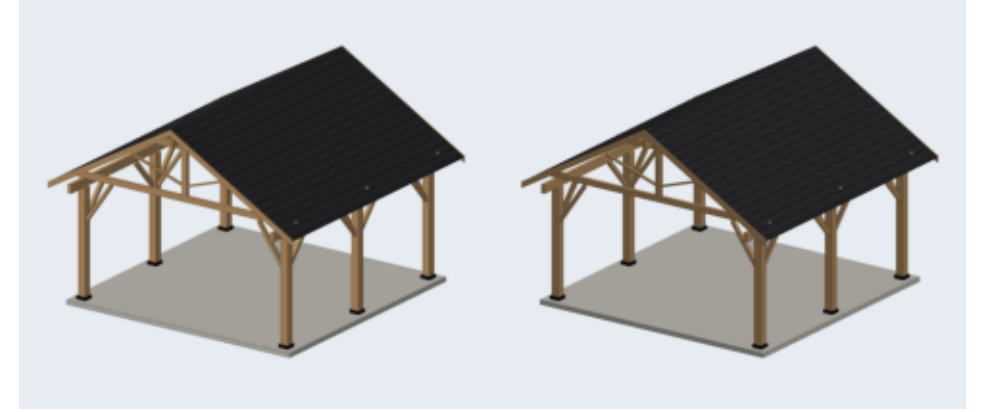

رقم اللوحة

A-01 (1/6)

التاريخ

2026-10-07

المقياس

1:50

عنوان اللوحة

المسقط ومسقط السقف

المشروع / العميل



برجولة خشب 6×6 بجمالونات مكشوفة  
عميل — برجولة

مصنع وتد الأخشاب  
Watad Wood Factory



الواجهة الأمامية — جمالون مكشوف  
مقياس 1:50

الواجهة الجانبية  
مقياس 1:50

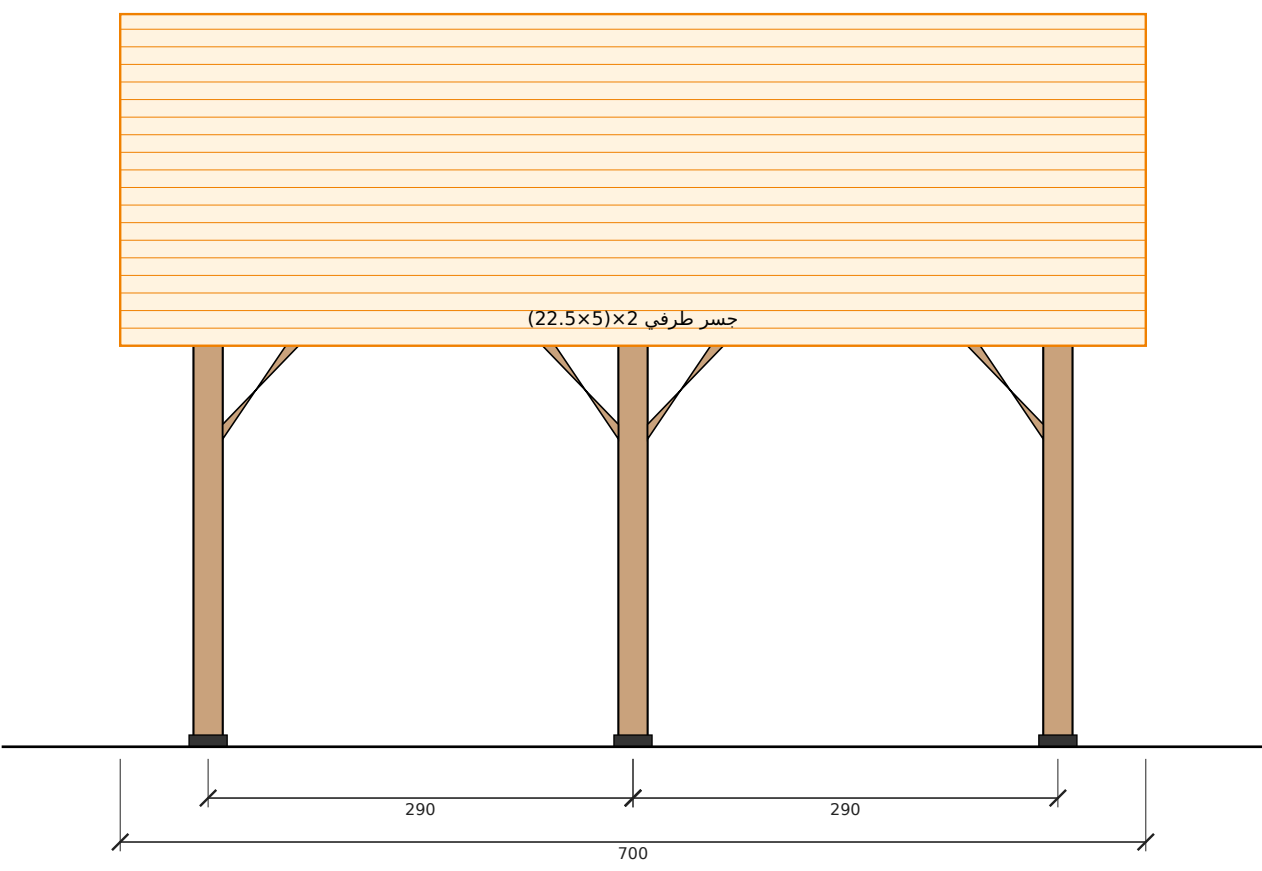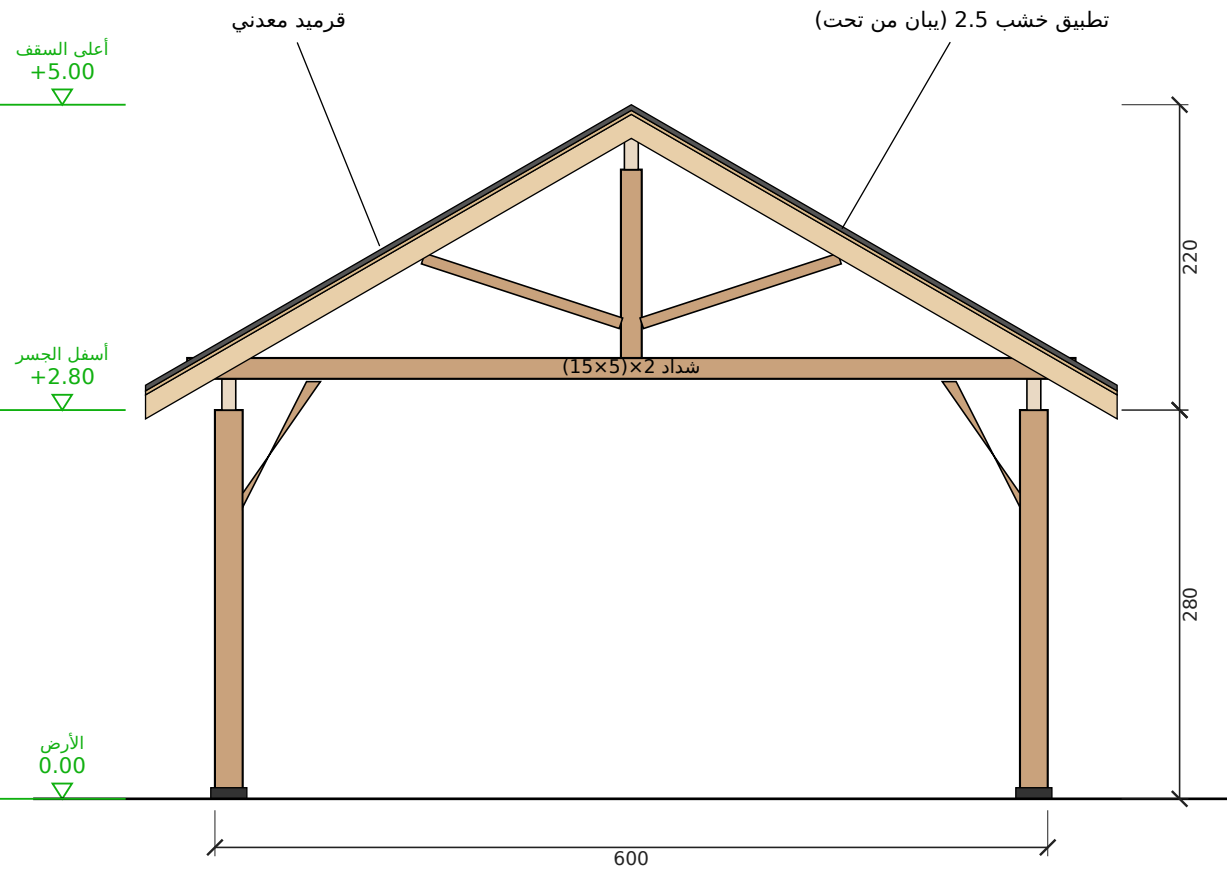

رقم اللوحة

التاريخ

المقياس

عنوان اللوحة

المشروع / العميل

A-02 (2/6)

2026-10-07

1:50


الواجهات

برجولة خشب 6x6 بجمالونات مكشوفة  
عميل — برجولة


مصنع وتد الأخشاب  
Watad Wood Factory



قطاع الجمالون (كل جمالون)

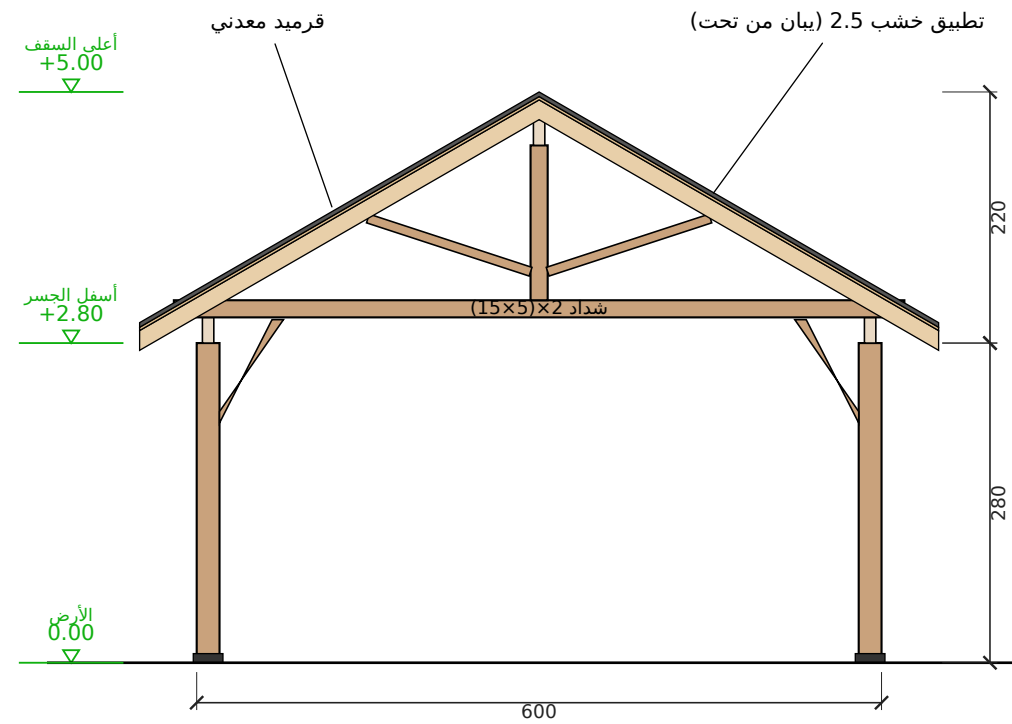

تفصيلة قاعدة العمود  
مقياس 1:10

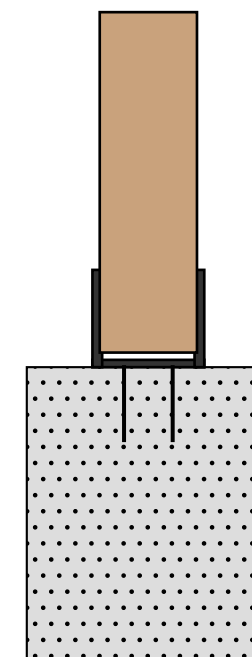


عمود 20×20 (4 طبقات 5 سم مبرغية)

قاعدة حديد U مجلفنة + برغرين M12  
ترفع الخشب 3 سم عن الأرض (ما يلمس المويه)

قاعدة خرسانة 60×50×50 + مسامير تثبيت

تفصيلة السقف – طبقتين فقط  
مقياس 1:5

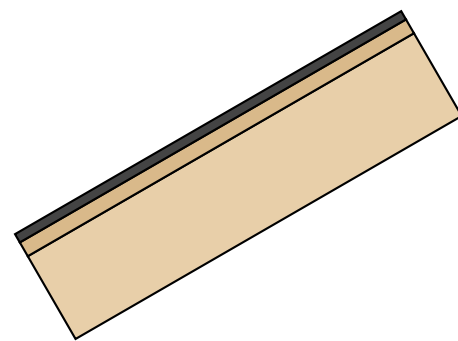

(2) قرميد معدني مثبت ببراعي على التطبيق  
(1) تطبيق خشب لسان ونقر 2.5 سم (السقف الداخلي)

مداد 15×5 كل 60 سم

|                                            |                                         |                                         |                                                      |                                                                                                |   |
|--------------------------------------------|-----------------------------------------|-----------------------------------------|------------------------------------------------------|------------------------------------------------------------------------------------------------|---|
| <p>رقم اللوحة</p> <p><b>A-03 (3/6)</b></p> | <p>التاريخ</p> <p><b>2026-10-07</b></p> | <p>المقياس</p> <p><b>1:50 / 1:5</b></p> | <p>عنوان اللوحة</p> <p><b>الجمالون والتفاصيل</b></p> | <p>المشروع / العميل</p> <p><b>برجولة خشب 6×6 بجمالونات مكشوفة</b><br/><b>عميل — برجولة</b></p> | <p><b>مصنع وتد الأخشاب</b><br/>Watad Wood Factory</p>  |
|--------------------------------------------|-----------------------------------------|-----------------------------------------|------------------------------------------------------|------------------------------------------------------------------------------------------------|---|

جدول الكميات وبيانات المشروع

الكميات

| البند                                               | الوصف           | العدد | الطول (سم) | المقطع |
|-----------------------------------------------------|-----------------|-------|------------|--------|
| أعمدة 20×20 (4 طبقات 20×5 مقصوصة من 22.5×5 مبرغية)  | 6 عمود × 280 سم | 24    | 290        | 5×22.5 |
| جسور طرفية (طبقتين 22.5×5) — وصلة فوق العمود الأوسط | 2 خط × 700 سم   | 8     | 350        | 5×22.5 |
| جسر القمة (طبقتين 22.5×5)                           | 700 سم          | 4     | 350        | 5×22.5 |
| شداد الجمالون (طبقتين 15×5) — نصين                  | 3 جمالون        | 12    | 320        | 5×15   |
| قائم الجمالون (طبقتين 15×5)                         | 3 جمالون        | 6     | 136        | 5×15   |
| أذرع الجمالون المائلة 15×5                          | 3 × 2           | 6     | 157        | 5×15   |
| مدادات 15×5 كل 60 سم                                | 2 × 13 جهة      | 26    | 404        | 5×15   |
| كوابيل الأعمدة (طبقتين 15×5)                        |                 | 28    | 110        | 5×15   |
| تطبيق خشب 2.5 سم (الطبقة 1)                         | 56.6 م²         | 88    | 400        | لوح    |
| قرميد معدني (الطبقة 2) + غطاء الحرف وحواف الجملون   | 56.6 م²         | —     | حرف 700    | م²     |
| قواعد حديد U مجلفنة + قواعد خرسانة 60×50×50         |                 | 6     | —          | طقم    |

| العدد | الطلبات 22.5×5        |
|-------|-----------------------|
| 32    | طلبية 320 سم (15×5)   |
| 24    | طلبية 320 سم (22.5×5) |
| 26    | طلبية 480 سم (15×5)   |
| 12    | طلبية 480 سم (22.5×5) |
| 94    | الإجمالي              |

بيانات المشروع


| البند      | البيان                                      |
|------------|---------------------------------------------|
| المشروع    | برجولة خشب 6×6 بجمالونات مكشوفة             |
| العميل     | عميل — برجولة                               |
| التاريخ    | 2026-10-07                                  |
| المقاس     | 6.00 × 6.00 م = 36.0 م²                     |
| الأعمدة    | 6 أعمدة 20×20 نازلة للأرض على قواعد حديد    |
| السقف      | جملون 30° — طبقتين: تطبيق خشب + قرميد معدني |
| الجمالونات | 3 جمالون مكشوف (شداد + قائم + ذراعين)       |

التسعير

| البند        | القيمة             |
|--------------|--------------------|
| المساحة (م²) | 36.00              |
| سعر المتر    | يُحدد بعد الاعتماد |
| الإجمالي     | —                  |

• الأرضية (بلاط/خرسانة) على العميل ما لم يُذكر غير ذلك. • الطلبات حسب طرق المصنع — TO\_CONFIRM

## المنظور ثلاثي الأبعاد

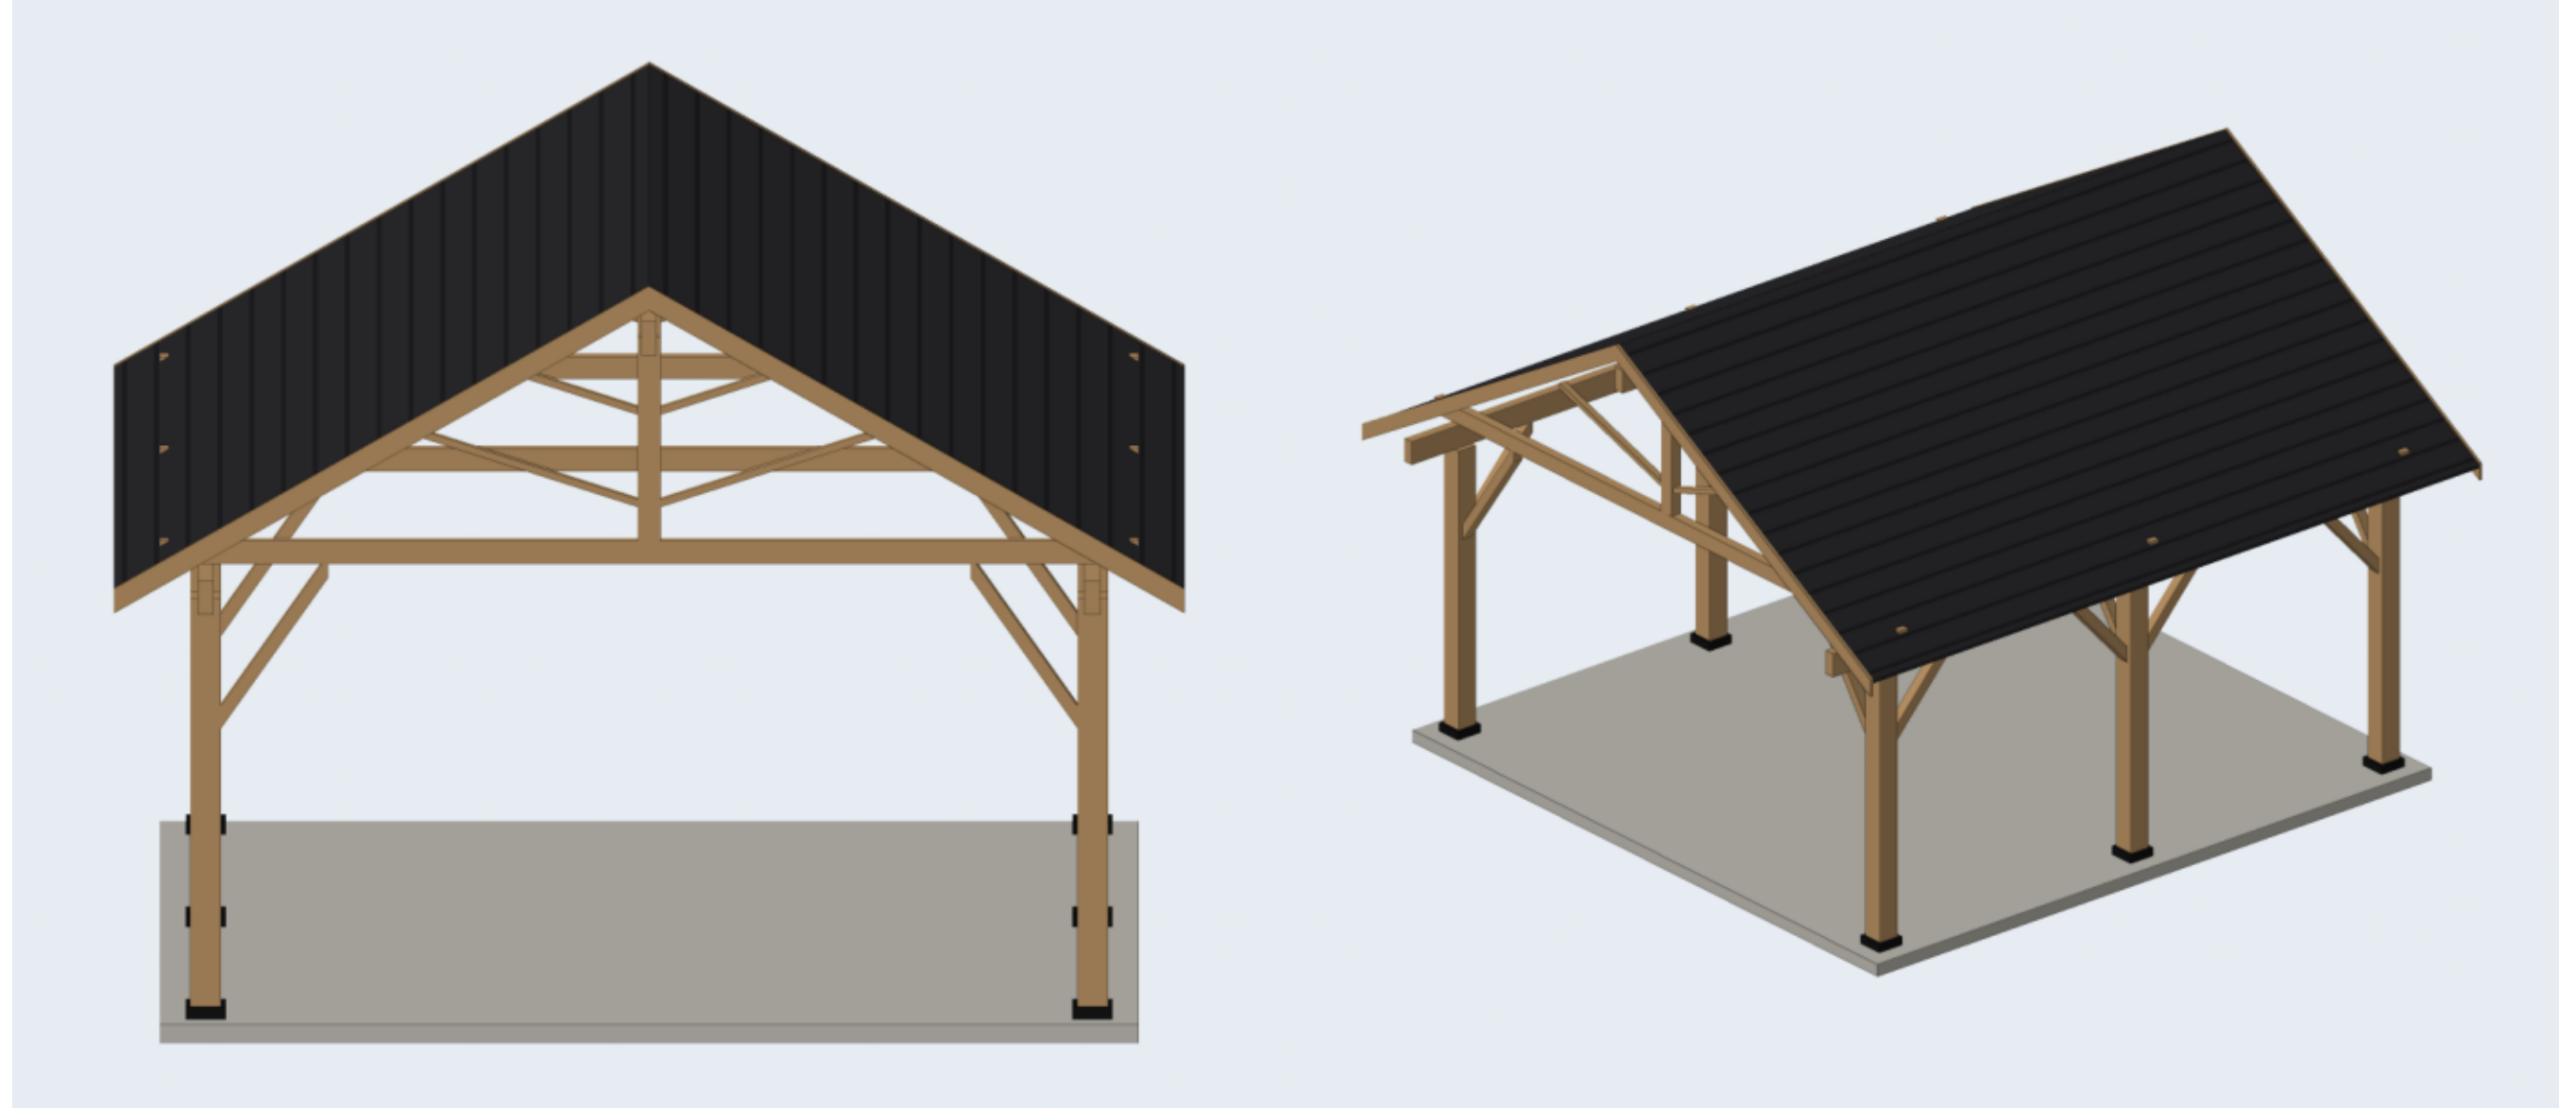

رقم اللوحة

A-05 (5/6)

التاريخ

2026-10-07

المقياس

—

عنوان اللوحة

المنظور

المشروع / العميل

برجولة خشب 6×6 بجمالونات مكشوفة  
عميل — برجولة

مصنع وتد الأخشاب  
Watad Wood Factory



الصور الواقعية



|            |            |         |                |                                                  |                                        |
|------------|------------|---------|----------------|--------------------------------------------------|----------------------------------------|
| رقم اللوحة | التاريخ    | المقياس | عنوان اللوحة   | المشروع / العميل                                 | مصنع وتد الأخشاب<br>Watad Wood Factory |
| A-06 (6/6) | 2026-10-07 | —       | الصور الواقعية | برجولة خشب 6×6 بجمالونات مكشوفة<br>عميل — برجولة |                                        |