

المسقط الأفقي مع الفرش

الأبعاد بالسنتيمتر - الجدران: قوائم 7×5 + تلبيس 2.5 من الجهتين (12 سم)

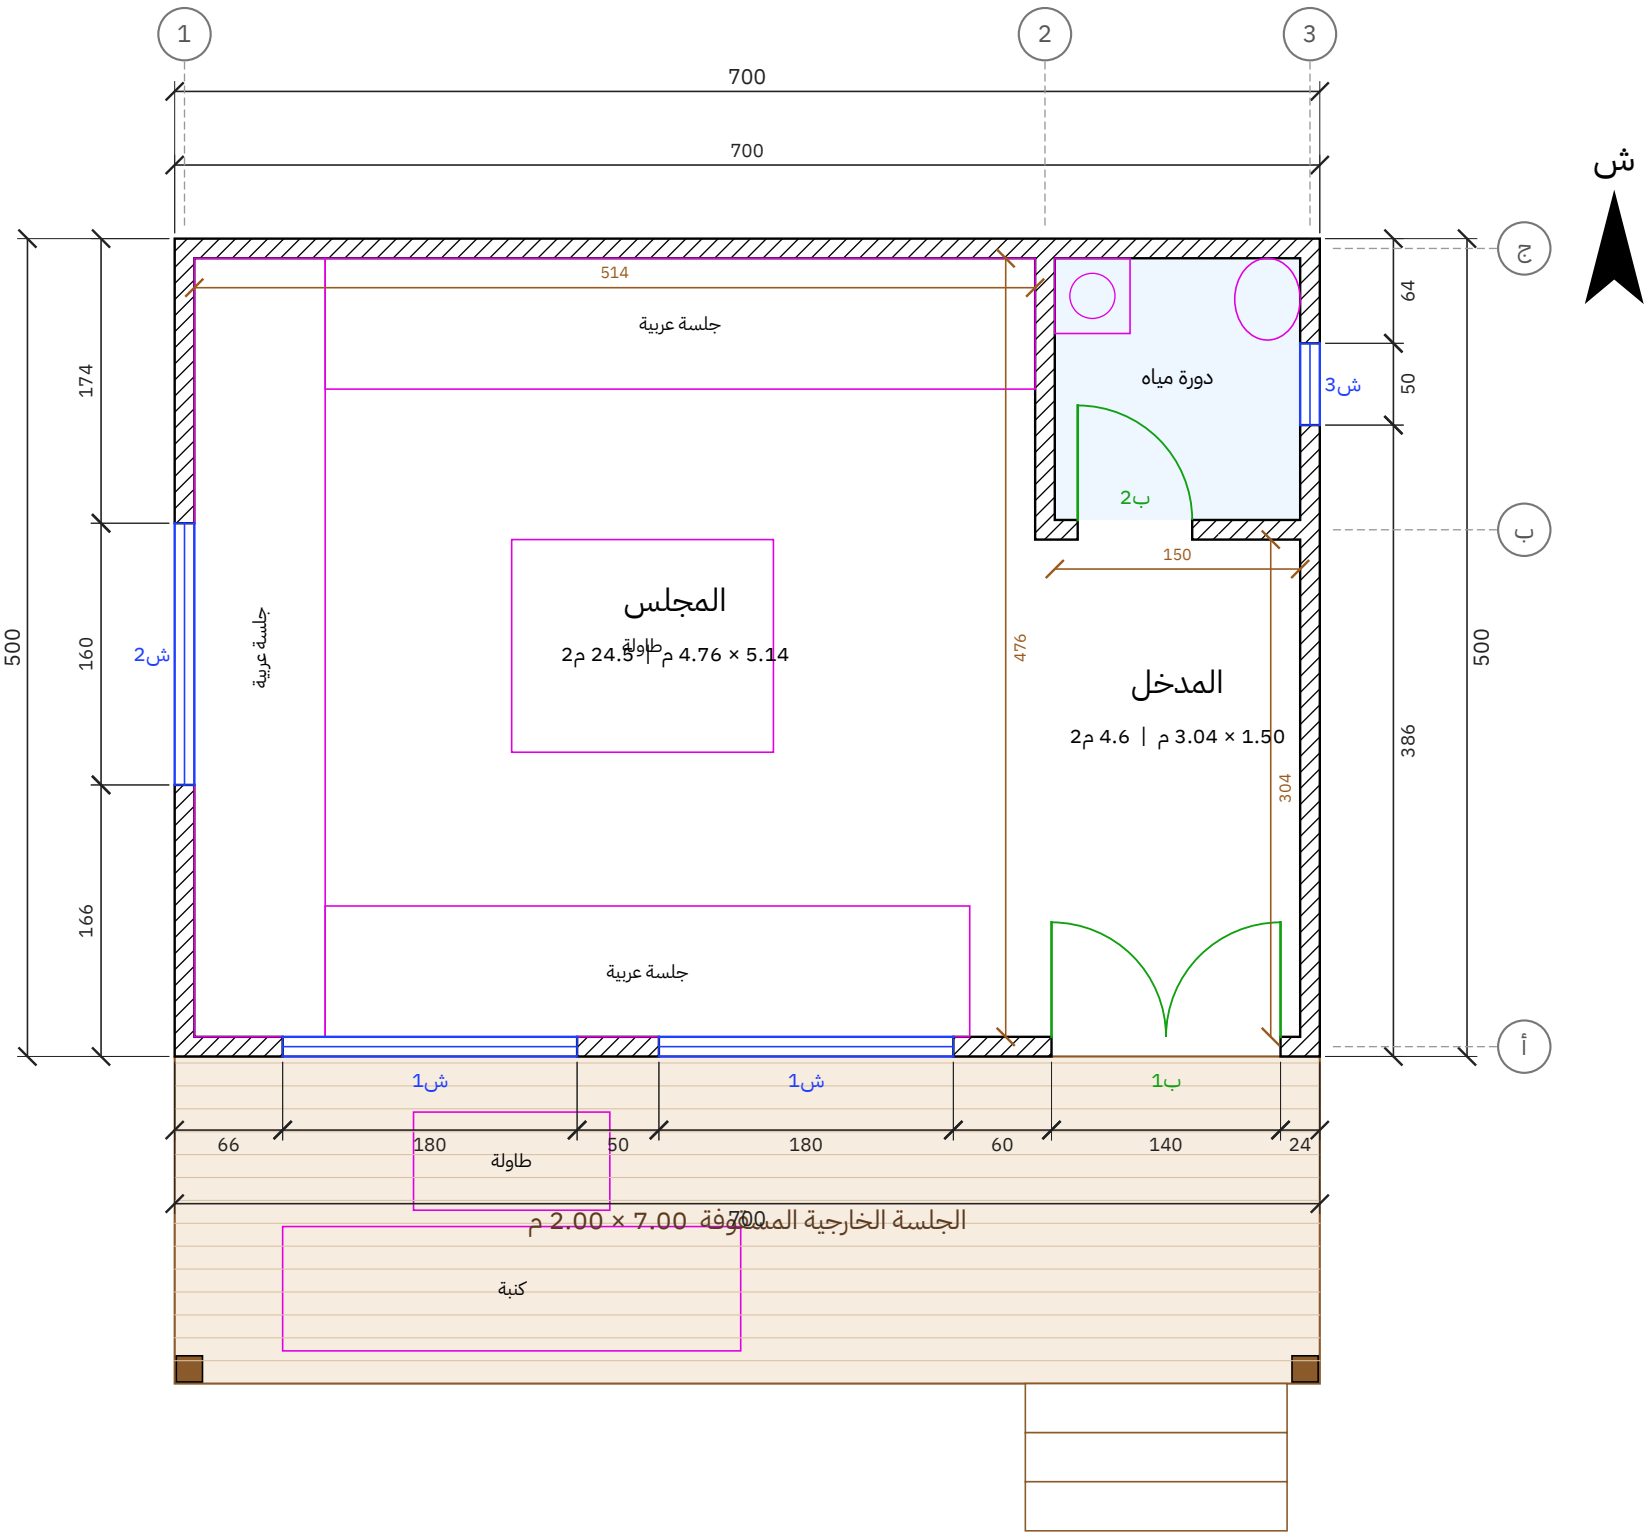


مصنع وتد الأخشاب Watad Wood Factory	المشروع / العميل مجلس خشب 7.00 × 5.00 م – سقف مائل ممتد على جلسة خارجية عميل – مجلس 7×5	عنوان اللوحة المسقط الأفقي	المقياس 1:50	التاريخ 2026-10-29	رقم اللوحة A-01 (1/9)

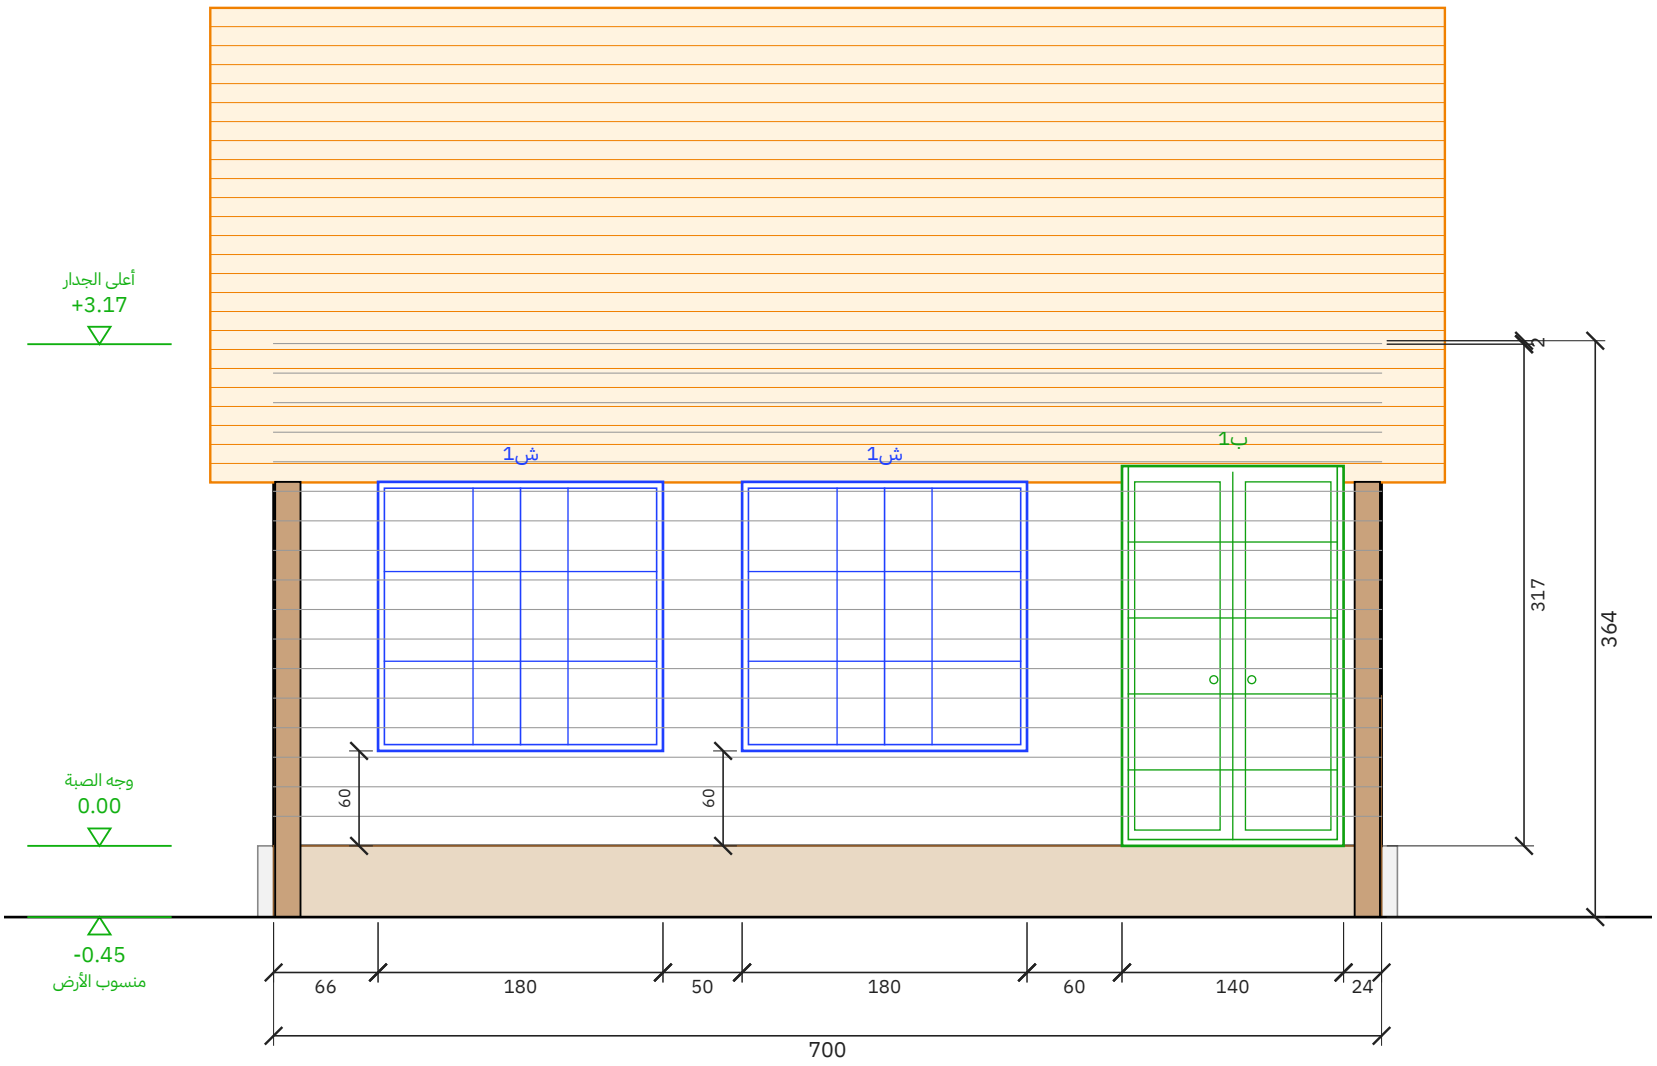

الواجهة الأمامية (على الحوش)

مقياس 1:50 | الوحدة: سم

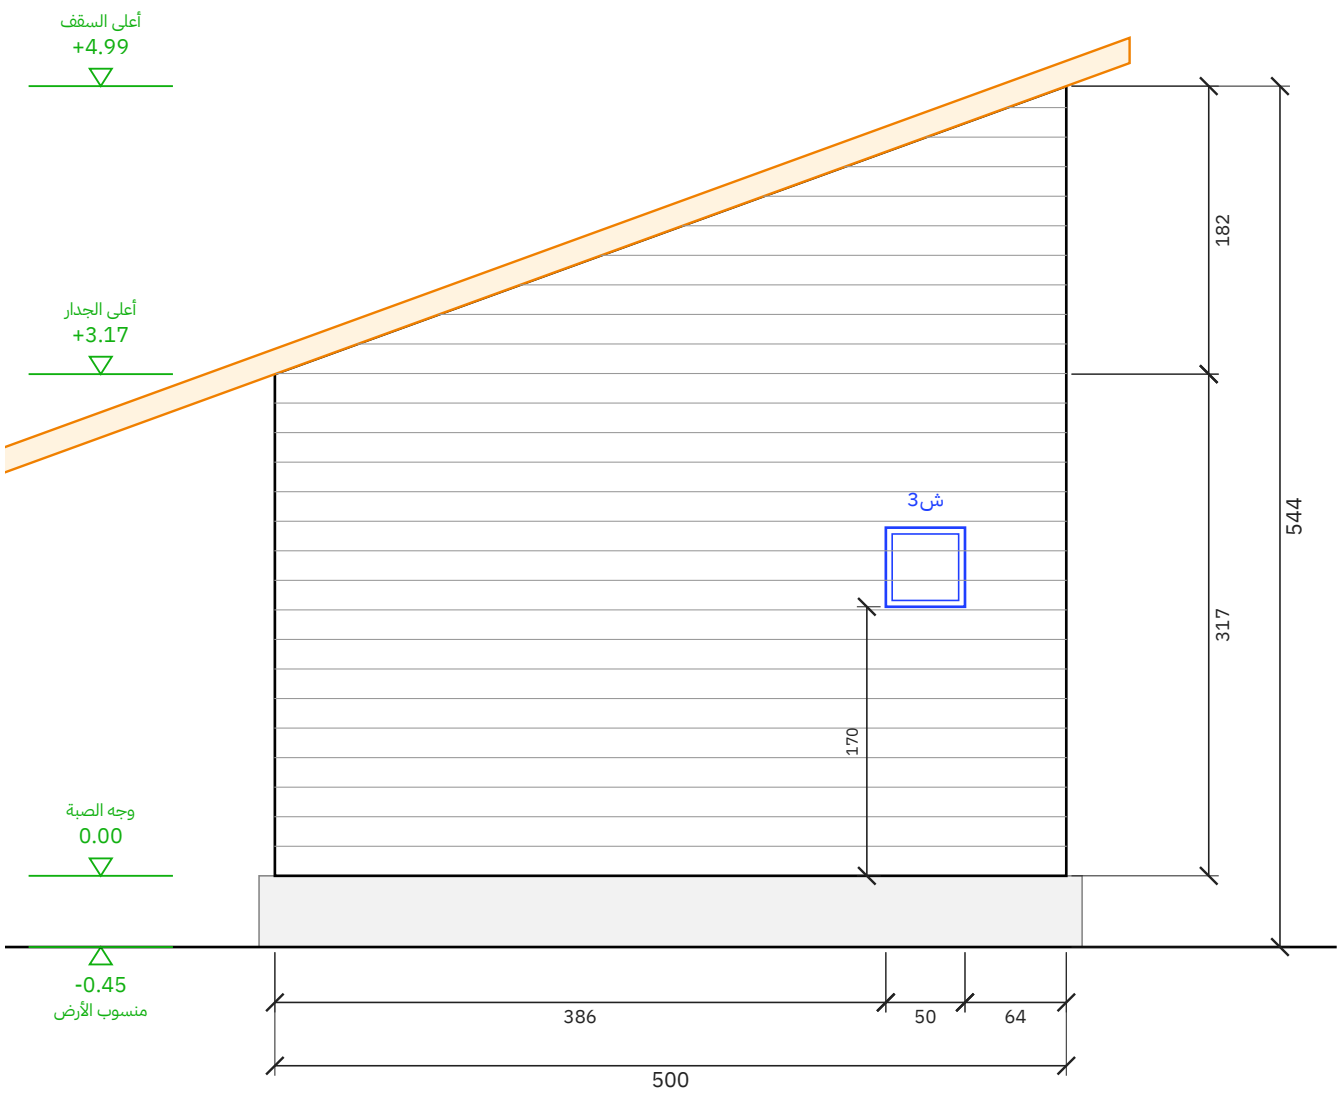


الواجهة الشرقية

مقياس 1:50 | الوحدة: سم


المشروع / العميل	عنوان اللوحة	المقياس	التاريخ	رقم اللوحة
مجلس خشب 7.00 × 5.00 م — سقف مائل ممتد على جلسة خارجية عميل — مجلس 7×5	الواجهة الأمامية (على الحوش) والواجهة الشرقية	1:50	2026-10-29	A-02 (2/9)

مصنع وتد الأخشاب
Watad Wood Factory

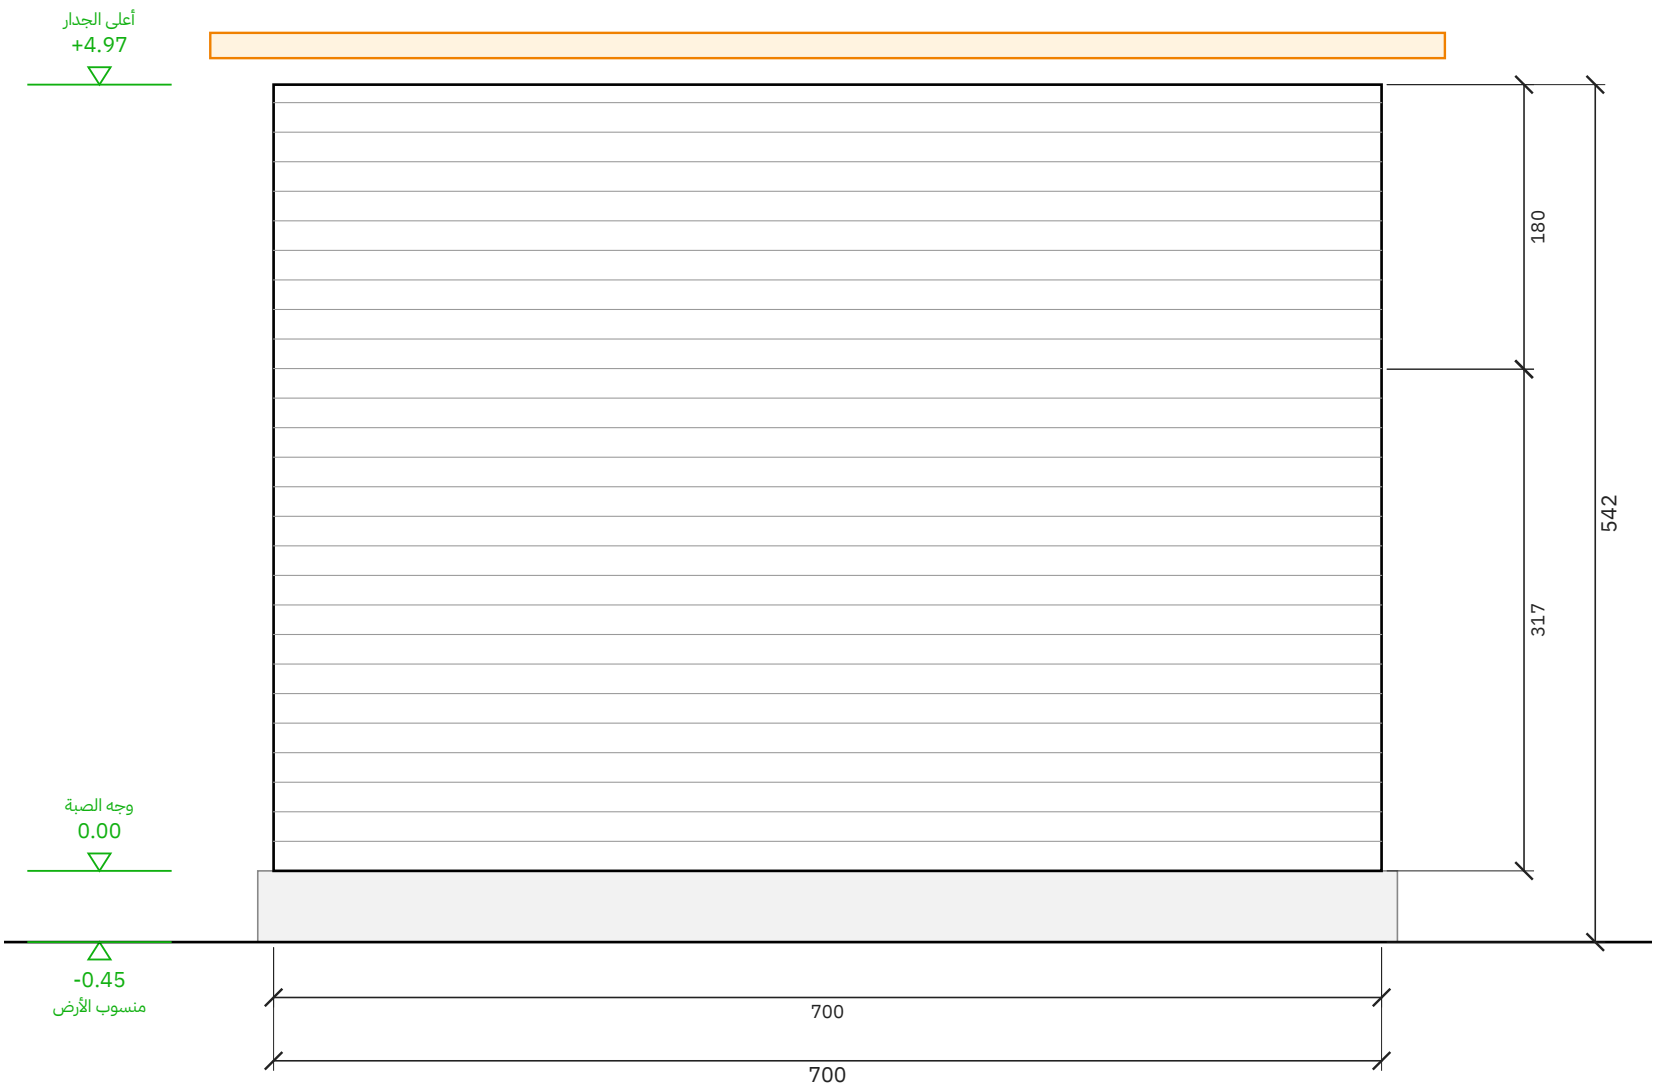

الواجهة الخلفية

مقياس 1:50 | الوحدة: سم

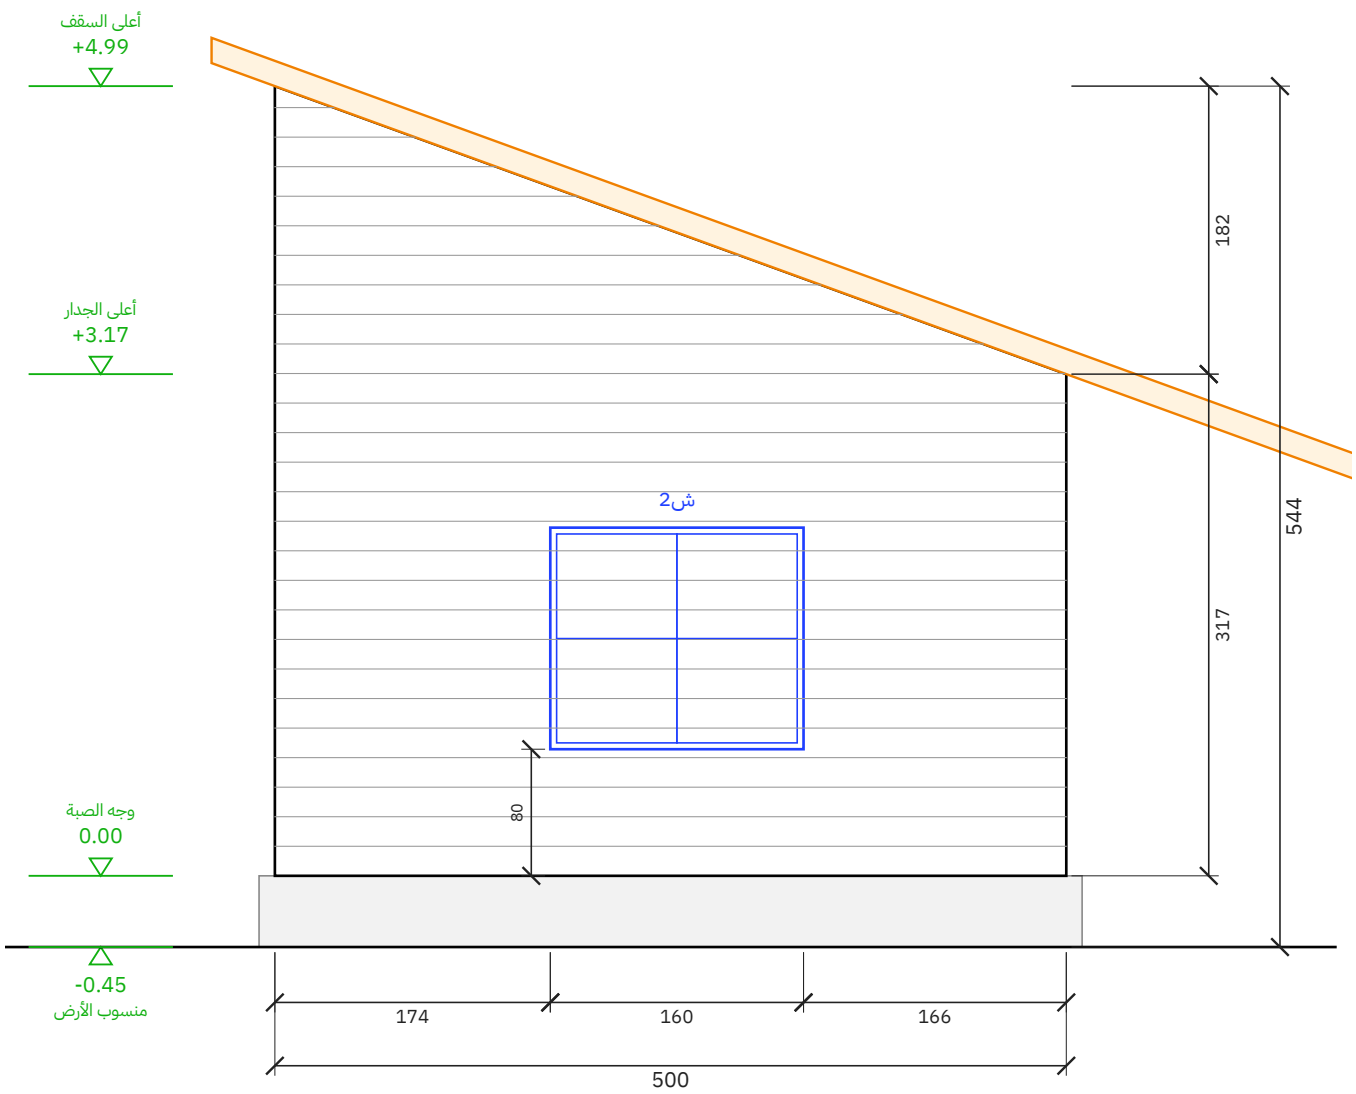

الواجهة الغربية


مقياس 1:50 | الوحدة: سم

المشروع / العميل	عنوان اللوحة	المقياس	التاريخ	رقم اللوحة
مجلس خشب 7.00 × 5.00 م — سقف مائل ممتد على جلسة خارجية **عميل — مجلس 7×5**	**الواجهة الخلفية والواجهة الغربية**	**1:50**	**2026-10-29**	**A-03 (3/9)**

مصنع وتد الأخشاب
Watad Wood Factory


مسقط السقف (مائل باتجاه واحد)

رفرف 40 سم من كل جهة | مقياس 1:50

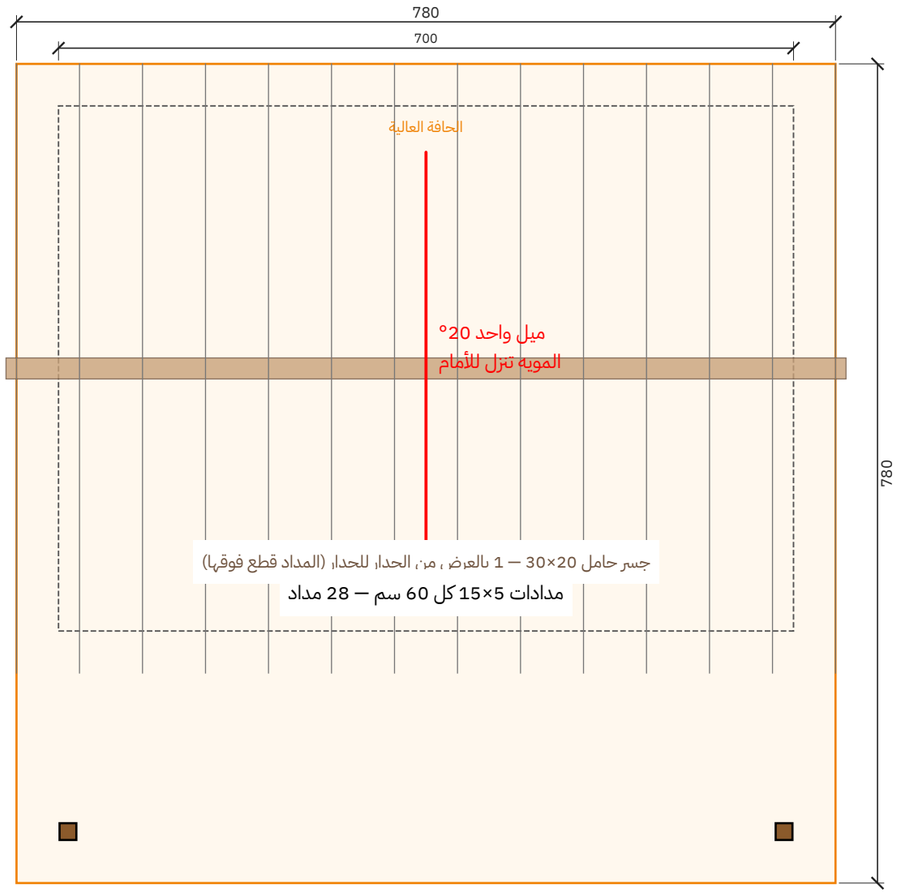


قطاع عرضي أ-أ

مقياس 1:50 | الوحدة: سم

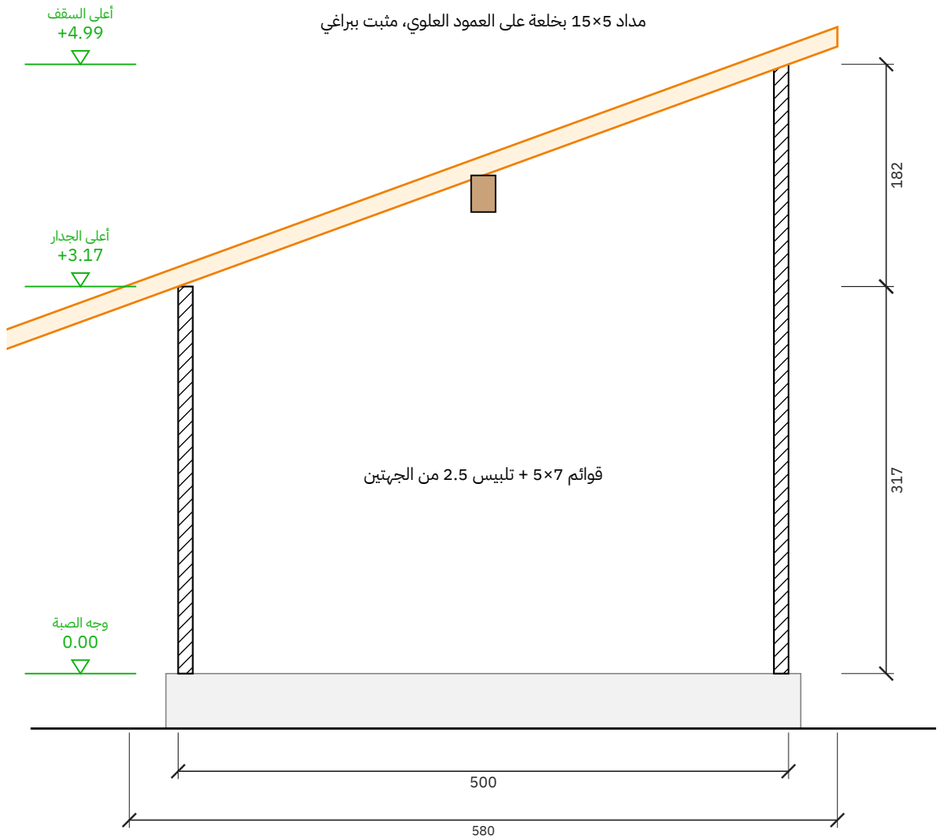

تفصيلة جلوس المداد على العلوي (1:5)

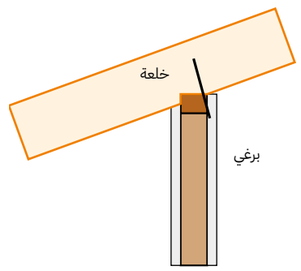

مصنع وتد الأخشاب Watad Wood Factory	المشروع / العميل مجلس خشب 7.00 × 5.00 م — سقف مائل ممتد على جلسة خارجية عميل — مجلس 7×5	عنوان اللوحة مسقط السقف والقطاع	المقياس 1:50	التاريخ 2026-10-29	رقم اللوحة A-04 (4/9)

جدول مقاسات الأبواب والشبابيك

مقاس الفتحة الصافي في الجدار - الوحدة: سم

الرمز	النوع	العرض (سم)	الارتفاع (سم)	ارتفاع الجلسة (سم)	العدد	الموقع
ب1	باب مزدوج	140	240	-	1	الأمامية (على الحوش)
ب2	باب	70	210	-	1	دورة المياه
ش1	شباك	180	170	60	2	الأمامية (على الحوش) 2
ش2	شباك	160	140	80	1	الغربية
ش3	شباك	50	50	170	1	الشرقية

الإجمالي: أبواب 2 - شبابيك 4

جدول المساحات وبيانات المشروع

بيانات المشروع


البند	البيان
المشروع	مجلس خشب 7.00 × 5.00 م — سقف مائل ممتد على جلسة خارجية
العميل	عميل — مجلس 7×5
الموقع	—
الاستخدام	مجلس ضيافة
التاريخ	2026-10-29
نظام البناء	هيكل خشب 7×5 + تلبيس 2.5 سم من الجهتين
السقف	مائل باتجاه واحد 20° — قرميد معدني

جدول المساحات

م	الفراغ	الأبعاد (م)	المساحة (م2)
1	المجلس	5.14 × 4.76	24.47
2	المدخل	1.50 × 3.04	4.56
3	دورة مياه	1.50 × 1.60	2.40
	المساحة الصافية الداخلية		**31.43**
	الجلسة الخارجية المسقوفة	**7.00 × 2.00**	**14.00**
	المساحة الإجمالية المبنية	**7.00 × 5.00**	**35.00**
	المساحة الكلية (المبنية + التراس)		**49.00**

لقطات المنظور الخارجي

المنظور الأمامي

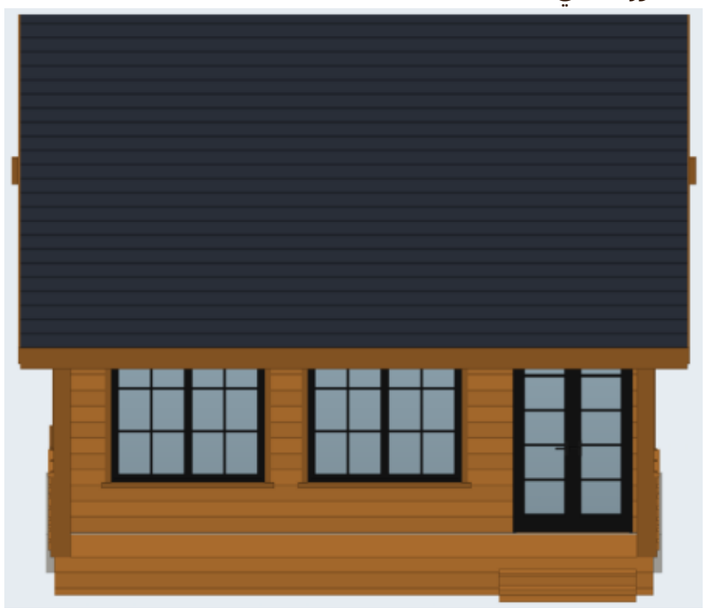


منظور أمامي من اليسار



منظور أمامي من اليمين




المنظور الخلفي

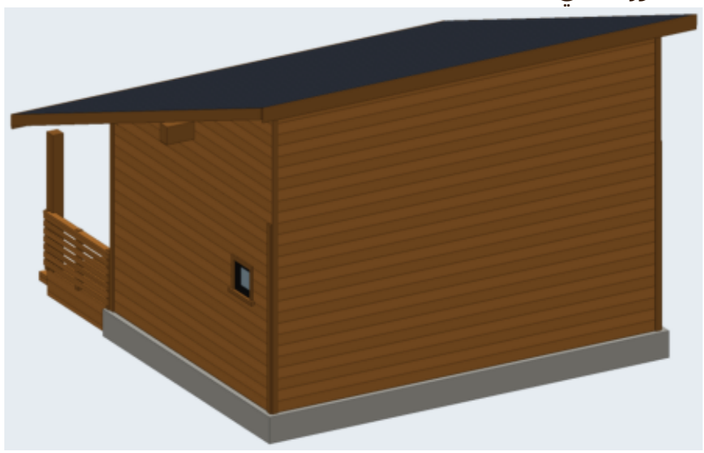

منظور خلفي من اليمين




منظر علوي

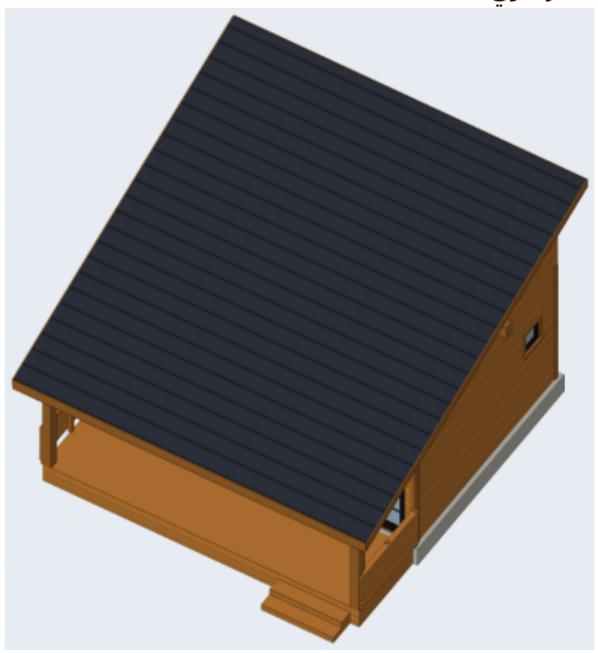

مصنع وتد الأخشاب Watad Wood Factory	المشروع / العميل مجلس خشب 7.00 × 5.00 م – سقف مائل ممتد على جلسة خارجية عميل – مجلس 7×5	عنوان اللوحة لقطات المنظور	المقياس –	التاريخ 2026-10-29	رقم اللوحة A-07 (7/9)

المقطع العلوي بالفرش

مقطع أفقي على ارتفاع 1.90 م — توزيع الفرش ومسار الحركة

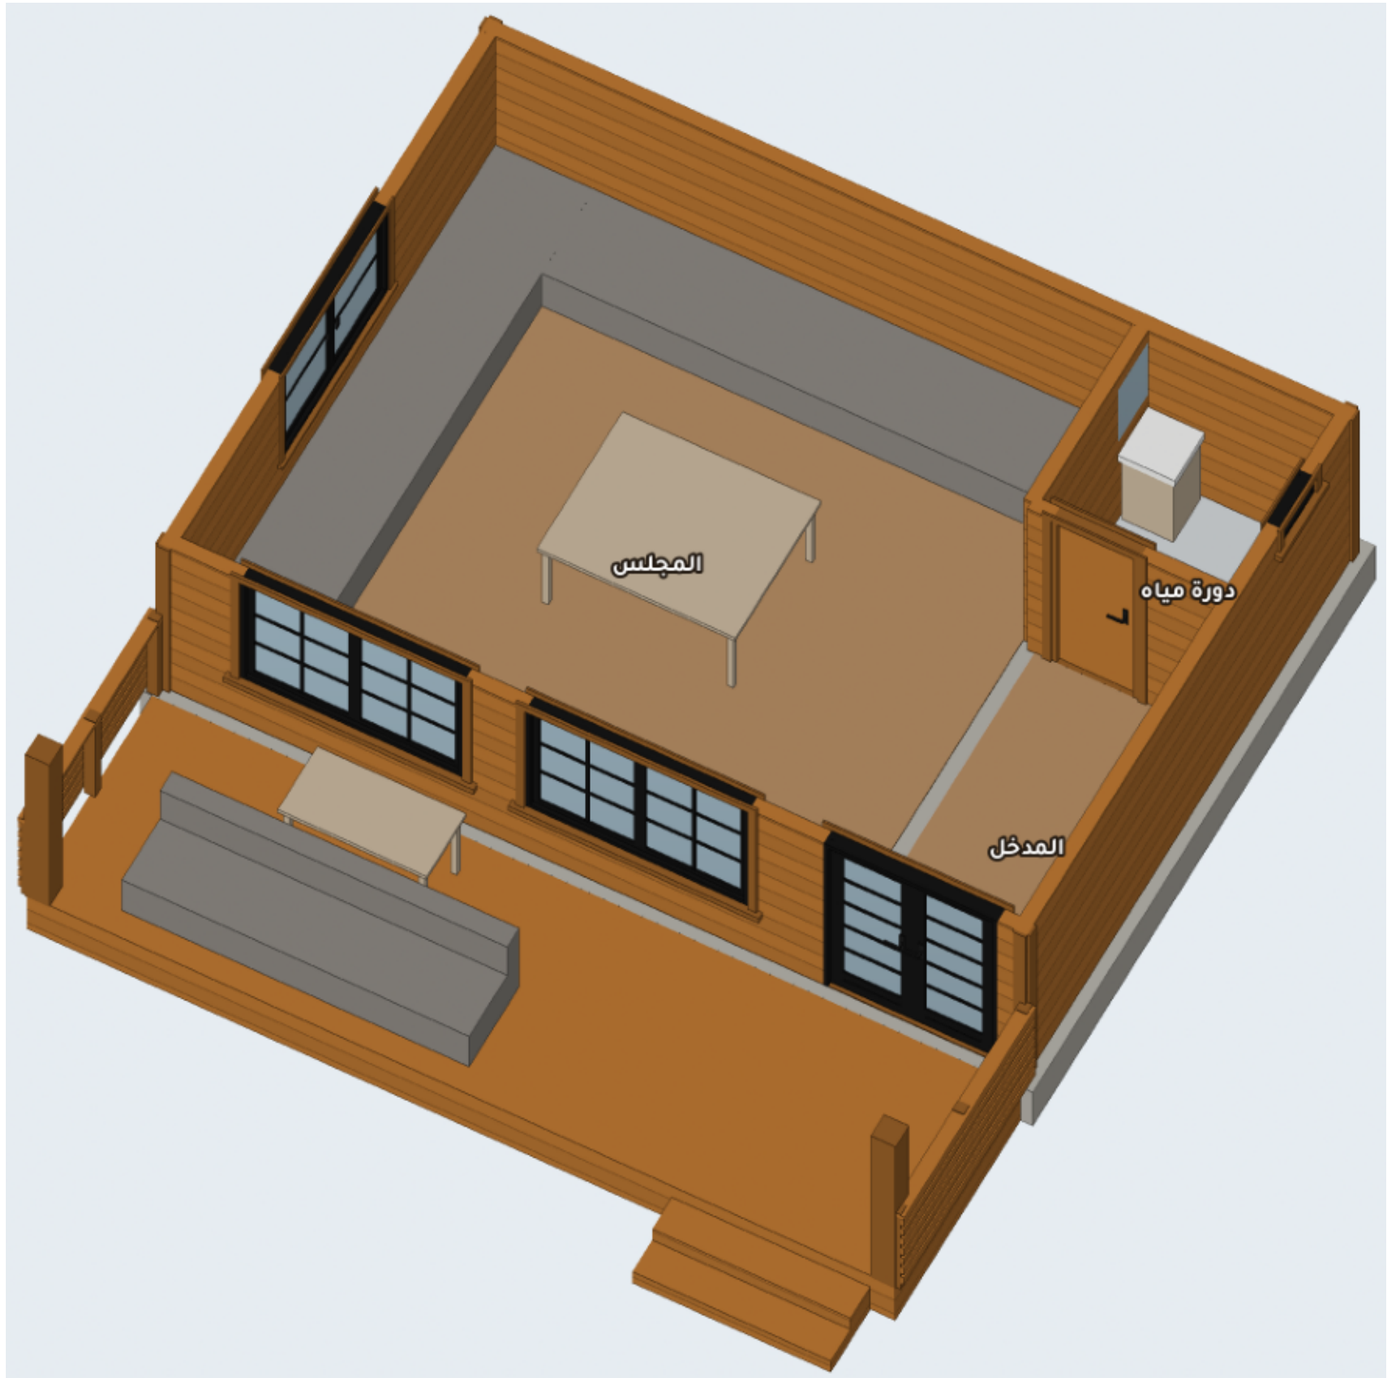

المشروع / العميل	عنوان اللوحة	المقياس	التاريخ	رقم اللوحة
مجلس خشب 7.00 × 5.00 م — سقف مائل ممتد على جلسة خارجية عميل — مجلس 7×5	المقطع العلوي بالفرش	—	2026-10-29	A-08 (8/9)

مصنع وتد الأخشاب
Watad Wood Factory

المنظور ثلاثي الأبعاد والمواد

النمط: برتقالي محمر + قرميد فحمي + دربزين X — رندر واقعي بخامات حقيقية



جدول المواد والألوان

الخشب / الصبغة

صبغة عسلي / سيدر

القرميد

قرميد فحمي / أسود مزرق

الزجاج

زجاج شفاف

إطارات الشبابيك والأبواب

إطار ألمنيوم أسود

الكنار والزوايا

نفس الصبغة أغمق درجة


الصبة

خرسانة 45 سم


الدربزين: ألواح أفقية متقاربة (عصري)

تقسيم الشبابيك: شبكة | الباب الرئيسي: زجاج بتقسيمات (فرنسي)

أنواع الدربزين المعتمدة (من مشاريع المصنع)

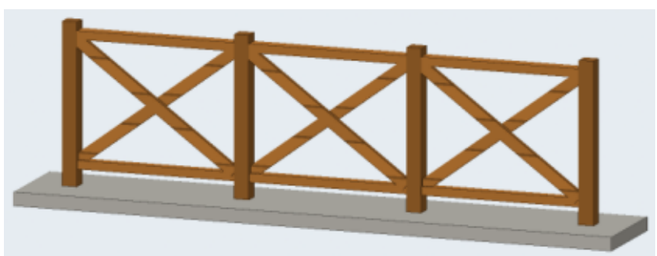

تقاطع X (صورة 5)

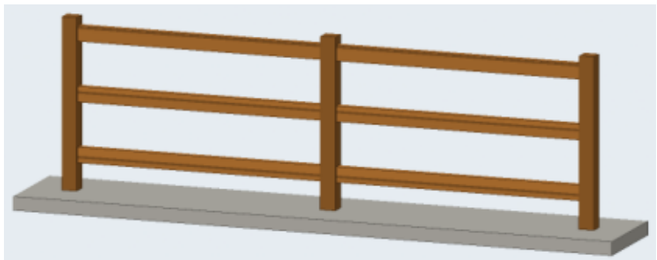

3 مرابيع أفقية (صورة 2)



قوائم رأسية متقاربة (صورة 1)

مصنع وتد الأخشاب Watad Wood Factory	المشروع / العميل **مجلس خشب 7.00 × 5.00 م — سقف مائل ممتد على جلسة خارجية** **عميل — مجلس 7×5**	عنوان اللوحة **المنظور والمواد**	المقياس —	التاريخ **2026-10-29**	رقم اللوحة **A-09 (9/9)**