
المنظور ثلاثي الأبعاد والمواد

النمط: جوزي غامق + إطارات سوداء — رندر واقعي بخامات حقيقية

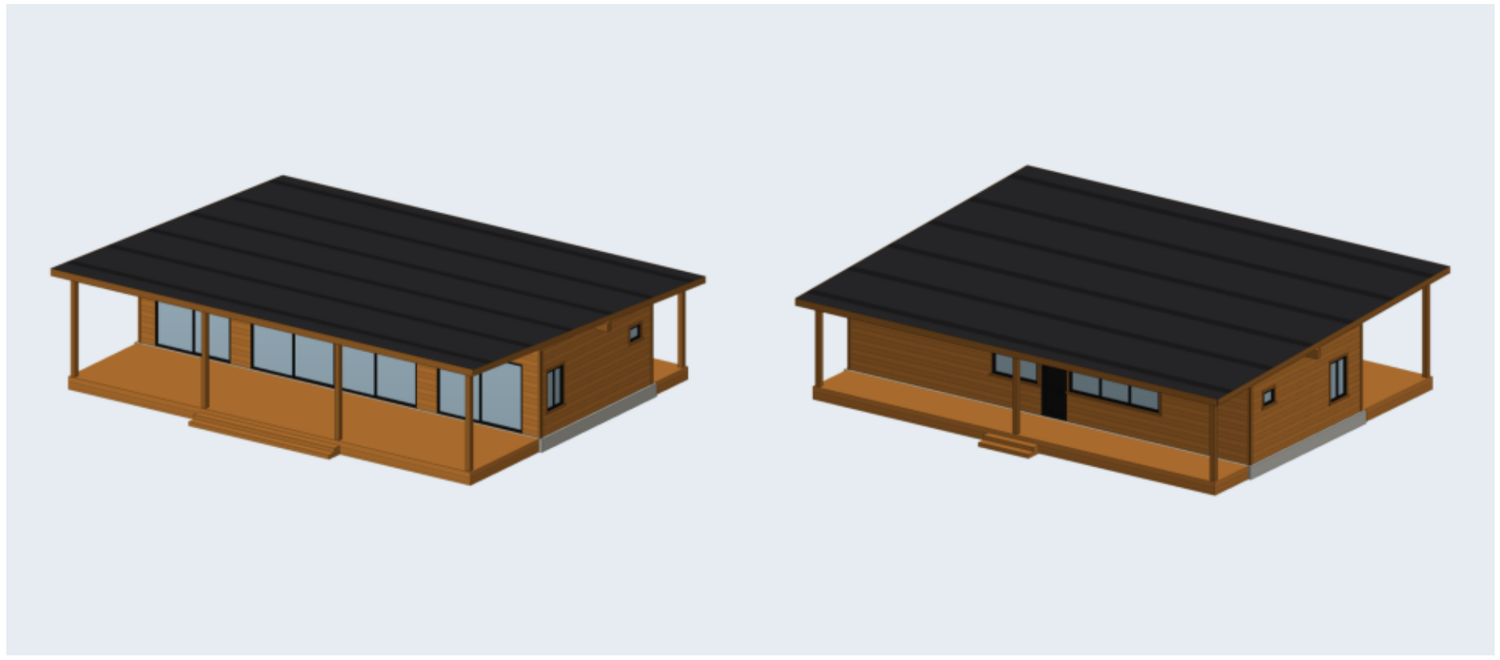

جدول المواد والألوان

الخشب / الصبغة
صبغة عسلي / سيدر

السقف (صاج معدني)
صاج رمادي غامق

الزجاج
زجاج شفاف

إطارات الشبابيك والأبواب
إطار ألمنيوم أسود


الكنار والزوايا
نفس الصبغة أغمق درجة

الصبة
خرسانة 45 سم


الدربزين: ألواح أفقية متقاربة (عصري)

تقسيم الشبابيك: بدون | الباب الرئيسي: سحاب زجاج

أنواع الدربزين المعتمدة (من مشاريع المصنع)

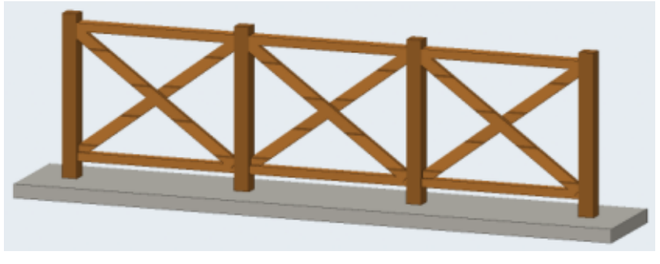

تقاطع X (صورة 5)

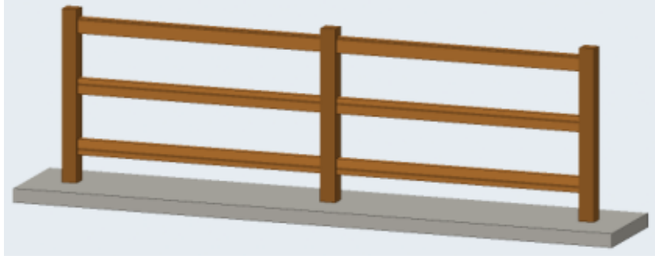

3 مرابيع أفقية (صورة 2)




قوائم رأسية متقاربة (صورة 1)

المشروع / العميل **كوخ 16.00 × 6.36 م — غرفتين نوم + صالة + حمامين + تراس أمامي 4.00 وخلفي 2.00** **عميل — كوخ 16 × 8.5**	عنوان اللوحة **المنظور والمواد**	المقياس **1:50**	التاريخ **2026-11-10**	رقم اللوحة **W-01 (1/15)**

مصنع وتد الأخشاب
Watad Wood Factory


المسقط الأفقي مع الفرش

الأبعاد بالسنتيمتر - الجدران: قوائم 7×5 + تلبيس 2.5 من الجهتين (12 سم)

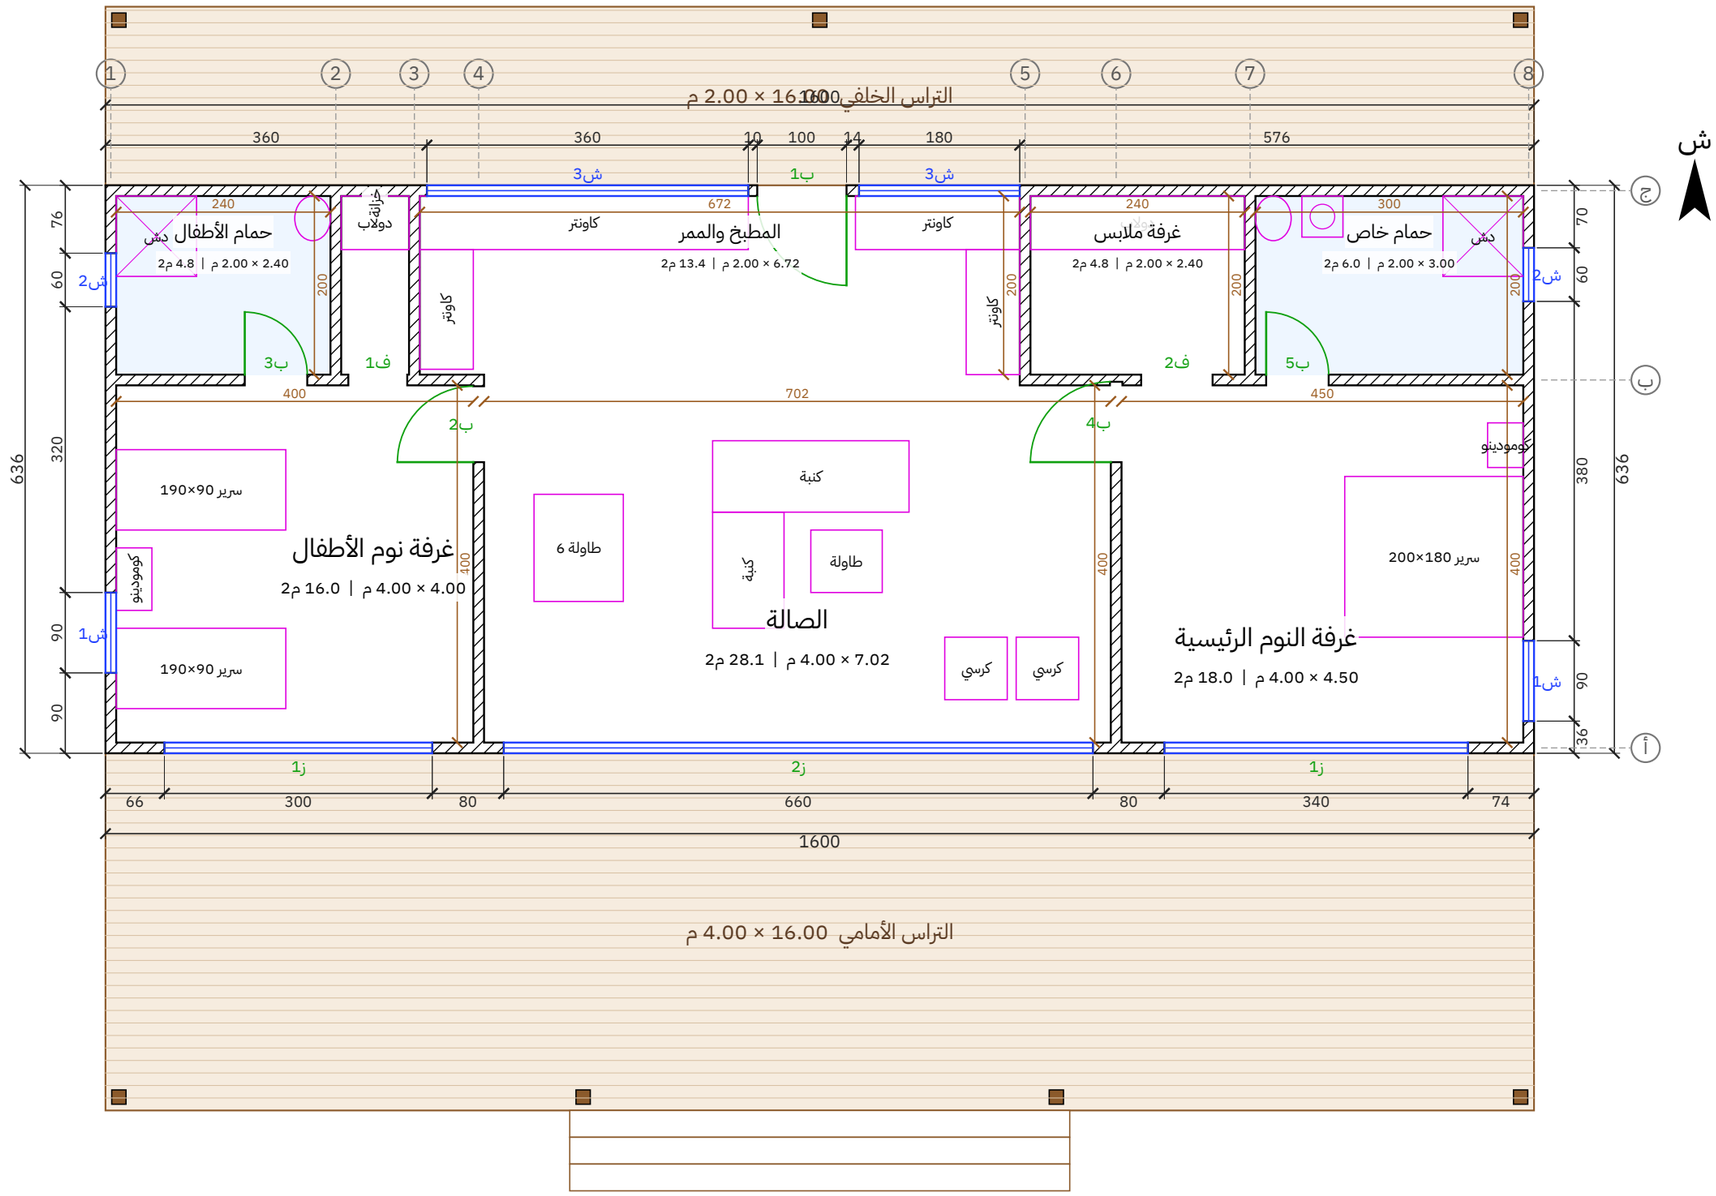


المشروع / العميل **كوخ 16.00 × 6.36 م — غرفتين نوم + صالة + حمامين + تراس أمامي 4.00 وخلفي 2.00** **عميل — كوخ 16 × 8.5**	عنوان اللوحة **المسقط الأفقي**	المقياس **1:50**	التاريخ **2026-11-10**	رقم اللوحة **W-02 (2/15)**

مصنع وتد الأخشاب
Watad Wood Factory

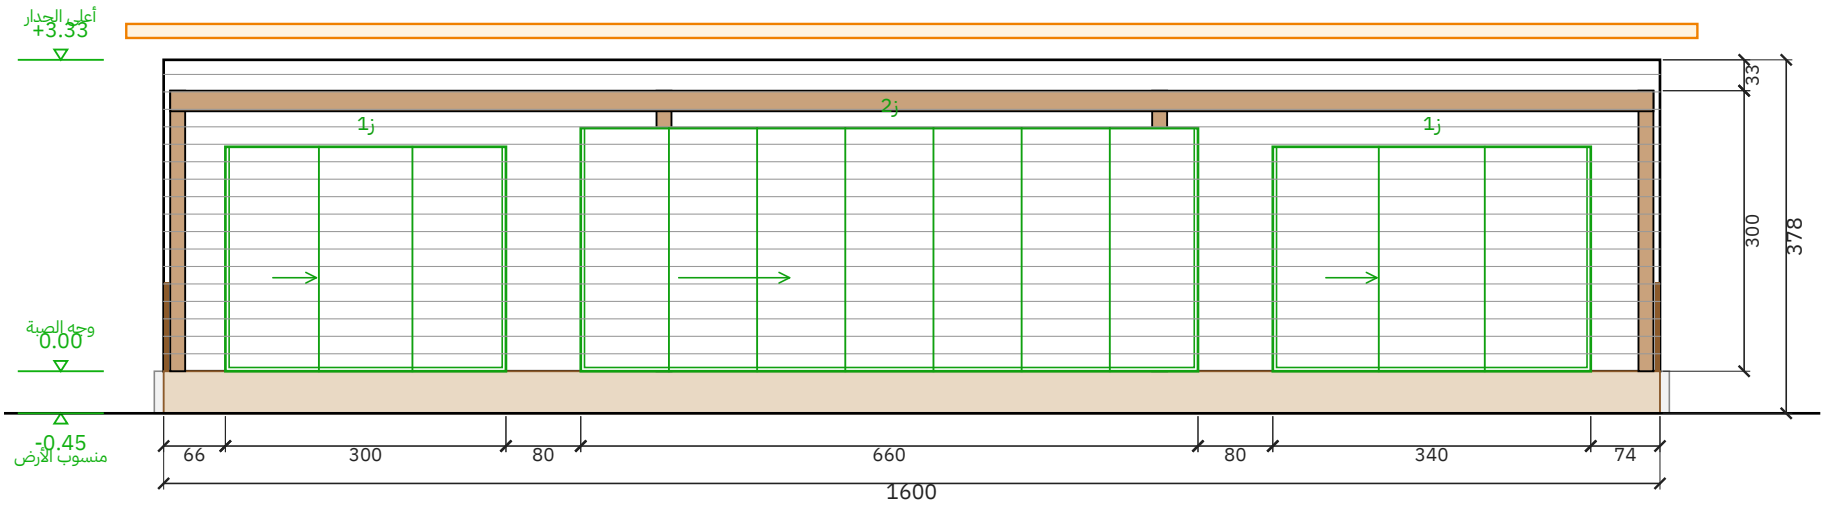

الواجهة الأمامية (على التراس)

مقياس 1:50 | الوحدة: سم

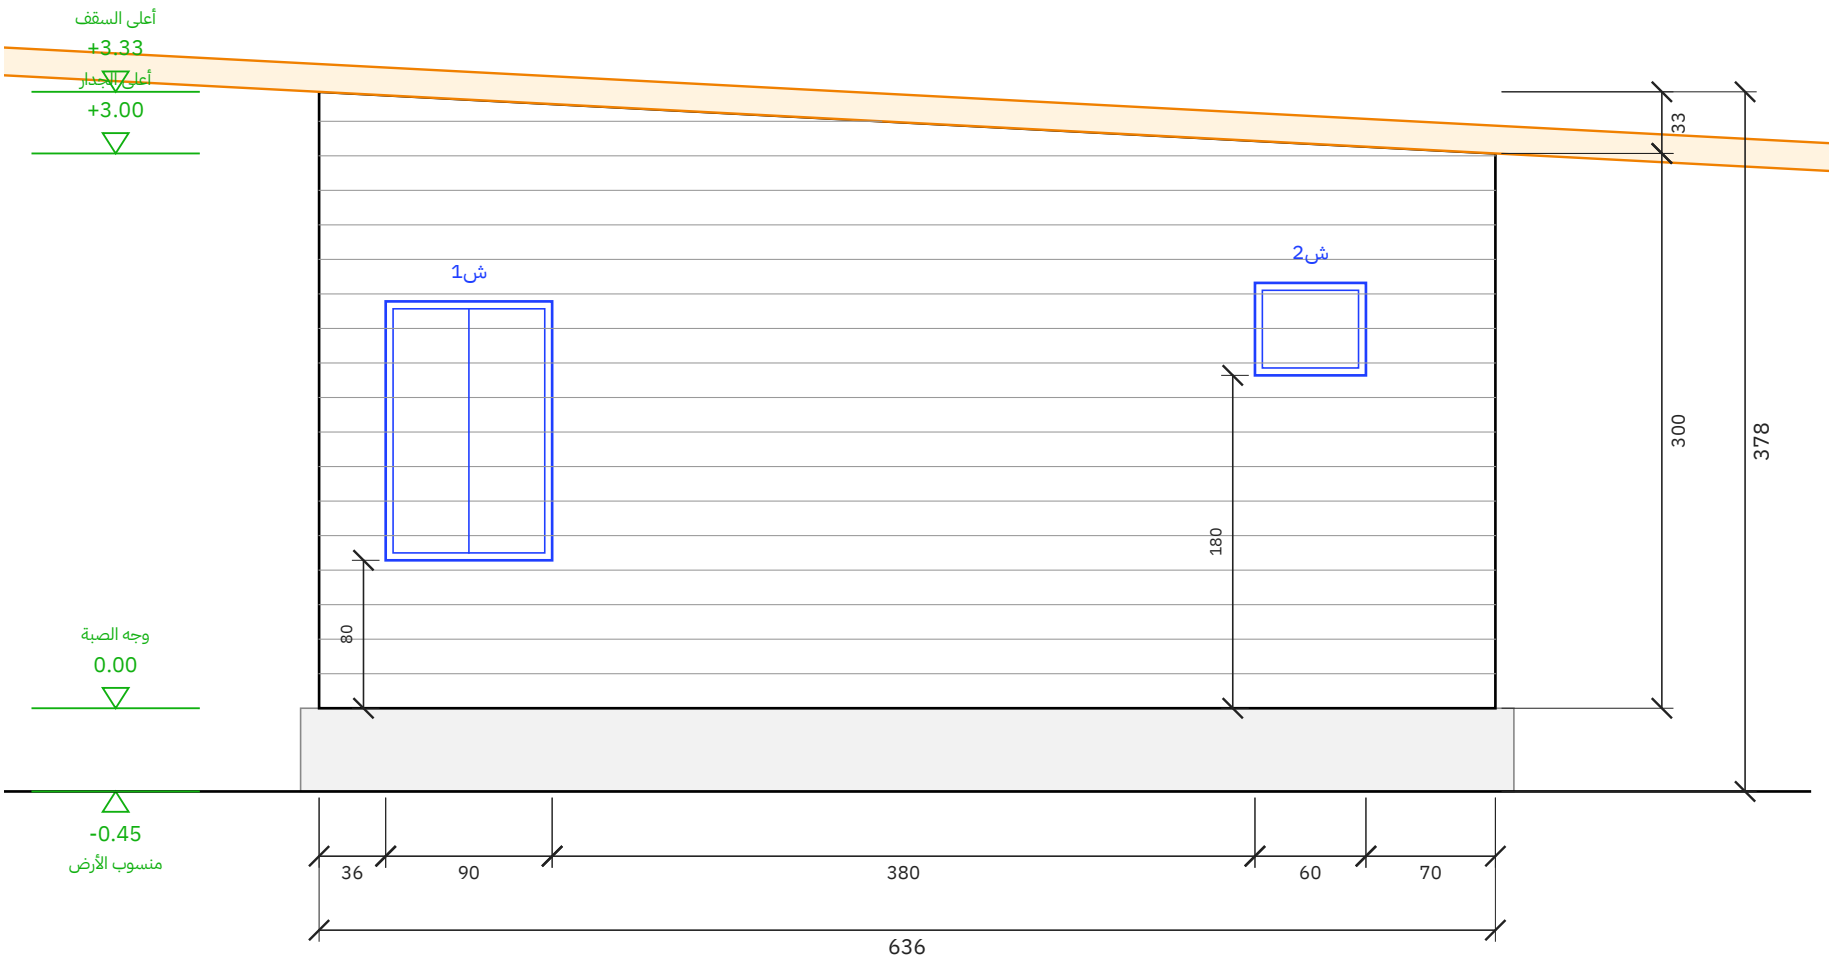


الواجهة الشرقية

مقياس 1:50 | الوحدة: سم


المشروع / العميل	عنوان اللوحة	المقياس	التاريخ	رقم اللوحة
كوخ 16.00 × 6.36 م — غرفتين نوم + صالة + حمامين + تراس أمامي 4.00 وخلفي 2.00 عميل — كوخ 16 × 8.5	الواجهة الأمامية (على التراس) والواجهة الشرقية	1:50	2026-11-10	W-03 (3/15)

مصنع وتد الأخشاب
Watad Wood Factory

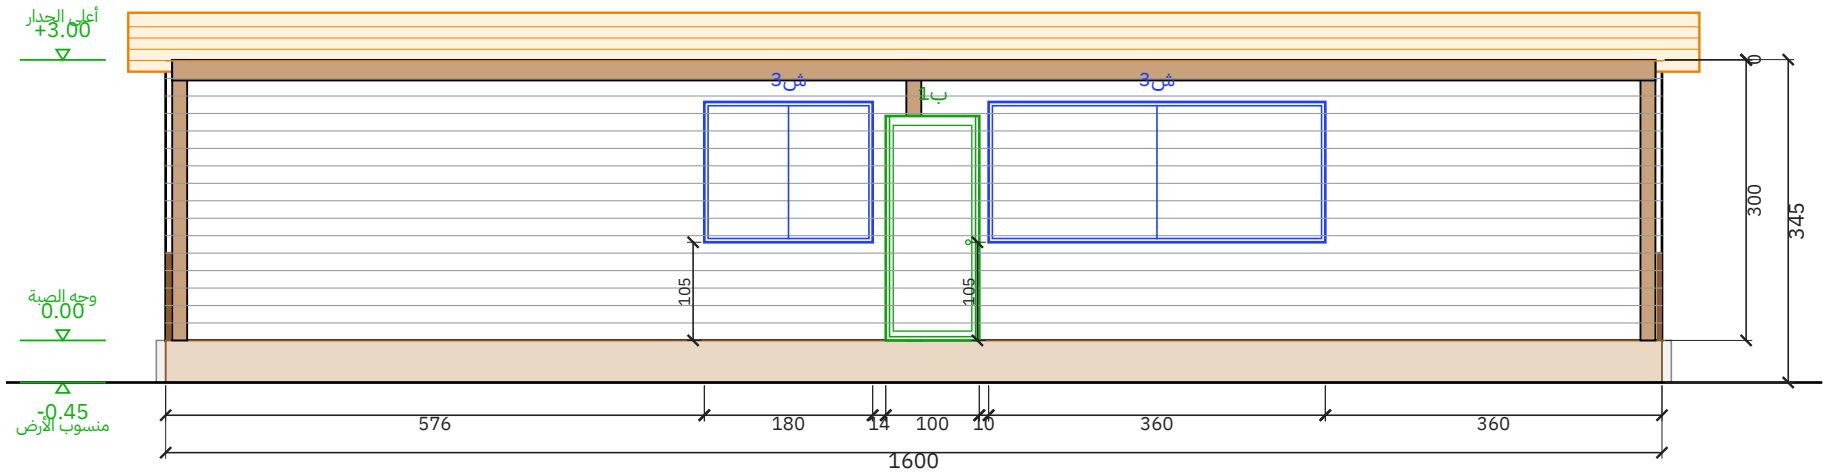

الواجهة الخلفية (المدخل)

مقياس 1:50 | الوحدة: سم

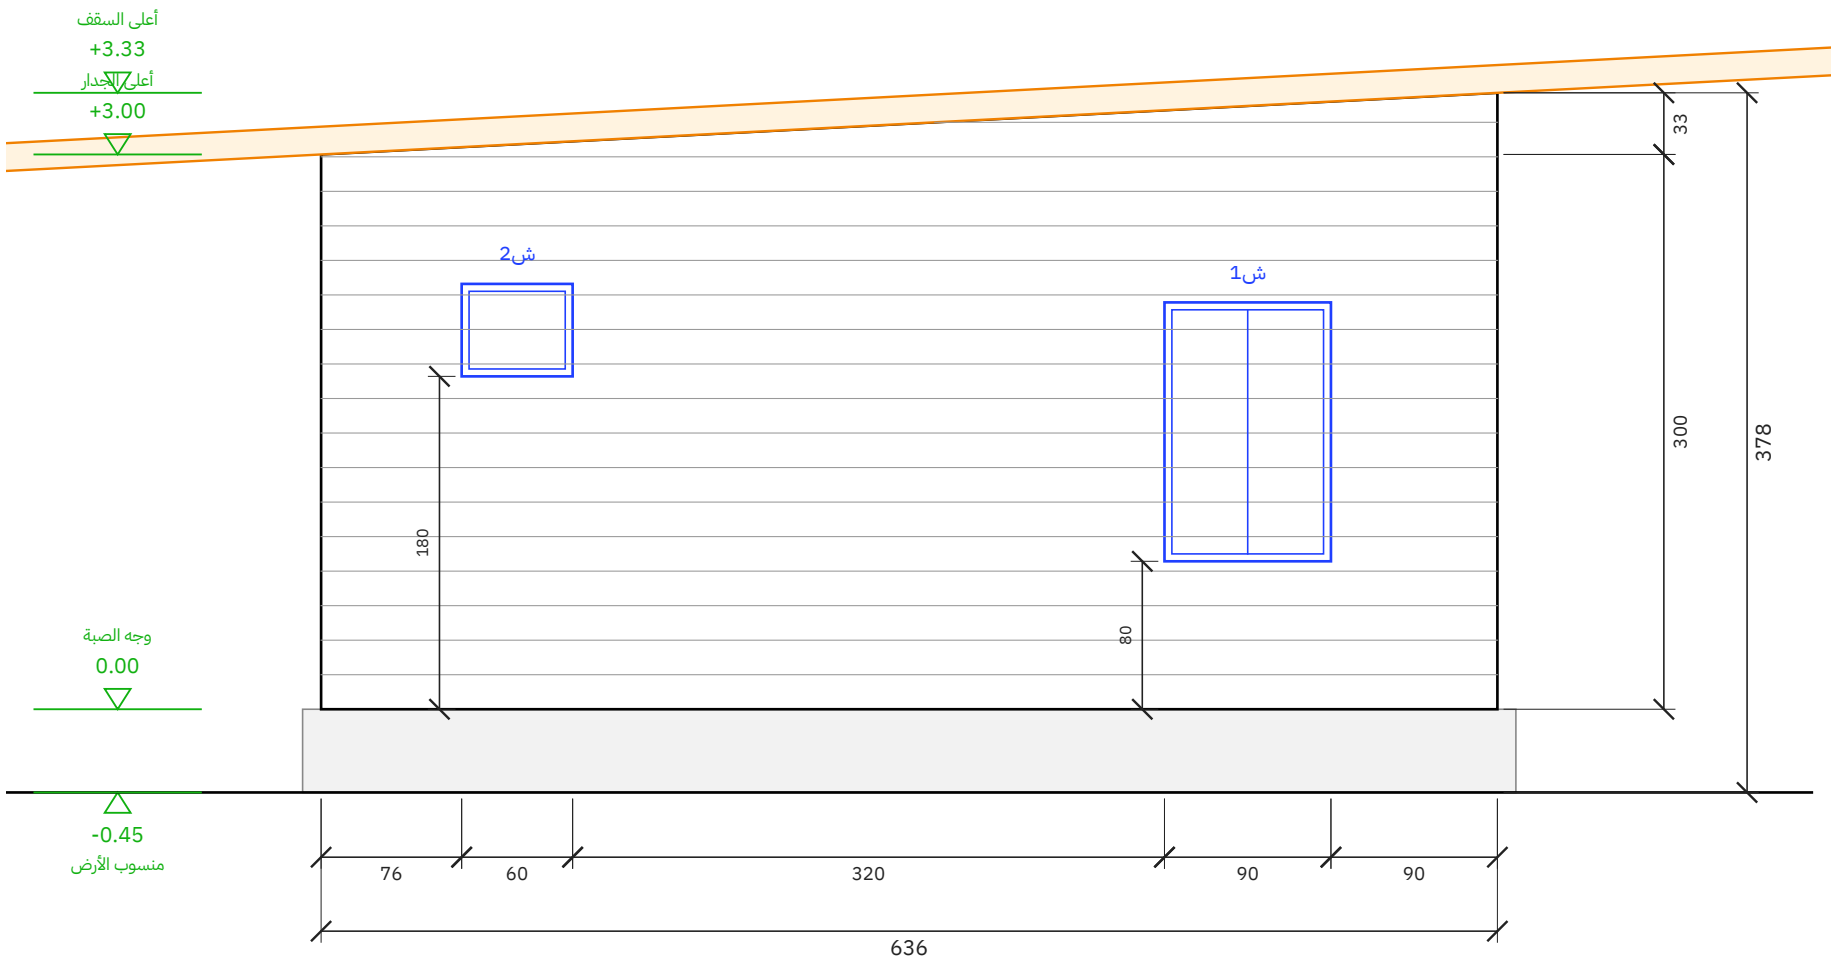

الواجهة الغربية


مقياس 1:50 | الوحدة: سم

المشروع / العميل	عنوان اللوحة	المقياس	التاريخ	رقم اللوحة
كوخ 16.00 × 6.36 م — غرفتين نوم + صالة + حمامين + تراس أمامي 4.00 وخلفي 2.00 عميل — كوخ 16 × 8.5	الواجهة الخلفية (المدخل) والواجهة الغربية	1:50	2026-11-10	W-04 (4/15)

مصنع وتد الأخشاب
Watad Wood Factory


مسقط السقف (مائل باتجاه واحد)

رفرف 40 سم من كل جهة | مقياس 1:50

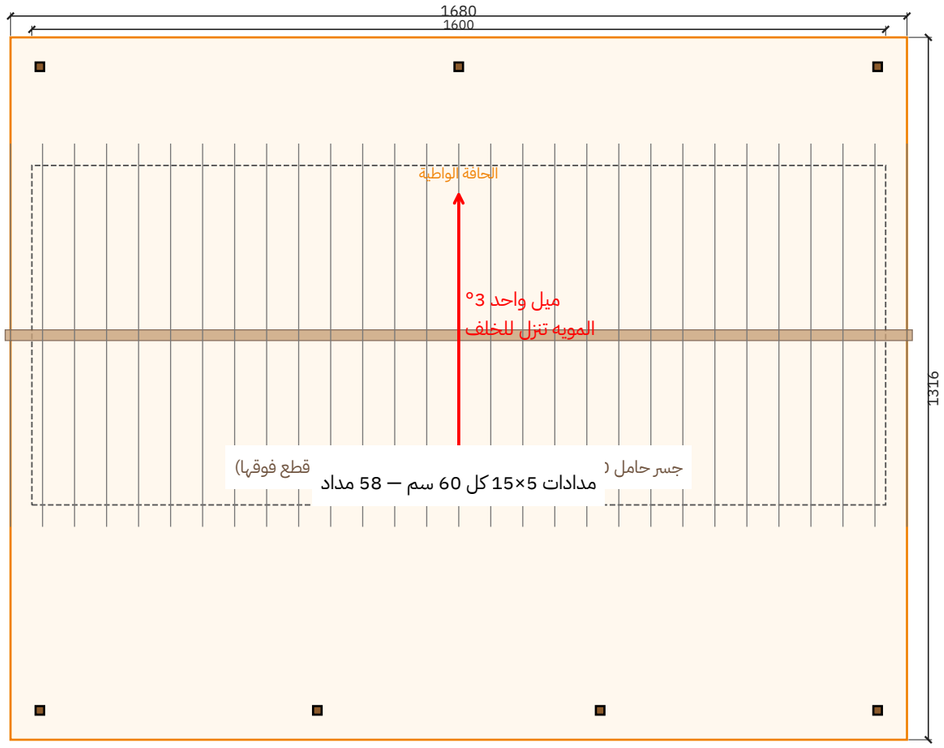


قطاع عرضي أ-أ

مقياس 1:50 | الوحدة: سم

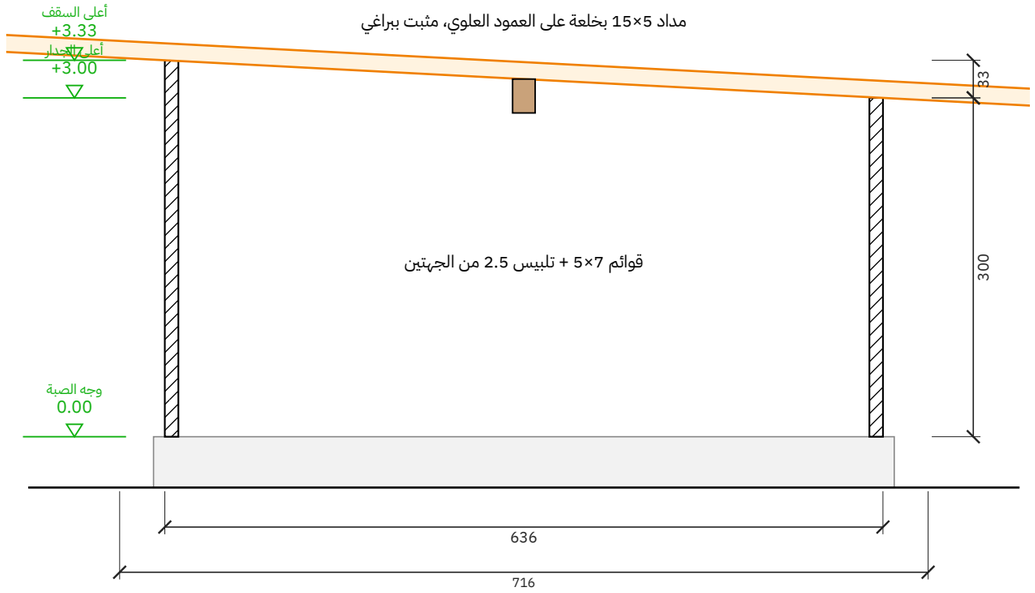

تفصيلة جلوس المداد على العلوي (1:5)

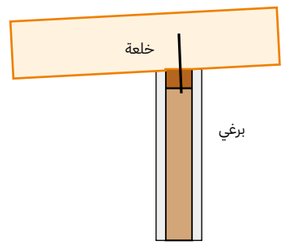

علوي 7×5 على قائم 7×5

المشروع / العميل	عنوان اللوحة	المقياس	التاريخ	رقم اللوحة
مصنع وتد الأخشاب Watad Wood Factory — **كوخ 16.00 × 6.36 م — غرفتين نوم + صالة + حمامين + تراس أمامي 4.00 وخلفي 2.00 عميل — كوخ 16 × 8.5**	**مسقط السقف والقطاع**	**1:50**	**2026-11-10**	**W-05 (5/15)**

جدول مقاسات الأبواب والشبابيك

مقاس الفتحة الصافي في الجدار - الوحدة: سم

الرمز	النوع	العرض (سم)	الارتفاع (سم)	ارتفاع الجلسة (سم)	العدد	الموقع
ب1	باب	100	240	-	1	الخلفية (المدخل)
ب2	باب	85	220	-	1	غرفة الأطفال
ب3	باب	70	210	-	1	حمام الأطفال
ب4	باب	90	220	-	1	غرفة النوم الرئيسية
ب5	باب	70	210	-	1	الحمام الخاص
ز1	باب مزدوج	300	240	-	1	الأمامية (على التراس)
ز1	باب مزدوج	340	240	-	1	الأمامية (على التراس)
ز2	باب	660	260	-	1	الأمامية (على التراس)
ف1	باب	66	220	-	1	خزانة غرفة الأطفال
ف2	باب	80	220	-	1	غرفة الملابس
ش1	شباك	90	140	80	2	الشرقية - الغربية
ش2	شباك	60	50	180	2	الشرقية - الغربية
ش3	شباك	180	150	105	1	الخلفية (المدخل)
ش3	شباك	360	150	105	1	الخلفية (المدخل)

الإجمالي: أبواب 10 - شبابيك 6

جدول المساحات وبيانات المشروع


بيانات المشروع

البند	البيان
المشروع	كوخ 16.00 × 6.36 م — غرفتين نوم + صالة + حمامين + تراس أمامي 4.00 وخلفي 2.00
العميل	عميل — كوخ 16 × 8.5
الموقع	—
الاستخدام	سكني
التاريخ	2026-11-10
نظام البناء	هيكل خشب 5×7 + تلبيس 2.5 سم من الجهتين
السقف	مائل باتجاه واحد 3° — صاج معدني + عزل مائي


جدول المساحات

م	الفراغ	الأبعاد (م)	المساحة (م2)
1	غرفة نوم الأطفال	4.00 × 4.00	16.00
2	حمام الأطفال	2.40 × 2.00	4.80
3	خزانة	0.76 × 2.00	1.52
4	الصالة	7.02 × 4.00	28.08
5	المطبخ والممر	6.72 × 2.00	13.44
6	غرفة ملابس	2.40 × 2.00	4.80
7	حمام خاص	3.00 × 2.00	6.00
8	غرفة النوم الرئيسية	4.50 × 4.00	18.00
	المساحة الصافية الداخلية		92.64
	المساحة الإجمالية المبنية	**16.00 × 6.36**	**101.76**
	التراس الأمامي (خارج مساحة الكوخ)	**16.00 × 4.00**	**64.00**
	التراس الخلفي (خارج مساحة الكوخ)	**16.00 × 2.00**	**32.00**

تأطير جدار جنوب — الطول 1588 سم، الارتفاع 333 سم

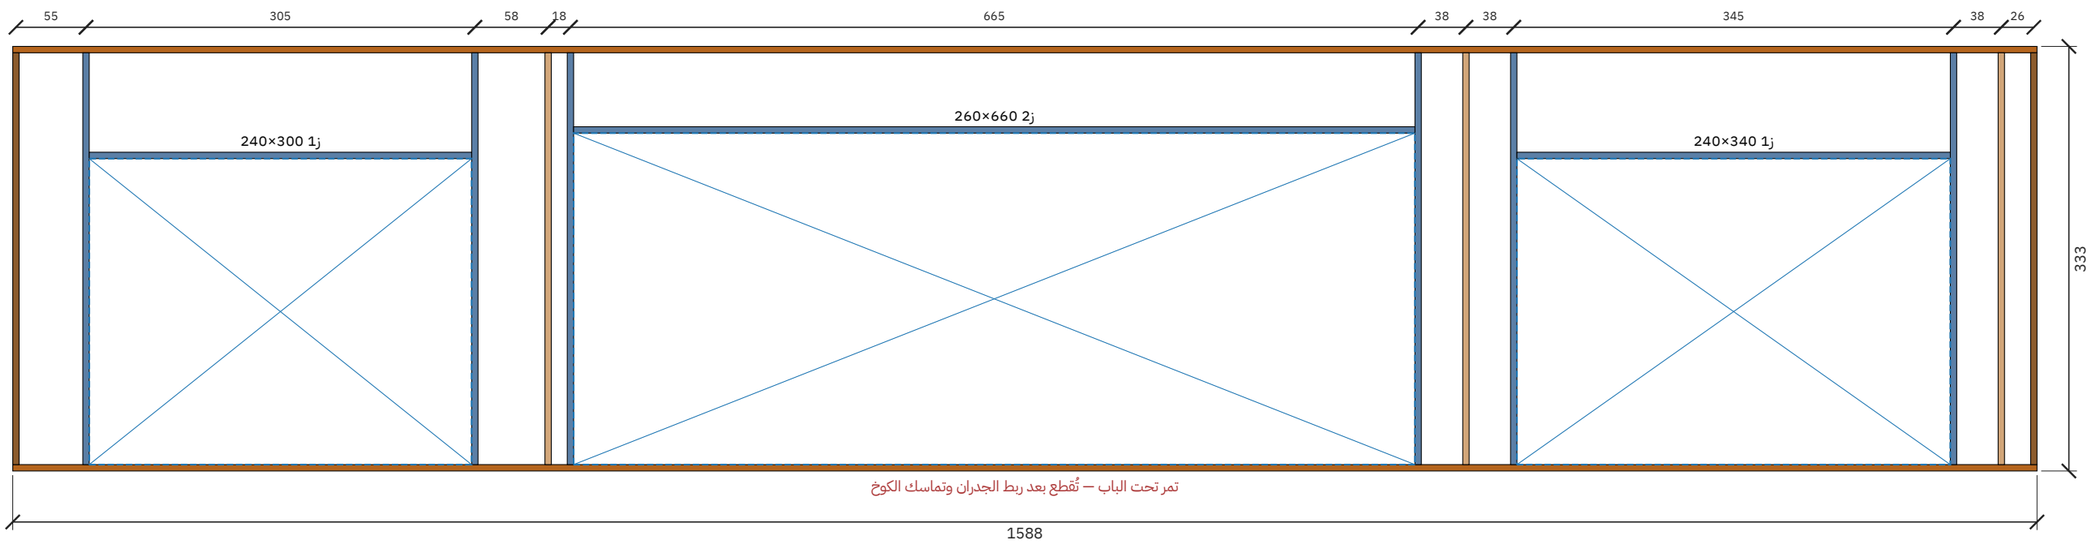

تأطير جدار شرق — الطول 624 سم، الارتفاع 300 سم

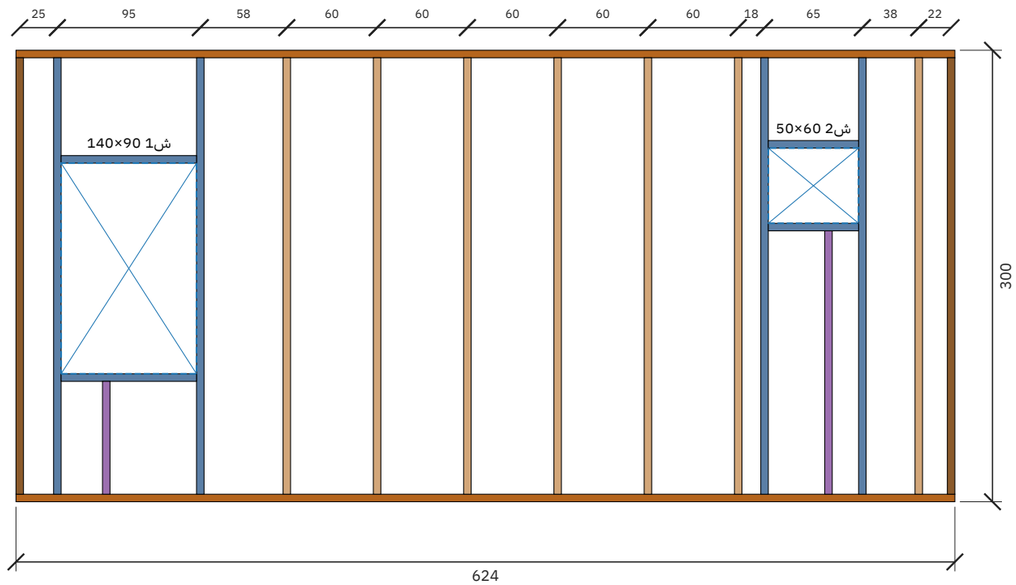


قاعدة سفلية | علوي | عمود | عمود زاوية | جنب فتحة | رأس فتحة | جلسة شباك | عمود قصير


المشروع / العميل	عنوان اللوحة	المقياس	التاريخ	رقم اللوحة
كوخ 16.00 × 6.36 م – غرفتين نوم + صالة + حمامين + تراس أمامي 4.00 وخلفي 2.00 **عميل – كوخ 16 × 8.5**	**لوحات التأطير (للورشة)**	**–**	**2026-11-10**	**W-08 (8/15)**

مصنع وتد الأخشاب
Watad Wood Factory

تأطير جدار شمال — الطول 1588 سم، الارتفاع 300 سم

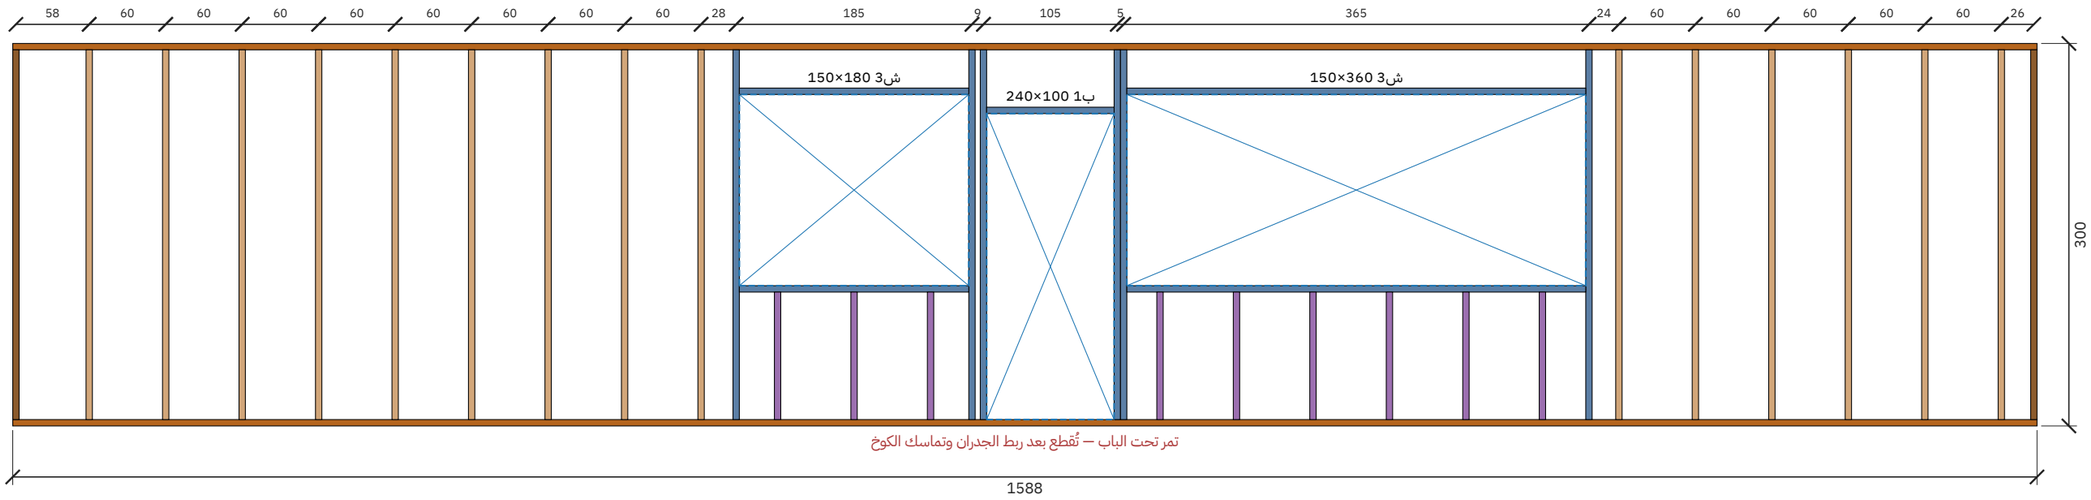


تأطير جدار غرب — الطول 624 سم، الارتفاع 300 سم

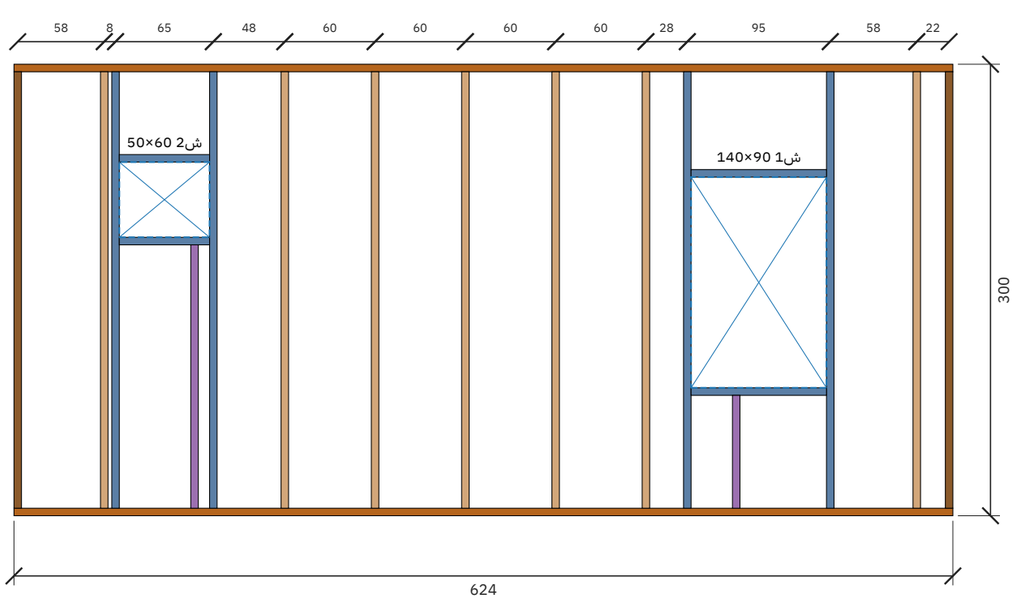


قاعدة سفلية — علوي — عمود — عمود زاوية — جنب فتحة — رأس فتحة — جلسة شباك — عمود قصير

مصنع وتد الأخشاب Watad Wood Factory	المشروع / العميل **كوخ 16.00 × 6.36 م – غرفتين نوم + صالة + حمامين + تراس أمامي 4.00 وخلفي 2.00** **عميل – كوخ 16 × 8.5**	عنوان اللوحة **لوحات التأطير (للورشة)**	المقياس **–**	التاريخ **2026-11-10**	رقم اللوحة **W-09 (9/15)**

تأطير جدار جدار غرفة الأطفال — الصالة — الطول 412 سم، الارتفاع 300 سم (داخلي)

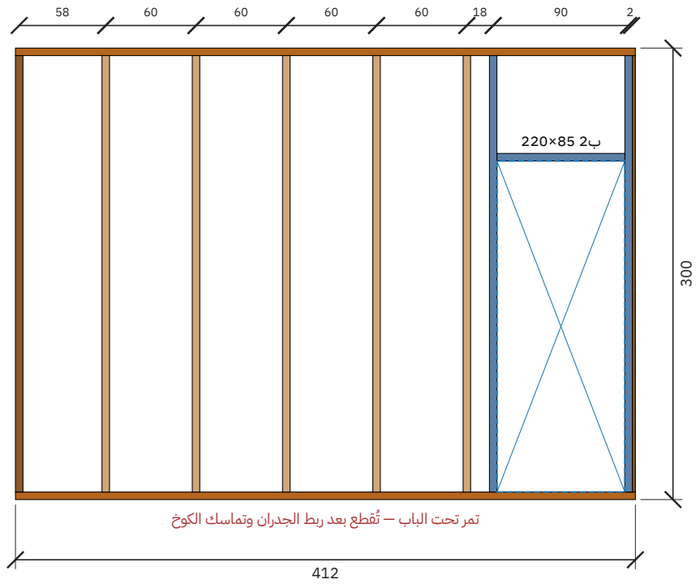


تأطير جدار جدار غرفة الأطفال — الحمام — الطول 412 سم، الارتفاع 300 سم (داخلي)

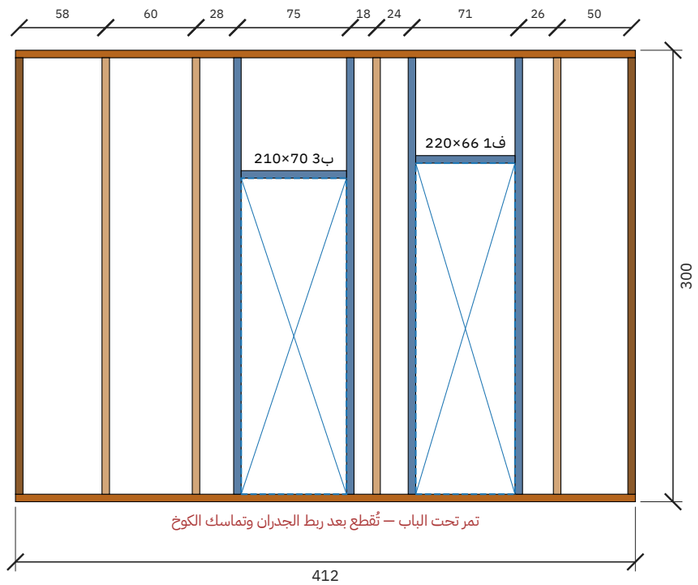


قاعدة سفلية | علوي | عمود | عمود زاوية | جنب فتحة | رأس فتحة | جلسة شباك | عمود قصير

مصنع وتد الأخشاب Watad Wood Factory	المشروع / العميل **كوخ 16.00 × 6.36 م — غرفتين نوم + صالة + حمامين + تراس أمامي 4.00 وخلفي 2.00** **عميل — كوخ 16 × 8.5**	عنوان اللوحة **لوحات التأطير (للورشة)**	المقياس **—**	التاريخ **2026-11-10**	رقم اللوحة **W-10 (10/15)**

تأطير جدار جدار حمام الأطفال — الخزانة — الطول 212 سم، الارتفاع 300 سم (داخلي)

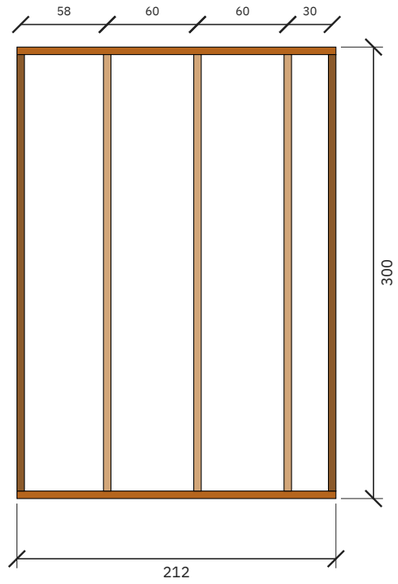


تأطير جدار جدار الخزانة — المطبخ — الطول 212 سم، الارتفاع 300 سم (داخلي)

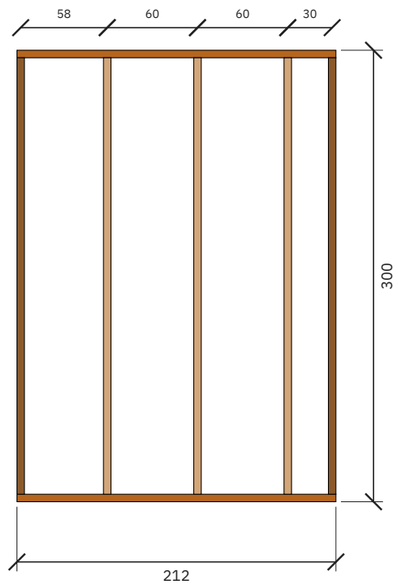


قاعدة سفلية | علوي | عمود | عمود زاوية | جنب فتحة | رأس فتحة | جلسة شباك | عمود قصير

مصنع وتد الأخشاب Watad Wood Factory	المشروع / العميل **كوخ 16.00 × 6.36 م — غرفتين نوم + صالة + حمامين + تراس أمامي 4.00 وخلفي 2.00** **عميل — كوخ 16 × 8.5**	عنوان اللوحة **لوحات التأطير (للورشة)**	المقياس **—**	التاريخ **2026-11-10**	رقم اللوحة **W-11 (11/15)**

تأطير جدار جدار الغرفة الرئيسية — الصالة — الطول 412 سم، الارتفاع 300 سم (داخلي)

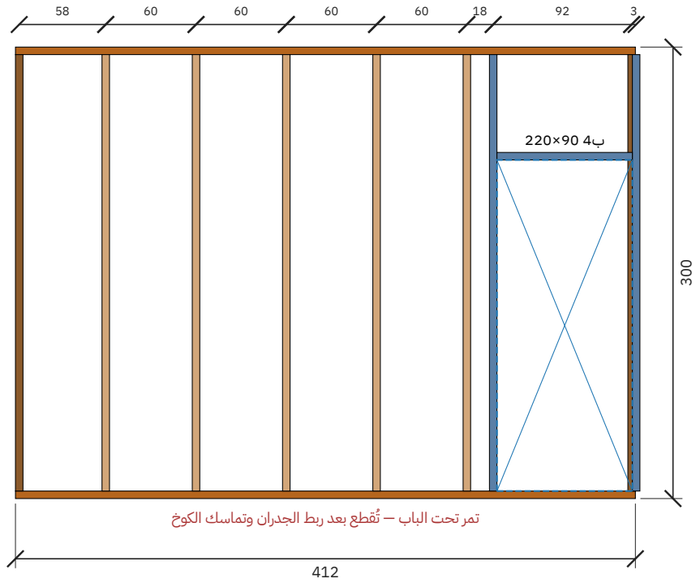


تأطير جدار جدار الغرفة الرئيسية — الملابس والحمام — الطول 564 سم، الارتفاع 300 سم (داخلي)

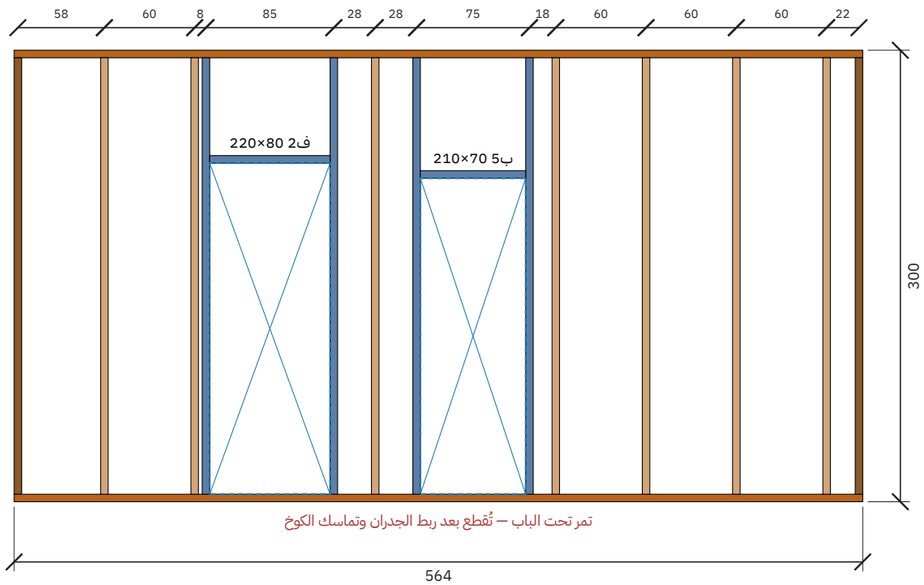


قاعدة سفلية | علوي | عمود | عمود زاوية | جنب فتحة | رأس فتحة | جلسة شباك | عمود قصير

مصنع وتد الأخشاب Watad Wood Factory	المشروع / العميل **كوخ 16.00 × 6.36 م — غرفتين نوم + صالة + حمامين + تراس أمامي 4.00 وخلفي 2.00** **عميل — كوخ 16 × 8.5**	عنوان اللوحة **لوحات التأطير (للورشة)**	المقياس **—**	التاريخ **2026-11-10**	رقم اللوحة **W-12 (12/15)**

تأطير جدار جدار الملابس — الصالة — الطول 212 سم، الارتفاع 300 سم (داخلي)

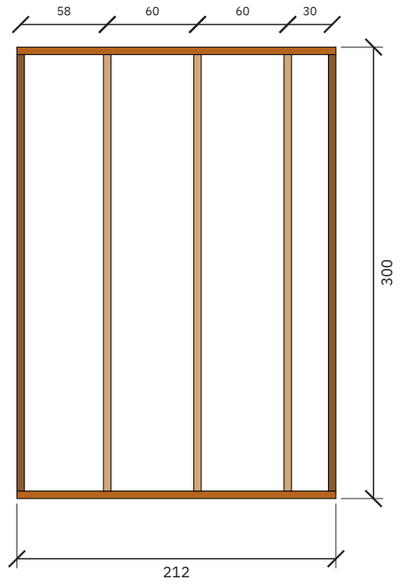

تأطير جدار جدار الملابس — الحمام — الطول 212 سم، الارتفاع 300 سم (داخلي)

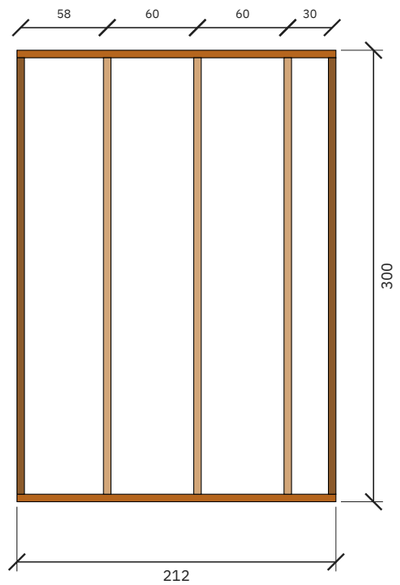

عمود قصير
جلسة شباك
رأس فتحة
جنب فتحة
عمود زاوية
عمود
علوي
قاعدة سفلية

مصنع وتد الأخشاب Watad Wood Factory	المشروع / العميل **كوخ 16.00 × 6.36 م — غرفتين نوم + صالة + حمامين + تراس أمامي 4.00 وخلفي 2.00** **عميل — كوخ 16 × 8.5**	عنوان اللوحة **لوحات التأطير (للورشة)**	المقياس **—**	التاريخ **2026-11-10**	رقم اللوحة **W-13 (13/15)**

جدول الكميات وخطة تقطيع الطبليات

البند	القيمة
الارتفاع المطلوب / المعتمد	300 / 300 سم
السقف	مائل باتجاه واحد 3° — أعلى نقطة 333 سم من وجه الصبة
المدادات 5×15	58 مداد (29 خط × قطعتين موصولة فوق الجسر الحامل بتراكب 60 سم) × حتى 388 سم — من طبلية 480
طبليات الطريقة الأولى (مداد + عمود)	58 طبلية × 480 سم
طبليات الطريقة الثانية (3 أعمدة)	37 طبلية × 320 سم
إجمالي الطبليات 5×22.5	95
إجمالي قطع 5×7	180
قائمة تقطيع 5×7	1588سم×4 | 660سم×1 | 624سم×4 | 564سم×2 | 412سم×6 | 360سم×2 | 340سم×1 | 323سم×11 | 300سم×1
	290سم×110 | 212سم×8 | 180سم×2 | 175سم×2 | 100سم×10 | 90سم×5 | 85سم×1 | 80سم×1 | 75سم×2
ألواح تلبيس 2.5 سم	459 لوح × 400 سم (مجموع الصفوف 1476.8 م، 24 وجه)
أسمنت بورد 12 مم (122×244)	36 لوح (داخل دورات المياه)
العزل	224 لوح فوم صخري 80
الصبة	يجهزها العميل — 20 سم، مفرغة تحت دورات المياه

مراجعة التصميم مقابل قواعد المصنع

النوع	البند	التفاصيل	المقترح
خطأ	ش3 زجاج المطبخ (نص جدار + نص زجاج) — يمين المدخل في شمال	الفتحة تقع على التقاء الجدار جدار الملابس — الصالة (عند 564 سم) — الباب يصطدم بالجدار ولا يوجد مكان لجنب الإطار 7×5.	تُبعد حافة الفتحة 11 سم على الأقل عن محور الجدار الملتقي، أو يُعاد توزيع الجدران الداخلية.
خطأ	ب2 غرفة الأطفال في جدار غرفة الأطفال — الصالة	الفتحة ملاصقة لطرف الجدار — ما فيه مكان لإطار 7×5.	تُزاح الفتحة 10 سم على الأقل عن الزاوية.
خطأ	ف1 خزانة غرفة الأطفال في جدار غرفة الأطفال — الحمام	الفتحة تقع على التقاء الجدار جدار الخزانة — المطبخ (عند 340 سم) — الباب يصطدم بالجدار ولا يوجد مكان لجنب الإطار 7×5.	تُبعد حافة الفتحة 11 سم على الأقل عن محور الجدار الملتقي، أو يُعاد توزيع الجدران الداخلية.
خطأ	ب4 غرفة النوم الرئيسية في جدار الغرفة الرئيسية — الصالة	الفتحة ملاصقة لطرف الجدار — ما فيه مكان لإطار 7×5.	تُزاح الفتحة 10 سم على الأقل عن الزاوية.
ملاحظة	بحر المدادات	أطول بحر بدون جدار داخلي يحمل المداد: جهة أ: 636 سم. يحتاج رقم المصنع لأقصى بحر مسموح لتحديد المدادات اللي تُقوّى 20×5.	
ملاحظة	الصبة والدرج	ارتفاع الصبة 45 سم ← 3 درجة بقائمة 15.0 سم.	
ملاحظة	مناسيب رؤوس الفتحات	رؤوس الأبواب والشبابيك على مناسيب مختلفة: 210، 220، 230، 240، 255، 260 سم.	
تنبيه	ميل سقف خفيف (بموافقة المصنع)	ميل 3° أقل من 20° — يصرّف باتجاه واحد بس يحتاج تغطية صاج معدني (مو قرميد) وعزل مائي تحت الصاج ووصلات مختومة.	صاج معدني بطول واحد من الحافة العالية للواطية بدون وصلات عرضية.
سؤال	يحتاج تأكيد	أقصى بحر للمداد بدون جدار داخلي قبل إضافة تقوية 7×5 (مداد 20×5)؟	
سؤال	يحتاج تأكيد	التغطية الصافية للوح التلبيس بعد التعشيق (مستنتجة مؤقتاً 18.67 سم من 280/15)؟	
سؤال	يحتاج تأكيد	هل يوضع أعمدة قصيرة فوق رأس الشباك/الباب إلى العلوي؟	
سؤال	يحتاج تأكيد	مكان الوصلة في القاعدة والعلوي إذا الجدار أطول من الطبلية؟	