
 


المنظور ثلاثي الأبعاد والمواد

النمط: جوزي غامق + إطارات سوداء — رندر واقعي بخامات حقيقية

جدول المواد والألوان

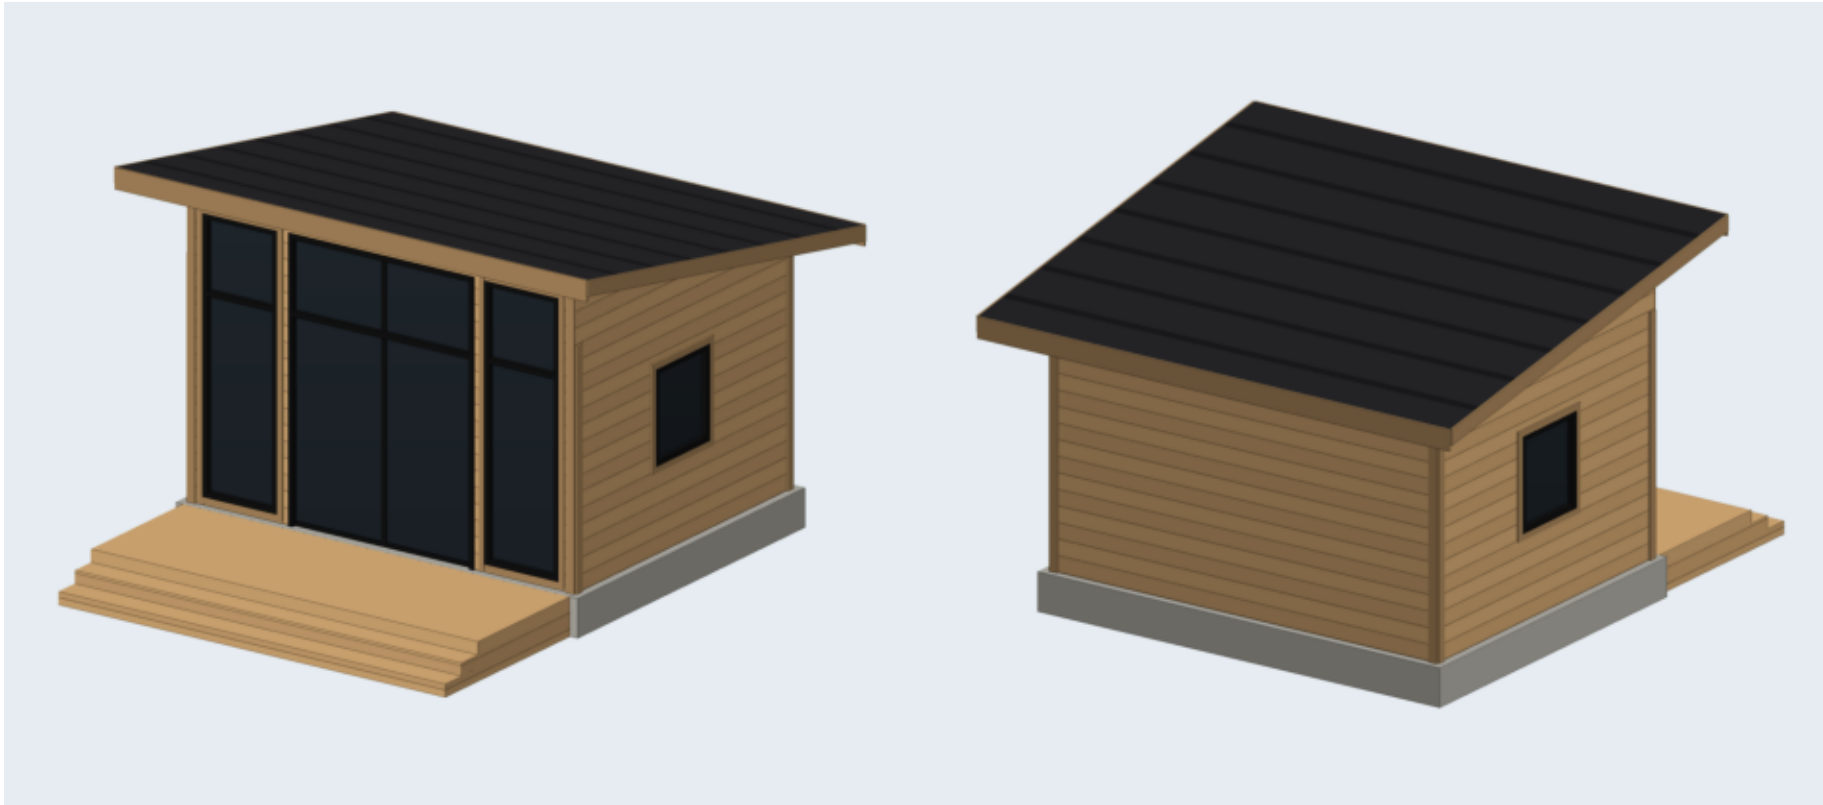

الخشب / الصبغة

خشب طبيعي فاتح (بدون صبغة)



القرميد

قرميد رمادي غامق



الزجاج

زجاج عاكس غامق



إطارات الشبابيك والأبواب

إطار ألومنيوم أسود



الكنار والزوايا

نفس الصبغة أعمق درجة



الصبغة

خرسانة 45 سم


الدريزين: ألواح أفقية متقاربة (عصري)

تقسيم الشبابيك: بدون | الباب الرئيسي: سحب زجاج


أنواع الدريزين المعتمدة (من مشاريع المصنع)



قوائم رأسية متقاربة (صورة 1)

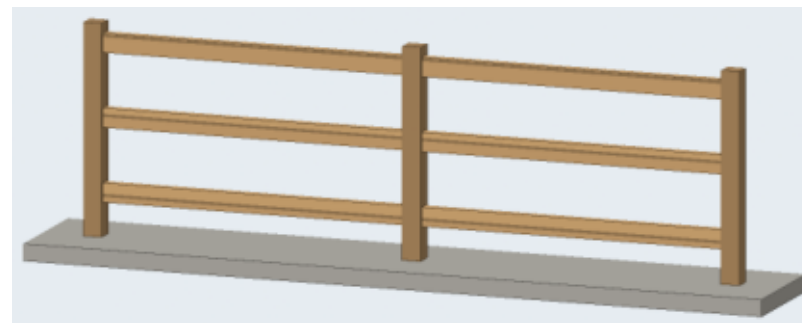

3 مربيع أفقية (صورة 2)

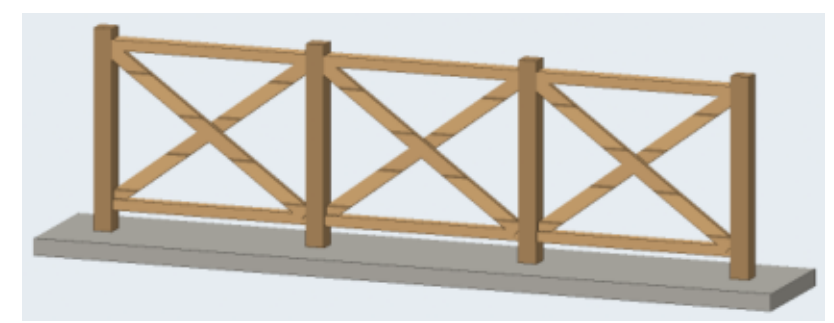

تقاطع X (صورة 5)

رقم اللوحة

W-01 (1/11)

التاريخ

2026-10-06

المقياس

1:50

عنوان اللوحة

المنظور والمواد

المشروع / العميل


مجلس 5x4 بواجهة زجاج
عميل — مجلس

مصنع وتد الأخشاب


Watad Wood Factory



المسقط الأفقي مع الفرش
الأبعاد بالسنتيمتر - الجدران: قوائم 5×7 + تليس 2.5 من الجهتين (12 سم)

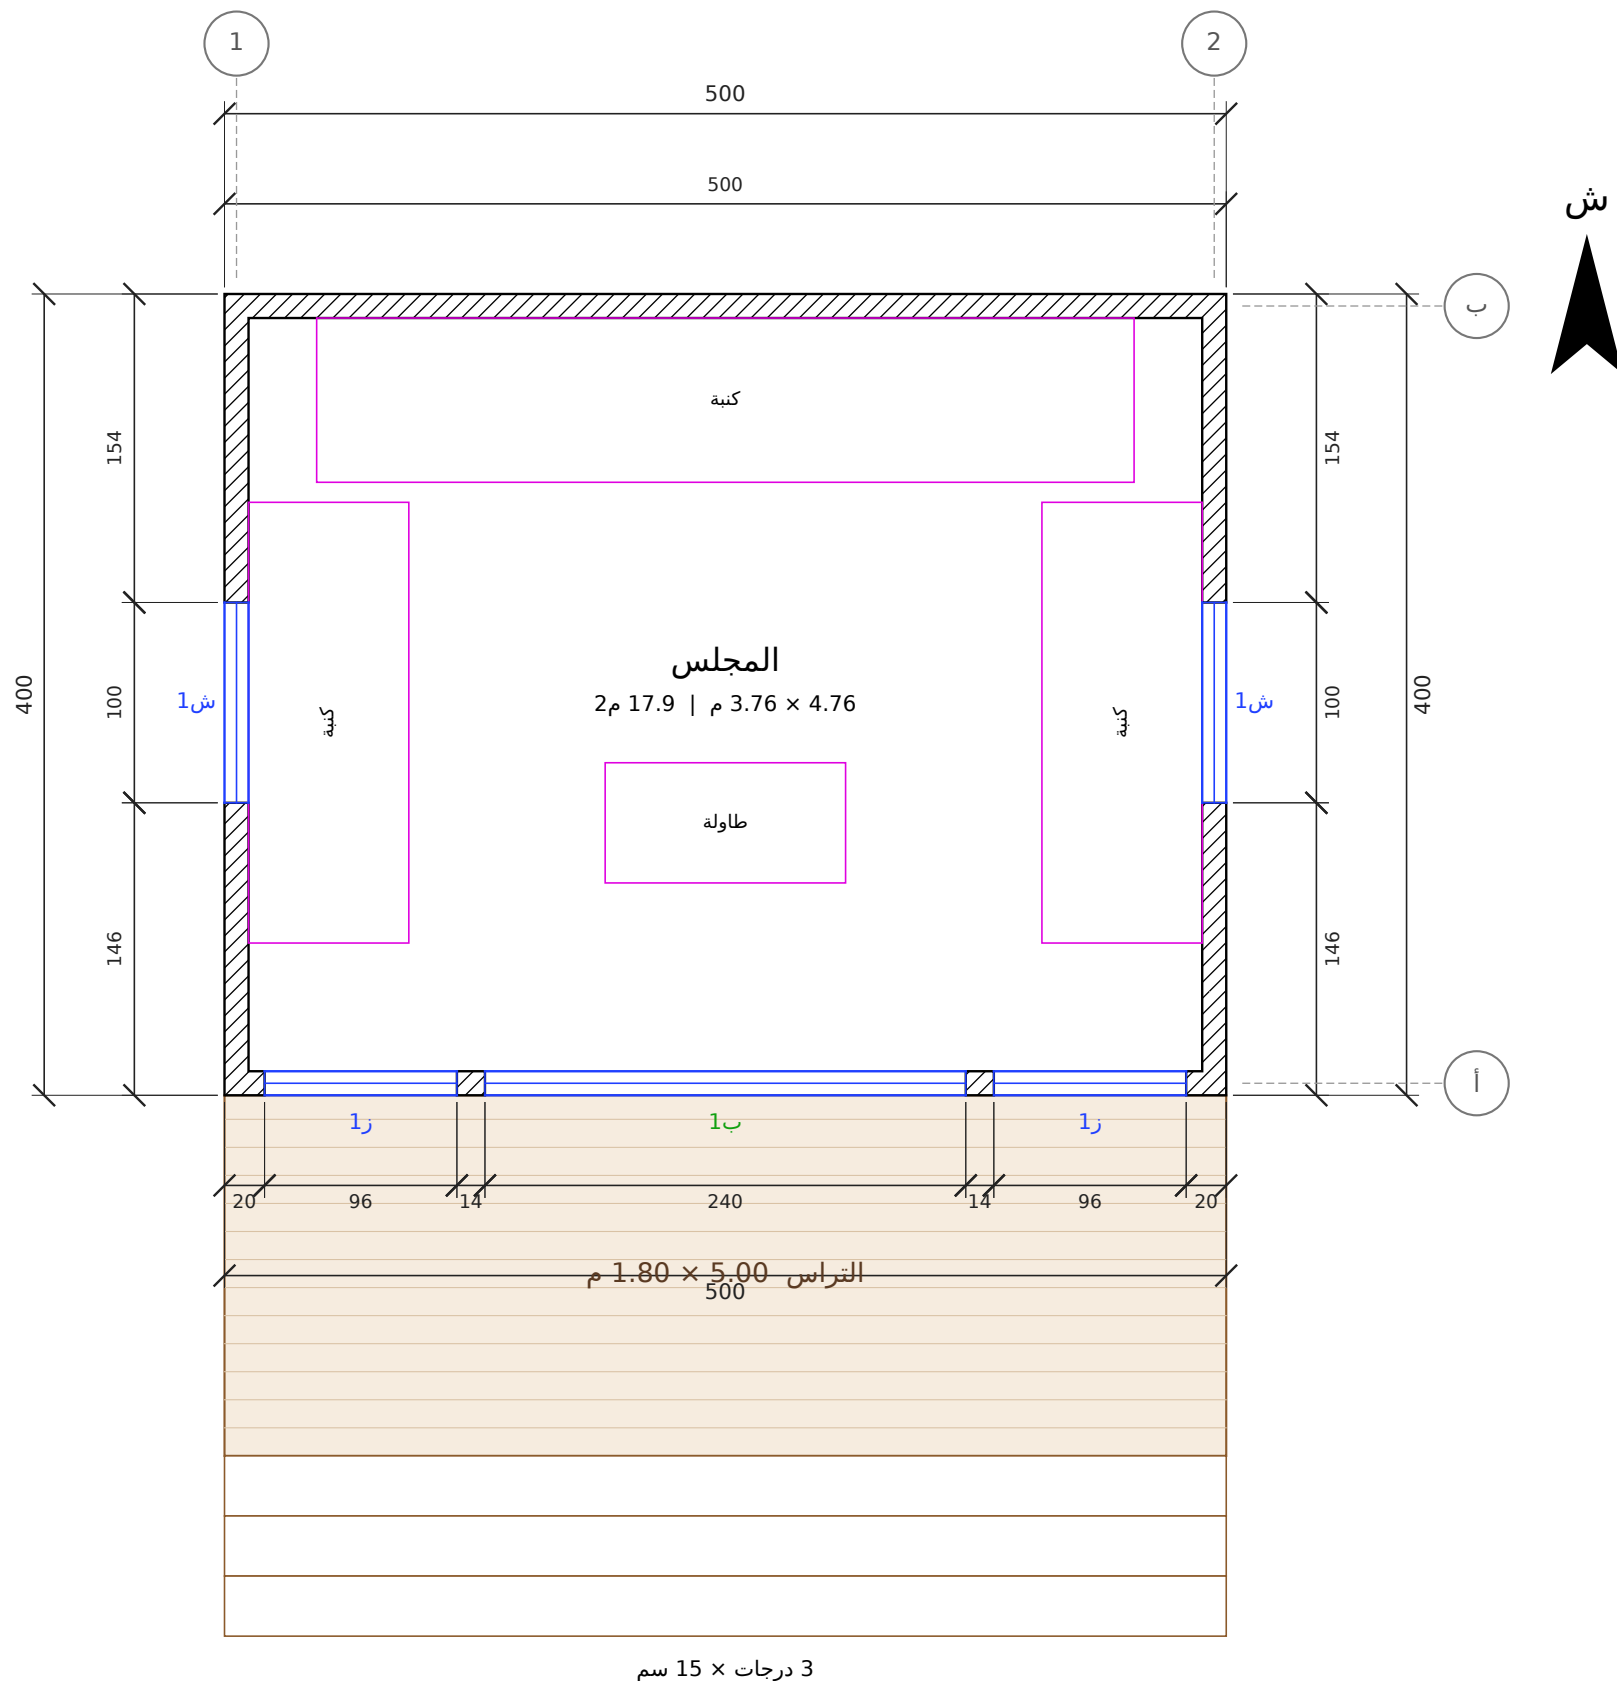


رقم اللوحة	التاريخ	المقياس	عنوان اللوحة	المشروع / العميل	مصنع وتد الأخشاب Watad Wood Factory
W-02 (2/11)	2026-10-06	1:50	المسقط الأفقي	مجلس 5×4 بواجهة زجاج عميل — مجلس	

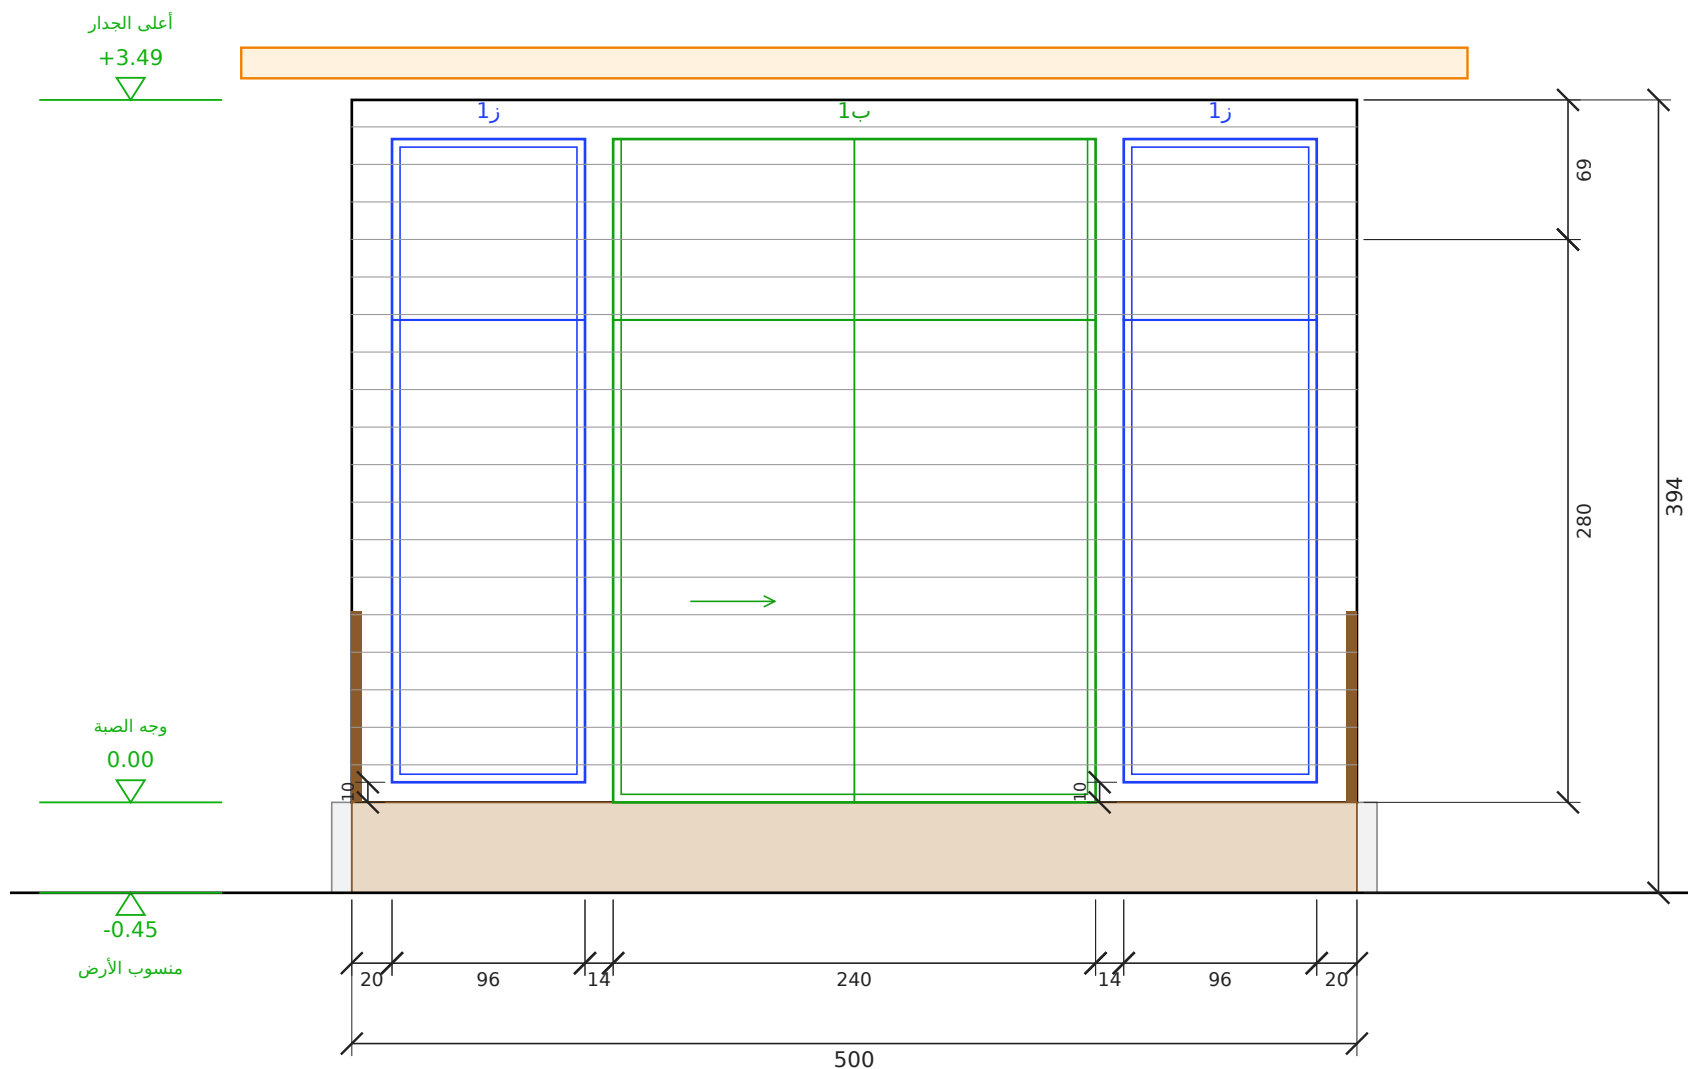

الواجهة الأمامية (زجاج)


مقياس 1:50 | الوحدة: سم

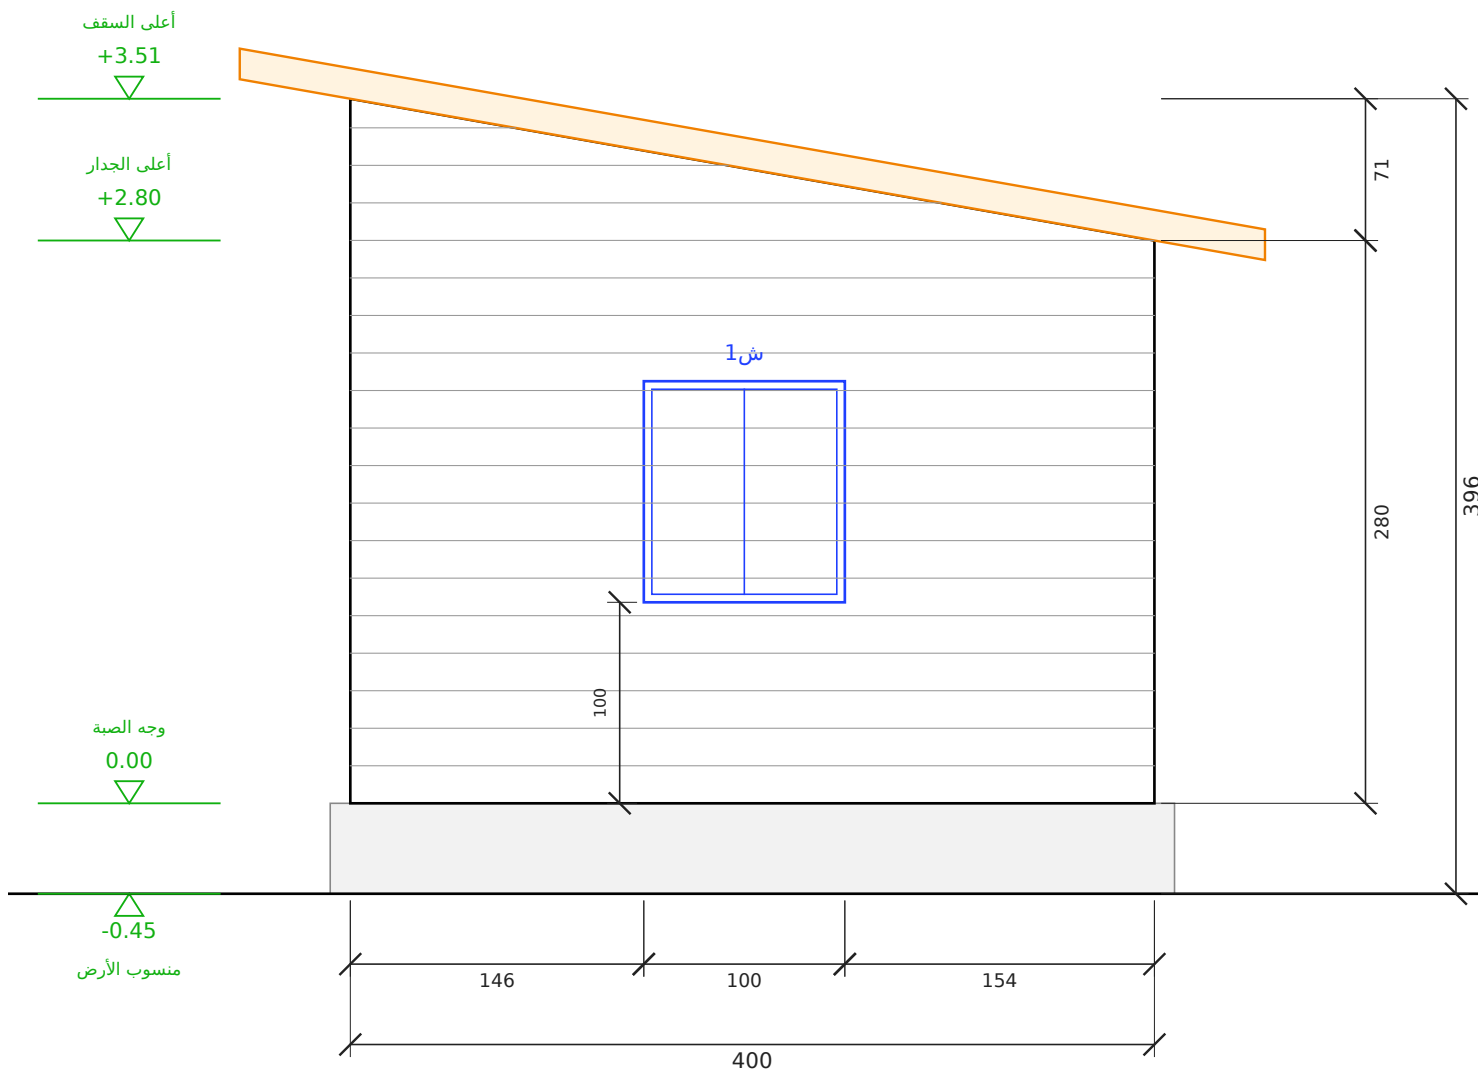

الواجهة الشرقية


مقياس 1:50 | الوحدة: سم

رقم اللوحة	التاريخ	المقياس	عنوان اللوحة	المشروع / العميل	مصنع وتد الأخشاب Watad Wood Factory
W-03 (3/11)	2026-10-06	1:50	الواجهة الأمامية (زجاج) والواجهة الشرقية	مجلس 5x4 بواجهة زجاج عميل - مجلس	

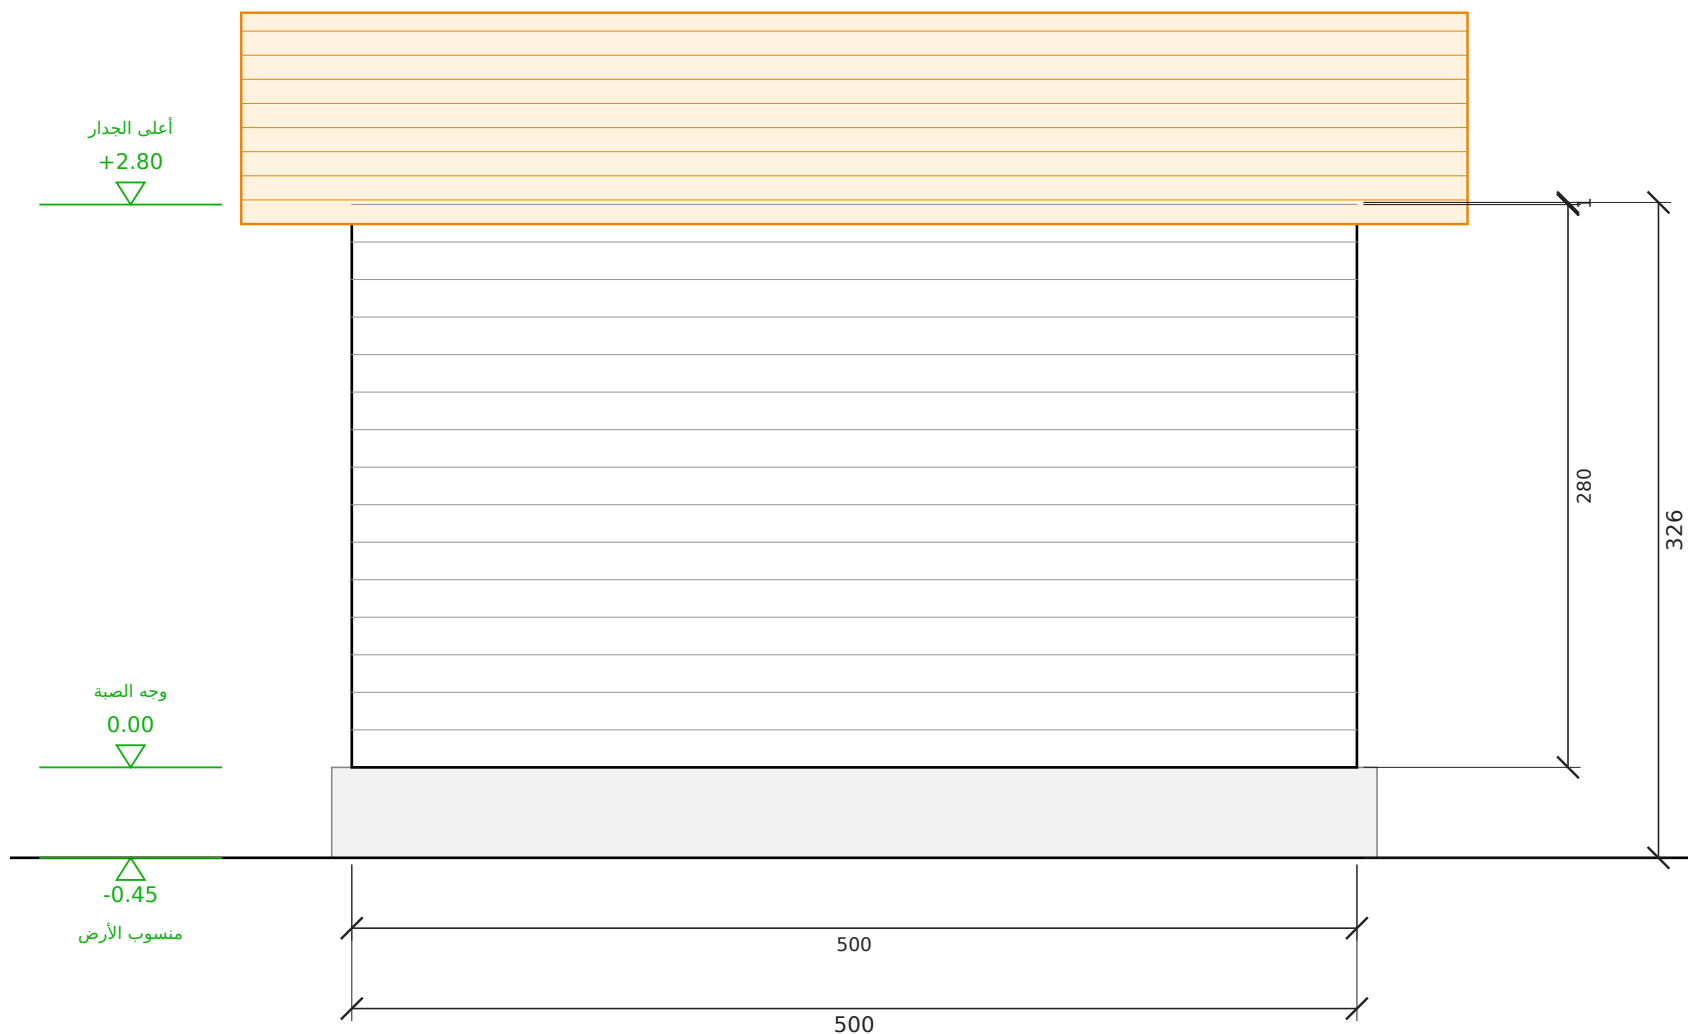

الواجهة الخلفية

مقياس 1:50 | الوحدة: سم

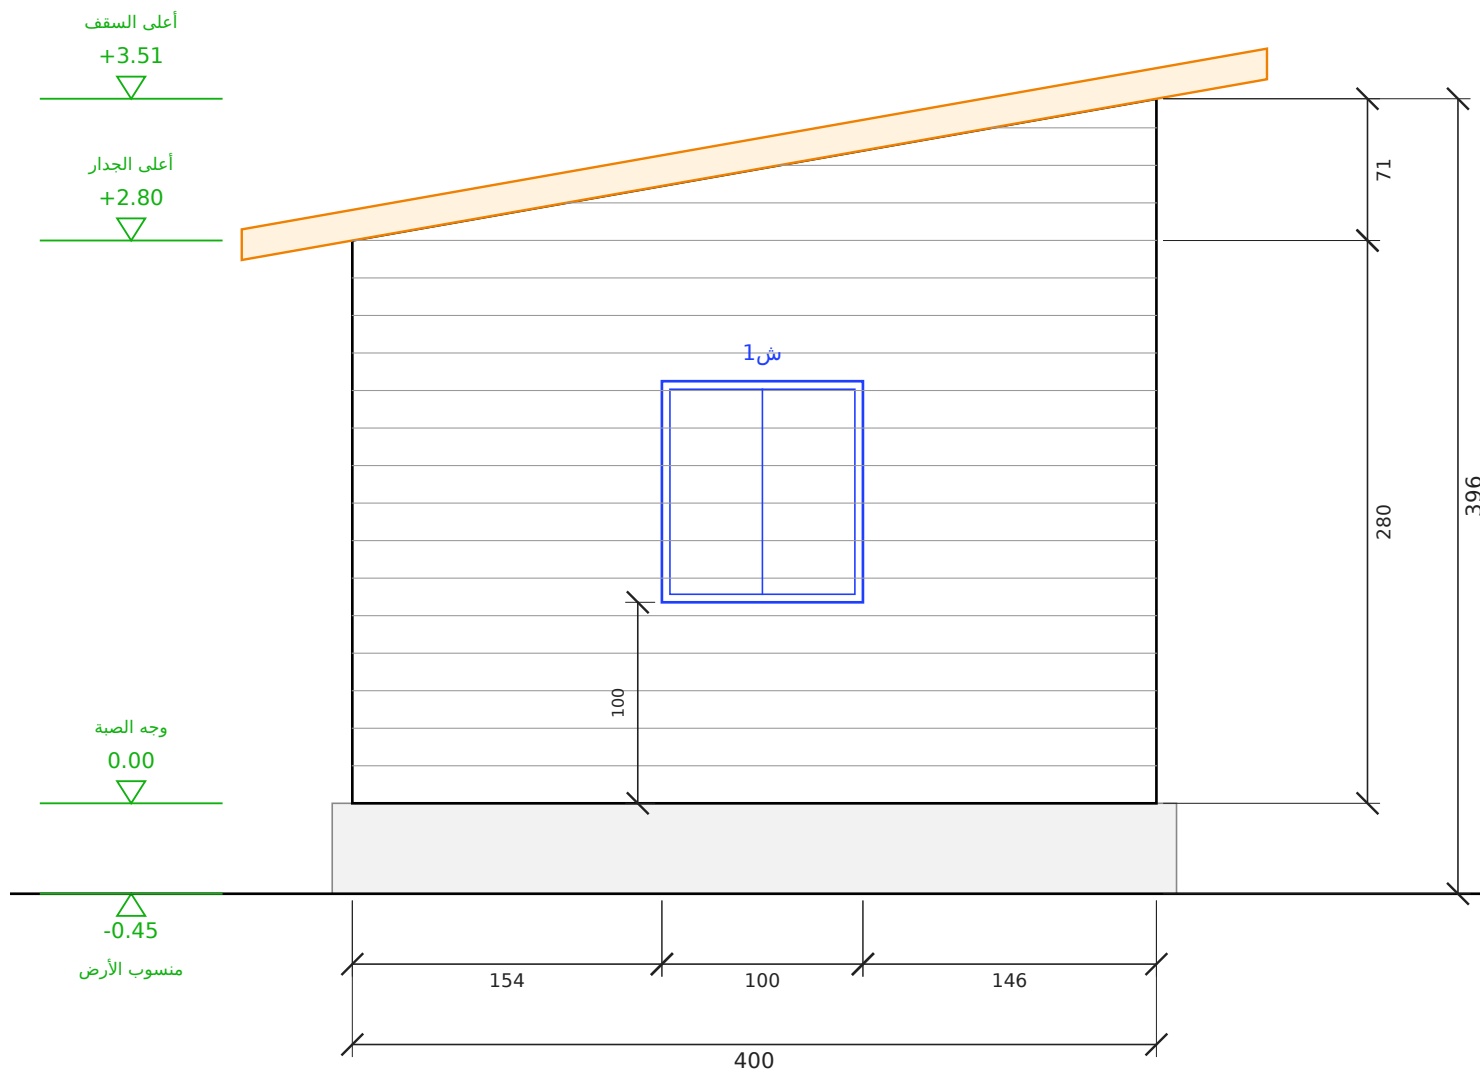


الواجهة الغربية


مقياس 1:50 | الوحدة: سم

رقم اللوحة	التاريخ	المقياس	عنوان اللوحة	المشروع / العميل	مصنع وتد الأخشاب Watad Wood Factory
W-04 (4/11)	2026-10-06	1:50	الواجهة الخلفية والواجهة الغربية	مجلس 5x4 بواجهة زجاج عميل - مجلس	


مسقط السقف (مائل باتجاه واحد)
رفر 55 سم من كل جهة | مقياس 1:50

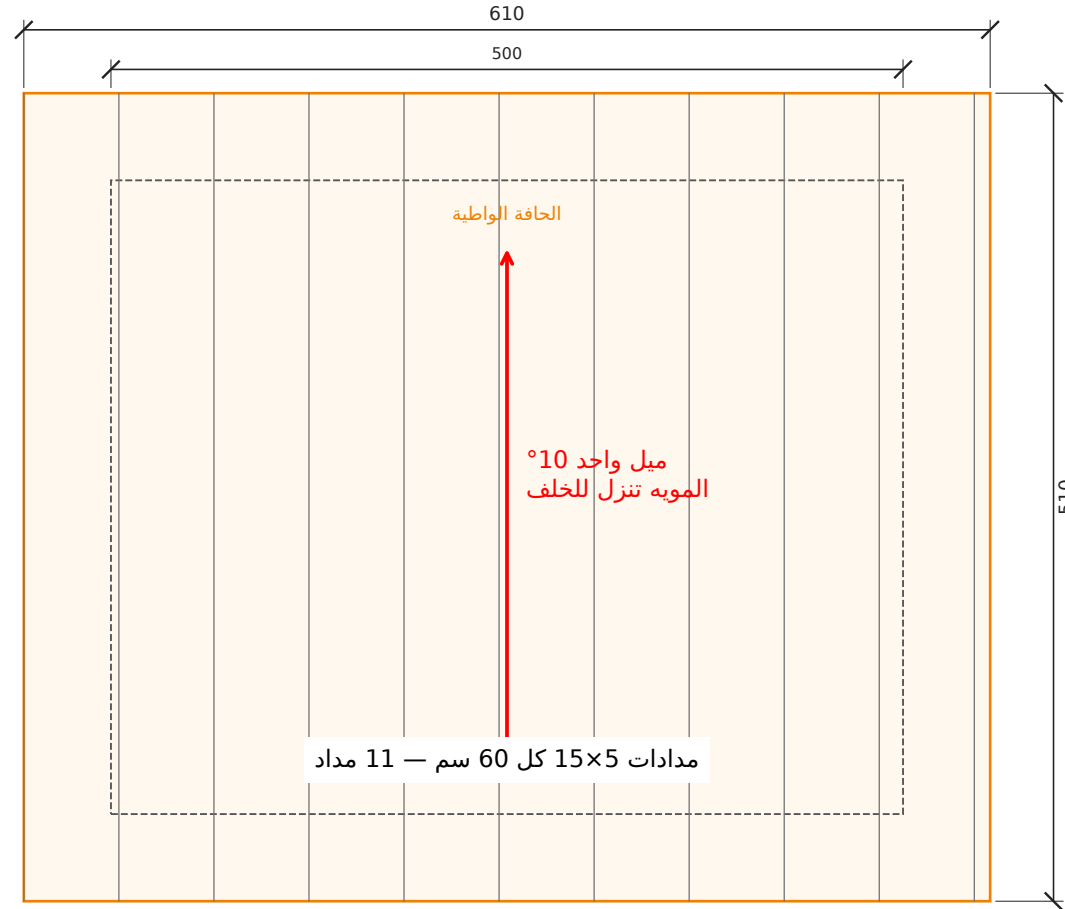

قطاع عرضي أ-أ
مقياس 1:50 | الوحدة: سم

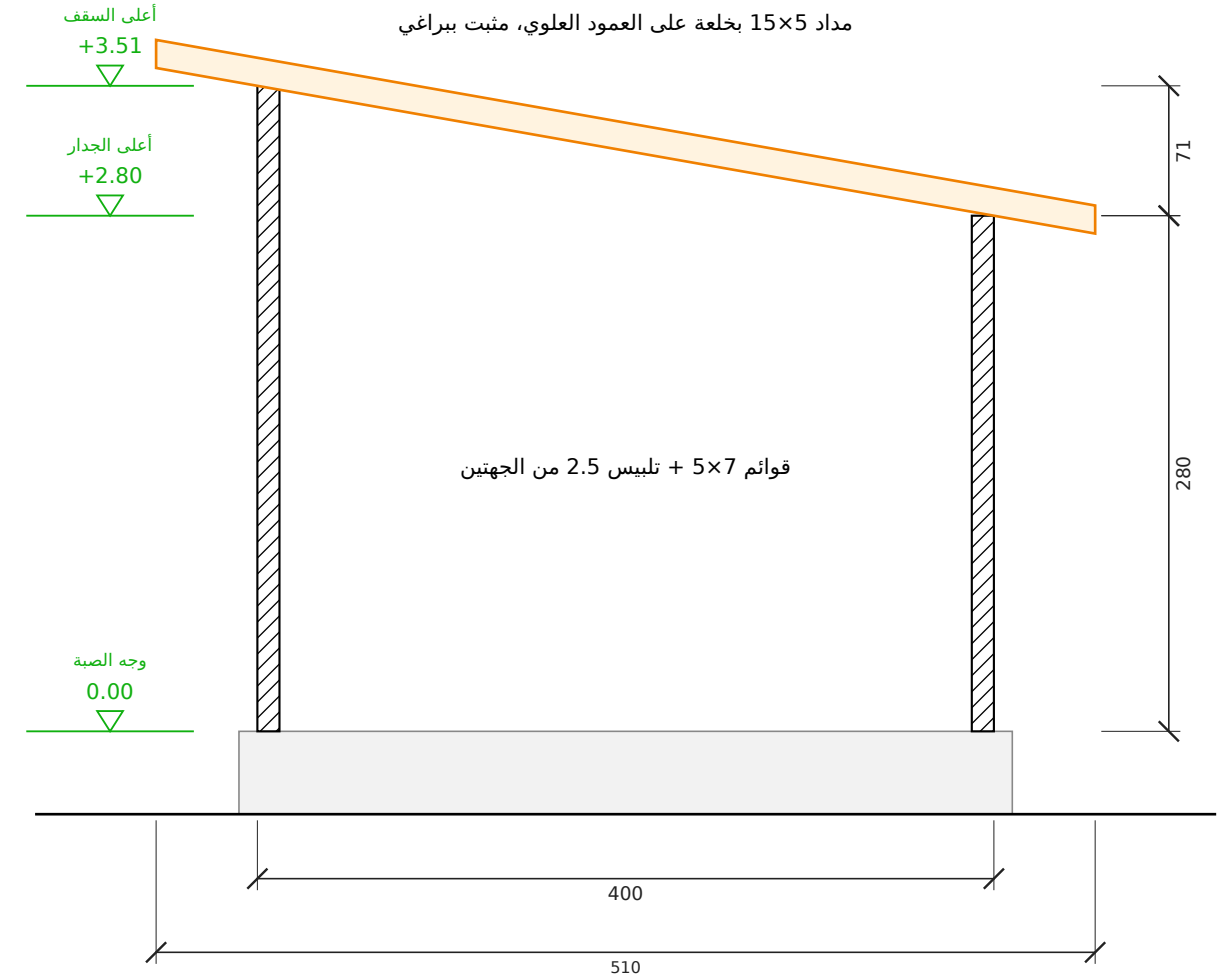

تفصيلة جلوس المداد على العلوي (1:5)

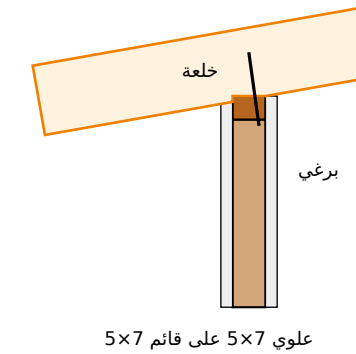

رقم اللوحة

W-05 (5/11)

التاريخ

2026-10-06

المقياس

1:50

عنوان اللوحة

مسقط السقف والقطاع

المشروع / العميل

مجلس 5x4 بواجهة زجاج
عميل — مجلس

مصنع وتد الأخشاب
Watad Wood Factory



جدول مقاسات الأبواب والشبابيك
مقاس الفتحة الصافي في الجدار - الوحدة: سم

الرمز	النوع	العرض (سم)	الارتفاع (سم)	ارتفاع الجلسة (سم)	العدد	الموقع
ب1	باب	240	330	-	1	الأمامية (زجاج)
ر1	شباك	96	320	10	2	الأمامية (زجاج) 2
ش1	شباك	100	110	100	2	الشرقية - الغربية

الإجمالي: أبواب 1 - شبابيك 4

جدول المساحات وبيانات المشروع والتسعير

جدول المساحات

م	الفراغ	الأبعاد (م)	المساحة (م2)
1	المجلس	4.76 × 3.76	17.90
	المساحة الصافية الداخلية		17.90
	التراس المسقوف (مجاناً)	5.00 × 1.80	9.00
	المساحة الإجمالية المبنية	5.00 × 4.00	20.00

بيانات المشروع

البند	البيان
المشروع	مجلس 5×4 بواجهة زجاج
العميل	عميل — مجلس
الموقع	—
الاستخدام	مجلس
التاريخ	2026-10-06
نظام البناء	هيكل خشب 5×7 + تليس 2.5 سم من الجهتين
السقف	مائل باتجاه واحد 10° — قرميد معدني


التسعير

البند	القيمة
المساحة المبنية (م2)	20.00
سعر المتر المربع	1,096 ريال
الإجمالي	21,920 ريال


ملاحظات:

- السعر للمساحة المبنية حسب المخطط المعتمد.
- الصبة والتמידات الخارجية على العميل ما لم يُذكر غير ذلك.

تأطير جدار جنوب — الطول 488 سم، الارتفاع 351 سم

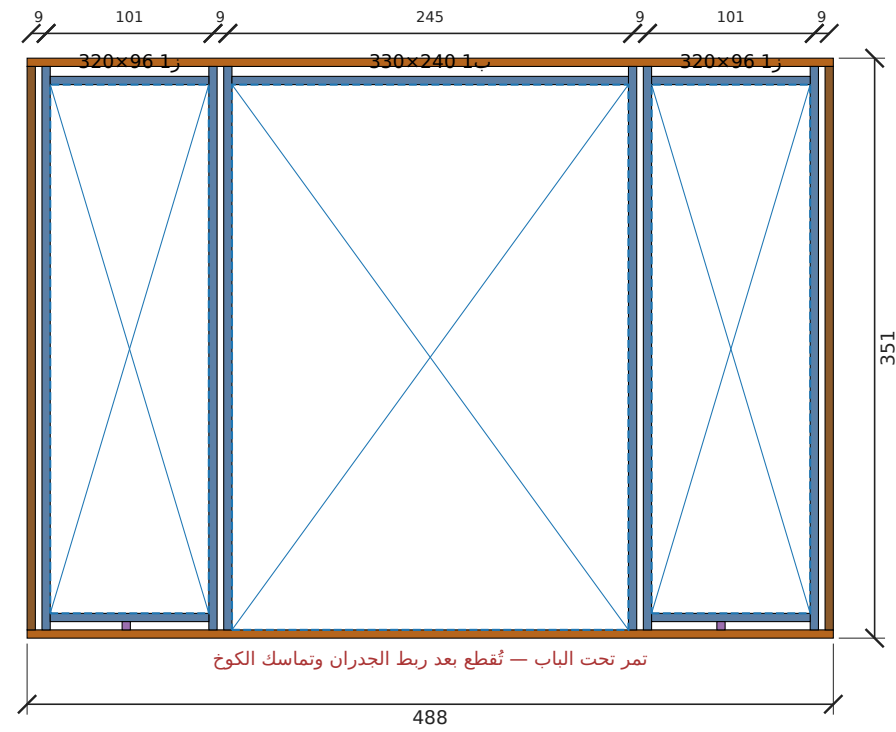


تأطير جدار شرق — الطول 388 سم، الارتفاع 280 سم

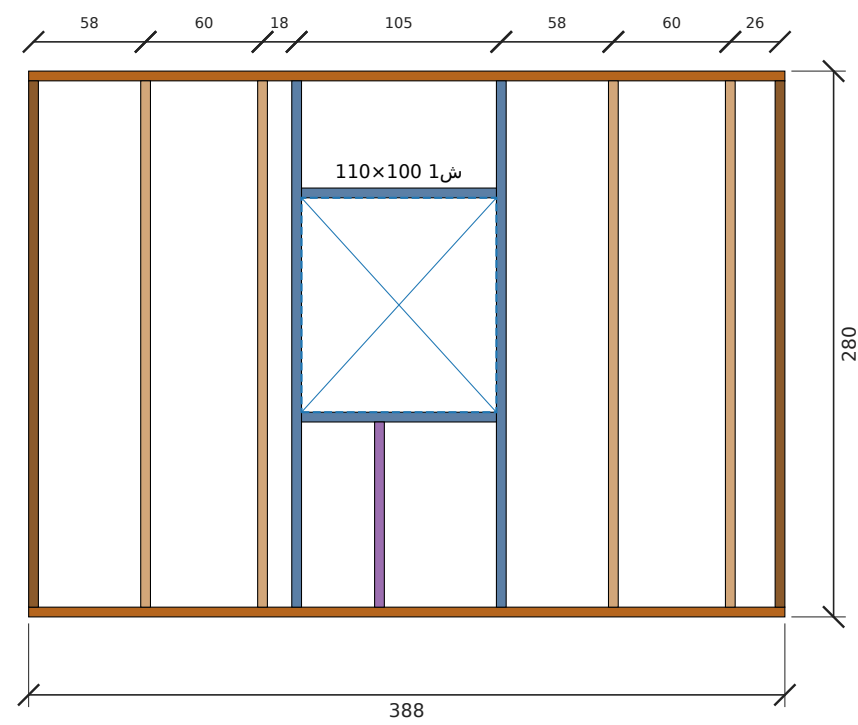


عمود قصير جلسة شباك رأس فتحة جنب فتحة عمود زاوية عمود علوي قاعدة سفلية

رقم اللوحة W-08 (8/11)	التاريخ 2026-10-06	المقياس —	عنوان اللوحة لوحات التأطير (للورشة)	المشروع / العمل مجلس 5x4 بواجهة زجاج عميل – مجلس	مصنع وتد الأخشاب Watad Wood Factory 
---	---	--------------------------------	--	---	---

تأطير جدار شمال — الطول 488 سم، الارتفاع 280 سم

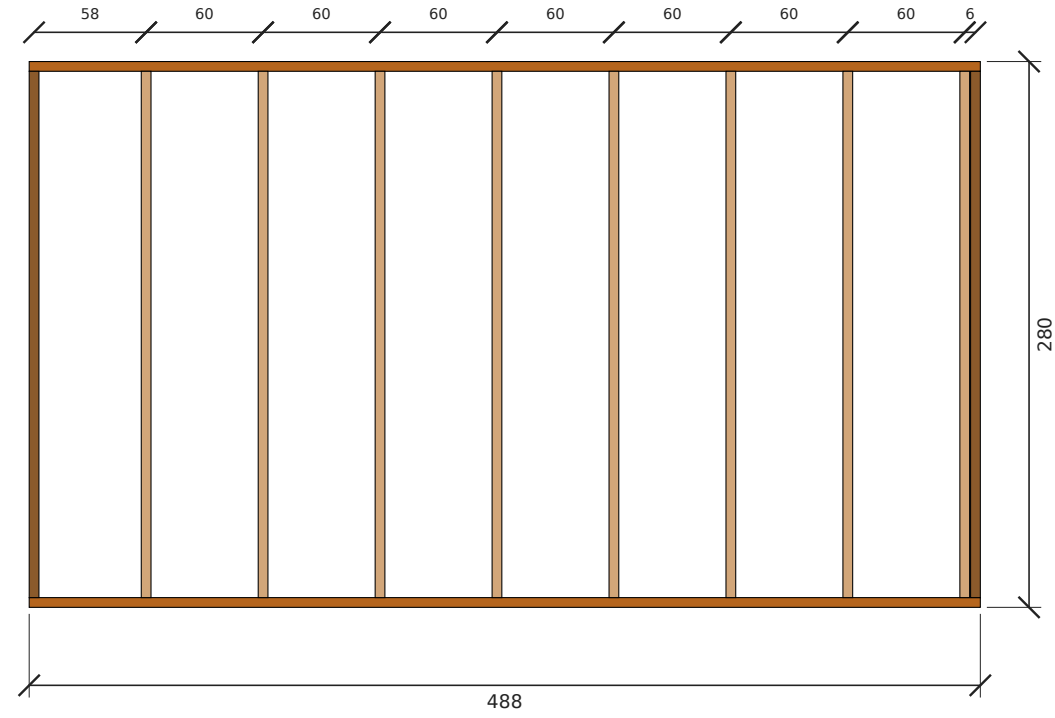

تأطير جدار غرب — الطول 388 سم، الارتفاع 280 سم

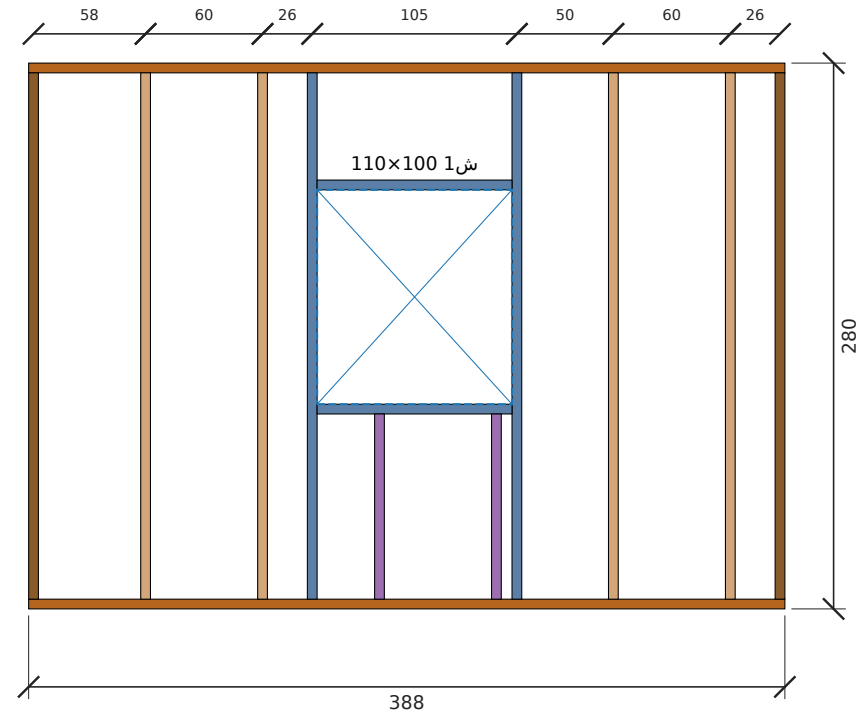

قاعدة سفلية علوي عمود عمود زاوية جنب فتحة رأس فتحة جلسة شباك عمود قصير

رقم اللوحة

W-09 (9/11)

التاريخ

2026-10-06

المقياس

—

عنوان اللوحة

لوحات التأطير (للورشة)

المشروع / العميل

مجلس 5x4 بواجهة زجاج
عميل — مجلس

مصنع وتد الأخشاب
Watad Wood Factory



جدول الكميات وخطة تقطيع الطبلیات

البند	القيمة
الارتفاع المطلوب / المعتمد	280 / 280 سم
السقف	جملون 10° — قمة 350 سم من وجه الصبة
المدادات 15×5	11 مداد (11 لكل جهة) × 518 سم — من طبلية 520
طبلیات الطريقة الأولى (مداد + عمود)	11 طبلية × 520 سم
طبلیات الطريقة الثانية (3 أعمدة)	10 طبلية × 320 سم
طبلیات الطريقة الثانية (طويلة)	2 طبلية × 520 سم
إجمالي الطبلیات 22.5×5	23
إجمالي قطع 5×7	56
قائمة تقطيع 5×7	488سم×4 388سم×4 341سم×8 270سم×26 240سم×1 100سم×4 96سم×4 95سم×3 5سم×2
ألواح تلبیس 2.5 سم	97 لوح × 400 سم (مجموع الصفوف 381.1 م، 8 وجه)
أسمنت بورد 12 مم (244×122)	0 لوح (داخل دورات المياه)
العزل	بدون (غير مطلوب)
الصبة	یجهزها العميل — 20 سم، مفرغة تحت دورات المياه

مراجعة التصميم مقابل قواعد المصنع

النوع	البند	التفاصيل	المقترح
ملاحظة	بحر المدادات	أطول بحر بدون جدار داخلي يحمل المداد: جهة أ: 400 سم. يحتاج رقم المصنع لأقصى بحر مسموح لتحديد المدادات اللي تُقوَّى 5×20.	
ملاحظة	الصبة والدرج	ارتفاع الصبة 45 سم ← 3 درجة بقائمة 15.0 سم.	
ملاحظة	مناسيب رؤوس الفتحات	رؤوس الأبواب والشبابيك على مناسيب مختلفة: 210، 330 سم.	
تنبيه	ميل سقف خفيف (بموافقة المصنع)	ميل 10° أقل من 20° — يصرّف باتجاه واحد بس يحتاج تغطية صاج معدني (مو قرميد) وعزل مائي تحت الصاج ووصلات مختومة.	صاج معدني بطول واحد من الحافة العالية للواطية بدون وصلات عرضية.
سؤال	يحتاج تأكيد	أقصى بحر للمداد بدون جدار داخلي قبل إضافة تقوية 5×7 (مداد 5×20)؟	
سؤال	يحتاج تأكيد	التغطية الصافية للوح التليس بعد التعشيق (مستنتجة مؤقتاً 18.67 سم من 280/15)؟	
سؤال	يحتاج تأكيد	هل بوضع أعمدة قصيرة فوق رأس الشباك/الباب إلى العلوي؟	
سؤال	يحتاج تأكيد	مكان الوصلة في القاعدة والعلوي إذا الجدار أطول من الطيلية؟	