



المسقط الأفقي مع الفرش
الأبعاد بالسنتيمتر - الجدران: قوائم 5×7 + تليس 2.5 من الجهتين (12 سم)

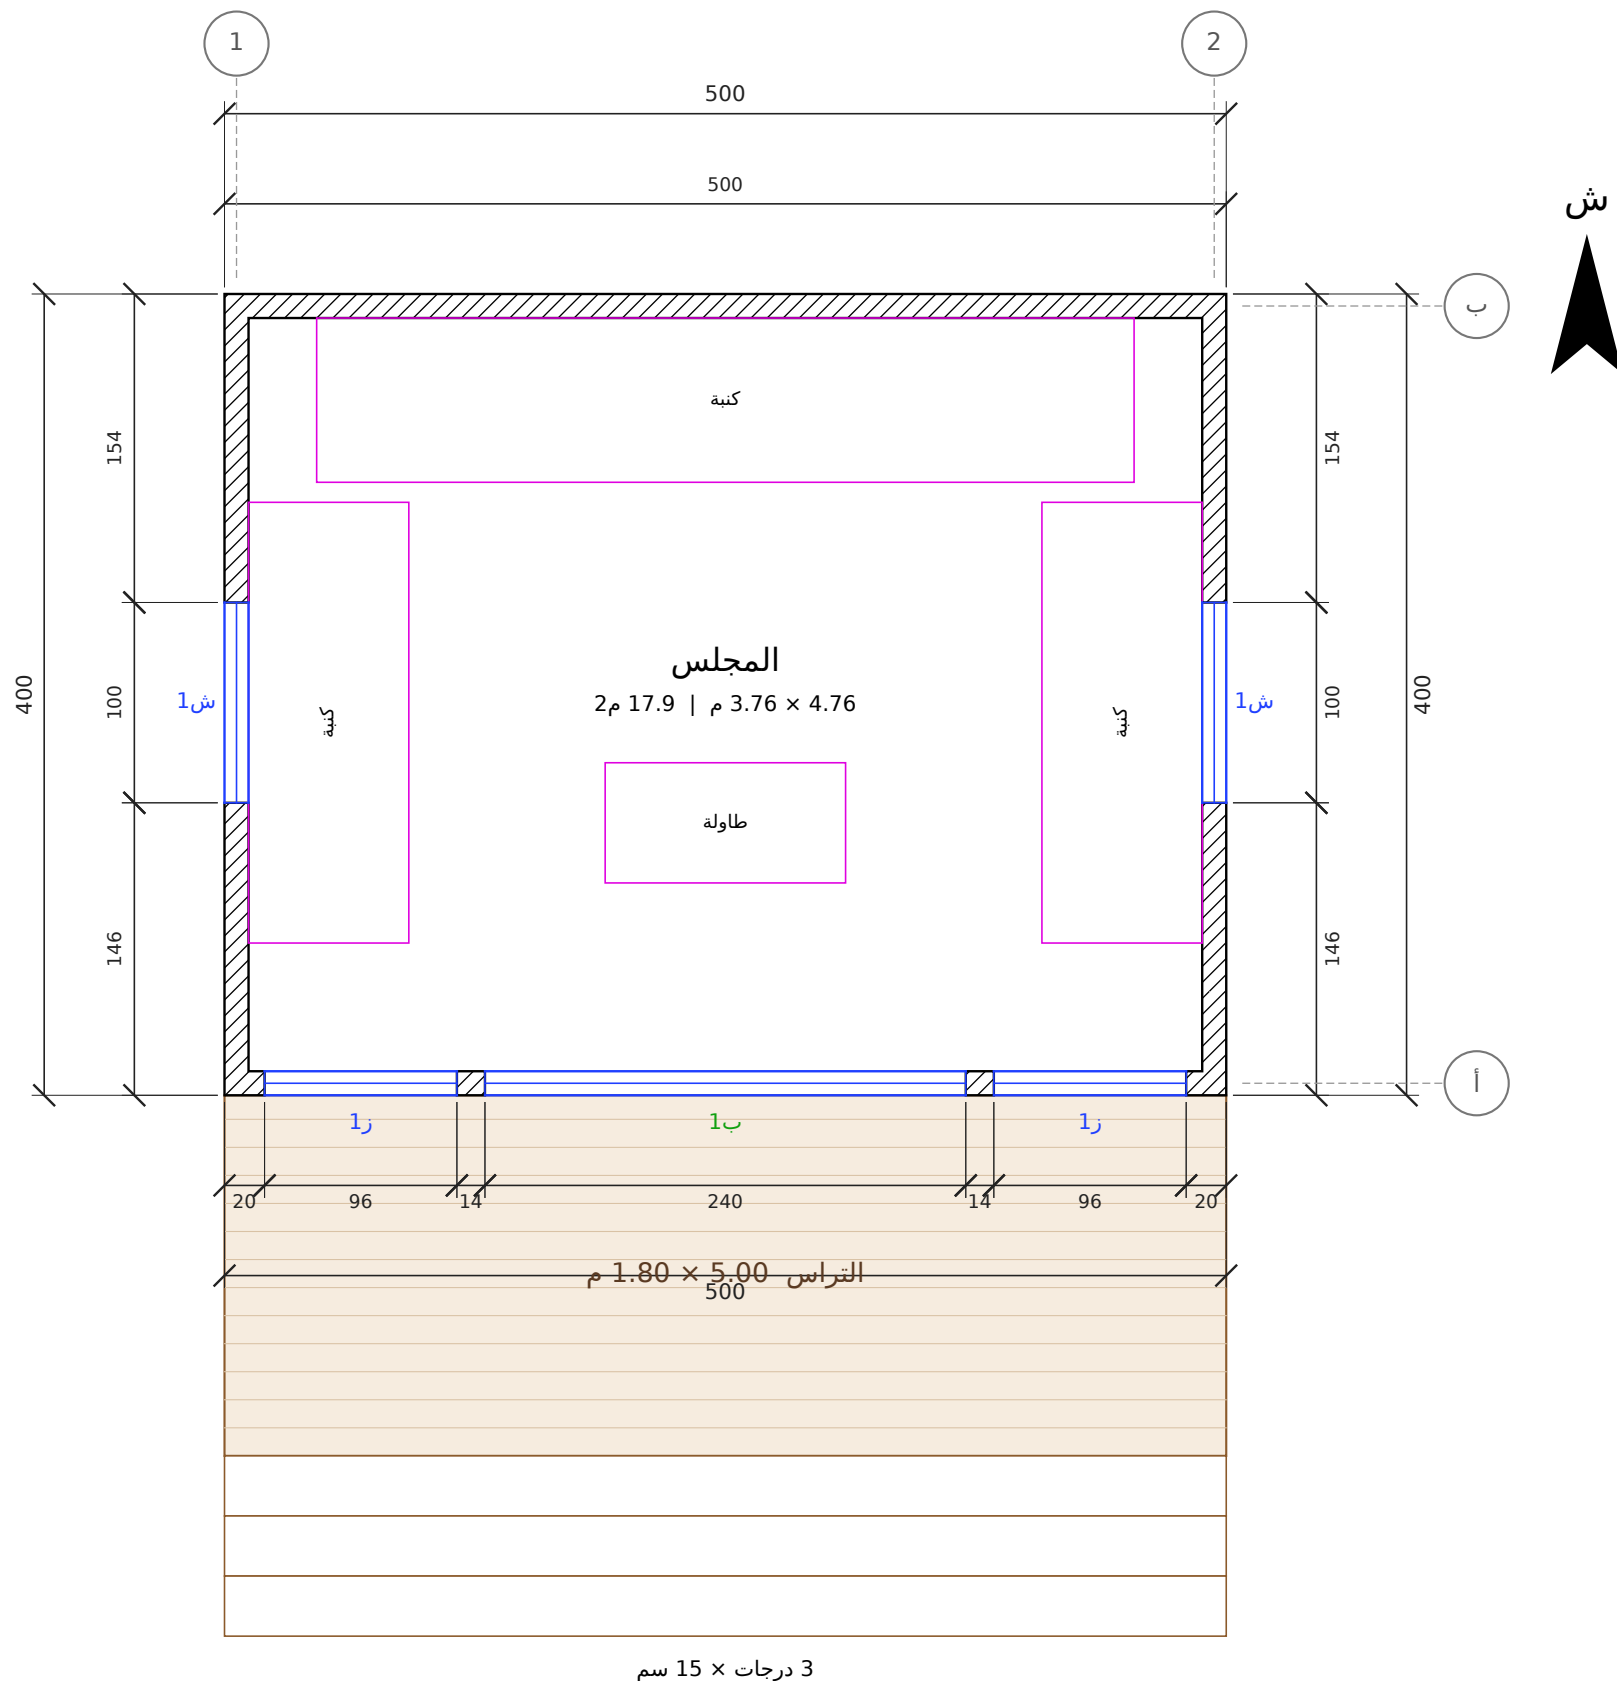


رقم اللوحة	التاريخ	المقياس	عنوان اللوحة	المشروع / العميل	مصنع وتد الأخشاب Watad Wood Factory
A-01 (1/9)	2026-10-06	1:50	المسقط الأفقي	مجلس 5×4 بواجهة زجاج عميل - مجلس	

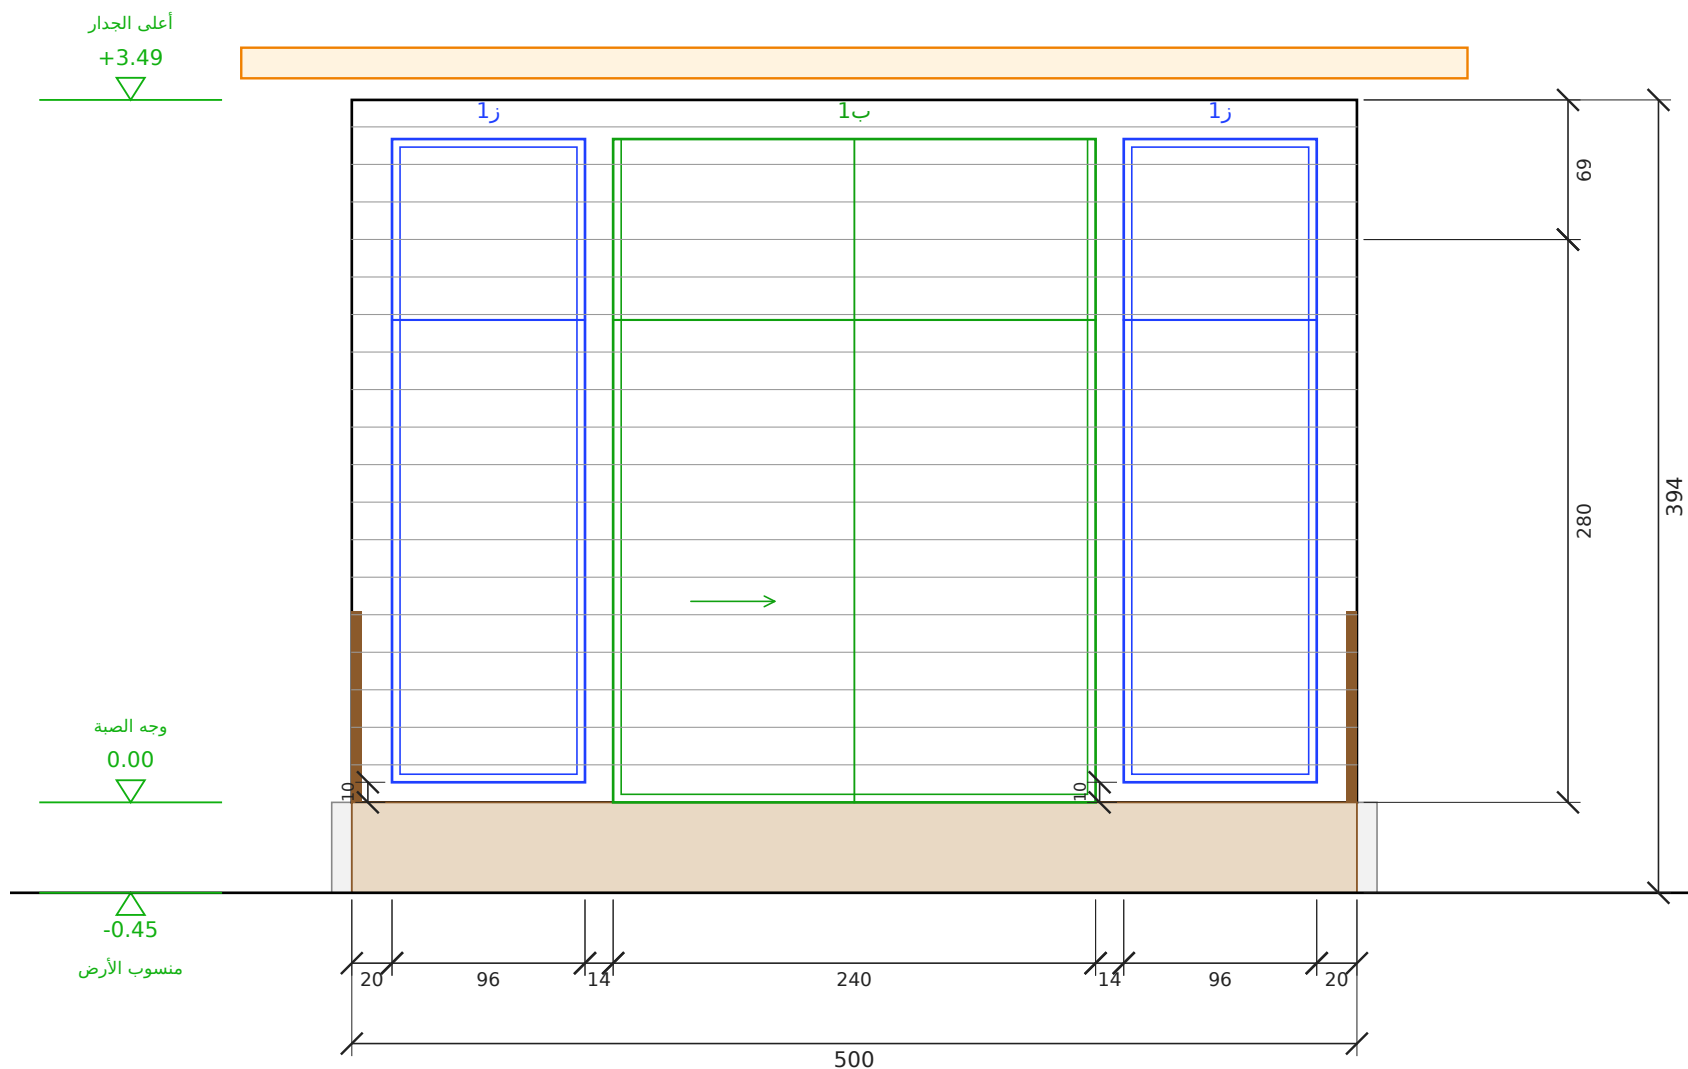

الواجهة الأمامية (زجاج)


مقياس 1:50 | الوحدة: سم

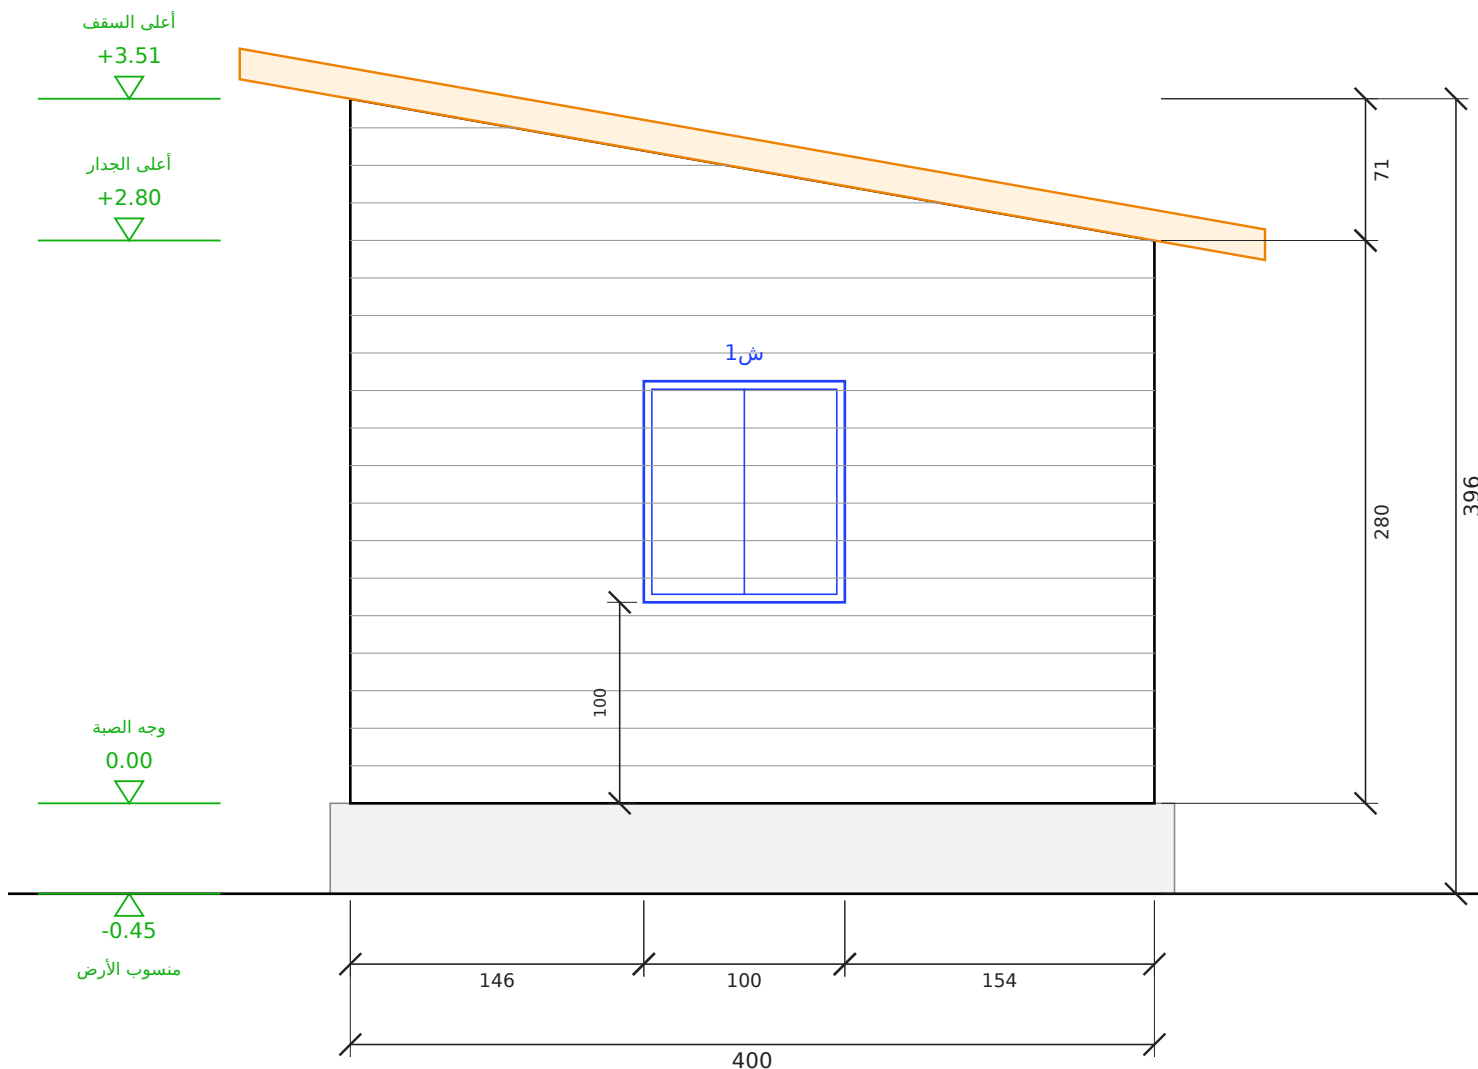

الواجهة الشرقية


مقياس 1:50 | الوحدة: سم

رقم اللوحة	التاريخ	المقياس	عنوان اللوحة	المشروع / العميل	مصنع وتد الأخشاب Watad Wood Factory
A-02 (2/9)	2026-10-06	1:50	الواجهة الأمامية (زجاج) والواجهة الشرقية	مجلس 5x4 بواجهة زجاج عميل - مجلس	

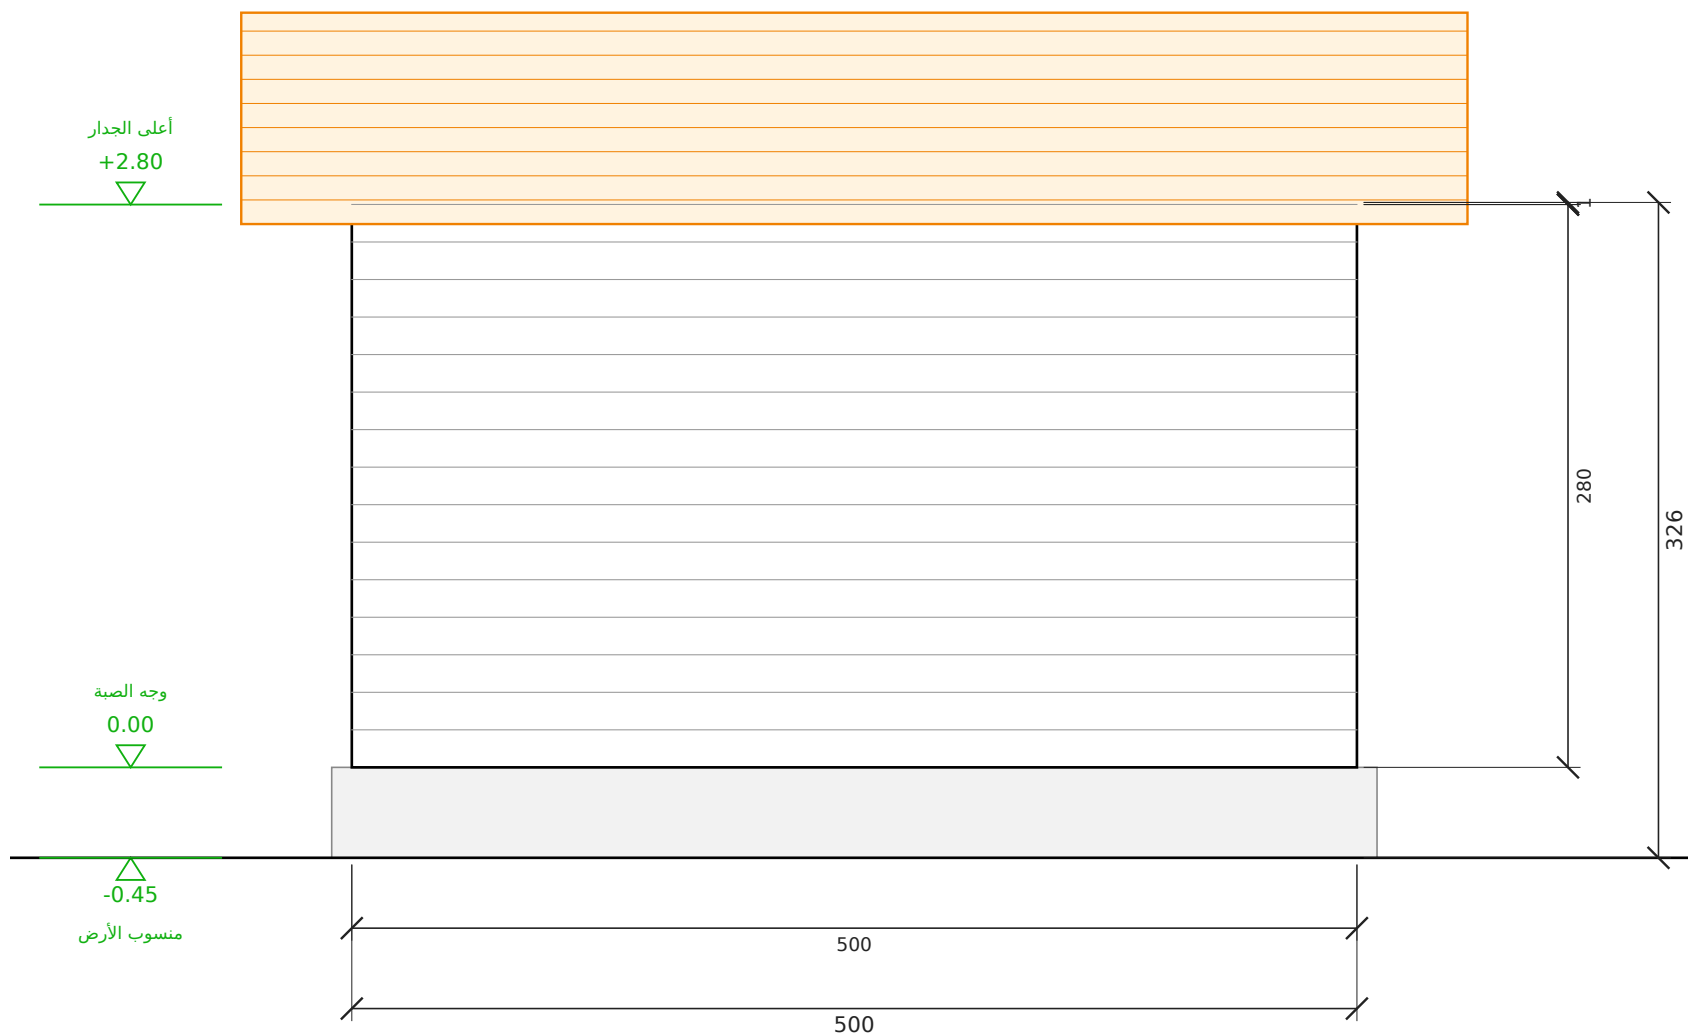

الواجهة الخلفية

مقياس 1:50 | الوحدة: سم

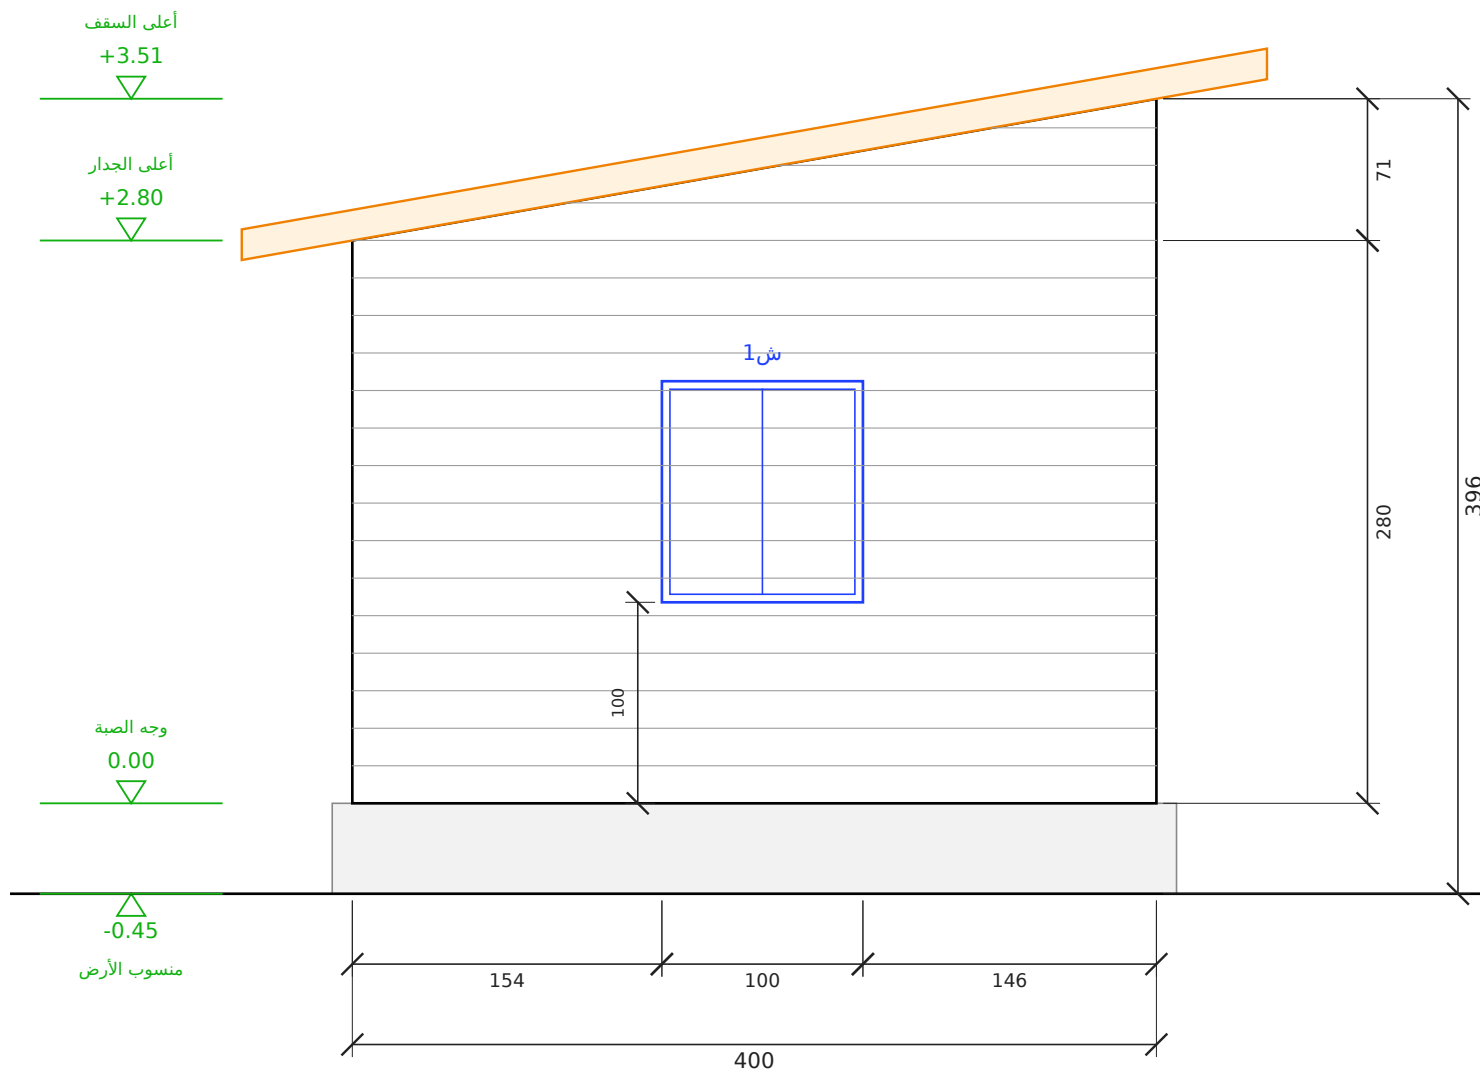


الواجهة الغربية


مقياس 1:50 | الوحدة: سم

رقم اللوحة	التاريخ	المقياس	عنوان اللوحة	المشروع / العميل	مصنع وتد الأخشاب Watad Wood Factory
A-03 (3/9)	2026-10-06	1:50	الواجهة الخلفية والواجهة الغربية	مجلس 5x4 بواجهة زجاج عميل - مجلس	


مسقط السقف (مائل باتجاه واحد)
رفر 55 سم من كل جهة | مقياس 1:50

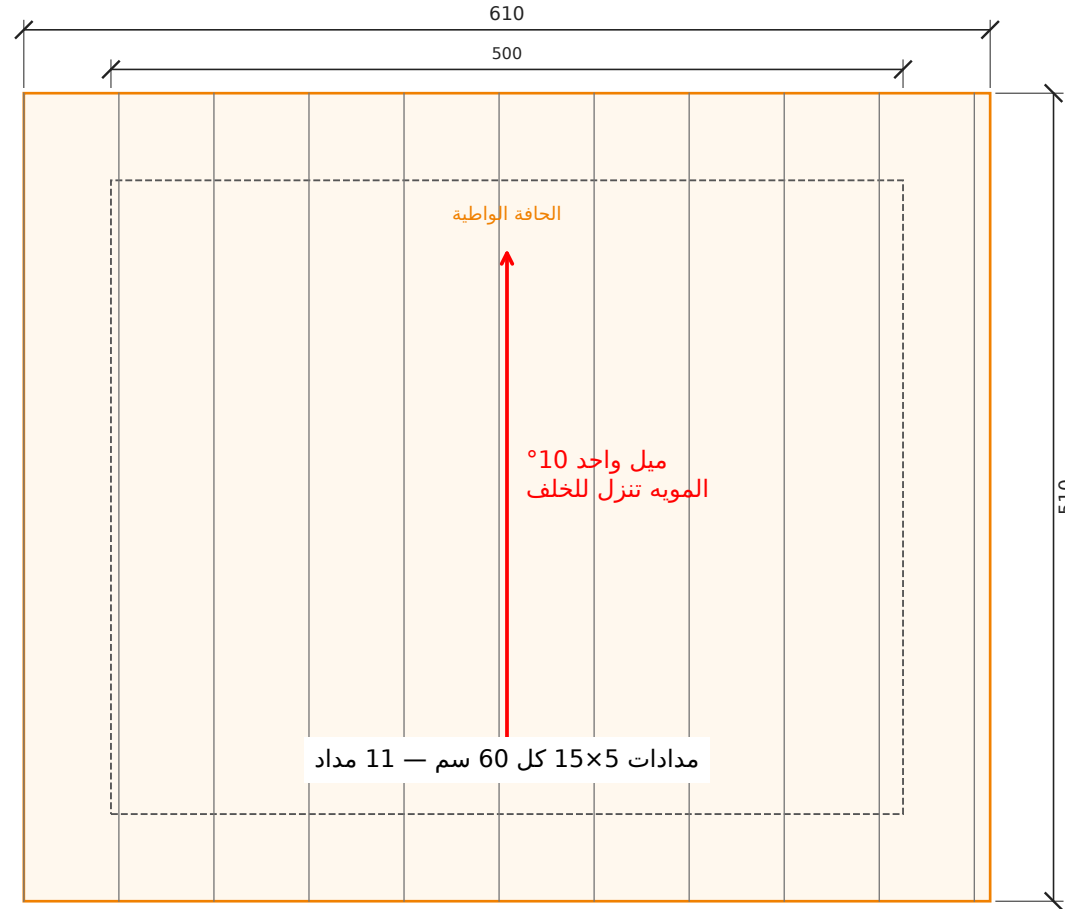

قطاع عرضي أ-أ
مقياس 1:50 | الوحدة: سم

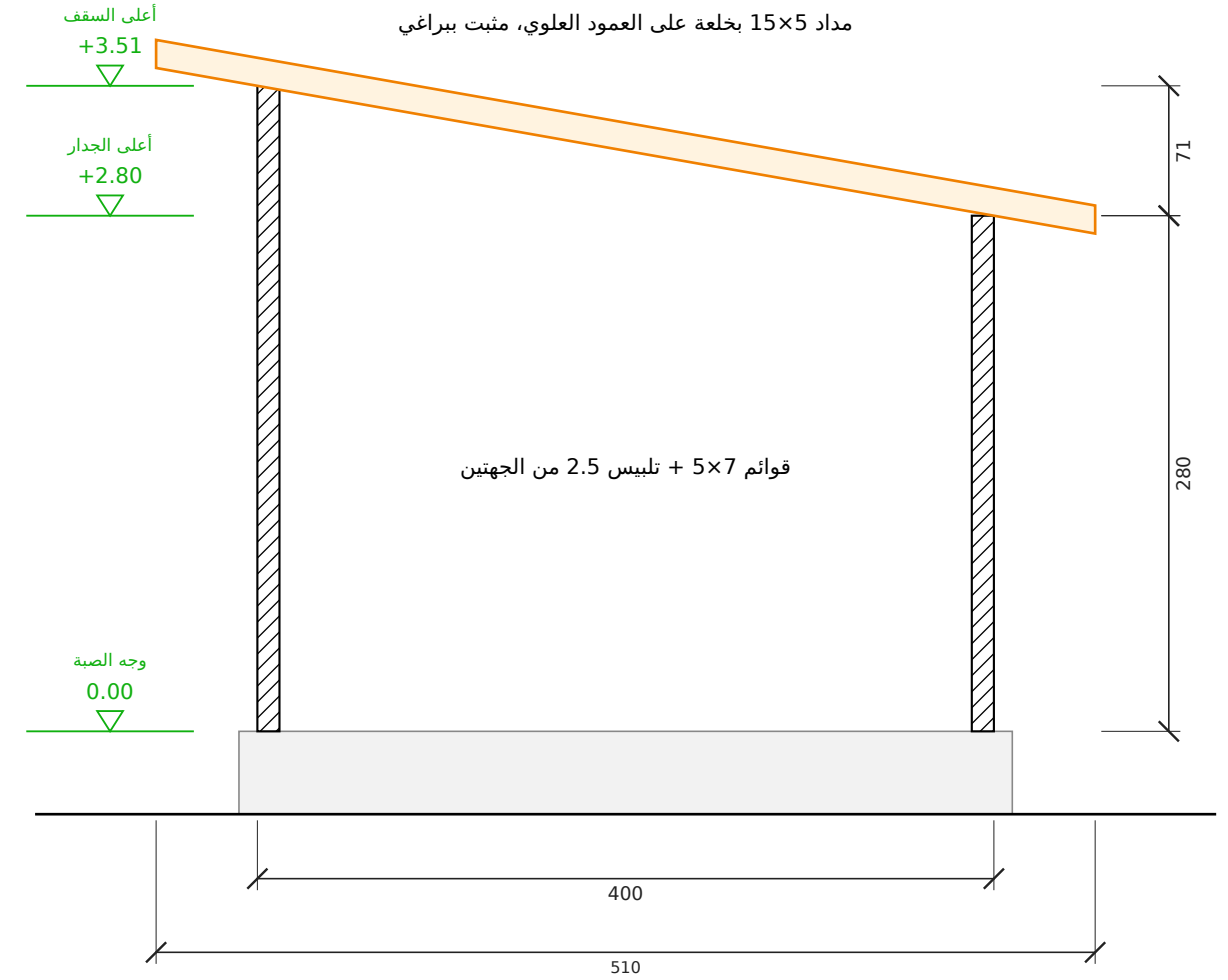

تفصيلة جلوس المداد على العلوي (1:5)

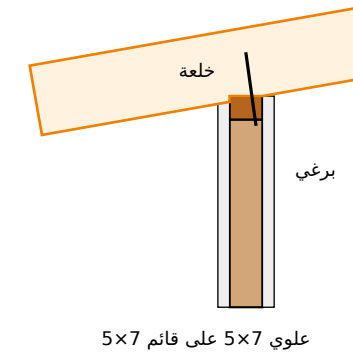

رقم اللوحة

A-04 (4/9)

التاريخ

2026-10-06

المقياس

1:50

عنوان اللوحة

مسقط السقف والقطاع

المشروع / العميل

مجلس 5x4 بواجهة زجاج
عميل — مجلس

مصنع وتد الأخشاب
Watad Wood Factory



جدول مقاسات الأبواب والشبابيك
مقاس الفتحة الصافي في الجدار - الوحدة: سم

الرمز	النوع	العرض (سم)	الارتفاع (سم)	ارتفاع الجلسة (سم)	العدد	الموقع
ب1	باب	240	330	-	1	الأمامية (زجاج)
ر1	شباك	96	320	10	2	الأمامية (زجاج) 2
ش1	شباك	100	110	100	2	الشرقية - الغربية

الإجمالي: أبواب 1 - شبابيك 4

جدول المساحات وبيانات المشروع والتسعير

جدول المساحات

م	الفراغ	الأبعاد (م)	المساحة (م2)
1	المجلس	4.76 × 3.76	17.90
	المساحة الصافية الداخلية		17.90
	التراس المسقوف (مجاناً)	5.00 × 1.80	9.00
	المساحة الإجمالية المبنية	5.00 × 4.00	20.00

بيانات المشروع

البند	البيان
المشروع	مجلس 5×4 بواجهة زجاج
العميل	عميل — مجلس
الموقع	—
الاستخدام	مجلس
التاريخ	2026-10-06
نظام البناء	هيكل خشب 5×7 + تليس 2.5 سم من الجهتين
السقف	مائل باتجاه واحد 10° — قرميد معدني

التسعير

البند	القيمة
المساحة المبنية (م2)	20.00
سعر المتر المربع	1,096 ريال
الإجمالي	21,920 ريال

ملاحظات:

- السعر للمساحة المبنية حسب المخطط المعتمد.
- الصبة والتמידات الخارجية على العميل ما لم يُذكر غير ذلك.

لقطات المنظور الخارجي


منظور أمامي من اليمين



منظور أمامي من اليسار




المنظور الأمامي

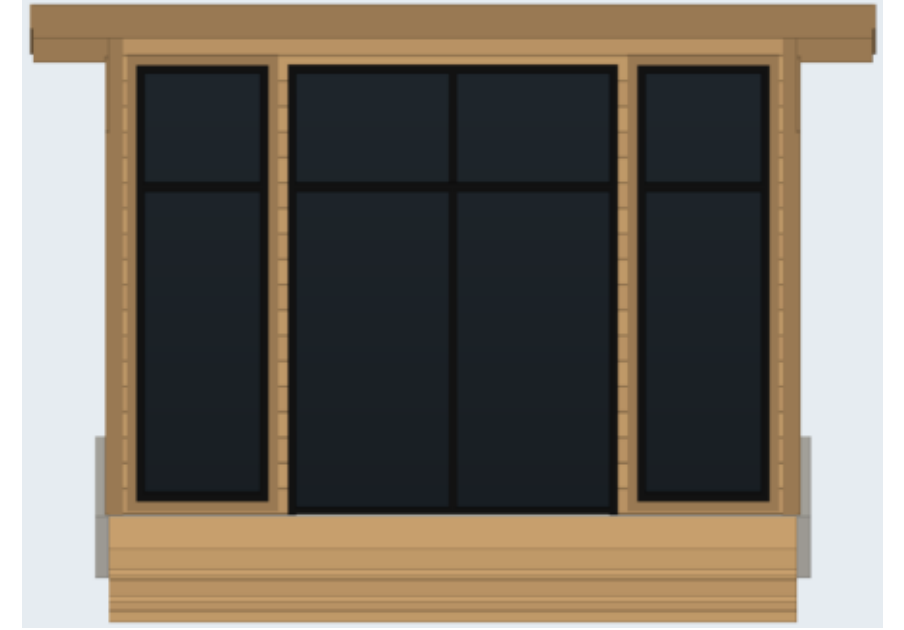


منظر علوي



منظور خلفي من اليمين

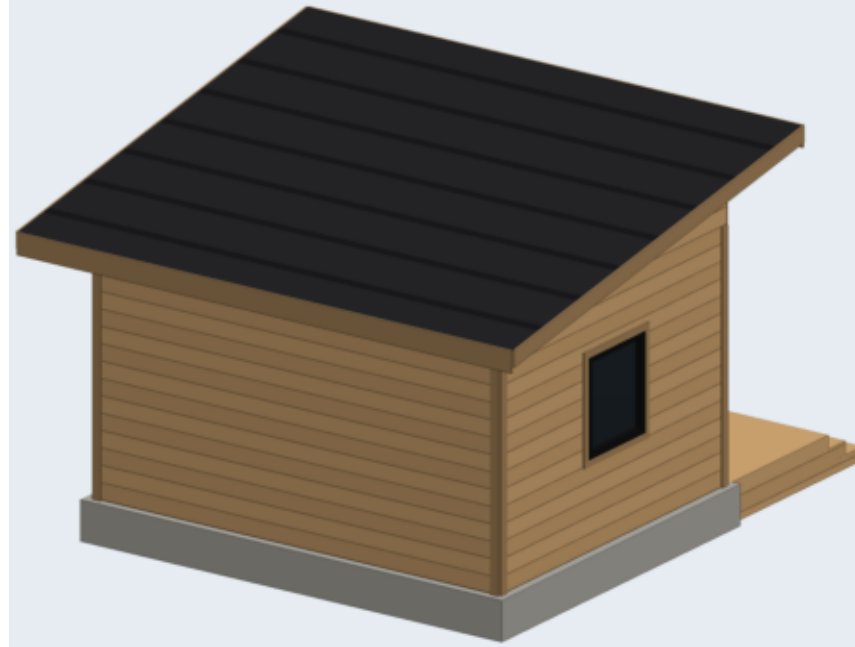

المنظور الخلفي

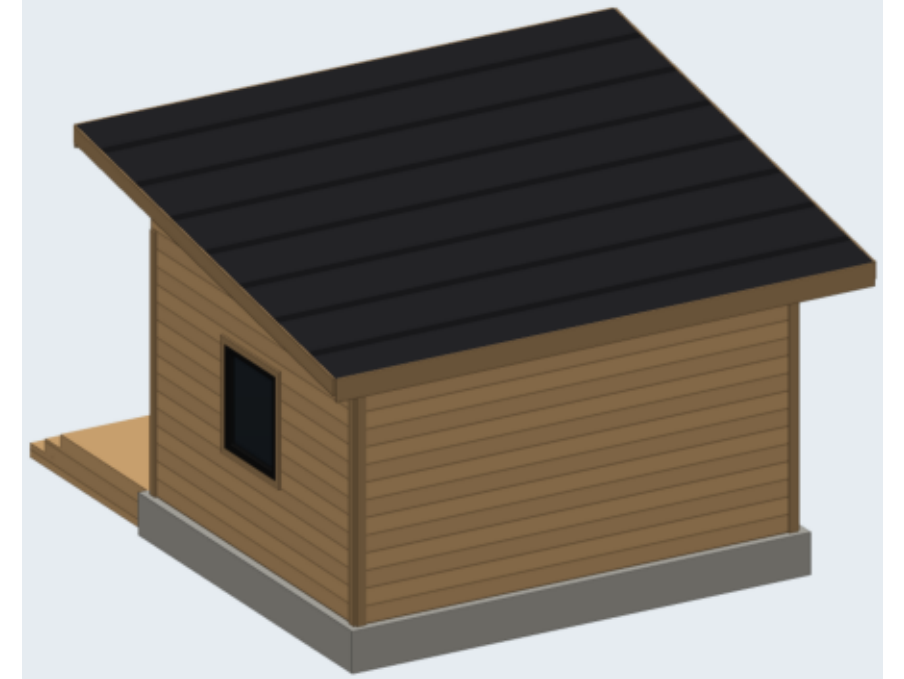

رقم اللوحة

A-07 (7/9)

التاريخ

2026-10-06

المقياس

—

عنوان اللوحة

لقطات المنظور

المشروع / العميل

مجلس 5x4 بواجهة زجاج
عميل — مجلس

مصنع وتد الأخشاب
Watad Wood Factory



المقطع العلوي بالفرش

مقطع أفقي على ارتفاع 1.90 م — توزيع الفرش ومسار الحركة



رقم اللوحة

A-08 (8/9)

التاريخ

2026-10-06

المقياس

—

عنوان اللوحة

المقطع العلوي بالفرش

المشروع / العميل

مجلس 5x4 بواجهة زجاج
عميل — مجلس


مصنع وتد الأخشاب
Watad Wood Factory



المنظور ثلاثي الأبعاد والمواد

النمط: جوزي غامق + إطارات سوداء — رندر واقعي بخامات حقيقية

جدول المواد والألوان

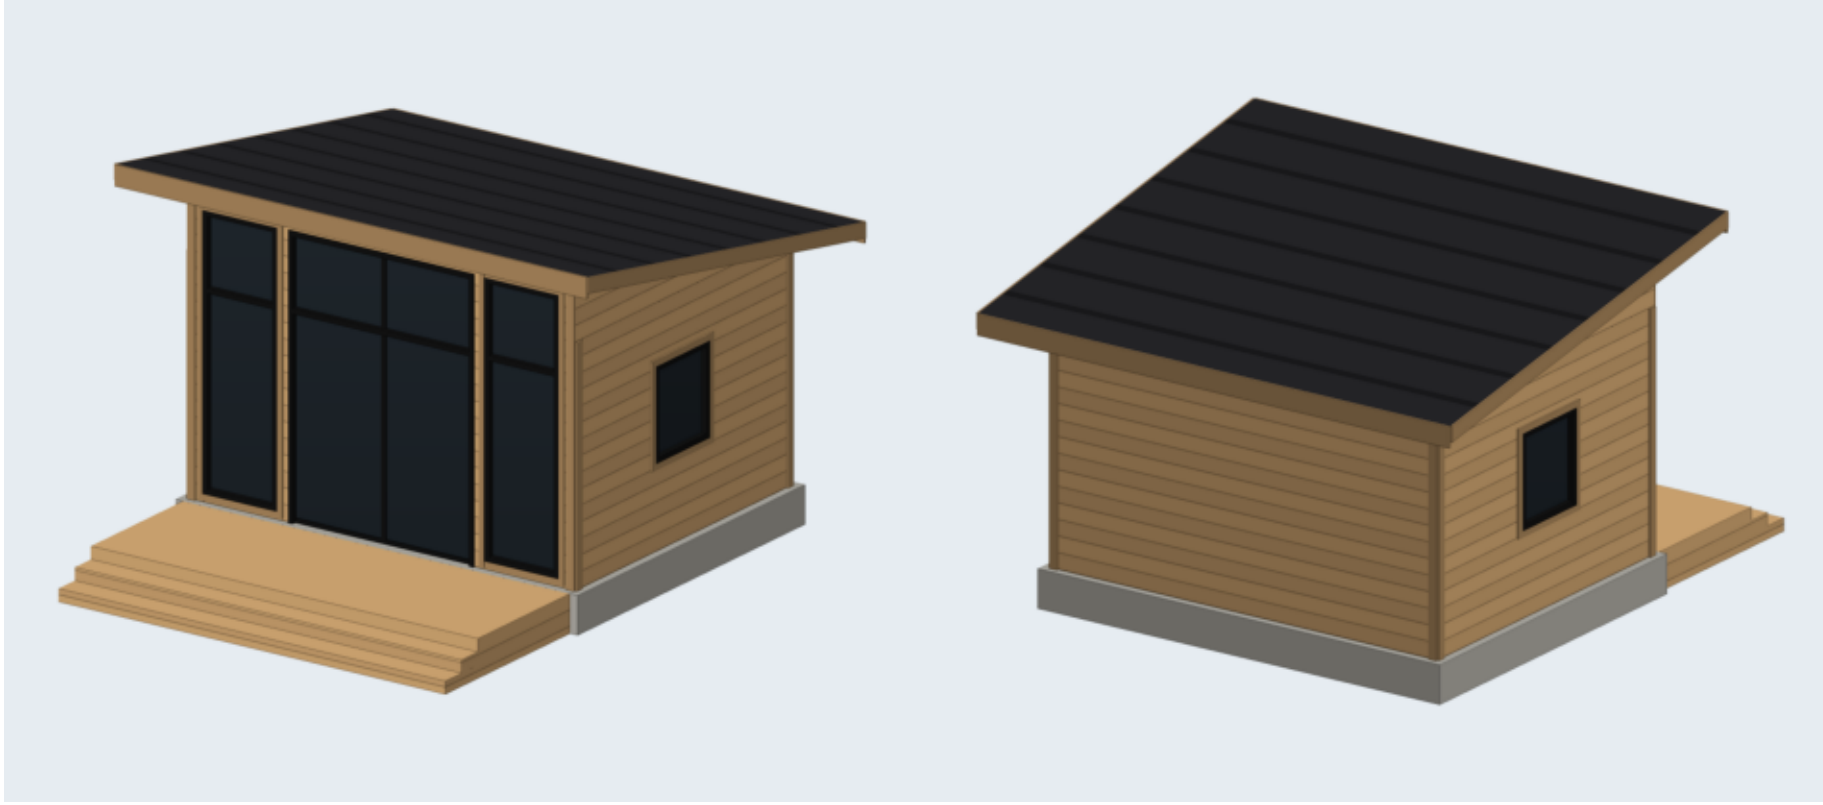

الخشب / الصبغة

خشب طبيعي فاتح (بدون صبغة)



القرميد

قرميد رمادي غامق



الزجاج

زجاج عاكس غامق




إطارات الشبابيك والأبواب

إطار ألومنيوم أسود



الكنار والزوايا

نفس الصبغة أعمق درجة

 

الصبغة

خرسانة 45 سم


الدريزين: ألواح أفقية متقاربة (عصري)

تقسيم الشبابيك: بدون | الباب الرئيسي: سحب زجاج


أنواع الدريزين المعتمدة (من مشاريع المصنع)



قوائم رأسية متقاربة (صورة 1)

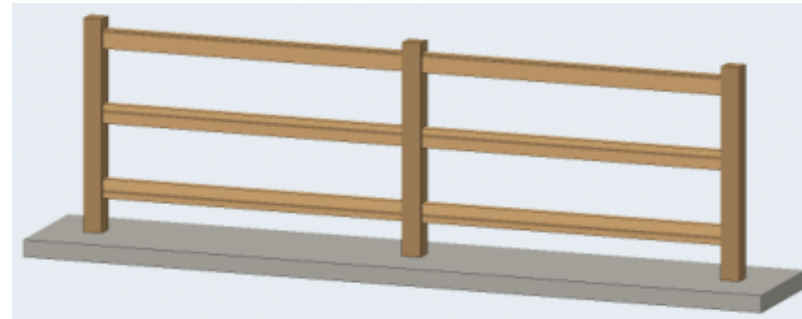

3 مربيع أفقية (صورة 2)

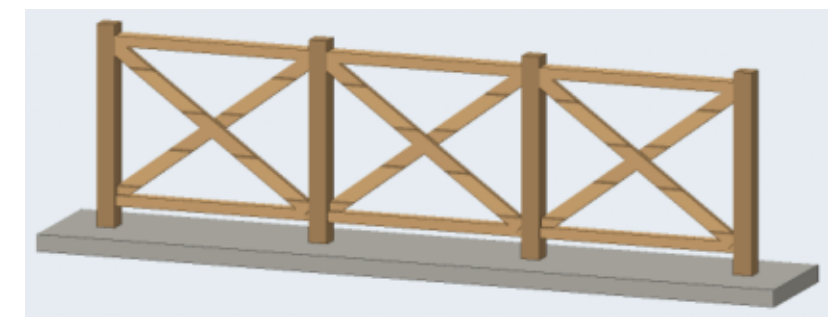

تقاطع X (صورة 5)

رقم اللوحة

A-09 (9/9)

التاريخ

2026-10-06

المقياس

—

عنوان اللوحة

المنظور والمواد

المشروع / العميل

مجلس 5x4 بواجهة زجاج
عميل — مجلس

مصنع وتد الأخشاب
Watad Wood Factory

