



المسقط الأفقي مع الفرش
الأبعاد بالسنتيمتر - الجدران: قوائم 5×7 + تليس 2.5 من الجهتين (12 سم)

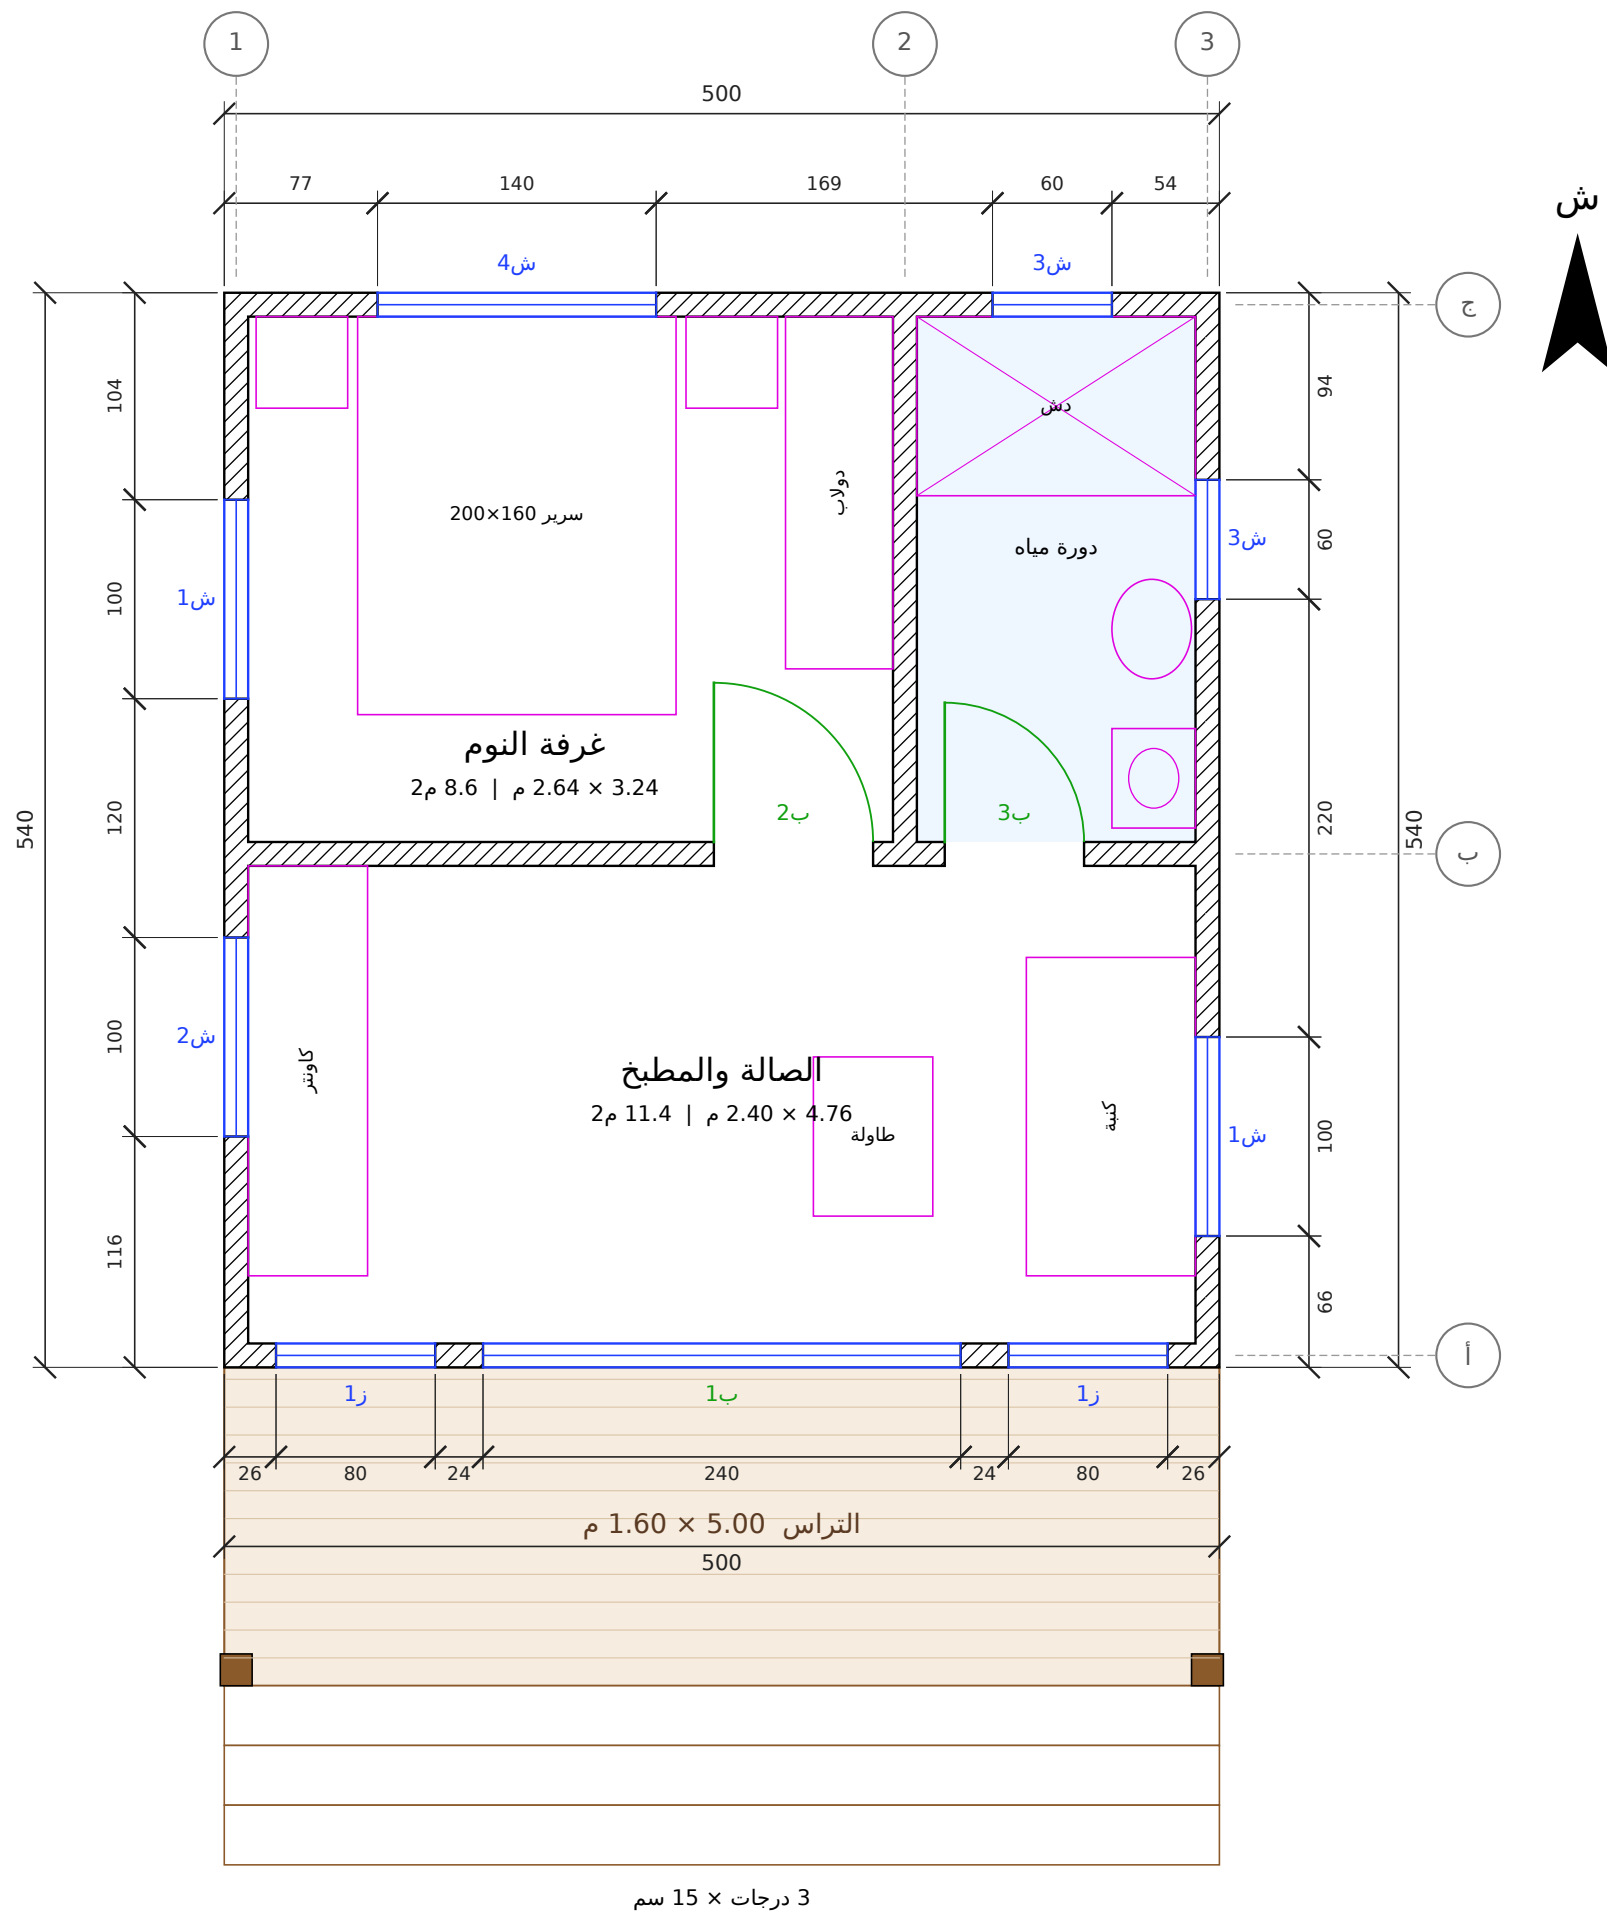


3 درجات × 15 سم

رقم اللوحة	التاريخ	المقياس	عنوان اللوحة	المشروع / العميل	مصنع وتد الأخشاب Watad Wood Factory
A-01 (1/10)	2026-09-29	1:50	المسقط الأفقي	كوخ غرفة وتراس 7×5 شامل التراس عميل - تصميم حسب الصورة	

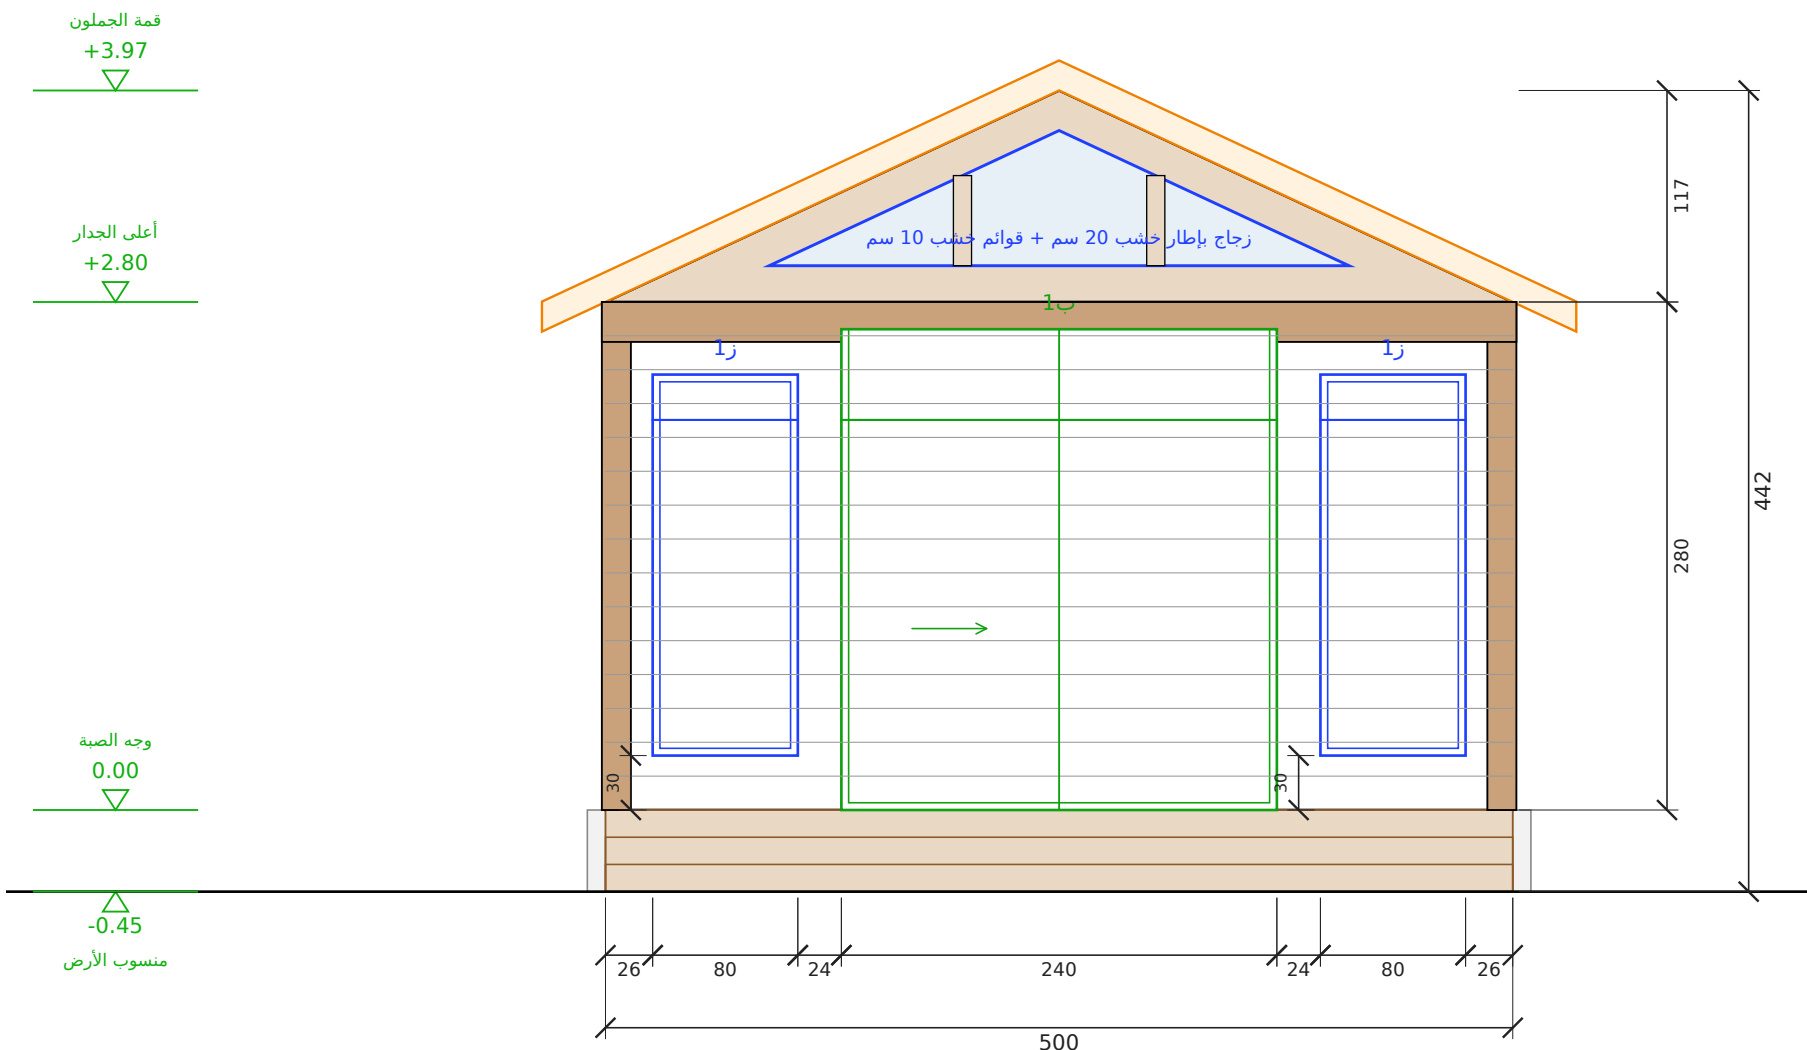

الواجهة الأمامية (التراس)


مقياس 1:50 | الوحدة: سم

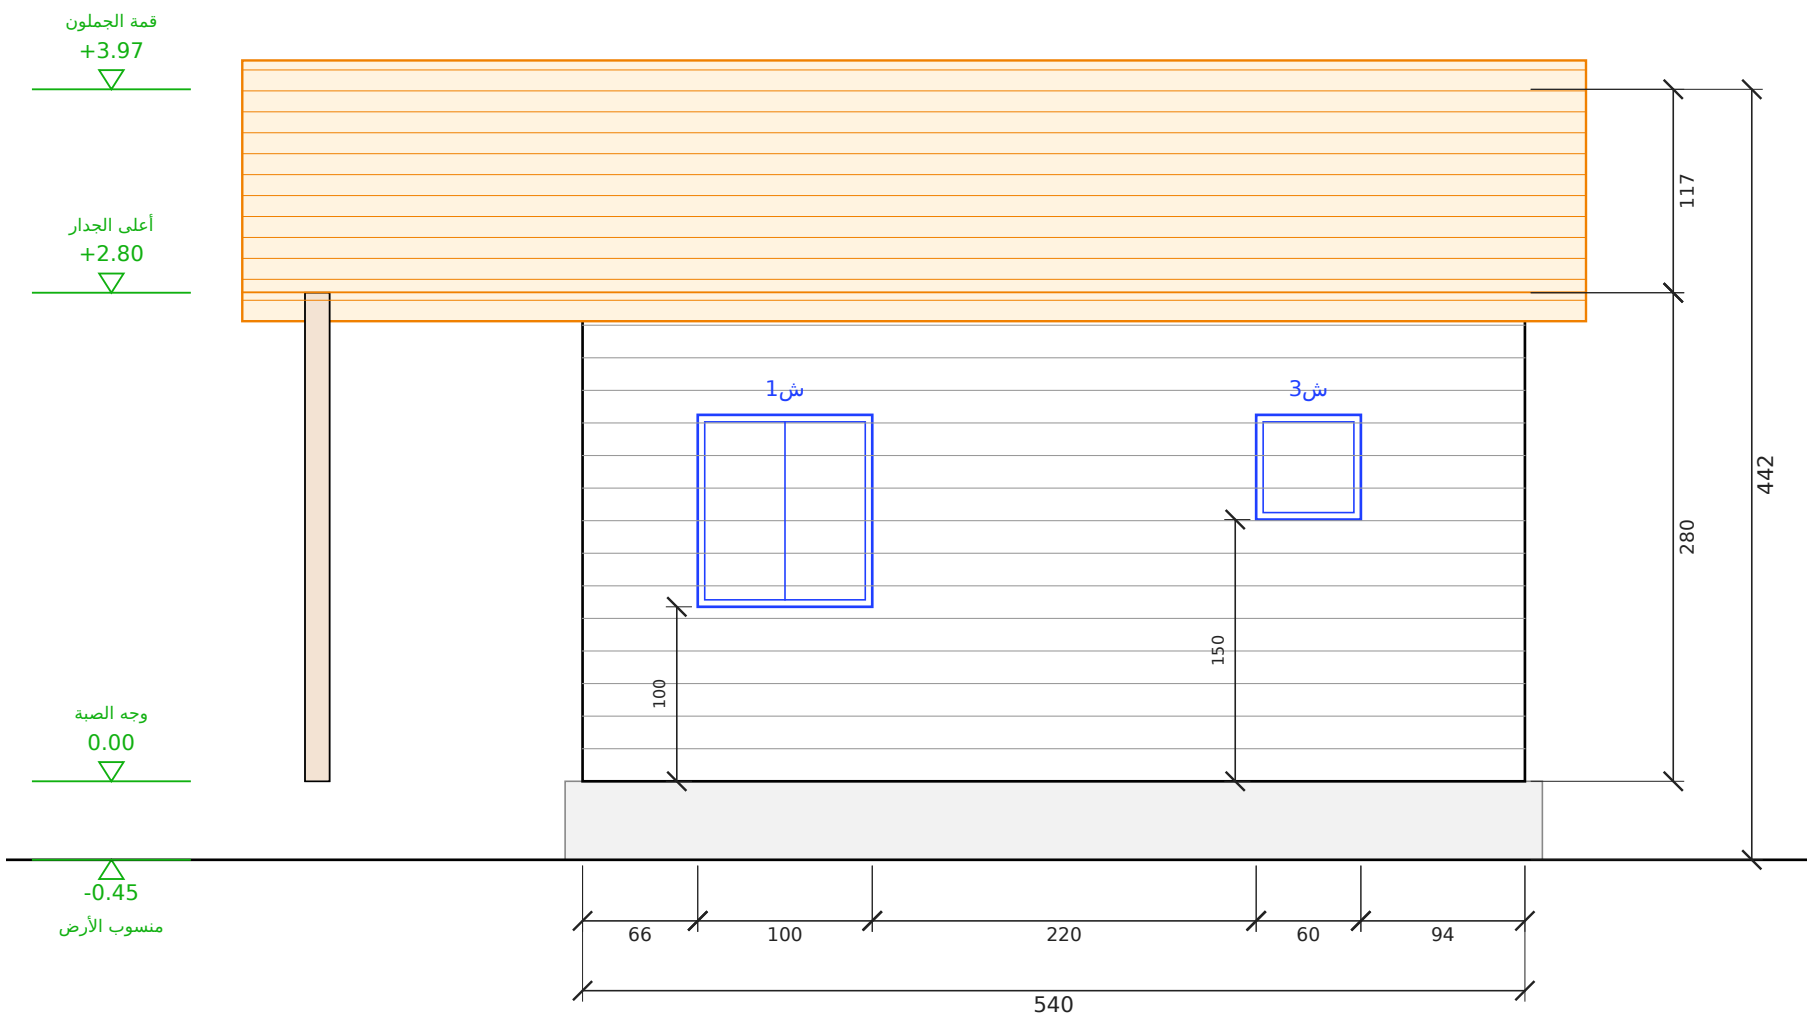

الواجهة الشرقية


مقياس 1:50 | الوحدة: سم

رقم اللوحة	التاريخ	المقياس	عنوان اللوحة	المشروع / العميل	مصنع وتد الأخشاب Watad Wood Factory
A-02 (2/10)	2026-09-29	1:50	الواجهة الأمامية (التراس) والواجهة الشرقية	كوخ غرفة وتراس 7x5 شامل التراس عميل - تصميم حسب الصورة	

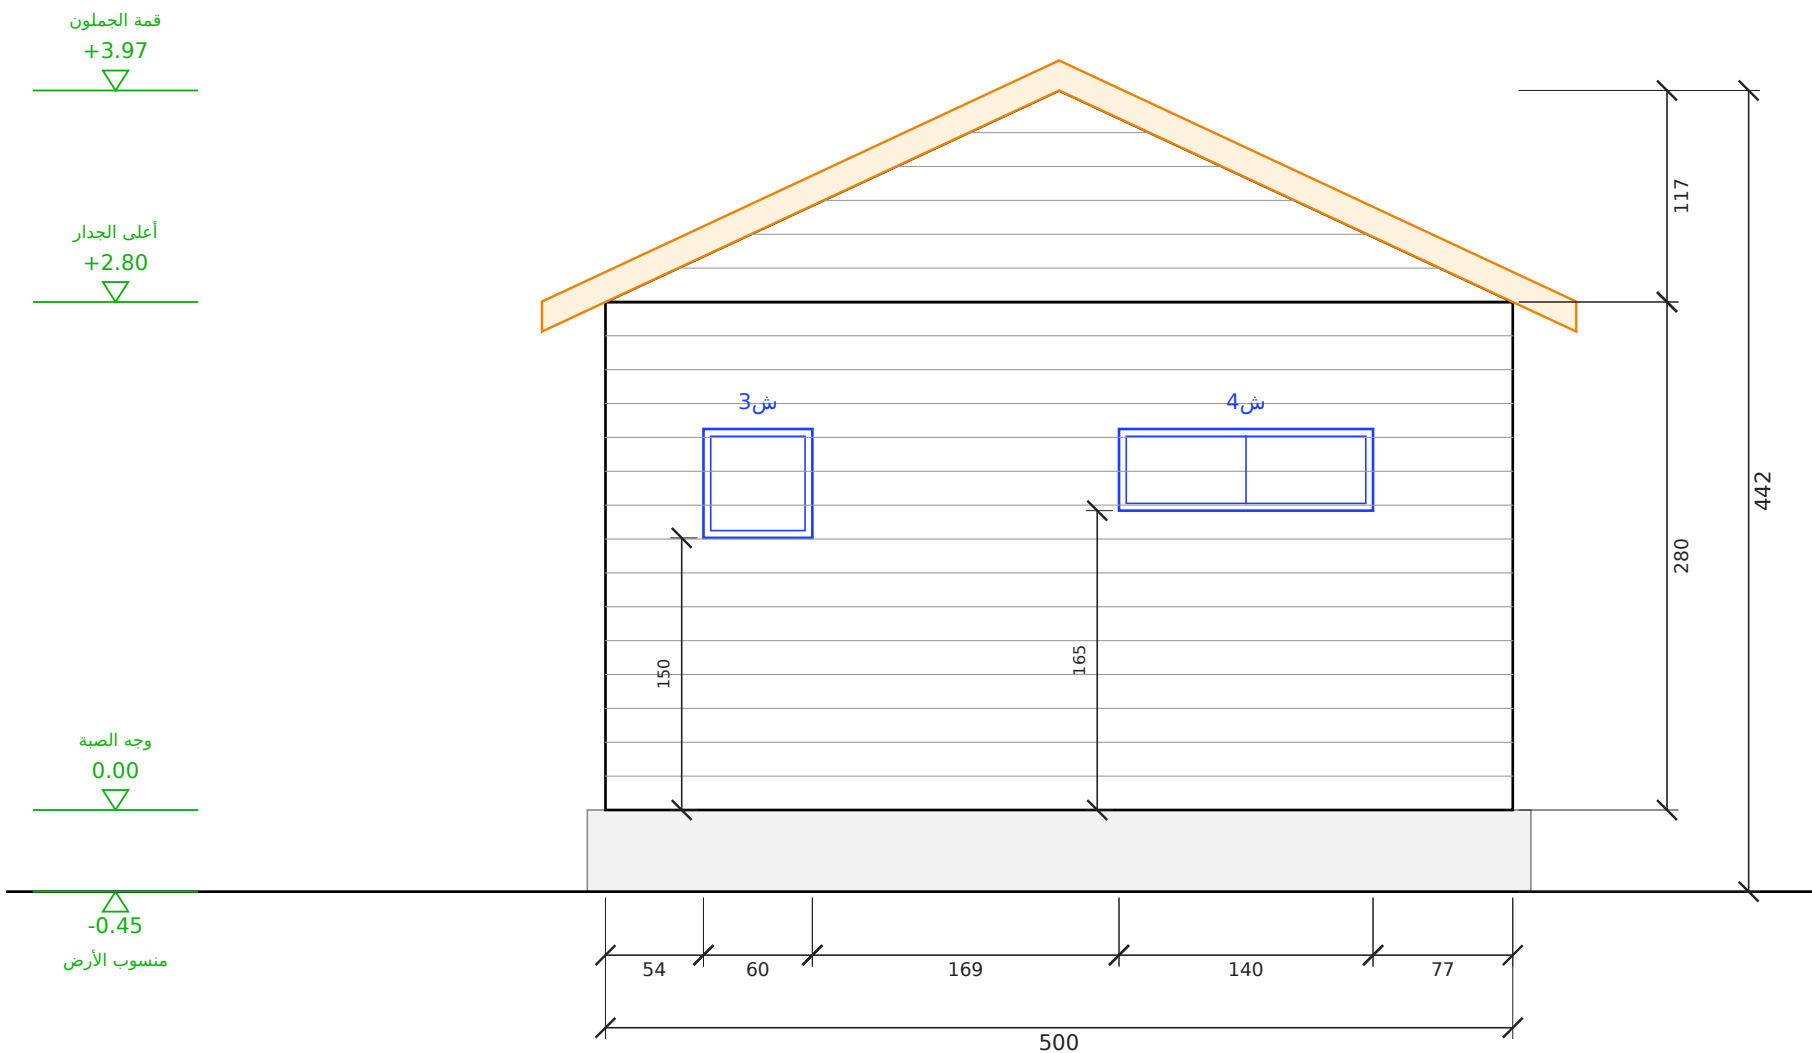

الواجهة الخلفية

مقياس 1:50 | الوحدة: سم

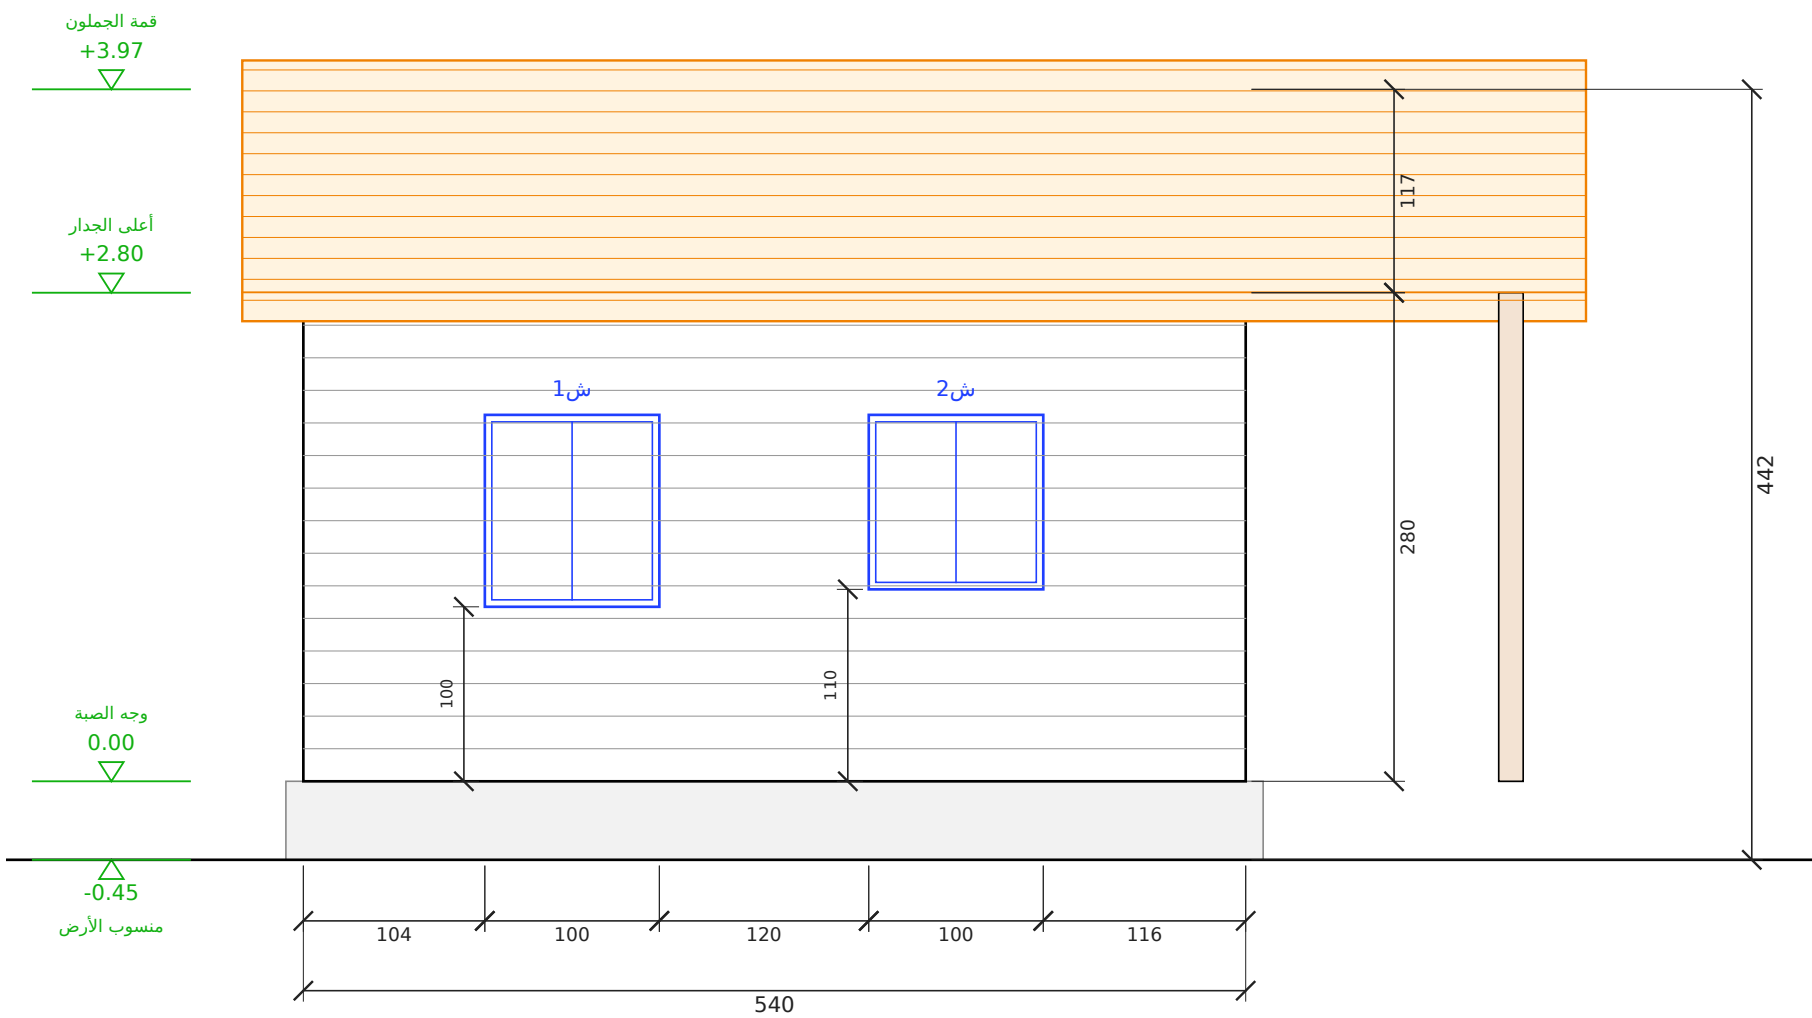


الواجهة الغربية


مقياس 1:50 | الوحدة: سم

رقم اللوحة	التاريخ	المقياس	عنوان اللوحة	المشروع / العميل	مصنع وتد الأخشاب Watad Wood Factory
A-03 (3/10)	2026-09-29	1:50	الواجهة الخلفية والواجهة الغربية	كوخ غرفة وتراس 7x5 شامل التراس عميل - تصميم حسب الصورة	


مسقط السقف (جملون)
ررف 35 سم من كل جهة | مقياس 1:50

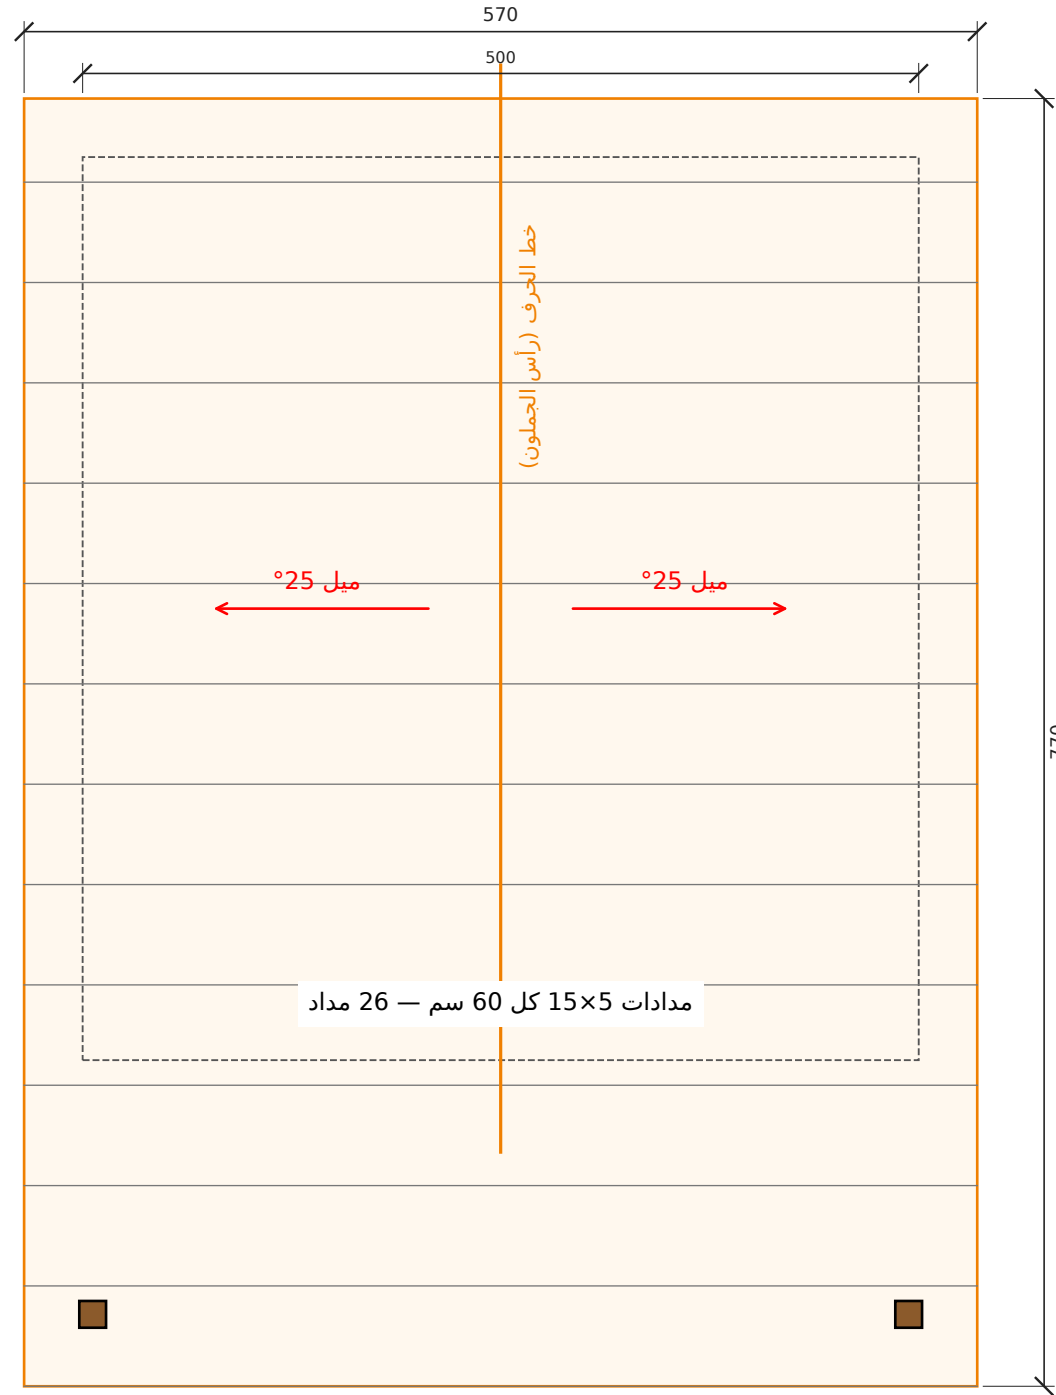

قطاع عرضي أ-أ
مقياس 1:50 | الوحدة: سم

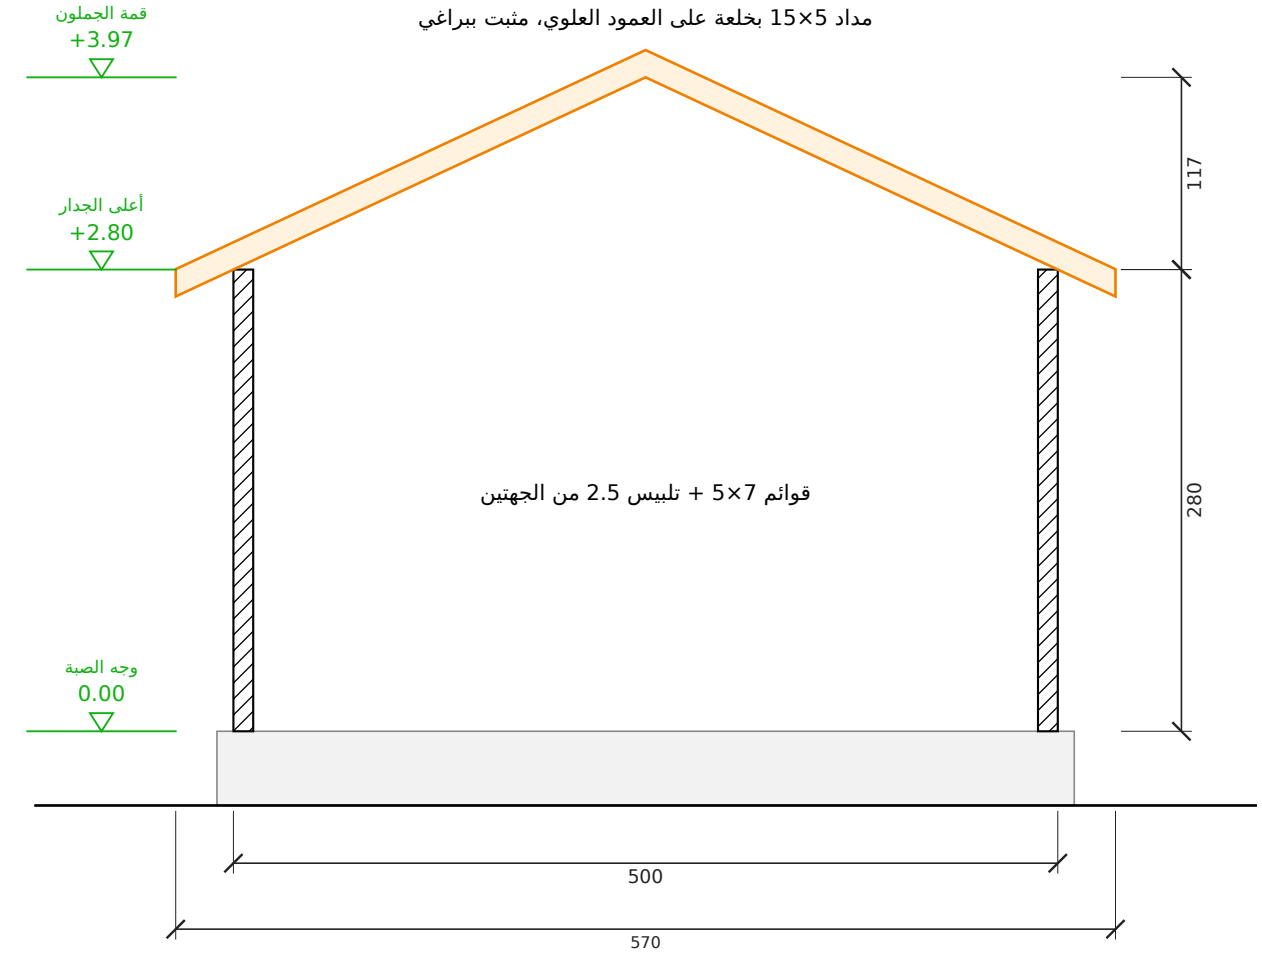

تفصيلة جلوس المداد على العلوي (1:5)

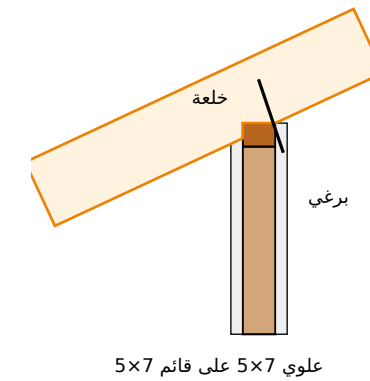

رقم اللوحة

A-04 (4/10)

التاريخ

2026-09-29

المقياس

1:50

عنوان اللوحة

مسقط السقف والقطاع

المشروع / العميل

كوخ غرفة وتراس 7x5 شامل التراس
عميل — تصميم حسب الصورة

مصنع وتد الأخشاب
Watad Wood Factory



جدول مقاسات الأبواب والشبابيك
مقاس الفتحة الصافي في الجدار - الوحدة: سم

الرمز	النوع	العرض (سم)	الارتفاع (سم)	ارتفاع الجلسة (سم)	العدد	الموقع
ب1	باب مزدوج	240	265	-	1	الأمامية (التراس)
ب2	باب	80	210	-	1	غرفة النوم
ب3	باب	70	210	-	1	حمام
ز1	شباك	80	210	30	2	الأمامية (التراس) 2
ش1	شباك	100	110	100	2	الشرقية - الغربية
ش2	شباك	100	100	110	1	الغربية
ش3	شباك	60	60	150	2	الشرقية - الخلفية
ش4	شباك	140	45	165	1	الخلفية

الإجمالي: أبواب 3 - شبابيك 8

جدول المساحات وبيانات المشروع

جدول المساحات


م	الفراغ	الأبعاد (م)	المساحة (م2)
1	الصالة والمطبخ	4.76 × 2.40	11.42
2	غرفة النوم	3.24 × 2.64	8.55
3	دورة مياه	1.40 × 2.64	3.70
	المساحة الصافية الداخلية		23.67
	التراس المسقوف	5.00 × 1.60	8.00
	المساحة الإجمالية المبنية	5.00 × 5.40	27.00

بيانات المشروع

البند	البيان
المشروع	كوخ غرفة وتراس 7×5 شامل التراس
العميل	عميل — تصميم حسب الصورة
الموقع	—
الاستخدام	استراحة / استجمام
التاريخ	2026-09-29
نظام البناء	هيكل خشب 5×7 + تليس 2.5 سم من الجهتين
السقف	جملون 25° — قرميد معدني

الصور الواقعية


أمامي

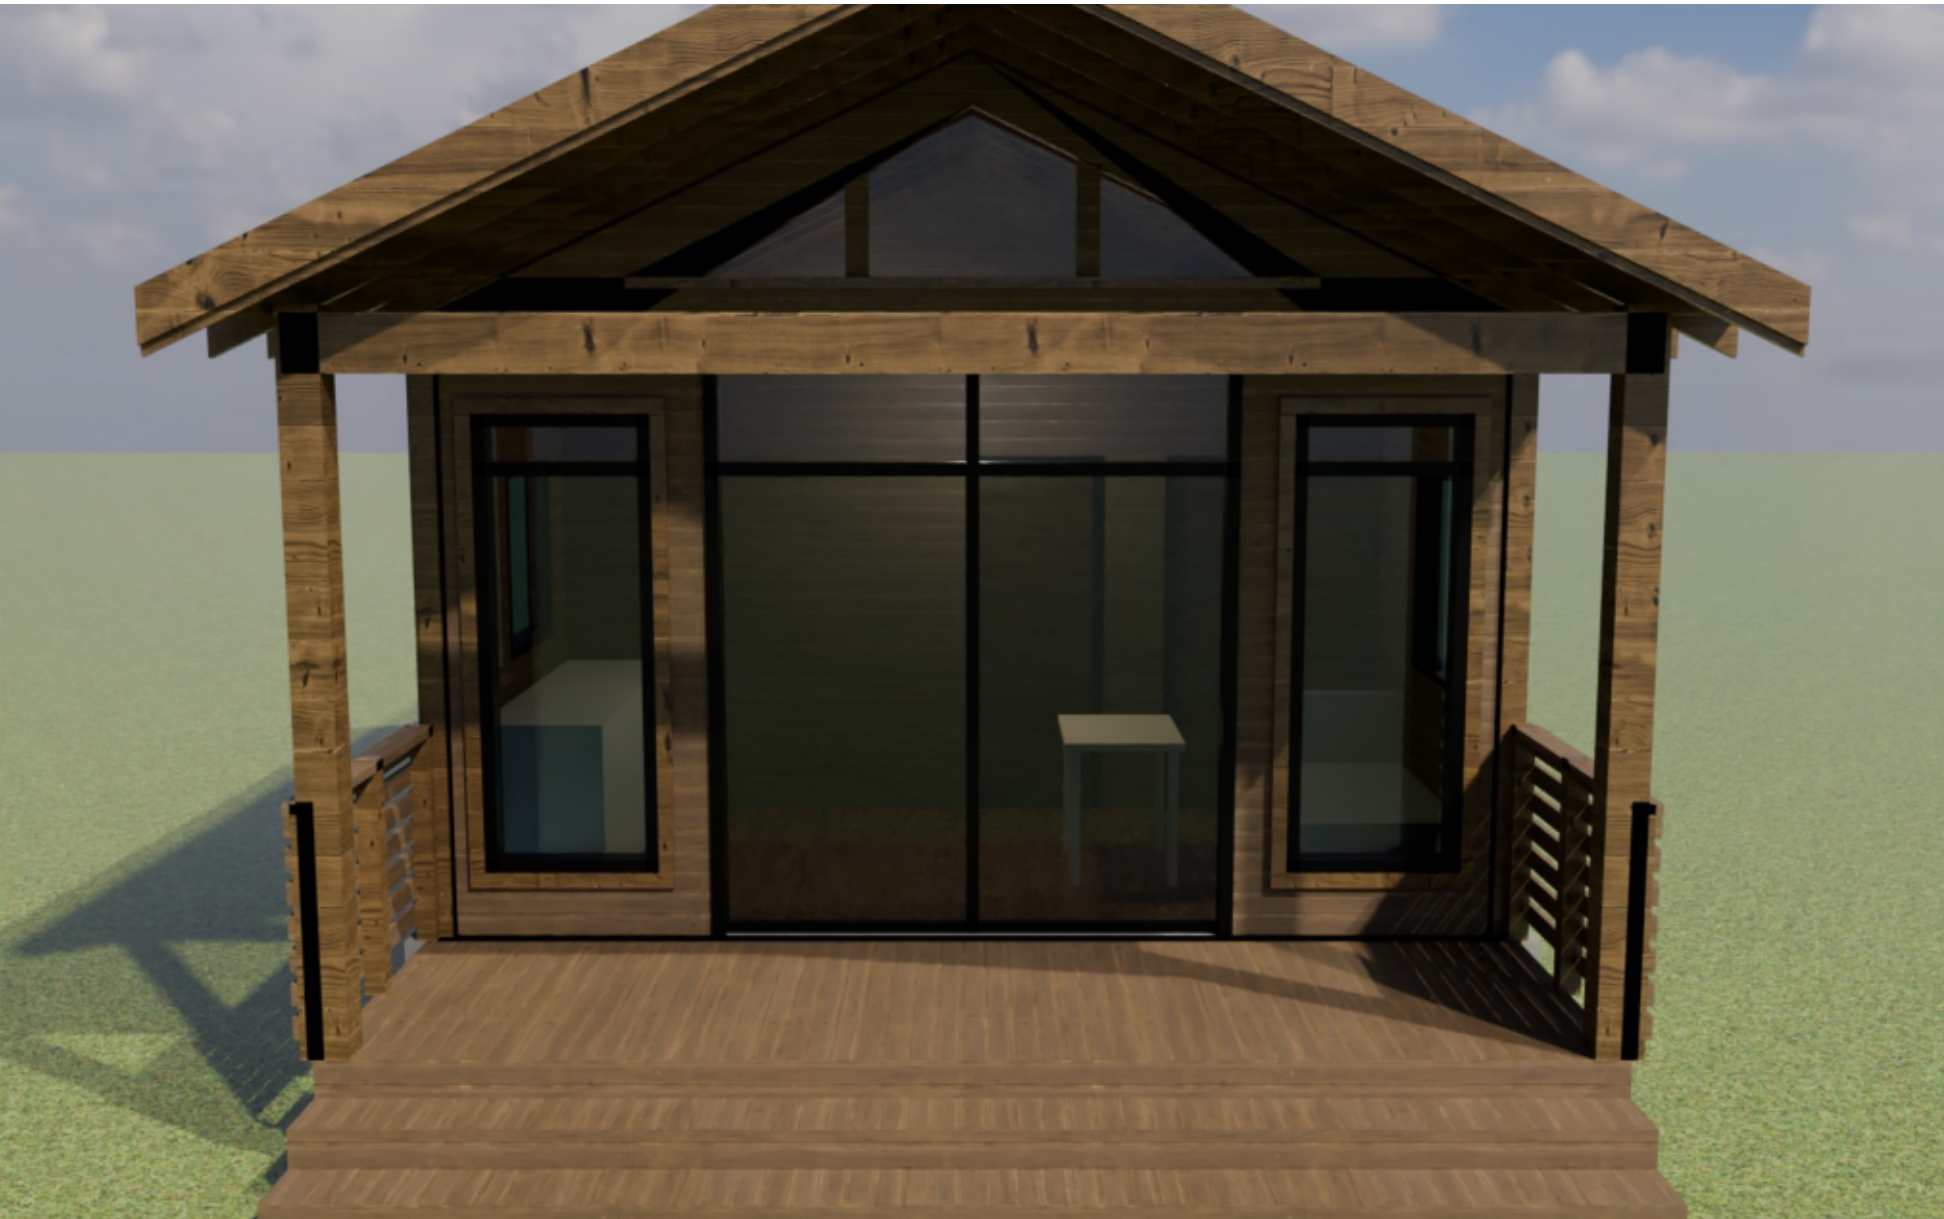

أمامي يسار



أمامي يمين

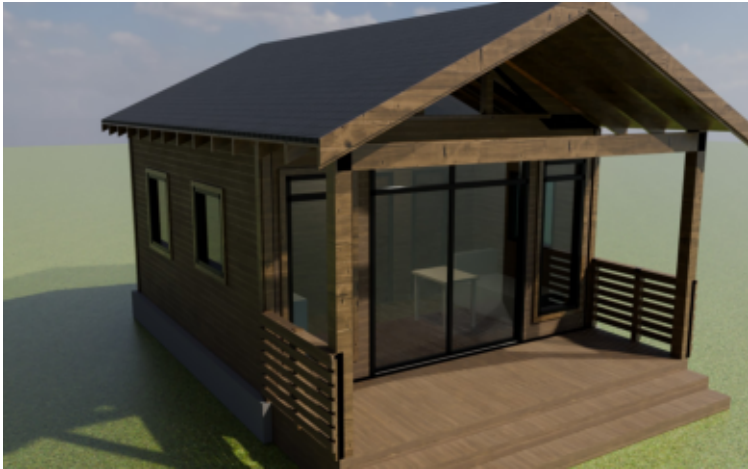

خلفي



رندر واقعي بخامات حقيقية وإضاءة طبيعية — الألوان النهائية حسب عينات المورد


رقم اللوحة	التاريخ	المقياس	عنوان اللوحة	المشروع / العميل	مصنع وتد الأخشاب Watad Wood Factory
A-07 (7/10)	2026-09-29	—	الصور الواقعية	كوخ غرفة وتراس 7×5 شامل التراس عميل — تصميم حسب الصورة	

لقطات المنظور الخارجي


المنظور الأمامي




منظور أمامي من اليسار

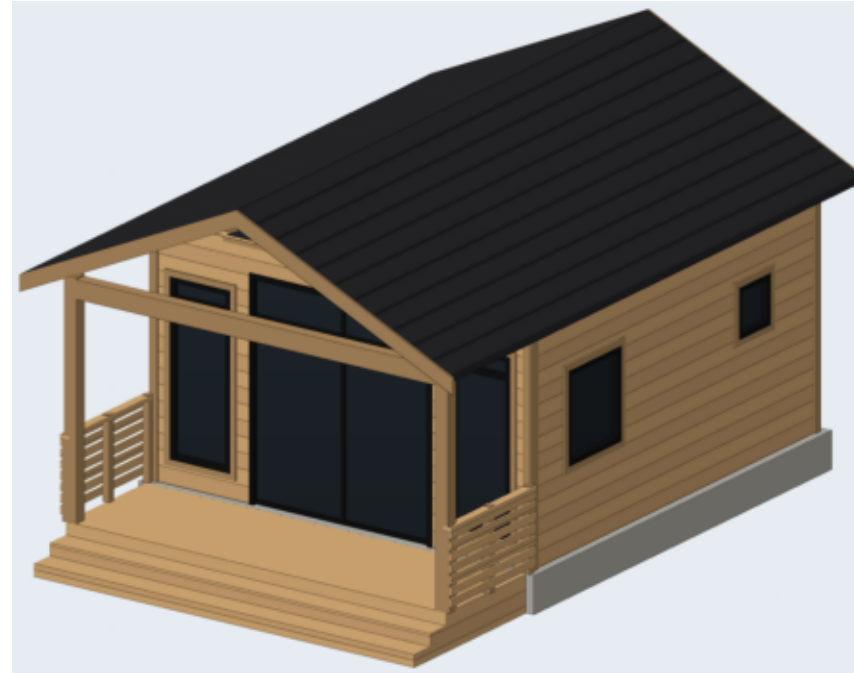

منظور أمامي من اليمين

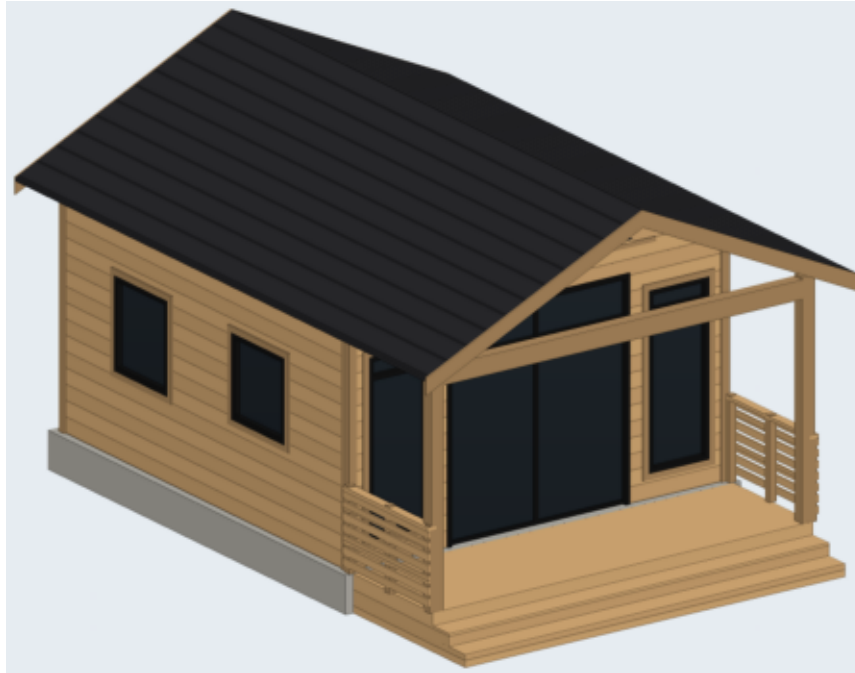

المنظور الخلفي

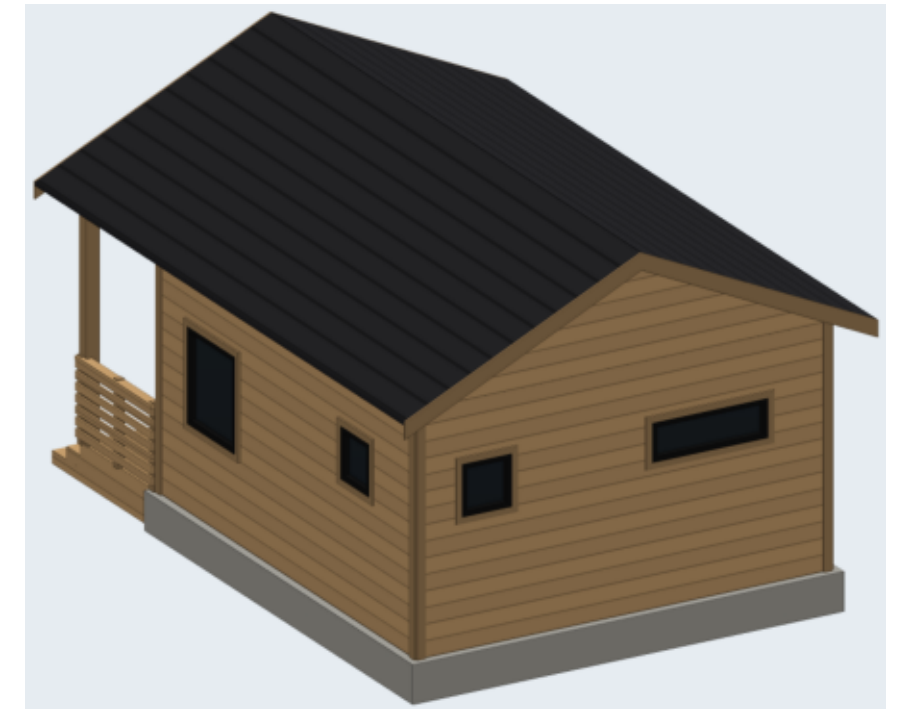

منظور خلفي من اليمين




منظر علوي



المقطع العلوي بالفرش

مقطع أفقي على ارتفاع 1.90 م — توزيع الفرش ومسار الحركة

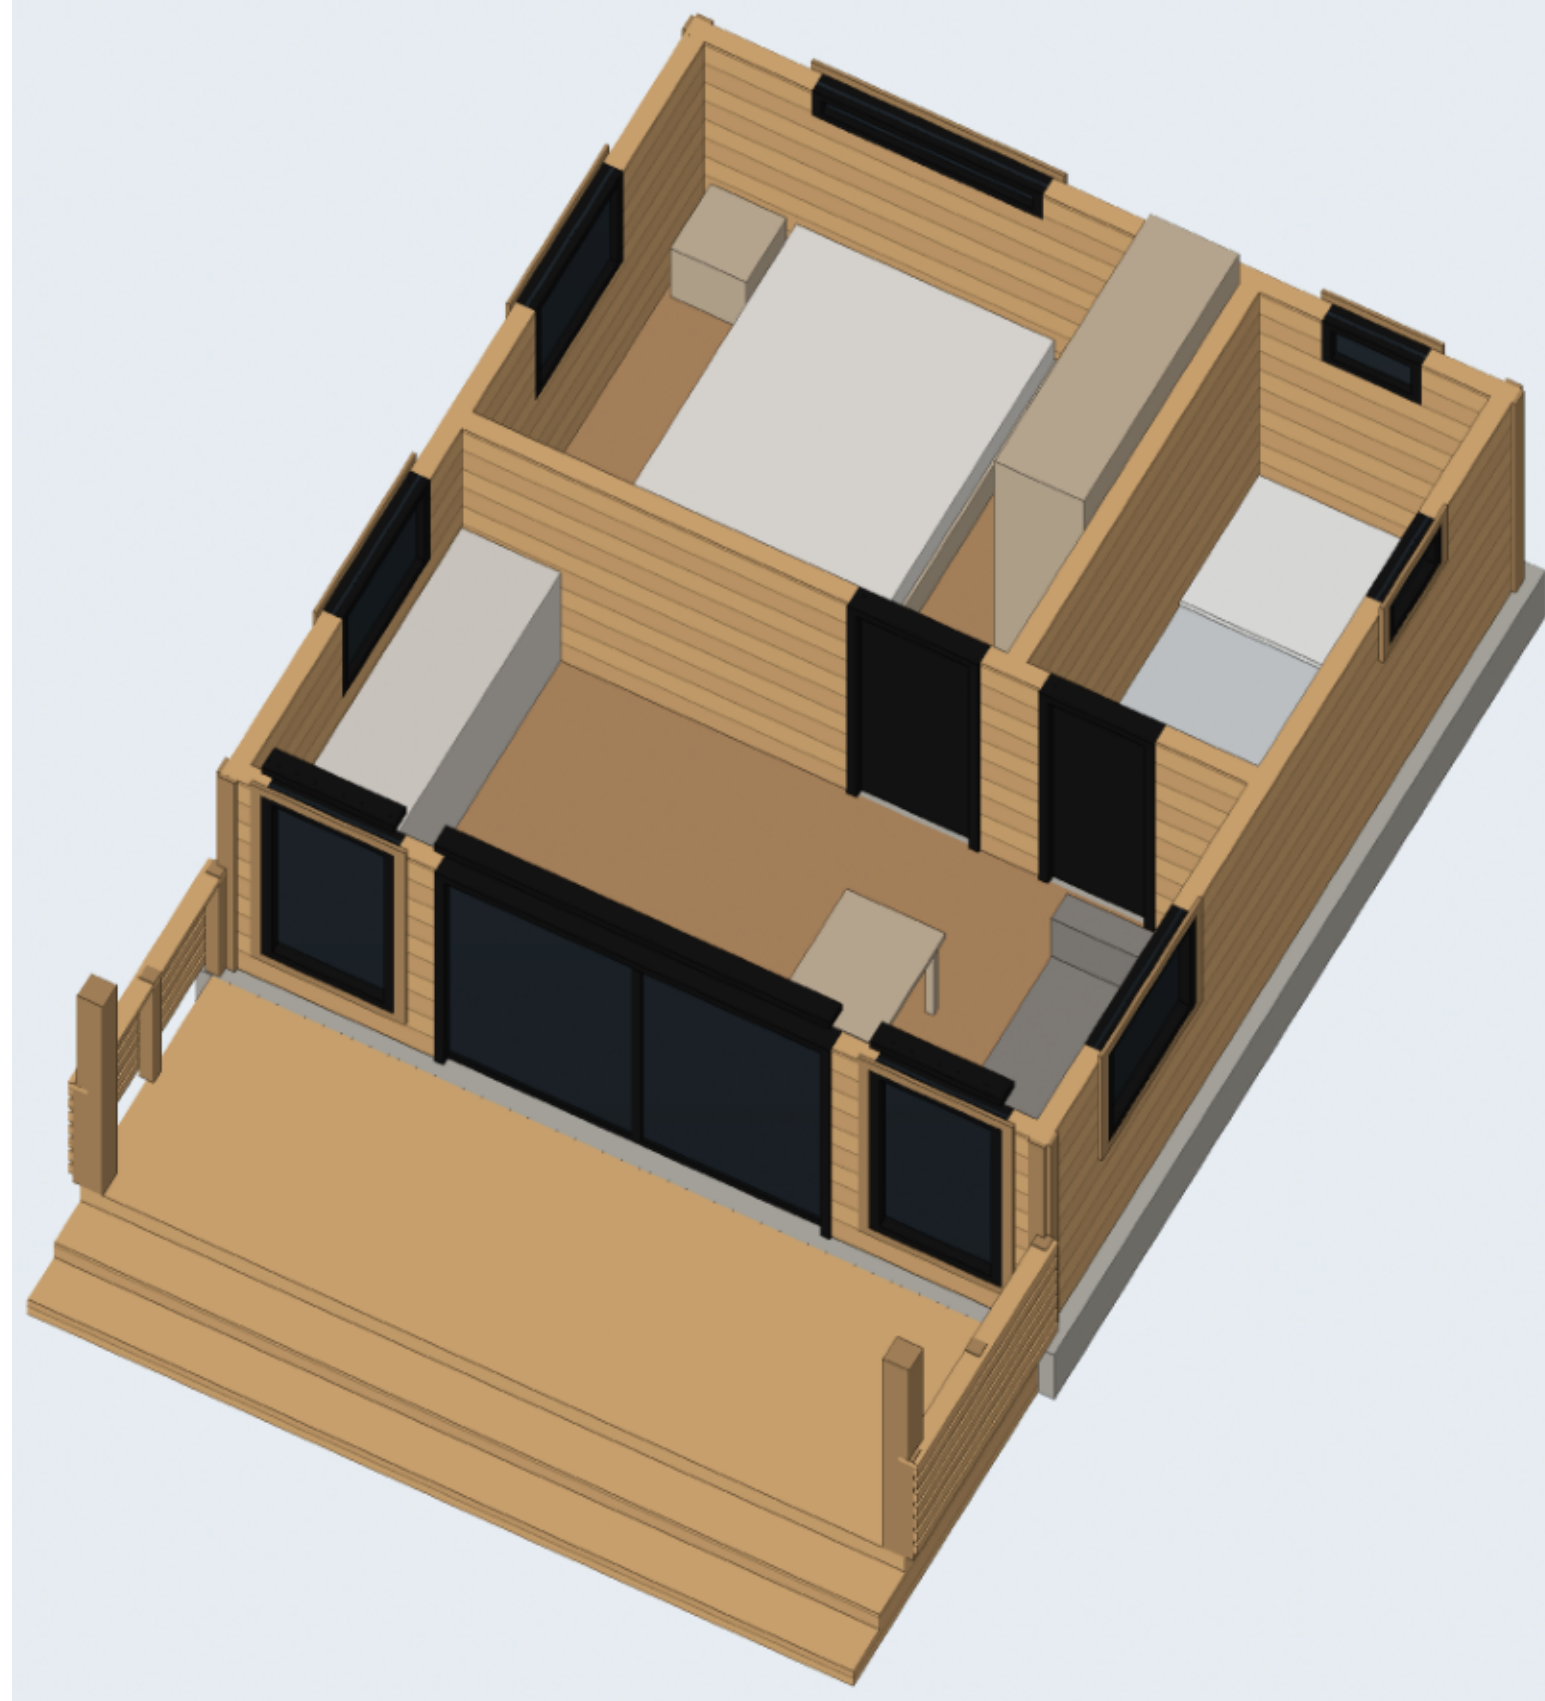

رقم اللوحة

A-09 (9/10)

التاريخ

2026-09-29

المقياس

—

عنوان اللوحة

المقطع العلوي بالفرش

المشروع / العميل

كوخ غرفة وتراس 7×5 شامل التراس
عميل — تصميم حسب الصورة


مصنع وتد الأخشاب
Watad Wood Factory



المنظور ثلاثي الأبعاد والمواد

النمط: جوزي غامق + إطارات سوداء — معاينة تقريبية، الإخراج النهائي من 3ds Max

جدول المواد والألوان

 

الخشب / الصبغة

خشب طبيعي فاتح (بدون صبغة)



القرميد

قرميد رمادي غامق



الزجاج

زجاج عاكس غامق



إطارات الشبابيك والأبواب

إطار ألومنيوم أسود



الكنار والزوايا

نفس الصبغة أعمق درجة



الصبة

خرسانة 45 سم


الدريزين: ألواح أفقية متقاربة (عصري)

تقسيم الشبابيك: بدون | الباب الرئيسي: سحب زجاج


أنواع الدريزين المعتمدة (من مشاريع المصنع)



قوائم رأسية متقاربة (صورة 1)

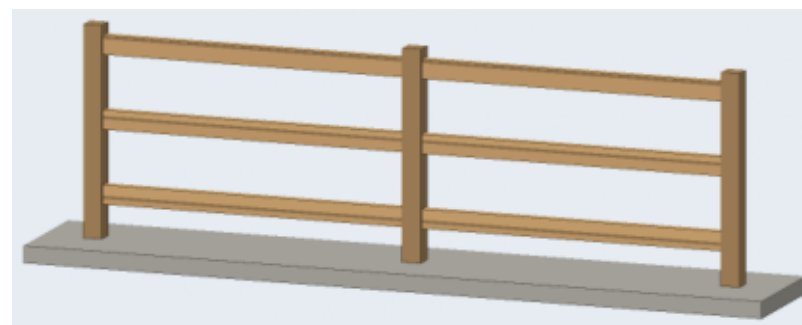

3 مربيع أفقية (صورة 2)

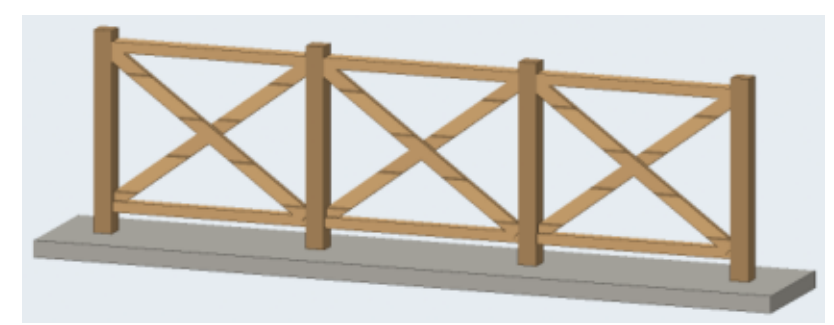

تقاطع X (صورة 5)

رقم اللوحة

A-10 (10/10)

التاريخ

2026-09-29

المقياس

—

عنوان اللوحة

المنظور والمواد

المشروع / العميل

كوخ غرفة وتراس 5x7 شامل التراس
عميل — تصميم حسب الصورة

مصنع وتد الأخشاب

Watad Wood Factory

