
المنظور ثلاثي الأبعاد والمواد

النمط: جوزي غامق + إطارات سوداء — رندر واقعي بخامات حقيقية

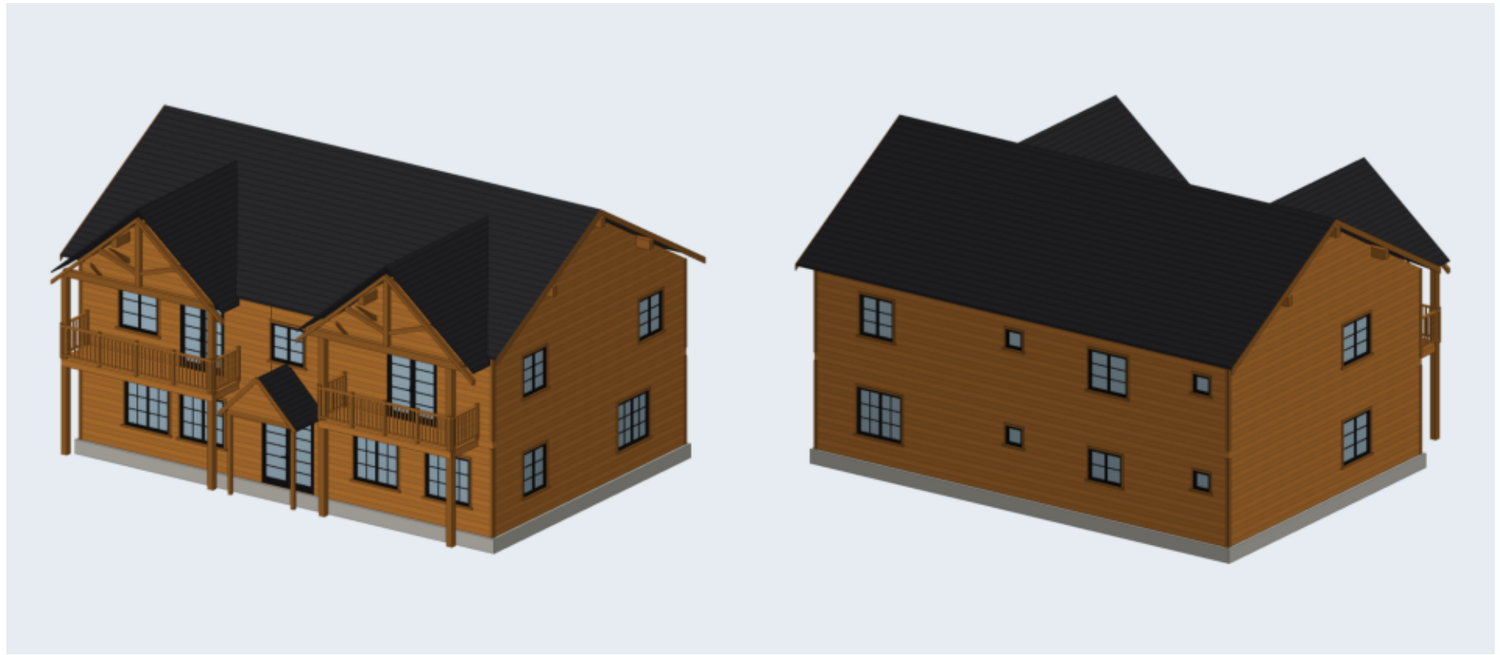

جدول المواد والألوان

الخشب / الصبغة

صبغة عسلي / سيدر

القرميد

قرميد رمادي غامق

الزجاج

زجاج شفاف

إطارات الشبابيك والأبواب

إطار ألمنيوم أسود

الكنار والزوايا

نفس الصبغة أغمق درجة


الصبة

خرسانة 45 سم


الدربزين: ألواح أفقية متقاربة (عصري)

تقسيم الشبابيك: شبكة | الباب الرئيسي: زجاج بتقسيمات (فرنسي)

أنواع الدربزين المعتمدة (من مشاريع المصنع)

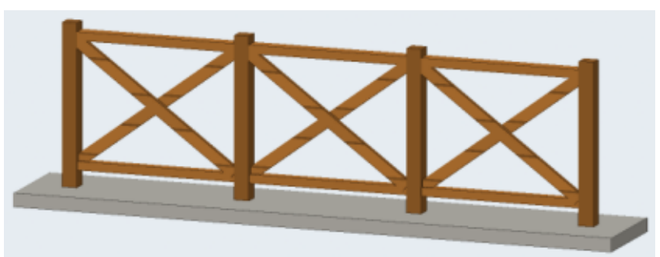

تقاطع X (صورة 5)

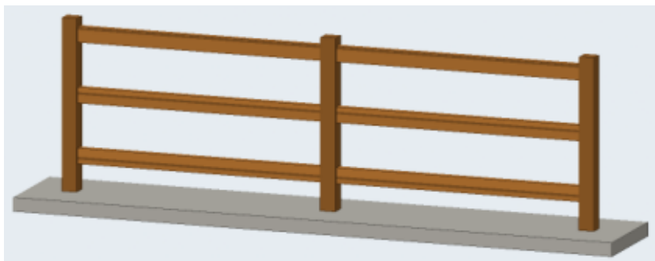

3 مرابيع أفقية (صورة 2)




قوائم رأسية متقاربة (صورة 1)

المشروع / العميل	عنوان اللوحة	المقياس	التاريخ	رقم اللوحة
مصنع وتد الأخشاب Watad Wood Factory — **كوخ خشب دورين — مجلس رجال ومجلس نساء + 4 غرف — 15.00 × 10.00 م (300 م²)** — **عميل — كوخ دورين**	**المنظور والمواد**	**1:50**	**2026-10-24**	**W-01 (1/23)**

المسقط الأفقي مع الفرش — الدور الأرضي

الأبعاد بالسنتيمتر - الجدران: قوائم 7×5 + تلبيس 2.5 من الجهتين (12 سم) | منسوب الأرضية +0.00

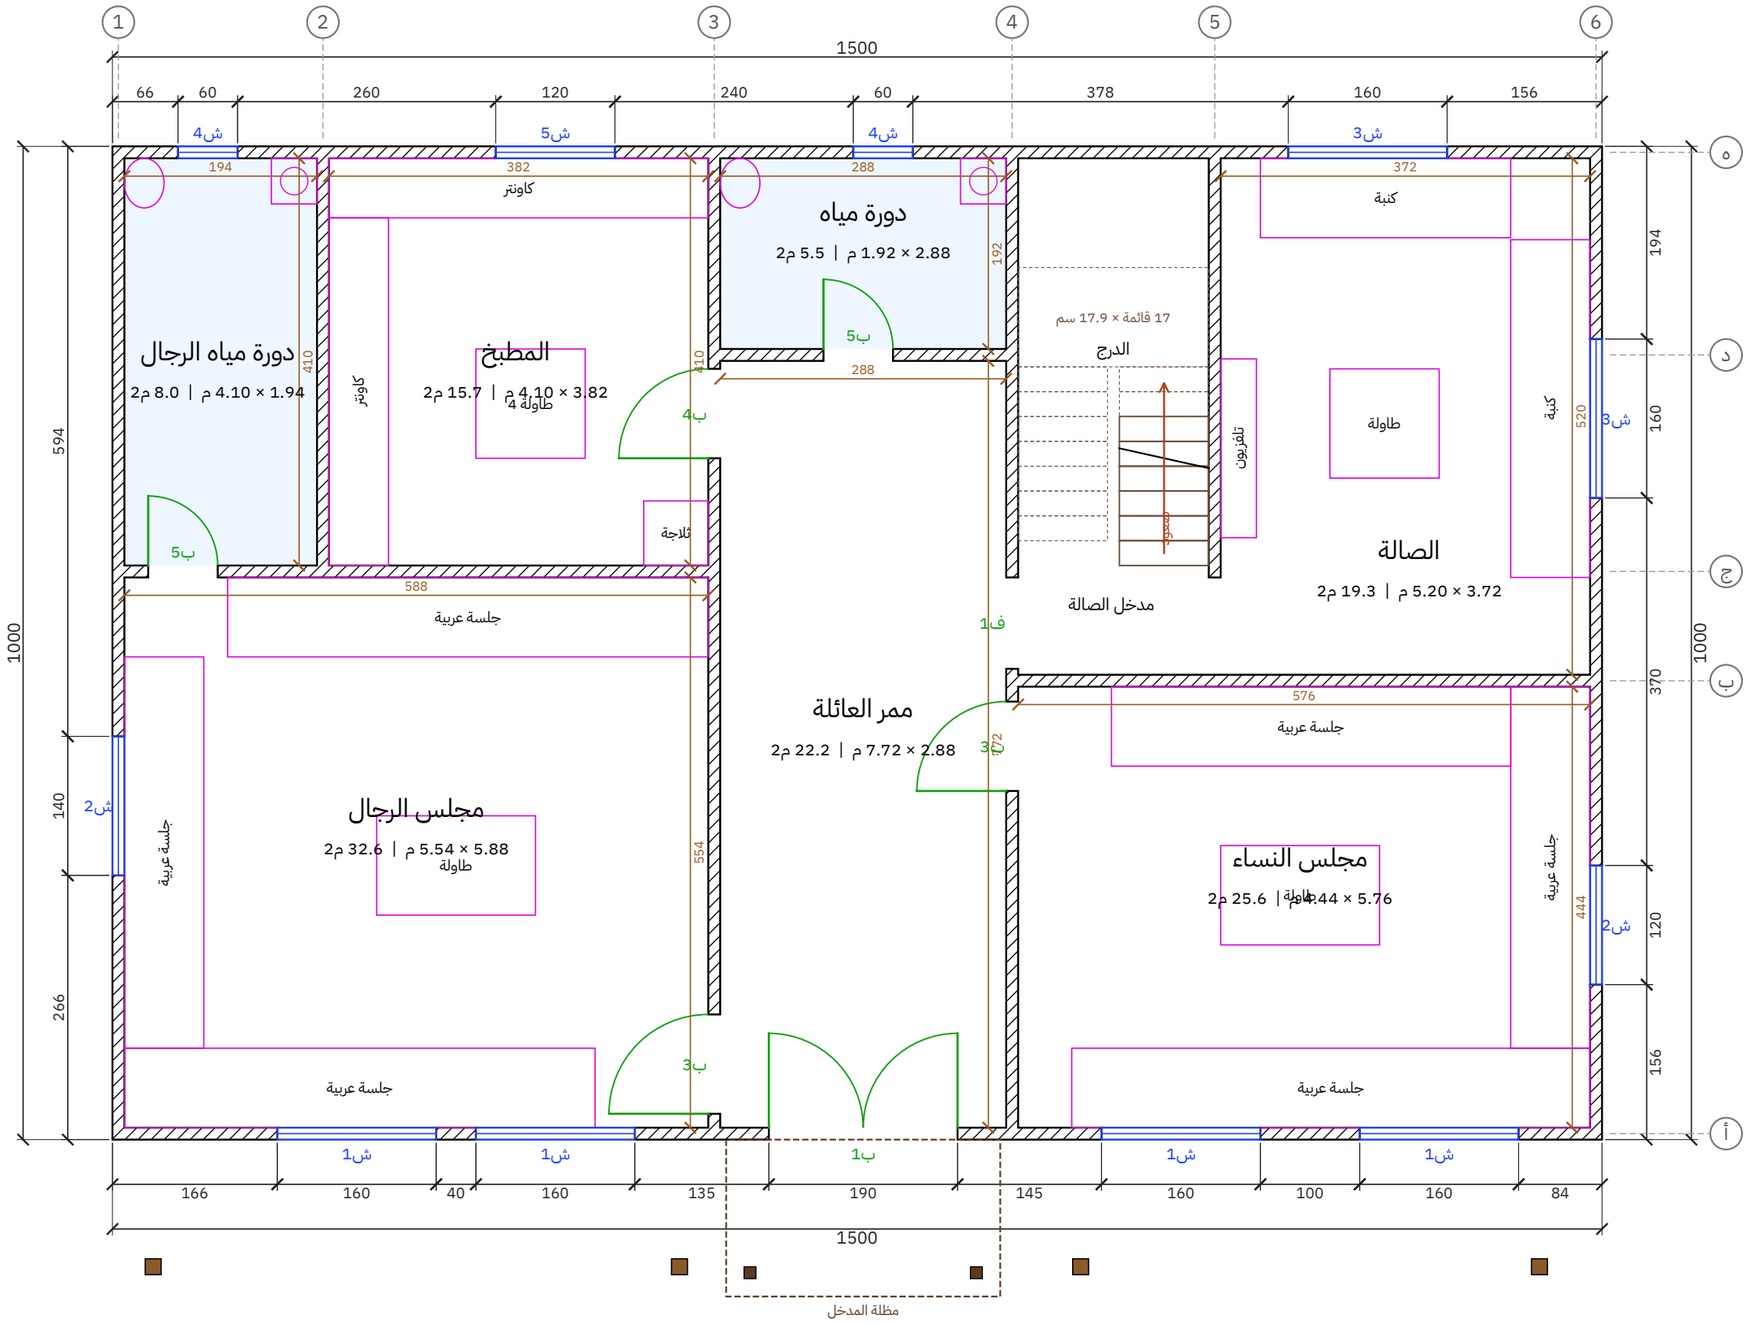


المشروع / العميل	عنوان اللوحة	المقياس	التاريخ	رقم اللوحة
كوخ خشب دورين — مجلس رجال ومجلس نساء + 4 غرف — 15.00 × 10.00 م (300 م²) **عميل — كوخ دورين**	**المسقط الأفقي — الدور الأرضي**	**1:50**	**2026-10-24**	**W-02 (2/23)**

مصنع وتد الأخشاب
Watad Wood Factory


المسقط الأفقي مع الفرش — الدور الأول

الأبعاد بالسنتيمتر - الجدران: قوائم 7×5 + تلبيس 2.5 من الجهتين (12 سم) | منسوب الأرضية +3.05

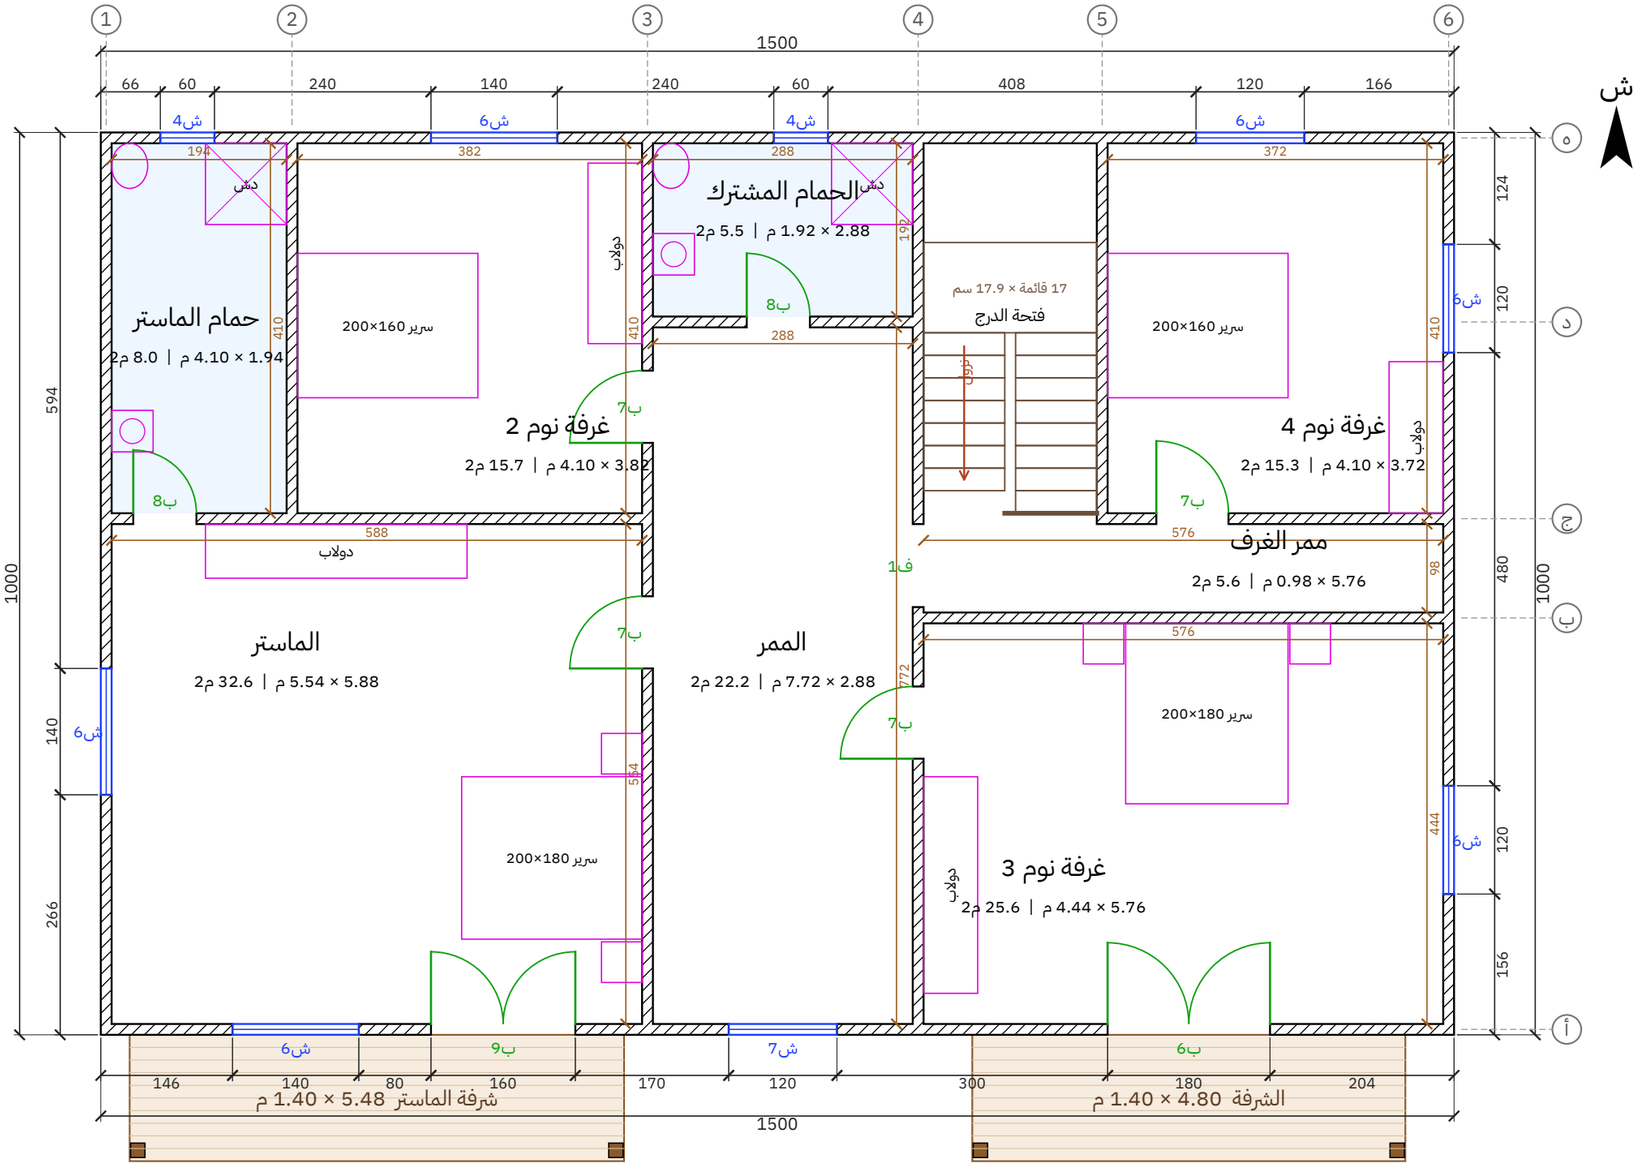


المشروع / العميل	عنوان اللوحة	المقياس	التاريخ	رقم اللوحة
كوخ خشب دورين — مجلس رجال ومجلس نساء + 4 غرف — 15.00 × 10.00 م (300 م²) عميل — كوخ دورين	المسقط الأفقي — الدور الأول	1:50	2026-10-24	W-03 (3/23)

مصنع وتد الأخشاب
Watad Wood Factory

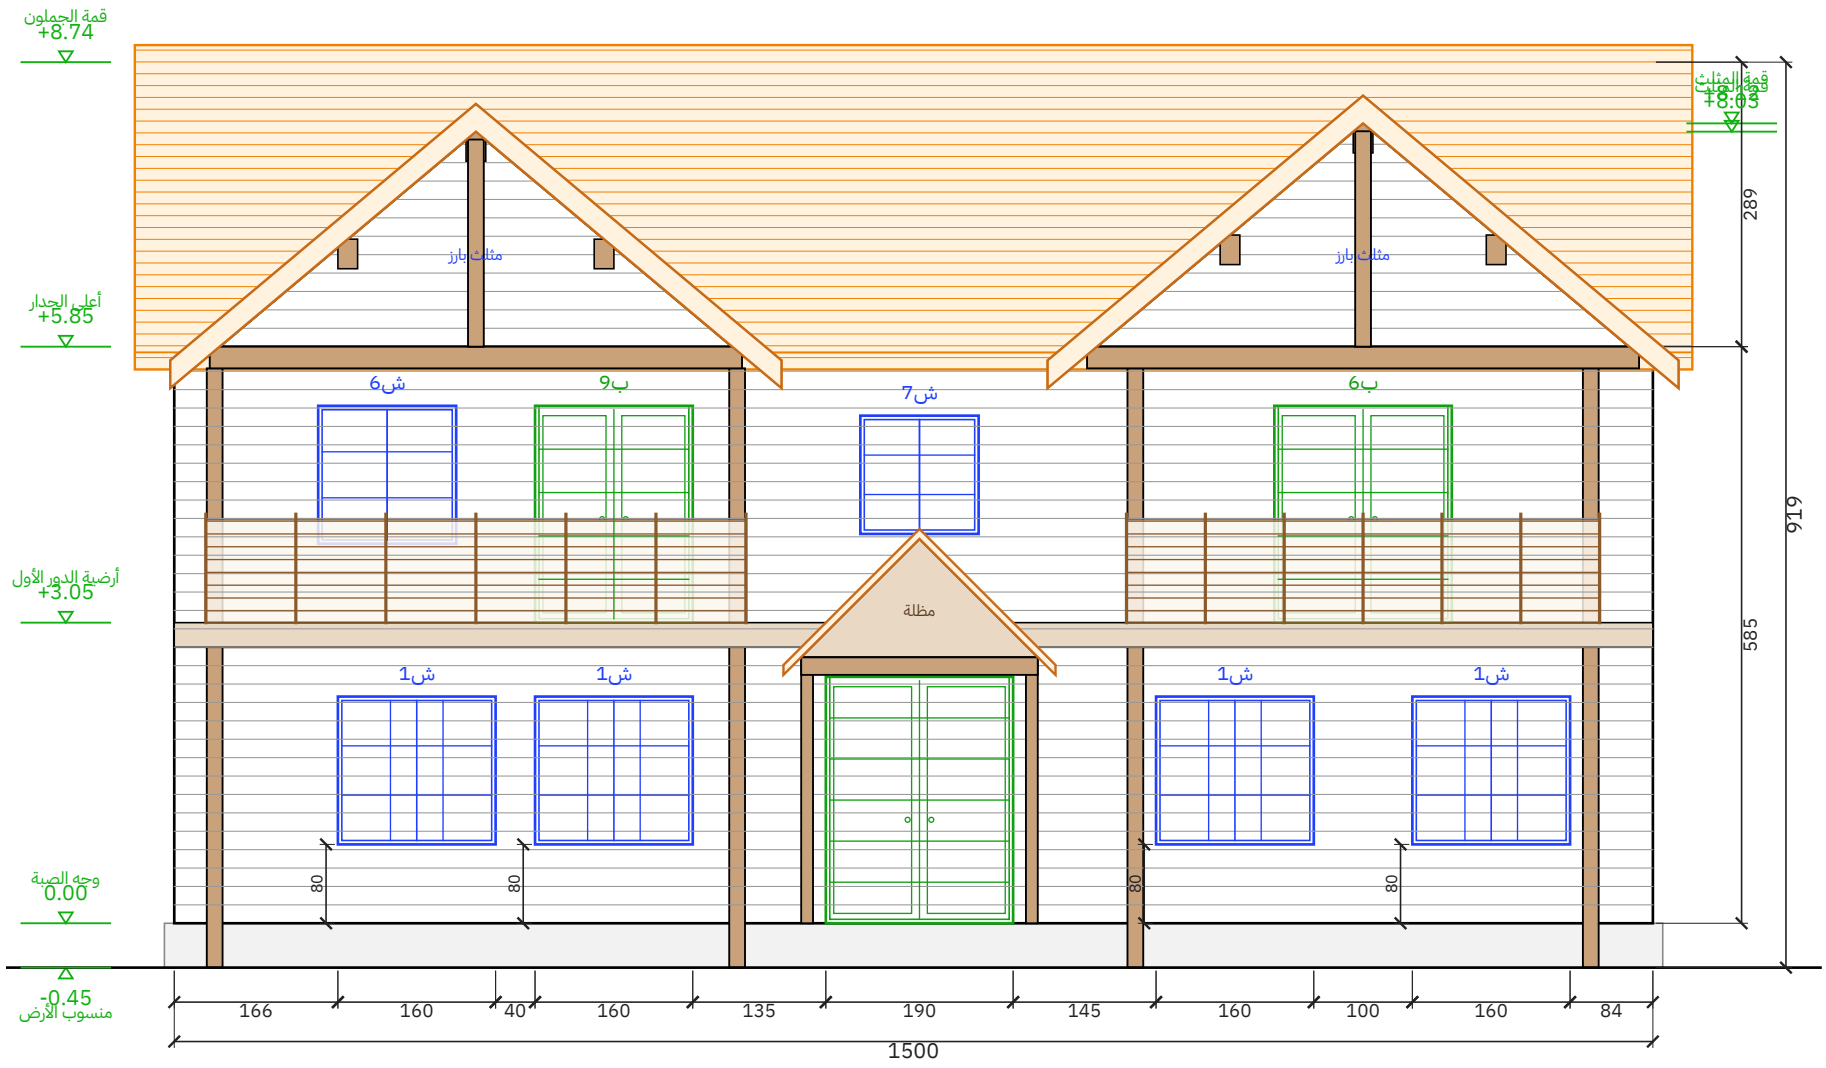

الواجهة الأمامية

مقياس 1:50 | الوحدة: سم

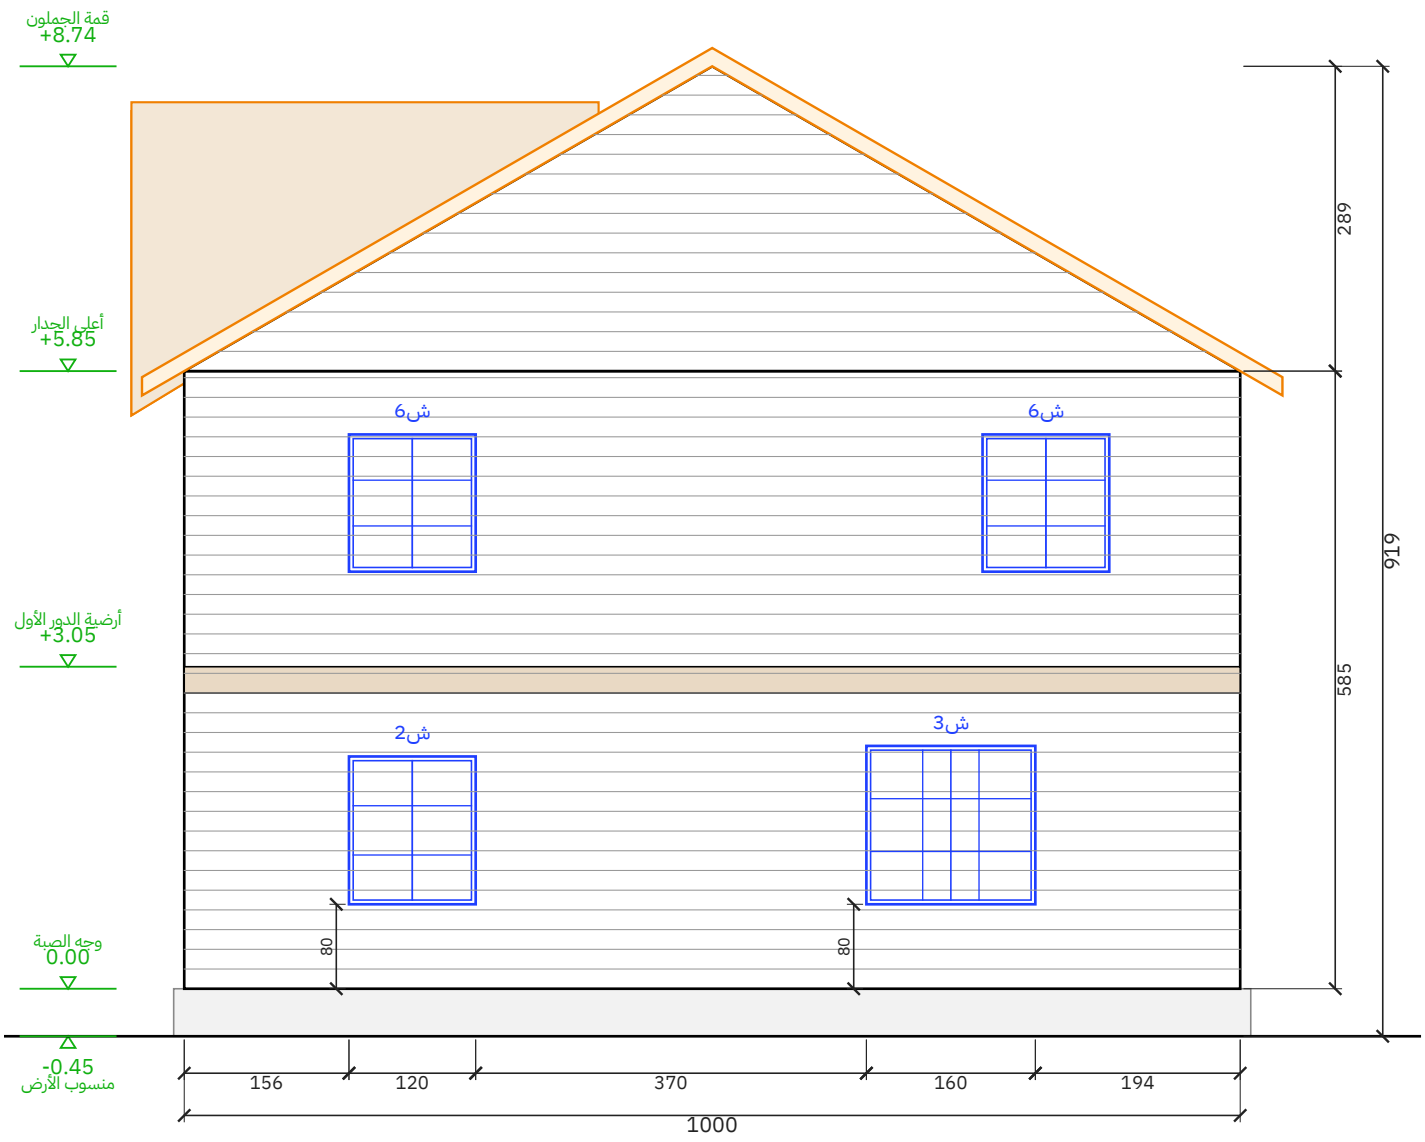


الواجهة الشرقية

مقياس 1:50 | الوحدة: سم


المشروع / العميل	عنوان اللوحة	المقياس	التاريخ	رقم اللوحة
كوخ خشب دورين – مجلس رجال ومجلس نساء + 4 غرف – 10.00 × 15.00 م (300 م²) عميل – كوخ دورين	الواجهة الأمامية والواجهة الشرقية	1:50	2026-10-24	W-04 (4/23)

مصنع وتد الأخشاب
Watad Wood Factory

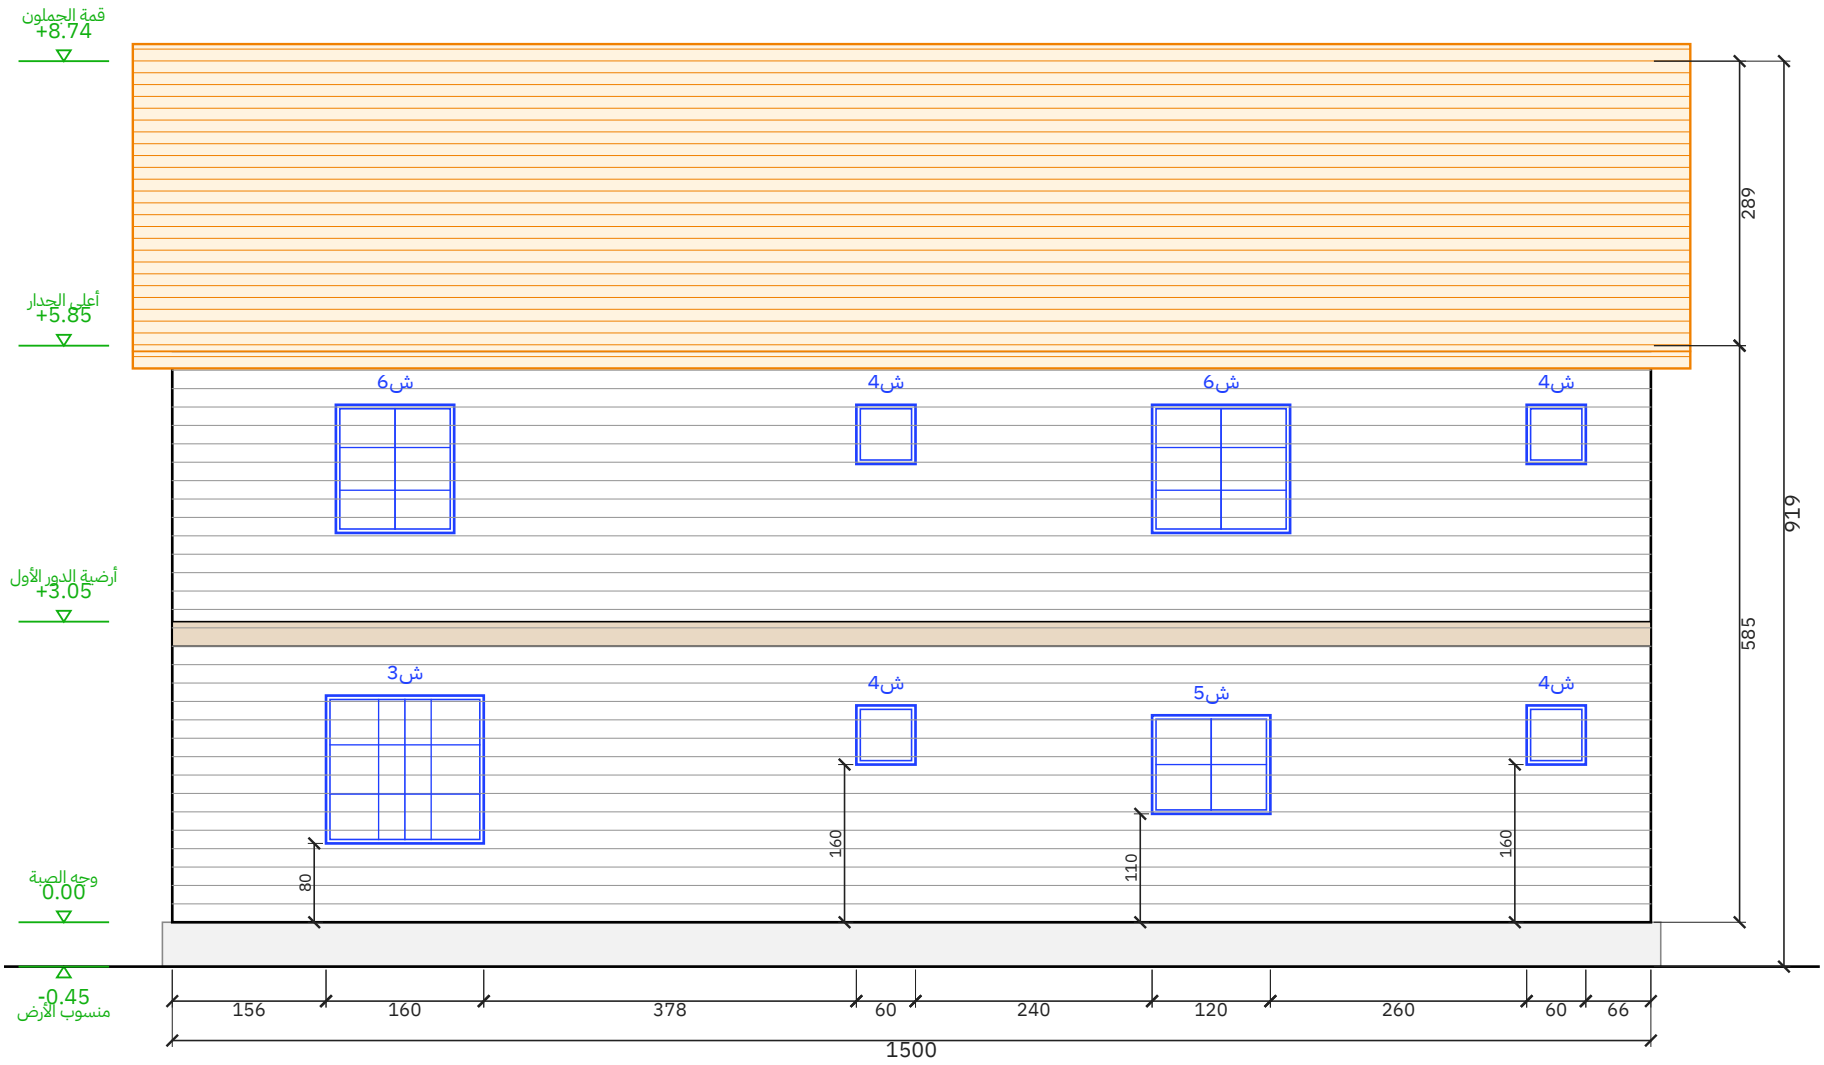

الواجهة الخلفية

مقياس 1:50 | الوحدة: سم

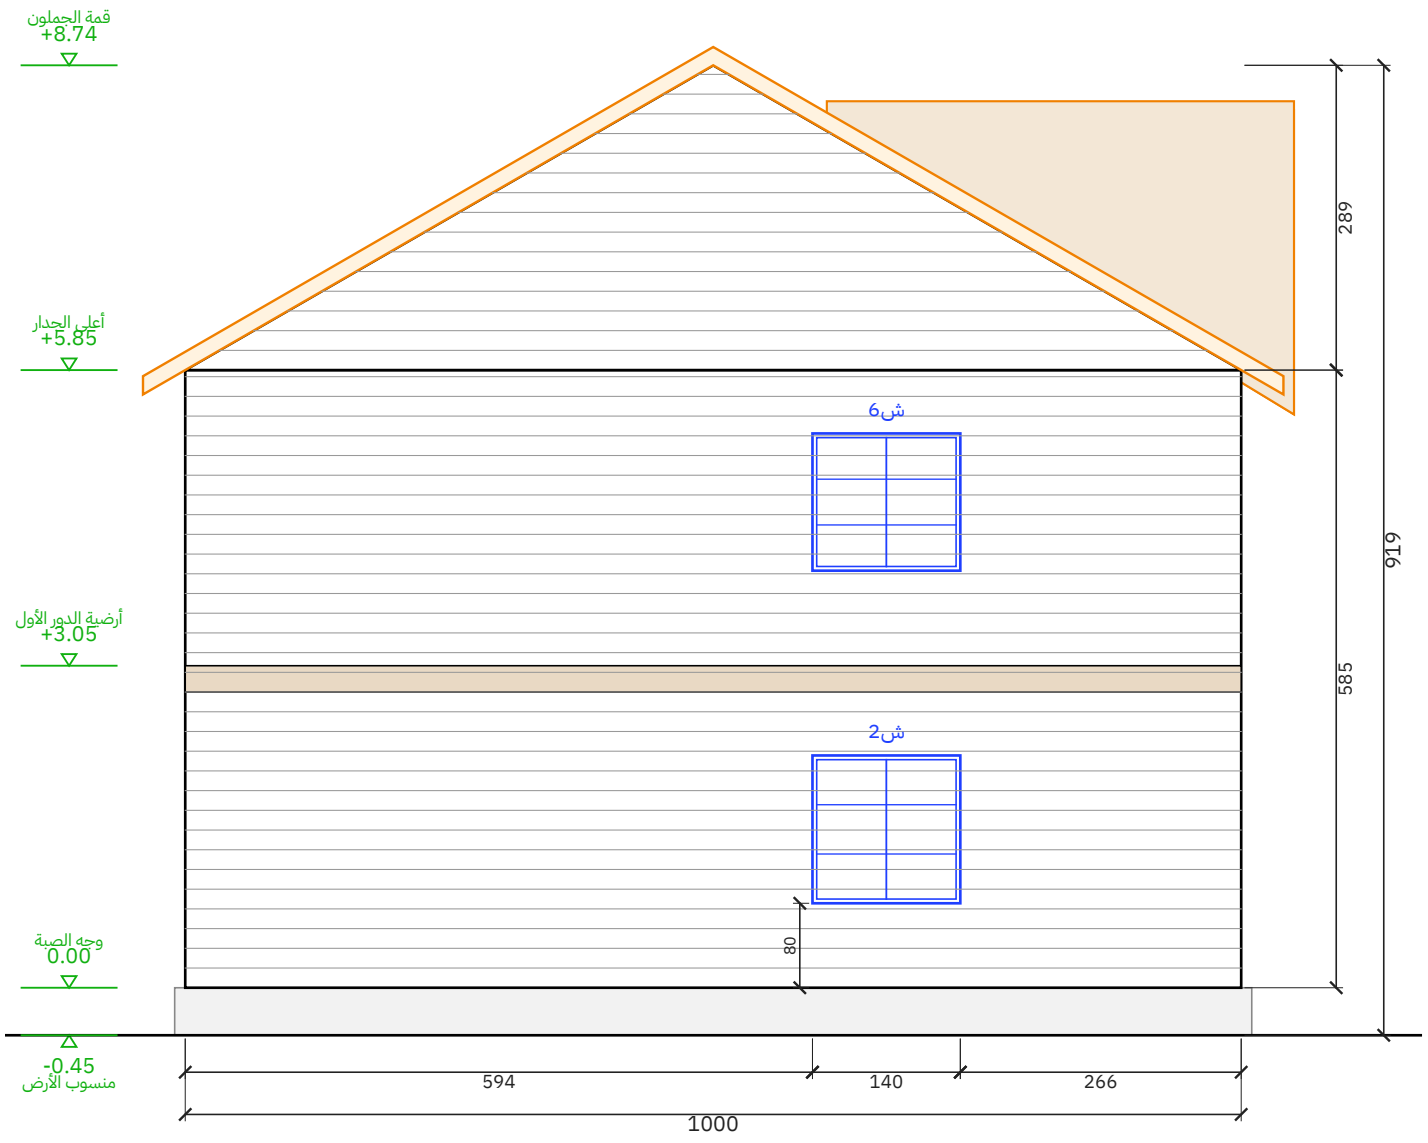

الواجهة الغربية


مقياس 1:50 | الوحدة: سم

المشروع / العميل	عنوان اللوحة	المقياس	التاريخ	رقم اللوحة
كوخ خشب دورين – مجلس رجال ومجلس نساء + 4 غرف – 10.00 × 15.00 م (300 م²) عميل – كوخ دورين	الواجهة الخلفية والواجهة الغربية	1:50	2026-10-24	W-05 (5/23)


مصنع وتد الأخشاب
Watad Wood Factory

قطاع عرضي أ-أ

مقياس 1:50 | الوحدة: سم

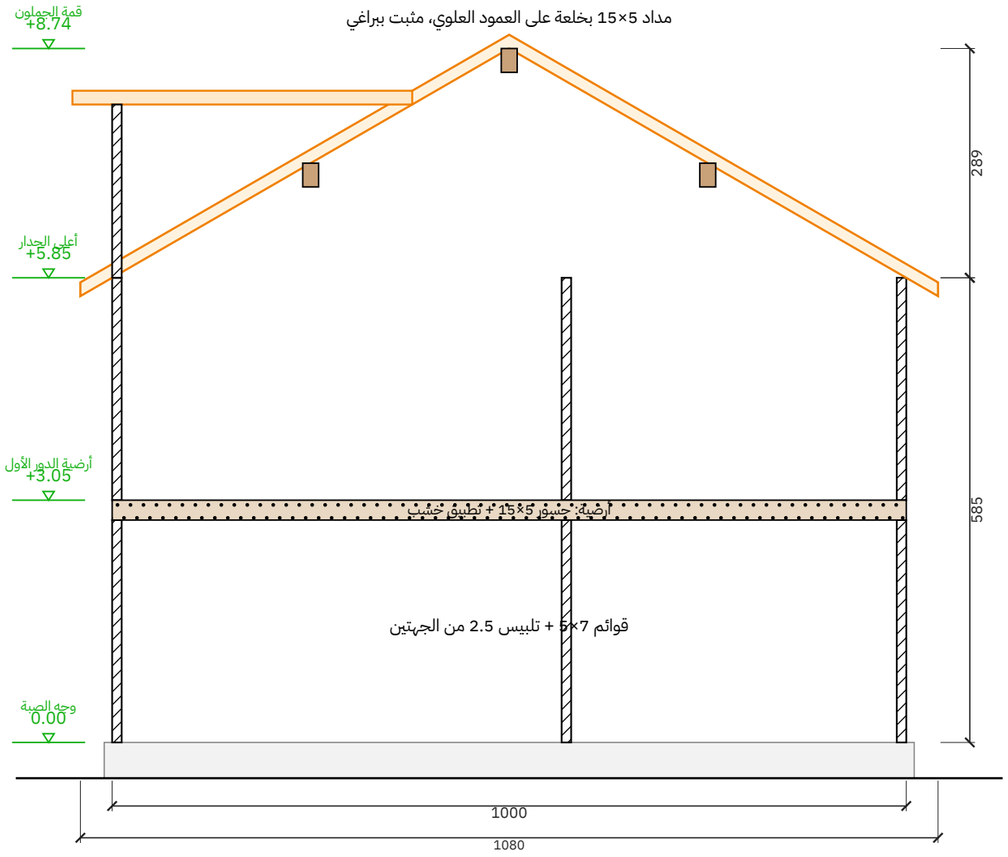


تفصيلة جلوس المداد على العلوي (1:5)

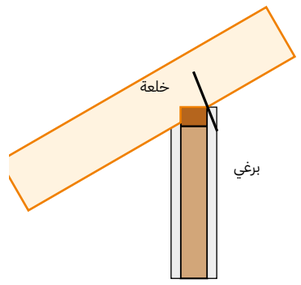

علوي 7×5 على قائم 7×5

مسقط السقف (جملون)

رفرف 40 سم من كل جهة | مقياس 1:50

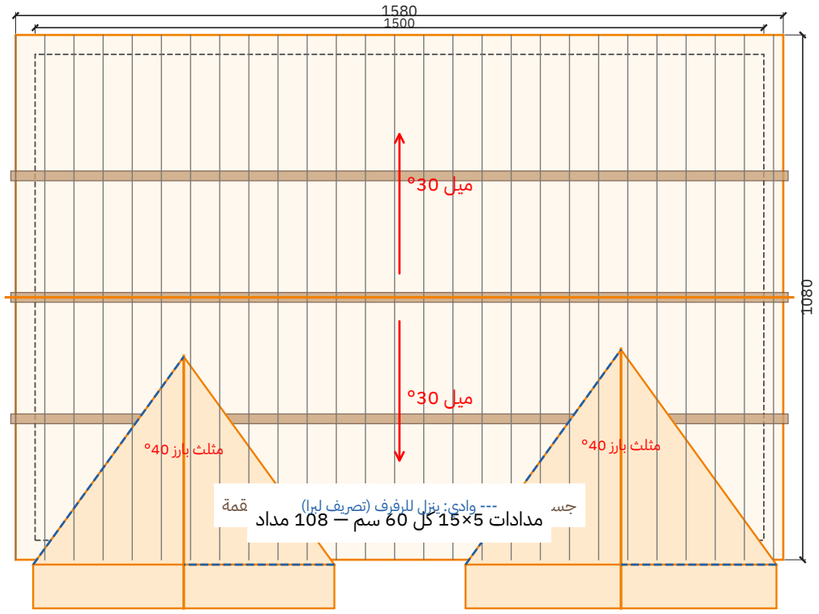

المشروع / العميل	عنوان اللوحة	المقياس	التاريخ	رقم اللوحة
كوخ خشب دورين — مجلس رجال ومجلس نساء + 4 غرف — 15.00 × 10.00 م (300 م²) **عميل — كوخ دورين**	**مسقط السقف والقطاع**	**—**	**2026-10-24**	**W-06 (6/23)**

مصنع وتد الأخشاب
Watad Wood Factory

جدول مقاسات الأبواب والشبابيك

مقاس الفتحة الصافي في الجدار - الوحدة: سم

الرمز	النوع	العرض (سم)	الارتفاع (سم)	ارتفاع الجلسة (سم)	العدد	الموقع
ب1	باب مزدوج	190	250	-	1	الأمامية
ب3	باب	100	220	-	1	مجلس الرجال
ب3	باب	90	210	-	1	مجلس النساء
ب4	باب	90	210	-	1	المطبخ
ب5	باب	70	210	-	2	دورة مياه الرجال - دورة مياه
ب6	باب مزدوج	180	220	-	1	الأمامية
ب7	باب	80	210	-	4	الماستر - غرفة 2 - غرفة 3 - غرفة 4
ب8	باب	70	210	-	2	حمام الماستر - الحمام المشترك
ب9	باب مزدوج	160	220	-	1	الأمامية
ف1	باب	92	220	-	2	الممر — الصالة - الممر — الدرج
ش1	شباك	160	150	80	4	الأمامية 4
ش2	شباك	120	140	80	1	الشرقية
ش2	شباك	140	140	80	1	الغربية
ش3	شباك	160	150	80	2	الشرقية - الخلفية
ش4	شباك	60	60	160	4	الخلفية 4
ش5	شباك	120	100	110	1	الخلفية
ش6	شباك	140	140	80	1	الأمامية
ش6	شباك	120	130	90	3	الشرقية 2 - الخلفية
ش6	شباك	140	130	90	2	الخلفية - الغربية
ش7	شباك	120	120	90	1	الأمامية

الإجمالي: أبواب 16 - شبابيك 20

جدول المساحات وبيانات المشروع


بيانات المشروع

البند	البيان
المشروع	كوخ خشب دورين — مجلس رجال ومجلس نساء + 4 غرف — 15.00 × 10.00 م (300 م²)
العميل	عميل — كوخ دورين
الموقع	—
الاستخدام	سكن عائلي
التاريخ	2026-10-24
نظام البناء	هيكل خشب 5×7 + تلبيس 2.5 سم من الجهتين
السقف	جملون 30° — قرميد معدني + 2 مثلث بارز


جدول المساحات

م	الفراغ	الأبعاد (م)	المساحة (م2)
1	أرضي — مجلس الرجال	5.88 × 5.54	32.58
2	أرضي — دورة مياه الرجال	1.94 × 4.10	7.95
3	أرضي — المطبخ	3.82 × 4.10	15.66
4	أرضي — ممر العائلة	2.88 × 7.72	22.23
5	أرضي — دورة مياه	2.88 × 1.92	5.53
6	أرضي — مجلس النساء	5.76 × 4.44	25.57
7	أرضي — مدخل الصالة	1.92 × 1.04	2.00
8	أرضي — الدرج	1.92 × 4.10	7.87
9	أرضي — الصالة	3.72 × 5.20	19.34
10	أول — الماستر	5.88 × 5.54	32.58
11	أول — حمام الماستر	1.94 × 4.10	7.95
12	أول — غرفة نوم 2	3.82 × 4.10	15.66
13	أول — الممر	2.88 × 7.72	22.23
14	أول — الحمام المشترك	2.88 × 1.92	5.53
15	أول — غرفة نوم 3	5.76 × 4.44	25.57
16	أول — ممر الغرف	5.76 × 0.98	5.64
17	أول — غرفة نوم 4	3.72 × 4.10	15.25
	المساحة الصافية الداخلية		269.17
	الشرفة	**4.80 × 1.40**	**6.72**
	شرفة الماستر	**5.48 × 1.40**	**7.67**
	المساحة الإجمالية المبنية	**15.00 × 10.00 × 2 دور**	**300.00**
	المساحة الكلية (المبنية + التراسات)		**314.39**

تأطير جدار أ-جنوب — الطول 1488 سم، الارتفاع 280 سم

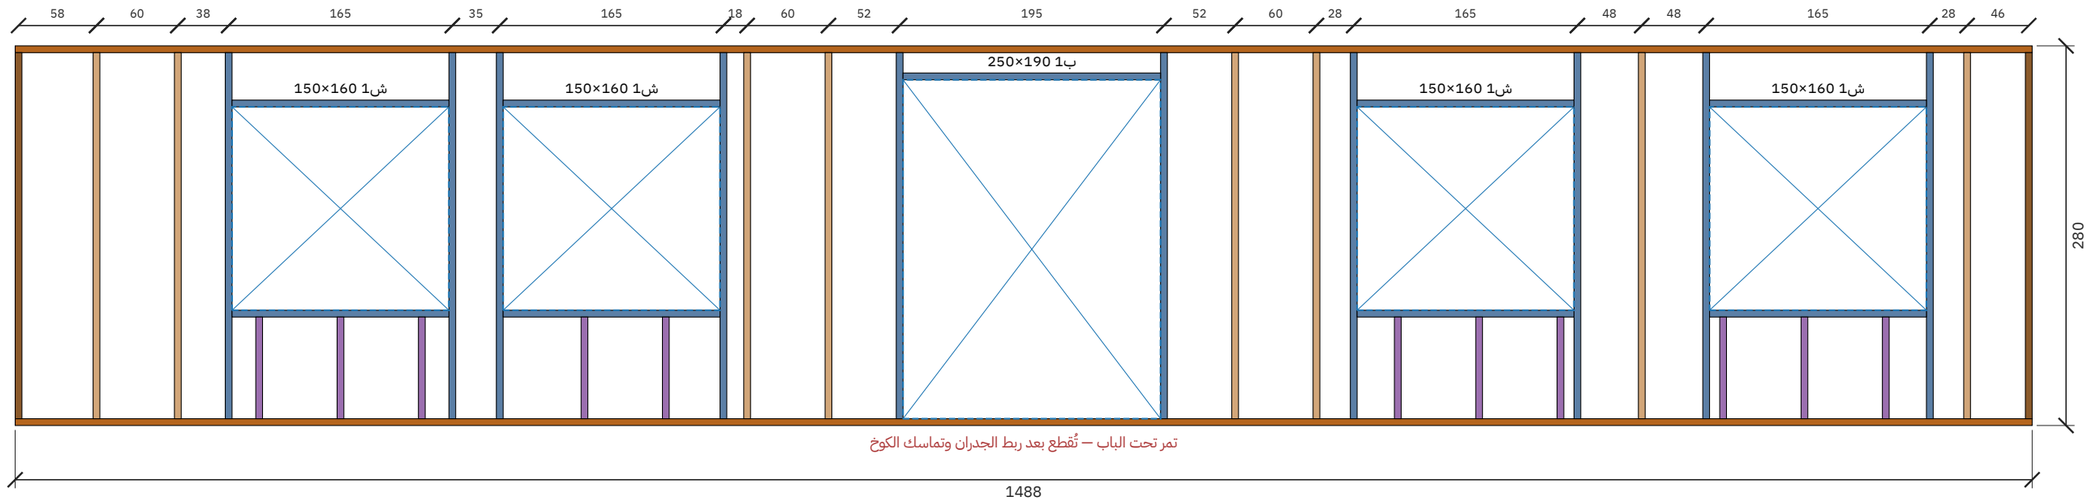

تأطير جدار أ-شرق — الطول 988 سم، الارتفاع 280 سم

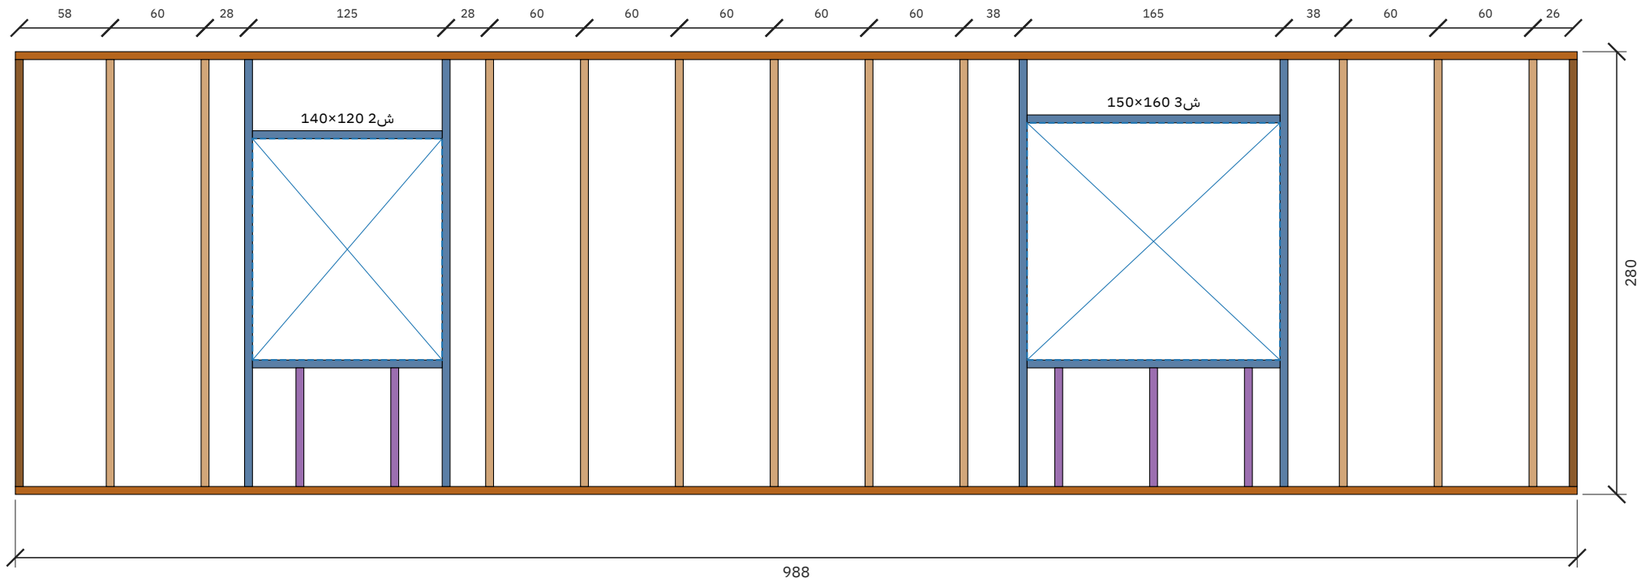


قاعدة سفلية | علوي | عمود | عمود زاوية | جنب فتحة | رأس فتحة | جلسة شباك | عمود قصير


المشروع / العميل	عنوان اللوحة	المقياس	التاريخ	رقم اللوحة
كوخ خشب دورين — مجلس رجال ومجلس نساء + 4 غرف — 15.00 × 10.00 م (300 م²) **عميل — كوخ دورين**	**لوحات التأطير (للورشة)**	**—**	**2026-10-24**	**W-09 (9/23)**

مصنع وتد الأخشاب
Watad Wood Factory

تأطير جدار أ-شمال — الطول 1488 سم، الارتفاع 280 سم

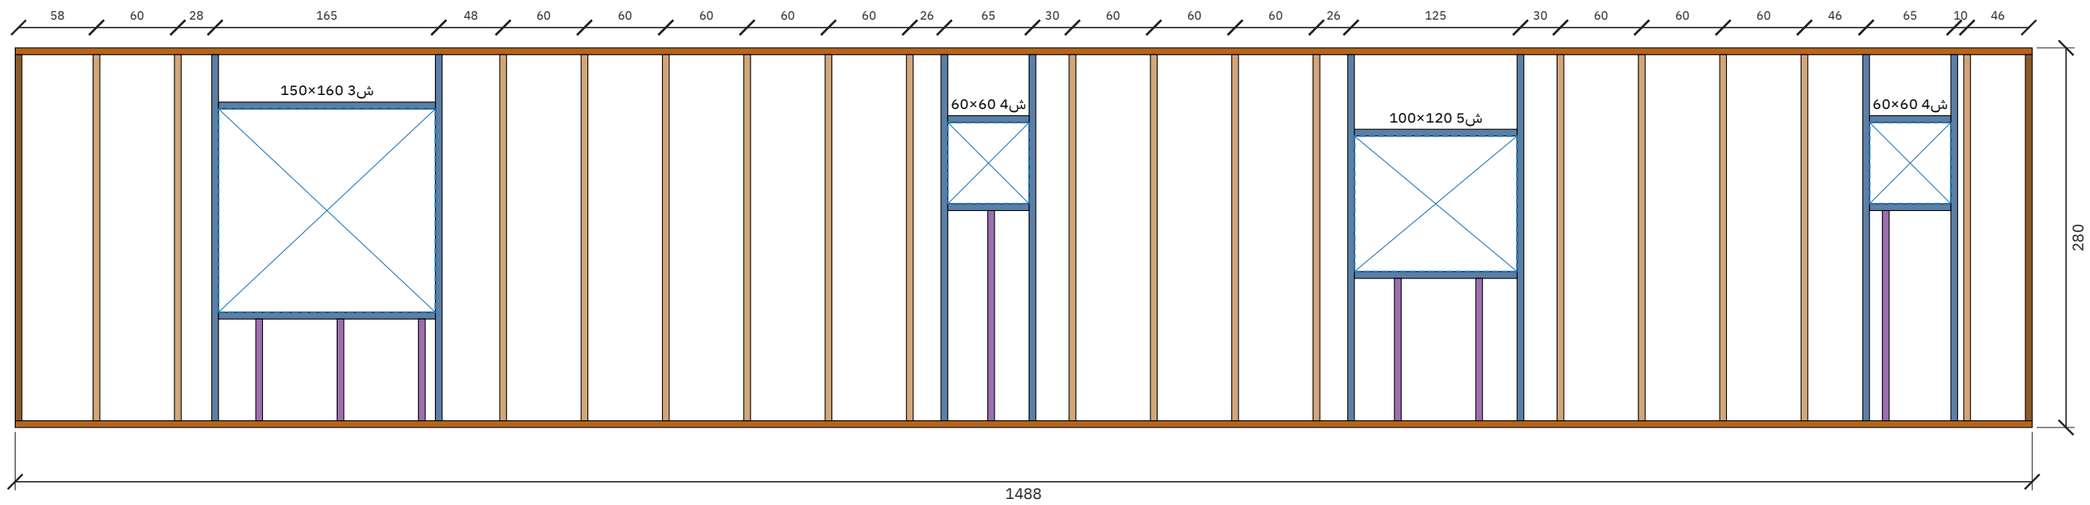


تأطير جدار أ-غرب — الطول 988 سم، الارتفاع 280 سم

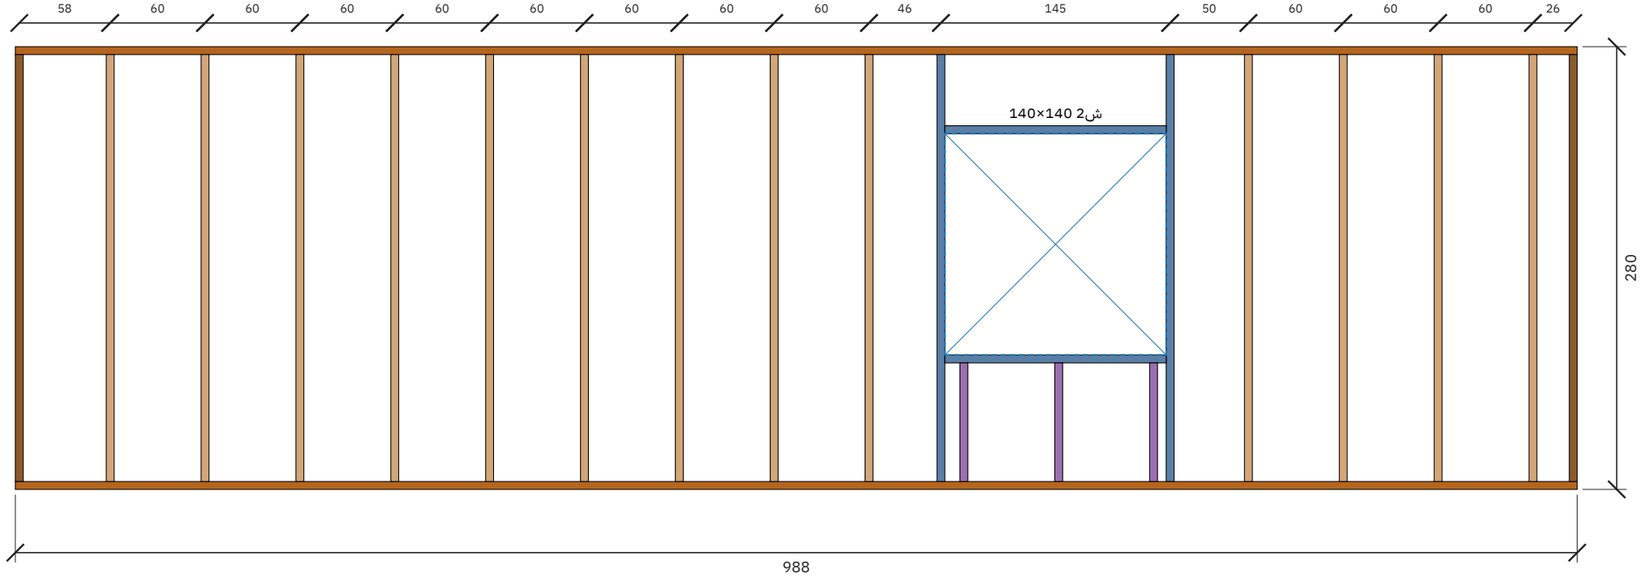


قاعدة سفلية | علوي | عمود | عمود زاوية | جنب فتحة | رأس فتحة | جلسة شباك | عمود قصير

مصنع وتد الأخشاب Watad Wood Factory	المشروع / العميل كوخ خشب دورين — مجلس رجال ومجلس نساء + 4 غرف — 15.00 × 10.00 م (300 م²) عميل — كوخ دورين	عنوان اللوحة لوحات التأطير (للورشة)	المقياس —	التاريخ 2026-10-24	رقم اللوحة W-10 (10/23)

تأطير جدار أ-جدار المجلس — الطول 988 سم، الارتفاع 280 سم (داخلي)

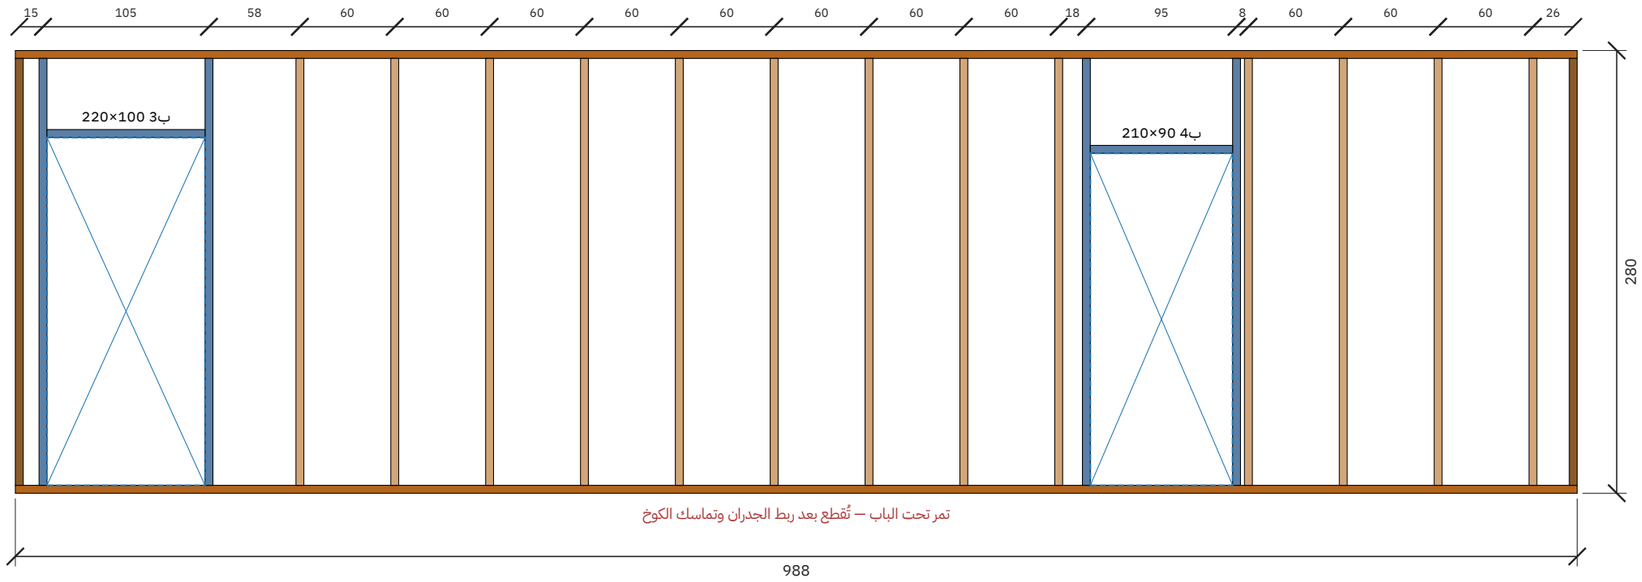


تأطير جدار أ-خلف المجلس — الطول 600 سم، الارتفاع 280 سم (داخلي)

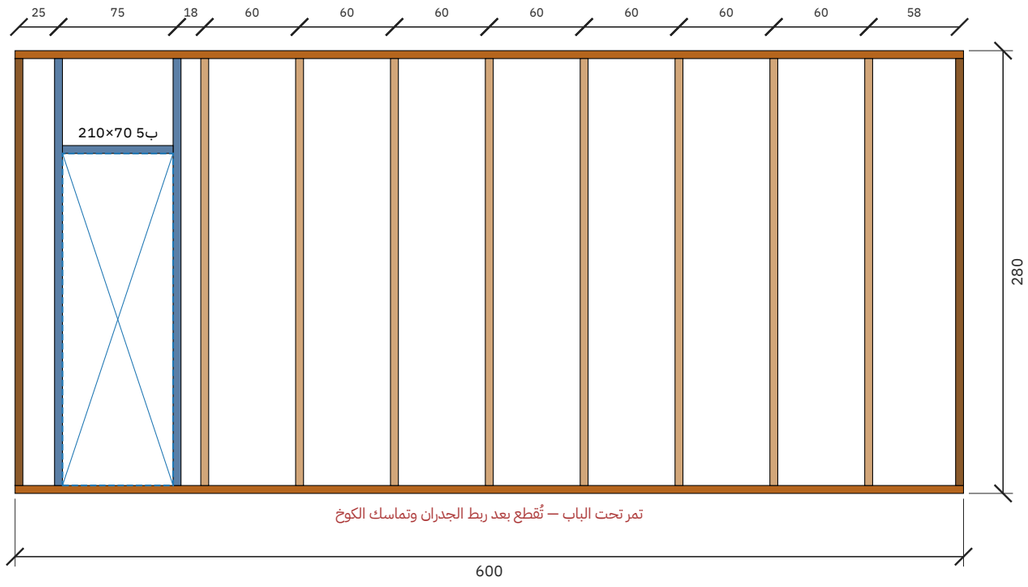


قاعدة سفلية | علوي | عمود | عمود زاوية | جنب فتحة | رأس فتحة | جلسة شباك | عمود قصير

مصنع وتد الأخشاب Watad Wood Factory	المشروع / العميل **كوخ خشب دورين — مجلس رجال ومجلس نساء + 4 غرف — 15.00 × 10.00 م (300 م²)** **عميل — كوخ دورين**	عنوان اللوحة **لوحات التأطير (للورشة)**	المقياس **—**	التاريخ **2026-10-24**	رقم اللوحة **W-11 (11/23)**

تأطير جدار أ-جدار الدورة — الطول 422 سم، الارتفاع 280 سم (داخلي)

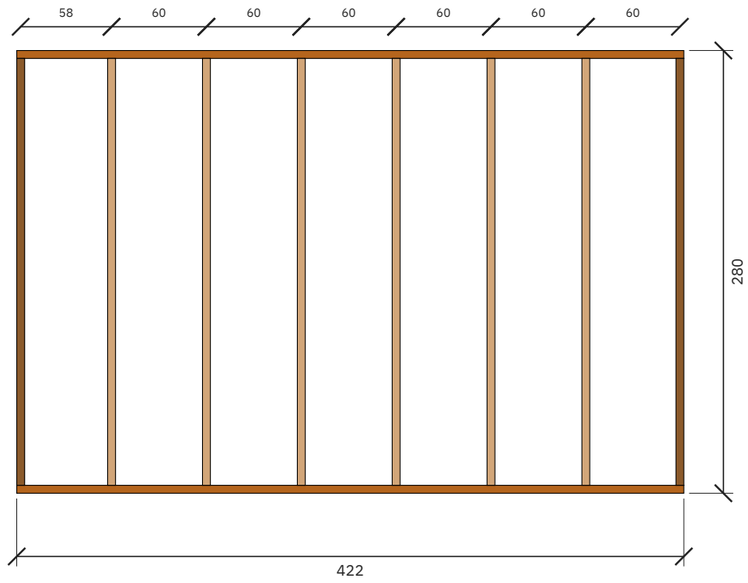

تأطير جدار أ-دورة الممر — الطول 300 سم، الارتفاع 280 سم (داخلي)

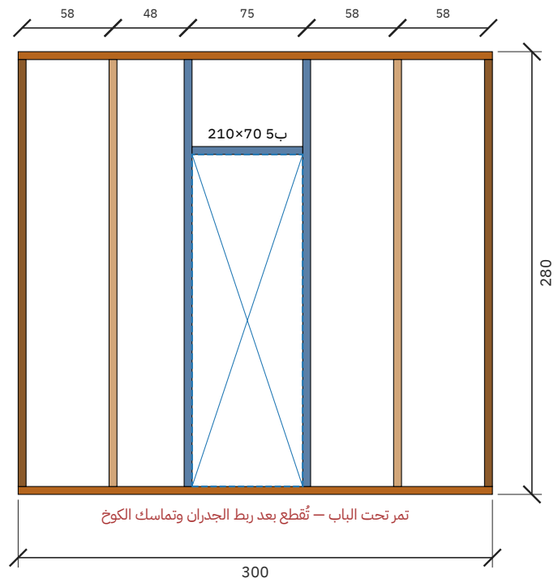


قاعدة سفلية | علوي | عمود | عمود زاوية | جنب فتحة | رأس فتحة | جلسة شباك | عمود قصير


المشروع / العميل	عنوان اللوحة	المقياس	التاريخ	رقم اللوحة
كوخ خشب دورين — مجلس رجال ومجلس نساء + 4 غرف — 15.00 × 10.00 م (300 م²) **عميل — كوخ دورين**	**لوحات التأطير (للورشة)**	**—**	**2026-10-24**	**W-12 (12/23)**

مصنع وتد الأخشاب
Watad Wood Factory

تأطير جدار أ-جدار النساء — الطول 988 سم، الارتفاع 280 سم (داخلي)

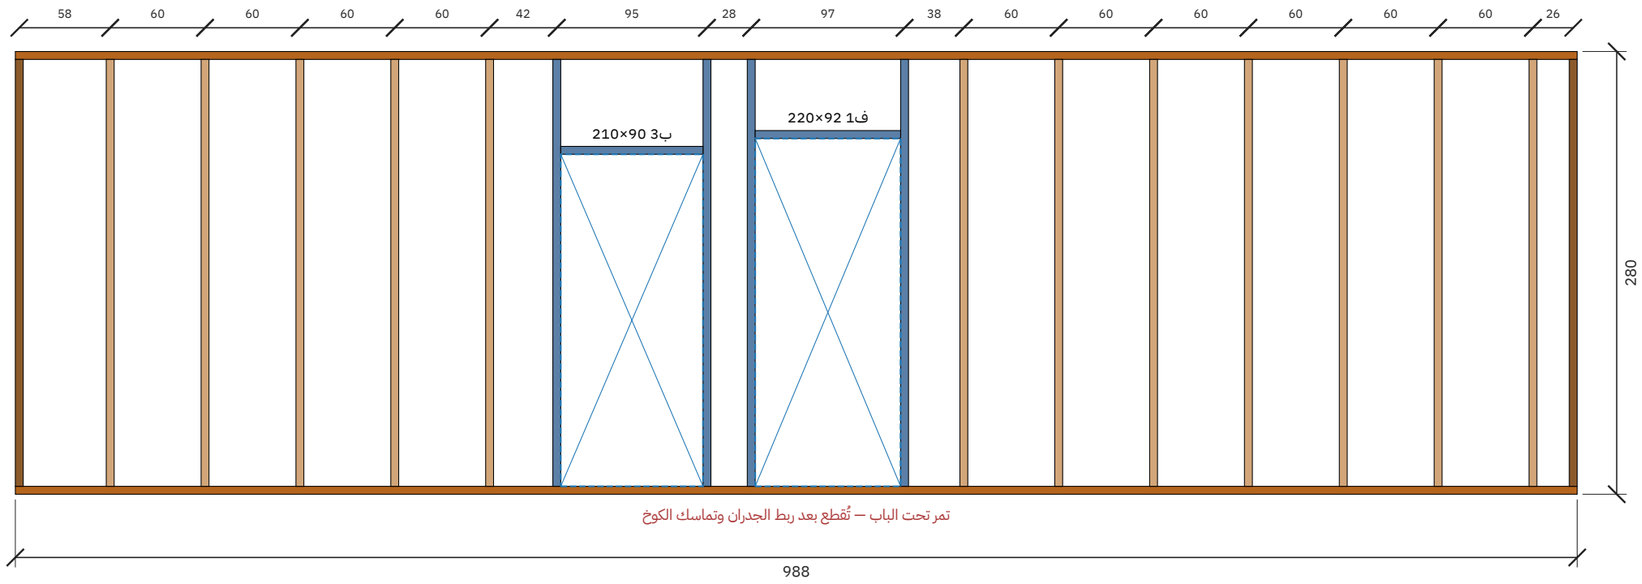

تأطير جدار أ-خلف النساء — الطول 588 سم، الارتفاع 280 سم (داخلي)

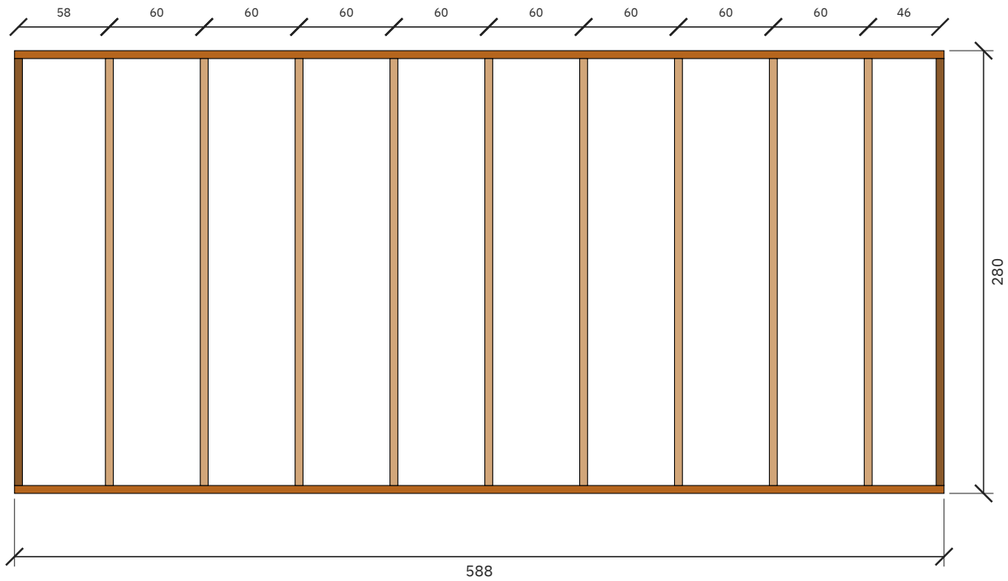


قاعدة سفلية | علوي | عمود | عمود زاوية | جنب فتحة | رأس فتحة | جلسة شباك | عمود قصير


المشروع / العميل	عنوان اللوحة	المقياس	التاريخ	رقم اللوحة
كوخ خشب دورين — مجلس رجال ومجلس نساء + 4 غرف — 15.00 × 10.00 م (300 م²) عميل — كوخ دورين	لوحات التأطير (للورشة)	—	2026-10-24	W-13 (13/23)

مصنع وتد الأخشاب
Watad Wood Factory

تأطير جدار أ-جدار الدرج — الطول 422 سم، الارتفاع 280 سم (داخلي)

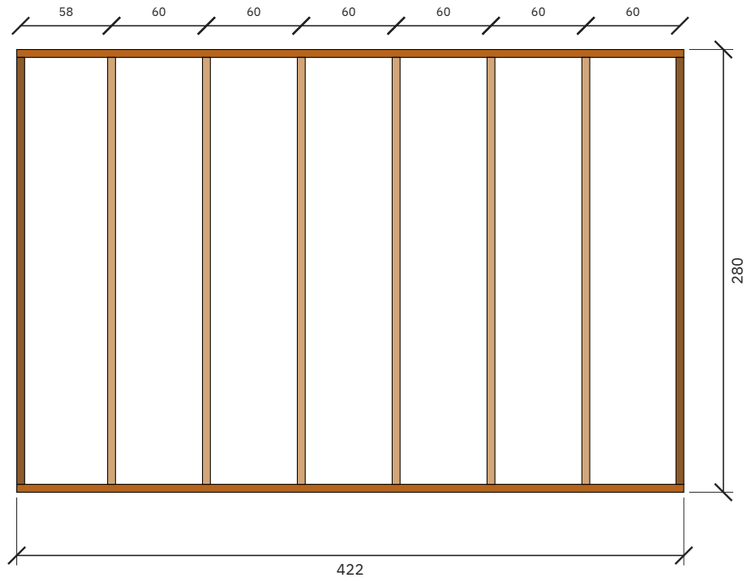

تأطير جدار ب-جنوب — الطول 1488 سم، الارتفاع 280 سم

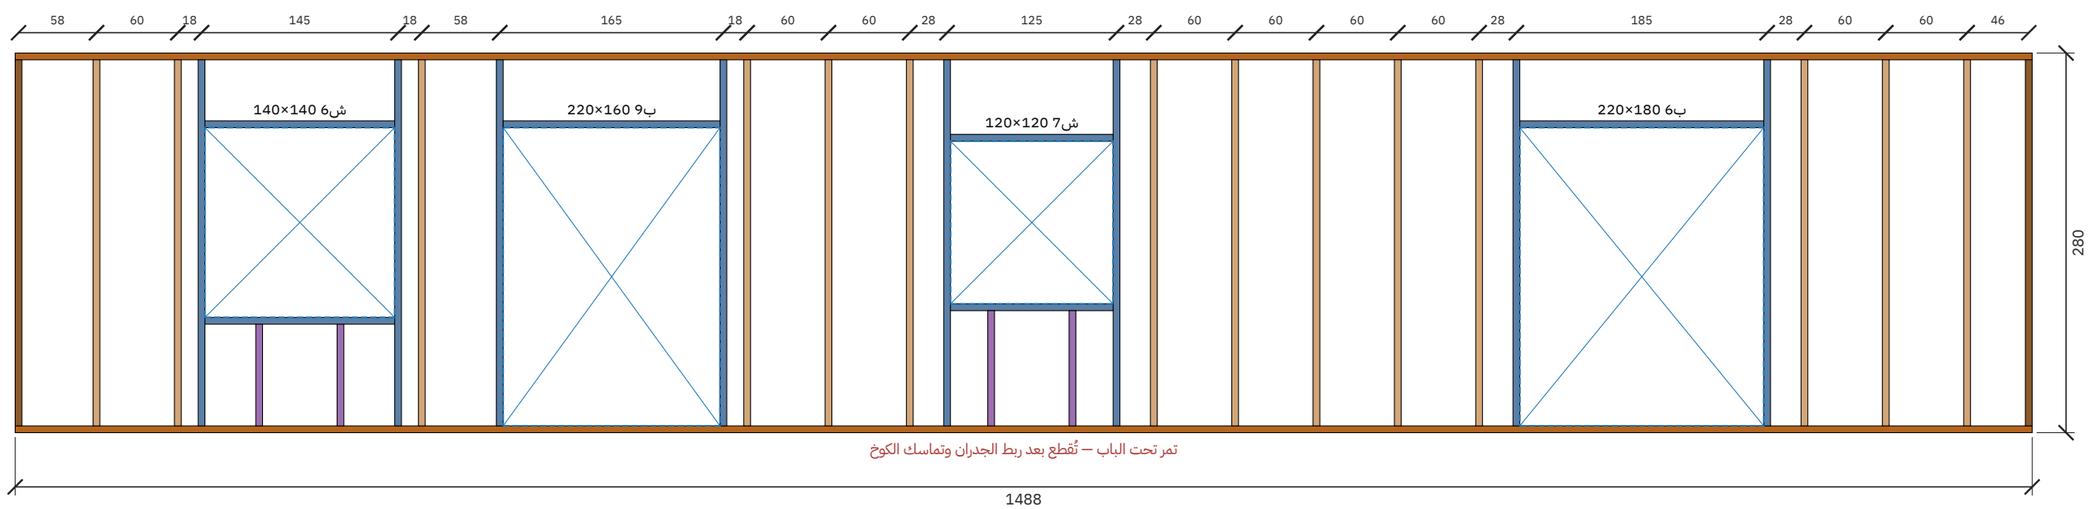


قاعدة سفلية | علوي | عمود | عمود زاوية | جنب فتحة | رأس فتحة | جلسة شباك | عمود قصير


المشروع / العميل	عنوان اللوحة	المقياس	التاريخ	رقم اللوحة
كوخ خشب دورين — مجلس رجال ومجلس نساء + 4 غرف — 15.00 × 10.00 م (300 م²) **عميل — كوخ دورين**	**لوحات التأطير (للورشة)**	**—**	**2026-10-24**	**W-14 (14/23)**

مصنع وتد الأخشاب
Watad Wood Factory

تأطير جدار ب-شرق — الطول 988 سم، الارتفاع 280 سم

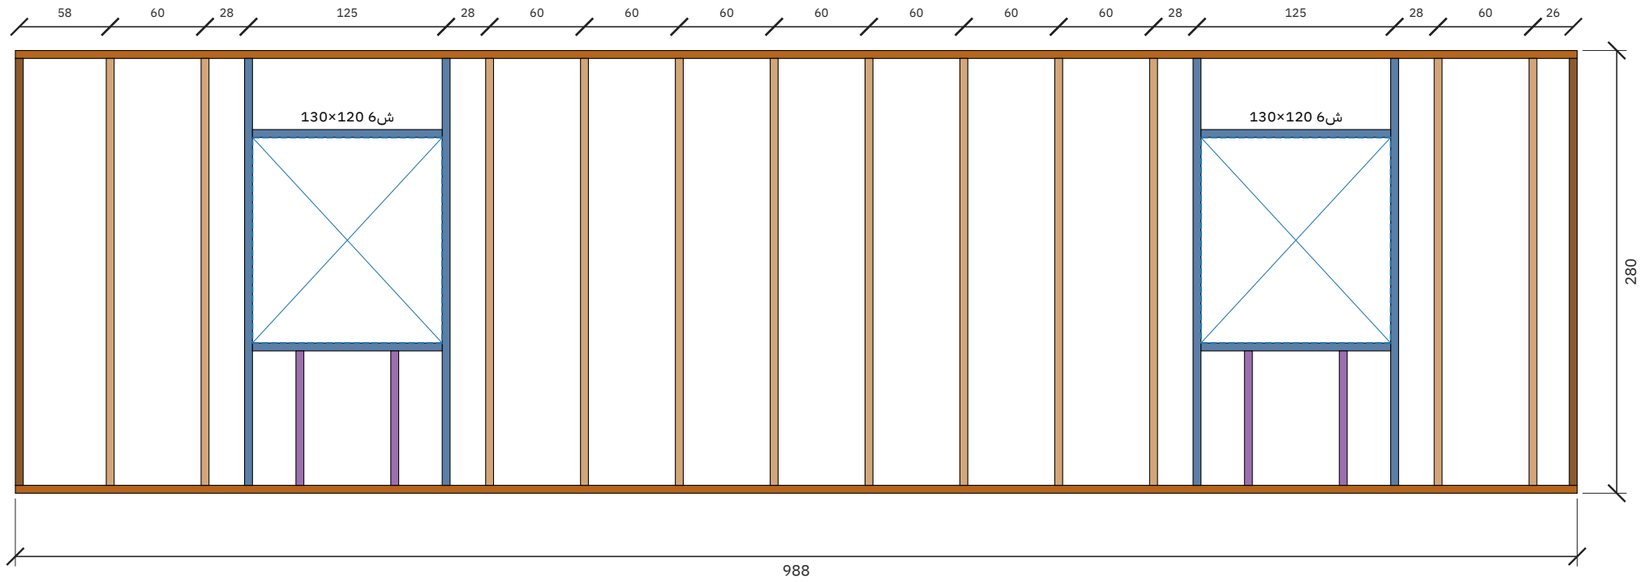

تأطير جدار ب-شمال — الطول 1488 سم، الارتفاع 280 سم

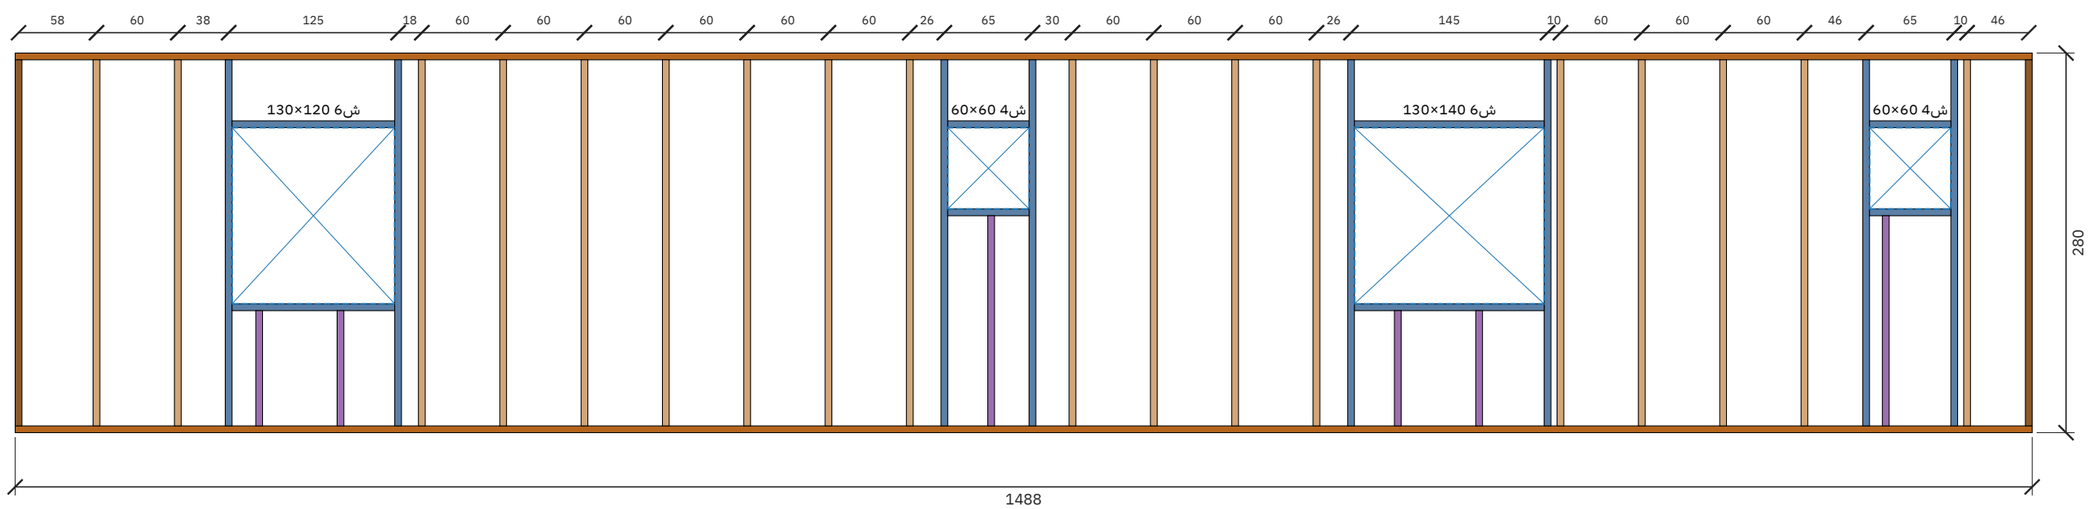


قاعدة سفلية | علوي | عمود | عمود زاوية | جنب فتحة | رأس فتحة | جلسة شباك | عمود قصير


المشروع / العميل	عنوان اللوحة	المقياس	التاريخ	رقم اللوحة
كوخ خشب دورين — مجلس رجال ومجلس نساء + 4 غرف — 15.00 × 10.00 م (300 م²) **عميل — كوخ دورين**	**لوحات التأطير (للورشة)**	**—**	**2026-10-24**	**W-15 (15/23)**

مصنع وتد الأخشاب
Watad Wood Factory

تأطير جدار ب-غرب — الطول 988 سم، الارتفاع 280 سم

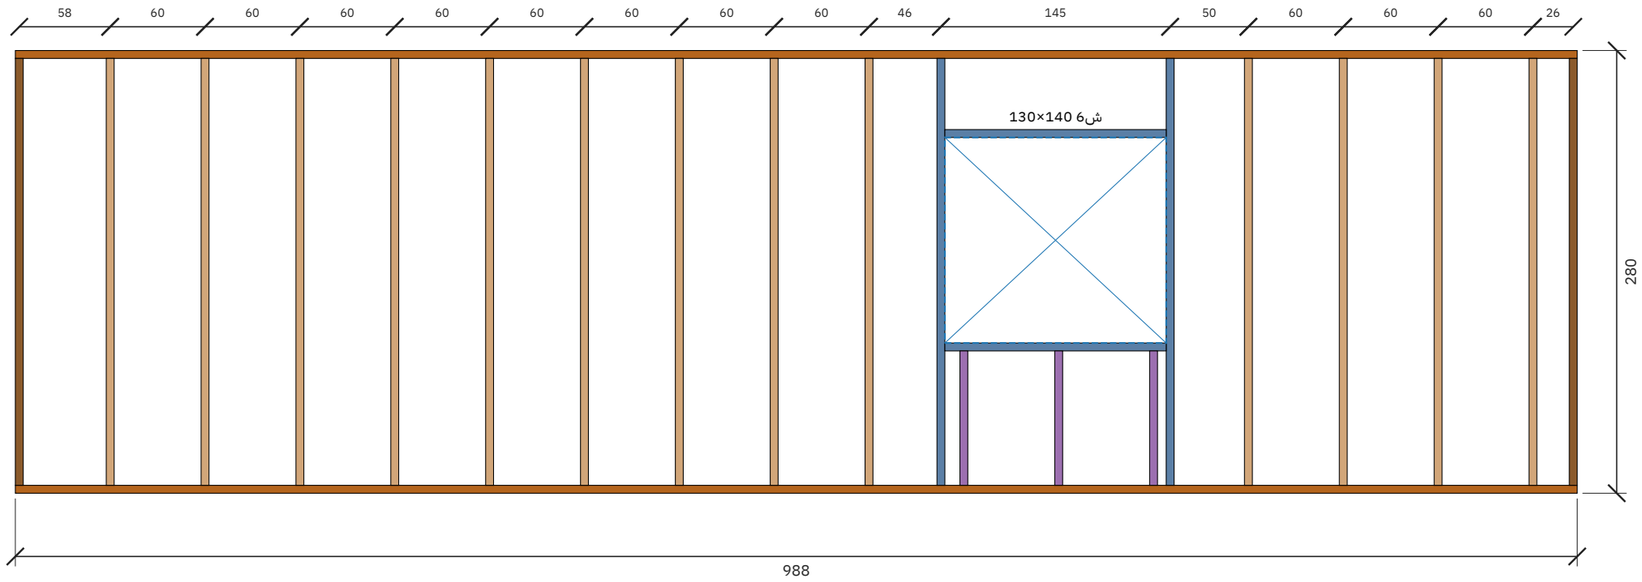


تأطير جدار ب-جدار الماستر — الطول 988 سم، الارتفاع 280 سم (داخلي)

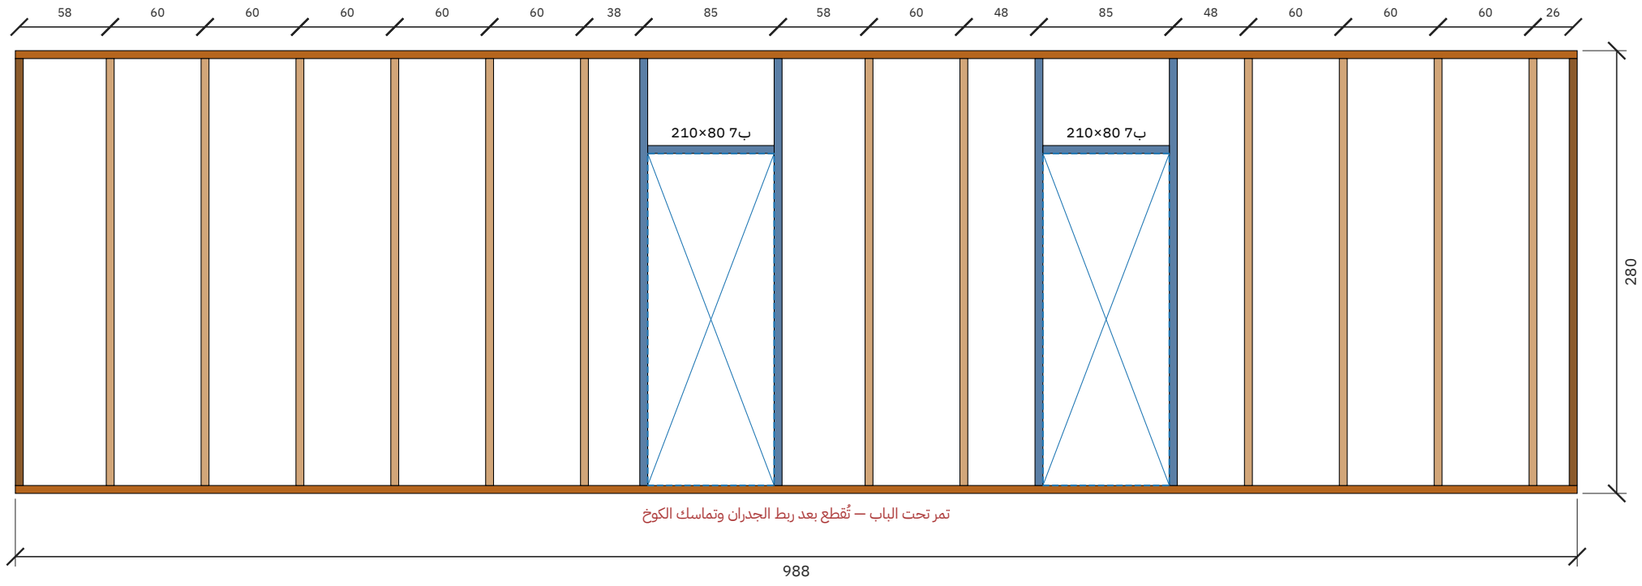


قاعدة سفلية | علوي | عمود | عمود زاوية | جنب فتحة | رأس فتحة | جلسة شباك | عمود قصير

مصنع وتد الأخشاب Watad Wood Factory	المشروع / العميل **كوخ خشب دورين — مجلس رجال ومجلس نساء + 4 غرف — 15.00 × 10.00 م (300 م²)** **عميل — كوخ دورين**	عنوان اللوحة **لوحات التأطير (للورشة)**	المقياس **—**	التاريخ **2026-10-24**	رقم اللوحة **W-16 (16/23)**

تأطير جدار ب-خلف الماستر — الطول 600 سم، الارتفاع 280 سم (داخلي)

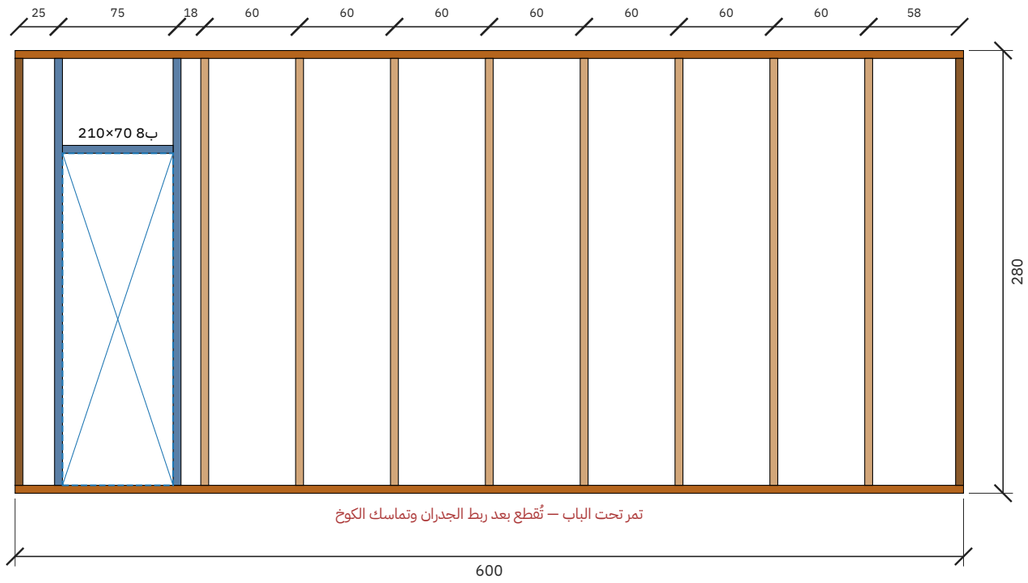

تأطير جدار ب-جدار الحمام — الطول 422 سم، الارتفاع 280 سم (داخلي)

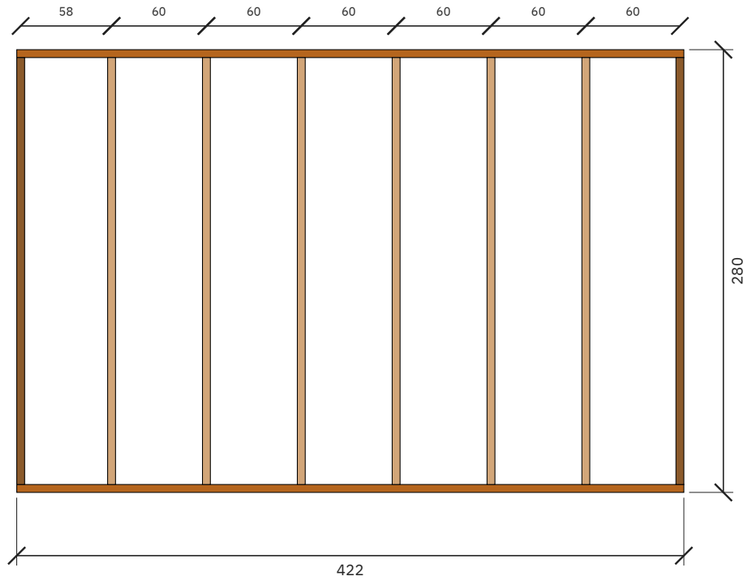


قاعدة سفلية | علوي | عمود | عمود زاوية | جنب فتحة | رأس فتحة | جلسة شباك | عمود قصير


المشروع / العميل	عنوان اللوحة	المقياس	التاريخ	رقم اللوحة
كوخ خشب دورين — مجلس رجال ومجلس نساء + 4 غرف — 15.00 × 10.00 م (300 م²) **عميل — كوخ دورين**	**لوحات التأطير (للورشة)**	**—**	**2026-10-24**	**W-17 (17/23)**

مصنع وتد الأخشاب
Watad Wood Factory

تأطير جدار ب-حمام الممر — الطول 300 سم، الارتفاع 280 سم (داخلي)

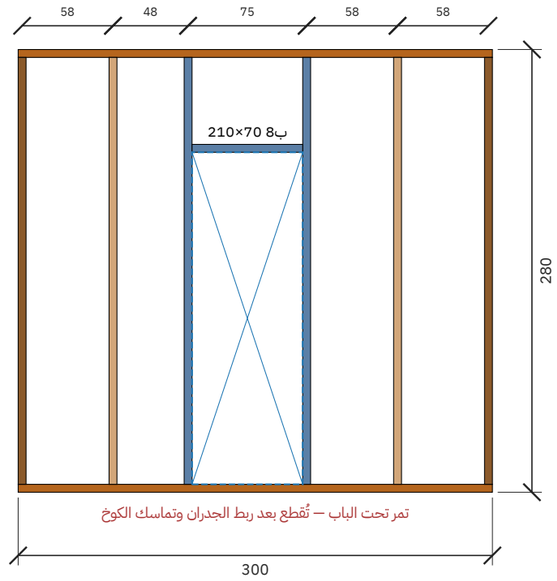


تأطير جدار ب-جدار الغرف — الطول 988 سم، الارتفاع 280 سم (داخلي)

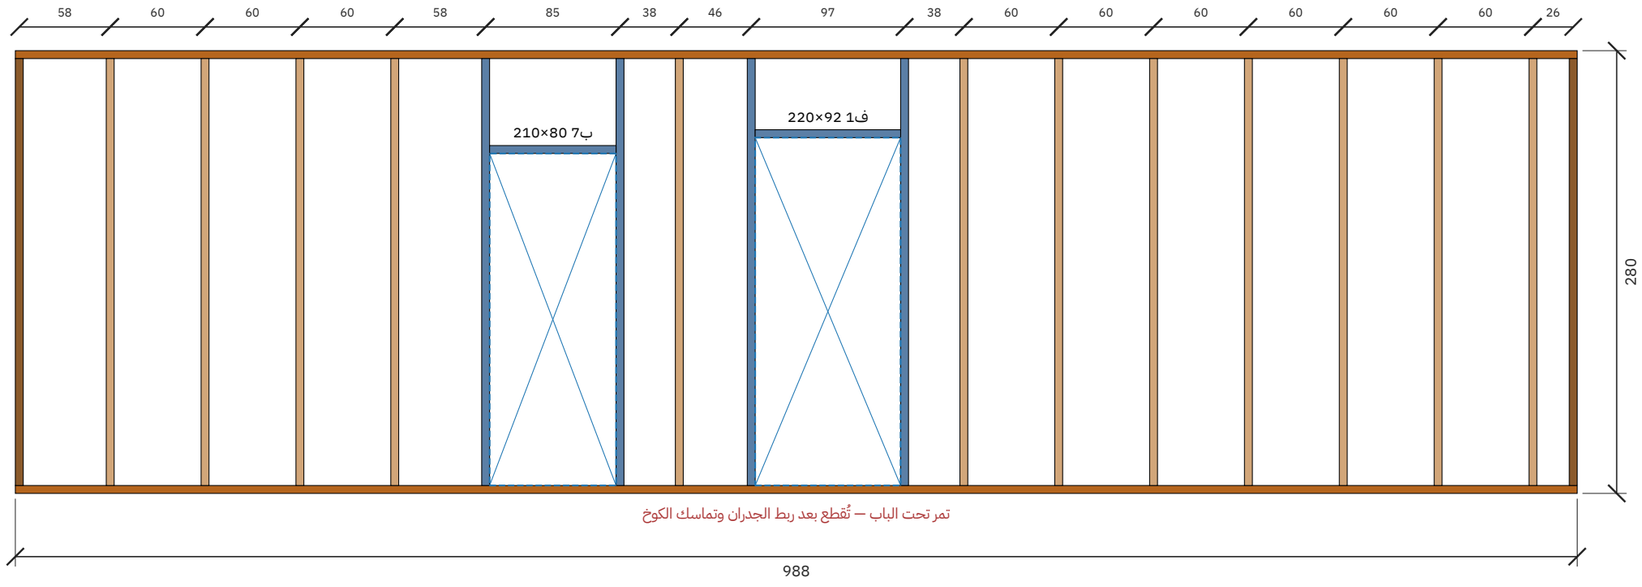


قاعدة سفلية | علوي | عمود | عمود زاوية | جنب فتحة | رأس فتحة | جلسة شباك | عمود قصير

مصنع وتد الأخشاب Watad Wood Factory	المشروع / العميل **كوخ خشب دورين — مجلس رجال ومجلس نساء + 4 غرف — 15.00 × 10.00 م (300 م²)** **عميل — كوخ دورين**	عنوان اللوحة **لوحات التأطير (للورشة)**	المقياس **—**	التاريخ **2026-10-24**	رقم اللوحة **W-18 (18/23)**

تأطير جدار ب-خلف غرفة 3 — الطول 588 سم، الارتفاع 280 سم (داخلي)

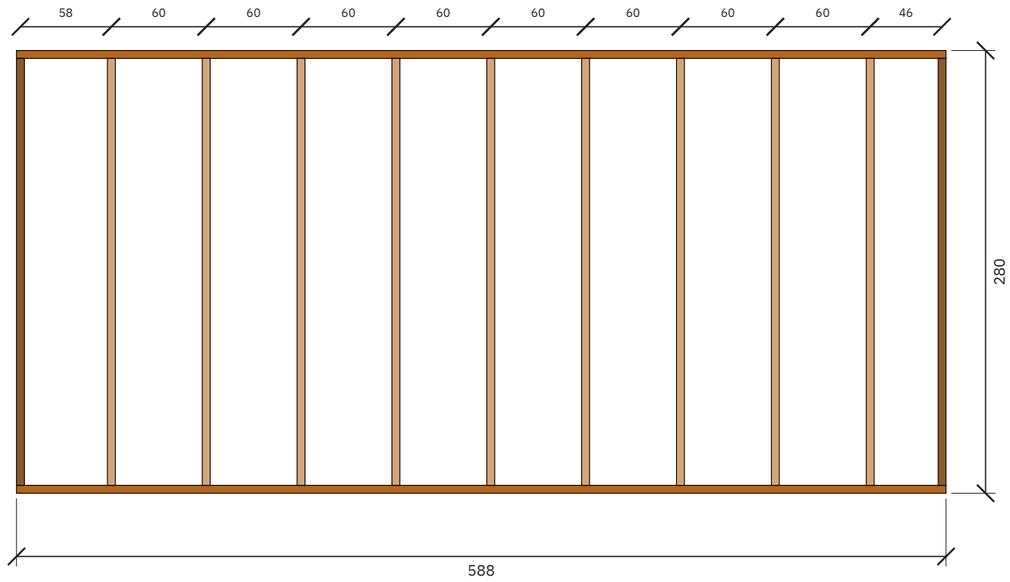


تأطير جدار ب-غرفة 4 — الطول 384 سم، الارتفاع 280 سم (داخلي)

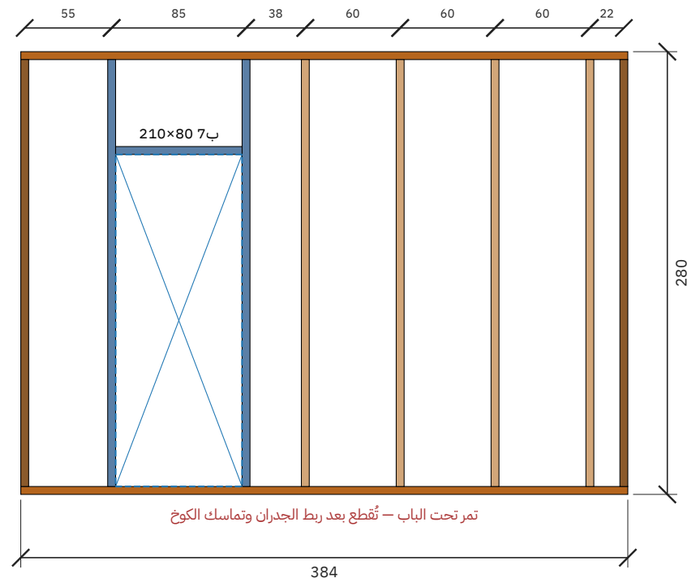

قاعدة سفلية | علوي | عمود | عمود زاوية | جنب فتحة | رأس فتحة | جلسة شباك | عمود قصير

مصنع وتد الأخشاب Watad Wood Factory	المشروع / العميل **كوخ خشب دورين — مجلس رجال ومجلس نساء + 4 غرف — 15.00 × 10.00 م (300 م²)** **عميل — كوخ دورين**	عنوان اللوحة **لوحات التأطير (للورشة)**	المقياس **—**	التاريخ **2026-10-24**	رقم اللوحة **W-19 (19/23)**

تأطير جدار ب-جدار الدرج — الطول 422 سم، الارتفاع 280 سم (داخلي)

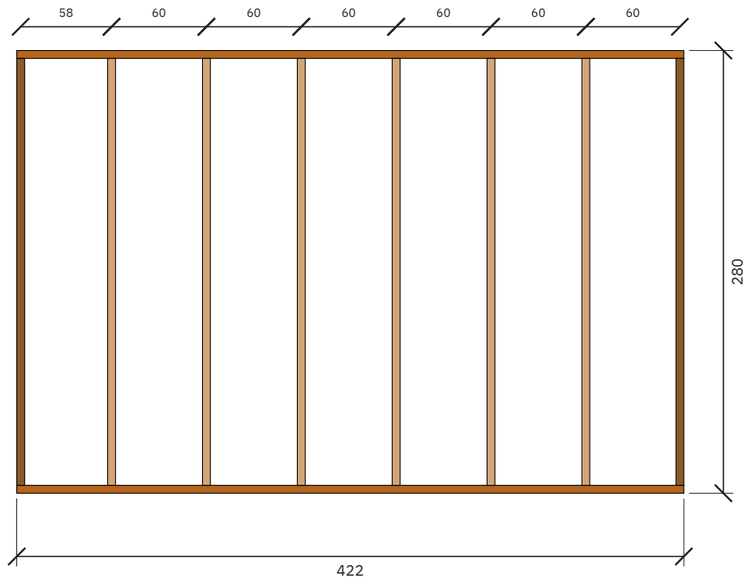

عمود قصير
جلسة شباك
رأس فتحة
جنب فتحة
عمود زاوية
عمود
علوي
قاعدة سفلية

مصنع وتد الأخشاب Watad Wood Factory	المشروع / العميل كوخ خشب دورين — مجلس رجال ومجلس نساء + 4 غرف — 15.00 × 10.00 م (300 م²) عميل — كوخ دورين	عنوان اللوحة لوحات التأطير (للورشة)	المقياس —	التاريخ 2026-10-24	رقم اللوحة W-20 (20/23)

جدول الكميات وخطة تقطيع الطبليات

البند	القيمة
الارتفاع المطلوب / المعتمد	280 / 280 سم
السقف	جملون 30° — أعلى نقطة 874 سم من وجه الصبة
المدادات 5×15	108 مداد (27 خط × قطعتين موصولة فوق الجسر الحامل بتراكب 60 سم) × حتى 370 سم — من طبلية 480
طبليات الطريقة الأولى (مداد + عمود)	108 طبلية × 480 سم
طبليات الطريقة الثانية (3 أعمدة)	114 طبلية × 320 سم
مدادات أرضية الدور العلوي 5×15 كل 60 سم	85 مداد — 214سم×17، 216سم×17، 310سم×17، 394سم×17، 404سم×17 (طبلية 480 بالطريقة الأولى)
مدادات المثلث البارز (S) 40°	16 مداد حتى 274 سم (طبلية 320) + 2 مداد وادي 589 سم — وصلة
	16 مداد حتى 281 سم (طبلية 320) + 2 مداد وادي 608 سم — وصلة
إجمالي الطبليات 5×22.5	343
إجمالي قطع 5×7	484
قائمة تقطيع 5×7	1488سم×8 | 988سم×16 | 600سم×4 | 588سم×4 | 422سم×8 | 384سم×2 | 300سم×4 | 270سم×339 | 190سم×1
	180سم×1 | 160سم×13 | 155سم×4 | 140سم×8 | 120سم×12 | 105سم×2 | 100سم×1 | 92سم×2 | 90سم×2
ألواح تلبيس 2.5 سم	1273 لوح × 400 سم (مجموع الصفوف 4261.4 م، 46 وجه)
أسمنت بورد 12 مم (122×244)	88 لوح (داخل دورات المياه)

جدول الكميات وخطة تقطيع الطبليات

البند	القيمة
العزل	642 لوح فوم صخري 80
الصبة	يجهزها العميل — 20 سم، مفرغة تحت دورات المياه

مراجعة التصميم مقابل قواعد المصنع

النوع	البند	التفاصيل	المقترح
ملاحظة	بحر المدادات	أطول بحر بدون جدار داخلي يحمل المداد: جهة أ: 500 سم، جهة ب: 500 سم. يحتاج رقم المصنع لأقصى بحر مسموح لتحديد المدادات اللي تُقوّى 20×5.	
ملاحظة	الصبة والدرج	ارتفاع الصبة 45 سم ← 3 درجة بقائمة 15.0 سم.	
ملاحظة	مناسيب رؤوس الفتحات	رؤوس الأبواب والشبابيك على مناسيب مختلفة: 210، 220، 230، 250 سم.	
تنبيه	مداد الوادي	مداد الوادي 589 سم أطول من الطبلية — يُوصل بوصلة مثبتة فوق جدار/دعامة	وصلة مزدوجة 5×15 مع براغي، ومرتكزة على جدار أو دعامة 5×7.
تنبيه	مداد الوادي	مداد الوادي 608 سم أطول من الطبلية — يُوصل بوصلة مثبتة فوق جدار/دعامة	وصلة مزدوجة 5×15 مع براغي، ومرتكزة على جدار أو دعامة 5×7.
سؤال	يحتاج تأكيد	أقصى بحر للمداد بدون جدار داخلي قبل إضافة تقوية 5×7 (مداد 20×5)؟	
سؤال	يحتاج تأكيد	التغطية الصافية للوح التلبيس بعد التعشيق (مستنتجة مؤقتاً 18.67 سم من 280/15)؟	
سؤال	يحتاج تأكيد	هل يوضع أعمدة قصيرة فوق رأس الشباك/الباب إلى العلوي؟	
سؤال	يحتاج تأكيد	مكان الوصلة في القاعدة والعلوي إذا الجدار أطول من الطبلية؟	