
المنظور ثلاثي الأبعاد والمواد

النمط: برتقالي محمر + قرميد فحمي + دربزين X — رندر واقعي بخامات حقيقية

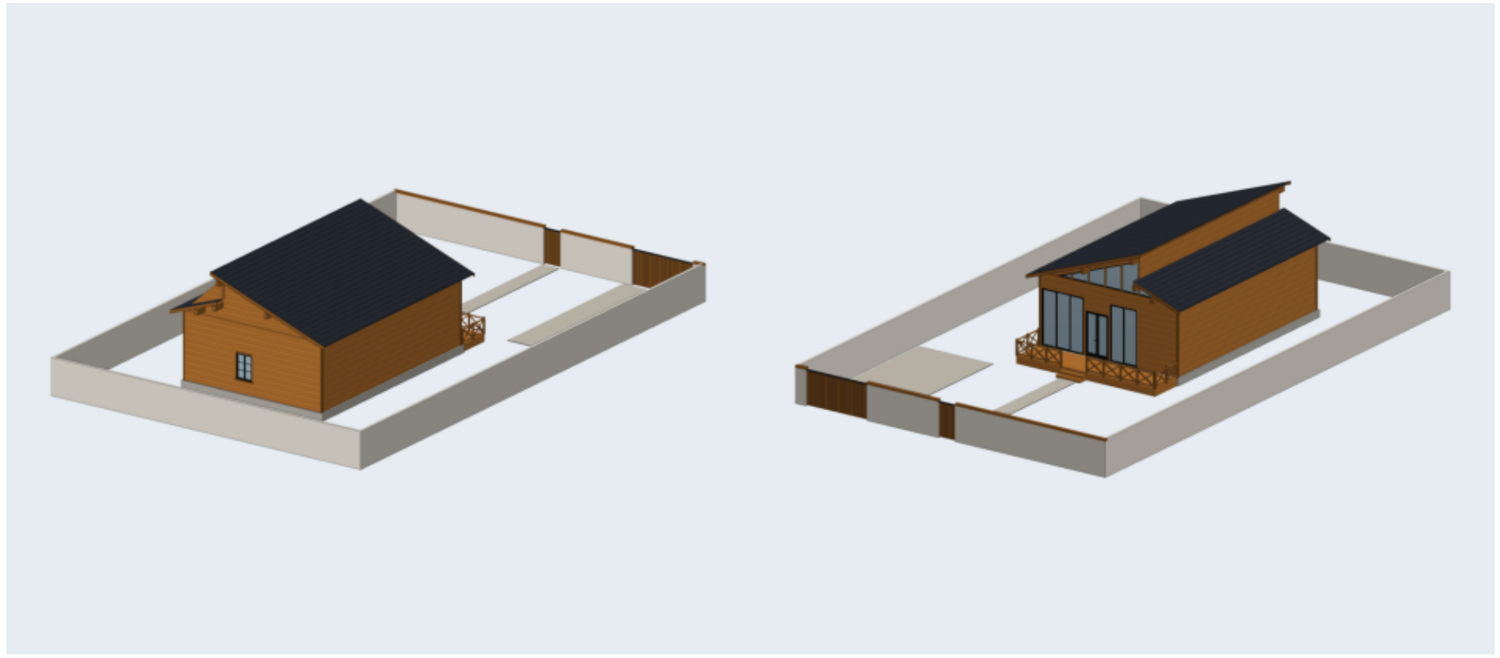

جدول المواد والألوان

الخشب / الصبغة

صبغة عسلي / سيدر

القرميد

قرميد فحمي / أسود مزرق

الزجاج

زجاج شفاف

إطارات الشبابيك والأبواب

إطار ألمنيوم أسود

الكنار والزوايا

نفس الصبغة أغمق درجة


الصبة

خرسانة 45 سم


الدربزين: تقاطع X (صورة 5)

تقسيم الشبابيك: شبكة | الباب الرئيسي: زجاج بتقسيمات (فرنسي)

أنواع الدربزين المعتمدة (من مشاريع المصنع)

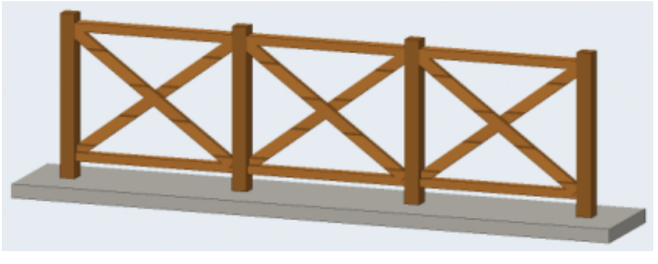

تقاطع X (صورة 5)

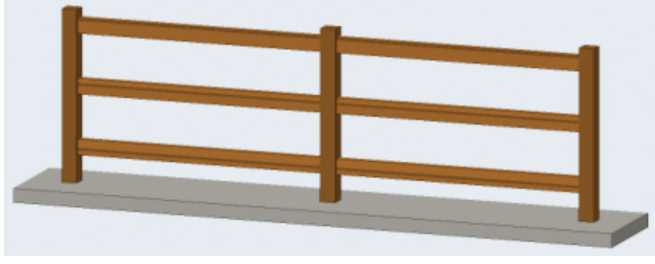

3 مرابيع أفقية (صورة 2)




قوائم رأسية متقاربة (صورة 1)

المشروع / العميل	عنوان اللوحة	المقياس	التاريخ	رقم اللوحة
مجلس وجلسة خارجية مغلقة وغرفة نوم 9.00 × 13.00 م — الحوية **عميل — الحوية**	**المنظور والمواد**	**1:50**	**2026-11-05**	**W-01 (1/14)**

مصنع وتد الأخشاب
Watad Wood Factory


المسقط الأفقي مع الفرش

الأبعاد بالسنتيمتر - الجدران: قوائم 7×5 + تلبيس 2.5 من الجهتين (12 سم)

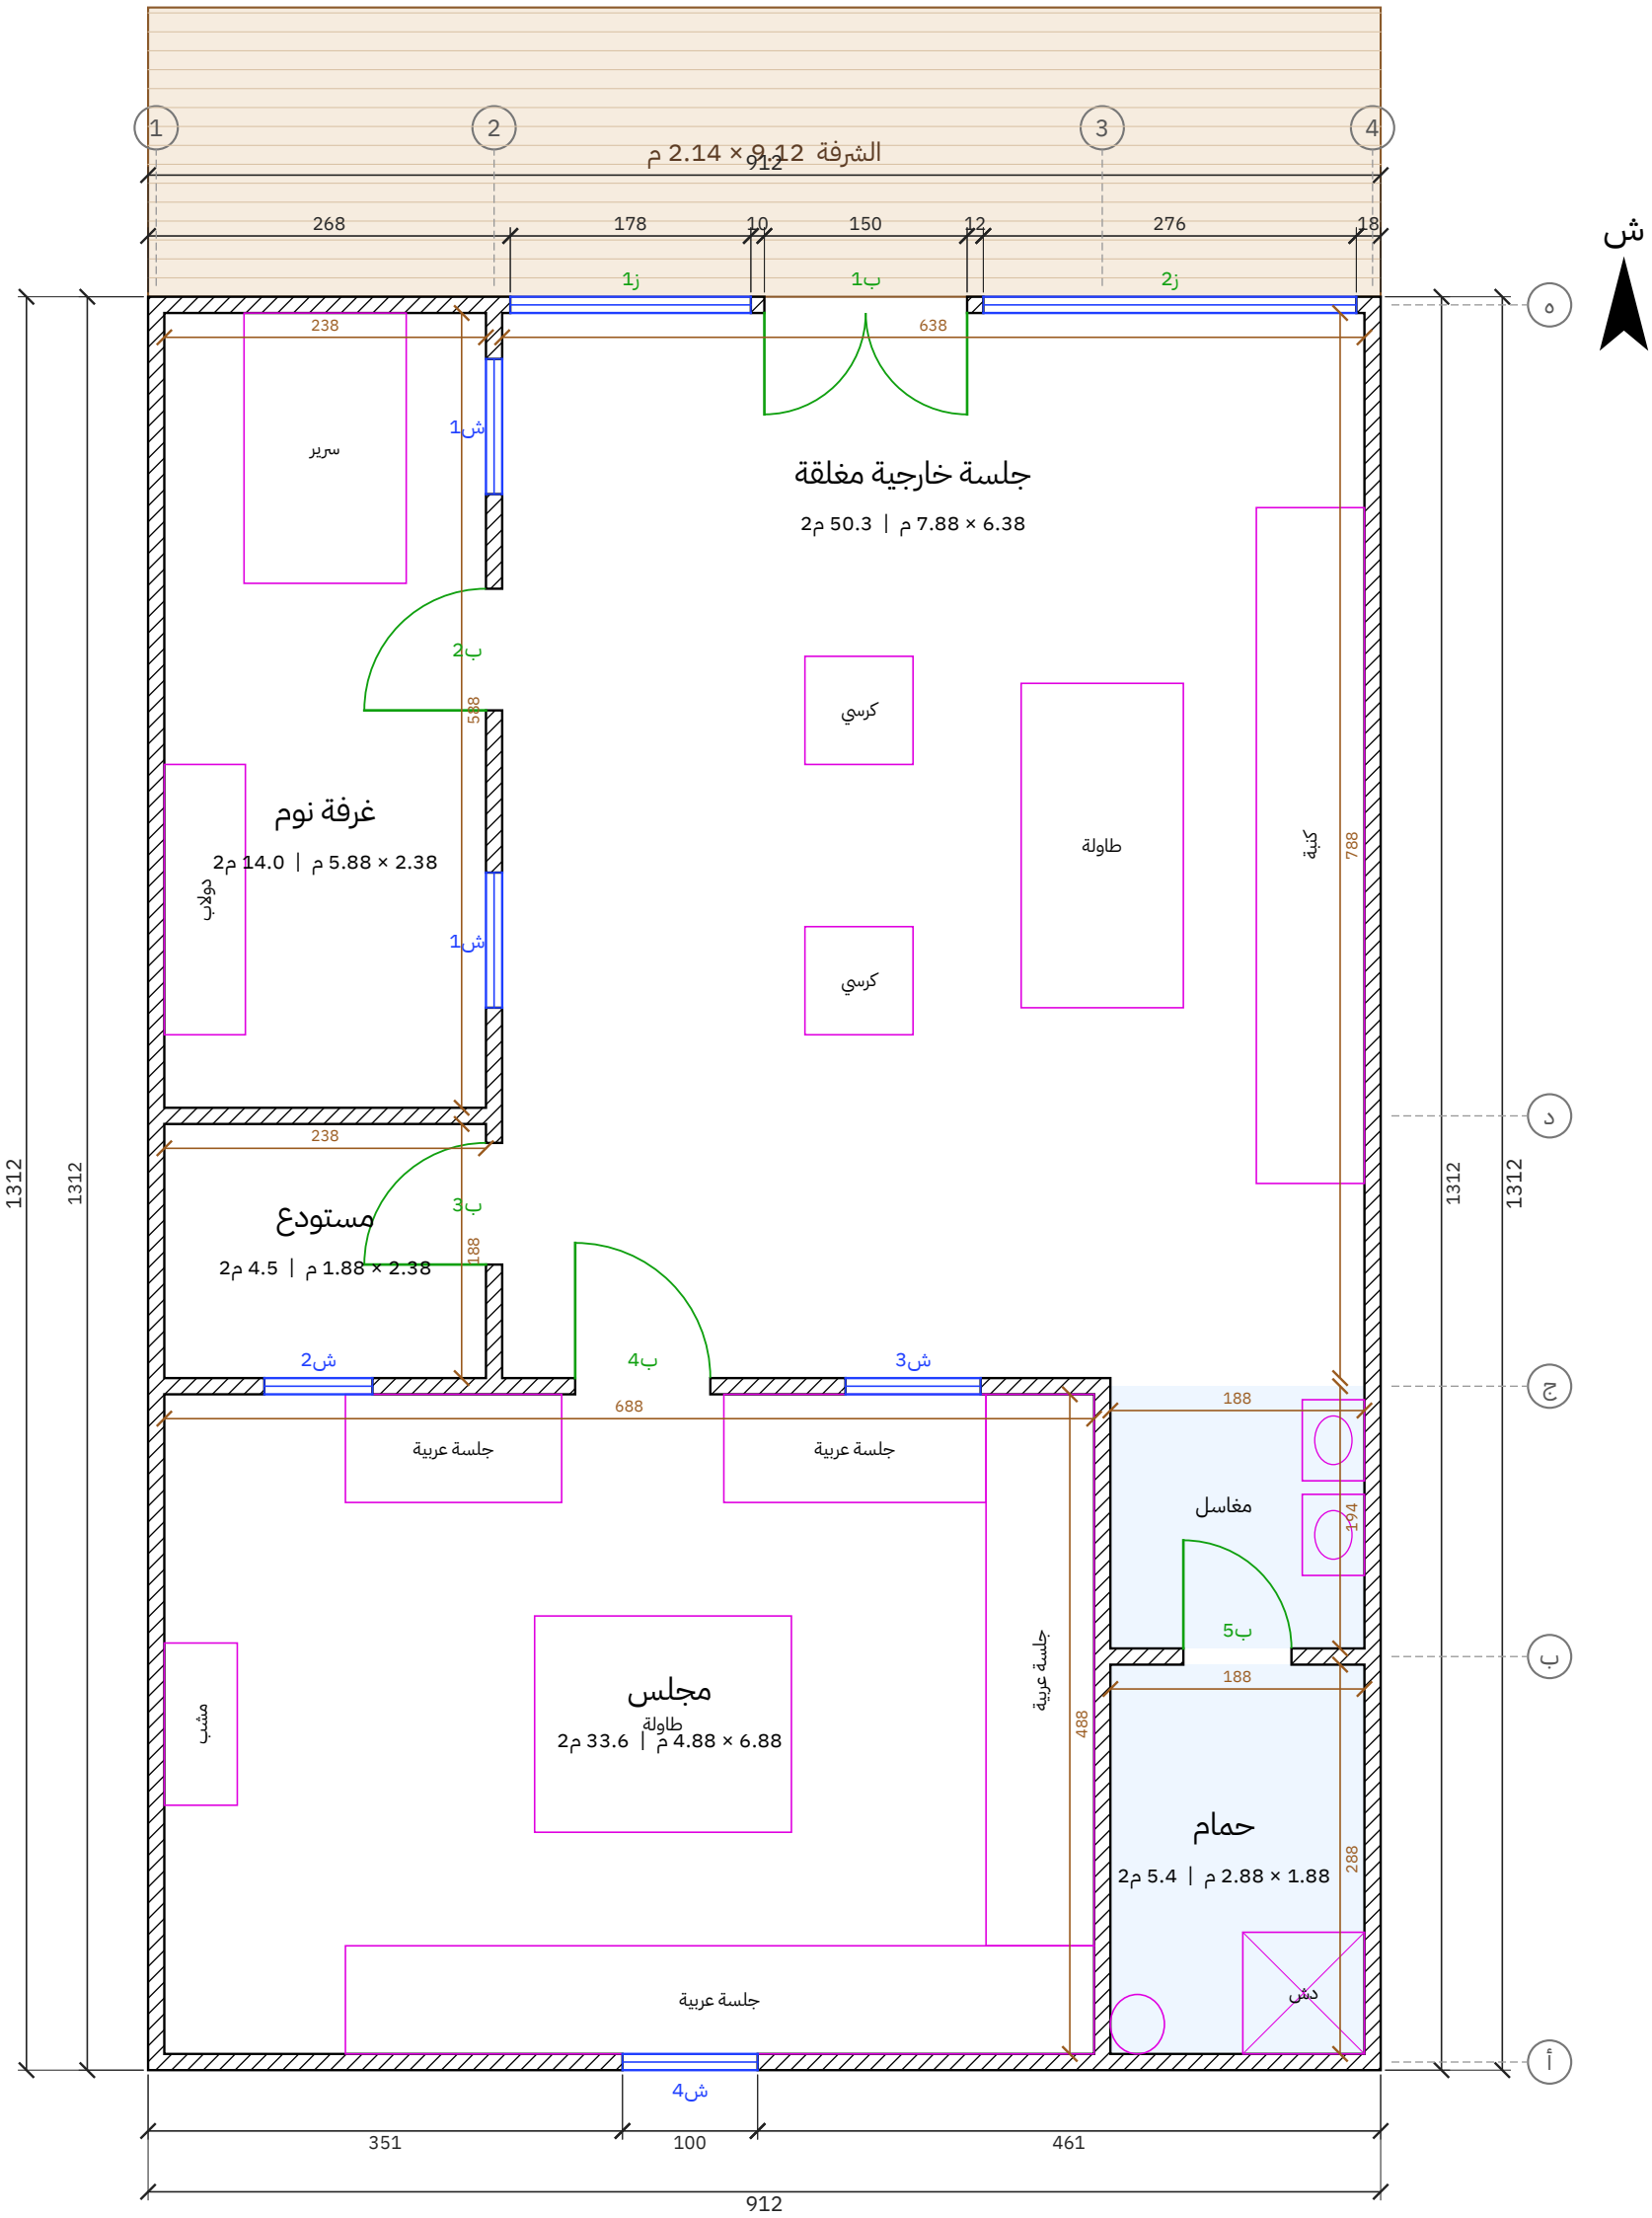


المشروع / العميل	عنوان اللوحة	المقياس	التاريخ	رقم اللوحة
مجلس وجلسة خارجية مغلقة وغرفة نوم 9.00 × 13.00 م – الحوية **عميل – الحوية**	**المسقط الأفقي**	**1:50**	**2026-11-05**	**W-02 (2/14)**

مصنع وتد الأخشاب
Watad Wood Factory

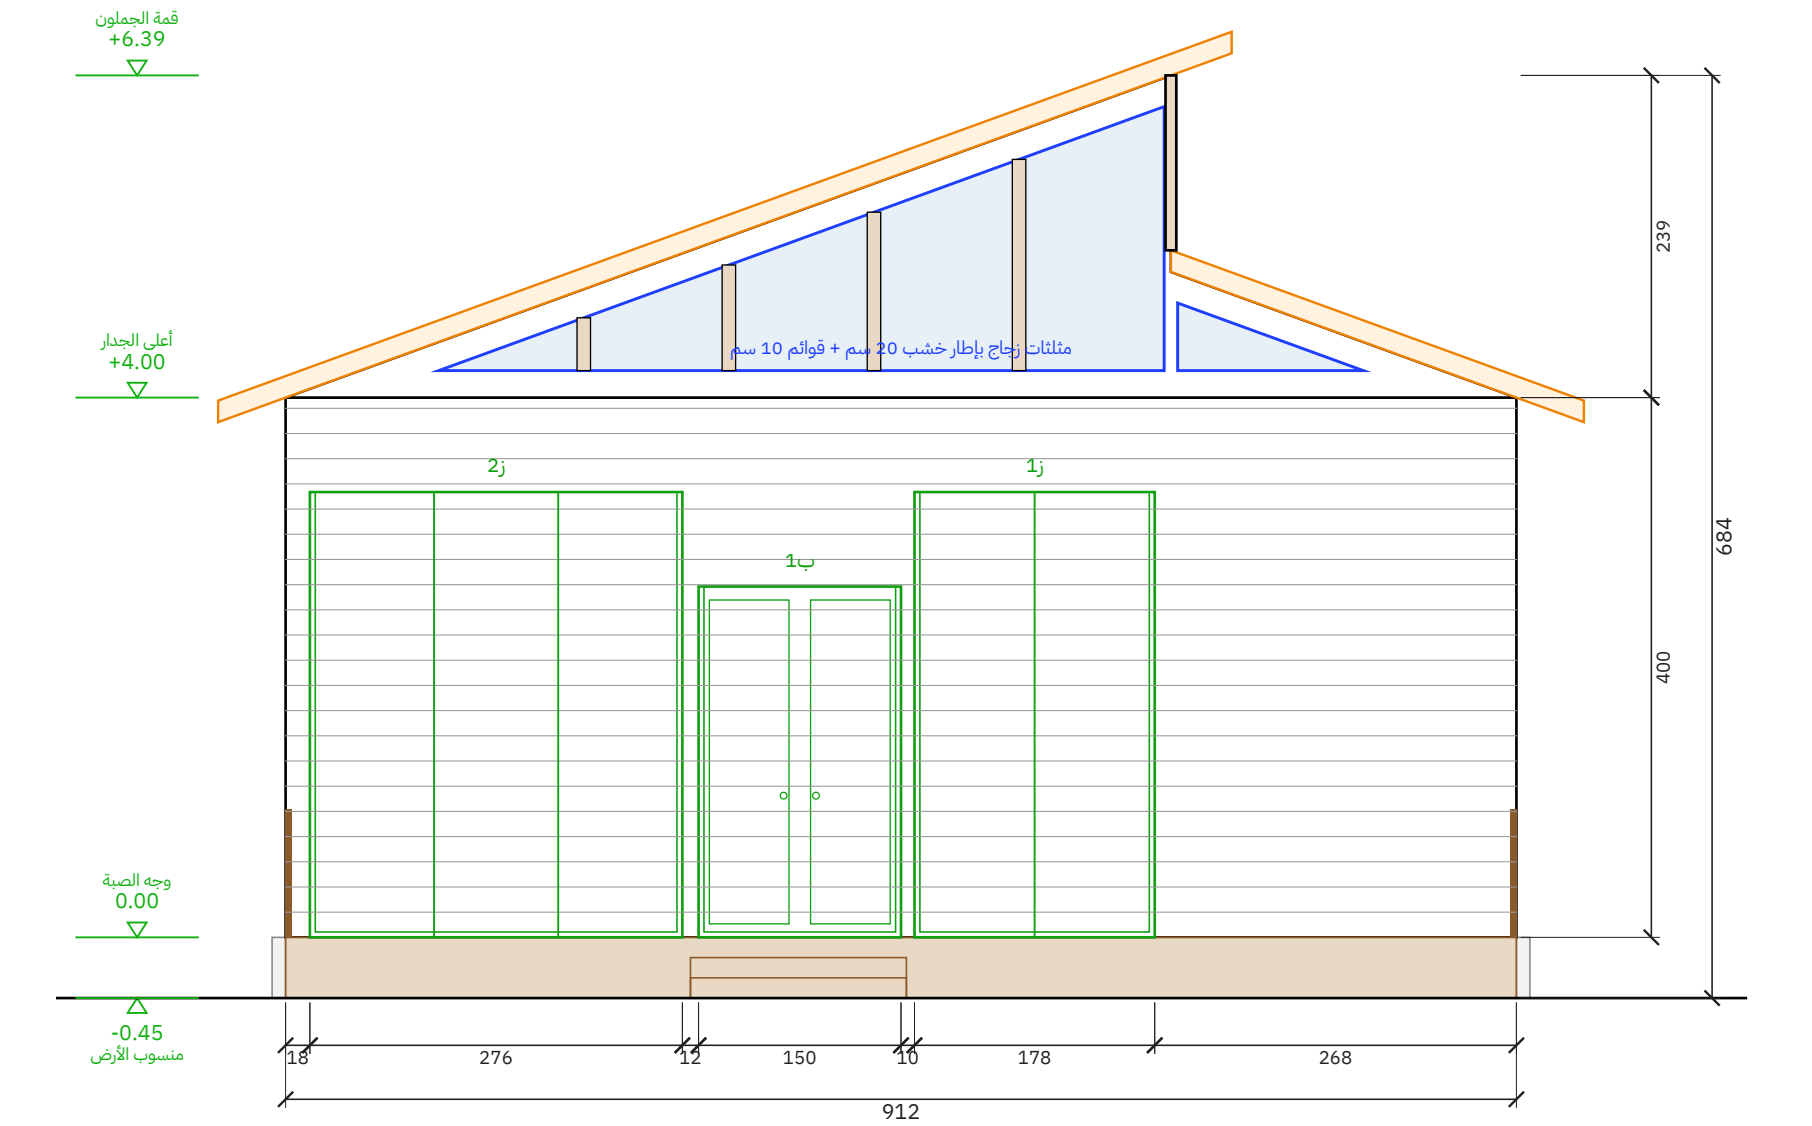

واجهة المدخل (أعلى المخطط)

مقياس 1:50 | الوحدة: سم

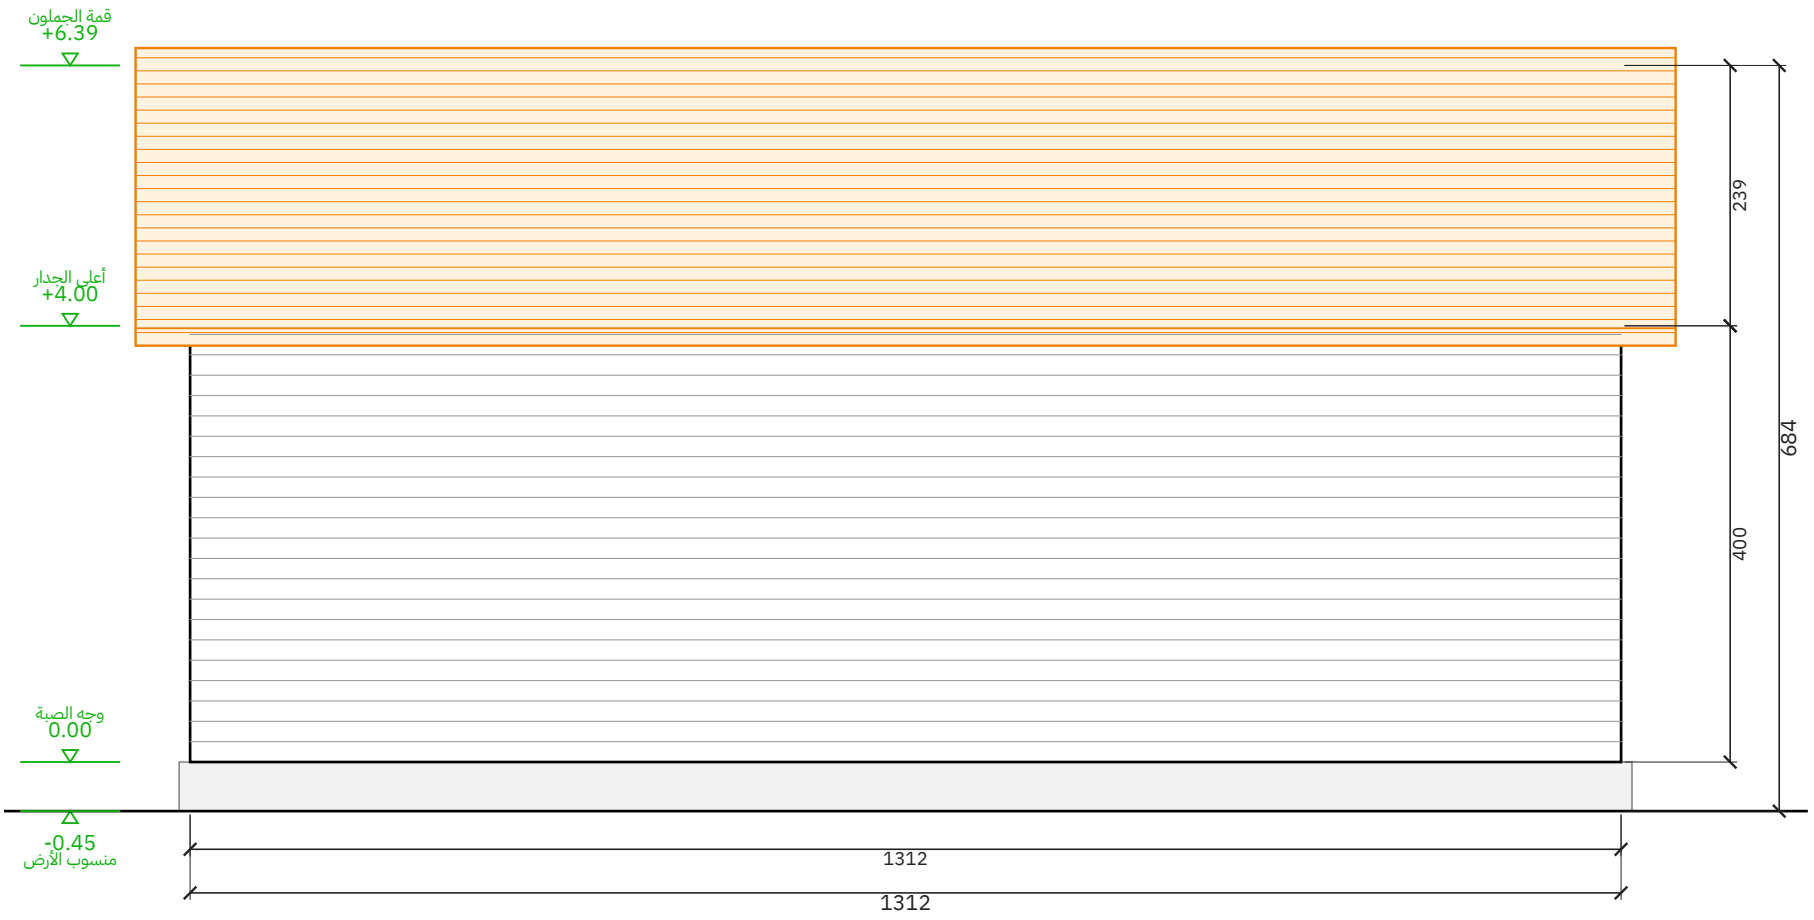


الواجهة اليمنى

مقياس 1:50 | الوحدة: سم


المشروع / العميل	عنوان اللوحة	المقياس	التاريخ	رقم اللوحة
مجلس وجلسة خارجية مغلقة وغرفة نوم 9.00 × 13.00 م – الحوية **عميل – الحوية**	**واجهة المدخل (أعلى المخطط) والواجهة اليمنى**	**1:50**	**2026-11-05**	**W-03 (3/14)**

مصنع وتد الأخشاب
Watad Wood Factory

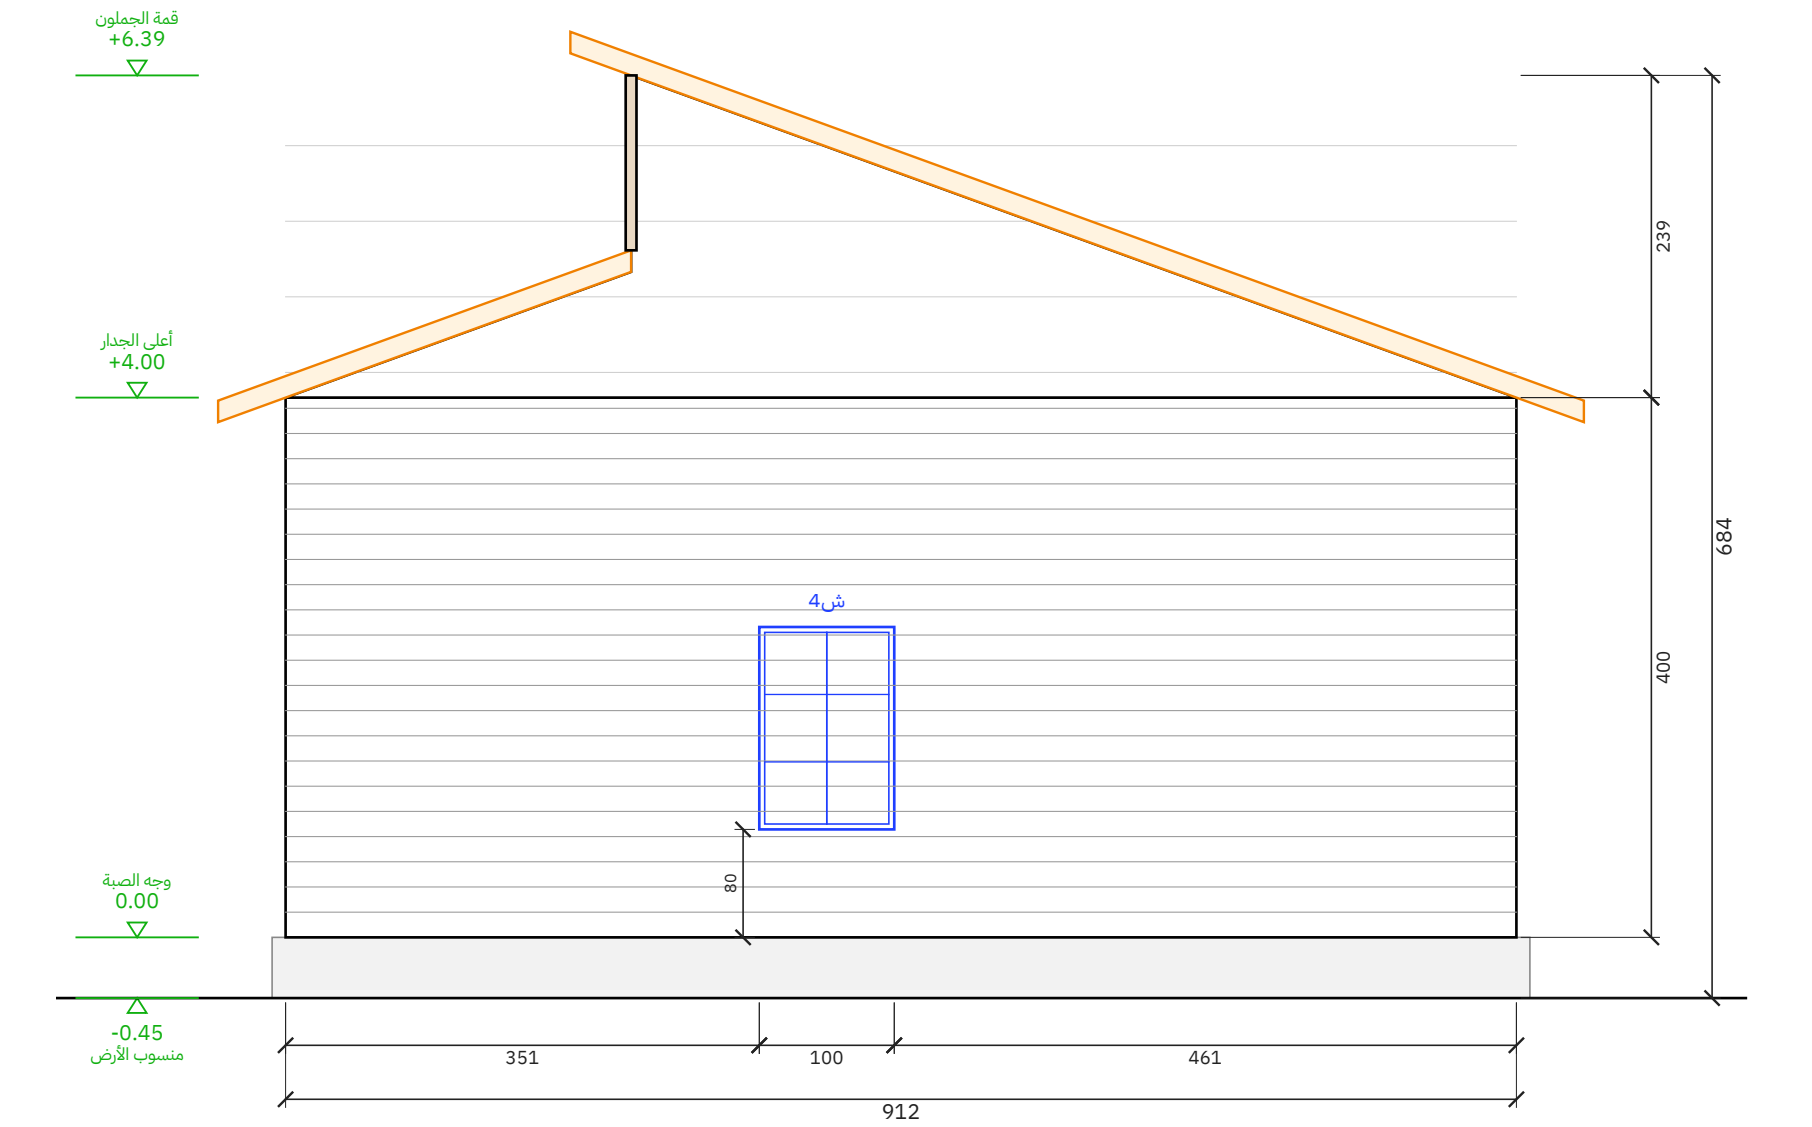

الواجهة السفلية (المجلس)

مقياس 1:50 | الوحدة: سم

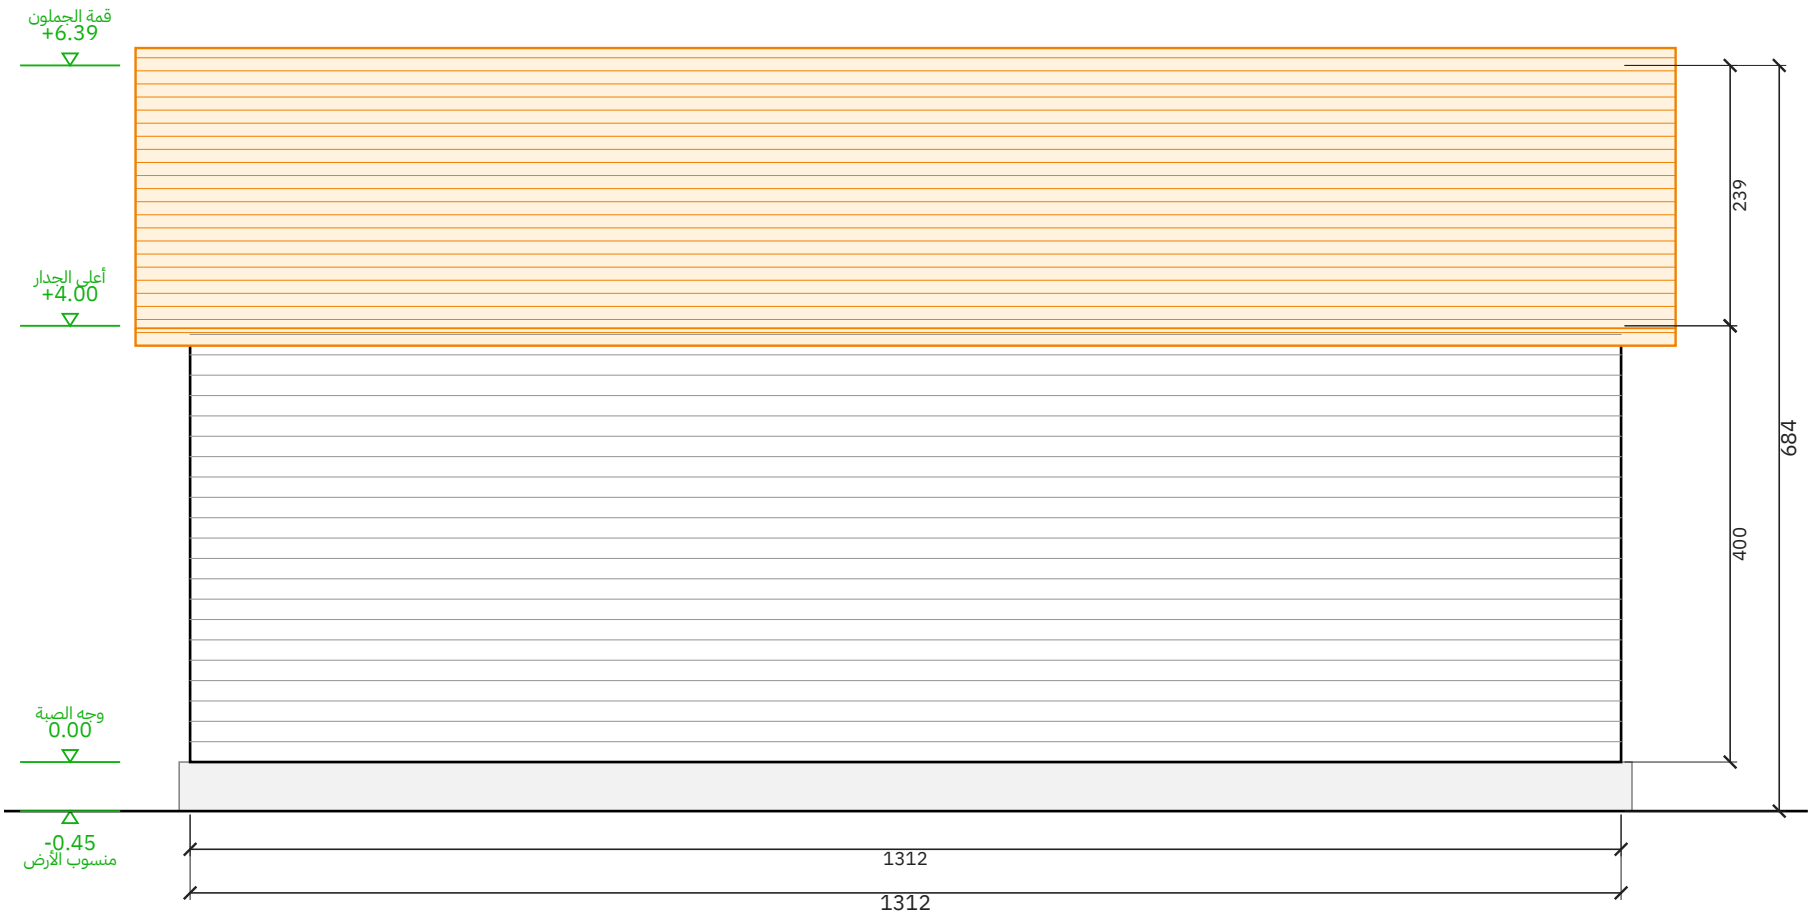

الواجهة اليسرى


مقياس 1:50 | الوحدة: سم

المشروع / العميل	عنوان اللوحة	المقياس	التاريخ	رقم اللوحة
مجلس وجلسة خارجية مغلقة وغرفة نوم 9.00 × 13.00 م – الحوية عميل – الحوية	الواجهة السفلية (المجلس) والواجهة اليسرى	1:50	2026-11-05	W-04 (4/14)

مصنع وتد الأخشاب
Watad Wood Factory


مسقط السقف (جملون متداخل)

رفرف 50 سم من كل جهة | مقياس 1:50

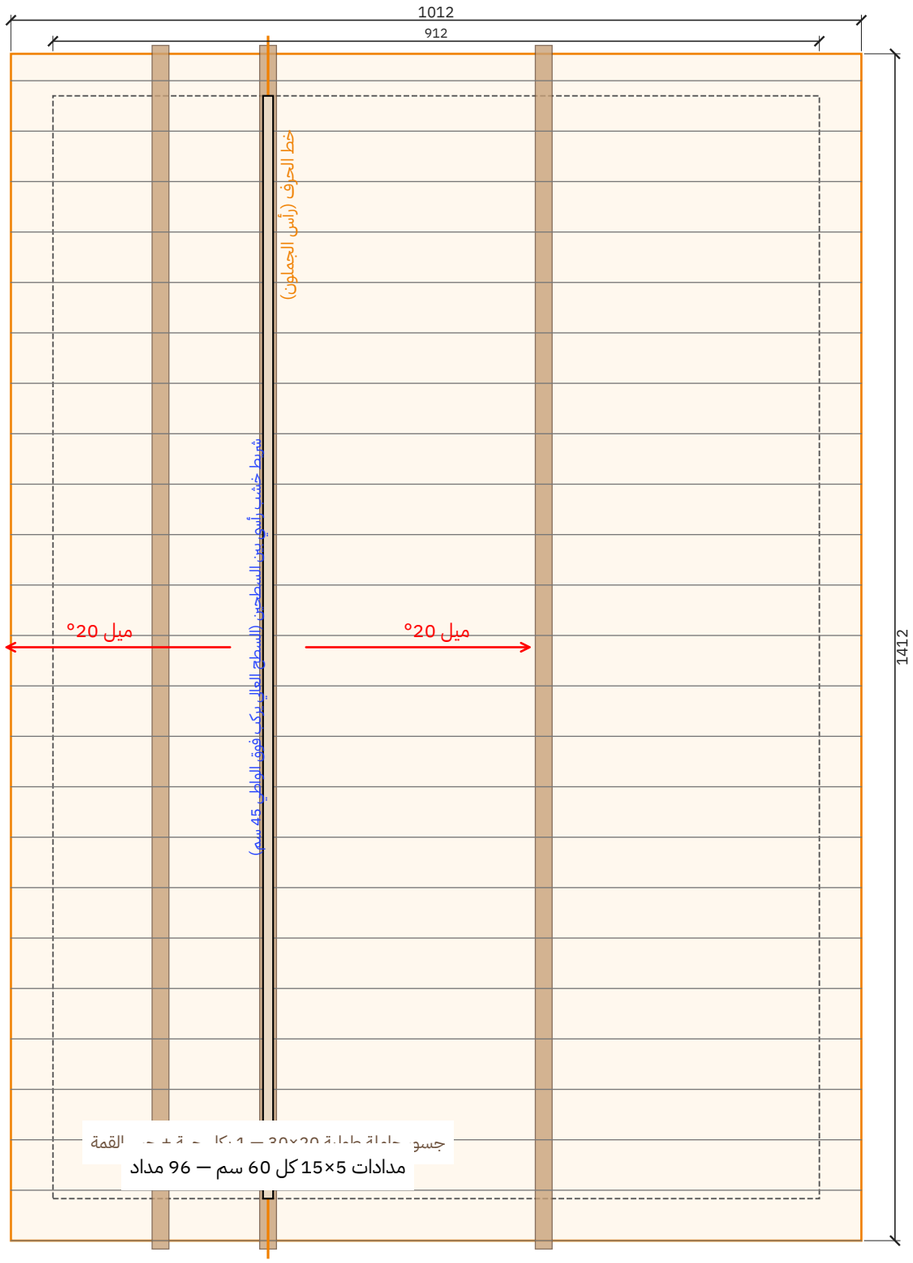


قطاع عرضي أ-أ

مقياس 1:50 | الوحدة: سم

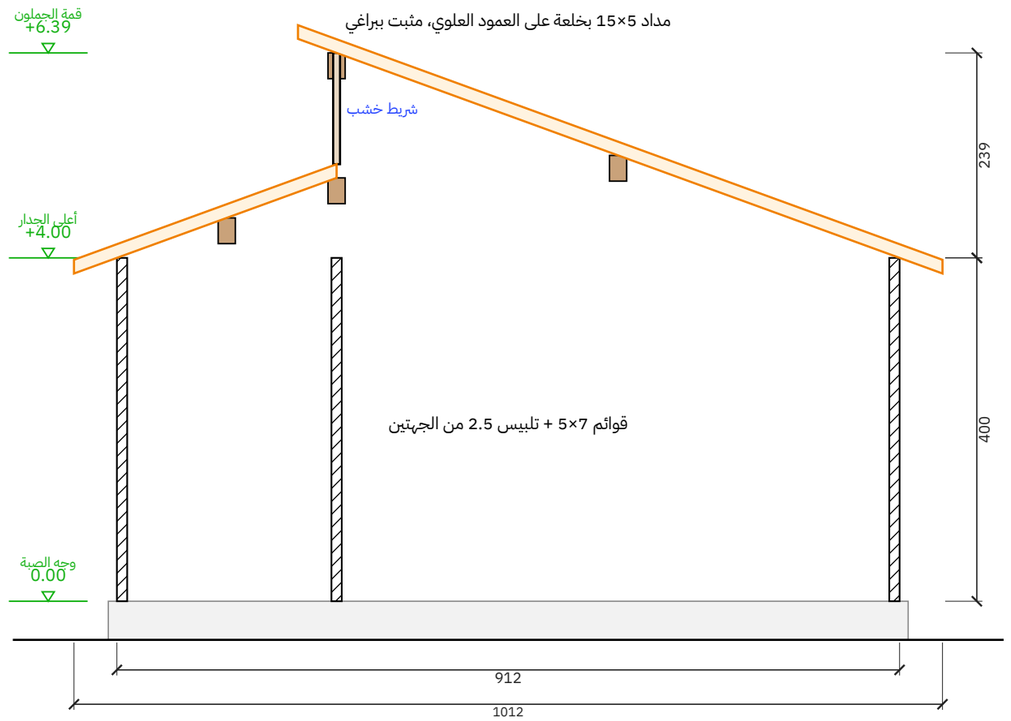

تفصيلة جلوس المداد على العلوي (1:5)

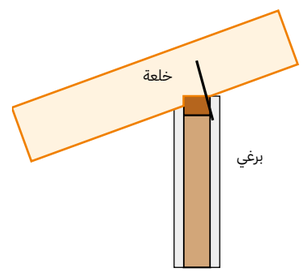

المشروع / العميل	عنوان اللوحة	المقياس	التاريخ	رقم اللوحة
مجلس وجلسة خارجية مغلقة وغرفة نوم 9.00 × 13.00 م — الحوية عميل — الحوية	مسقط السقف والقطاع	1:50	2026-11-05	W-05 (5/14)

مصنع وتد الأخشاب
Watad Wood Factory

جدول مقاسات الأبواب والشبابيك

مقاس الفتحة الصافي في الجدار - الوحدة: سم

الرمز	النوع	العرض (سم)	الارتفاع (سم)	ارتفاع الجلسة (سم)	العدد	الموقع
ب1	باب مزدوج	150	260	-	1	واجهة المدخل (أعلى المخطط)
ب2	باب	90	220	-	1	غرفة النوم
ب3	باب	90	220	-	1	المستودع
ب4	باب	100	230	-	1	المجلس
ب5	باب	80	210	-	1	الحمام
ز1	باب مزدوج	178	330	-	1	واجهة المدخل (أعلى المخطط)
ز2	باب	276	330	-	1	واجهة المدخل (أعلى المخطط)
ش1	شباك	100	120	100	2	الغرفة على الجلسة 2
ش2	شباك	80	100	120	1	المجلس على المستودع
ش3	شباك	100	150	90	1	المجلس على الجلسة
ش4	شباك	100	150	80	1	السفلية (المجلس)

الإجمالي: أبواب 7 - شبابيك 5

جدول المساحات وبيانات المشروع


بيانات المشروع

البند	البيان
المشروع	مجلس وجلسة خارجية مغلقة وغرفة نوم 9.00 × 13.00 م — الحوية
العميل	عميل — الحوية
الموقع	الحوية
الاستخدام	مجلس ضيافة + جلسة مغلقة + غرفة نوم
التاريخ	2026-11-05
نظام البناء	هيكل خشب 5×7 + تلبيس 2.5 سم من الجهتين
السقف	جملون 20° — قرميد معدني


جدول المساحات

م	الفراغ	الأبعاد (م)	المساحة (م2)
1	غرفة نوم	2.38 × 5.88	13.99
2	مستودع	2.38 × 1.88	4.47
3	جلسة خارجية مغلقة	6.38 × 7.88	50.27
4	مجلس	6.88 × 4.88	33.57
5	مغاسل	1.88 × 1.94	3.65
6	حمام	1.88 × 2.88	5.41
	المساحة الصافية الداخلية		**111.38**
	الشرفة	**9.12 × 2.14**	**19.52**
	المساحة الإجمالية المبنية	**9.12 × 13.12**	**119.65**
	المساحة الكلية (المبنية + التراس)		**139.17**

تأطير جدار الواجهة العلوية — الطول 900 سم، الارتفاع 400 سم

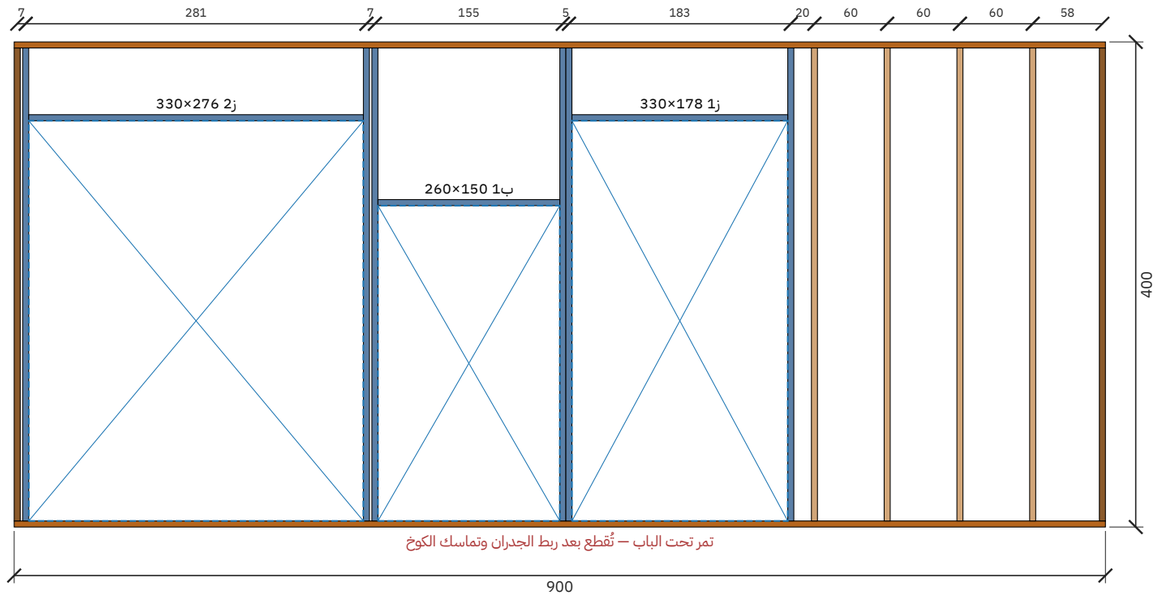

تأطير جدار الجدار الأيمن — الطول 1300 سم، الارتفاع 400 سم

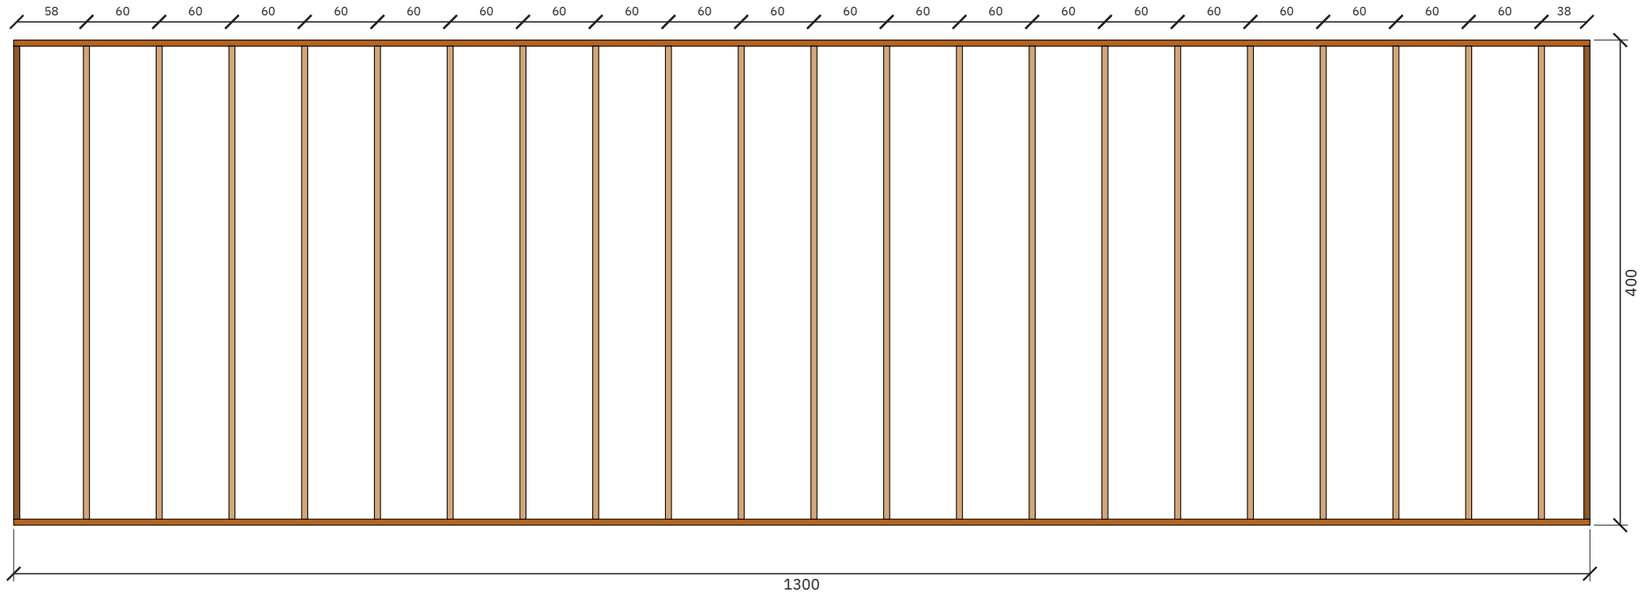


قاعدة سفلية | علوي | عمود | عمود زاوية | جنب فتحة | رأس فتحة | جلسة شباك | عمود قصير


المشروع / العميل	عنوان اللوحة	المقياس	التاريخ	رقم اللوحة
مجلس وجلسة خارجية مغلقة وغرفة نوم 9.00 × 13.00 م — الحوية **عميل — الحوية**	**لوحات التأطير (للورشة)**	—	**2026-11-05**	**W-08 (8/14)**

مصنع وتد الأخشاب
Watad Wood Factory

تأطير جدار الواجهة السفلية — الطول 900 سم، الارتفاع 400 سم

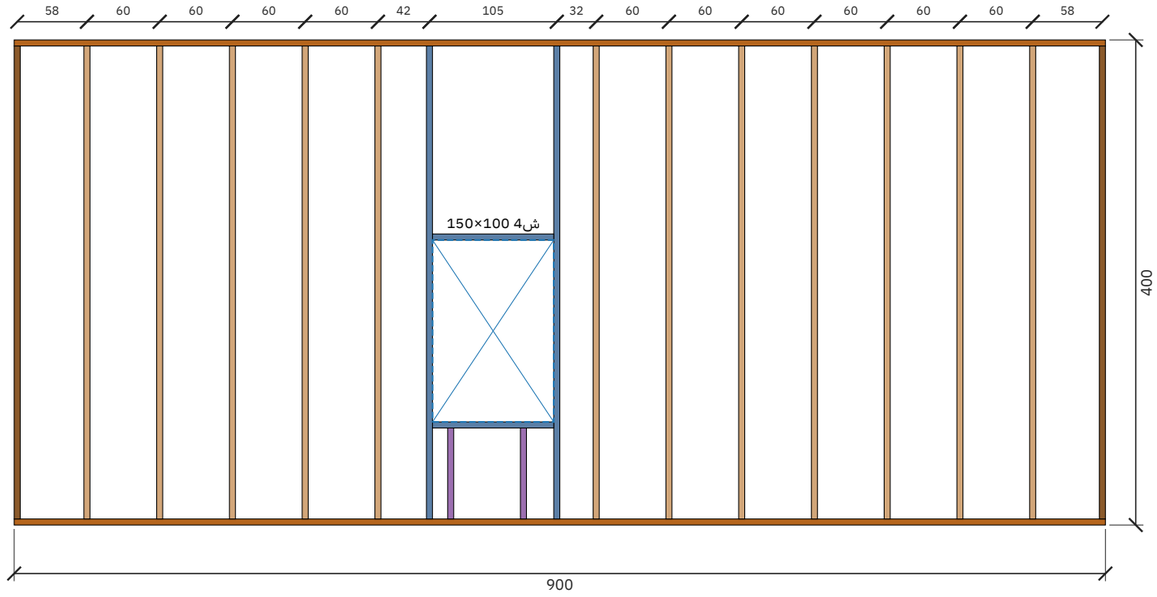

تأطير جدار الجدار الأيسر — الطول 1300 سم، الارتفاع 400 سم

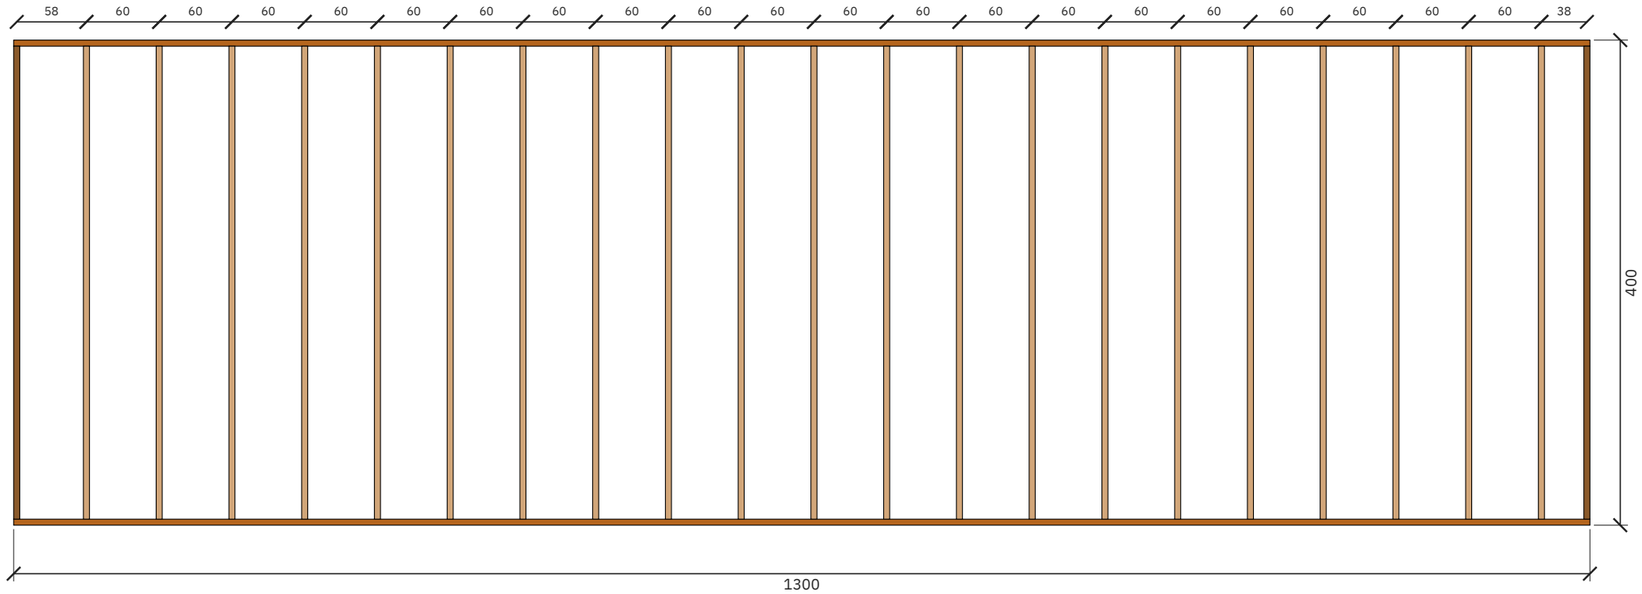


قاعدة سفلية | علوي | عمود | عمود زاوية | جنب فتحة | رأس فتحة | جلسة شباك | عمود قصير


المشروع / العميل	عنوان اللوحة	المقياس	التاريخ	رقم اللوحة
مجلس وجلسة خارجية مغلقة وغرفة نوم 9.00 × 13.00 م — الحوية **عميل — الحوية**	**لوحات التأطير (للورشة)**	—	**2026-11-05**	**W-09 (9/14)**

مصنع وتد الأخشاب
Watad Wood Factory

تأطير جدار جدار الغرفة والمستودع — الجلسة — الطول 800 سم، الارتفاع 400 سم (داخلي)

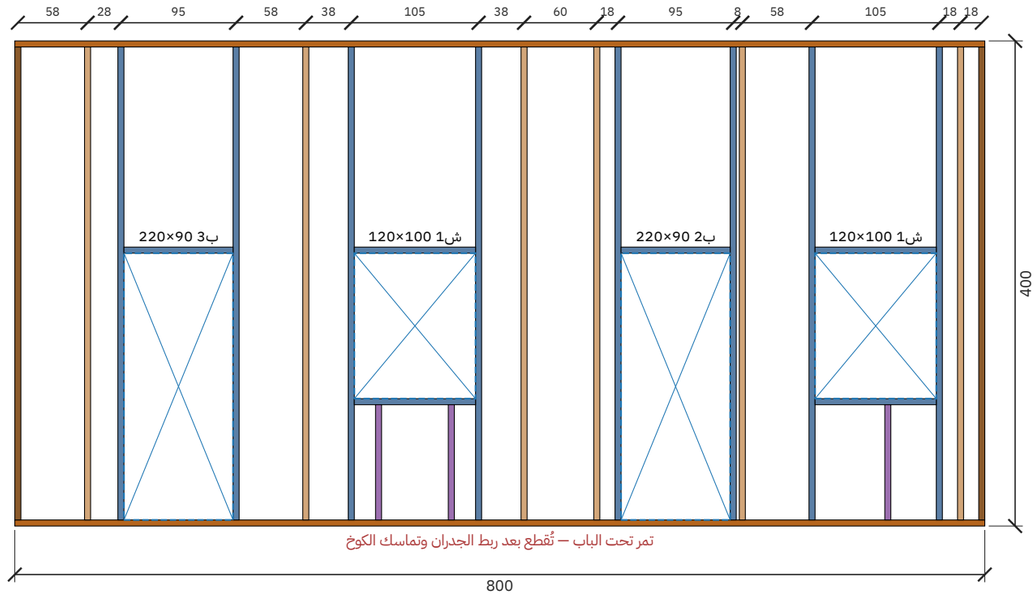

تأطير جدار جدار الغرفة — المستودع — الطول 250 سم، الارتفاع 400 سم (داخلي)

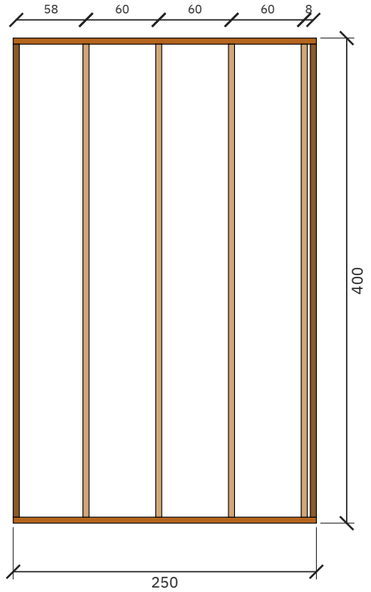


قاعدة سفلية | علوي | عمود | عمود زاوية | جنب فتحة | رأس فتحة | جلسة شباك | عمود قصير


المشروع / العميل	عنوان اللوحة	المقياس	التاريخ	رقم اللوحة
مجلس وجلسة خارجية مغلقة وغرفة نوم 9.00 × 13.00 م — الحوية **عميل — الحوية**	**لوحات التأطير (للورشة)**	—	**2026-11-05**	**W-10 (10/14)**

مصنع وتد الأخشاب
Watad Wood Factory

تأطير جدار جدار المجلس العلوي — الطول 700 سم، الارتفاع 400 سم (داخلي)

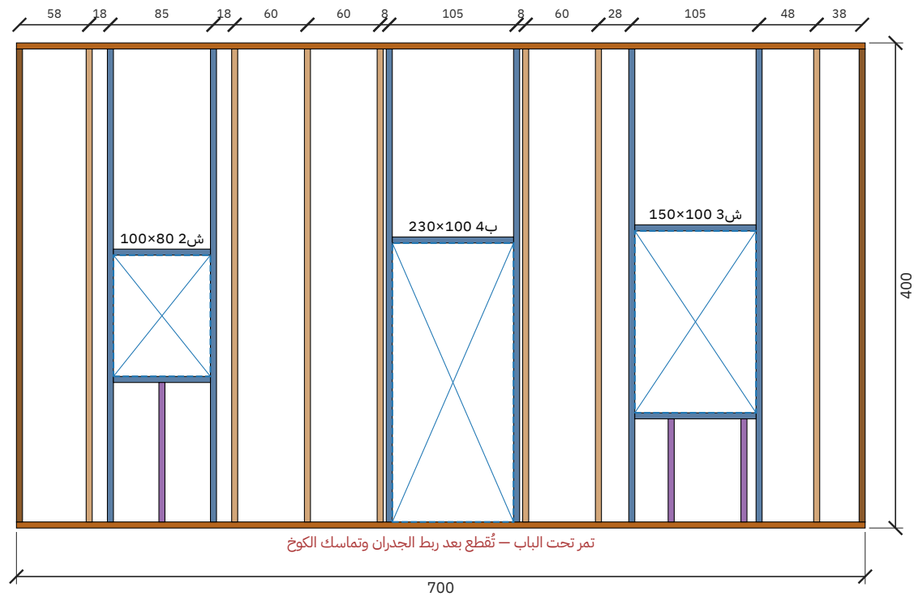

تأطير جدار جدار المجلس — المغاسل والحمام — الطول 500 سم، الارتفاع 400 سم (داخلي)

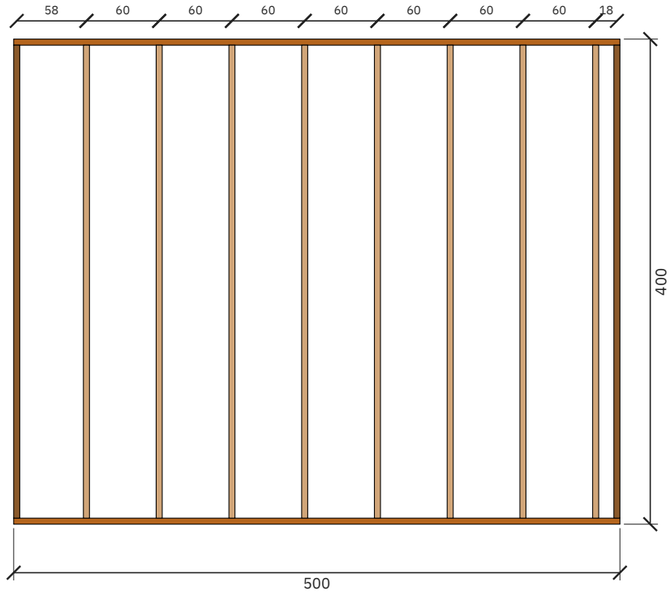


قاعدة سفلية | علوي | عمود | عمود زاوية | جنب فتحة | رأس فتحة | جلسة شباك | عمود قصير

المشروع / العميل	عنوان اللوحة	المقياس	التاريخ	رقم اللوحة
مجلس وجلسة خارجية مغلقة وغرفة نوم 9.00 × 13.00 م — الحوية **عميل — الحوية**	**لوحات التأطير (للورشة)**	**—**	**2026-11-05**	**W-11 (11/14)**

مصنع وتد الأخشاب
Watad Wood Factory

تأطير جدار جدار المغاسل — الحمام — الطول 200 سم، الارتفاع 400 سم (داخلي)

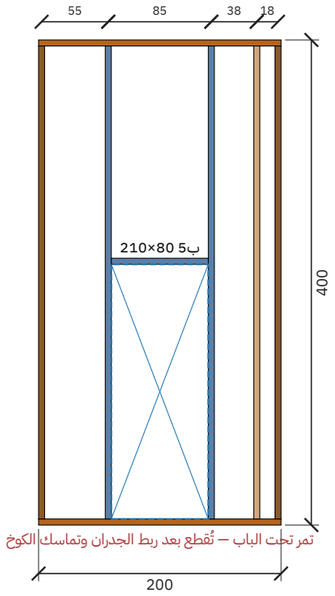

عمود قصير
جلسة شباك
رأس فتحة
جنب فتحة
عمود زاوية
عمود
علوي
قاعدة سفلية

مصنع وتد الأخشاب Watad Wood Factory	المشروع / العميل مجلس وجلسة خارجية مغلقة وغرفة نوم 9.00 × 13.00 م – الحوية عميل – الحوية	عنوان اللوحة لوحات التأطير (للورشة)	المقياس –	التاريخ 2026-11-05	رقم اللوحة W-12 (12/14)

جدول الكميات وخطة تقطيع الطبليات

البند	القيمة
الارتفاع المطلوب / المعتمد	400 / 400 سم
السقف	جملون 20° — أعلى نقطة 639 سم من وجه الصبة
المدادات 5×15	96 مداد (24 خط × قطعتين موصولة فوق الجسر الحامل بتراكب 60 سم) × حتى 458 سم — من طبلية 480
طبليات الطريقة الأولى (مداد + عمود)	96 طبلية × 480 سم
طبليات الطريقة الثانية (3 أعمدة)	5 طبلية × 320 سم
طبليات الطريقة الثانية (طويلة)	20 طبلية × 480 سم
إجمالي الطبليات 5×22.5	121
إجمالي قطع 5×7	169
قائمة تقطيع 5×7	1300سم×4 | 900سم×4 | 800سم×2 | 700سم×2 | 500سم×2 | 390سم×126 | 276سم×1 | 250سم×2 | 200سم×2
	178سم×1 | 150سم×1 | 115سم×1 | 100سم×9 | 95سم×3 | 90سم×2 | 85سم×2 | 80سم×3 | 75سم×2
ألواح تلبيس 2.5 سم	680 لوح × 400 سم (مجموع الصفوف 2317.4 م، 18 وجه)
أسمنت بورد 12 مم (122×244)	32 لوح (داخل دورات المياه)
العزل	335 لوح فوم صخري 80
الصبة	يجهزها العميل — 20 سم، مفرغة تحت دورات المياه

مراجعة التصميم مقابل قواعد المصنع

النوع	البند	التفاصيل	المقترح
تنبيه	تهوية مغاسل	لا يوجد شباك — يحتاج شفاط هواء.	إضافة شفاط أو شباك صغير.
تنبيه	تهوية حمام	لا يوجد شباك — يحتاج شفاط هواء.	إضافة شفاط أو شباك صغير.
ملاحظة	بحر المدادات	أطول بحر بدون جدار داخلي يحمل المداد: جهة أ: 456 سم، جهة ب: 456 سم. يحتاج رقم المصنع لأقصى بحر مسموح لتحديد المدادات اللي تُقوّى 20×5.	
ملاحظة	الصبة والدرج	ارتفاع الصبة 45 سم ← 3 درجة بقائمة 15.0 سم.	
ملاحظة	مناسيب رؤوس الفتحات	رؤوس الأبواب والشبابيك على مناسيب مختلفة: 210، 220، 230، 240، 260، 330 سم.	
تنبيه	ممر حول سرير ضيق	الجنبين 59 / 59 سم وعند الرجلين 388 سم — السرير المزدوج يحتاج ≥ 55 سم من الجهتين و ≥ 60 عند الرجلين (وسّع الغرفة أوغيّر اتجاه السرير).	تحريك القطعة أو الباب/الشباك.
سؤال	يحتاج تأكيد	أقصى بحر للمداد بدون جدار داخلي قبل إضافة تقوية 5×7 (مداد 20×5)؟	
سؤال	يحتاج تأكيد	التغطية الصافية للوح التلبيس بعد التعشيق (مستنتجة مؤقتاً 18.67 سم من 280/15)؟	
سؤال	يحتاج تأكيد	هل يوضع أعمدة قصيرة فوق رأس الشباك/الباب إلى العلوي؟	
سؤال	يحتاج تأكيد	مكان الوصلة في القاعدة والعلوي إذا الجدار أطول من الطبلية؟	