

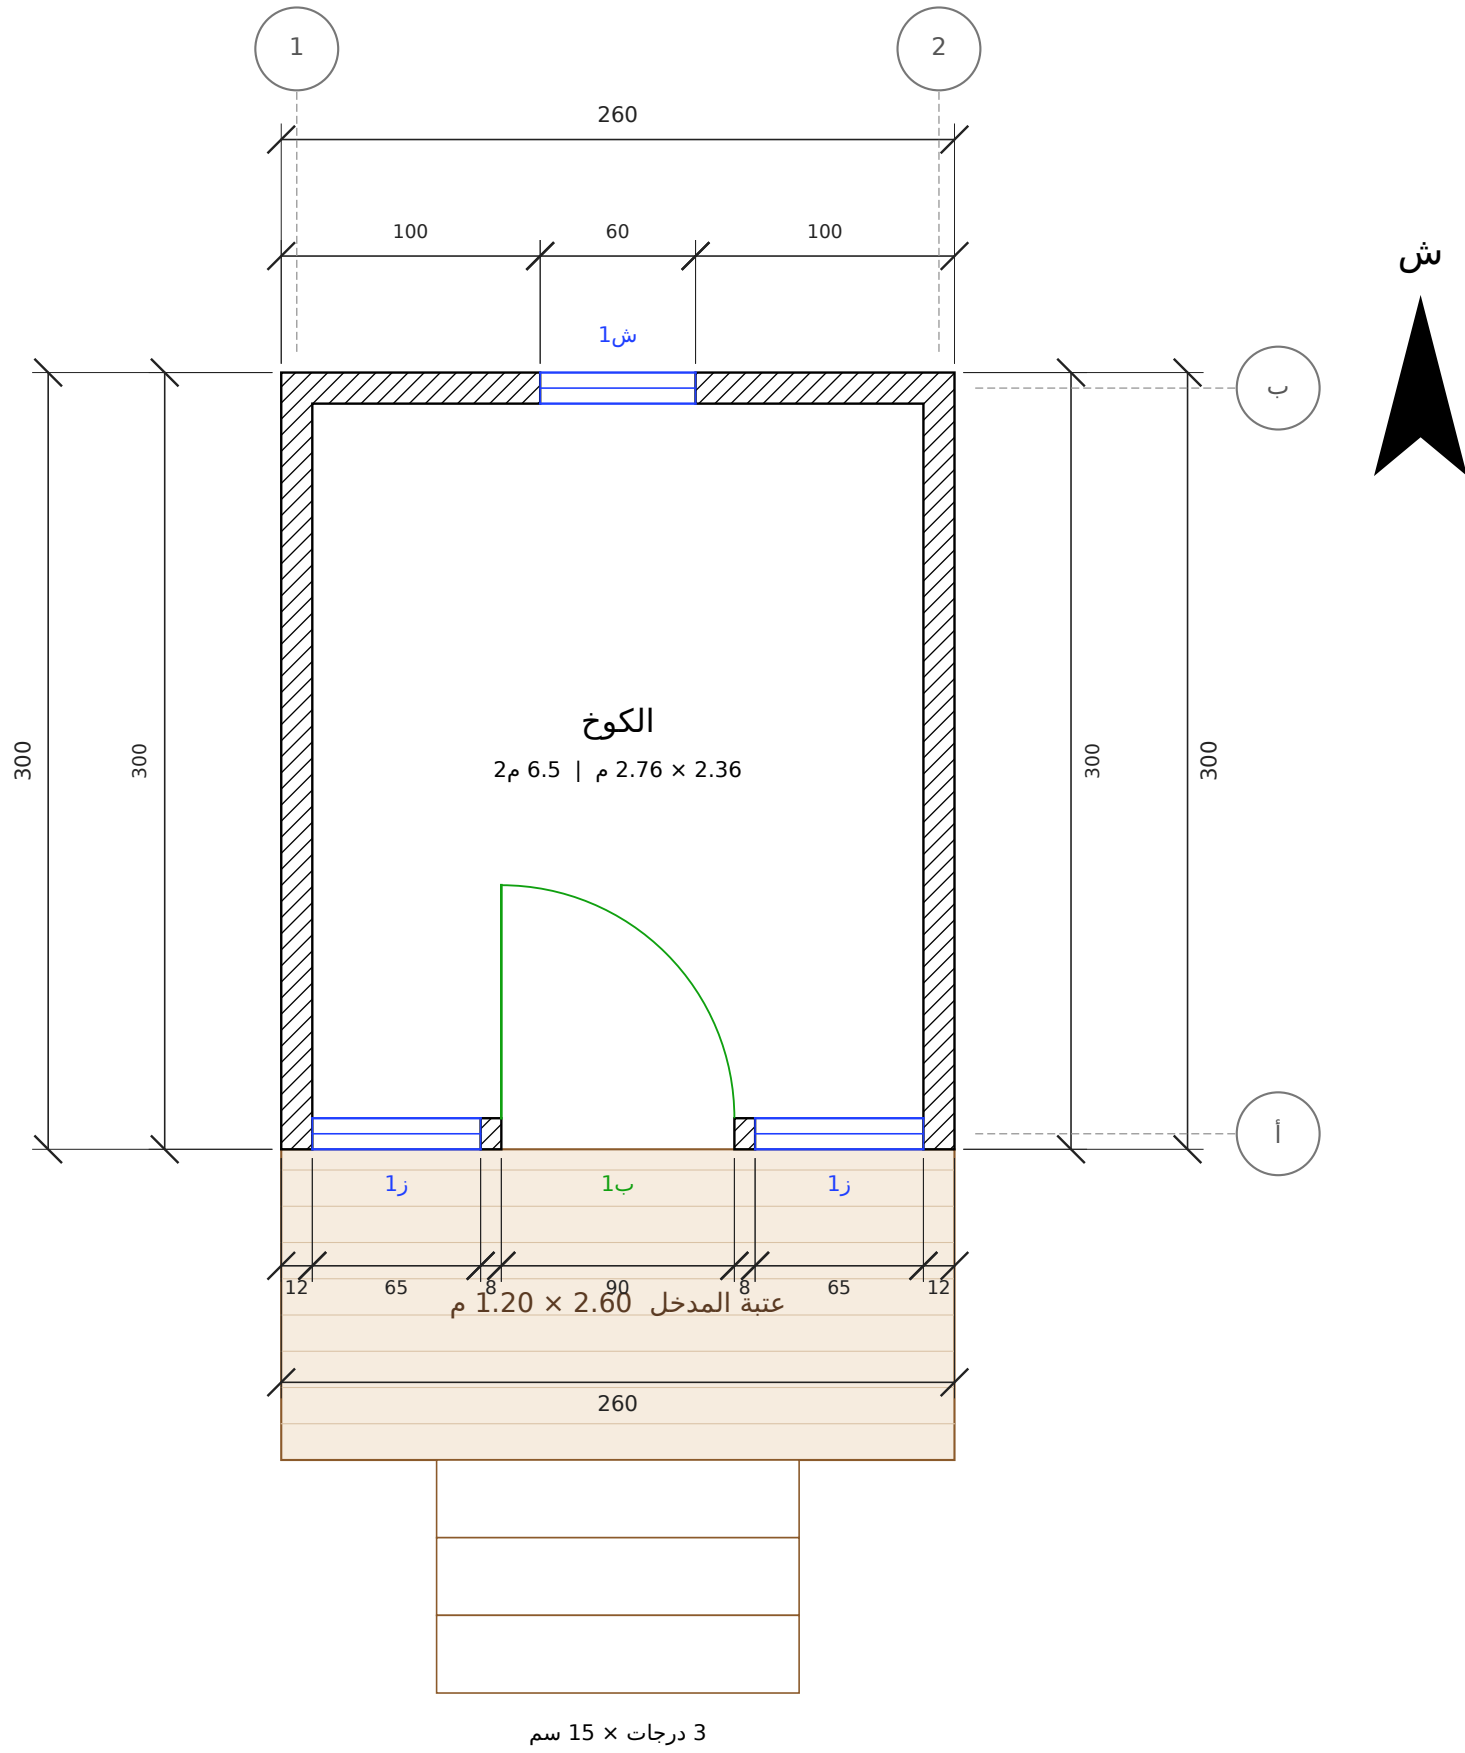



المسقط الأفقي مع الفرش
الأبعاد بالسنتيمتر - الجدران: قوائم 5×7 + تليس 2.5 من الجهتين (12 سم)

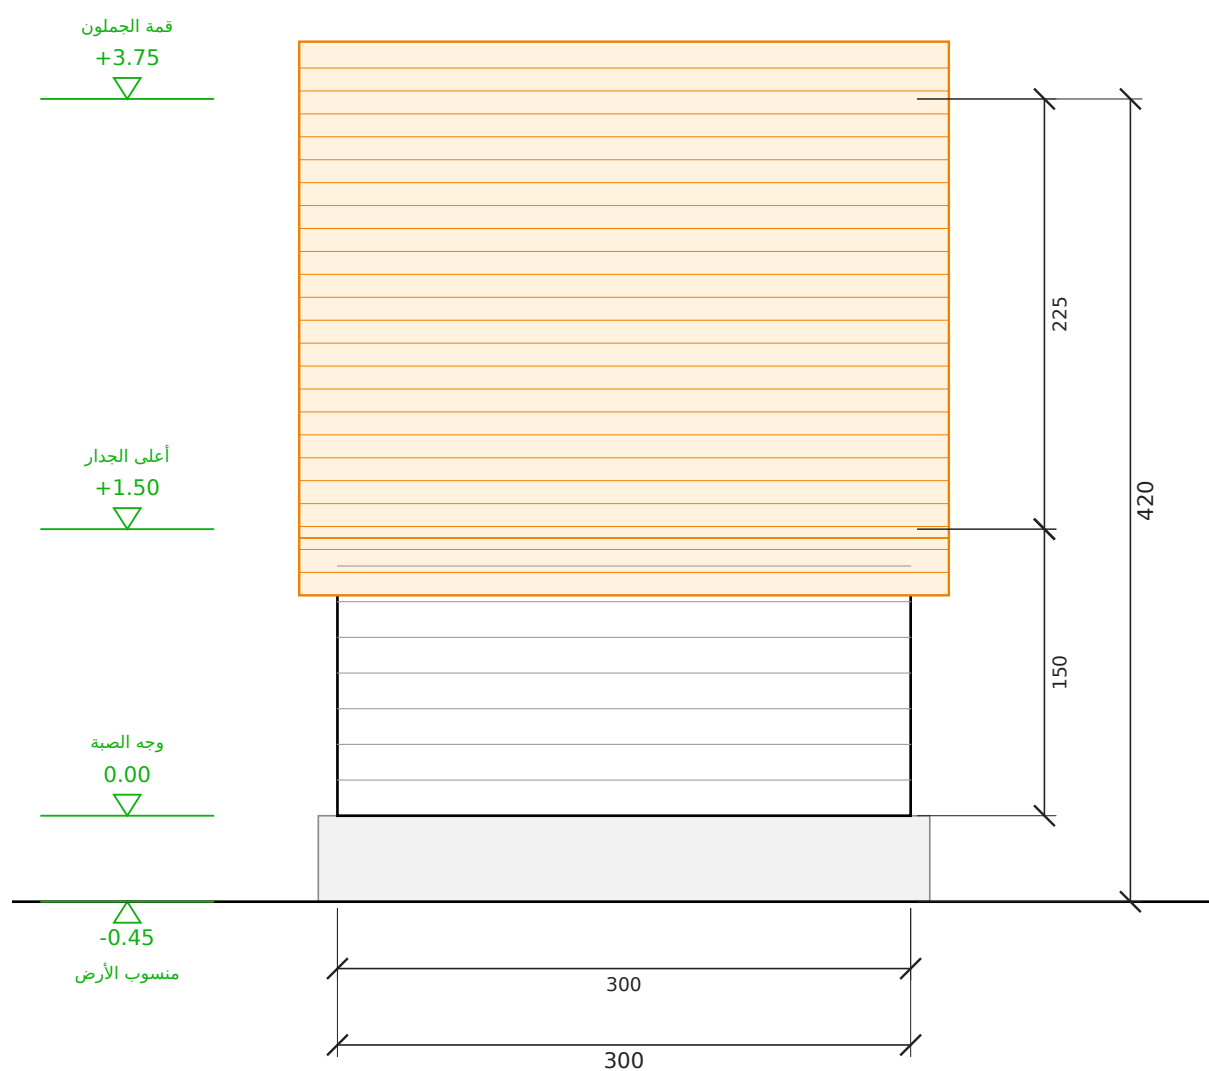

رقم اللوحة	التاريخ	المقياس	عنوان اللوحة	المشروع / العميل	مصنع وتد الأخشاب Watad Wood Factory
A-01 (1/9)	2026-10-09	1:50	المسقط الأفقي	كوخ A-frame بواجهة زجاج 3.00×2.60 عميل - كوخ A-frame	

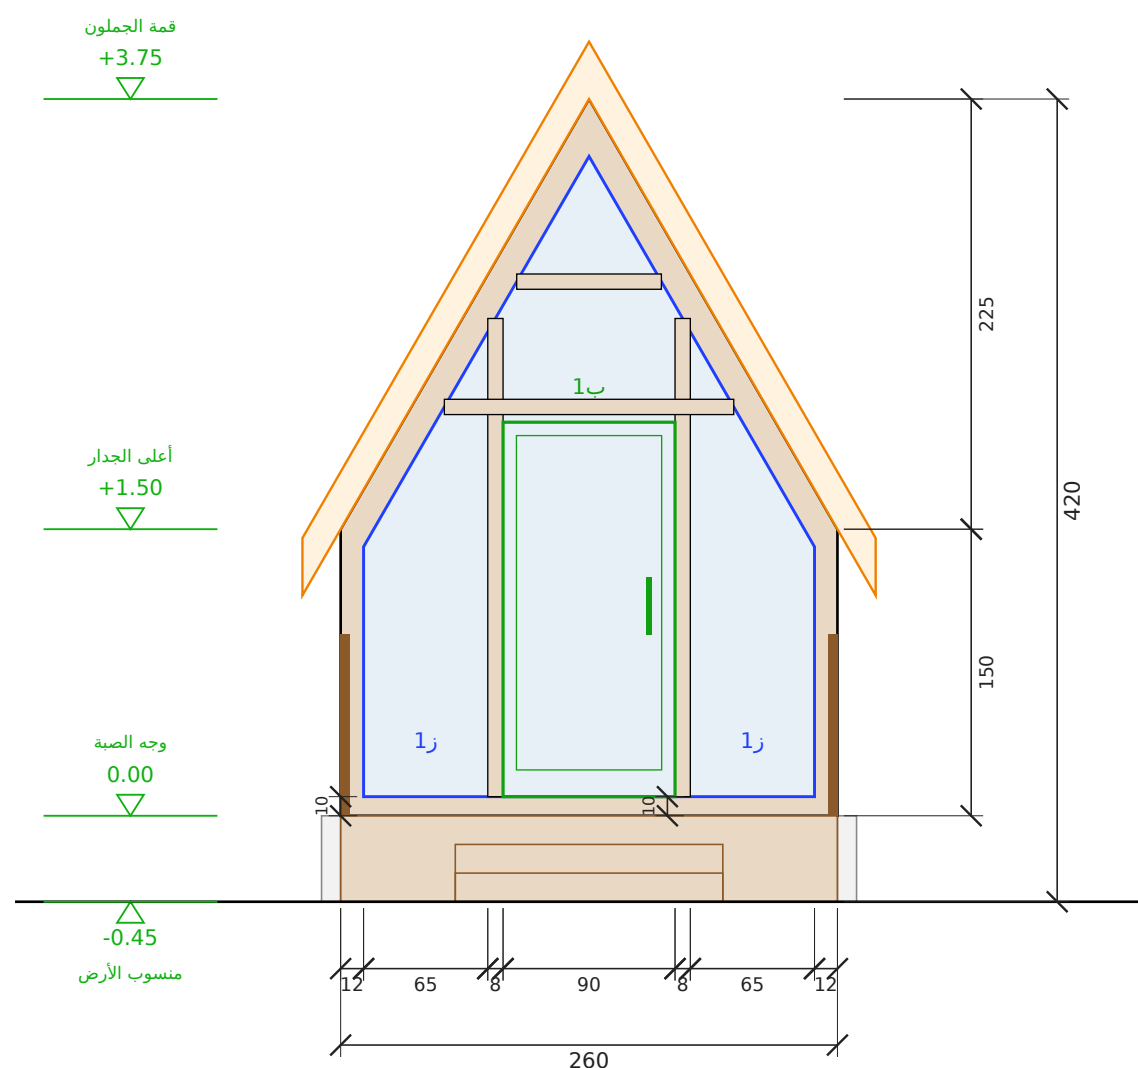


المشروع / العمل	عنوان اللوحة	المقياس	التاريخ	رقم اللوحة
كوخ A-frame بواجهة زجاج 3.00×2.60 عمل — كوخ A-frame	الواجهة الأمامية والواجهة الشرقية	1:50	2026-10-09	A-02 (2/9)

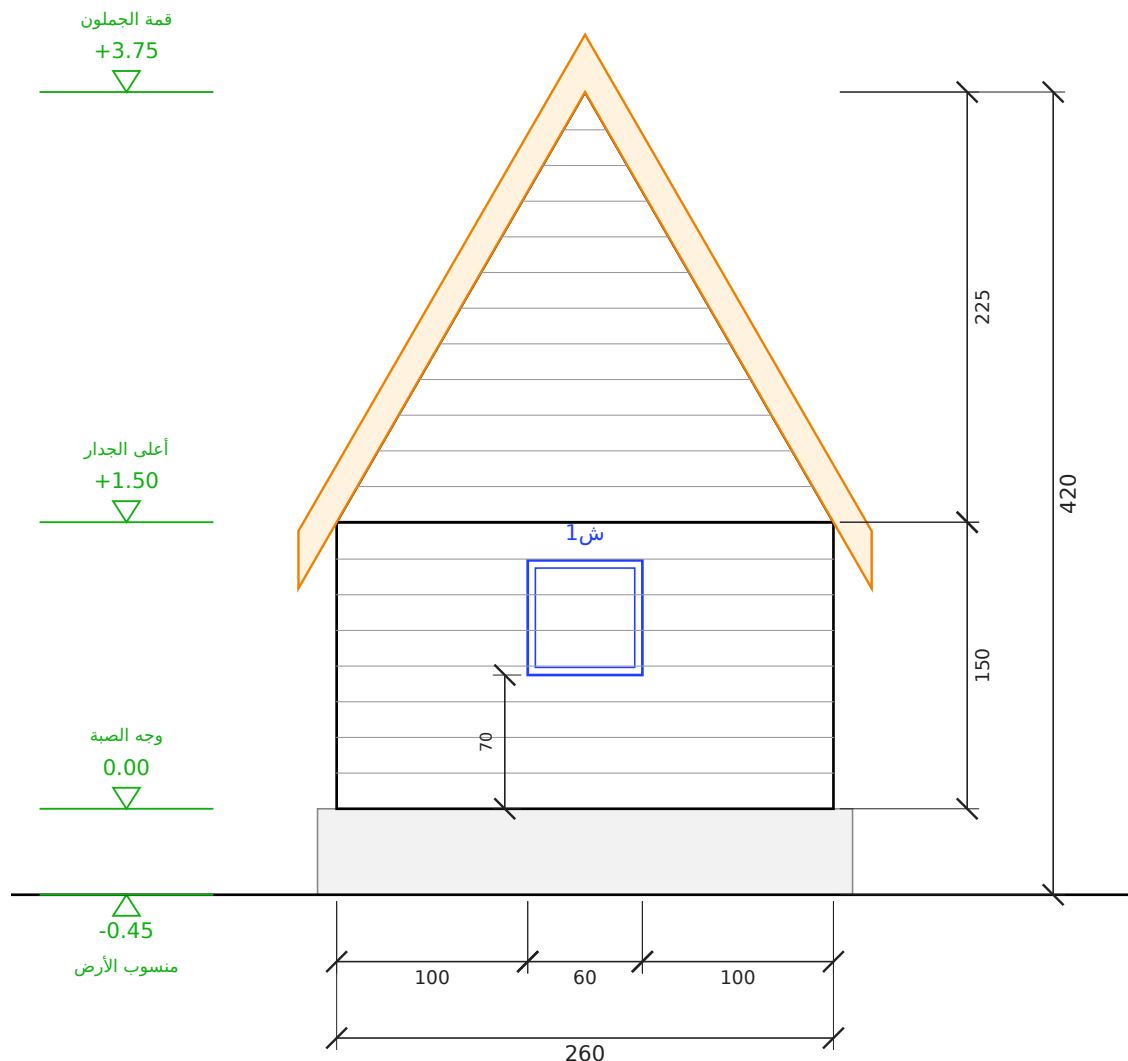

الواجهة الخلفية

مقياس 1:50 | الوحدة: سم

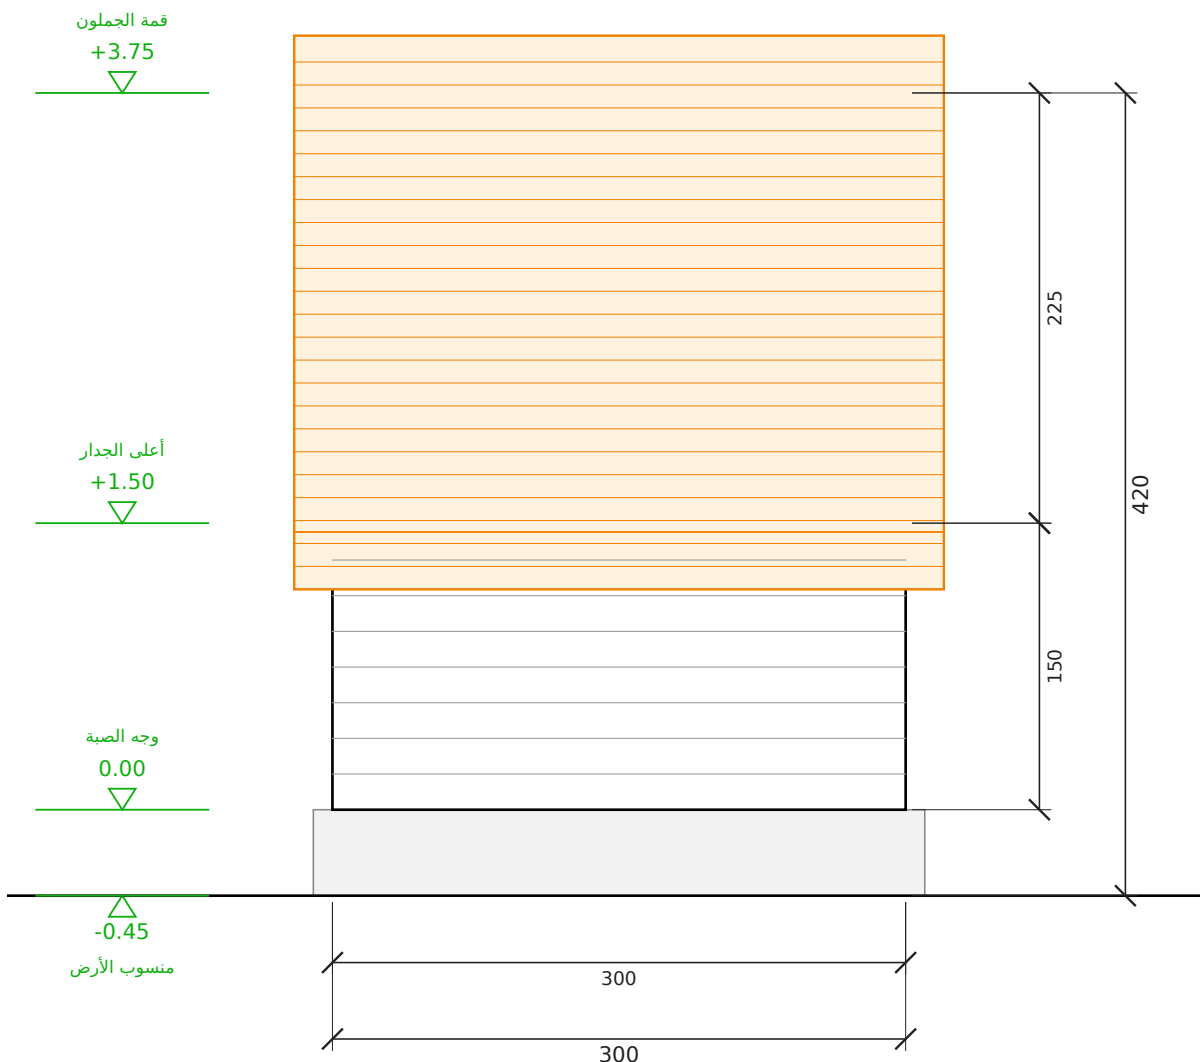


الواجهة الغربية


مقياس 1:50 | الوحدة: سم

رقم اللوحة	التاريخ	المقياس	عنوان اللوحة	المشروع / العميل	مصنع وتد الأخشاب Watad Wood Factory
A-03 (3/9)	2026-10-09	1:50	الواجهة الخلفية والواجهة الغربية	كوخ A-frame بواجهة زجاج 3.00×2.60 عميل – كوخ A-frame	


مسقط السقف (جملون)
رفر 20 سم من كل جهة | مقياس 1:50

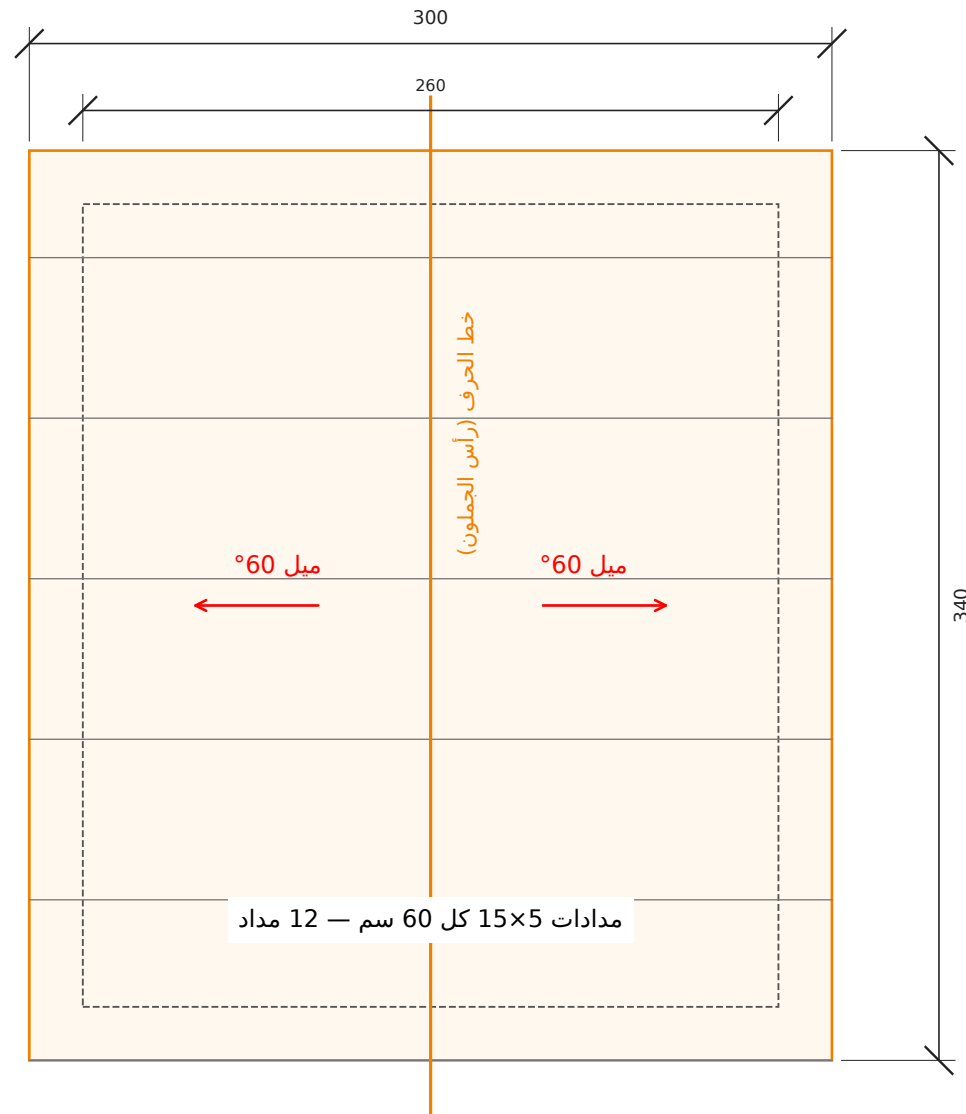

قطاع عرضي أ-أ
مقياس 1:50 | الوحدة: سم

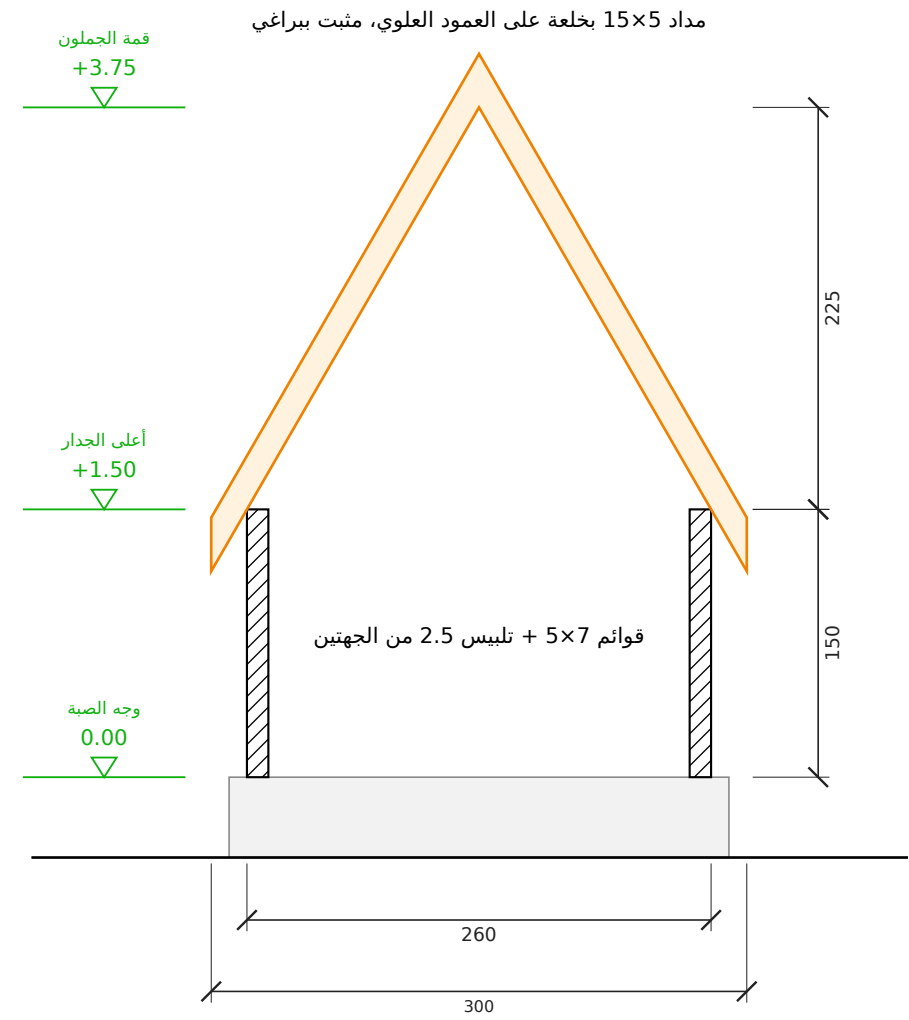

تفصيلة جلوس المداد على العلوي (1:5)

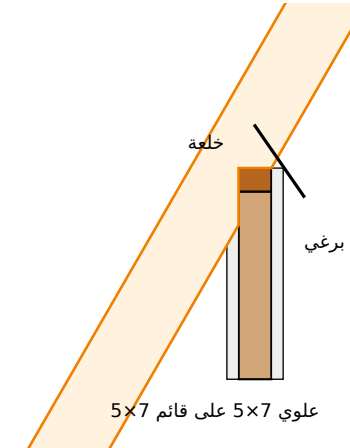

رقم اللوحة

A-04 (4/9)

التاريخ

2026-10-09

المقياس

1:50

عنوان اللوحة

مسقط السقف والقطاع

المشروع / العميل

كوخ A-frame بواجهة زجاج 3.00x2.60
عميل — كوخ A-frame

مصنع وند الأخشاب
Watad Wood Factory



جدول مقاسات الأبواب والشبابيك
مقاس الفتحة الصافي في الجدار - الوحدة: سم

الرمز	النوع	العرض (سم)	الارتفاع (سم)	ارتفاع الجلسة (سم)	العدد	الموقع
ب1	باب	90	210	-	1	الأمامية
ر1	شباك	65	140	10	2	الأمامية 2
ش1	شباك	60	60	70	1	الخلفية

الإجمالي: أبواب 1 - شبابيك 3

جدول المساحات وبيانات المشروع والتسعير

جدول المساحات

م	الفراغ	الأبعاد (م)	المساحة (م2)
1	الكوخ	2.36 × 2.76	6.51
	المساحة الصافية الداخلية		6.51
	التراس المسقوف (مجاناً)	2.60 × 1.20	3.12
	المساحة الإجمالية المبنية	2.60 × 3.00	7.80

بيانات المشروع

البند	البيان
المشروع	كوخ A-frame بواجهة زجاج 3.00×2.60
العميل	عميل — كوخ A-frame
الموقع	—
الاستخدام	كوخ / استراحة
التاريخ	2026-10-09
نظام البناء	هيكل خشب 5×7 + تليس 2.5 سم من الجهتين
السقف	جملون 60° — قرميد معدني

التسعير

البند	القيمة
المساحة المبنية (م2)	7.80
سعر المتر المربع	1,196 ريال
الإجمالي	9,329 ريال

ملاحظات:

- السعر للمساحة المبنية حسب المخطط المعتمد.
- الصبة والتوريدات الخارجية على العميل ما لم يُذكر غير ذلك.

لقطات المنظور الخارجي


منظور أمامي من اليمين



منظور أمامي من اليسار



المنظور الأمامي

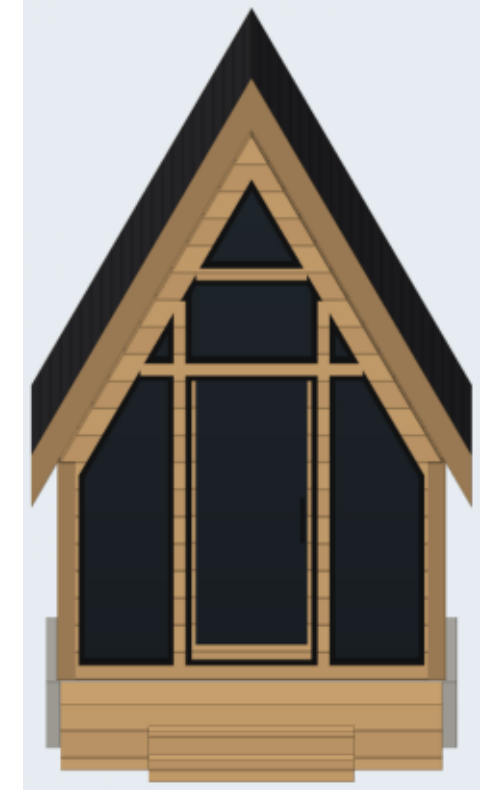

منظر علوي



منظور خلفي من اليمين



المنظور الخلفي



رقم اللوحة

A-07 (7/9)

التاريخ

2026-10-09

المقياس

—

عنوان اللوحة

لقطات المنظور

المشروع / العميل


كوخ A-frame بواجهة زجاج 3.00×2.60
عميل — كوخ A-frame

مصنع وتد الأخشاب
Watad Wood Factory



المقطع العلوي بالفرش

مقطع أفقي على ارتفاع 1.90 م — توزيع الفرش ومسار الحركة

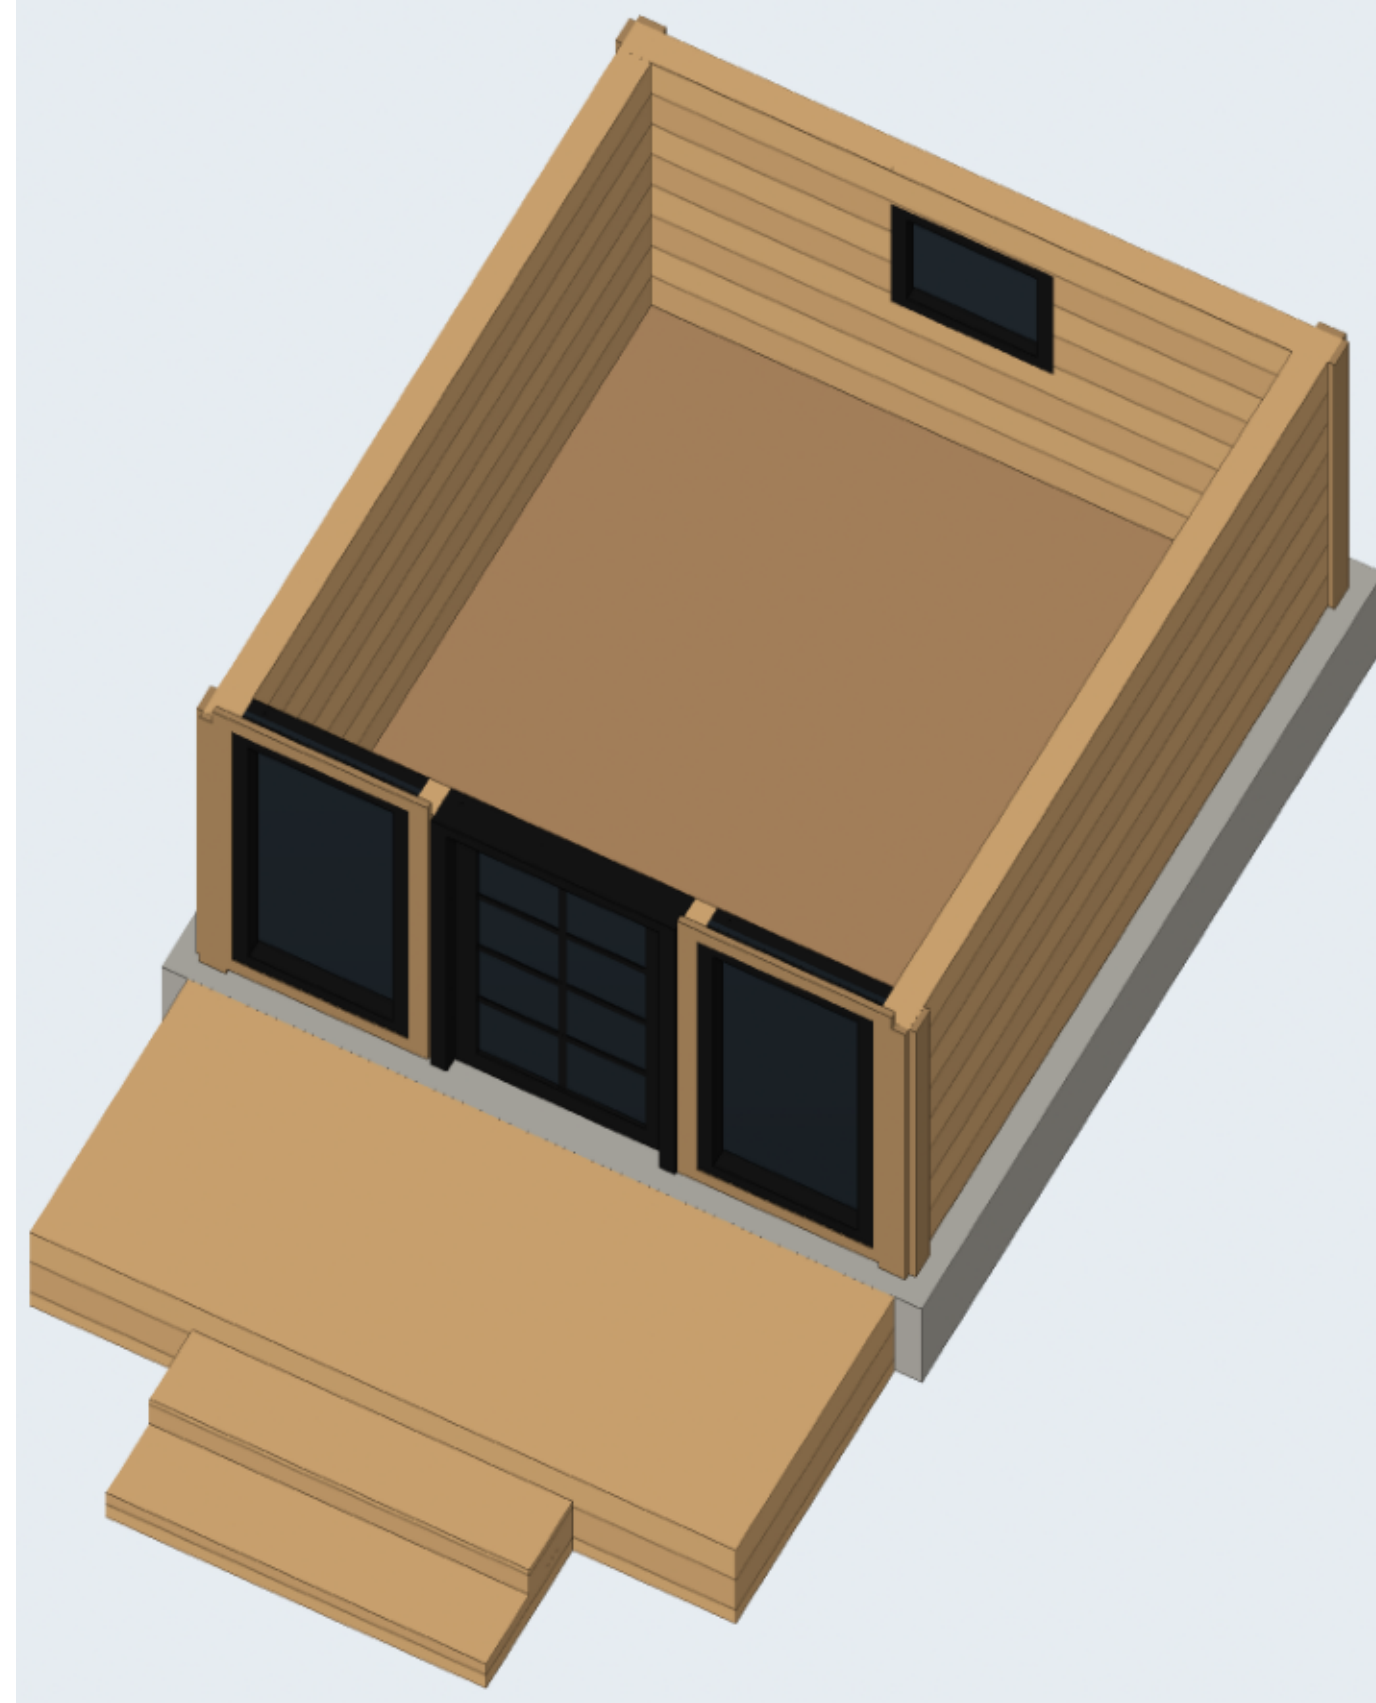

رقم اللوحة

A-08 (8/9)

التاريخ

2026-10-09

المقياس

—

عنوان اللوحة

المقطع العلوي بالفرش

المشروع / العميل

كوخ A-frame بواجهة زجاج 3.00×2.60
عميل — كوخ A-frame


مصنع وتد الأخشاب
Watad Wood Factory



المنظور ثلاثي الأبعاد والمواد

النمط: جوزي غامق + إطارات سوداء — رندر واقعي بخامات حقيقية

جدول المواد والألوان

 

الخشب / الصبغة
خشب طبيعي فاتح (بدون صبغة)



القرميد
قرميد رمادي غامق



الزجاج
زجاج عاكس غامق



إطارات الشبابيك والأبواب
إطار ألومنيوم أسود



الكنار والزوايا
نفس الصبغة أعمق درجة



الصبة
خرسانة 45 سم


الدريزين: ألواح أفقية متقاربة (عصري)

تقسيم الشبابيك: بدون | الباب الرئيسي: زجاج بتقسيمات (فرنسي)


أنواع الدريزين المعتمدة (من مشاريع المصنع)



قوائم رأسية متقاربة (صورة 1)

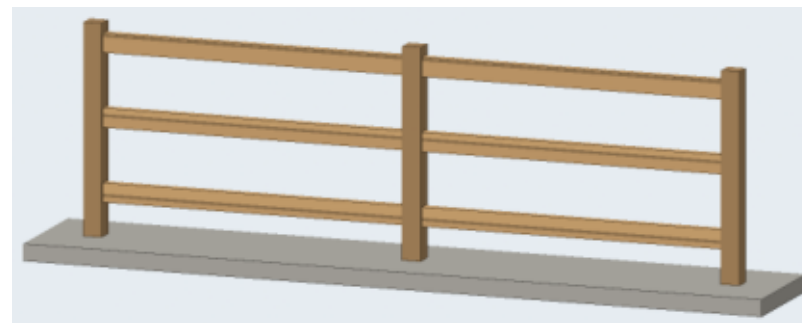

3 مربيع أفقية (صورة 2)

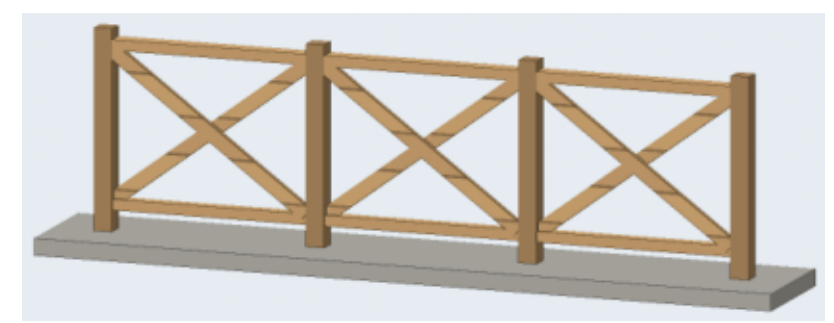

تقاطع X (صورة 5)

رقم اللوحة

A-09 (9/9)

التاريخ

2026-10-09

المقياس

—

عنوان اللوحة

المنظور والمواد

المشروع / العميل

كوخ A-frame بواجهة زجاج 3.00×2.60
عميل — كوخ A-frame

مصنع وتد الأخشاب
Watad Wood Factory

