
المسقط الأفقي مع الفرش — الدور الأرضي

الأبعاد بالسنتيمتر - الجدران: قوائم 7×5 + تلبيس 2.5 من الجهتين (12 سم) | منسوب الأرضية +0.00

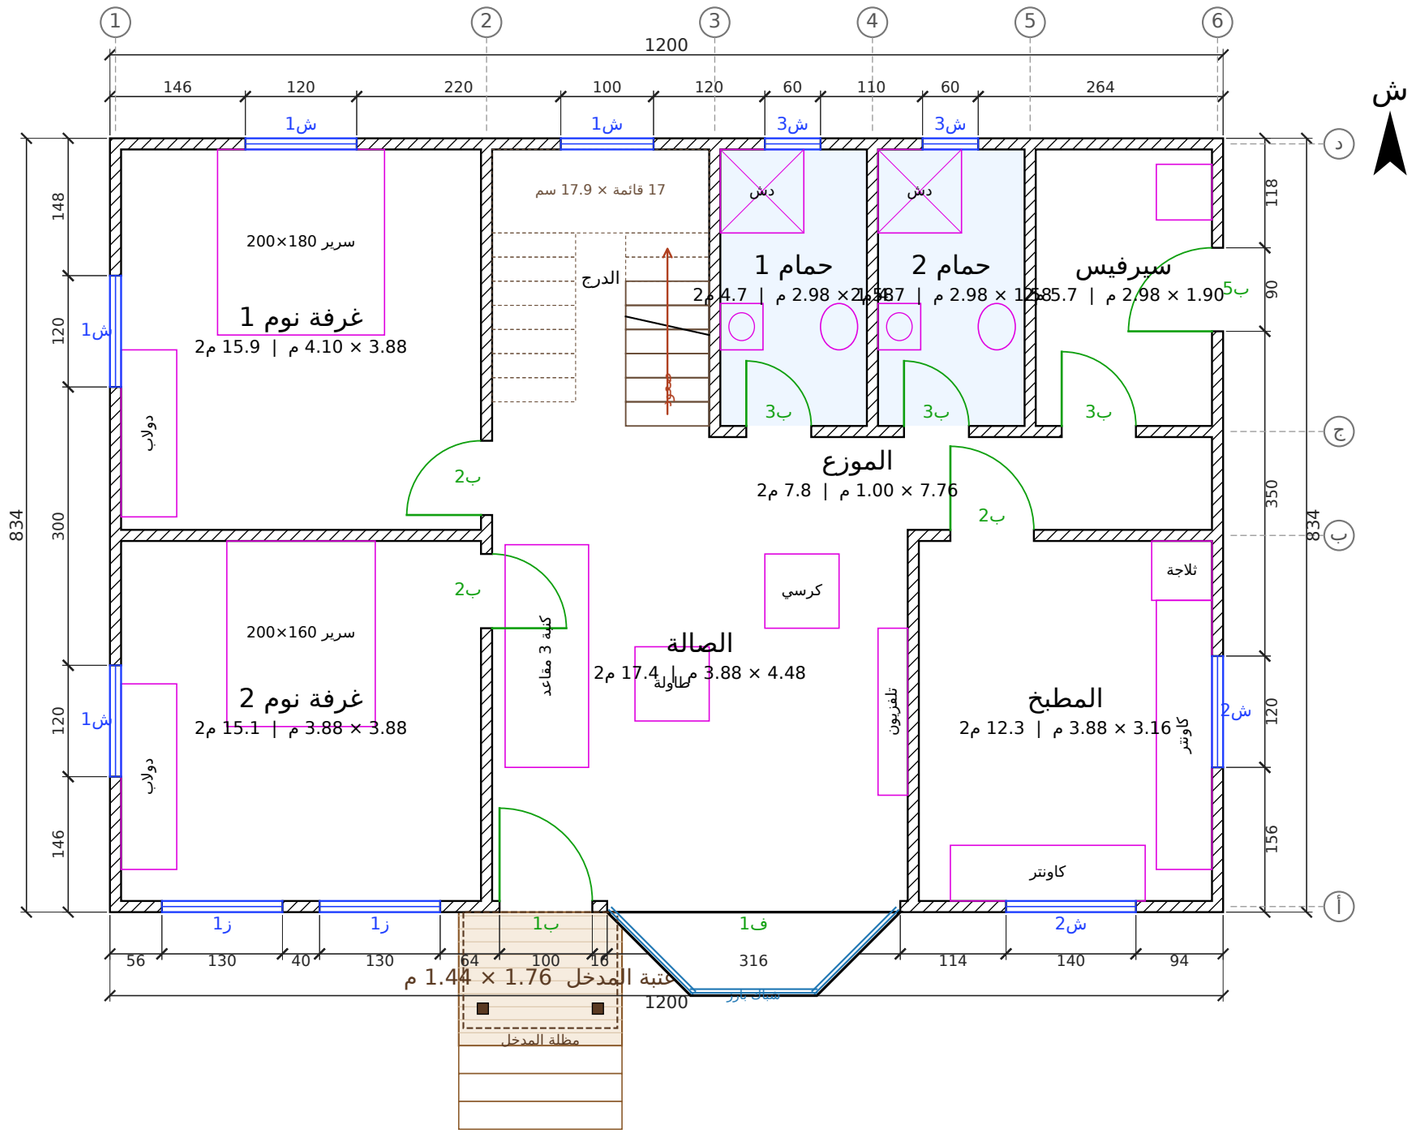


المشروع / العميل	عنوان اللوحة	المقياس	التاريخ	رقم اللوحة
كوخ دورين 6 غرف — 200 م² **عميل — ذهبان**	**المسقط الأفقي — الدور الأرضي**	**1:50**	**2026-10-11**	**A-01 (1/11)**

مصنع وتد الأخشاب
Watad Wood Factory

المسقط الأفقي مع الفرش — الدور الأول

الأبعاد بالسنتيمتر - الجدران: قوائم 7×5 + تلبيس 2.5 من الجهتين (12 سم) | منسوب الأرضية +3.05

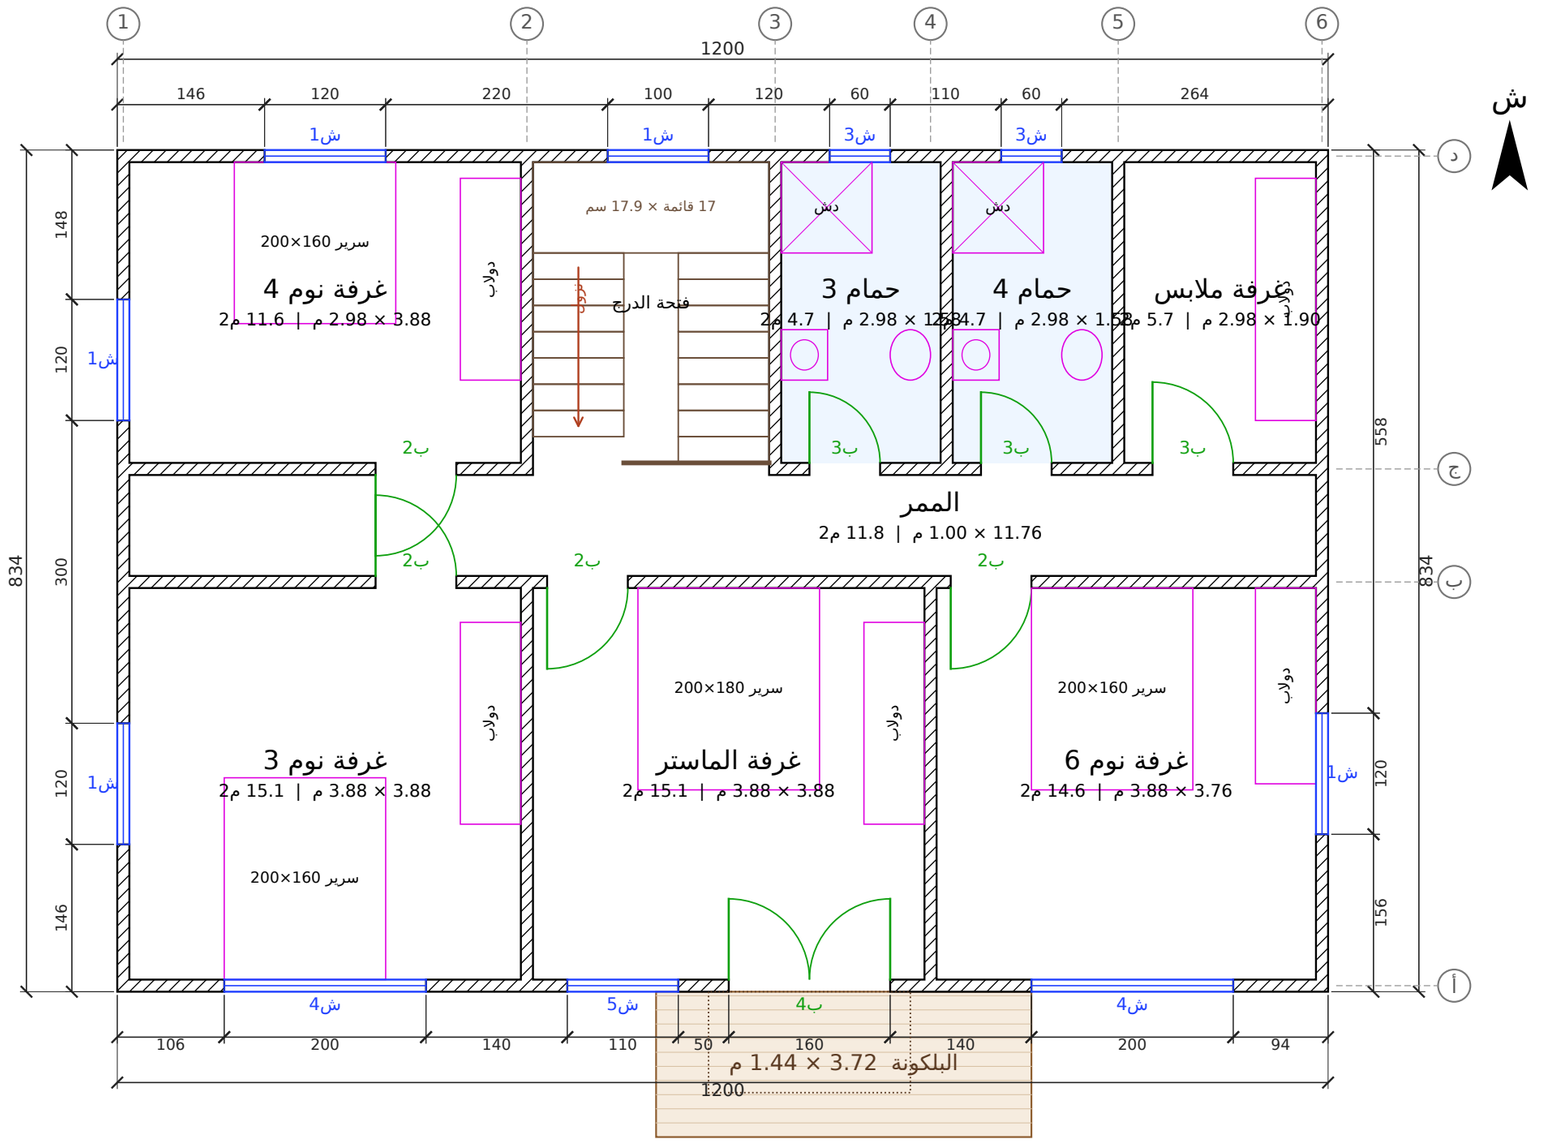


المشروع / العميل	عنوان اللوحة	المقياس	التاريخ	رقم اللوحة
كوخ دورين 6 غرف — 200 م² عميل — ذهبان	المسقط الأفقي — الدور الأول	1:50	2026-10-11	A-02 (2/11)

مصنع وتد الأخشاب
Watad Wood Factory



الواجهة الأمامية

مقياس 1:50 | الوحدة: سم

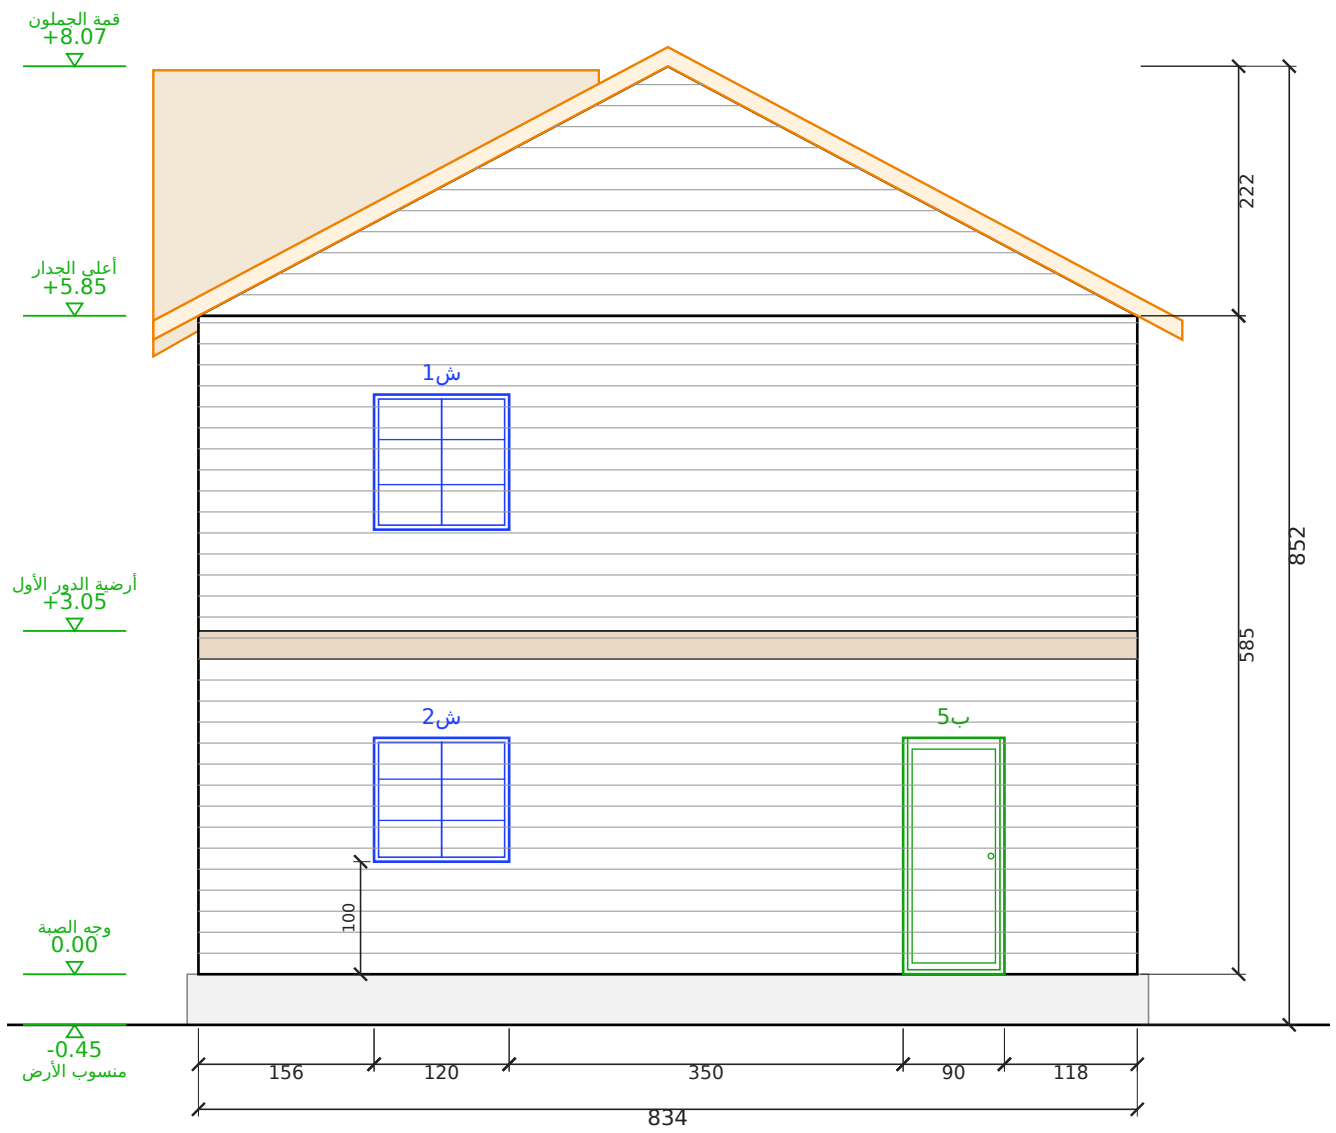


الواجهة الشرقية

مقياس 1:50 | الوحدة: سم


المشروع / العميل	عنوان اللوحة	المقياس	التاريخ	رقم اللوحة
كوخ دورين 6 غرف — 200 م² عميل — ذهبان	الواجهة الأمامية والواجهة الشرقية	1:50	2026-10-11	A-03 (3/11)

مصنع وتد الأخشاب
Watad Wood Factory

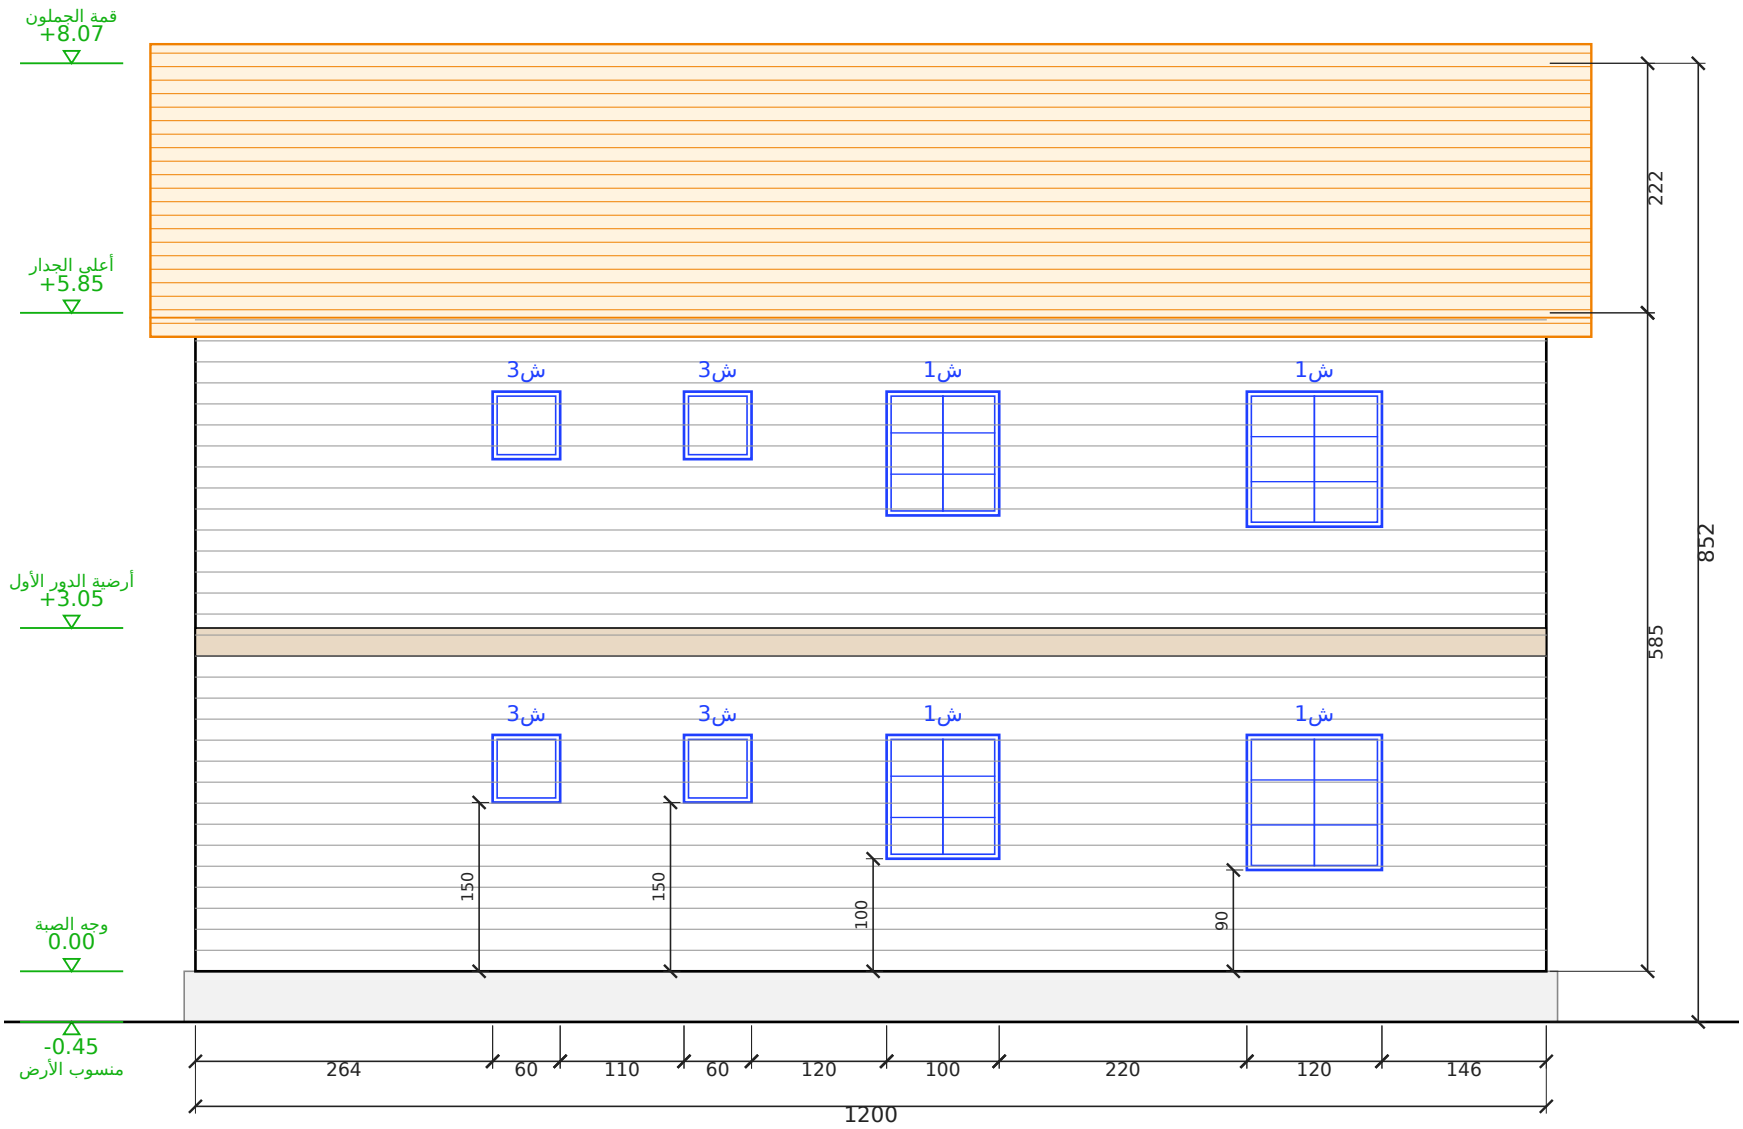

الواجهة الخلفية

مقياس 1:50 | الوحدة: سم

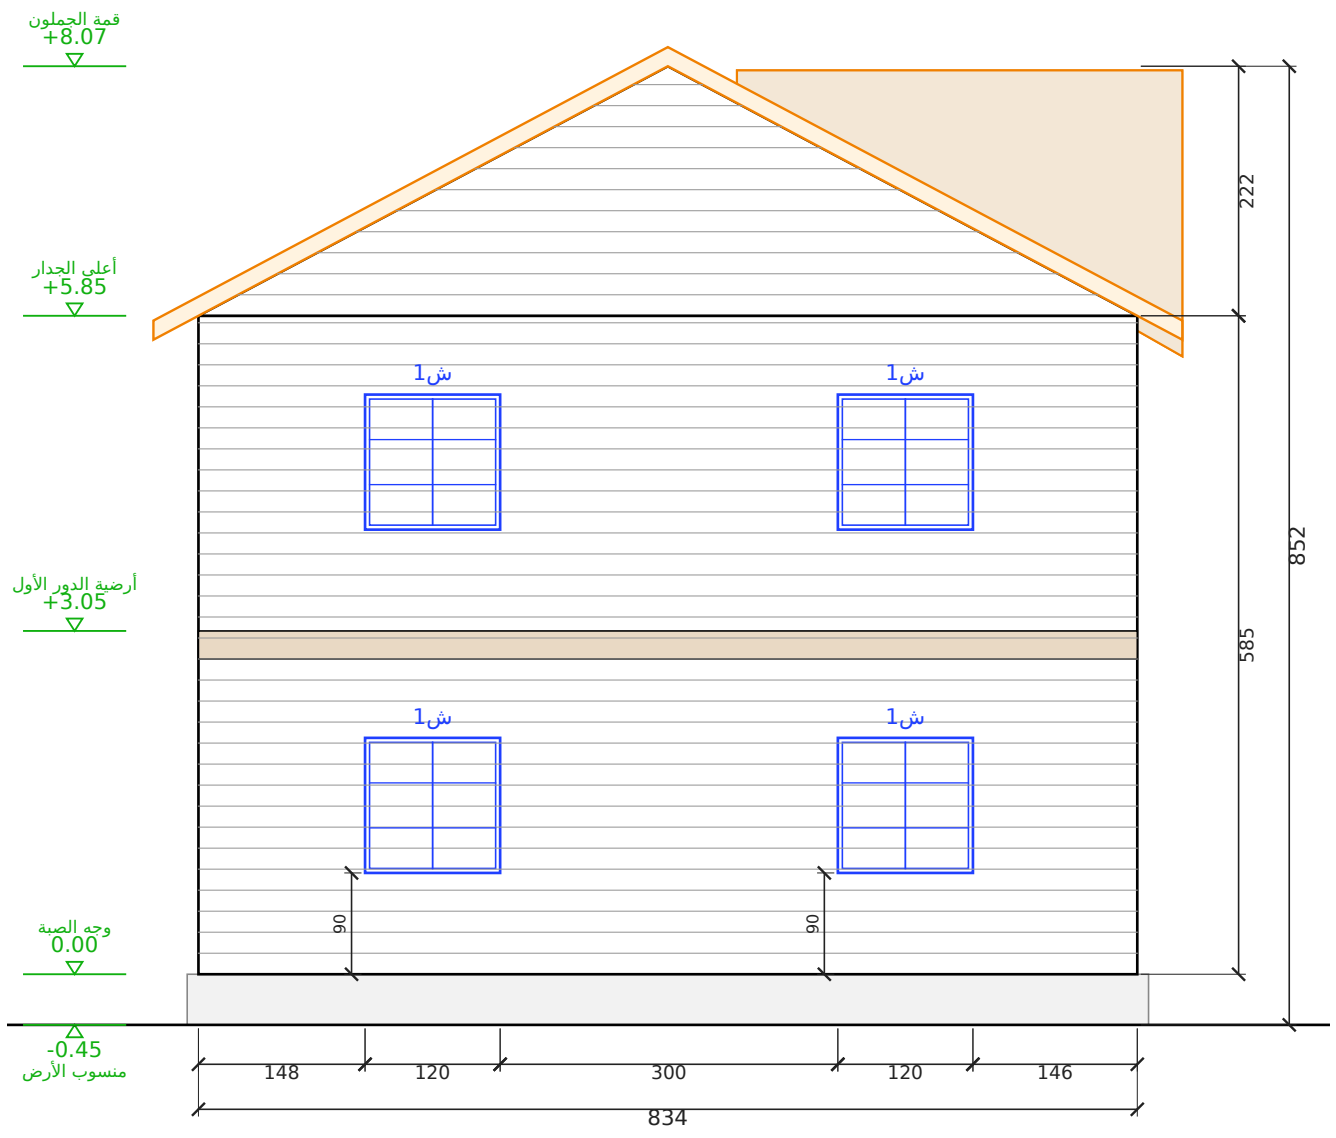


الواجهة الغربية

مقياس 1:50 | الوحدة: سم


المشروع / العميل	عنوان اللوحة	المقياس	التاريخ	رقم اللوحة
كوخ دورين 6 غرف — 200 م² **عميل — ذهبان**	**الواجهة الخلفية والواجهة الغربية**	**1:50**	**2026-10-11**	**A-04 (4/11)**

مصنع وتد الأخشاب
Watad Wood Factory


مسقط السقف (جملون)
رفرف 40 سم من كل جهة | مقياس 1:50

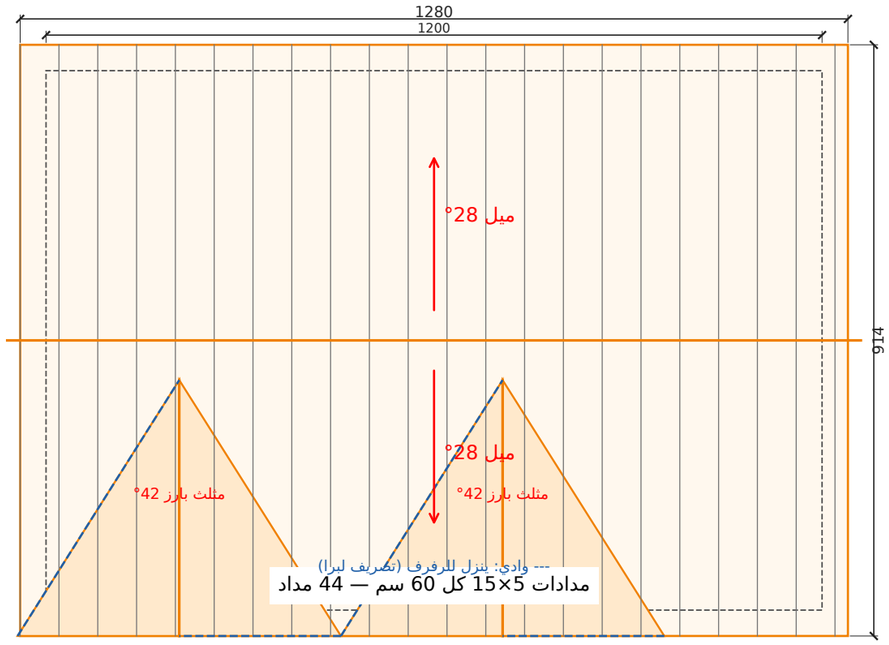

قطاع عرضي أ-أ
مقياس 1:50 | الوحدة: سم

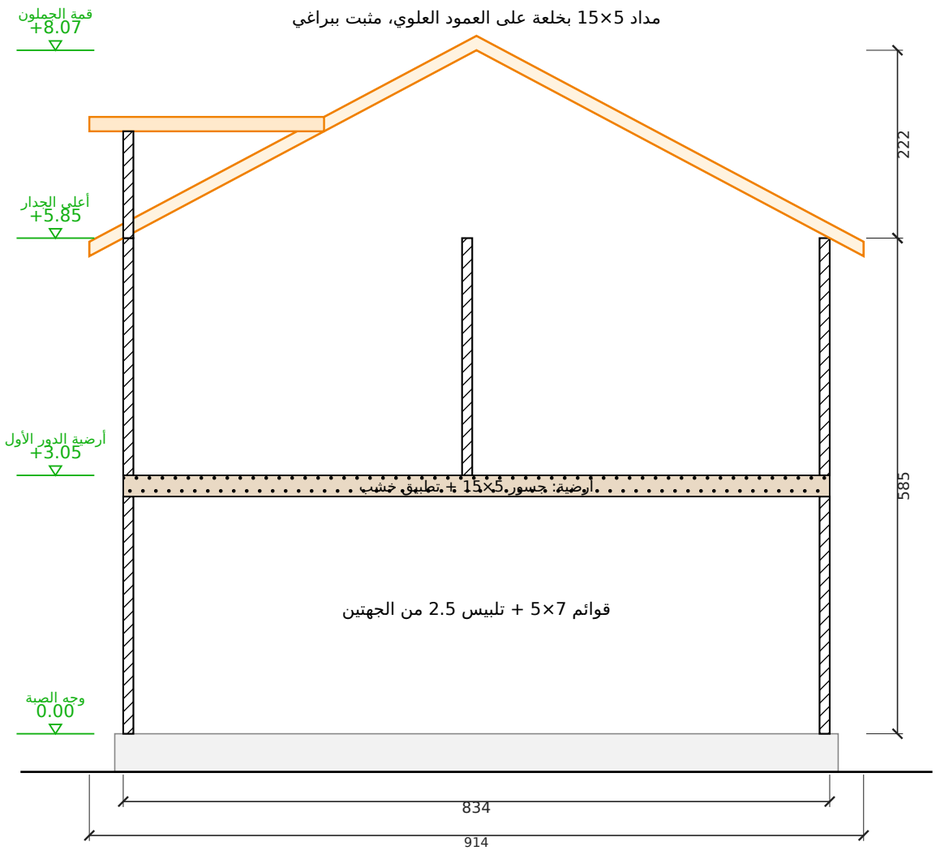

تفصيلة جلوس المداد على العلوي (1:5)

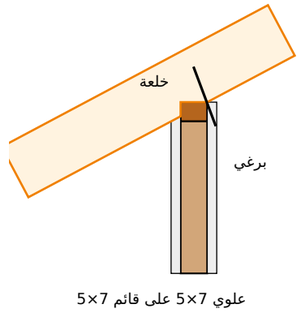

المشروع / العميل	عنوان اللوحة	المقياس	التاريخ	رقم اللوحة
كوخ دورين 6 غرف — 200 م² **عميل — ذهبان**	**مسقط السقف والقطاع**	**1:50**	**2026-10-11**	**A-05 (5/11)**

مصنع وتد الأخشاب
Watad Wood Factory

جدول مقاسات الأبواب والشبابيك
مقاس الفتحة الصافي في الجدار - الوحدة: سم

الرمز	النوع	العرض (سم)	الارتفاع (سم)	ارتفاع الجلسة (سم)	العدد	الموقع
ب1	باب	100	225	-	1	الأمامية
ب2	باب	80	210	-	6	غرفة 2 - غرفة 1 - غرفة 3 - الماستر - غرفة 6 - غرفة 4
ب2	باب	90	210	-	1	المطبخ
ب3	باب	70	210	-	4	حمام 1 - حمام 2 - حمام 3 - حمام 4
ب3	باب	80	210	-	2	السيرفيس - غرفة الملابس
ب4	باب مزدوج	160	230	-	1	الأمامية
ب5	باب	90	210	-	1	الشرقية
ف1	باب	316	250	-	1	الأمامية
ز1	شباك	130	220	20	2	الأمامية 2
ش1	شباك	100	110	100	2	الخلفية 2
ش1	شباك	120	120	90	7	الخلفية 2 - الغربية 4 - الشرقية
ش2	شباك	140	110	100	1	الأمامية
ش2	شباك	120	110	100	1	الشرقية
ش3	شباك	60	60	150	4	الخلفية 4
ش4	شباك	200	150	80	2	الأمامية 2
ش5	شباك	110	150	80	1	الأمامية

الإجمالي: أبواب 17 - شبابيك 20

جدول المساحات وبيانات المشروع والتسعير

بيانات المشروع

البند	البيان
المشروع	كوخ دورين 6 غرف — 200 م²
العميل	عميل — ذهبان
الموقع	ذهبان
الاستخدام	سكن خاص
التاريخ	2026-10-11
نظام البناء	هيكل خشب 5×7 + تلبيس 2.5 سم من الجهتين
السقف	جملون 28° — قرميد معدني + 2 مثلث بارز

جدول المساحات

م	الفراغ	الأبعاد (م)	المساحة (م2)
1	أرضي — غرفة نوم 2	3.88 × 3.88	15.05
2	أرضي — الصالة	4.48 × 3.88	17.38
3	أرضي — المطبخ	3.16 × 3.88	12.26
4	أرضي — الموزع	7.76 × 1.00	7.76
5	أرضي — غرفة نوم 1	3.88 × 4.10	15.91
6	أرضي — الدرج	2.34 × 2.98	6.97
7	أرضي — حمام 1	1.58 × 2.98	4.71
8	أرضي — حمام 2	1.58 × 2.98	4.71
9	أرضي — سيرفيس	1.90 × 2.98	5.66
10	أول — غرفة نوم 3	3.88 × 3.88	15.05
11	أول — غرفة الماستر	3.88 × 3.88	15.05
12	أول — غرفة نوم 6	3.76 × 3.88	14.59
13	أول — الممر	11.76 × 1.00	11.76
14	أول — غرفة نوم 4	3.88 × 2.98	11.56
15	أول — حمام 3	1.58 × 2.98	4.71
16	أول — حمام 4	1.58 × 2.98	4.71
17	أول — غرفة ملابس	1.90 × 2.98	5.66
	المساحة الصافية الداخلية		**173.52**
	التراس المسقوف + تراس الدور الأول (مجاناً)	**1.76 × 1.44 × 2**	**7.89**
	المساحة الإجمالية المبنية	**12.00 × 8.34 × 2 دور**	**200.16**

التسعير

عرض اليوم الوطني 96


البند	القيمة
المساحة المبنية (م2)	200.16
سعر المتر المربع — عرض اليوم الوطني 96	1,096 ريال
الإجمالي	**219,375 ريال**

ملاحظات:


- السعر للمساحة المبنية 200 م² (دورين) — الشباك البارز والبلكونة وعتبة المدخل مجاناً.
- الصبة والتمديدات الخارجية على العميل ما لم يُذكر غير ذلك.

لقطات المنظور الخارجي


المنظور الأمامي

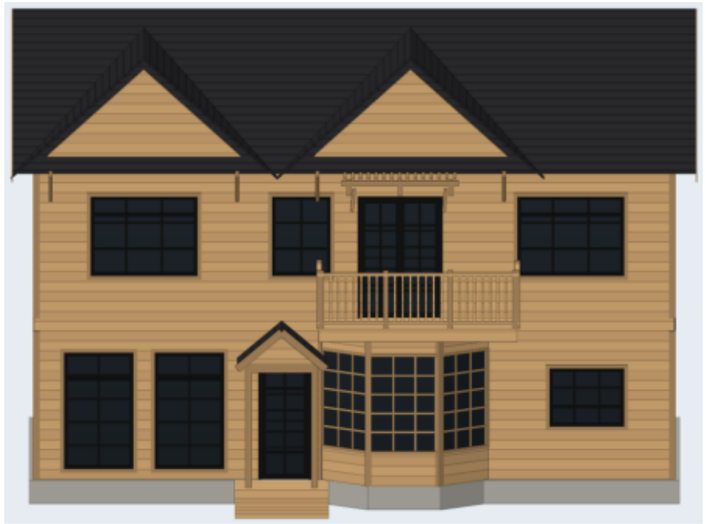


منظور أمامي من اليسار

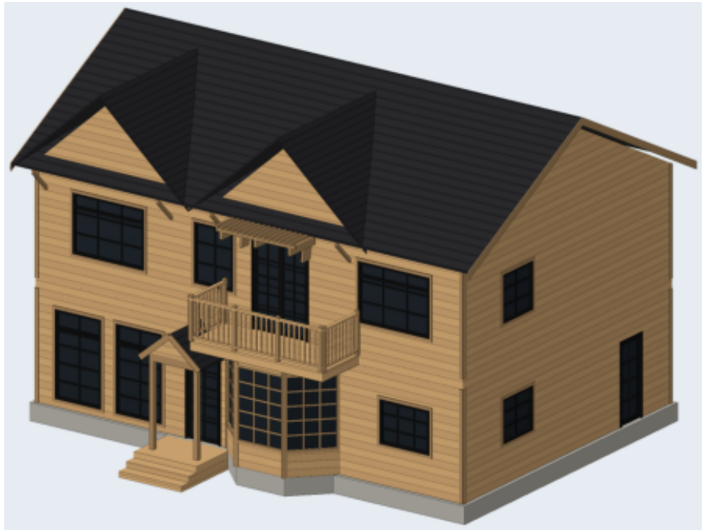


منظور أمامي من اليمين

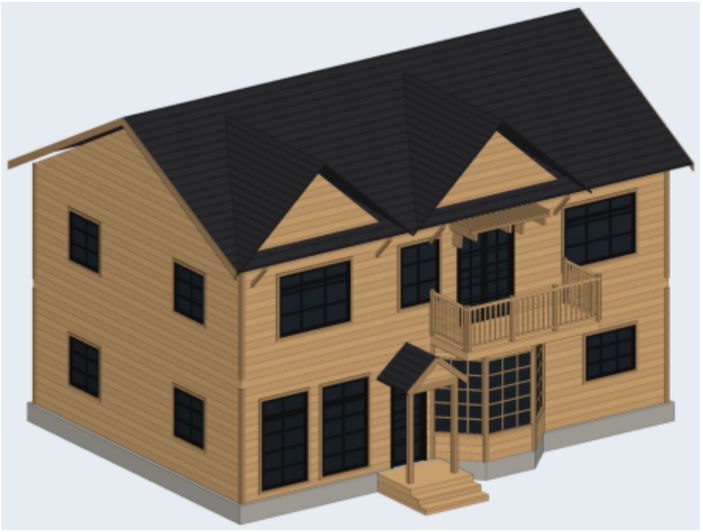


المنظور الخلفي

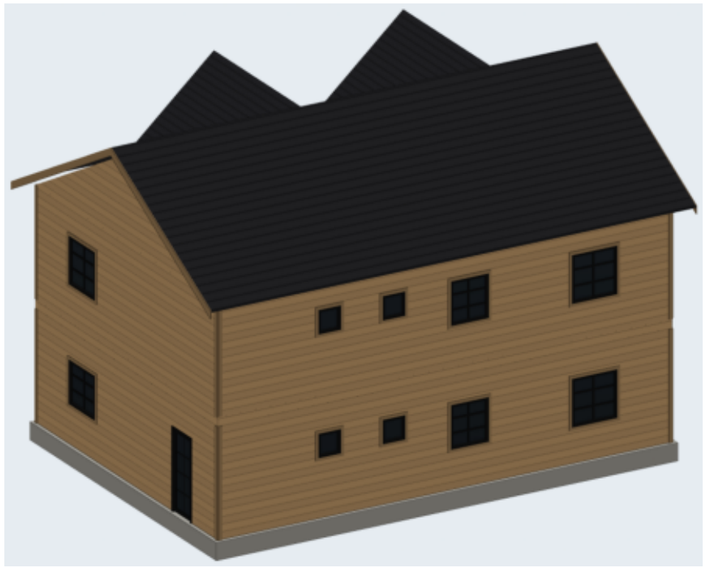

منظور خلفي من اليمين

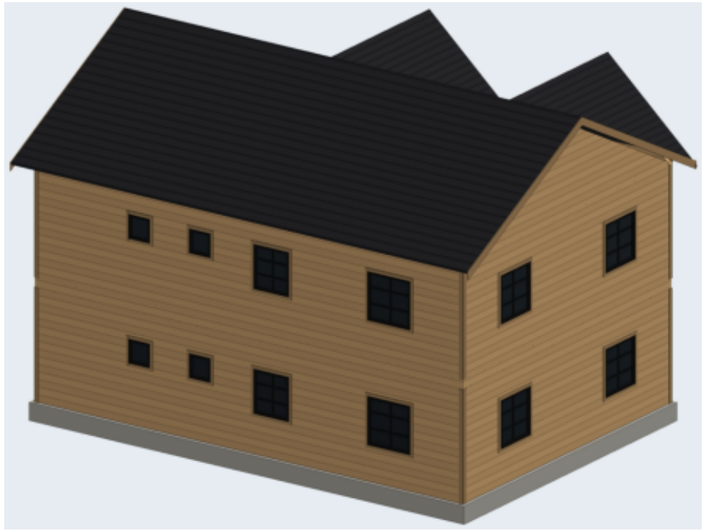

منظر علوي

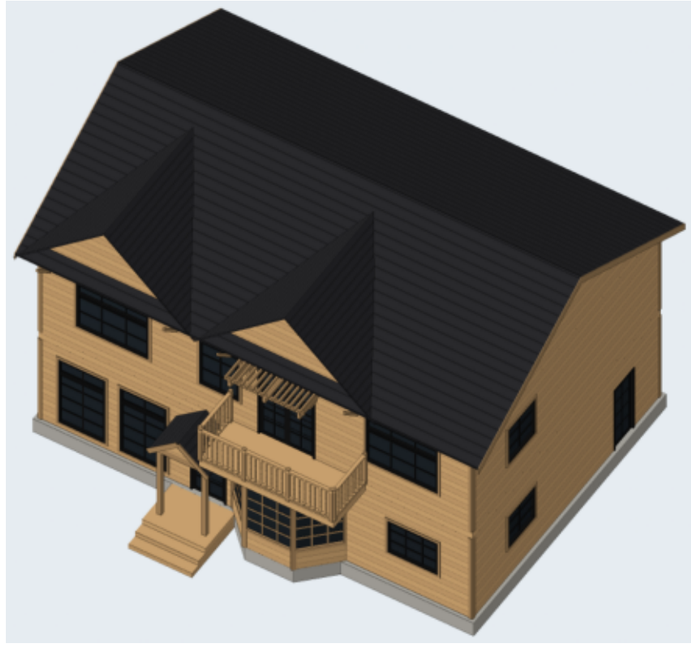


المشروع / العميل	عنوان اللوحة	المقياس	التاريخ	رقم اللوحة
كوخ دورين 6 غرف — 200 م² **عميل — ذهبان**	**لقطات المنظور**	**—**	**2026-10-11**	**A-08 (8/11)**

مصنع وتد الأخشاب
Watad Wood Factory

المقطع العلوي بالفرش — الدور الأرضي

مقطع أفقي على ارتفاع 1.90 م — توزيع الفرش ومسار الحركة

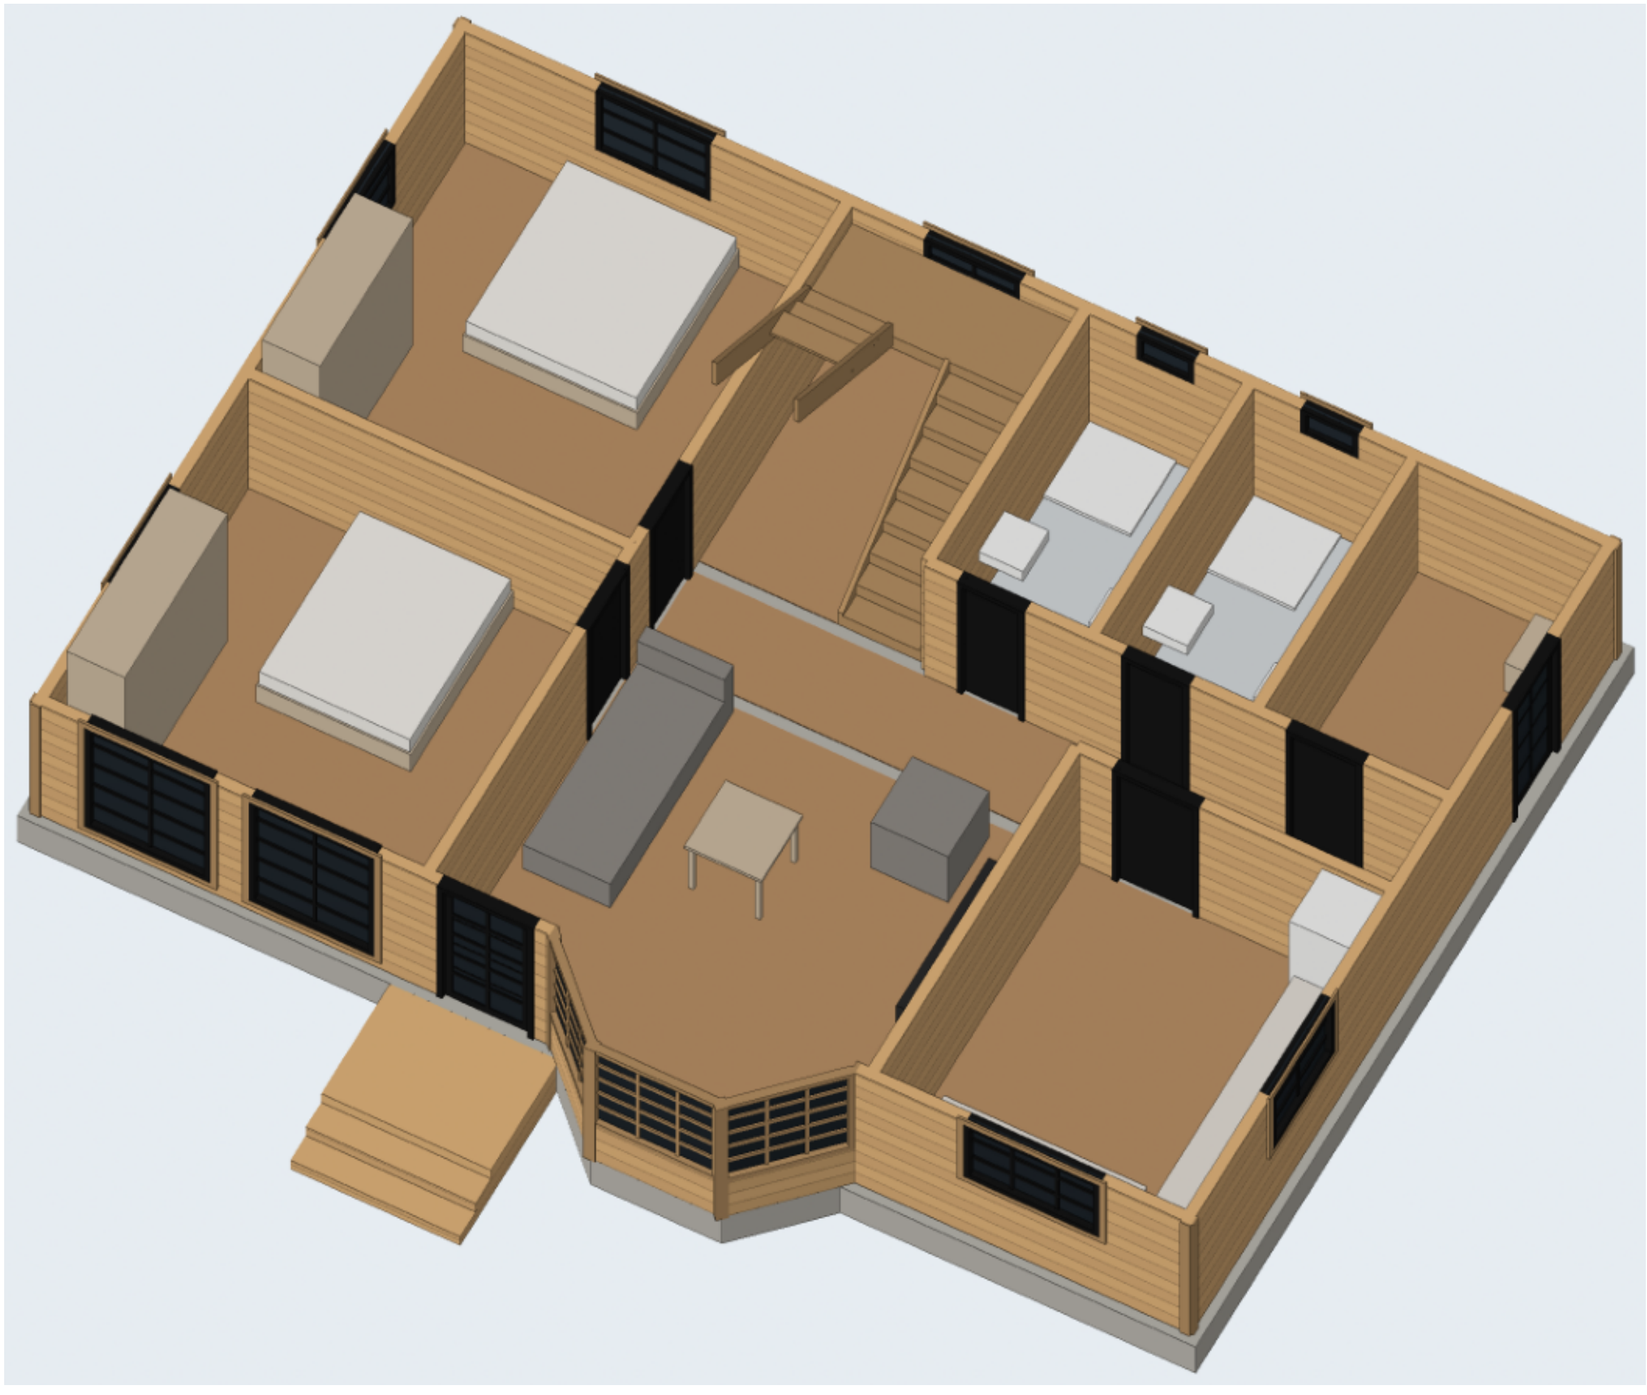


المشروع / العميل	عنوان اللوحة	المقياس	التاريخ	رقم اللوحة
كوخ دورين 6 غرف — 200 م² **عميل — ذهبان**	**المقطع العلوي بالفرش — الدور الأرضي**	**—**	**2026-10-11**	**A-09 (9/11)**

مصنع وتد الأخشاب
Watad Wood Factory

المقطع العلوي بالفرش — الدور الأول

مقطع أفقي على ارتفاع 1.90 م — توزيع الفرش ومسار الحركة

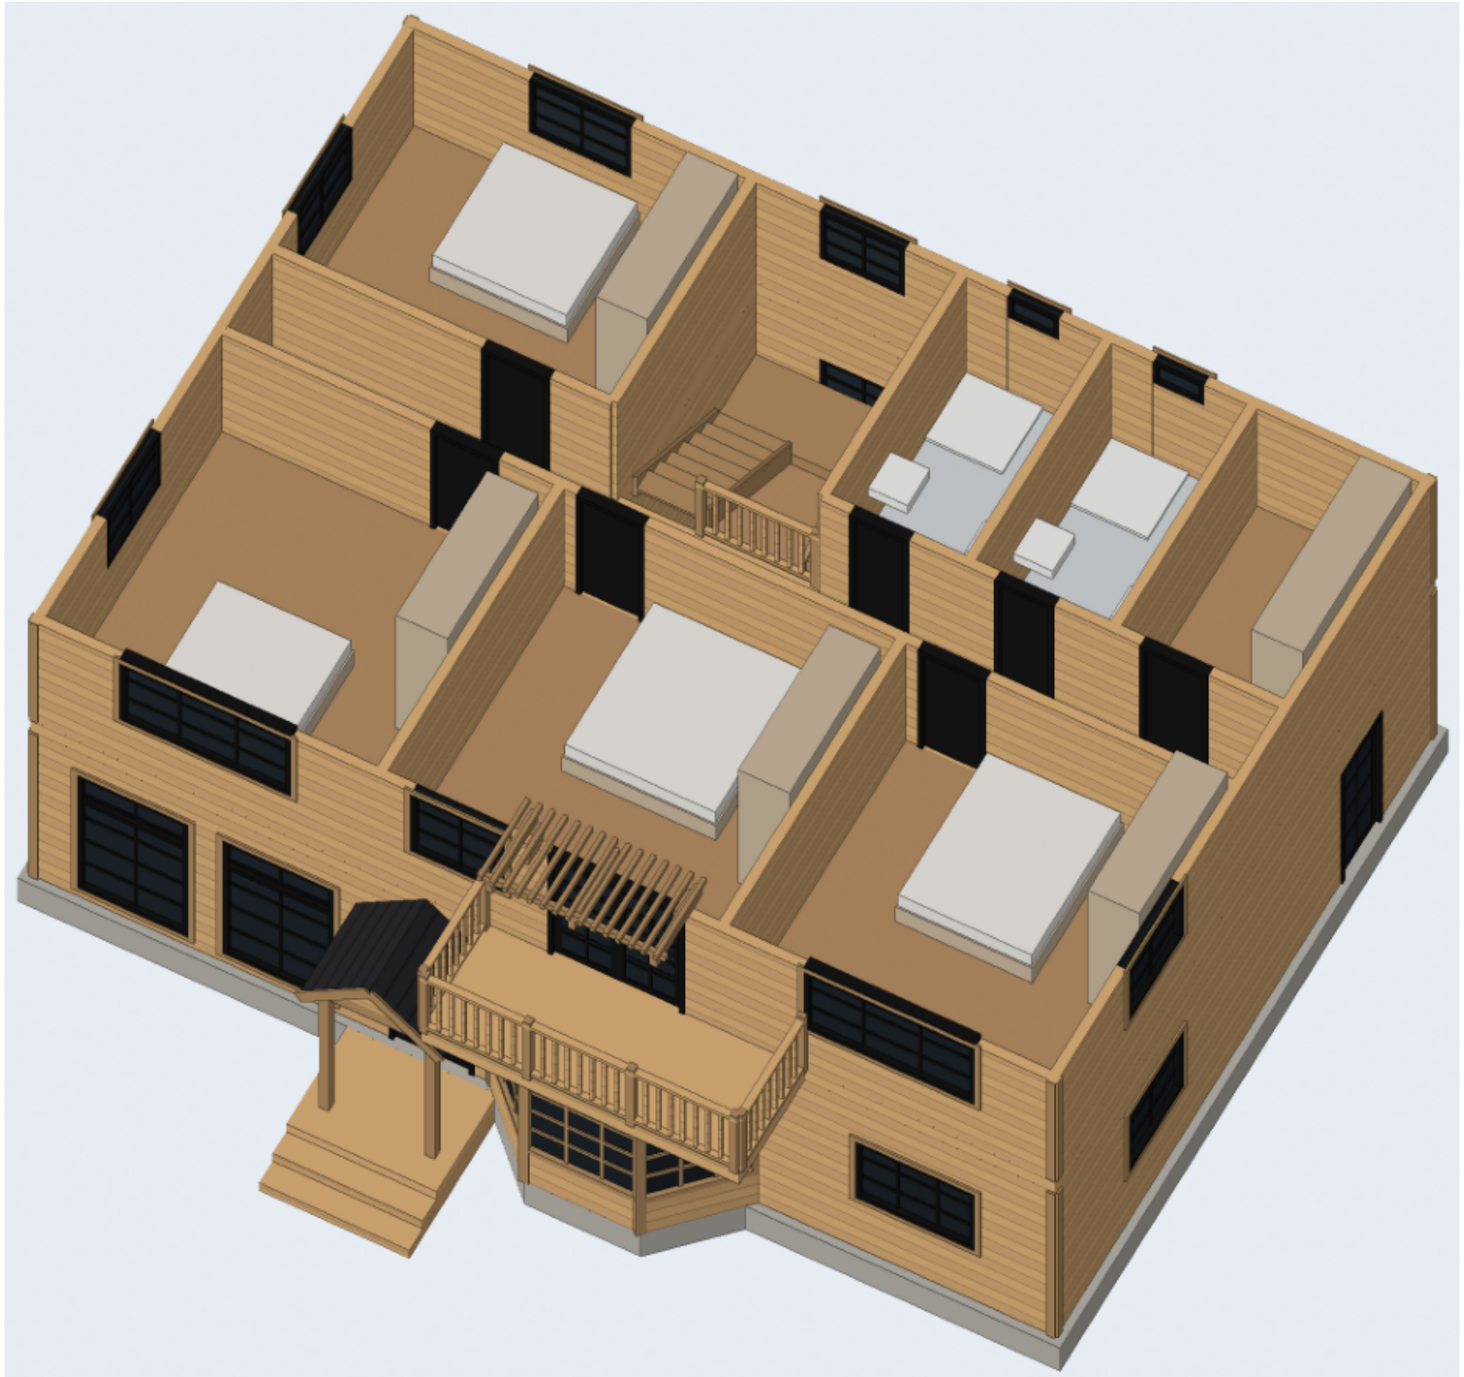

المشروع / العميل	عنوان اللوحة	المقياس	التاريخ	رقم اللوحة
كوخ دورين 6 غرف — 200 م² **عميل — ذهبان**	**المقطع العلوي بالفرش — الدور الأول**	**—**	**2026-10-11**	**A-10 (10/11)**

مصنع وتد الأخشاب
Watad Wood Factory

المنظور ثلاثي الأبعاد والمواد

النمط: جوزي غامق + إطارات سوداء — رندر واقعي بخامات حقيقية



جدول المواد والألوان

الخشب / الصبغة

خشب طبيعي فاتح (بدون صبغة)

القرميد

قرميد رمادي غامق

الزجاج

زجاج عاكس غامق

إطارات الشبابيك والأبواب

إطار ألمنيوم أسود

الكنار والزوايا

نفس الصبغة أغمق درجة


الصبة

خرسانة 45 سم


الدربزين: ألواح أفقية متقاربة (عصري)

تقسيم الشبابيك: بدون | الباب الرئيسي: زجاج بتقسيمات (فرنسي)

أنواع الدربزين المعتمدة (من مشاريع المصنع)

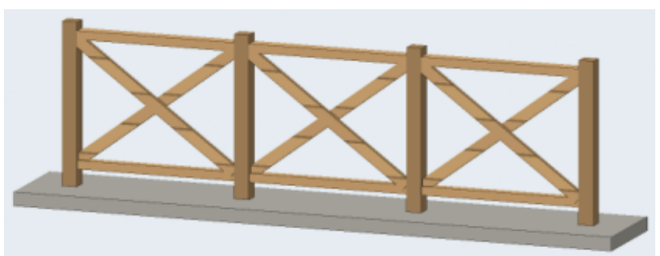

تقاطع X (صورة 5)

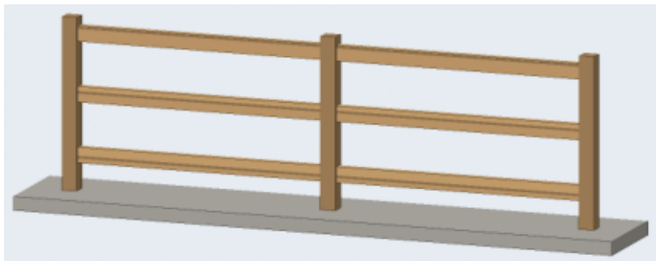

3 مرابيع أفقية (صورة 2)



قوائم رأسية متقاربة (صورة 1)

المشروع / العميل	عنوان اللوحة	المقياس	التاريخ	رقم اللوحة
كوخ دورين 6 غرف — 200 م² **عميل — ذهبان**	**المنظور والمواد**	**—**	**2026-10-11**	**A-11 (11/11)**

مصنع وتد الأخشاب
Watad Wood Factory