
# الموقع العام وتنسيق الحديقة (لاندسكيب)

الأرض 10 × 30 م = 300 م² | الأبعاد بالسنتيمتر

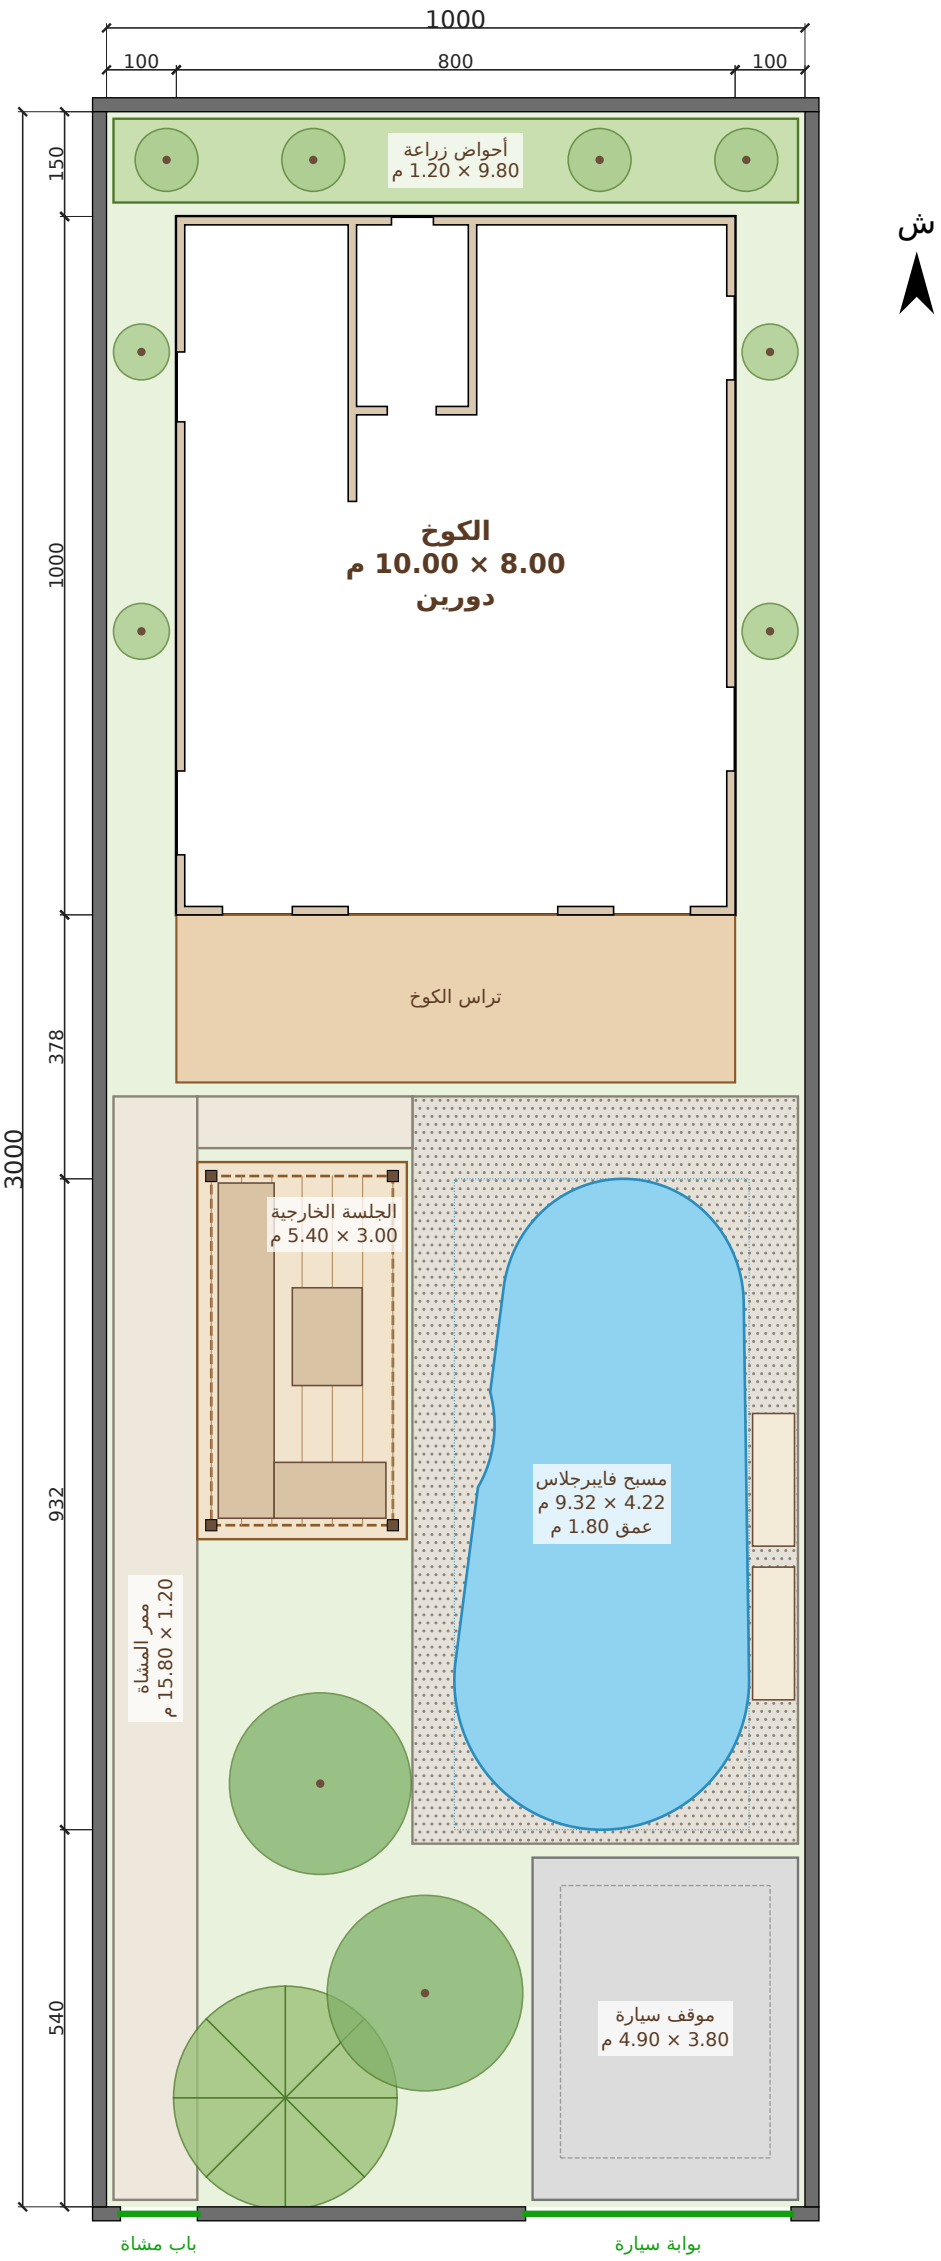


شارع عرض 16 م

## جدول مساحات الموقع

| البند | المقاس | المساحة (م²) |
|---|---|---|
| مساحة الأرض | 10.00 × 30.00 م | 300.0 |
| مسطح الكوخ (البصمة) | 8.00 × 10.00 م | 80.0 |
| تراس الكوخ | 2.40 × 8.00 م | 19.2 |
| مسبح | 4.22 × 9.32 م | 39.3 |
| جلسة خارجية | 3.00 × 5.40 م | 16.2 |
| بلاط | | 19.7 |
| موقف سيارة | 3.80 × 4.90 م | 18.6 |
| ممر | | 21.2 |
| أحواض زراعة | 9.80 × 1.20 م | 11.8 |
| المسطحات الخضراء (حديقة) | الباقي | 73.9 |


- الكوخ في آخر الأرض بعيد عن الشارع (خصوصية)، والصالة والبلكونة يطلّون على المسبح والحديقة.
- بوابة سيارة 3.80 م + باب مشاة مستقل، سور بلك 2.50 م بغطاء خشب أعلى السور.
- ممر المشاة من الباب للتراس بمحاذاة السور الغربي، والموقف عند البوابة بدون ما يقطع الحديقة.
- مسبح فايبرجلاس جاهز بشكل حر 9.32 × 4.22 م بعمق 1.20–1.80 م، حوله بلاط وإطار رخام، وكراسي استلقاء على الجهة الشرقية.
- جلسة خارجية تحت برجولة خشب بين المسبح والسور، وظل أشجار من جهة الشارع.
- بلكونة بطول الواجهة على الدور الأول، أعمدة خشب من الأرض للسقف، والسقف ممتد 2 م يغطيها.

| المشروع / العميل | عنوان اللوحة | المقياس | التاريخ | رقم اللوحة |
|---|---|---|---|---|
| **كوخ دورين + تنسيق حديقة ومسبح — جدة**<br>**عميل جديد — جدة** | **الموقع العام واللاندسكيب** | **1:200** | **2026-10-18** | **A-01 (1/15)** |

**مصنع وتد الأخشاب**
Watad Wood Factory

# المسقط الأفقي مع الفرش — الدور الأرضي


الأبعاد بالسنتيمتر - الجدران: قوائم 7×5 + تلبيس 2.5 من الجهتين (12 سم) | منسوب الأرضية +0.00

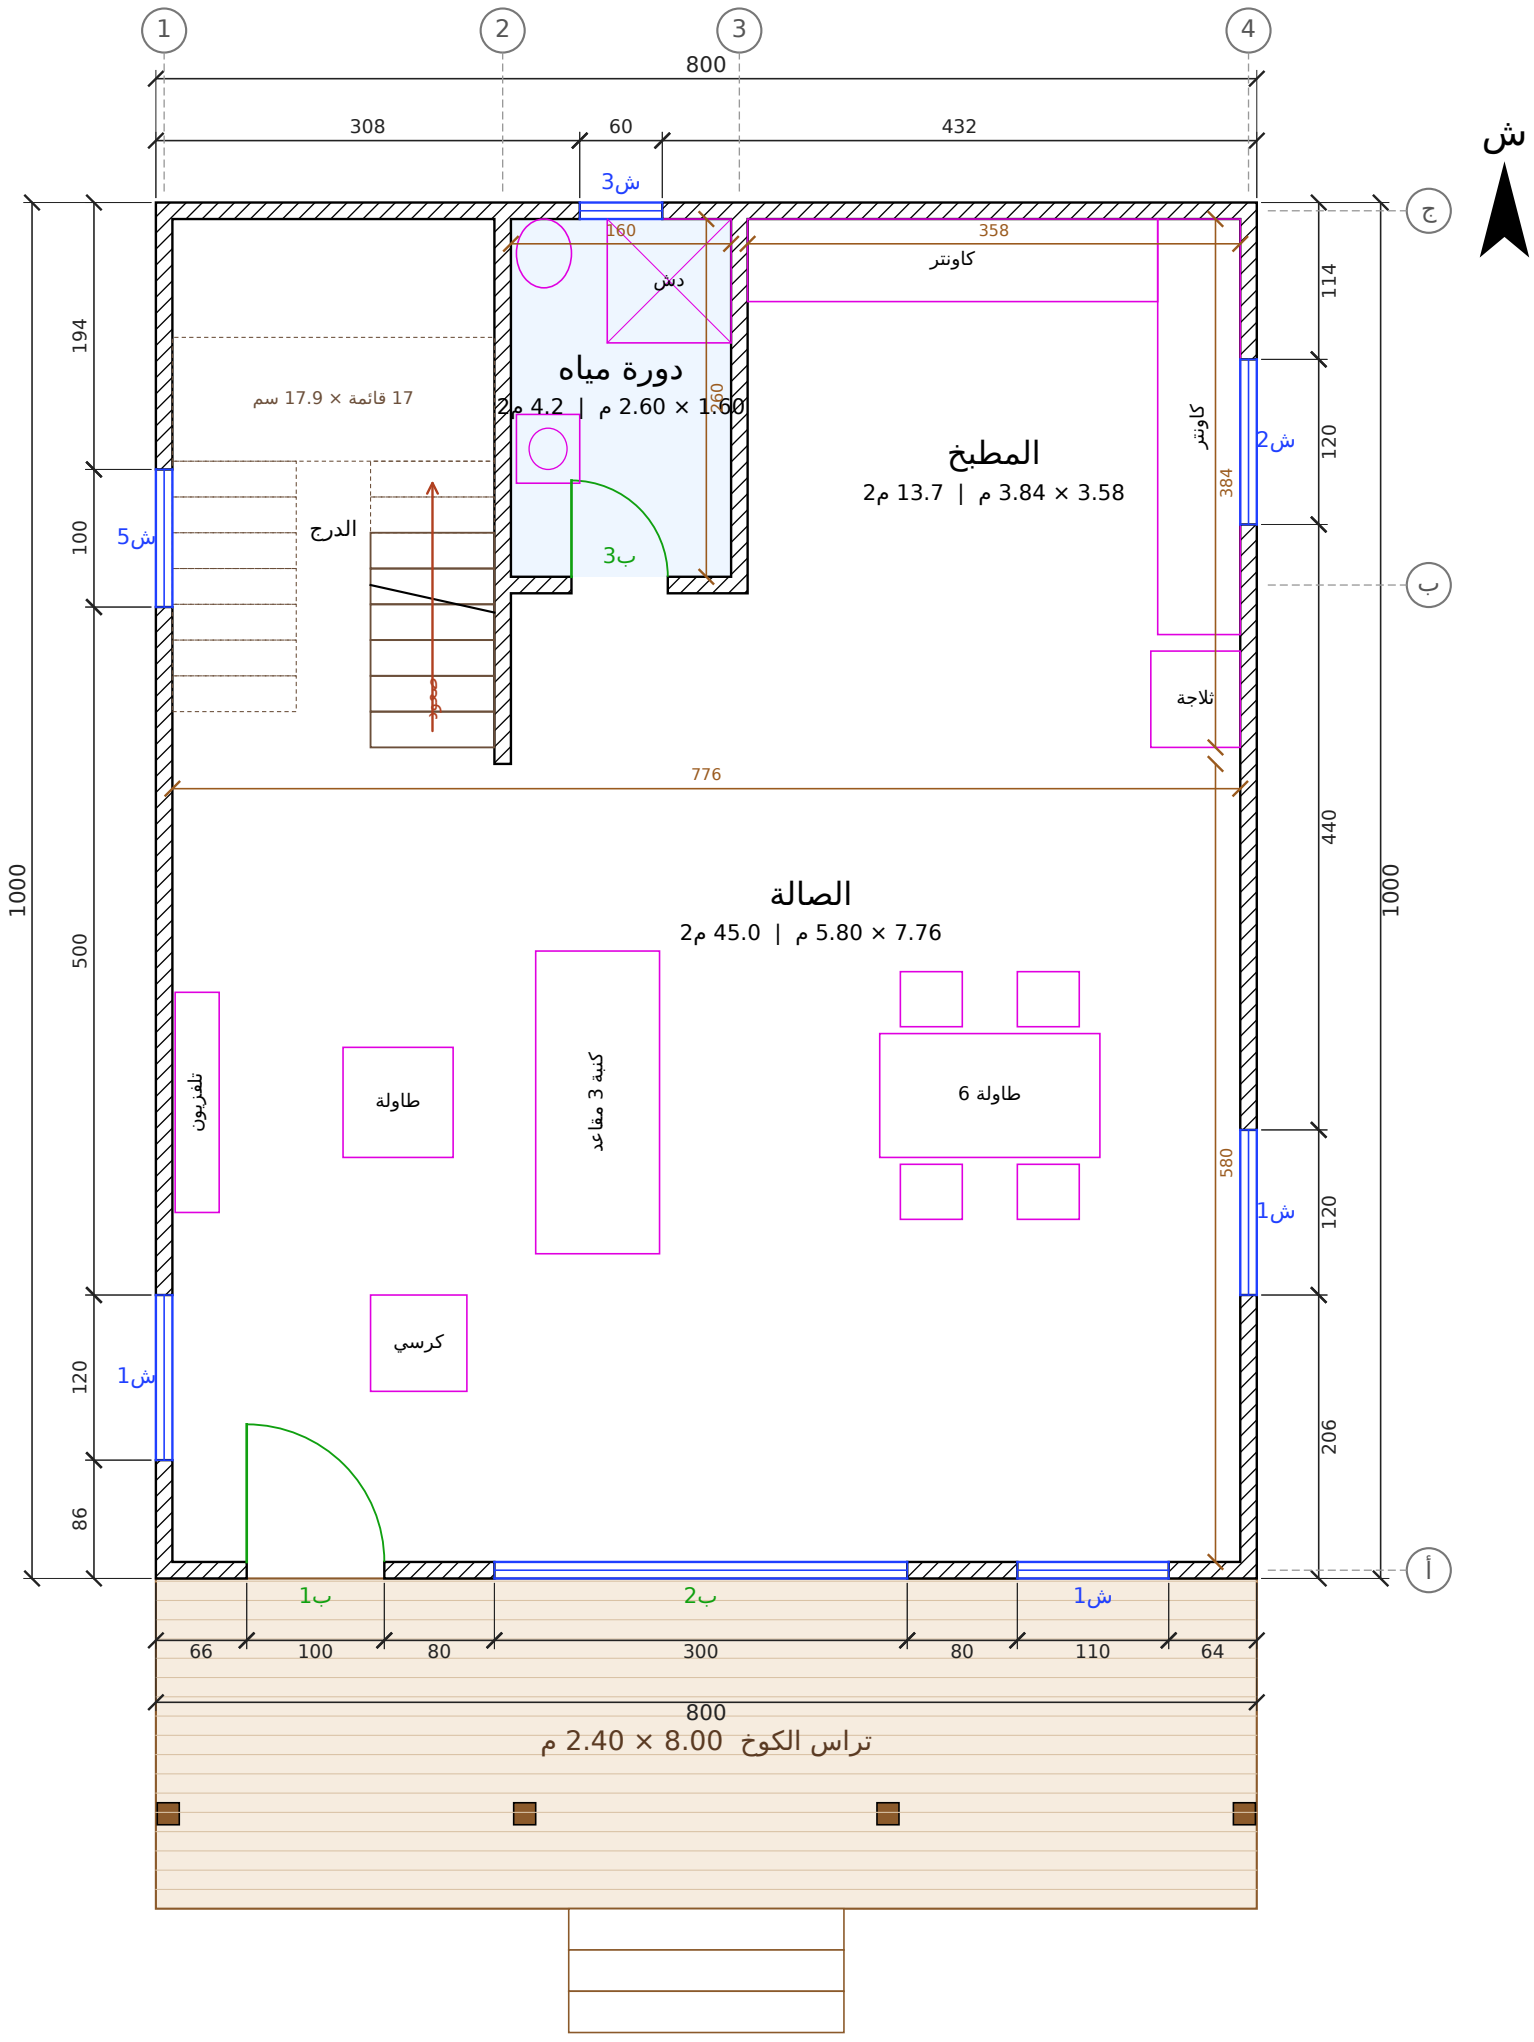



| المشروع / العميل | عنوان اللوحة | المقياس | التاريخ | رقم اللوحة |
|---|---|---|---|---|
| **مصنع وتد الأخشاب** Watad Wood Factory<br>**كوخ دورين + تنسيق حديقة ومسبح — جدة**<br>**عميل جديد — جدة** | **المسقط الأفقي — الدور الأرضي** | **1:50** | **2026-10-18** | **A-02 (2/15)** |

# المسقط الأفقي مع الفرش — الدور الأول

الأبعاد بالسنتيمتر - الجدران: قوائم 7×5 + تلبيس 2.5 من الجهتين (12 سم) | منسوب الأرضية +3.05

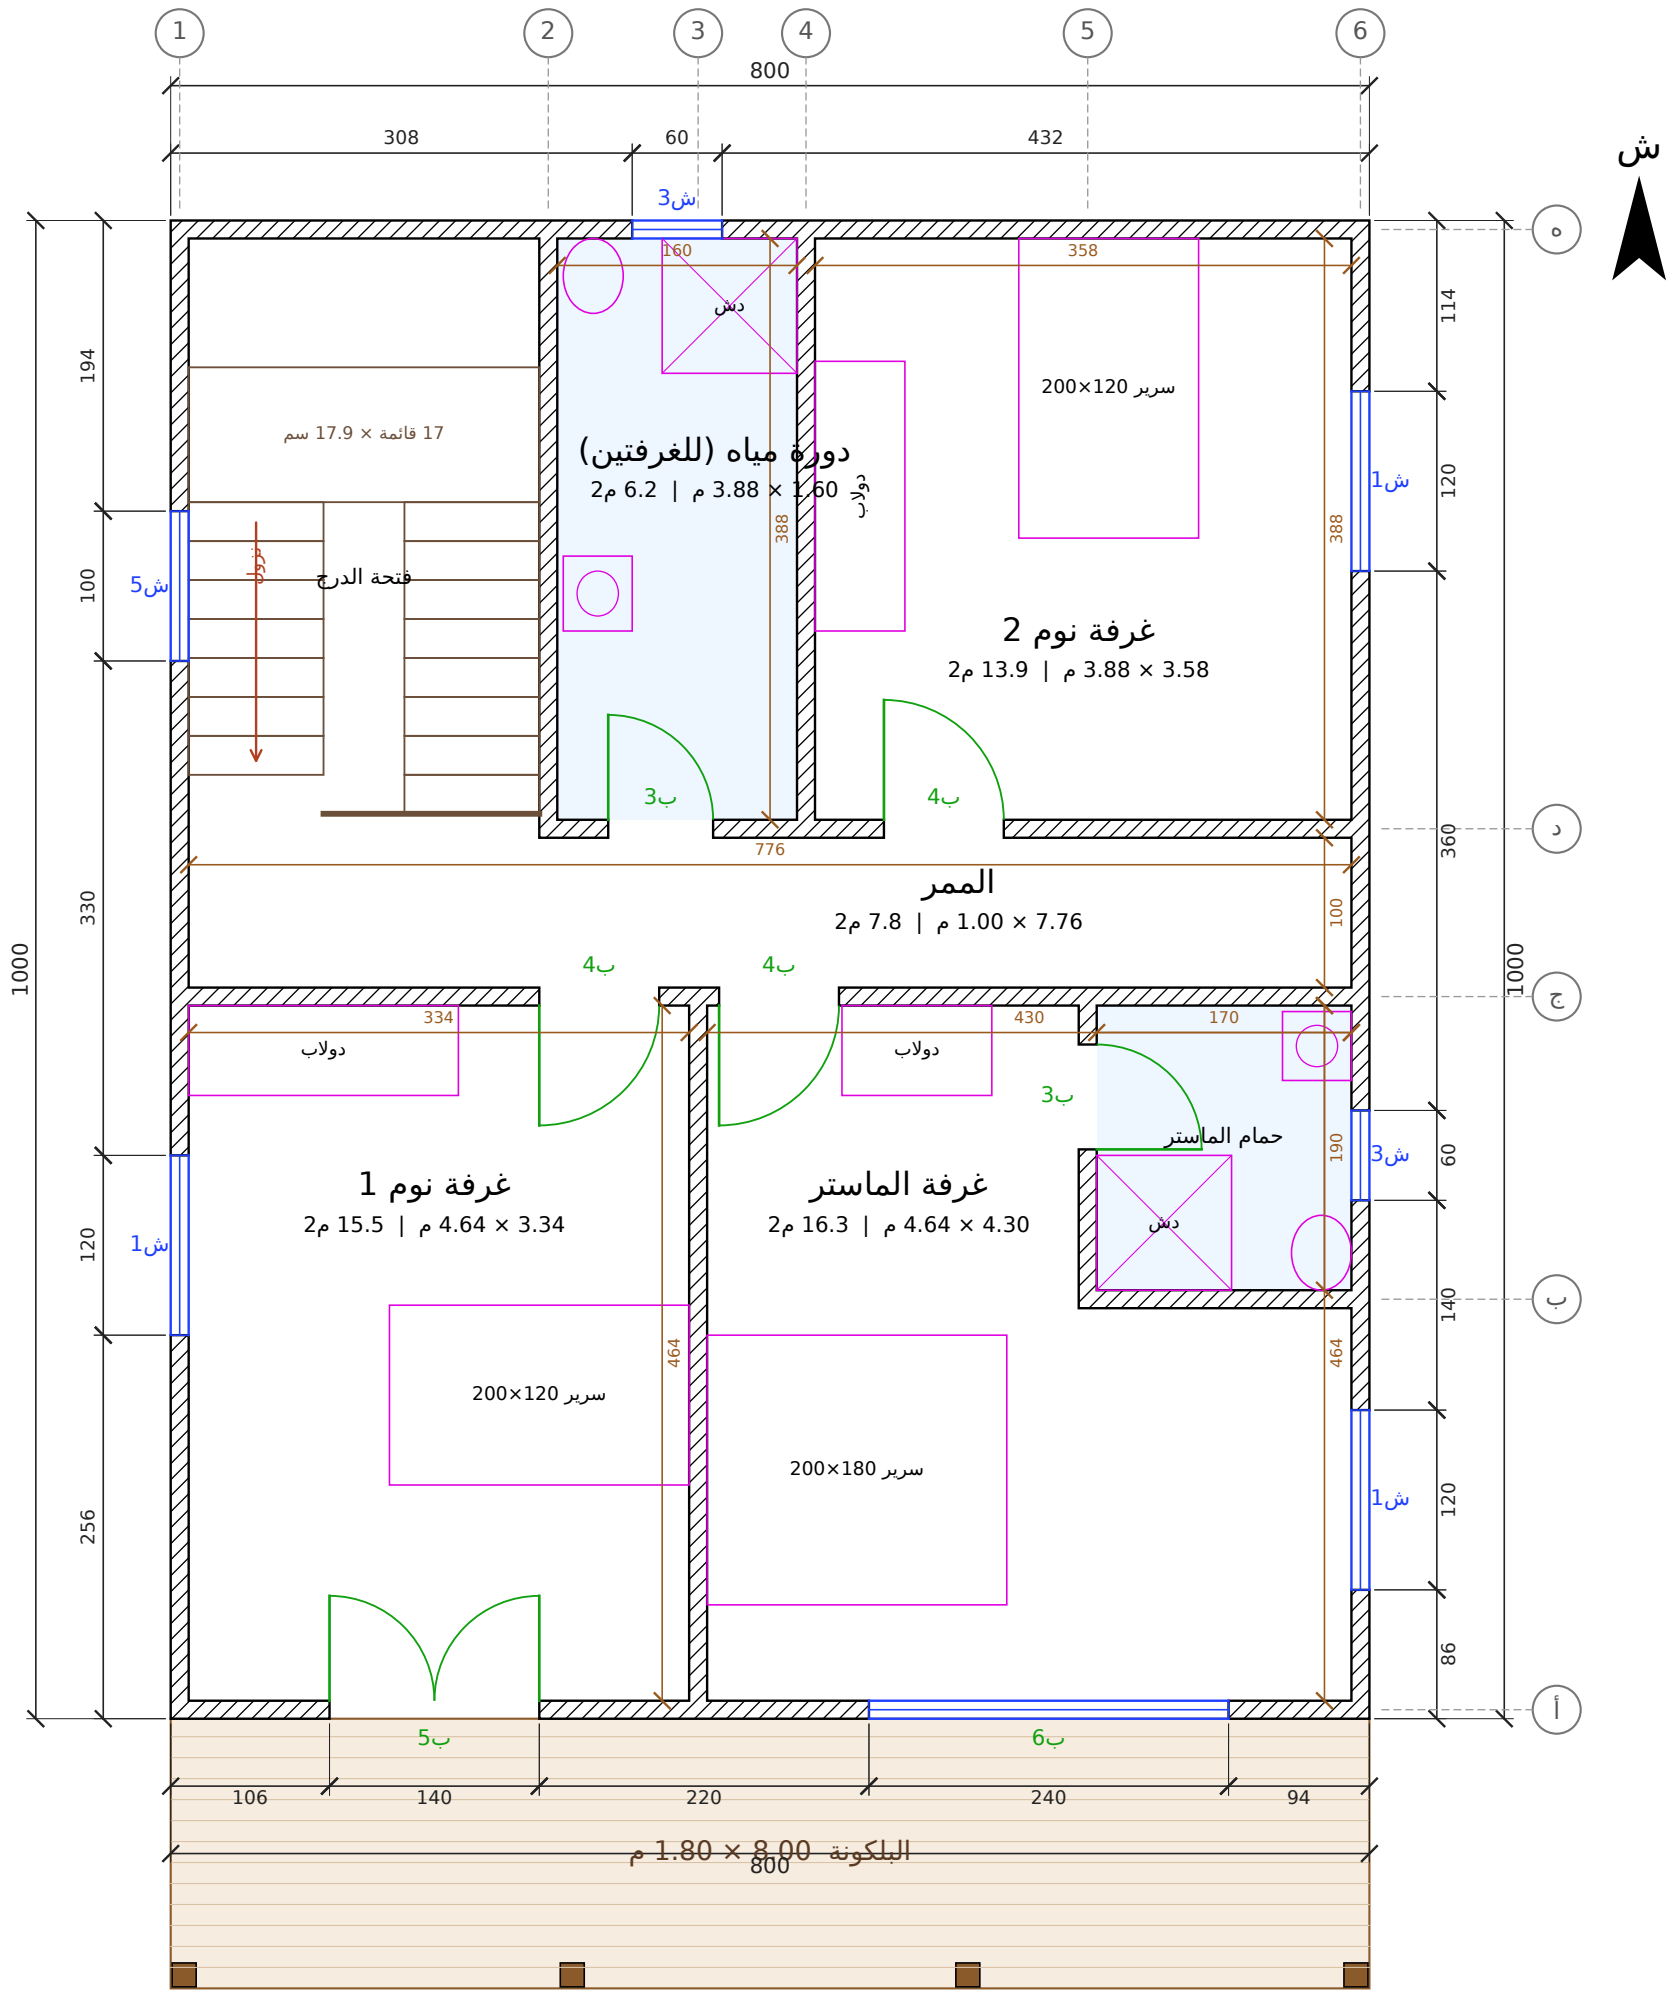



| المشروع / العميل | عنوان اللوحة | المقياس | التاريخ | رقم اللوحة |
|---|---|---|---|---|
| **مصنع وتد الأخشاب** Watad Wood Factory<br>**كوخ دورين + تنسيق حديقة ومسبح — جدة**<br>**عميل جديد — جدة** | **المسقط الأفقي — الدور الأول** | **1:50** | **2026-10-18** | **A-03 (3/15)** |

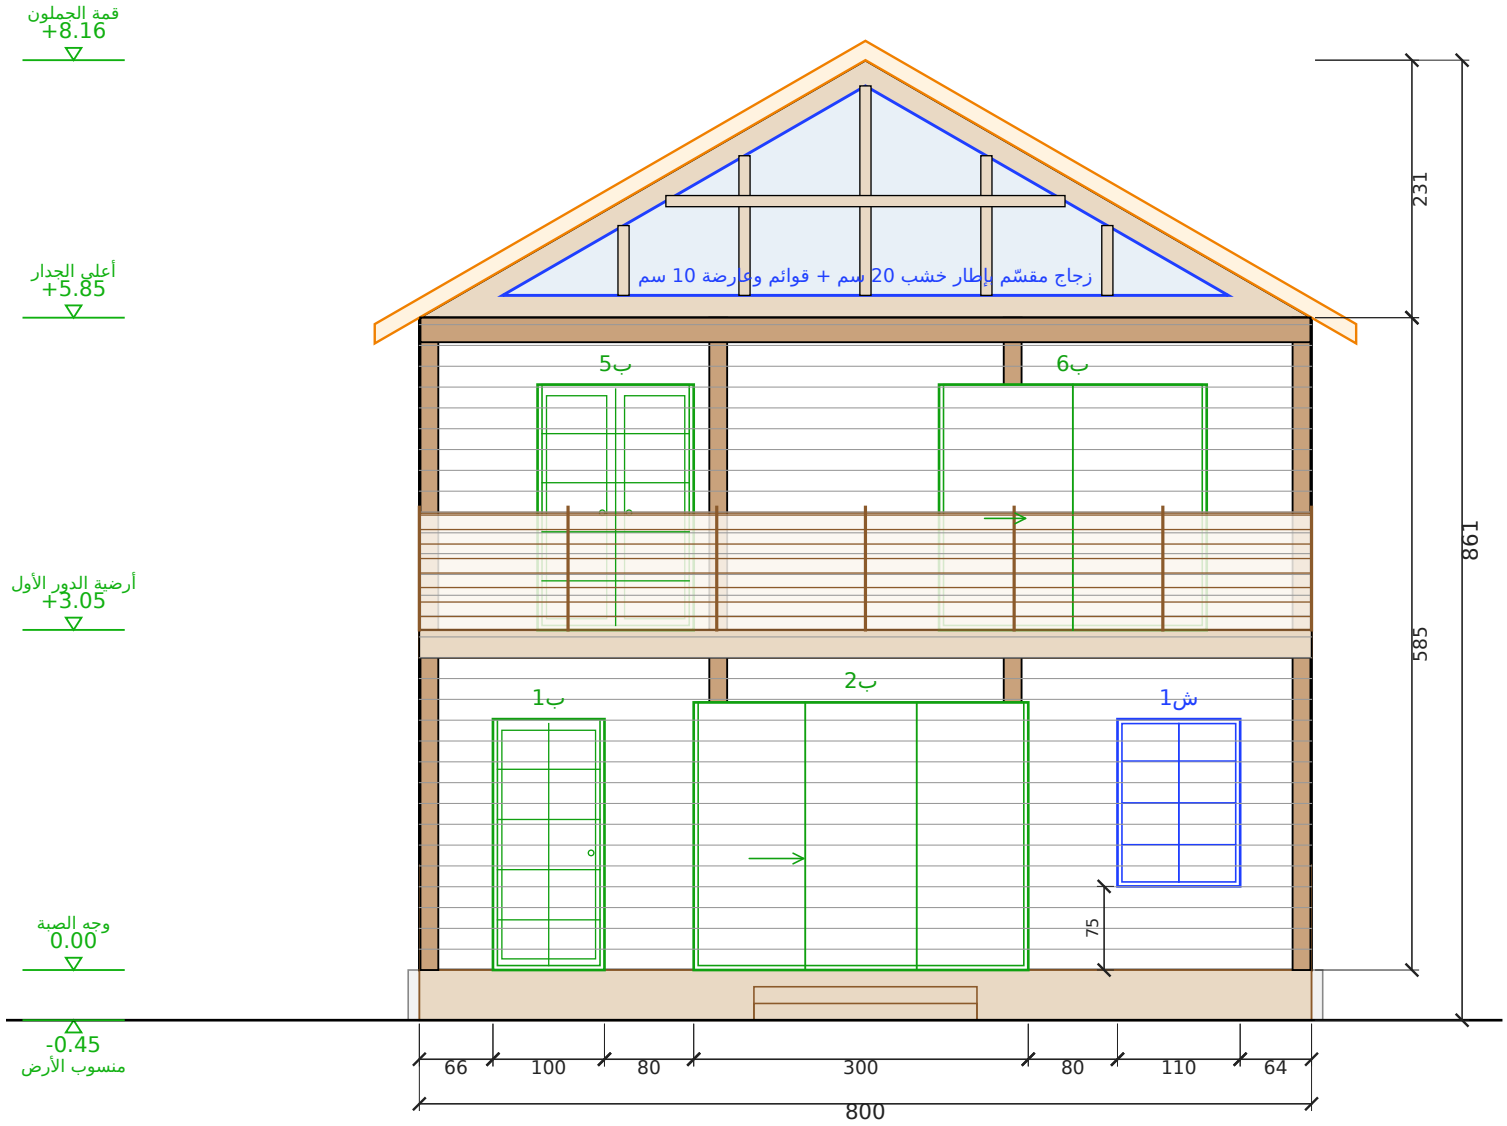


## الواجهة الأمامية (على الحديقة)

مقياس 1:50 | الوحدة: سم

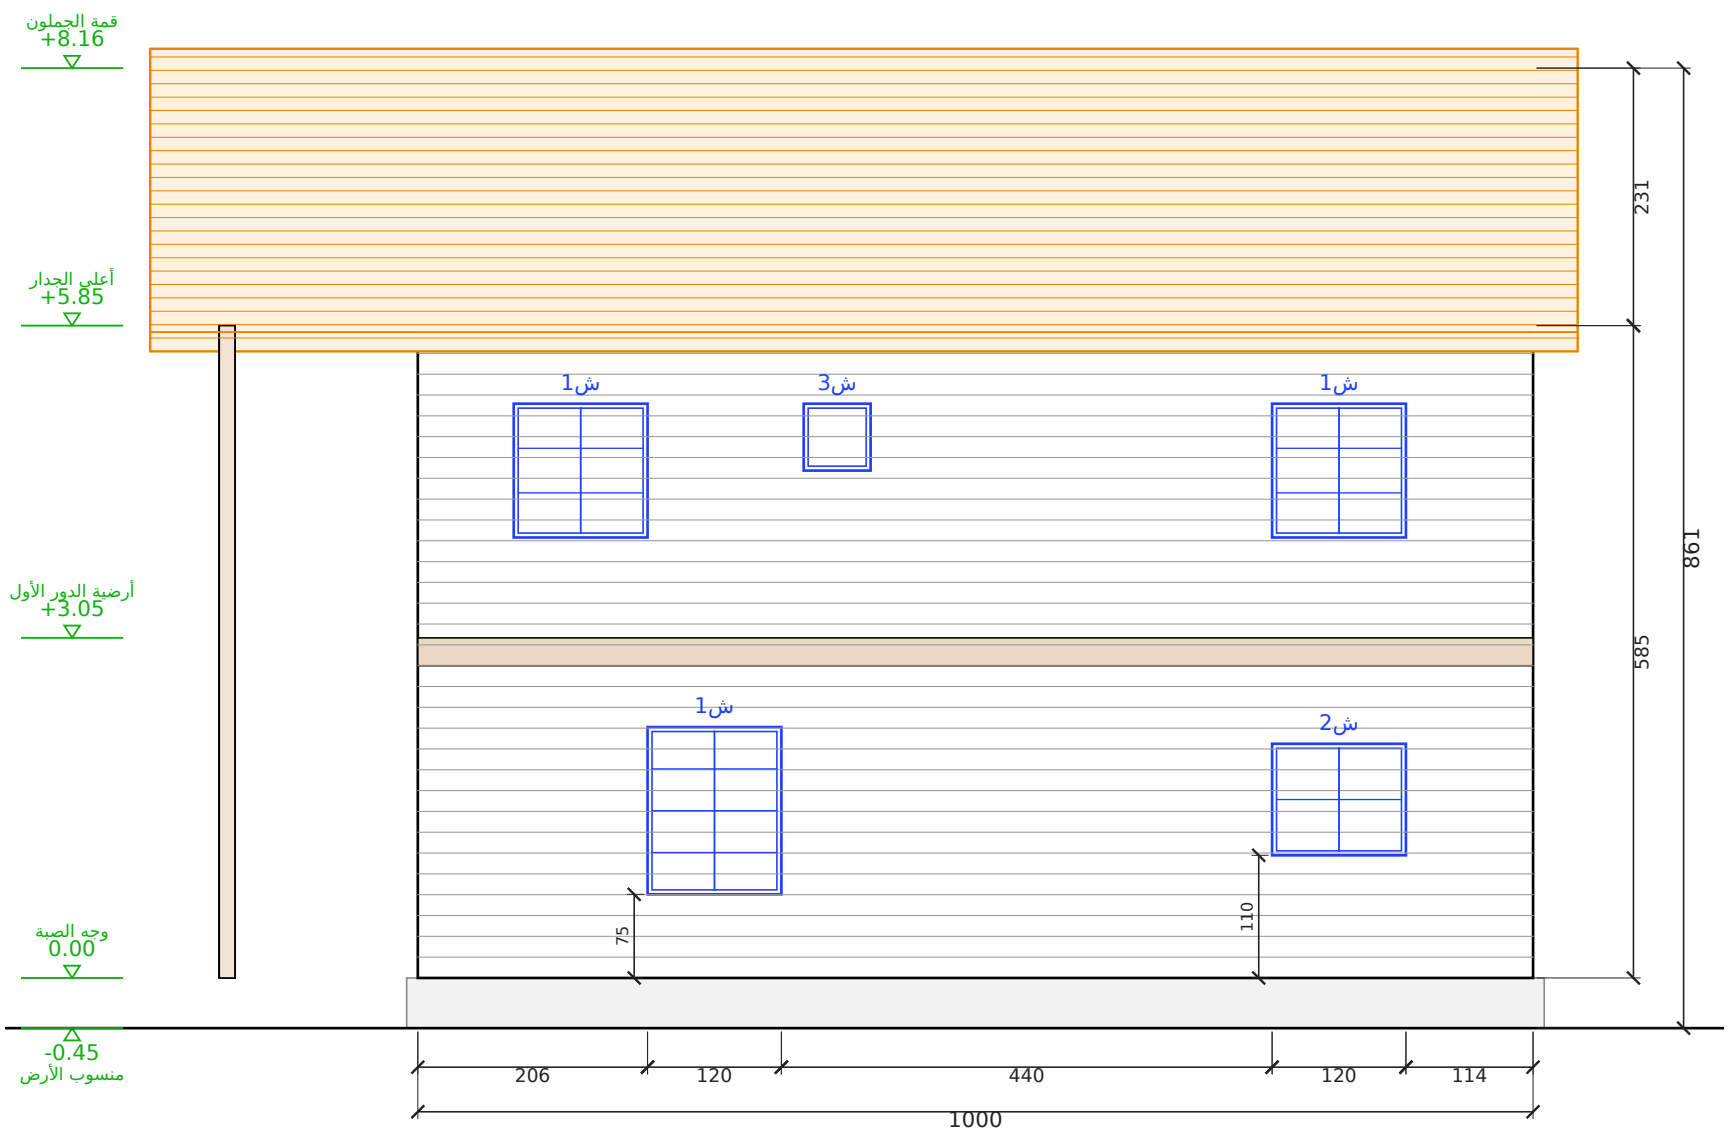



## الواجهة الشرقية

مقياس 1:50 | الوحدة: سم


| المشروع / العميل | عنوان اللوحة | المقياس | التاريخ | رقم اللوحة |
|---|---|---|---|---|
| كوخ دورين + تنسيق حديقة ومسبح — جدة<br>عميل جديد — جدة | الواجهة الأمامية (على الحديقة) والواجهة الشرقية | 1:50 | 2026-10-18 | A-04 (4/15) |

مصنع وتد الأخشاب
Watad Wood Factory

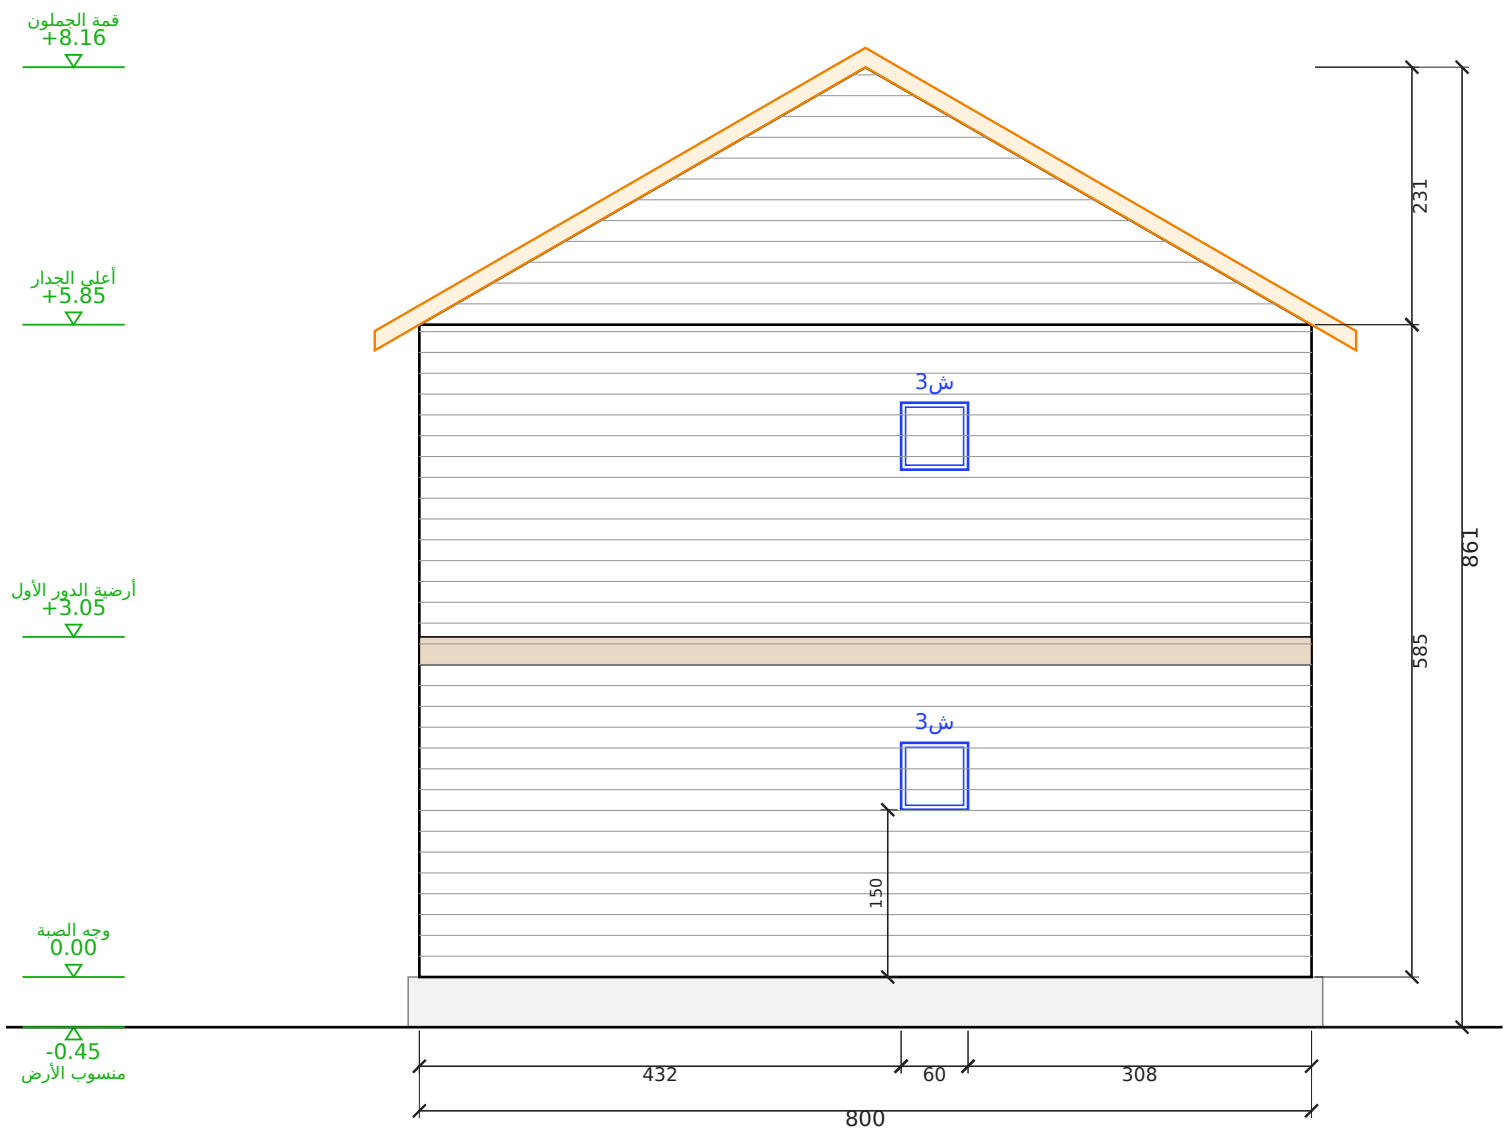


## الواجهة الخلفية

مقياس 1:50 | الوحدة: سم

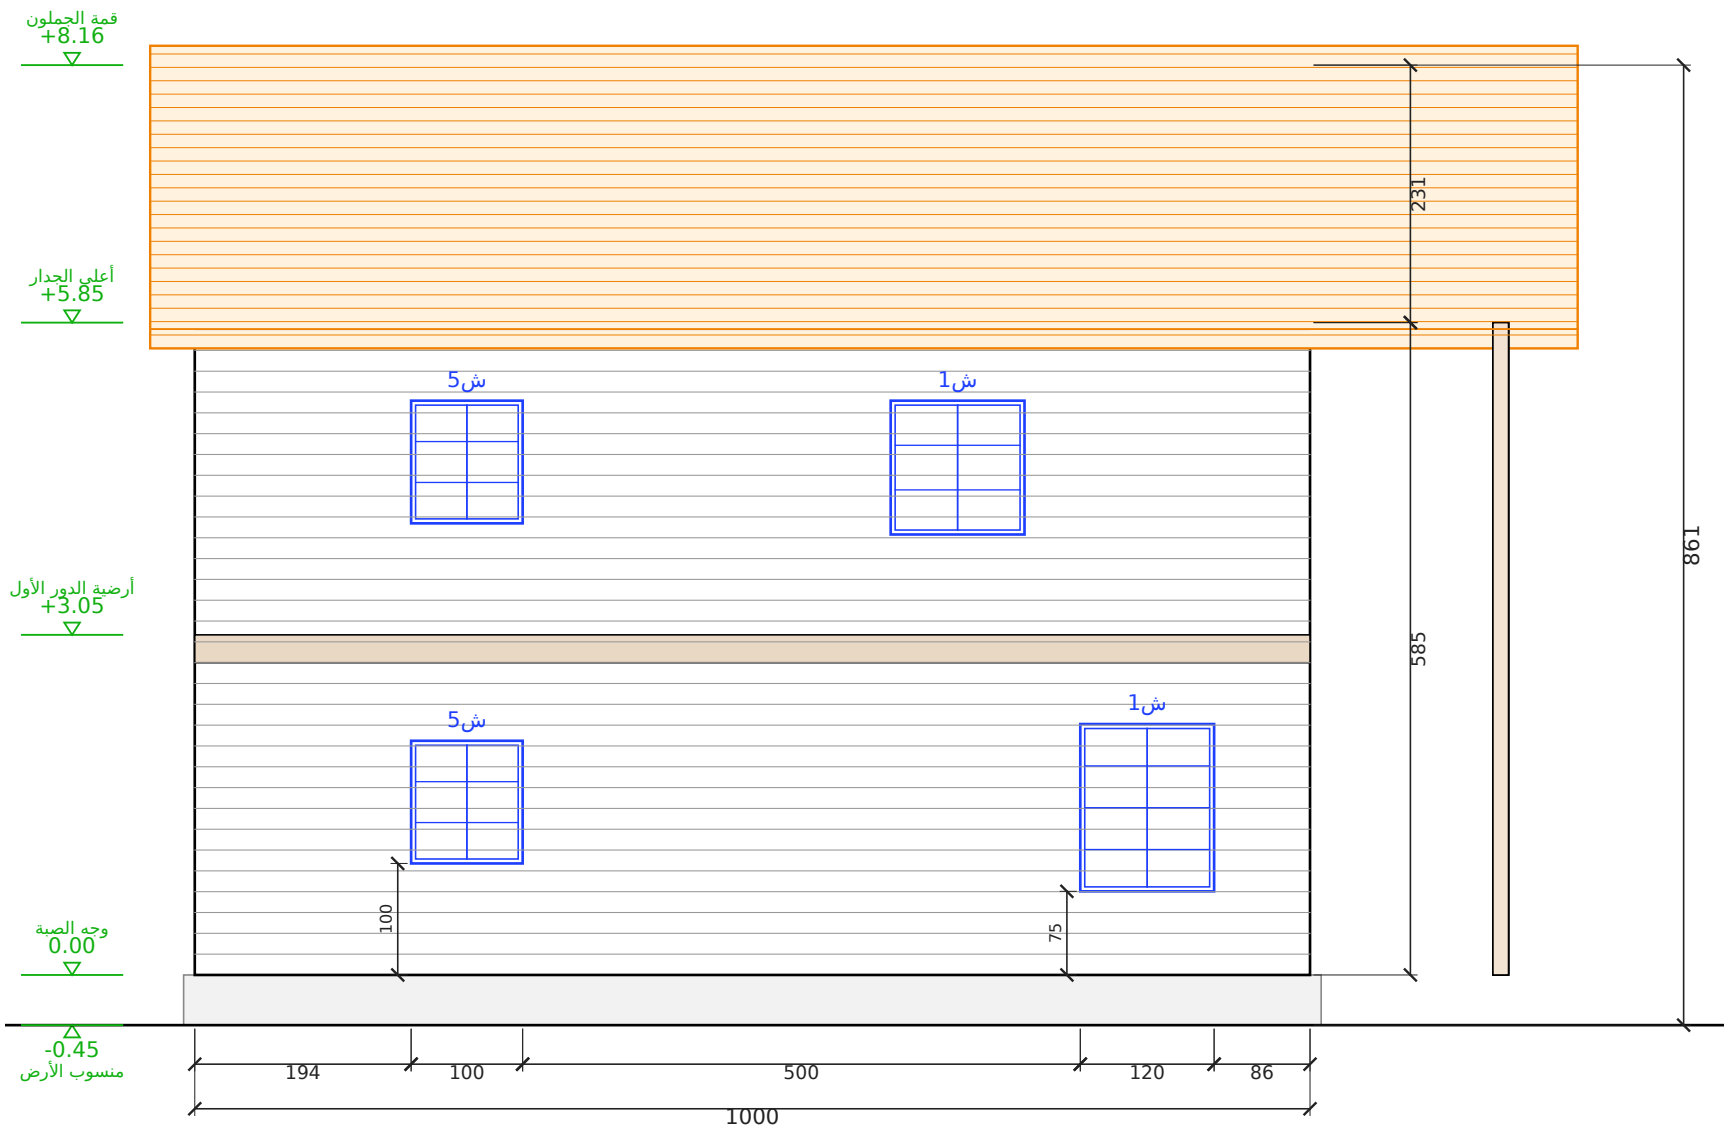



## الواجهة الغربية

مقياس 1:50 | الوحدة: سم


| المشروع / العميل | عنوان اللوحة | المقياس | التاريخ | رقم اللوحة |
|---|---|---|---|---|
| **كوخ دورين + تنسيق حديقة ومسبح — جدة**<br>**عميل جديد — جدة** | **الواجهة الخلفية والواجهة الغربية** | **1:50** | **2026-10-18** | **A-05 (5/15)** |

**مصنع وتد الأخشاب**
Watad Wood Factory


## مسقط السقف (جملون)
رفرف 40 سم من كل جهة | مقياس 1:50

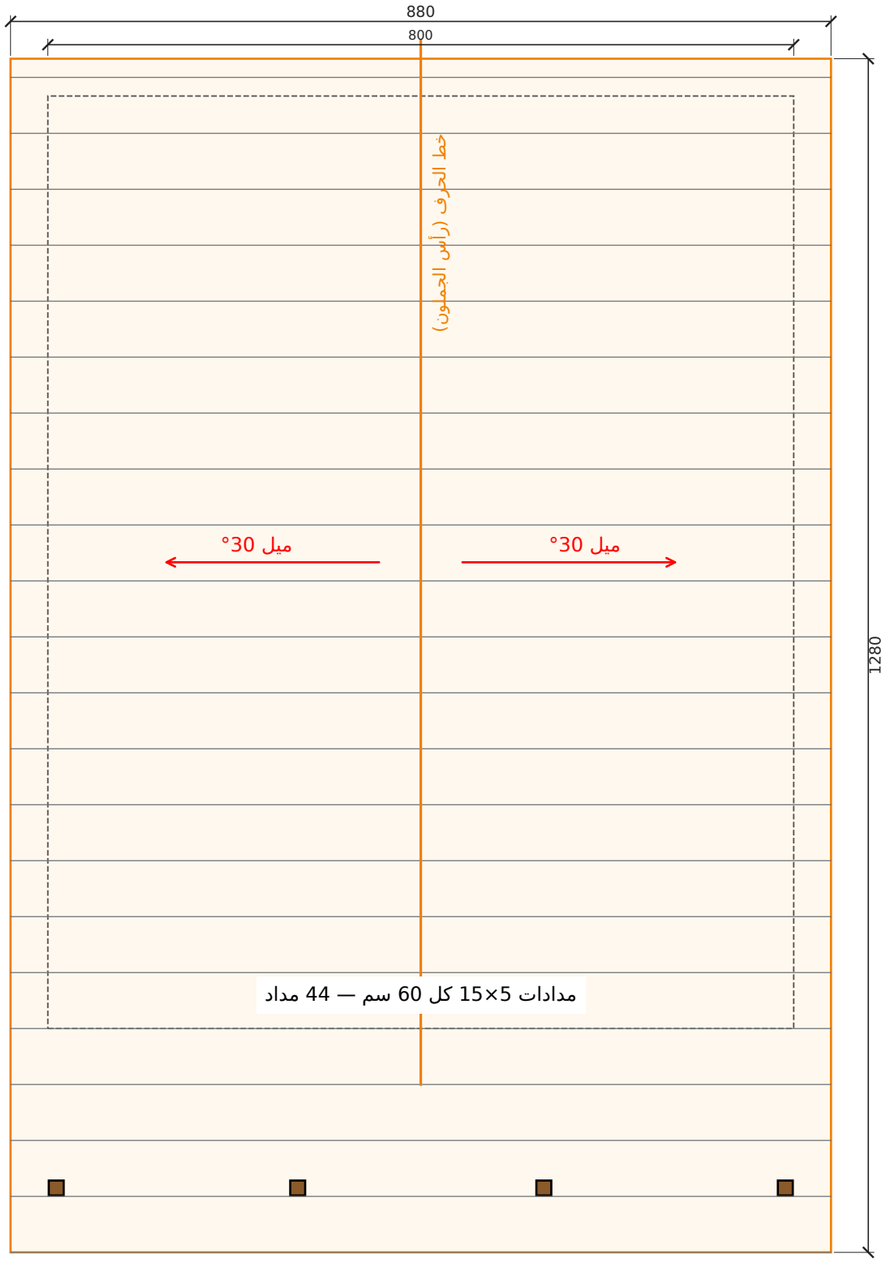


## قطاع عرضي أ-أ
مقياس 1:50 | الوحدة: سم

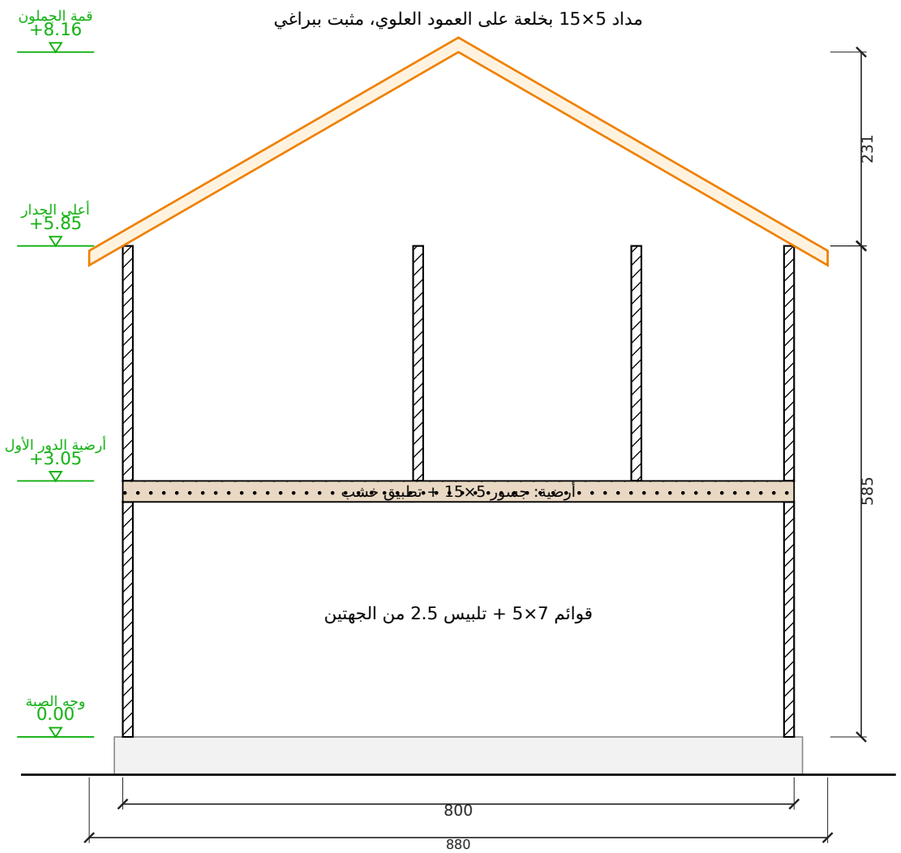


### تفصيلة جلوس المداد على العلوي (1:5)

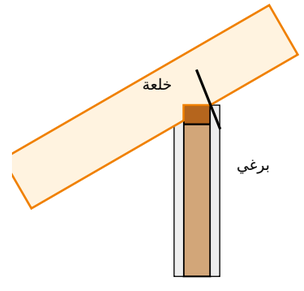


علوي 5×7 على قائم 5×7

| المشروع / العميل | عنوان اللوحة | المقياس | التاريخ | رقم اللوحة |
|---|---|---|---|---|
| كوخ دورين + تنسيق حديقة ومسبح — جدة<br>عميل جديد — جدة | مسقط السقف والقطاع | 1:50 | 2026-10-18 | A-06 (6/15) |

مصنع وتد الأخشاب
Watad Wood Factory

## جدول مقاسات الأبواب والشبابيك
## مقاس الفتحة الصافي في الجدار - الوحدة: سم

| الرمز | النوع | العرض (سم) | الارتفاع (سم) | ارتفاع الجلسة (سم) | العدد | الموقع |
|---|---|---|---|---|---|---|
| ب1 | باب | 100 | 225 | - | 1 | الأمامية (على الحديقة) |
| ب2 | باب | 300 | 240 | - | 1 | الأمامية (على الحديقة) |
| ب3 | باب | 70 | 210 | - | 3 | دورة المياه 2 - حمام الماستر |
| ب4 | باب | 80 | 210 | - | 3 | غرفة 1 - الماستر - غرفة 2 |
| ب5 | باب مزدوج | 140 | 220 | - | 1 | الأمامية (على الحديقة) |
| ب6 | باب مزدوج | 240 | 220 | - | 1 | الأمامية (على الحديقة) |
| ش1 | شباك | 110 | 150 | 75 | 1 | الأمامية (على الحديقة) |
| ش1 | شباك | 120 | 150 | 75 | 2 | الشرقية - الغربية |
| ش1 | شباك | 120 | 120 | 90 | 3 | الشرقية 2 - الغربية |
| ش2 | شباك | 120 | 100 | 110 | 1 | الشرقية |
| ش3 | شباك | 60 | 60 | 150 | 3 | الخلفية 2 - الشرقية |
| ش5 | شباك | 100 | 110 | 100 | 2 | الغربية 2 |

الإجمالي: أبواب 10 - شبابيك 12

# جدول المساحات وبيانات المشروع والتسعير

## بيانات المشروع

| البند | البيان |
|---|---|
| المشروع | كوخ دورين + تنسيق حديقة ومسبح — جدة |
| العميل | عميل جديد — جدة |
| الموقع | جدة |
| الاستخدام | سكن خاص / استجمام |
| التاريخ | 2026-10-18 |
| نظام البناء | هيكل خشب 7×5 + تلبيس 2.5 سم من الجهتين |
| السقف | جملون 30° — قرميد معدني |

## التسعير

| البند | القيمة |
|---|---|
| المساحة المبنية (م2) | 160.00 |
| سعر المتر المربع | 1,096 ريال |
| **الإجمالي** | **175,360 ريال** |

**ملاحظات:**

- السعر للمساحة المبنية للكوخ (دورين) — التراس والبلكونة والأعمدة مجاناً.
- أعمال الموقع (السور، المسبح، الحديقة، البيارة، الخزان، التمديدات الخارجية) تقديرية بأسعار السوق وتُنفّذ مع مقاول الموقع.

## جدول المساحات

| م | الفراغ | الأبعاد (م) | المساحة (م2) |
|---|---|---|---|
| 1 | أرضي — الصالة | 7.76 × 5.80 | 45.01 |
| 2 | أرضي — الدرج | 2.34 × 3.00 | 7.02 |
| 3 | أرضي — دورة مياه | 1.60 × 2.60 | 4.16 |
| 4 | أرضي — المطبخ | 3.58 × 3.84 | 13.75 |
| 5 | أول — غرفة نوم 1 | 3.34 × 4.64 | 15.50 |
| 6 | أول — غرفة الماستر | 4.30 × 4.64 | 16.28 |
| 7 | أول — حمام الماستر | 1.70 × 1.90 | 3.23 |
| 8 | أول — الممر | 7.76 × 1.00 | 7.76 |
| 9 | أول — دورة مياه (للغرفتين) | 1.60 × 3.88 | 6.21 |
| 10 | أول — غرفة نوم 2 | 3.58 × 3.88 | 13.89 |
| | **المساحة الصافية الداخلية** | | **132.80** |
| | **التراس المسقوف + تراس الدور الأول (مجاناً)** | **8.00 × 2.40 × 2** | **33.60** |
| | **المساحة الإجمالية المبنية** | **8.00 × 10.00 × 2 دور** | **160.00** |

# التكلفة التقديرية للمشروع (الكوخ + أعمال الموقع)

| البند | الكمية | سعر الوحدة (ريال) | الإجمالي (ريال) |
|---|---|---|---|
| الكوخ الخشبي — سعر المصنع | 160 م² | 1,096 | 175,360 |
| السور البلك 2.50 م (قواعد + أعمدة + لياسة ودهان + غطاء خشب) | 75 م.ط | 550 – 750 | 41,250 – 56,250 |
| بوابة سيارة 3.80 م حديثة (حديد + شرائح خشب) + باب مشاة | 1 مقطوعية | 9,000 – 15,000 | 9,000 – 15,000 |
| مسبح فايبرجلاس جاهز 9.32 × 4.22 (عمق 1.20–1.80) شامل المعدات + الحفر والرافعة وفرشة البحص والإطار | 1 مقطوعية | 58,000 – 72,000 | 58,000 – 72,000 |
| بلاط خارجي (حول المسبح + الممرات + الموقف) | 67 م² | 110 – 170 | 7,370 – 11,390 |
| برجولة خشب للجلسة الخارجية + جلسة مبنية | 1 مقطوعية | 8,000 – 14,000 | 8,000 – 14,000 |
| المسطحات الخضراء (تربة زراعية + ثيل + شبكة ري) + نخيل وأشجار وشجيرات + الأحواض | 1 مقطوعية | 14,000 – 24,000 | 14,000 – 24,000 |
| بيارة خرسانية (غرفتين) + التوصيلات | 1 مقطوعية | 12,000 – 20,000 | 12,000 – 20,000 |
| خزان أرضي خرساني ≈ 20 م³ + مضخة + خزان علوي | 1 مقطوعية | 18,000 – 28,000 | 18,000 – 28,000 |
| تمديدات الكهرباء الخارجية (التغذية + إنارة الحديقة والمسبح والسور) | 1 مقطوعية | 10,000 – 18,000 | 10,000 – 18,000 |
| تمديدات السباكة الخارجية (المسبح + الري + الصرف للبيارة + الخزان) | 1 مقطوعية | 8,000 – 14,000 | 8,000 – 14,000 |
| **الإجمالي التقديري (الكوخ + الموقع)** | | | **361,000 – 448,000** |

- الكوخ بسعر المصنع للمتر المربع على المساحة المبنية (دورين) — التراس والبلكونة والأعمدة مجاناً.
- أعمال الموقع تقديرية بأسعار السوق السعودي وتختلف حسب المقاول والمواصفات ونوع التربة — تُعتمد بعرض سعر من المقاول.
- التوفير ممكن: مسبح أصغر أو فايبرجلاس جاهز، سور بلك بدون لياسة خارجية، ثيل صناعي بدل الطبيعي.
- غير شامل: الصبة/القواعد الخرسانية تحت الكوخ، رسوم البلدية والعداد، الأثاث والمكيفات.

| مصنع وتد الأخشاب<br>Watad Wood Factory | المشروع / العميل<br>**كوخ دورين + تنسيق حديقة ومسبح — جدة**<br>**عميل جديد — جدة** | عنوان اللوحة<br>**التكلفة التقديرية** | المقياس<br>— | التاريخ<br>**2026-10-18** | رقم اللوحة<br>**A-09 (9/15)** |
|---|---|---|---|---|---|

# التكلفة التقديرية — التجهيزات الداخلية والفرش

| البند | الكمية | سعر الوحدة (ريال) | الإجمالي (ريال) |
|---|---|---|---|
| الكهرباء الداخلية — حسب جدول الكميات التفصيلي (الفنار) | 1 جدول | | 13,980 – 19,370 |
| توزيعات الإنارة الداخلية (سبوتات LED + ثريا الصالة + إنارة الدرج والممرات + إنارة البلكونة) | 1 مقطوعية | 5,000 – 10,000 | 5,000 – 10,000 |
| مكيف سبليت 18,000 وحدة إنفرتر (الصالة ×2 + الماستر) — شامل النحاس والتركيب | 3 جهاز | 3,000 – 4,200 | 9,000 – 12,600 |
| مكيف سبليت 12,000 وحدة إنفرتر (المطبخ + غرفة 1 + غرفة 2) — شامل النحاس والتركيب | 3 جهاز | 2,300 – 3,200 | 6,900 – 9,600 |
| ثلاجة دبل دور 18–22 قدم | 1 جهاز | 2,500 – 4,500 | 2,500 – 4,500 |
| شاشة بلازما (LED/QLED) 65 بوصة + حامل جداري | 1 جهاز | 2,500 – 5,000 | 2,500 – 5,000 |
| فرش الصالة: كنبة 3 مقاعد + كرسيين + طاولة وسط + طاولة تلفزيون + زولية | 1 طقم | 7,000 – 15,000 | 7,000 – 15,000 |
| طاولة طعام 6 كراسي | 1 طقم | 2,500 – 5,000 | 2,500 – 5,000 |
| غرفة نوم ماستر: سرير 180 + مرتبة + دولاب + كومدينتين + تسريحة | 1 طقم | 6,000 – 12,000 | 6,000 – 12,000 |
| غرفة نوم مفردة: سرير 120 + مرتبة + دولاب + كومدينة (غرفة 1 + غرفة 2) | 2 طقم | 3,000 – 6,000 | 6,000 – 12,000 |
| ستائر (بلاك أوت + شيفون) مع المجاري — شبابيك وأبواب زجاج الدورين ≈ 20 م.ط | 20 م.ط | 180 – 320 | 3,600 – 6,400 |
| **إجمالي التجهيزات الداخلية والفرش** | | | **65,000 – 111,000** |
| **الإجمالي الكلي للمشروع (الكوخ + الموقع + التجهيزات والفرش)** | | | **426,000 – 559,000** |

• الأسعار تقديرية من السوق السعودي (جدة) وتختلف حسب الماركة والمواصفات — تُعتمد بعروض أسعار من الموردين.
• المكيفات محسوبة حسب مساحة كل فراغ لجو جدة (حار ورطب): الصالة 45 م² بجهازين 18 ألف، الماستر 18 ألف، والباقي 12 ألف.
• غير شامل: أجهزة المطبخ الأخرى (فرن، غسالة، مايكروويف)، السخانات، والديكور والإكسسوارات.

# جدول كميات الكهرباء الداخلية — الفنار (ماسة أسود) — الكوخ دورين 160 م²

| البند | الكمية | سعر الوحدة (ريال) | الإجمالي (ريال) |
|---|---|---|---|
| فيش 13 أمبير مع مفتاح ماسة أسود (الصالة 7، المطبخ 4، الغرف 4+4+5، الممرات والدرج 3، التراس والبلكونة 2) | 29 حبة | 22 – 26 | 638 – 754 |
| فيش ثنائي 13 أمبير 7×14 ماسة أسود (جدار التلفزيون + كاونتر المطبخ) | 4 حبة | 36 – 41 | 144 – 164 |
| مفتاح مكيف 45 أمبير ماسة أسود (لكل مكيف سبليت) | 6 حبة | 46 – 55 | 276 – 330 |
| مفتاح سخان 20 أمبير ماسة أسود (3 دورات مياه + المطبخ) | 4 حبة | 38 – 44 | 152 – 176 |
| مفتاح ثلاثي ماسة أسود (المدخل + باب الحديقة) | 2 حبة | 20 – 24 | 40 – 48 |
| مفتاح ثنائي/مجوز ماسة أسود (المطبخ، التراس، الغرف الثلاث) | 5 حبة | 16 – 20 | 80 – 100 |
| مفتاح مفرد ماسة أسود (دورات المياه، الممرات، البلكونة، الدرج تحت/فوق) | 9 حبة | 9 – 11 | 81 – 99 |
| فيش دش/تلفزيون ماسة أسود (الصالة + الماستر + غرفة) | 3 حبة | 23 – 27 | 69 – 81 |
| فيش انترنت/كمبيوتر ماسة أسود (الصالة + الماستر) | 2 حبة | 35 – 40 | 70 – 80 |
| قاطع حساس الفنار 1 قطب (إنارة 4× 10A، أفياش 6× 20A، سخانات 4× 20A) | 14 حبة | 20 – 30 | 280 – 420 |
| قاطع حساس الفنار C32 (مكيفات 6× + أجهزة المطبخ 2×) | 8 حبة | 25 – 35 | 200 – 280 |
| قاطع رئيسي 2 قطب 63A + قاطع تسريب أرضي RCCB | 1 طقم | 220 – 380 | 220 – 380 |
| لوحة توزيع الفنار 24 خط مدفونة (لوحة رئيسية) + لوحة 12 خط للدور الأول | 1 طقم | 450 – 750 | 450 – 750 |
| سلك الفنار 1.5 ملم لفة 500 قدم (الإنارة — أحمر/أسود/أصفر-أخضر) | 4 لفة | 190 – 240 | 760 – 960 |
| سلك الفنار 2.5 ملم لفة 500 قدم (الأفياش) | 6 لفة | 285 – 330 | 1,710 – 1,980 |
| سلك الفنار 4 ملم لفة 500 قدم (السخانات + المكيفات 12 ألف) | 3 لفة | 430 – 500 | 1,290 – 1,500 |
| سلك الفنار 6 ملم لفة 500 قدم (المكيفات 18 ألف + تغذية اللوحة الفرعية) | 2 لفة | 600 – 720 | 1,200 – 1,440 |
| كيبل التغذية الرئيسي من العداد للوحة (4×16 ملم) — تقريبي 25 م | 25 م | 45 – 65 | 1,125 – 1,625 |
| مواسير PVC 20/25 ملم + أكواع + علب 7×7 و 7×14 + لوازم | 1 مقطوعية | 1,200 – 1,800 | 1,200 – 1,800 |
| أجور كهربائي (تمديد + تركيب + تشغيل وفحص) — دورين | 160 م² | 25 – 40 | 4,000 – 6,400 |
| **إجمالي الكهرباء الداخلية** | | | **13,980 – 19,370** |

- الكميات محسوبة من المساقط (عدد الأفياش والمفاتيح لكل غرفة + مكيف ومفتاح لكل غرفة + سخان لكل دورة مياه) — تُراجع مع الكهربائي بالموقع.
- الأسعار من متاجر سعودية (أكتوبر 2026) لمجموعة الفنار ماسة أسود بيانو وأسلاك الفنار 500 قدم وقواطع حساس — قد تختلف حسب الموزع.
- الإنارة (سبوتات/ثريا) والمكيفات محسوبة في لوحة التجهيزات والفرش.

| المشروع / العميل | عنوان اللوحة | المقياس | التاريخ | رقم اللوحة |
|---|---|---|---|---|
| **كوخ دورين + تنسيق حديقة ومسبح — جدة**<br>**عميل جديد — جدة** | **جدول كميات الكهرباء** | — | **2026-10-18** | **A-11 (11/15)** |


**مصنع وتد الأخشاب**
Watad Wood Factory

# لقطات المنظور الخارجي


المنظور الأمامي




منظور أمامي من اليسار

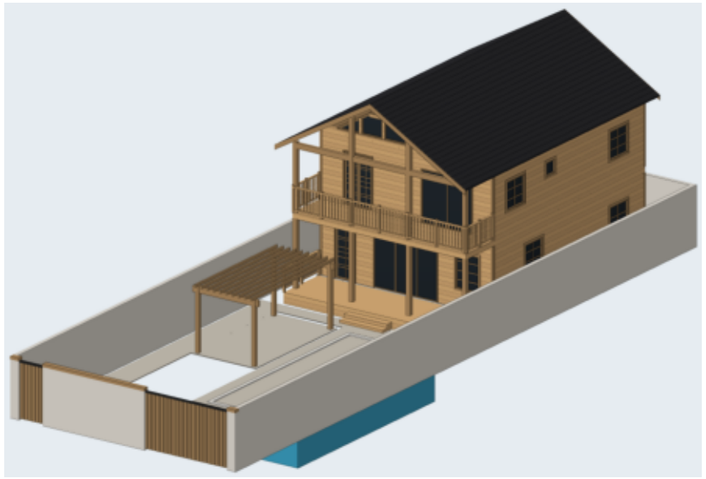


منظور أمامي من اليمين

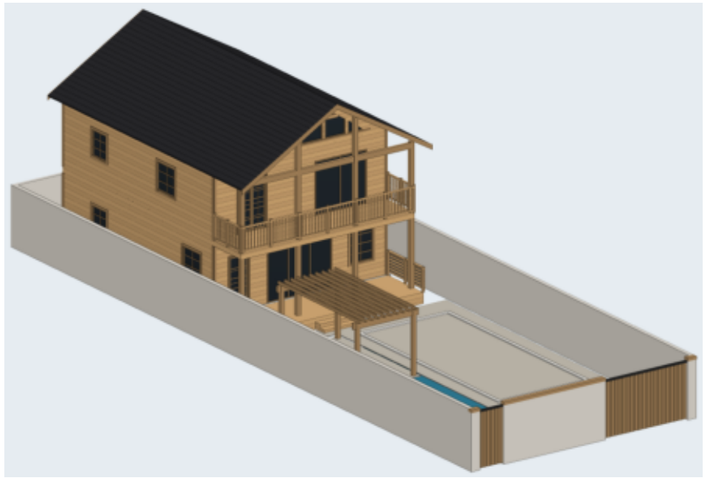


منظر علوي

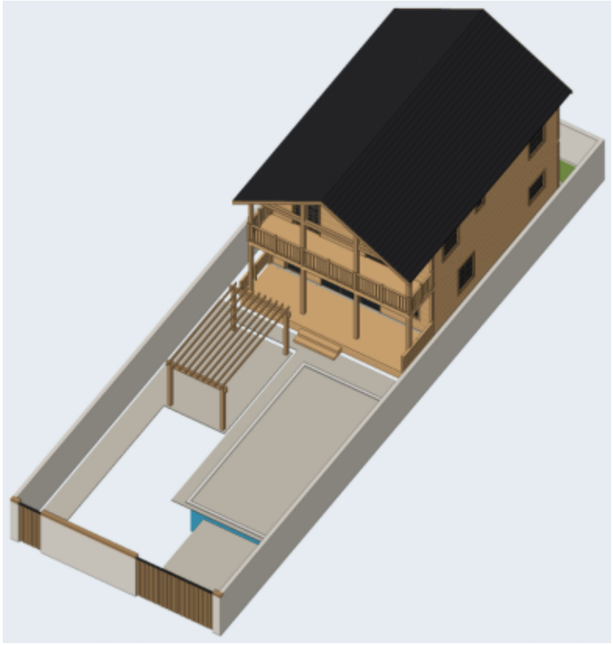

المنظور الخلفي

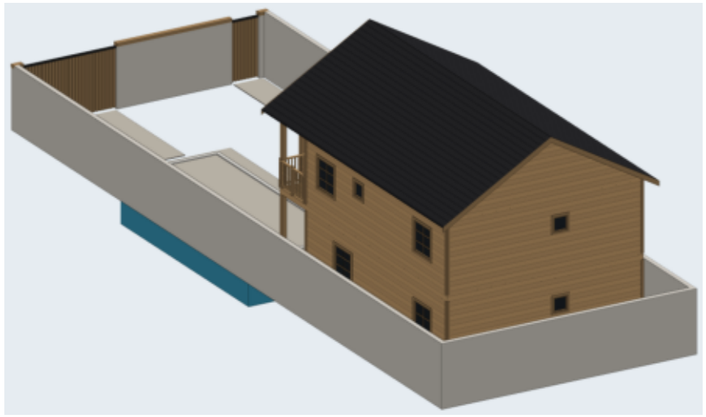

منظور خلفي من اليمين

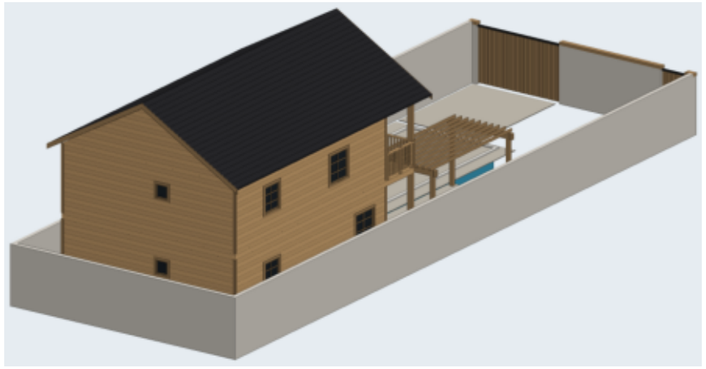


| المشروع / العميل | عنوان اللوحة | المقياس | التاريخ | رقم اللوحة |
|---|---|---|---|---|
| **كوخ دورين + تنسيق حديقة ومسبح — جدة**<br>**عميل جديد — جدة** | **لقطات المنظور** | **—** | **2026-10-18** | **A-12 (12/15)** |

**مصنع وتد الأخشاب**
Watad Wood Factory

# المقطع العلوي بالفرش — الدور الأرضي

مقطع أفقي على ارتفاع 1.90 م — توزيع الفرش ومسار الحركة

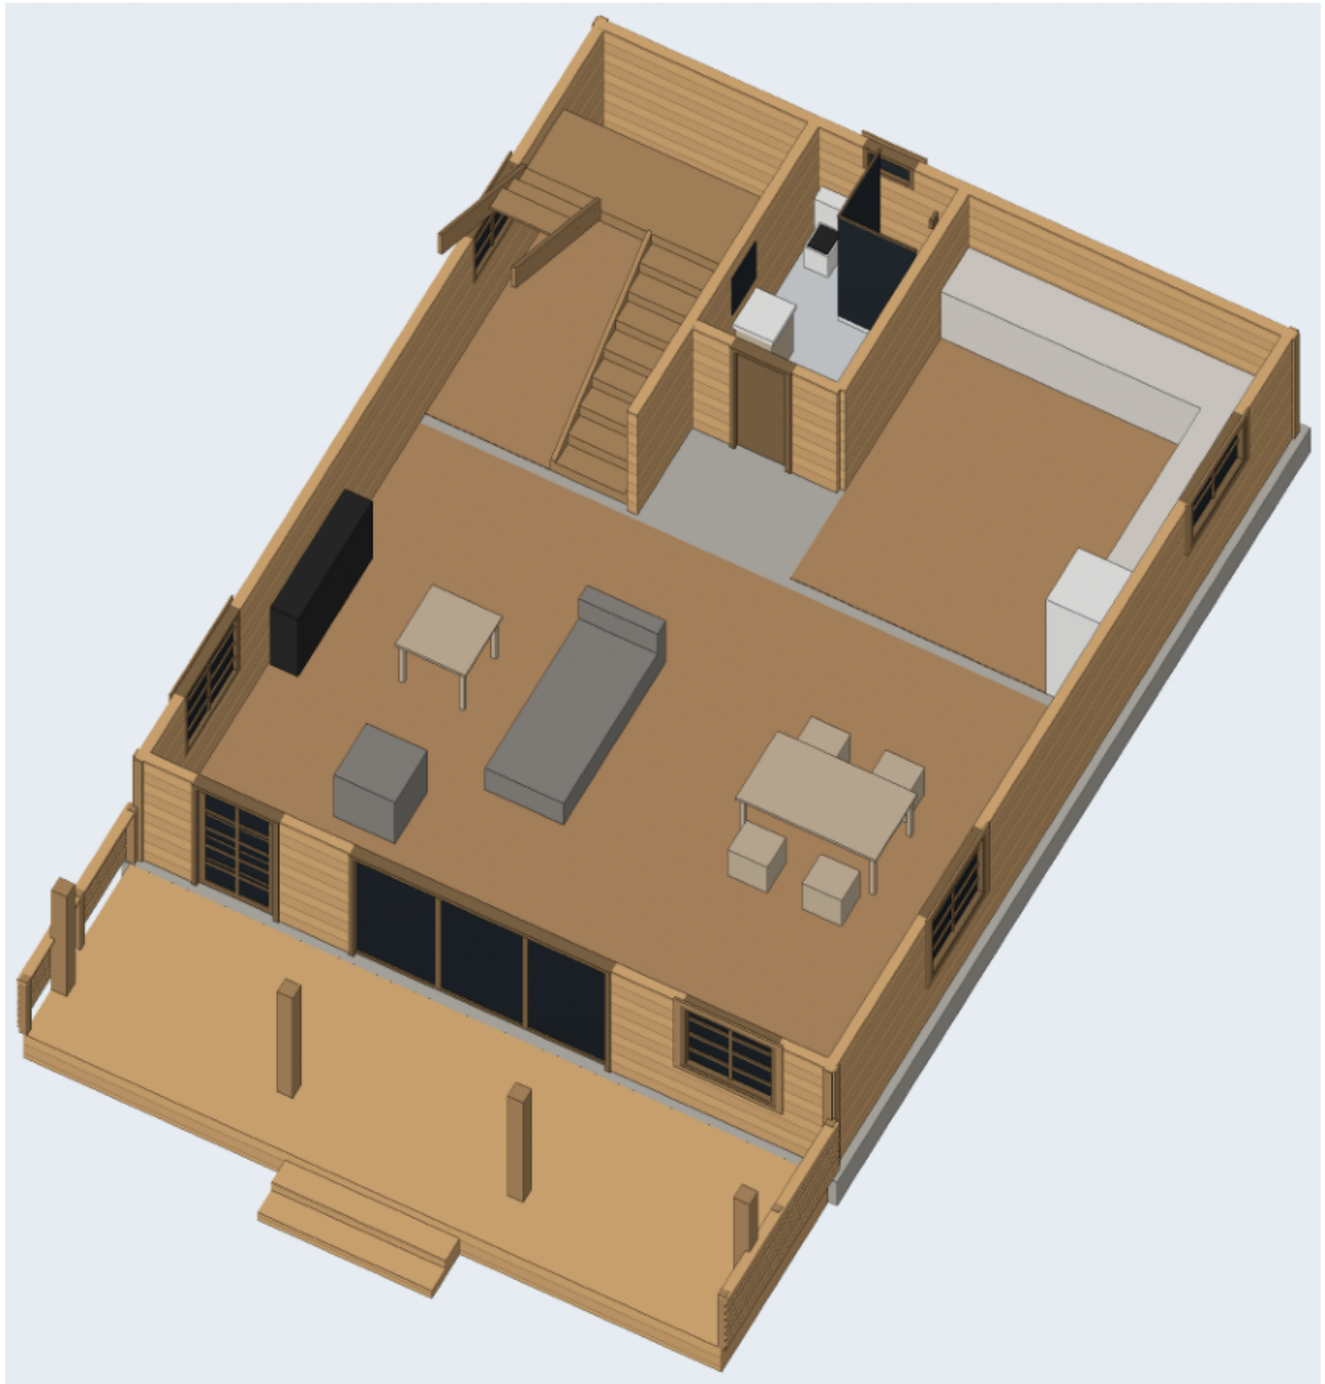


| المشروع / العميل | عنوان اللوحة | المقياس | التاريخ | رقم اللوحة |
|---|---|---|---|---|
| **كوخ دورين + تنسيق حديقة ومسبح — جدة**<br>**عميل جديد — جدة** | **المقطع العلوي بالفرش — الدور الأرضي** | **—** | **2026-10-18** | **A-13 (13/15)** |

**مصنع وتد الأخشاب**
Watad Wood Factory

# المقطع العلوي بالفرش — الدور الأول

مقطع أفقي على ارتفاع 1.90 م — توزيع الفرش ومسار الحركة

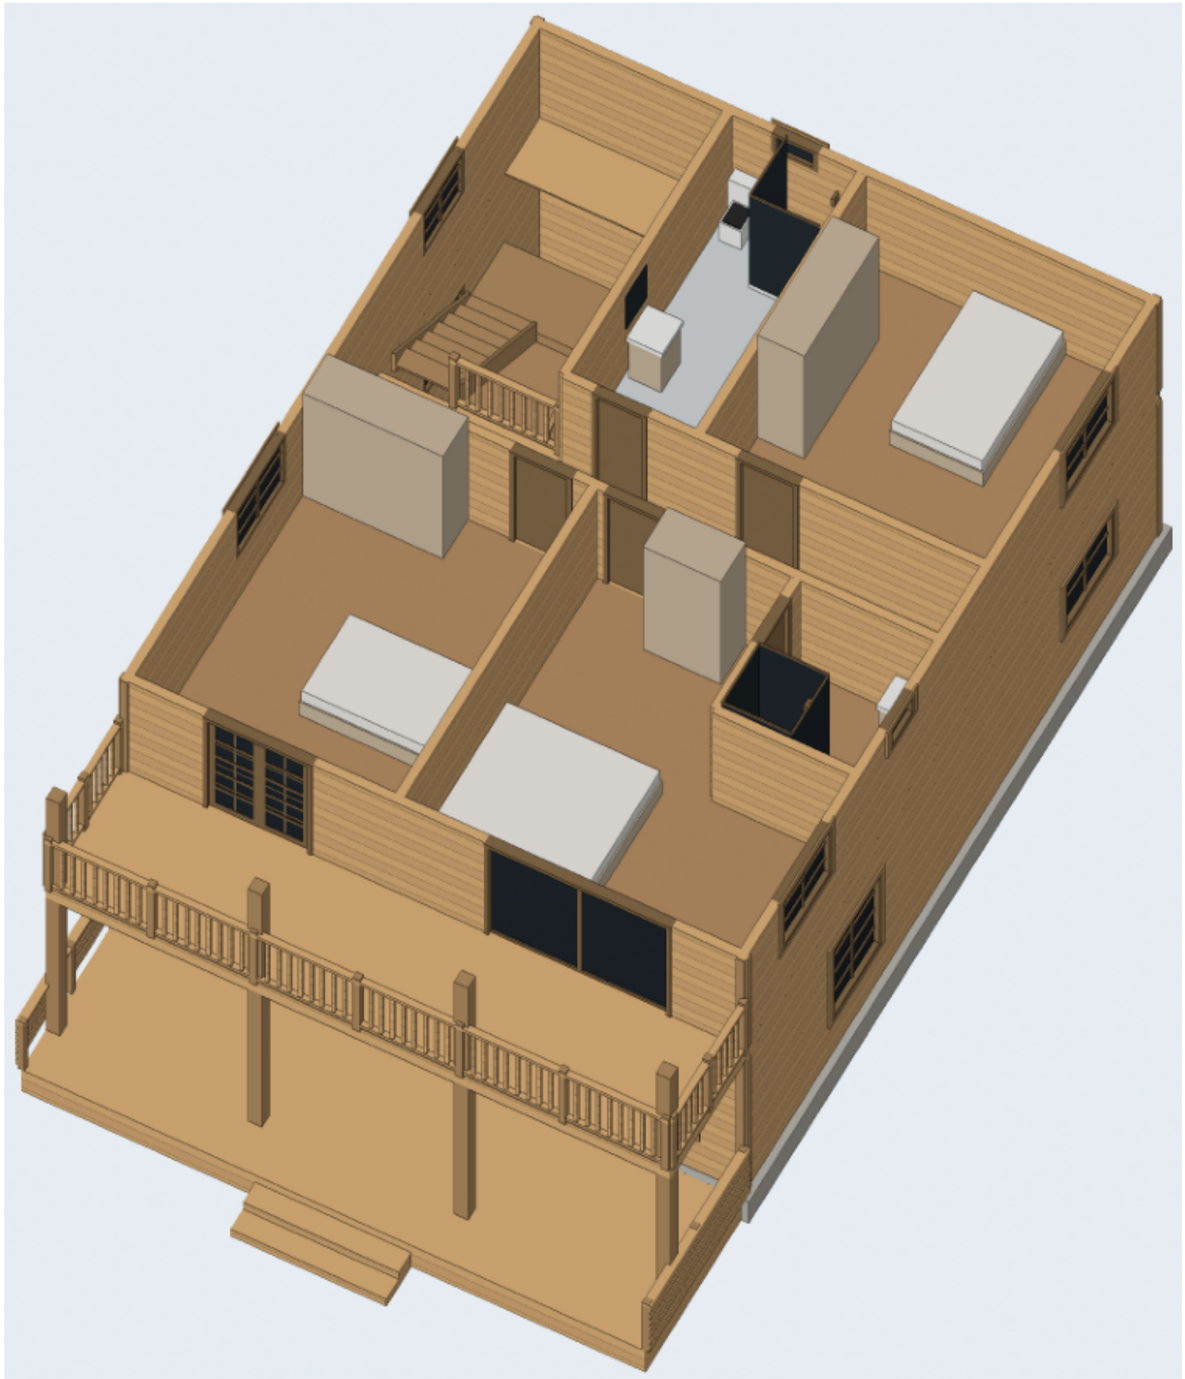


| المشروع / العميل | عنوان اللوحة | المقياس | التاريخ | رقم اللوحة |
|---|---|---|---|---|
| **كوخ دورين + تنسيق حديقة ومسبح — جدة**<br>**عميل جديد — جدة** | **المقطع العلوي بالفرش — الدور الأول** | **—** | **2026-10-18** | **A-14  (14/15)** |

**مصنع وتد الأخشاب**
Watad Wood Factory

# المنظور ثلاثي الأبعاد والمواد

النمط: جوزي غامق + إطارات سوداء — رندر واقعي بخامات حقيقية

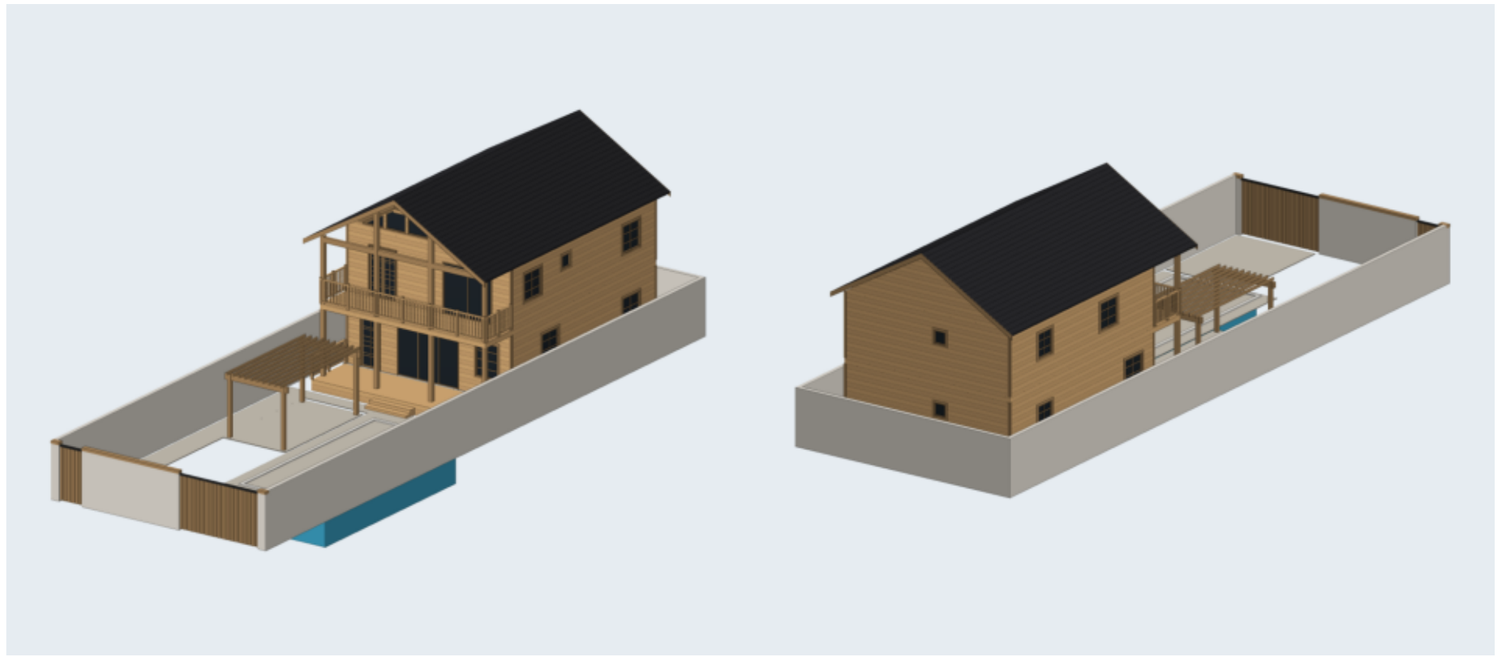

## جدول المواد والألوان

**الخشب / الصبغة**

خشب طبيعي فاتح (بدون صبغة)

**القرميد**

قرميد رمادي غامق

**الزجاج**

زجاج عاكس غامق

**إطارات الشبابيك والأبواب**

إطار خشب بنفس الصبغة أغمق

**الكنار والزوايا**

نفس الصبغة أغمق درجة


**الصبة**

خرسانة 45 سم


الدربزين: ألواح أفقية متقاربة (عصري)

تقسيم الشبابيك: بدون | الباب الرئيسي: زجاج بتقسيمات (فرنسي)

## أنواع الدربزين المعتمدة (من مشاريع المصنع)

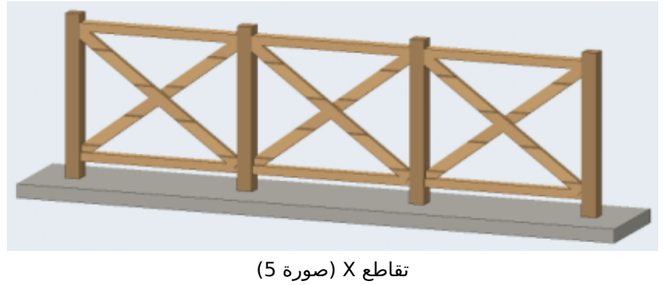

تقاطع X (صورة 5)

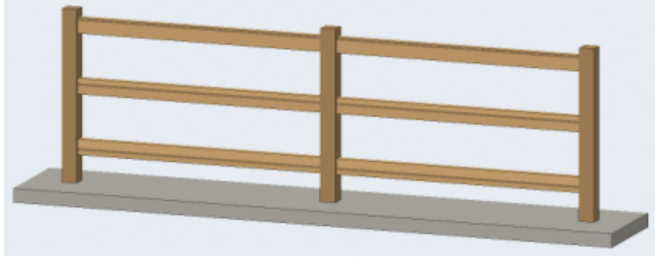

3 مرابيع أفقية (صورة 2)



قوائم رأسية متقاربة (صورة 1)

| المشروع / العميل | عنوان اللوحة | المقياس | التاريخ | رقم اللوحة |
|---|---|---|---|---|
| **كوخ دورين + تنسيق حديقة ومسبح — جدة**<br>**عميل جديد — جدة** | **المنظور والمواد** | **—** | **2026-10-18** | **A-15 (15/15)** |

**مصنع وتد الأخشاب**
Watad Wood Factory