جدول مساحات الموقع

البند	المقاس	المساحة (م²)
مساحة الأرض	25.00 × 36.00 م	900.0
الوحدة الواحدة (3 وحدات)	8.20 × 36.00 م	295.2
مسطح الأكواخ (3)	3 × 7.00 × 11.00 م	231.0
تراس الكوخ	3 × 2.40 × 7.00 م	50.4
مسبح	3 × 3.50 × 7.00 م	73.5
جلسة خارجية	3 × 3.04 × 4.20 م	38.3
بلاط		112.4
موقف سيارة	3 × 3.60 × 5.50 م	59.4
ممر	3 × 1.00 × 11.96 م	35.9
أحواض زراعة	3 × 0.70 × 8.00 م	16.8
المسطحات الخضراء (حديقة)	الباقي	282.4

الموقع العام وتنسيق الحديقة (لاندسكيب)

الأرض 25 × 36 م = 900 م² | الأبعاد بالسنتيمتر



شارع عرض 16 م


- تقسيم الأرض 25 × 36 م إلى 3 وحدات متساوية (8.20 × 36 م صافي) بجدران فاصلة 2.50 م — خصوصية كاملة لكل وحدة.
- لكل وحدة بوابة سيارة 3.60 م + باب مشاة مستقل، الموقف عند البوابة والممر بمحاذاة الجدار للتراس.
- الكوخ 7.00 × 11.00 = 77 م²: صالة ومطبخ تحضيري يطلّون على المسبح + غرفتين نوم كل غرفة بدورة مياه خاصة.
- مسبح 3.50 × 7.00 م بعمق 1.40 م قدام التراس المسقوف، جلسة تحت برجولة خشب وكراسي استلقاء.
- حديقة وأشجار ونخيل بين الموقف والمسبح تعزل منطقة الجلوس عن الشارع.

المشروع / العميل	عنوان اللوحة	المقياس	التاريخ	رقم اللوحة
مشروع 3 أكواخ استثمارية + لاندسكيب — أرض 25 × 36 م **عميل — مشروع استثماري**	**الموقع العام واللاندسكيب**	**1:200**	**2026-10-19**	**A-01 (1/10)**


مصنع وتد الأخشاب
Watad Wood Factory

المسقط الأفقي مع الفرش

الأبعاد بالسنتيمتر - الجدران: قوائم 7×5 + تلبيس 2.5 من الجهتين (12 سم)

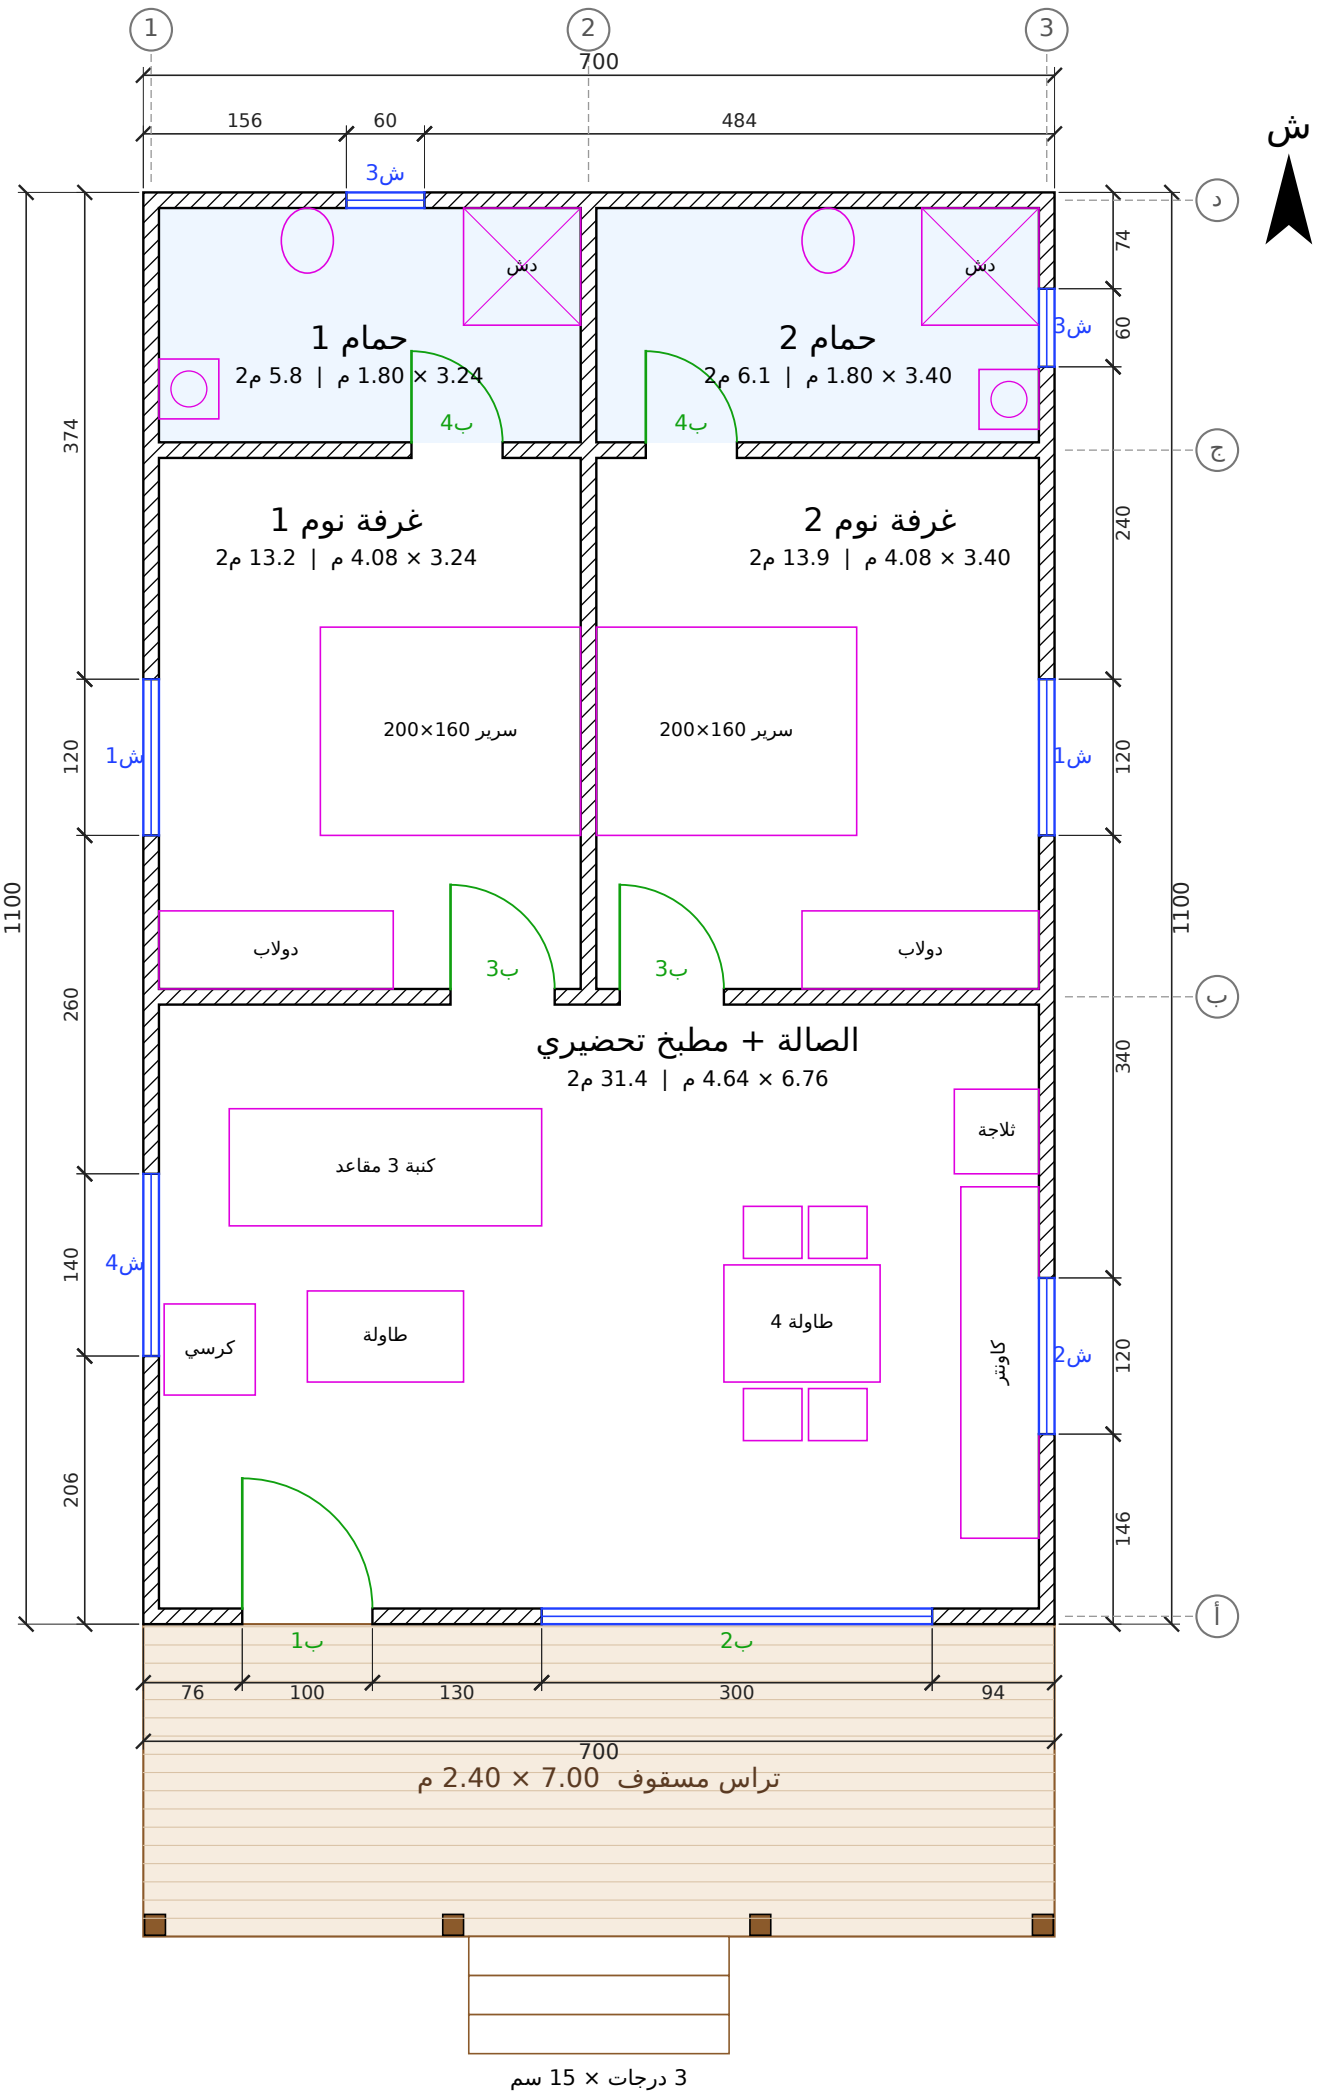


مصنع وتد الأخشاب Watad Wood Factory	المشروع / العميل **مشروع 3 أكواخ استثمارية + لاندسكيب — أرض 25 × 36 م** **عميل — مشروع استثماري**	عنوان اللوحة **المسقط الأفقي**	المقياس **1:50**	التاريخ **2026-10-19**	رقم اللوحة **A-02 (2/10)**

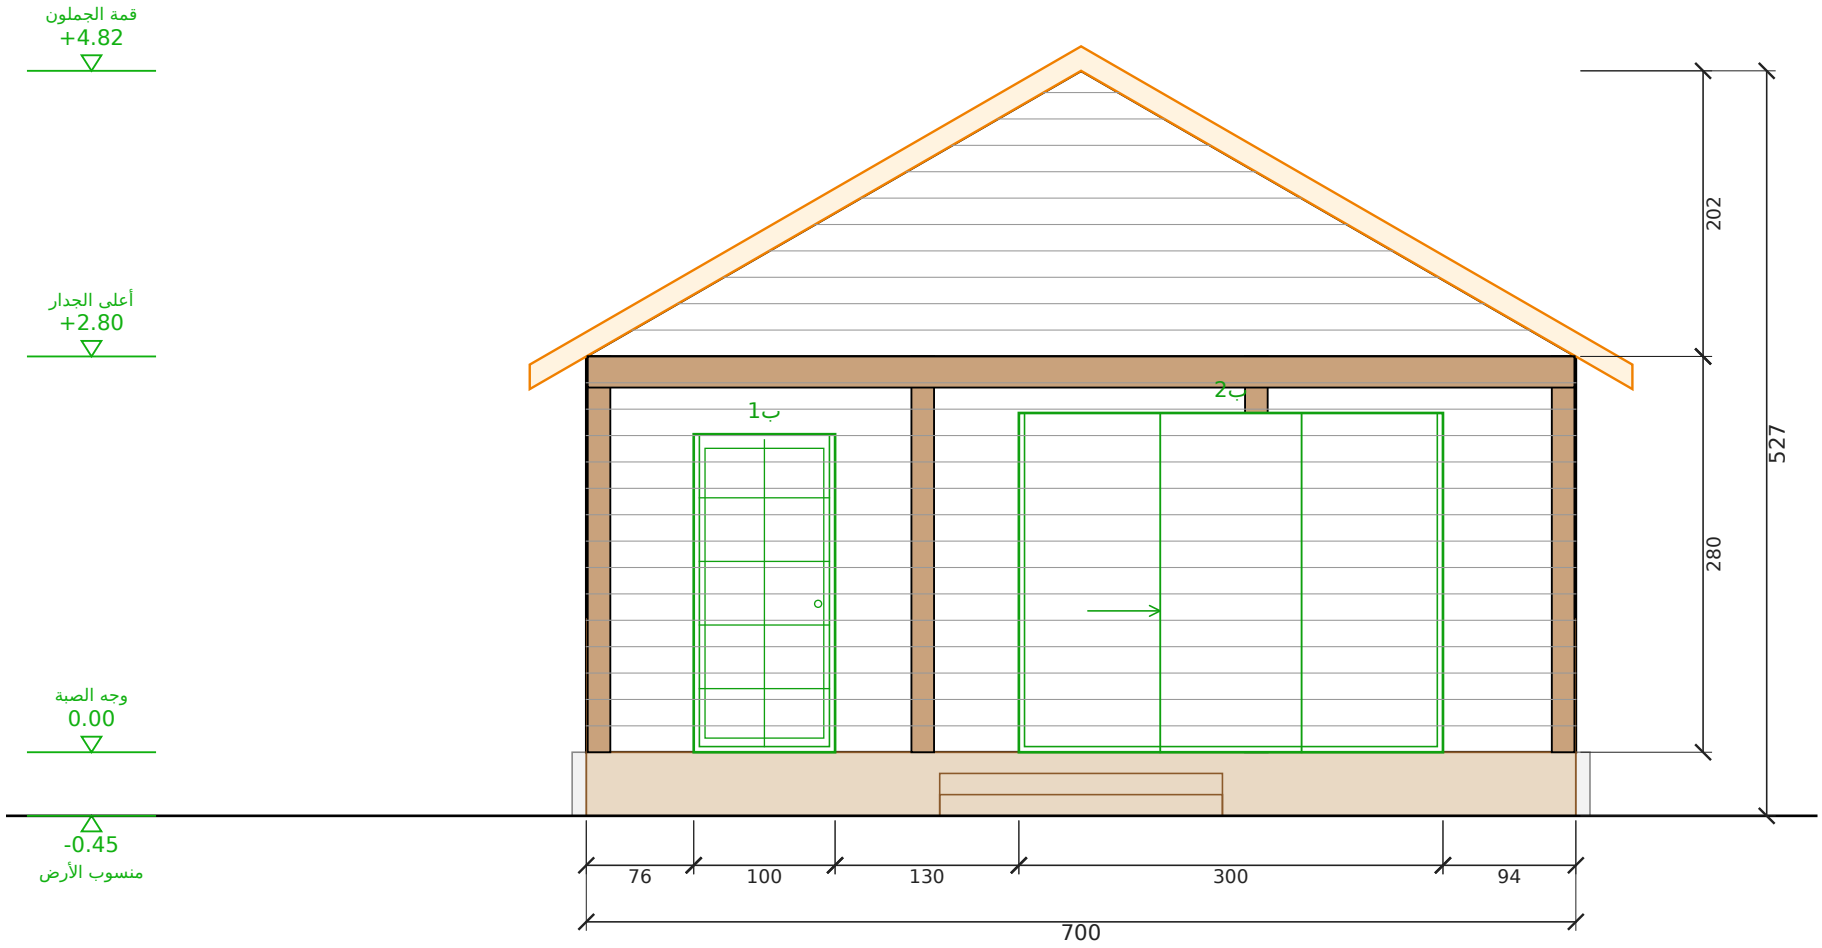

الواجهة الأمامية (على المسبح)

مقياس 1:50 | الوحدة: سم

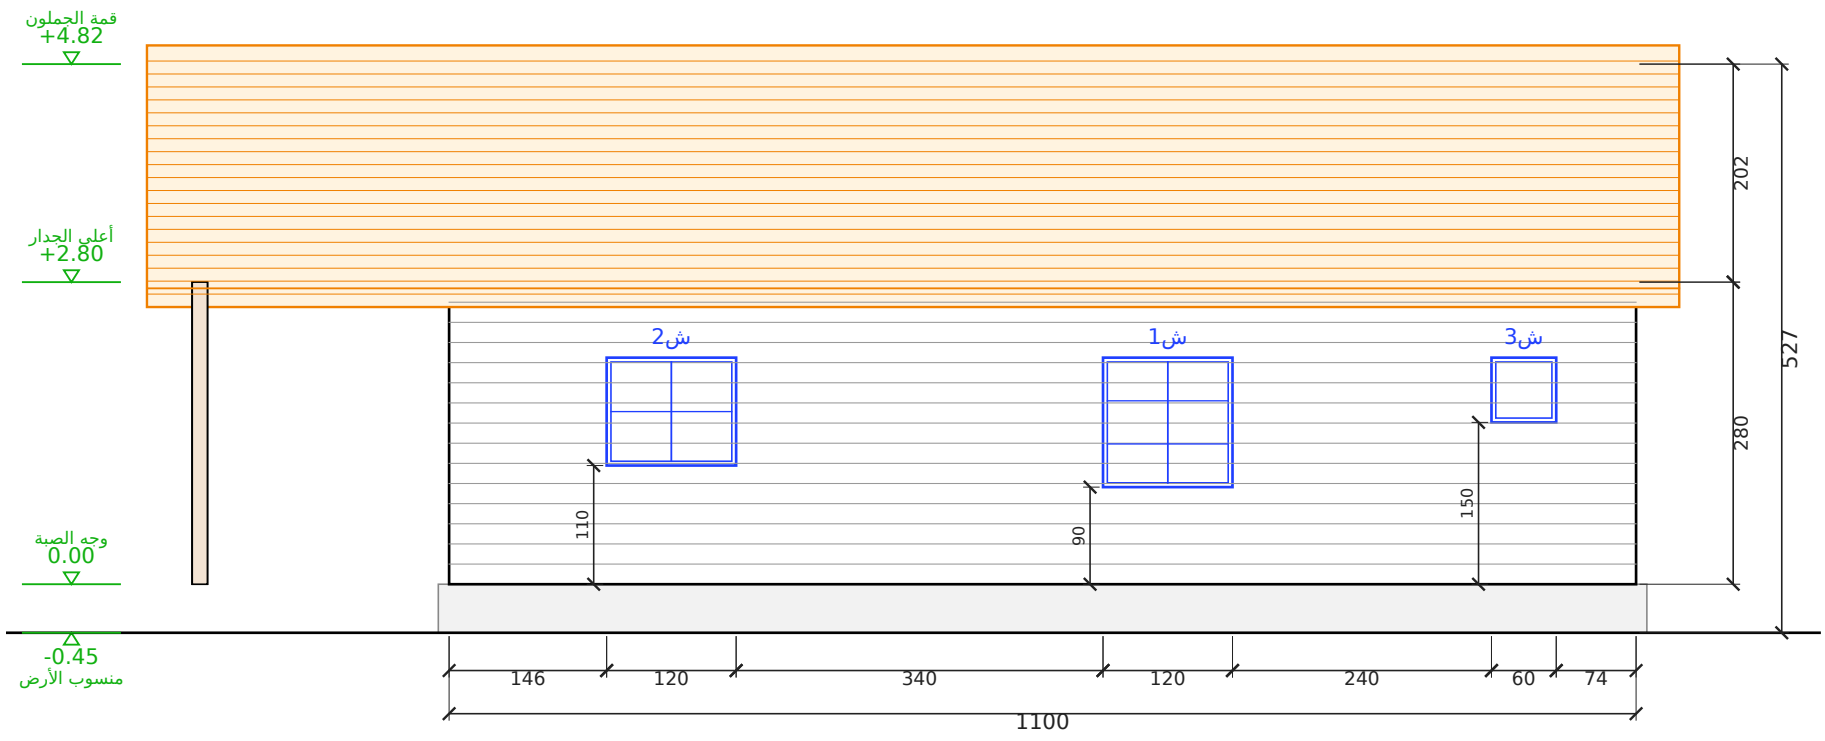


الواجهة الشرقية

مقياس 1:50 | الوحدة: سم


المشروع / العميل	عنوان اللوحة	المقياس	التاريخ	رقم اللوحة
مشروع 3 أكواخ استثمارية + لاندسكيب — أرض 25 × 36 م عميل — مشروع استثماري	الواجهة الأمامية (على المسبح) والواجهة الشرقية	1:50	2026-10-19	A-03 (3/10)

مصنع وتد الأخشاب
Watad Wood Factory

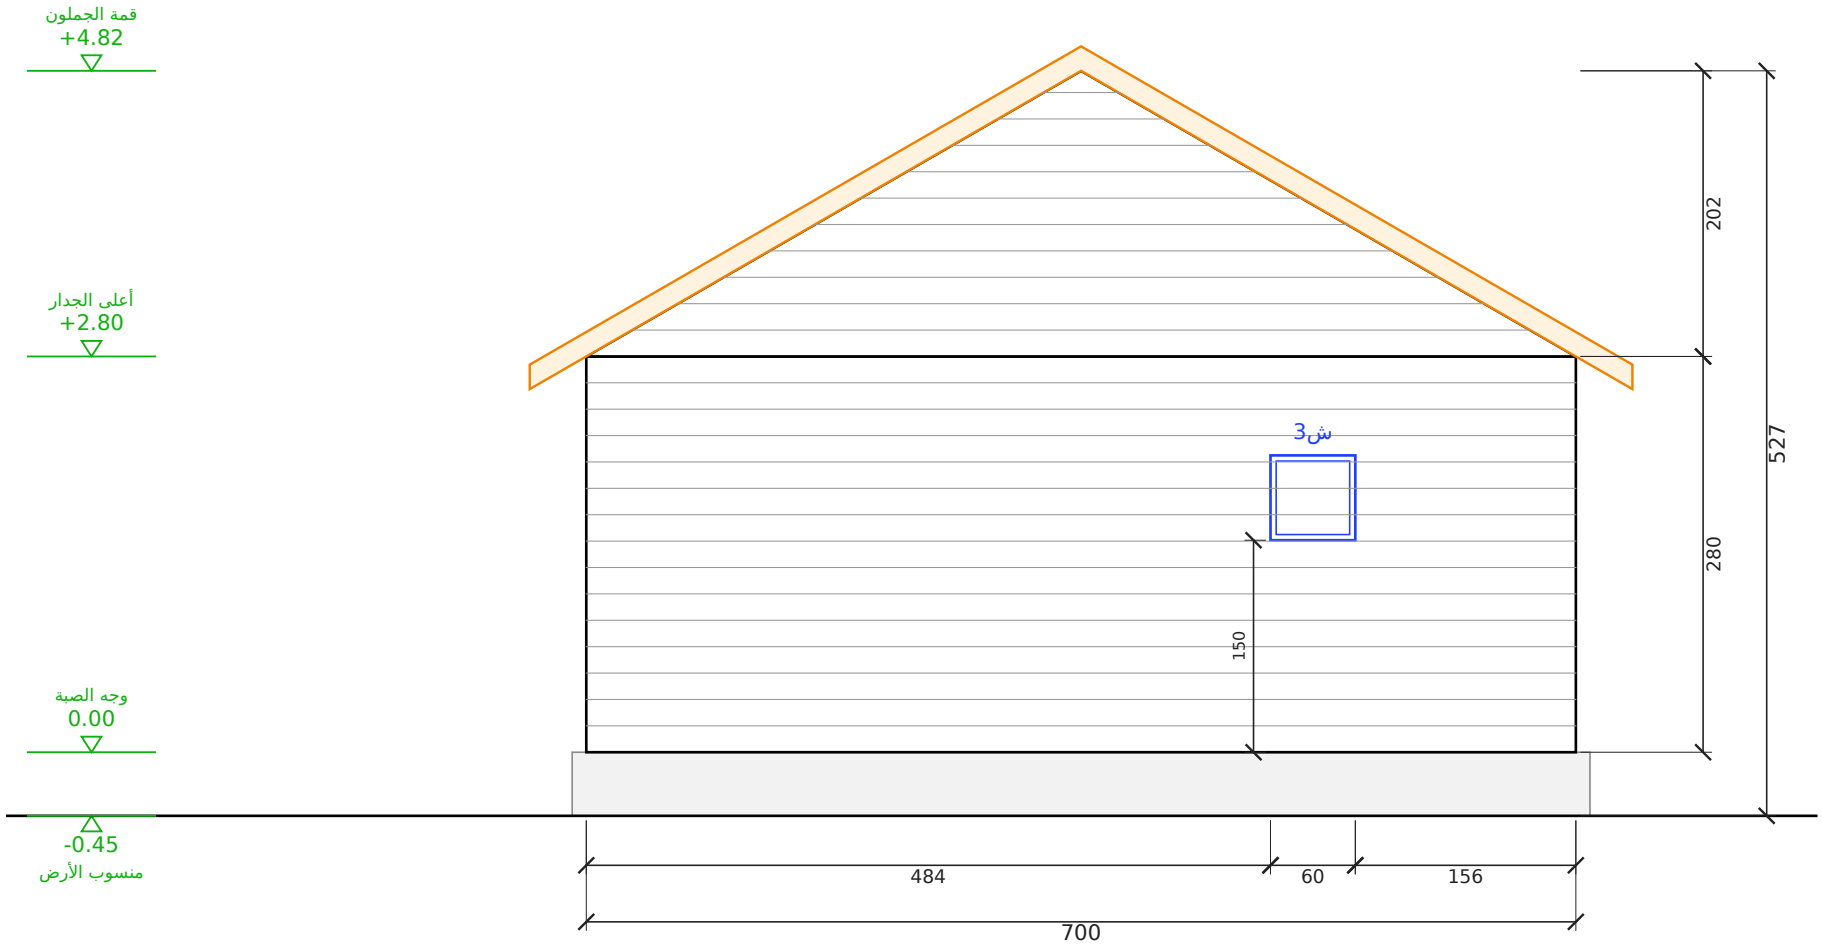

الواجهة الخلفية

مقياس 1:50 | الوحدة: سم

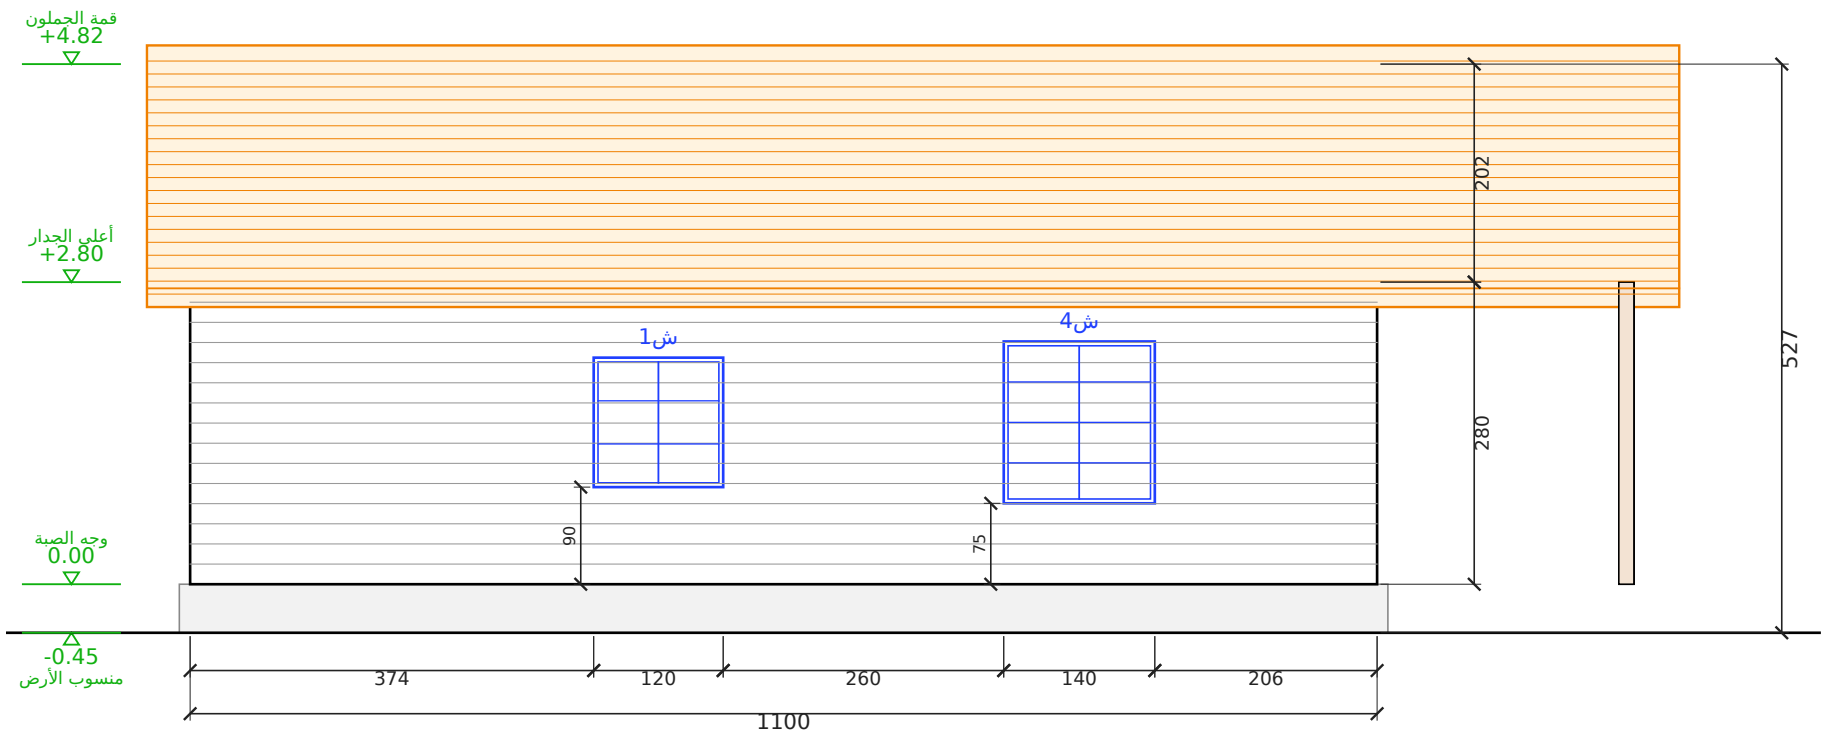


الواجهة الغربية

مقياس 1:50 | الوحدة: سم


المشروع / العميل	عنوان اللوحة	المقياس	التاريخ	رقم اللوحة
مشروع 3 أكواخ استثمارية + لاندسكيب — أرض 25 × 36 م عميل — مشروع استثماري	الواجهة الخلفية والواجهة الغربية	1:50	2026-10-19	A-04 (4/10)

مصنع وتد الأخشاب
Watad Wood Factory


مسقط السقف (جملون)
رفرف 40 سم من كل جهة | مقياس 1:50

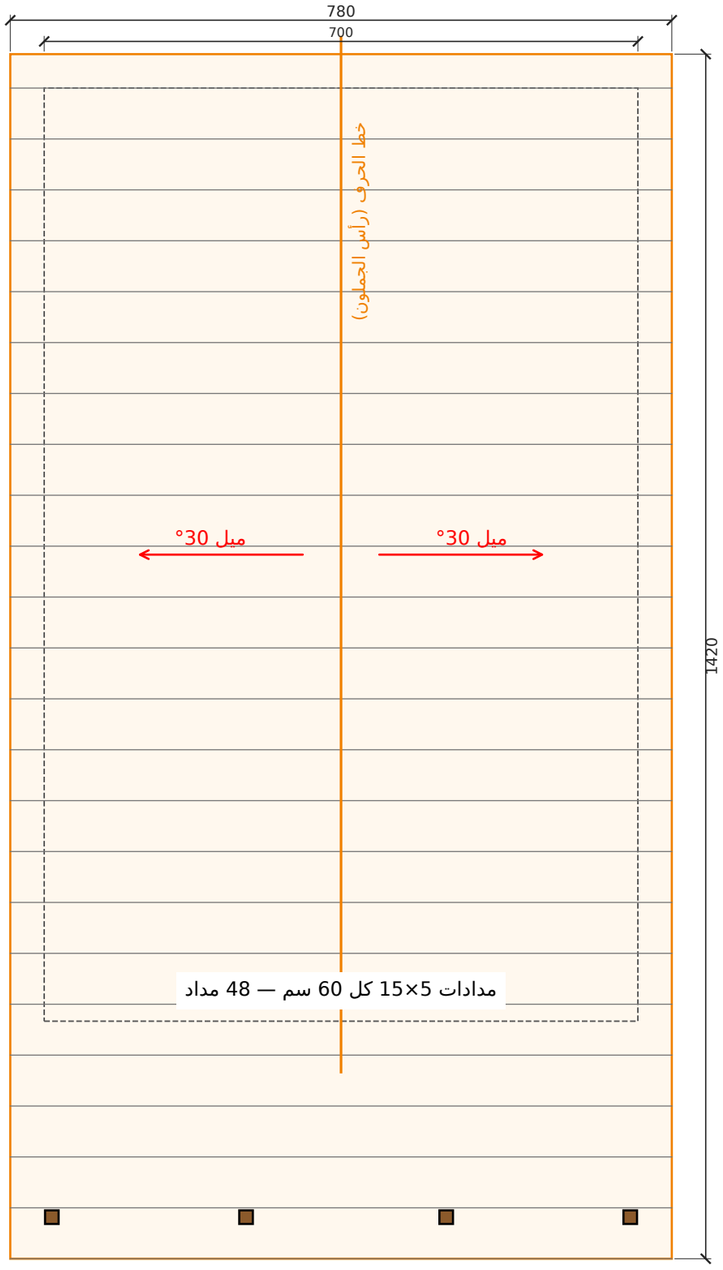

قطاع عرضي أ-أ
مقياس 1:50 | الوحدة: سم

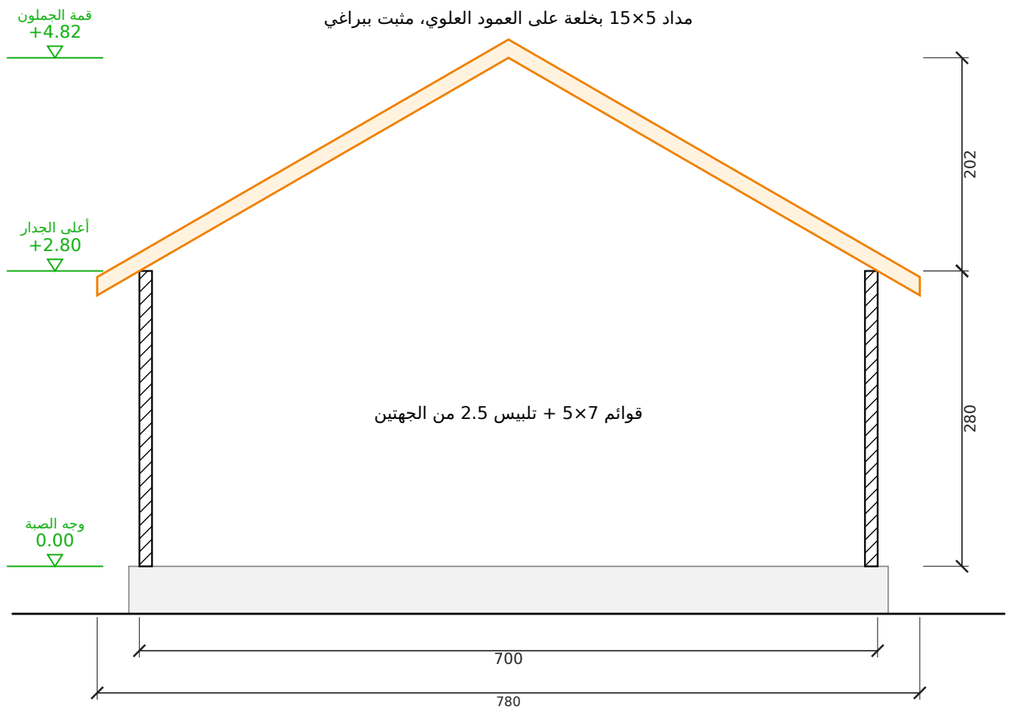

تفصيلة جلوس المداد على العلوي (1:5)

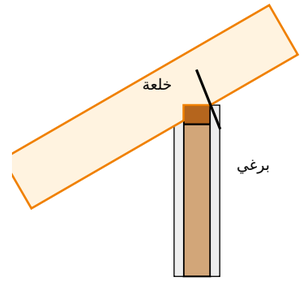

علوي 7×5 على قائم 7×5

المشروع / العميل	عنوان اللوحة	المقياس	التاريخ	رقم اللوحة
مشروع 3 أكواخ استثمارية + لاندسكيب — أرض 25 × 36 م عميل — مشروع استثماري	مسقط السقف والقطاع	1:50	2026-10-19	A-05 (5/10)

مصنع وتد الأخشاب
Watad Wood Factory

جدول مقاسات الأبواب والشبابيك
مقاس الفتحة الصافي في الجدار - الوحدة: سم

الرمز	النوع	العرض (سم)	الارتفاع (سم)	ارتفاع الجلسة (سم)	العدد	الموقع
ب1	باب	100	225	-	1	الأمامية (على المسبح)
ب2	باب	300	240	-	1	الأمامية (على المسبح)
ب3	باب	80	210	-	2	غرفة 1 - غرفة 2
ب4	باب	70	210	-	2	حمام 1 - حمام 2
ش1	شباك	120	120	90	2	الشرقية - الغربية
ش2	شباك	120	100	110	1	الشرقية
ش3	شباك	60	60	150	2	الشرقية - الخلفية
ش4	شباك	140	150	75	1	الغربية

الإجمالي: أبواب 6 - شبابيك 6

جدول المساحات وبيانات المشروع

بيانات المشروع

البند	البيان
المشروع	مشروع 3 أكواخ استثمارية + لاندسكيب — أرض 25 × 36 م
العميل	عميل — مشروع استثماري
الموقع	—
الاستخدام	استثماري (شاليهات / أكواخ تأجير)
التاريخ	2026-10-19
نظام البناء	هيكل خشب 5×7 + تلبيس 2.5 سم من الجهتين
السقف	جملون 30° — قرميد معدني

جدول المساحات


م	الفراغ	الأبعاد (م)	المساحة (م2)
1	الصالة + مطبخ تحضيري	6.76 × 4.64	31.37
2	غرفة نوم 1	3.24 × 4.08	13.22
3	غرفة نوم 2	3.40 × 4.08	13.87
4	حمام 1	3.24 × 1.80	5.83
5	حمام 2	3.40 × 1.80	6.12
	المساحة الصافية الداخلية		**70.41**
	التراس المسقوف	**7.00 × 2.40**	**16.80**
	المساحة الإجمالية المبنية	**7.00 × 11.00**	**77.00**

لقطات المنظور الخارجي


المنظور الأمامي




منظور أمامي من اليسار

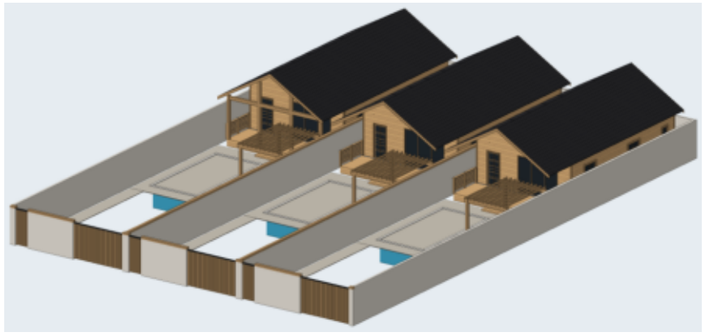


منظور أمامي من اليمين

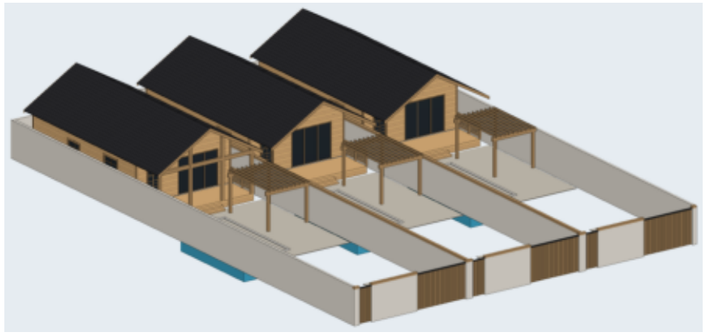


المنظور الخلفي

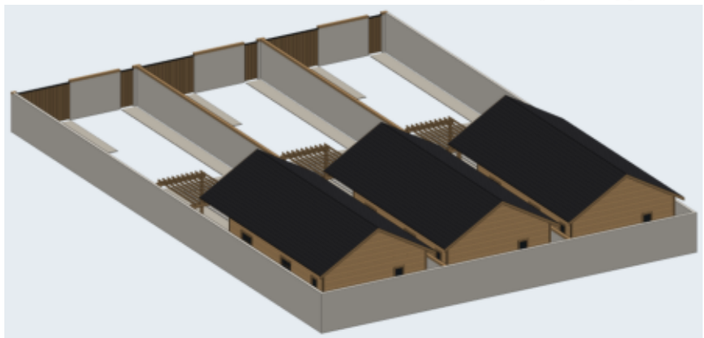

منظور خلفي من اليمين

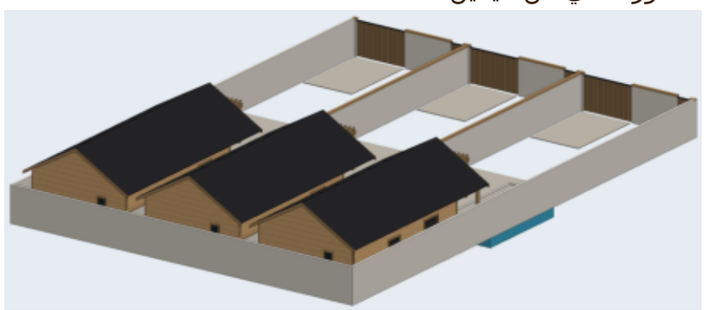

منظر علوي

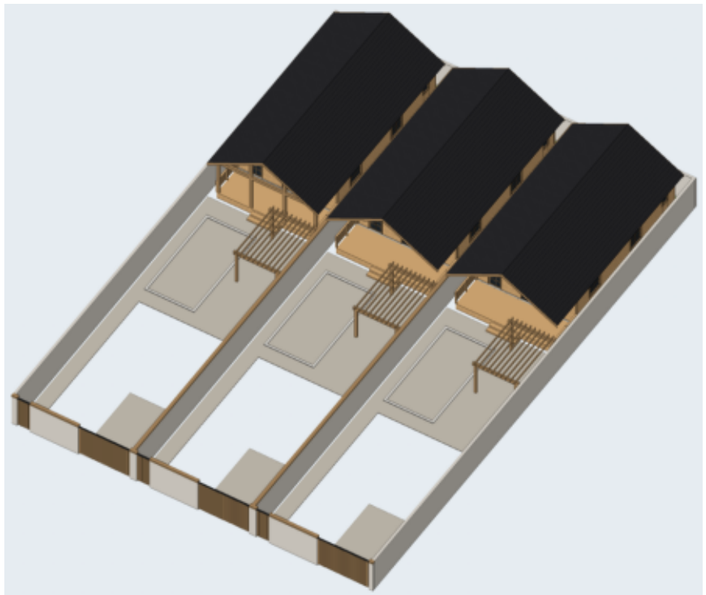


المشروع / العميل	عنوان اللوحة	المقياس	التاريخ	رقم اللوحة
مشروع 3 أكواخ استثمارية + لاندسكيب — أرض 25 × 36 م **عميل — مشروع استثماري**	**لقطات المنظور**	**—**	**2026-10-19**	**A-08 (8/10)**

مصنع وتد الأخشاب
Watad Wood Factory

المقطع العلوي بالفرش

مقطع أفقي على ارتفاع 1.90 م — توزيع الفرش ومسار الحركة

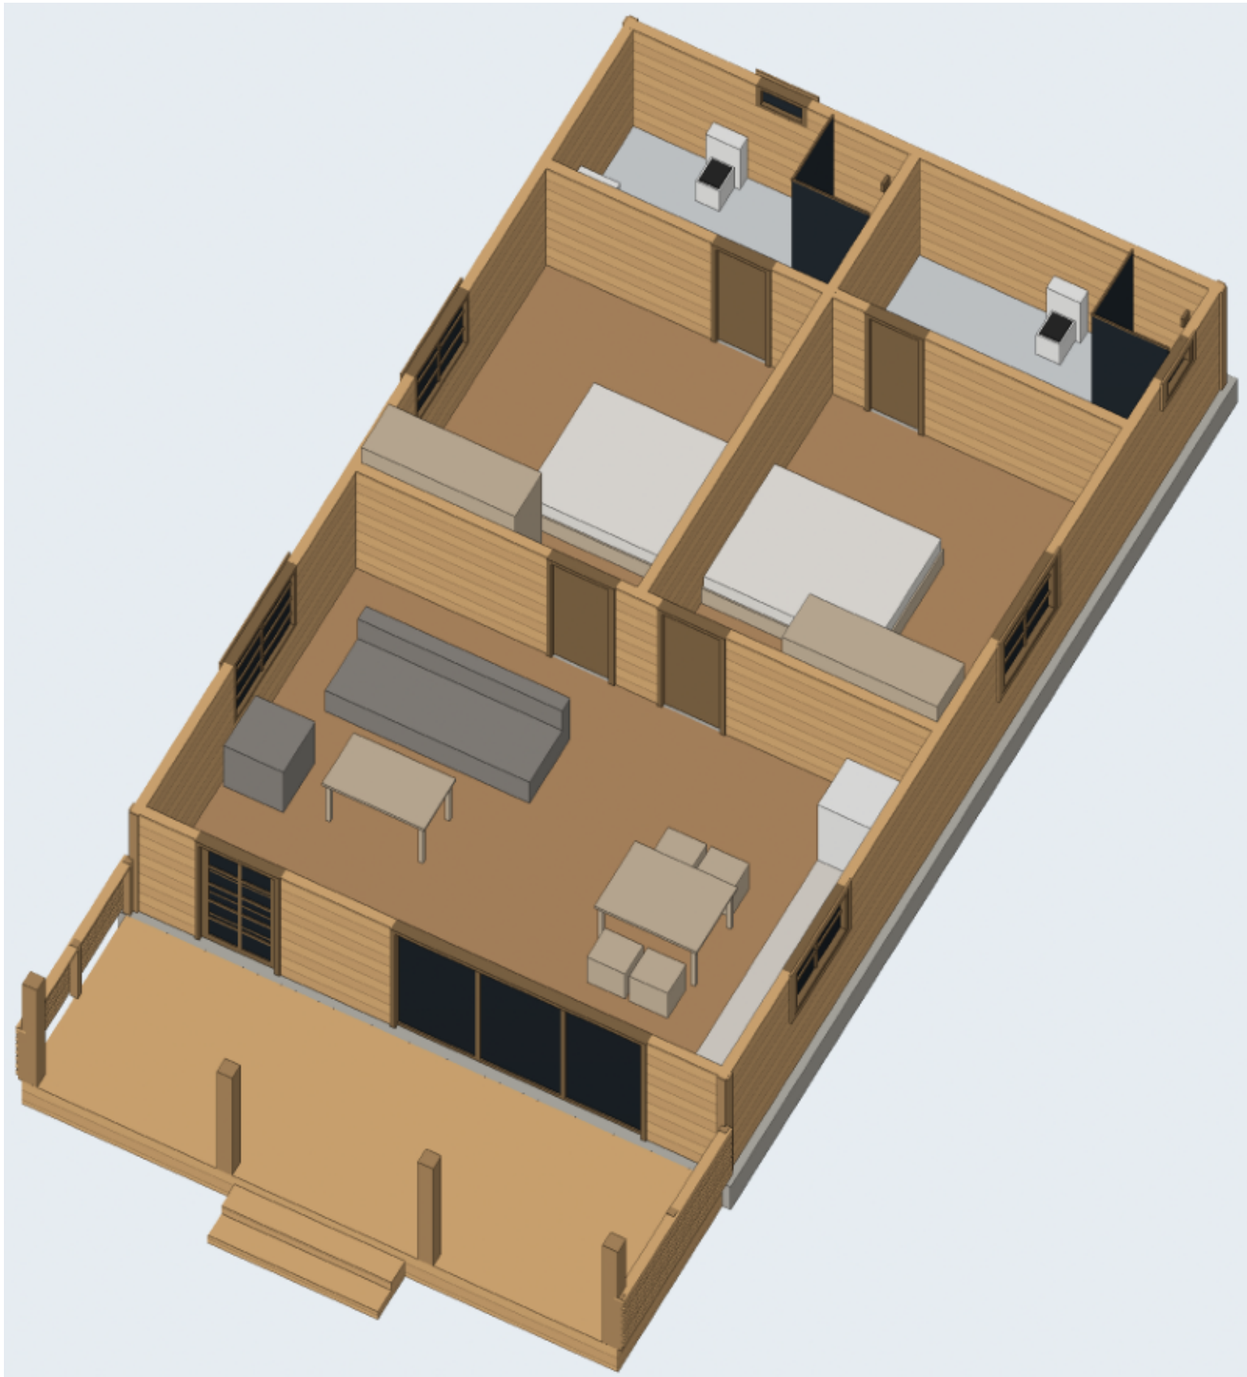


المشروع / العميل	عنوان اللوحة	المقياس	التاريخ	رقم اللوحة
مشروع 3 أكواخ استثمارية + لاندسكيب — أرض 25 × 36 م **عميل — مشروع استثماري**	**المقطع العلوي بالفرش**	**—**	**2026-10-19**	**A-09 (9/10)**

مصنع وتد الأخشاب
Watad Wood Factory

المنظور ثلاثي الأبعاد والمواد

النمط: جوزي غامق + إطارات سوداء — رندر واقعي بخامات حقيقية

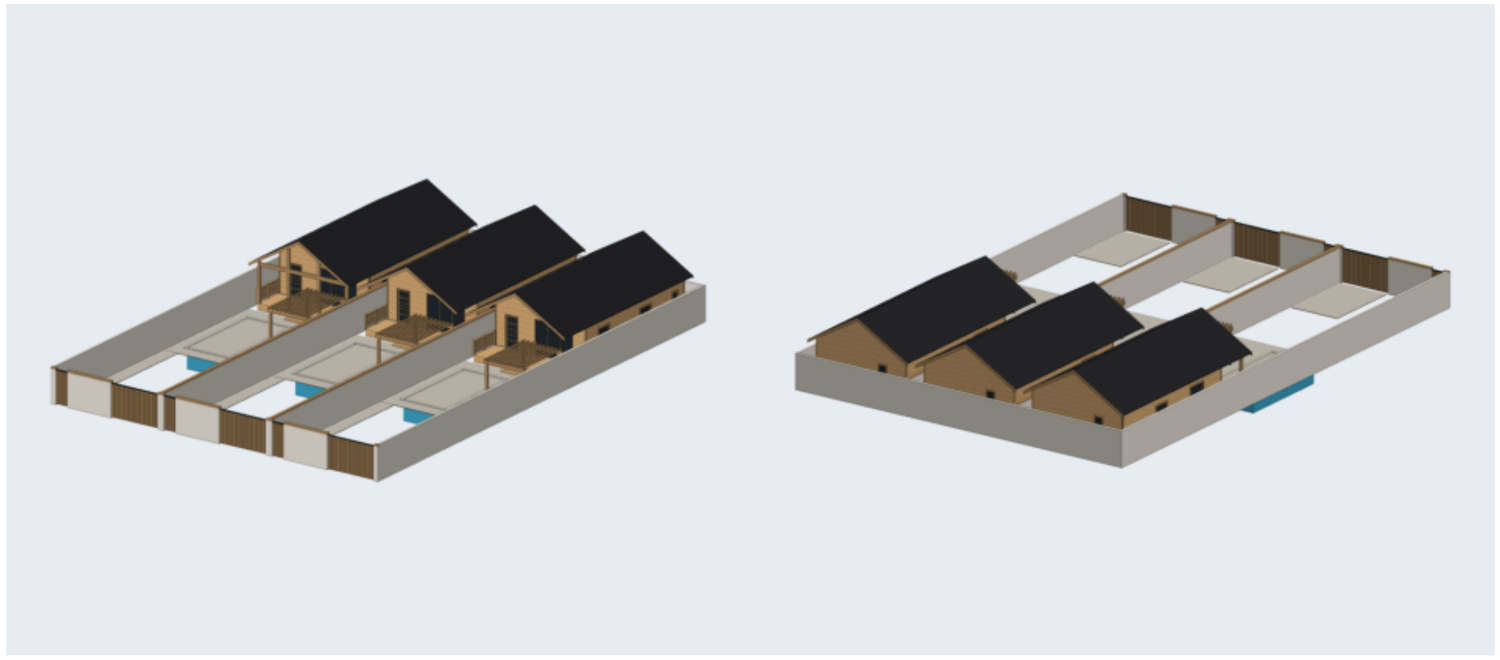

جدول المواد والألوان

الخشب / الصبغة

خشب طبيعي فاتح (بدون صبغة)

القرميد

قرميد رمادي غامق

الزجاج

زجاج عاكس غامق

إطارات الشبابيك والأبواب

إطار خشب بنفس الصبغة أغمق

الكنار والزوايا

نفس الصبغة أغمق درجة


الصبة

خرسانة 45 سم


الدربزين: ألواح أفقية متقاربة (عصري)

تقسيم الشبابيك: بدون | الباب الرئيسي: زجاج بتقسيمات (فرنسي)

أنواع الدربزين المعتمدة (من مشاريع المصنع)

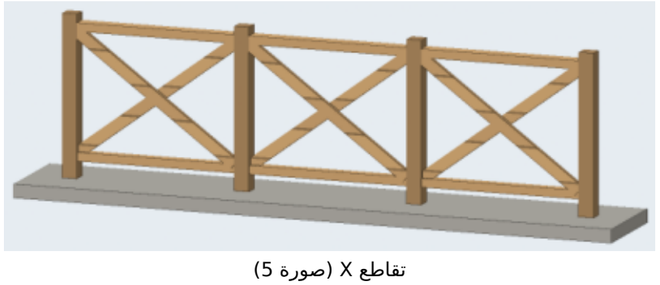

تقاطع X (صورة 5)

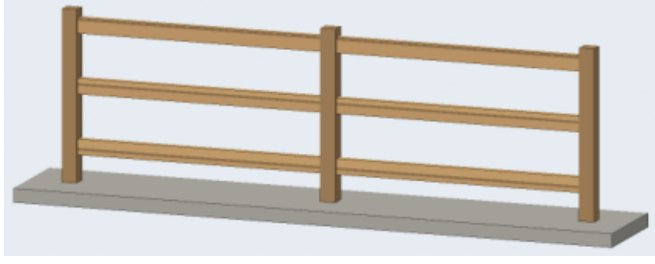

3 مرابيع أفقية (صورة 2)



قوائم رأسية متقاربة (صورة 1)

المشروع / العميل	عنوان اللوحة	المقياس	التاريخ	رقم اللوحة
مصنع وتد الأخشاب Watad Wood Factory **مشروع 3 أكواخ استثمارية + لاندسكيب — أرض 25 × 36 م** **عميل — مشروع استثماري**	**المنظور والمواد**	**—**	**2026-10-19**	**A-10 (10/10)**