
# المنظور ثلاثي الأبعاد والمواد

النمط: جوزي غامق + إطارات سوداء — رندر واقعي بخامات حقيقية

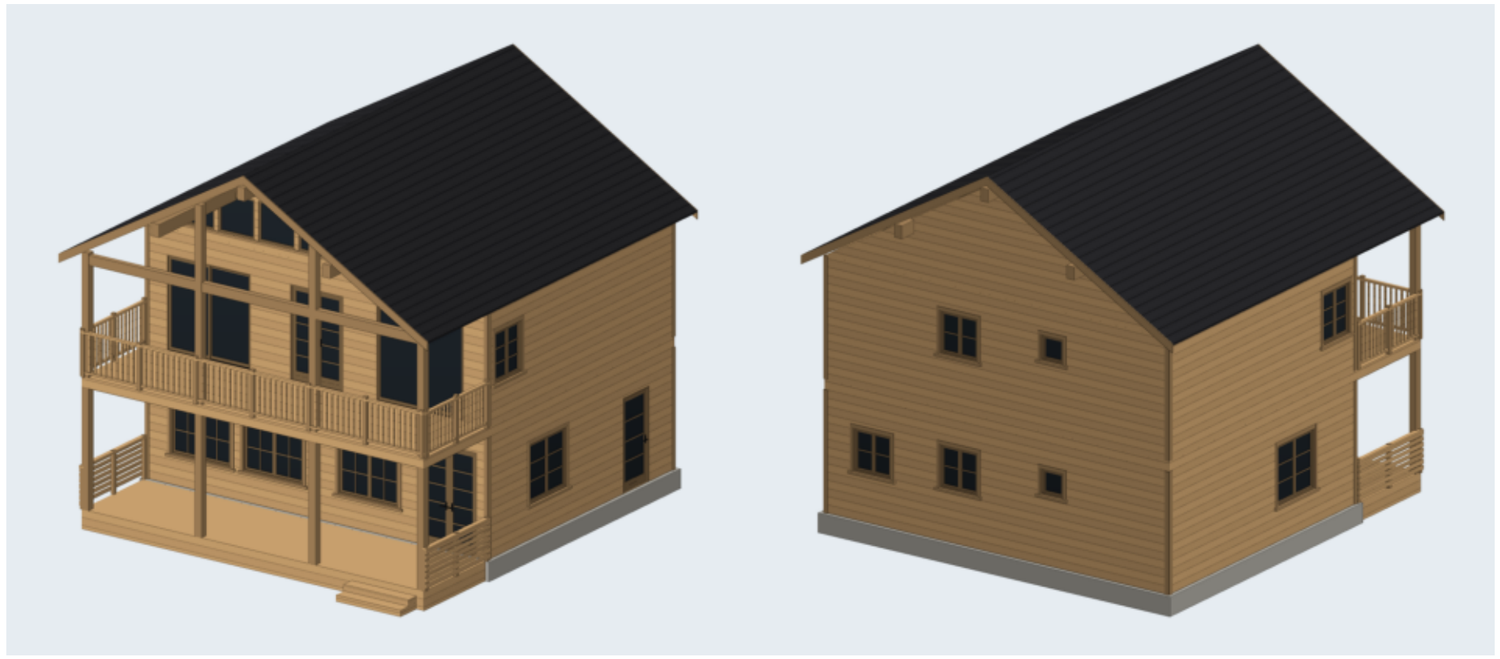

## جدول المواد والألوان

**الخشب / الصبغة**

خشب طبيعي فاتح (بدون صبغة)

**القرميد**

قرميد رمادي غامق

**الزجاج**

زجاج عاكس غامق

**إطارات الشبابيك والأبواب**

إطار خشب بنفس الصبغة أغمق

**الكنار والزوايا**

نفس الصبغة أغمق درجة


**الصبة**

خرسانة 45 سم


الدربزين: ألواح أفقية متقاربة (عصري)

تقسيم الشبابيك: بدون | الباب الرئيسي: زجاج بتقسيمات (فرنسي)

## أنواع الدربزين المعتمدة (من مشاريع المصنع)

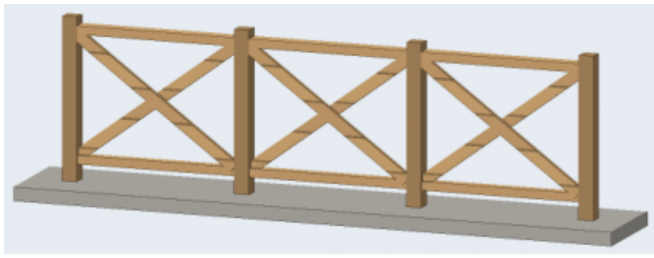

تقاطع X (صورة 5)

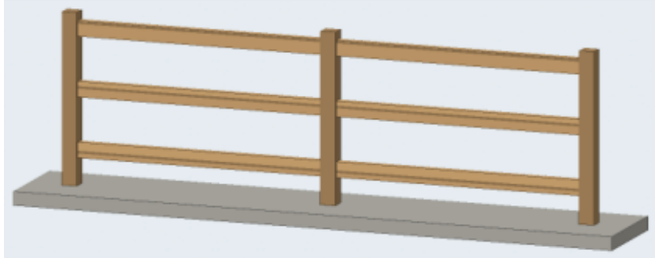

3 مرابيع أفقية (صورة 2)




قوائم رأسية متقاربة (صورة 1)

| المشروع / العميل | عنوان اللوحة | المقياس | التاريخ | رقم اللوحة |
|---|---|---|---|---|
| **فيلا خشب دورين — مجلس + غرفتين — 9.00 × 7.00 م (63 م² للدور)**<br>**عميل — تبوك** | **المنظور والمواد** | **1:50** | **2026-10-24** | **W-01 (1/21)** |

**مصنع وتد الأخشاب**
Watad Wood Factory

# المسقط الأفقي مع الفرش — الدور الأرضي

الأبعاد بالسنتيمتر - الجدران: قوائم 7×5 + تلبيس 2.5 من الجهتين (12 سم) | منسوب الأرضية +0.00

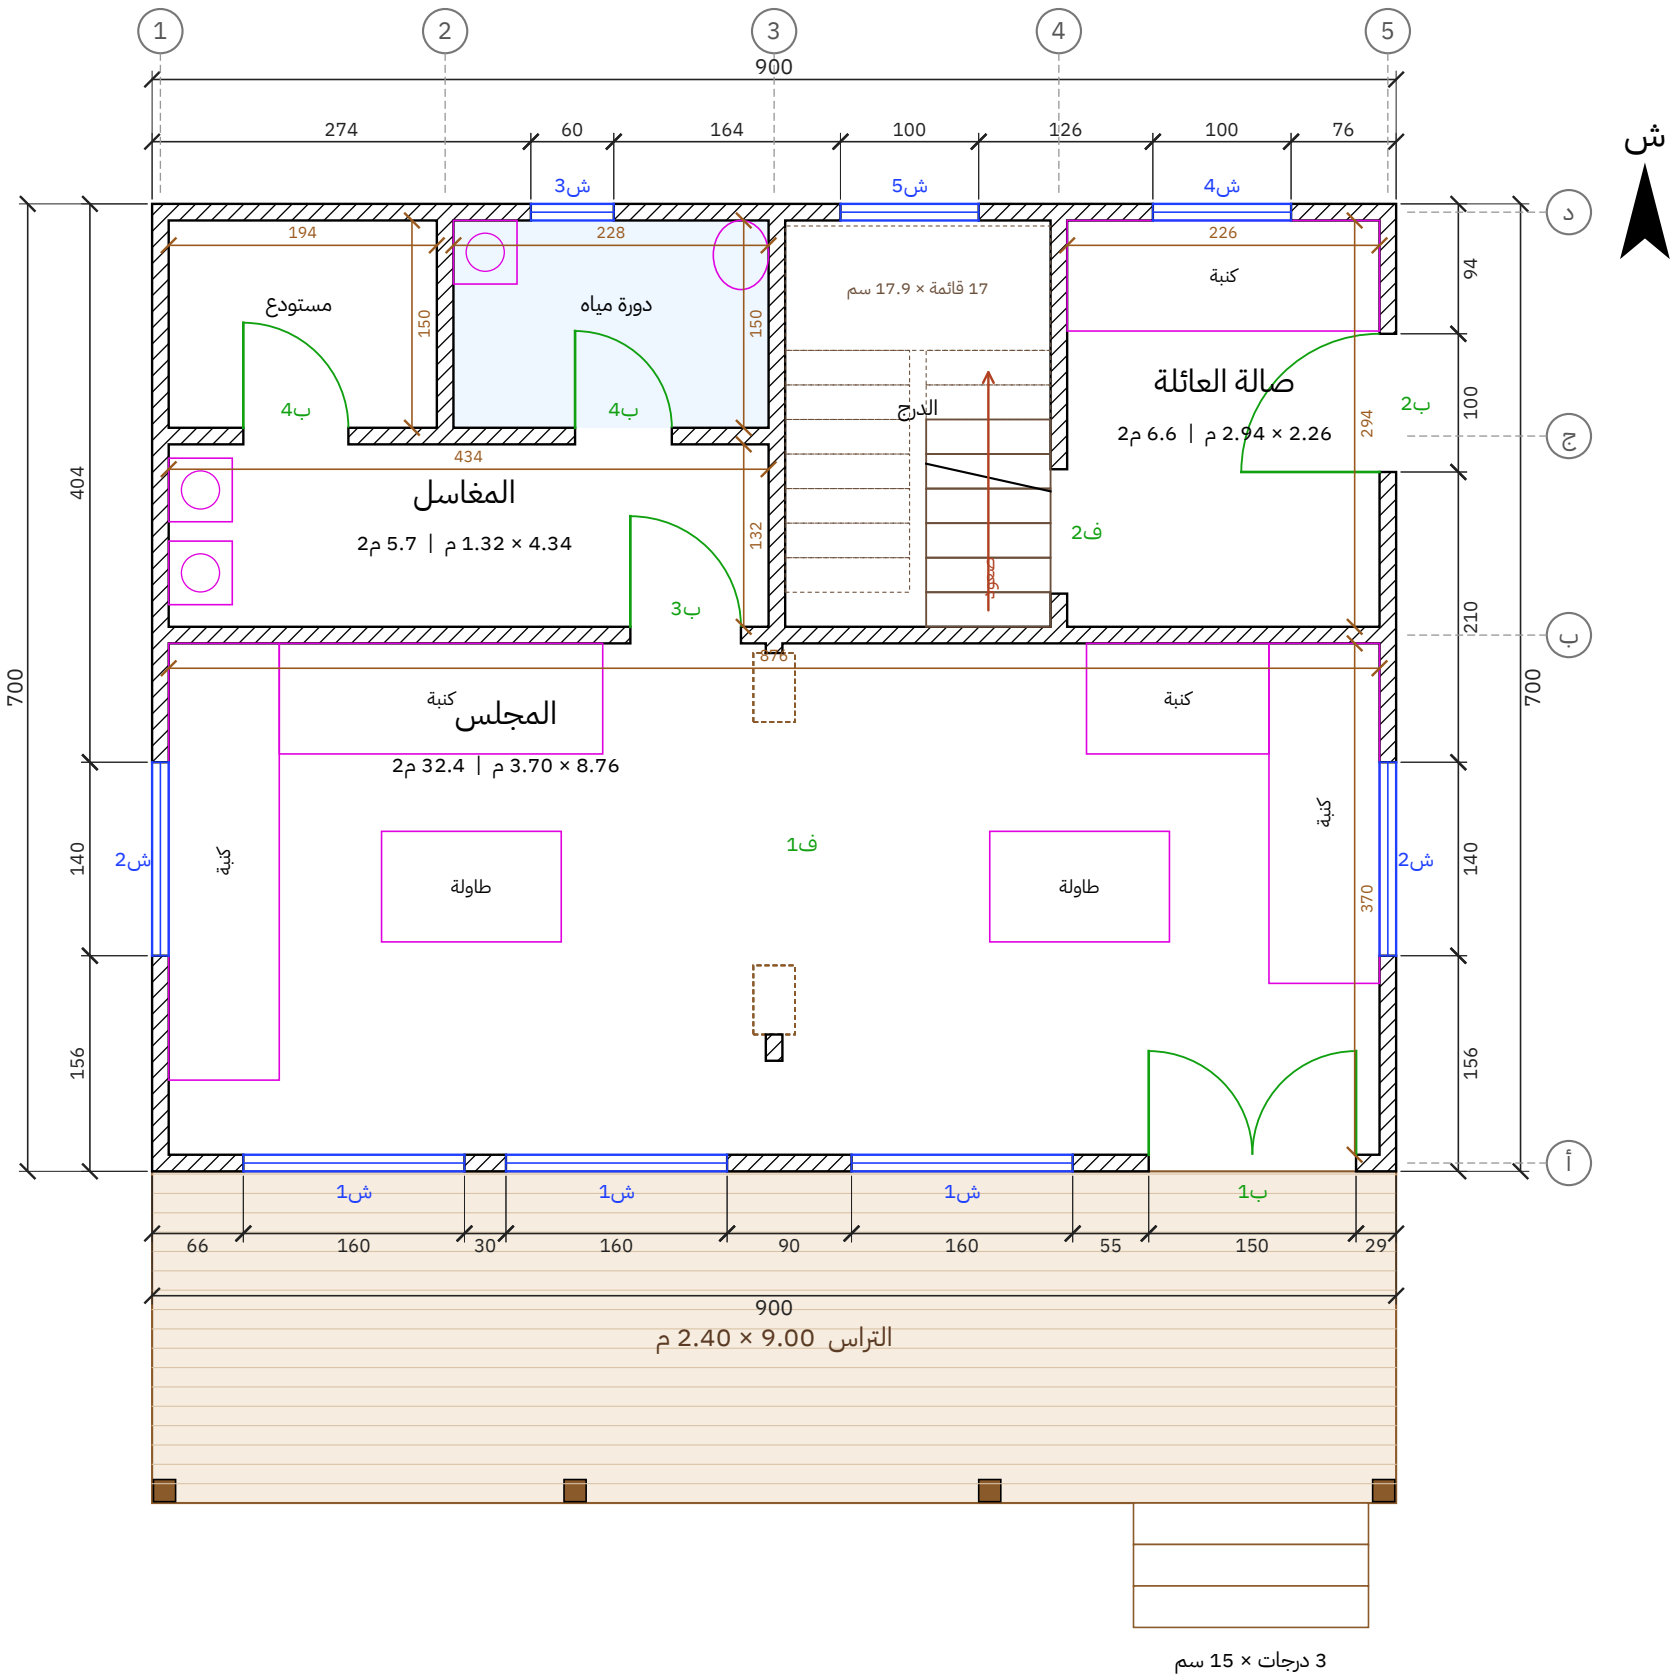



| المشروع / العميل | عنوان اللوحة | المقياس | التاريخ | رقم اللوحة |
|---|---|---|---|---|
| فيلا خشب دورين — مجلس + غرفتين — 9.00 × 7.00 م (63 م² للدور)<br>عميل — تبوك | المسقط الأفقي — الدور الأرضي | 1:50 | 2026-10-24 | W-02 (2/21) |


مصنع وتد الأخشاب
Watad Wood Factory

المسقط الأفقي مع الفرش — الدور الأول

الأبعاد بالسنتيمتر - الجدران: قوائم 7×5 + تلبيس 2.5 من الجهتين (12 سم) | منسوب الأرضية +3.05

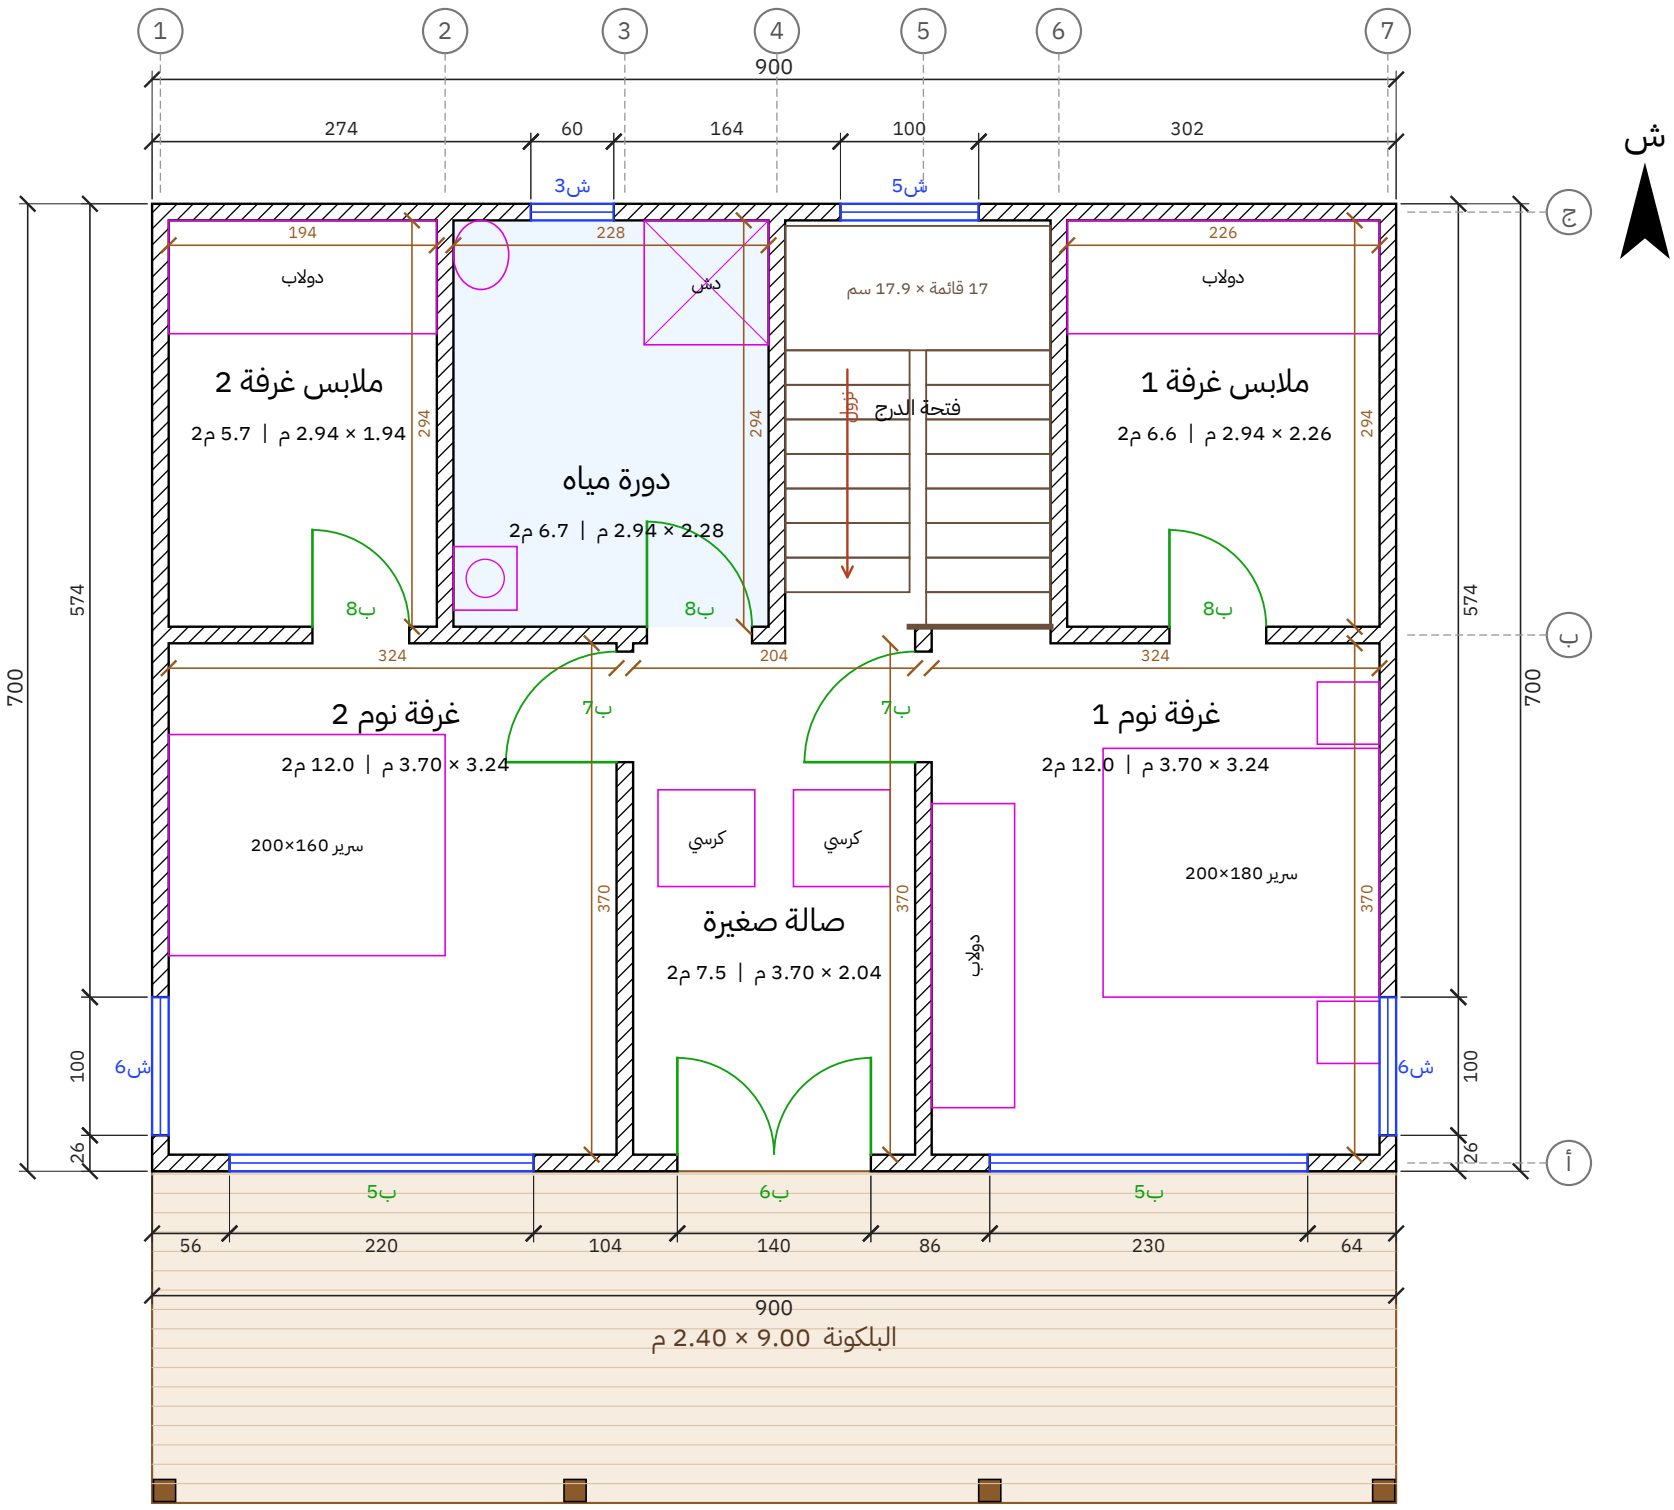



| | | | | | |
|---|---|---|---|---|---|
| مصنع وتد الأخشاب<br>Watad Wood Factory | المشروع / العميل<br>فيلا خشب دورين — مجلس + غرفتين — 9.00 × 7.00 م (63 م² للدور)<br>عميل — تبوك | عنوان اللوحة<br>المسقط الأفقي — الدور الأول | المقياس<br>1:50 | التاريخ<br>2026-10-24 | رقم اللوحة<br>W-03 (3/21) |

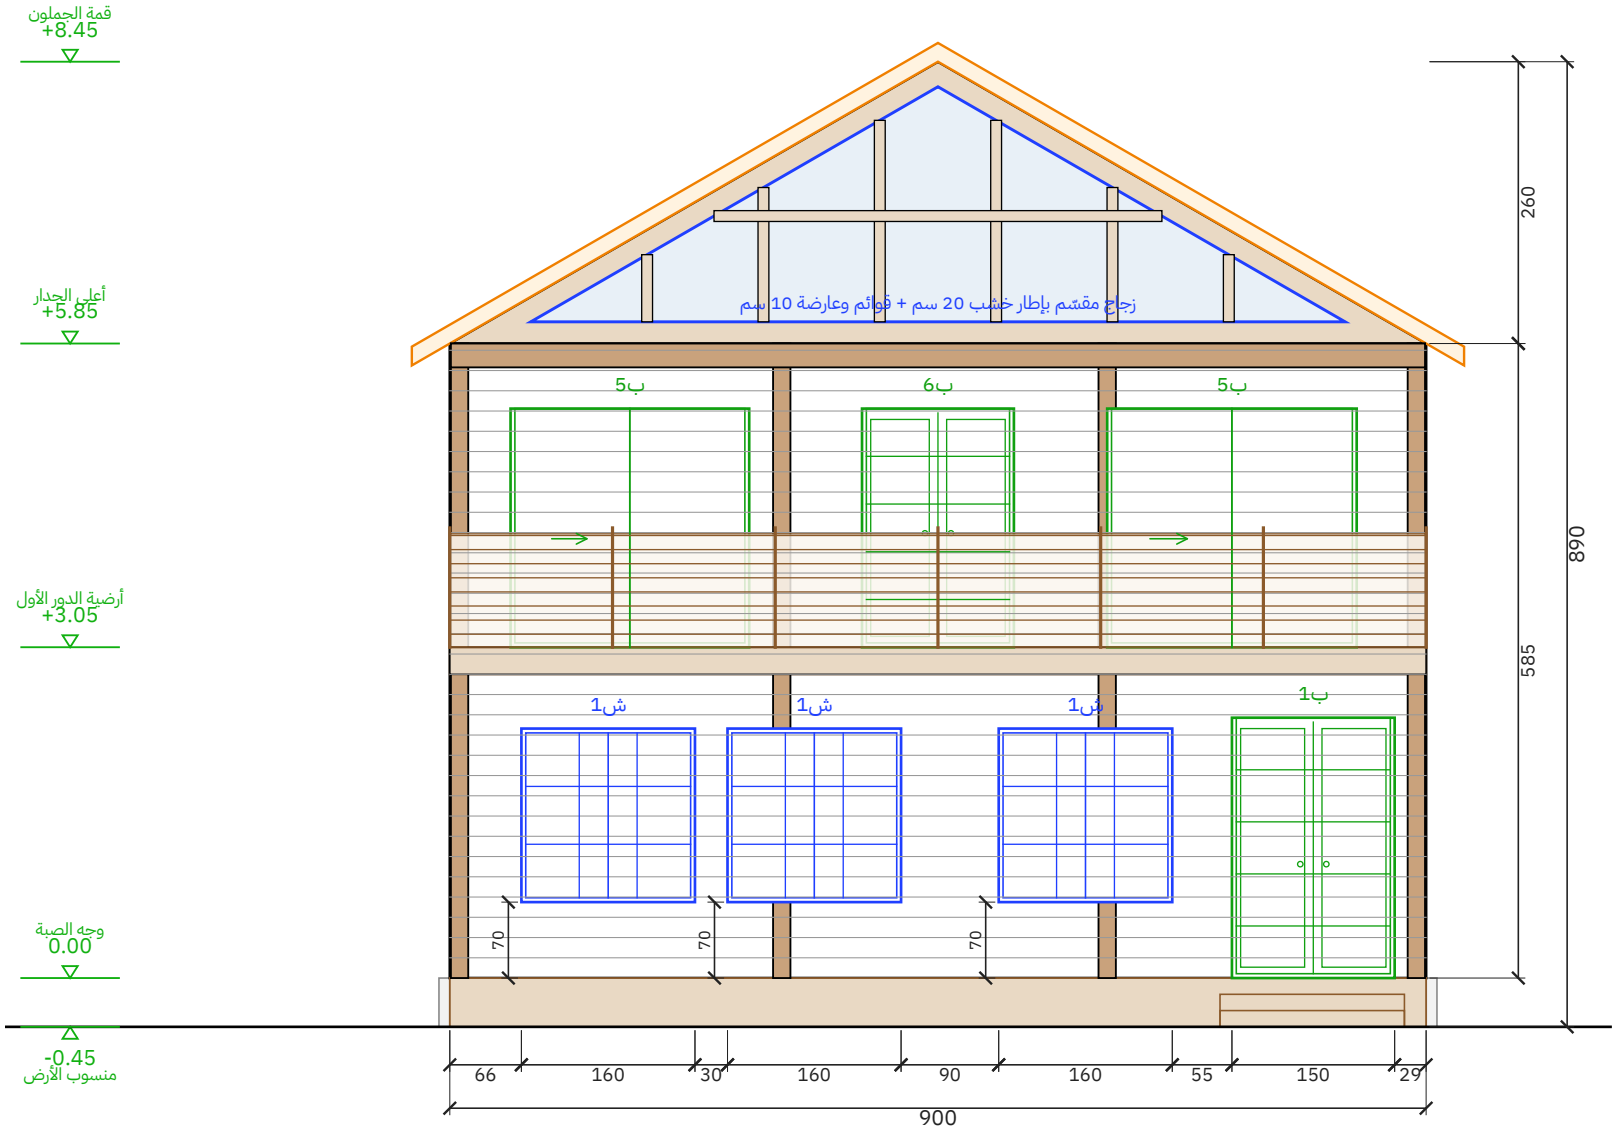


## الواجهة الأمامية


مقياس 1:50 | الوحدة: سم

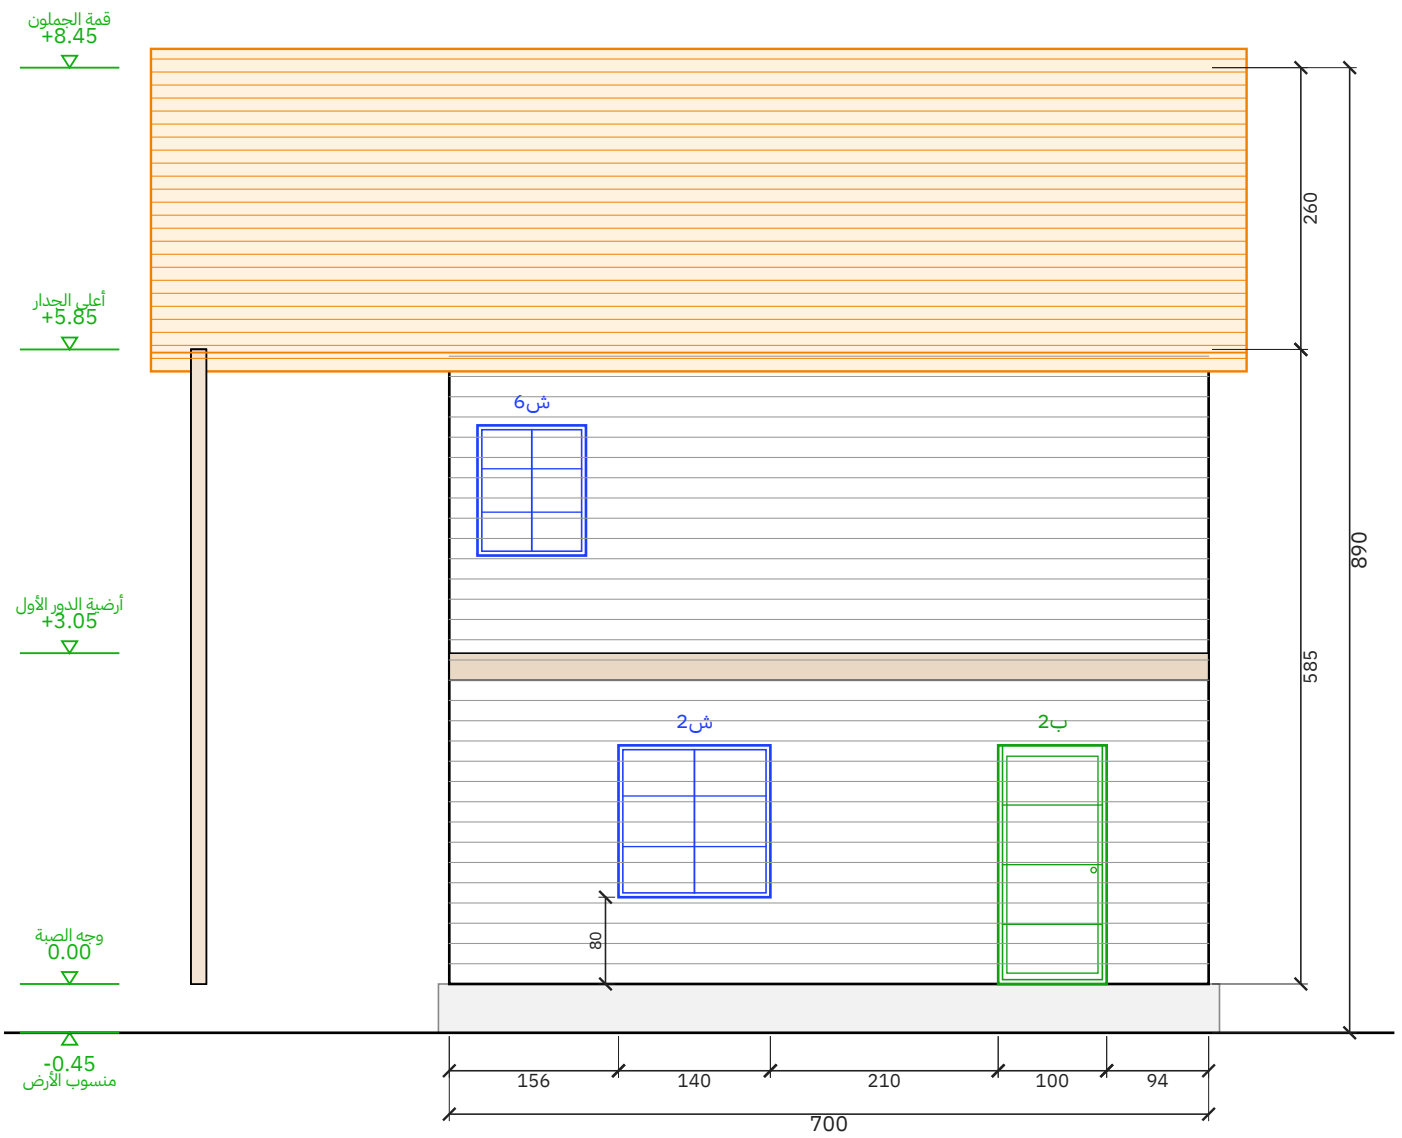


## الواجهة الشرقية


مقياس 1:50 | الوحدة: سم

| المشروع / العميل | عنوان اللوحة | المقياس | التاريخ | رقم اللوحة |
|---|---|---|---|---|
| مصنع وتد الأخشاب<br>Watad Wood Factory<br>فيلا خشب دورين – مجلس + غرفتين – 9.00 × 7.00 م (63 م² للدور)<br>عميل – تبوك | الواجهة الأمامية والواجهة الشرقية | 1:50 | 2026-10-24 | W-04 (4/21) |

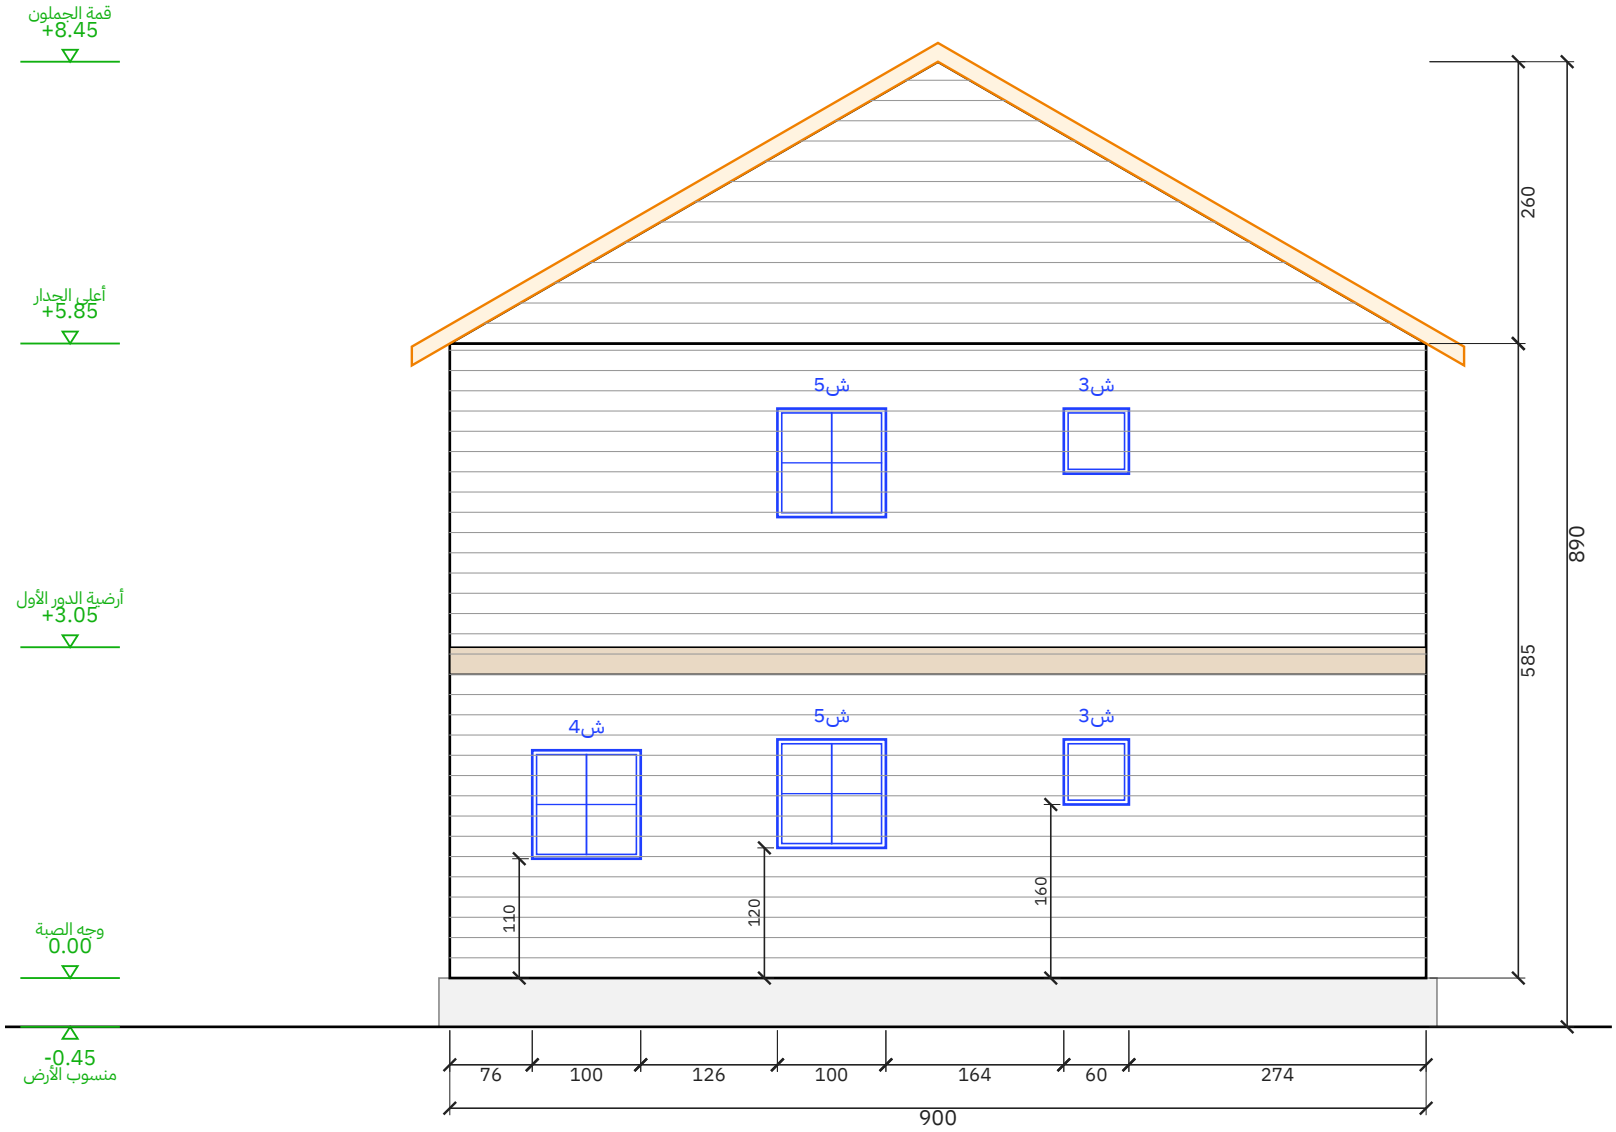


## الواجهة الخلفية

مقياس 1:50 | الوحدة: سم

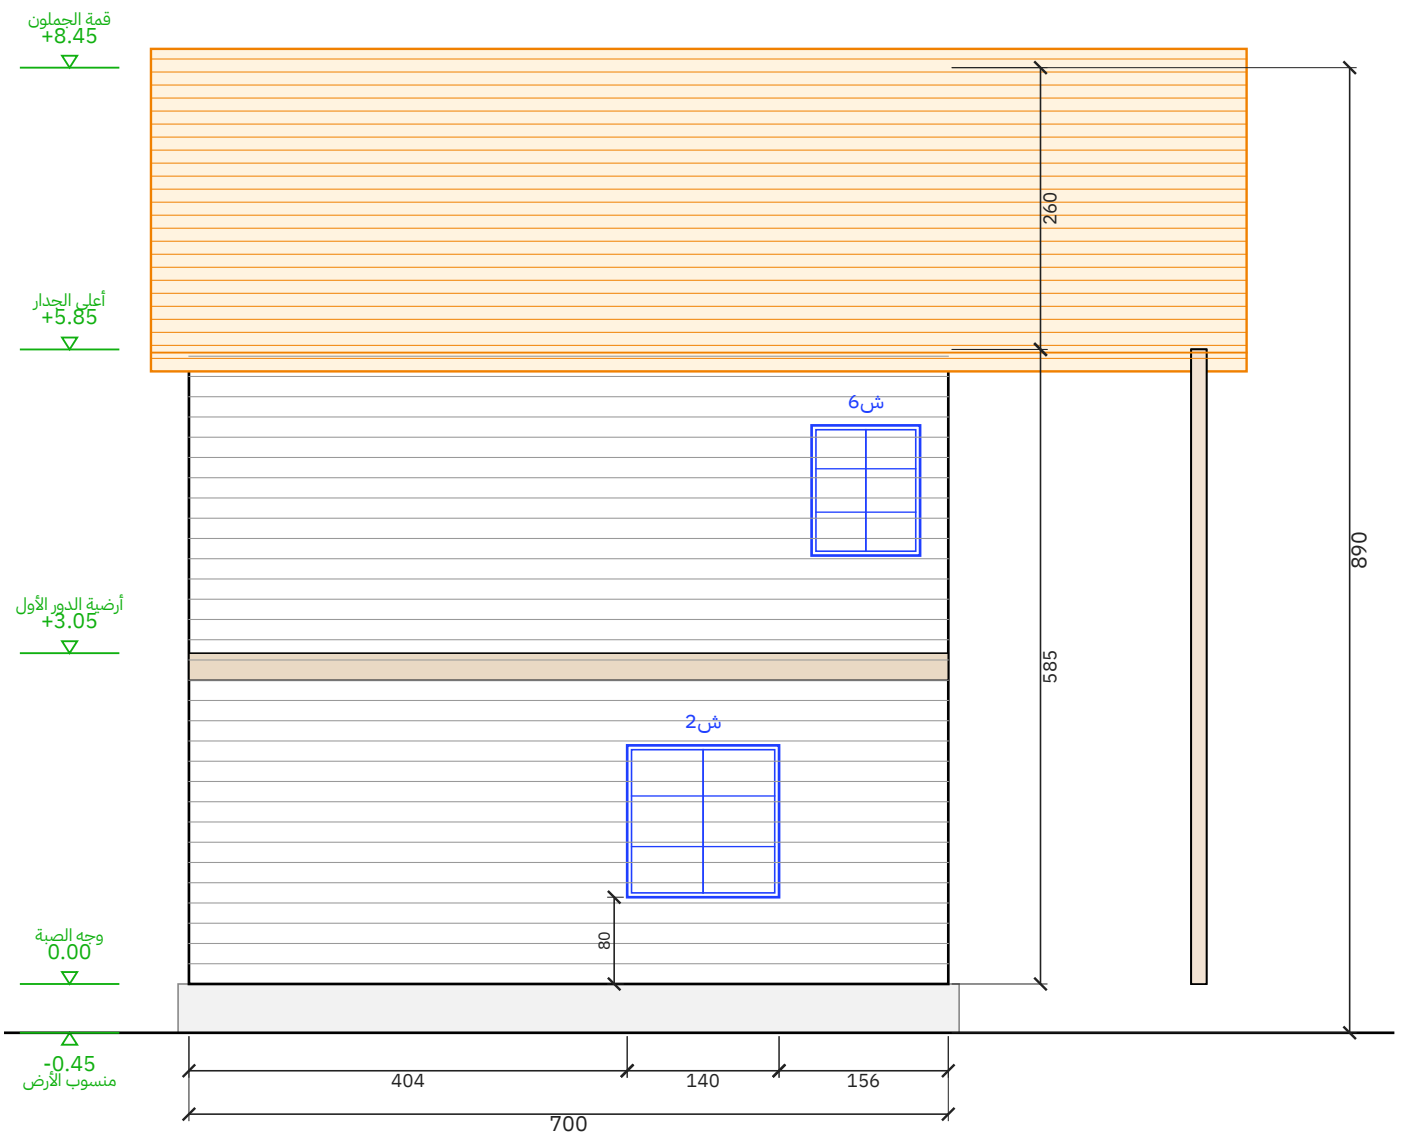


## الواجهة الغربية


مقياس 1:50 | الوحدة: سم

| المشروع / العميل | عنوان اللوحة | المقياس | التاريخ | رقم اللوحة |
|---|---|---|---|---|
| فيلا خشب دورين – مجلس + غرفتين – 9.00 × 7.00 م (63 م² للدور)<br>عميل – تبوك | الواجهة الخلفية والواجهة الغربية | 1:50 | 2026-10-24 | W-05 (5/21) |


مصنع وتد الأخشاب
Watad Wood Factory

## قطاع عرضي أ-أ

مقياس 1:50 | الوحدة: سم

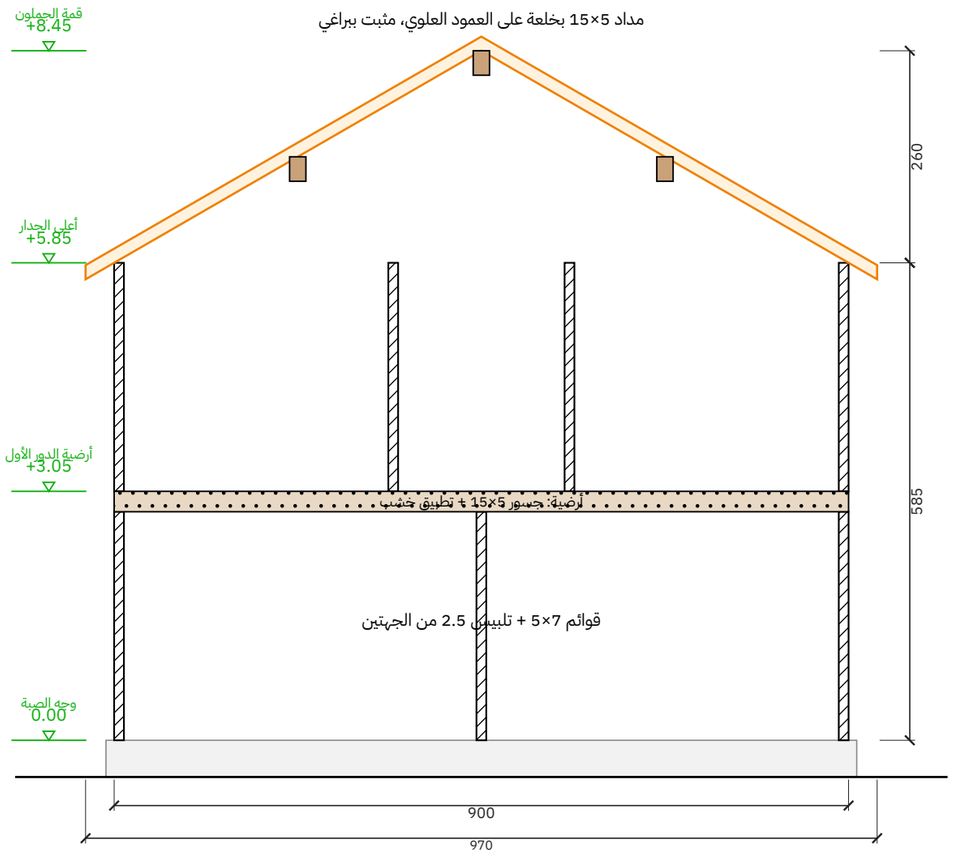



تفصيلة جلوس المداد على العلوي (1:5)

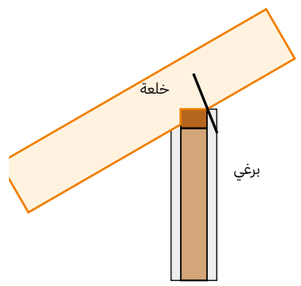


علوي 7×5 على قائم 7×5

## مسقط السقف (جملون)

رفرف 35 سم من كل جهة | مقياس 1:50

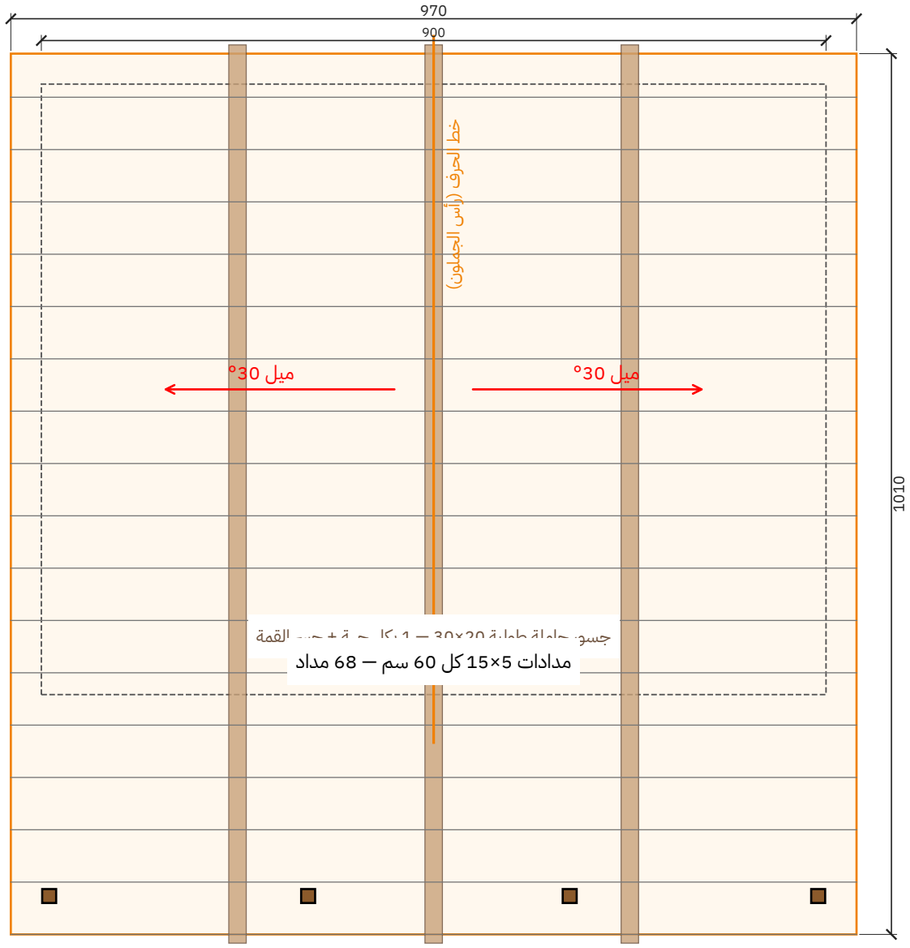


| | | | | |
|---|---|---|---|---|
| المشروع / العميل: فيلا خشب دورين — مجلس + غرفتين — 9.00 × 7.00 م (63 م² للدور) — عميل — تبوك | عنوان اللوحة: مسقط السقف والقطاع | المقياس: — | التاريخ: 2026-10-24 | رقم اللوحة: W-06 (6/21) |

مصنع وتد الأخشاب
Watad Wood Factory

# جدول مقاسات الأبواب والشبابيك

## مقاس الفتحة الصافي في الجدار - الوحدة: سم

| الرمز | النوع | العرض (سم) | الارتفاع (سم) | ارتفاع الجلسة (سم) | العدد | الموقع |
|---|---|---|---|---|---|---|
| ب1 | باب مزدوج | 150 | 240 | - | 1 | الأمامية |
| ب2 | باب | 100 | 220 | - | 1 | الشرقية |
| ب3 | باب | 80 | 220 | - | 1 | المجلس — المغاسل |
| ب4 | باب | 76 | 210 | - | 1 | المستودع |
| ب4 | باب | 70 | 210 | - | 1 | دورة المياه |
| ب5 | باب مزدوج | 220 | 220 | - | 1 | الأمامية (على البلكونة) |
| ب5 | باب مزدوج | 230 | 220 | - | 1 | الأمامية (على البلكونة) |
| ب6 | باب مزدوج | 140 | 220 | - | 1 | الأمامية (على البلكونة) |
| ب7 | باب | 80 | 210 | - | 2 | غرفة 2 - غرفة 1 |
| ب8 | باب | 70 | 210 | - | 2 | ملابس غرفة 2 - ملابس غرفة 1 |
| ب8 | باب | 76 | 210 | - | 1 | دورة المياه |
| ف1 | باب | 276 | 250 | - | 1 | بارتشن مفتوح بعمودين مكتبة |
| ف2 | باب | 90 | 220 | - | 1 | صالة العائلة — الدرج |
| ش1 | شباك | 160 | 160 | 70 | 3 | الأمامية 3 |
| ش2 | شباك | 140 | 140 | 80 | 2 | الشرقية - الغربية |
| ش3 | شباك | 60 | 60 | 160 | 2 | الخلفية 2 |
| ش4 | شباك | 100 | 100 | 110 | 1 | الخلفية |
| ش5 | شباك | 100 | 100 | 120 | 2 | الخلفية 2 |
| ش6 | شباك | 100 | 120 | 90 | 2 | الشرقية - الغربية |

الإجمالي: أبواب 15 - شبابيك 12

# جدول المساحات وبيانات المشروع والتسعير

## بيانات المشروع

| البند | البيان |
|---|---|
| المشروع | فيلا خشب دورين — مجلس + غرفتين — 9.00 × 7.00 م (63 م² للدور) |
| العميل | عميل — تبوك |
| الموقع | تبوك |
| الاستخدام | سكن — مجلس ضيوف + غرفتين |
| التاريخ | 2026-10-24 |
| نظام البناء | هيكل خشب 5×7 + تلبيس 2.5 سم من الجهتين |
| السقف | جملون 30° — قرميد معدني |

## جدول المساحات

| م | الفراغ | الأبعاد (م) | المساحة (م2) |
|---|---|---|---|
| 1 | أرضي — المجلس | 3.70 × 8.76 | 32.41 |
| 2 | أرضي — المغاسل | 1.32 × 4.34 | 5.73 |
| 3 | أرضي — مستودع | 1.50 × 1.94 | 2.91 |
| 4 | أرضي — دورة مياه | 1.50 × 2.28 | 3.42 |
| 5 | أرضي — الدرج | 2.94 × 1.92 | 5.64 |
| 6 | أرضي — صالة العائلة | 2.94 × 2.26 | 6.64 |
| 7 | أول — غرفة نوم 2 | 3.70 × 3.24 | 11.99 |
| 8 | أول — صالة صغيرة | 3.70 × 2.04 | 7.55 |
| 9 | أول — غرفة نوم 1 | 3.70 × 3.24 | 11.99 |
| 10 | أول — ملابس غرفة 2 | 2.94 × 1.94 | 5.70 |
| 11 | أول — دورة مياه | 2.94 × 2.28 | 6.70 |
| 12 | أول — ملابس غرفة 1 | 2.94 × 2.26 | 6.64 |
|  | المساحة الصافية الداخلية |  | 107.34 |
|  | **التراس** | **9.00 × 2.40** | **21.60** |
|  | **البلكونة** | **9.00 × 2.40** | **21.60** |
|  | **المساحة الإجمالية المبنية** | **9.00 × 7.00 × 2 دور** | **126.00** |
|  | **المساحة الكلية (المبنية + التراس والبلكونة)** |  | **169.20** |


## التسعير المفصّل

| البند | المبلغ (ريال) |
|---|---|
| الكوخ المبني 126.00 م² × 1,096 | 138,096 |
| تراس الأرضي + بلكونة الأول (9.00 × 2.40 × 2) — 43.20 م² × 1,096 | 47,347 |
| **الإجمالي (ريال)** | **185,443** |


**ملاحظات:**

- السعر للدورين والتراس والبلكونة حسب المخطط المعتمد — التراس يُسعّر بنفس سعر متر الكوخ.
- الصبة والتمديدات الخارجية على العميل ما لم يُذكر غير ذلك.

## تأطير جدار أ-جنوب — الطول 888 سم، الارتفاع 280 سم

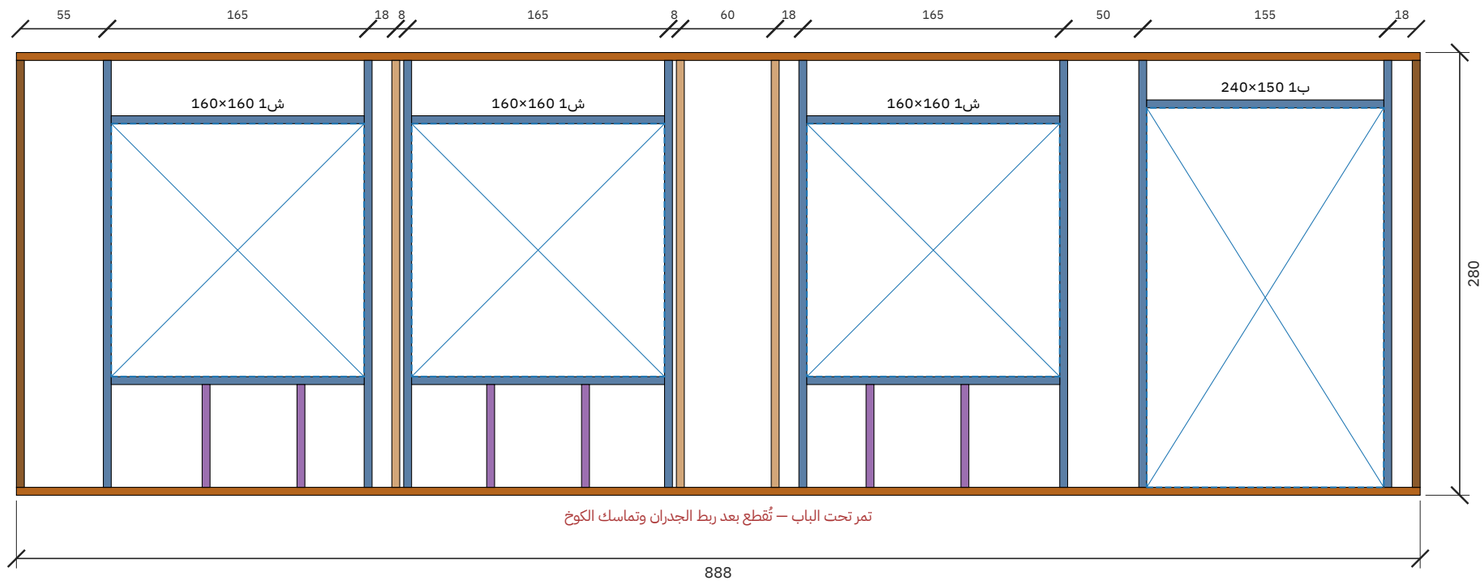


## تأطير جدار أ-شرق — الطول 688 سم، الارتفاع 280 سم

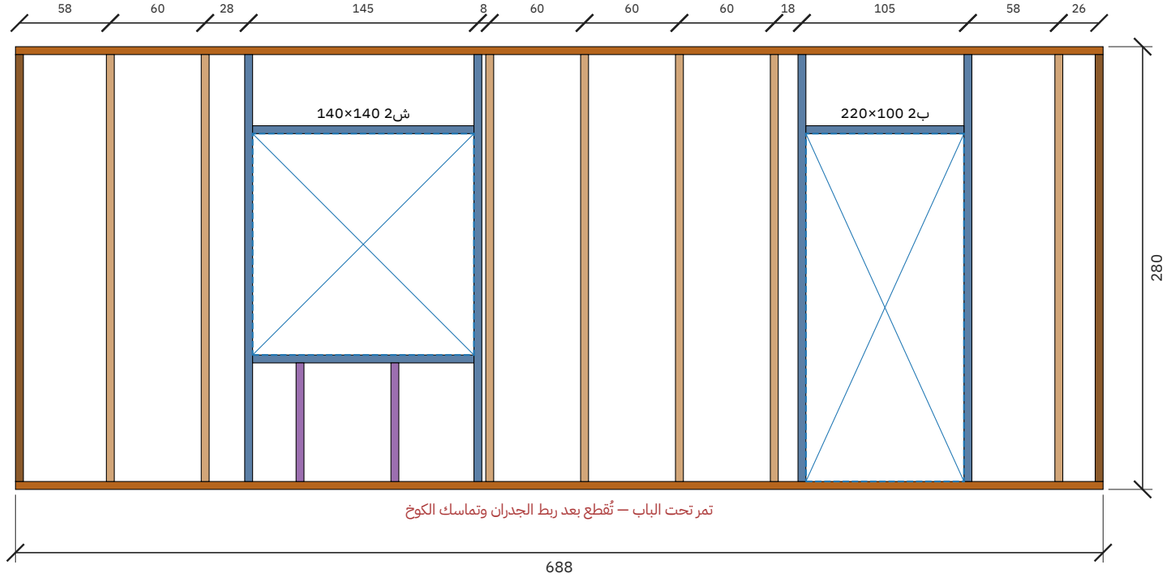



قاعدة سفلية | علوي | عمود | عمود زاوية | جنب فتحة | رأس فتحة | جلسة شباك | عمود قصير


| المشروع / العميل | عنوان اللوحة | المقياس | التاريخ | رقم اللوحة |
|---|---|---|---|---|
| فيلا خشب دورين — مجلس + غرفتين — 9.00 × 7.00 م (63 م² للدور)<br>عميل — تبوك | لوحات التأطير (للورشة) | — | 2026-10-24 | W-09 (9/21) |

مصنع وتد الأخشاب
Watad Wood Factory

## تأطير جدار أ-شمال — الطول 888 سم، الارتفاع 280 سم

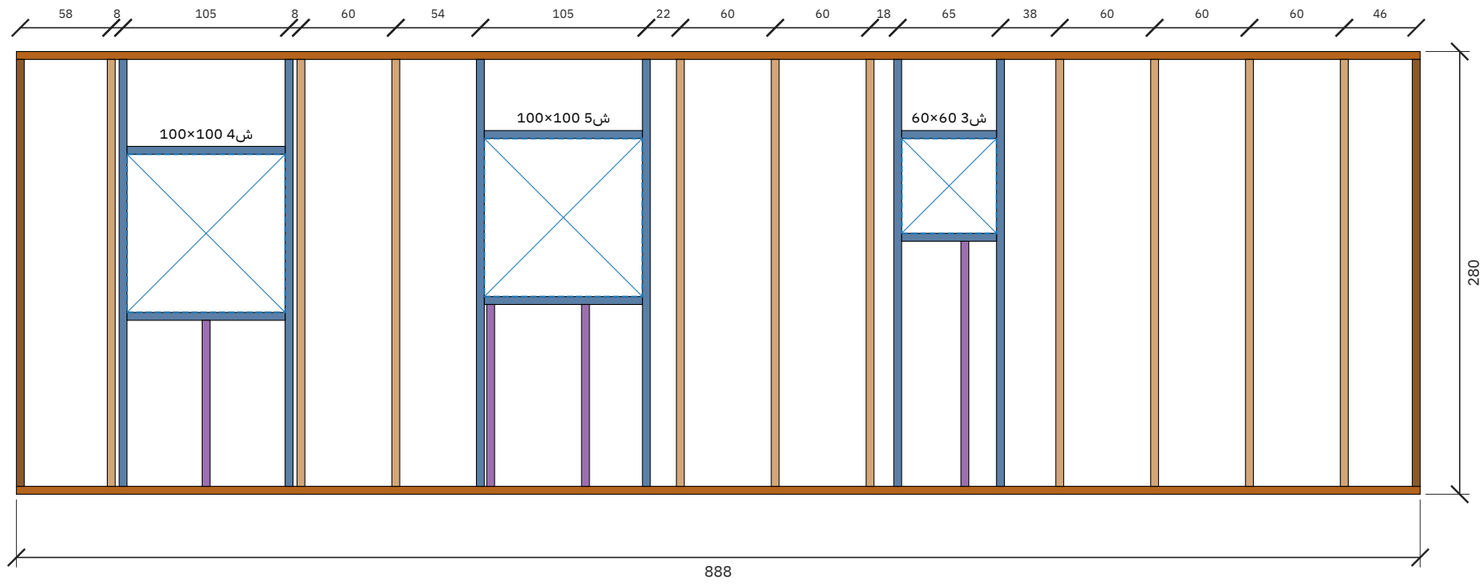


## تأطير جدار أ-غرب — الطول 688 سم، الارتفاع 280 سم

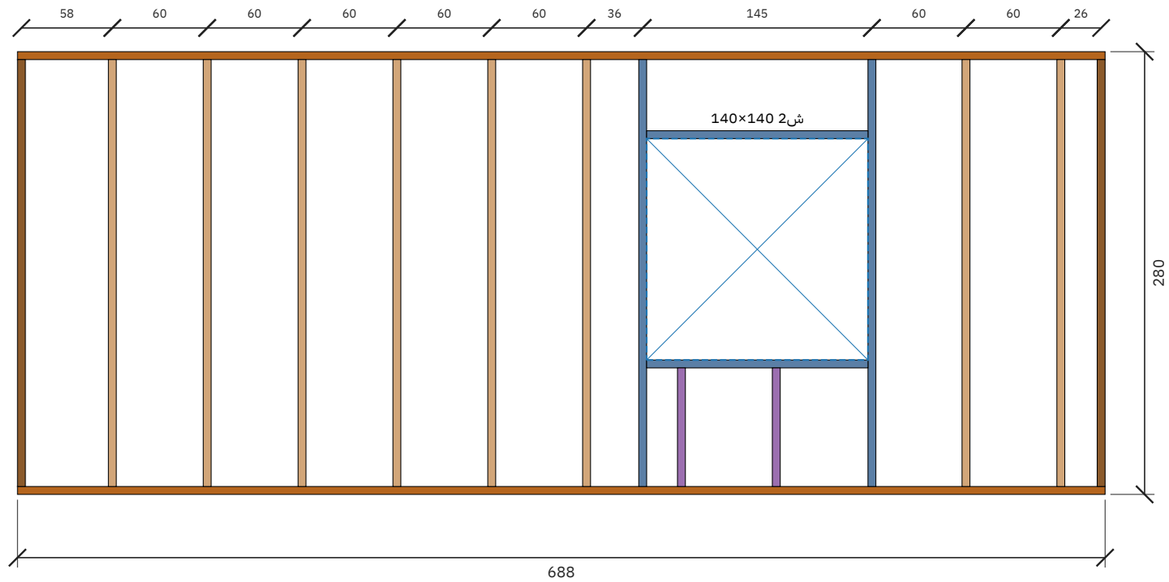



قاعدة سفلية — علوي — عمود — عمود زاوية — جنب فتحة — رأس فتحة — جلسة شباك — عمود قصير


| المشروع / العميل | عنوان اللوحة | المقياس | التاريخ | رقم اللوحة |
|---|---|---|---|---|
| **فيلا خشب دورين — مجلس + غرفتين — 9.00 × 7.00 م (63 م² للدور)**<br>**عميل — تبوك** | **لوحات التأطير (للورشة)** | **—** | **2026-10-24** | **W-10 (10/21)** |

**مصنع وتد الأخشاب**
Watad Wood Factory

## تأطير جدار أ-خلف المجلس — الطول 888 سم، الارتفاع 280 سم (داخلي)

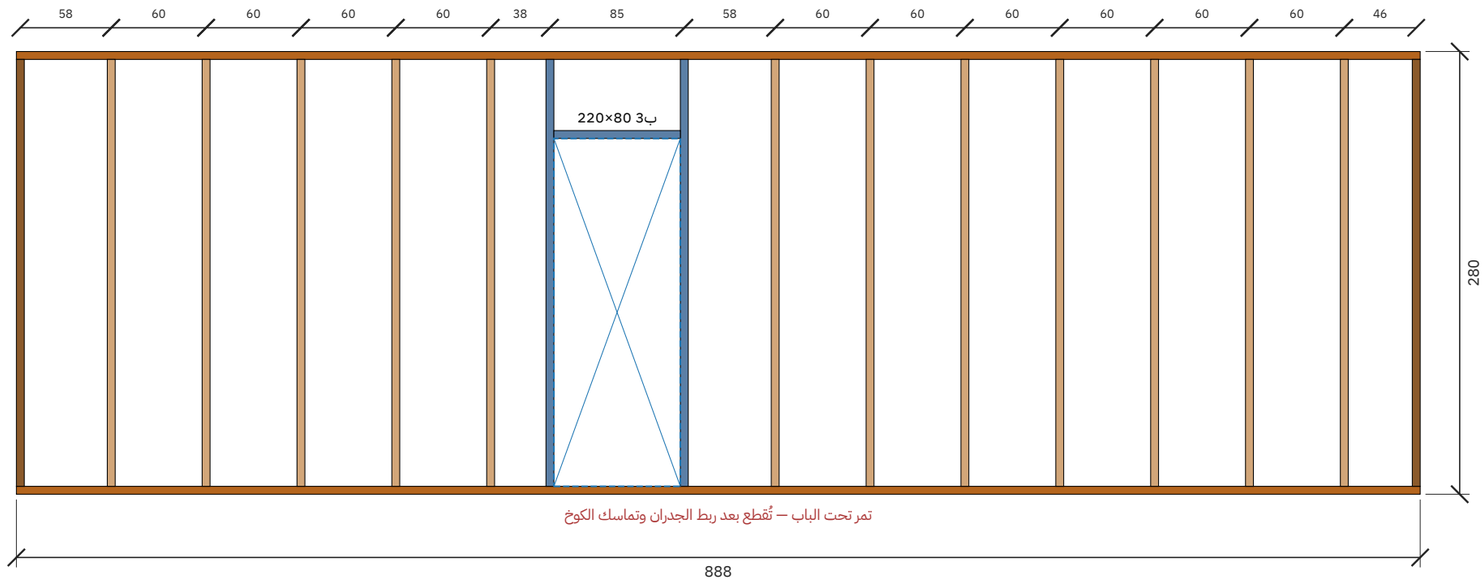



## تأطير جدار أ-بارتشن المجلس — الطول 302 سم، الارتفاع 280 سم (داخلي)

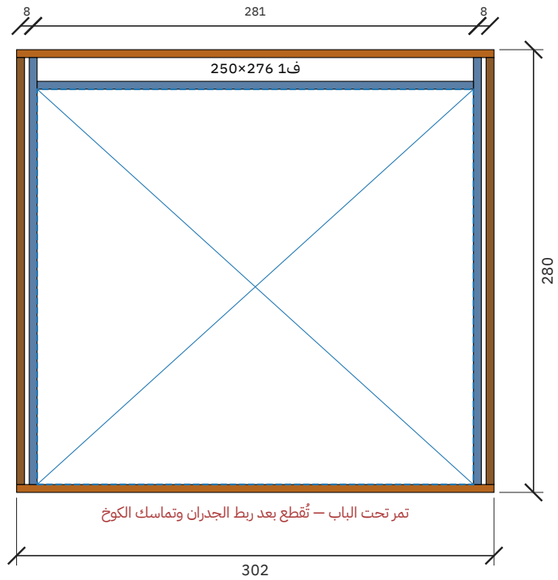



قاعدة سفلية | علوي | عمود | عمود زاوية | جنب فتحة | رأس فتحة | جلسة شباك | عمود قصير

| | | | | |
|---|---|---|---|---|
| مصنع وتد الأخشاب<br>Watad Wood Factory | المشروع / العميل<br>**فيلا خشب دورين — مجلس + غرفتين — 9.00 × 7.00 م (63 م² للدور)**<br>**عميل — تبوك** | عنوان اللوحة<br>**لوحات التأطير (للورشة)** | المقياس<br>**—** | التاريخ<br>**2026-10-24** | رقم اللوحة<br>**W-11 (11/21)** |

## تأطير جدار أ-جدار الدرج الغربي — الطول 306 سم، الارتفاع 280 سم (داخلي)

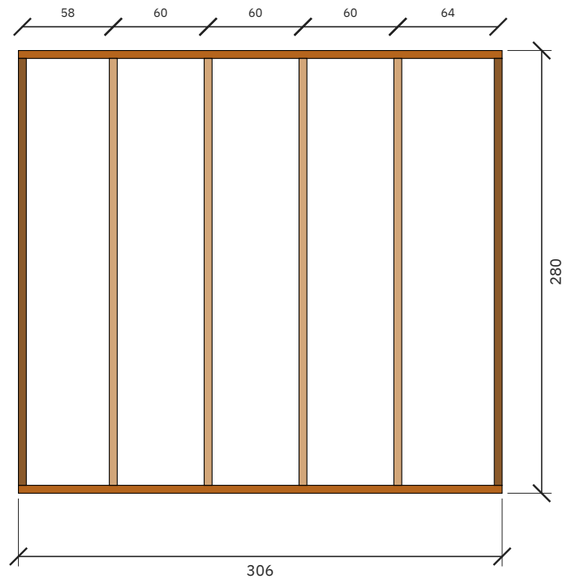


## تأطير جدار أ-جدار الدرج الشرقي — الطول 306 سم، الارتفاع 280 سم (داخلي)

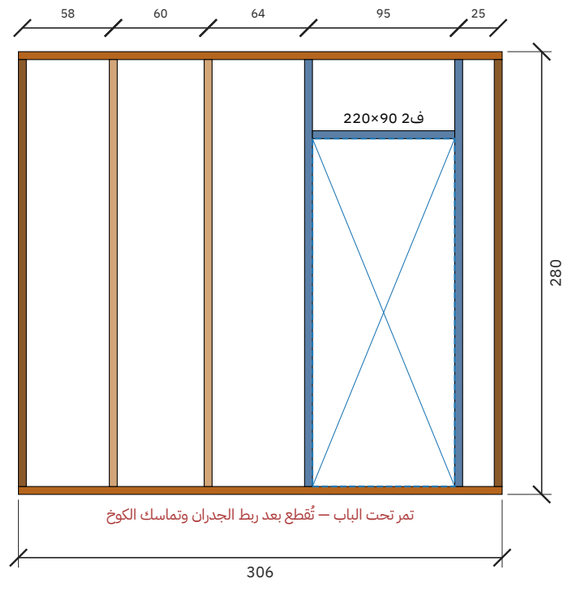



قاعدة سفلية | علوي | عمود | عمود زاوية | جنب فتحة | رأس فتحة | جلسة شباك | عمود قصير


| المشروع / العميل | عنوان اللوحة | المقياس | التاريخ | رقم اللوحة |
|---|---|---|---|---|
| **فيلا خشب دورين — مجلس + غرفتين — 9.00 × 7.00 م (63 م² للدور)**<br>**عميل — تبوك** | **لوحات التأطير (للورشة)** | **—** | **2026-10-24** | **W-12 (12/21)** |

**مصنع وتد الأخشاب**
Watad Wood Factory

## تأطير جدار أ-فاصل المغاسل — الطول 446 سم، الارتفاع 280 سم (داخلي)

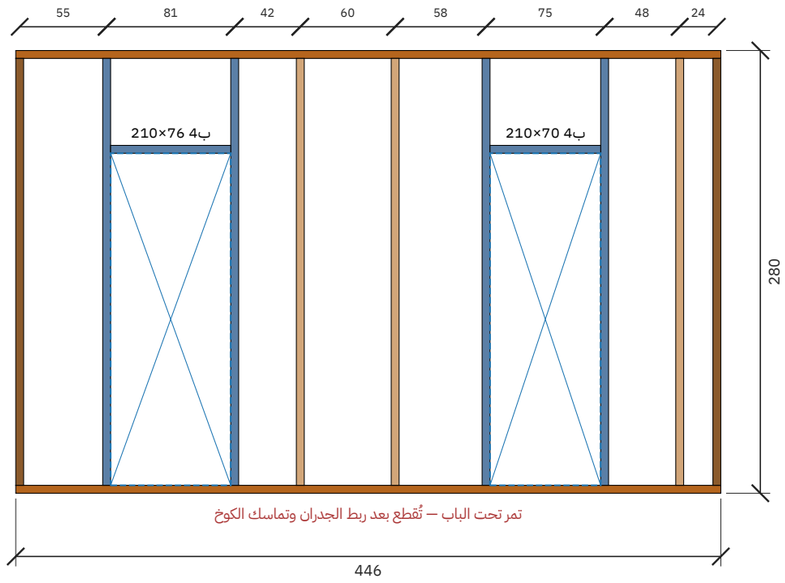


## تأطير جدار أ-جدار الدورة — الطول 162 سم، الارتفاع 280 سم (داخلي)

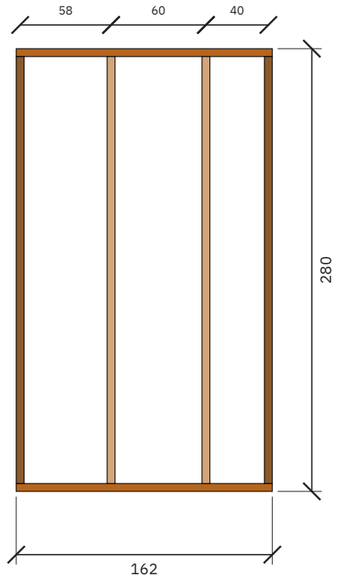



قاعدة سفلية | علوي | عمود | عمود زاوية | جنب فتحة | رأس فتحة | جلسة شباك | عمود قصير


| المشروع / العميل | عنوان اللوحة | المقياس | التاريخ | رقم اللوحة |
|---|---|---|---|---|
| **فيلا خشب دورين — مجلس + غرفتين — 9.00 × 7.00 م (63 م² للدور)**<br>**عميل — تبوك** | **لوحات التأطير (للورشة)** | **—** | **2026-10-24** | **W-13 (13/21)** |

مصنع وتد الأخشاب
Watad Wood Factory

## تأطير جدار ب-جنوب — الطول 888 سم، الارتفاع 280 سم

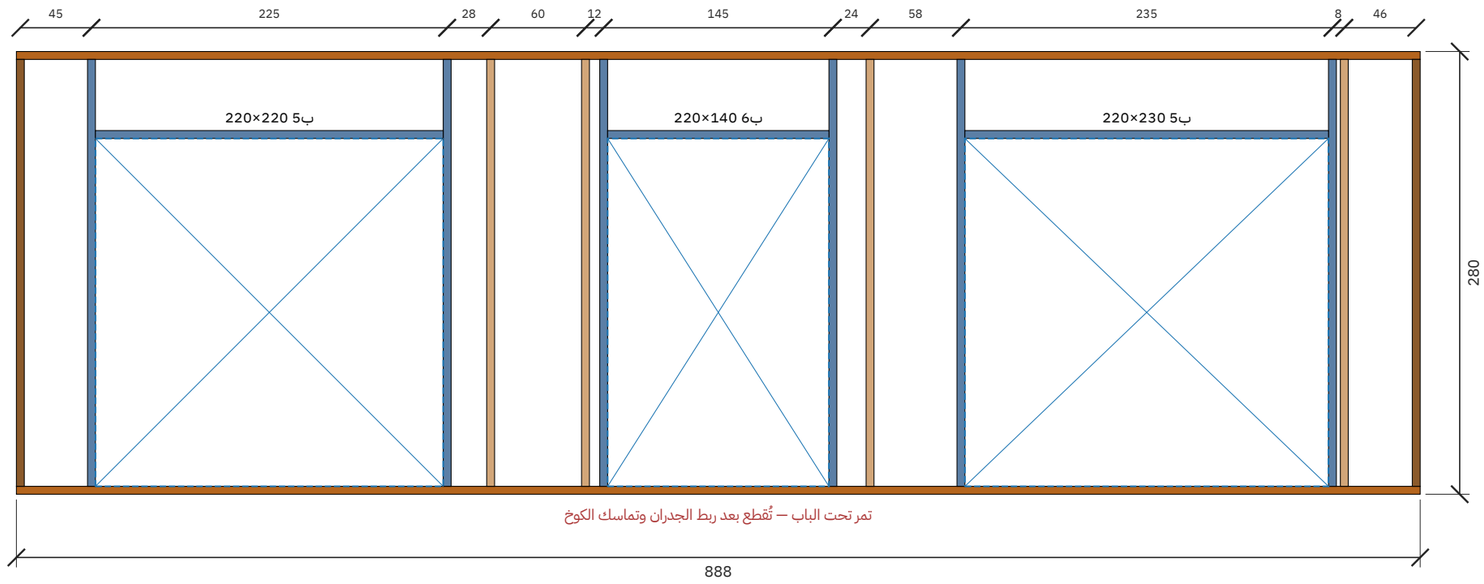


## تأطير جدار ب-شرق — الطول 688 سم، الارتفاع 280 سم

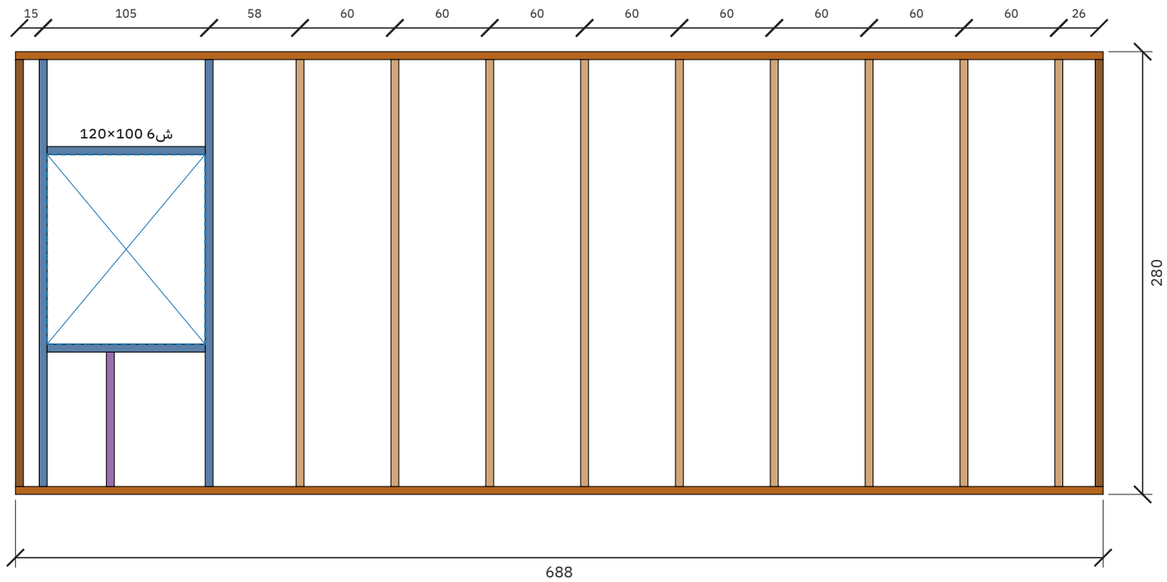



قاعدة سفلية | علوي | عمود | عمود زاوية | جنب فتحة | رأس فتحة | جلسة شباك | عمود قصير


| المشروع / العميل | عنوان اللوحة | المقياس | التاريخ | رقم اللوحة |
|---|---|---|---|---|
| فيلا خشب دورين — مجلس + غرفتين — 9.00 × 7.00 م (63 م² للدور)<br>عميل — تبوك | لوحات التأطير (للورشة) | — | 2026-10-24 | W-14 (14/21) |

مصنع وتد الأخشاب
Watad Wood Factory

## تأطير جدار ب-شمال — الطول 888 سم، الارتفاع 280 سم

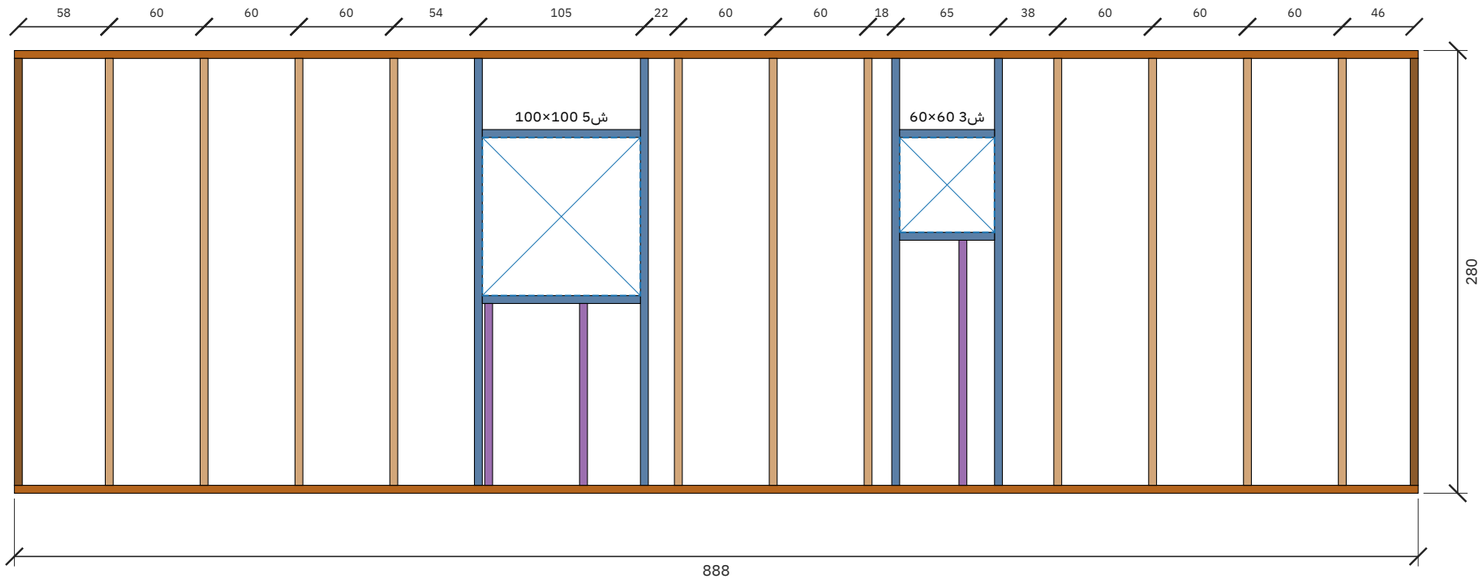



## تأطير جدار ب-غرب — الطول 688 سم، الارتفاع 280 سم

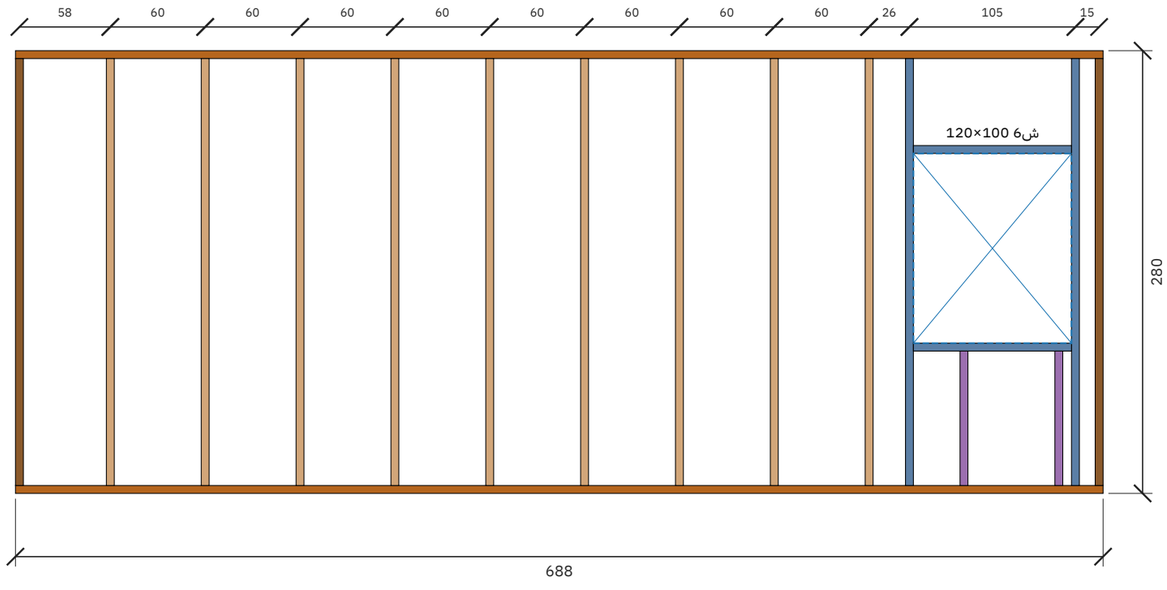



قاعدة سفلية | علوي | عمود | عمود زاوية | جنب فتحة | رأس فتحة | جلسة شباك | عمود قصير

| | | | | | |
|---|---|---|---|---|---|
| مصنع وتد الأخشاب<br>Watad Wood Factory | المشروع / العميل<br>فيلا خشب دورين — مجلس + غرفتين — 9.00 × 7.00 م (63 م² للدور)<br>عميل — تبوك | عنوان اللوحة<br>لوحات التأطير (للورشة) | المقياس<br>— | التاريخ<br>2026-10-24 | رقم اللوحة<br>W-15 (15/21) |

## تأطير جدار ب-جدار غرفة 2 — الطول 382 سم، الارتفاع 280 سم (داخلي)

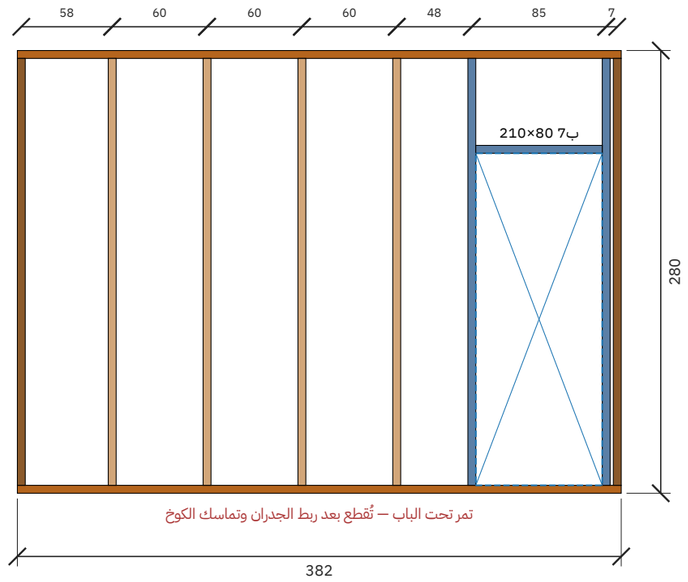



## تأطير جدار ب-جدار غرفة 1 — الطول 382 سم، الارتفاع 280 سم (داخلي)

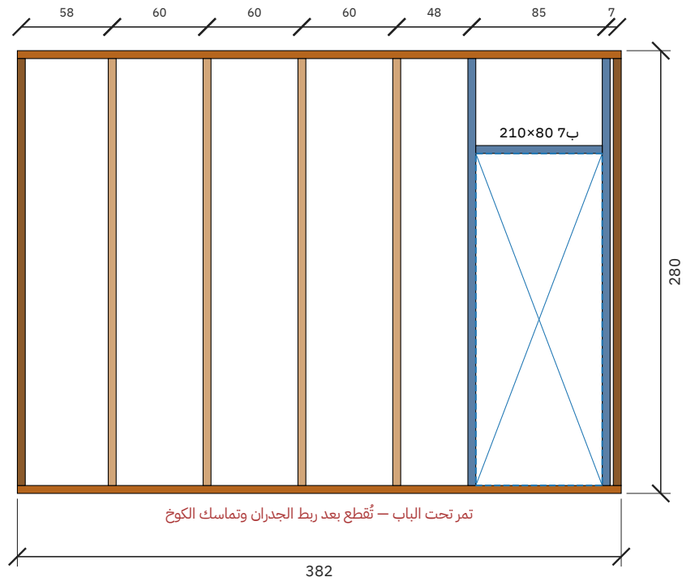



قاعدة سفلية | علوي | عمود | عمود زاوية | جنب فتحة | رأس فتحة | جلسة شباك | عمود قصير

| | | | | | |
|---|---|---|---|---|---|
| مصنع وتد الأخشاب<br>Watad Wood Factory | المشروع / العميل<br>فيلا خشب دورين — مجلس + غرفتين — 9.00 × 7.00 م (63 م² للدور)<br>عميل — تبوك | عنوان اللوحة<br>لوحات التأطير (للورشة) | المقياس<br>— | التاريخ<br>2026-10-24 | رقم اللوحة<br>W-16 (16/21) |

## تأطير جدار ب-خلف الغرف غرب — الطول 446 سم، الارتفاع 280 سم (داخلي)

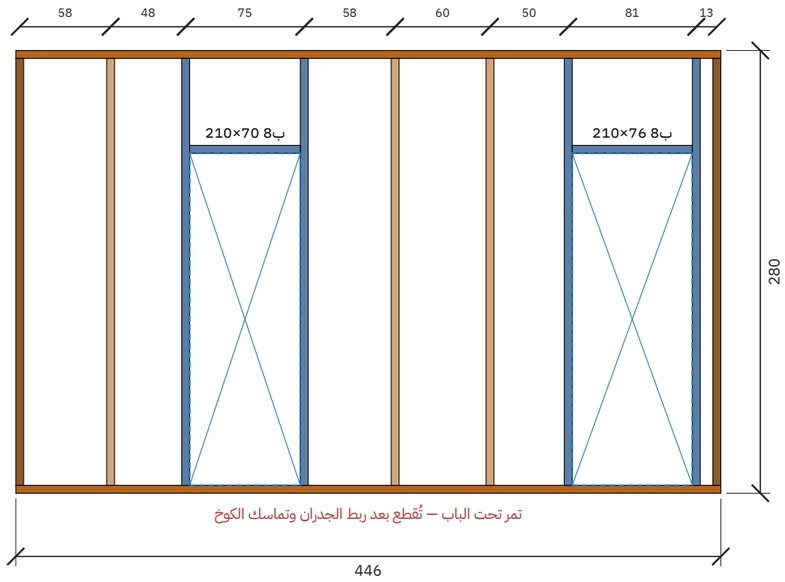



## تأطير جدار ب-خلف الغرف شرق — الطول 238 سم، الارتفاع 280 سم (داخلي)

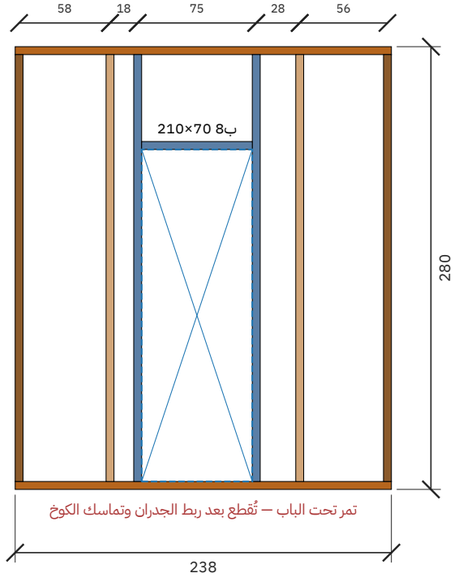



قاعدة سفلية | علوي | عمود | عمود زاوية | جنب فتحة | رأس فتحة | جلسة شباك | عمود قصير

| | | | | |
|---|---|---|---|---|
| مصنع وتد الأخشاب<br>Watad Wood Factory | المشروع / العميل<br>فيلا خشب دورين — مجلس + غرفتين — 9.00 × 7.00 م (63 م² للدور)<br>عميل — تبوك | عنوان اللوحة<br>لوحات التأطير (للورشة) | المقياس<br>— | التاريخ<br>2026-10-24 | رقم اللوحة<br>W-17 (17/21) |

## تأطير جدار ب-جدار الدرج الغربي — الطول 306 سم، الارتفاع 280 سم (داخلي)

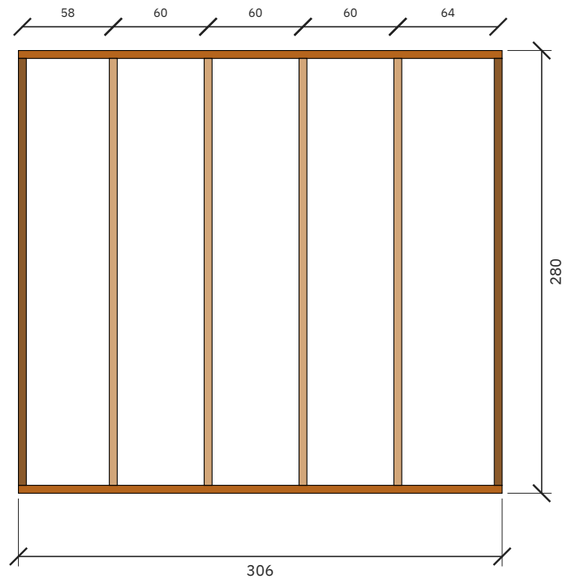



## تأطير جدار ب-جدار الدرج الشرقي — الطول 306 سم، الارتفاع 280 سم (داخلي)

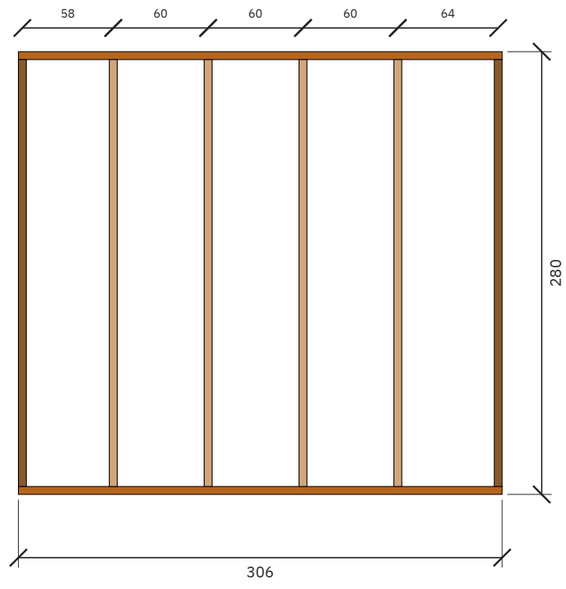


قاعدة سفلية | علوي | عمود | عمود زاوية | جنب فتحة | رأس فتحة | جلسة شباك | عمود قصير

| | | | | |
|---|---|---|---|---|
| مصنع وتد الأخشاب<br>Watad Wood Factory | المشروع / العميل<br>فيلا خشب دورين — مجلس + غرفتين — 9.00 × 7.00 م (63 م² للدور)<br>عميل — تبوك | عنوان اللوحة<br>لوحات التأطير (للورشة) | المقياس<br>— | التاريخ<br>2026-10-24 | رقم اللوحة<br>W-18 (18/21) |

## تأطير جدار ب-جدار الدورة — الطول 306 سم، الارتفاع 280 سم (داخلي)

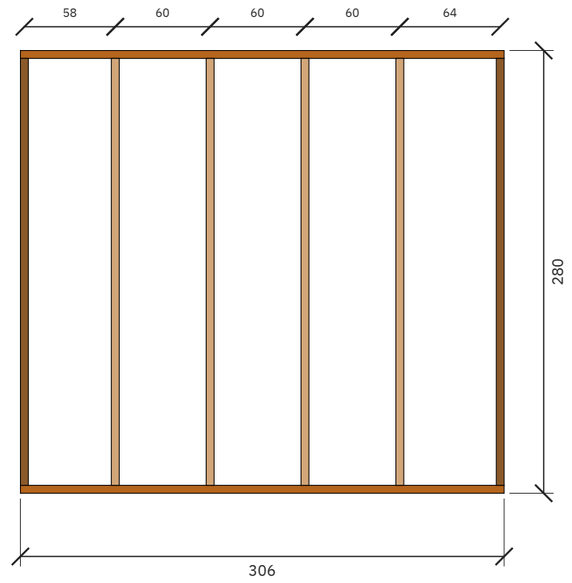


عمود قصير
جلسة شباك
رأس فتحة
جنب فتحة
عمود زاوية
عمود
علوي
قاعدة سفلية

| المشروع / العميل | عنوان اللوحة | المقياس | التاريخ | رقم اللوحة |
|---|---|---|---|---|
| **فيلا خشب دورين — مجلس + غرفتين — 9.00 × 7.00 م (63 م² للدور)**<br>**عميل — تبوك** | **لوحات التأطير (للورشة)** | **—** | **2026-10-24** | **W-19 (19/21)** |

مصنع وتد الأخشاب
Watad Wood Factory

## جدول الكميات وخطة تقطيع الطبليات

| البند | القيمة |
|---|---|
| الارتفاع المطلوب / المعتمد | 280 / 280 سم |
| السقف | جملون 30° — أعلى نقطة 845 سم من وجه الصبة |
| المدادات 5×15 | 68 مداد (17 خط × قطعتين موصولة فوق الجسر الحامل بتراكب 60 سم) × حتى 335 سم — من طبلية 480 |
| طبليات الطريقة الأولى (مداد + عمود) | 68 طبلية × 480 سم |
| طبليات الطريقة الثانية (3 أعمدة) | 66 طبلية × 320 سم |
| مدادات أرضية الدور العلوي 5×15 كل 60 سم | 48 مداد — 214سم×12، 216سم×12، 248سم×24 (طبلية 320 بالطريقة الأولى) |
| إجمالي الطبليات 5×22.5 | 182 |
| إجمالي قطع 5×7 | 306 |
| قائمة تقطيع 5×7 | 888سم×10 \| 688سم×8 \| 446سم×4 \| 382سم×4 \| 306سم×10 \| 302سم×2 \| 276سم×1 \| 270سم×205 \| 238سم×2 |
| | 230سم×1 \| 220سم×1 \| 162سم×2 \| 160سم×6 \| 155سم×2 \| 150سم×1 \| 140سم×5 \| 115سم×4 \| 105سم×1 |
| ألواح تلبيس 2.5 سم | 641 لوح × 400 سم (مجموع الصفوف 2392.6 م، 42 وجه) |
| أسمنت بورد 12 مم (122×244) | 36 لوح (داخل دورات المياه) |
| العزل | 351 لوح فوم صخري 80 |
| الصبة | يجهزها العميل — 20 سم، مفرغة تحت دورات المياه |

## مراجعة التصميم مقابل قواعد المصنع

| النوع | البند | التفاصيل | المقترح |
|---|---|---|---|
| ملاحظة | بحر المدادات | أطول بحر بدون جدار داخلي يحمل المداد: جهة أ: 342 سم، جهة ب: 342 سم. يحتاج رقم المصنع لأقصى بحر مسموح لتحديد المدادات اللي تُقوّى 20×5. | |
| ملاحظة | الصبة والدرج | ارتفاع الصبة 45 سم ← 3 درجة بقائمة 15.0 سم. | |
| ملاحظة | مناسيب رؤوس الفتحات | رؤوس الأبواب والشبابيك على مناسيب مختلفة: 210، 220، 230، 240، 250 سم. | |
| سؤال | يحتاج تأكيد | أقصى بحر للمداد بدون جدار داخلي قبل إضافة تقوية 5×7 (مداد 20×5)؟ | |
| سؤال | يحتاج تأكيد | التغطية الصافية للوح التلبيس بعد التعشيق (مستنتجة مؤقتاً 18.67 سم من 280/15)؟ | |
| سؤال | يحتاج تأكيد | هل يوضع أعمدة قصيرة فوق رأس الشباك/الباب إلى العلوي؟ | |
| سؤال | يحتاج تأكيد | مكان الوصلة في القاعدة والعلوي إذا الجدار أطول من الطبلية؟ | |