
المنظور ثلاثي الأبعاد والمواد

النمط: جوزي غامق + إطارات سوداء — رندر واقعي بخامات حقيقية

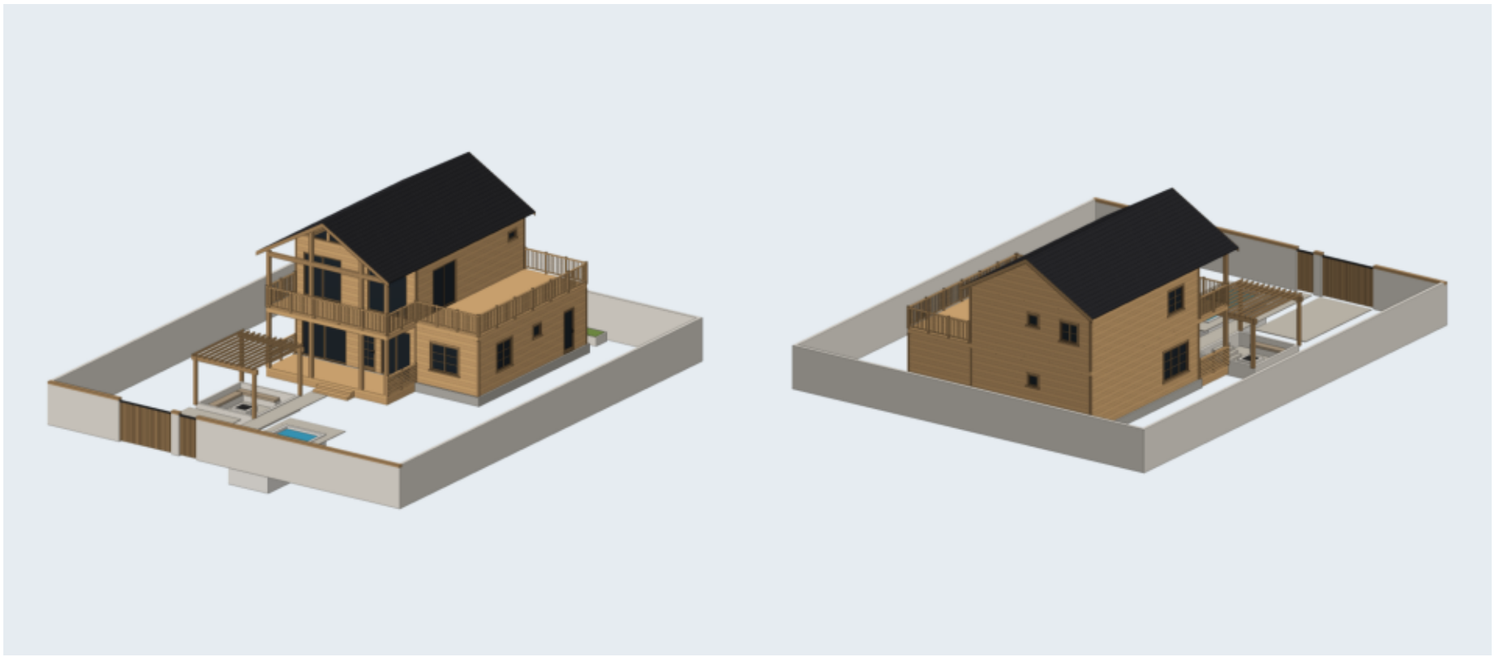

جدول المواد والألوان

الخشب / الصبغة

خشب طبيعي فاتح (بدون صبغة)

القرميد

قرميد رمادي غامق

الزجاج

زجاج عاكس غامق

إطارات الشبابيك والأبواب

إطار خشب بنفس الصبغة أغمق

الكنار والزوايا

نفس الصبغة أغمق درجة


الصبة

خرسانة 45 سم


الدربزين: ألواح أفقية متقاربة (عصري)

تقسيم الشبابيك: بدون | الباب الرئيسي: سحاب زجاج

أنواع الدربزين المعتمدة (من مشاريع المصنع)

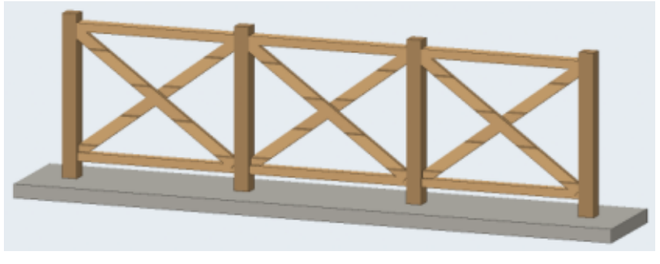

تقاطع X (صورة 5)

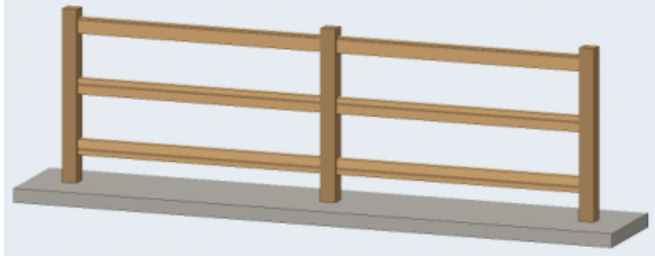

3 مرابيع أفقية (صورة 2)




قوائم رأسية متقاربة (صورة 1)

المشروع / العميل	عنوان اللوحة	المقياس	التاريخ	رقم اللوحة
مصنع وتد الأخشاب Watad Wood Factory **كوخ الهدا — دورين — 3 غرف نوم + بلكونة جانبية — 10.60 × 9.00 م** **عميل — الهدا**	**المنظور والمواد**	**1:50**	**2026-11-08**	**W-01 (1/24)**

المسقط الأفقي مع الفرش — الدور الأرضي


الأبعاد بالسنتيمتر - الجدران: قوائم 7×5 + تلبيس 2.5 من الجهتين (12 سم) | منسوب الأرضية +0.00

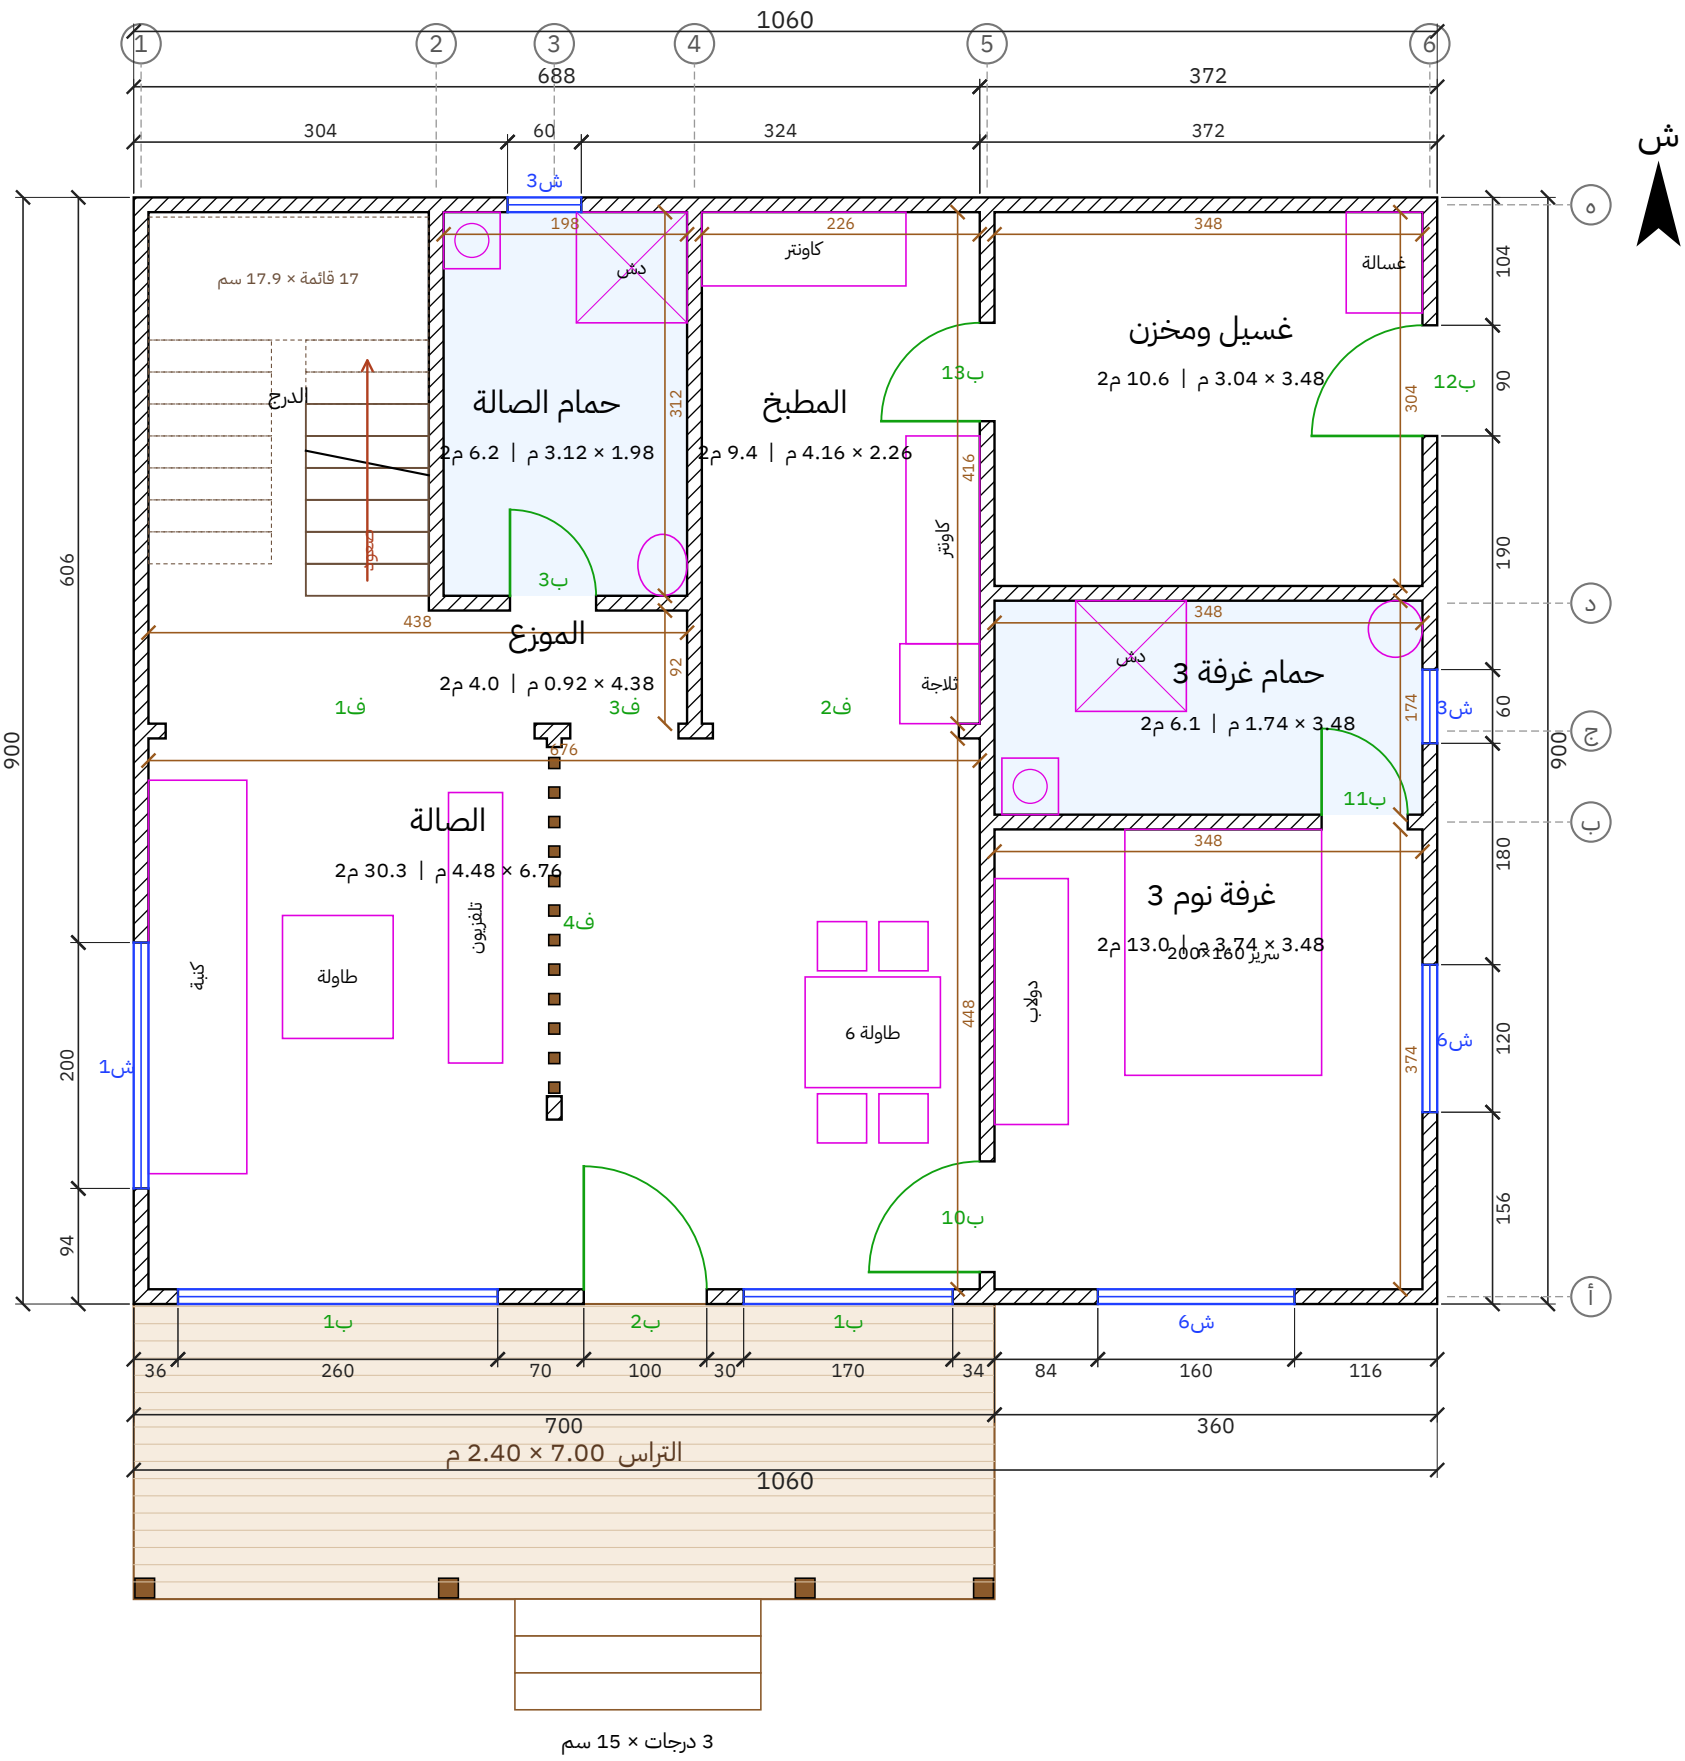

مصنع وتد الأخشاب Watad Wood Factory	المشروع / العميل كوخ الهدا — دورين — 3 غرف نوم + بلكونة جانبية — 10.60 × 9.00 م عميل — الهدا	عنوان اللوحة المسقط الأفقي — الدور الأرضي	المقياس 1:50	التاريخ 2026-11-08	رقم اللوحة W-02 (2/24)


المسقط الأفقي مع الفرش — الدور الأول

الأبعاد بالسنتيمتر - الجدران: قوائم 7×5 + تلبيس 2.5 من الجهتين (12 سم) | منسوب الأرضية +3.05

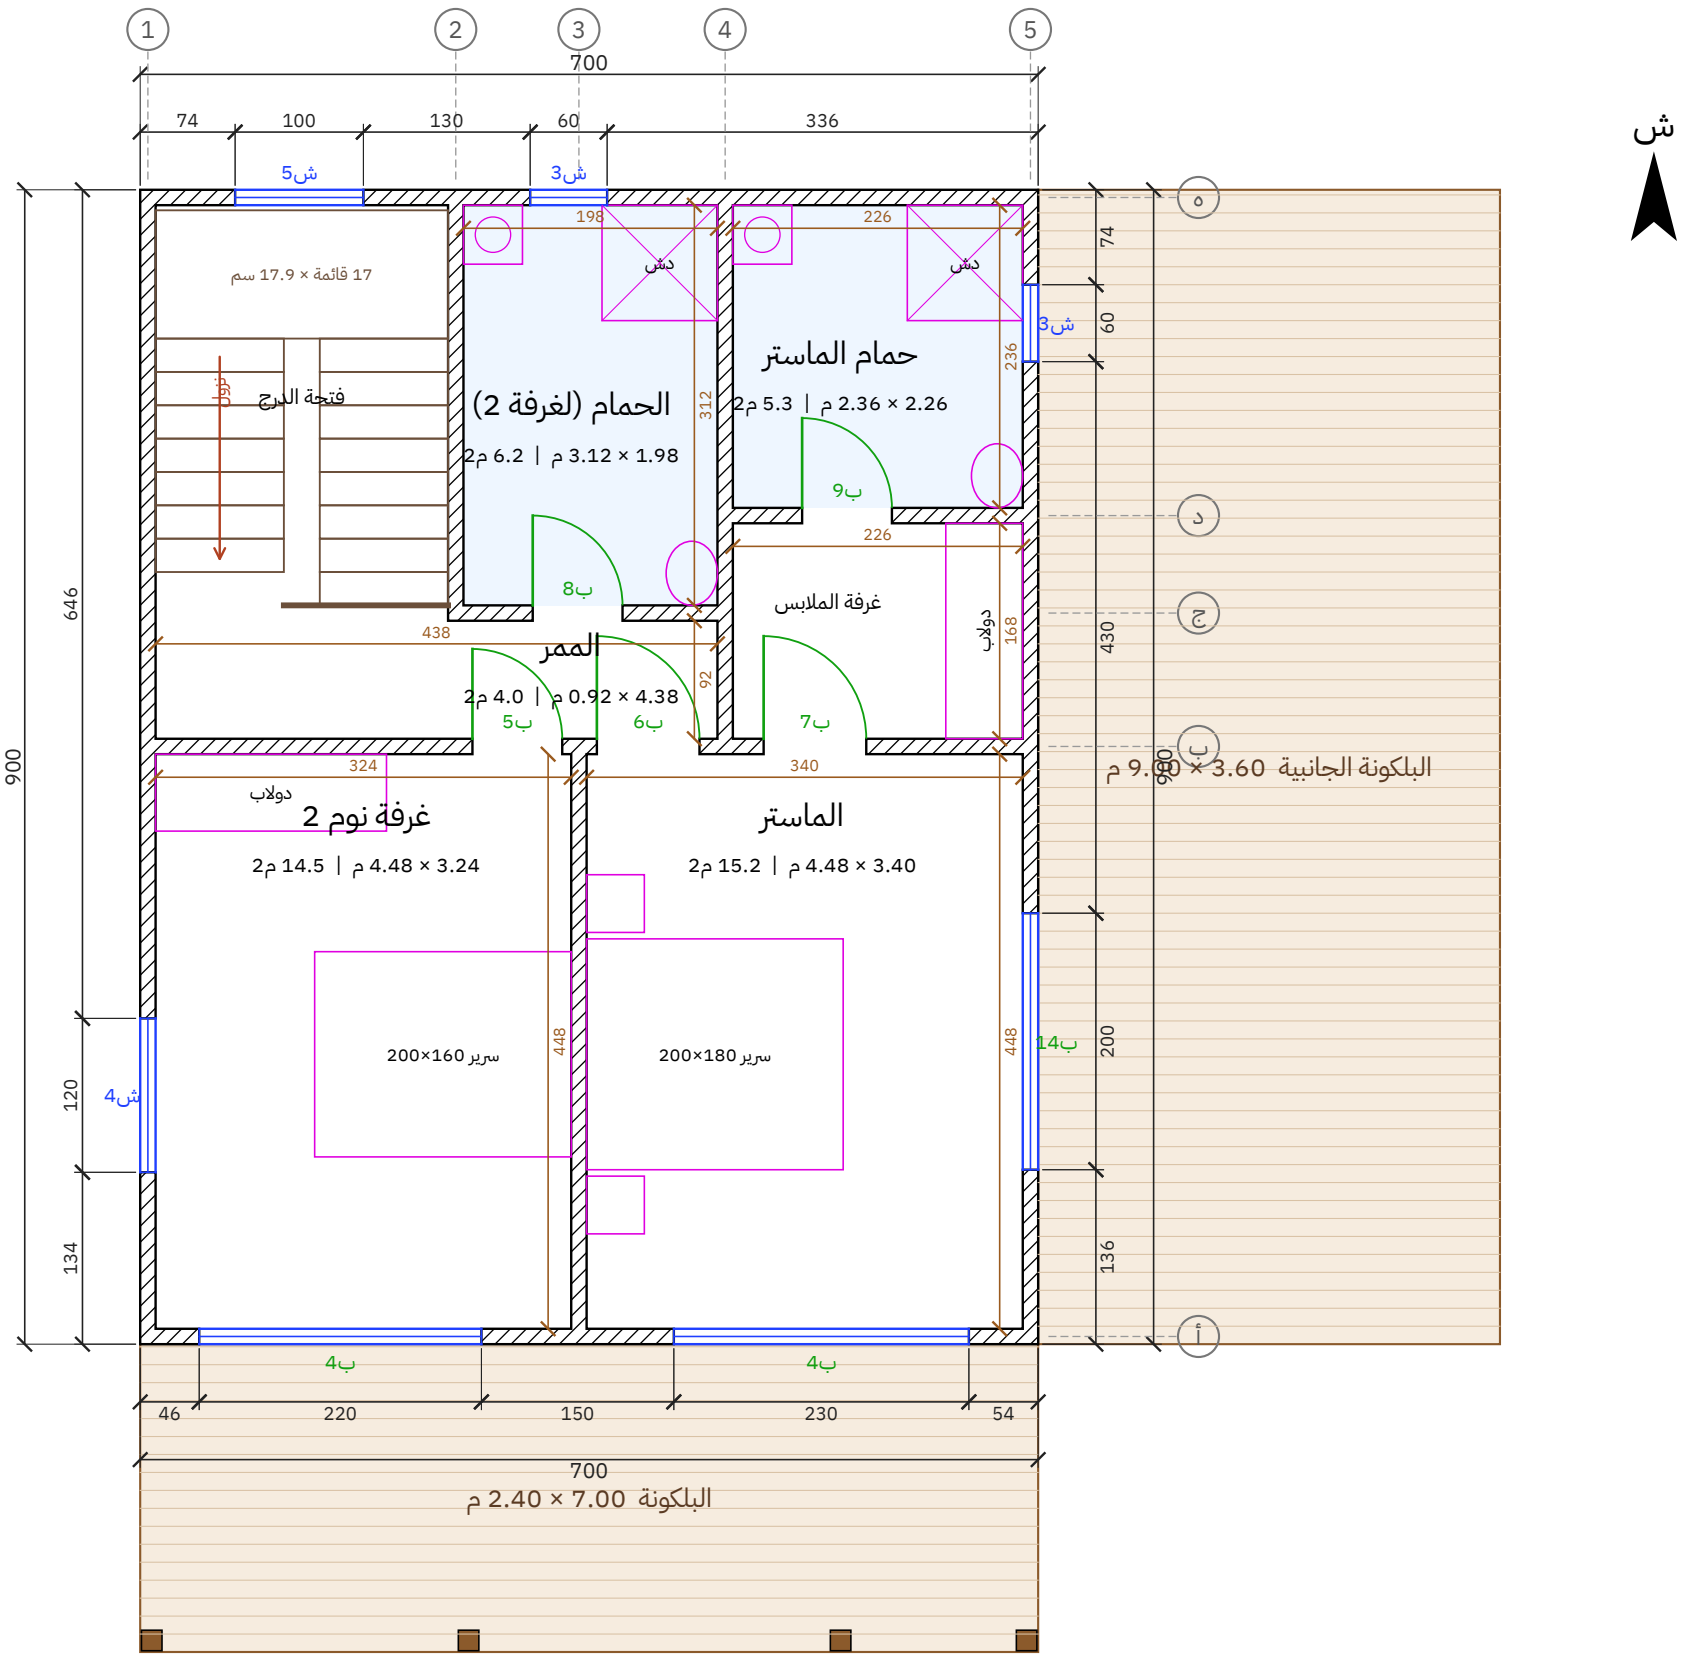


المشروع / العميل	عنوان اللوحة	المقياس	التاريخ	رقم اللوحة
كوخ الهدا — دورين — 3 غرف نوم + بلكونة جانبية — 10.60 × 9.00 م عميل — الهدا	المسقط الأفقي — الدور الأول	1:50	2026-11-08	W-03 (3/24)

مصنع وتد الأخشاب
Watad Wood Factory

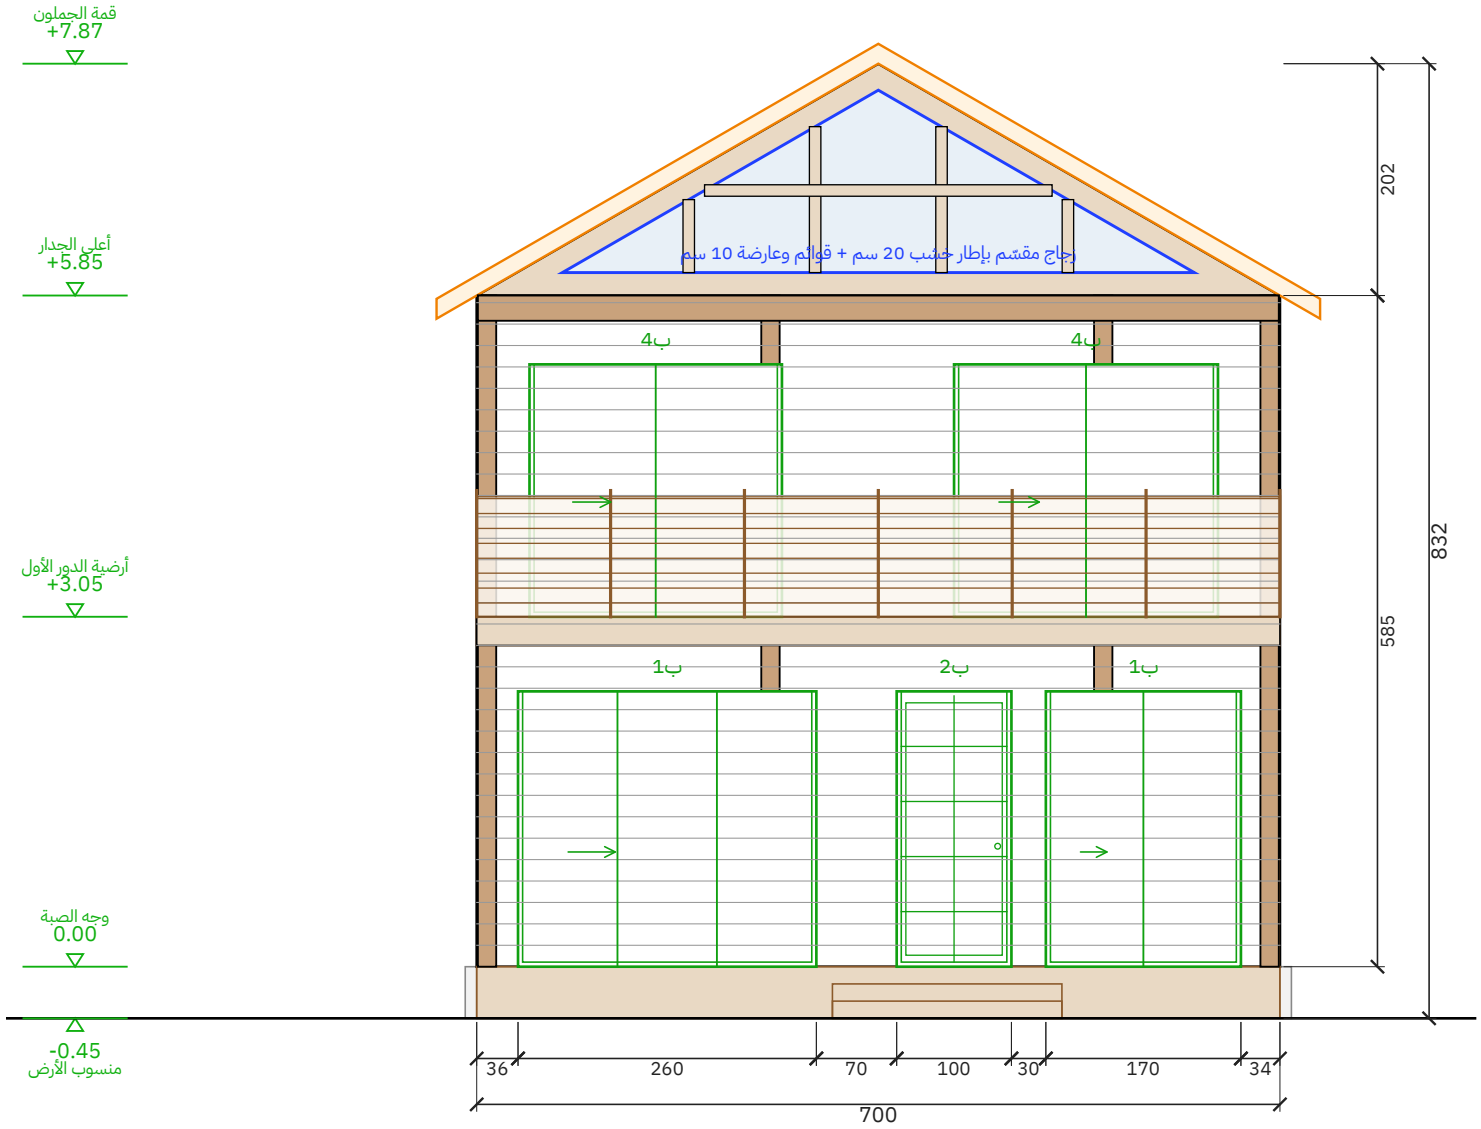

الواجهة الأمامية

مقياس 1:50 | الوحدة: سم

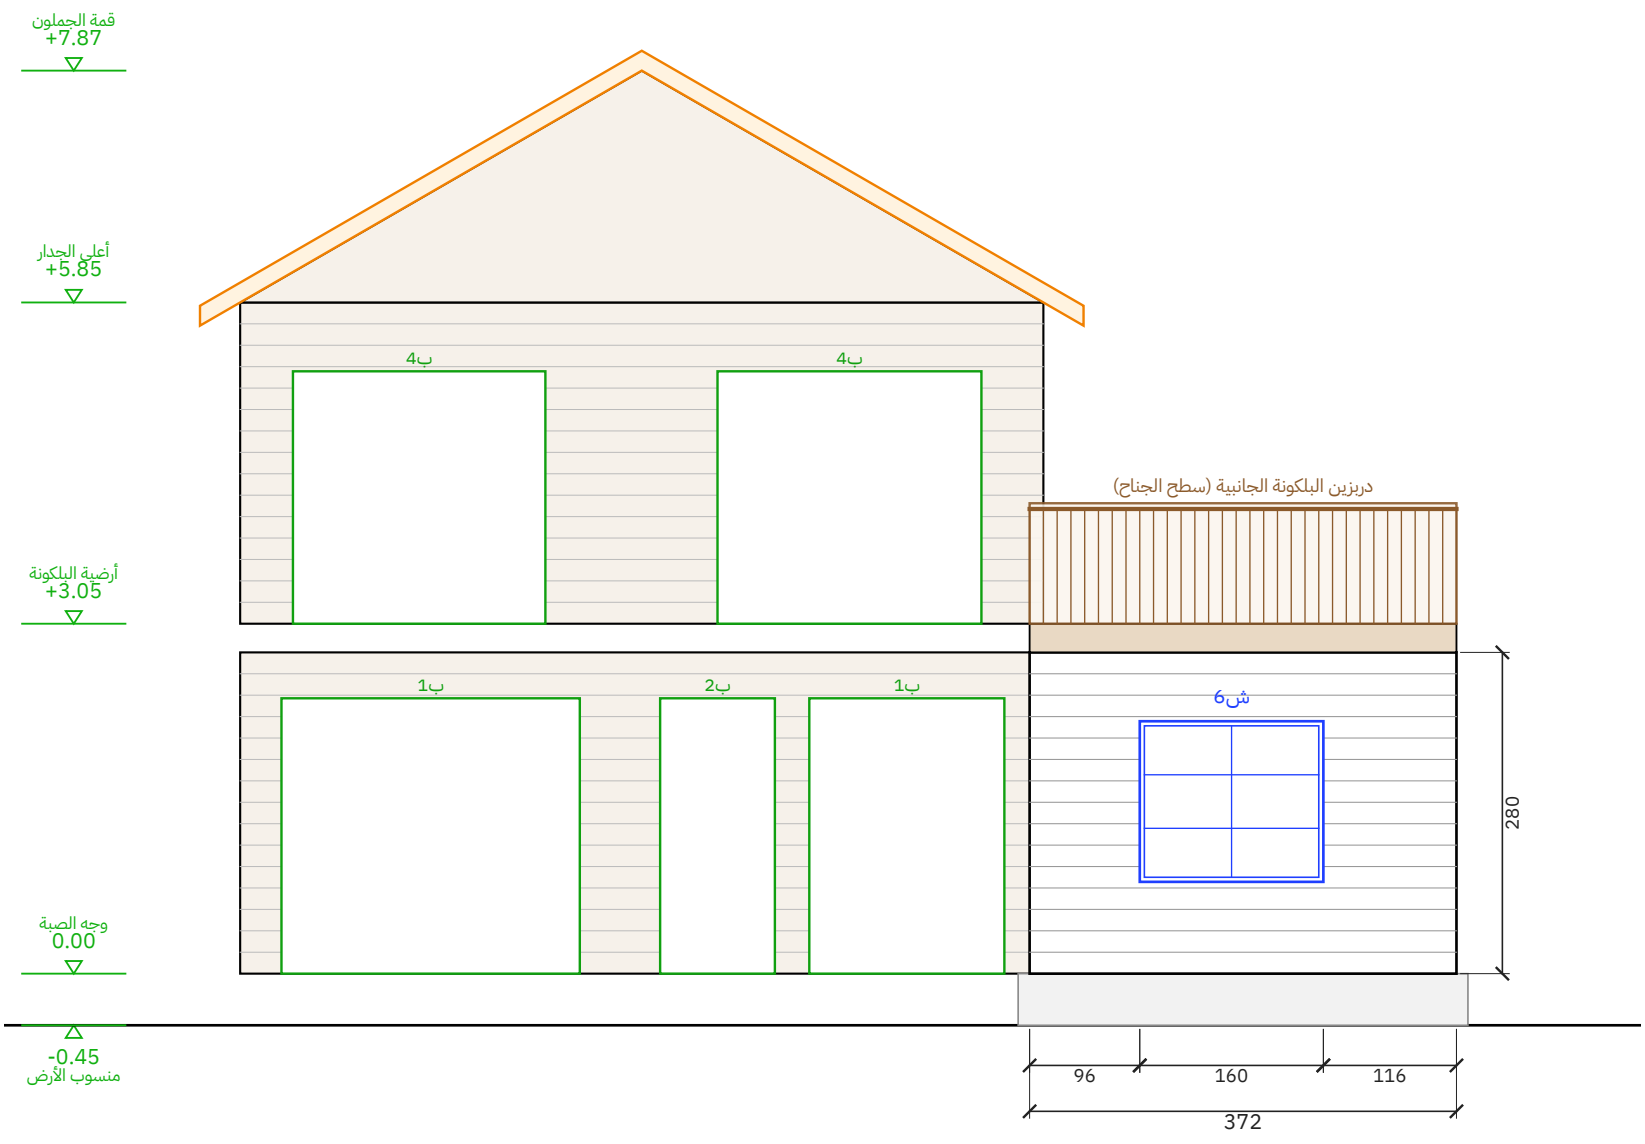


الواجهة الأمامية – الجناح (غرفة 3)

مقياس 1:50 | الوحدة: سم


المشروع / العميل	عنوان اللوحة	المقياس	التاريخ	رقم اللوحة
كوخ الهدا – دورين – 3 غرف نوم + بلكونة جانبية – 10.60 × 9.00 م عميل – الهدا	الواجهة الأمامية والواجهة الأمامية – الجناح (غرفة 3)	1:50	2026-11-08	W-04 (4/24)

مصنع وتد الأخشاب
Watad Wood Factory

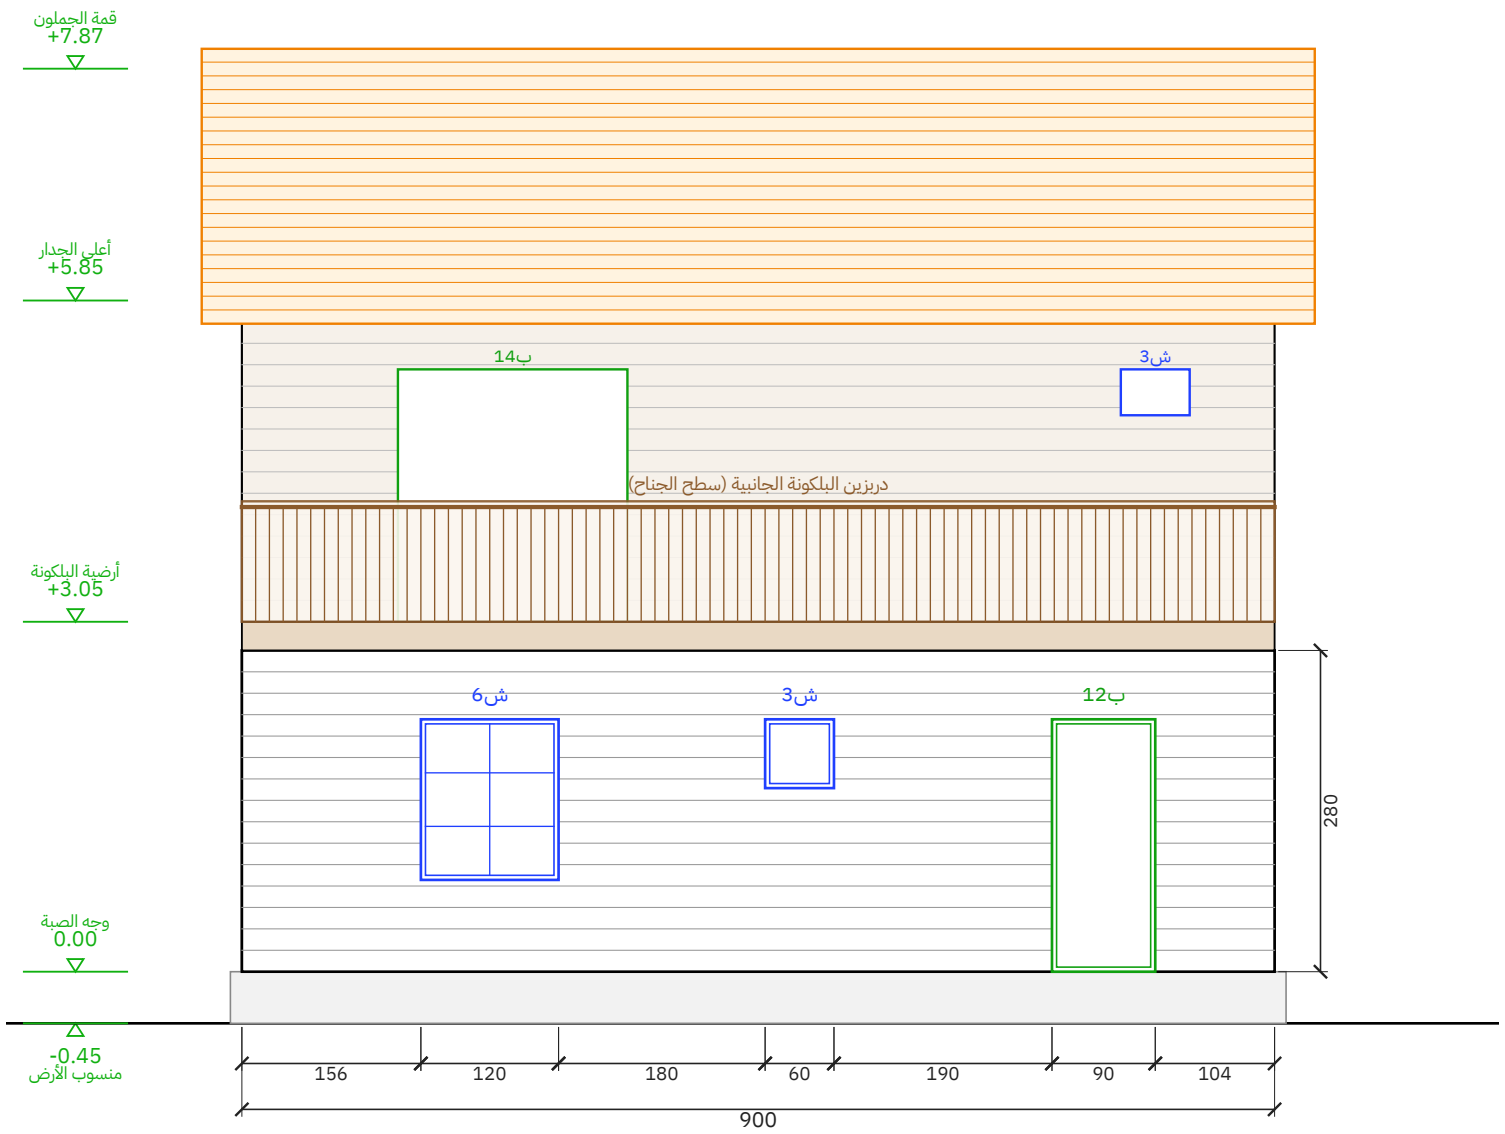

الواجهة الشرقية

مقياس 1:50 | الوحدة: سم

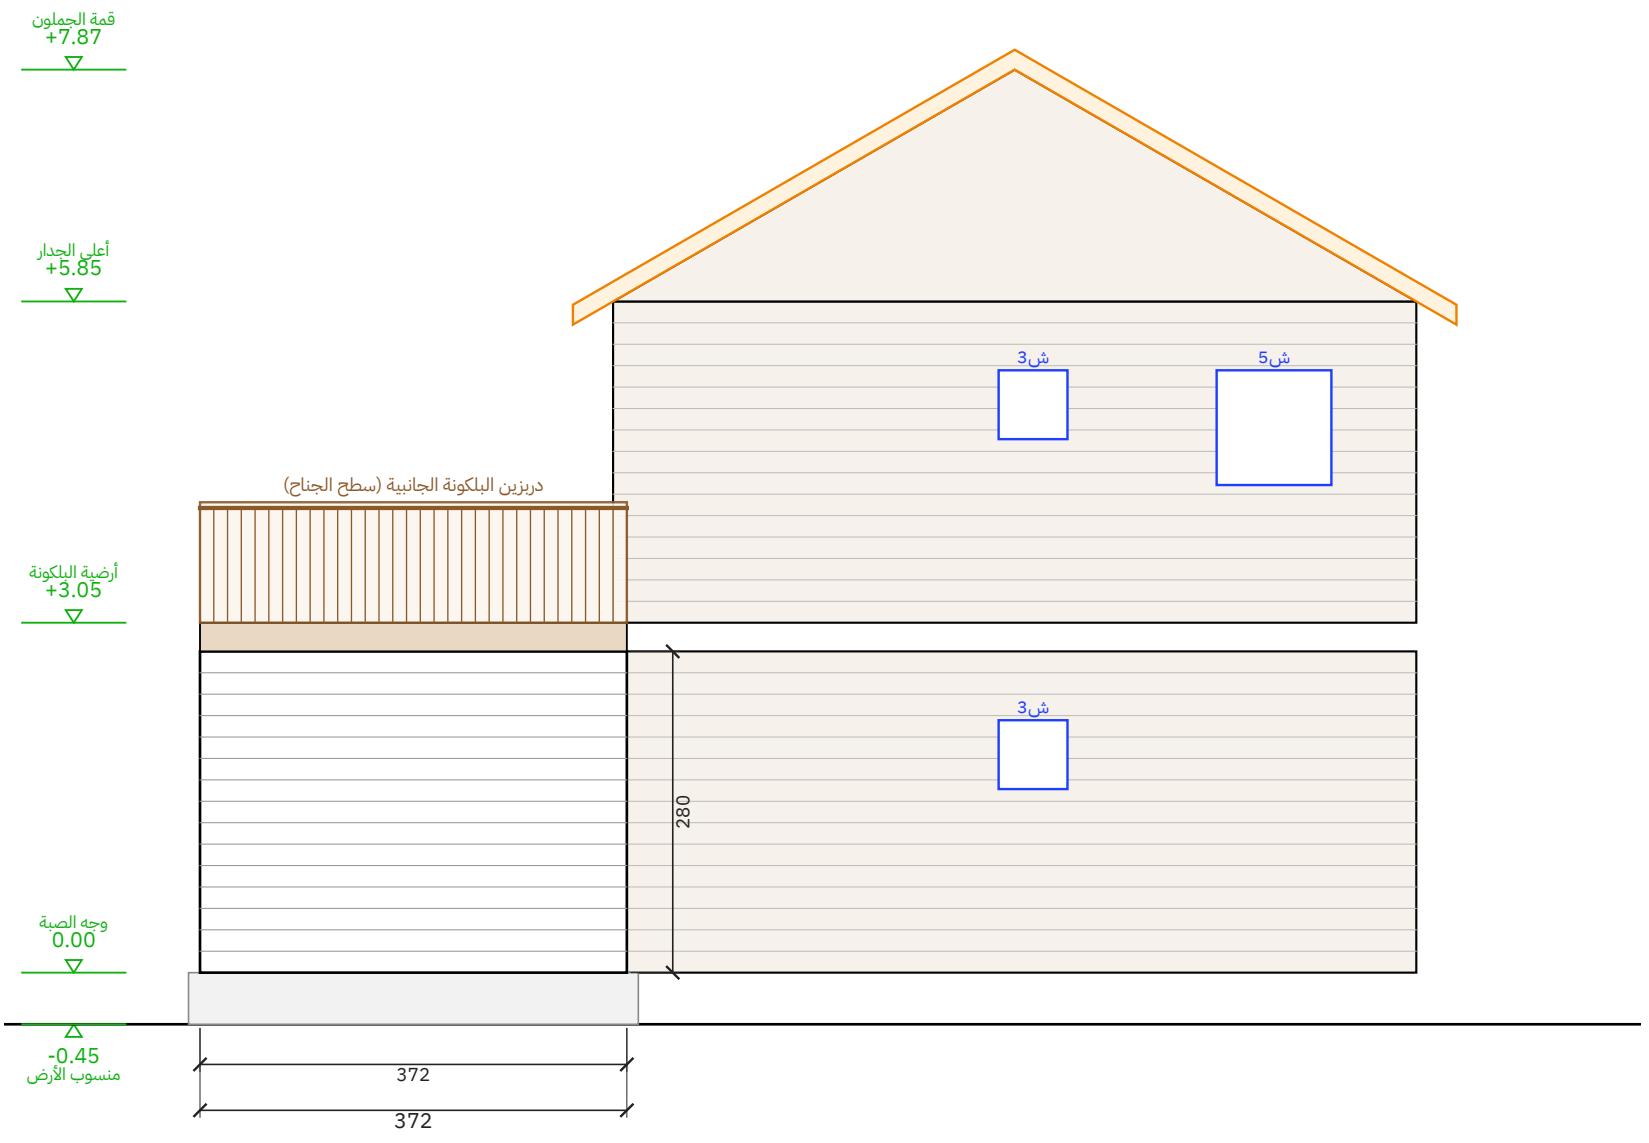


الواجهة الخلفية – الجناح

مقياس 1:50 | الوحدة: سم


المشروع / العميل	عنوان اللوحة	المقياس	التاريخ	رقم اللوحة
كوخ الهدا – دورين – 3 غرف نوم + بلكونة جانبية – 10.60 × 9.00 م عميل – الهدا	الواجهة الشرقية والواجهة الخلفية – الجناح	1:50	2026-11-08	W-05 (5/24)

مصنع وتد الأخشاب
Watad Wood Factory

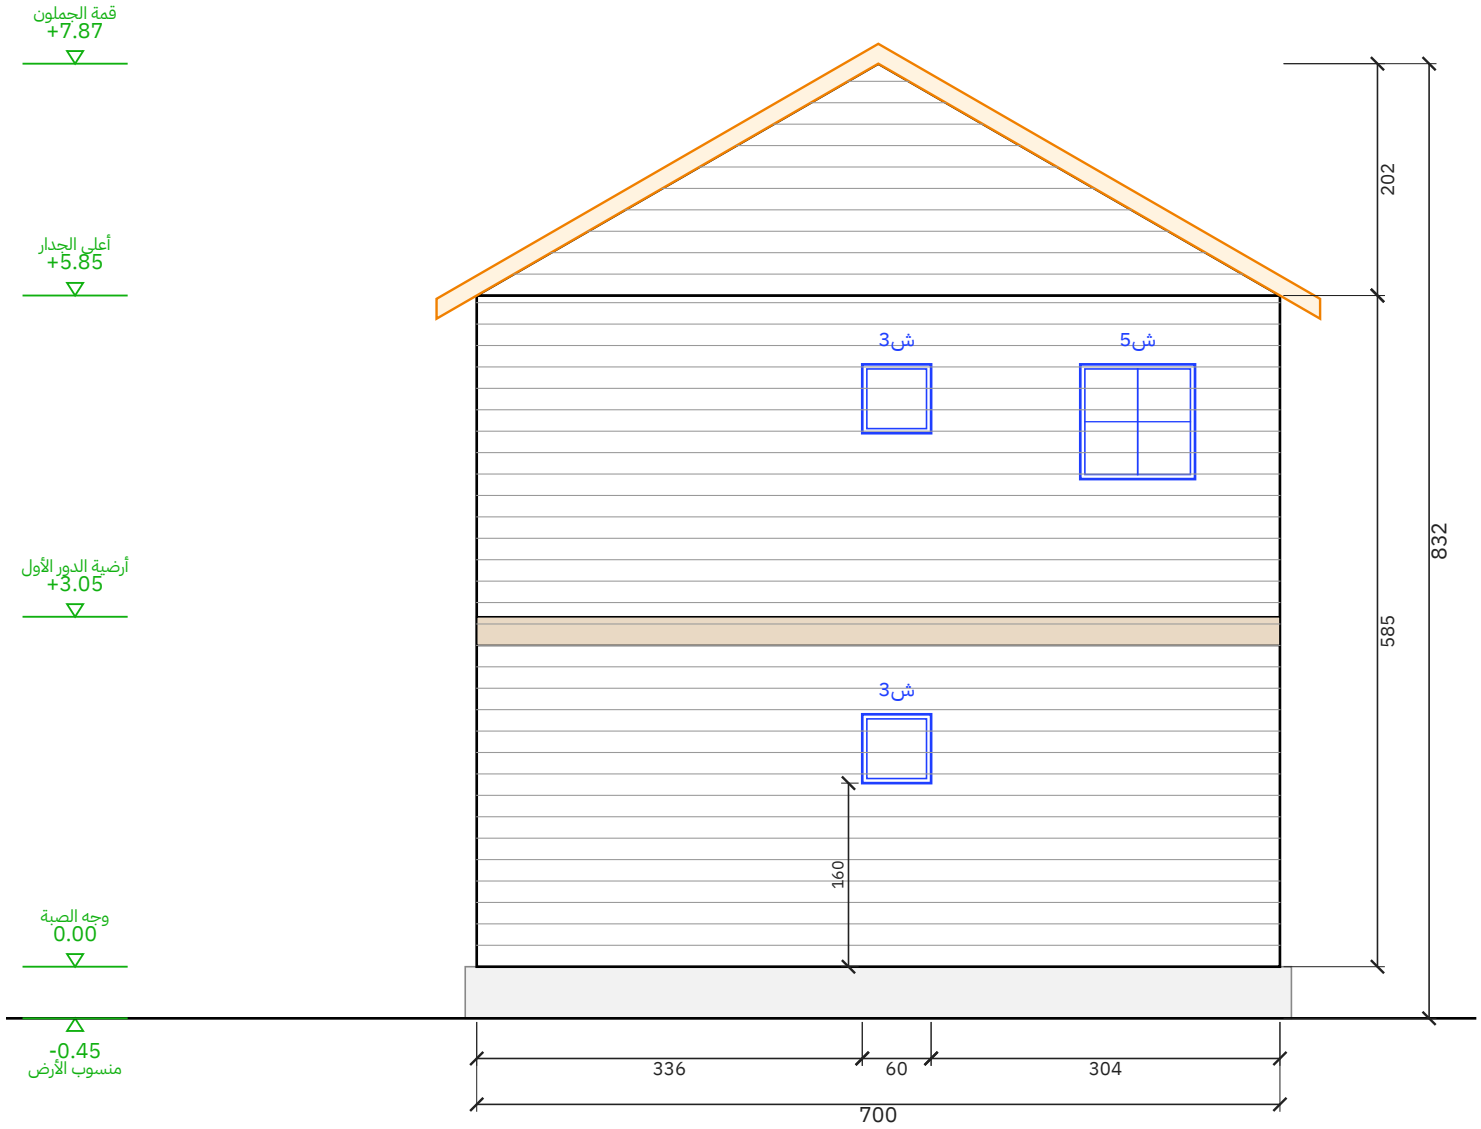

الواجهة الخلفية

مقياس 1:50 | الوحدة: سم

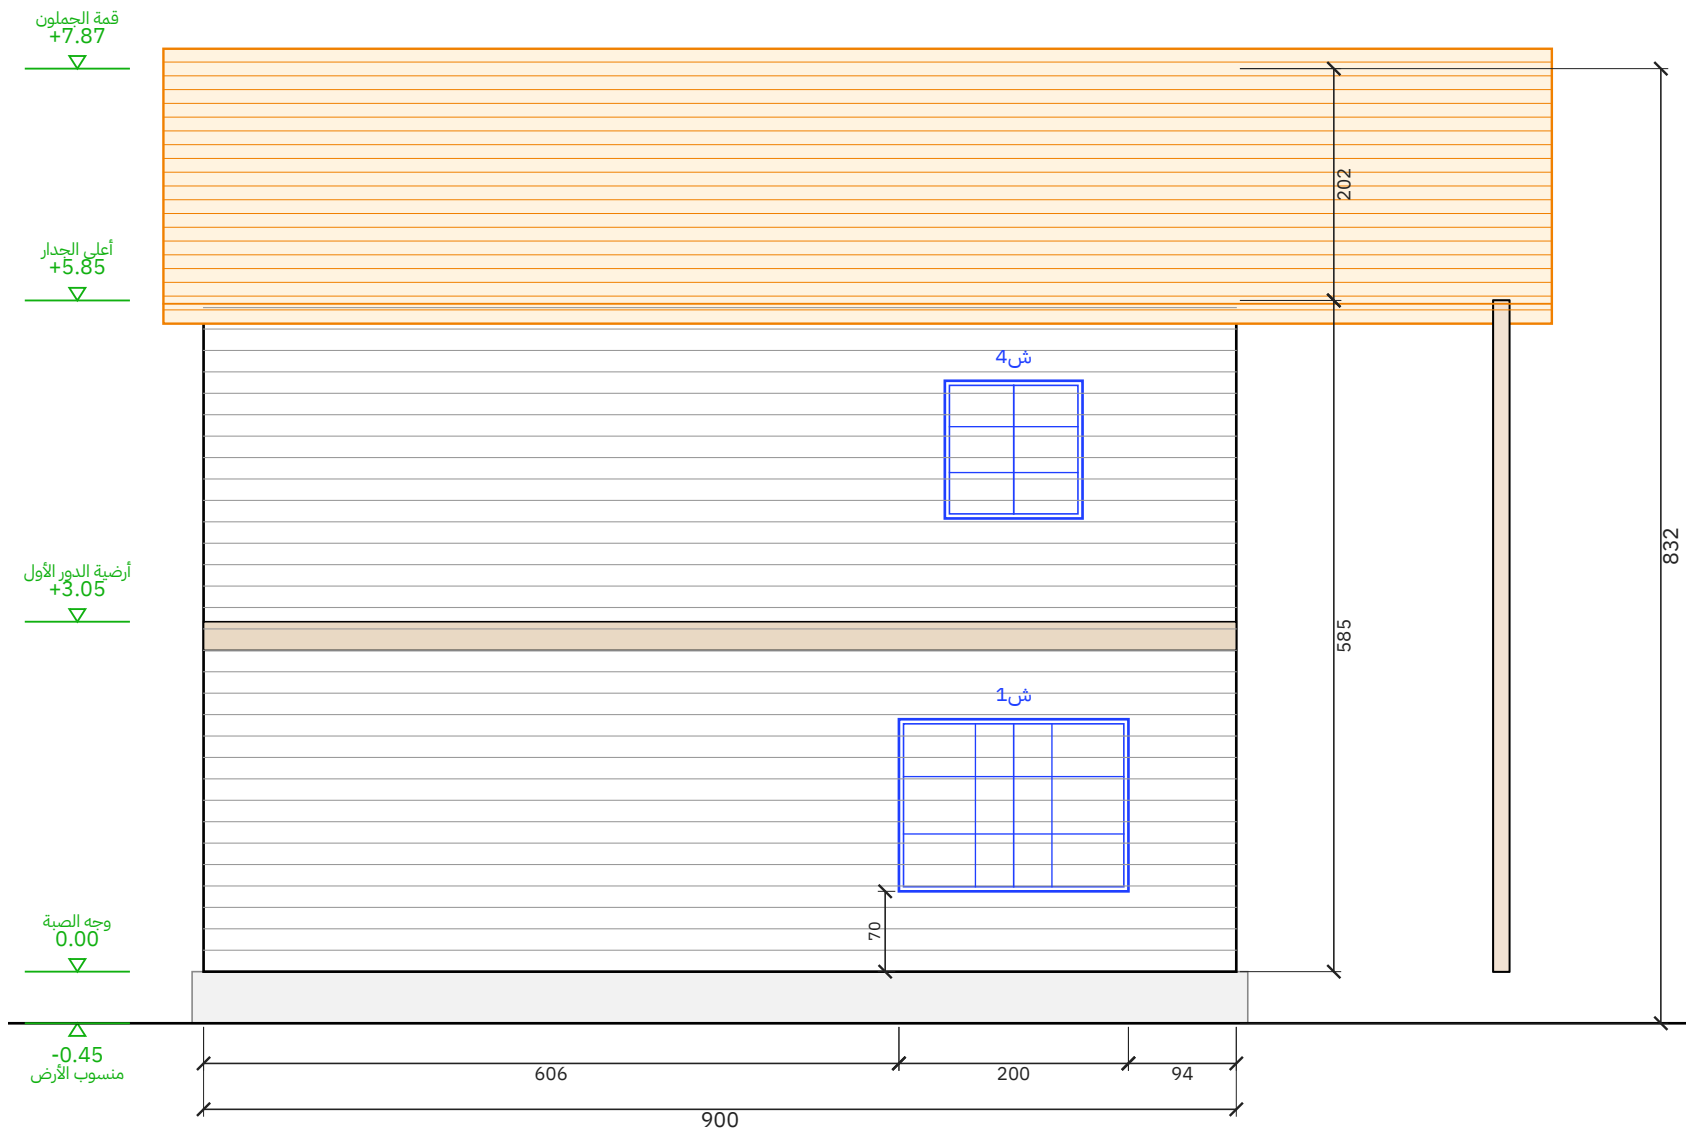

الواجهة الغربية


مقياس 1:50 | الوحدة: سم

المشروع / العميل	عنوان اللوحة	المقياس	التاريخ	رقم اللوحة
كوخ الهدا – دورين – 3 غرف نوم + بلكونة جانبية – 10.60 × 9.00 م **عميل – الهدا**	**الواجهة الخلفية والواجهة الغربية**	**–**	**2026-11-08**	**W-06 (6/24)**

مصنع وتد الأخشاب
Watad Wood Factory


مسقط السقف (جملون)

رفرف 35 سم من كل جهة | مقياس 1:50

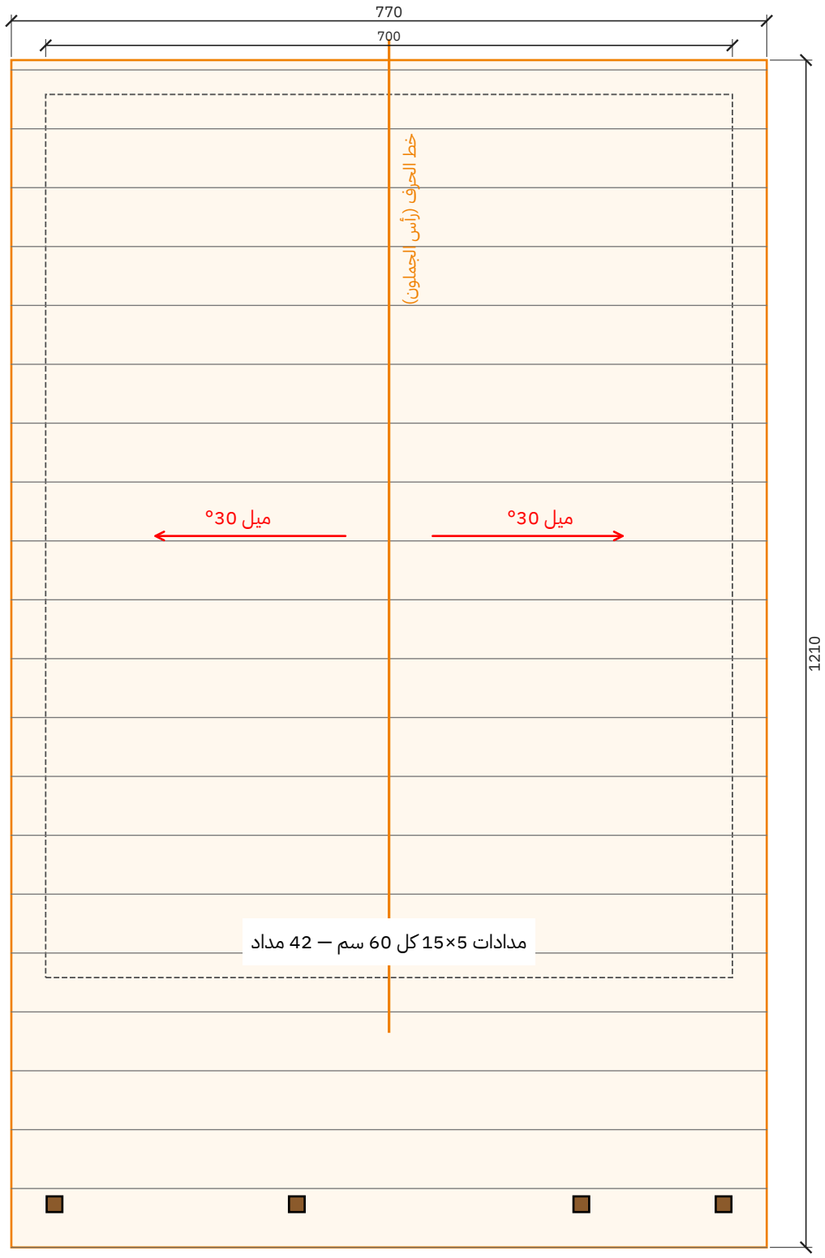


قطاع عرضي أ-أ

مقياس 1:50 | الوحدة: سم

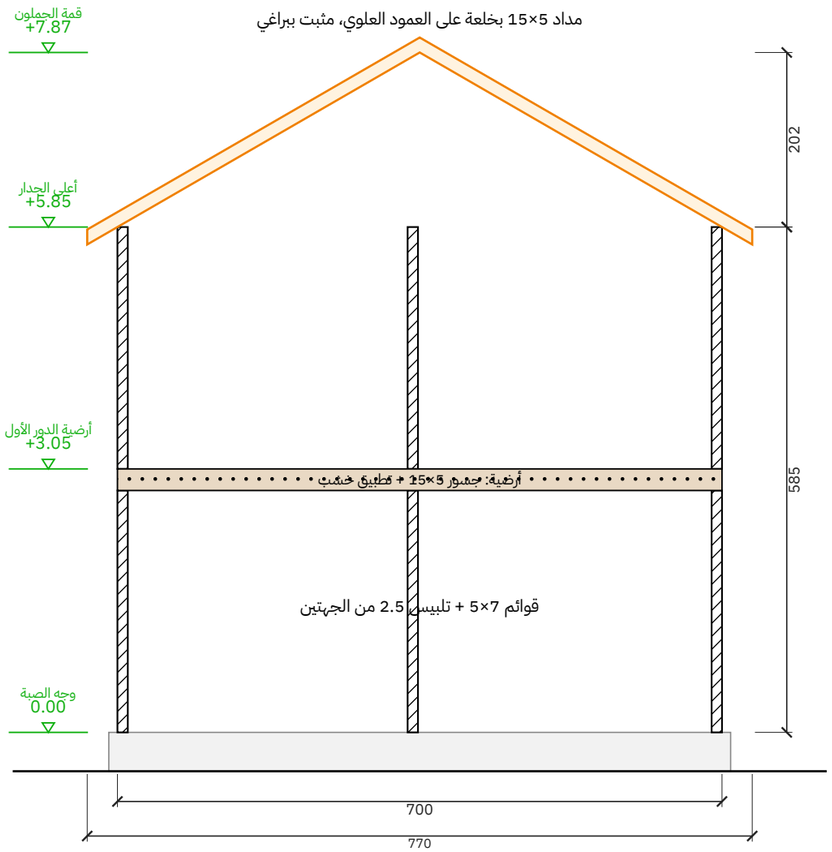

تفصيلة جلوس المداد على العلوي (1:5)

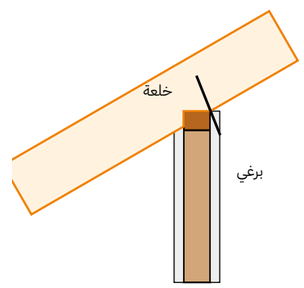

علوي 7×5 على قائم 7×5

المشروع / العميل **كوخ الهدا — دورين — 3 غرف نوم + بلكونة جانبية — 10.60 × 9.00 م** **عميل — الهدا**	عنوان اللوحة **مسقط السقف والقطاع**	المقياس **—**	التاريخ **2026-11-08**	رقم اللوحة **W-07 (7/24)**

مصنع وتد الأخشاب
Watad Wood Factory

جدول مقاسات الأبواب والشبابيك

مقاس الفتحة الصافي في الجدار - الوحدة: سم

الرمز	النوع	العرض (سم)	الارتفاع (سم)	ارتفاع الجلسة (سم)	العدد	الموقع
ب1	باب مزدوج	260	240	-	1	الأمامية
ب1	باب مزدوج	170	240	-	1	الأمامية
ب10	باب	90	220	-	1	غرفة نوم 3 (من الصالة)
ب11	باب	70	210	-	1	حمام غرفة 3
ب12	باب	90	220	-	1	الشرقية
ب13	باب	80	210	-	1	الغسيل (من المطبخ)
ب14	باب مزدوج	200	220	-	1	الشرقية
ب2	باب	100	240	-	1	الأمامية
ب3	باب	70	210	-	1	حمام الصالة
ب4	باب مزدوج	220	220	-	1	الأمامية (على البلكونة)
ب4	باب مزدوج	230	220	-	1	الأمامية (على البلكونة)
ب5	باب	70	210	-	1	غرفة نوم 2
ب6	باب	80	210	-	1	الماستر
ب7	باب	80	210	-	1	غرفة الملابس
ب8	باب	70	210	-	1	الحمام
ب9	باب	70	210	-	1	حمام الماستر
ف1	باب	300	220	-	1	فتحة الجلسة — الموزع والدرج
ف2	باب	200	220	-	1	فتحة المطبخ
ف3	باب	88	220	-	1	فتحة المدخل — الموزع
ف4	باب	284	250	-	1	بارتشن أعمدة خشب
ش1	شباك	200	150	70	1	الغربية
ش3	شباك	60	60	160	3	الشرقية - الخلفية 2
ش3	شباك	60	40	180	1	الشرقية
ش4	شباك	120	120	90	1	الغربية
ش5	شباك	100	100	120	1	الخلفية
ش6	شباك	160	140	80	1	الأمامية — الجناح (غرفة 3)
ش6	شباك	120	140	80	1	الشرقية

الإجمالي: أبواب 20 - شبابيك 9

جدول المساحات وبيانات المشروع والتسعير

بيانات المشروع

البند	البيان
المشروع	كوخ الهدا — دورين — 3 غرف نوم + بلكونة جانبية — 10.60 × 9.00 م
العميل	عميل — الهدا
الموقع	الهدا — الطائف
الاستخدام	كوخ سكني/استثماري
التاريخ	2026-11-08
نظام البناء	هيكل خشب 5×7 + تلبيس 2.5 سم من الجهتين
السقف	جملون 30° — قرميد معدني

جدول المساحات

م	الفراغ	الأبعاد (م)	المساحة (م2)
1	أرضي — الصالة	4.48 × 6.76	30.28
2	أرضي — الموزع	0.92 × 4.38	4.03
3	أرضي — الدرج	2.28 × 3.00	6.84
4	أرضي — حمام الصالة	1.98 × 3.12	6.18
5	أرضي — المطبخ	2.26 × 4.16	9.40
6	أرضي — غرفة نوم 3	3.48 × 3.74	13.02
7	أرضي — حمام غرفة 3	3.48 × 1.74	6.06
8	أرضي — غسيل ومخزن	3.48 × 3.04	10.58
9	أول — غرفة نوم 2	4.48 × 3.24	14.52
10	أول — الماستر	4.48 × 3.40	15.23
11	أول — الممر	0.92 × 4.38	4.03
12	أول — الحمام (لغرفة 2)	3.12 × 1.98	6.18
13	أول — غرفة الملابس	1.68 × 2.26	3.80
14	أول — حمام الماستر	2.36 × 2.26	5.33
	المساحة الصافية الداخلية		135.47
	التراس	2.40 × 7.00	16.80
	البلكونة	2.40 × 7.00	16.80
	البلكونة الجانبية	9.00 × 3.60	32.40
	مسطح الدور الأرضي	**9.00 × 10.60**	**95.40**
	مسطح الدور الأول	**9.00 × 7.00**	**63.00**
	المساحة الإجمالية المبنية	**مجموع الأدوار**	**158.40**
	المساحة الكلية (المبنية + التراس والبلكونة)		**224.40**


التسعير المفصّل

البند	المبلغ (ريال)
الكوخ المبني 158.40 م² × 1,096	173,606
تراس الأرضي + البلكونة الأمامية بالأول (7.00 × 2.40 × 2) — 33.60 م² × 1,096	36,826
البلكونة الجانبية بالأول (3.60 × 9.00) — 32.40 م² × 1,096	35,510
الإجمالي (ريال)	**245,942**


ملاحظات:

- السعر للكوخ (الدورين) والتراس والبلكونات حسب المخطط المعتمد — التراس والبلكونة تُسعّر بنفس سعر متر الكوخ.
- أعمال الموقع (السور والبوابات والمسبح والجلسة الشتوية والبلاط والزراعة) عن طريق المقاول وتُسعّر منفصلة.
- الصبة والتمديدات الخارجية على العميل ما لم يُذكر غير ذلك.

تأطير جدار أ-جنوب — الطول 688 سم، الارتفاع 280 سم

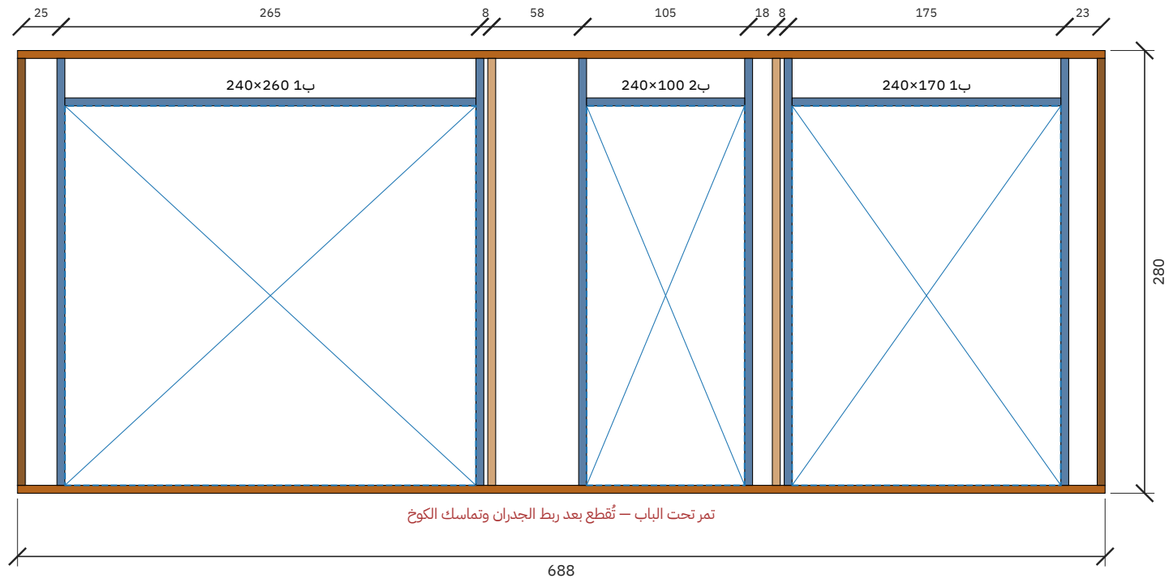


تأطير جدار أ-جنوب الجناح — الطول 360 سم، الارتفاع 280 سم

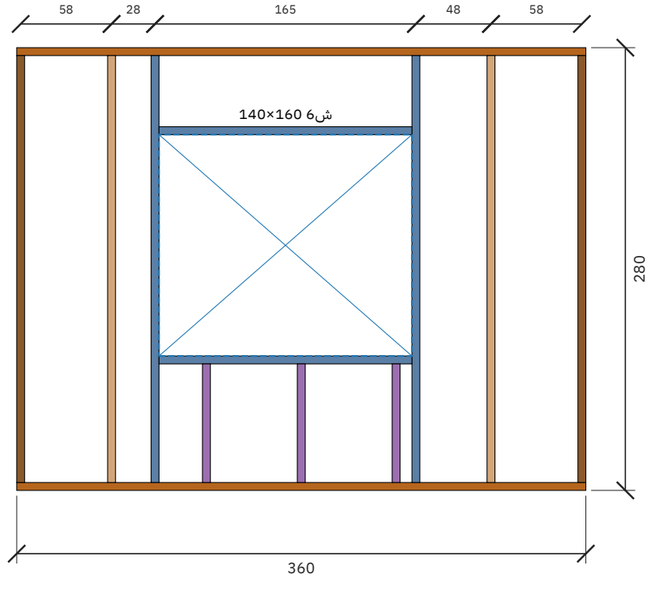


قاعدة سفلية | علوي | عمود | عمود زاوية | جنب فتحة | رأس فتحة | جلسة شباك | عمود قصير

مصنع وتد الأخشاب Watad Wood Factory	المشروع / العميل كوخ الهدا — دورين — 3 غرف نوم + بلكونة جانبية — 10.60 × 9.00 م عميل — الهدا	عنوان اللوحة لوحات التأطير (للورشة)	المقياس —	التاريخ 2026-11-08	رقم اللوحة W-10 (10/24)

تأطير جدار أ-شرق — الطول 888 سم، الارتفاع 280 سم

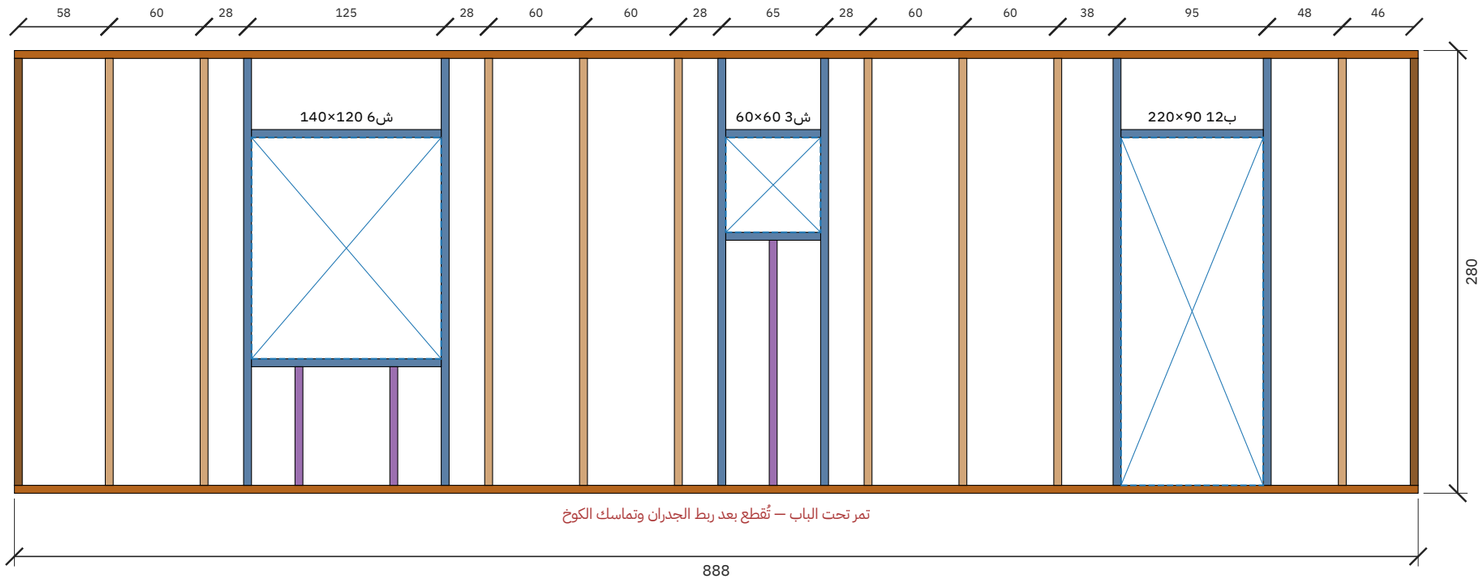


تأطير جدار أ-شمال الجناح — الطول 360 سم، الارتفاع 280 سم

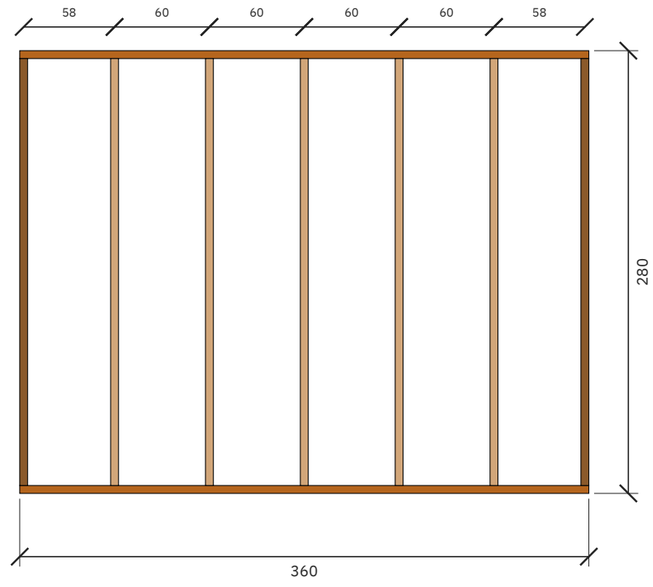


قاعدة سفلية | علوي | عمود | عمود زاوية | جنب فتحة | رأس فتحة | جلسة شباك | عمود قصير

مصنع وتد الأخشاب Watad Wood Factory	المشروع / العميل كوخ الهدا — دورين — 3 غرف نوم + بلكونة جانبية — 10.60 × 9.00 م عميل — الهدا	عنوان اللوحة لوحات التأطير (للورشة)	المقياس —	التاريخ 2026-11-08	رقم اللوحة W-11 (11/24)

تأطير جدار أ-فاصل الجناح — الطول 888 سم، الارتفاع 280 سم (داخلي)

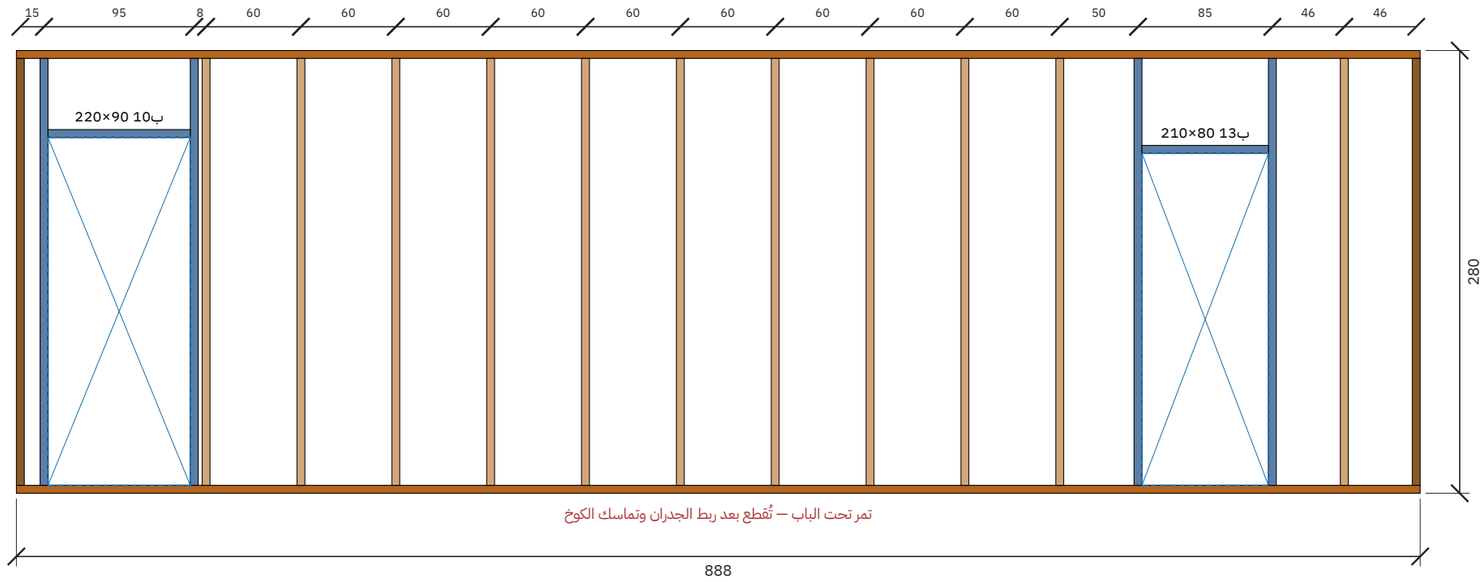


تأطير جدار أ-فاصل غرفة 3 — الطول 360 سم، الارتفاع 280 سم (داخلي)

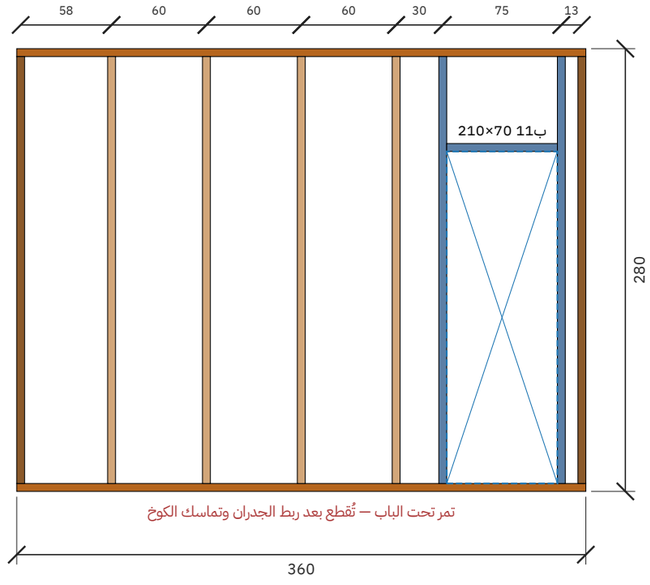


قاعدة سفلية | علوي | عمود | عمود زاوية | جنب فتحة | رأس فتحة | جلسة شباك | عمود قصير

مصنع وتد الأخشاب Watad Wood Factory	المشروع / العميل كوخ الهدا — دورين — 3 غرف نوم + بلكونة جانبية — 10.60 × 9.00 م عميل — الهدا	عنوان اللوحة لوحات التأطير (للورشة)	المقياس —	التاريخ 2026-11-08	رقم اللوحة W-12 (12/24)

تأطير جدار أ-فاصل الغسيل — الطول 360 سم، الارتفاع 280 سم (داخلي)

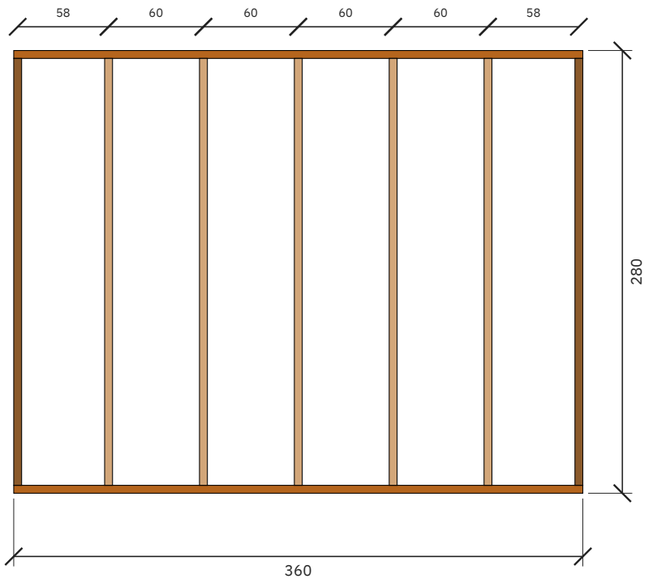


تأطير جدار أ-شمال — الطول 688 سم، الارتفاع 280 سم

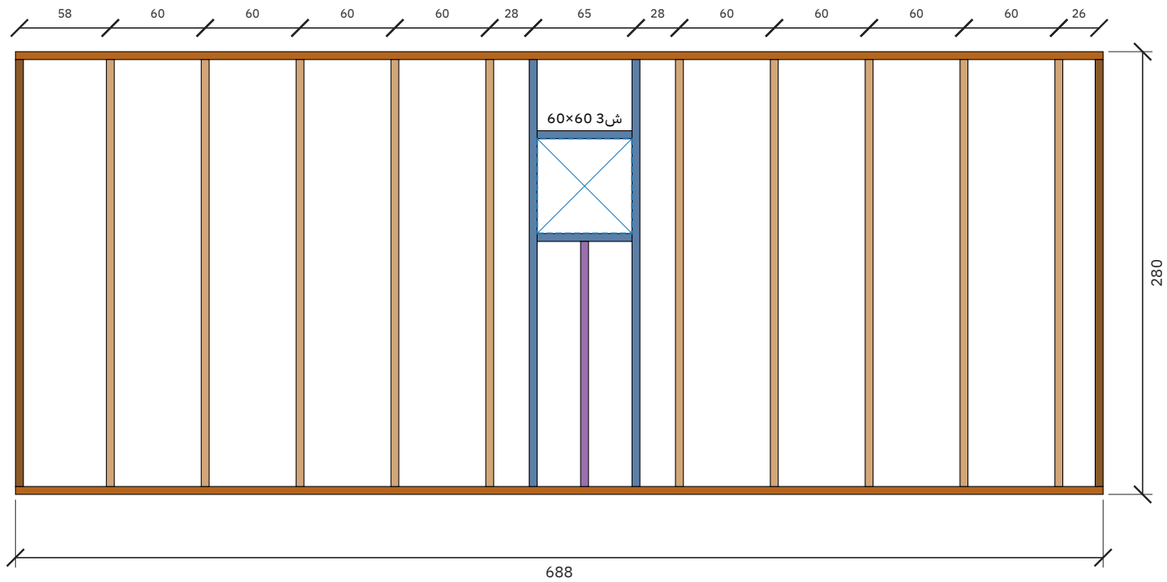


مصنع وتد الأخشاب Watad Wood Factory	المشروع / العميل كوخ الهدا — دورين — 3 غرف نوم + بلكونة جانبية — 10.60 × 9.00 م عميل — الهدا	عنوان اللوحة لوحات التأطير (للورشة)	المقياس —	التاريخ 2026-11-08	رقم اللوحة W-13 (13/24)

تأطير جدار أ-غرب — الطول 888 سم، الارتفاع 280 سم

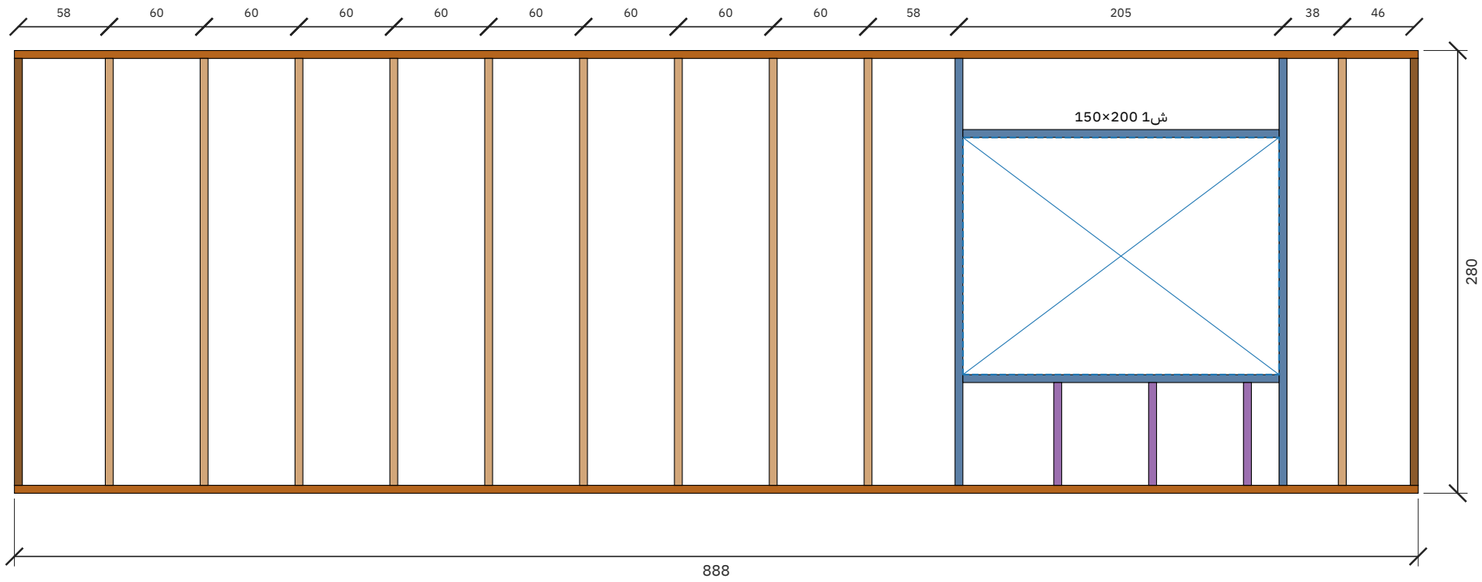


تأطير جدار أ-فاصل الصالة — الطول 688 سم، الارتفاع 280 سم (داخلي)

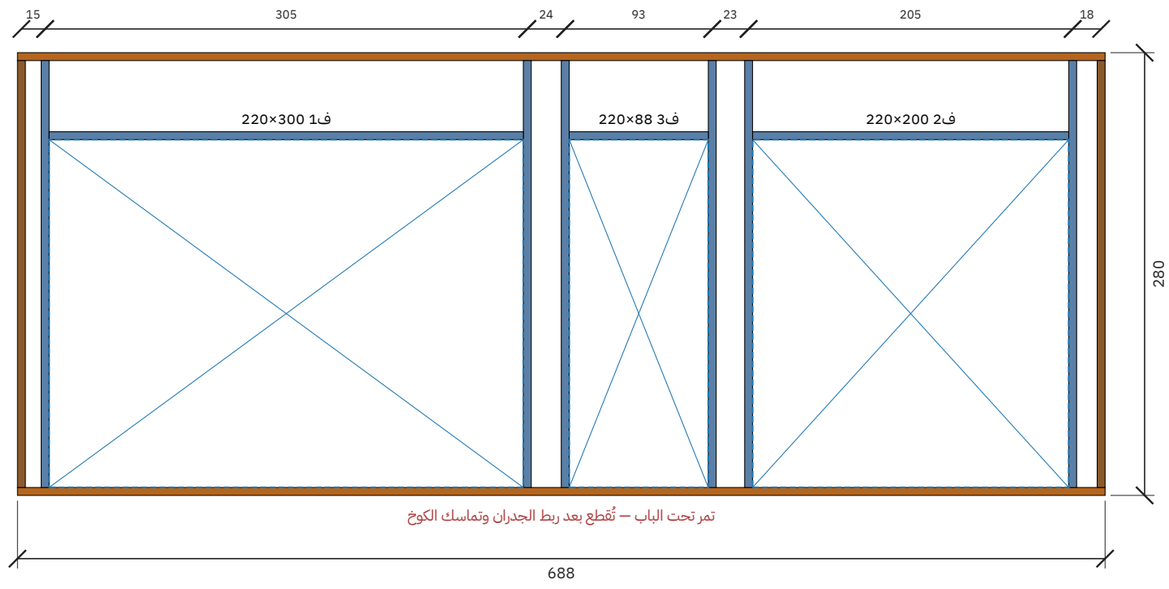


قاعدة سفلية | علوي | عمود | عمود زاوية | جنب فتحة | رأس فتحة | جلسة شباك | عمود قصير

مصنع وتد الأخشاب Watad Wood Factory	المشروع / العميل **كوخ الهدا — دورين — 3 غرف نوم + بلكونة جانبية — 10.60 × 9.00 م** **عميل — الهدا**	عنوان اللوحة **لوحات التأطير (للورشة)**	المقياس **—**	التاريخ **2026-11-08**	رقم اللوحة **W-14 (14/24)**

تأطير جدار أ-بارتشن الصالة — الطول 310 سم، الارتفاع 280 سم (داخلي)

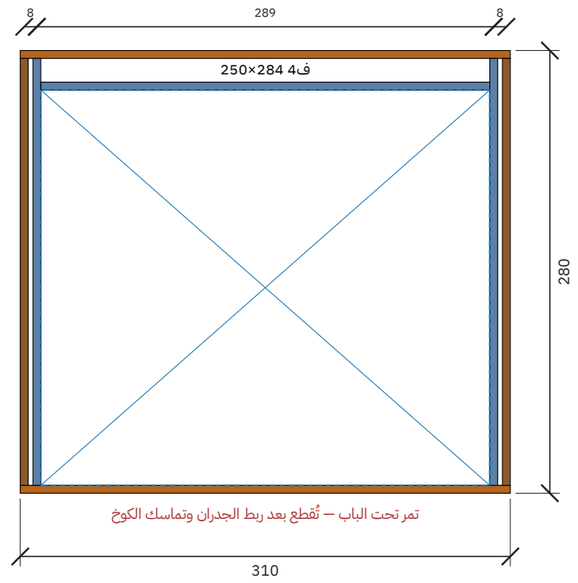


تأطير جدار أ-فاصل الحمام — الطول 210 سم، الارتفاع 280 سم (داخلي)

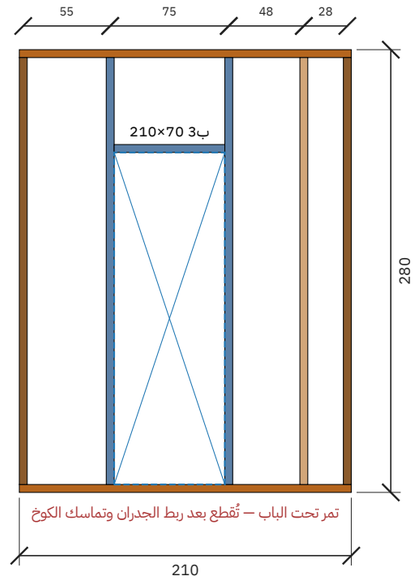


قاعدة سفلية | علوي | عمود | عمود زاوية | جنب فتحة | رأس فتحة | جلسة شباك | عمود قصير

مصنع وتد الأخشاب Watad Wood Factory	المشروع / العميل كوخ الهدا — دورين — 3 غرف نوم + بلكونة جانبية — 10.60 × 9.00 م عميل — الهدا	عنوان اللوحة لوحات التأطير (للورشة)	المقياس —	التاريخ 2026-11-08	رقم اللوحة W-15 (15/24)

تأطير جدار أ-جدار الدرج — الطول 324 سم، الارتفاع 280 سم (داخلي)

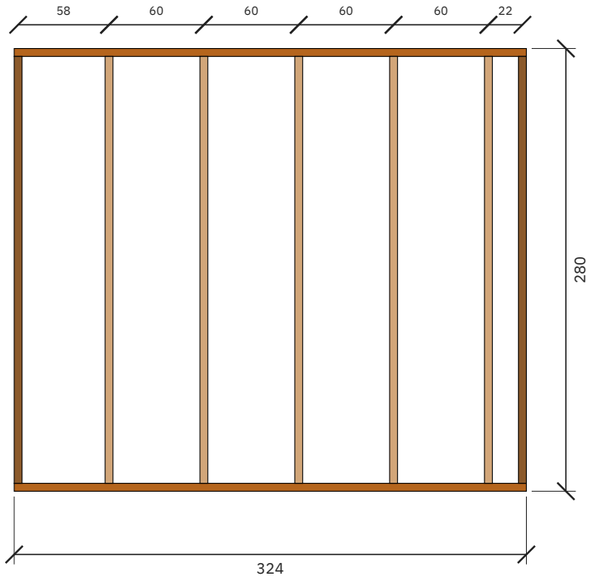


تأطير جدار أ-جدار المطبخ — الطول 428 سم، الارتفاع 280 سم (داخلي)

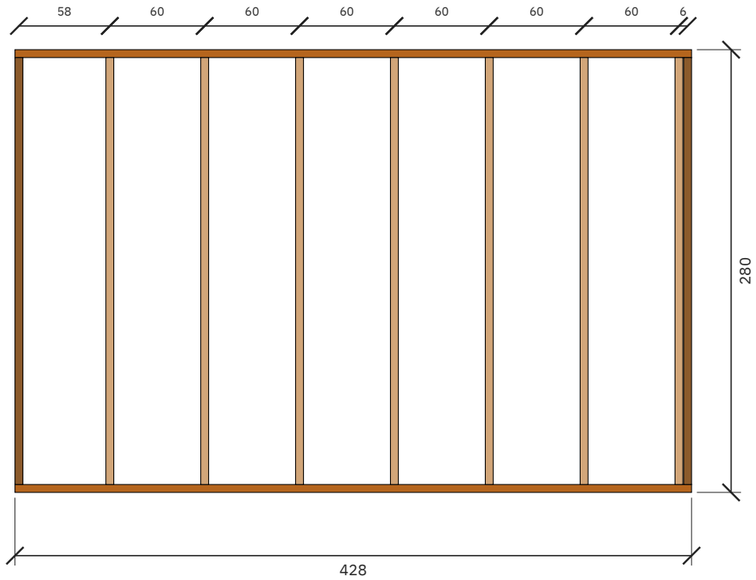


قاعدة سفلية | علوي | عمود | عمود زاوية | جنب فتحة | رأس فتحة | جلسة شباك | عمود قصير

مصنع وتد الأخشاب Watad Wood Factory	المشروع / العميل **كوخ الهدا — دورين — 3 غرف نوم + بلكونة جانبية — 10.60 × 9.00 م** **عميل — الهدا**	عنوان اللوحة **لوحات التأطير (للورشة)**	المقياس **—**	التاريخ **2026-11-08**	رقم اللوحة **W-16 (16/24)**

تأطير جدار ب-جنوب — الطول 688 سم، الارتفاع 280 سم

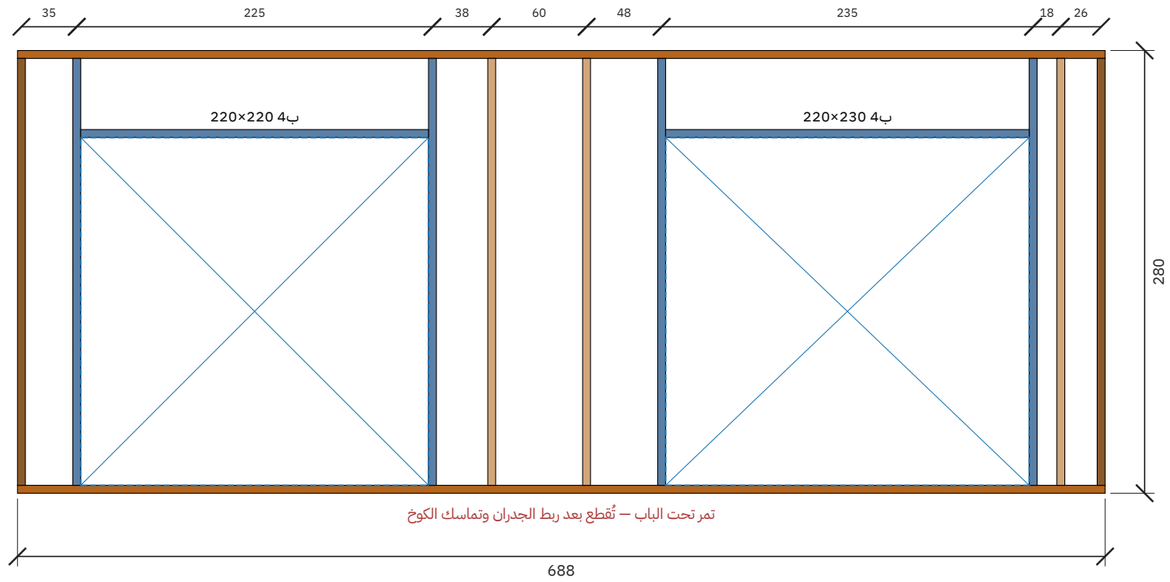

تأطير جدار ب-شرق — الطول 888 سم، الارتفاع 280 سم

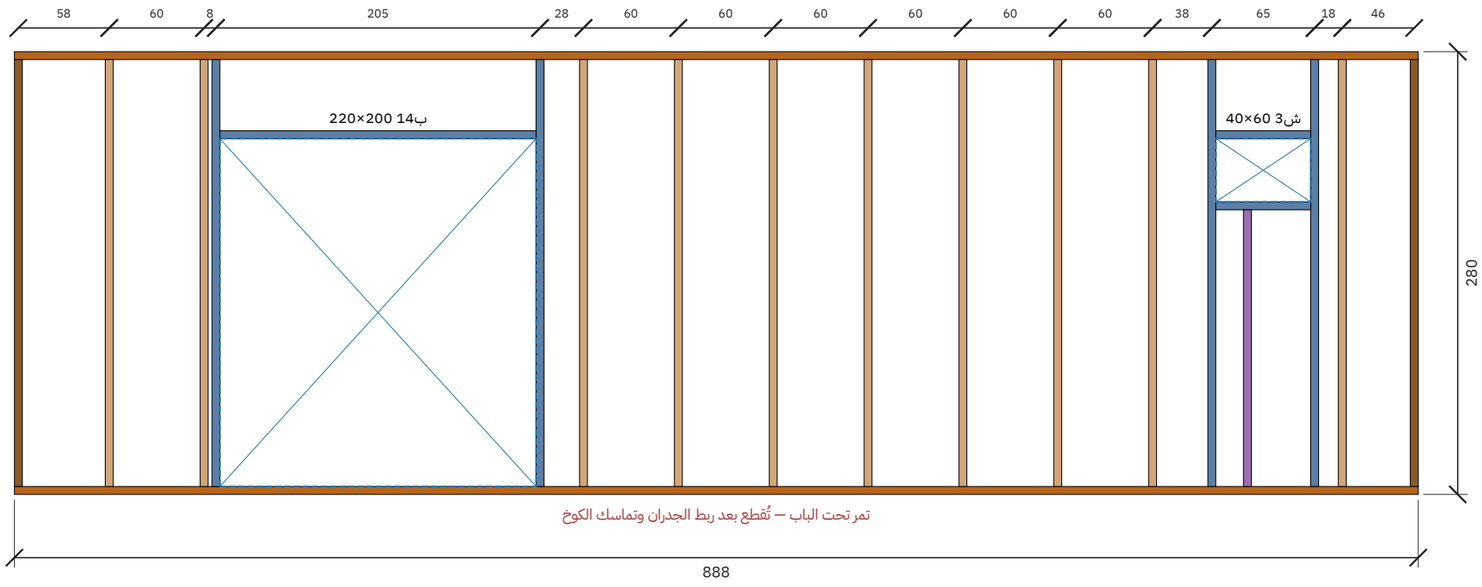


قاعدة سفلية | علوي | عمود | عمود زاوية | جنب فتحة | رأس فتحة | جلسة شباك | عمود قصير


المشروع / العميل	عنوان اللوحة	المقياس	التاريخ	رقم اللوحة
كوخ الهدا — دورين — 3 غرف نوم + بلكونة جانبية — 10.60 × 9.00 م **عميل — الهدا**	**لوحات التأطير (للورشة)**	—	**2026-11-08**	**W-17 (17/24)**

مصنع وتد الأخشاب
Watad Wood Factory

تأطير جدار ب-شمال — الطول 688 سم، الارتفاع 280 سم

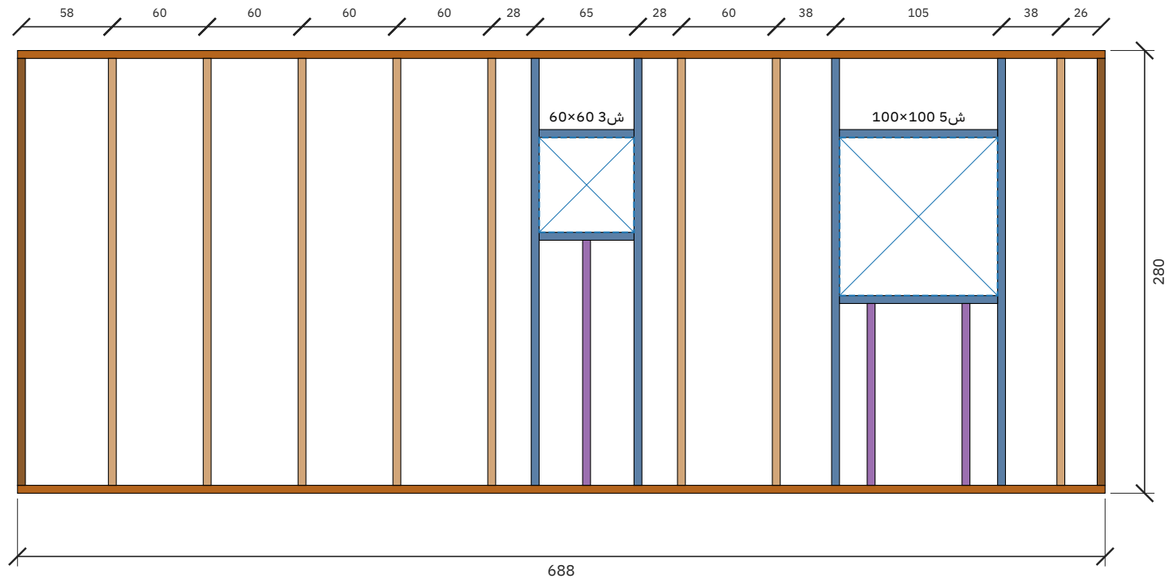


تأطير جدار ب-غرب — الطول 888 سم، الارتفاع 280 سم

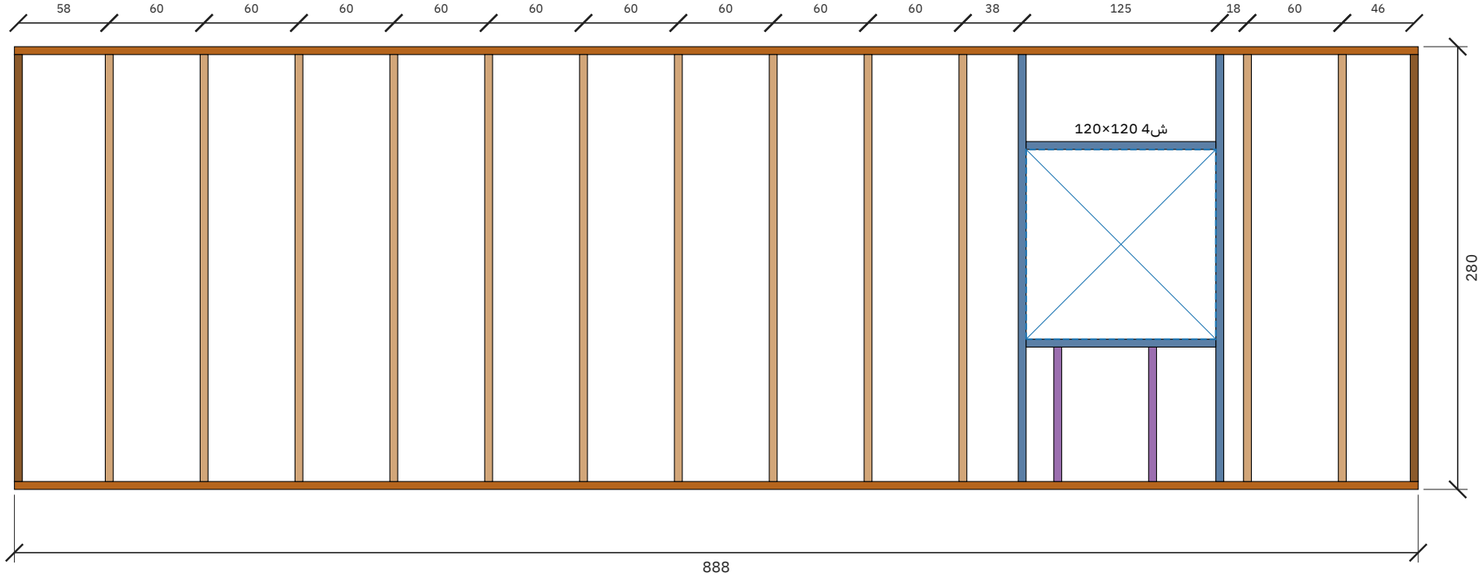


قاعدة سفلية | علوي | عمود | عمود زاوية | جنب فتحة | رأس فتحة | جلسة شباك | عمود قصير

مصنع وتد الأخشاب Watad Wood Factory	المشروع / العميل كوخ الهدا — دورين — 3 غرف نوم + بلكونة جانبية — 10.60 × 9.00 م عميل — الهدا	عنوان اللوحة لوحات التأطير (للورشة)	المقياس —	التاريخ 2026-11-08	رقم اللوحة W-18 (18/24)

تأطير جدار ب-فاصل أمامي — الطول 688 سم، الارتفاع 280 سم (داخلي)

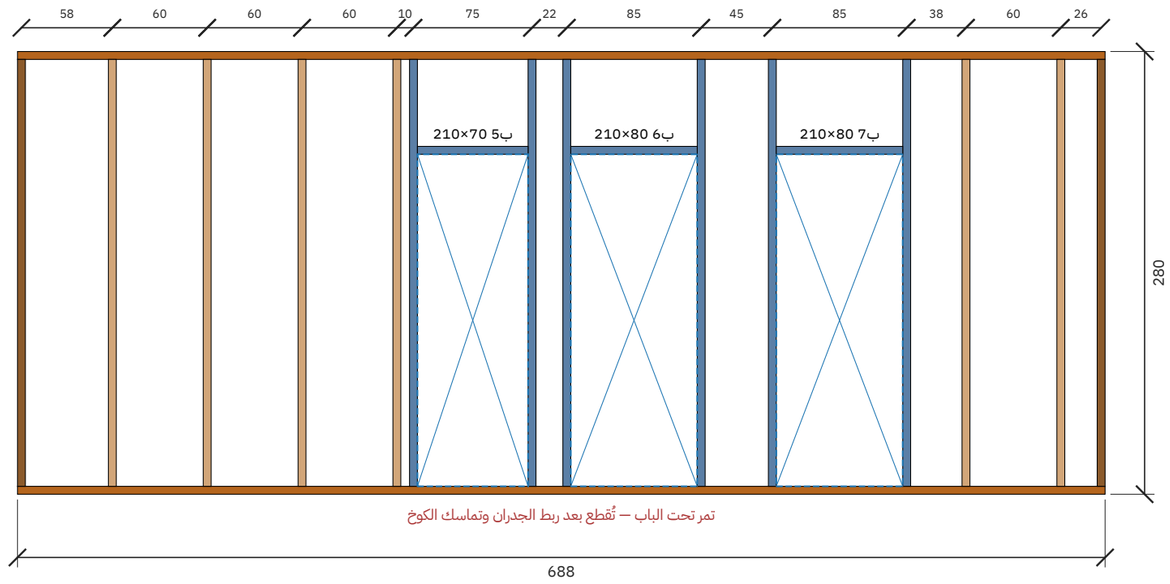

تأطير جدار ب-فاصل الغرف — الطول 460 سم، الارتفاع 280 سم (داخلي)

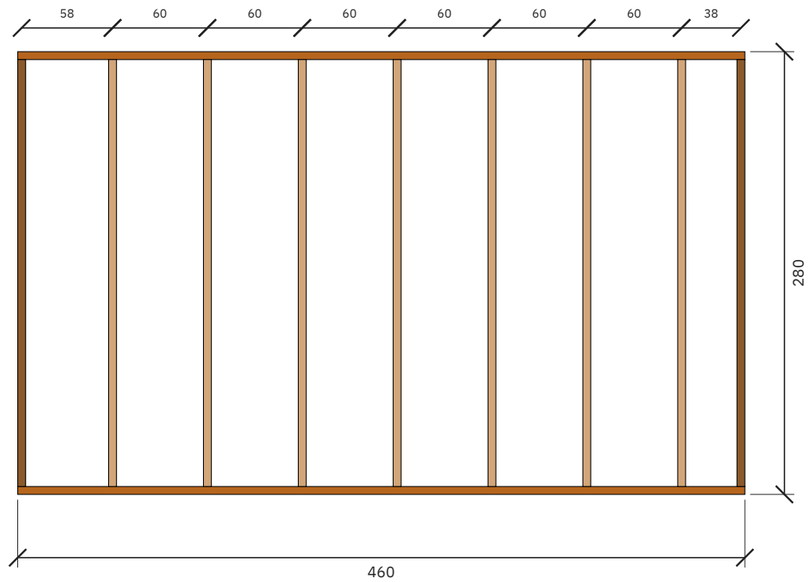


قاعدة سفلية | علوي | عمود | عمود زاوية | جنب فتحة | رأس فتحة | جلسة شباك | عمود قصير


المشروع / العميل	عنوان اللوحة	المقياس	التاريخ	رقم اللوحة
كوخ الهدا — دورين — 3 غرف نوم + بلكونة جانبية — 10.60 × 9.00 م **عميل — الهدا**	**لوحات التأطير (للورشة)**	—	**2026-11-08**	**W-19 (19/24)**

مصنع وتد الأخشاب
Watad Wood Factory

تأطير جدار ب-فاصل الحمام — الطول 210 سم، الارتفاع 280 سم (داخلي)

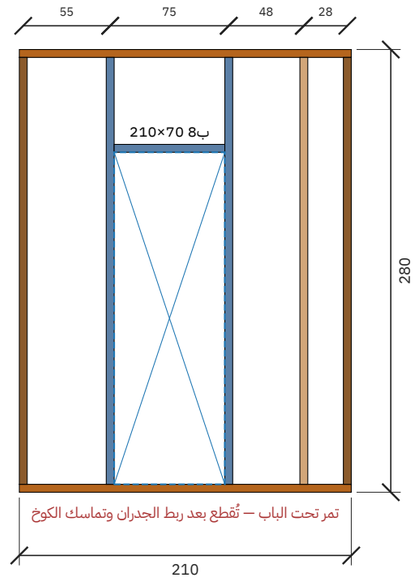

تأطير جدار ب-جدار الدرج — الطول 324 سم، الارتفاع 280 سم (داخلي)

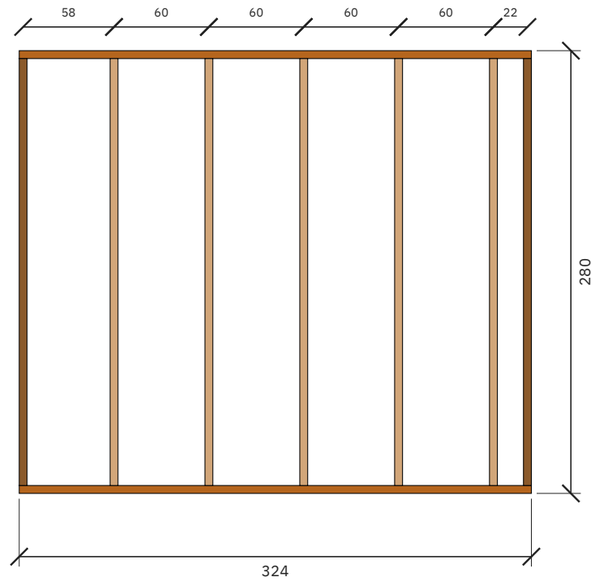


عمود قصير | جلسة شباك | رأس فتحة | جنب فتحة | عمود زاوية | عمود | علوي | قاعدة سفلية


المشروع / العميل	عنوان اللوحة	المقياس	التاريخ	رقم اللوحة
كوخ الهدا — دورين — 3 غرف نوم + بلكونة جانبية — 10.60 × 9.00 م **عميل — الهدا**	**لوحات التأطير (للورشة)**	—	**2026-11-08**	**W-20 (20/24)**

مصنع وتد الأخشاب
Watad Wood Factory

تأطير جدار ب-جدار الملابس — الطول 428 سم، الارتفاع 280 سم (داخلي)

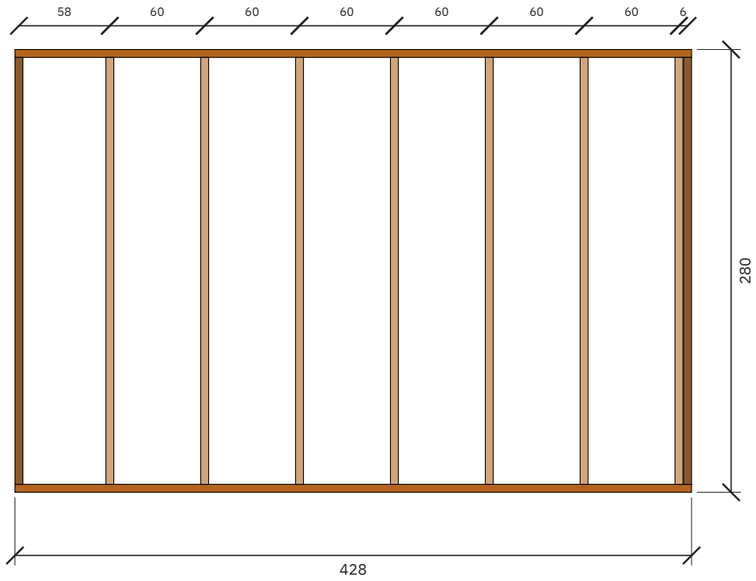

تأطير جدار ب-فاصل حمام الماستر — الطول 238 سم، الارتفاع 280 سم (داخلي)

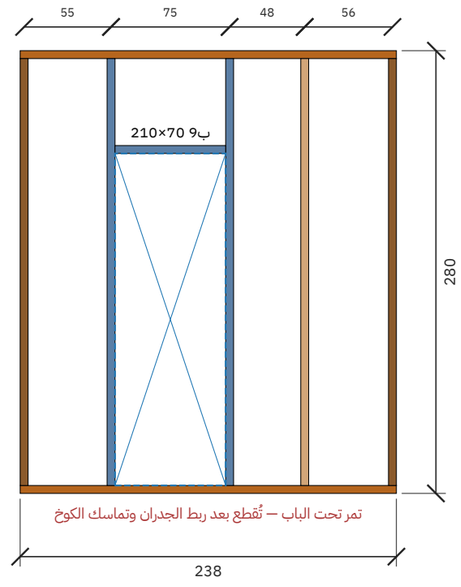

قاعدة سفلية | علوي | عمود | عمود زاوية | جنب فتحة | رأس فتحة | جلسة شباك | عمود قصير

مصنع وتد الأخشاب Watad Wood Factory	المشروع / العميل كوخ الهدا — دورين — 3 غرف نوم + بلكونة جانبية — 10.60 × 9.00 م عميل — الهدا	عنوان اللوحة لوحات التأطير (للورشة)	المقياس —	التاريخ 2026-11-08	رقم اللوحة W-21 (21/24)

جدول الكميات وخطة تقطيع الطبليات

البند	القيمة
الارتفاع المطلوب / المعتمد	280 / 280 سم
السقف	جملون 30° — أعلى نقطة 787 سم من وجه الصبة
المدادات 5×15	42 مداد (21 لكل جهة) × حتى 445 سم — من طبلية 480
طبليات الطريقة الأولى (مداد + عمود)	42 طبلية × 480 سم
طبليات الطريقة الثانية (3 أعمدة)	87 طبلية × 320 سم
طبليات الطريقة الثانية (طويلة)	7 طبلية × 480 سم
مدادات أرضية الدور العلوي 5×15 كل 60 سم	75 مداد — 106سم×15، 124سم×15، 248سم×15، 250سم×15، 370سم×15 (طبلية 480 بالطريقة الأولى)
إجمالي الطبليات 5×22.5	211
إجمالي قطع 5×7	339
قائمة تقطيع 5×7	888سم×10 | 688سم×12 | 460سم×2 | 428سم×4 | 360سم×8 | 324سم×4 | 310سم×2 | 300سم×1 | 284سم×1
	270سم×237 | 260سم×1 | 238سم×2 | 230سم×1 | 220سم×1 | 210سم×4 | 200سم×4 | 175سم×1 | 170سم×1
ألواح تلبيس 2.5 سم	632 لوح × 400 سم (مجموع الصفوف 2447.6 م، 48 وجه)
أسمنت بورد 12 مم (122×244)	76 لوح (داخل دورات المياه)
العزل	401 لوح فوم صخري 80

جدول الكميات وخطة تقطيع الطبليات

البند	القيمة
الصبة	يجهزها العميل — 20 سم، مفرغة تحت دورات المياه

مراجعة التصميم مقابل قواعد المصنع

النوع	البند	التفاصيل	المقترح
ملاحظة	حمام الماستر غير مكدّس	دورة المياه العلوية ليست فوق دورة مياه أرضية — تحتاج خط صرف خارجي مستقل على الجدار.	يُفضّل تكديس الحمامات فوق بعض (قاعدة المصنع).
ملاحظة	بحر المدادات	أطول بحر بدون جدار داخلي يحمل المداد: جهة أ: 350 سم، جهة ب: 350 سم. يحتاج رقم المصنع لأقصى بحر مسموح لتحديد المدادات اللي تُقوّى 20×5.	
ملاحظة	الصبة والدرج	ارتفاع الصبة 45 سم ← 3 درجة بقائمة 15.0 سم.	
ملاحظة	مناسيب رؤوس الفتحات	رؤوس الأبواب والشبابيك على مناسيب مختلفة: 210، 220، 240، 250 سم.	
سؤال	يحتاج تأكيد	أقصى بحر للمداد بدون جدار داخلي قبل إضافة تقوية 7×5 (مداد 20×5)؟	
سؤال	يحتاج تأكيد	التغطية الصافية للوح التلبيس بعد التعشيق (مستنتجة مؤقتاً 18.67 سم من 280/15)؟	
سؤال	يحتاج تأكيد	هل يوضع أعمدة قصيرة فوق رأس الشباك/الباب إلى العلوي؟	
سؤال	يحتاج تأكيد	مكان الوصلة في القاعدة والعلوي إذا الجدار أطول من الطبلية؟	