
المسقط الأفقي مع الفرش — الدور الأرضي

الأبعاد بالسنتيمتر - الجدران: قوائم 7×5 + تلبيس 2.5 من الجهتين (12 سم) | منسوب الأرضية +0.00

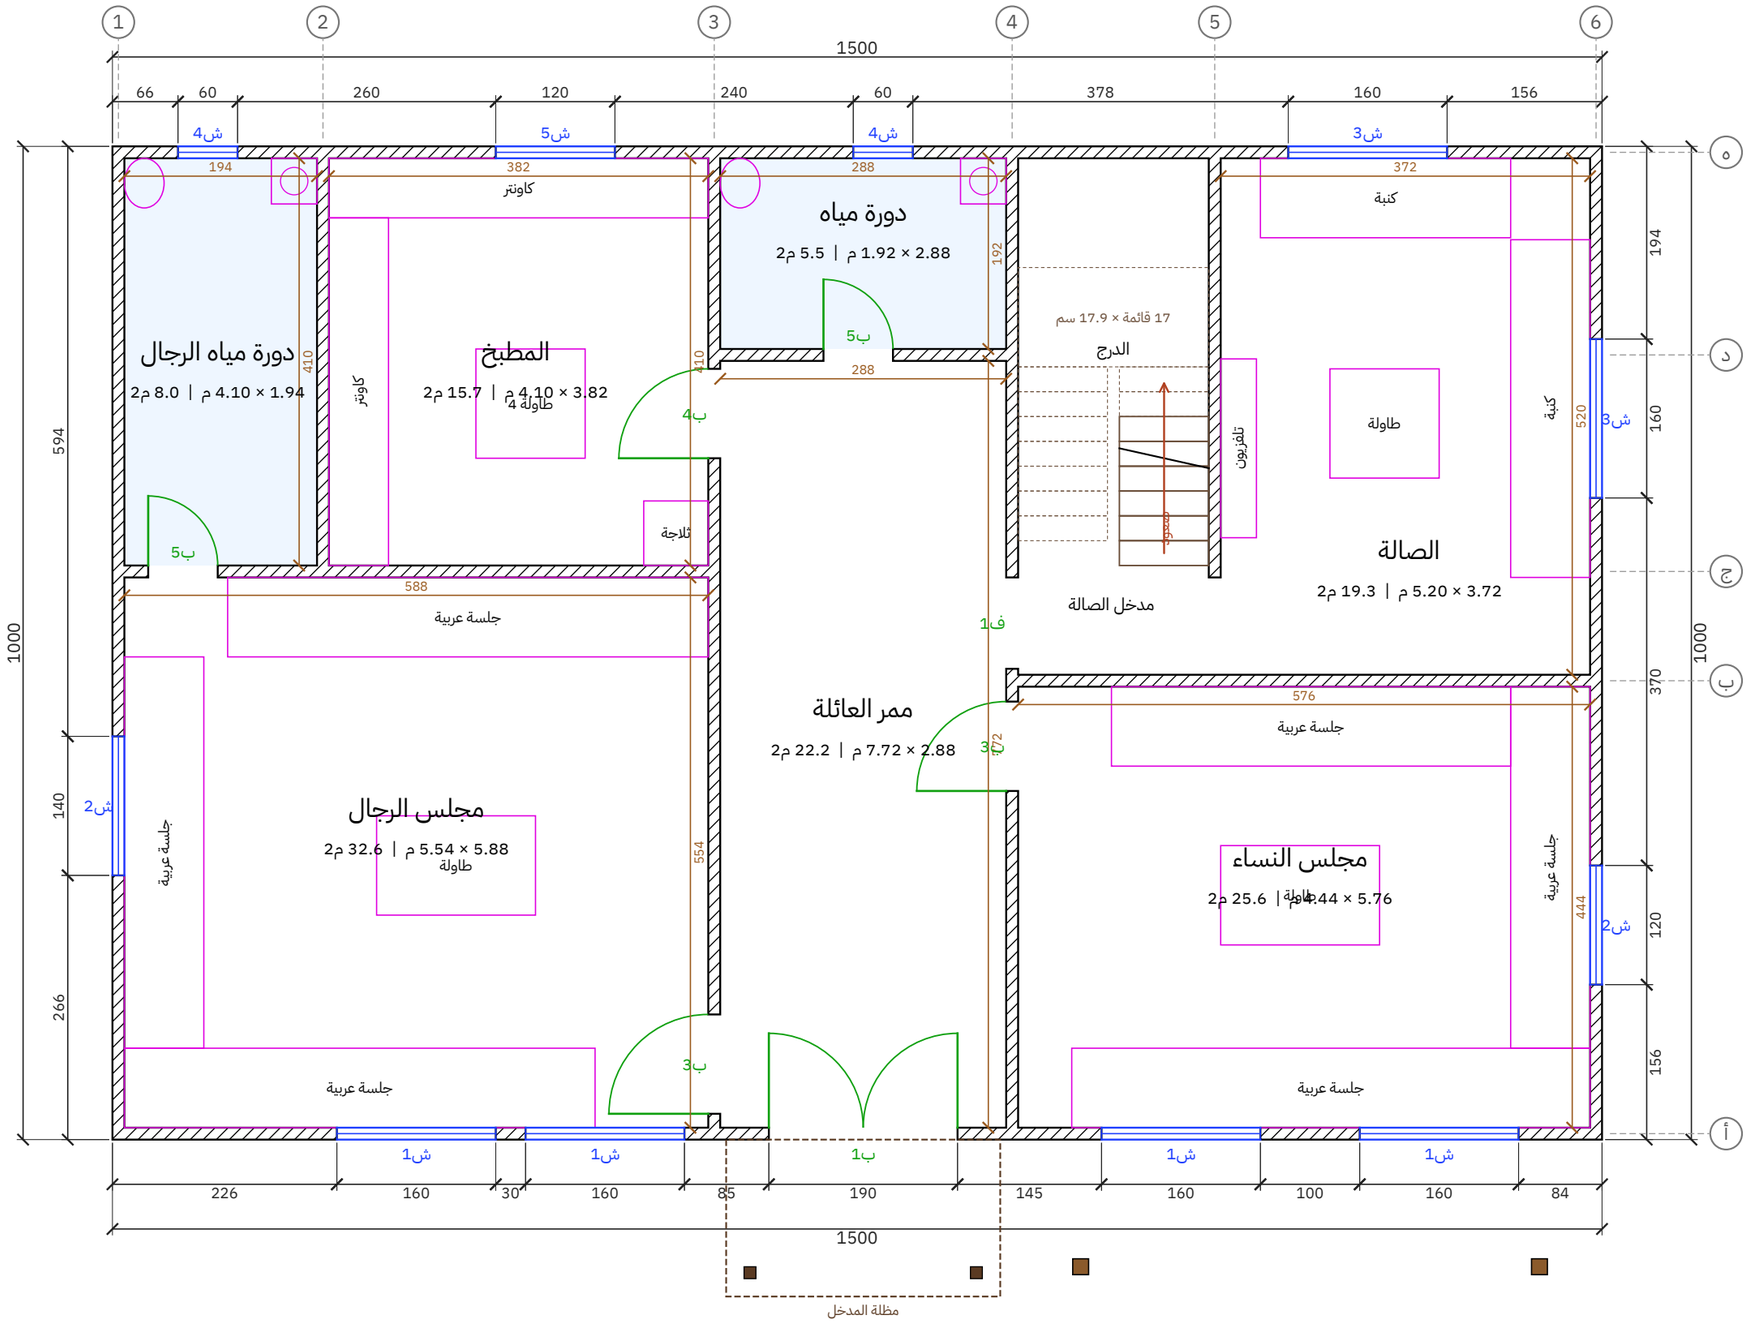


المشروع / العميل	عنوان اللوحة	المقياس	التاريخ	رقم اللوحة
كوخ خشب دورين — مجلس رجال ومجلس نساء + 4 غرف — 15.00 × 10.00 م (300 م²) **عميل — كوخ دورين**	**المسقط الأفقي — الدور الأرضي**	**1:50**	**2026-10-24**	**A-01 (1/11)**

مصنع وتد الأخشاب
Watad Wood Factory


المسقط الأفقي مع الفرش — الدور الأول

الأبعاد بالسنتيمتر - الجدران: قوائم 7×5 + تلبيس 2.5 من الجهتين (12 سم) | منسوب الأرضية +3.05

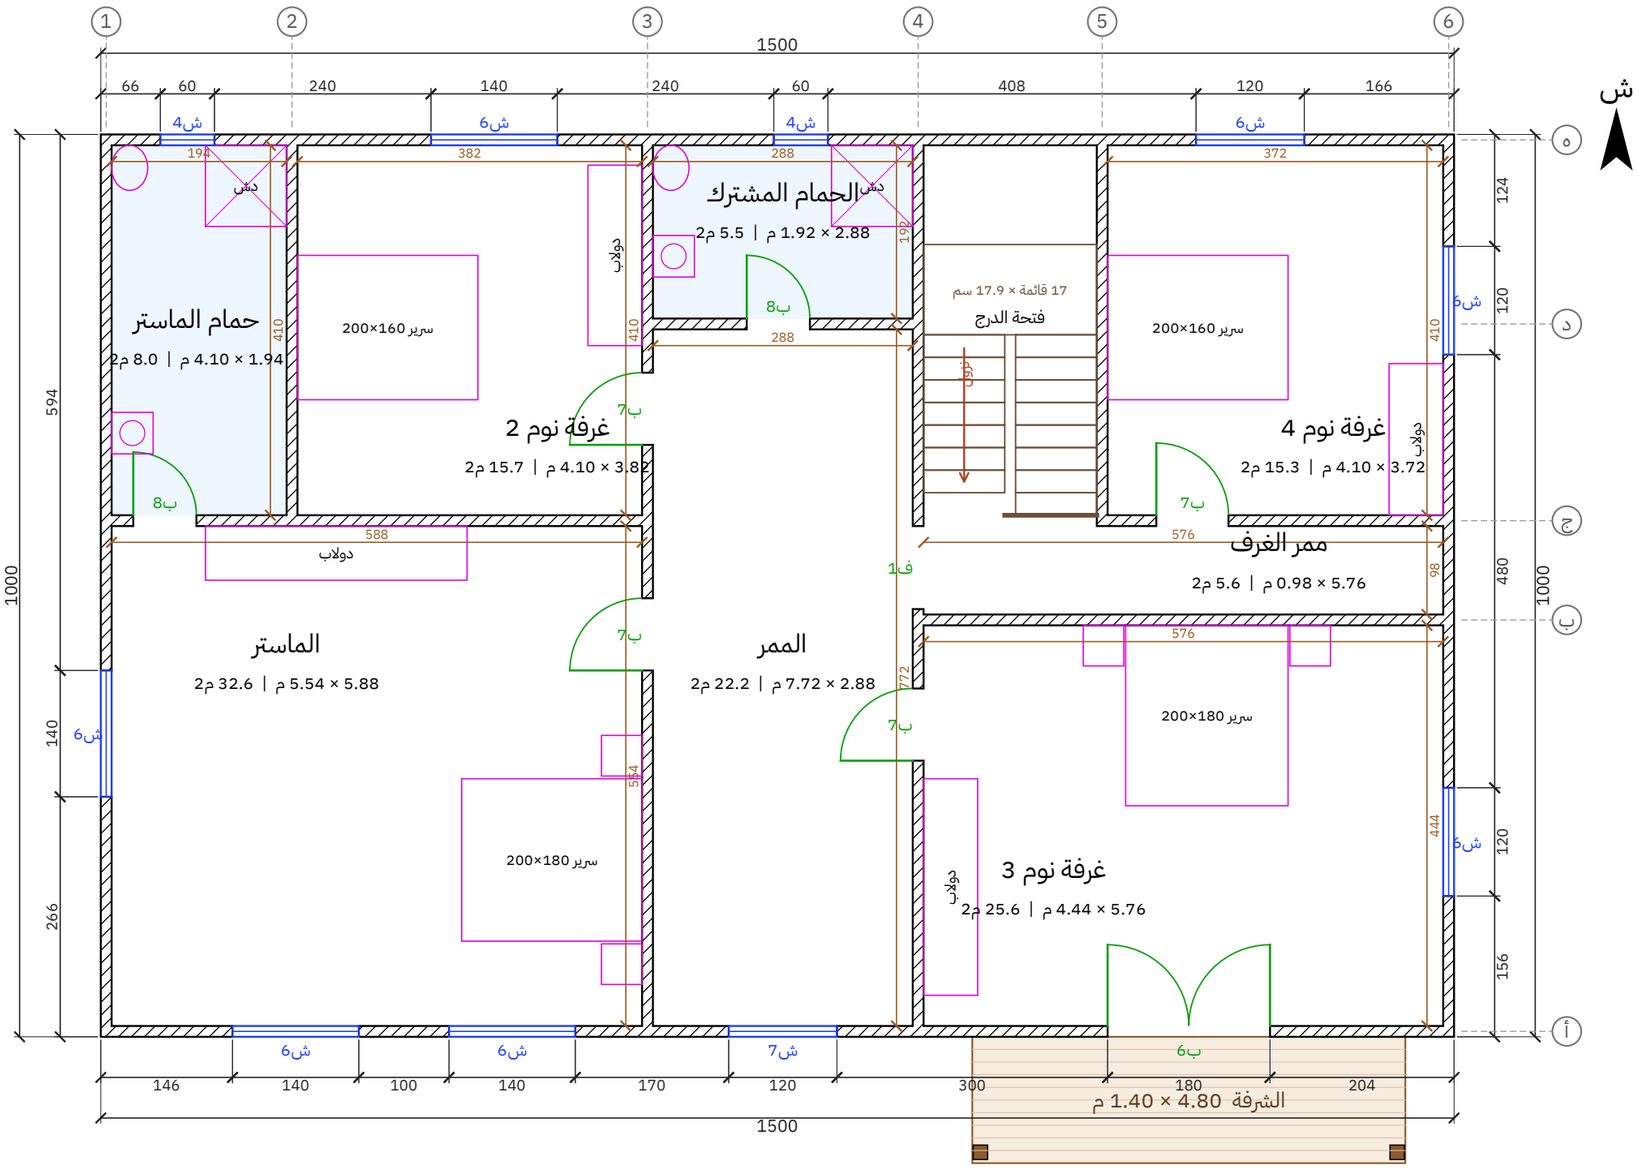


المشروع / العميل	عنوان اللوحة	المقياس	التاريخ	رقم اللوحة
كوخ خشب دورين — مجلس رجال ومجلس نساء + 4 غرف — 15.00 × 10.00 م (300 م²) عميل — كوخ دورين	المسقط الأفقي — الدور الأول	1:50	2026-10-24	A-02 (2/11)

مصنع وتد الأخشاب
Watad Wood Factory

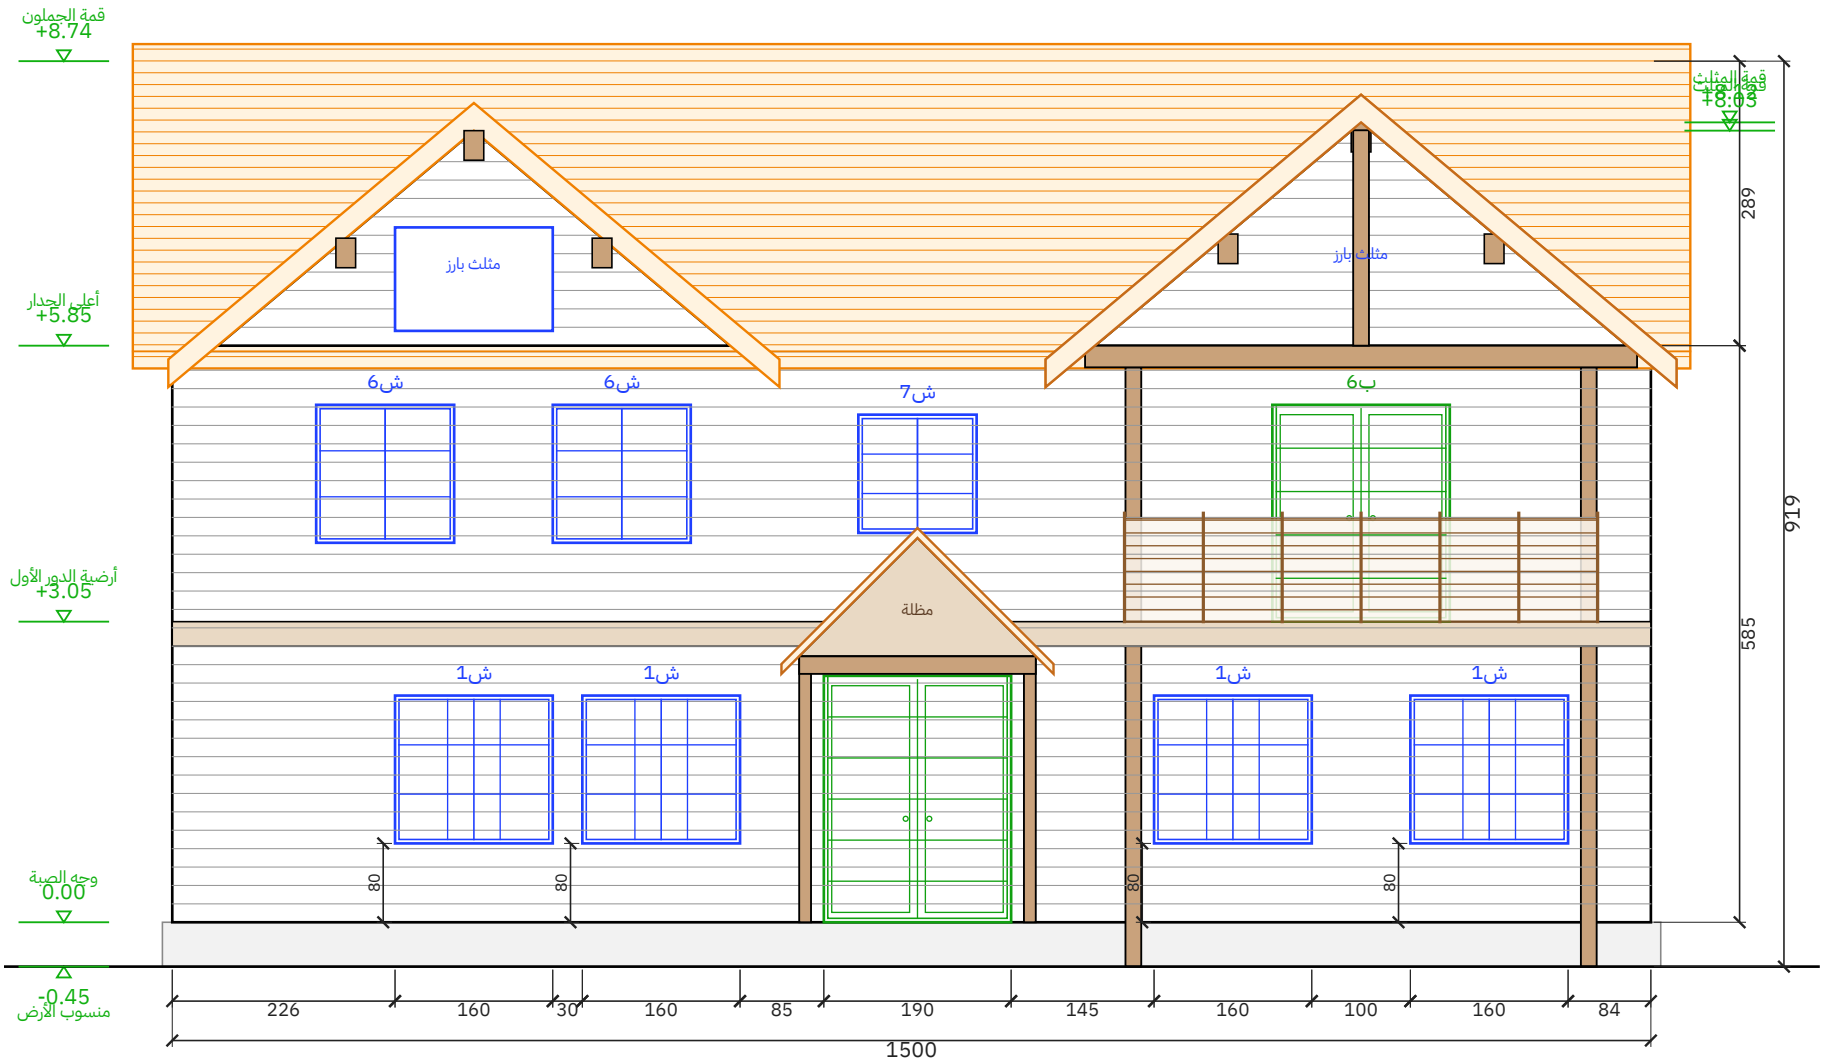

الواجهة الأمامية

مقياس 1:50 | الوحدة: سم

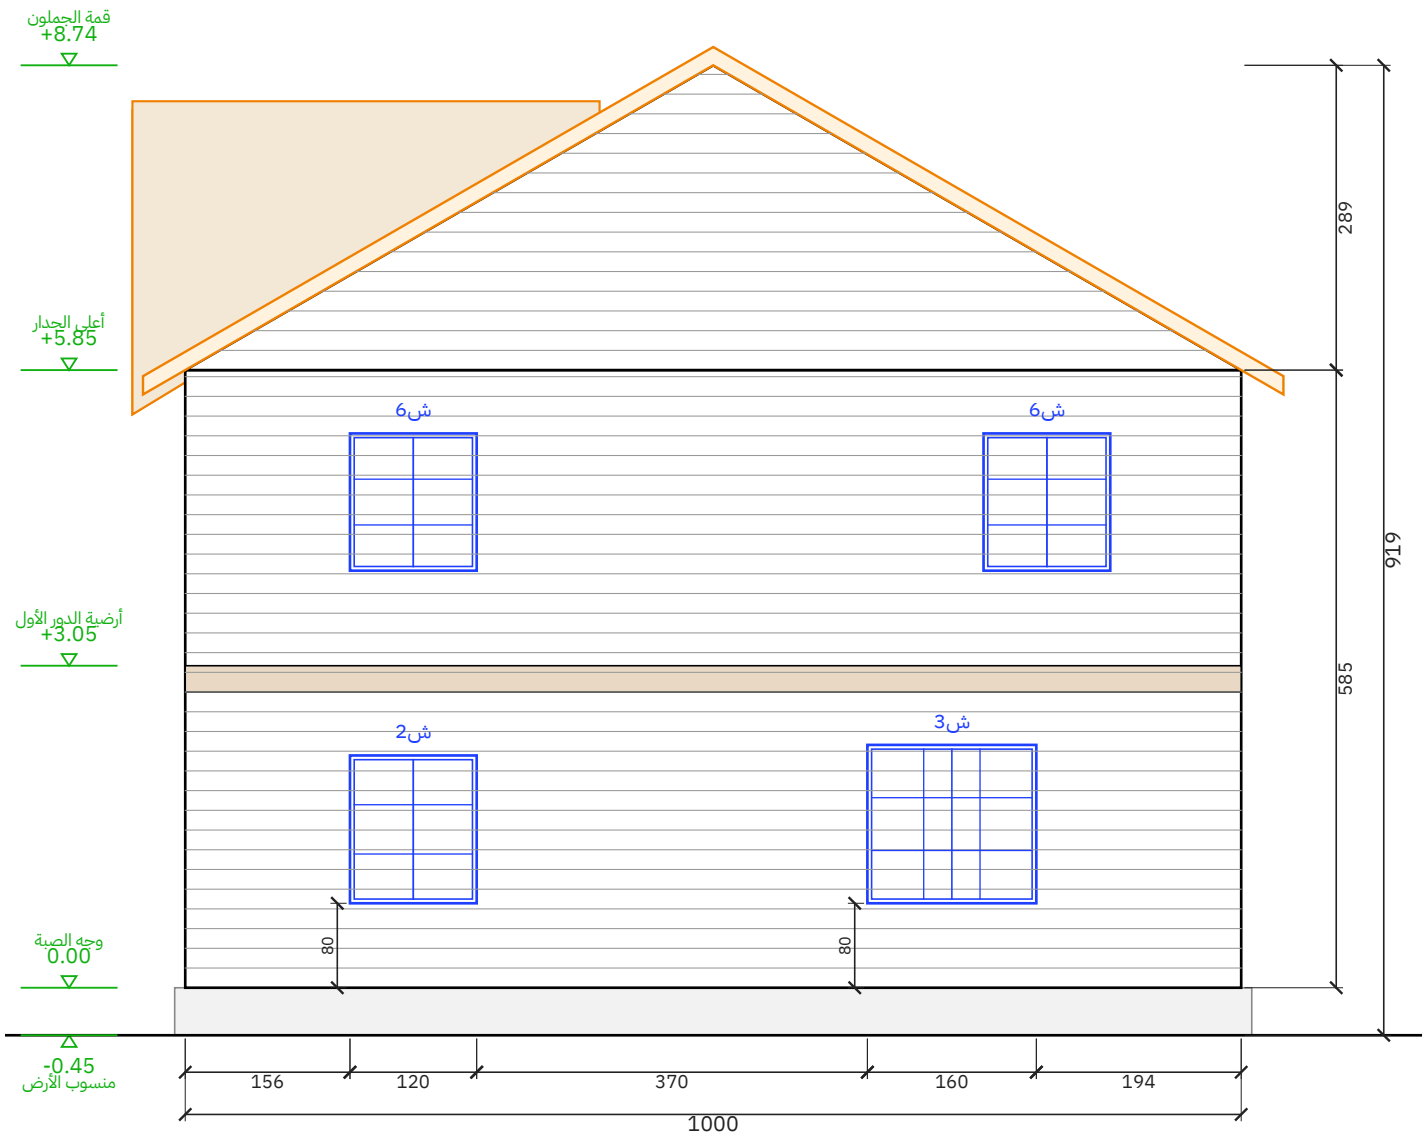


الواجهة الشرقية

مقياس 1:50 | الوحدة: سم


المشروع / العميل	عنوان اللوحة	المقياس	التاريخ	رقم اللوحة
كوخ خشب دورين – مجلس رجال ومجلس نساء + 4 غرف – 10.00 × 15.00 م (300 م²) **عميل – كوخ دورين**	**الواجهة الأمامية والواجهة الشرقية**	**1:50**	**2026-10-24**	**A-03 (3/11)**

مصنع وتد الأخشاب
Watad Wood Factory

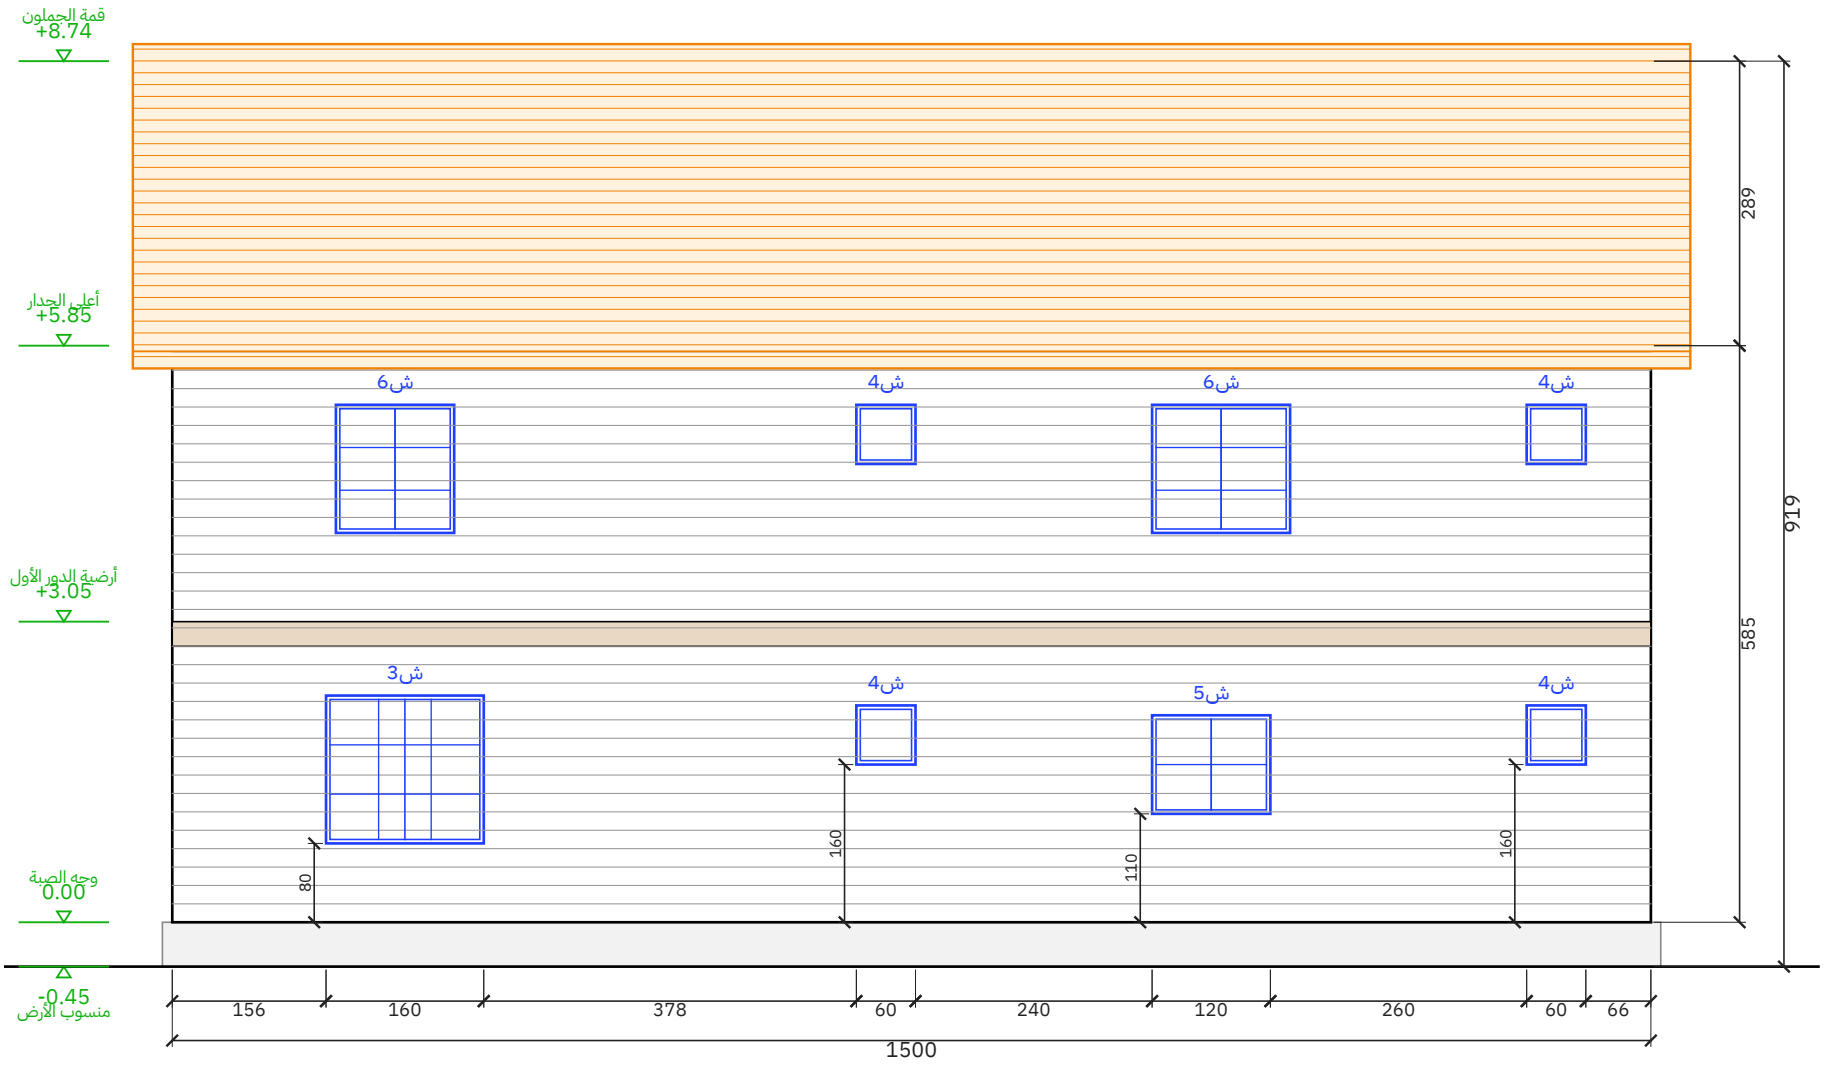

الواجهة الخلفية

مقياس 1:50 | الوحدة: سم

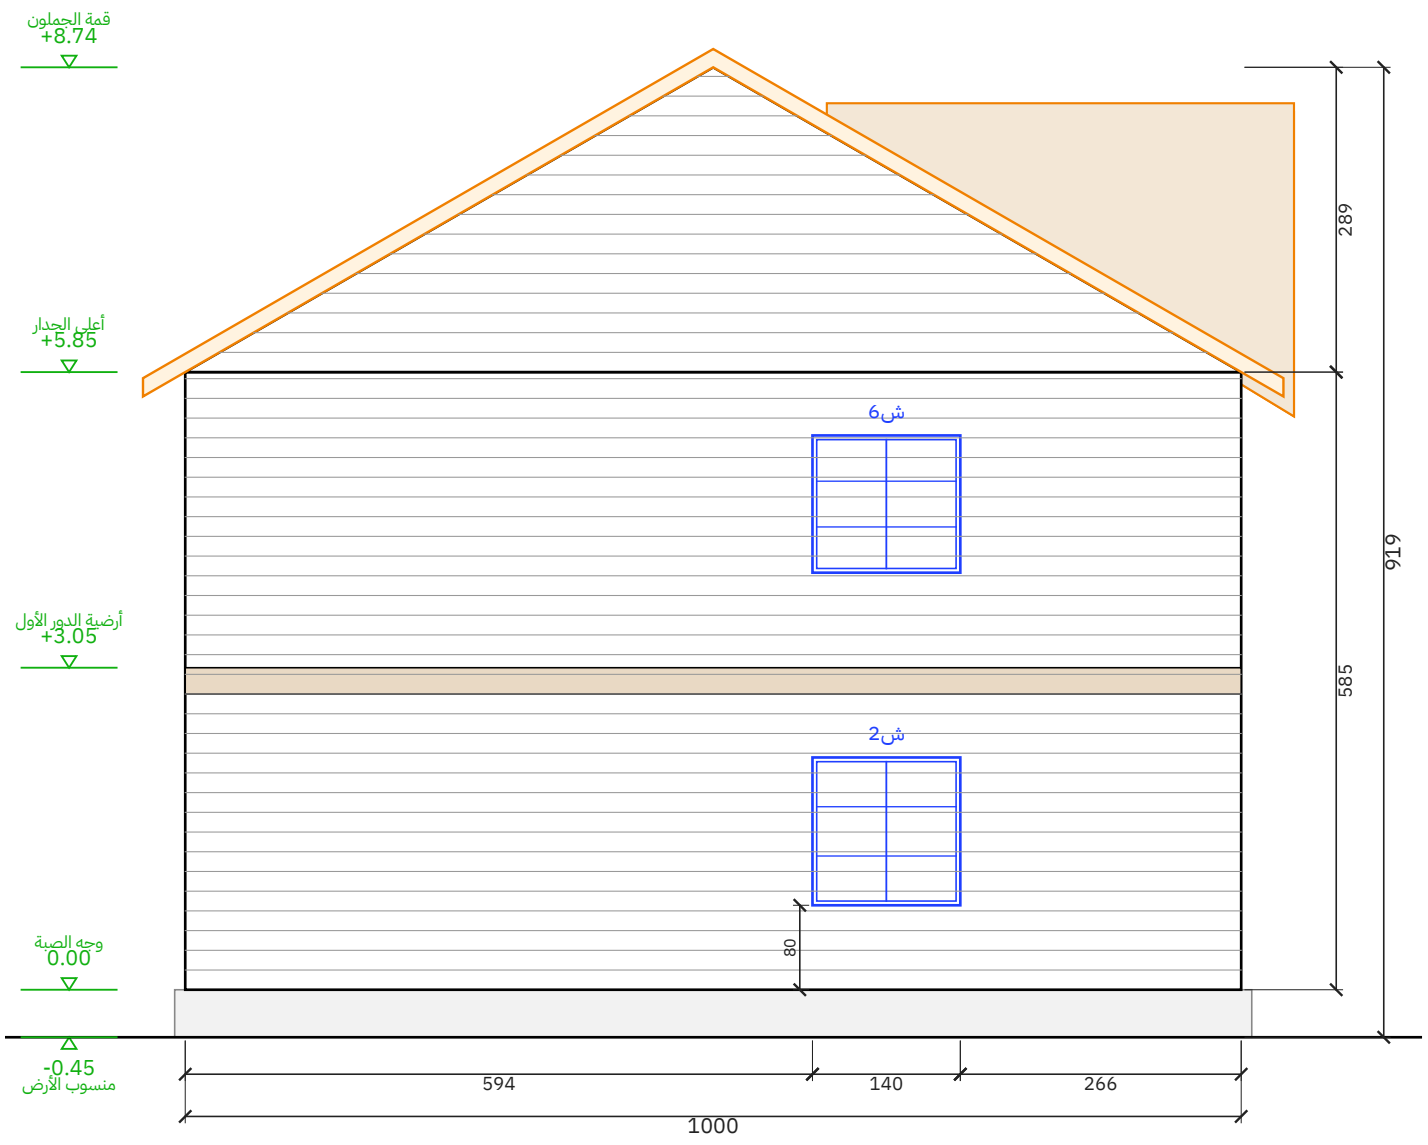

الواجهة الغربية


مقياس 1:50 | الوحدة: سم

المشروع / العميل	عنوان اللوحة	المقياس	التاريخ	رقم اللوحة
كوخ خشب دورين – مجلس رجال ومجلس نساء + 4 غرف – 10.00 × 15.00 م (300 م²) عميل – كوخ دورين	الواجهة الخلفية والواجهة الغربية	1:50	2026-10-24	A-04 (4/11)


مصنع وتد الأخشاب
Watad Wood Factory

قطاع عرضي أ-أ

مقياس 1:50 | الوحدة: سم

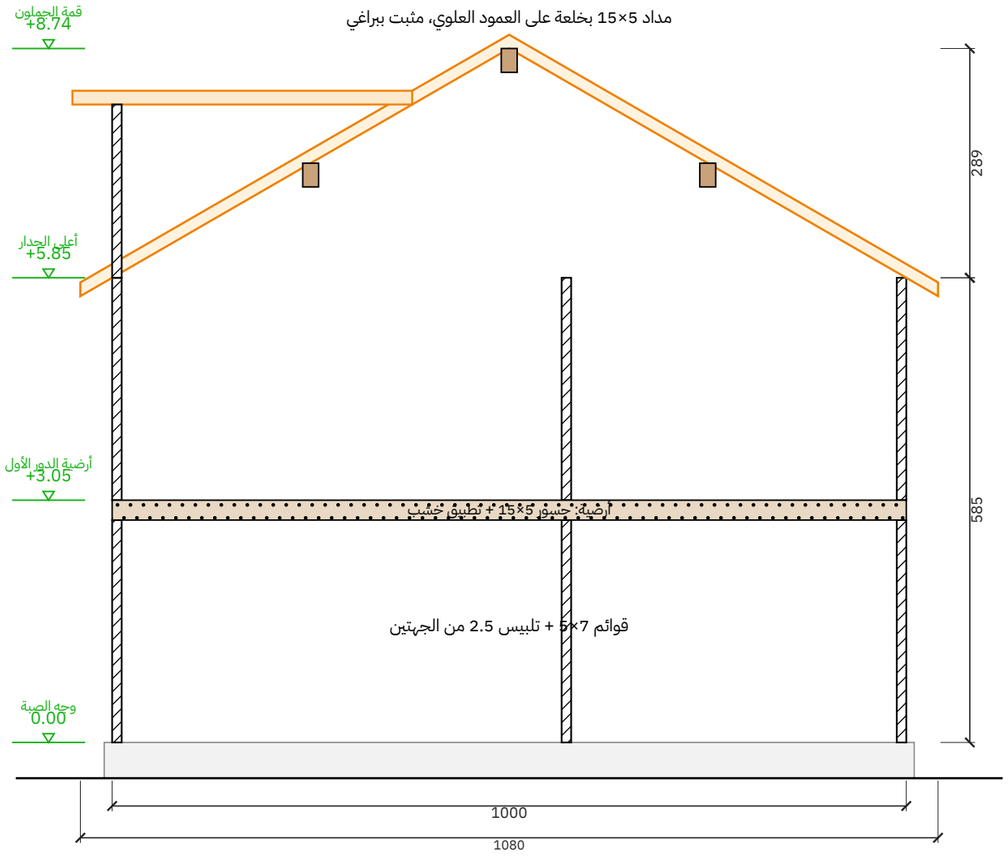


تفصيلة جلوس المداد على العلوي (1:5)

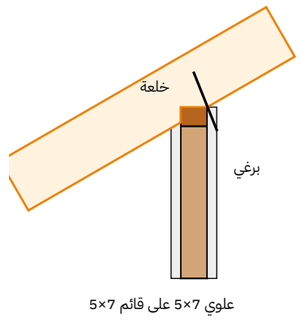

علوي 7×5 على قائم 7×5

مسقط السقف (جملون)

رفرف 40 سم من كل جهة | مقياس 1:50

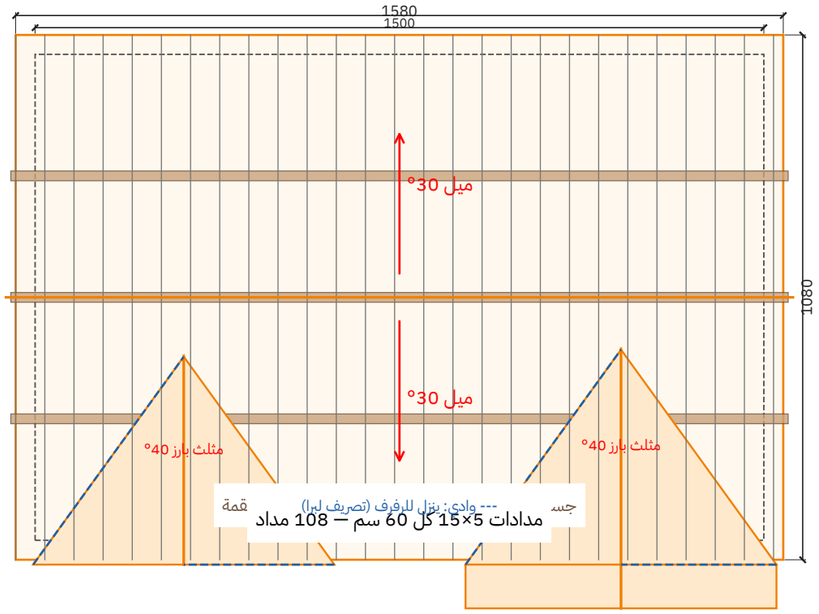

المشروع / العميل	عنوان اللوحة	المقياس	التاريخ	رقم اللوحة
كوخ خشب دورين — مجلس رجال ومجلس نساء + 4 غرف — 15.00 × 10.00 م (300 م²) **عميل — كوخ دورين**	**مسقط السقف والقطاع**	**1:50**	**2026-10-24**	**A-05 (5/11)**

مصنع وتد الأخشاب
Watad Wood Factory

جدول مقاسات الأبواب والشبابيك

مقاس الفتحة الصافي في الجدار - الوحدة: سم

الرمز	النوع	العرض (سم)	الارتفاع (سم)	ارتفاع الجلسة (سم)	العدد	الموقع
ب1	باب مزدوج	190	250	-	1	الأمامية
ب3	باب	100	220	-	1	مجلس الرجال
ب3	باب	90	210	-	1	مجلس النساء
ب4	باب	90	210	-	1	المطبخ
ب5	باب	70	210	-	2	دورة مياه الرجال - دورة مياه
ب6	باب مزدوج	180	220	-	1	الأمامية
ب7	باب	80	210	-	4	الماستر - غرفة 2 - غرفة 3 - غرفة 4
ب8	باب	70	210	-	2	حمام الماستر - الحمام المشترك
ف1	باب	92	220	-	2	الممر — الصالة - الممر — الدرج
ش1	شباك	160	150	80	4	الأمامية 4
ش2	شباك	120	140	80	1	الشرقية
ش2	شباك	140	140	80	1	الغربية
ش3	شباك	160	150	80	2	الشرقية - الخلفية
ش4	شباك	60	60	160	4	الخلفية 4
ش5	شباك	120	100	110	1	الخلفية
ش6	شباك	140	140	80	2	الأمامية 2
ش6	شباك	120	130	90	3	الشرقية 2 - الخلفية
ش6	شباك	140	130	90	2	الخلفية - الغربية
ش7	شباك	120	120	90	1	الأمامية

الإجمالي: أبواب 15 - شبابيك 21

جدول المساحات وبيانات المشروع

بيانات المشروع


البند	البيان
المشروع	كوخ خشب دورين — مجلس رجال ومجلس نساء + 4 غرف — 15.00 × 10.00 م (300 م²)
العميل	عميل — كوخ دورين
الموقع	—
الاستخدام	سكن عائلي
التاريخ	2026-10-24
نظام البناء	هيكل خشب 5×7 + تلبيس 2.5 سم من الجهتين
السقف	جملون 30° — قرميد معدني + 2 مثلث بارز

جدول المساحات


م	الفراغ	الأبعاد (م)	المساحة (م2)
1	أرضي — مجلس الرجال	5.88 × 5.54	32.58
2	أرضي — دورة مياه الرجال	1.94 × 4.10	7.95
3	أرضي — المطبخ	3.82 × 4.10	15.66
4	أرضي — ممر العائلة	2.88 × 7.72	22.23
5	أرضي — دورة مياه	2.88 × 1.92	5.53
6	أرضي — مجلس النساء	5.76 × 4.44	25.57
7	أرضي — مدخل الصالة	1.92 × 1.04	2.00
8	أرضي — الدرج	1.92 × 4.10	7.87
9	أرضي — الصالة	3.72 × 5.20	19.34
10	أول — الماستر	5.88 × 5.54	32.58
11	أول — حمام الماستر	1.94 × 4.10	7.95
12	أول — غرفة نوم 2	3.82 × 4.10	15.66
13	أول — الممر	2.88 × 7.72	22.23
14	أول — الحمام المشترك	2.88 × 1.92	5.53
15	أول — غرفة نوم 3	5.76 × 4.44	25.57
16	أول — ممر الغرف	5.76 × 0.98	5.64
17	أول — غرفة نوم 4	3.72 × 4.10	15.25
	المساحة الصافية الداخلية		**269.17**
	الشرفة	**4.80 × 1.40**	**6.72**
	المساحة الإجمالية المبنية	**15.00 × 10.00 × 2 دور**	**300.00**
	المساحة الكلية (المبنية + التراس)		**306.72**

لقطات المنظور الخارجي


المنظور الأمامي

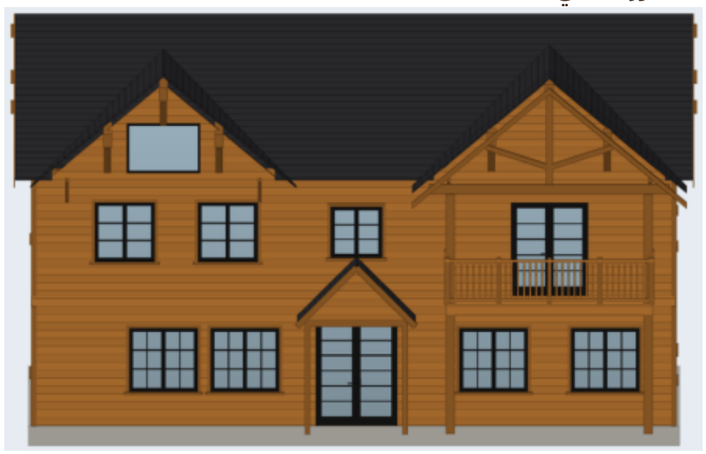

منظور أمامي من اليسار

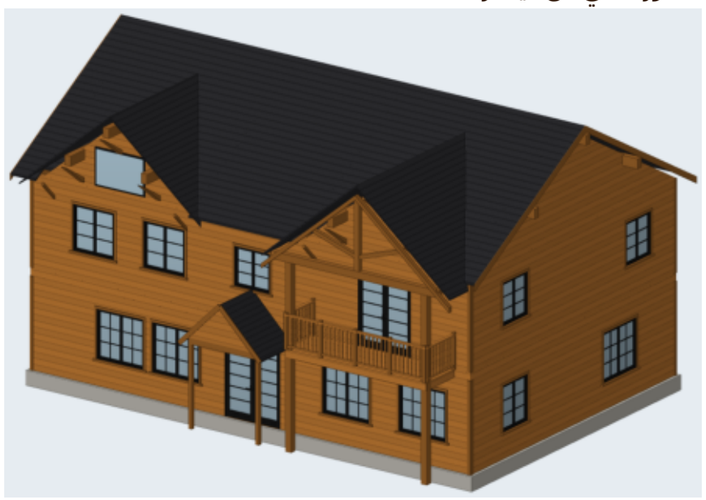

منظور أمامي من اليمين

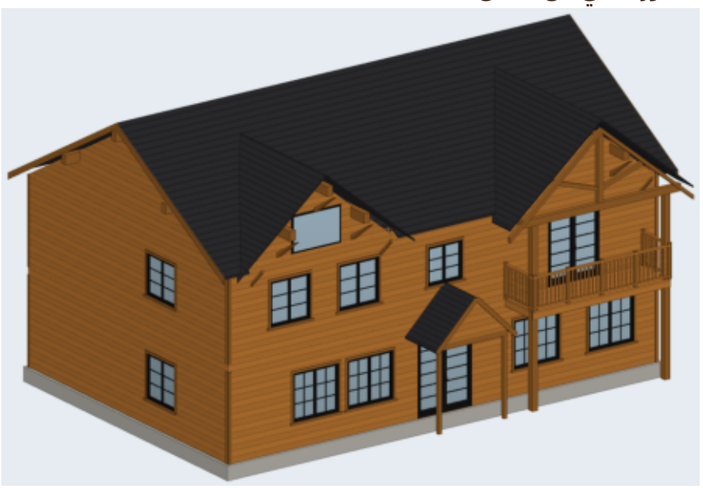


المنظور الخلفي



منظور خلفي من اليمين



منظر علوي

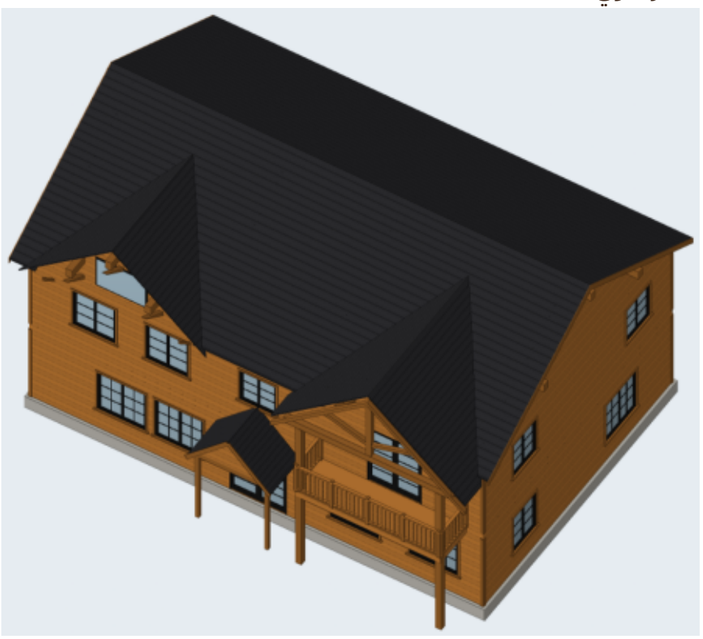

المشروع / العميل **كوخ خشب دورين – مجلس رجال ومجلس نساء + 4 غرف – 15.00 × 10.00 م (300 م²)** **عميل – كوخ دورين**	عنوان اللوحة **لقطات المنظور**	المقياس **–**	التاريخ **2026-10-24**	رقم اللوحة **A-08 (8/11)**

مصنع وتد الأخشاب
Watad Wood Factory

المقطع العلوي بالفرش — الدور الأرضي


مقطع أفقي على ارتفاع 1.90 م — توزيع الفرش ومسار الحركة



مصنع وتد الأخشاب Watad Wood Factory	المشروع / العميل كوخ خشب دورين — مجلس رجال ومجلس نساء + 4 غرف — 15.00 × 10.00 م (300 م²) عميل — كوخ دورين	عنوان اللوحة المقطع العلوي بالفرش — الدور الأرضي	المقياس —	التاريخ 2026-10-24	رقم اللوحة A-09 (9/11)

المقطع العلوي بالفرش — الدور الأول


مقطع أفقي على ارتفاع 1.90 م — توزيع الفرش ومسار الحركة

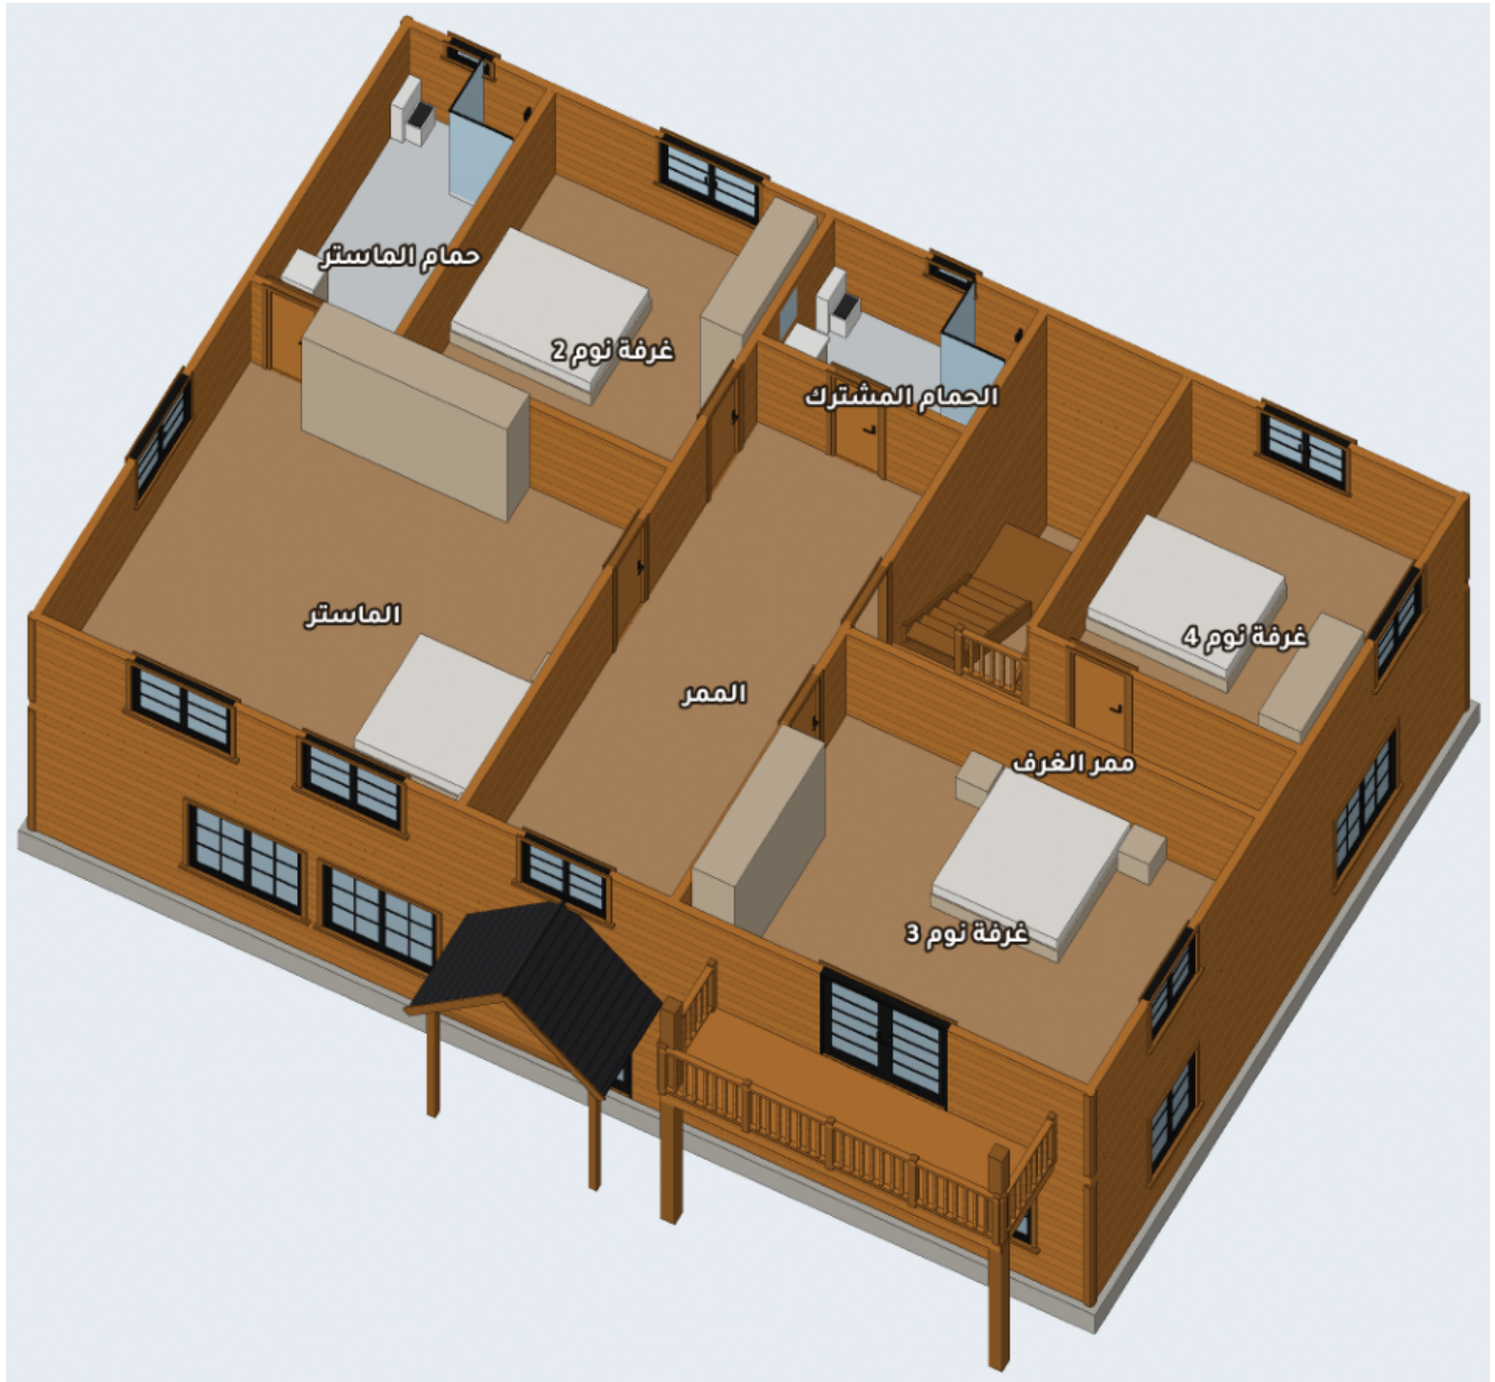

مصنع وتد الأخشاب Watad Wood Factory	المشروع / العميل كوخ خشب دورين — مجلس رجال ومجلس نساء + 4 غرف — 15.00 × 10.00 م (300 م²) عميل — كوخ دورين	عنوان اللوحة المقطع العلوي بالفرش — الدور الأول	المقياس —	التاريخ 2026-10-24	رقم اللوحة A-10 (10/11)

المنظور ثلاثي الأبعاد والمواد

النمط: جوزي غامق + إطارات سوداء — رندر واقعي بخامات حقيقية

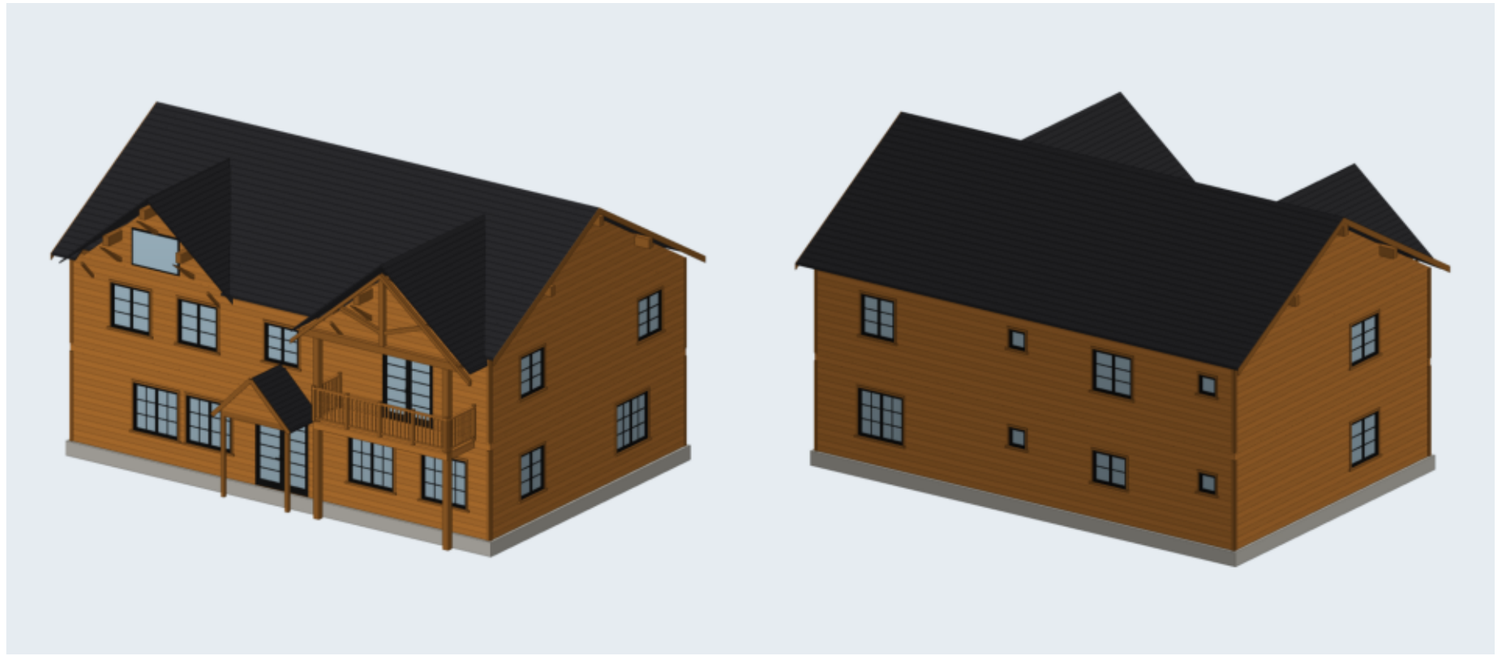

جدول المواد والألوان

الخشب / الصبغة
صبغة عسلي / سيدر

القرميد
قرميد رمادي غامق

الزجاج
زجاج شفاف

إطارات الشبابيك والأبواب
إطار ألمنيوم أسود


الكنار والزوايا
نفس الصبغة أغمق درجة

الصبة
خرسانة 45 سم


الدربزين: ألواح أفقية متقاربة (عصري)

تقسيم الشبابيك: شبكة | الباب الرئيسي: زجاج بتقسيمات (فرنسي)

أنواع الدربزين المعتمدة (من مشاريع المصنع)

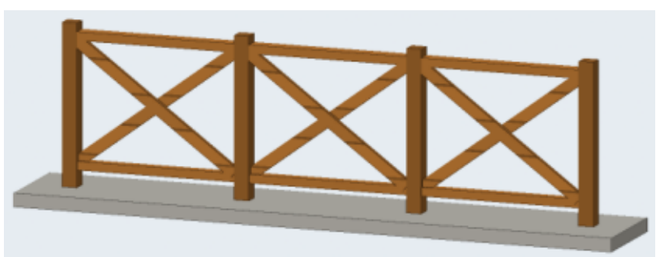

تقاطع X (صورة 5)

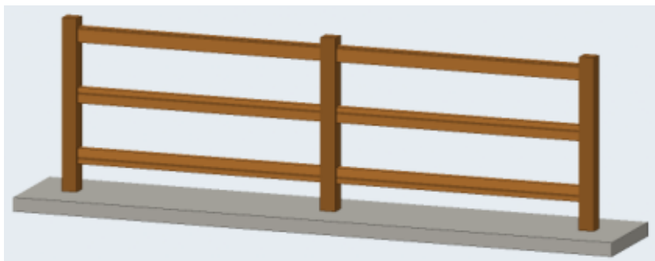

3 مرابيع أفقية (صورة 2)



قوائم رأسية متقاربة (صورة 1)

المشروع / العميل	عنوان اللوحة	المقياس	التاريخ	رقم اللوحة
مصنع وتد الأخشاب Watad Wood Factory — **كوخ خشب دورين — مجلس رجال ومجلس نساء + 4 غرف — 15.00 × 10.00 م (300 م²)** — **عميل — كوخ دورين**	**المنظور والمواد**	**—**	**2026-10-24**	**A-11 (11/11)**