



المسقط الأفقي مع الفرش — الدور الأول
الأبعاد بالسنتيمتر - الجدران: قوائم 5×7 + تليس 2.5 من الجهتين (12 سم) | منسوب الأرضية +3.05

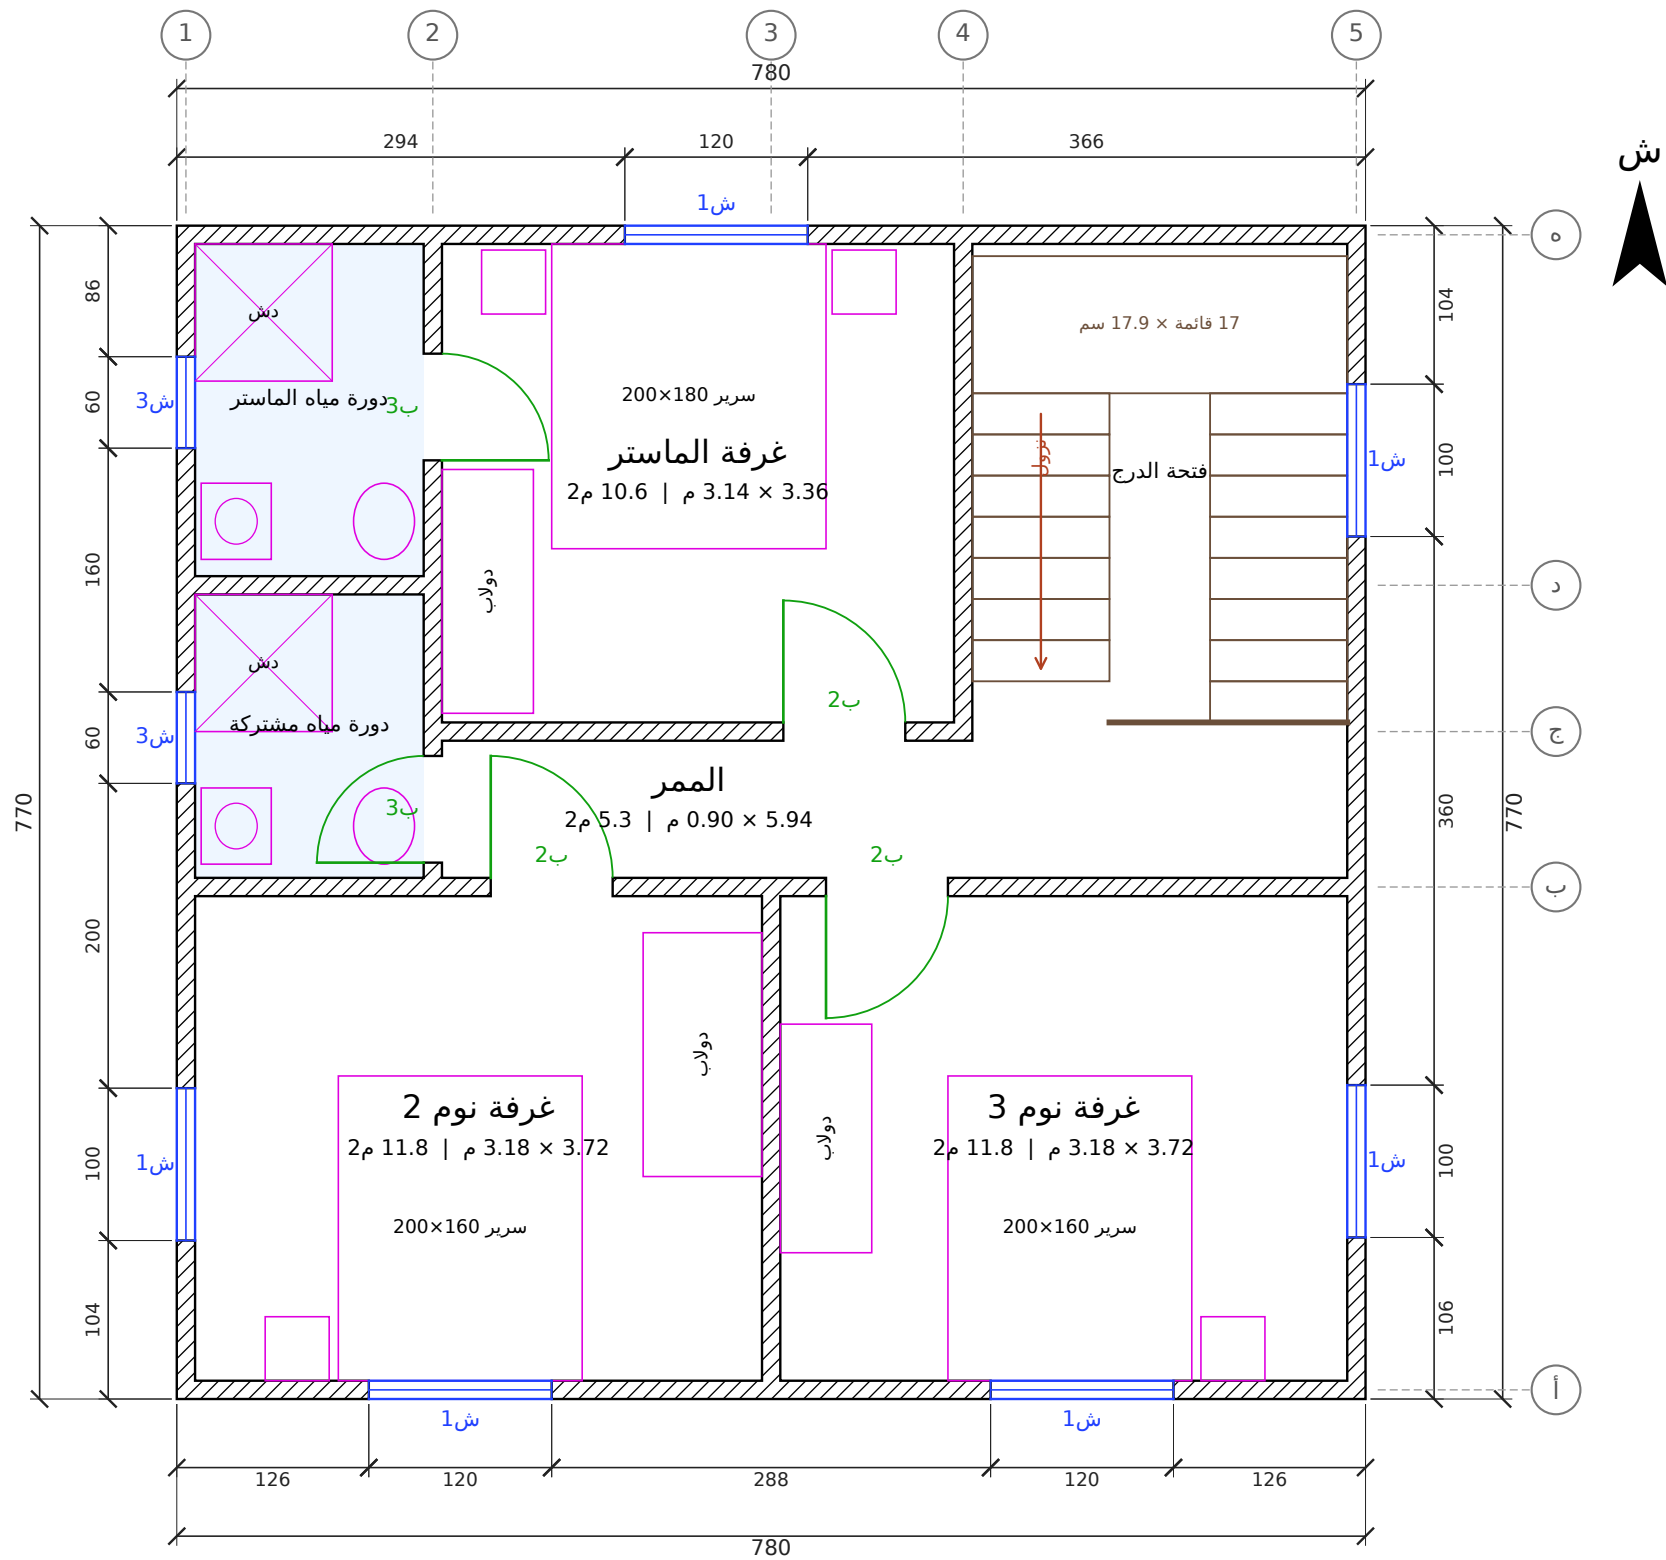


رقم اللوحة	التاريخ	المقياس	عنوان اللوحة	المشروع / العميل	مصنع وتد الأخشاب Watad Wood Factory
A-02 (2/11)	2026-10-06	1:50	المسقط الأفقي — الدور الأول	دورين 3 غرف نوم + غرفة خادمة — 120 م² عميل جديد	

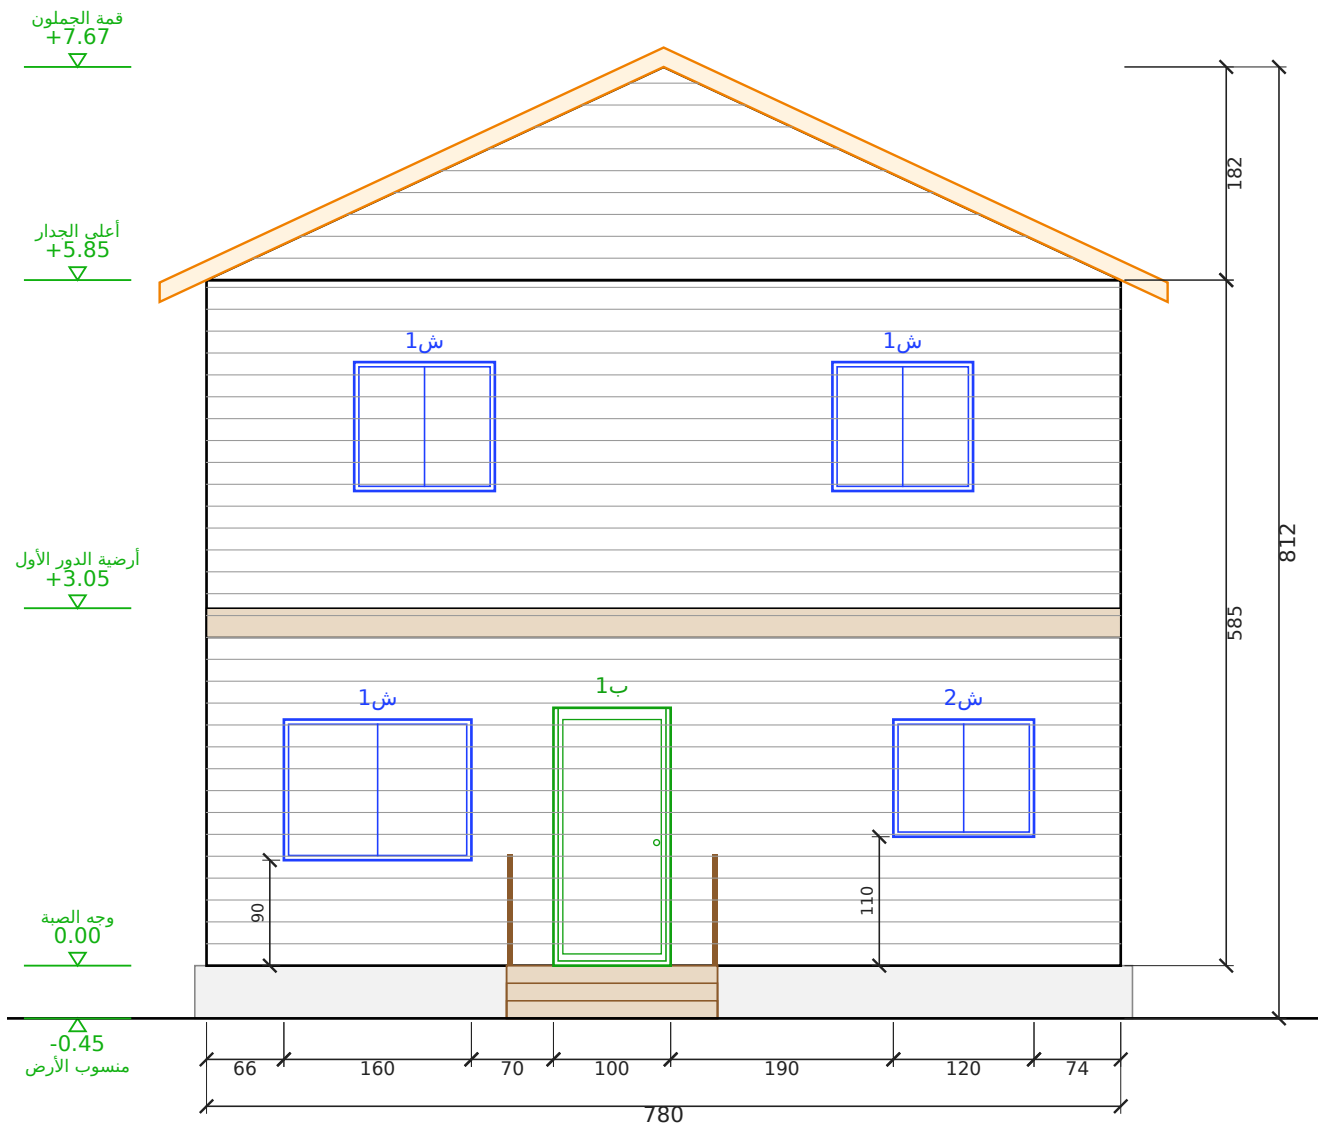

الواجهة الأمامية


مقياس 1:50 | الوحدة: سم

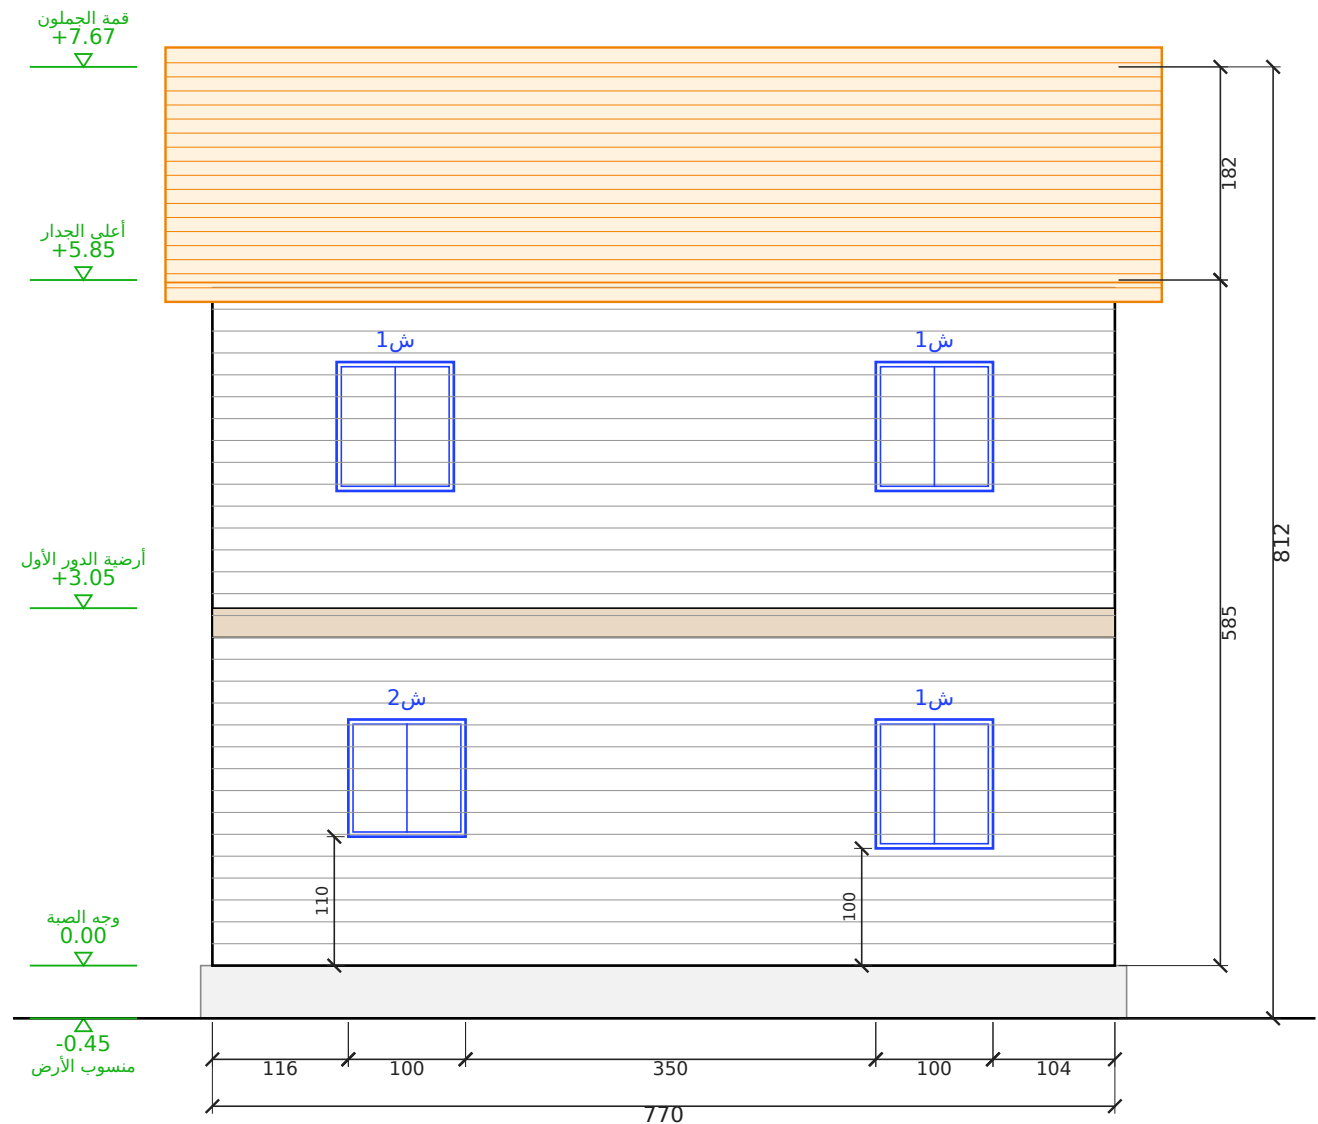

الواجهة الشرقية


مقياس 1:50 | الوحدة: سم

رقم اللوحة	التاريخ	المقياس	عنوان اللوحة	المشروع / العميل	مصنع وتد الأخشاب Watad Wood Factory
A-03 (3/11)	2026-10-06	1:50	الواجهة الأمامية والواجهة الشرقية	دورين 3 غرف نوم + غرفة خادمة - 120 م ² عميل جديد	

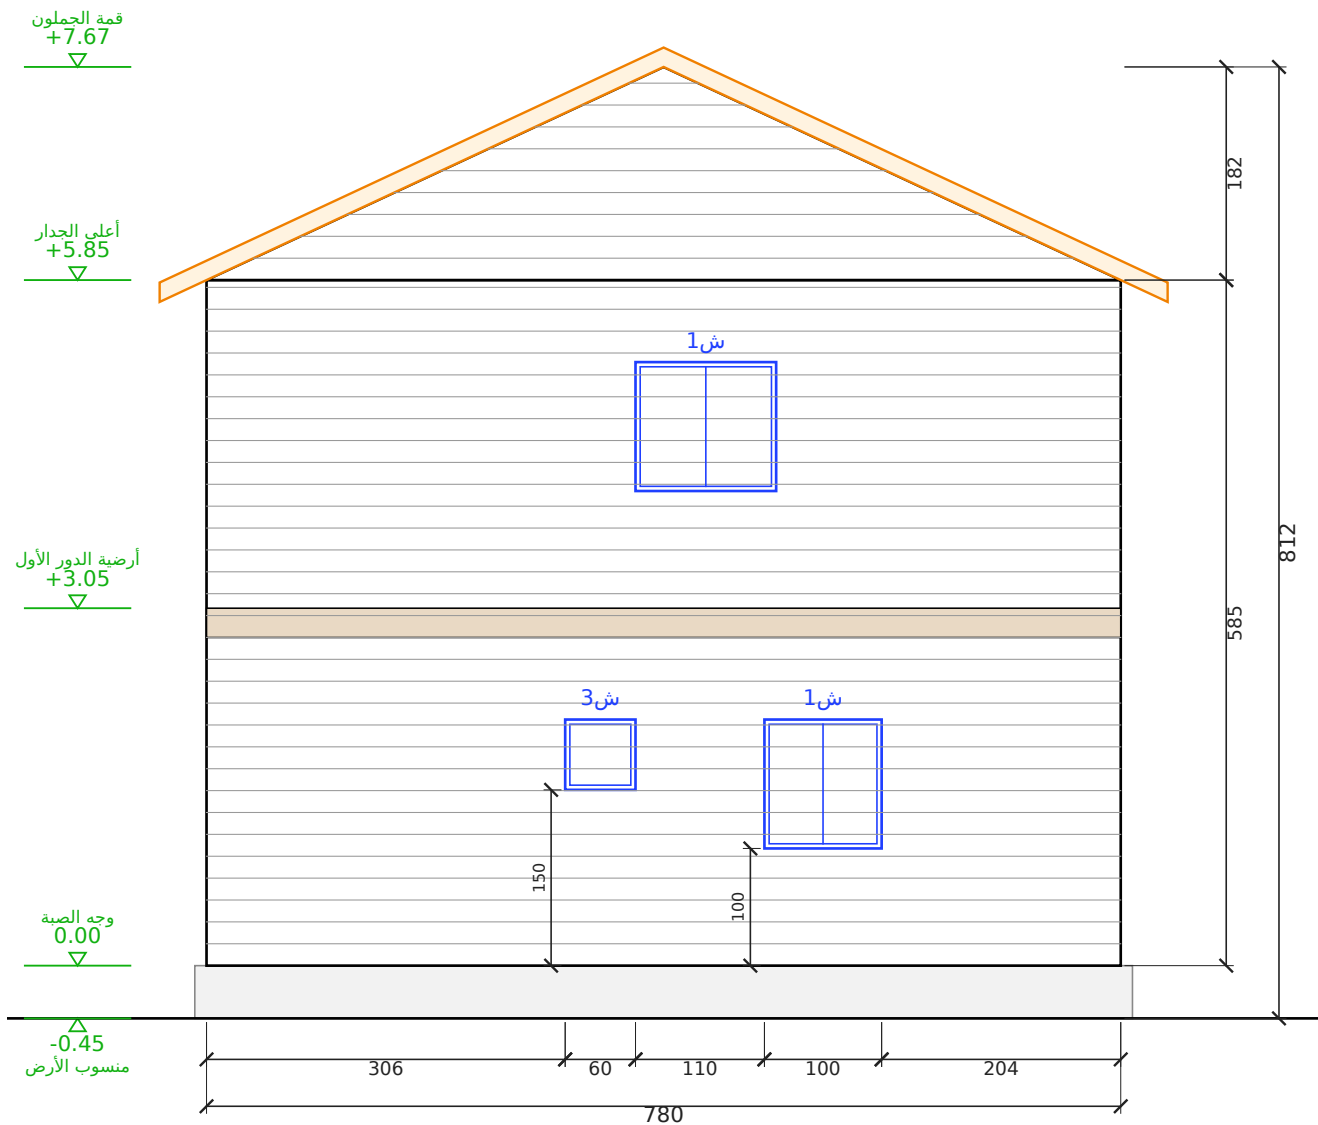

الواجهة الخلفية

مقياس 1:50 | الوحدة: سم

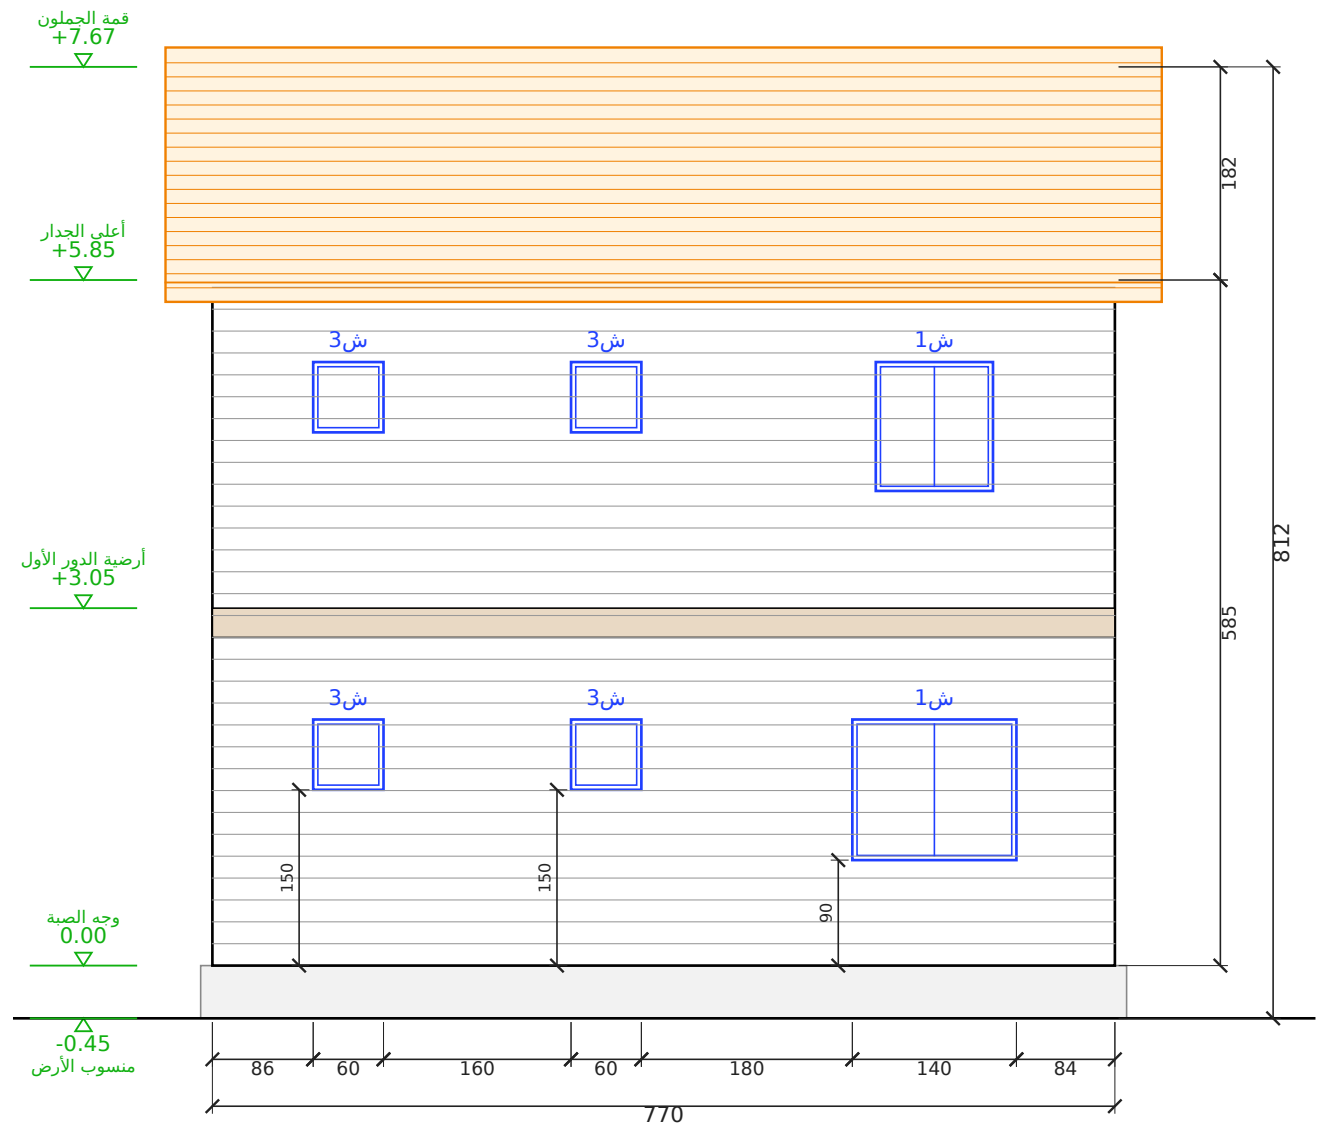


الواجهة الغربية


مقياس 1:50 | الوحدة: سم

رقم اللوحة	التاريخ	المقياس	عنوان اللوحة	المشروع / العميل	مصنع وتد الأخشاب Watad Wood Factory
A-04 (4/11)	2026-10-06	1:50	الواجهة الخلفية والواجهة الغربية	دورين 3 غرف نوم + غرفة خادمة - 120 م ² عميل جديد	


مسقط السقف (جملون)
رفرف 40 سم من كل جهة | مقياس 1:50

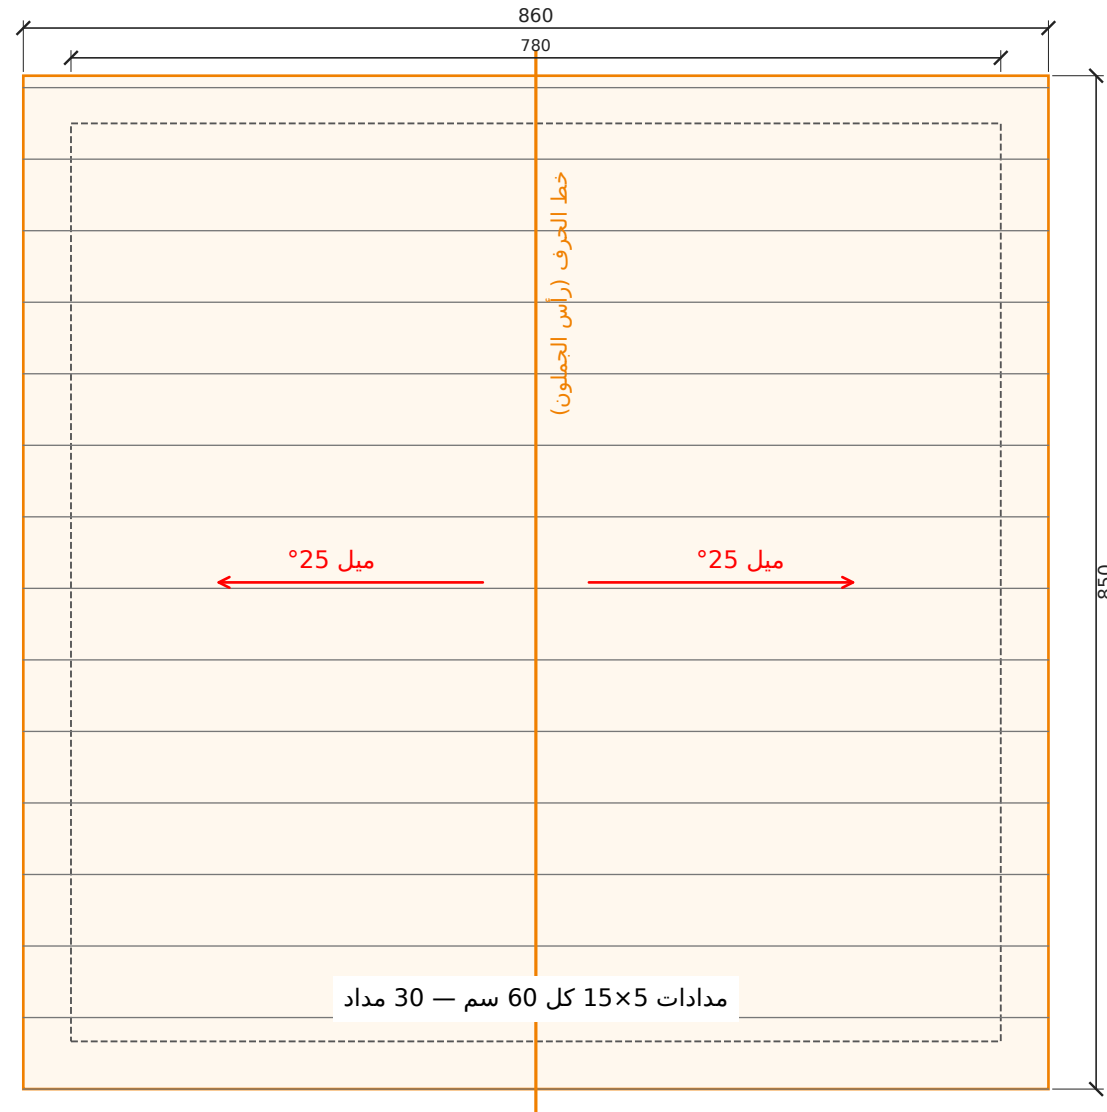

قطاع عرضي أ-أ
مقياس 1:50 | الوحدة: سم

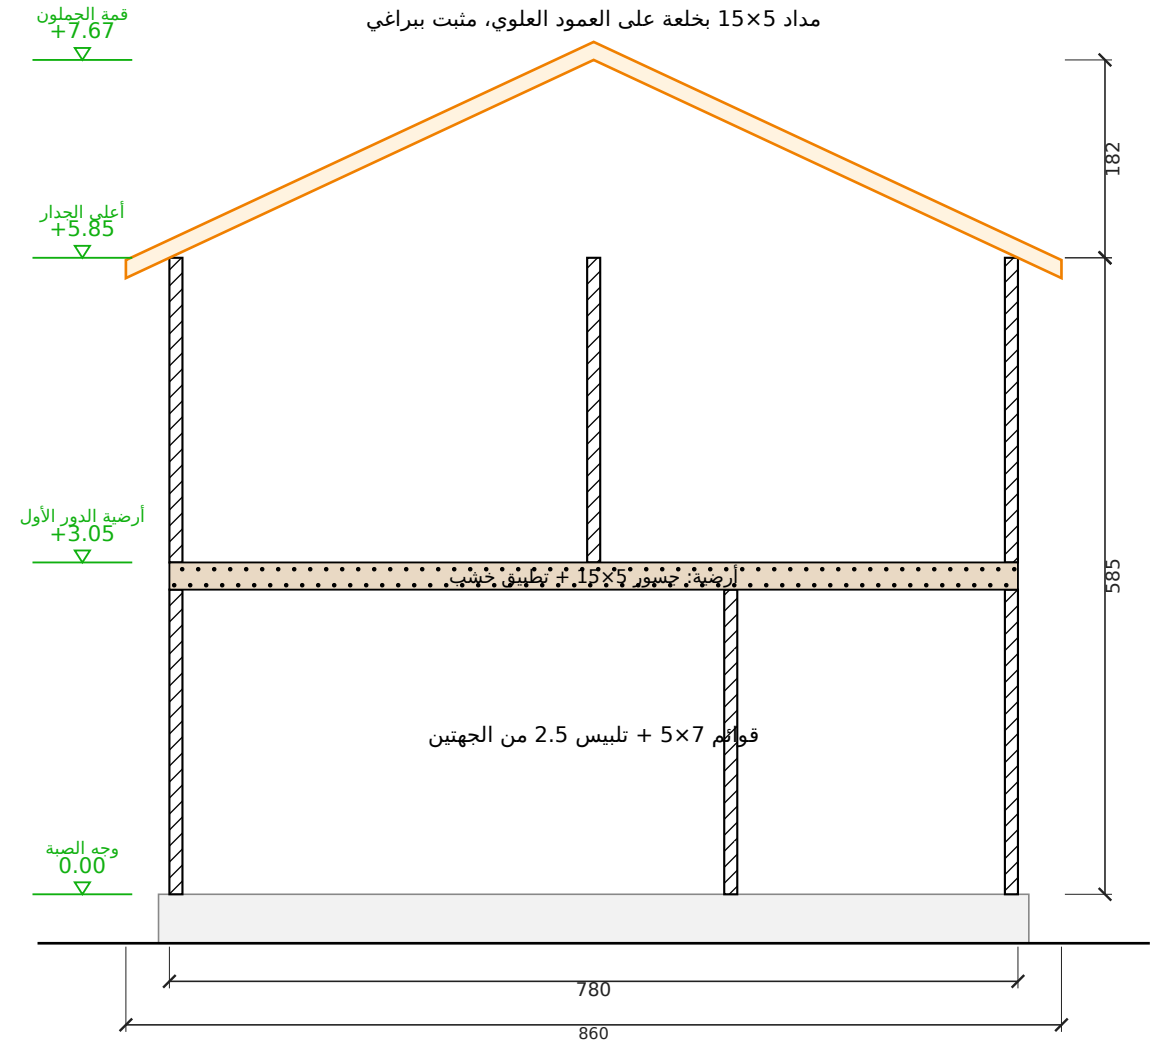

تفصيلة جلوس المداد على العلوي (1:5)

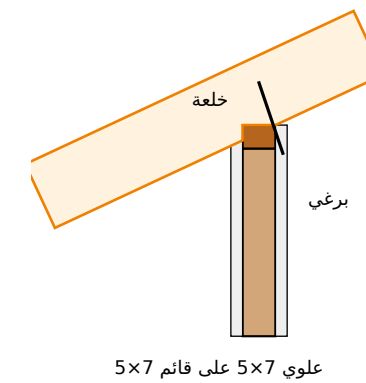

رقم اللوحة

A-05 (5/11)

التاريخ

2026-10-06

المقياس

1:50

عنوان اللوحة

مسقط السقف والقطاع

المشروع / العميل

دورين 3 غرف نوم + غرفة خادمة - 120 م²
عميل جديد

مصنع وتد الأخشاب
Watad Wood Factory



جدول مقاسات الأبواب والشبابيك
مقاس الفتحة الصافي في الجدار - الوحدة: سم

الرمز	النوع	العرض (سم)	الارتفاع (سم)	ارتفاع الجلسة (سم)	العدد	الموقع
ب1	باب	100	220	-	1	الأمامية
ب2	باب	80	210	-	4	غرفة الخادمة - غرفة 2 - غرفة 3 - ماستر
ب2	باب	70	210	-	1	مخزن
ب3	باب	70	210	-	4	حمام الضيوف - حمام الخادمة - حمام مشترك - حمام الماستر
ف1	باب	100	210	-	1	فتحة المطبخ
ش1	شباك	160	120	90	1	الأمامية
ش1	شباك	100	110	100	5	الشرقية 3 - الخلفية - الغربية
ش1	شباك	140	120	90	1	الغربية
ش1	شباك	120	110	100	3	الأمامية 2 - الخلفية
ش2	شباك	120	100	110	1	الأمامية
ش2	شباك	100	100	110	1	الشرقية
ش3	شباك	60	60	150	5	الخلفية - الغربية 4

الإجمالي: أبواب 11 - شبابيك 17

جدول المساحات وبيانات المشروع والتسعير

جدول المساحات

م	الفراغ	الأبعاد (م)	المساحة (م2)
1	أرضي — الصالة	4.98 × 3.18	15.84
2	أرضي — الموزع	5.94 × 0.90	5.35
3	أرضي — المطبخ	2.46 × 3.18	7.82
4	أرضي — دورة مياه ضيوف	1.50 × 1.86	2.79
5	أرضي — دورة مياه الخادمة	1.50 × 2.18	3.27
6	أرضي — غرفة الخادمة	2.16 × 3.14	6.78
7	أرضي — مخزن / غسيل	1.08 × 3.14	3.39
8	أرضي — الدرج	2.46 × 3.14	7.72
9	أول — غرفة نوم 2	3.72 × 3.18	11.83
10	أول — غرفة نوم 3	3.72 × 3.18	11.83
11	أول — الممر	5.94 × 0.90	5.35
12	أول — دورة مياه مشتركة	1.50 × 1.86	2.79
13	أول — دورة مياه الماستر	1.50 × 2.18	3.27
14	أول — غرفة الماستر	3.36 × 3.14	10.55
	المساحة الصافية الداخلية		98.58
	التراس المسقوف (مجاناً)	1.80 × 1.20	2.16
	المساحة الإجمالية المبنية	2 × 7.70 × 7.80 دور	120.12

بيانات المشروع

البند	البيان
المشروع	دورين 3 غرف نوم + غرفة خادمة — 120 م²
العميل	عميل جديد
الموقع	—
الاستخدام	سكن
التاريخ	2026-10-06
نظام البناء	هيكل خشب 5×7 + تليس 2.5 سم من الجهتين
السقف	جملون 25° — قرميد معدني

التسعير


البند	القيمة
المساحة المبنية (م2)	120.12
سعر المتر المربع	1,096 ريال
الإجمالي	131,652 ريال

ملاحظات:


- السعر للمساحة المبنية حسب المخطط المعتمد.
- الصبة والتמידات الخارجية على العميل ما لم يُذكر غير ذلك.

لقطات المنظور الخارجي

منظور أمامي من اليمين

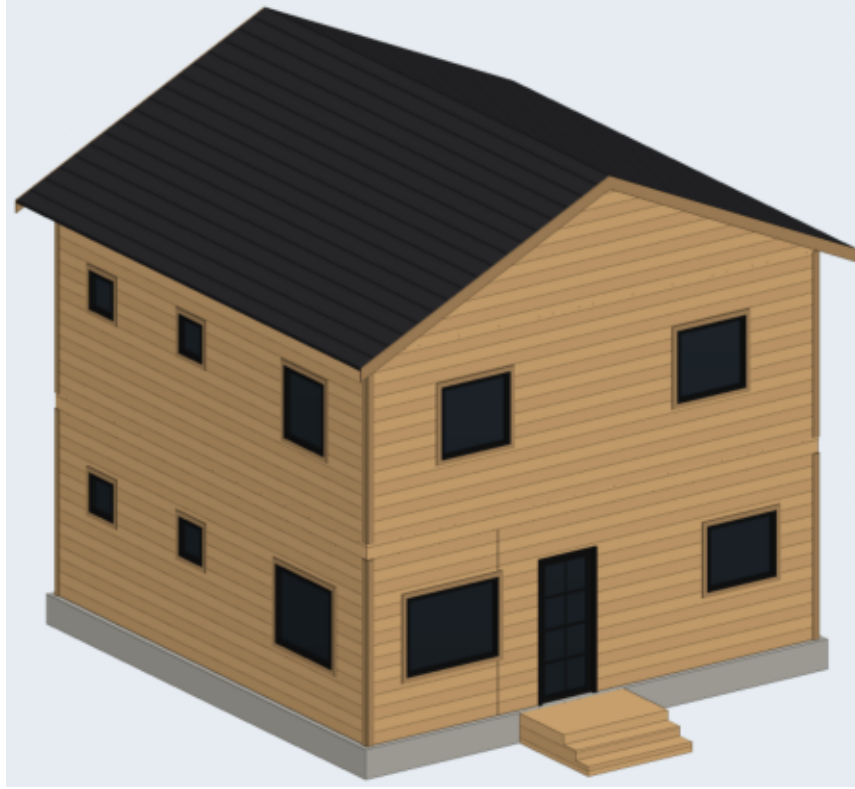

منظور أمامي من اليسار

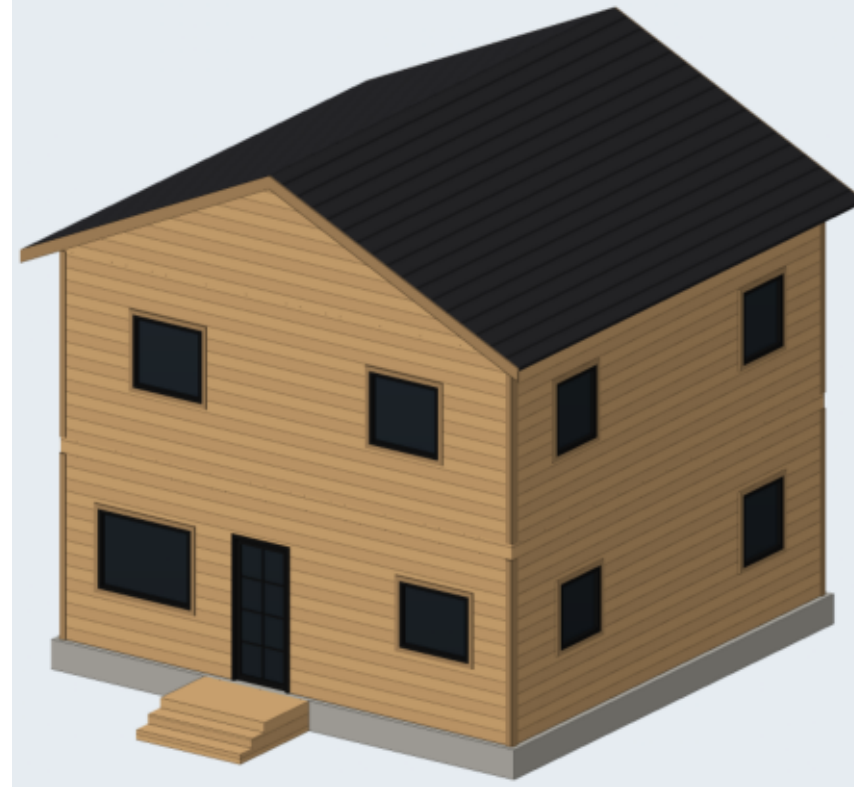


المنظور الأمامي




منظر علوي



منظور خلفي من اليمين

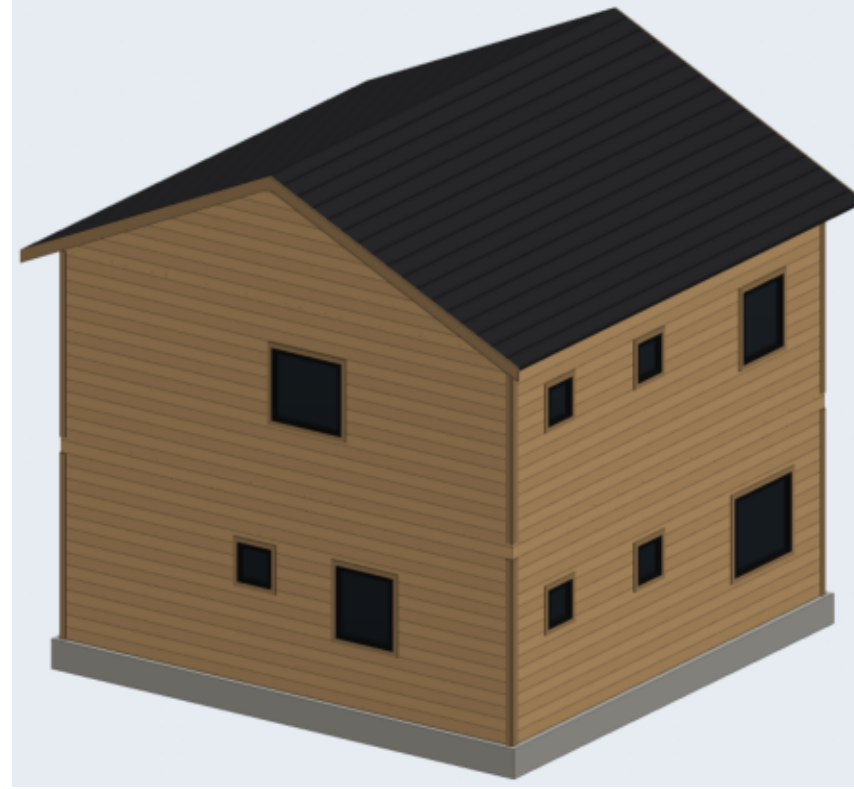

المنظور الخلفي

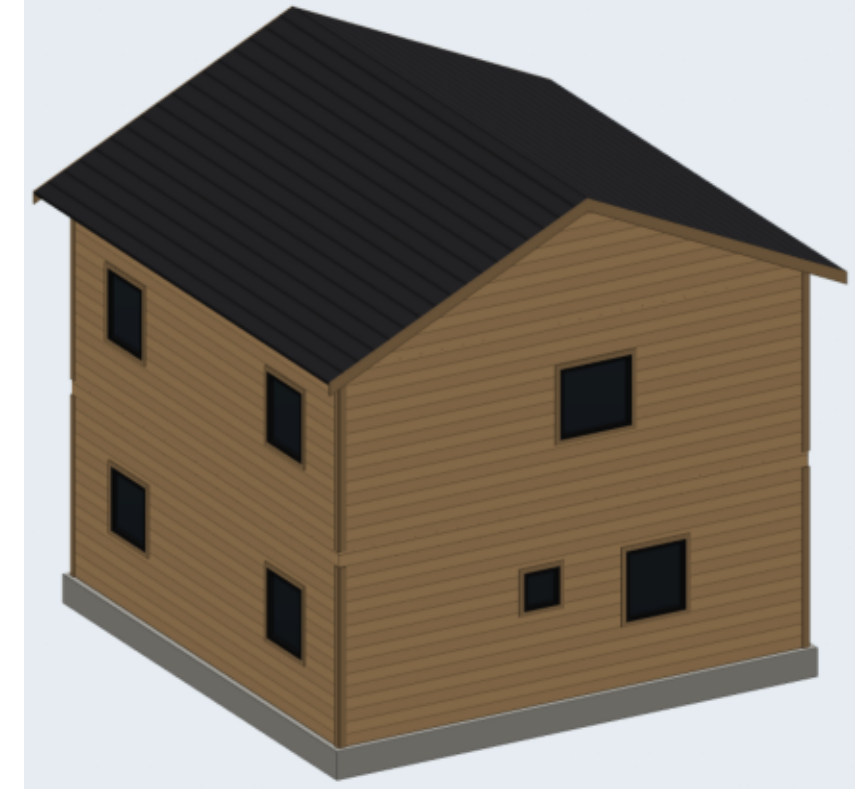

رقم اللوحة

A-08 (8/11)

التاريخ

2026-10-06

المقياس

—

عنوان اللوحة

لقطات المنظور

المشروع / العميل


دورين 3 غرف نوم + غرفة خادمة — 120 م²
عميل جديد

مصنع وتد الأخشاب
Watad Wood Factory



المقطع العلوي بالفرش – الدور الأرضي

مقطع أفقي على ارتفاع 1.90 م – توزيع الفرش ومسار الحركة

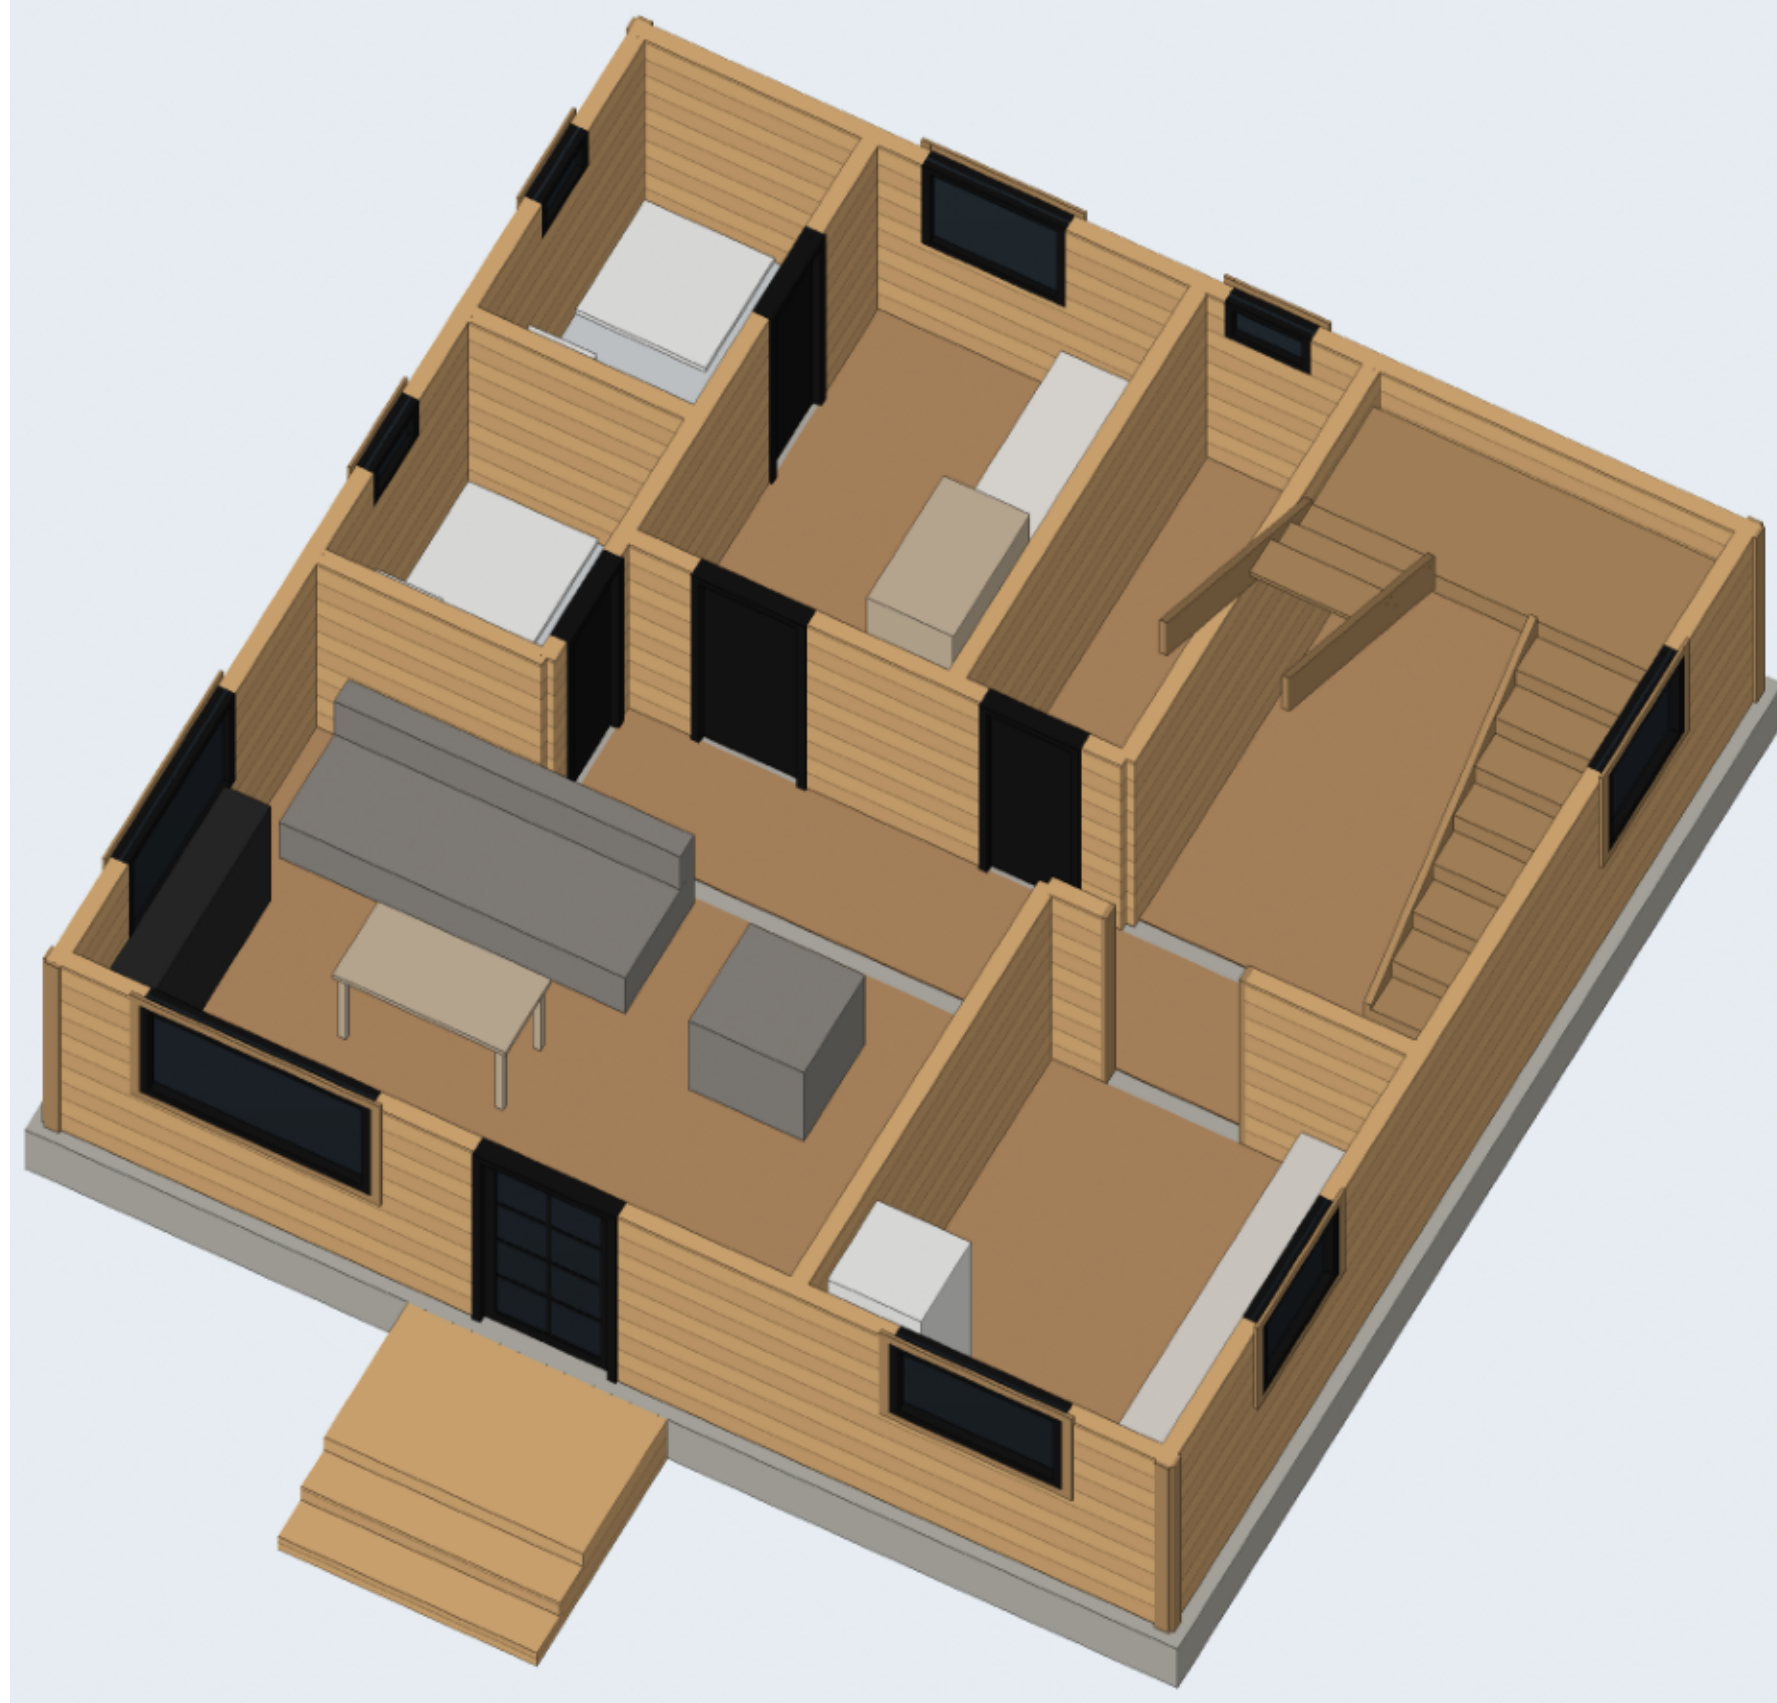

رقم اللوحة

A-09 (9/11)

التاريخ

2026-10-06

المقياس

—

عنوان اللوحة

المقطع العلوي بالفرش – الدور الأرضي

المشروع / العميل


دورين 3 غرف نوم + غرفة خادمة – 120 م²
عميل جديد

مصنع وتد الأخشاب
Watad Wood Factory



المقطع العلوي بالفرش – الدور الأول

مقطع أفقي على ارتفاع 1.90 م – توزيع الفرش ومسار الحركة

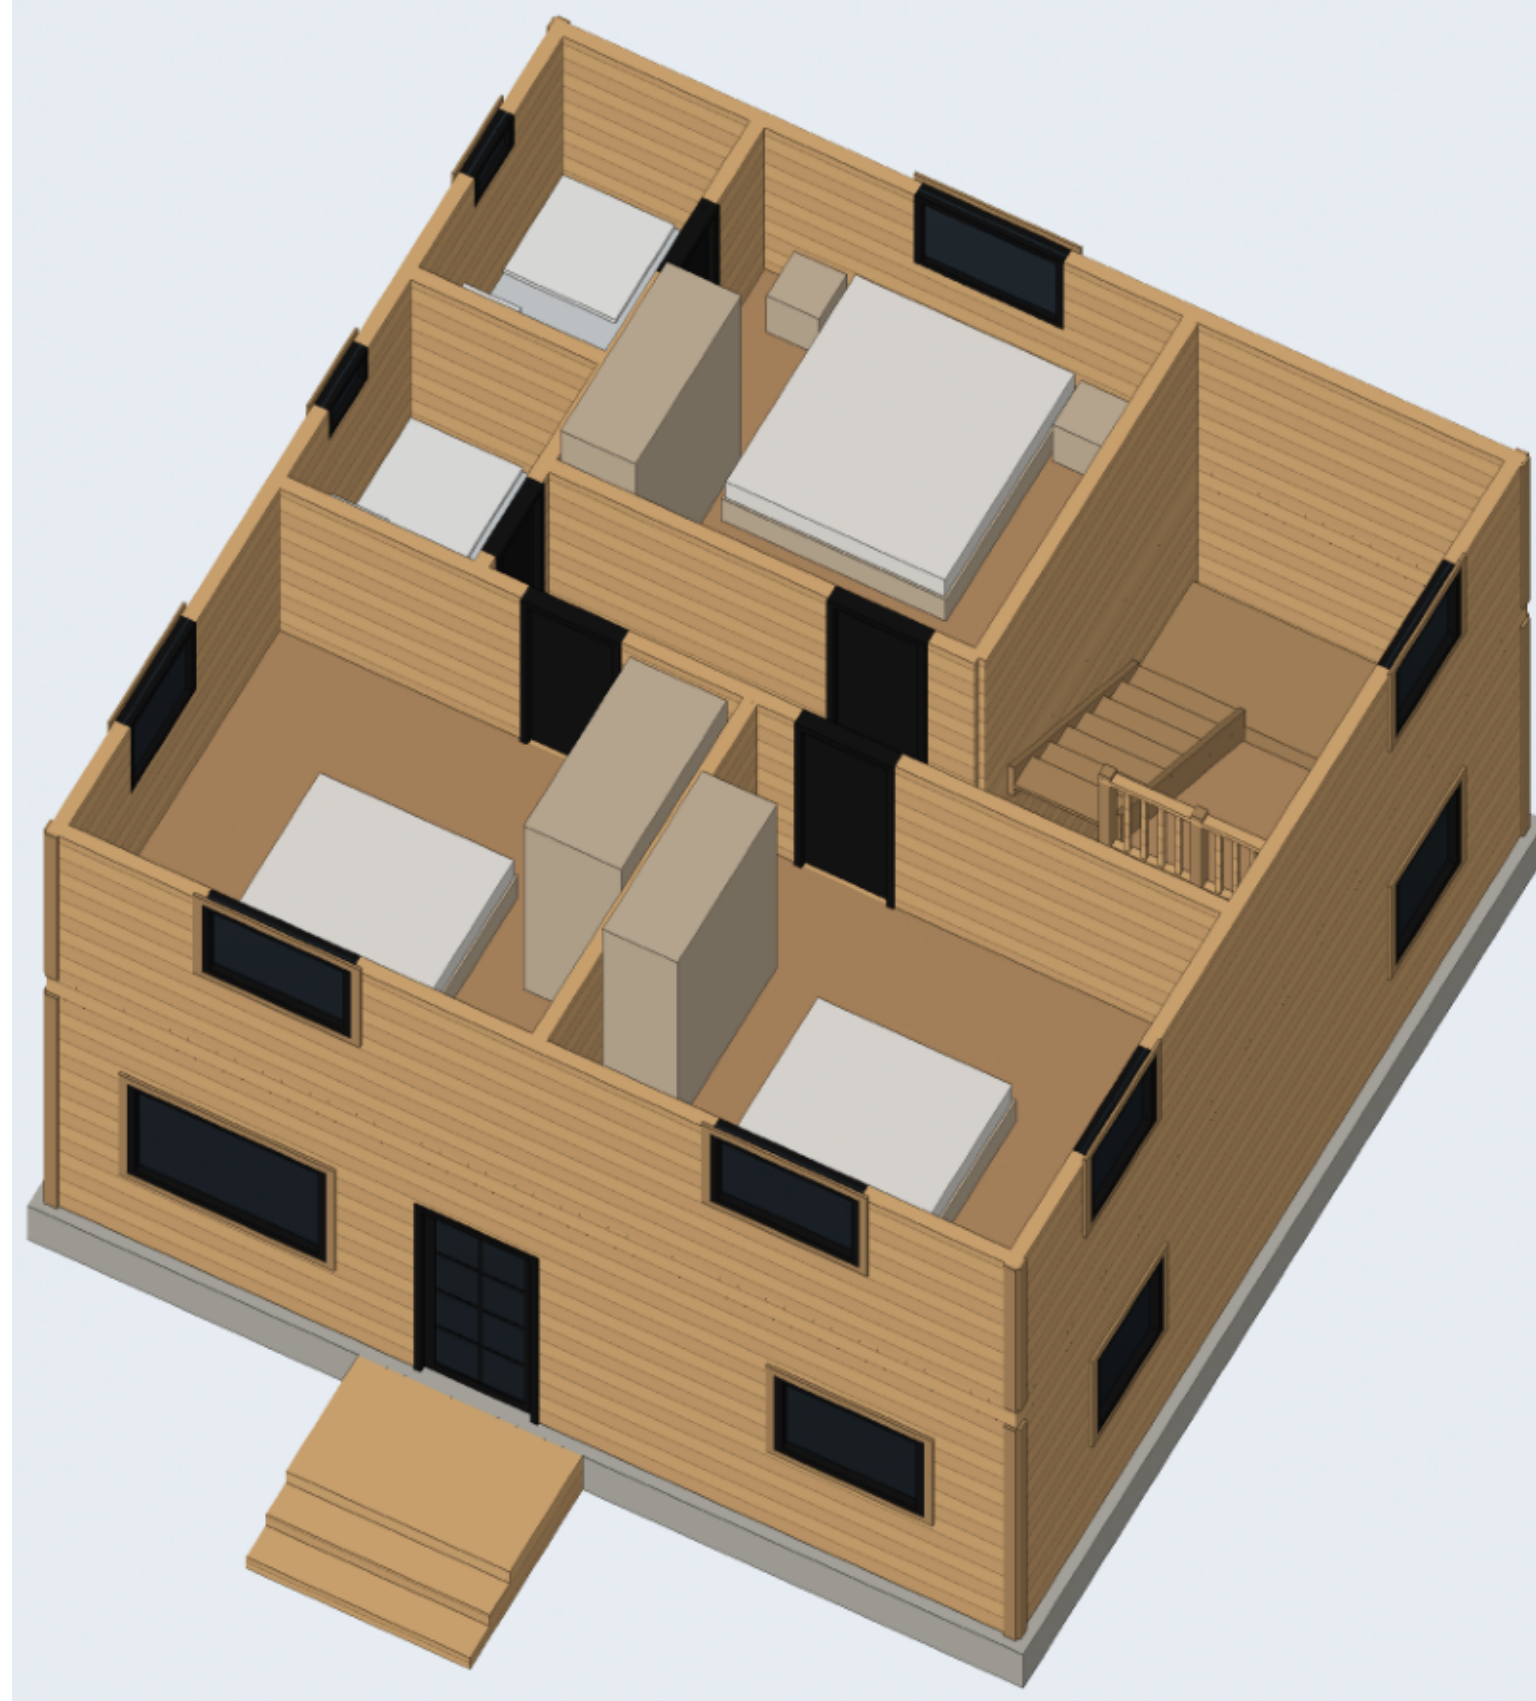

رقم اللوحة

A-10 (10/11)

التاريخ

2026-10-06

المقياس

—

عنوان اللوحة

المقطع العلوي بالفرش – الدور الأول

المشروع / العميل

دورين 3 غرف نوم + غرفة خادمة – 120 م²
عميل جديد


مصنع وتد الأخشاب
Watad Wood Factory



المنظور ثلاثي الأبعاد والمواد

النمط: جوزي غامق + إطارات سوداء — رندر واقعي بخامات حقيقية

جدول المواد والألوان

 

الخشب / الصبغة

خشب طبيعي فاتح (بدون صبغة)



القرميد

قرميد رمادي غامق



الزجاج

زجاج عاكس غامق



إطارات الشبابيك والأبواب

إطار ألومنيوم أسود



الكنار والزوايا

نفس الصبغة أعمق درجة



الصبة

خرسانة 45 سم


الدريزين: ألواح أفقية متقاربة (عصري)

تقسيم الشبابيك: بدون | الباب الرئيسي: زجاج بتقسيمات (فرنسي)


أنواع الدريزين المعتمدة (من مشاريع المصنع)



قوائم رأسية متقاربة (صورة 1)

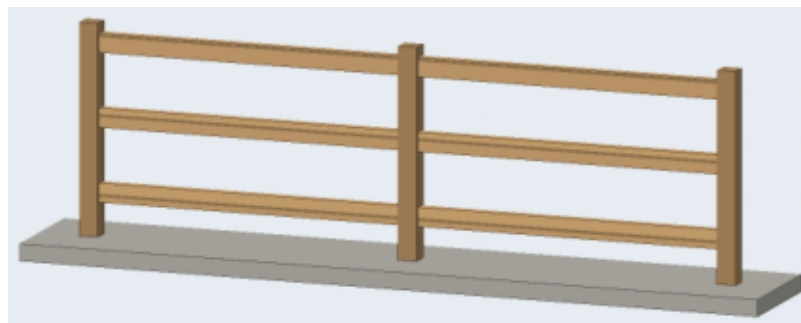

3 مربيع أفقية (صورة 2)

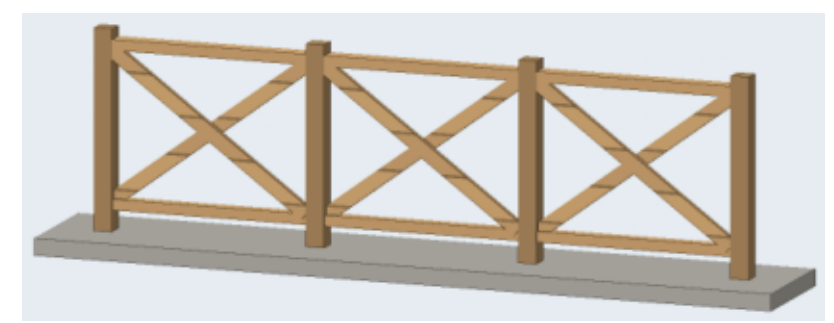

تقاطع X (صورة 5)

رقم اللوحة

A-11 (11/11)

التاريخ

2026-10-06

المقياس

—

عنوان اللوحة

المنظور والمواد

المشروع / العميل

دورين 3 غرف نوم + غرفة خادمة — 120 م²
عميل جديد

مصنع وتد الأخشاب

Watad Wood Factory

