
# المنظور ثلاثي الأبعاد والمواد

النمط: خشب طبيعي + قرميد فحمي — رندر واقعي بخامات حقيقية

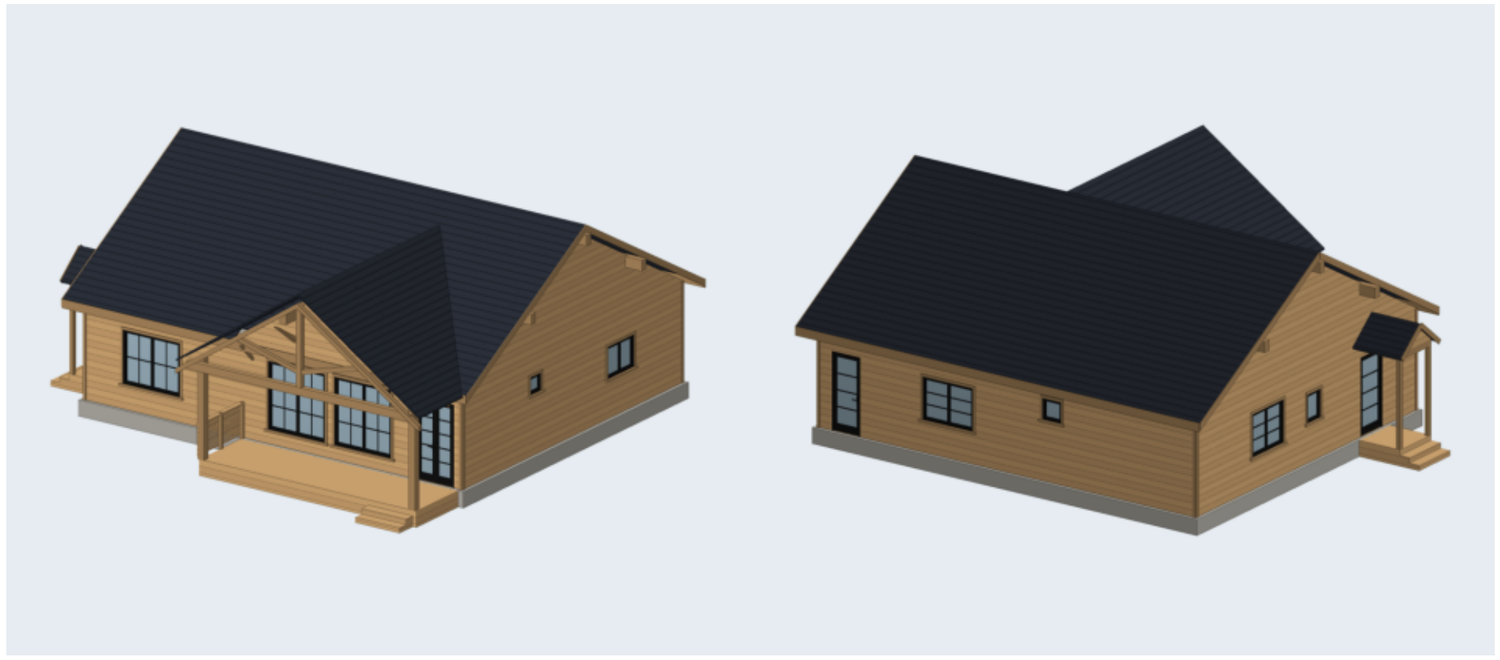

## جدول المواد والألوان

**الخشب / الصبغة**

خشب طبيعي فاتح (بدون صبغة)

**القرميد**

قرميد فحمي / أسود مزرق

**الزجاج**

زجاج شفاف

**إطارات الشبابيك والأبواب**

إطار ألمنيوم أسود

**الكنار والزوايا**

نفس الصبغة أغمق درجة


**الصبة**

خرسانة 45 سم


الدربزين: ألواح أفقية متقاربة (عصري)

تقسيم الشبابيك: شبكة | الباب الرئيسي: زجاج بتقسيمات (فرنسي)

## أنواع الدربزين المعتمدة (من مشاريع المصنع)

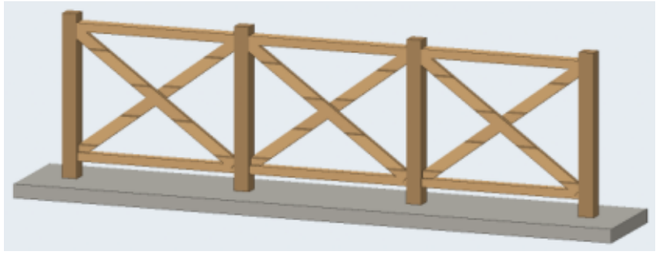

تقاطع X (صورة 5)

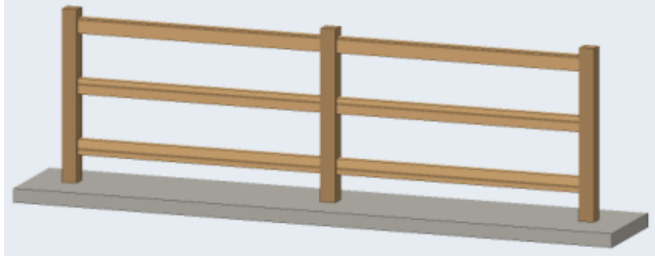

3 مرابيع أفقية (صورة 2)




قوائم رأسية متقاربة (صورة 1)

| المشروع / العميل | عنوان اللوحة | المقياس | التاريخ | رقم اللوحة |
|---|---|---|---|---|
| **مصنع وتد الأخشاب** Watad Wood Factory<br>**كوخ دور واحد — مجلس رجال ومجلس نساء + غرفتين — 12.00 × 10.00 م (120 م²)**<br>**عميل — كوخ 120** | **المنظور والمواد** | **1:50** | **2026-10-25** | **W-01 (1/15)** |


# المسقط الأفقي مع الفرش

## الأبعاد بالسنتيمتر - الجدران: قوائم 7×5 + تلبيس 2.5 من الجهتين (12 سم)

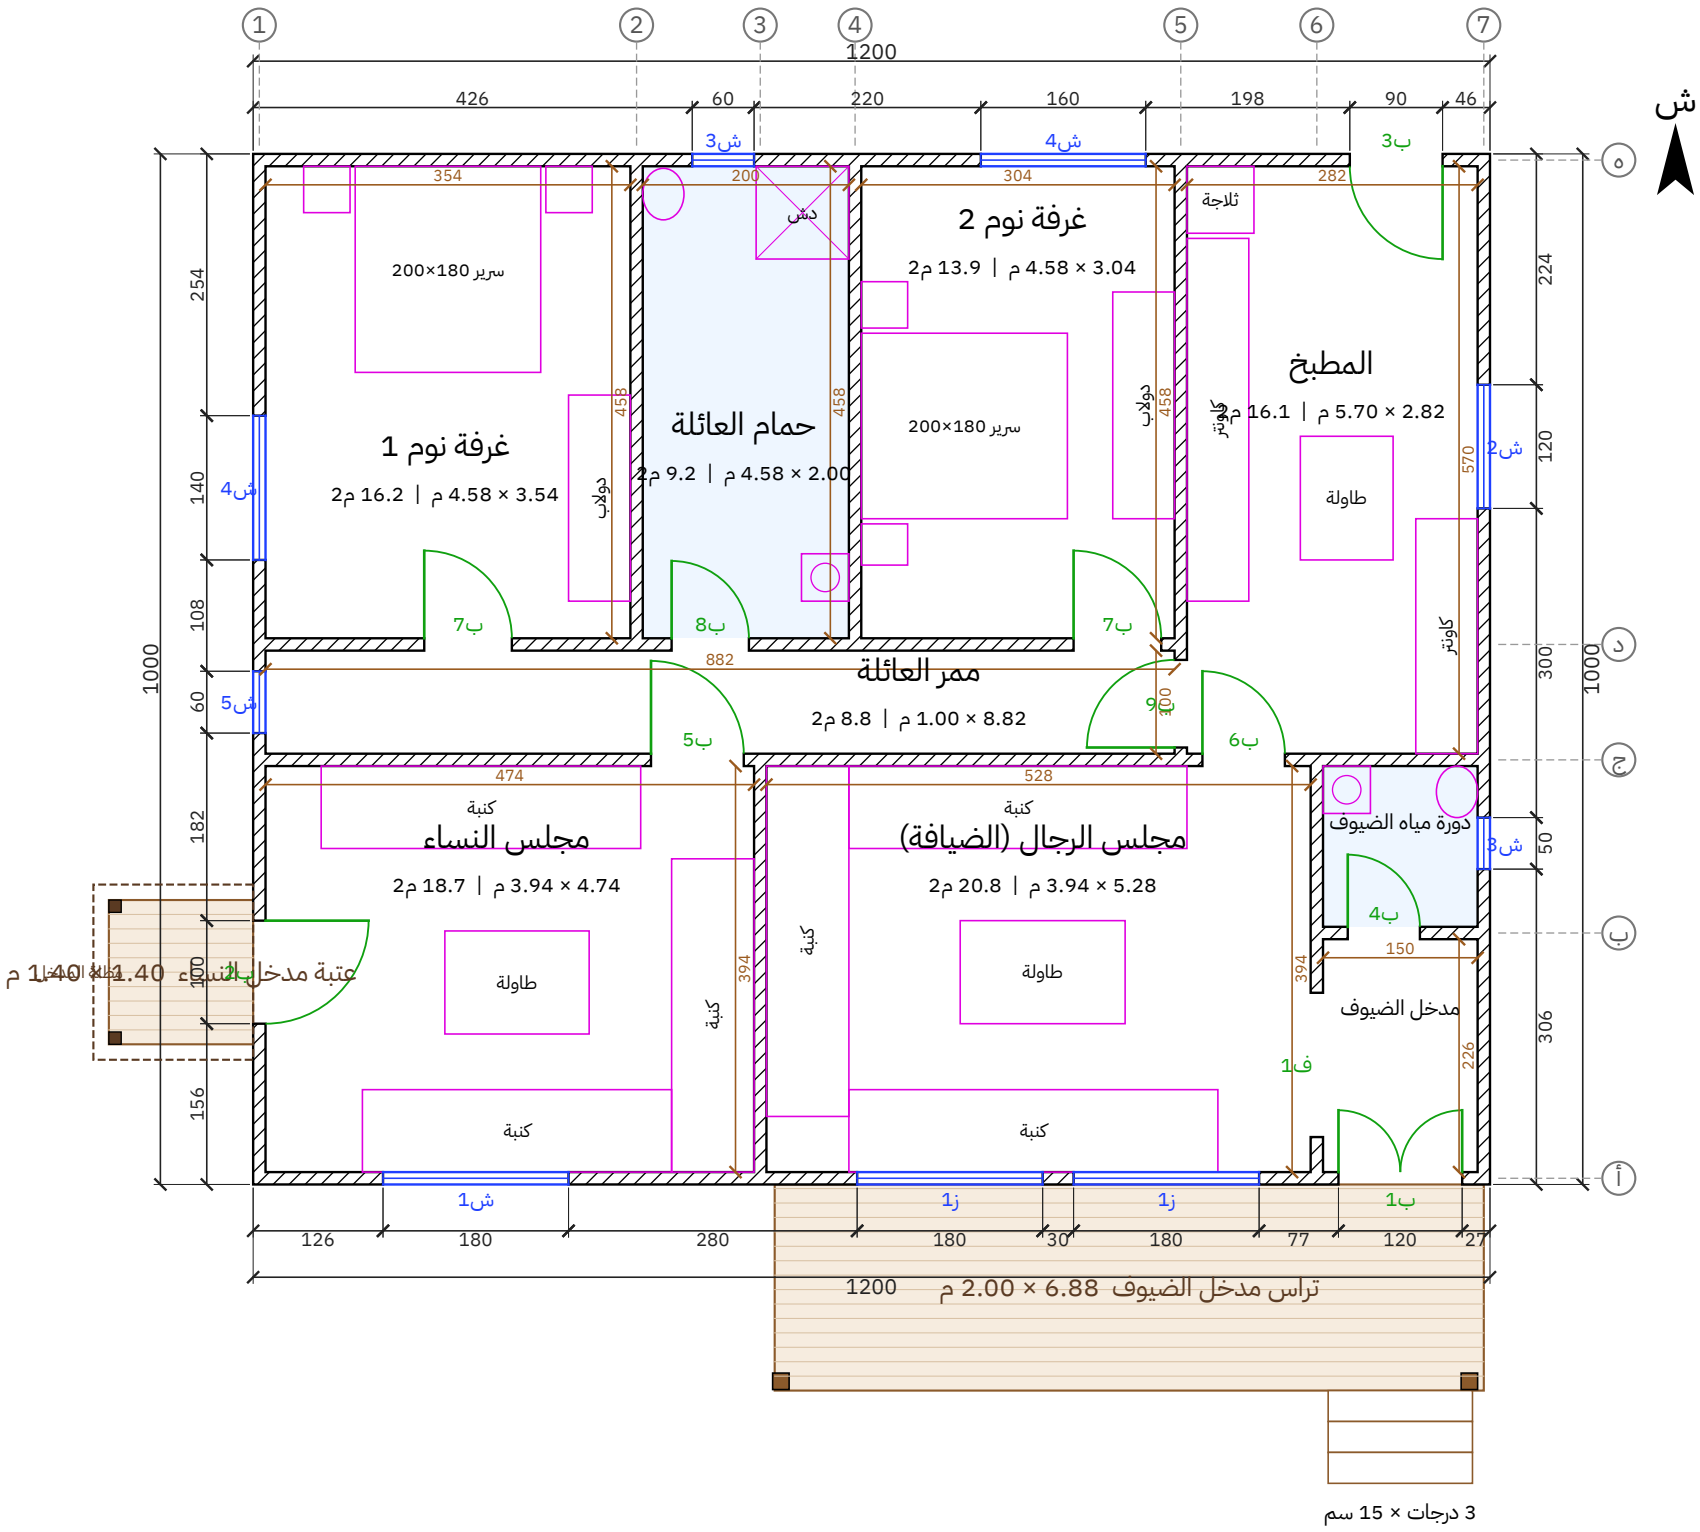



| المشروع / العميل | عنوان اللوحة | المقياس | التاريخ | رقم اللوحة |
|---|---|---|---|---|
| كوخ دور واحد – مجلس رجال ومجلس نساء + غرفتين – 12.00 × 10.00 م (120 م²)<br>عميل – كوخ 120 | المسقط الأفقي | 1:50 | 2026-10-25 | W-02 (2/15) |

مصنع وتد الأخشاب
Watad Wood Factory

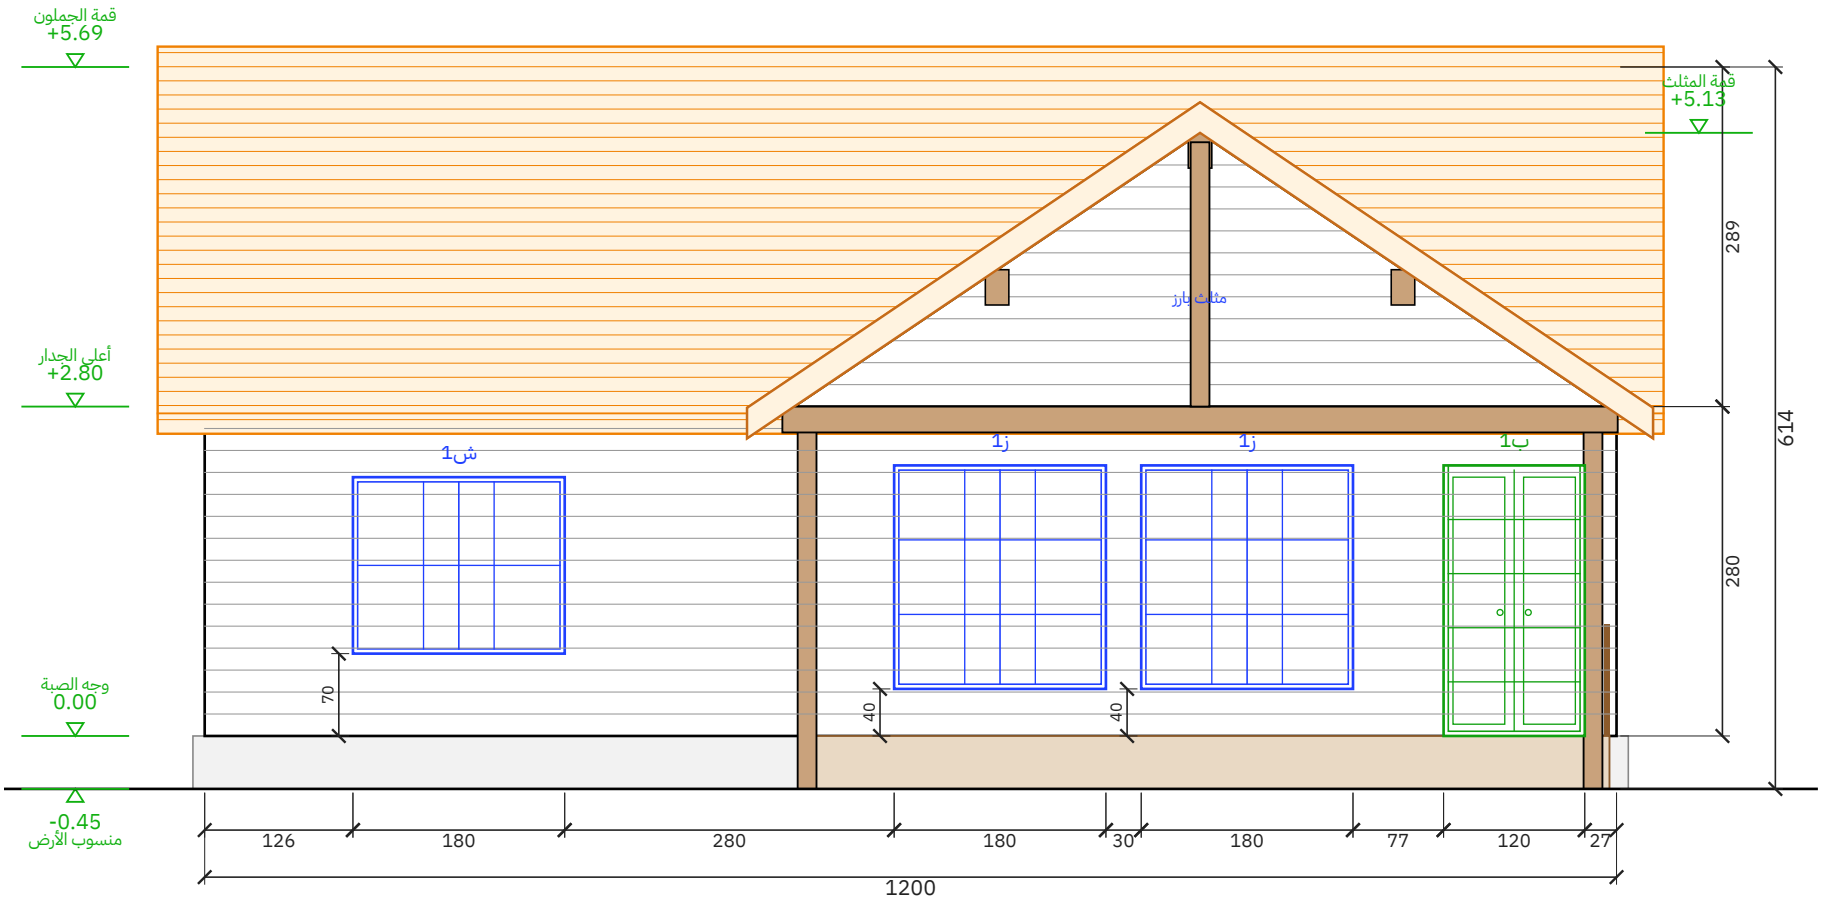


## الواجهة الأمامية (الضيافة)

مقياس 1:50 | الوحدة: سم

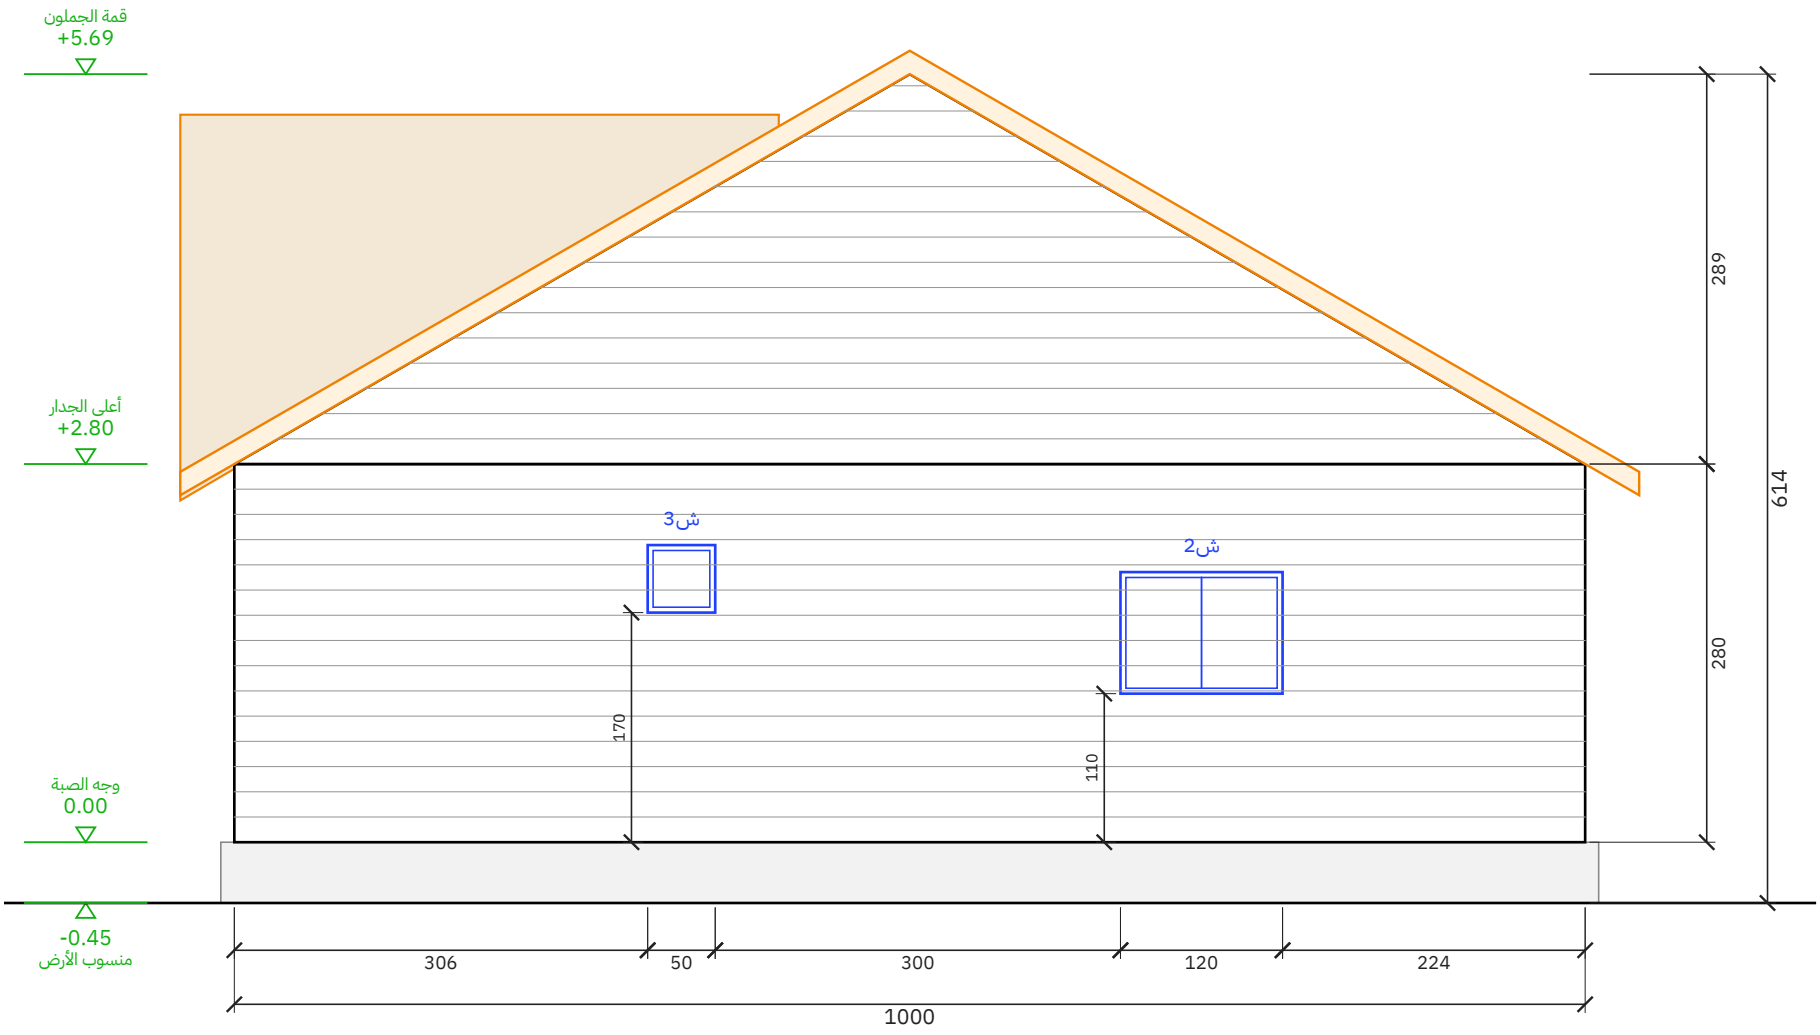



## الواجهة الشرقية

مقياس 1:50 | الوحدة: سم


| المشروع / العميل | عنوان اللوحة | المقياس | التاريخ | رقم اللوحة |
|---|---|---|---|---|
| كوخ دور واحد – مجلس رجال ومجلس نساء + غرفتين – 12.00 × 10.00 م (120 م²)<br>عميل – كوخ 120 | الواجهة الأمامية (الضيافة) والواجهة الشرقية | 1:50 | 2026-10-25 | W-03 (3/15) |

مصنع وتد الأخشاب
Watad Wood Factory

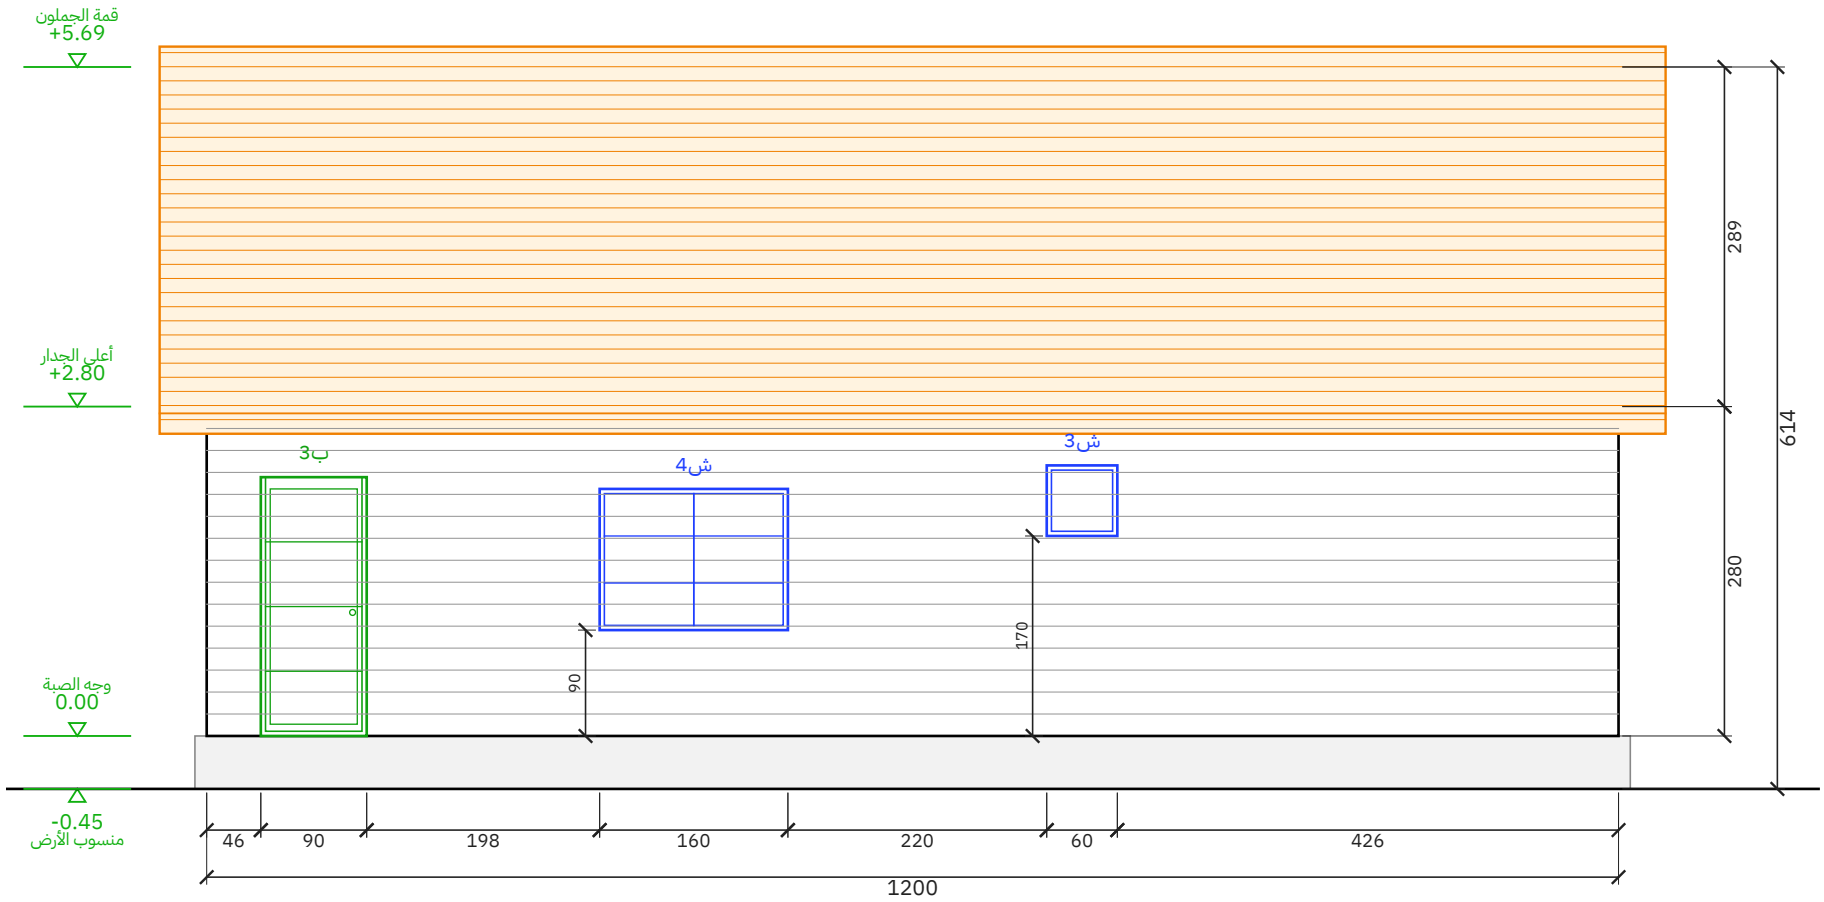


## الواجهة الخلفية

مقياس 1:50 | الوحدة: سم

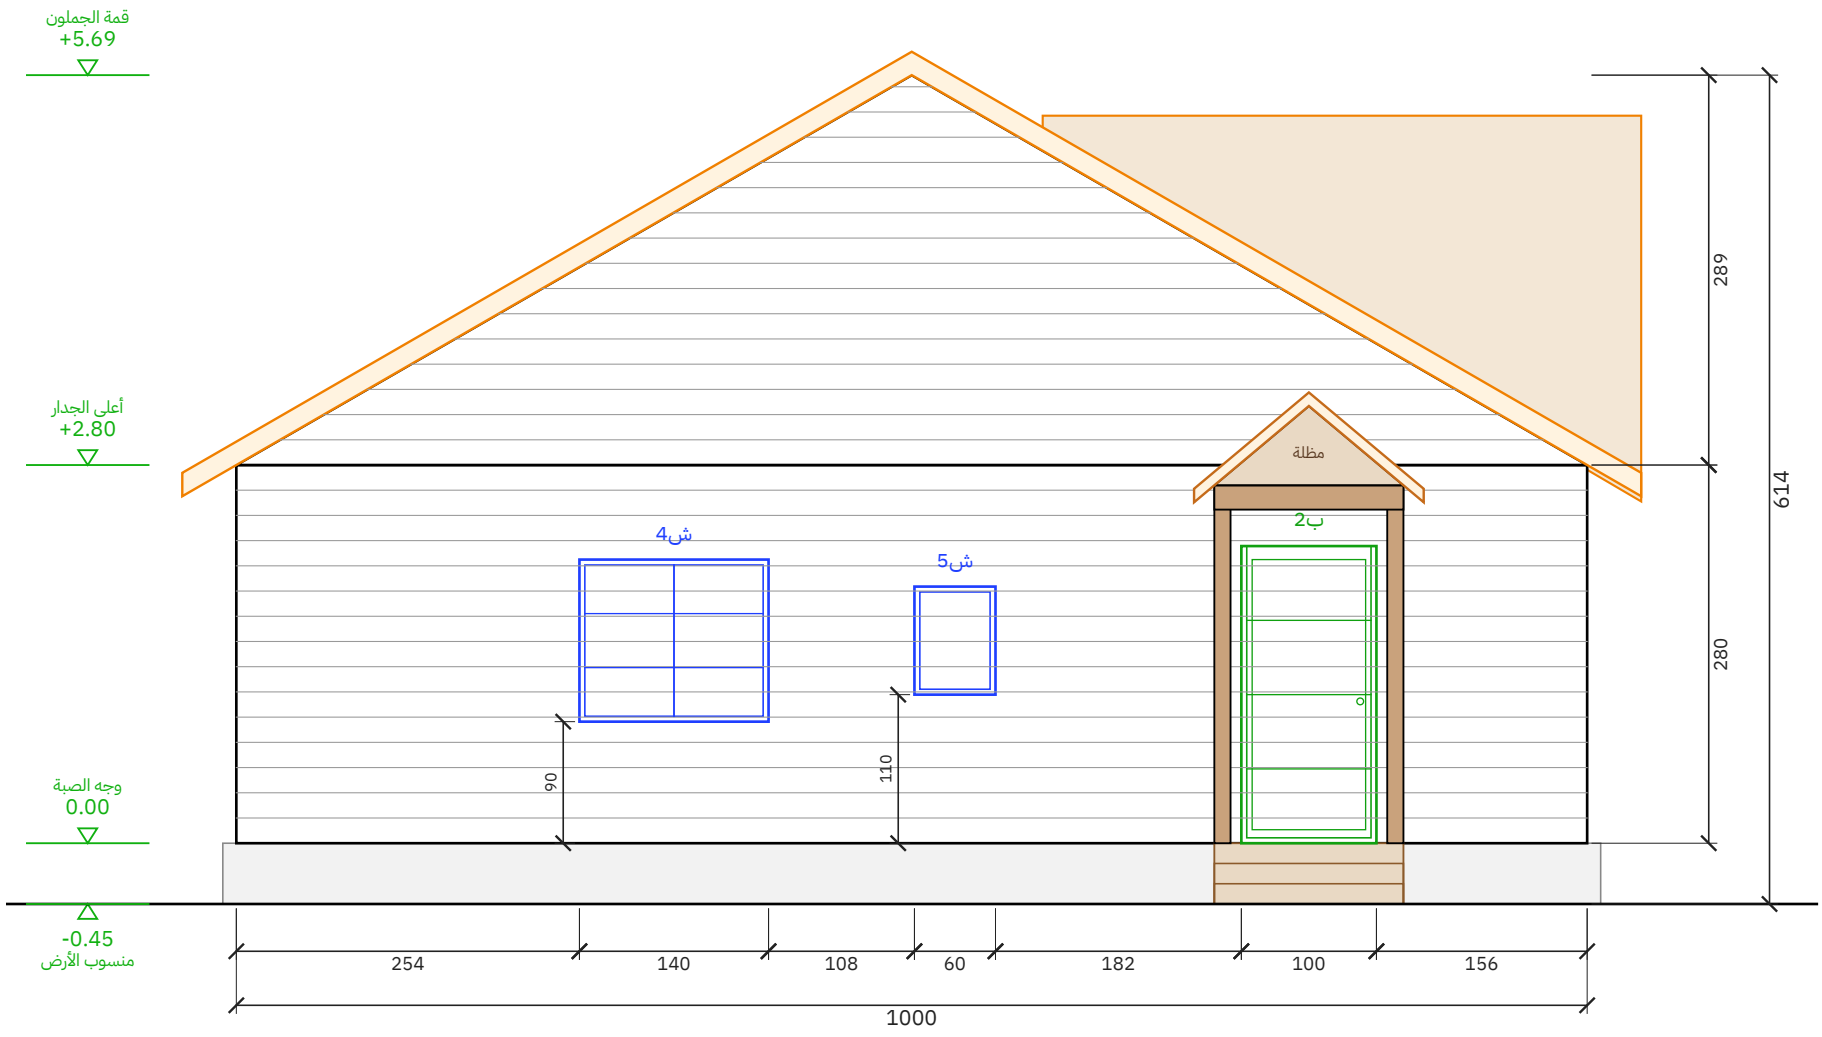


## الواجهة الغربية (مدخل النساء)


مقياس 1:50 | الوحدة: سم

| المشروع / العميل | عنوان اللوحة | المقياس | التاريخ | رقم اللوحة |
|---|---|---|---|---|
| كوخ دور واحد – مجلس رجال ومجلس نساء + غرفتين – 12.00 × 10.00 م (120 م²)<br>عميل – كوخ 120 | الواجهة الخلفية والواجهة الغربية (مدخل النساء) | 1:50 | 2026-10-25 | W-04 (4/15) |

مصنع وتد الأخشاب
Watad Wood Factory


## مسقط السقف (جملون)

رفرف 40 سم من كل جهة | مقياس 1:50

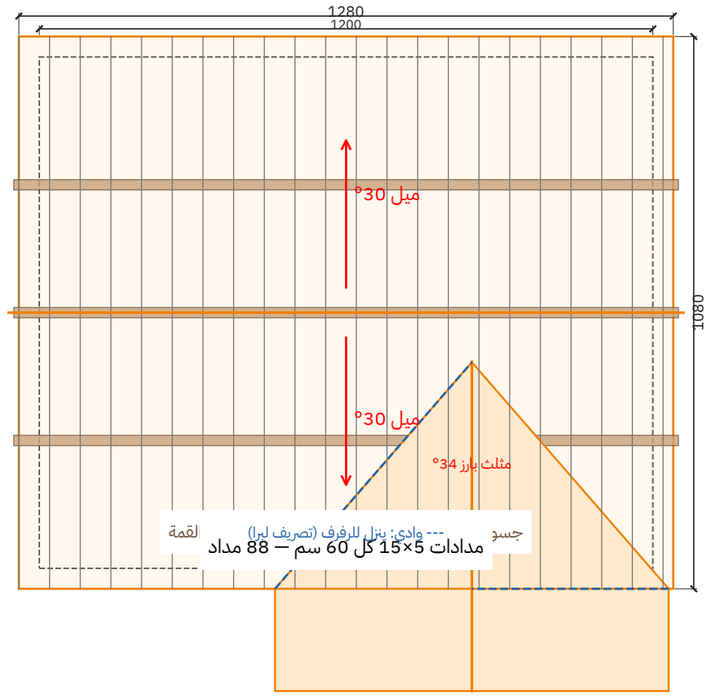



## قطاع عرضي أ-أ

مقياس 1:50 | الوحدة: سم

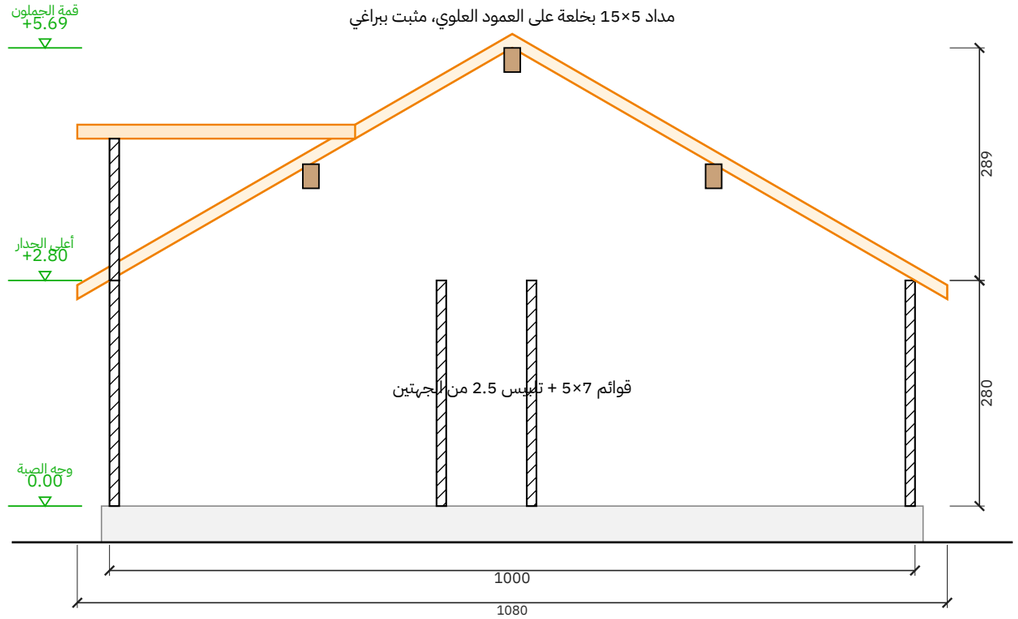


### تفصيلة جلوس المداد على العلوي (1:5)

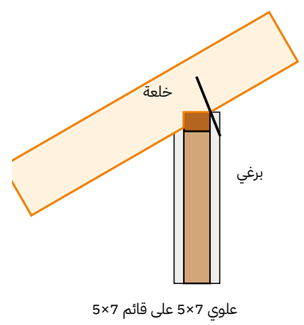


علوي 7×5 على قائم 7×5

| المشروع / العميل | عنوان اللوحة | المقياس | التاريخ | رقم اللوحة |
|---|---|---|---|---|
| **مصنع وتد الأخشاب** Watad Wood Factory — **كوخ دور واحد — مجلس رجال ومجلس نساء + غرفتين — 12.00 × 10.00 م (120 م²)** — **عميل — كوخ 120** | **مسقط السقف والقطاع** | **1:50** | **2026-10-25** | **W-05 (5/15)** |

# جدول مقاسات الأبواب والشبابيك

## مقاس الفتحة الصافي في الجدار - الوحدة: سم

| الرمز | النوع | العرض (سم) | الارتفاع (سم) | ارتفاع الجلسة (سم) | العدد | الموقع |
|---|---|---|---|---|---|---|
| ب1 | باب مزدوج | 120 | 230 | - | 1 | الأمامية (الضيافة) |
| ب2 | باب | 100 | 220 | - | 1 | الغربية (مدخل النساء) |
| ب3 | باب | 90 | 220 | - | 1 | الخلفية |
| ب4 | باب | 70 | 210 | - | 1 | دورة مياه الضيوف |
| ب5 | باب | 90 | 210 | - | 1 | مجلس النساء — ممر العائلة |
| ب6 | باب | 80 | 210 | - | 1 | باب خدمة المطبخ — مجلس الرجال |
| ب7 | باب | 85 | 210 | - | 2 | غرفة 1 - غرفة 2 |
| ب8 | باب | 75 | 210 | - | 1 | حمام العائلة |
| ب9 | باب | 85 | 210 | - | 1 | المطبخ — الممر |
| ف1 | باب | 140 | 230 | - | 1 | المدخل — مجلس الرجال |
| ز1 | شباك | 180 | 190 | 40 | 2 | الأمامية (الضيافة) 2 |
| ش1 | شباك | 180 | 150 | 70 | 1 | الأمامية (الضيافة) |
| ش2 | شباك | 120 | 90 | 110 | 1 | الشرقية |
| ش3 | شباك | 50 | 50 | 170 | 1 | الشرقية |
| ش3 | شباك | 60 | 60 | 170 | 1 | الخلفية |
| ش4 | شباك | 160 | 120 | 90 | 1 | الخلفية |
| ش4 | شباك | 140 | 120 | 90 | 1 | الغربية (مدخل النساء) |
| ش5 | شباك | 60 | 80 | 110 | 1 | الغربية (مدخل النساء) |

الإجمالي: أبواب 11 - شبابيك 9

# جدول المساحات وبيانات المشروع


## بيانات المشروع

| البند | البيان |
|---|---|
| المشروع | كوخ دور واحد — مجلس رجال ومجلس نساء + غرفتين — 12.00 × 10.00 م (120 م²) |
| العميل | عميل — كوخ 120 |
| الموقع | القصيم |
| الاستخدام | سكن |
| التاريخ | 2026-10-25 |
| نظام البناء | هيكل خشب 7×5 + تلبيس 2.5 سم من الجهتين |
| السقف | جملون 30° — قرميد معدني + 1 مثلث بارز |


## جدول المساحات

| م | الفراغ | الأبعاد (م) | المساحة (م2) |
|---|---|---|---|
| 1 | مجلس النساء | 4.74 × 3.94 | 18.68 |
| 2 | مجلس الرجال (الضيافة) | 5.28 × 3.94 | 20.80 |
| 3 | مدخل الضيوف | 1.50 × 2.26 | 3.39 |
| 4 | دورة مياه الضيوف | 1.50 × 1.56 | 2.34 |
| 5 | ممر العائلة | 8.82 × 1.00 | 8.82 |
| 6 | غرفة نوم 1 | 3.54 × 4.58 | 16.21 |
| 7 | حمام العائلة | 2.00 × 4.58 | 9.16 |
| 8 | غرفة نوم 2 | 3.04 × 4.58 | 13.92 |
| 9 | المطبخ | 2.82 × 5.70 | 16.07 |
|  | المساحة الصافية الداخلية |  | 109.40 |
|  | **تراس مدخل الضيوف** | **6.88 × 2.00** | **13.76** |
|  | **عتبة مدخل النساء** | **1.40 × 1.40** | **1.96** |
|  | **المساحة الإجمالية المبنية** | **12.00 × 10.00** | **120.00** |
|  | **المساحة الكلية (المبنية + التراسات)** |  | **135.72** |

## تأطير جدار جنوب — الطول 1188 سم، الارتفاع 280 سم

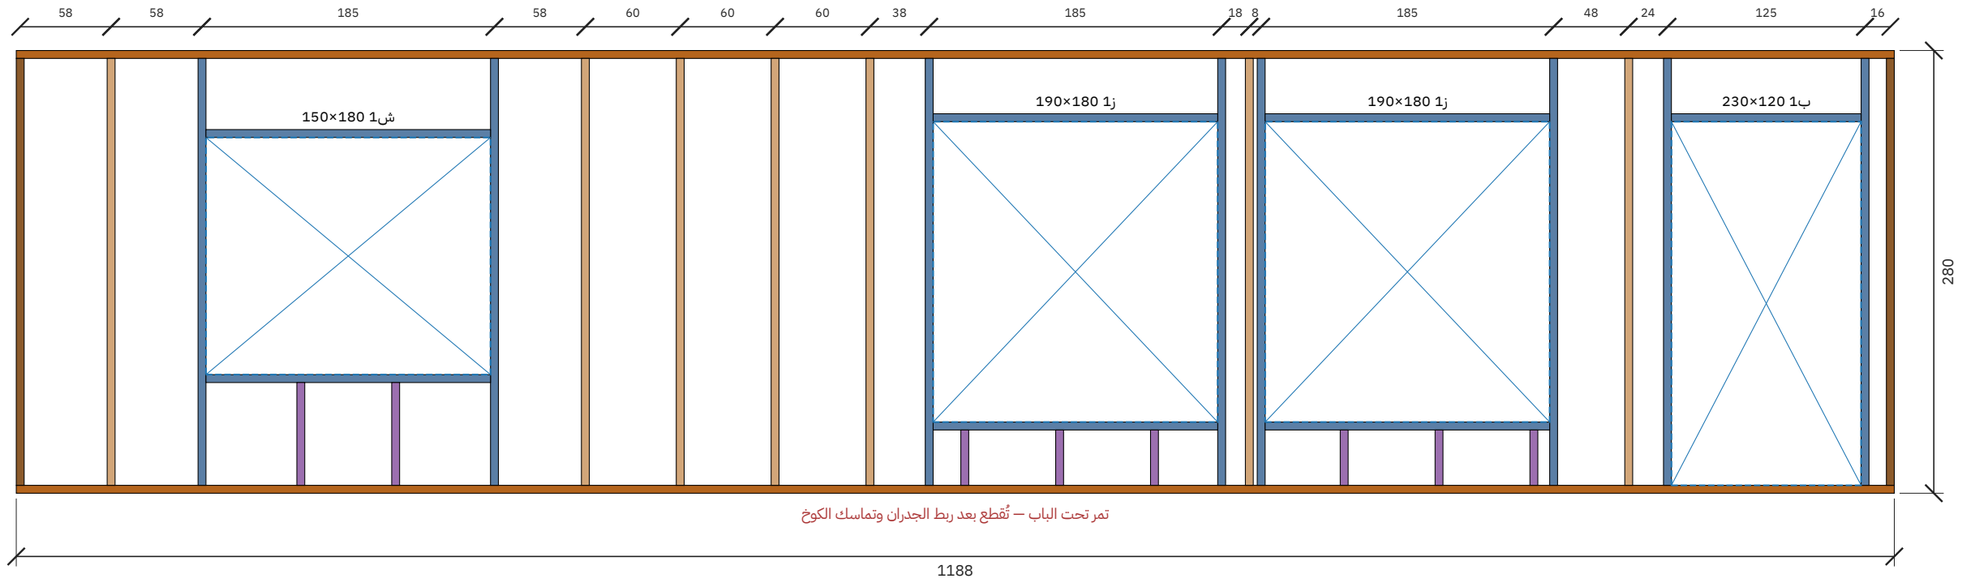



## تأطير جدار شرق — الطول 988 سم، الارتفاع 280 سم

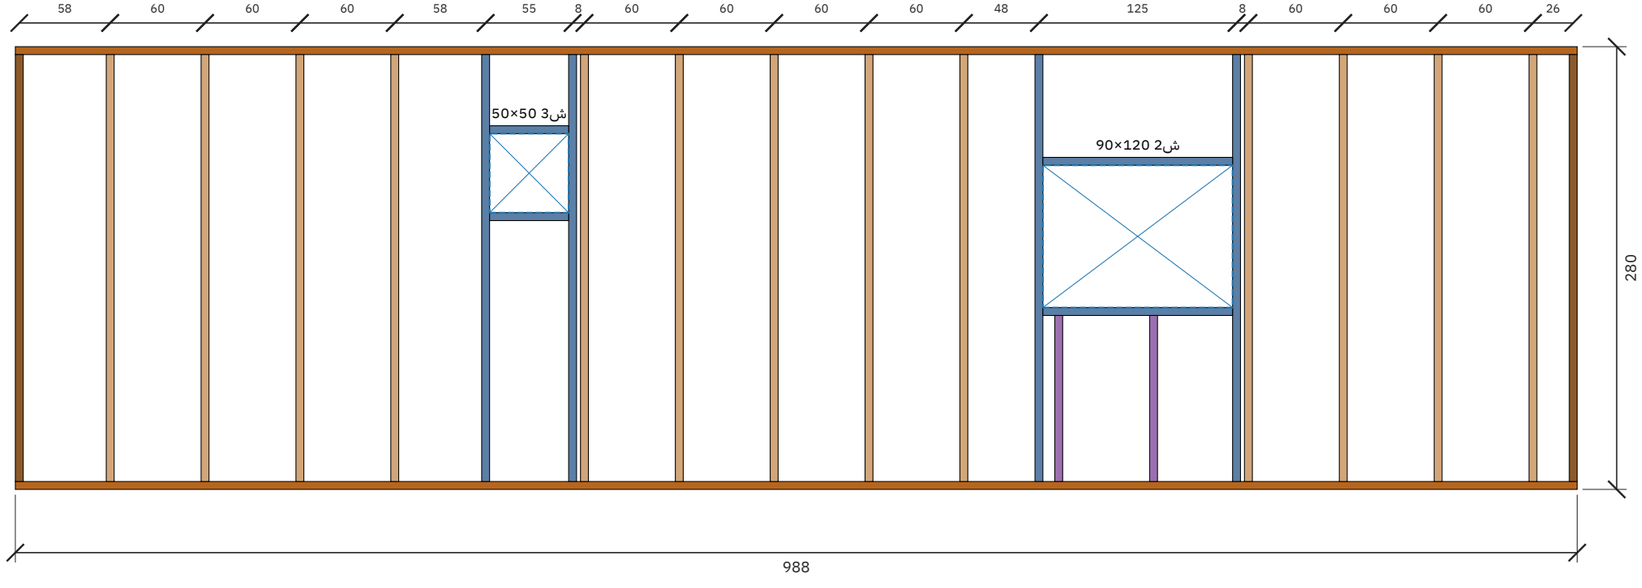



قاعدة سفلية | علوي | عمود | عمود زاوية | جنب فتحة | رأس فتحة | جلسة شباك | عمود قصير

| | | | | |
|---|---|---|---|---|
| مصنع وتد الأخشاب<br>Watad Wood Factory | المشروع / العميل<br>كوخ دور واحد — مجلس رجال ومجلس نساء + غرفتين — 12.00 × 10.00 م (120 م²)<br>عميل — كوخ 120 | عنوان اللوحة<br>لوحات التأطير (للورشة) | المقياس<br>— | التاريخ<br>2026-10-25 | رقم اللوحة<br>W-08 (8/15) |

## تأطير جدار شمال — الطول 1188 سم، الارتفاع 280 سم

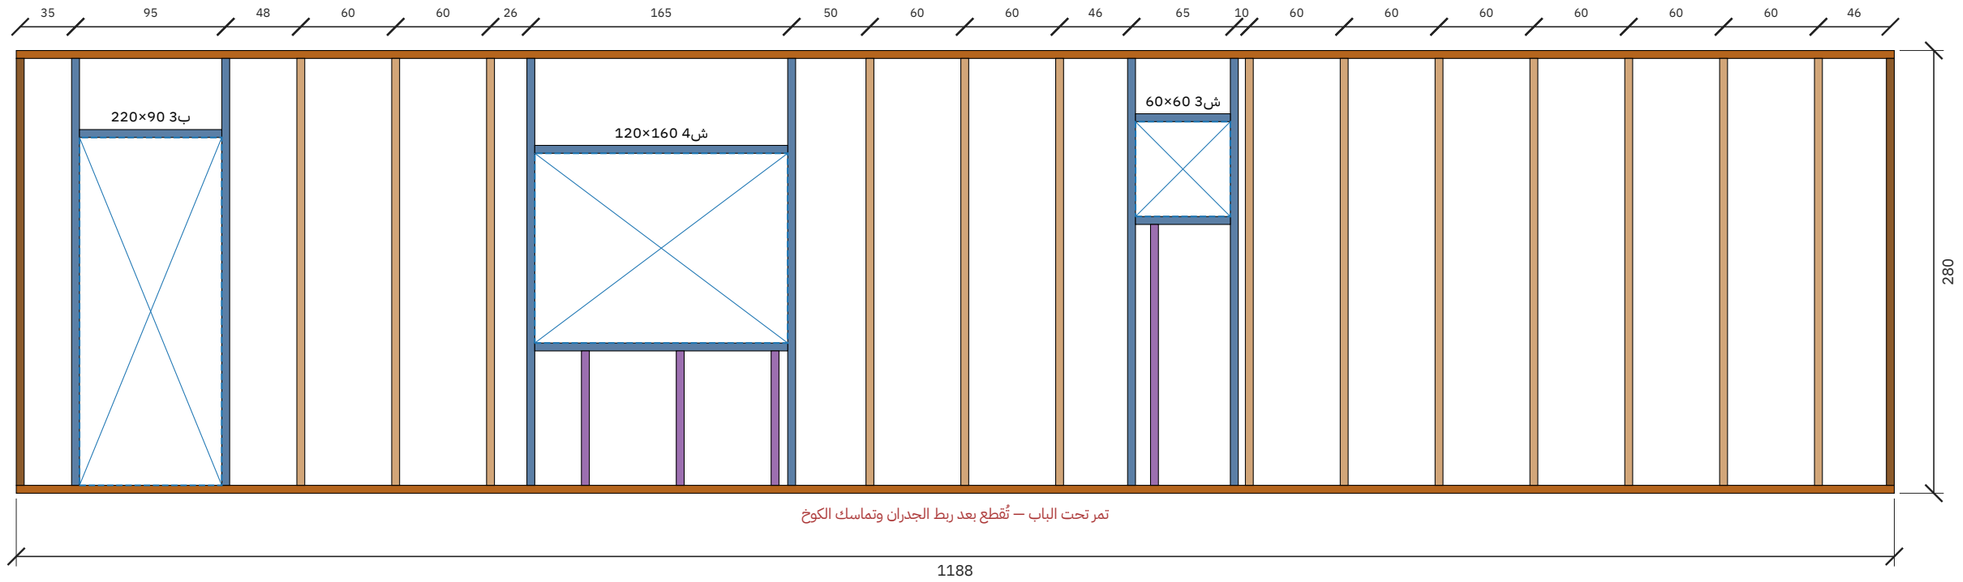


## تأطير جدار غرب — الطول 988 سم، الارتفاع 280 سم

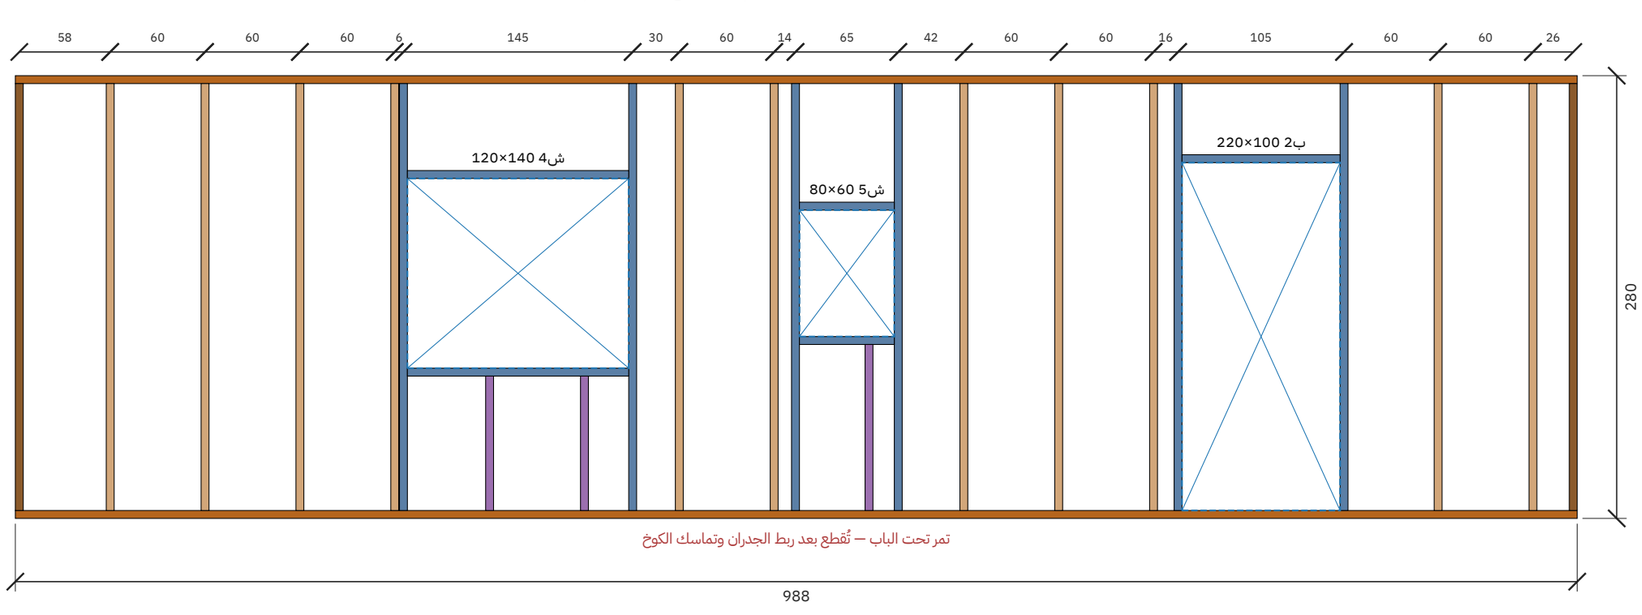



قاعدة سفلية | علوي | عمود | عمود زاوية | جنب فتحة | رأس فتحة | جلسة شباك | عمود قصير


| المشروع / العميل | عنوان اللوحة | المقياس | التاريخ | رقم اللوحة |
|---|---|---|---|---|
| **كوخ دور واحد — مجلس رجال ومجلس نساء + غرفتين — 12.00 × 10.00 م (120 م²)**<br>**عميل — كوخ 120** | **لوحات التأطير (للورشة)** | **—** | **2026-10-25** | **W-09 (9/15)** |

**مصنع وتد الأخشاب**
Watad Wood Factory

## تأطير جدار فاصل المجالس — الطول 406 سم، الارتفاع 280 سم (داخلي)

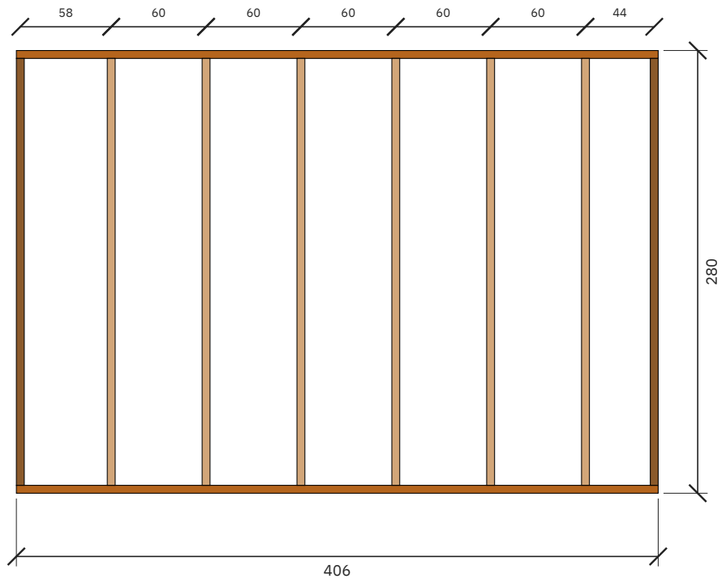



## تأطير جدار جدار المدخل — الطول 406 سم، الارتفاع 280 سم (داخلي)

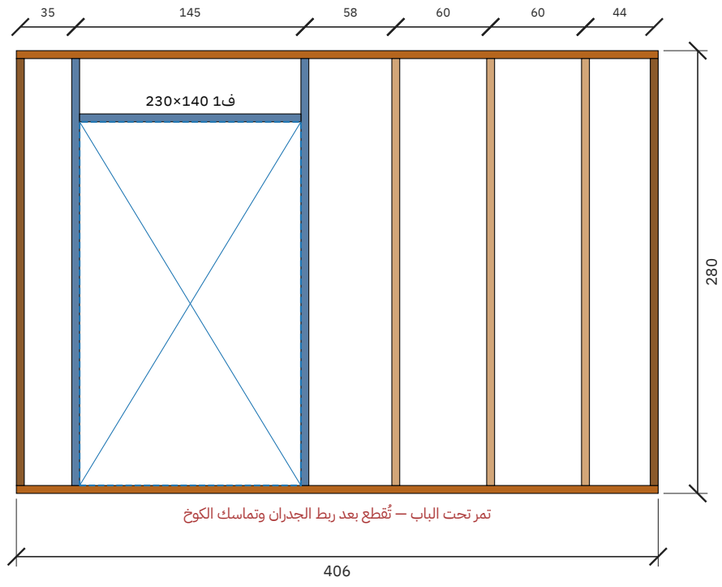



قاعدة سفلية | علوي | عمود | عمود زاوية | جنب فتحة | رأس فتحة | جلسة شباك | عمود قصير

| | | | | |
|---|---|---|---|---|
| **مصنع وتد الأخشاب**<br>Watad Wood Factory | المشروع / العميل<br>**كوخ دور واحد — مجلس رجال ومجلس نساء + غرفتين — 12.00 × 10.00 م (120 م²)**<br>**عميل — كوخ 120** | عنوان اللوحة<br>**لوحات التأطير (للورشة)** | المقياس<br>**—** | التاريخ<br>**2026-10-25** | رقم اللوحة<br>**W-10 (10/15)** |

## تأطير جدار جدار دورة مياه الضيوف — الطول 162 سم، الارتفاع 280 سم (داخلي)

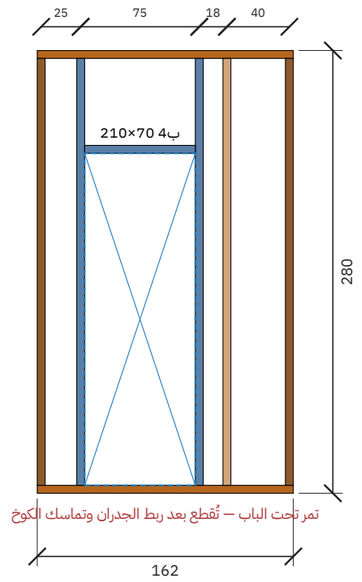



## تأطير جدار خلف المجالس — الطول 1188 سم، الارتفاع 280 سم (داخلي)

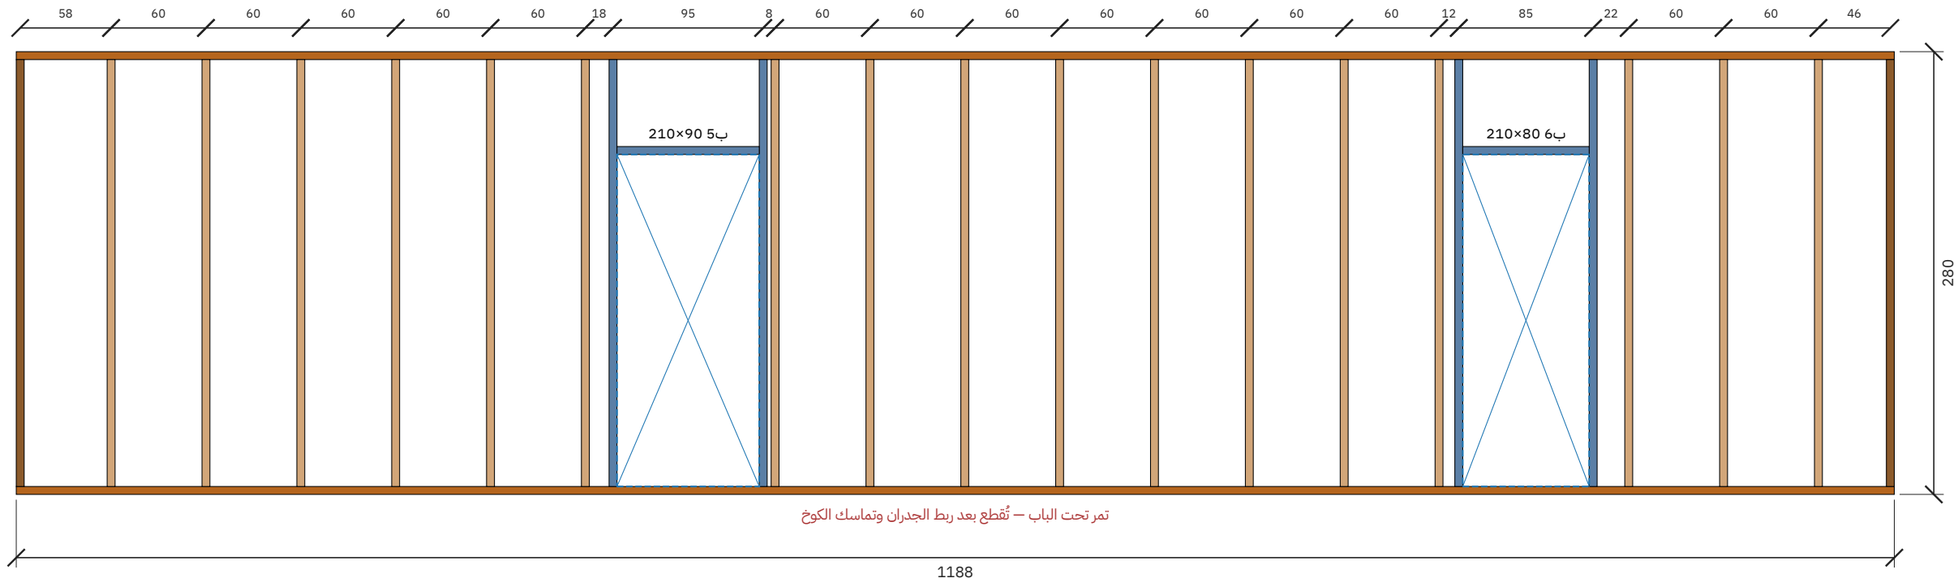



عمود قصير | جلسة شباك | رأس فتحة | جنب فتحة | عمود زاوية | عمود | علوي | قاعدة سفلية

| | | | | |
|---|---|---|---|---|
| مصنع وتد الأخشاب<br>Watad Wood Factory | المشروع / العميل<br>كوخ دور واحد — مجلس رجال ومجلس نساء + غرفتين — 12.00 × 10.00 م (120 م²)<br>عميل — كوخ 120 | عنوان اللوحة<br>لوحات التأطير (للورشة) | المقياس<br>— | التاريخ<br>2026-10-25 | رقم اللوحة<br>W-11 (11/15) |

## تأطير جدار جدار الممر — الطول 894 سم، الارتفاع 280 سم (داخلي)

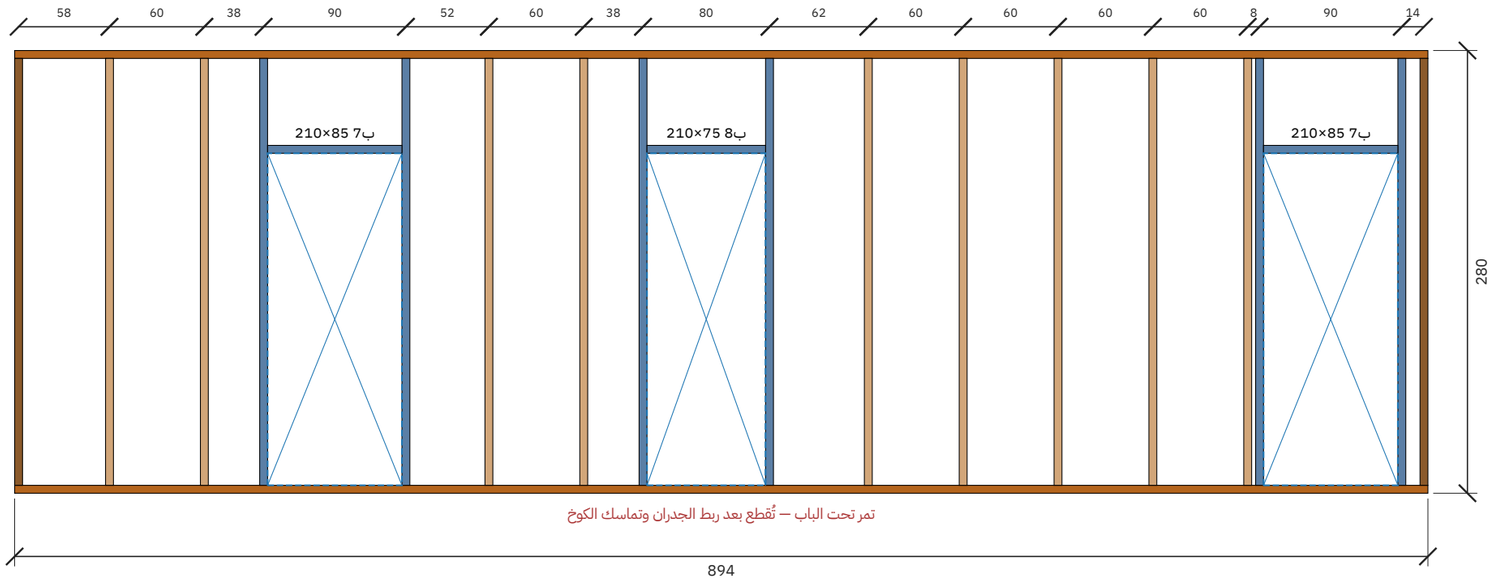



## تأطير جدار فاصل غرفة 1 — الطول 470 سم، الارتفاع 280 سم (داخلي)

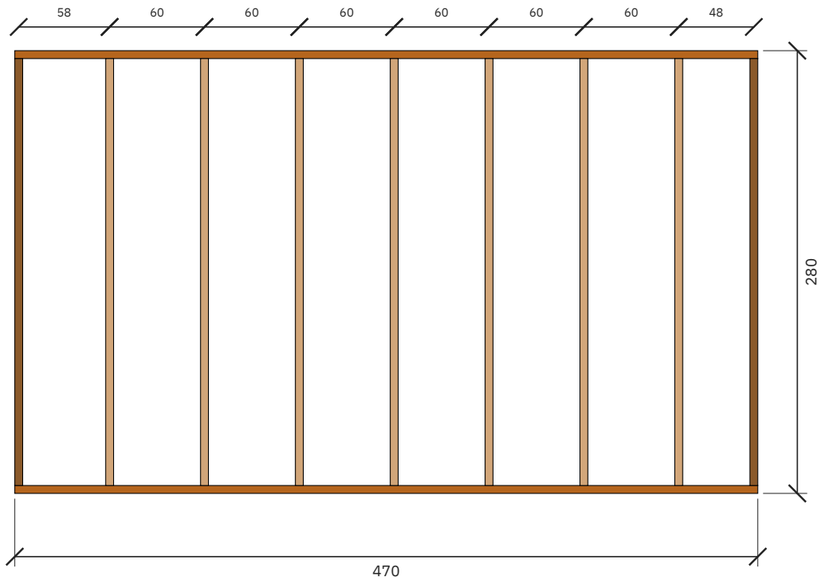



قاعدة سفلية | علوي | عمود | عمود زاوية | جنب فتحة | رأس فتحة | جلسة شباك | عمود قصير

| | | | | |
|---|---|---|---|---|
| مصنع وتد الأخشاب<br>Watad Wood Factory | المشروع / العميل<br>كوخ دور واحد — مجلس رجال ومجلس نساء + غرفتين — 12.00 × 10.00 م (120 م²)<br>عميل — كوخ 120 | عنوان اللوحة<br>لوحات التأطير (للورشة) | المقياس<br>— | التاريخ<br>2026-10-25 | رقم اللوحة<br>W-12 (12/15) |

## تأطير جدار فاصل الحمام — الطول 470 سم، الارتفاع 280 سم (داخلي)

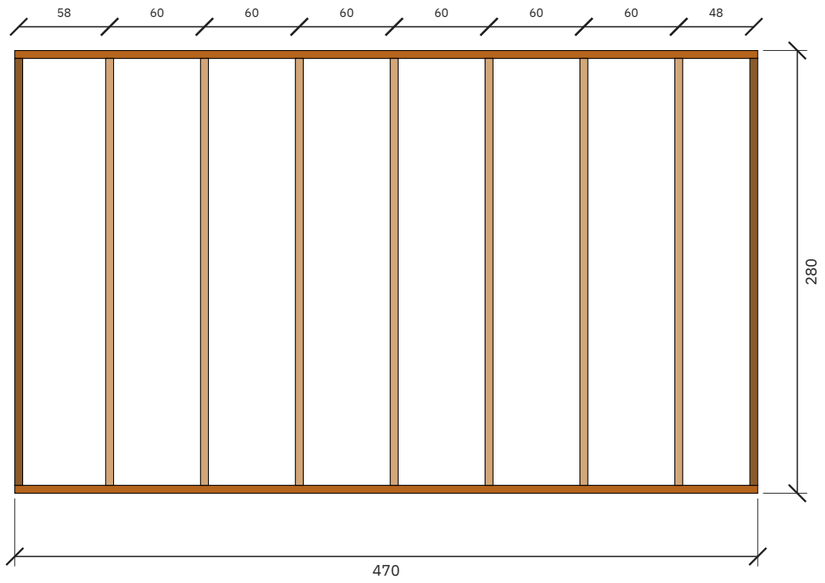


## تأطير جدار جدار المطبخ — الطول 582 سم، الارتفاع 280 سم (داخلي)

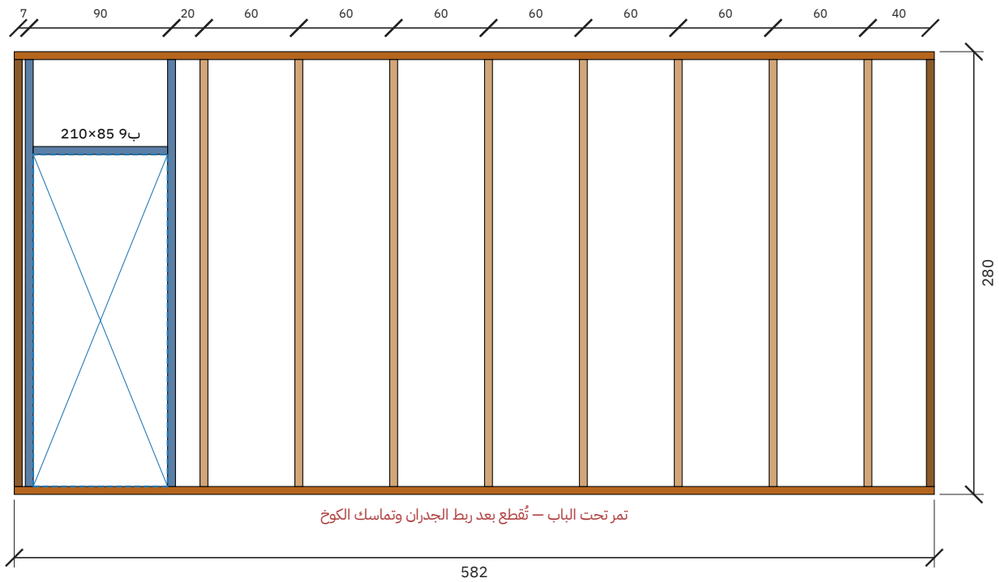


قاعدة سفلية | علوي | عمود | عمود زاوية | جنب فتحة | رأس فتحة | جلسة شباك | عمود قصير

| | | | | |
|---|---|---|---|---|
| مصنع وتد الأخشاب<br>Watad Wood Factory | المشروع / العميل<br>**كوخ دور واحد — مجلس رجال ومجلس نساء + غرفتين — 12.00 × 10.00 م (120 م²)**<br>**عميل — كوخ 120** | عنوان اللوحة<br>**لوحات التأطير (للورشة)** | المقياس<br>**—** | التاريخ<br>**2026-10-25** | رقم اللوحة<br>**W-13 (13/15)** |

# جدول الكميات وخطة تقطيع الطبليات

| البند | القيمة |
|---|---|
| الارتفاع المطلوب / المعتمد | 280 / 280 سم |
| السقف | جملون 30° — أعلى نقطة 569 سم من وجه الصبة |
| المدادات 5×15 | 88 مداد (22 خط × قطعتين موصولة فوق الجسر الحامل بتراكب 60 سم) × حتى 370 سم — من طبلية 480 |
| طبليات الطريقة الأولى (مداد + عمود) | 88 طبلية × 480 سم |
| طبليات الطريقة الثانية (3 أعمدة) | 42 طبلية × 320 سم |
| مدادات المثلث البارز (S) 34° | 16 مداد حتى 292 سم (طبلية 320) + 2 مداد وادي 642 سم — وصلة |
| إجمالي الطبليات 5×22.5 | 148 |
| إجمالي قطع 5×7 | 236 |
| قائمة تقطيع 5×7 | 1188سم×6 \| 988سم×4 \| 894سم×2 \| 582سم×2 \| 470سم×4 \| 406سم×4 \| 270سم×166 \| 180سم×6 \| 165سم×1 |
| | 162سم×2 \| 160سم×2 \| 140سم×3 \| 120سم×3 \| 105سم×3 \| 100سم×1 \| 90سم×2 \| 85سم×8 \| 80سم×1 |
| ألواح تلبيس 2.5 سم | 602 لوح × 400 سم (مجموع الصفوف 1977.4 م، 24 وجه) |
| أسمنت بورد 12 مم (122×244) | 40 لوح (داخل دورات المياه) |
| العزل | 296 لوح فوم صخري 80 |
| الصبة | يجهزها العميل — 20 سم، مفرغة تحت دورات المياه |

# مراجعة التصميم مقابل قواعد المصنع

| النوع | البند | التفاصيل | المقترح |
|---|---|---|---|
| ملاحظة | بحر المدادات | أطول بحر بدون جدار داخلي يحمل المداد: جهة أ: 412 سم، جهة ب: 500 سم. يحتاج رقم المصنع لأقصى بحر مسموح لتحديد المدادات اللي تُقوّى 20×5. | |
| ملاحظة | الصبة والدرج | ارتفاع الصبة 45 سم ← 3 درجة بقائمة 15.0 سم. | |
| ملاحظة | مناسيب رؤوس الفتحات | رؤوس الأبواب والشبابيك على مناسيب مختلفة: 190، 200، 210، 220، 230 سم. | |
| تنبيه | مداد الوادي | مداد الوادي 642 سم أطول من الطبلية — يُوصل بوصلة مثبتة فوق جدار/دعامة | وصلة مزدوجة 5×15 مع براغي، ومرتكزة على جدار أو دعامة 5×7. |
| سؤال | يحتاج تأكيد | أقصى بحر للمداد بدون جدار داخلي قبل إضافة تقوية 5×7 (مداد 20×5)؟ | |
| سؤال | يحتاج تأكيد | التغطية الصافية للوح التلبيس بعد التعشيق (مستنتجة مؤقتاً 18.67 سم من 280/15)؟ | |
| سؤال | يحتاج تأكيد | هل يوضع أعمدة قصيرة فوق رأس الشباك/الباب إلى العلوي؟ | |
| سؤال | يحتاج تأكيد | مكان الوصلة في القاعدة والعلوي إذا الجدار أطول من الطبلية؟ | |