

المسقط الأفقي مع الفرش

الأبعاد بالسنتيمتر - الجدران: قوائم 7×5 + تلبيس 2.5 من الجهتين (12 سم)

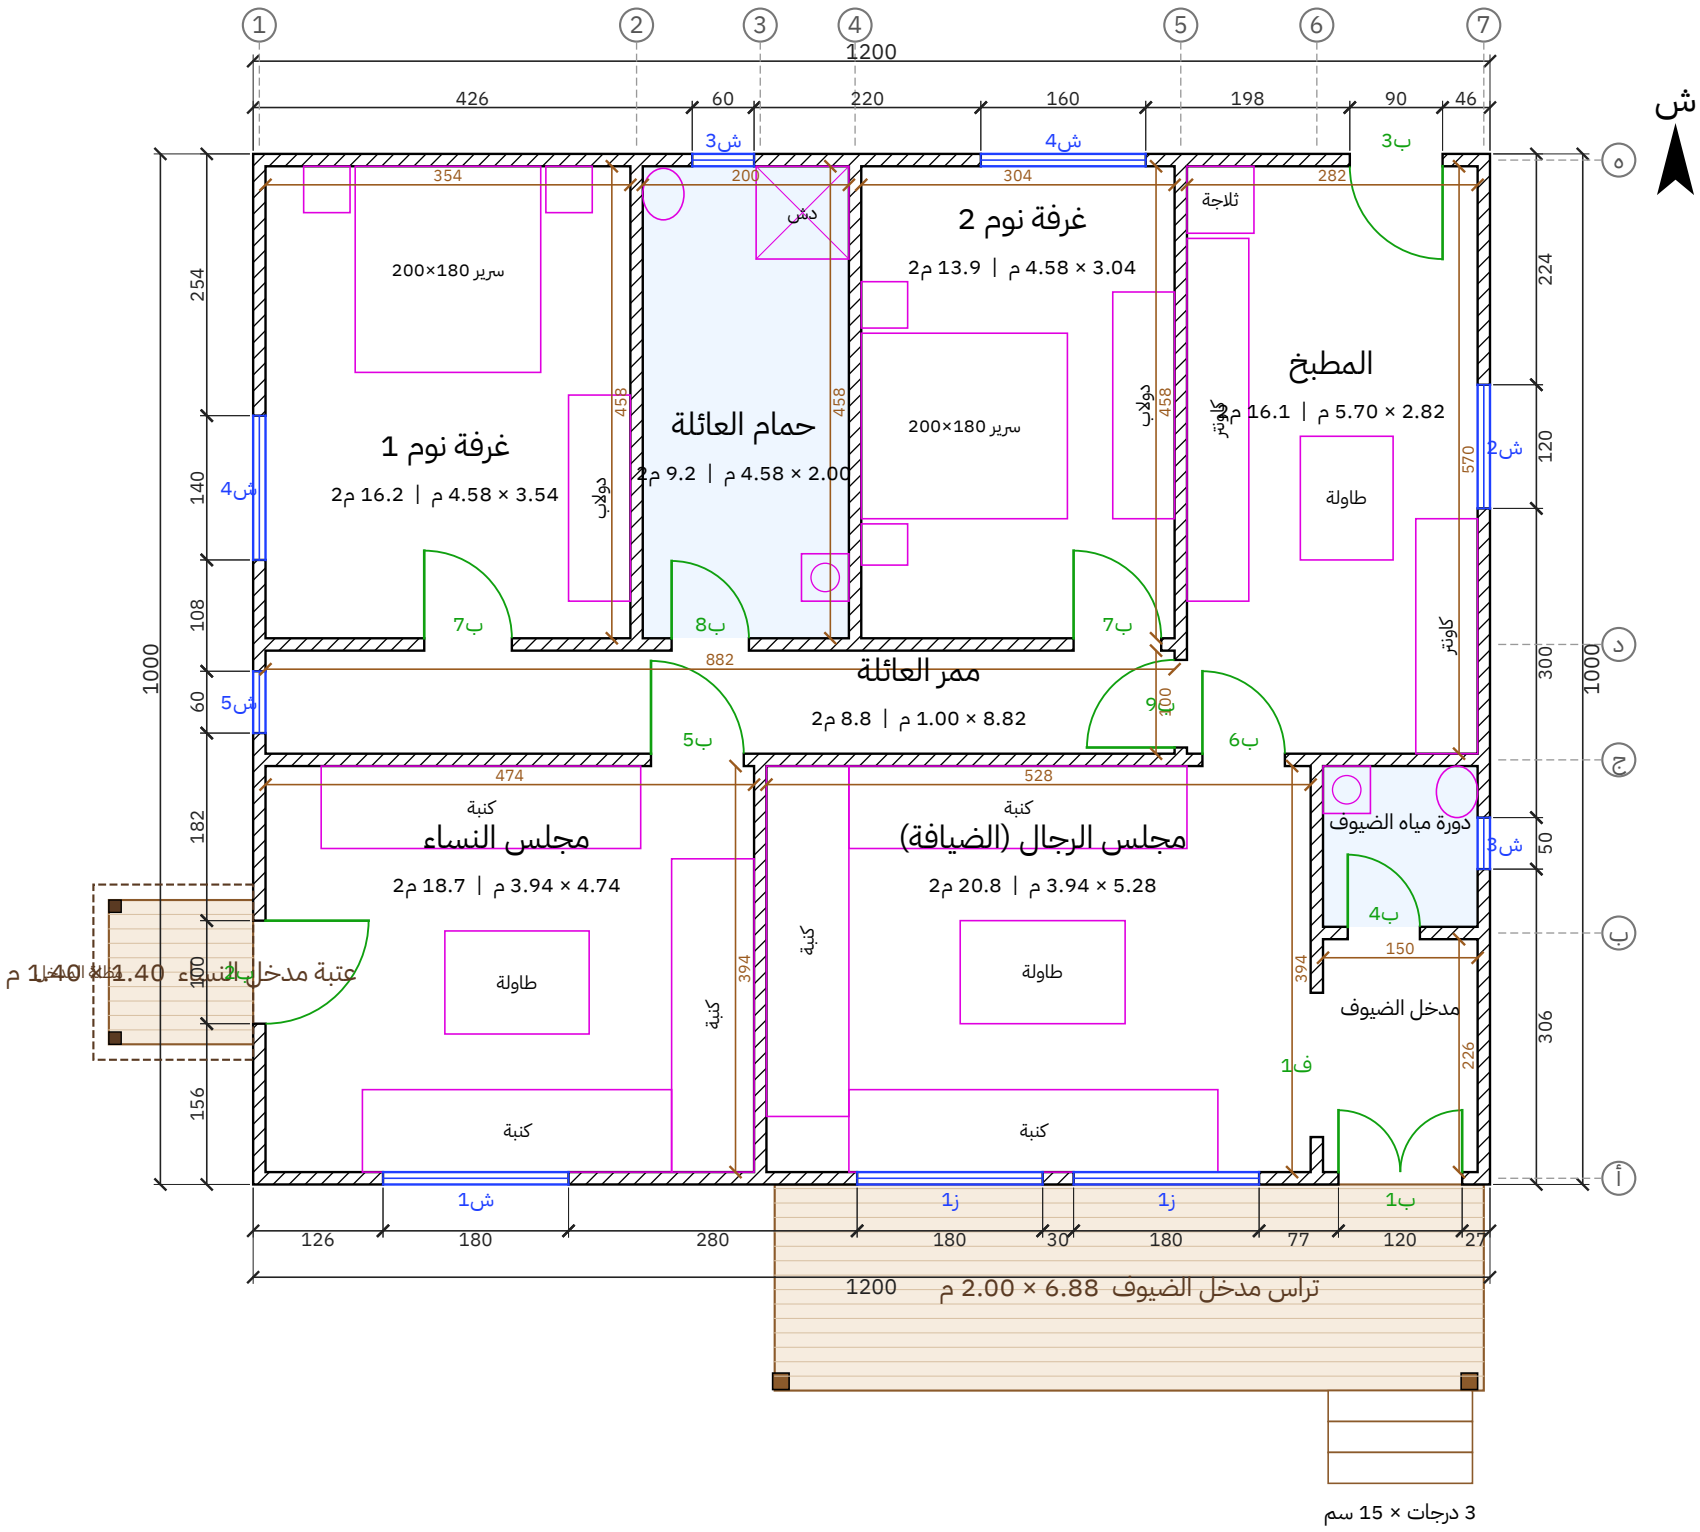


مصنع وتد الأخشاب Watad Wood Factory	المشروع / العميل كوخ دور واحد – مجلس رجال ومجلس نساء + غرفتين – 12.00 × 10.00 م (120 م²) عميل – كوخ 120	عنوان اللوحة المسقط الأفقي	المقياس 1:50	التاريخ 2026-10-25	رقم اللوحة A-01 (1/9)

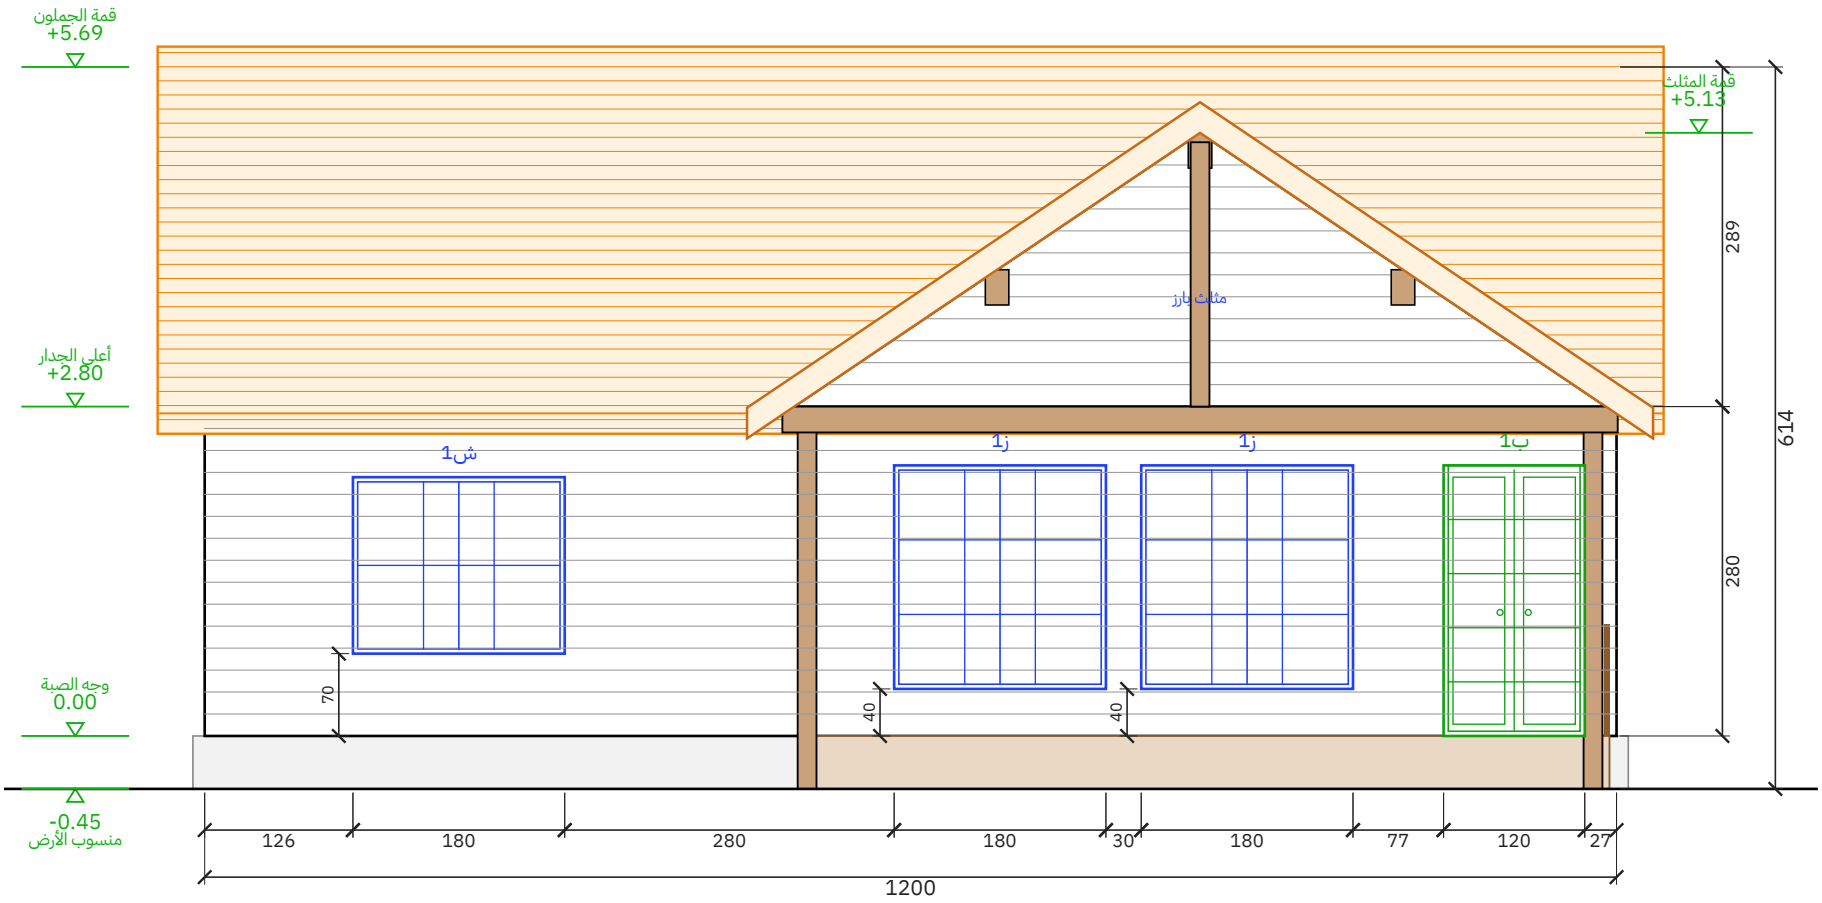

الواجهة الأمامية (الضيافة)

مقياس 1:50 | الوحدة: سم

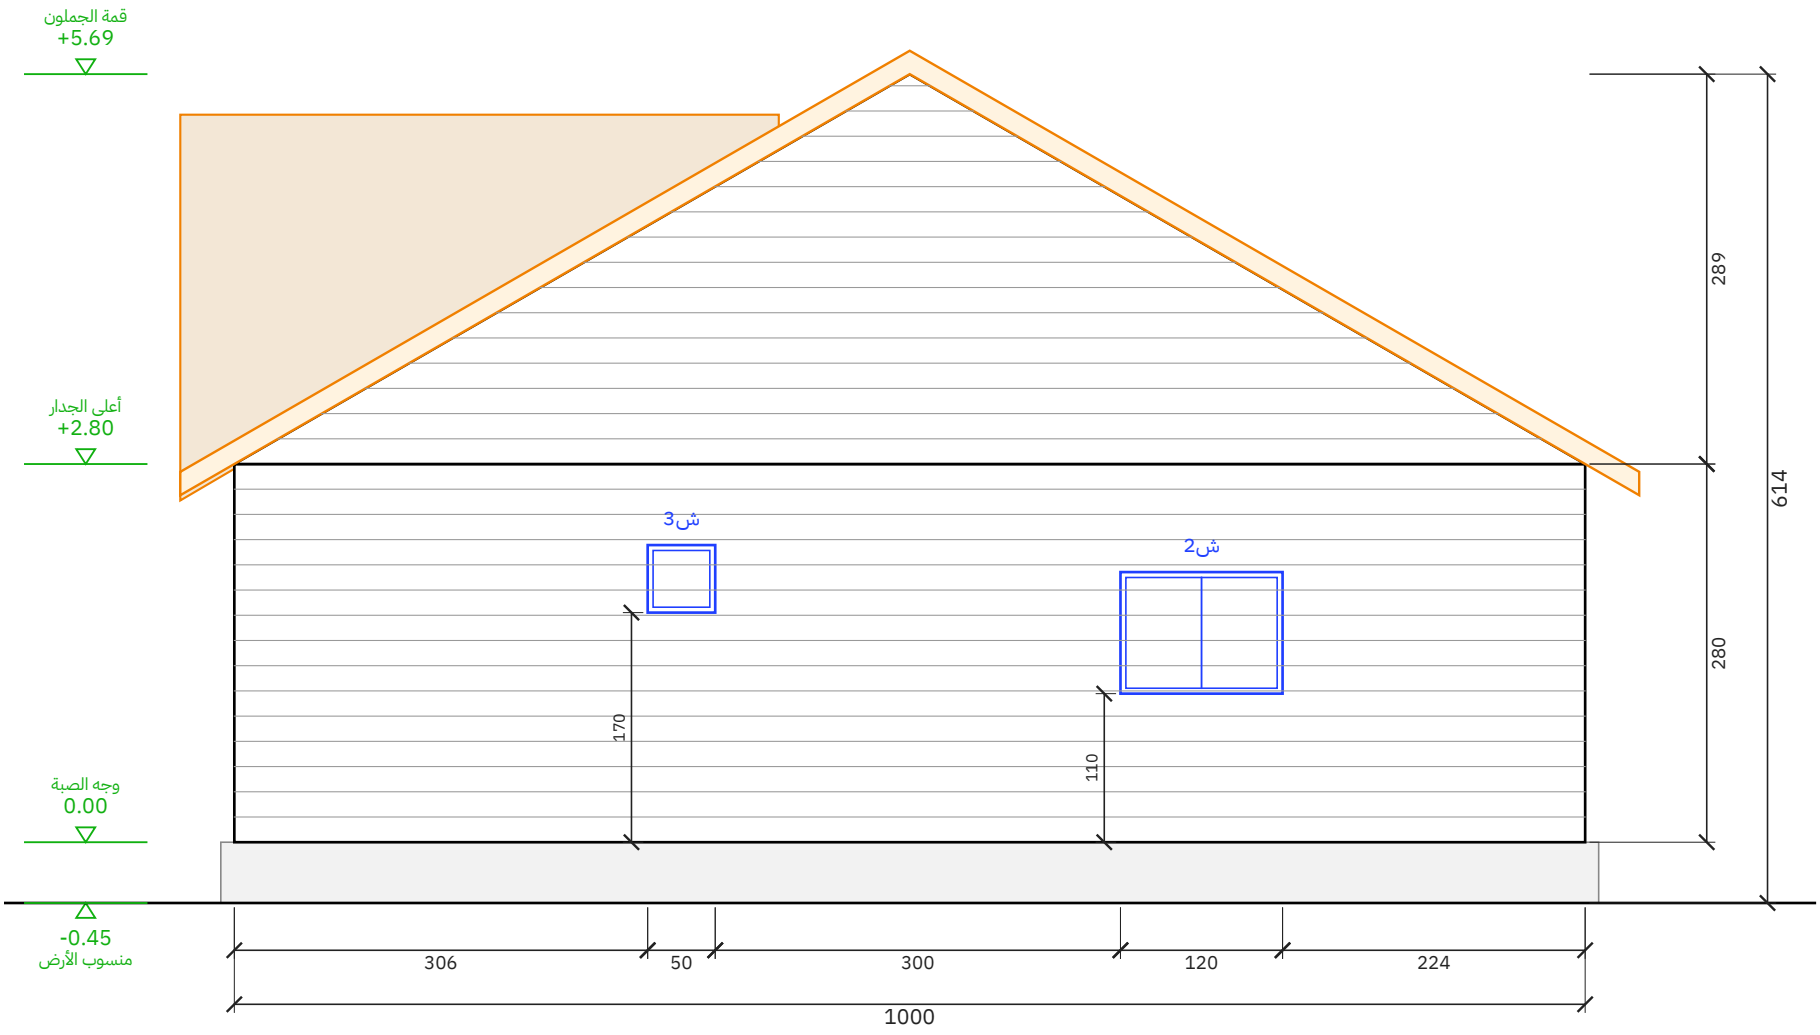


الواجهة الشرقية

مقياس 1:50 | الوحدة: سم


المشروع / العميل	عنوان اللوحة	المقياس	التاريخ	رقم اللوحة
كوخ دور واحد – مجلس رجال ومجلس نساء + غرفتين – 10.00 × 12.00 م (120 م²) عميل – كوخ 120	الواجهة الأمامية (الضيافة) والواجهة الشرقية	1:50	2026-10-25	A-02 (2/9)

مصنع وتد الأخشاب
Watad Wood Factory

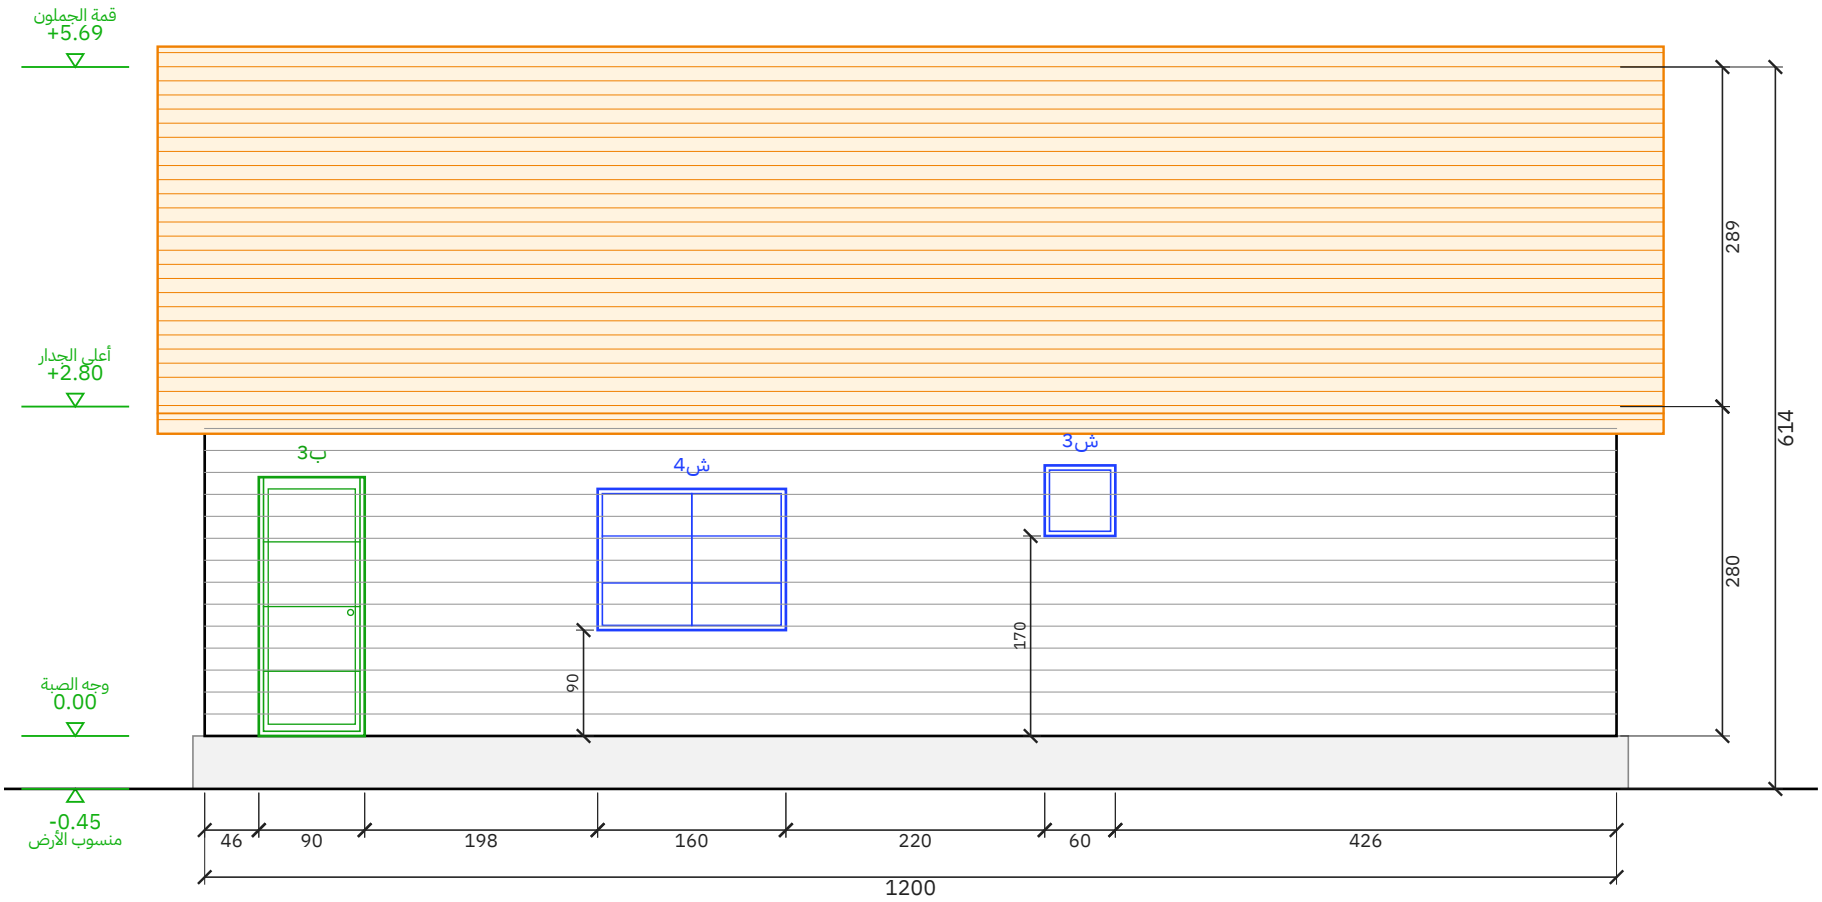

الواجهة الخلفية

مقياس 1:50 | الوحدة: سم

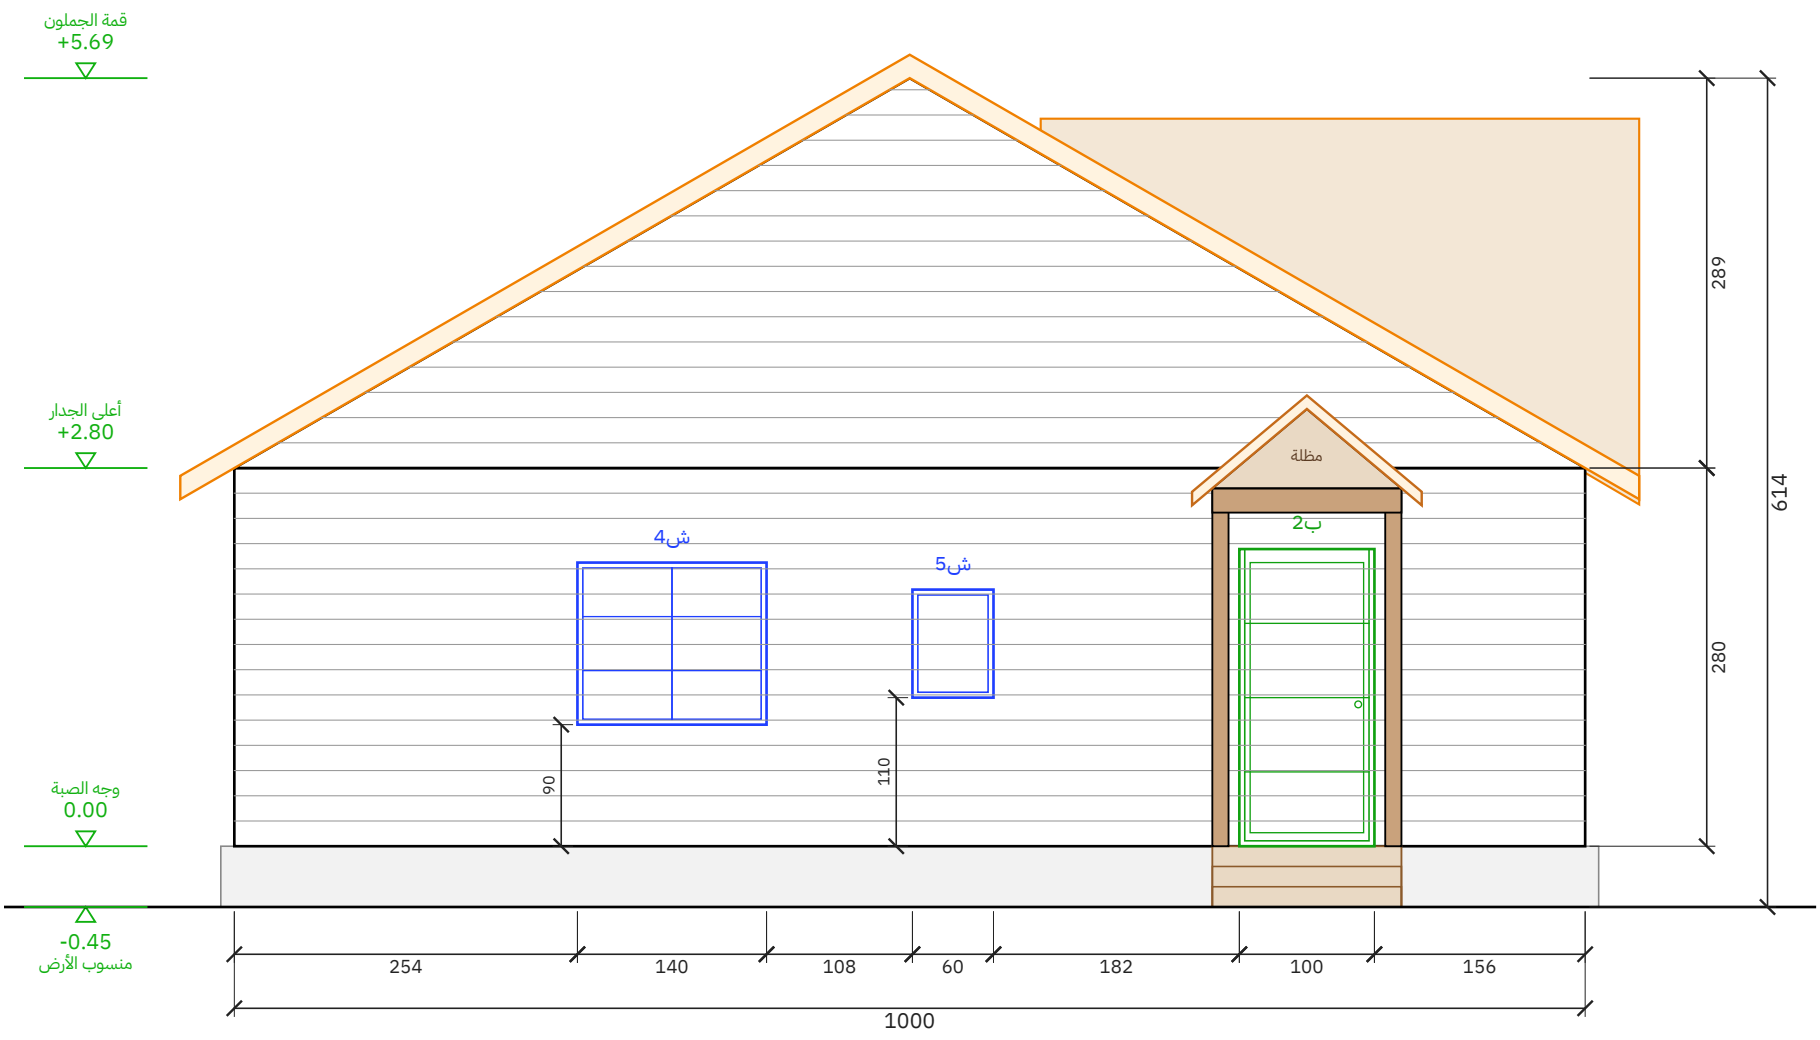

الواجهة الغربية (مدخل النساء)


مقياس 1:50 | الوحدة: سم

المشروع / العميل	عنوان اللوحة	المقياس	التاريخ	رقم اللوحة
كوخ دور واحد – مجلس رجال ومجلس نساء + غرفتين – 12.00 × 10.00 م (120 م²) عميل – كوخ 120	الواجهة الخلفية والواجهة الغربية (مدخل النساء)	1:50	2026-10-25	A-03 (3/9)

مصنع وتد الأخشاب
Watad Wood Factory


مسقط السقف (جملون)

رفرف 40 سم من كل جهة | مقياس 1:50

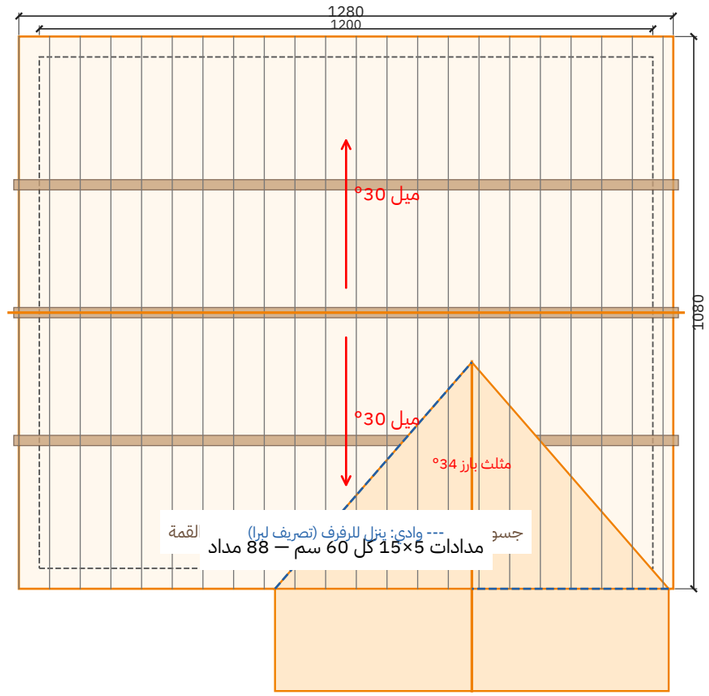


قطاع عرضي أ-أ

مقياس 1:50 | الوحدة: سم

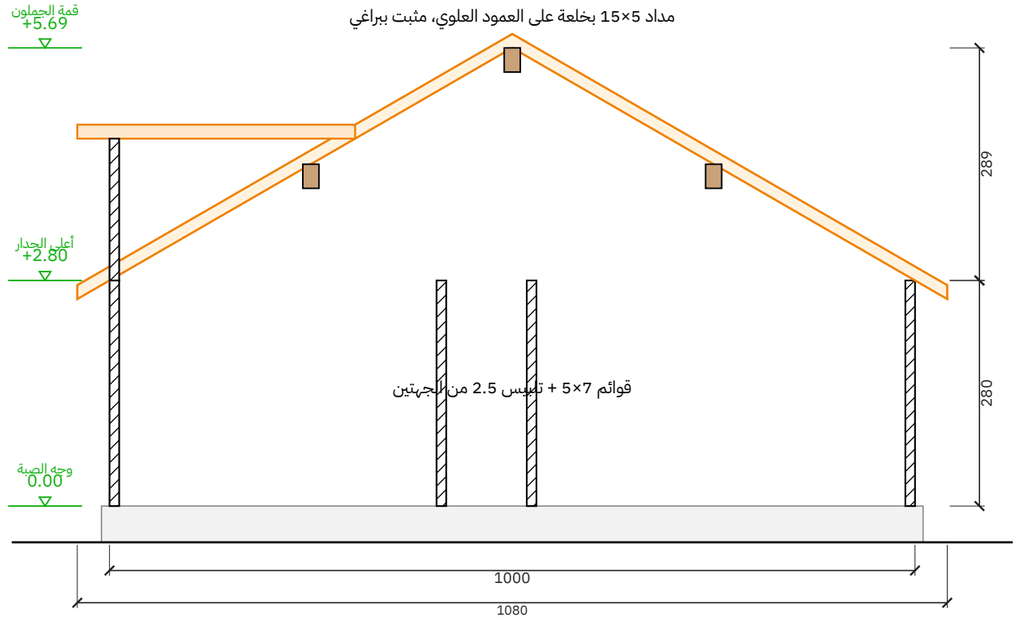

تفصيلة جلوس المداد على العلوي (1:5)

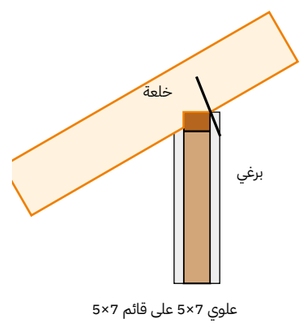

علوي 7×5 على قائم 7×5

المشروع / العميل	عنوان اللوحة	المقياس	التاريخ	رقم اللوحة
كوخ دور واحد — مجلس رجال ومجلس نساء + غرفتين — 12.00 × 10.00 م (120 م²) **عميل — كوخ 120**	**مسقط السقف والقطاع**	**1:50**	**2026-10-25**	**A-04 (4/9)**

مصنع وتد الأخشاب
Watad Wood Factory

جدول مقاسات الأبواب والشبابيك

مقاس الفتحة الصافي في الجدار - الوحدة: سم

الرمز	النوع	العرض (سم)	الارتفاع (سم)	ارتفاع الجلسة (سم)	العدد	الموقع
ب1	باب مزدوج	120	230	-	1	الأمامية (الضيافة)
ب2	باب	100	220	-	1	الغربية (مدخل النساء)
ب3	باب	90	220	-	1	الخلفية
ب4	باب	70	210	-	1	دورة مياه الضيوف
ب5	باب	90	210	-	1	مجلس النساء — ممر العائلة
ب6	باب	80	210	-	1	باب خدمة المطبخ — مجلس الرجال
ب7	باب	85	210	-	2	غرفة 1 - غرفة 2
ب8	باب	75	210	-	1	حمام العائلة
ب9	باب	85	210	-	1	المطبخ — الممر
ف1	باب	140	230	-	1	المدخل — مجلس الرجال
ز1	شباك	180	190	40	2	الأمامية (الضيافة) 2
ش1	شباك	180	150	70	1	الأمامية (الضيافة)
ش2	شباك	120	90	110	1	الشرقية
ش3	شباك	50	50	170	1	الشرقية
ش3	شباك	60	60	170	1	الخلفية
ش4	شباك	160	120	90	1	الخلفية
ش4	شباك	140	120	90	1	الغربية (مدخل النساء)
ش5	شباك	60	80	110	1	الغربية (مدخل النساء)

الإجمالي: أبواب 11 - شبابيك 9

جدول المساحات وبيانات المشروع

بيانات المشروع

البند	البيان
المشروع	كوخ دور واحد — مجلس رجال ومجلس نساء + غرفتين — 12.00 × 10.00 م (120 م²)
العميل	عميل — كوخ 120
الموقع	القصيم
الاستخدام	سكن
التاريخ	2026-10-25
نظام البناء	هيكل خشب 7×5 + تلبيس 2.5 سم من الجهتين
السقف	جملون 30° — قرميد معدني + 1 مثلث بارز

جدول المساحات


م	الفراغ	الأبعاد (م)	المساحة (م2)
1	مجلس النساء	4.74 × 3.94	18.68
2	مجلس الرجال (الضيافة)	5.28 × 3.94	20.80
3	مدخل الضيوف	1.50 × 2.26	3.39
4	دورة مياه الضيوف	1.50 × 1.56	2.34
5	ممر العائلة	8.82 × 1.00	8.82
6	غرفة نوم 1	3.54 × 4.58	16.21
7	حمام العائلة	2.00 × 4.58	9.16
8	غرفة نوم 2	3.04 × 4.58	13.92
9	المطبخ	2.82 × 5.70	16.07
	المساحة الصافية الداخلية		109.40
	تراس مدخل الضيوف	**6.88 × 2.00**	**13.76**
	عتبة مدخل النساء	**1.40 × 1.40**	**1.96**
	المساحة الإجمالية المبنية	**12.00 × 10.00**	**120.00**
	المساحة الكلية (المبنية + التراسات)		**135.72**

لقطات المنظور الخارجي


المنظور الأمامي




منظور أمامي من اليسار

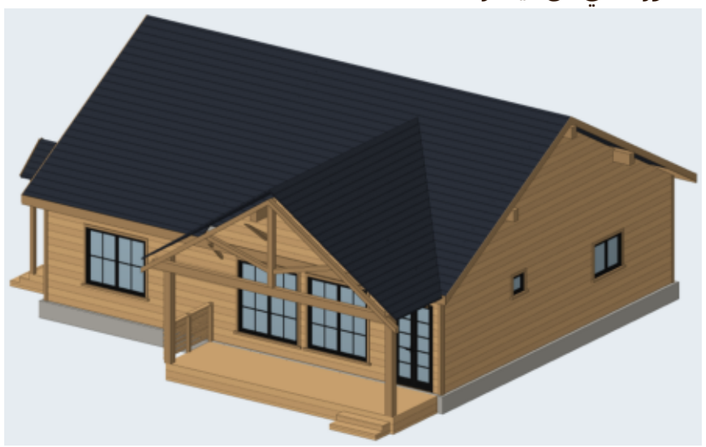

منظور أمامي من اليمين

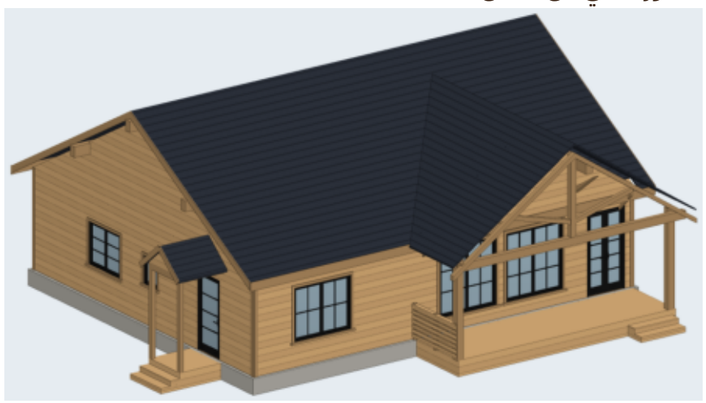


المنظور الخلفي

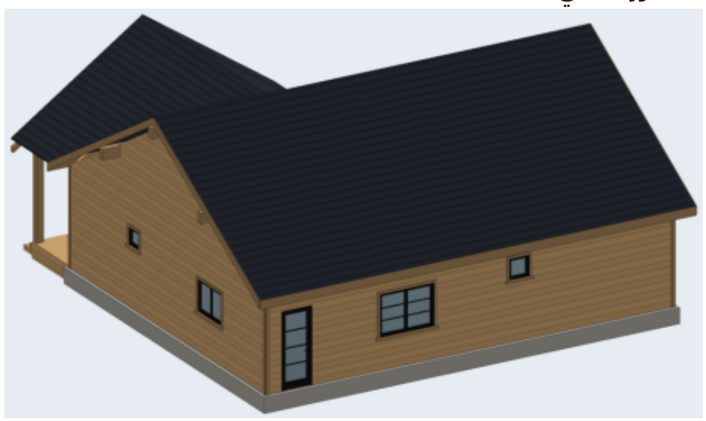

منظور خلفي من اليمين




منظر علوي

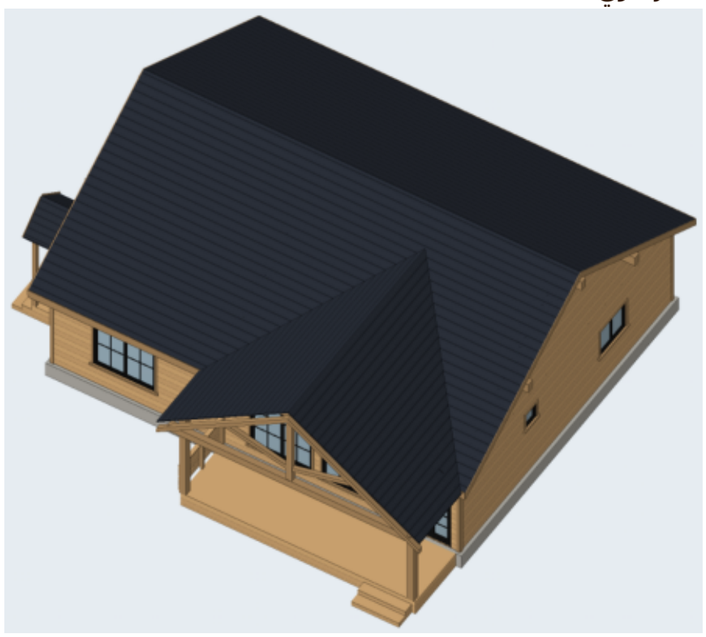

مصنع وتد الأخشاب Watad Wood Factory	المشروع / العميل كوخ دور واحد — مجلس رجال ومجلس نساء + غرفتين — 12.00 × 10.00 م (120 م²) عميل — كوخ 120	عنوان اللوحة لقطات المنظور	المقياس —	التاريخ 2026-10-25	رقم اللوحة A-07 (7/9)

المقطع العلوي بالفرش


مقطع أفقي على ارتفاع 1.90 م — توزيع الفرش ومسار الحركة

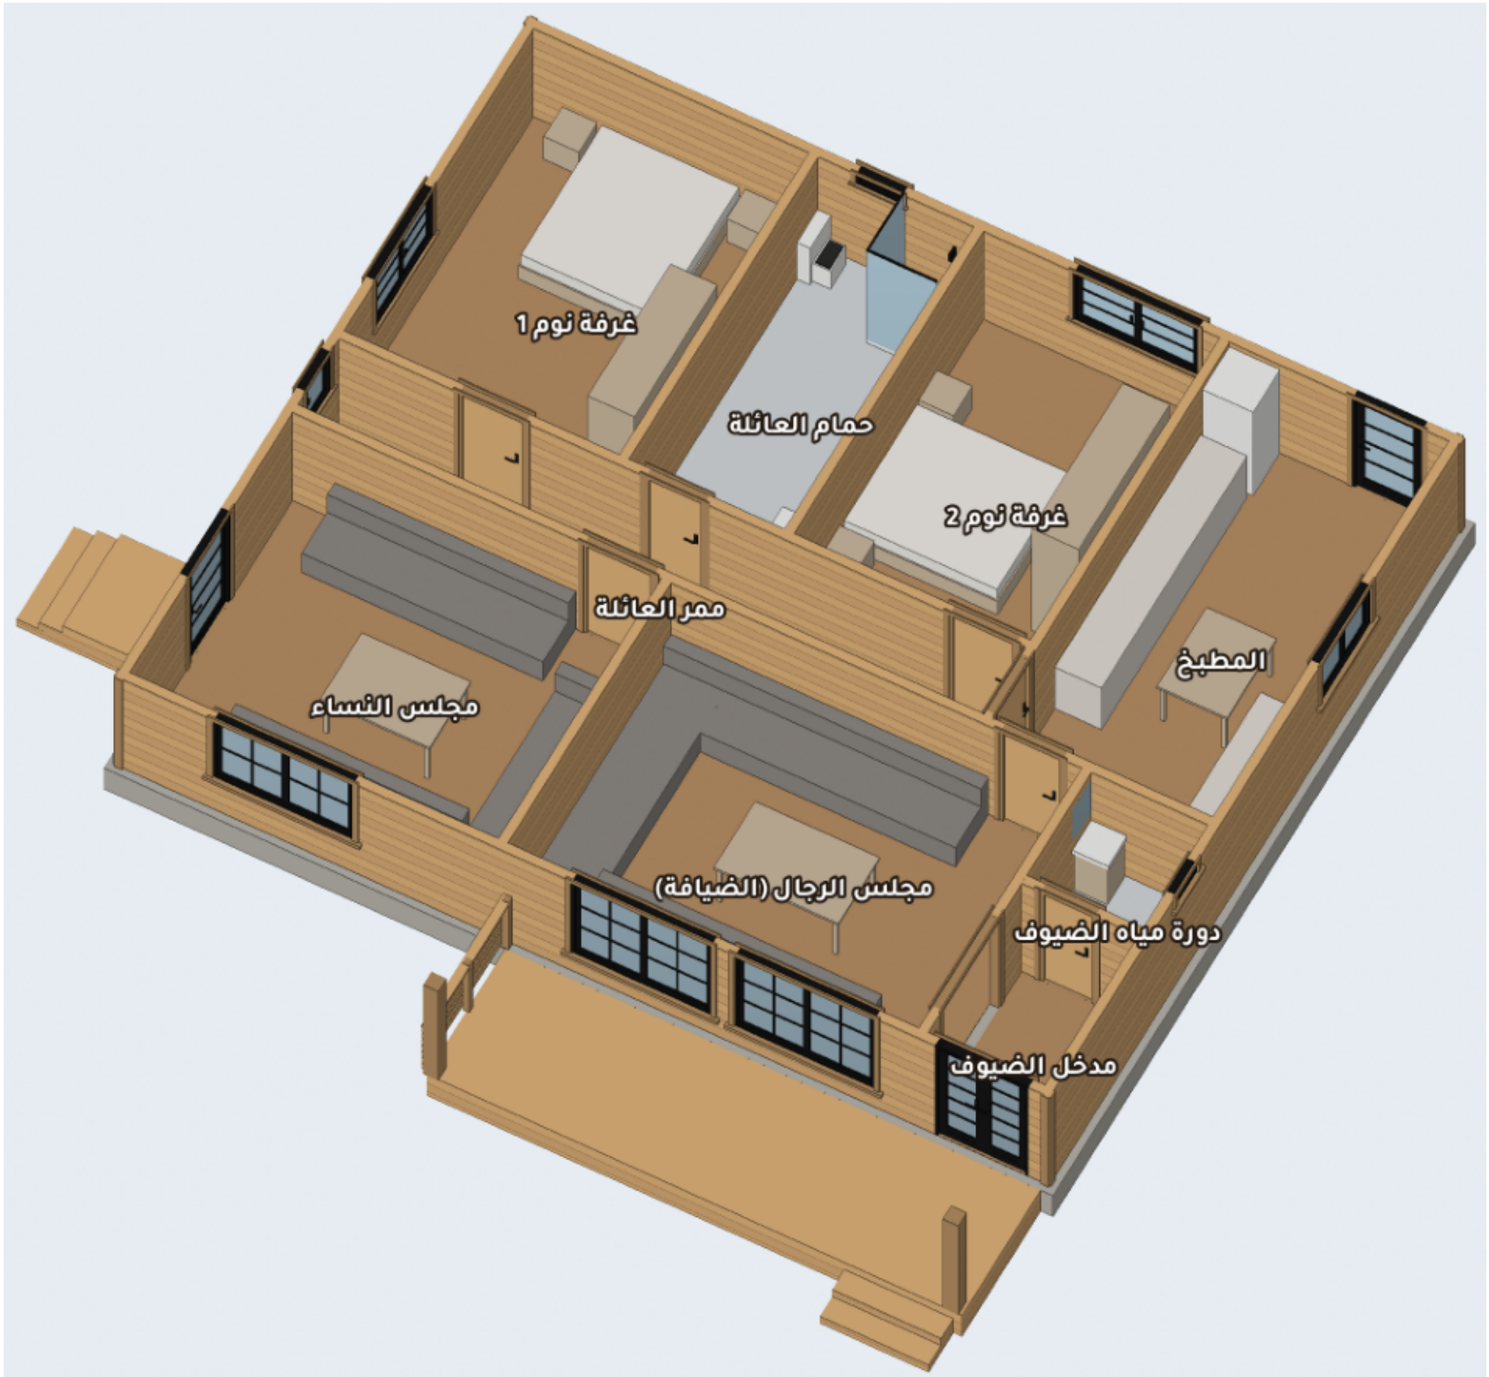

مصنع وتد الأخشاب Watad Wood Factory	المشروع / العميل كوخ دور واحد — مجلس رجال ومجلس نساء + غرفتين — 12.00 × 10.00 م (120 م²) عميل — كوخ 120	عنوان اللوحة المقطع العلوي بالفرش	المقياس —	التاريخ 2026-10-25	رقم اللوحة A-08 (8/9)

المنظور ثلاثي الأبعاد والمواد

النمط: خشب طبيعي + قرميد فحمي — رندر واقعي بخامات حقيقية

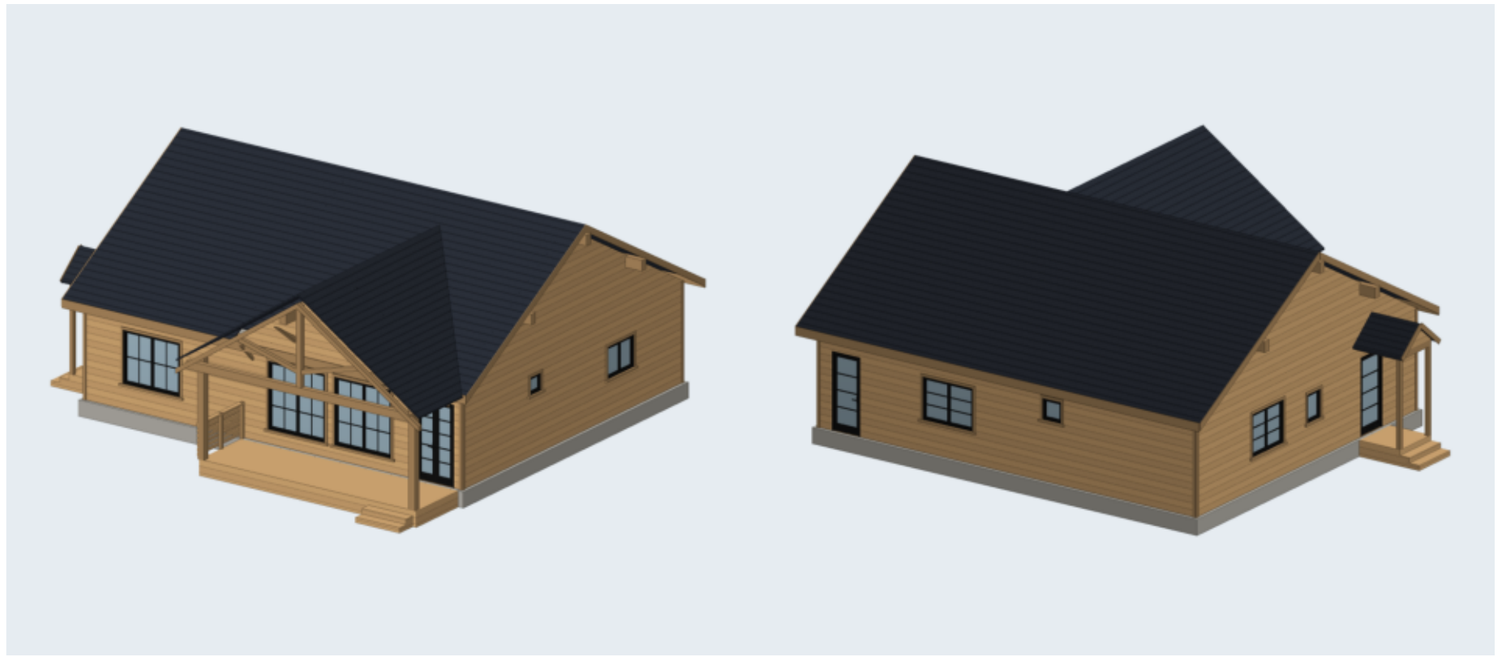

جدول المواد والألوان

الخشب / الصبغة

خشب طبيعي فاتح (بدون صبغة)

القرميد

قرميد فحمي / أسود مزرق

الزجاج

زجاج شفاف

إطارات الشبابيك والأبواب

إطار ألمنيوم أسود

الكنار والزوايا

نفس الصبغة أغمق درجة


الصبة

خرسانة 45 سم


الدربزين: ألواح أفقية متقاربة (عصري)

تقسيم الشبابيك: شبكة | الباب الرئيسي: زجاج بتقسيمات (فرنسي)

أنواع الدربزين المعتمدة (من مشاريع المصنع)

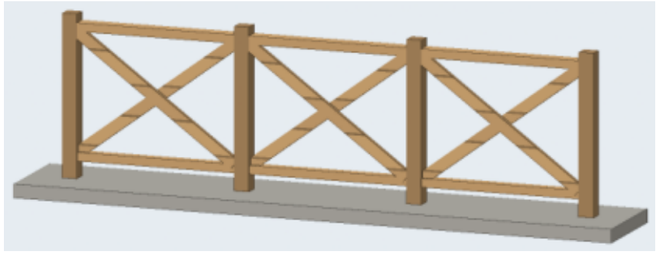

تقاطع X (صورة 5)

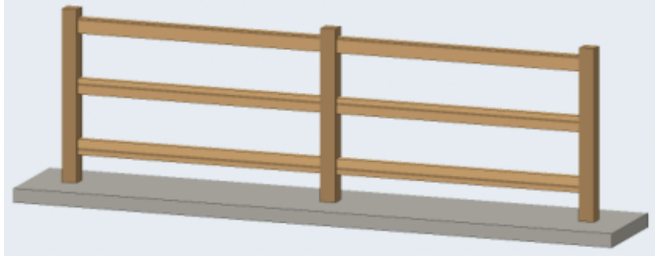

3 مرابيع أفقية (صورة 2)



قوائم رأسية متقاربة (صورة 1)

المشروع / العميل	عنوان اللوحة	المقياس	التاريخ	رقم اللوحة
كوخ دور واحد — مجلس رجال ومجلس نساء + غرفتين — 12.00 × 10.00 م (120 م²) **عميل — كوخ 120**	**المنظور والمواد**	**—**	**2026-10-25**	**A-09 (9/9)**

مصنع وتد الأخشاب
Watad Wood Factory