
المنظور ثلاثي الأبعاد والمواد

النمط: عسلي + قرميد عنابي — رندر واقعي بخامات حقيقية

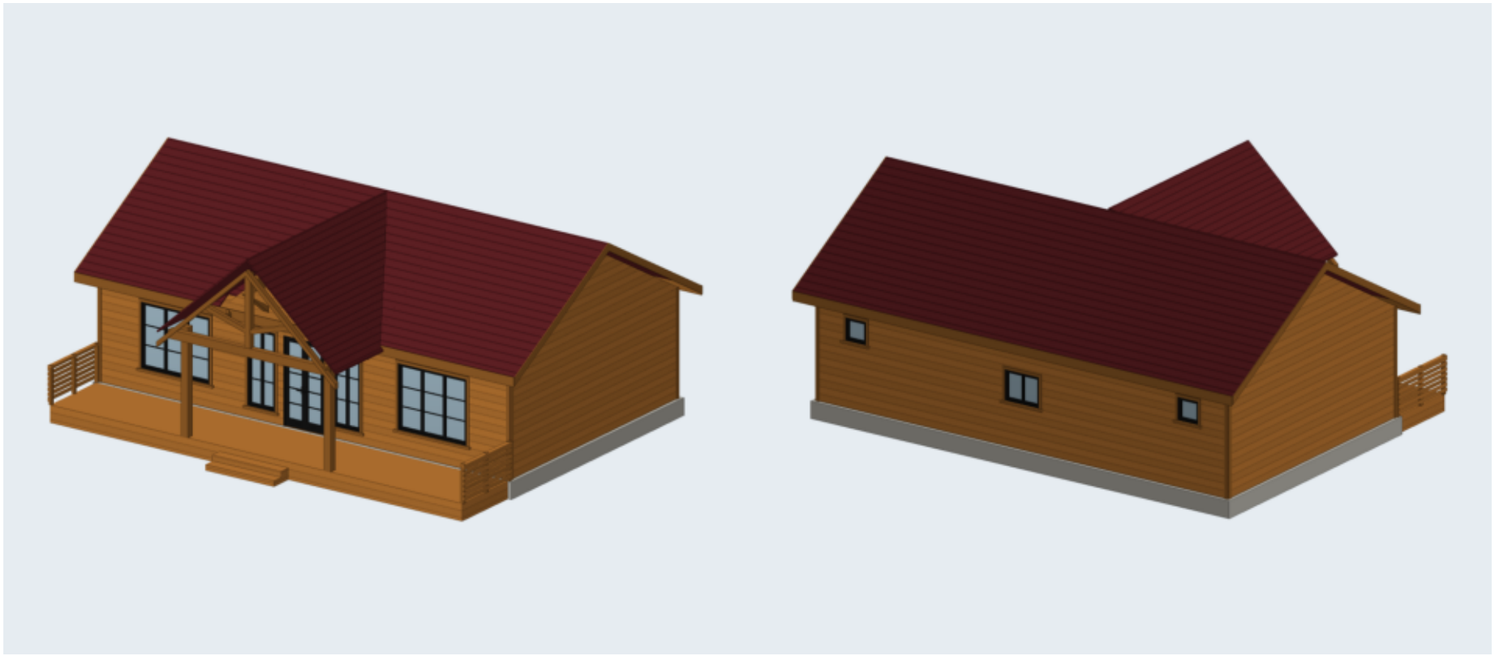

جدول المواد والألوان

الخشب / الصبغة

صبغة عسلي / سيدر

القرميد

قرميد عنابي

الزجاج

زجاج شفاف

إطارات الشبابيك والأبواب

إطار ألمنيوم أسود

الكنار والزوايا

نفس الصبغة أغمق درجة


الصبة

خرسانة 45 سم


الدربزين: ألواح أفقية متقاربة (عصري)

تقسيم الشبابيك: شبكة | الباب الرئيسي: زجاج بتقسيمات (فرنسي)

أنواع الدربزين المعتمدة (من مشاريع المصنع)

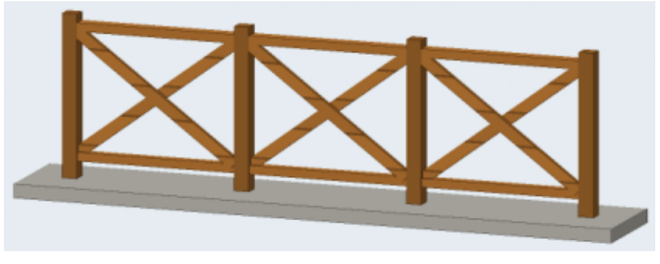

تقاطع X (صورة 5)

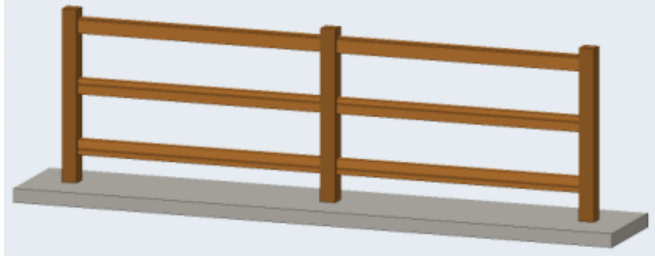

3 مرابيع أفقية (صورة 2)




قوائم رأسية متقاربة (صورة 1)

المشروع / العميل	عنوان اللوحة	المقياس	التاريخ	رقم اللوحة
كوخ غرفتين ماستر + صالة — 12.00 × 7.00 م (84 م²) **عميل — كوخ 120**	**المنظور والمواد**	**1:50**	**2026-10-25**	**W-01 (1/14)**

مصنع وتد الأخشاب
Watad Wood Factory

المسقط الأفقي مع الفرش


الأبعاد بالسنتيمتر - الجدران: قوائم 7×5 + تلبيس 2.5 من الجهتين (12 سم)

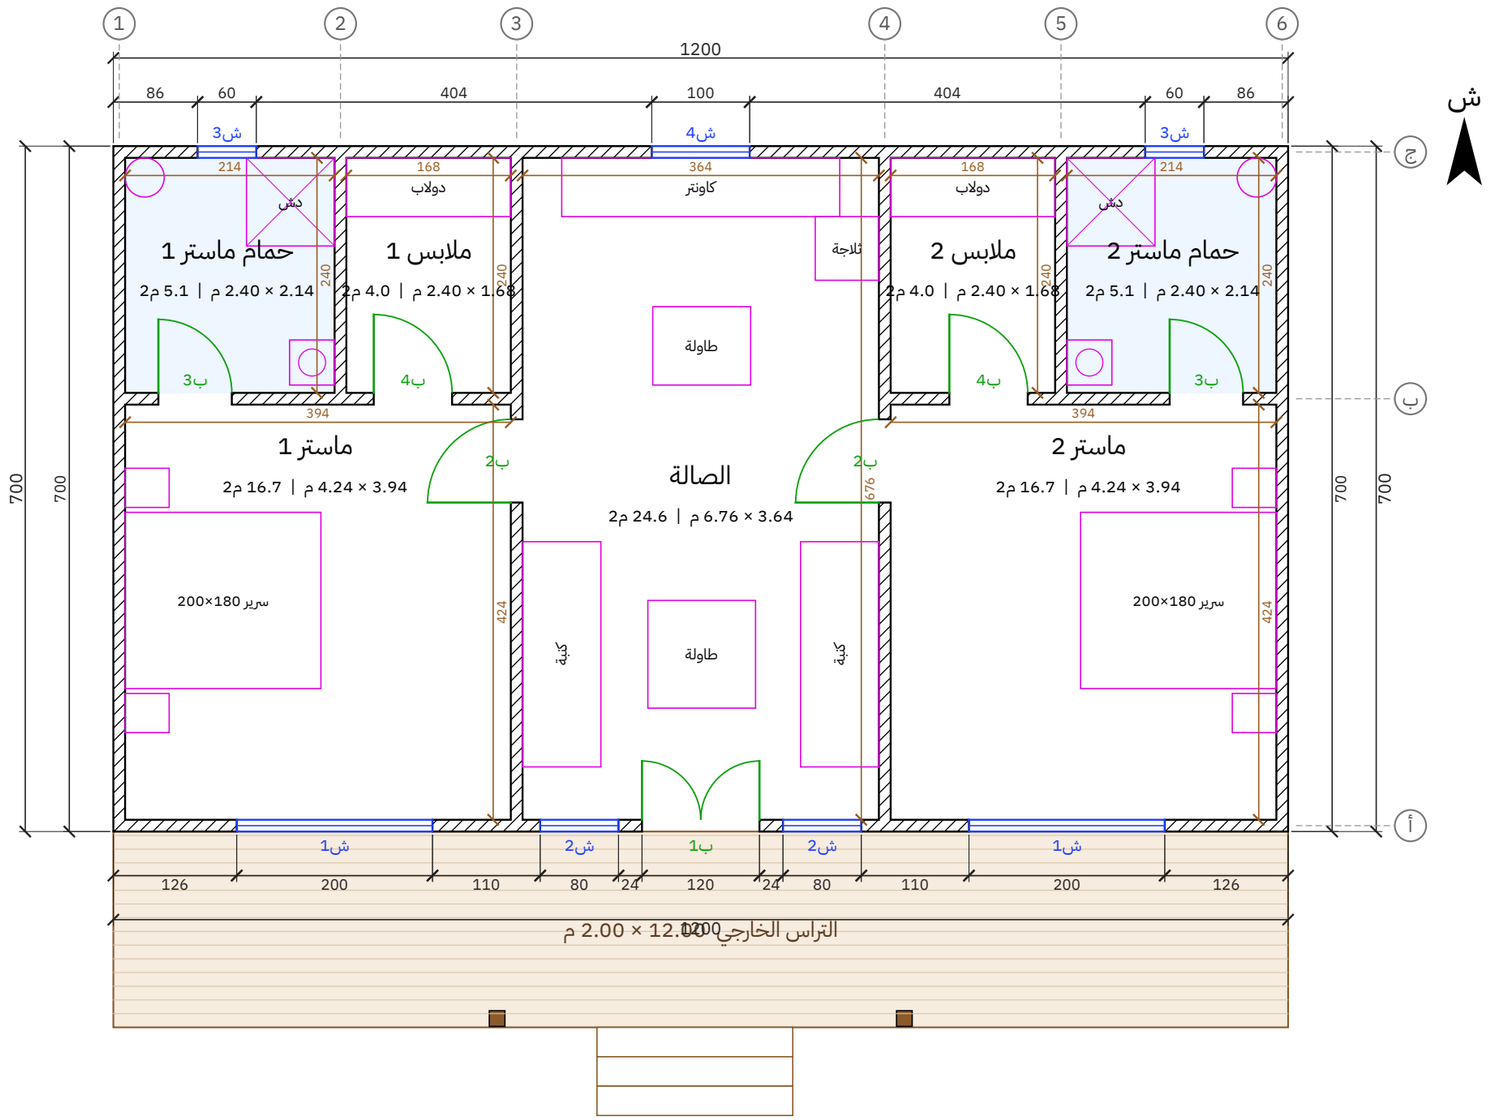

3 درجات × 15 سم


المشروع / العميل	عنوان اللوحة	المقياس	التاريخ	رقم اللوحة
كوخ غرفتين ماستر + صالة — 12.00 × 7.00 م (84 م²) عميل — كوخ 120	المسقط الأفقي	1:50	2026-10-25	W-02 (2/14)

مصنع وتد الأخشاب
Watad Wood Factory

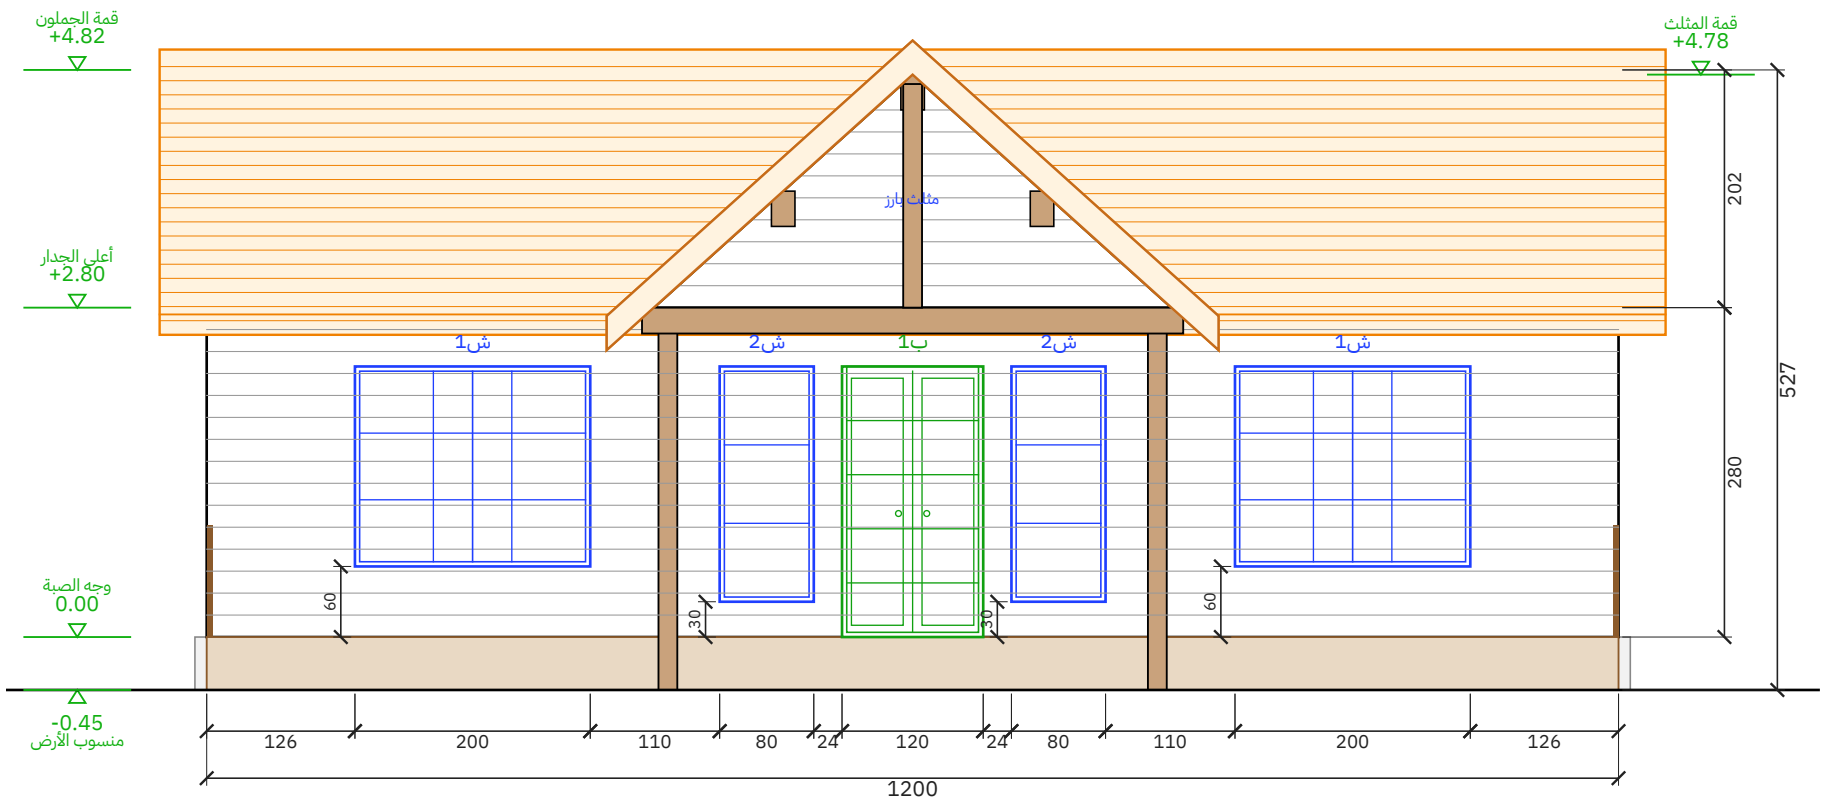

الواجهة الأمامية

مقياس 1:50 | الوحدة: سم

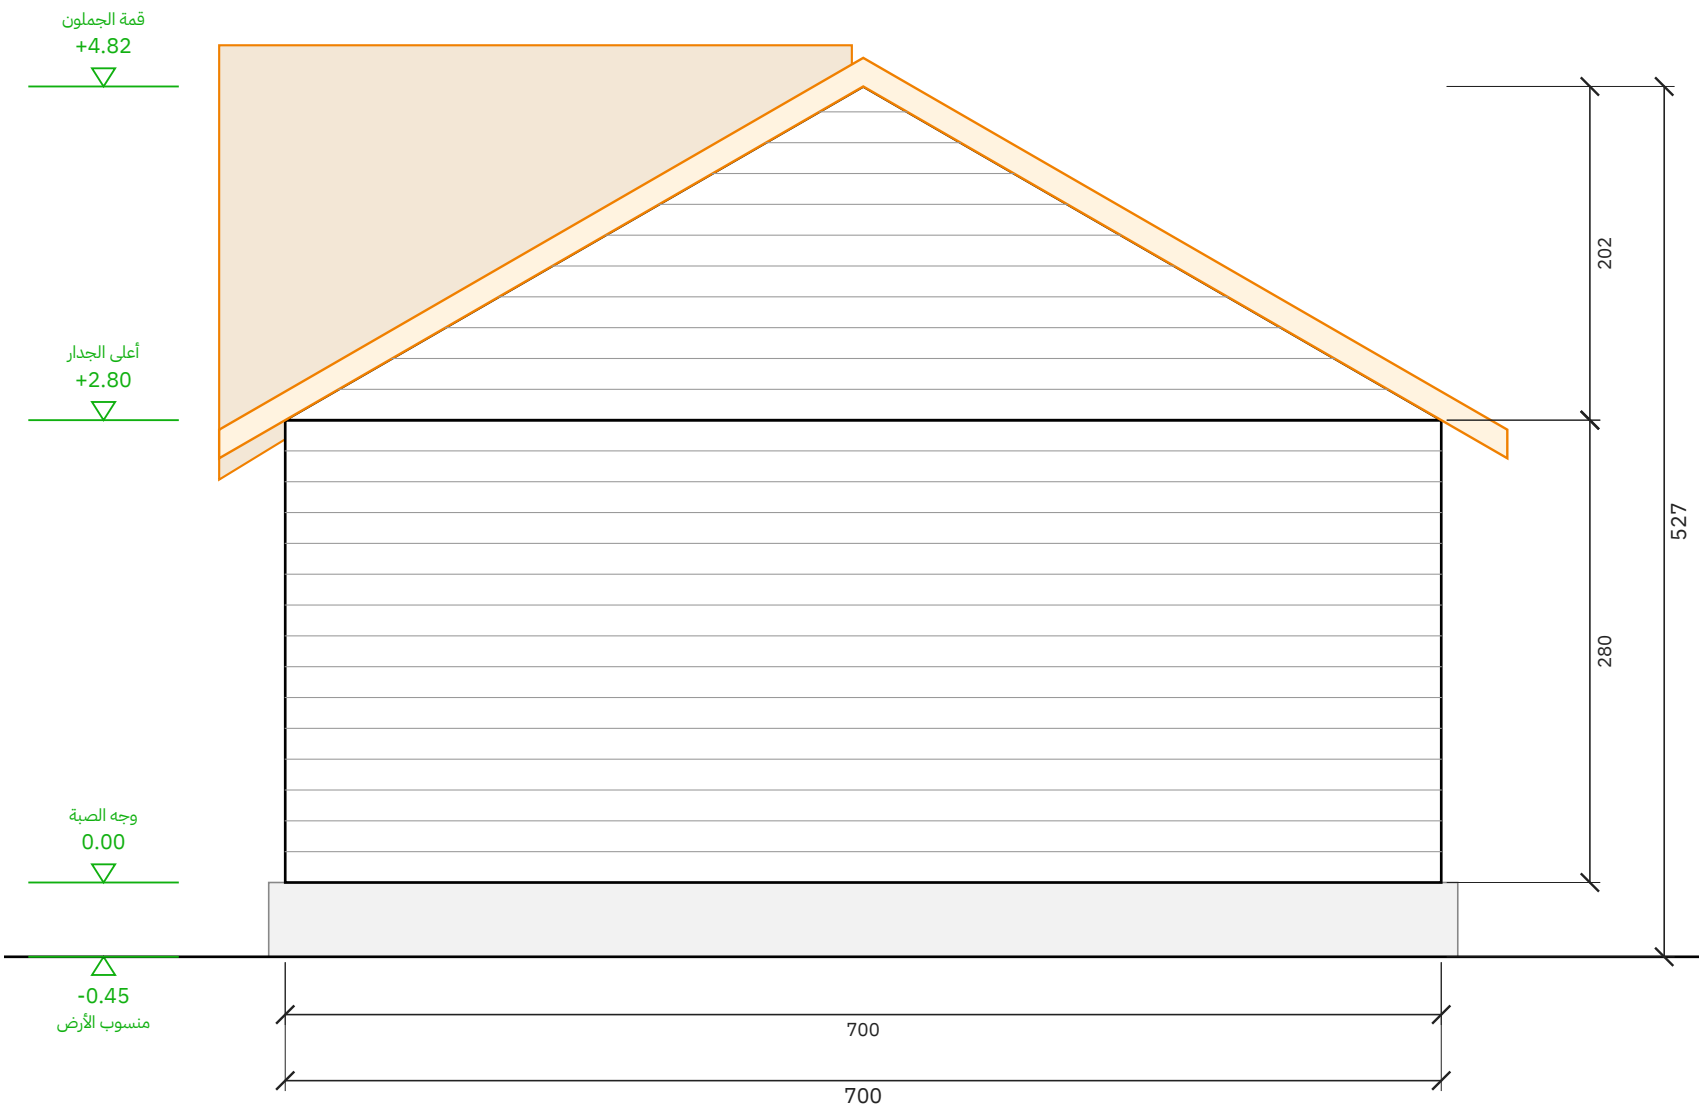


الواجهة الشرقية

مقياس 1:50 | الوحدة: سم


المشروع / العميل	عنوان اللوحة	المقياس	التاريخ	رقم اللوحة
كوخ غرفتين ماستر + صالة — 12.00 × 7.00 م (84 م²) **عميل — كوخ 120**	**الواجهة الأمامية والواجهة الشرقية**	**1:50**	**2026-10-25**	**W-03 (3/14)**

مصنع وتد الأخشاب
Watad Wood Factory

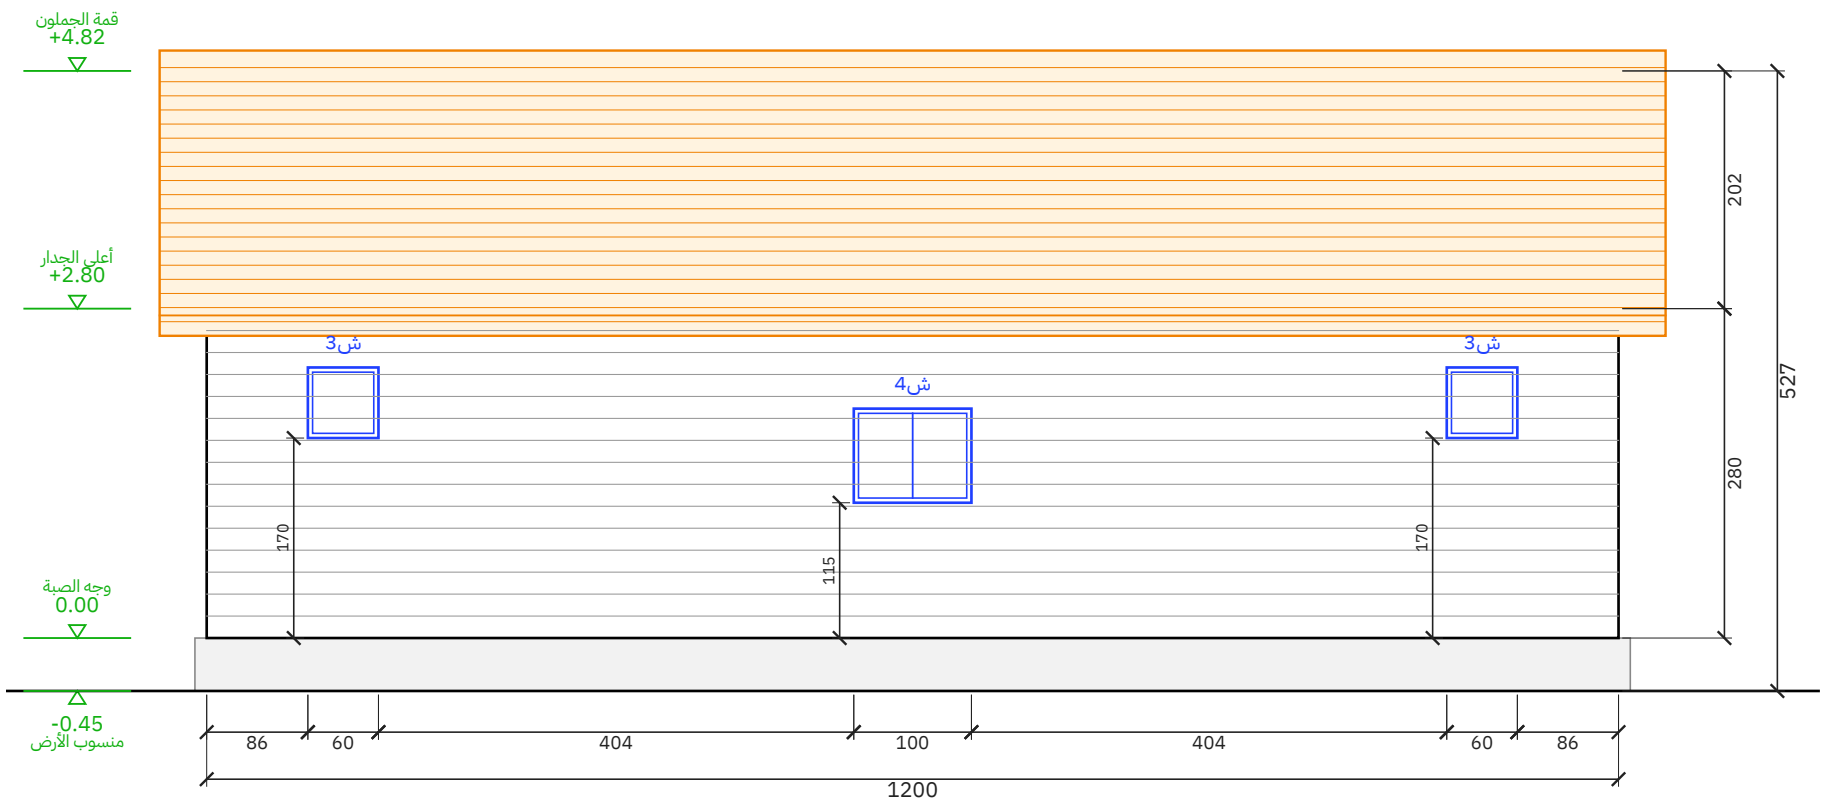

الواجهة الخلفية

مقياس 1:50 | الوحدة: سم

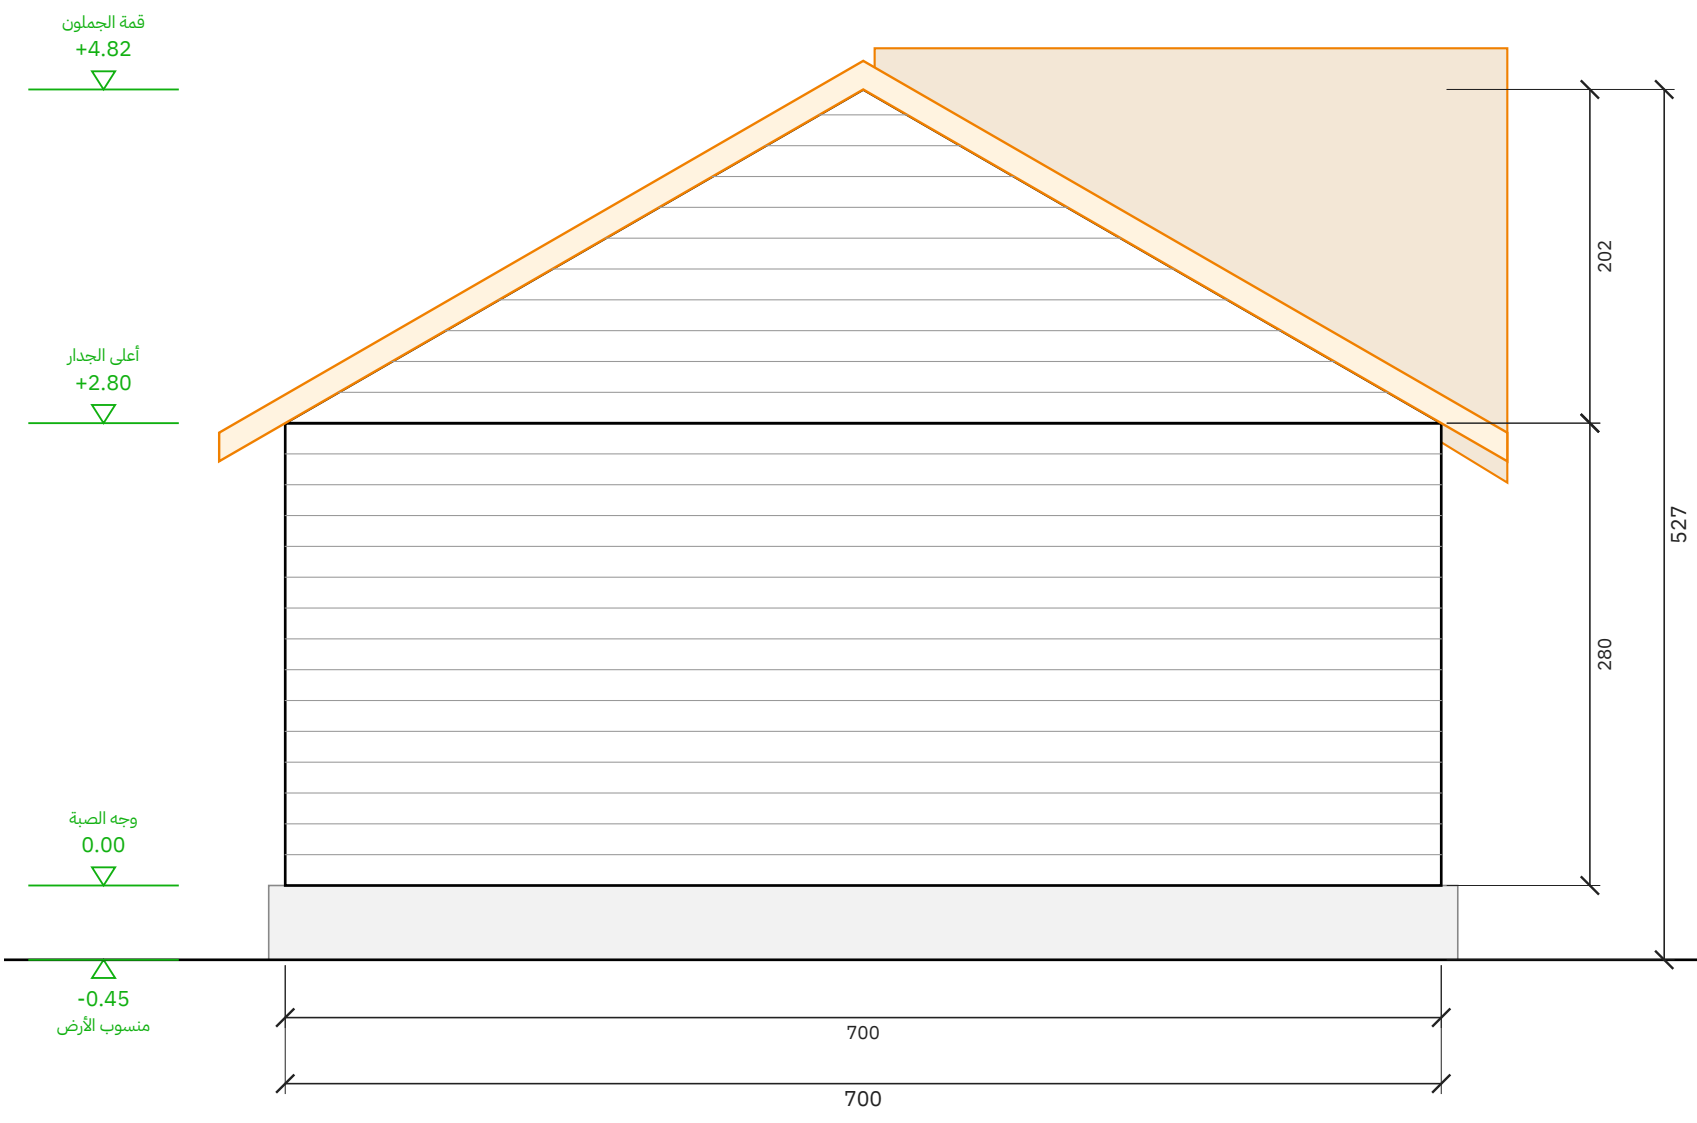

الواجهة الغربية


مقياس 1:50 | الوحدة: سم

المشروع / العميل	عنوان اللوحة	المقياس	التاريخ	رقم اللوحة
كوخ غرفتين ماستر + صالة — 12.00 × 7.00 م (84 م²) **عميل — كوخ 120**	**الواجهة الخلفية والواجهة الغربية**	**1:50**	**2026-10-25**	**W-04 (4/14)**

مصنع وتد الأخشاب
Watad Wood Factory


مسقط السقف (جملون)

رفرف 40 سم من كل جهة | مقياس 1:50

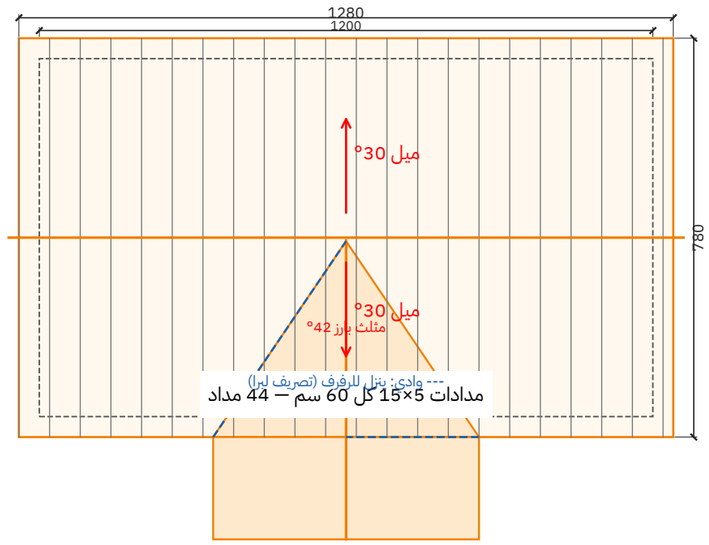


قطاع عرضي أ-أ

مقياس 1:50 | الوحدة: سم

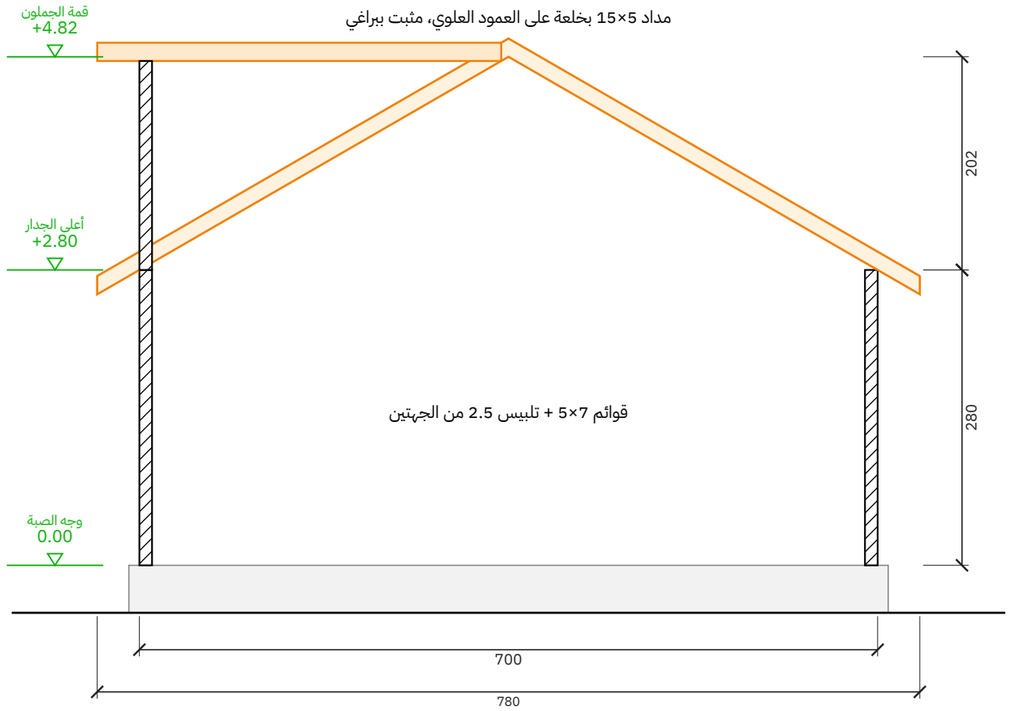

تفصيلة جلوس المداد على العلوي (1:5)

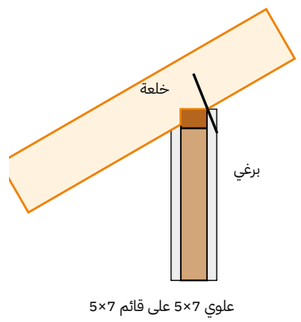

المشروع / العميل **كوخ غرفتين ماستر + صالة — 12.00 × 7.00 م (84 م²)** **عميل — كوخ 120**	عنوان اللوحة **مسقط السقف والقطاع**	المقياس **1:50**	التاريخ **2026-10-25**	رقم اللوحة **W-05 (5/14)**

مصنع وتد الأخشاب
Watad Wood Factory

جدول مقاسات الأبواب والشبابيك

مقاس الفتحة الصافي في الجدار - الوحدة: سم

الرمز	النوع	العرض (سم)	الارتفاع (سم)	ارتفاع الجلسة (سم)	العدد	الموقع
ب1	باب مزدوج	120	230	-	1	الأمامية
ب2	باب	85	210	-	2	ماستر 1 - ماستر 2
ب3	باب	75	210	-	2	حمام ماستر 1 - حمام ماستر 2
ب4	باب	80	210	-	2	ملابس ماستر 1 - ملابس ماستر 2
ش1	شباك	200	170	60	2	الأمامية 2
ش2	شباك	80	200	30	2	الأمامية 2
ش3	شباك	60	60	170	2	الخلفية 2
ش4	شباك	100	80	115	1	الخلفية

الإجمالي: أبواب 7 - شبابيك 7

جدول المساحات وبيانات المشروع


بيانات المشروع

البند	البيان
المشروع	كوخ غرفتين ماستر + صالة — 12.00 × 7.00 م (84 م²)
العميل	عميل — كوخ 120
الموقع	القصيم
الاستخدام	سكن / ضيافة
التاريخ	2026-10-25
نظام البناء	هيكل خشب 5×7 + تلبيس 2.5 سم من الجهتين
السقف	جملون 30° — قرميد معدني + 1 مثلث بارز


جدول المساحات

م	الفراغ	الأبعاد (م)	المساحة (م2)
1	ماستر 1	3.94 × 4.24	16.71
2	حمام ماستر 1	2.14 × 2.40	5.14
3	ملابس 1	1.68 × 2.40	4.03
4	الصالة	3.64 × 6.76	24.61
5	ماستر 2	3.94 × 4.24	16.71
6	ملابس 2	1.68 × 2.40	4.03
7	حمام ماستر 2	2.14 × 2.40	5.14
	المساحة الصافية الداخلية		**76.35**
	التراس المسقوف	**12.00 × 2.00**	**24.00**
	المساحة الإجمالية المبنية	**12.00 × 7.00**	**84.00**
	المساحة الكلية (المبنية + التراس)		**108.00**

تأطير جدار جنوب — الطول 1188 سم، الارتفاع 280 سم

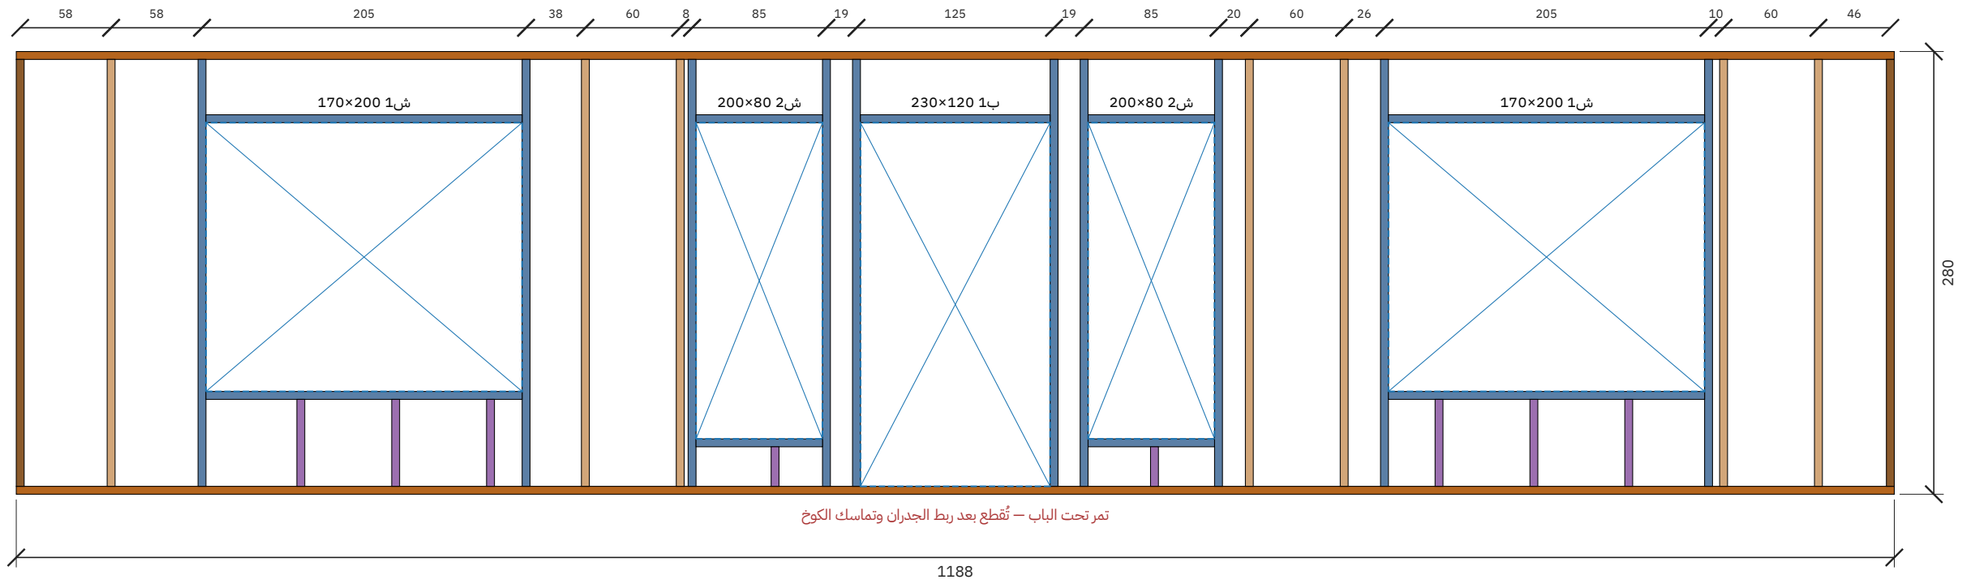

تأطير جدار شرق — الطول 688 سم، الارتفاع 280 سم

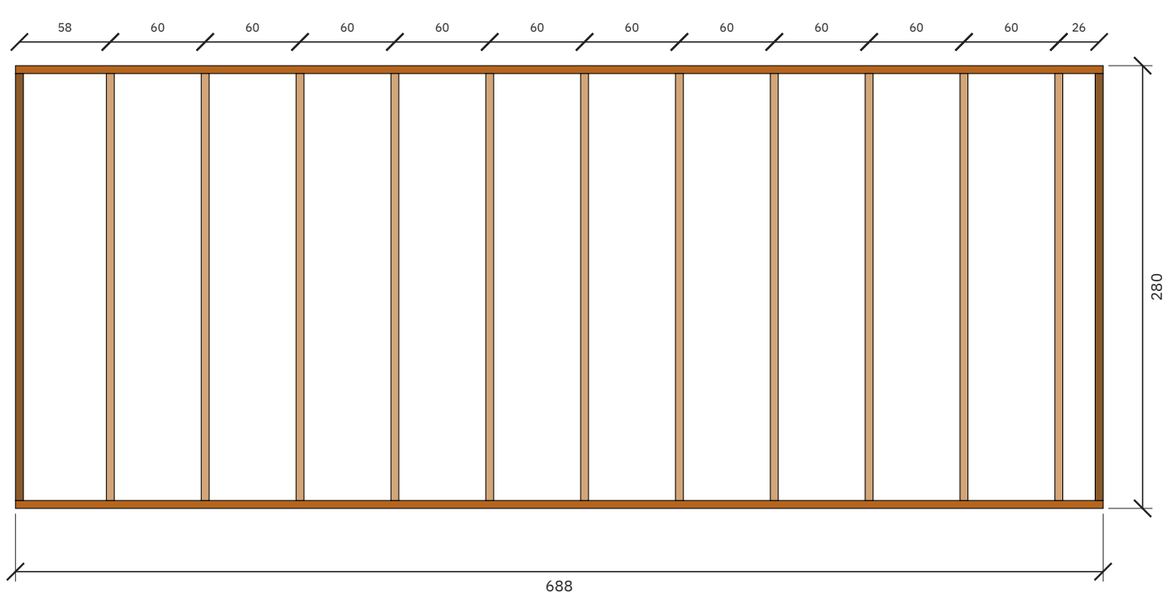


قاعدة سفلية | علوي | عمود | عمود زاوية | جنب فتحة | رأس فتحة | جلسة شباك | عمود قصير


المشروع / العميل	عنوان اللوحة	المقياس	التاريخ	رقم اللوحة
كوخ غرفتين ماستر + صالة — 12.00 × 7.00 م (84 م²) عميل — كوخ 120	لوحات التأطير (للورشة)	—	2026-10-25	W-08 (8/14)

مصنع وتد الأخشاب
Watad Wood Factory

تأطير جدار شمال — الطول 1188 سم، الارتفاع 280 سم

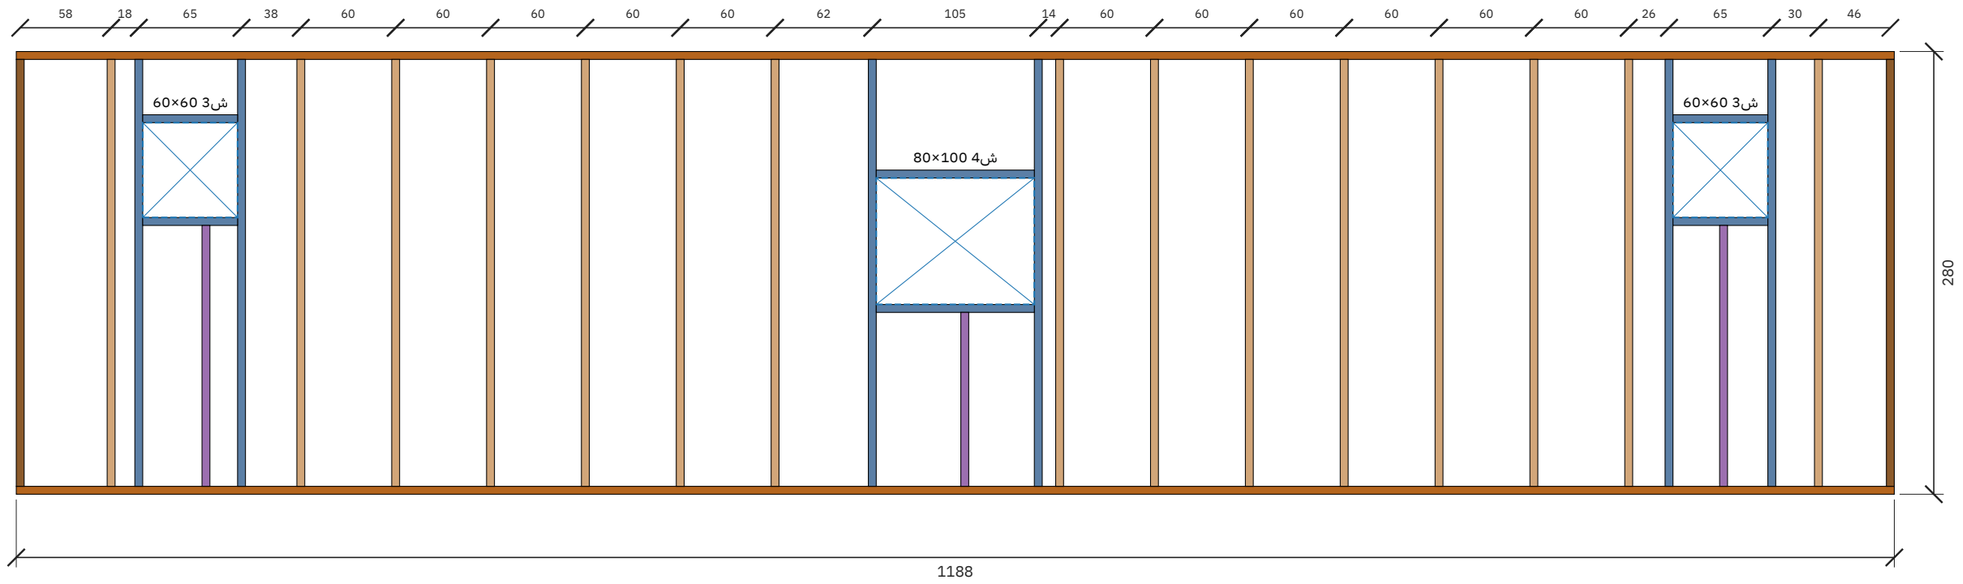


تأطير جدار غرب — الطول 688 سم، الارتفاع 280 سم

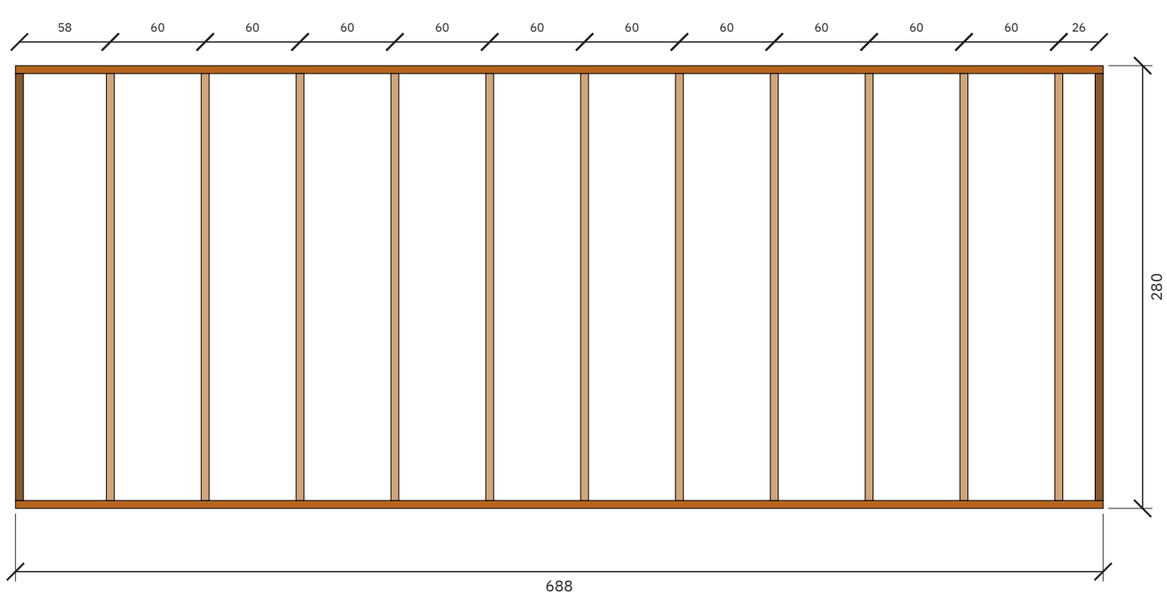


قاعدة سفلية | علوي | عمود | عمود زاوية | جنب فتحة | رأس فتحة | جلسة شباك | عمود قصير

مصنع وتد الأخشاب Watad Wood Factory	المشروع / العميل كوخ غرفتين ماستر + صالة — 12.00 × 7.00 م (84 م²) عميل — كوخ 120	عنوان اللوحة لوحات التأطير (للورشة)	المقياس —	التاريخ 2026-10-25	رقم اللوحة W-09 (9/14)

تأطير جدار جدار ماستر 1 — الطول 688 سم، الارتفاع 280 سم (داخلي)

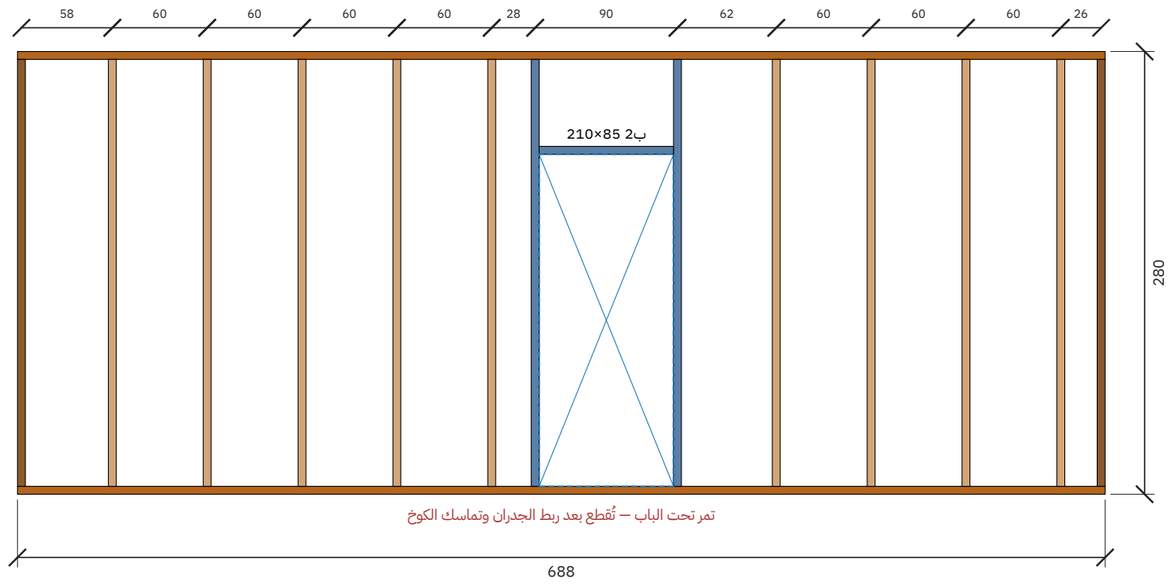


تأطير جدار جدار ماستر 2 — الطول 688 سم، الارتفاع 280 سم (داخلي)

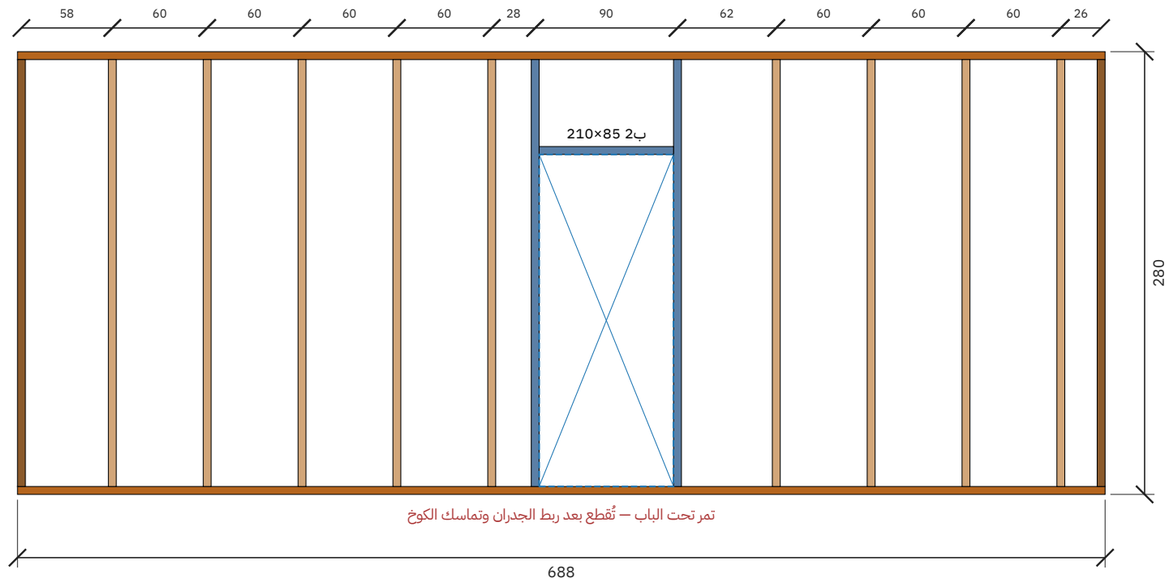


قاعدة سفلية | علوي | عمود | عمود زاوية | جنب فتحة | رأس فتحة | جلسة شباك | عمود قصير

مصنع وتد الأخشاب Watad Wood Factory	المشروع / العميل كوخ غرفتين ماستر + صالة — 12.00 × 7.00 م (84 م²) عميل — كوخ 120	عنوان اللوحة لوحات التأطير (للورشة)	المقياس —	التاريخ 2026-10-25	رقم اللوحة W-10 (10/14)

تأطير جدار خلف ماستر 1 — الطول 406 سم، الارتفاع 280 سم (داخلي)

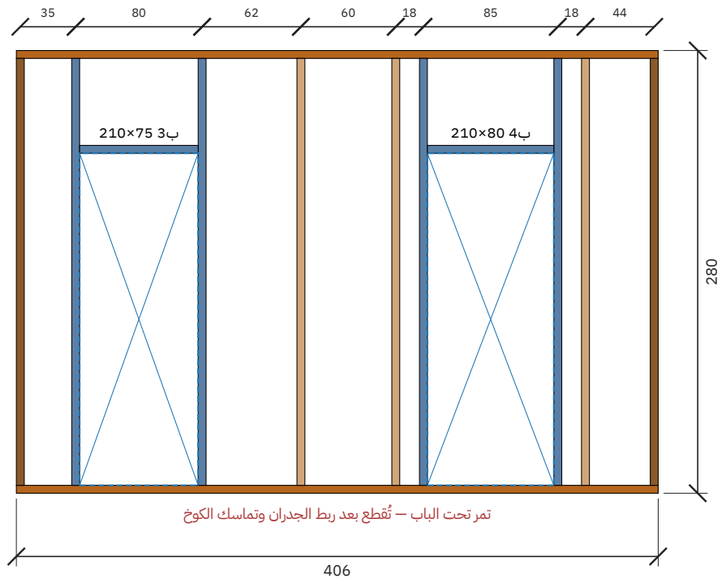


تأطير جدار فاصل حمام 1 — الطول 252 سم، الارتفاع 280 سم (داخلي)

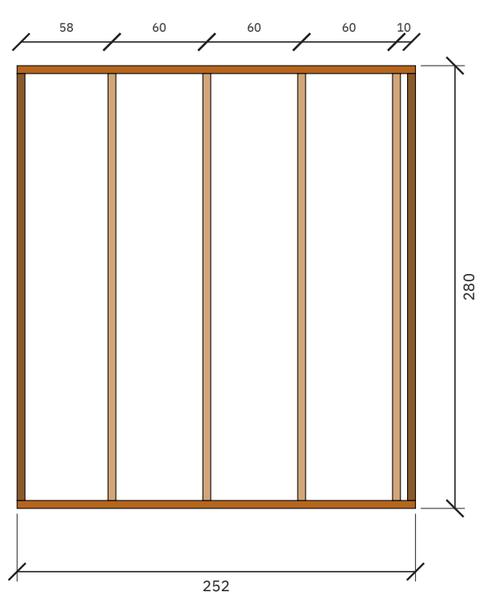


قاعدة سفلية | علوي | عمود | عمود زاوية | جنب فتحة | رأس فتحة | جلسة شباك | عمود قصير

مصنع وتد الأخشاب Watad Wood Factory	المشروع / العميل كوخ غرفتين ماستر + صالة — 12.00 × 7.00 م (84 م²) عميل — كوخ 120	عنوان اللوحة لوحات التأطير (للورشة)	المقياس —	التاريخ 2026-10-25	رقم اللوحة W-11 (11/14)

تأطير جدار خلف ماستر 2 — الطول 406 سم، الارتفاع 280 سم (داخلي)

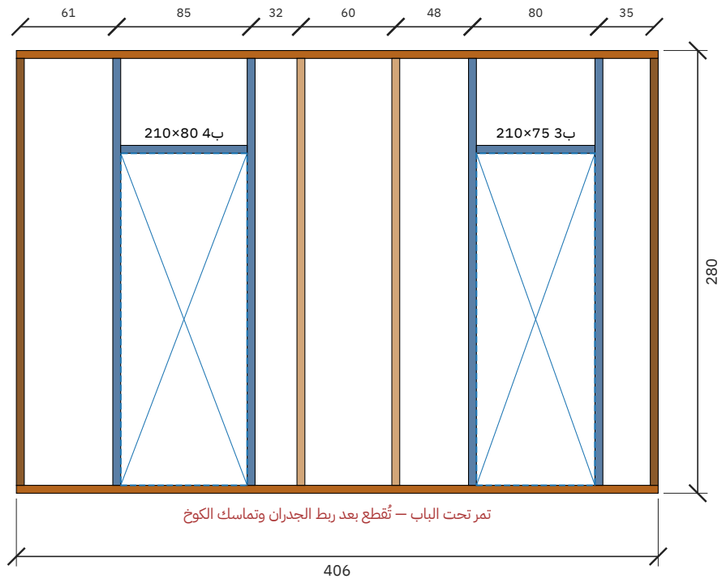

تأطير جدار فاصل حمام 2 — الطول 252 سم، الارتفاع 280 سم (داخلي)

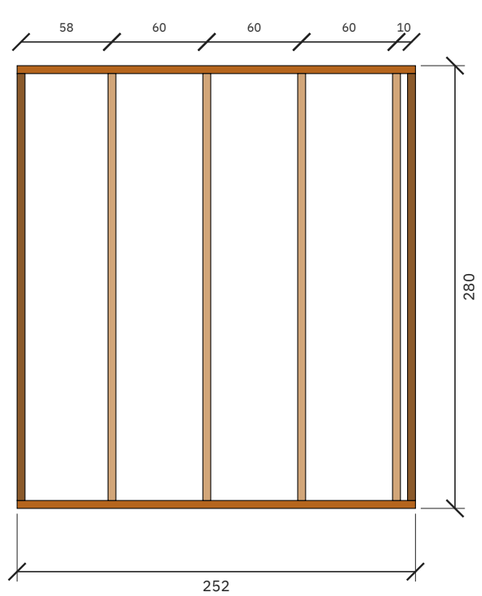

قاعدة سفلية | علوي | عمود | عمود زاوية | جنب فتحة | رأس فتحة | جلسة شباك | عمود قصير

مصنع وتد الأخشاب Watad Wood Factory	المشروع / العميل كوخ غرفتين ماستر + صالة — 12.00 × 7.00 م (84 م²) عميل — كوخ 120	عنوان اللوحة لوحات التأطير (للورشة)	المقياس —	التاريخ 2026-10-25	رقم اللوحة W-12 (12/14)

جدول الكميات وخطة تقطيع الطبليات

البند	القيمة
الارتفاع المطلوب / المعتمد	280 / 280 سم
السقف	جملون 30° — أعلى نقطة 482 سم من وجه الصبة
المدادات 5×15	44 مداد (22 لكل جهة) × حتى 450 سم — من طبلية 480
طبليات الطريقة الأولى (مداد + عمود)	44 طبلية × 480 سم
طبليات الطريقة الثانية (3 أعمدة)	39 طبلية × 320 سم
مدادات المثلث البارز (S) 42°	14 مداد حتى 242 سم (طبلية 320) + 2 مداد وادي 519 سم
إجمالي الطبليات 5×22.5	99
إجمالي قطع 5×7	175
قائمة تقطيع 5×7	1188سم×4 | 688سم×8 | 406سم×4 | 270سم×123 | 252سم×4 | 200سم×4 | 165سم×2 | 120سم×1 | 110سم×1
	100سم×2 | 85سم×2 | 80سم×6 | 75سم×2 | 60سم×4 | 55سم×6 | 25سم×2
ألواح تلبيس 2.5 سم	398 لوح × 400 سم (مجموع الصفوف 1399.2 م، 20 وجه)
أسمنت بورد 12 مم (122×244)	32 لوح (داخل دورات المياه)
العزل	217 لوح فوم صخري 80
الصبة	يجهزها العميل — 20 سم، مفرغة تحت دورات المياه

مراجعة التصميم مقابل قواعد المصنع

النوع	البند	التفاصيل	المقترح
ملاحظة	بحر المدادات	أطول بحر بدون جدار داخلي يحمل المداد: جهة أ: 350 سم، جهة ب: 350 سم. يحتاج رقم المصنع لأقصى بحر مسموح لتحديد المدادات اللي تُقوّى 20×5.	
ملاحظة	الصبة والدرج	ارتفاع الصبة 45 سم ← 3 درجة بقائمة 15.0 سم.	
ملاحظة	مناسيب رؤوس الفتحات	رؤوس الأبواب والشبابيك على مناسيب مختلفة: 195، 210، 230 سم.	
سؤال	يحتاج تأكيد	أقصى بحر للمداد بدون جدار داخلي قبل إضافة تقوية 5×7 (مداد 20×5)؟	
سؤال	يحتاج تأكيد	التغطية الصافية للوح التلبيس بعد التعشيق (مستنتجة مؤقتاً 18.67 سم من 280/15)؟	
سؤال	يحتاج تأكيد	هل يوضع أعمدة قصيرة فوق رأس الشباك/الباب إلى العلوي؟	
سؤال	يحتاج تأكيد	مكان الوصلة في القاعدة والعلوي إذا الجدار أطول من الطبلية؟	