
المسقط الأفقي مع الفرش


الأبعاد بالسنتيمتر - الجدران: قوائم 7×5 + تلبيس 2.5 من الجهتين (12 سم)

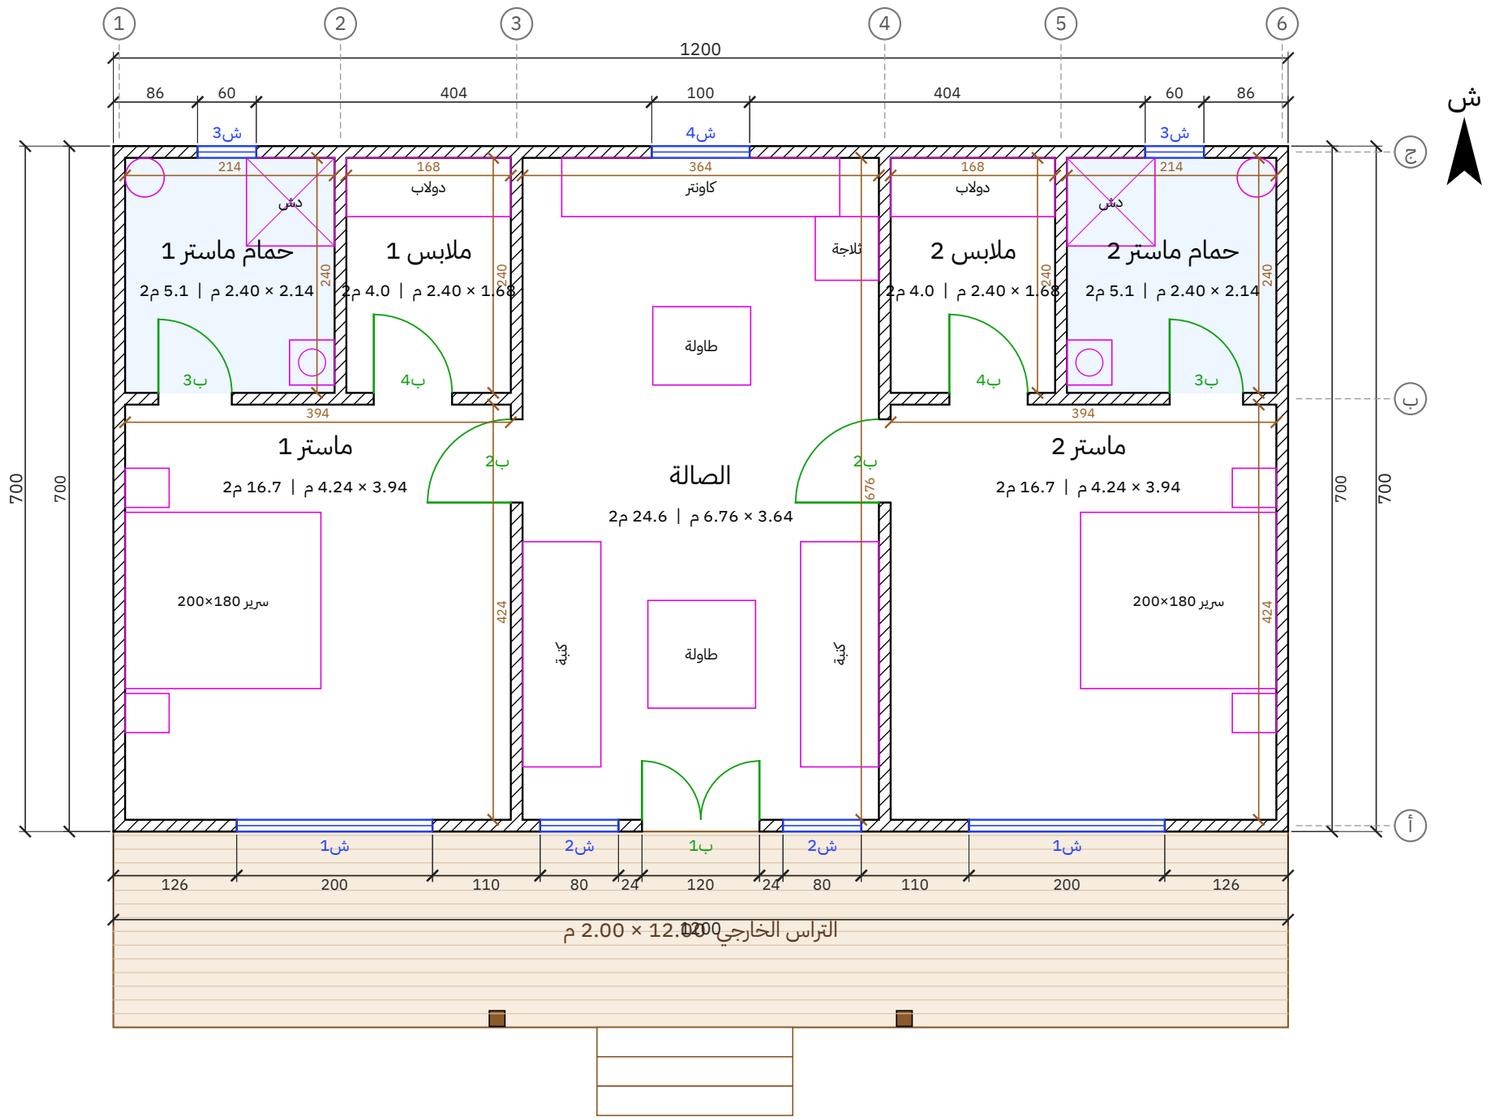

3 درجات × 15 سم


المشروع / العميل	عنوان اللوحة	المقياس	التاريخ	رقم اللوحة
كوخ غرفتين ماستر + صالة — 12.00 × 7.00 م (84 م²) عميل — كوخ 120	المسقط الأفقي	1:50	2026-10-25	A-01 (1/9)

مصنع وتد الأخشاب
Watad Wood Factory

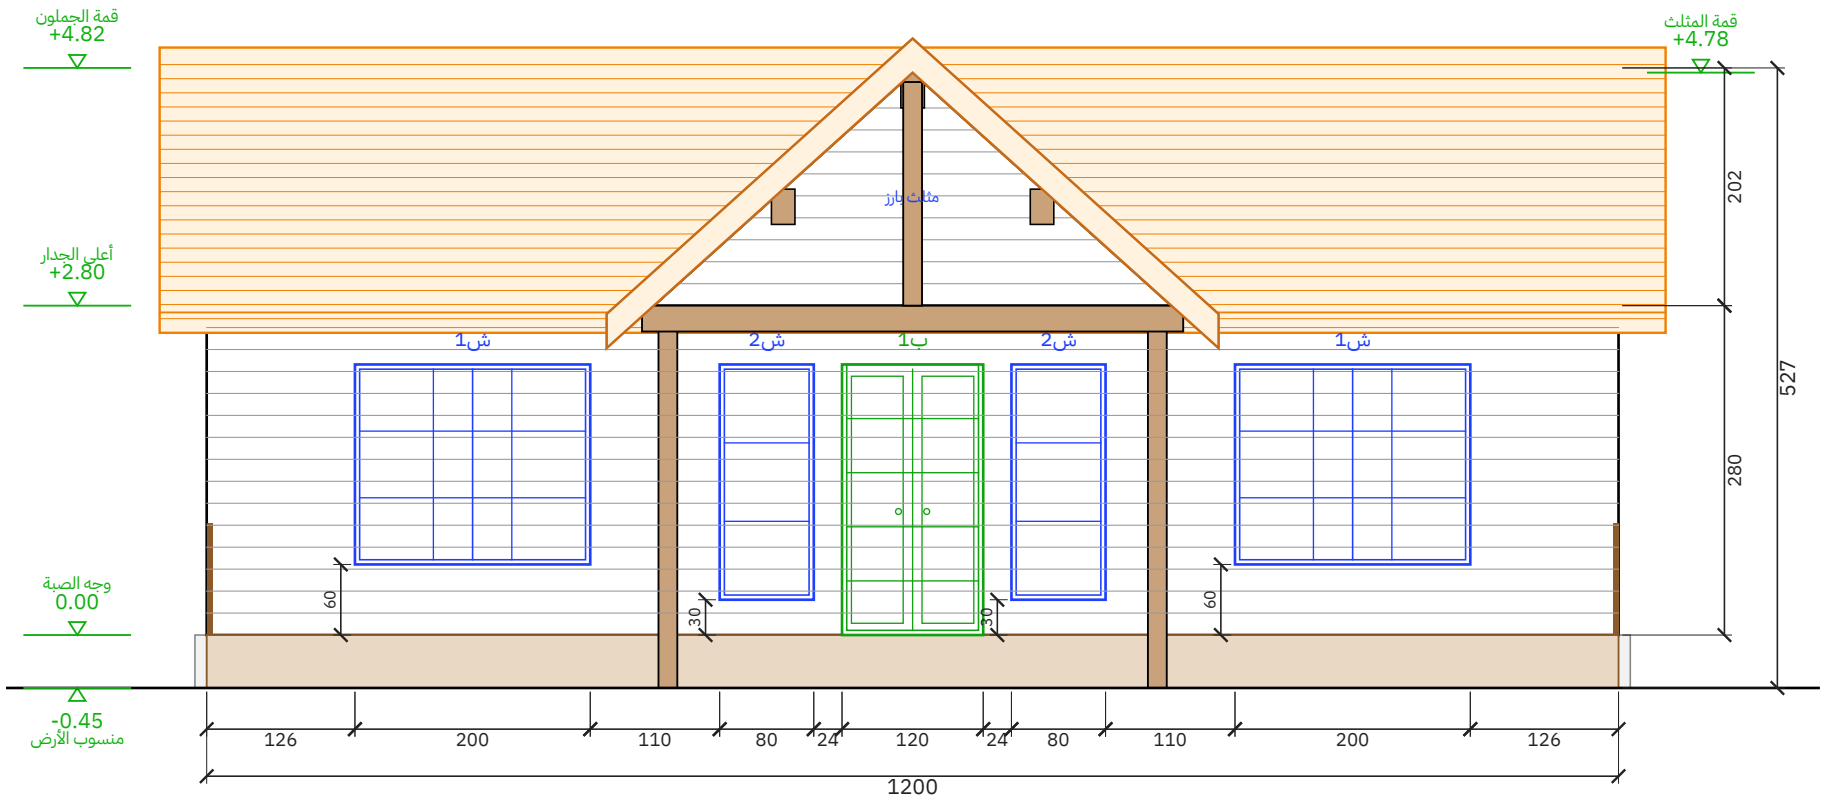

الواجهة الأمامية

مقياس 1:50 | الوحدة: سم

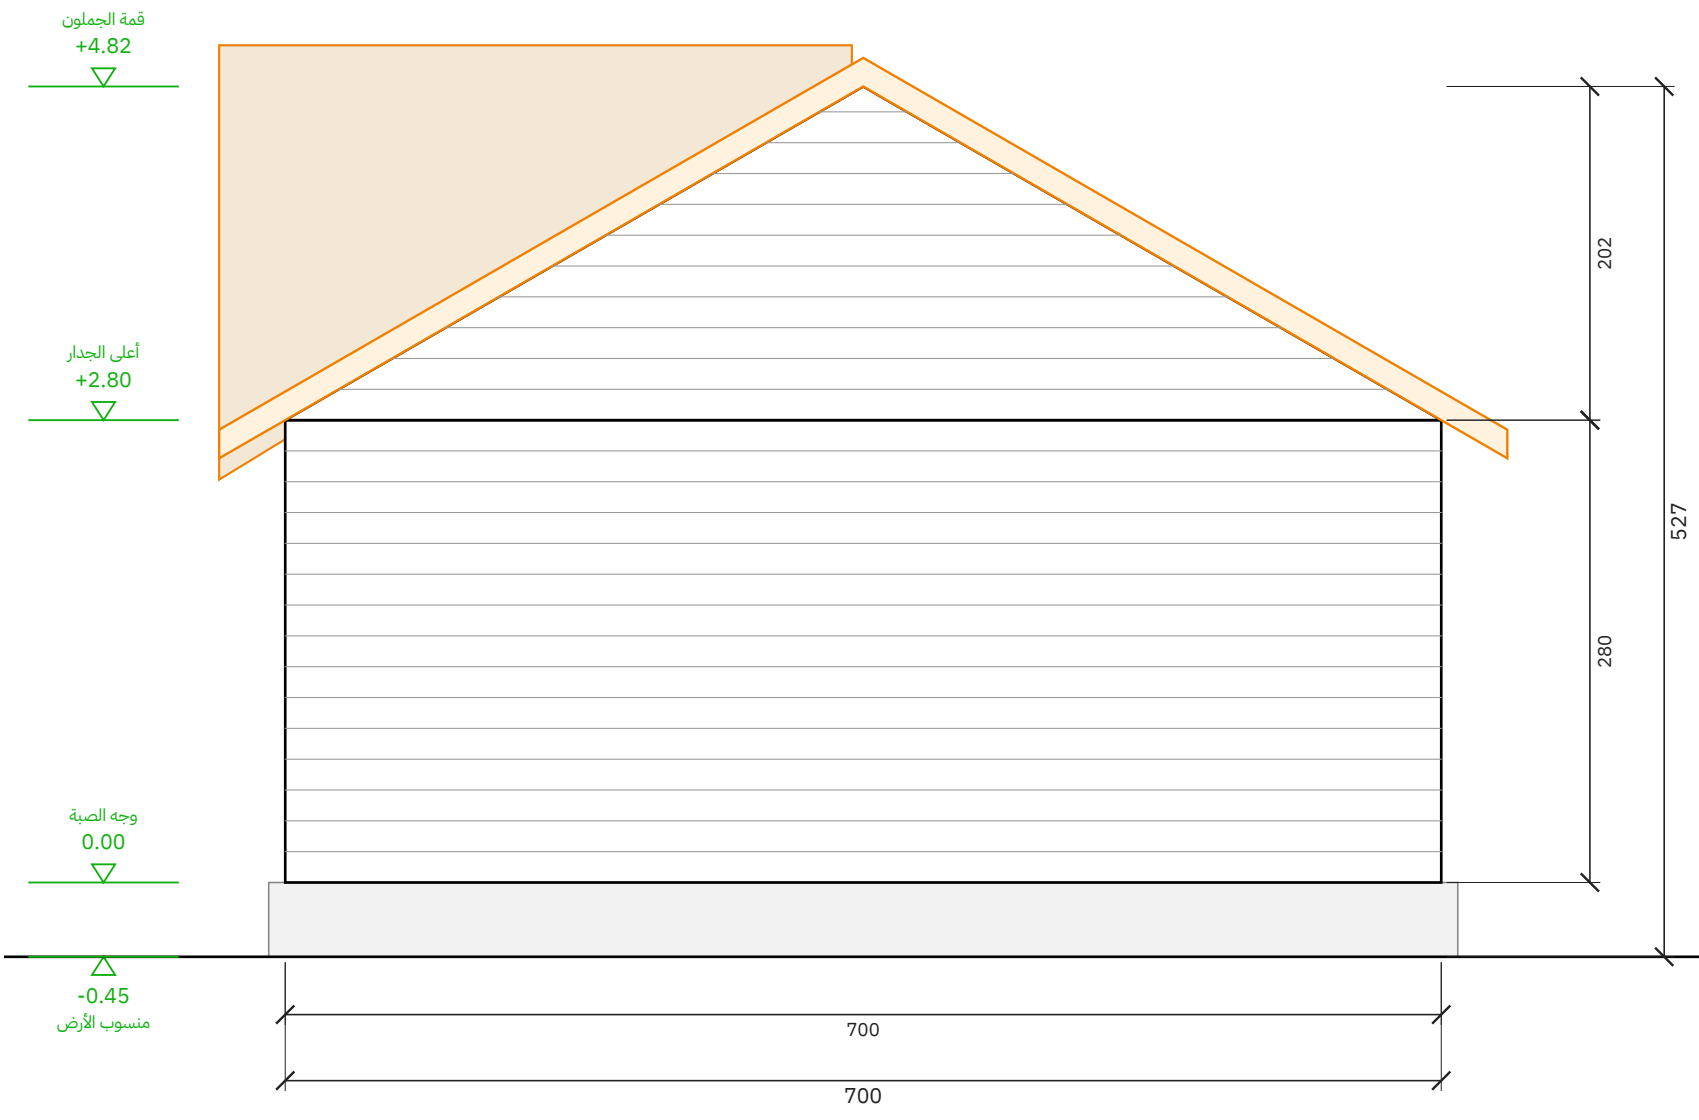


الواجهة الشرقية

مقياس 1:50 | الوحدة: سم


المشروع / العميل	عنوان اللوحة	المقياس	التاريخ	رقم اللوحة
كوخ غرفتين ماستر + صالة — 12.00 × 7.00 م (84 م²) **عميل — كوخ 120**	**الواجهة الأمامية والواجهة الشرقية**	**1:50**	**2026-10-25**	**A-02 (2/9)**

مصنع وتد الأخشاب
Watad Wood Factory

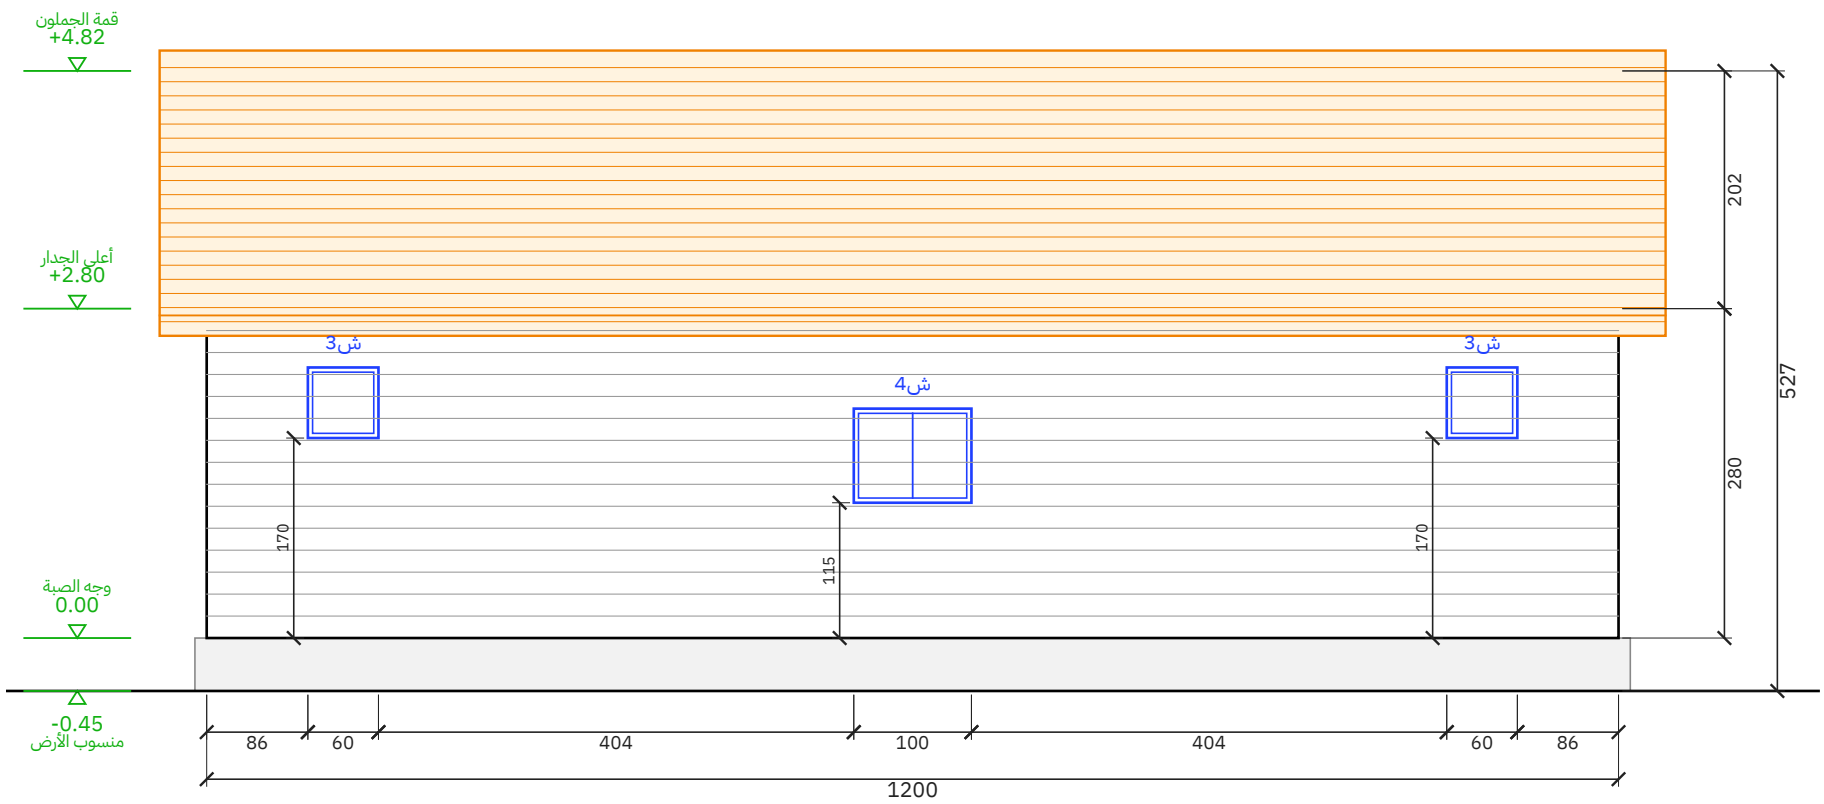

الواجهة الخلفية

مقياس 1:50 | الوحدة: سم

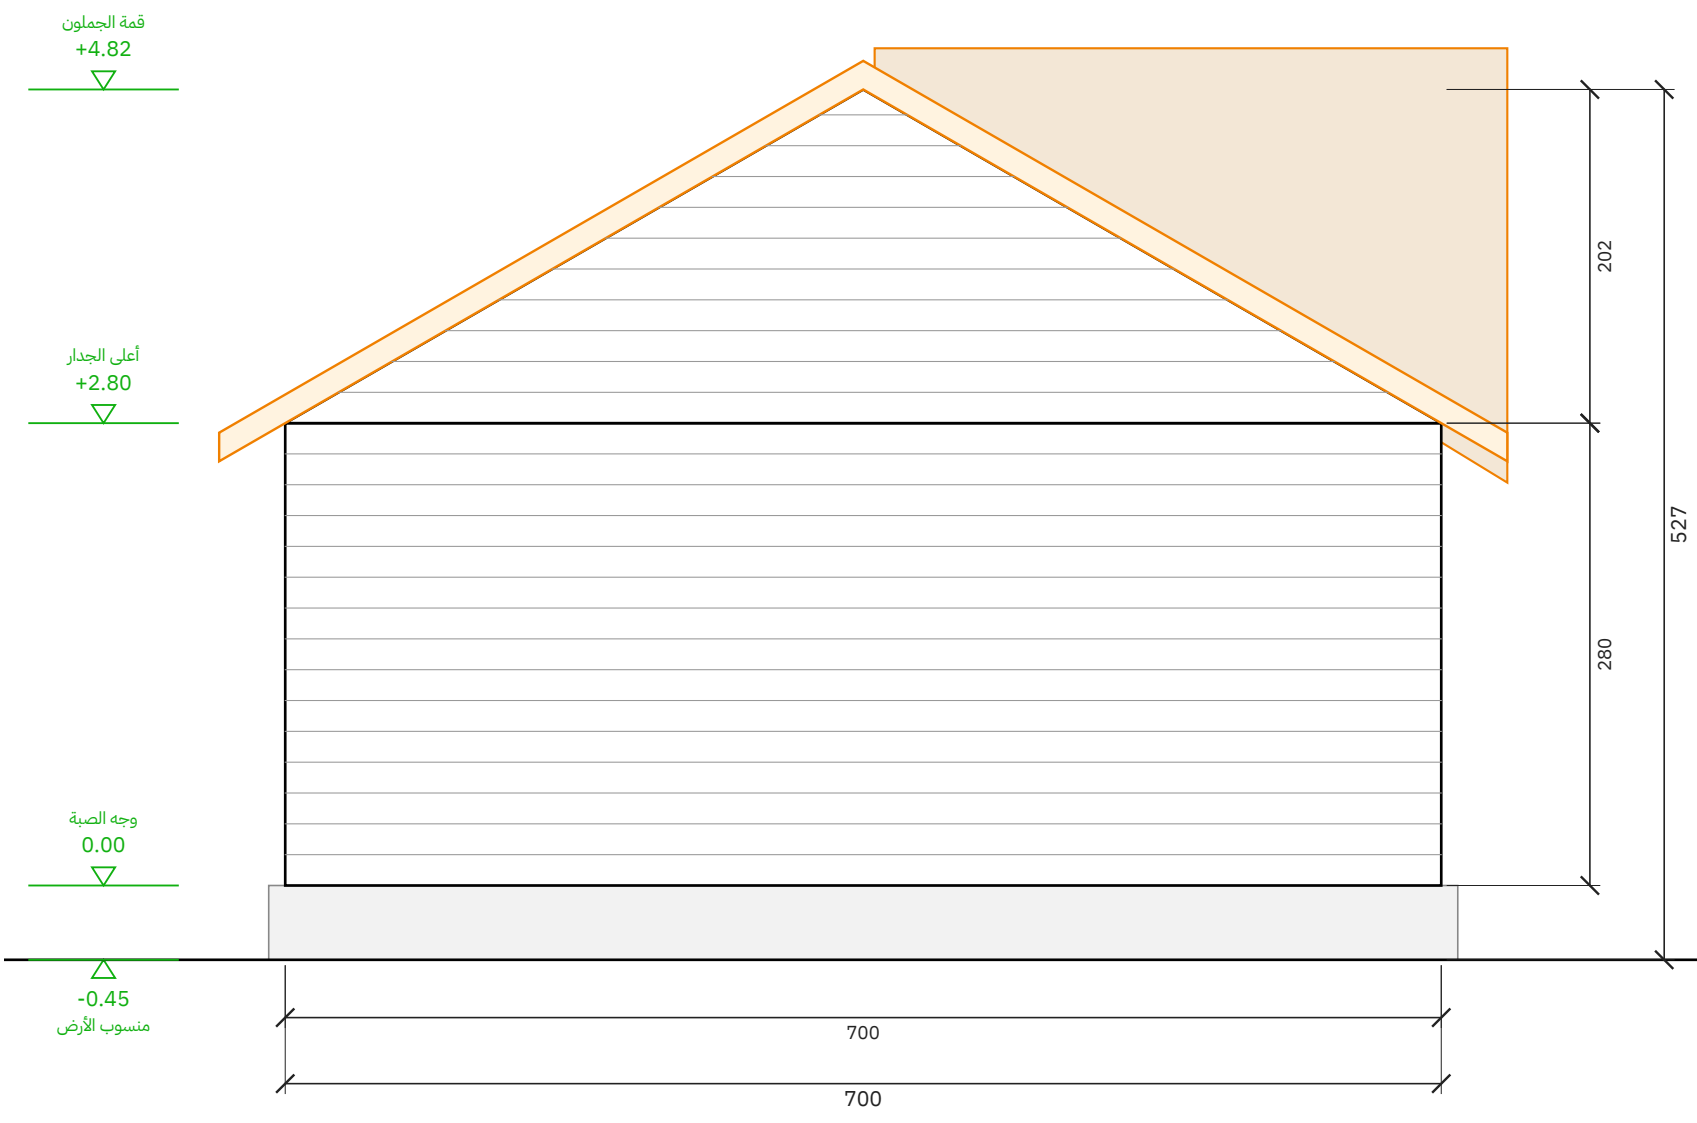

الواجهة الغربية


مقياس 1:50 | الوحدة: سم

المشروع / العميل	عنوان اللوحة	المقياس	التاريخ	رقم اللوحة
كوخ غرفتين ماستر + صالة — 12.00 × 7.00 م (84 م²) **عميل — كوخ 120**	**الواجهة الخلفية والواجهة الغربية**	**1:50**	**2026-10-25**	**A-03 (3/9)**

مصنع وتد الأخشاب
Watad Wood Factory


مسقط السقف (جملون)

رفرف 40 سم من كل جهة | مقياس 1:50

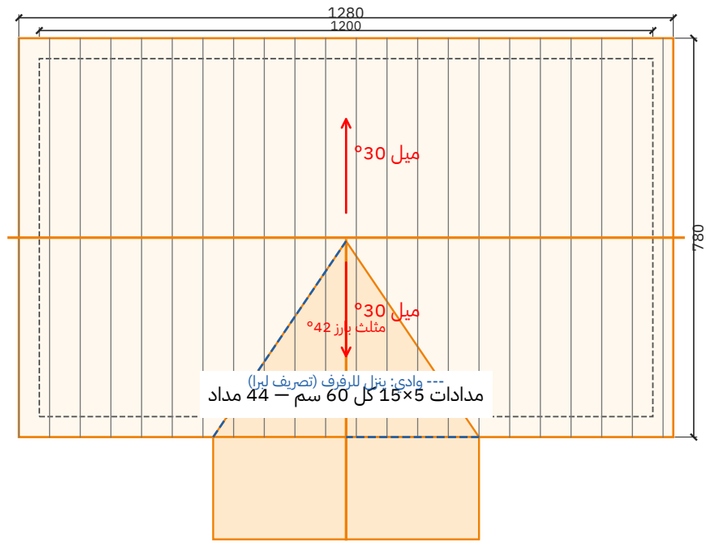


قطاع عرضي أ-أ

مقياس 1:50 | الوحدة: سم

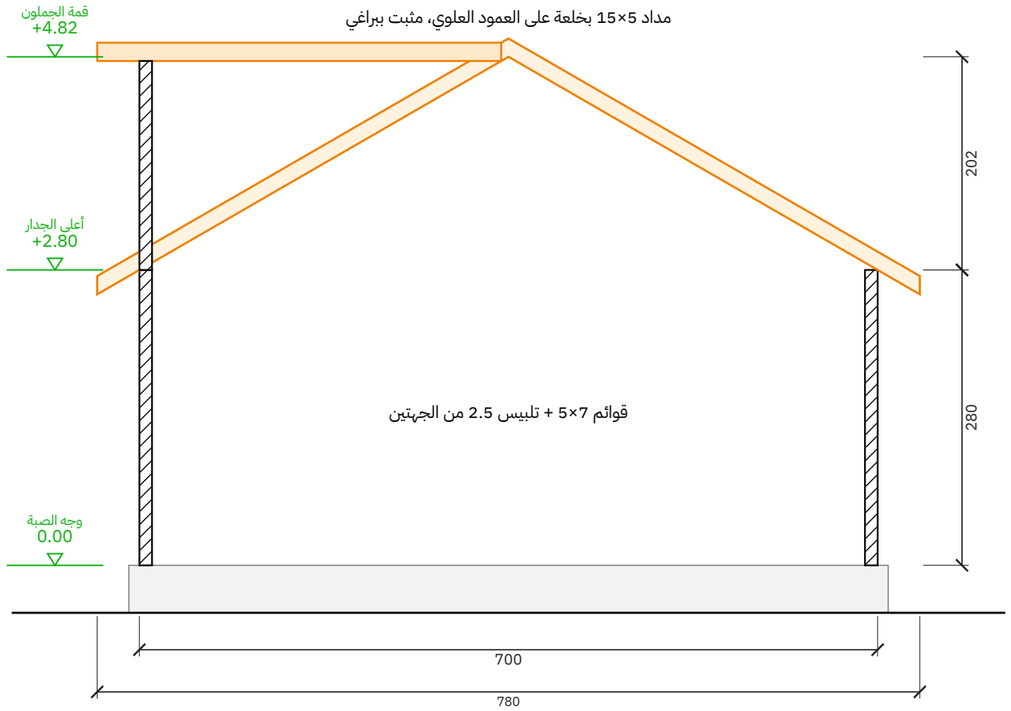

تفصيلة جلوس المداد على العلوي (1:5)

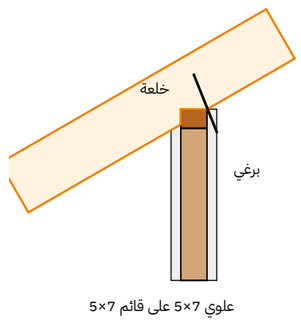

المشروع / العميل	عنوان اللوحة	المقياس	التاريخ	رقم اللوحة
مصنع وتد الأخشاب Watad Wood Factory **كوخ غرفتين ماستر + صالة — 12.00 × 7.00 م (84 م²)** **عميل — كوخ 120**	**مسقط السقف والقطاع**	**1:50**	**2026-10-25**	**A-04 (4/9)**

جدول مقاسات الأبواب والشبابيك

مقاس الفتحة الصافي في الجدار - الوحدة: سم

الرمز	النوع	العرض (سم)	الارتفاع (سم)	ارتفاع الجلسة (سم)	العدد	الموقع
ب1	باب مزدوج	120	230	-	1	الأمامية
ب2	باب	85	210	-	2	ماستر 1 - ماستر 2
ب3	باب	75	210	-	2	حمام ماستر 1 - حمام ماستر 2
ب4	باب	80	210	-	2	ملابس ماستر 1 - ملابس ماستر 2
ش1	شباك	200	170	60	2	الأمامية 2
ش2	شباك	80	200	30	2	الأمامية 2
ش3	شباك	60	60	170	2	الخلفية 2
ش4	شباك	100	80	115	1	الخلفية

الإجمالي: أبواب 7 - شبابيك 7

جدول المساحات وبيانات المشروع

بيانات المشروع

البند	البيان
المشروع	كوخ غرفتين ماستر + صالة — 12.00 × 7.00 م (84 م²)
العميل	عميل — كوخ 120
الموقع	القصيم
الاستخدام	سكن / ضيافة
التاريخ	2026-10-25
نظام البناء	هيكل خشب 5×7 + تلبيس 2.5 سم من الجهتين
السقف	جملون 30° — قرميد معدني + 1 مثلث بارز

جدول المساحات


م	الفراغ	الأبعاد (م)	المساحة (م2)
1	ماستر 1	3.94 × 4.24	16.71
2	حمام ماستر 1	2.14 × 2.40	5.14
3	ملابس 1	1.68 × 2.40	4.03
4	الصالة	3.64 × 6.76	24.61
5	ماستر 2	3.94 × 4.24	16.71
6	ملابس 2	1.68 × 2.40	4.03
7	حمام ماستر 2	2.14 × 2.40	5.14
	المساحة الصافية الداخلية		**76.35**
	التراس المسقوف	**12.00 × 2.00**	**24.00**
	المساحة الإجمالية المبنية	**12.00 × 7.00**	**84.00**
	المساحة الكلية (المبنية + التراس)		**108.00**

لقطات المنظور الخارجي


المنظور الأمامي




منظور أمامي من اليسار

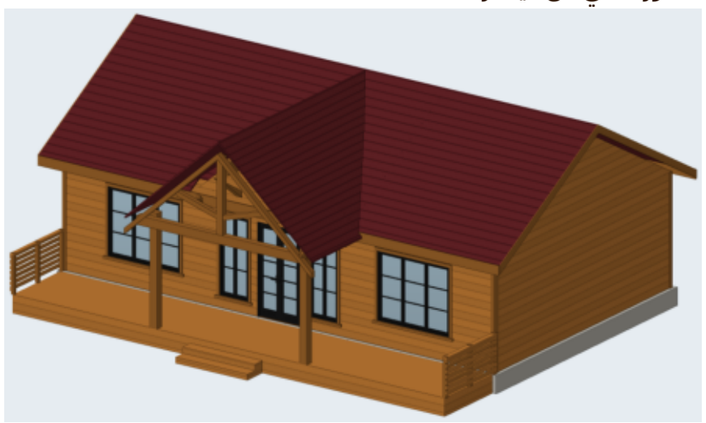


منظور أمامي من اليمين

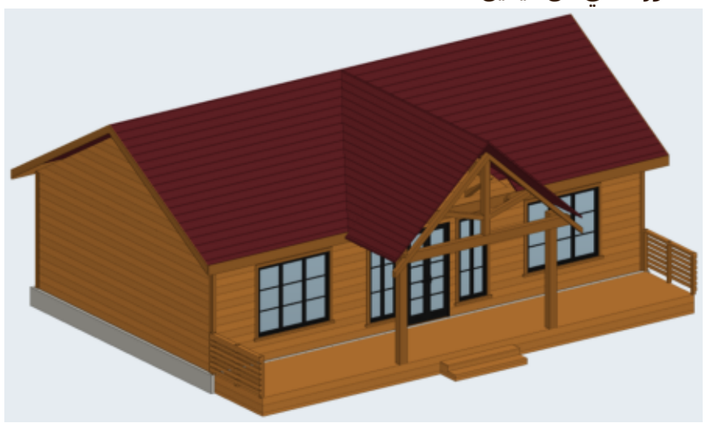


المنظور الخلفي

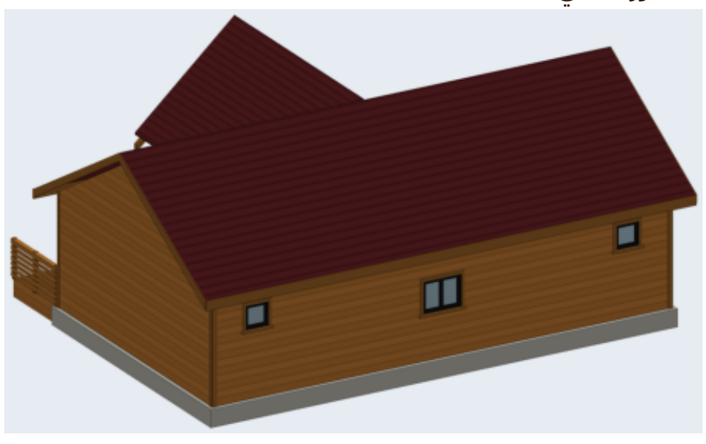

منظور خلفي من اليمين

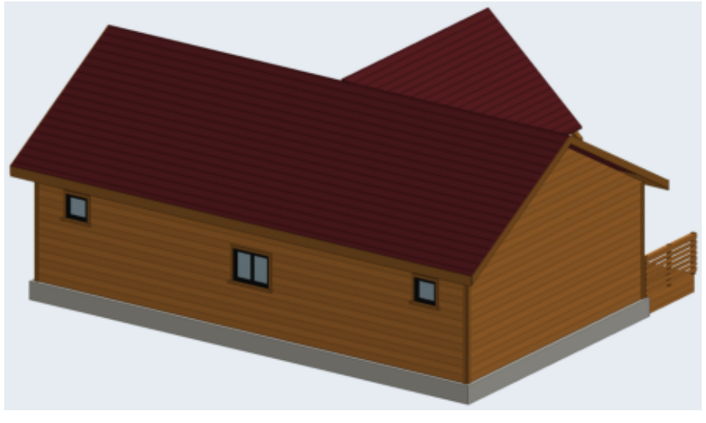


منظر علوي

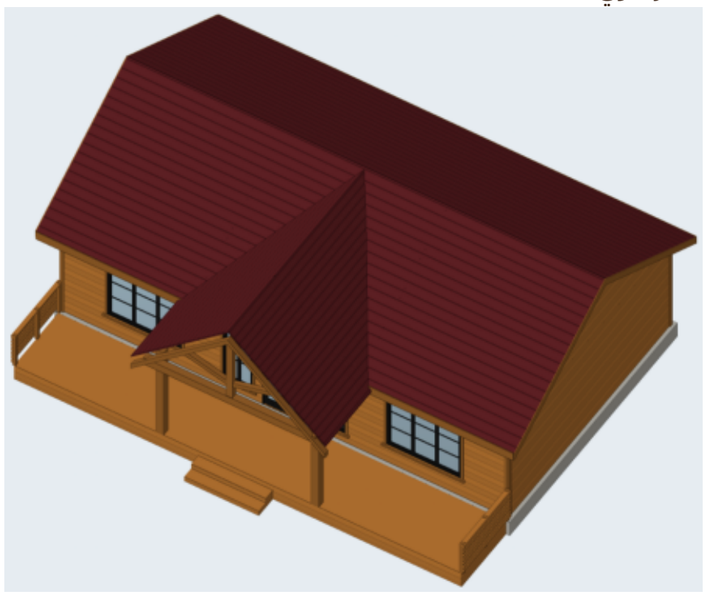

المشروع / العميل	عنوان اللوحة	المقياس	التاريخ	رقم اللوحة
مصنع وتد الأخشاب Watad Wood Factory **كوخ غرفتين ماستر + صالة — 12.00 × 7.00 م (84 م²)** **عميل — كوخ 120**	**لقطات المنظور**	—	**2026-10-25**	**A-07 (7/9)**

المقطع العلوي بالفرش


مقطع أفقي على ارتفاع 1.90 م — توزيع الفرش ومسار الحركة

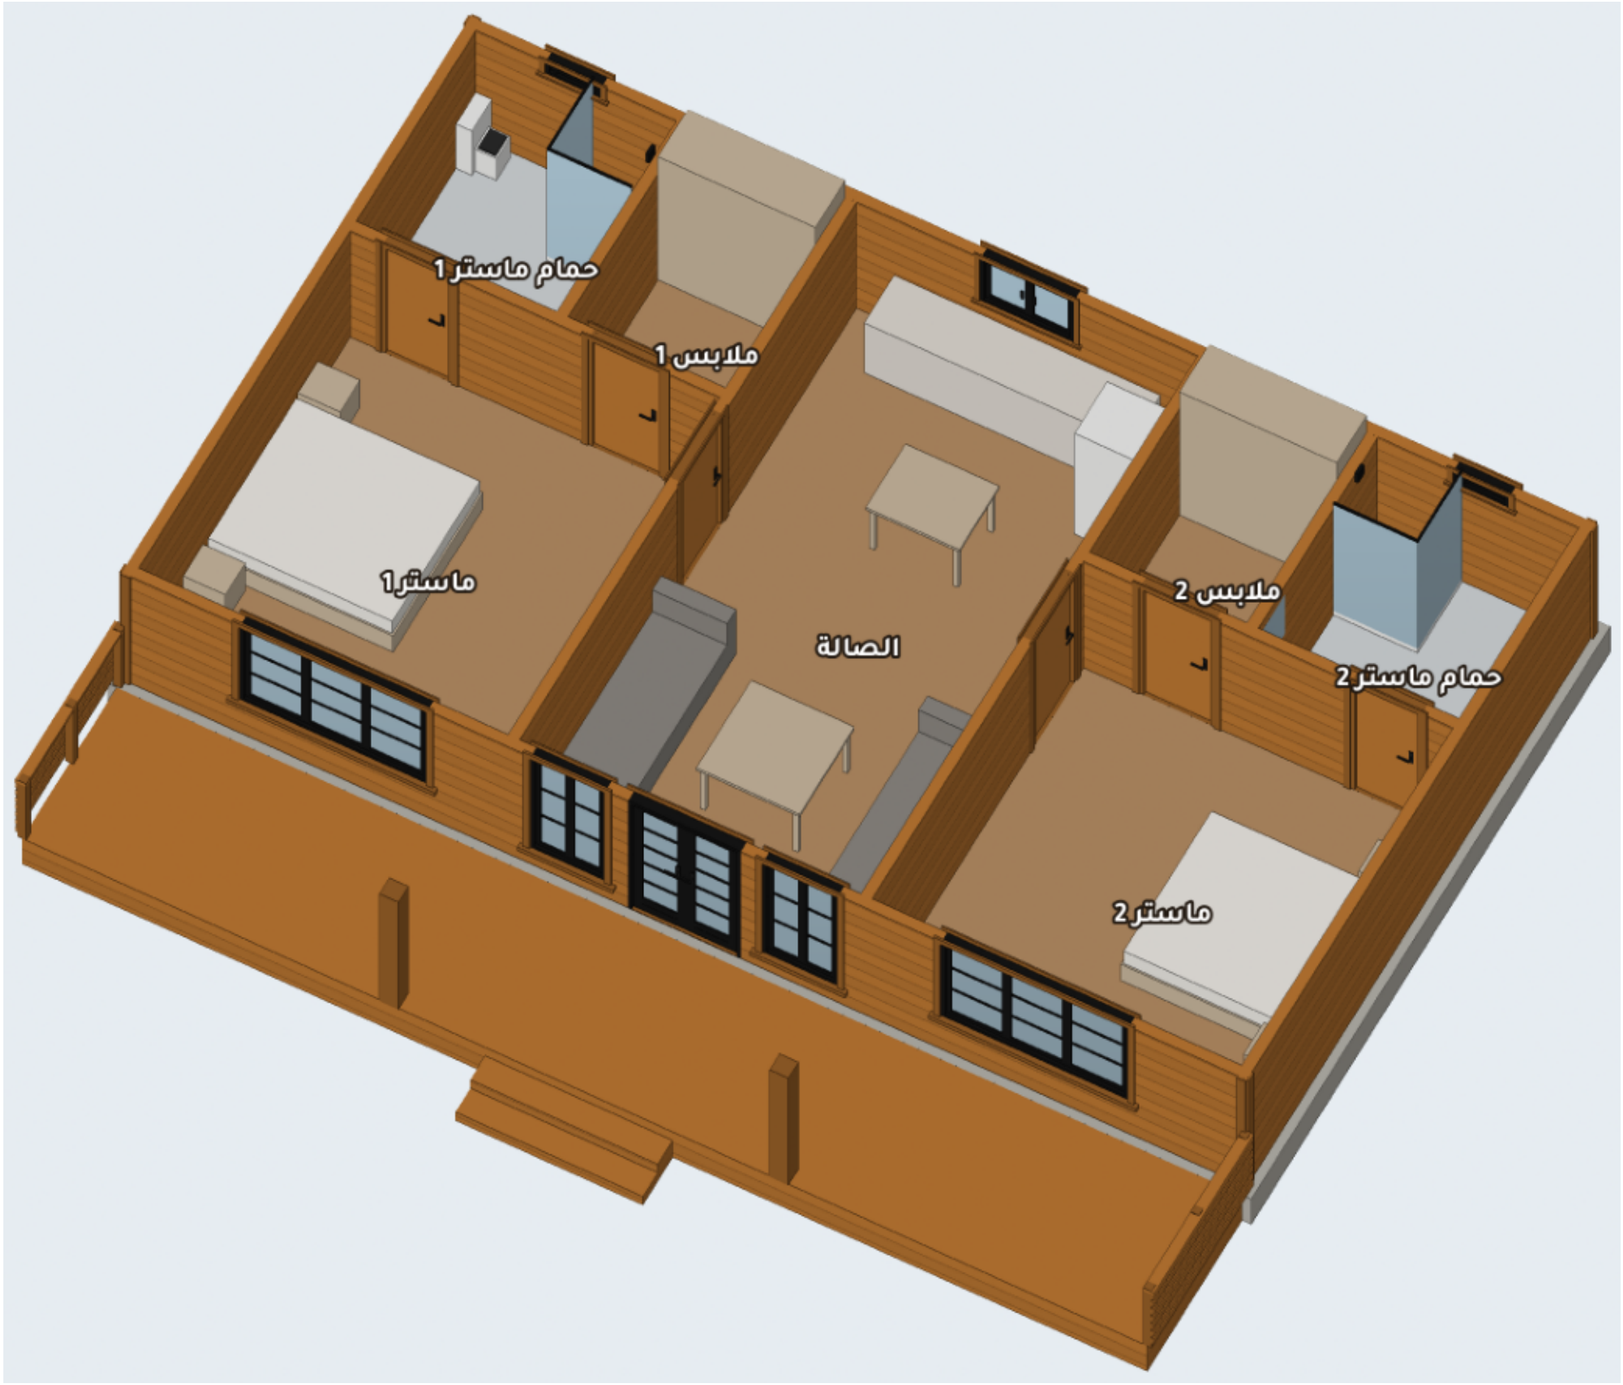

المشروع / العميل	عنوان اللوحة	المقياس	التاريخ	رقم اللوحة
مصنع وتد الأخشاب Watad Wood Factory كوخ غرفتين ماستر + صالة — 12.00 × 7.00 م (84 م²) عميل — كوخ 120	المقطع العلوي بالفرش	—	2026-10-25	A-08 (8/9)

المنظور ثلاثي الأبعاد والمواد

النمط: عسلي + قرميد عنابي — رندر واقعي بخامات حقيقية

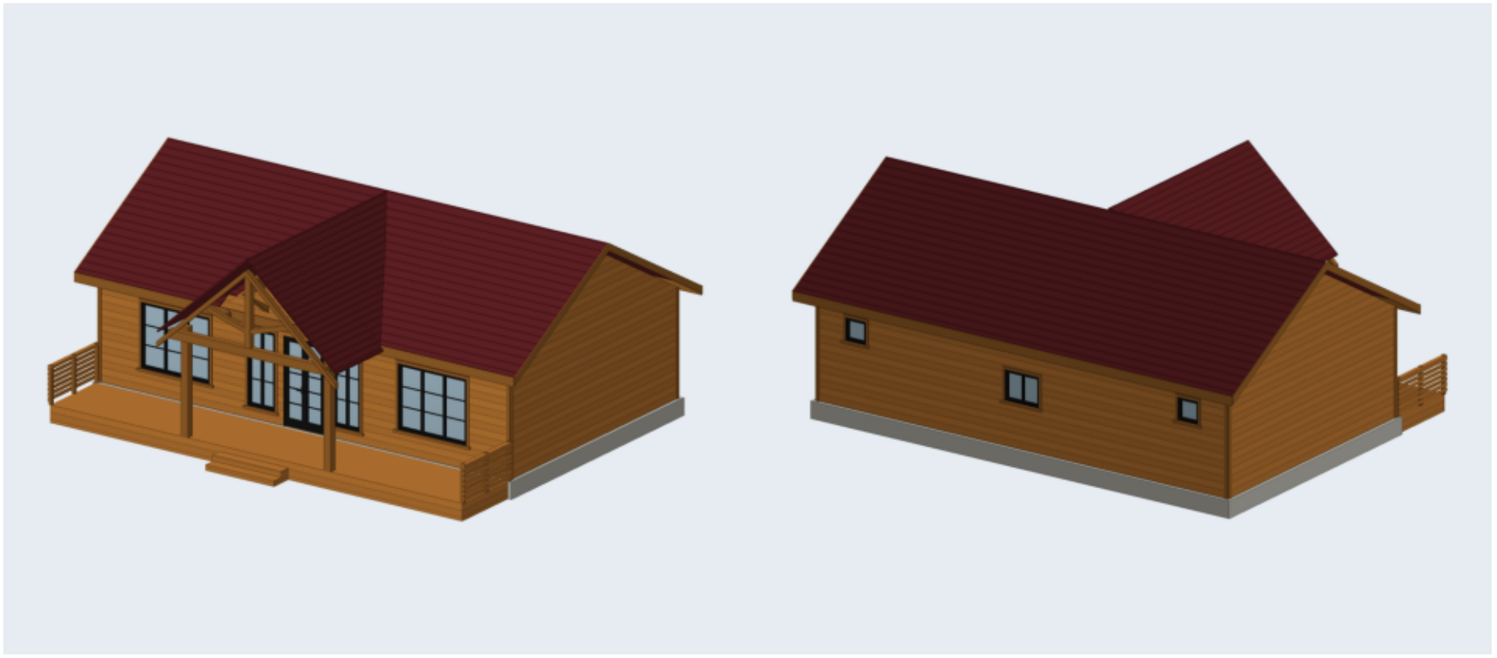

جدول المواد والألوان

الخشب / الصبغة

صبغة عسلي / سيدر

القرميد

قرميد عنابي

الزجاج

زجاج شفاف

إطارات الشبابيك والأبواب

إطار ألمنيوم أسود

الكنار والزوايا

نفس الصبغة أغمق درجة


الصبة

خرسانة 45 سم


الدربزين: ألواح أفقية متقاربة (عصري)

تقسيم الشبابيك: شبكة | الباب الرئيسي: زجاج بتقسيمات (فرنسي)

أنواع الدربزين المعتمدة (من مشاريع المصنع)

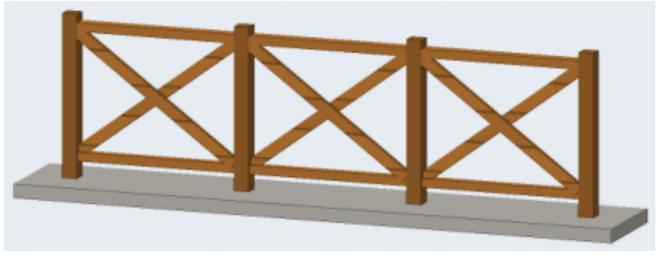

تقاطع X (صورة 5)

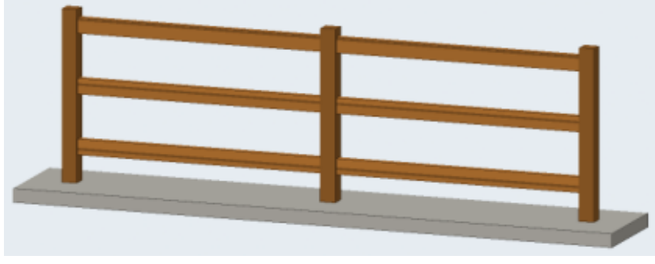

3 مرابيع أفقية (صورة 2)



قوائم رأسية متقاربة (صورة 1)

المشروع / العميل	عنوان اللوحة	المقياس	التاريخ	رقم اللوحة
مصنع وتد الأخشاب Watad Wood Factory **كوخ غرفتين ماستر + صالة — 12.00 × 7.00 م (84 م²)** **عميل — كوخ 120**	**المنظور والمواد**	**—**	**2026-10-25**	**A-09 (9/9)**