


المنظور ثلاثي الأبعاد والمواد

النمط: جوزي غامق + إطارات سوداء — معاينة تقريبية، الإخراج النهائي من 3ds Max

جدول المواد والألوان

 

الخشب / الصبغة

خشب طبيعي فاتح (بدون صبغة)



القرميد

قرميد رمادي غامق



الزجاج

زجاج عاكس غامق



إطارات الشبابيك والأبواب

إطار ألومنيوم أسود



الكنار والزوايا

نفس الصبغة أعمق درجة



الصبغة

خرسانة 45 سم


الدريزين: ألواح أفقية متقاربة (عصري)

تقسيم الشبابيك: بدون | الباب الرئيسي: سحب زجاج


أنواع الدريزين المعتمدة (من مشاريع المصنع)



قوائم رأسية متقاربة (صورة 1)

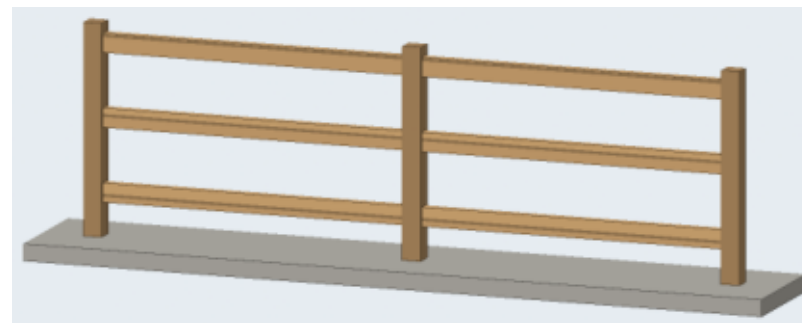

3 مربيع أفقية (صورة 2)

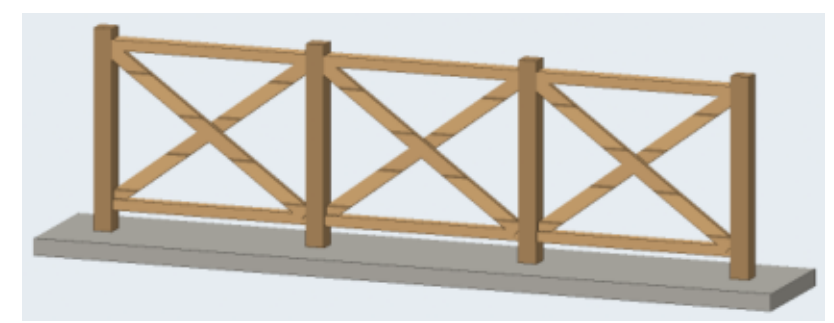

تقاطع X (صورة 5)

رقم اللوحة

W-01 (1/20)

التاريخ

2026-09-29

المقياس

1:50

عنوان اللوحة

المنظور والمواد

المشروع / العميل


كوخ دورين 3 غرف نوم — 120 م²
عميل جديد

مصنع وتد الأخشاب

Watad Wood Factory




المسقط الأفقي مع الفرش — الدور الأرضي
الأبعاد بالسنتيمتر - الجدران: قوائم 5×7 + تليس 2.5 من الجهتين (12 سم) | منسوب الأرضية 0.00+

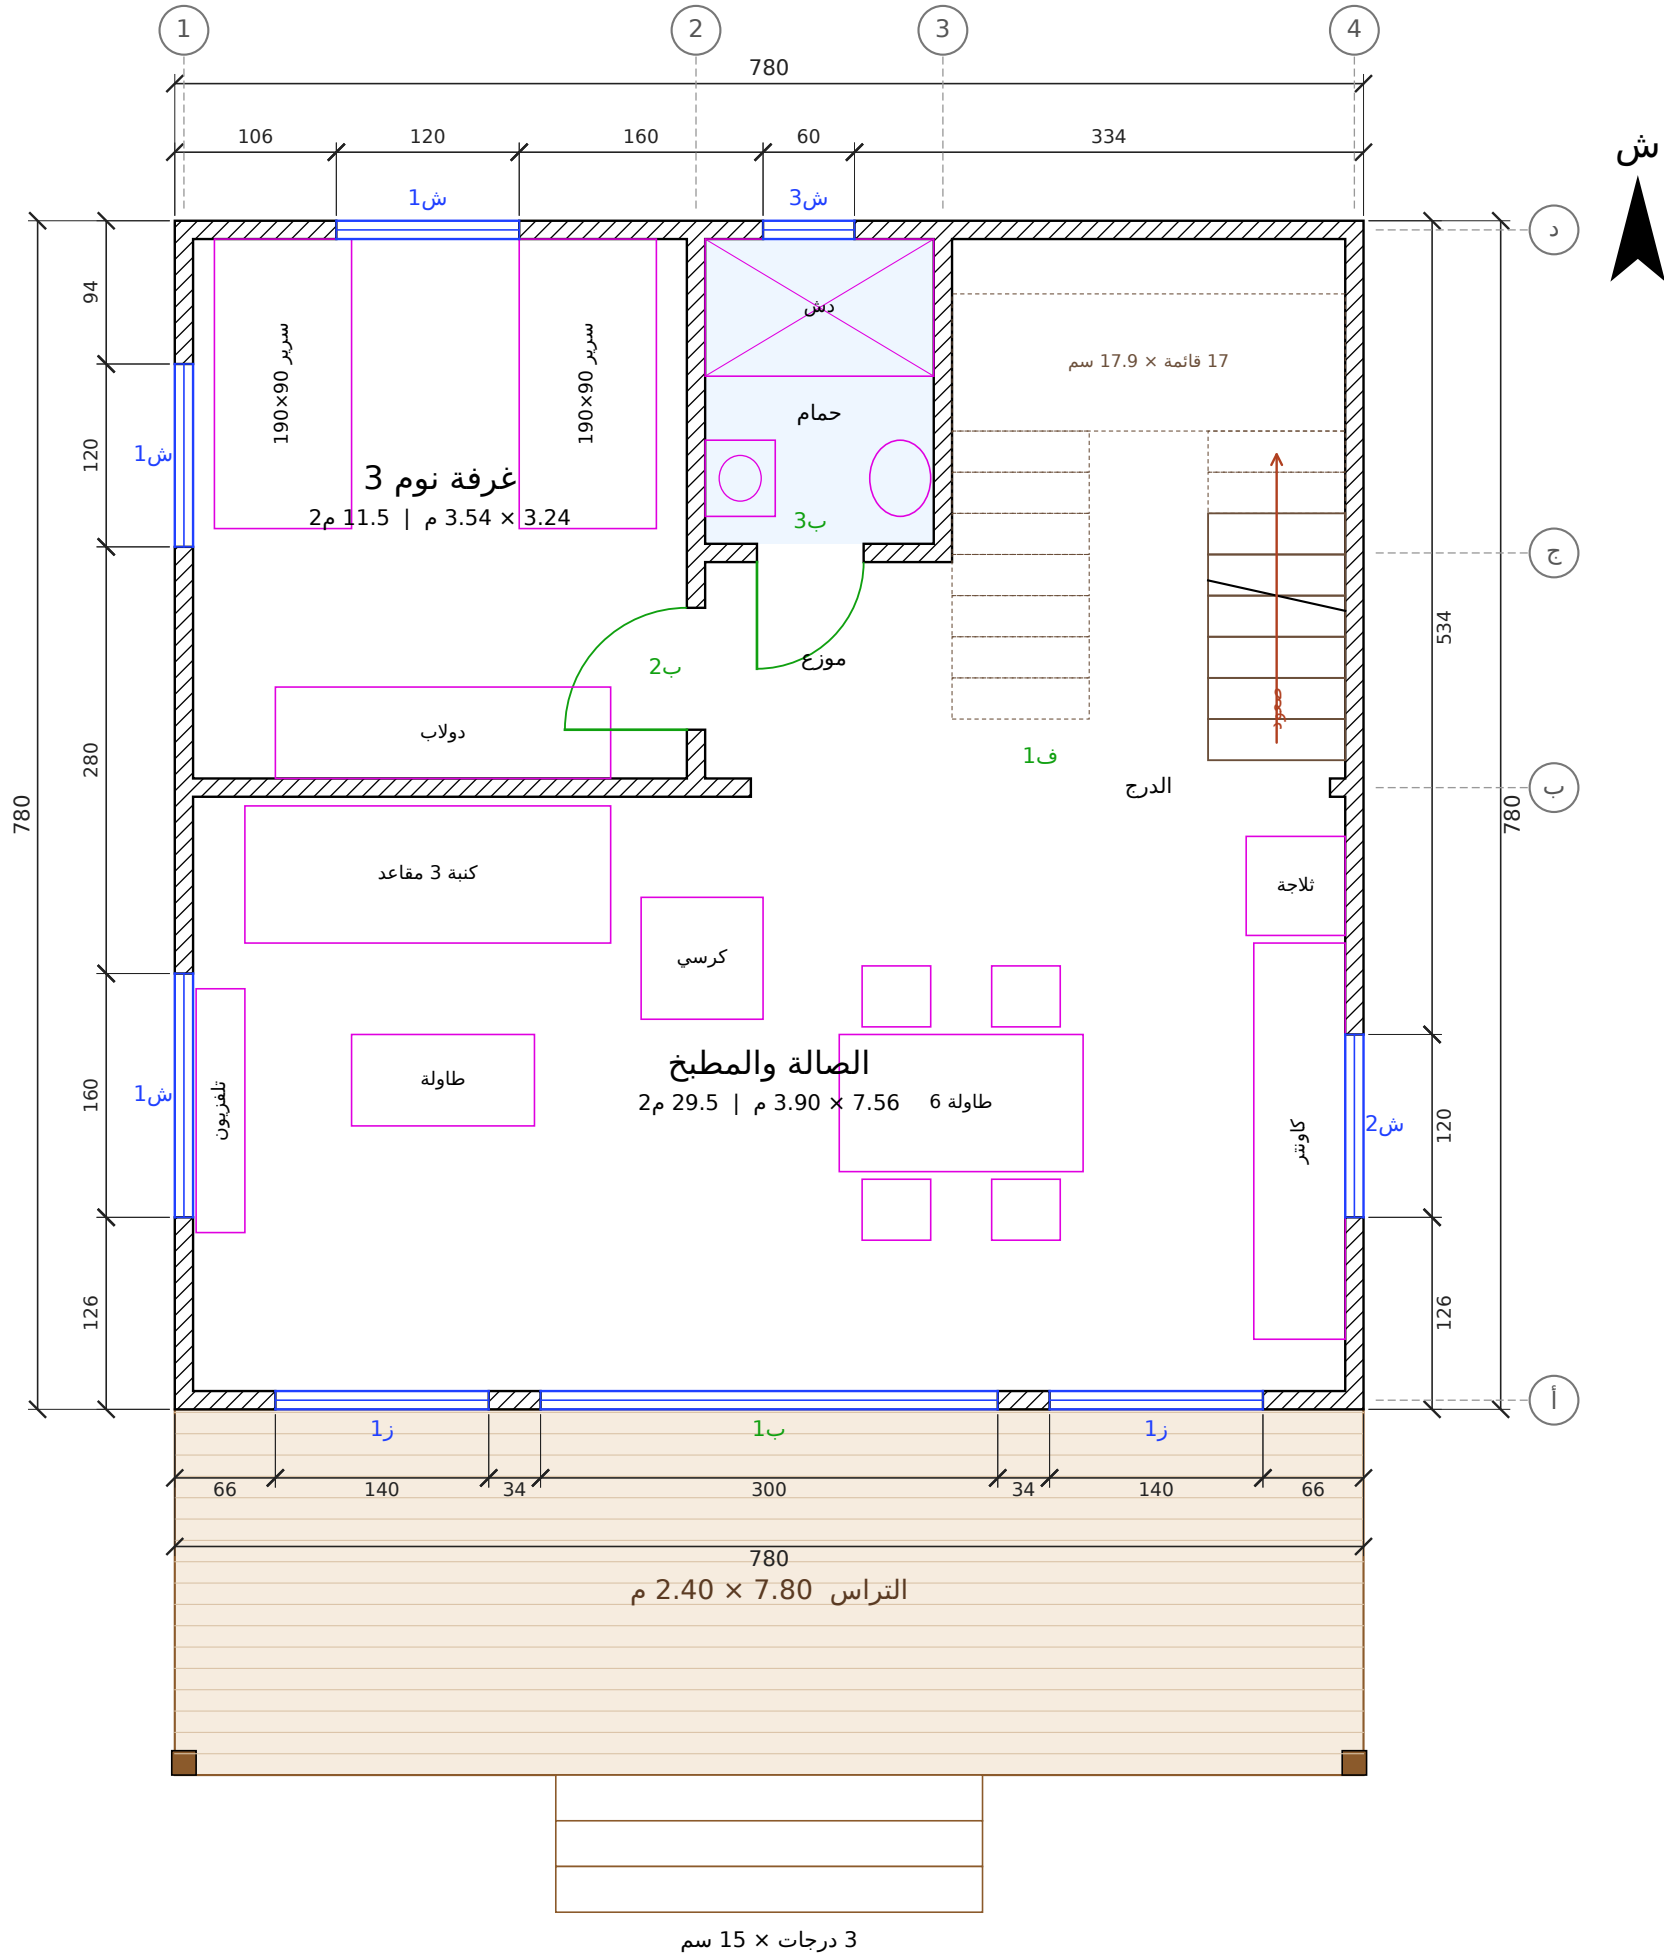


رقم اللوحة	التاريخ	المقياس	عنوان اللوحة	المشروع / العميل	مصنع وتد الأخشاب Watad Wood Factory
W-02 (2/20)	2026-09-29	1:50	المسقط الأفقي — الدور الأرضي	كوخ دورين 3 غرف نوم — 120 م ² عميل جديد	

المسقط الأفقي مع الفرش — الدور الأول

الأبعاد بالسنتيمتر - الجدران: قوائم 5×7 + تليس 2.5 من الجهتين (12 سم) | منسوب الأرضية +3.05

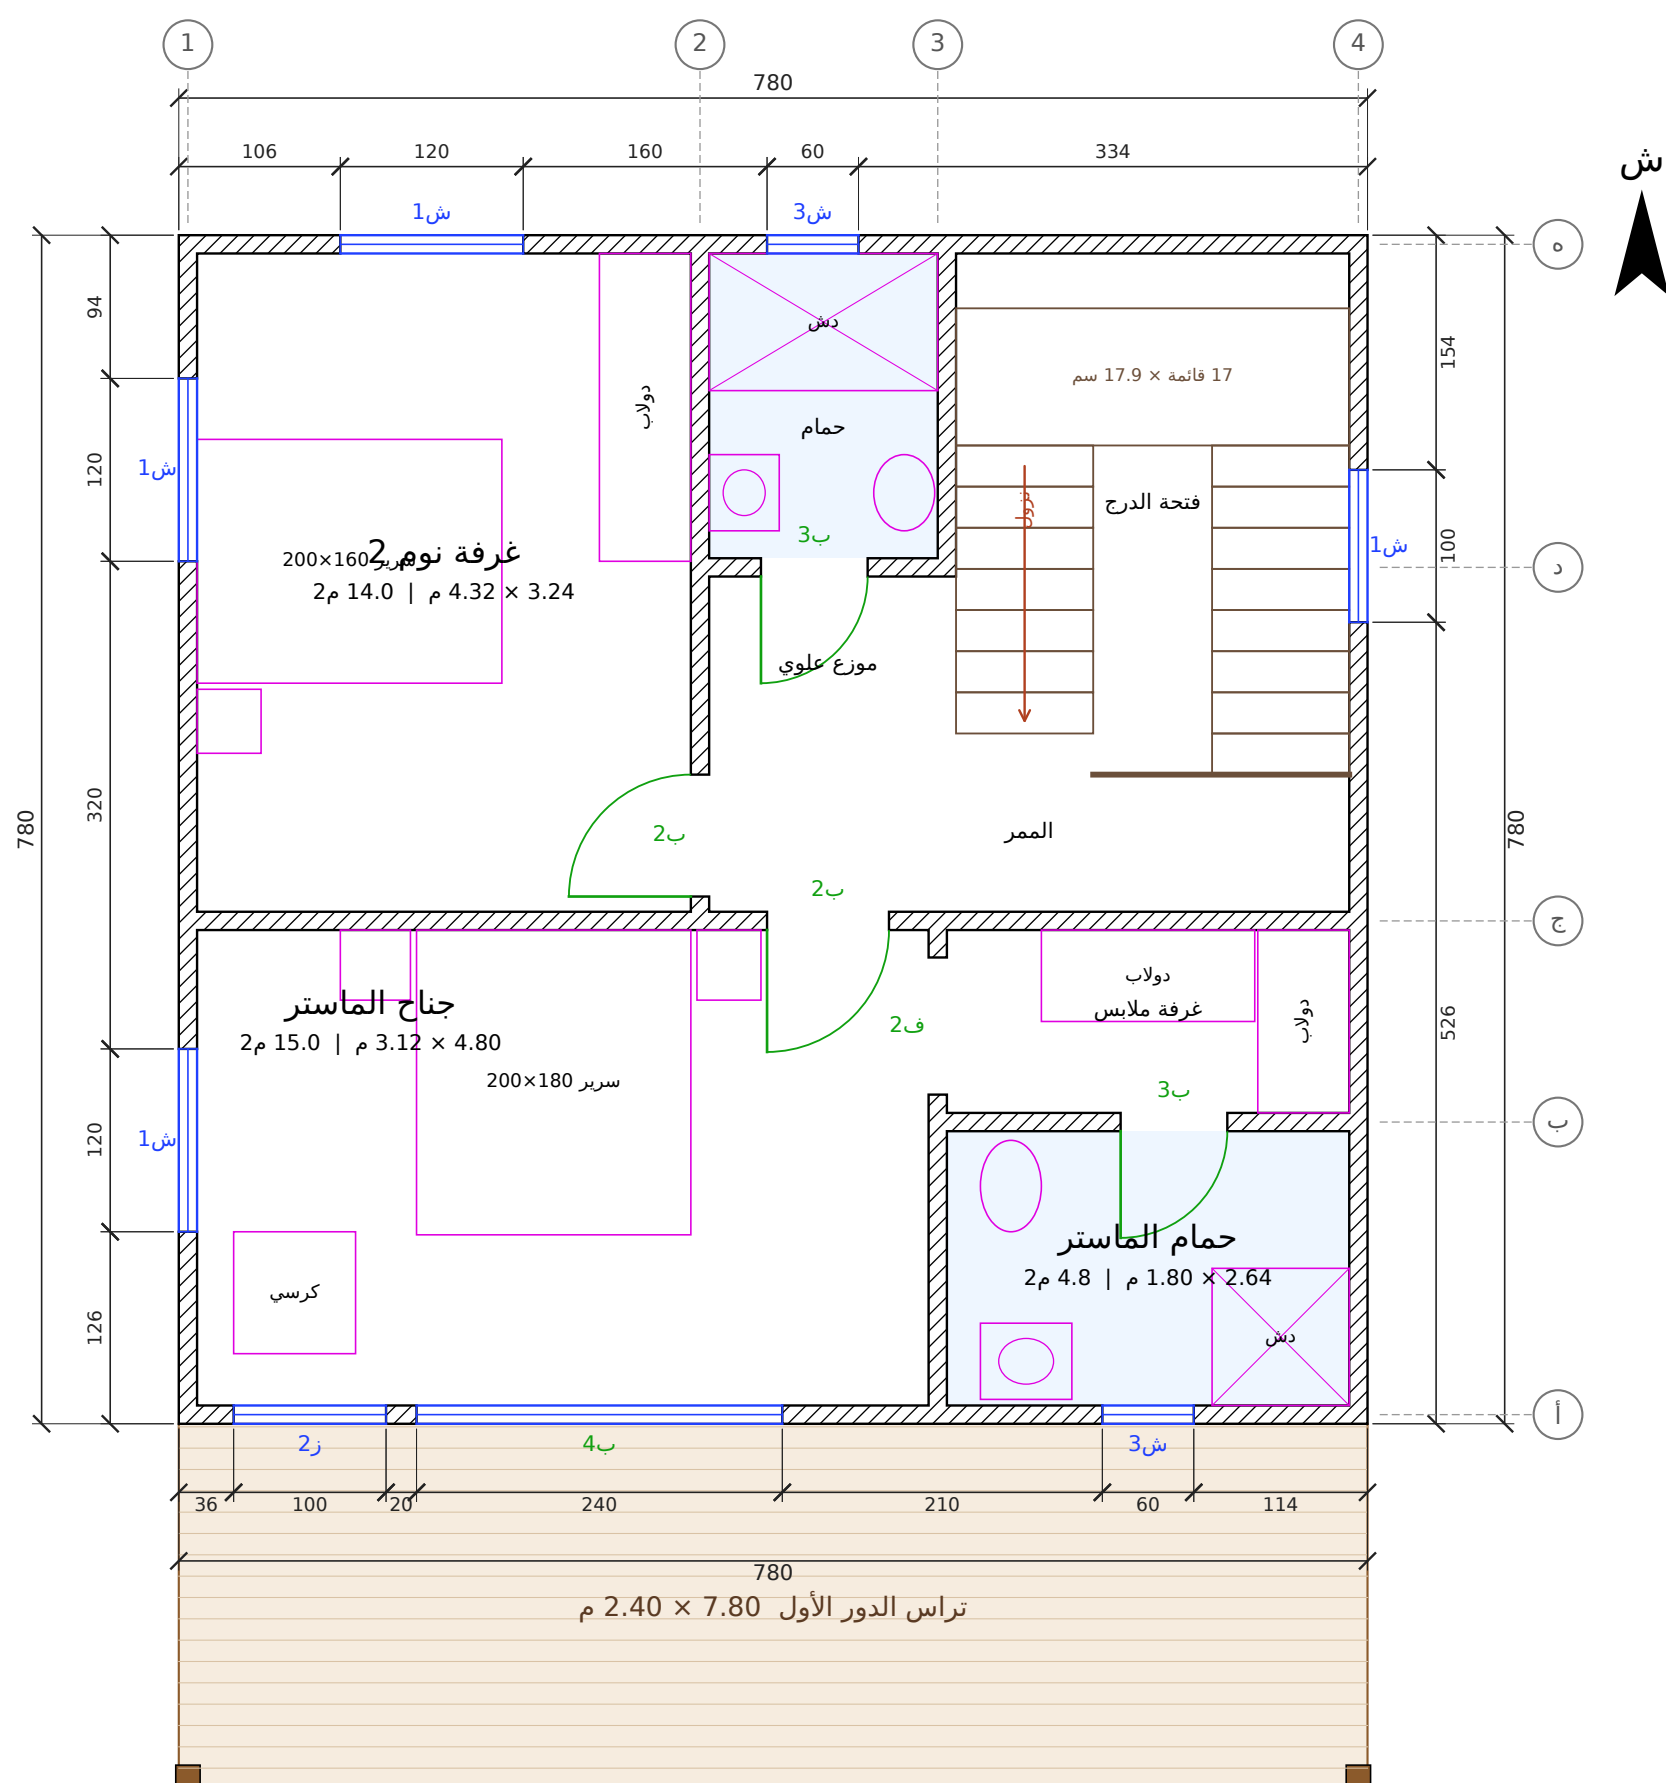


المشروع / العميل كوخ دورين 3 غرف نوم — 120 م² عميل جديد	عنوان اللوحة المسقط الأفقي — الدور الأول	المقياس 1:50	التاريخ 2026-09-29	رقم اللوحة W-03 (3/20)
--	--	----------------------------	----------------------------------	--------------------------------------

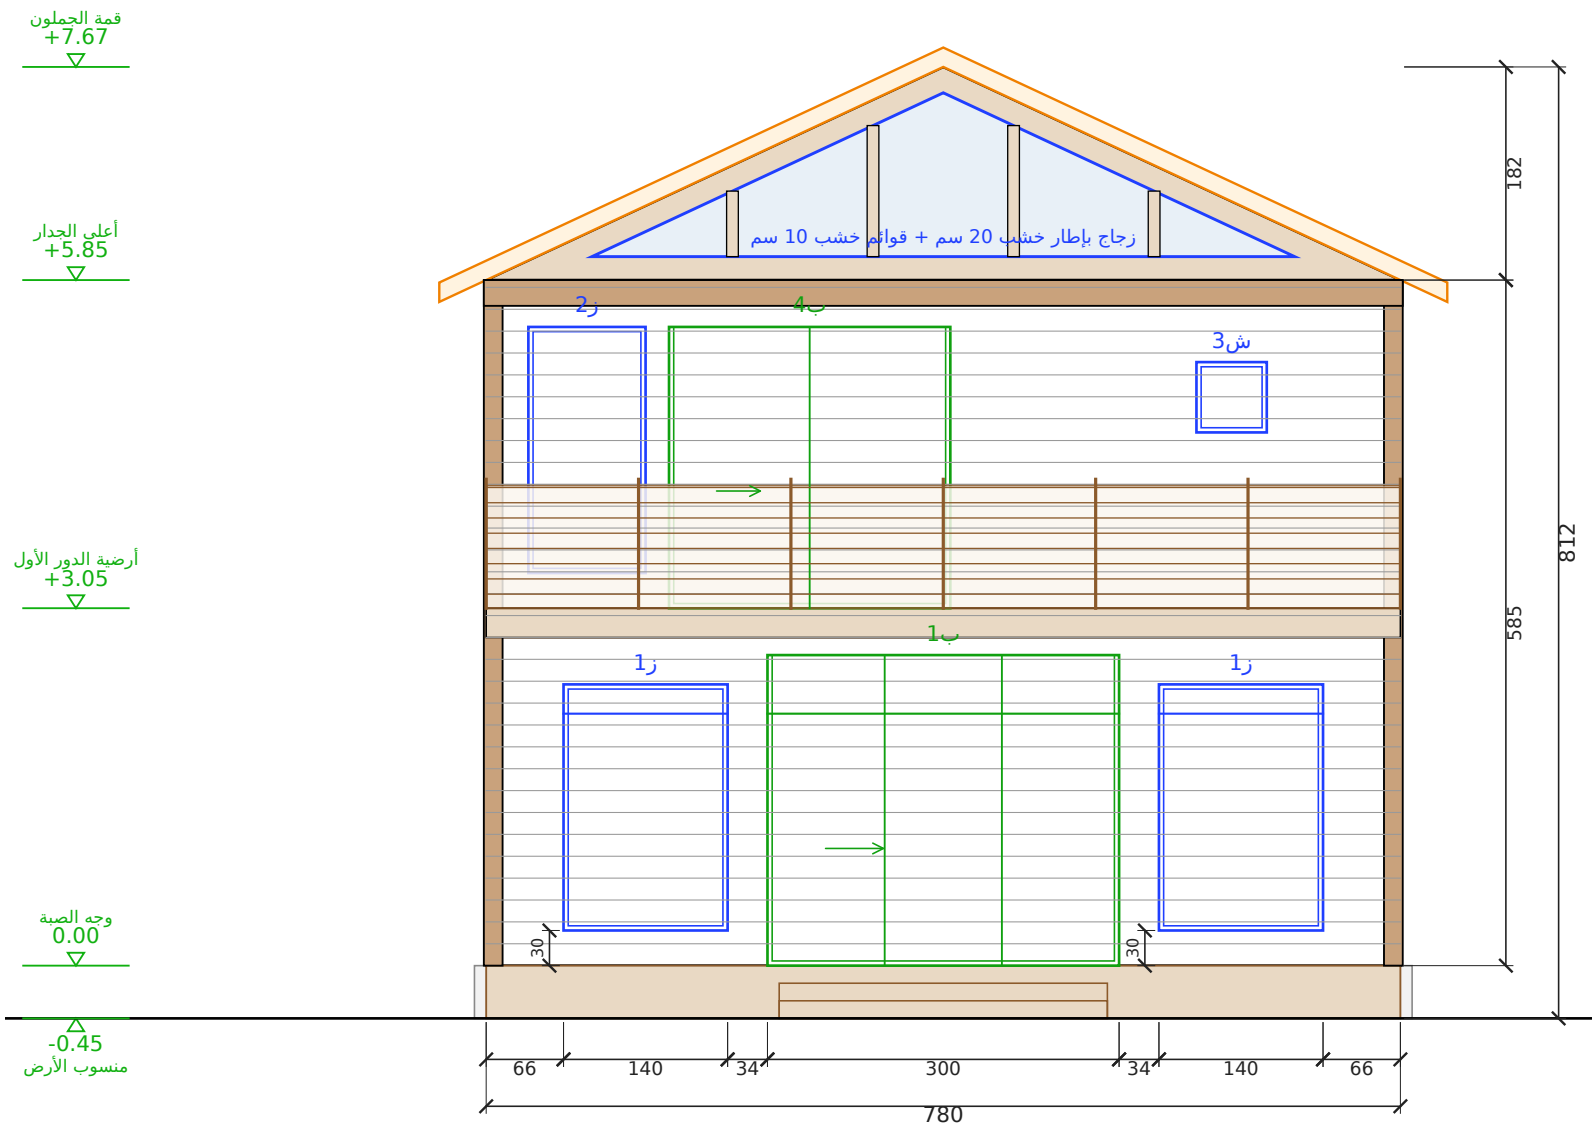

الواجهة الأمامية (التراس)


مقياس 1:50 | الوحدة: سم

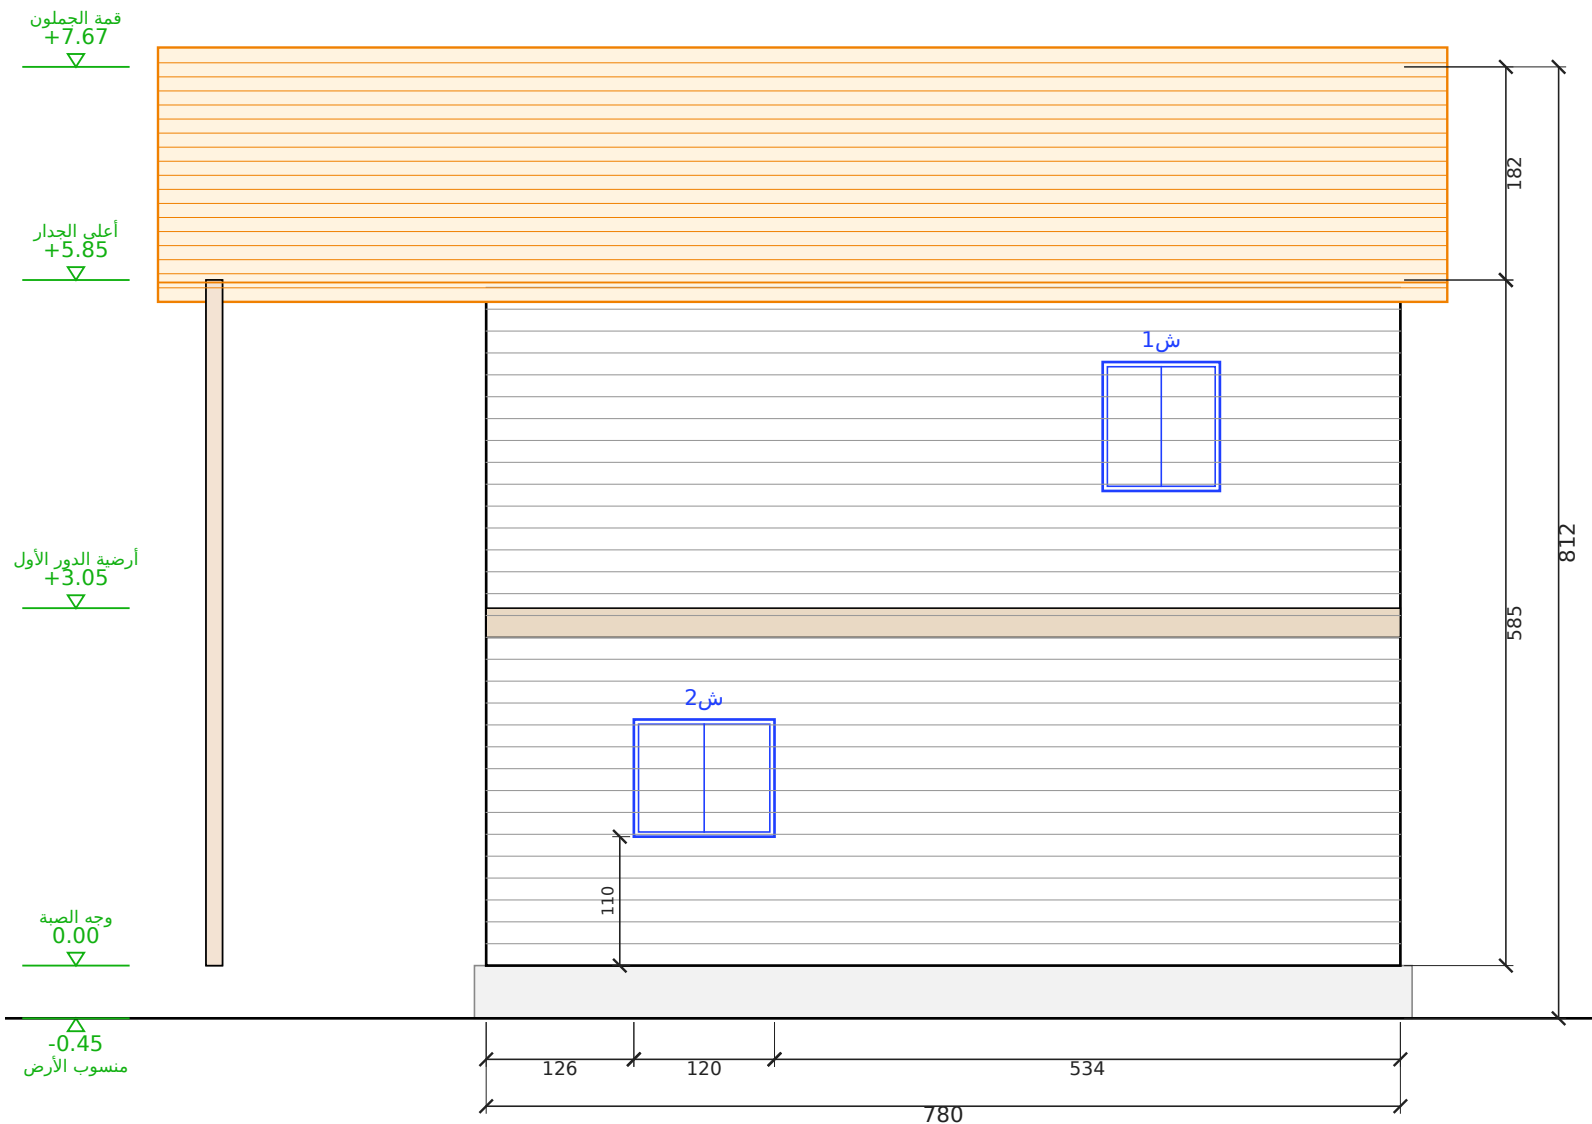

الواجهة الشرقية


مقياس 1:50 | الوحدة: سم

رقم اللوحة	التاريخ	المقياس	عنوان اللوحة	المشروع / العميل	مصنع وتد الأخشاب Watad Wood Factory
W-04 (4/20)	2026-09-29	1:50	الواجهة الأمامية (التراس) والواجهة الشرقية	كوخ دورين 3 غرف نوم — 120 م ² عميل جديد	

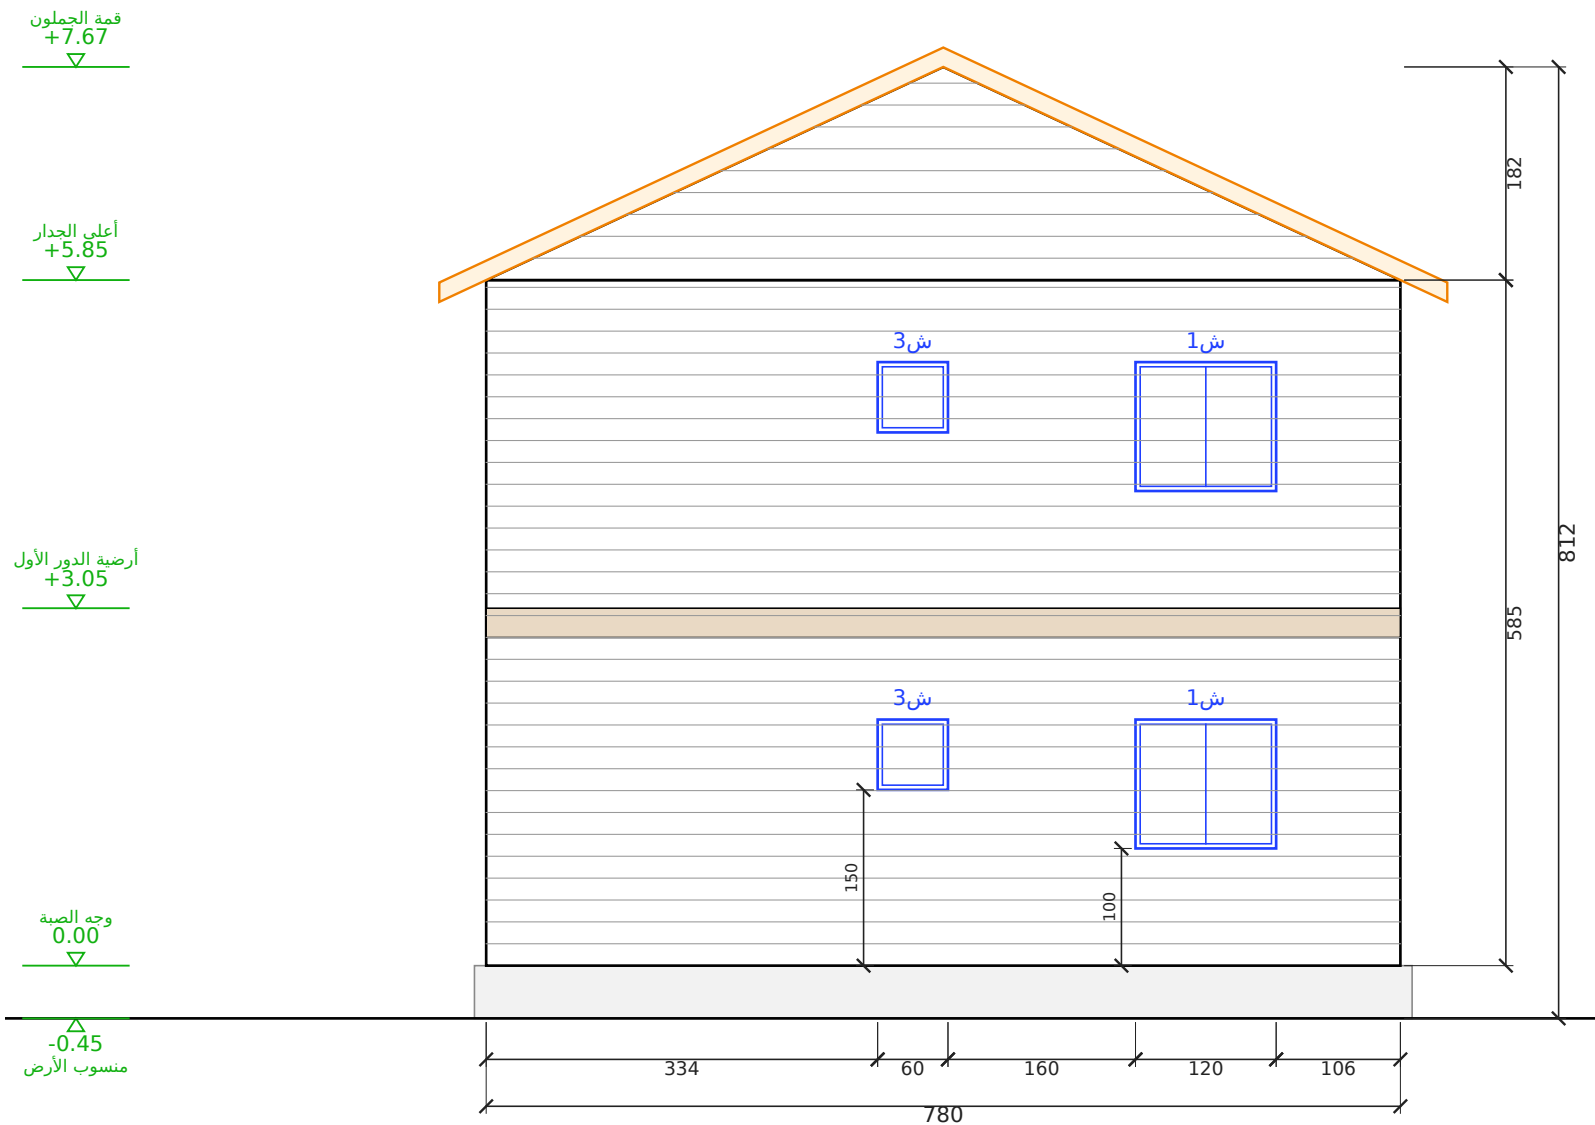

الواجهة الخلفية

مقياس 1:50 | الوحدة: سم

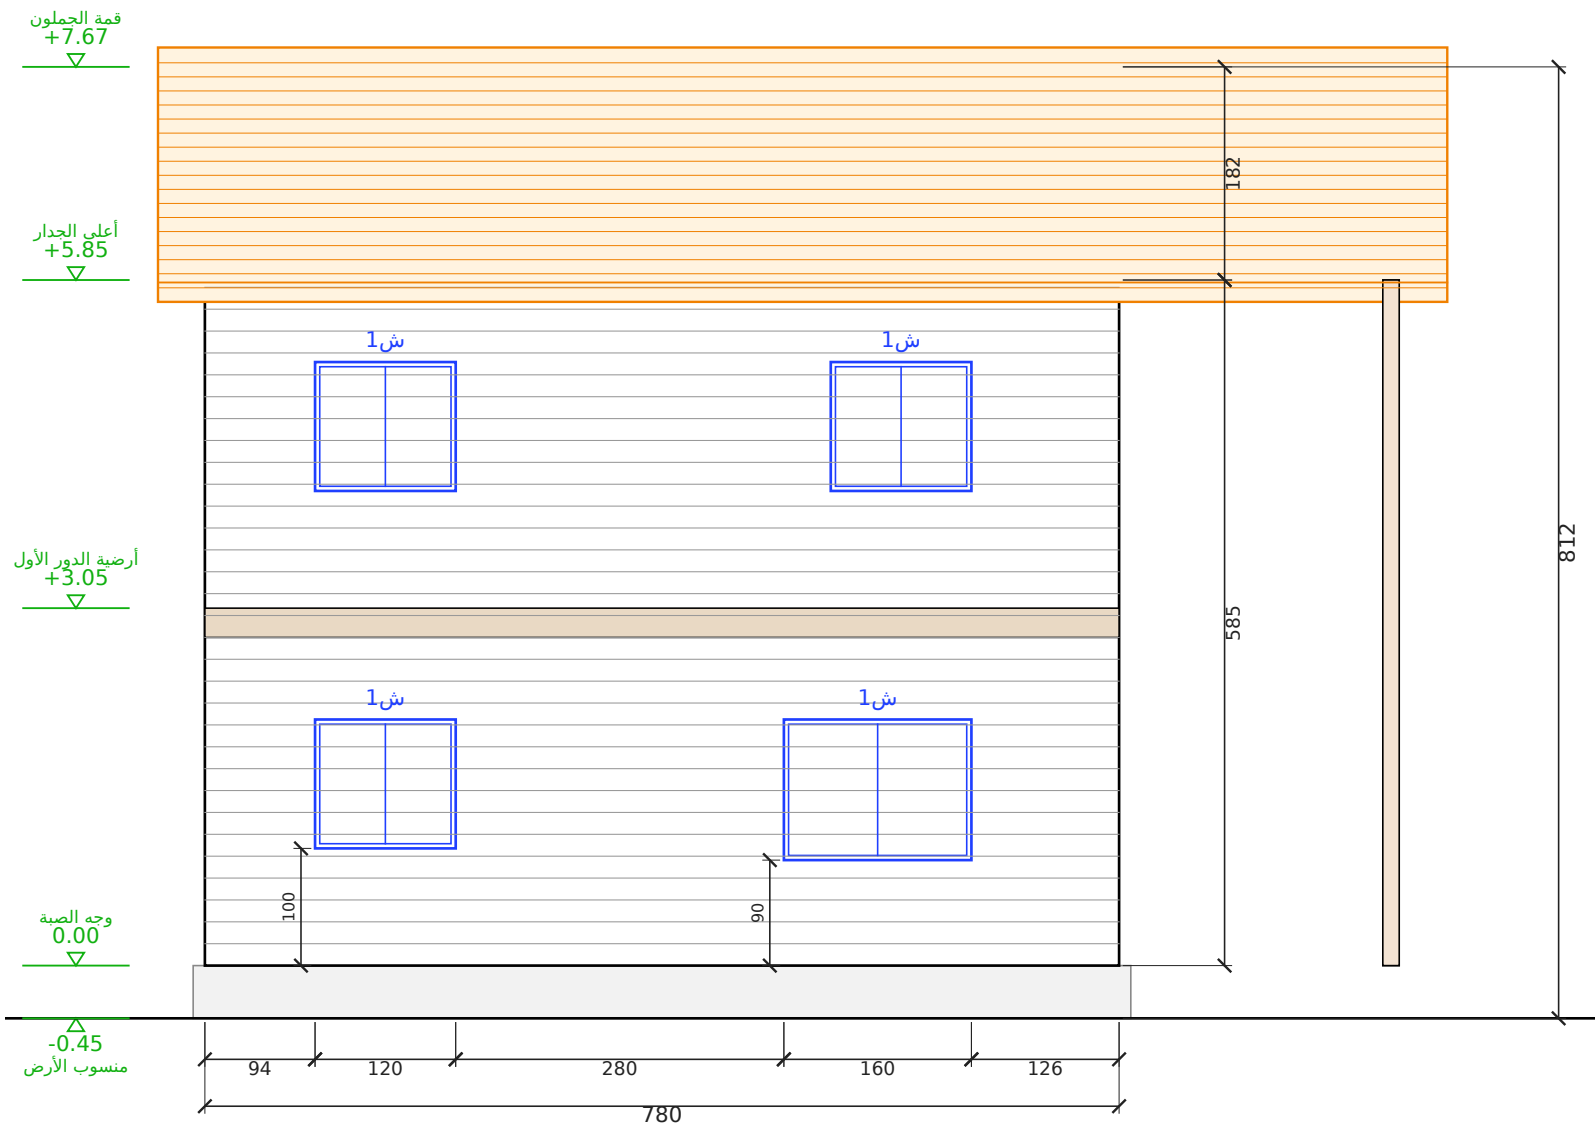


الواجهة الغربية


مقياس 1:50 | الوحدة: سم

رقم اللوحة	التاريخ	المقياس	عنوان اللوحة	المشروع / العميل	مصنع وتد الأخشاب Watad Wood Factory
W-05 (5/20)	2026-09-29	1:50	الواجهة الخلفية والواجهة الغربية	كوخ دورين 3 غرف نوم — 120 م ² عميل جديد	


مسقط السقف (جملون)
رفرف 40 سم من كل جهة | مقياس 1:50

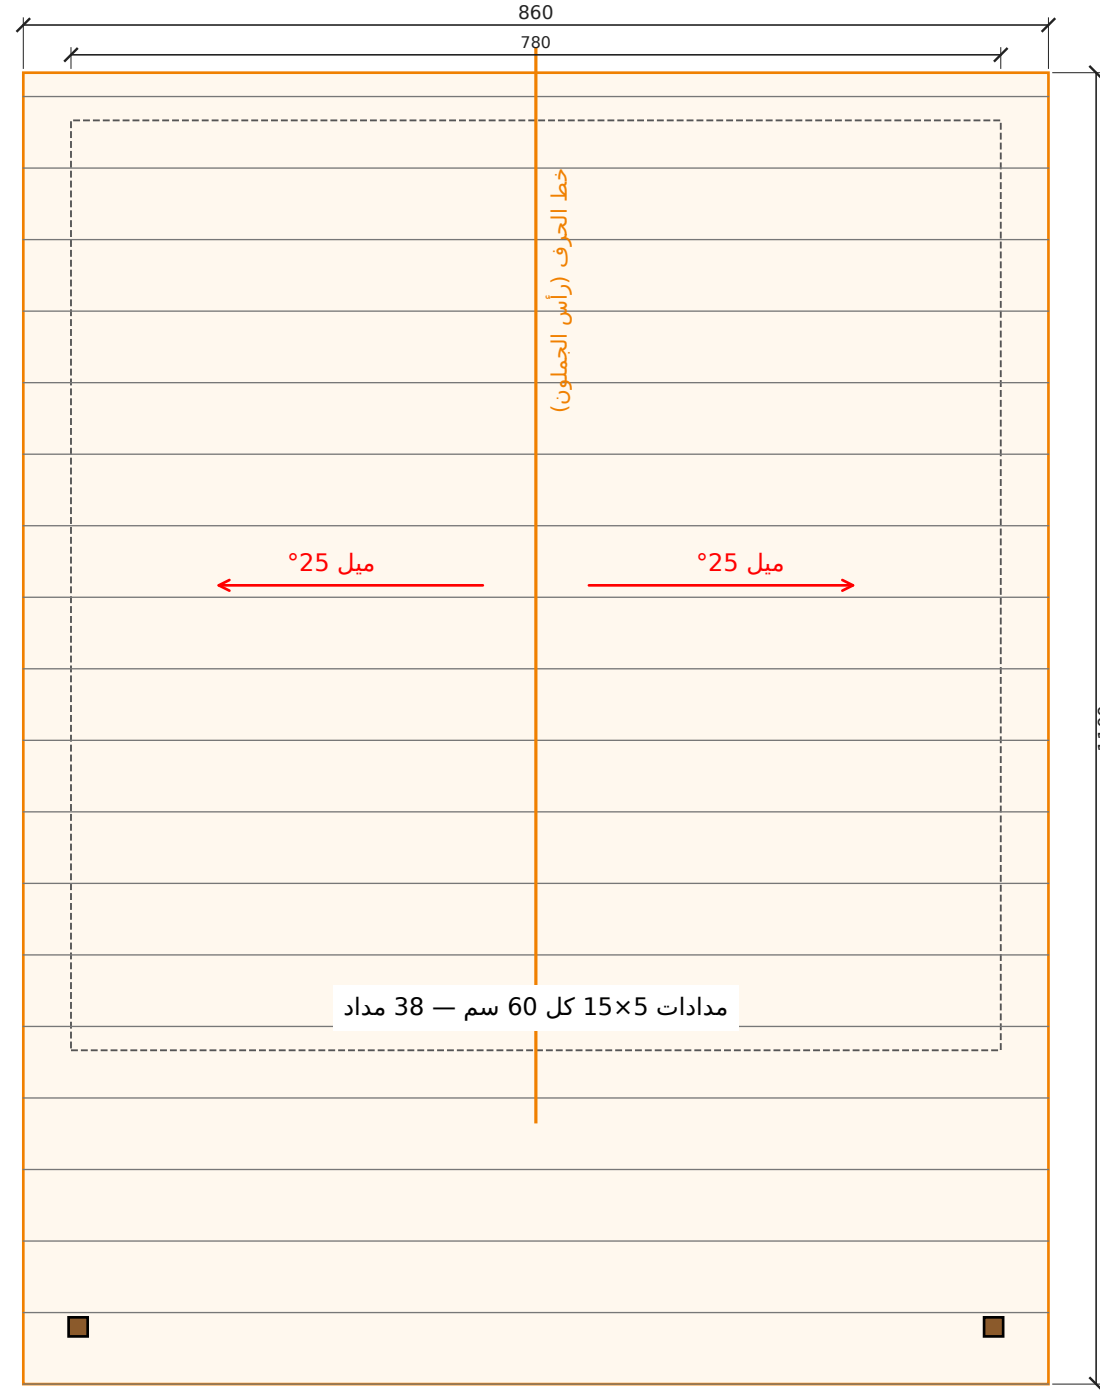

قطاع عرضي أ-أ
مقياس 1:50 | الوحدة: سم

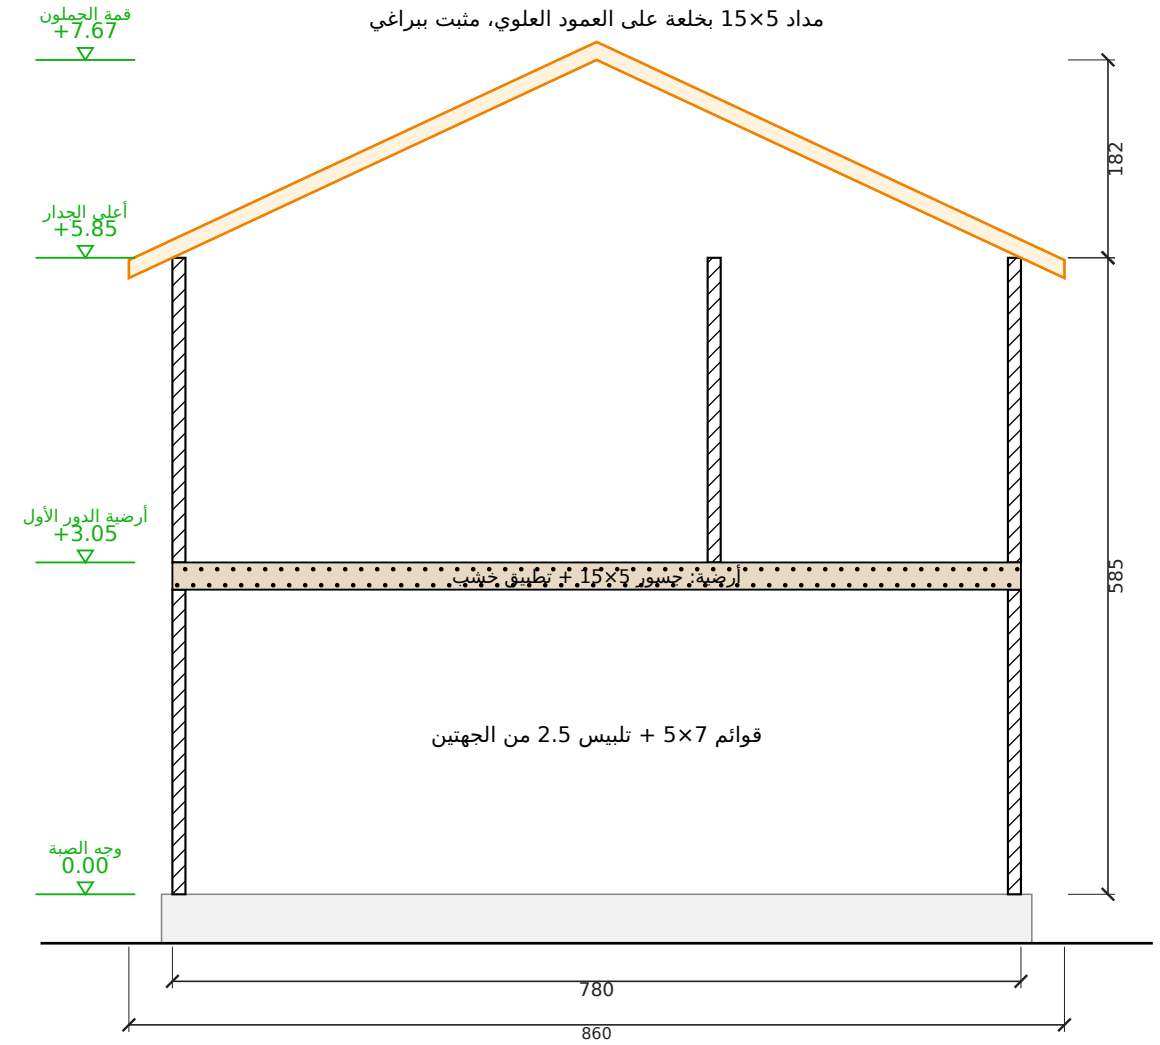

تفصيلة جلوس المداد على العلوي (1:5)

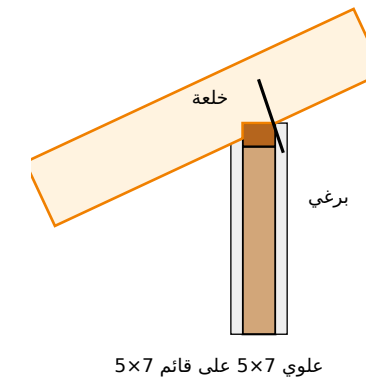

رقم اللوحة

W-06 (6/20)

التاريخ

2026-09-29

المقياس

—

عنوان اللوحة

مسقط السقف والقطاع

المشروع / العميل

كوخ دورين 3 غرف نوم - 120 م²
عميل جديد

مصنع وتد الأخشاب
Watad Wood Factory



جدول مقاسات الأبواب والشبابيك
مقاس الفتحة الصافي في الجدار - الوحدة: سم

الرمز	النوع	العرض (سم)	الارتفاع (سم)	ارتفاع الجلسة (سم)	العدد	الموقع
ب1	باب	300	265	-	1	الأمامية (التراس)
ب2	باب	80	210	-	3	غرفة 3 - ماستر - غرفة 2
ب3	باب	70	210	-	3	حمام 2 - حمام ماستر
ب4	باب مزدوج	240	240	-	1	الأمامية (التراس)
ف1	باب	380	240	-	1	فتحة الموزع والدرج
ف2	باب	90	210	-	1	فتحة غرفة الملابس
ز1	شباك	140	210	30	2	الأمامية (التراس) 2
ز2	شباك	100	210	30	1	الأمامية (التراس)
ش1	شباك	120	110	100	5	الخلفية 2 - الغربية 3
ش1	شباك	160	120	90	1	الغربية
ش1	شباك	100	110	100	1	الشرقية
ش2	شباك	120	100	110	1	الشرقية
ش3	شباك	60	60	150	3	الخلفية 2 - الأمامية (التراس)

الإجمالي: أبواب 10 - شبابيك 14

جدول المساحات وبيانات المشروع والتسعير

جدول المساحات

م	الفراغ	الأبعاد (م)	المساحة (م2)
1	أرضي — الصالة والمطبخ	7.56 × 3.90	29.48
2	أرضي — غرفة نوم 3	3.24 × 3.54	11.47
3	أرضي — موزع	1.56 × 1.42	2.22
4	أرضي — حمام	1.50 × 2.00	3.00
5	أرضي — الدرج	2.58 × 3.54	9.13
6	أول — جناح الماستر	4.80 × 3.12	14.98
7	أول — حمام الماستر	2.64 × 1.80	4.75
8	أول — غرفة ملابس	2.64 × 1.20	3.17
9	أول — غرفة نوم 2	3.24 × 4.32	14.00
10	أول — الممر	4.20 × 0.90	3.78
11	أول — موزع علوي	1.56 × 1.30	2.03
12	أول — حمام	1.50 × 2.00	3.00
	المساحة الصافية الداخلية		101.00
	التراس المسقوف + تراس الدور الأول	7.80 × 2.40 × 2	37.44
	المساحة الإجمالية المبنية	2 × 7.80 × 7.80 دور	121.68

بيانات المشروع

البند	البيان
المشروع	كوخ دورين 3 غرف نوم — 120 م ²
العميل	عميل جديد
الموقع	—
الاستخدام	سكن / استجمام
التاريخ	2026-09-29
نظام البناء	هيكل خشب 5×7 + تليس 2.5 سم من الجهتين
السقف	جملون 25° — قرميد معدني

التسعير

البند	القيمة
المساحة المبنية (م2)	121.68
سعر المتر المربع	يُحدد بعد الاعتماد
الإجمالي	—


ملاحظات:

- السعر للمساحة المبنية حسب المخطط المعتمد.
- الصبة والتوريدات الخارجية على العميل ما لم يُذكر غير ذلك.


Technical drawing of a wall section. The drawing shows a wall with a total height of 280 and a total width of 768. The wall is divided into vertical sections with the following dimensions (from left to right): 58, 58, 125, 58, 60, 60, 60, 60, 60, 60, 60, 46. A window is shown in the section with a width of 125 and a height of 100. The window is labeled 'ش 2 100x120'. The wall is constructed with a brown outer layer and a light brown inner layer. The window frame is blue, and the window opening is white. A vertical purple line is shown in the section with a width of 125.

المشروع / العميل كوخ دورين 3 غرف نوم – 120 م² عميل جديد	عنوان اللوحة لوحات التأطير (للورشة)	المقياس —	التاريخ 2026-09-29	رقم اللوحة W-09 (9/20)
--	---	-------------------------	----------------------------------	--------------------------------------

تأطير جدار أ-شمال — الطول 768 سم، الارتفاع 280 سم

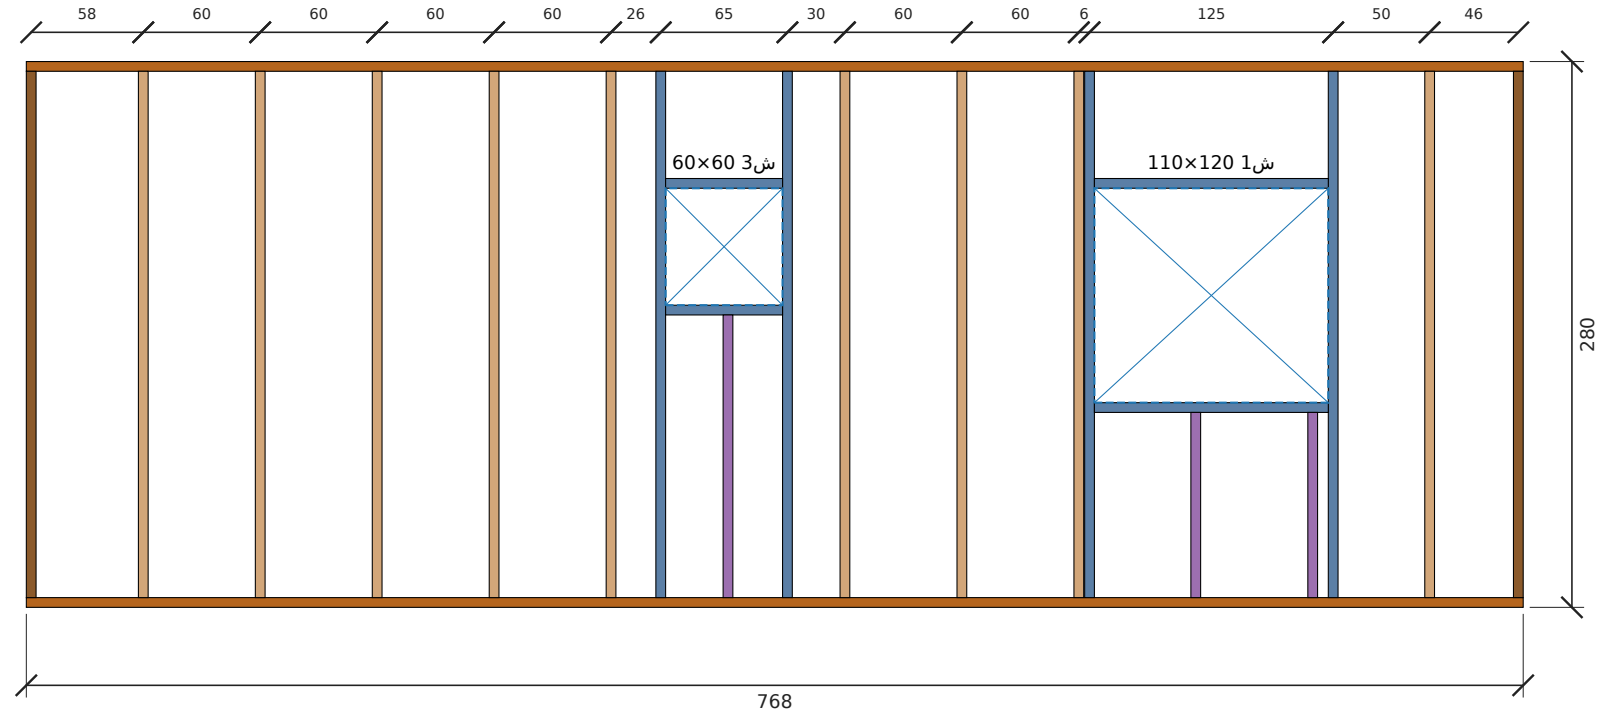

تأطير جدار أ-غرب — الطول 768 سم، الارتفاع 280 سم

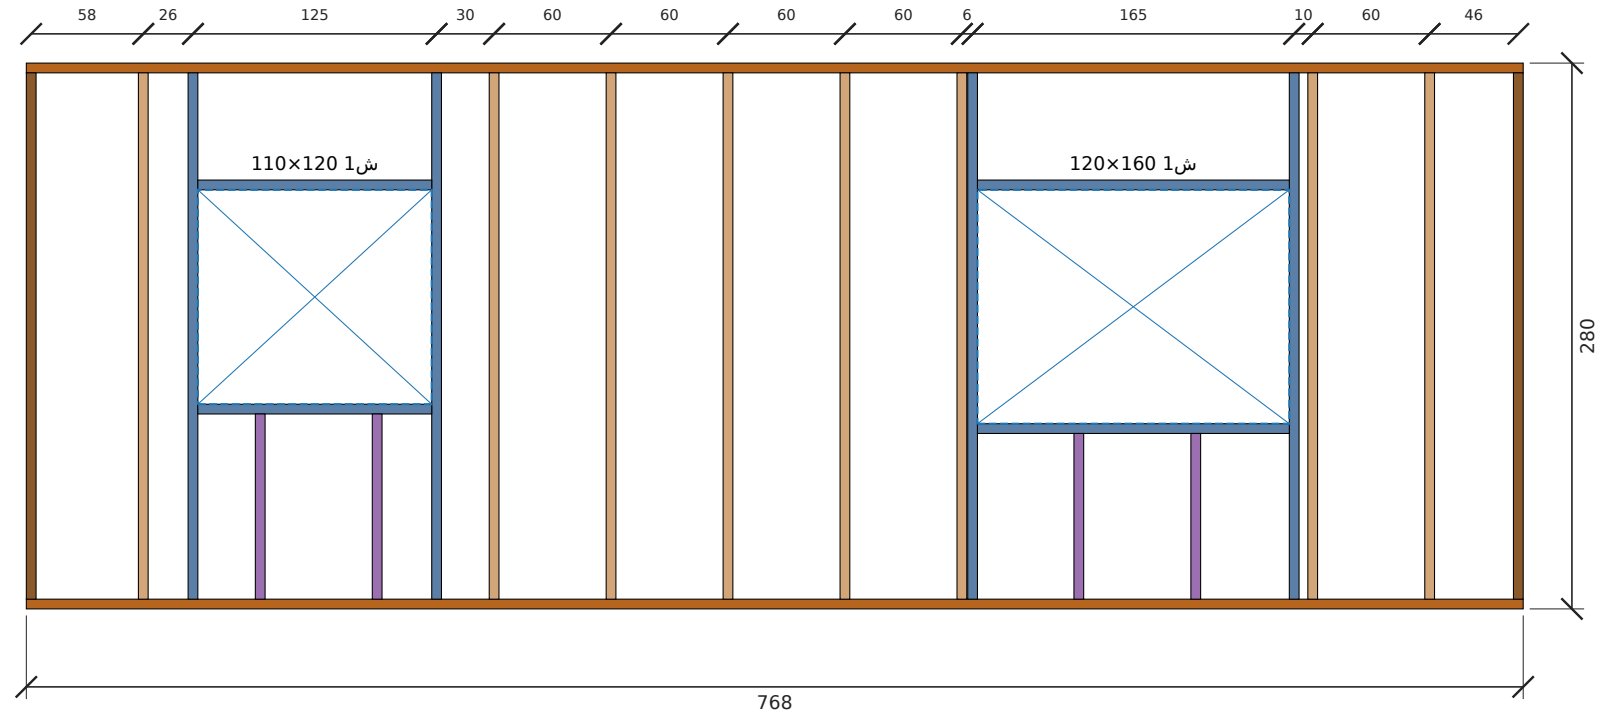

■ قاعدة سفلية
 ■ علوي
 ■ عمود
 ■ عمود زاوية
 ■ جنب فتحة
 ■ رأس فتحة
 ■ جلسة شباك
 ■ عمود قصير

رقم اللوحة

W-10 (10/20)

التاريخ

2026-09-29

المقياس

—

عنوان اللوحة

لوحات التأطير (للورشة)


المشروع / العميل

كوخ دورين 3 غرف نوم — 120 م²
عميل جديد


مصنع وتد الأخشاب
Watad Wood Factory



تأطير جدار أ-فاصل الصالة — الطول 768 سم، الارتفاع 280 سم (داخلي)

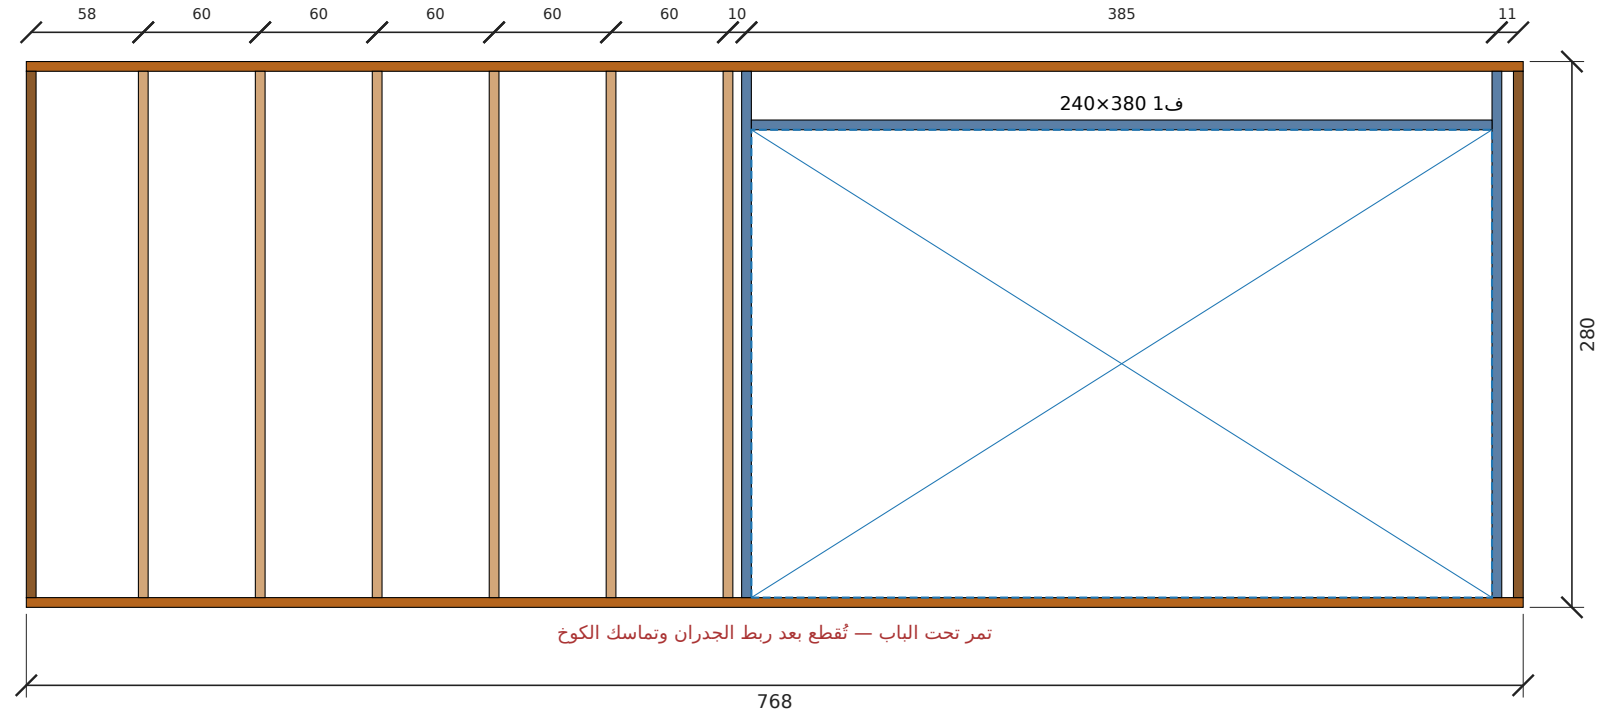

تأطير جدار أ-جدار غرفة 3 — الطول 366 سم، الارتفاع 280 سم (داخلي)

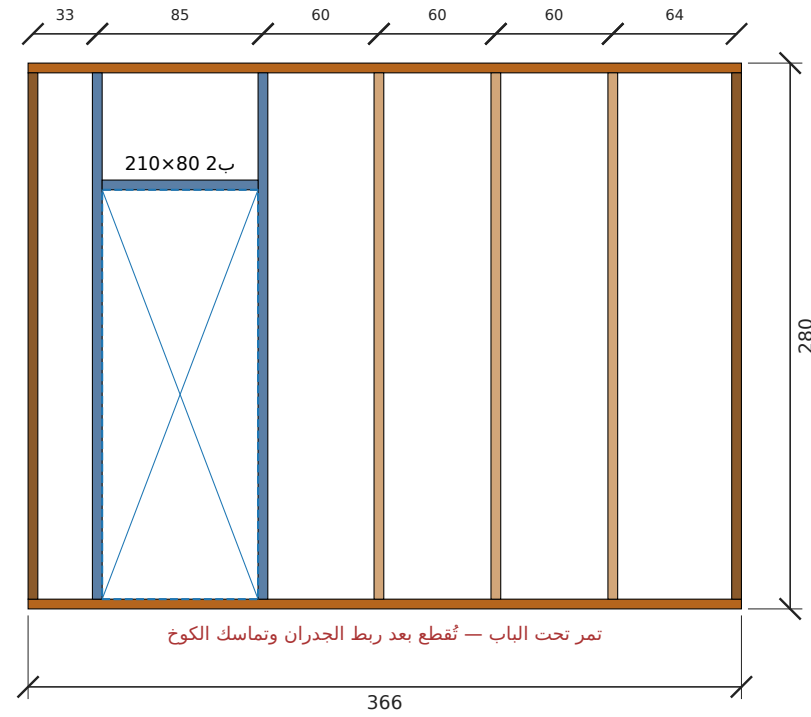

■ قاعدة سفلية
 ■ علوي
 ■ عمود
 ■ عمود زاوية
 ■ جنب فتحة
 ■ رأس فتحة
 ■ جلسة شباك
 ■ عمود قصير

رقم اللوحة

W-11 (11/20)

التاريخ

2026-09-29

المقياس

—

عنوان اللوحة

لوحات التأطير (للورشة)


المشروع / العميل

كوخ دورين 3 غرف نوم — 120 م²
عميل جديد


مصنع وتد الأخشاب
Watad Wood Factory



تأطير جدار أ-حمام جنوب — الطول 162 سم، الارتفاع 280 سم (داخلي)

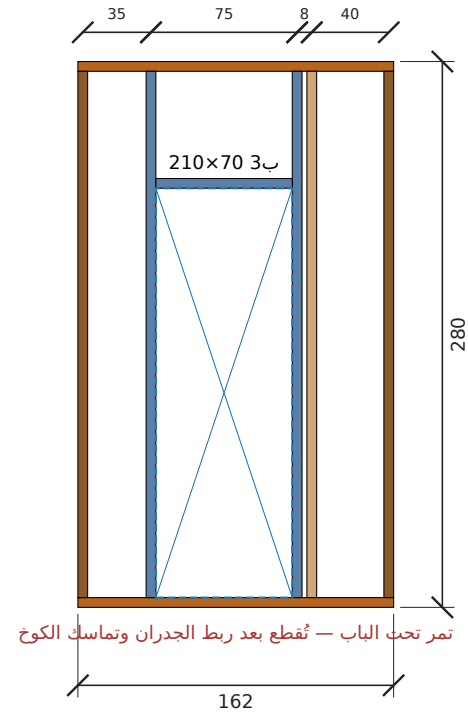

تأطير جدار أ-حمام شرق — الطول 212 سم، الارتفاع 280 سم (داخلي)

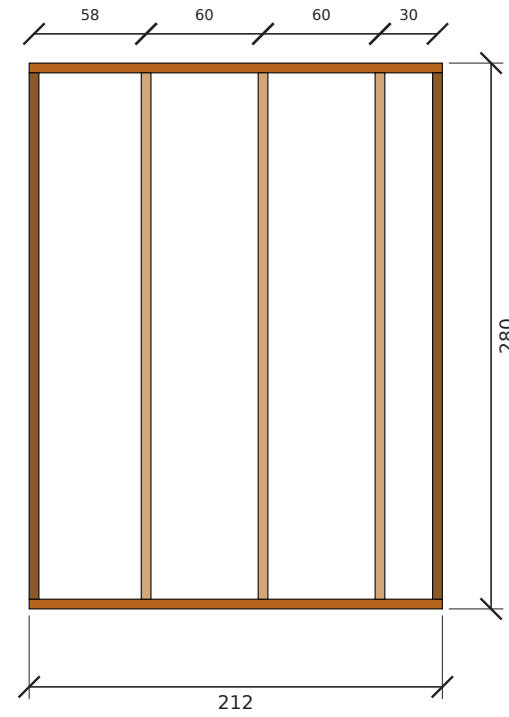

عمود قصير عمود زاوية عمود علوي قاعدة سفلية رأس فتحة جنب فتحة جلسة شباك

رقم اللوحة

W-12 (12/20)

التاريخ

2026-09-29

المقياس

—

عنوان اللوحة

لوحات التأطير (للورشة)


المشروع / العميل

كوخ دورين 3 غرف نوم — 120 م²
عميل جديد


مصنع وتد الأخشاب
Watad Wood Factory



تأطير جدار ب-جنوب — الطول 768 سم، الارتفاع 280 سم

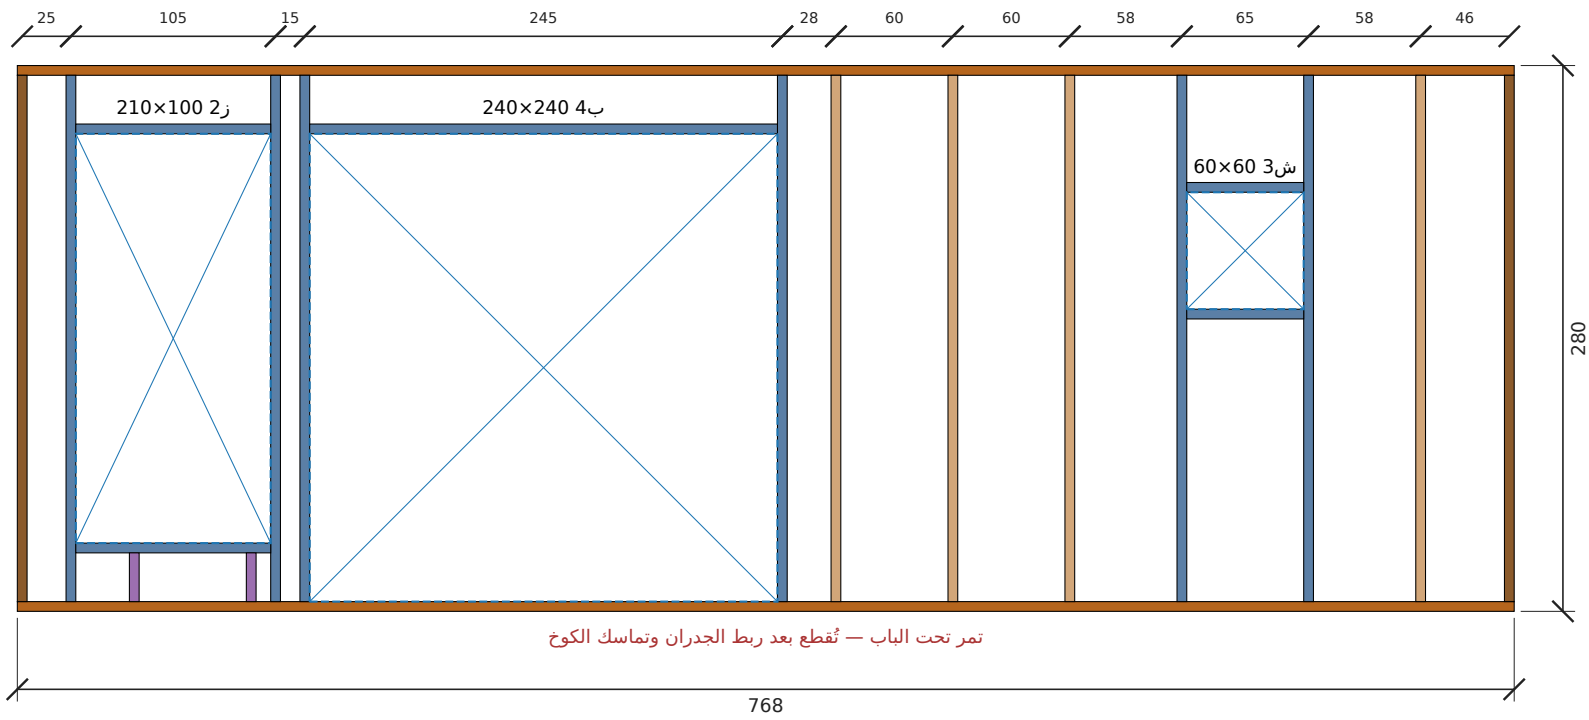


تأطير جدار ب-شرق — الطول 768 سم، الارتفاع 280 سم

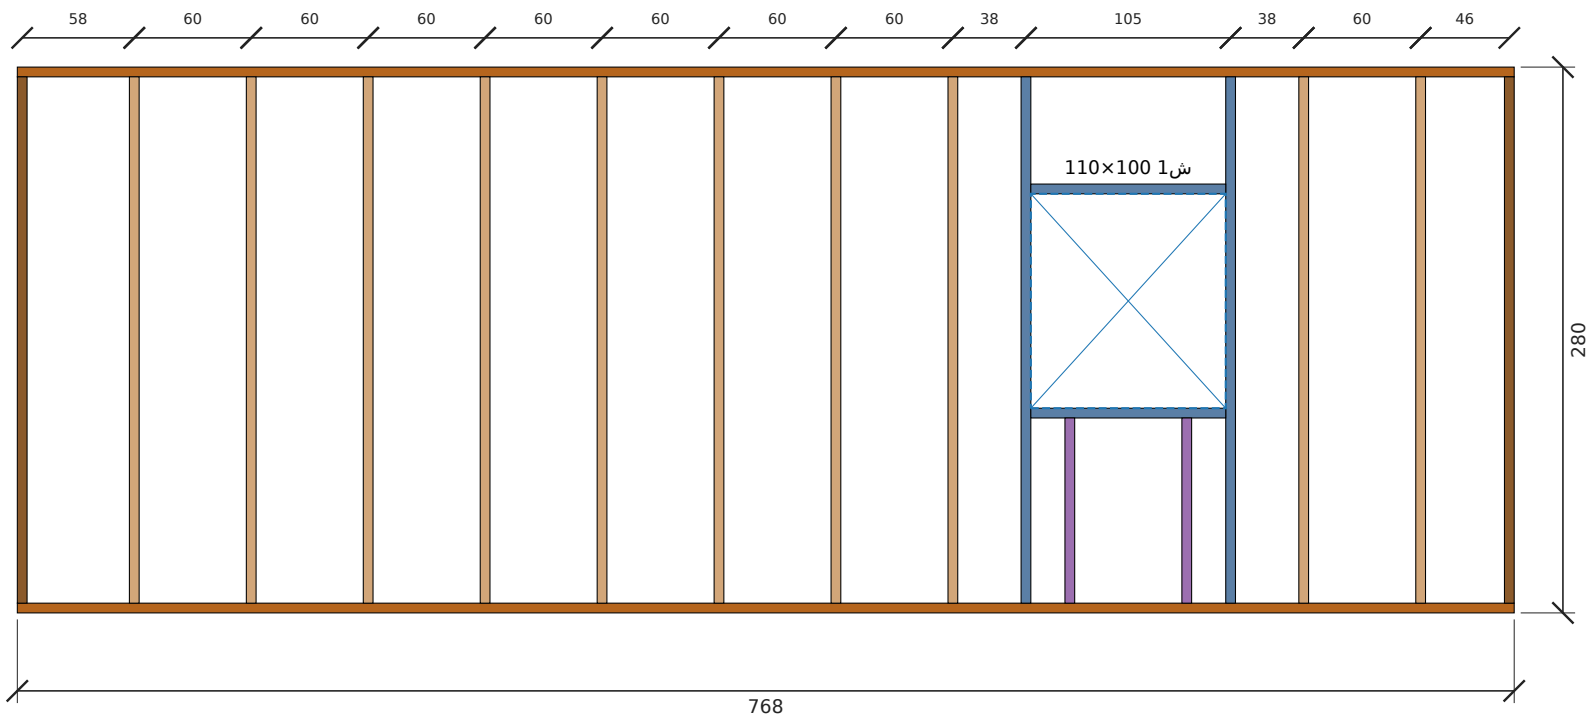


قاعدة سفلية علوي عمود عمود زاوية جنب فتحة رأس فتحة جلسة شباك عمود قصير

رقم اللوحة	التاريخ	المقياس	عنوان اللوحة	المشروع / العميل	مصنع وتد الأخشاب Watad Wood Factory
W-13 (13/20)	2026-09-29	—	لوحات التأطير (للورشة)	كوخ دورين 3 غرف نوم — 120 م ² عميل جديد	

تأطير جدار ب-شمال — الطول 768 سم، الارتفاع 280 سم

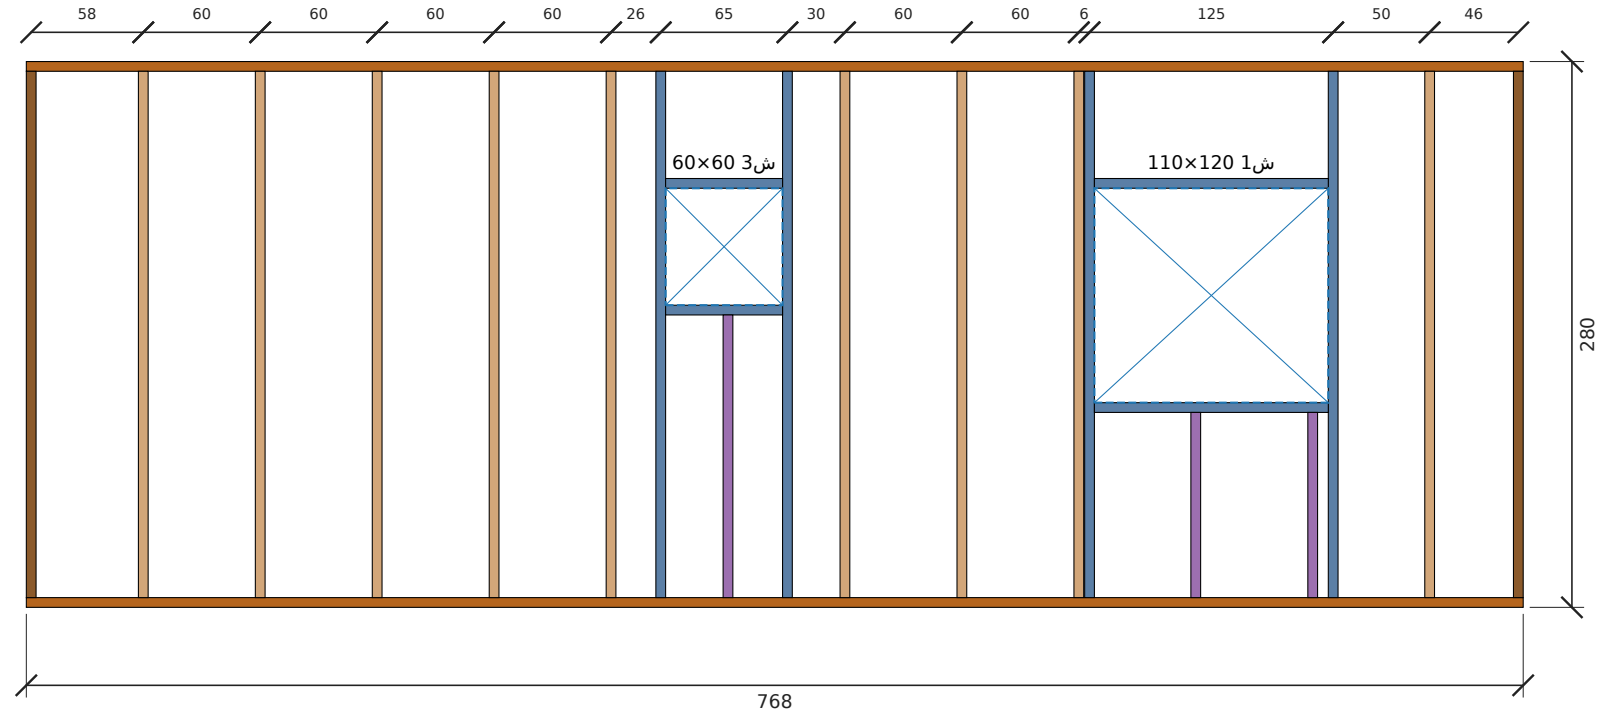

تأطير جدار ب-غرب — الطول 768 سم، الارتفاع 280 سم

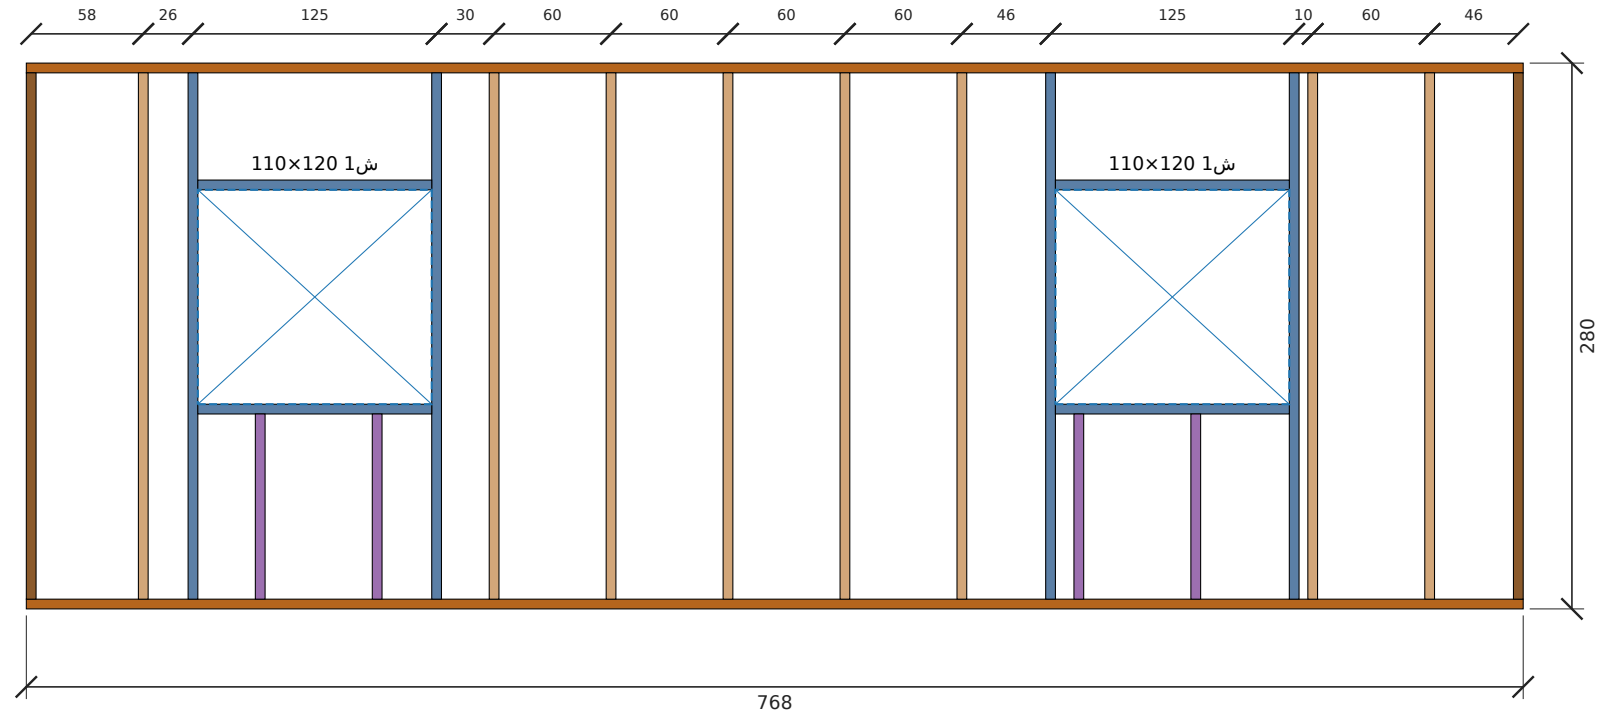

■ قاعدة سفلية
 ■ علوي
 ■ عمود
 ■ عمود زاوية
 ■ جنب فتحة
 ■ رأس فتحة
 ■ جلسة شباك
 ■ عمود قصير

رقم اللوحة

W-14 (14/20)

التاريخ

2026-09-29

المقياس

—

عنوان اللوحة

لوحات التأطير (للورشة)


المشروع / العميل

كوخ دورين 3 غرف نوم — 120 م²
عميل جديد


مصنع وتد الأخشاب
Watad Wood Factory



تأطير جدار ب-فاصل الماستر — الطول 768 سم، الارتفاع 280 سم (داخلي)

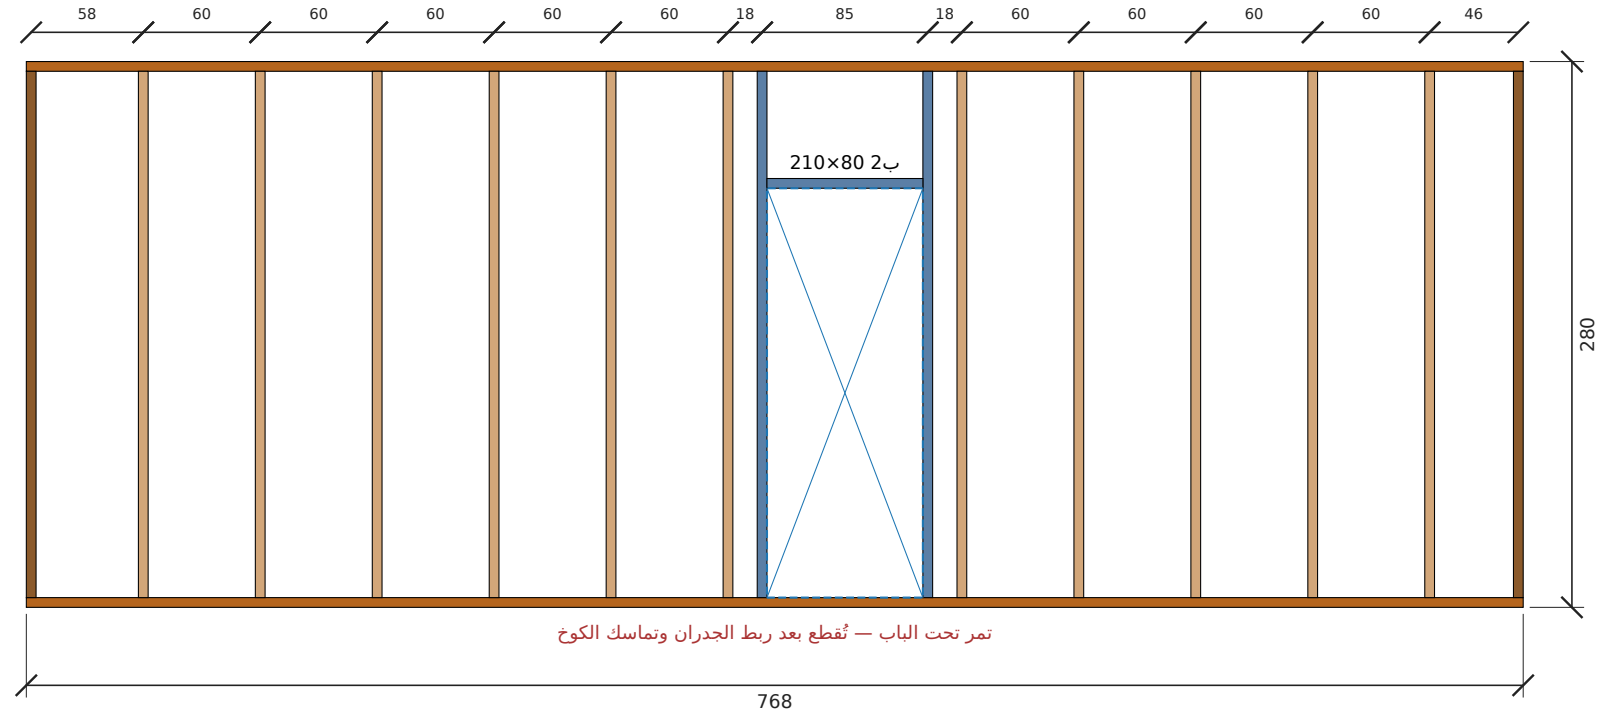

تأطير جدار ب-جدار غرفة 2 — الطول 444 سم، الارتفاع 280 سم (داخلي)

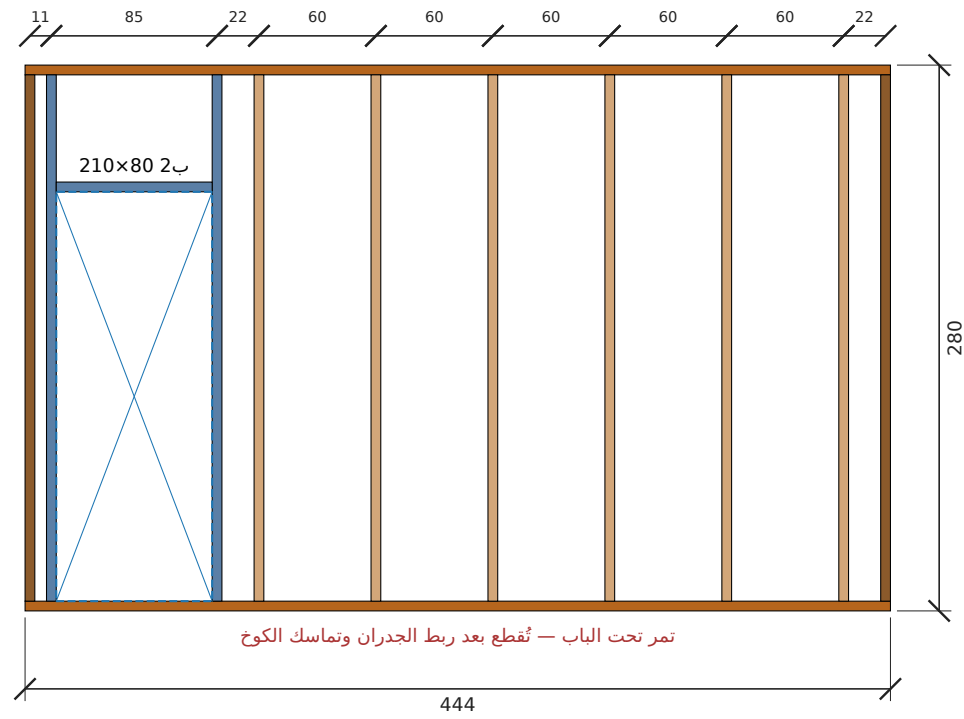

■ قاعدة سفلية
 ■ علوي
 ■ عمود
 ■ عمود زاوية
 ■ جنب فتحة
 ■ رأس فتحة
 ■ جلسة شباك
 ■ عمود قصير

رقم اللوحة

W-15 (15/20)

التاريخ

2026-09-29

المقياس

—

عنوان اللوحة

لوحات التأطير (للورشة)


المشروع / العميل

كوخ دورين 3 غرف نوم — 120 م²
عميل جديد


مصنع وتد الأخشاب
Watad Wood Factory



تأطير جدار ب-حمام جنوب — الطول 162 سم، الارتفاع 280 سم (داخلي)

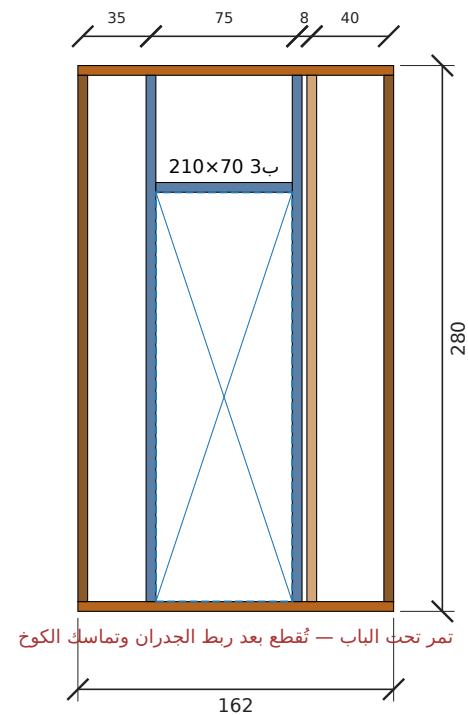


تأطير جدار ب-حمام شرق — الطول 212 سم، الارتفاع 280 سم (داخلي)

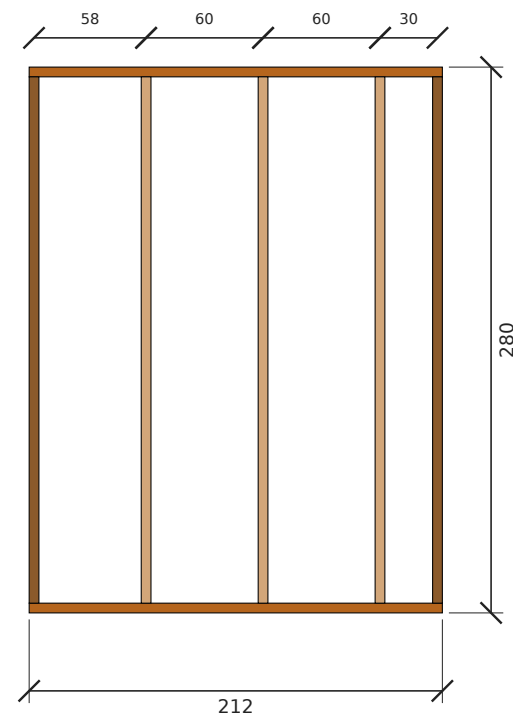


عمود قصير عمود زاوية عمود علوي قاعدة سفلية رأس فتحة جنب فتحة جلسة شباك

المشروع / العميل	كوخ دورين 3 غرف نوم — 120 م ² عميل جديد	عنوان اللوحة	لوحات التأطير (للورشة)	المقياس	—	التاريخ	2026-09-29	رقم اللوحة	W-16 (16/20)
------------------	---	--------------	------------------------	---------	---	---------	------------	------------	--------------

تأطير جدار ب-جناح الماستر — الطول 324 سم، الارتفاع 280 سم (داخلي)

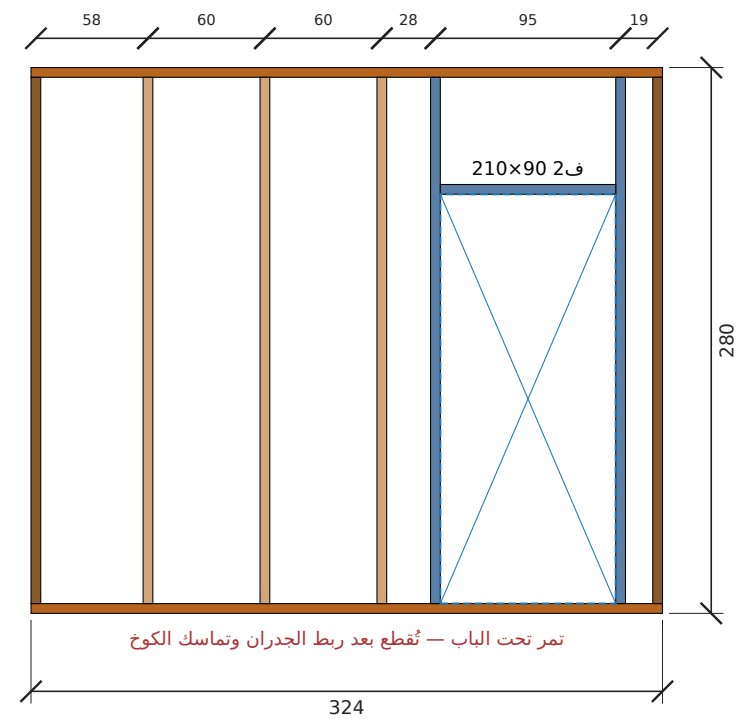

تأطير جدار ب-حمام الماستر — الطول 276 سم، الارتفاع 280 سم (داخلي)

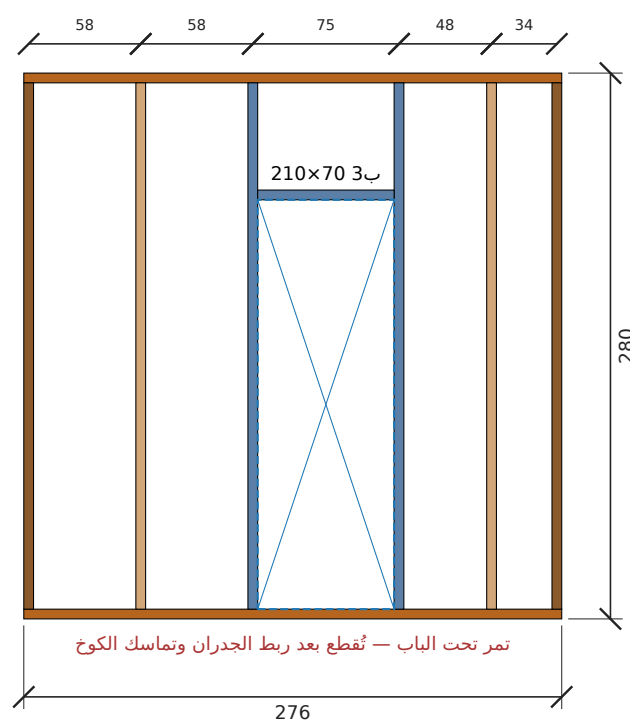

عمود قصير جلسة شباك رأس فتحة جنب فتحة عمود زاوية عمود علوي قاعدة سفلية

المشروع / العميل	عنوان اللوحة	المقياس	التاريخ	رقم اللوحة	م مصنع وتد الأخشاب Watad Wood Factory
كوخ دورين 3 غرف نوم — 120 م ² عميل جديد	لوحات التأطير (للورشة)	—	2026-09-29	W-17 (17/20)	

جدول الكميات وخطة تقطيع الطبلیات

البند	القيمة
الارتفاع المطلوب / المعتمد	280 / 280 سم
السقف	جملون 25° — قمة 767 سم من وجه الصبة
المدادات 15×5	38 مداد (19 لكل جهة) × 474 سم — من طبلية 480
طبلیات الطريقة الأولى (مداد + عمود)	38 طبلية × 480 سم
طبلیات الطريقة الثانية (3 أعمدة)	68 طبلية × 320 سم
طبلیات الطريقة الثانية (طويلة)	3 طبلية × 480 سم
جسور أرضية الدور العلوي 15×5 كل 40 سم	60 جسر — 172سم×20، 280سم×20، 346سم×20 (طبلية 480 بالطريقة الأولى)
إجمالي الطبلیات 22.5×5	169
إجمالي قطع 5×7	278
قائمة تقطيع 5×7	768سم×20 444سم×2 380سم×1 366سم×2 324سم×2 300سم×1 276سم×2 270سم×181 240سم×1
	212سم×4 162سم×4 160سم×2 145سم×2 140سم×4 120سم×12 105سم×1 100سم×4 95سم×12
ألواح تلبیس 2.5 سم	506 لوح × 400 سم (مجموع الصفوف 1999.4 م، 36 وجه)
أسمنت بورد 12 مم (244×122)	52 لوح (داخل دورات المياه)
العزل	بدون (غير مطلوب)

جدول الكميات وخطة تقطيع الطبليات

القيمة	البند
يجهزها العميل — 20 سم، مفرغة تحت دورات المياه	الصبة

مراجعة التصميم مقابل قواعد المصنع

النوع	البند	التفاصيل	المقترح
ملاحظة	حمام الماستر غير مكّسّ	دورة المياه العلوية ليست فوق دورة مياه أرضية — تحتاج خط صرف خارجي مستقل على الجدار.	يُفضّل تكديس الحمامات فوق بعض (قاعدة المصنع).
ملاحظة	بحر المدادات	أطول بحر بدون جدار داخلي يحمل المداد: جهة أ: 390 سم، جهة ب: 390 سم. يحتاج رقم المصنع لأقصى بحر مسموح لتحديد المدادات اللي تُقوّى 5×20.	
ملاحظة	الصبة والدرج	ارتفاع الصبة 45 سم ← 3 درجة بقائمة 15.0 سم.	
ملاحظة	مناسيب رؤوس الفتحات	رؤوس الأبواب والشبابيك على مناسيب مختلفة: 210، 240، 265 سم.	
سؤال	يحتاج تأكيد	أقصى بحر للمداد بدون جدار داخلي قبل إضافة تقوية 5×7 (مداد 5×20)؟	
سؤال	يحتاج تأكيد	التغطية الصافية للوح التليس بعد التعشيق (مستنتجة مؤقتاً 18.67 سم من 280/15)؟	
سؤال	يحتاج تأكيد	هل يوضع أعمدة قصيرة فوق رأس الشباك/الباب إلى العلوي؟	
سؤال	يحتاج تأكيد	مكان الوصلة في القاعدة والعلوي إذا الجدار أطول من الطلية؟	
سؤال	يحتاج تأكيد	جسور أرضية الدور العلوي: المقطع 5×15 والتباعد 40 سم مفترض — ما المعتمد عندكم؟	