


## المنظور ثلاثي الأبعاد والمواد

النمط: جوزي غامق + إطارات سوداء — رندر واقعي بخامات حقيقية

### جدول المواد والألوان

 

**الخشب / الصبغة**  
خشب طبيعي فاتح (بدون صبغة)



**القرميد**  
قرميد رمادي غامق



**الزجاج**  
زجاج عاكس غامق



**إطارات الشبابيك والأبواب**  
إطار ألومنيوم أسود



**الكنار والزوايا**  
نفس الصبغة أعمق درجة



**الصبة**  
خرسانة 45 سم


الدريزين: ألواح أفقية متقاربة (عصري)

تقسيم الشبابيك: بدون | الباب الرئيسي: زجاج بتقسيمات (فرنسي)


### أنواع الدريزين المعتمدة (من مشاريع المصنع)



قوائم رأسية متقاربة (صورة 1)

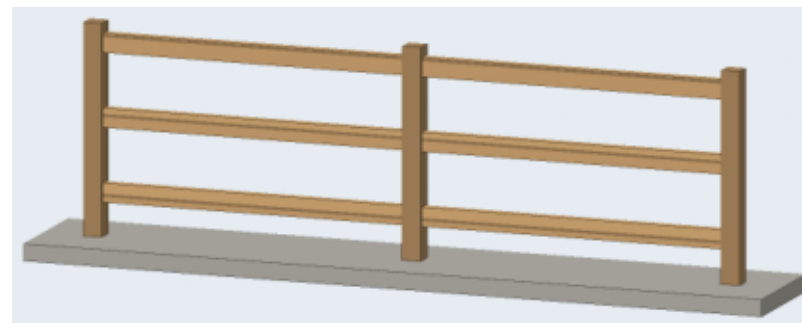

3 مربيع أفقية (صورة 2)

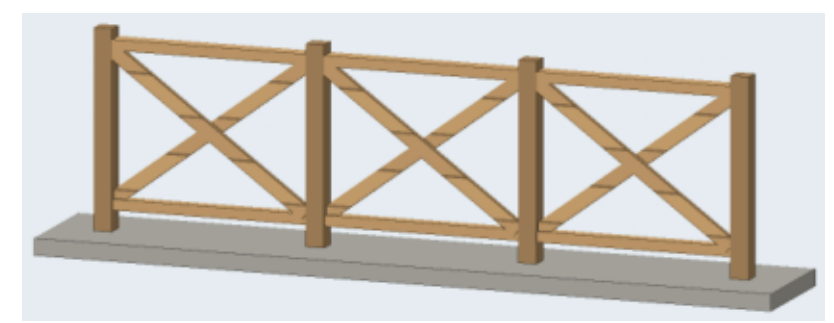

تقاطع X (صورة 5)

رقم اللوحة

W-01 (1/11)

التاريخ

2026-10-01

المقياس

1:50

عنوان اللوحة

المنظور والمواد

المشروع / العميل


غرفة 4x4 بسقف مانل  
عميل — غرفة مستقلة

مصنع وتد الأخشاب  
Watad Wood Factory




## المسقط الأفقي مع الفرش

الأبعاد بالسنتيمتر - الجدران: قوائم 5×7 + تليس 2.5 من الجهتين (12 سم)

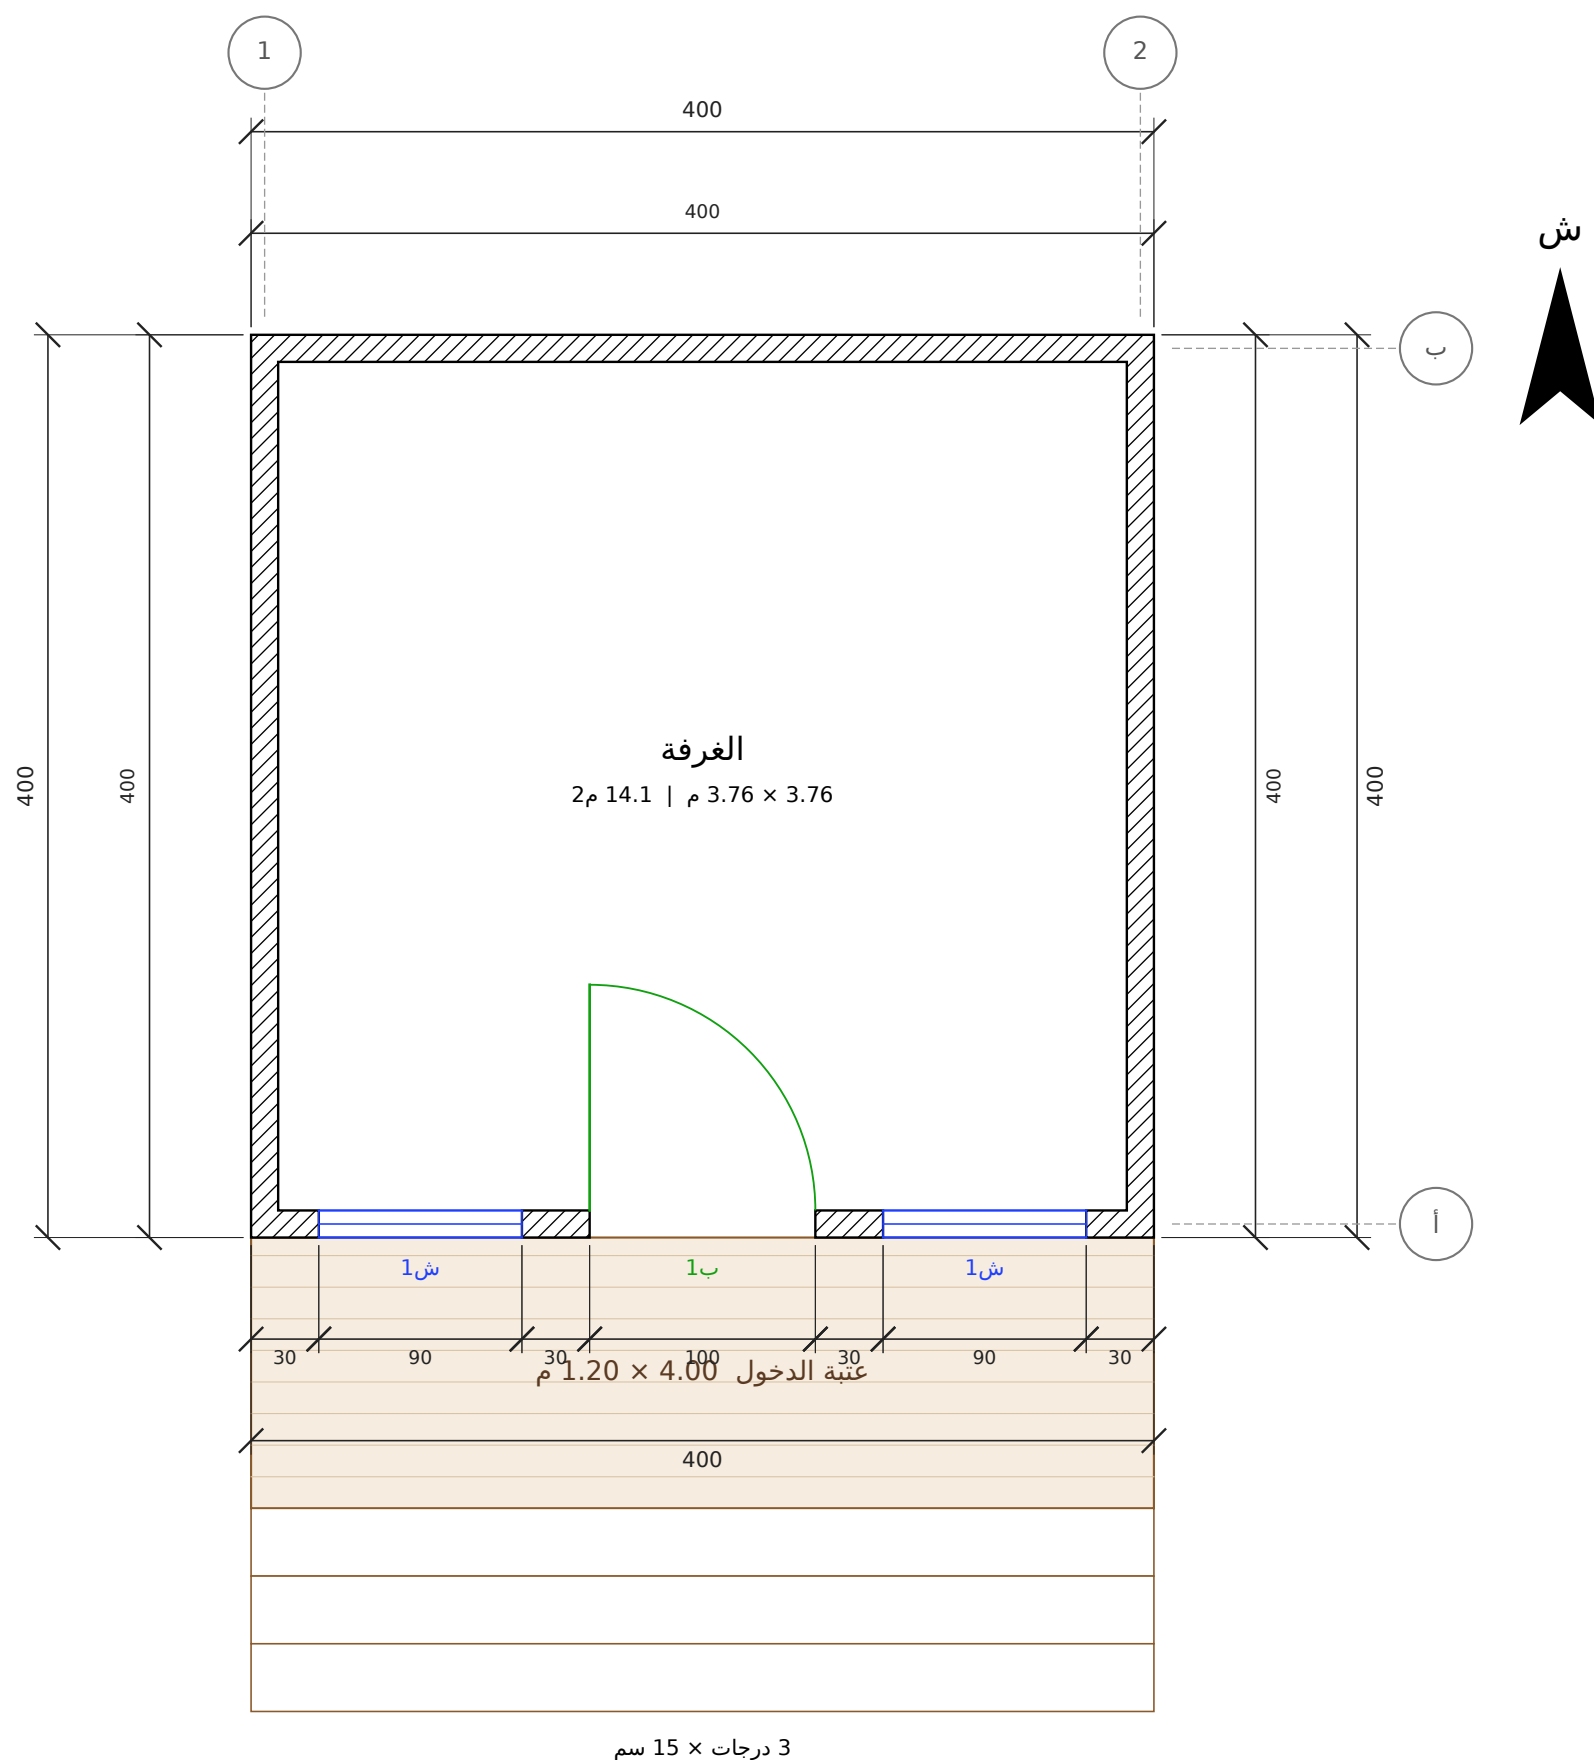


|                                        |                                         |               |            |             |
|----------------------------------------|-----------------------------------------|---------------|------------|-------------|
| المشروع / العميل                       | عنوان اللوحة                            | المقياس       | التاريخ    | رقم اللوحة  |
| مصنع وتد الأخشاب<br>Watad Wood Factory | غرفة 4×4 بسقف مائل<br>عمل — غرفة مستقلة | المسقط الأفقي | 2026-10-01 | W-02 (2/11) |

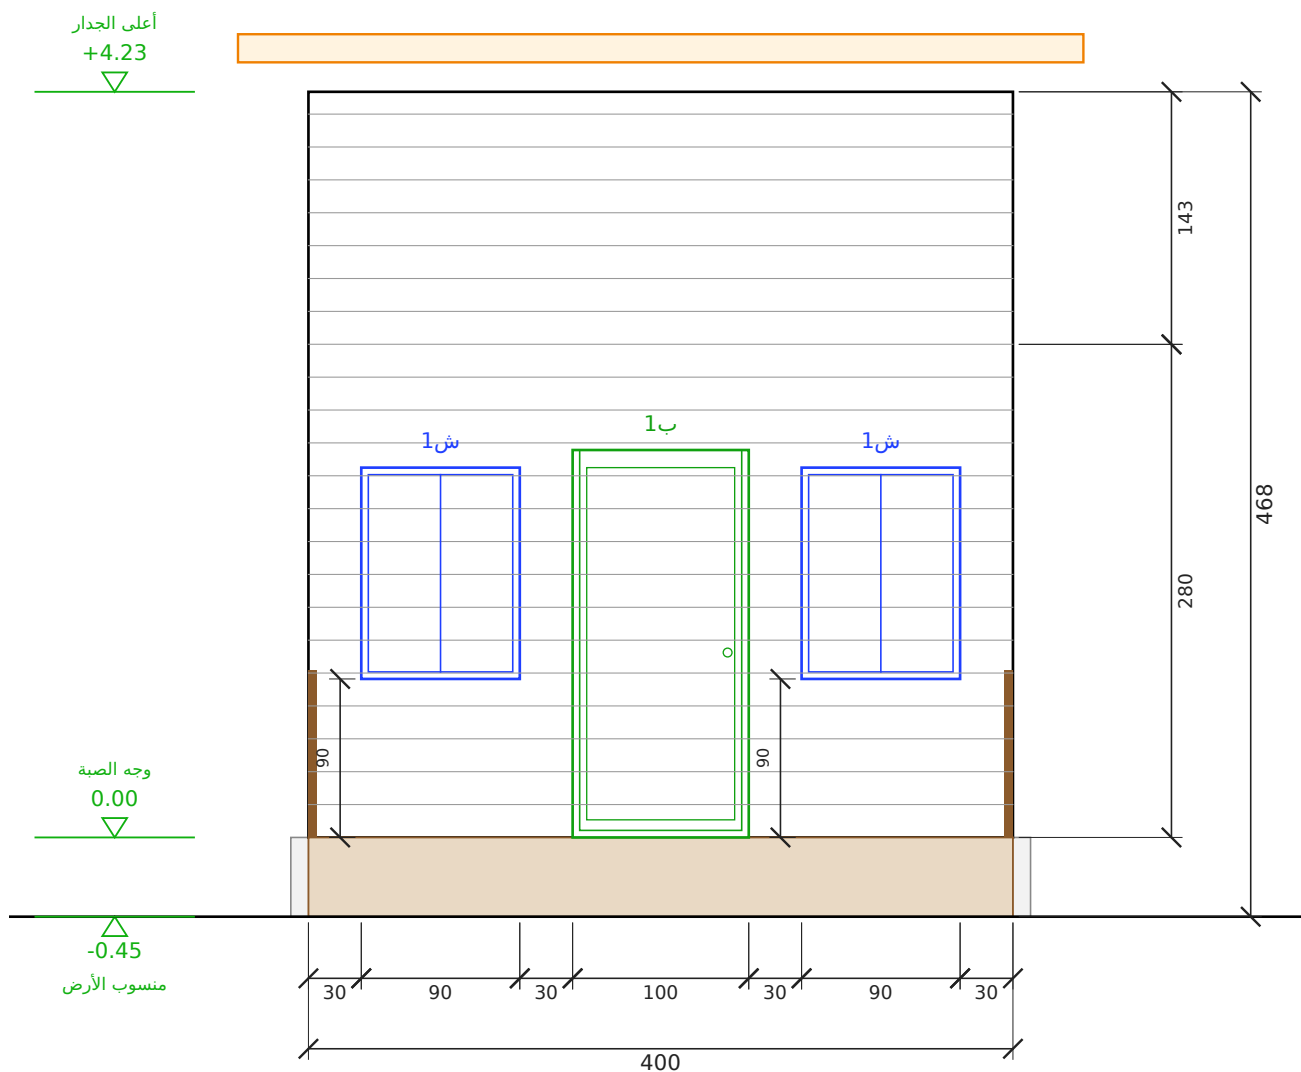

### الواجهة الأمامية


مقياس 1:50 | الوحدة: سم

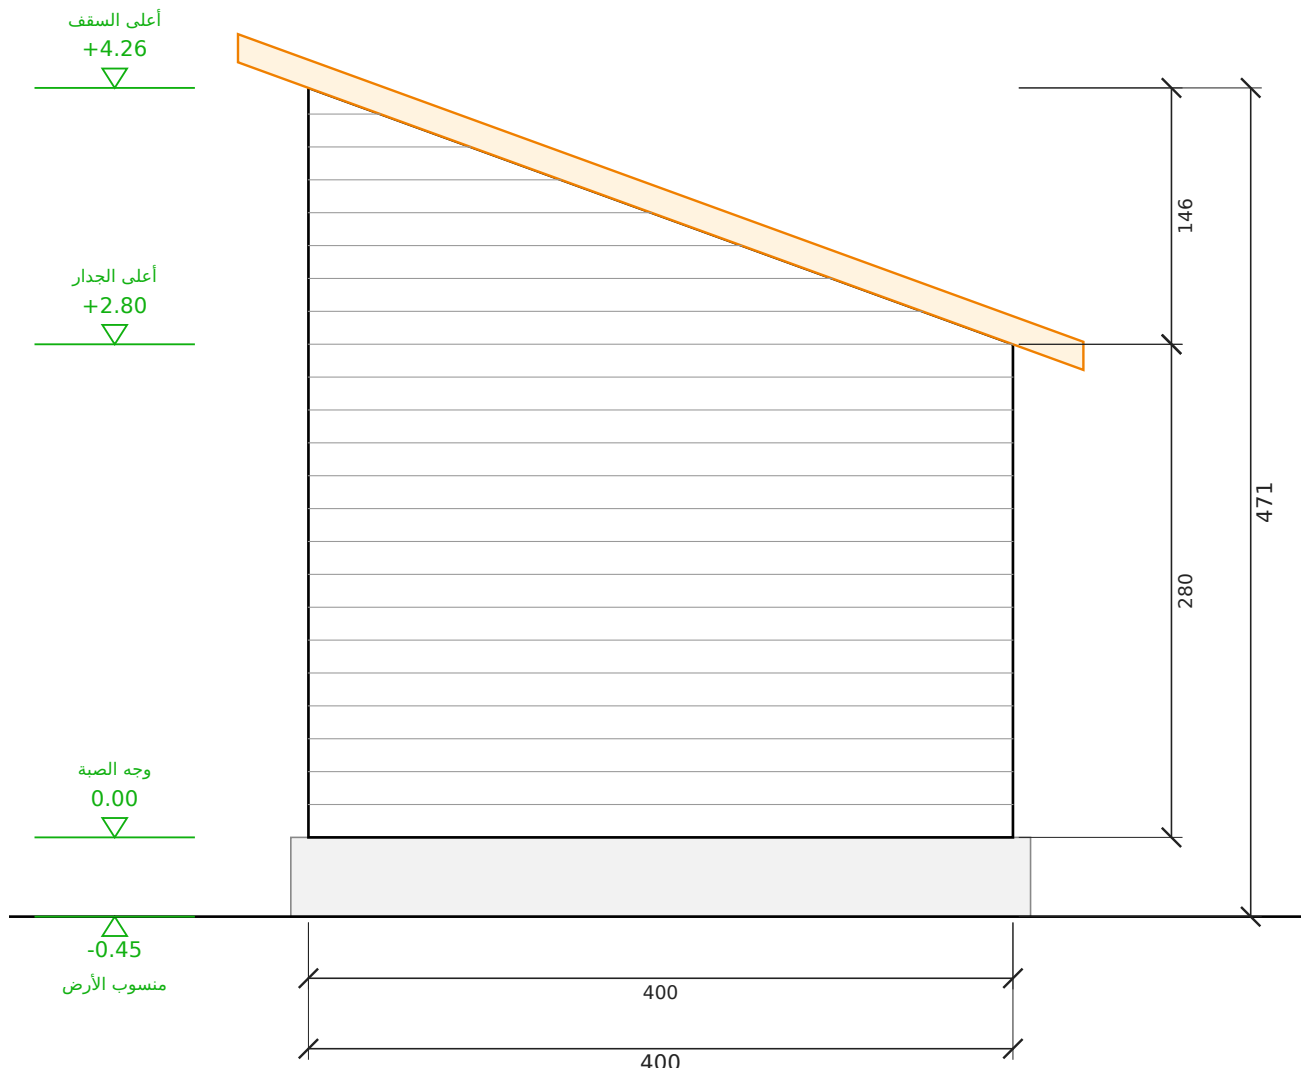

### الواجهة الشرقية


مقياس 1:50 | الوحدة: سم

| رقم اللوحة  | التاريخ    | المقياس | عنوان اللوحة                      | المشروع / العميل                         | مصنع وتد الأخشاب<br>Watad Wood Factory |
|-------------|------------|---------|-----------------------------------|------------------------------------------|----------------------------------------|
| W-03 (3/11) | 2026-10-01 | 1:50    | الواجهة الأمامية والواجهة الشرقية | غرفة 4x4 بسقف مائل<br>عميل - غرفة مستقلة |                                        |

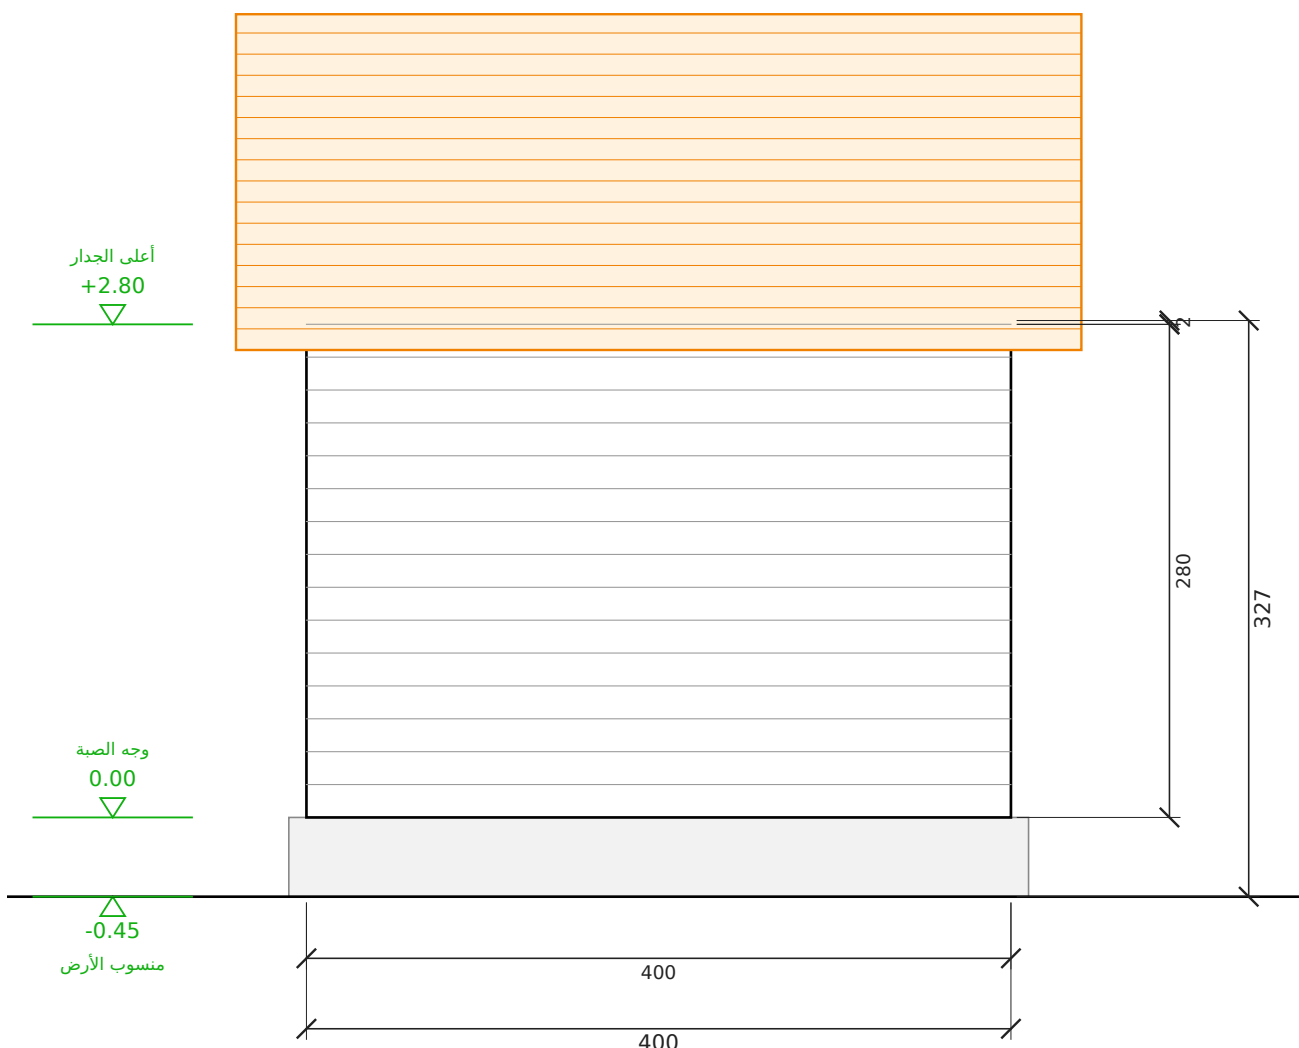

### الواجهة الخلفية

مقياس 1:50 | الوحدة: سم

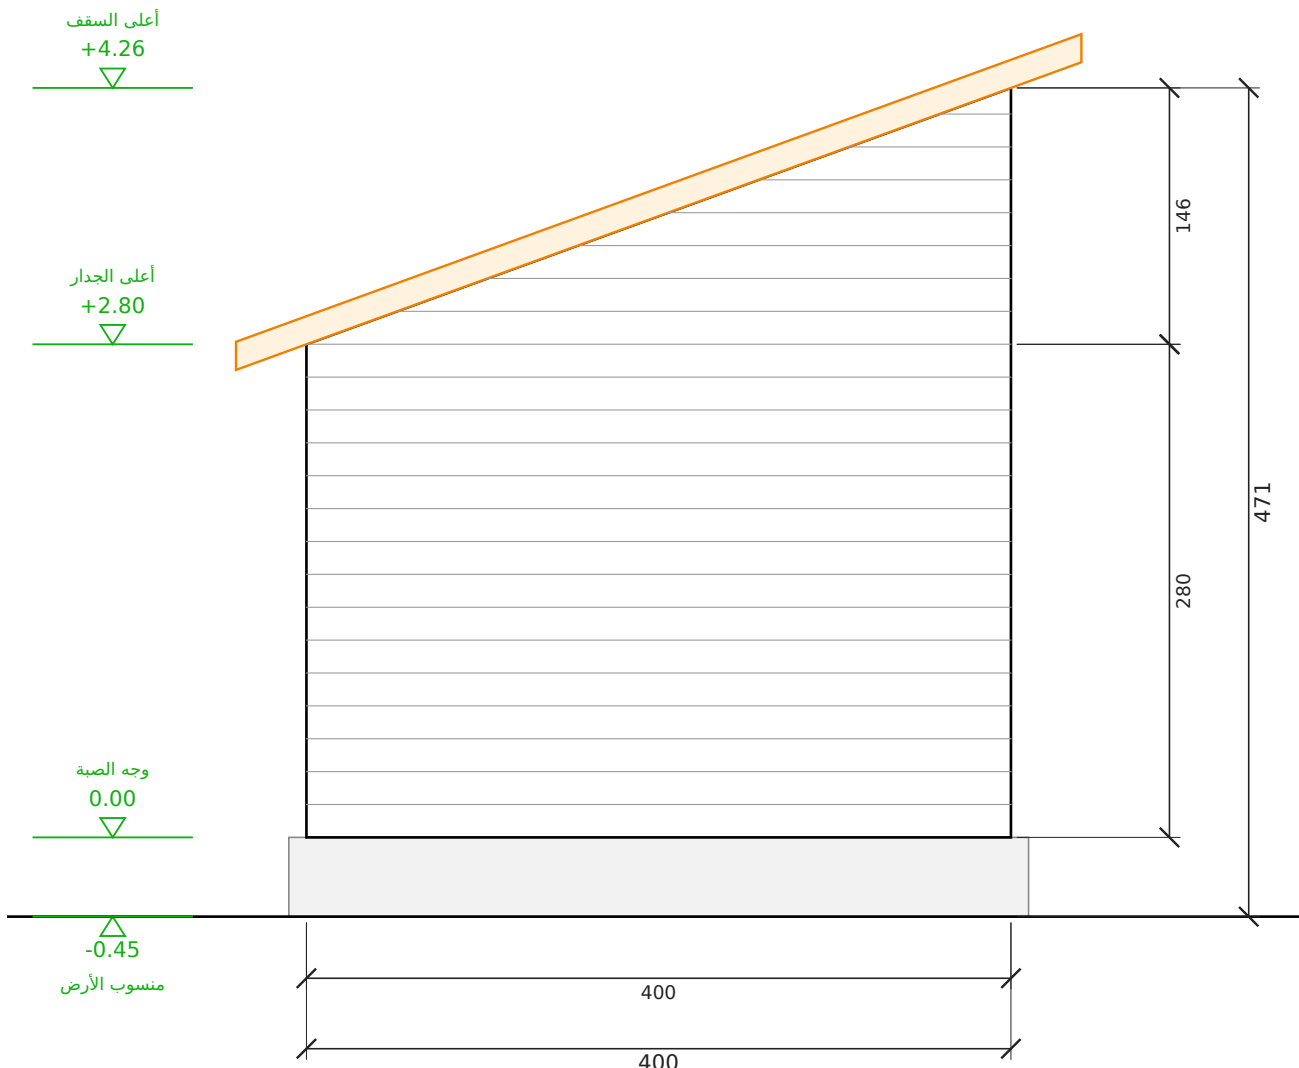


### الواجهة الغربية


مقياس 1:50 | الوحدة: سم

| رقم اللوحة  | التاريخ    | المقياس | عنوان اللوحة                     | المشروع / العميل                         | مصنع وتد الأخشاب<br>Watad Wood Factory |
|-------------|------------|---------|----------------------------------|------------------------------------------|----------------------------------------|
| W-04 (4/11) | 2026-10-01 | 1:50    | الواجهة الخلفية والواجهة الغربية | غرفة 4x4 بسقف مائل<br>عميل - غرفة مستقلة |                                        |


مسقط السقف (مائل باتجاه واحد)  
رفر 40 سم من كل جهة | مقياس 1:50

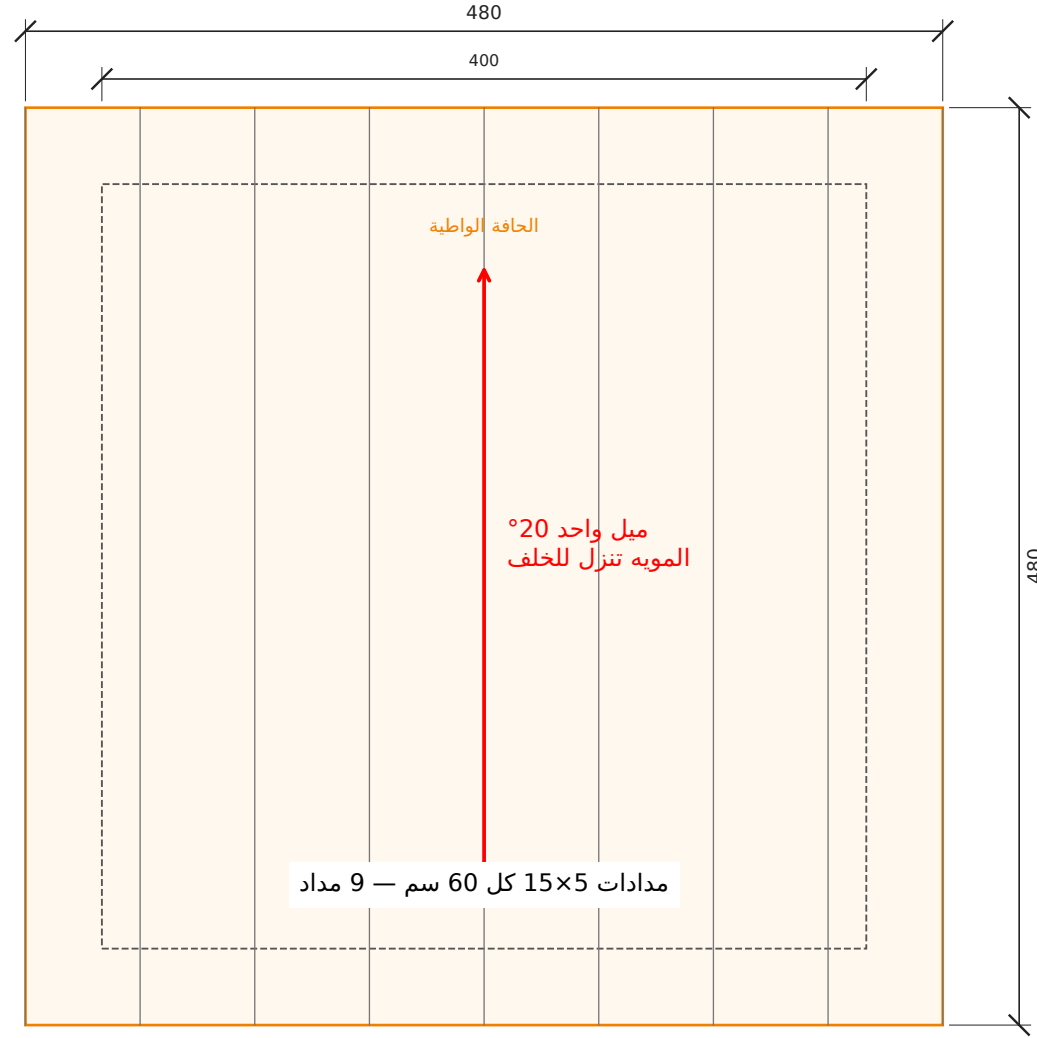

قطاع عرضي أ-أ  
مقياس 1:50 | الوحدة: سم

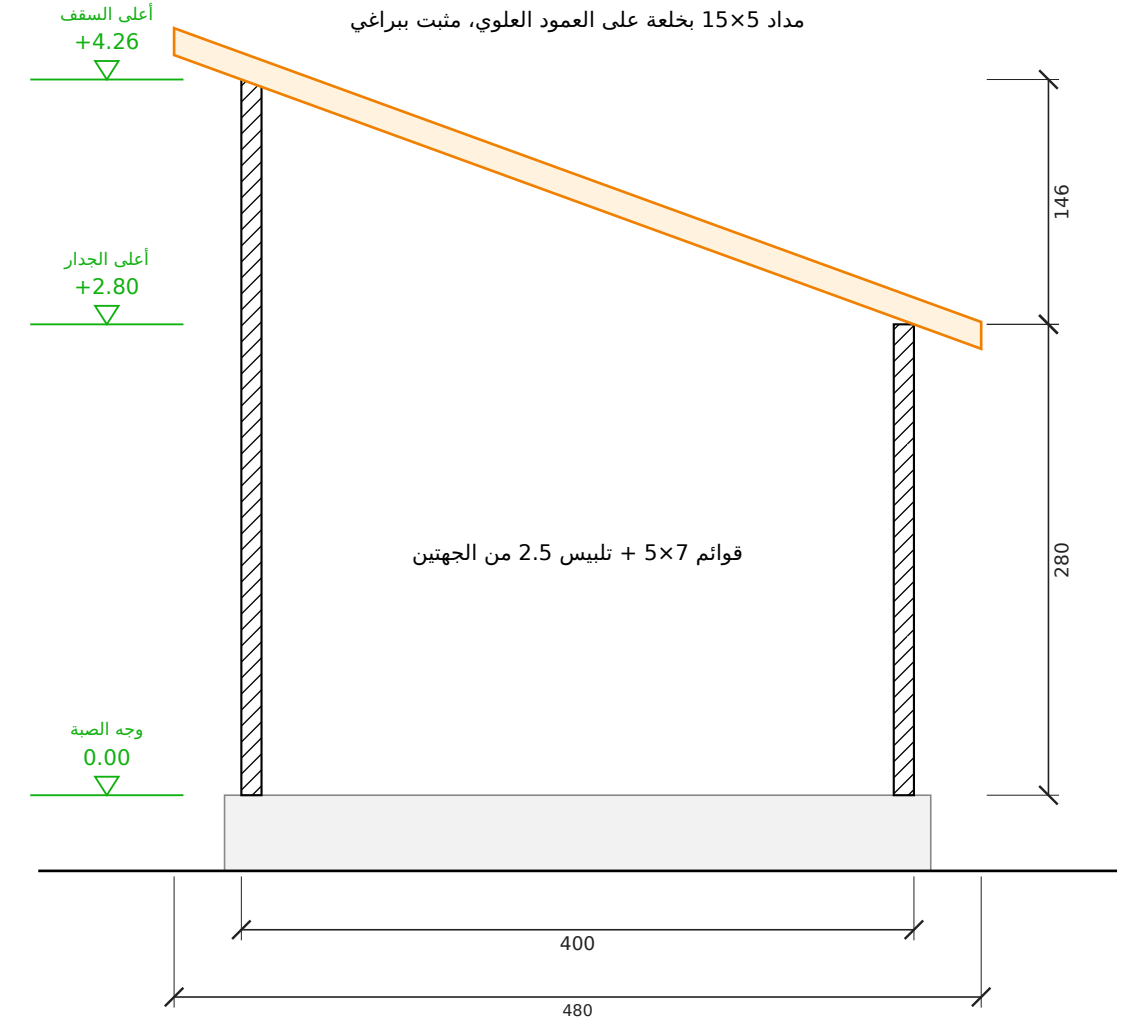

تفصيلة جلوس المدا على العلوي (1:5)

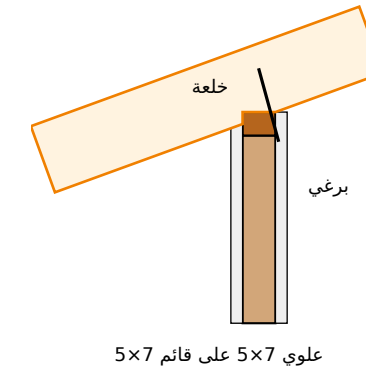

رقم اللوحة

W-05 (5/11)

التاريخ

2026-10-01

المقياس

1:50

عنوان اللوحة

مسقط السقف والقطاع

المشروع / العميل

غرفة 4×4 بسقف مائل  
عميل — غرفة مستقلة

مصنع وتد الأخشاب  
Watad Wood Factory



جدول مقاسات الأبواب والشبابيك  
مقاس الفتحة الصافي في الجدار - الوحدة: سم

| الرمز | النوع | العرض (سم) | الارتفاع (سم) | ارتفاع الجلسة (سم) | العدد | الموقع     |
|-------|-------|------------|---------------|--------------------|-------|------------|
| ب1    | باب   | 100        | 220           | -                  | 1     | الأمامية   |
| ش1    | شباك  | 90         | 120           | 90                 | 2     | الأمامية 2 |

الإجمالي: أبواب 1 - شبابيك 2

جدول المساحات وبيانات المشروع والتسعير

جدول المساحات

| م | الفراغ                    | الأبعاد (م) | المساحة (م2) |
|---|---------------------------|-------------|--------------|
| 1 | الغرفة                    | 3.76 × 3.76 | 14.14        |
|   | المساحة الصافية الداخلية  |             | 14.14        |
|   | التراس المسقوف (مجاناً)   | 4.00 × 1.20 | 4.80         |
|   | المساحة الإجمالية المبنية | 4.00 × 4.00 | 16.00        |

بيانات المشروع

| البند       | البيان                                |
|-------------|---------------------------------------|
| المشروع     | غرفة 4×4 بسقف مائل                    |
| العميل      | عميل — غرفة مستقلة                    |
| الموقع      | —                                     |
| الاستخدام   | غرفة / استراحة                        |
| التاريخ     | 2026-10-01                            |
| نظام البناء | هيكل خشب 5×7 + تليس 2.5 سم من الجهتين |
| السقف       | مائل باتجاه واحد 20° — قرميد معدني    |


التسعير

| البند                               | القيمة      |
|-------------------------------------|-------------|
| المساحة المبنية (م2)                | 16.00       |
| سعر المتر المربع — عرض اليوم الوطني | 1,096 ريال  |
| الإجمالي                            | 17,536 ريال |


ملاحظات:

- السعر للمساحة المبنية حسب المخطط المعتمد.
- الصبة والتوريدات الخارجية على العميل ما لم يُذكر غير ذلك.

تأطير جدار جنوب — الطول 388 سم، الارتفاع 426 سم

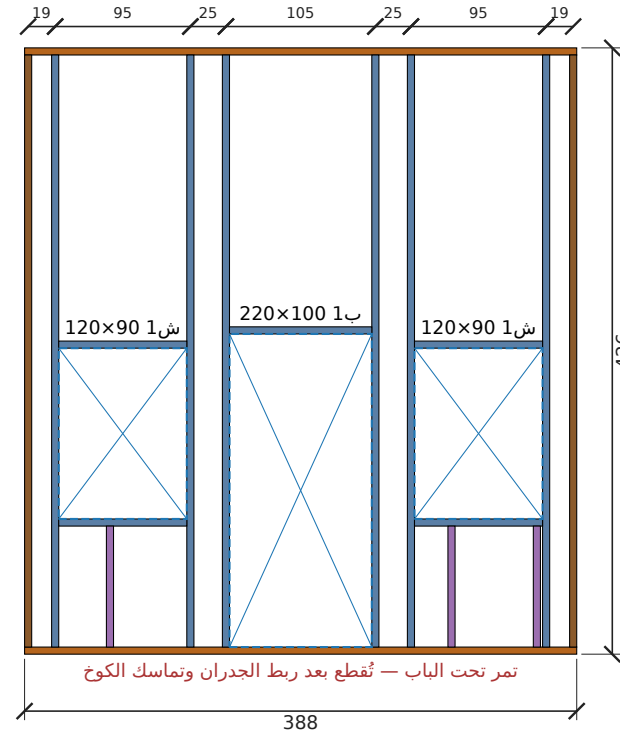


تأطير جدار شرق — الطول 388 سم، الارتفاع 280 سم

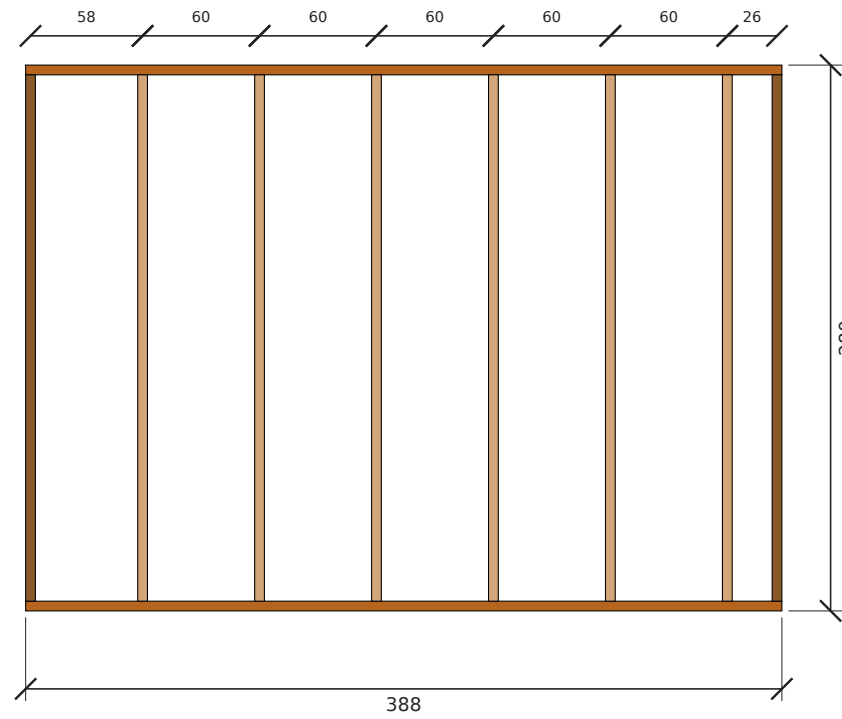


■ عمود قصير
 ■ جلسة شباك
 ■ رأس فتحة
 ■ جنب فتحة
 ■ عمود زاوية
 ■ عمود
 ■ علوي
 ■ قاعدة سفلية

|                                          |                        |         |            |             |                                        |
|------------------------------------------|------------------------|---------|------------|-------------|----------------------------------------|
| المشروع / العميل                         | عنوان اللوحة           | المقياس | التاريخ    | رقم اللوحة  | مصنع وتد الأخشاب<br>Watad Wood Factory |
| غرفة 4×4 بسقف مائل<br>عميل — غرفة مستقلة | لوحات التأطير (للورشة) | —       | 2026-10-01 | W-08 (8/11) |                                        |

تأطير جدار شمال — الطول 388 سم، الارتفاع 280 سم

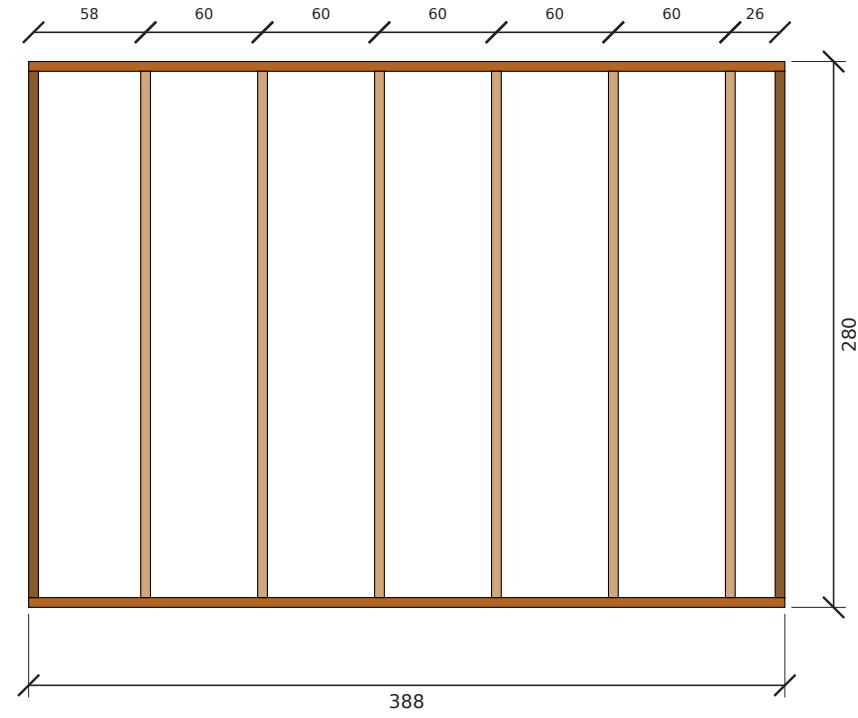

تأطير جدار غرب — الطول 388 سم، الارتفاع 280 سم

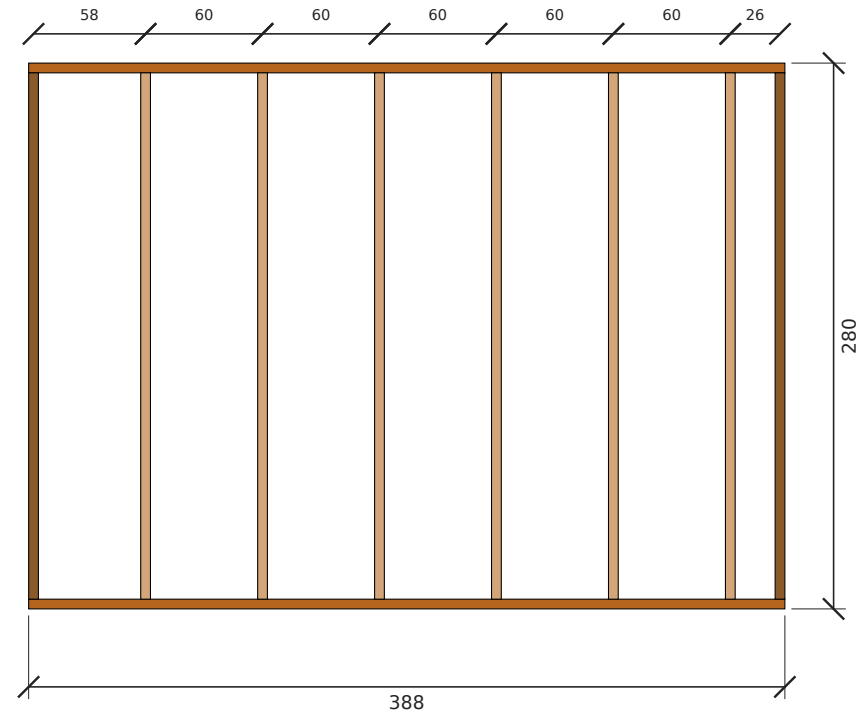

عمود قصير عمود زاوية علوي قاعدة سفلية رأس فتحة جنب فتحة جلسة شباك

|                                          |                        |         |            |             |                                        |
|------------------------------------------|------------------------|---------|------------|-------------|----------------------------------------|
| المشروع / العميل                         | عنوان اللوحة           | المقياس | التاريخ    | رقم اللوحة  | مصنع وتد الأخشاب<br>Watad Wood Factory |
| غرفة 4×4 بسقف مائل<br>عميل — غرفة مستقلة | لوحات التأطير (للورشة) | —       | 2026-10-01 | W-09 (9/11) |                                        |

جدول الكميات وخطة تقطيع الطبلیات

| البند                               | القيمة                                                   |
|-------------------------------------|----------------------------------------------------------|
| الارتفاع المطلوب / المعتمد          | 280 / 280 سم                                             |
| السقف                               | جملون 20° — قمة 426 سم من وجه الصبة                      |
| المدادات 15×5                       | 9 مداد (9 لكل جهة) × 511 سم — من طبلية 520               |
| طبلیات الطريقة الأولى (مداد + عمود) | 9 طبلية × 520 سم                                         |
| طبلیات الطريقة الثانية (3 أعمدة)    | 8 طبلية × 320 سم                                         |
| طبلیات الطريقة الثانية (طويلة)      | 3 طبلية × 520 سم                                         |
| إجمالي الطبلیات 22.5×5              | 20                                                       |
| إجمالي قطع 5×7                      | 48                                                       |
| قائمة تقطيع 5×7                     | 416سم×8   388سم×8   270سم×24   100سم×1   90سم×4   85سم×3 |
| ألواح تلبیس 2.5 سم                  | 124 لوح × 400 سم (مجموع الصفوف 476.5 م، 8 وجه)           |
| أسمنت بورد 12 مم (244×122)          | 0 لوح (داخل دورات المياه)                                |
| العزل                               | بدون (غير مطلوب)                                         |
| الصبة                               | يجهزها العميل — 20 سم، مفرغة تحت دورات المياه            |

مراجعة التصميم مقابل قواعد المصنع

| النوع  | البند               | التفاصيل   | المقترح |
|--------|---------------------|---|---------|
| ملاحظة | بحر المدادات        | أطول بحر بدون جدار داخلي يحمل المداد: جهة أ: 400 سم.<br>يحتاج رقم المصنع لأقصى بحر مسموح لتحديد المدادات اللي تُقوّى 5×20. |         |
| ملاحظة | الصبة والدرج        | ارتفاع الصبة 45 سم ← 3 درجة بقائمة 15.0 سم.                                                                                |         |
| ملاحظة | مناسيب رؤوس الفتحات | رؤوس الأبواب والشبابيك على مناسيب مختلفة: 210، 220 سم.                                                                     |         |
| سؤال   | يحتاج تأكيد         | أقصى بحر للمداد بدون جدار داخلي قبل إضافة تقوية 5×7 (مداد 5×20)؟                                                           |         |
| سؤال   | يحتاج تأكيد         | التغطية الصافية للوح التليس بعد التعشيق (مستنتجة مؤقتاً 18.67 سم من 280/15)؟                                               |         |
| سؤال   | يحتاج تأكيد         | هل يوضع أعمدة قصيرة فوق رأس الشباك/الباب إلى العلوي؟                                                                       |         |
| سؤال   | يحتاج تأكيد         | مكان الوصلة في القاعدة والعلوي إذا الجدار أطول من الطيلية؟                                                                 |         |