


المسقط الأفقي مع الفرش

الأبعاد بالسنتيمتر - الجدران: قوائم 5×7 + تليس 2.5 من الجهتين (12 سم)




المشروع / العمل غرفة 4×4 بسقف مائل عمل — غرفة مستقلة	عنوان اللوحة المسقط الأفقي	المقياس 1:50	التاريخ 2026-10-01	رقم اللوحة A-01 (1/9)
--	--	----------------------------	----------------------------------	-------------------------------------

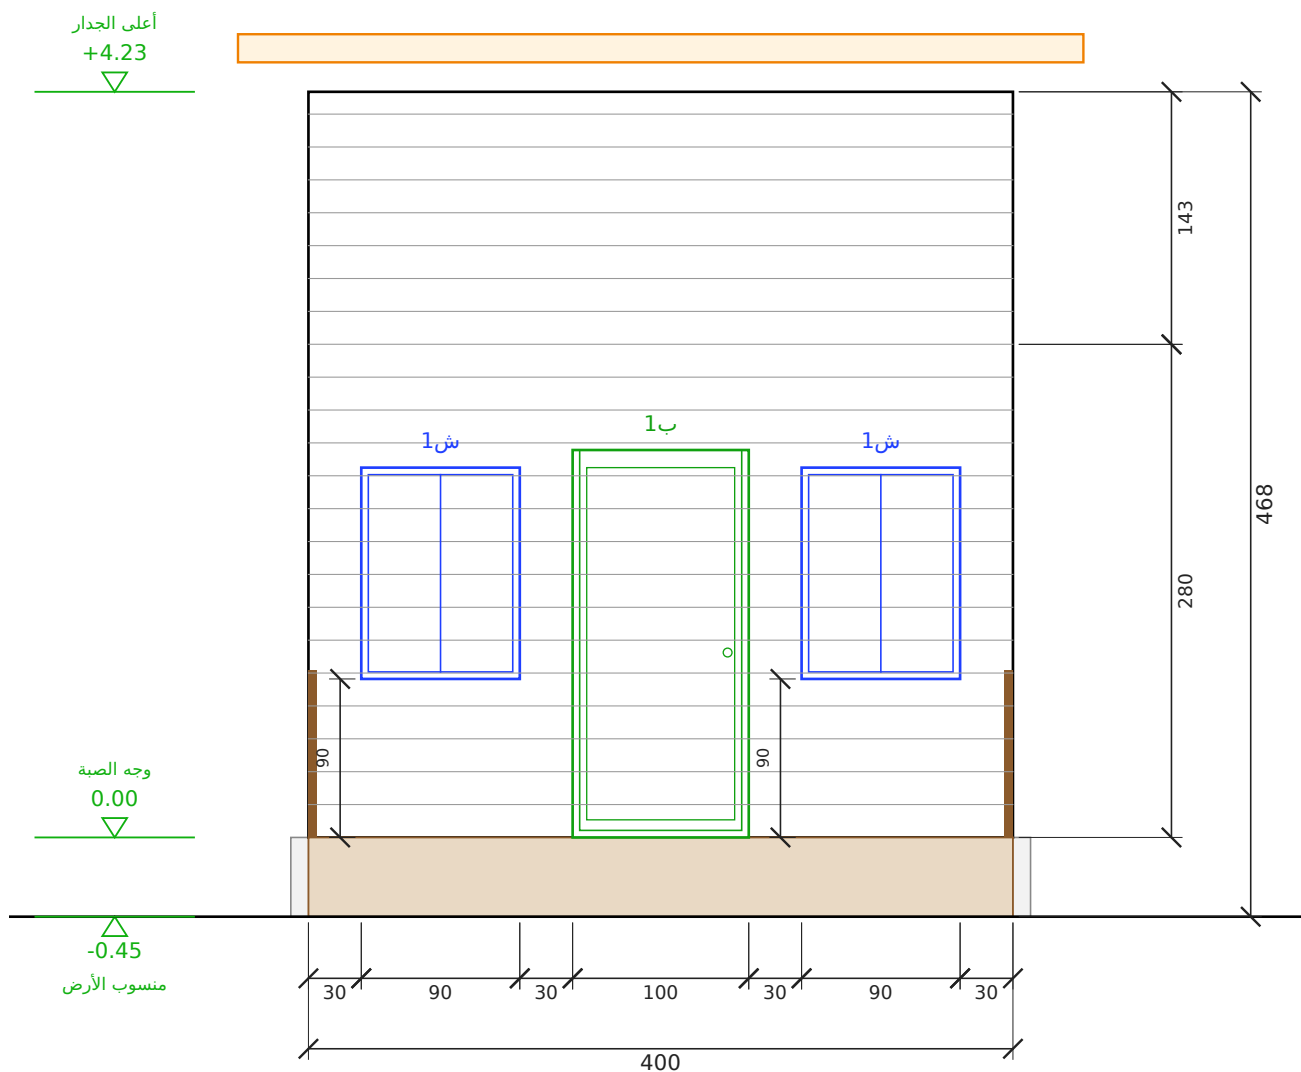

الواجهة الأمامية


مقياس 1:50 | الوحدة: سم

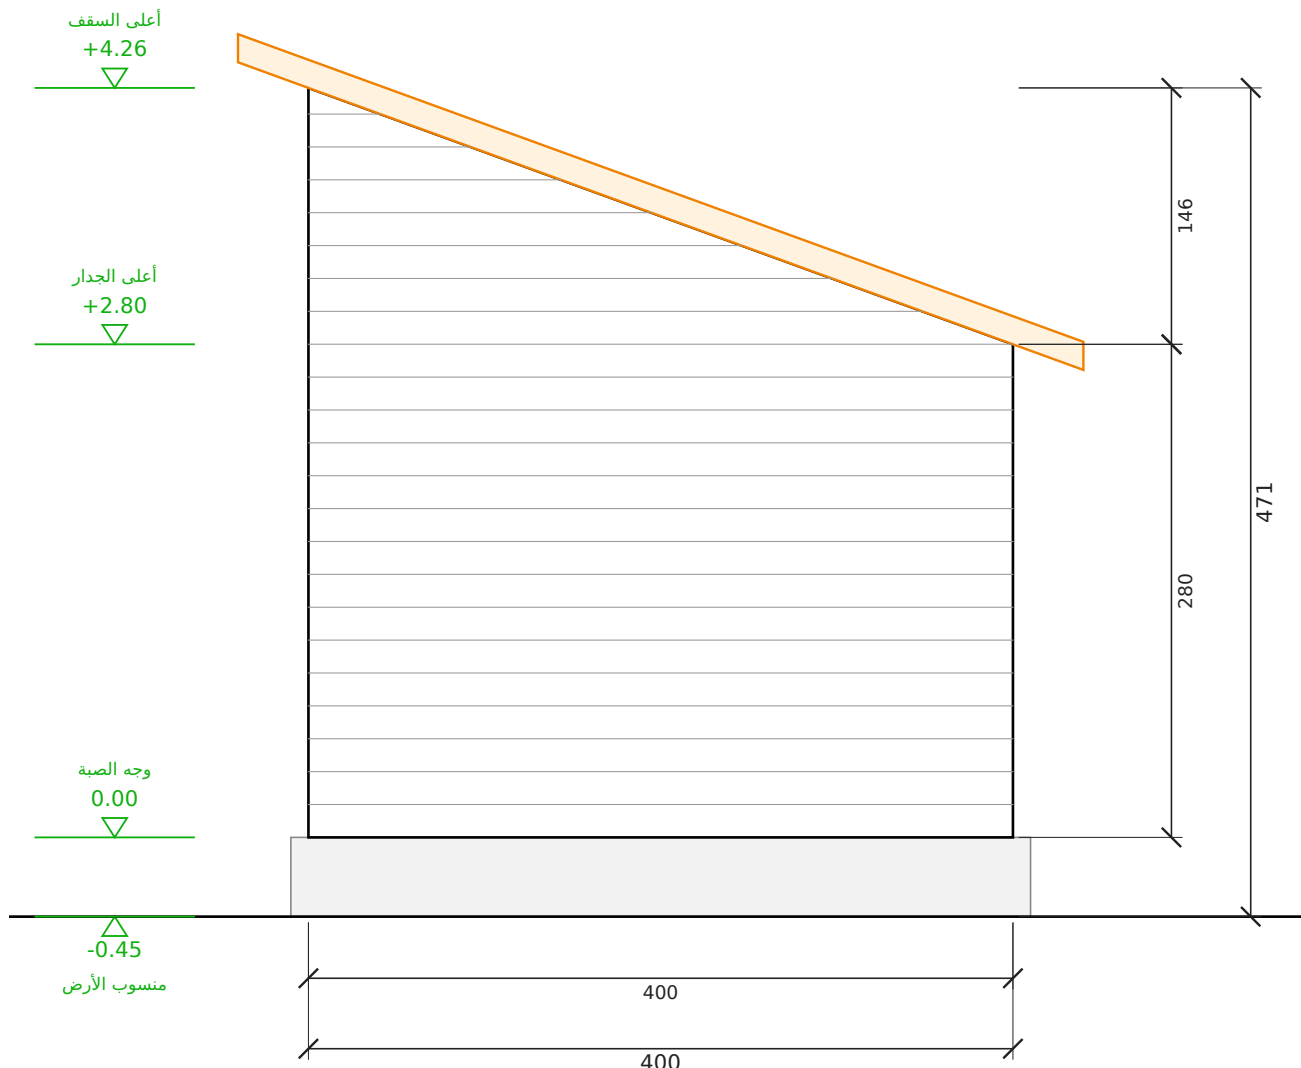

الواجهة الشرقية


مقياس 1:50 | الوحدة: سم

رقم اللوحة	التاريخ	المقياس	عنوان اللوحة	المشروع / العميل	مصنع وتد الأخشاب Watad Wood Factory
A-02 (2/9)	2026-10-01	1:50	الواجهة الأمامية والواجهة الشرقية	غرفة 4x4 بسقف مائل عميل - غرفة مستقلة	

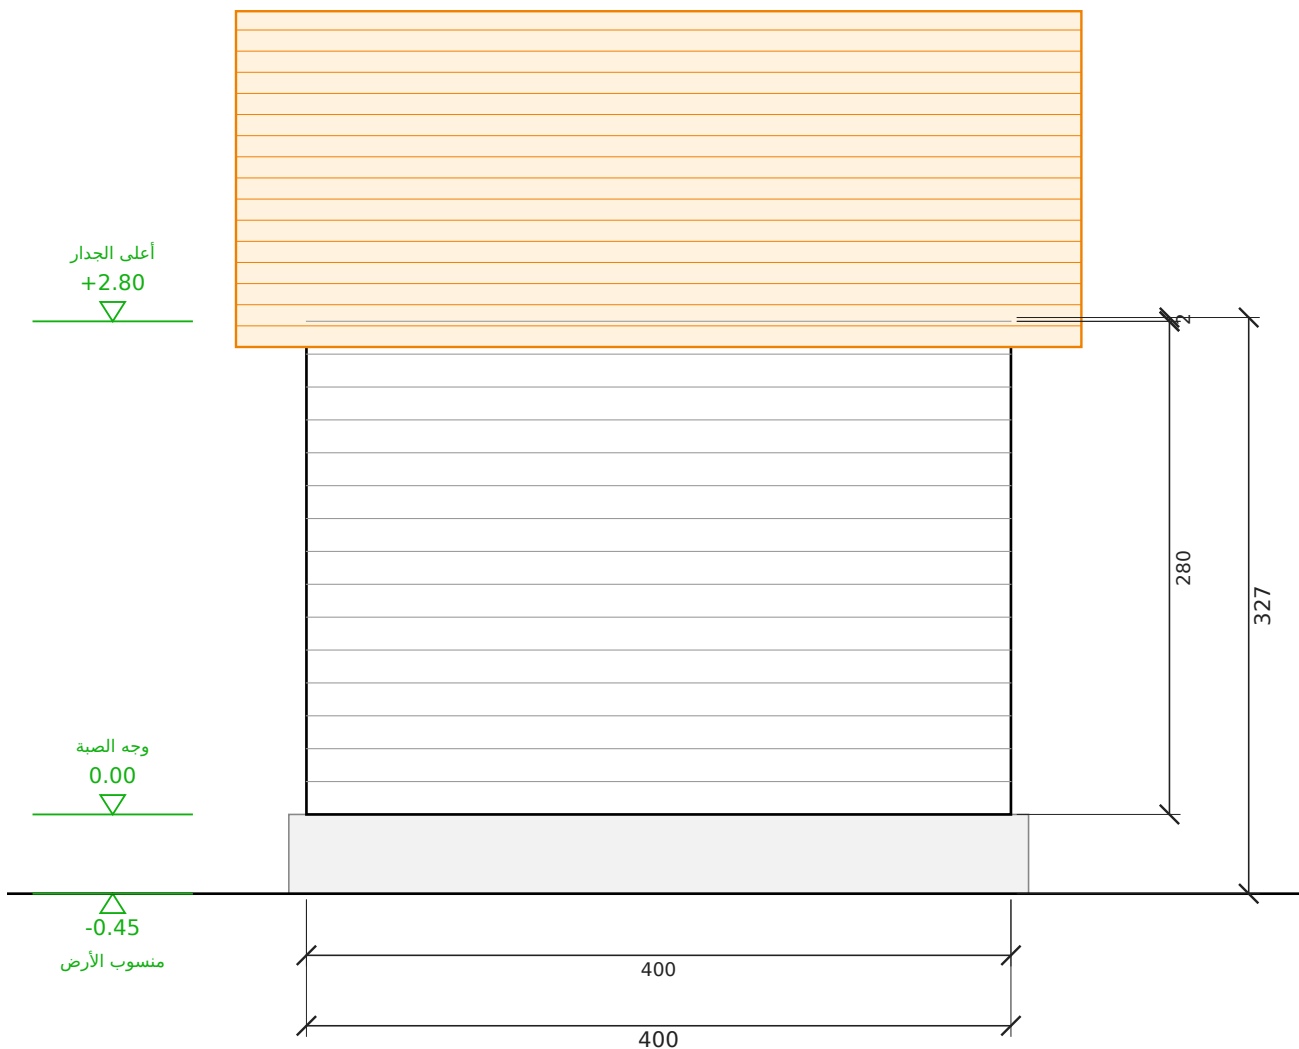

الواجهة الخلفية

مقياس 1:50 | الوحدة: سم

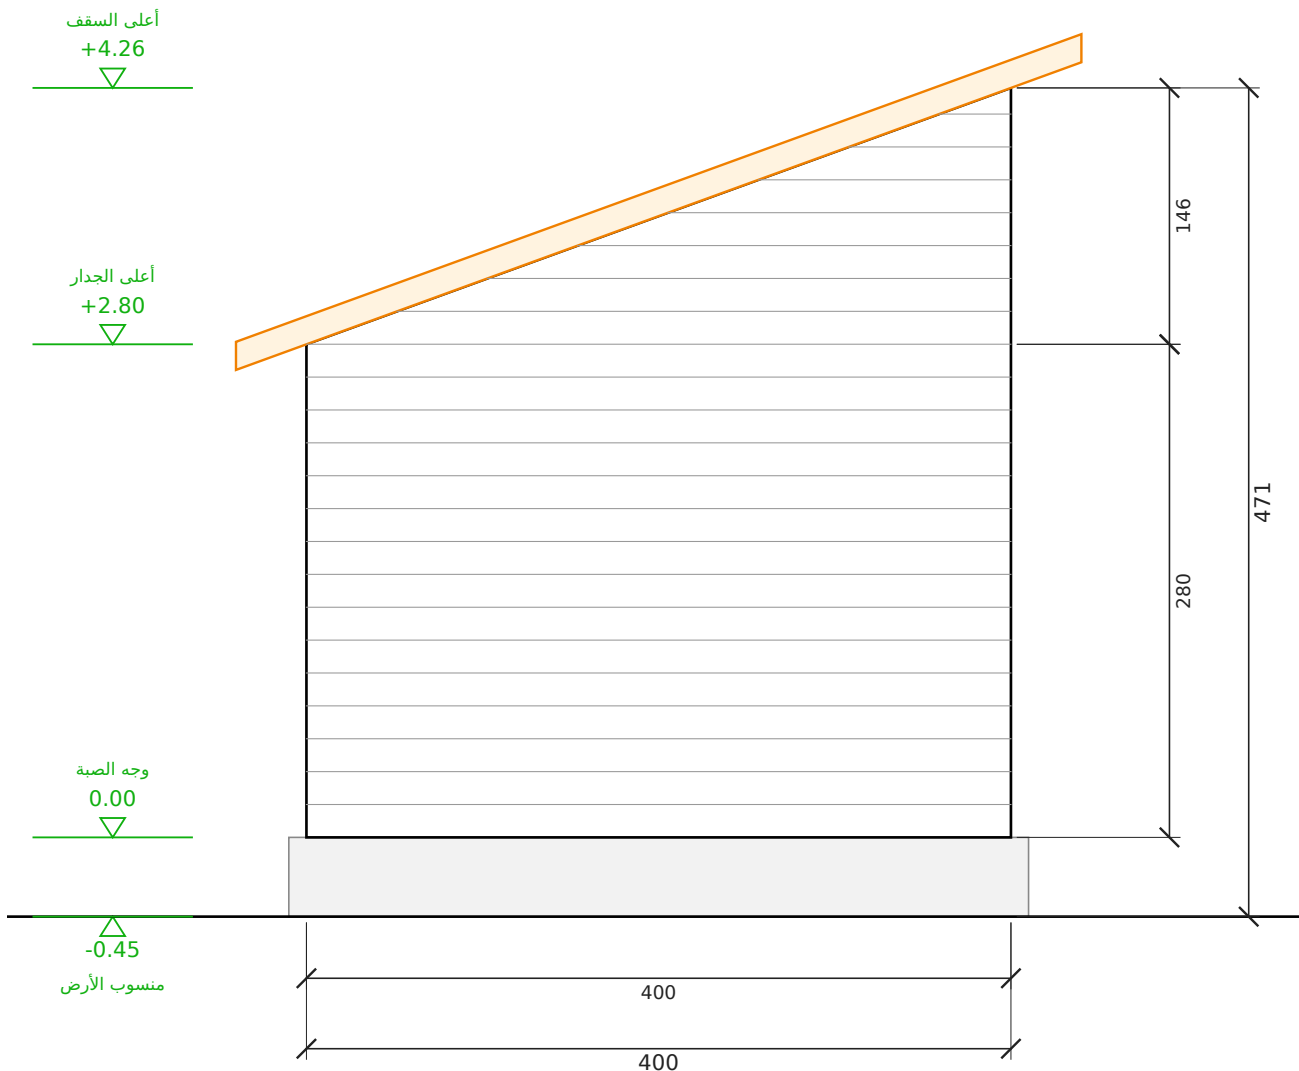


الواجهة الغربية



مقياس 1:50 | الوحدة: سم

رقم اللوحة	التاريخ	المقياس	عنوان اللوحة	المشروع / العميل	مصنع وتد الأخشاب Watad Wood Factory
A-03 (3/9)	2026-10-01	1:50	الواجهة الخلفية والواجهة الغربية	غرفة 4x4 بسقف مائل عميل - غرفة مستقلة	

مسقط السقف (مائل باتجاه واحد)
رفر 40 سم من كل جهة | مقياس 1:50

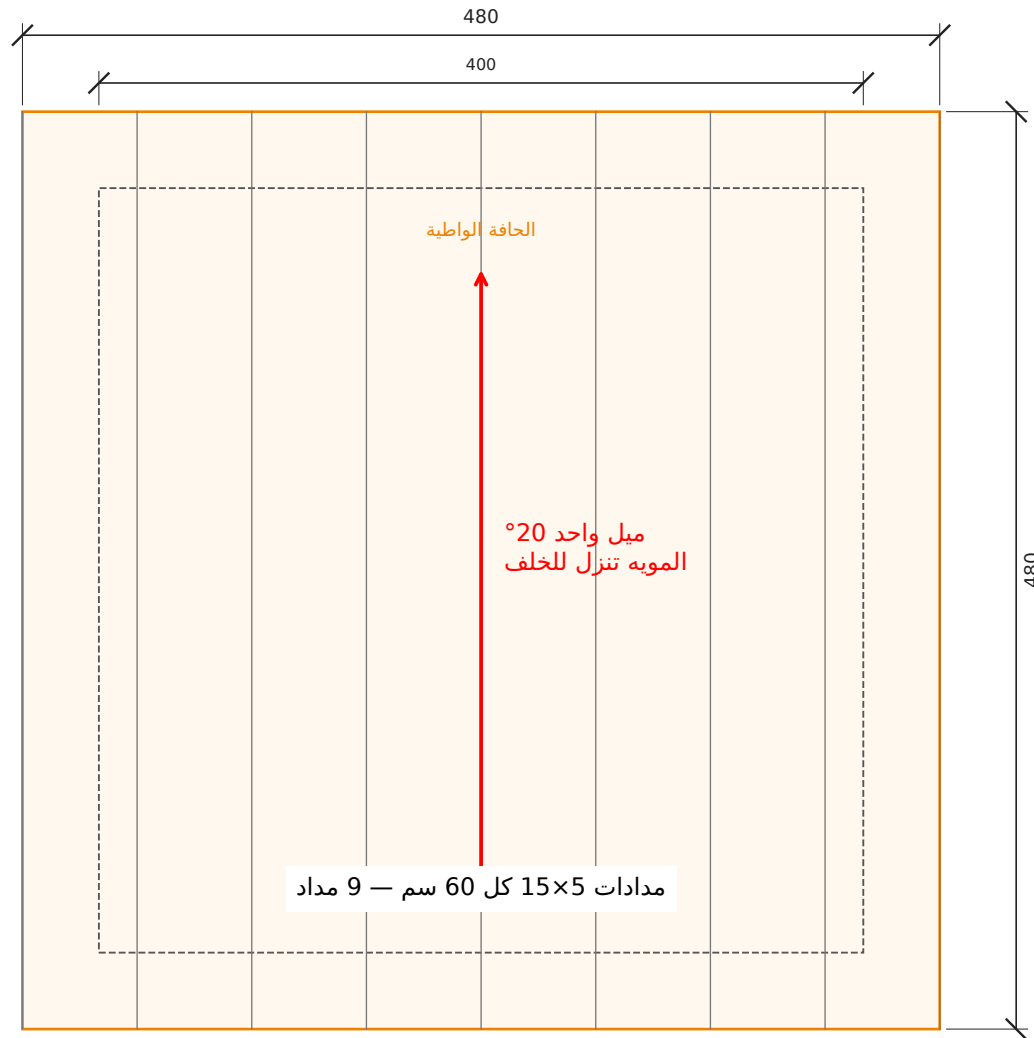

قطاع عرضي أ-أ
مقياس 1:50 | الوحدة: سم

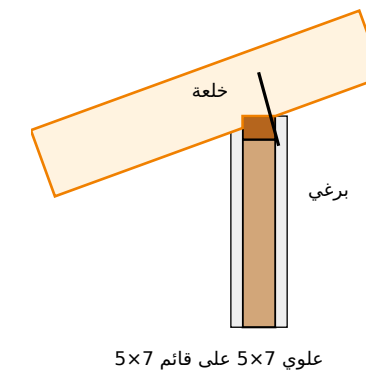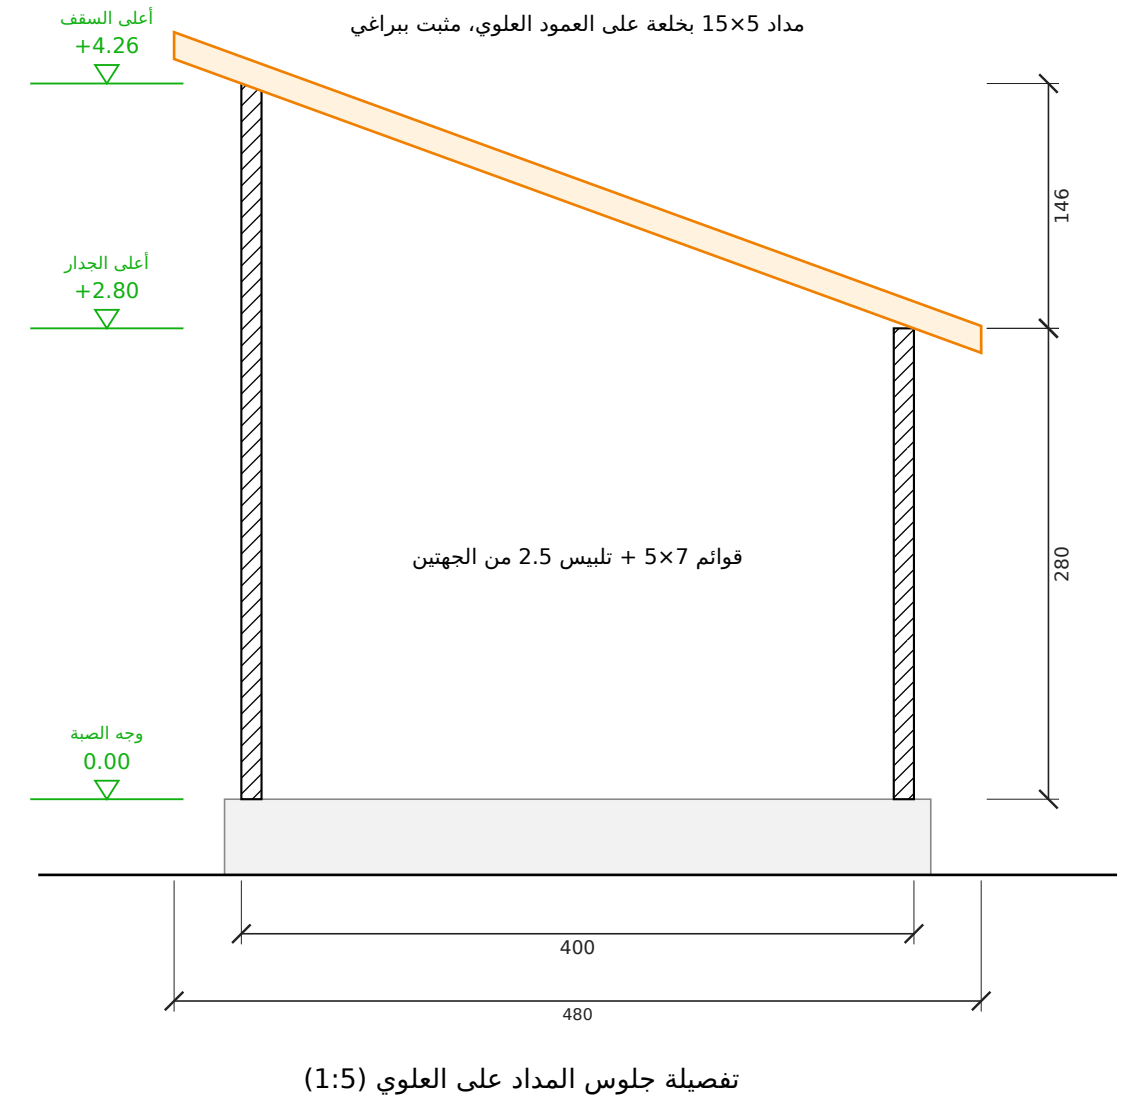

رقم اللوحة

A-04 (4/9)

التاريخ

2026-10-01

المقياس

1:50

عنوان اللوحة

مسقط السقف والقطاع

المشروع / العميل

غرفة 4×4 بسقف مائل
عميل — غرفة مستقلة

مصنع وتد الأخشاب
Watad Wood Factory



جدول مقاسات الأبواب والشبابيك
مقاس الفتحة الصافي في الجدار - الوحدة: سم

الرمز	النوع	العرض (سم)	الارتفاع (سم)	ارتفاع الجلسة (سم)	العدد	الموقع
ب1	باب	100	220	-	1	الأمامية
ش1	شباك	90	120	90	2	الأمامية 2

الإجمالي: أبواب 1 - شبابيك 2

جدول المساحات وبيانات المشروع والتسعير

جدول المساحات

م	الفراغ	الأبعاد (م)	المساحة (م2)
1	الغرفة	3.76 × 3.76	14.14
	المساحة الصافية الداخلية		14.14
	التراس المسقوف (مجاناً)	4.00 × 1.20	4.80
	المساحة الإجمالية المبنية	4.00 × 4.00	16.00

بيانات المشروع

البند	البيان
المشروع	غرفة 4×4 بسقف مائل
العميل	عميل — غرفة مستقلة
الموقع	—
الاستخدام	غرفة / استراحة
التاريخ	2026-10-01
نظام البناء	هيكل خشب 5×7 + تليس 2.5 سم من الجهتين
السقف	مائل باتجاه واحد 20° — قرميد معدني

التسعير

عرض اليوم الوطني

البند	القيمة
المساحة المبنية (م2)	16.00
سعر المتر المربع — عرض اليوم الوطني	1,096 ريال
الإجمالي	17,536 ريال

ملاحظات:

- السعر للمساحة المبنية حسب المخطط المعتمد.
- الصبة والتوريدات الخارجية على العميل ما لم يُذكر غير ذلك.

لقطات المنظور الخارجي

المنظور الأمامي



منظور أمامي من اليسار



منظور أمامي من اليمين



المنظور الخلفي



منظور خلفي من اليمين



منظر علوي



المشروع / العميل

غرفة 4×4 بسقف مائل
عميل — غرفة مستقلة

عنوان اللوحة

لقطات المنظور

المقياس

—

التاريخ

2026-10-01

رقم اللوحة


A-07 (7/9)

مصنع وتد الأخشاب
Watad Wood Factory



المقطع العلوي بالفرش

مقطع أفقي على ارتفاع 1.90 م — توزيع الفرش ومسار الحركة

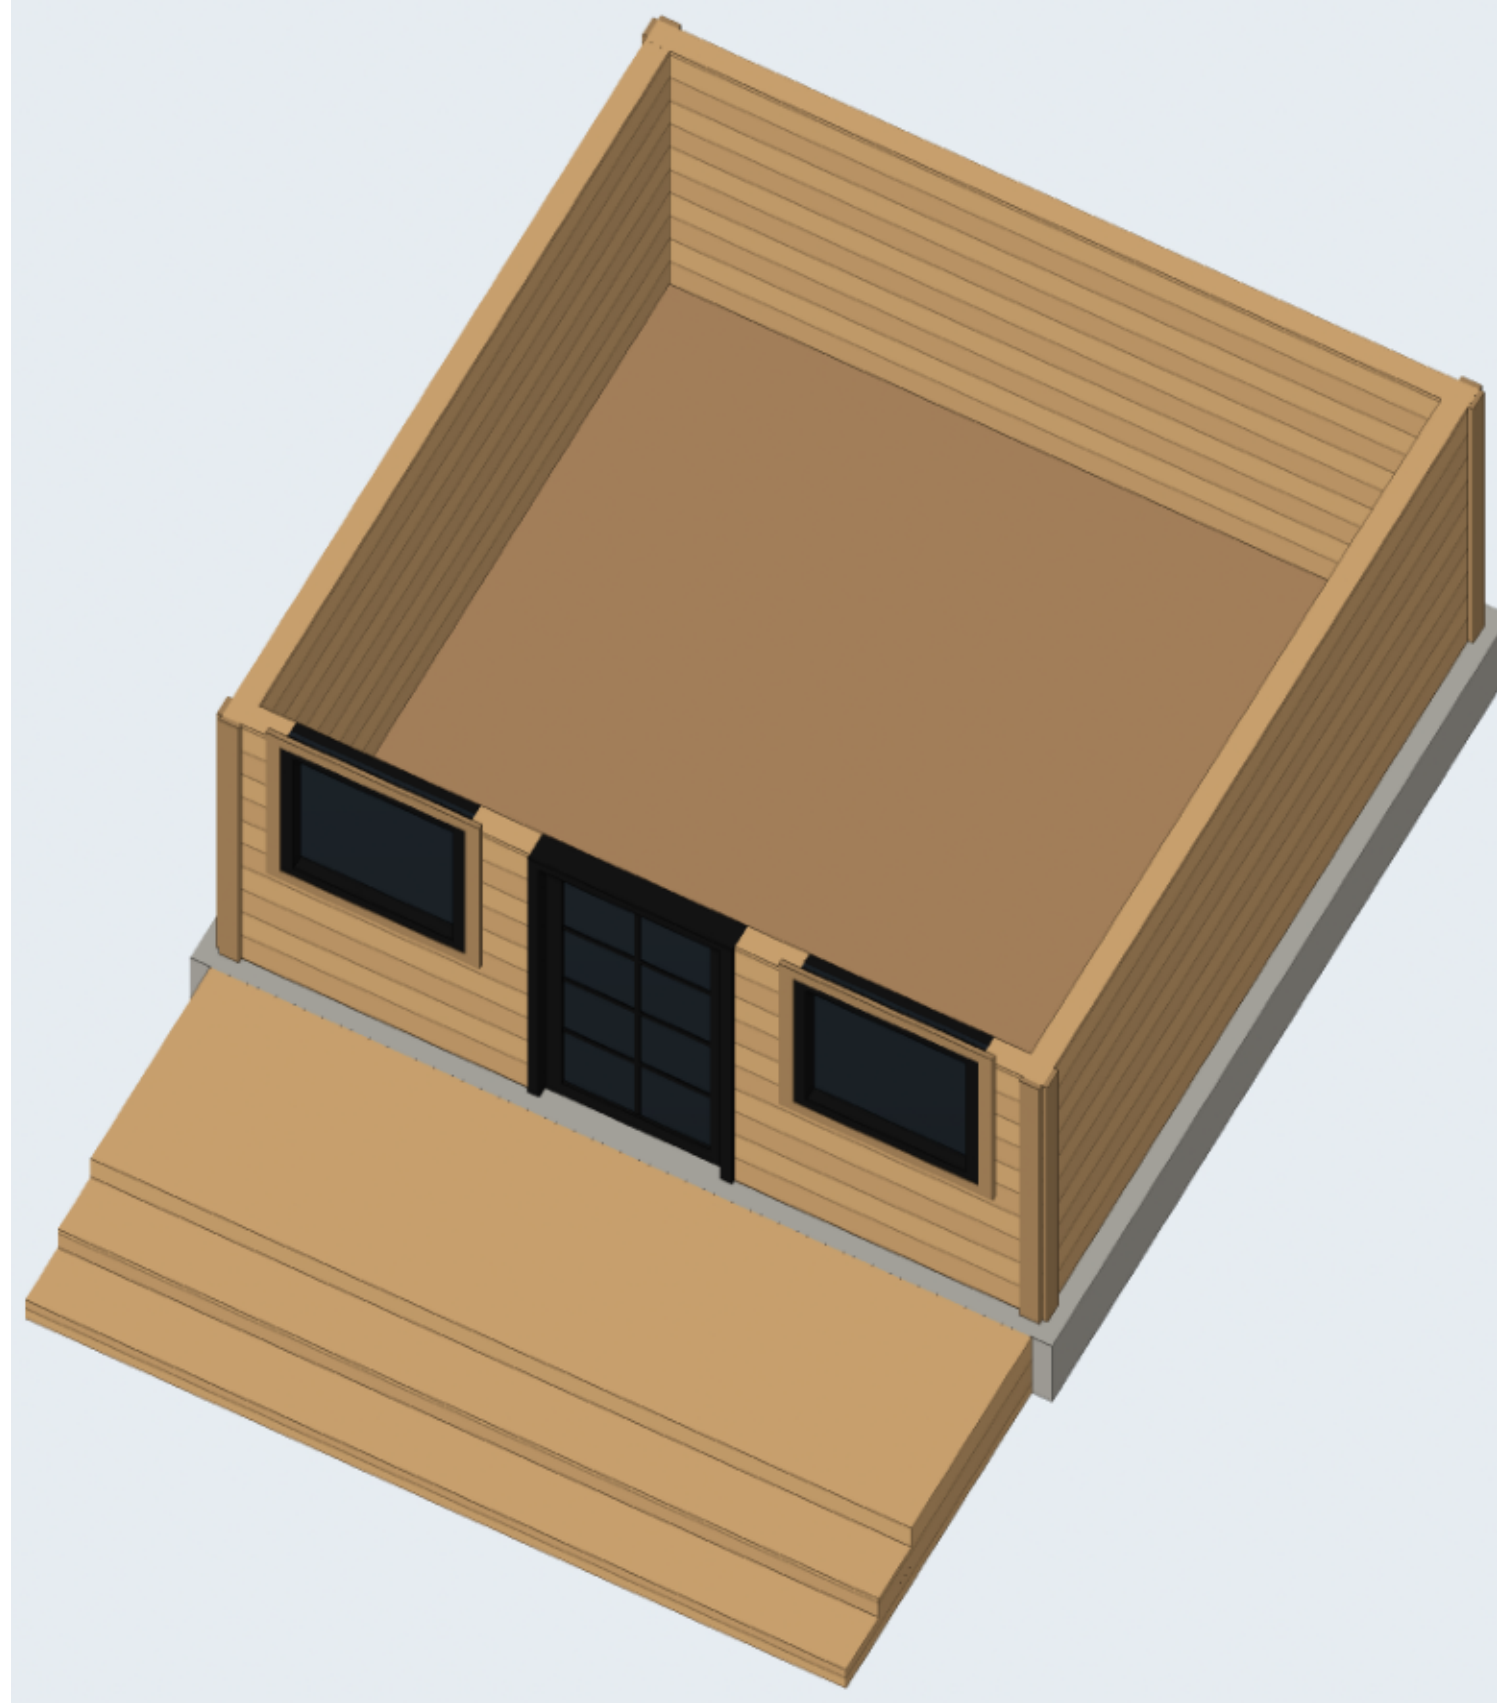

رقم اللوحة

A-08 (8/9)

التاريخ

2026-10-01

المقياس

—

عنوان اللوحة

المقطع العلوي بالفرش

المشروع / العميل

غرفة 4×4 بسقف مائل
عميل — غرفة مستقلة


مصنع وتد الأخشاب
Watad Wood Factory



المنظور ثلاثي الأبعاد والمواد

النمط: جوزي غامق + إطارات سوداء — رندر واقعي بخامات حقيقية

جدول المواد والألوان

 

الخشب / الصبغة
خشب طبيعي فاتح (بدون صبغة)



القرميد
قرميد رمادي غامق




الزجاج
زجاج عاكس غامق



إطارات الشبابيك والأبواب
إطار ألومنيوم أسود



الكنار والزوايا
نفس الصبغة أعمق درجة

 

الصبة
خرسانة 45 سم


الدريزين: ألواح أفقية متقاربة (عصري)

تقسيم الشبابيك: بدون | الباب الرئيسي: زجاج بتقسيمات (فرنسي)


أنواع الدريزين المعتمدة (من مشاريع المصنع)



قوائم رأسية متقاربة (صورة 1)

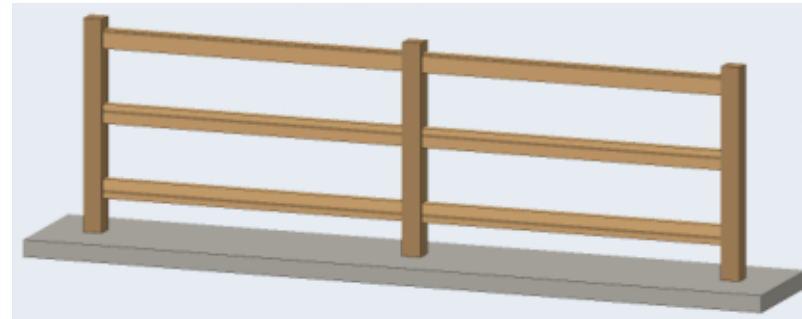

3 مربيع أفقية (صورة 2)

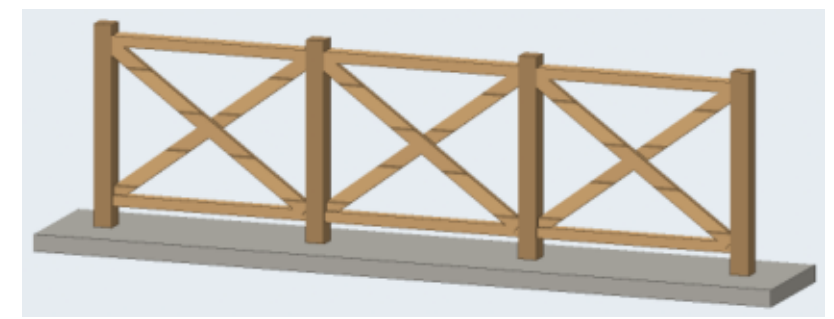

تقاطع X (صورة 5)

رقم اللوحة

A-09 (9/9)

التاريخ

2026-10-01

المقياس

—

عنوان اللوحة

المنظور والمواد

المشروع / العميل

غرفة 4×4 بسقف مانل
عميل — غرفة مستقلة

مصنع وتد الأخشاب
Watad Wood Factory

