

المسقط الأفقي مع الفرش

الأبعاد بالسنتيمتر - الجدران: قوائم 5×7 + تلبيس 2.5 من الجهتين (12 سم)

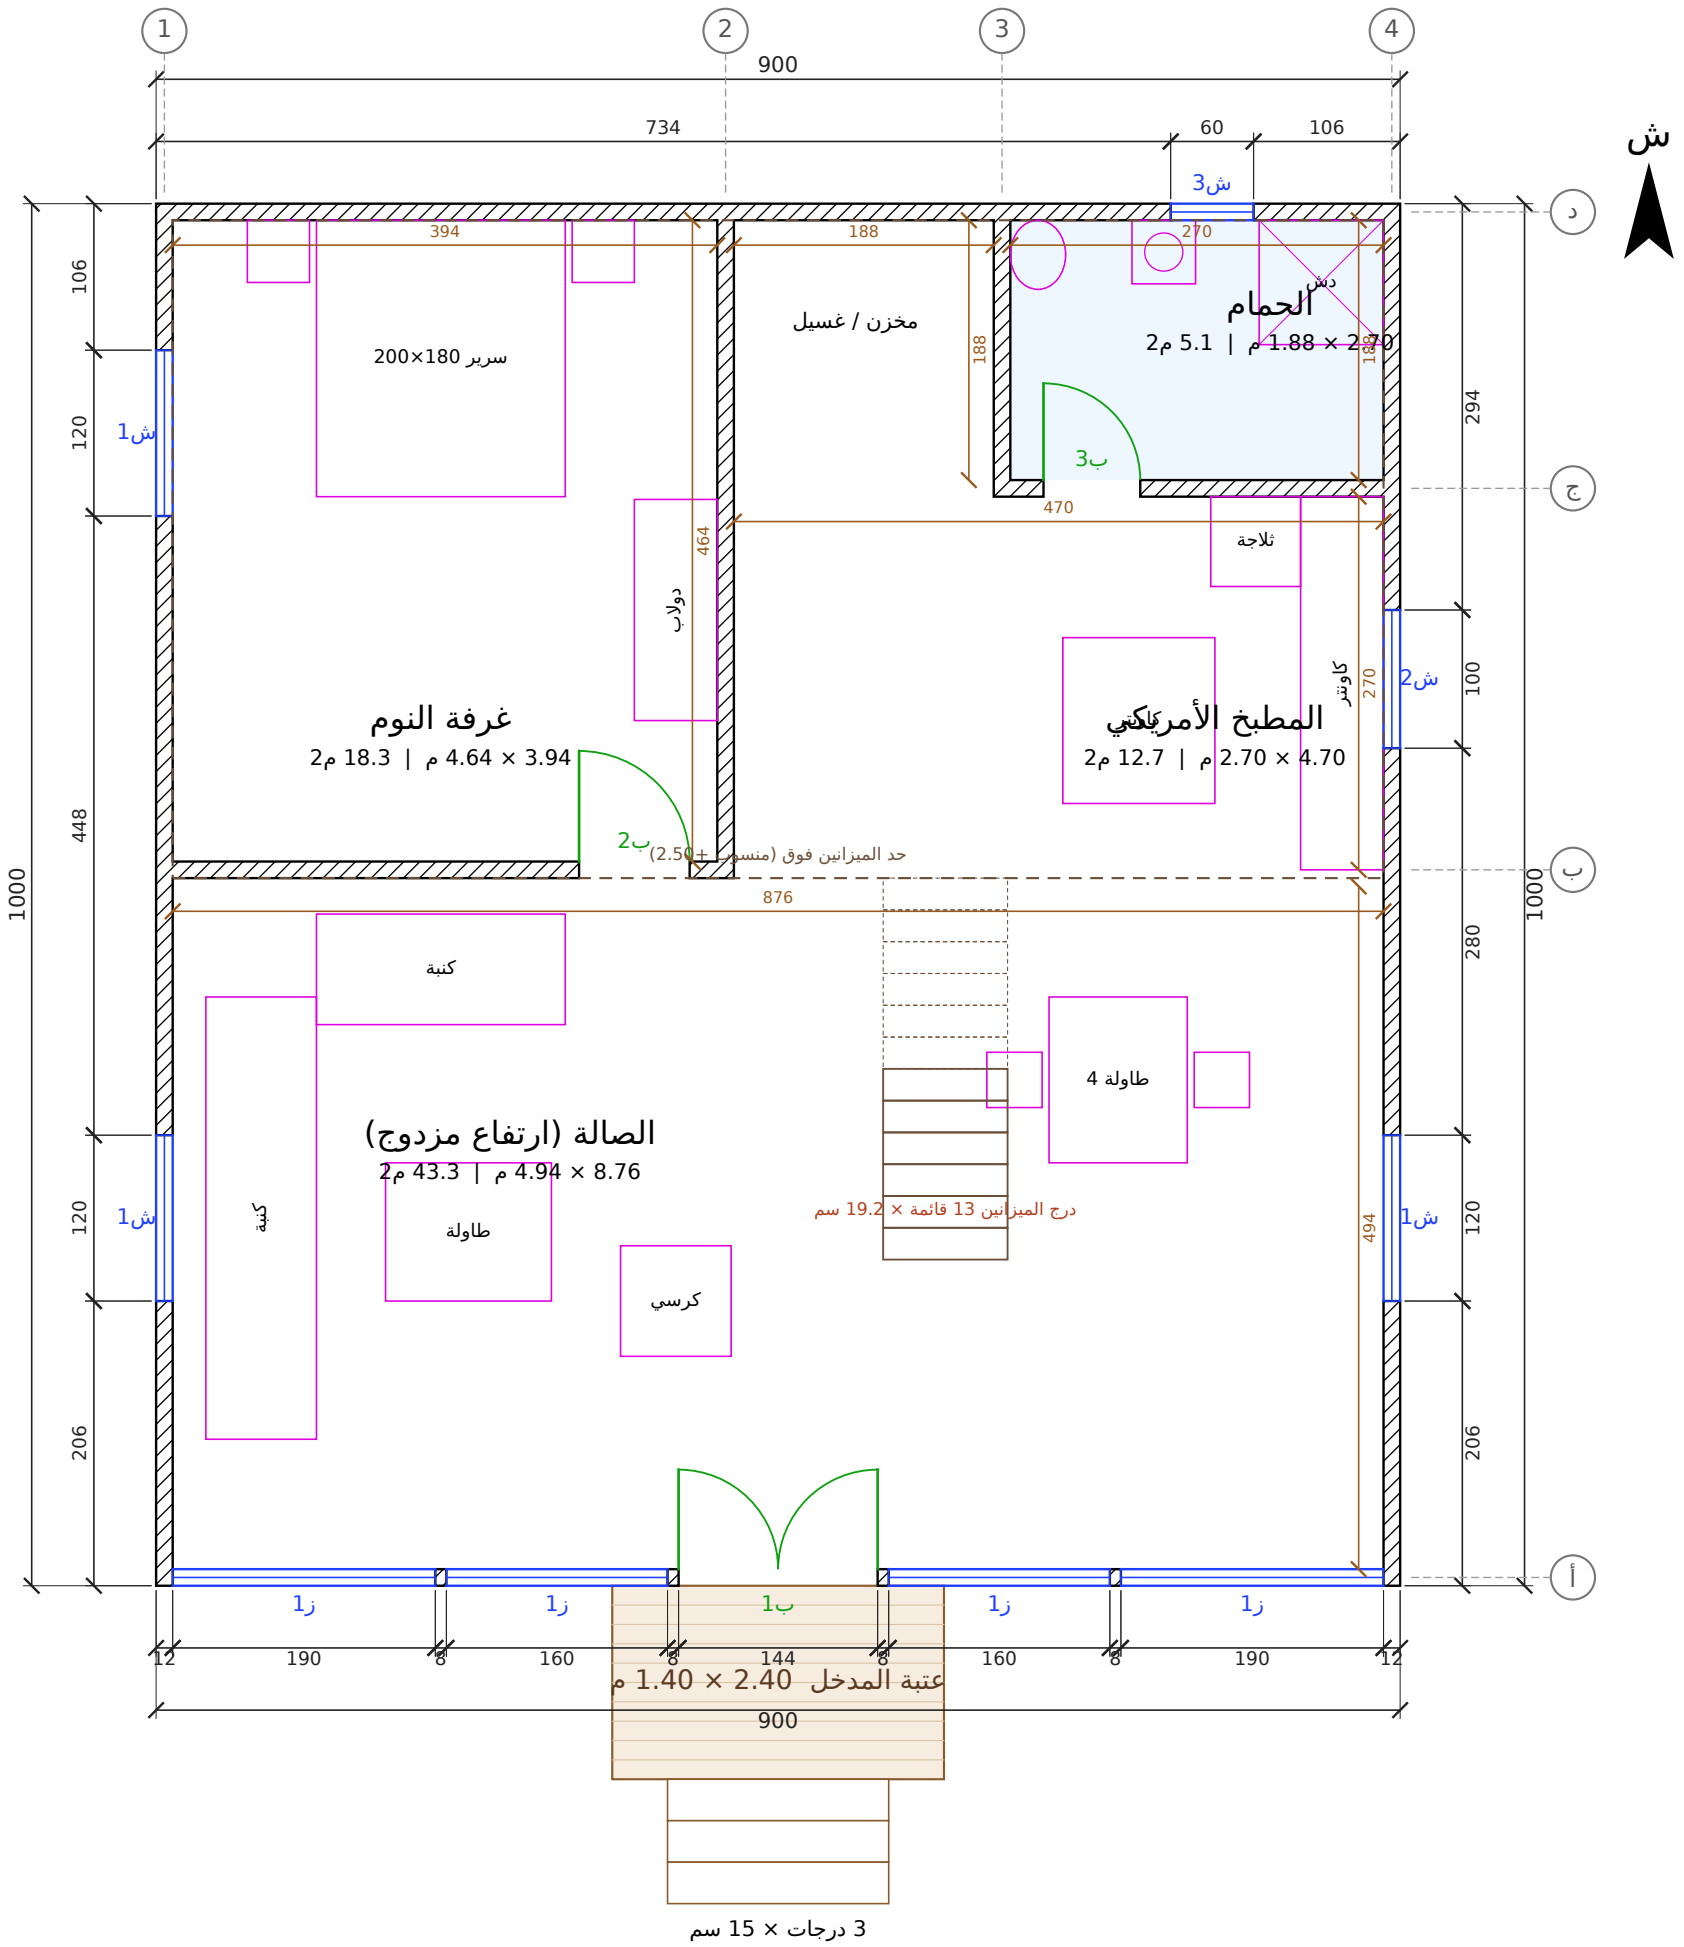


المشروع / العميل	عنوان اللوحة	المقياس	التاريخ	رقم اللوحة
مصنع وتد الأخشاب Watad Wood Factory **كوخ A-frame بواجهة زجاج + ميزانين — صالة وغرفة ومطبخ أمريكي وحمام — 9.00 × 10.00 م** **عميل — A-frame 9×10**	**المسقط الأفقي**	**1:50**	**2026-10-23**	**A-01 (1/10)**

مسقط الميزانين (نص الدور) — جلسة علوية / نوم إضافي
منسوب أرضية الميزانين +2.50 | الأبعاد بالسنتيمتر

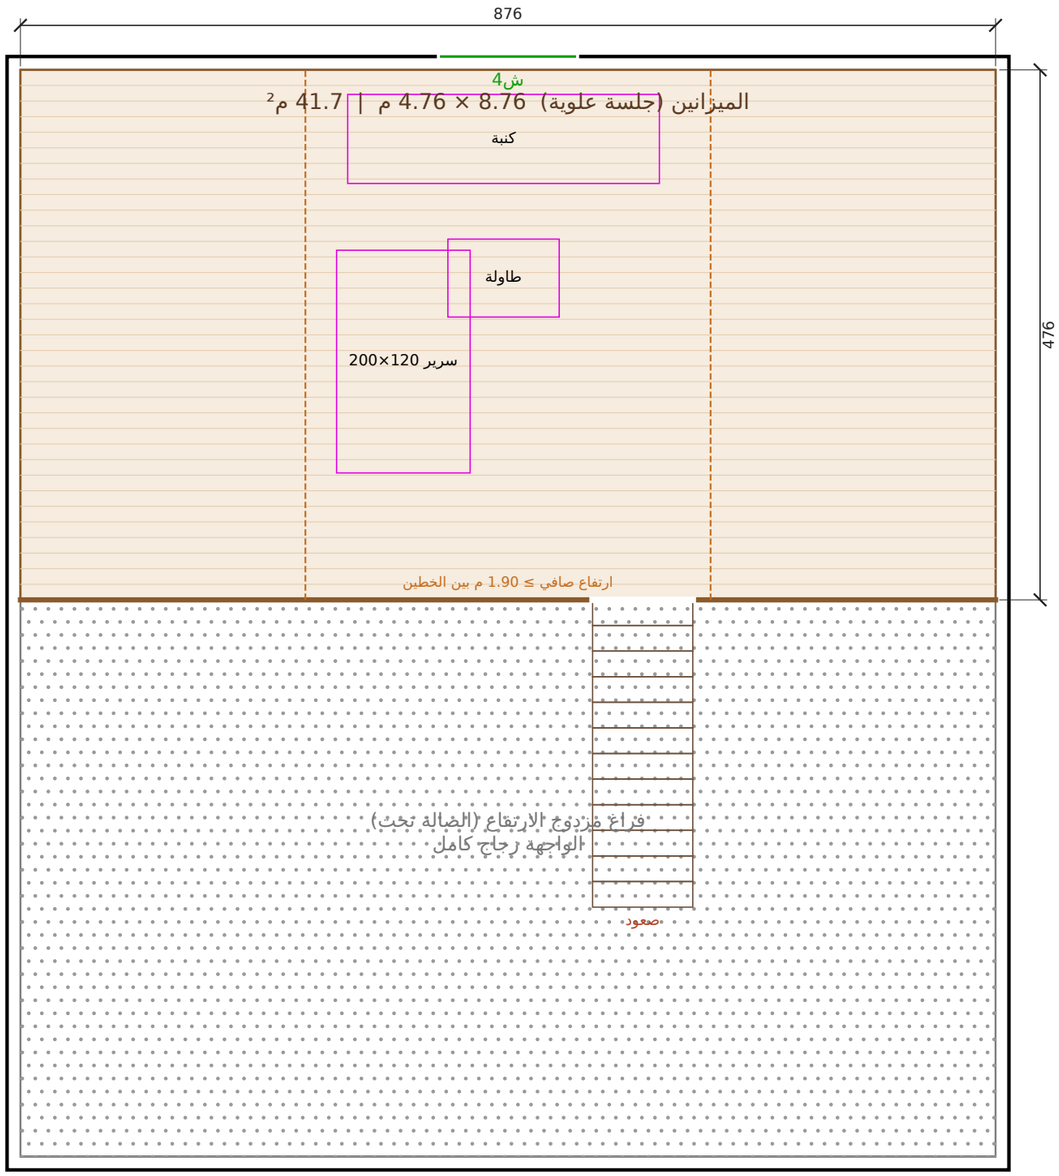


مصنع وتد الأخشاب Watad Wood Factory	المشروع / العميل كوخ A-frame بواجهة زجاج + ميزانين — صالة وغرفة ومطبخ أمريكي وحمام — 9.00 × 10.00 م عميل — A-frame 9×10	عنوان اللوحة مسقط الميزانين	المقياس 1:50	التاريخ 2026-10-23	رقم اللوحة A-02 (2/10)

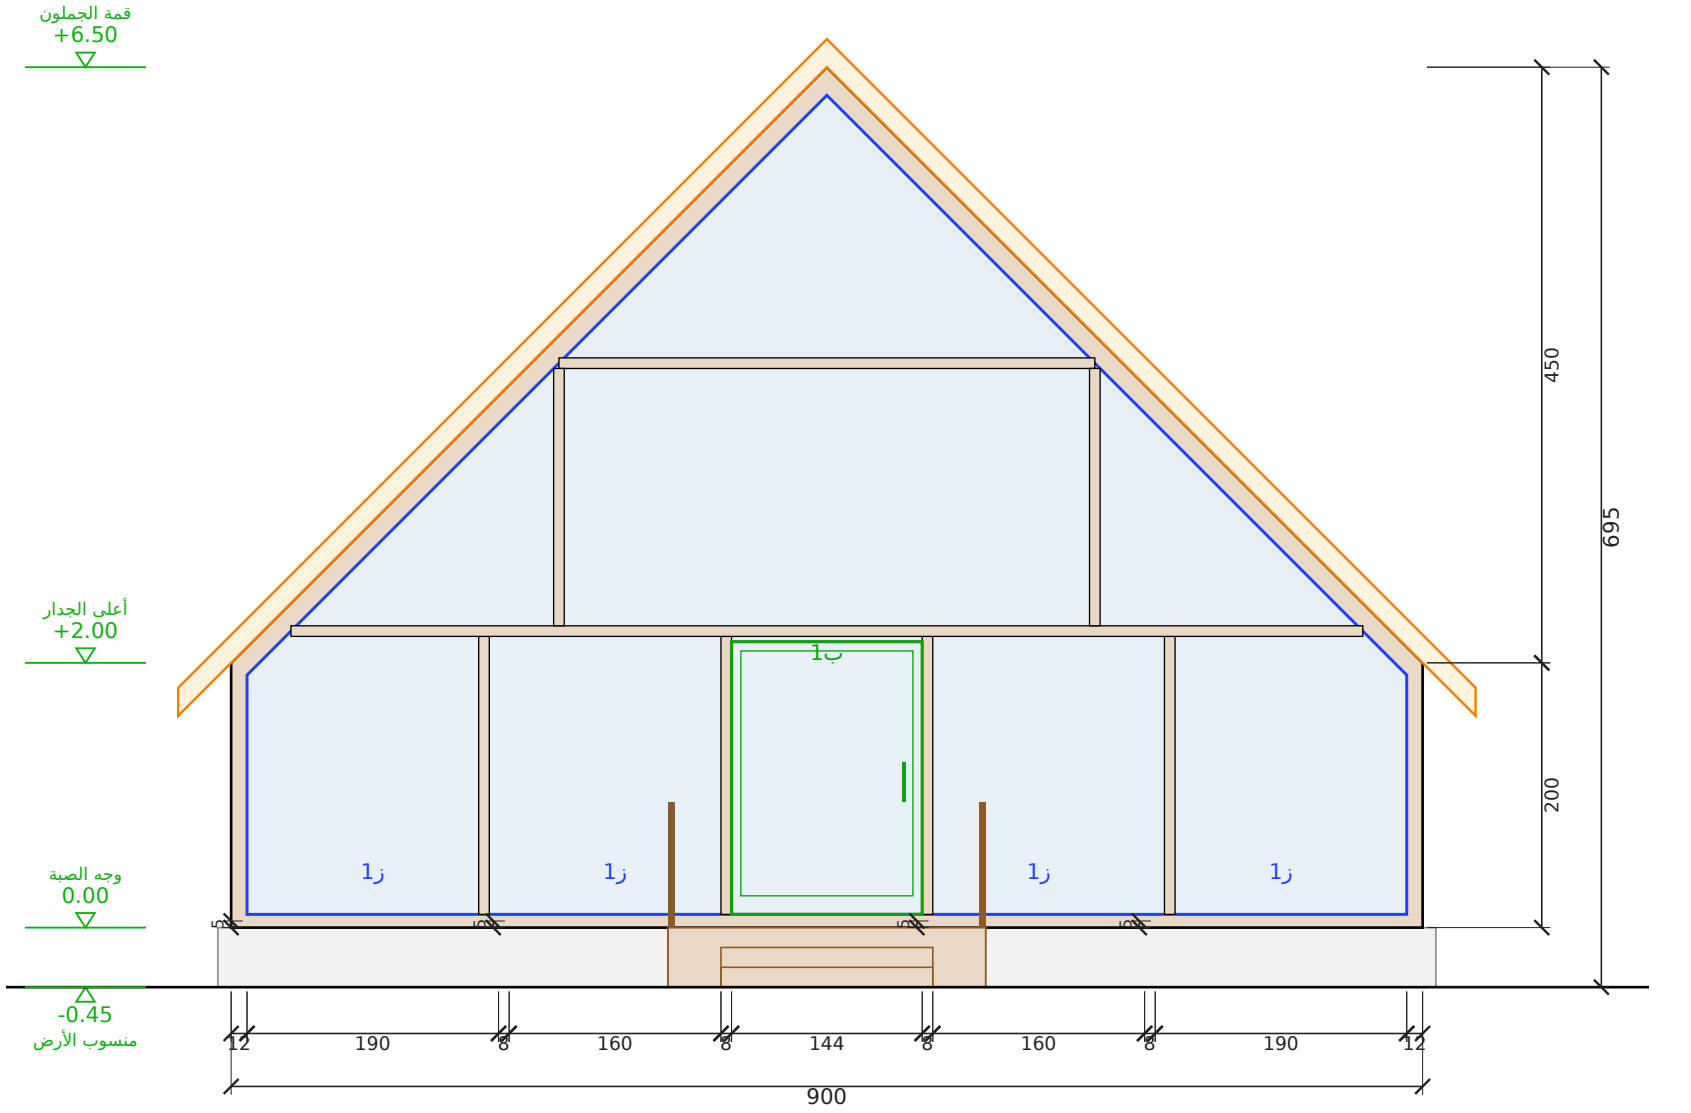

الواجهة الأمامية (زجاج كامل)

مقياس 1:50 | الوحدة: سم

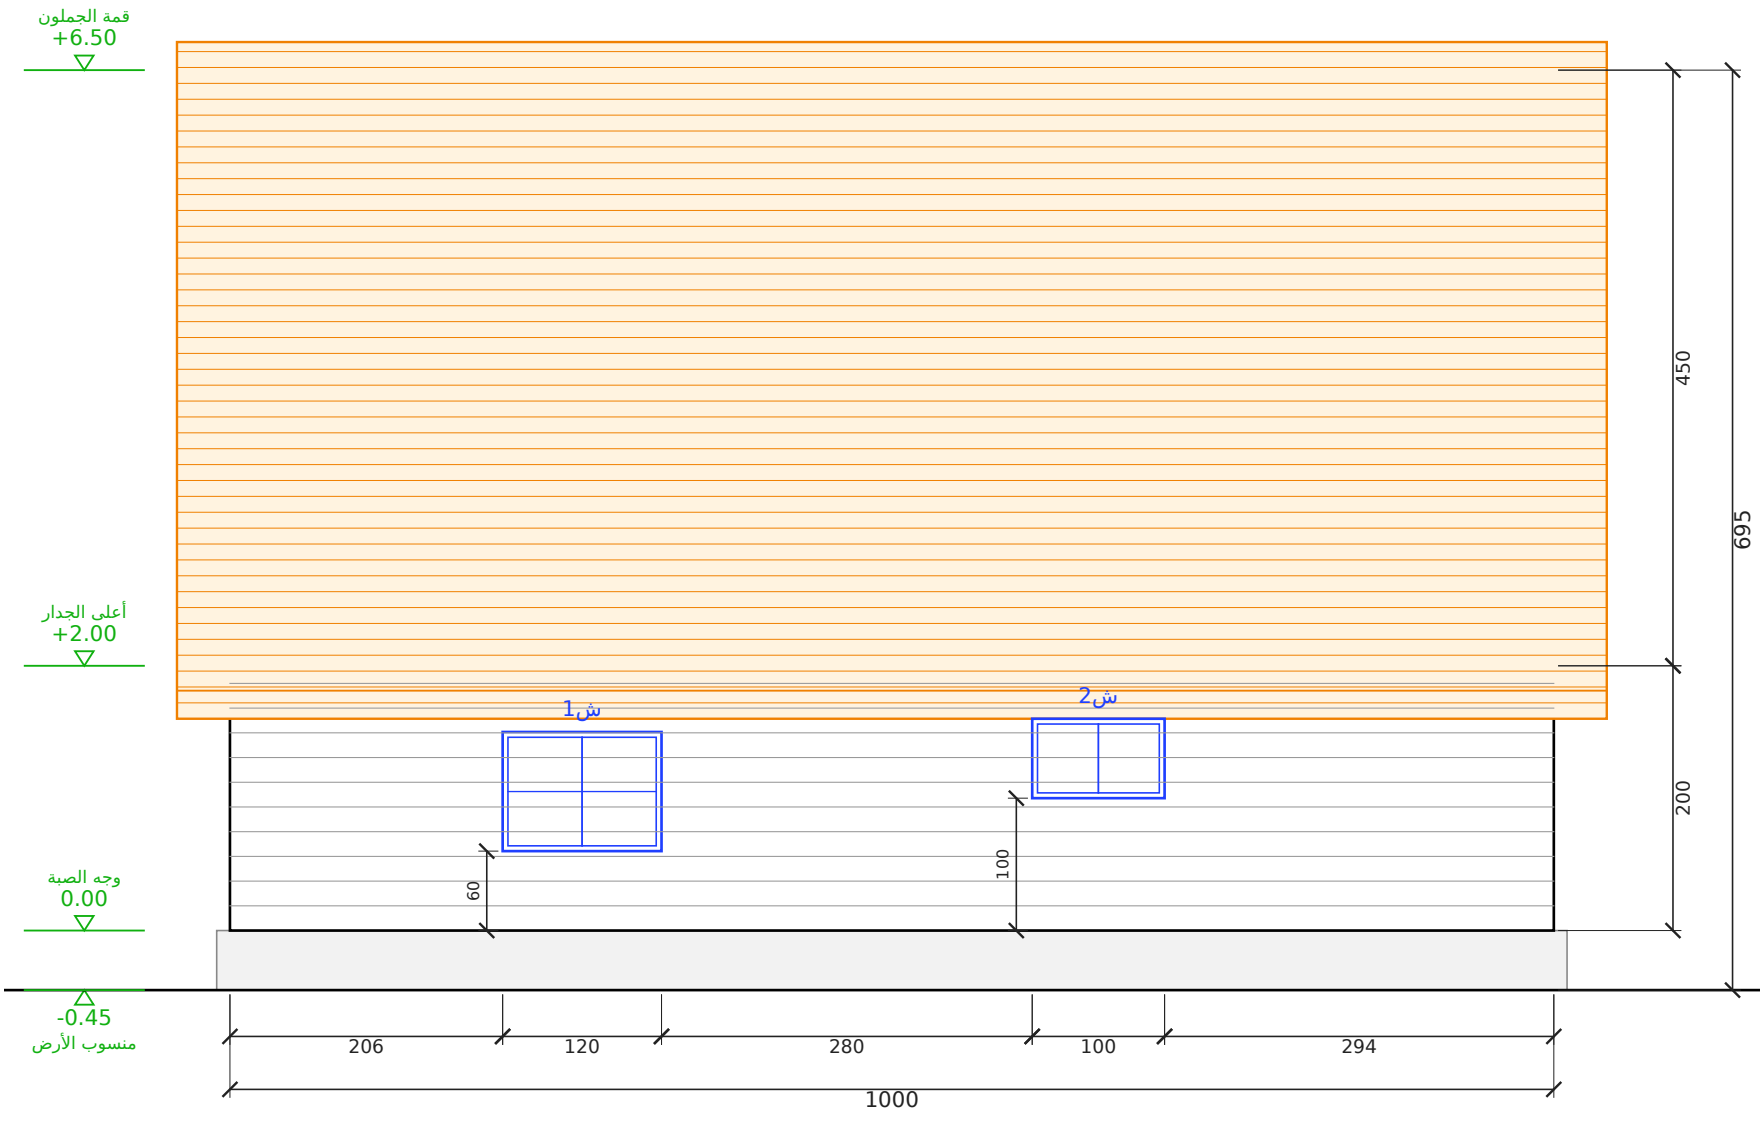


الواجهة الشرقية

مقياس 1:50 | الوحدة: سم


المشروع / العميل	عنوان اللوحة	المقياس	التاريخ	رقم اللوحة
كوخ A-frame بواجهة زجاج + ميزانين — صالة وغرفة ومطبخ أمريكي وحمام — 9.00 × 10.00 م **عميل — A-frame 9×10**	**الواجهة الأمامية (زجاج كامل) والواجهة الشرقية**	**1:50**	**2026-10-23**	**A-03 (3/10)**

مصنع وتد الأخشاب
Watad Wood Factory

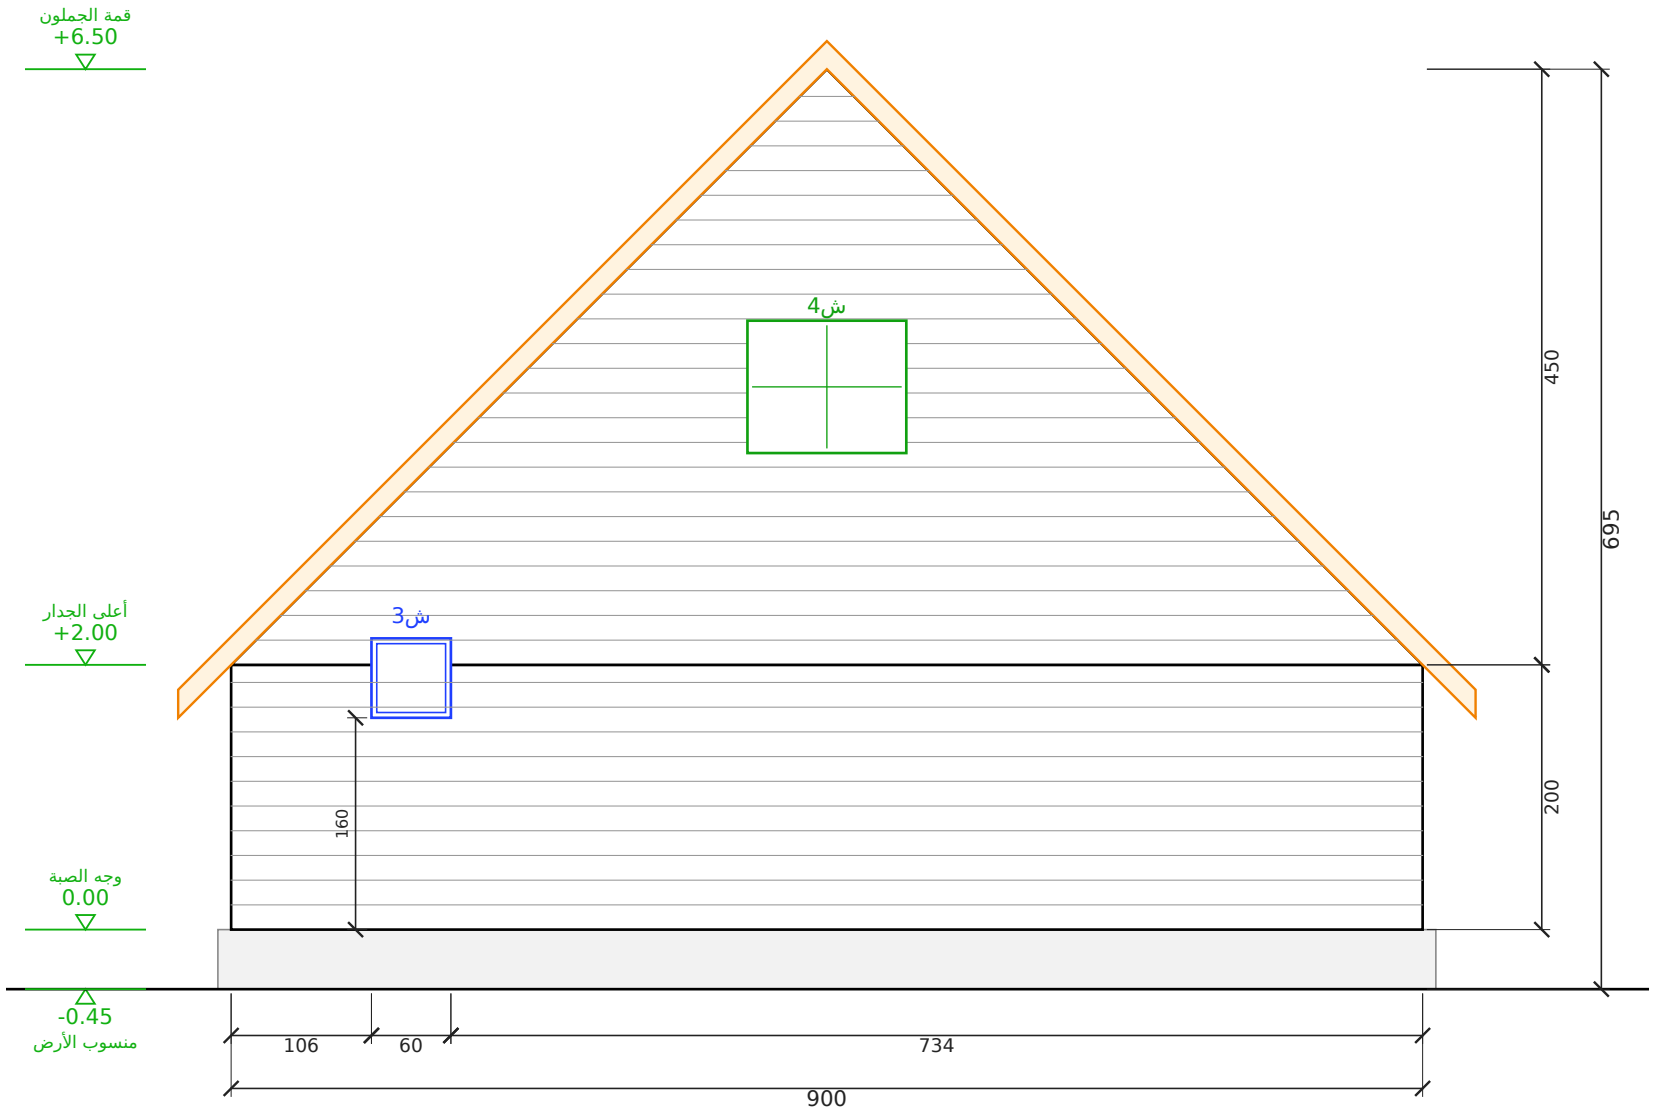

الواجهة الخلفية

مقياس 1:50 | الوحدة: سم

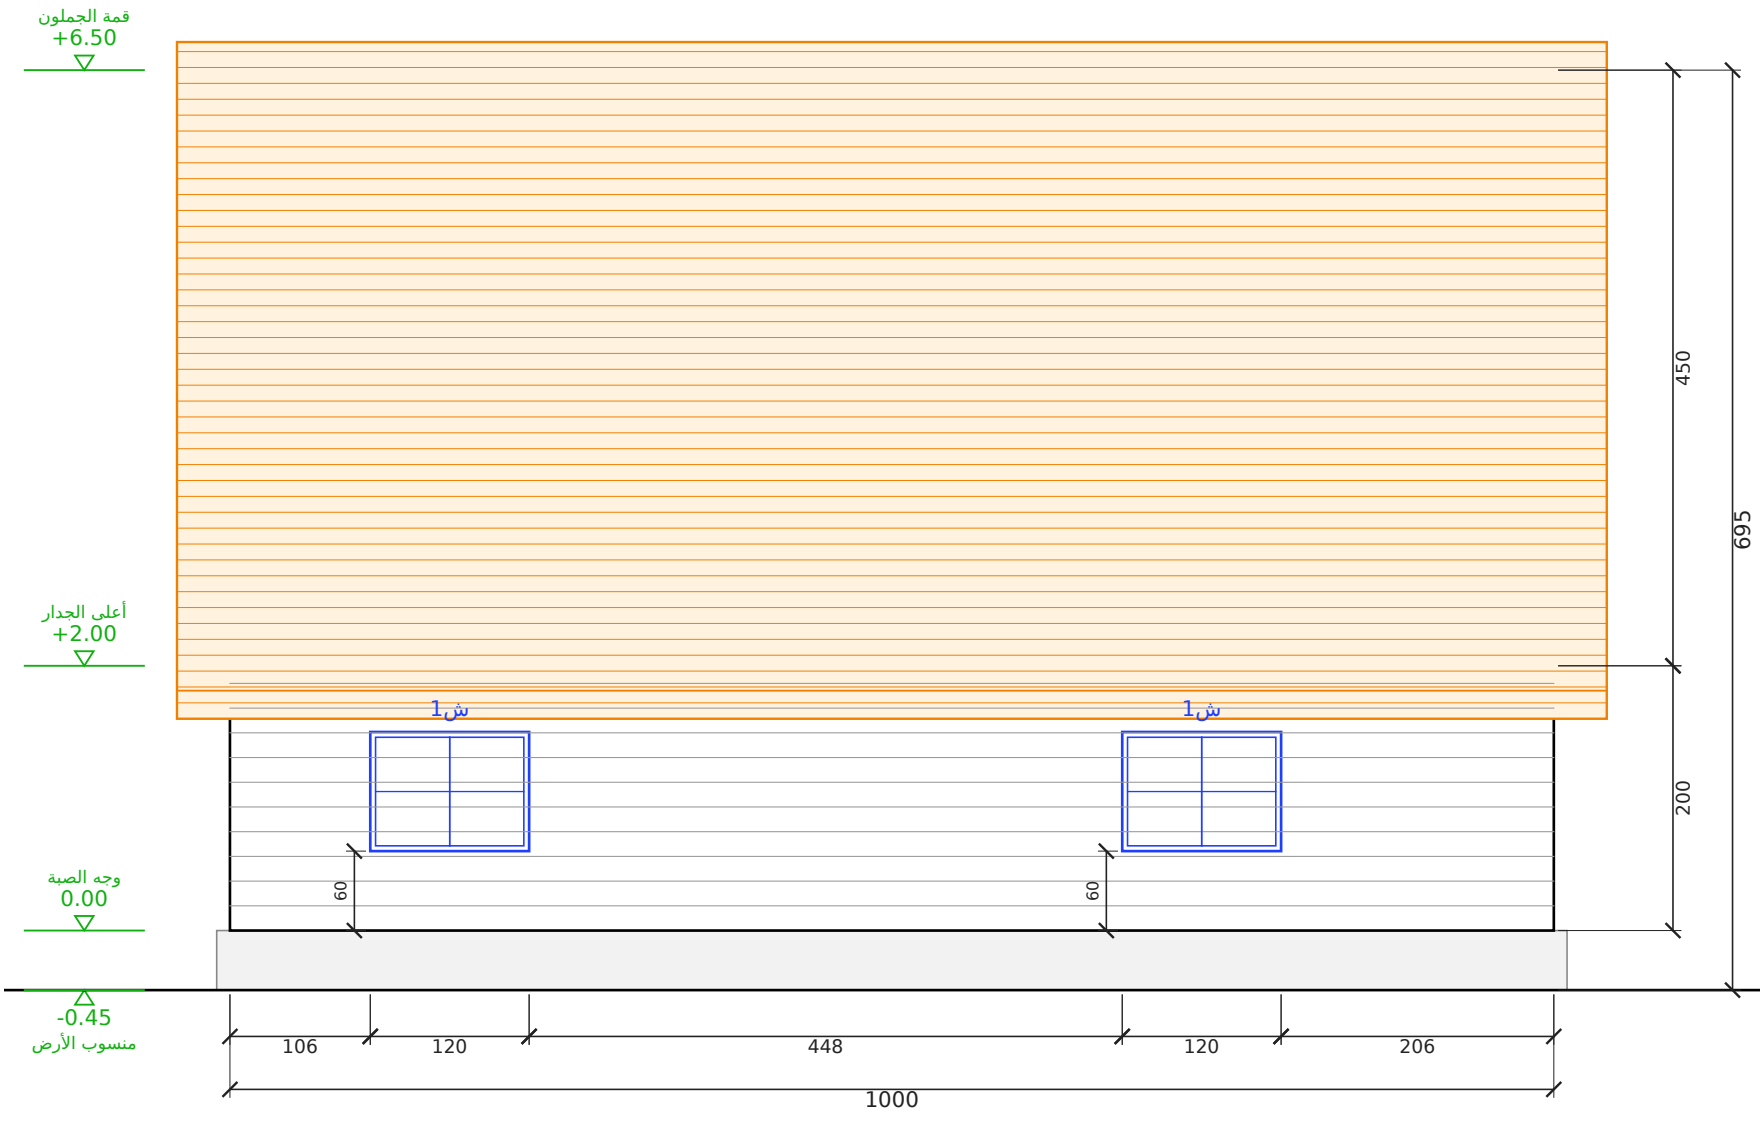


الواجهة الغربية

مقياس 1:50 | الوحدة: سم


المشروع / العميل	عنوان اللوحة	المقياس	التاريخ	رقم اللوحة
كوخ A-frame بواجهة زجاج + ميزانين — صالة وغرفة ومطبخ أمريكي وحمام — 10.00 × 9.00 **عميل — A-frame 9×10**	**الواجهة الخلفية والواجهة الغربية**	**1:50**	**2026-10-23**	**A-04 (4/10)**

مصنع وتد الأخشاب
Watad Wood Factory


مسقط السقف (جملون)
رفرف 40 سم من كل جهة | مقياس 1:50

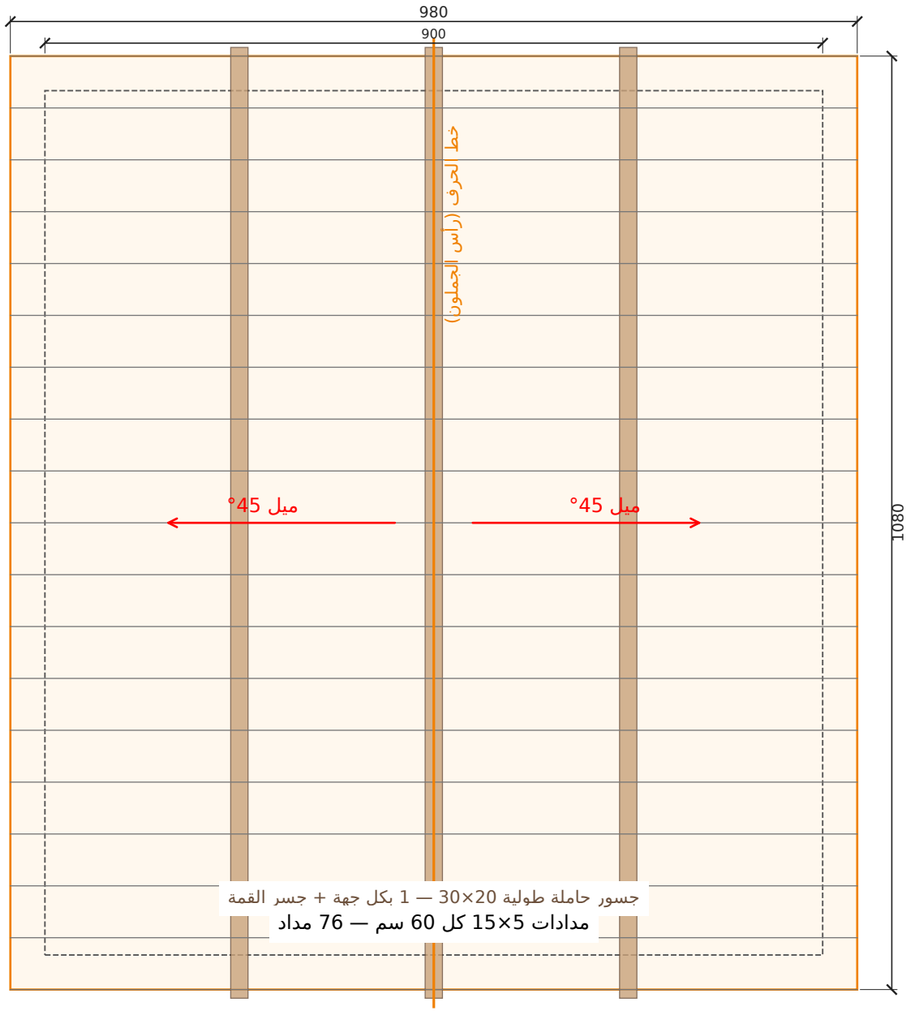

قطاع عرضي أ-أ
مقياس 1:50 | الوحدة: سم

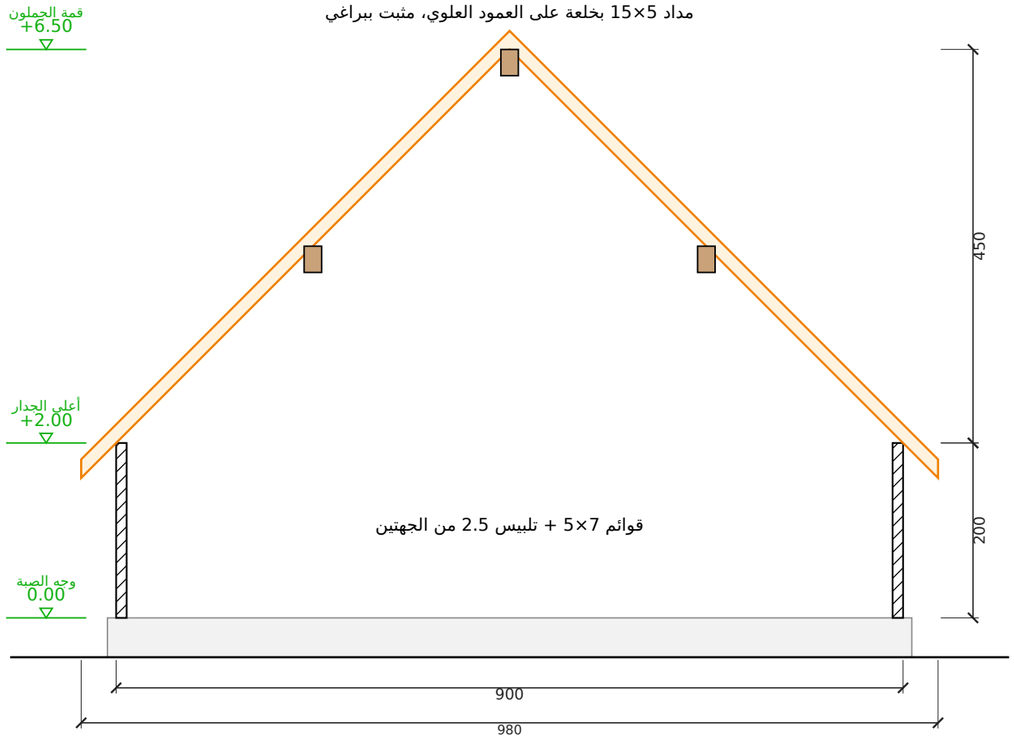

تفصيلة جلوس المداد على العلوي (1:5)

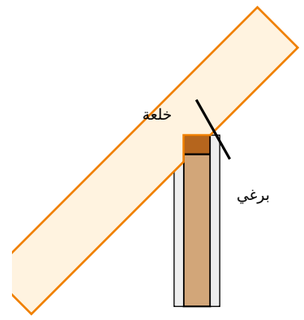

المشروع / العميل كوخ A-frame بواجهة زجاج + ميزانين — صالة وغرفة ومطبخ أمريكي وحمام — 9.00 × 10.00 م عميل — A-frame 9×10	عنوان اللوحة مسقط السقف والقطاع	المقياس 1:50	التاريخ 2026-10-23	رقم اللوحة A-05 (5/10)

مصنع وتد الأخشاب
Watad Wood Factory

جدول مقاسات الأبواب والشبابيك
مقاس الفتحة الصافي في الجدار - الوحدة: سم

الرمز	النوع	العرض (سم)	الارتفاع (سم)	ارتفاع الجلسة (سم)	العدد	الموقع
ب1	باب مزدوج	144	220	-	1	الأمامية (زجاج كامل)
ب2	باب	80	210	-	1	غرفة النوم
ب3	باب	70	210	-	1	الحمام
ش4	باب	120	100	-	1	الخلفية
ز1	شباك	190	190	5	2	الأمامية (زجاج كامل) 2
ز1	شباك	160	190	5	2	الأمامية (زجاج كامل) 2
ش1	شباك	120	90	60	3	الشرقية - الغربية 2
ش2	شباك	100	60	100	1	الشرقية
ش3	شباك	60	60	160	1	الخلفية

الإجمالي: أبواب 4 - شبابيك 9

مصنع وتد الأخشاب Watad Wood Factory	المشروع / العميل كوخ A-frame بواجهة زجاج + ميزانين — صالة وغرفة ومطبخ أمريكي وحمام — 9.00 × 10.00 م عميل — A-frame 9×10	عنوان اللوحة جدول الأبواب والشبابيك	المقياس —	التاريخ 2026-10-23	رقم اللوحة A-06 (6/10)

جدول المساحات وبيانات المشروع

بيانات المشروع

البند	البيان
المشروع	كوخ A-frame بواجهة زجاج + ميزانين — صالة وغرفة ومطبخ أمريكي وحمام — 9.00 × 10.00 م
العميل	عميل — A-frame 9×10
الموقع	—
الاستخدام	استراحة / سكن
التاريخ	2026-10-23
نظام البناء	هيكل خشب 5×7 + تلبيس 2.5 سم من الجهتين
السقف	جملون 45° — قرميد معدني

جدول المساحات

م	الفراغ	الأبعاد (م)	المساحة (م2)
1	الصالة (ارتفاع مزدوج)	8.76 × 4.94	43.27
2	غرفة النوم	3.94 × 4.64	18.28
3	المطبخ الأمريكي	4.70 × 2.70	12.69
4	الحمام	2.70 × 1.88	5.08
5	مخزن / غسيل	1.88 × 1.88	3.53
	المساحة الصافية الداخلية		**82.86**
	عتبة المدخل	**2.40 × 1.40**	**3.36**
	المساحة الإجمالية المبنية	**9.00 × 10.00**	**90.00**
	المساحة الكلية (المبنية + التراس)		**93.36**

لقطات المنظور الخارجي

المنظور الأمامي




منظور أمامي من اليسار



منظور أمامي من اليمين




المنظور الخلفي

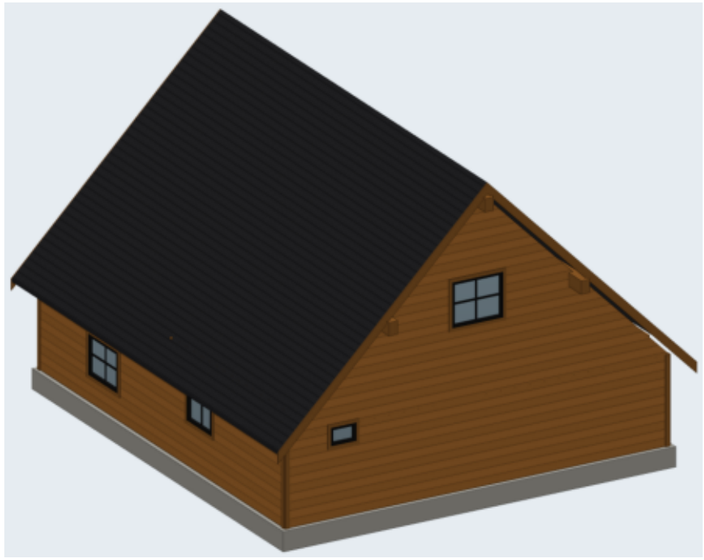

منظور خلفي من اليمين




منظر علوي

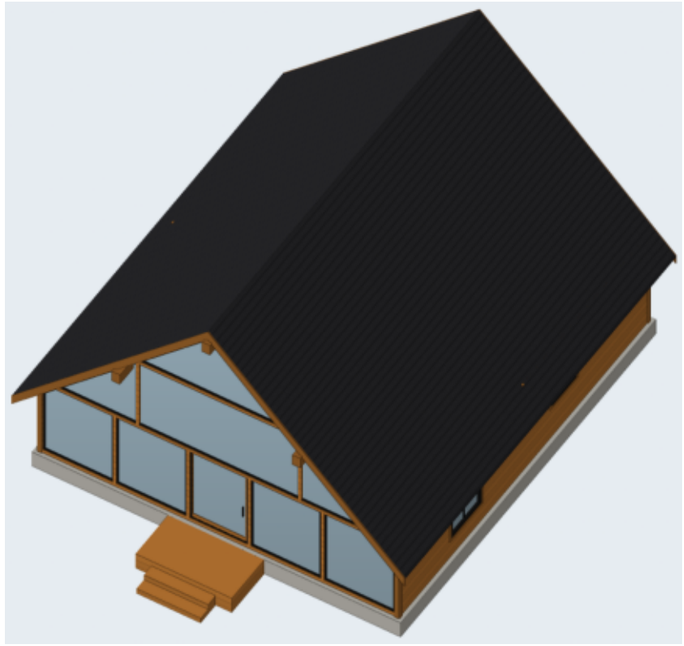

مصنع وتد الأخشاب Watad Wood Factory	المشروع / العميل **كوخ A-frame بواجهة زجاج + ميزانين — صالة وغرفة ومطبخ أمريكي وحمام — 9.00 × 10.00 م** **عميل — A-frame 9×10**	عنوان اللوحة **لقطات المنظور**	المقياس **—**	التاريخ **2026-10-23**	رقم اللوحة **A-08 (8/10)**

المقطع العلوي بالفرش

مقطع أفقي على ارتفاع 1.90 م — توزيع الفرش ومسار الحركة

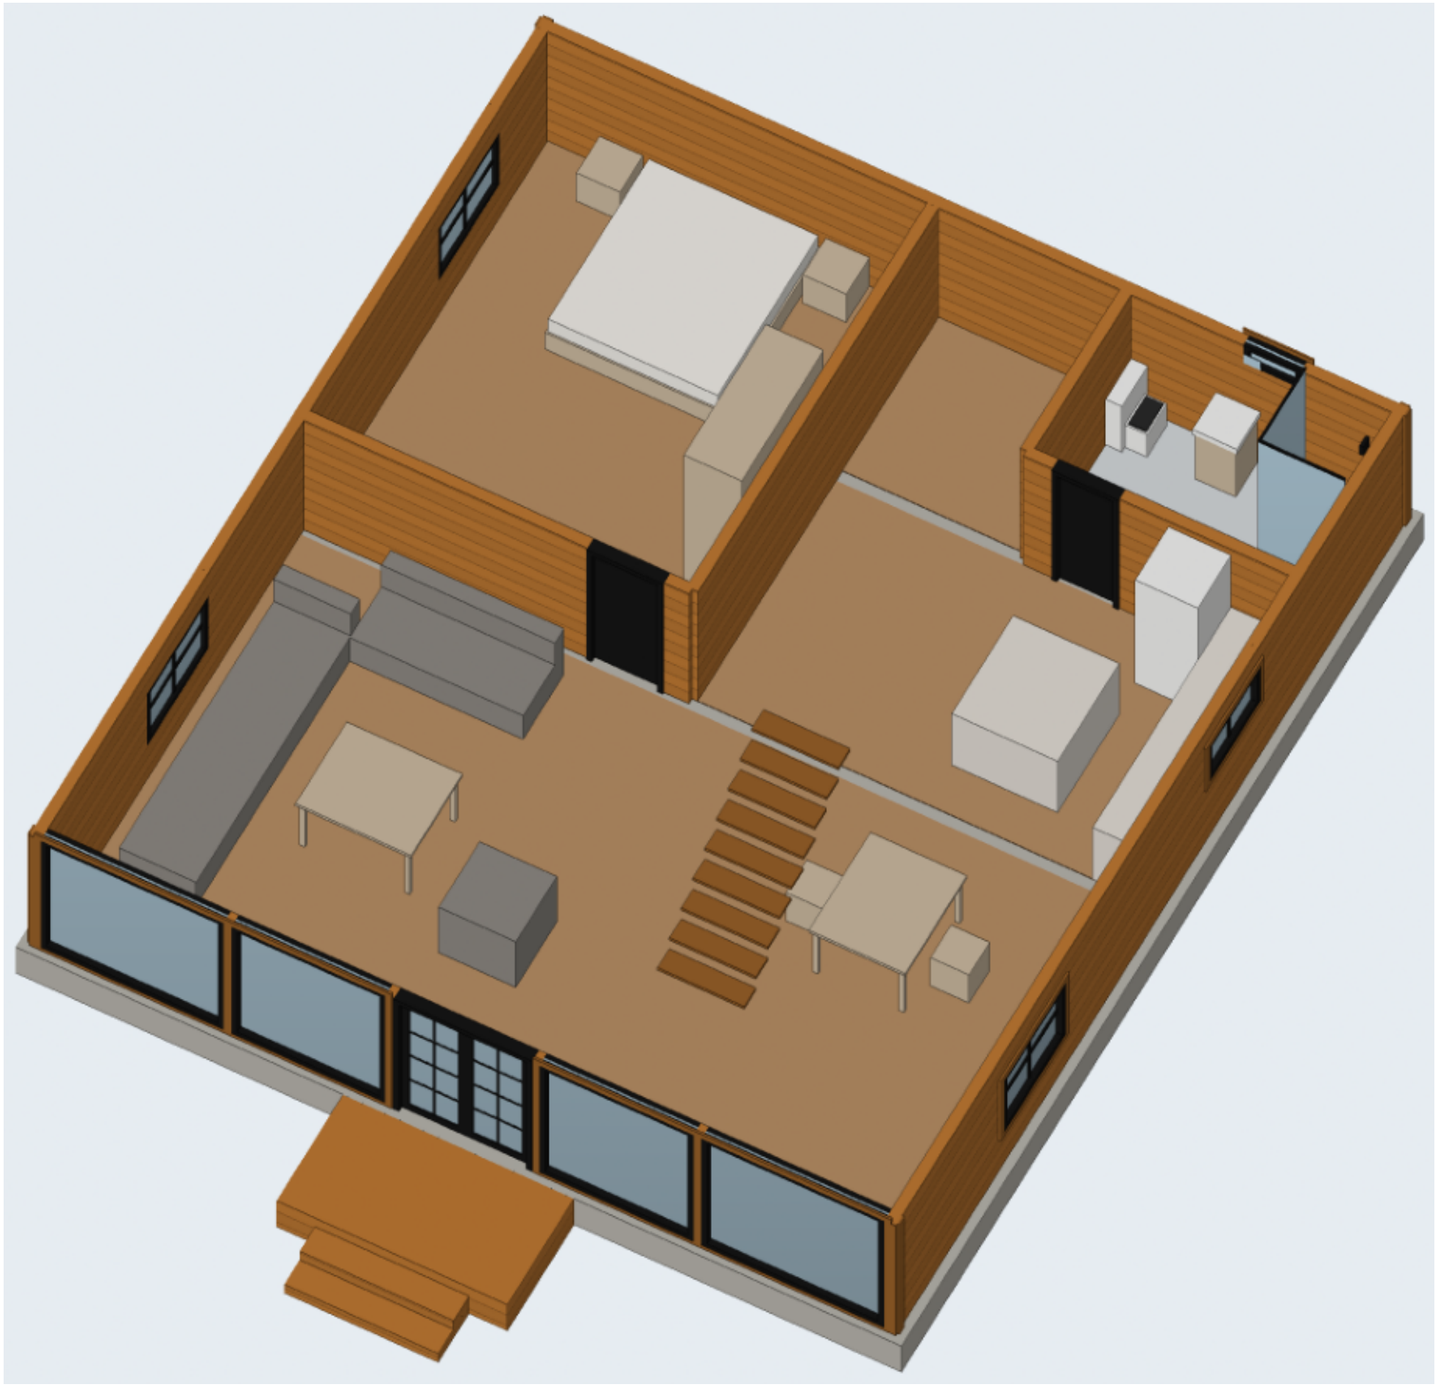

مصنع وتد الأخشاب Watad Wood Factory	المشروع / العميل كوخ A-frame بواجهة زجاج + ميزانين — صالة وغرفة ومطبخ أمريكي وحمام — 9.00 × 10.00 م عميل — A-frame 9×10	عنوان اللوحة المقطع العلوي بالفرش	المقياس —	التاريخ 2026-10-23	رقم اللوحة A-09 (9/10)

المنظور ثلاثي الأبعاد والمواد

النمط: جوزي غامق + إطارات سوداء — رندر واقعي بخامات حقيقية



جدول المواد والألوان

الخشب / الصبغة

صبغة عسلي / سيدر

القرميد

قرميد رمادي غامق

الزجاج

زجاج شفاف

إطارات الشبابيك والأبواب

إطار ألمنيوم أسود

الكنار والزوايا

نفس الصبغة أغمق درجة


الصبة

خرسانة 45 سم


الدربزين: ألواح أفقية متقاربة (عصري)

تقسيم الشبابيك: بدون | الباب الرئيسي: زجاج بتقسيمات (فرنسي)

أنواع الدربزين المعتمدة (من مشاريع المصنع)

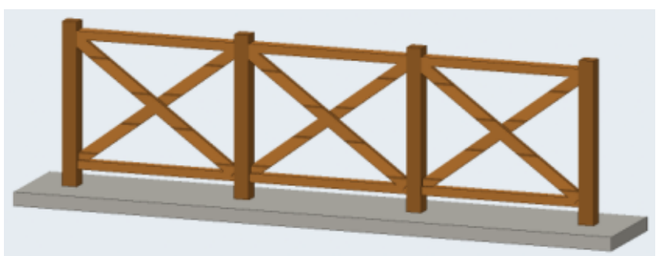

تقاطع X (صورة 5)

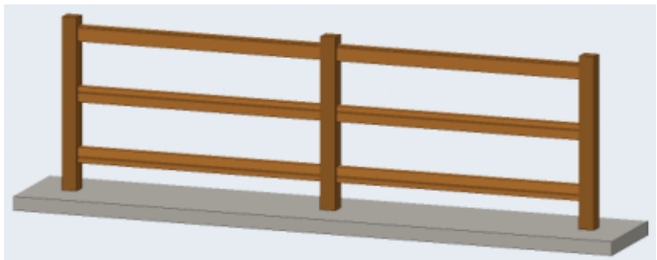

3 مرابيع أفقية (صورة 2)



قوائم رأسية متقاربة (صورة 1)

المشروع / العميل	عنوان اللوحة	المقياس	التاريخ	رقم اللوحة
كوخ A-frame بواجهة زجاج + ميزانين — صالة وغرفة ومطبخ أمريكي وحمام — 9.00 × 10.00 م **عميل — A-frame 9×10**	**المنظور والمواد**	**—**	**2026-10-23**	**A-10 (10/10)**

مصنع وتد الأخشاب
Watad Wood Factory